




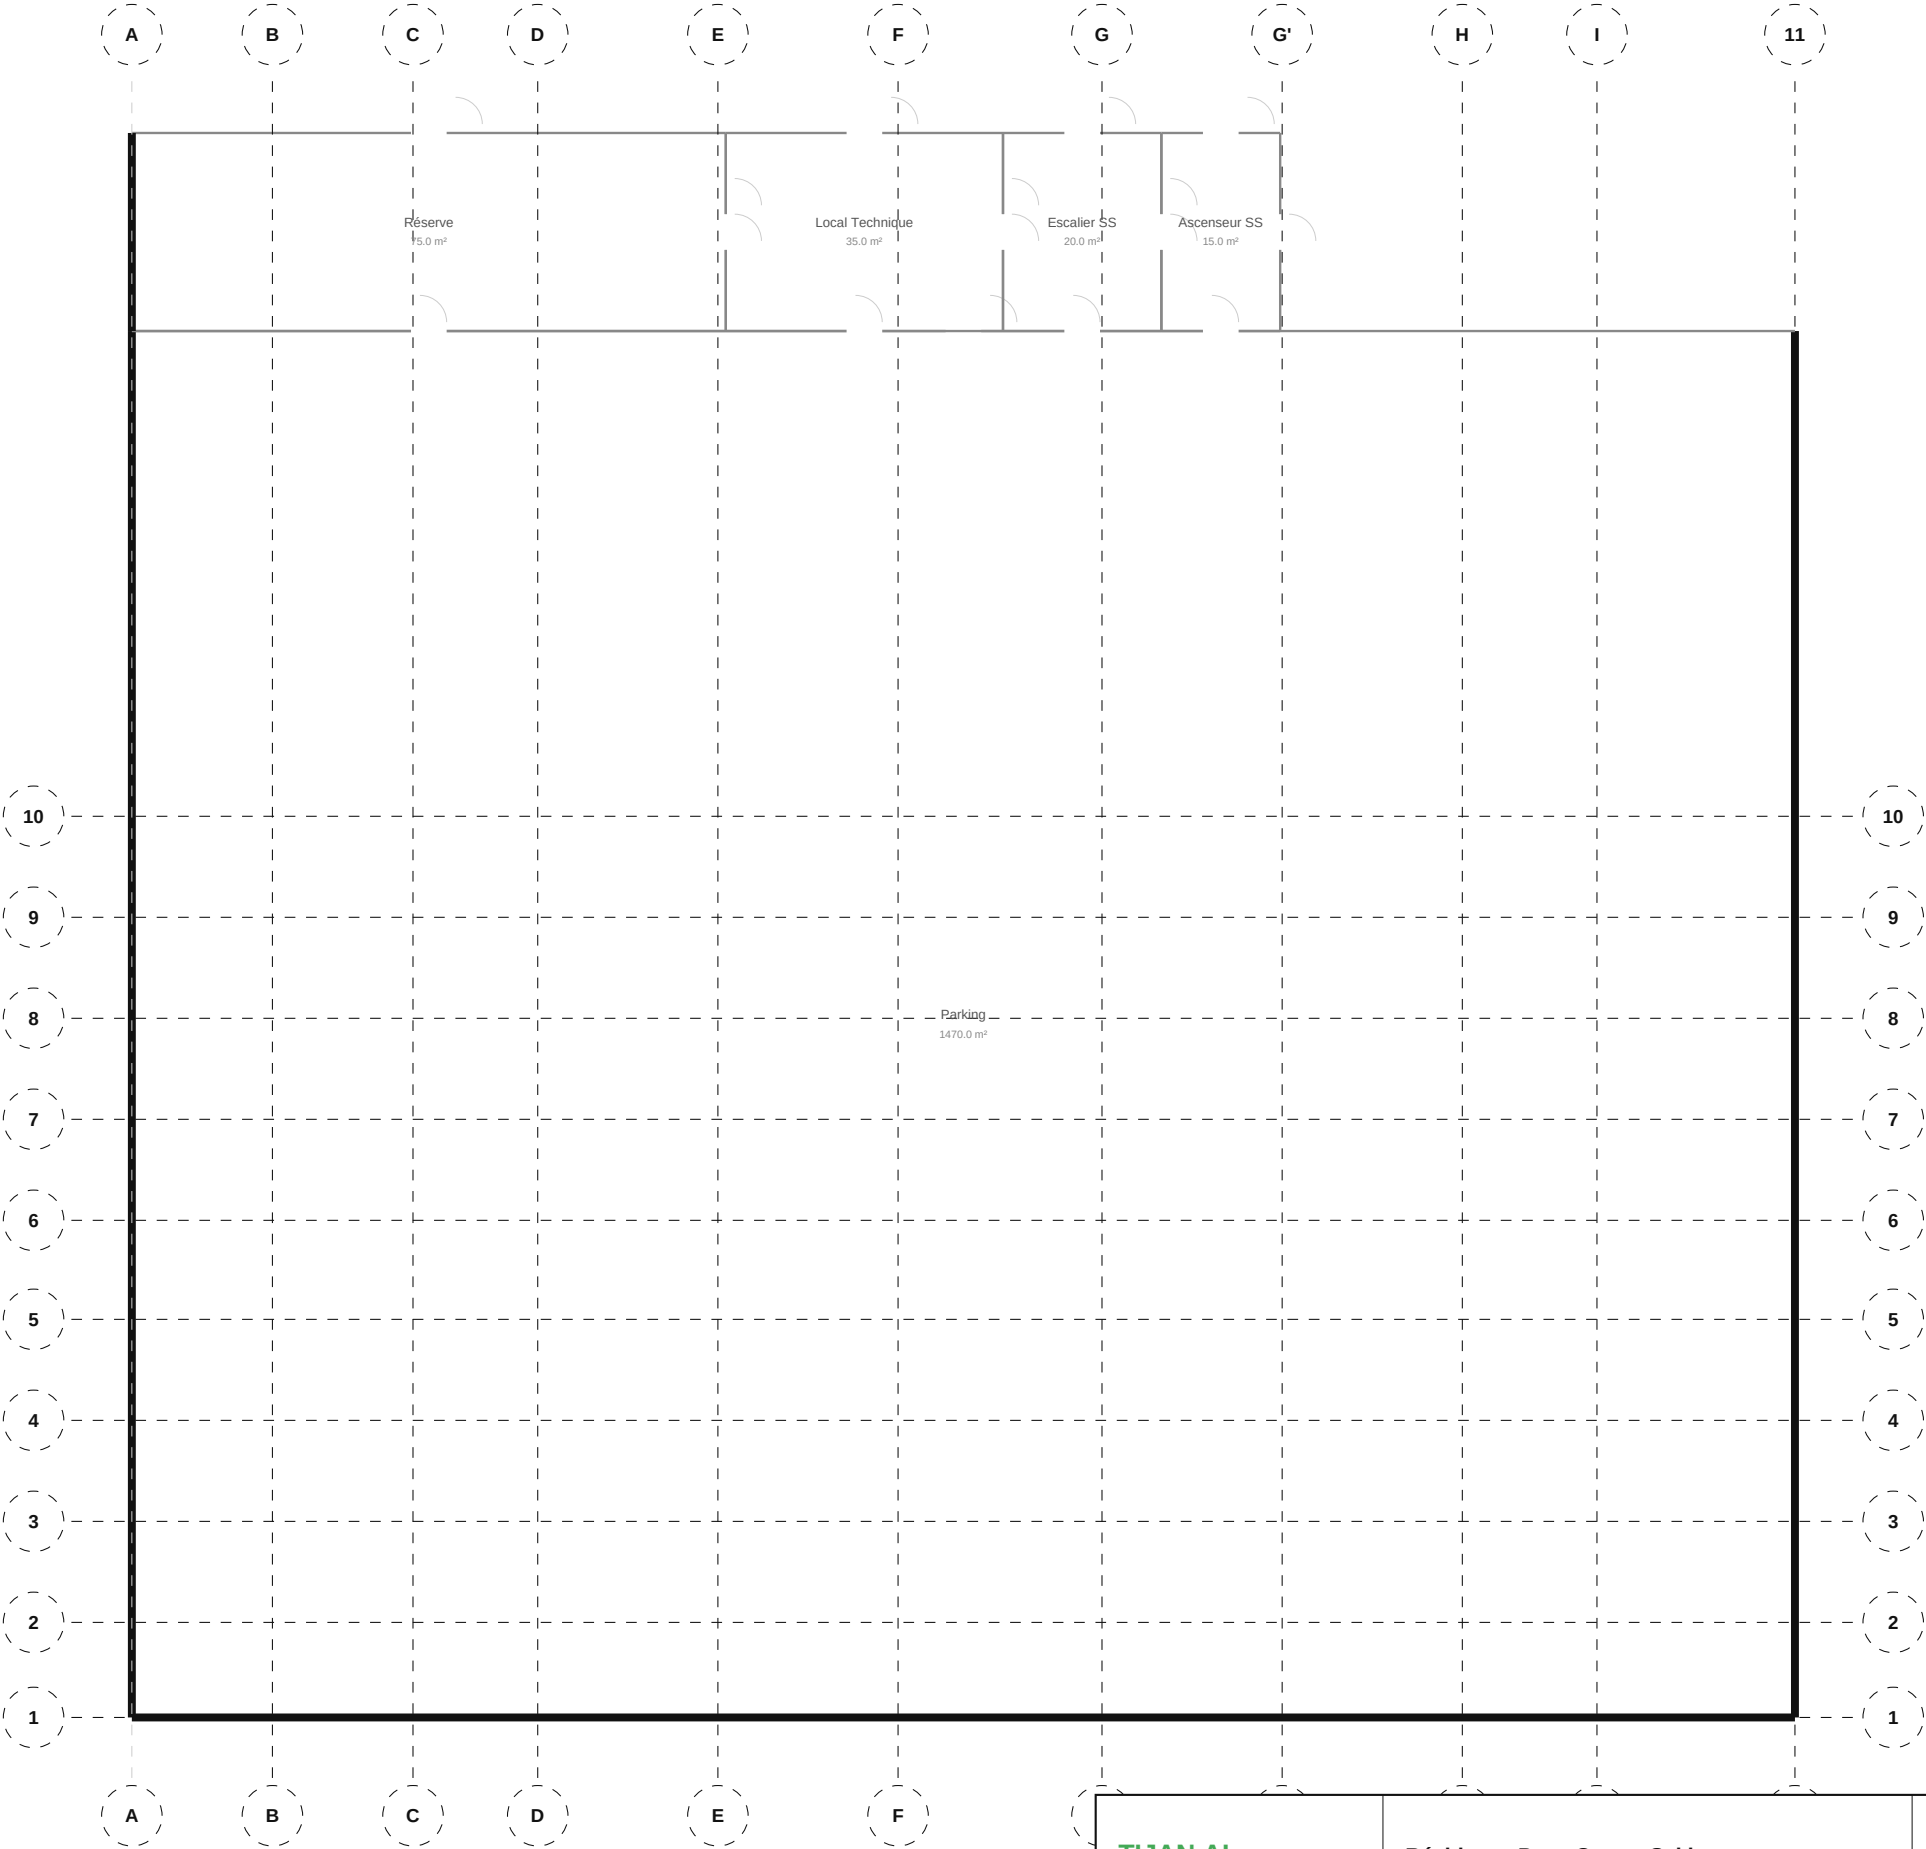


TIJAN AI Bureau d'Études Automatisé	Résidence Papa Oumar Sakho Dakar, Senegal	Éch: 1/100 Pl. 1/88
	Architecture — Sous-Sol	
Date: 06/05/2026	Réf: 1711	BIM vARC-001 Phase: APD

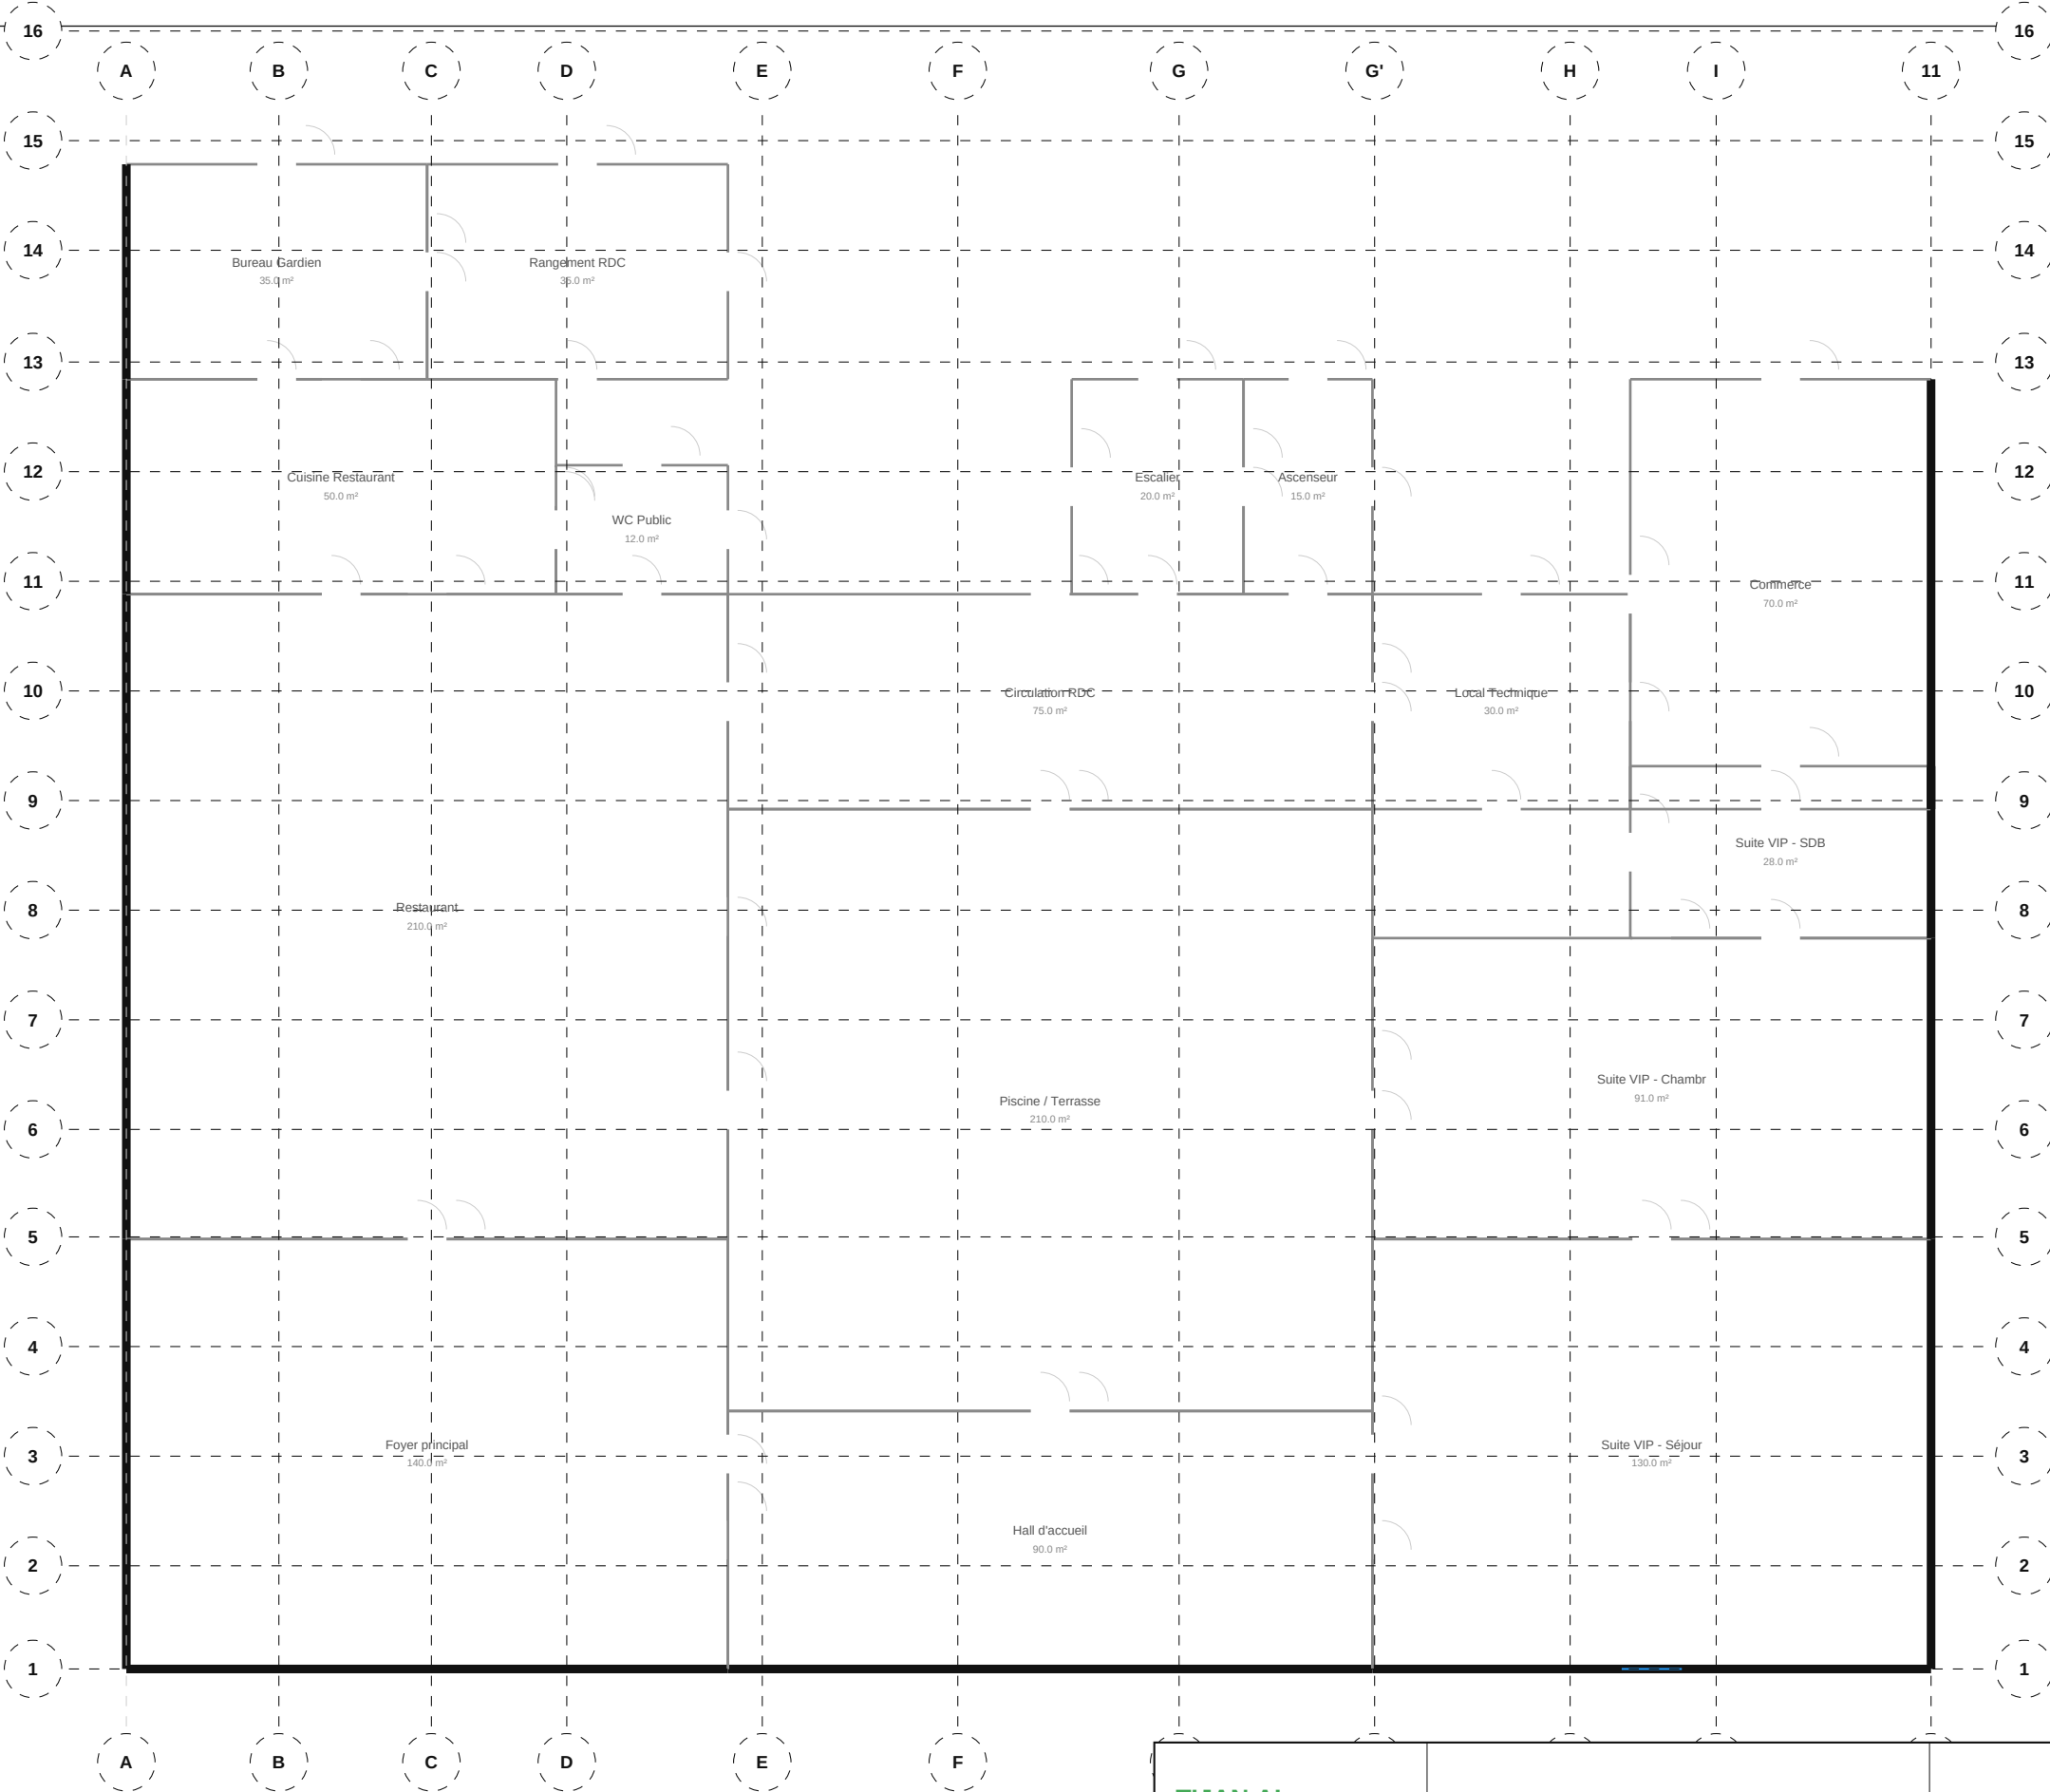


TIJAN AI Bureau d'Études Automatisé	Résidence Papa Oumar Sakho Dakar, Senegal	Éch: 1/100 Pl. 2/88
	Architecture — RDC	
Date: 06/05/2026	Réf: 1711	BIM vARC-002 Phase: APD

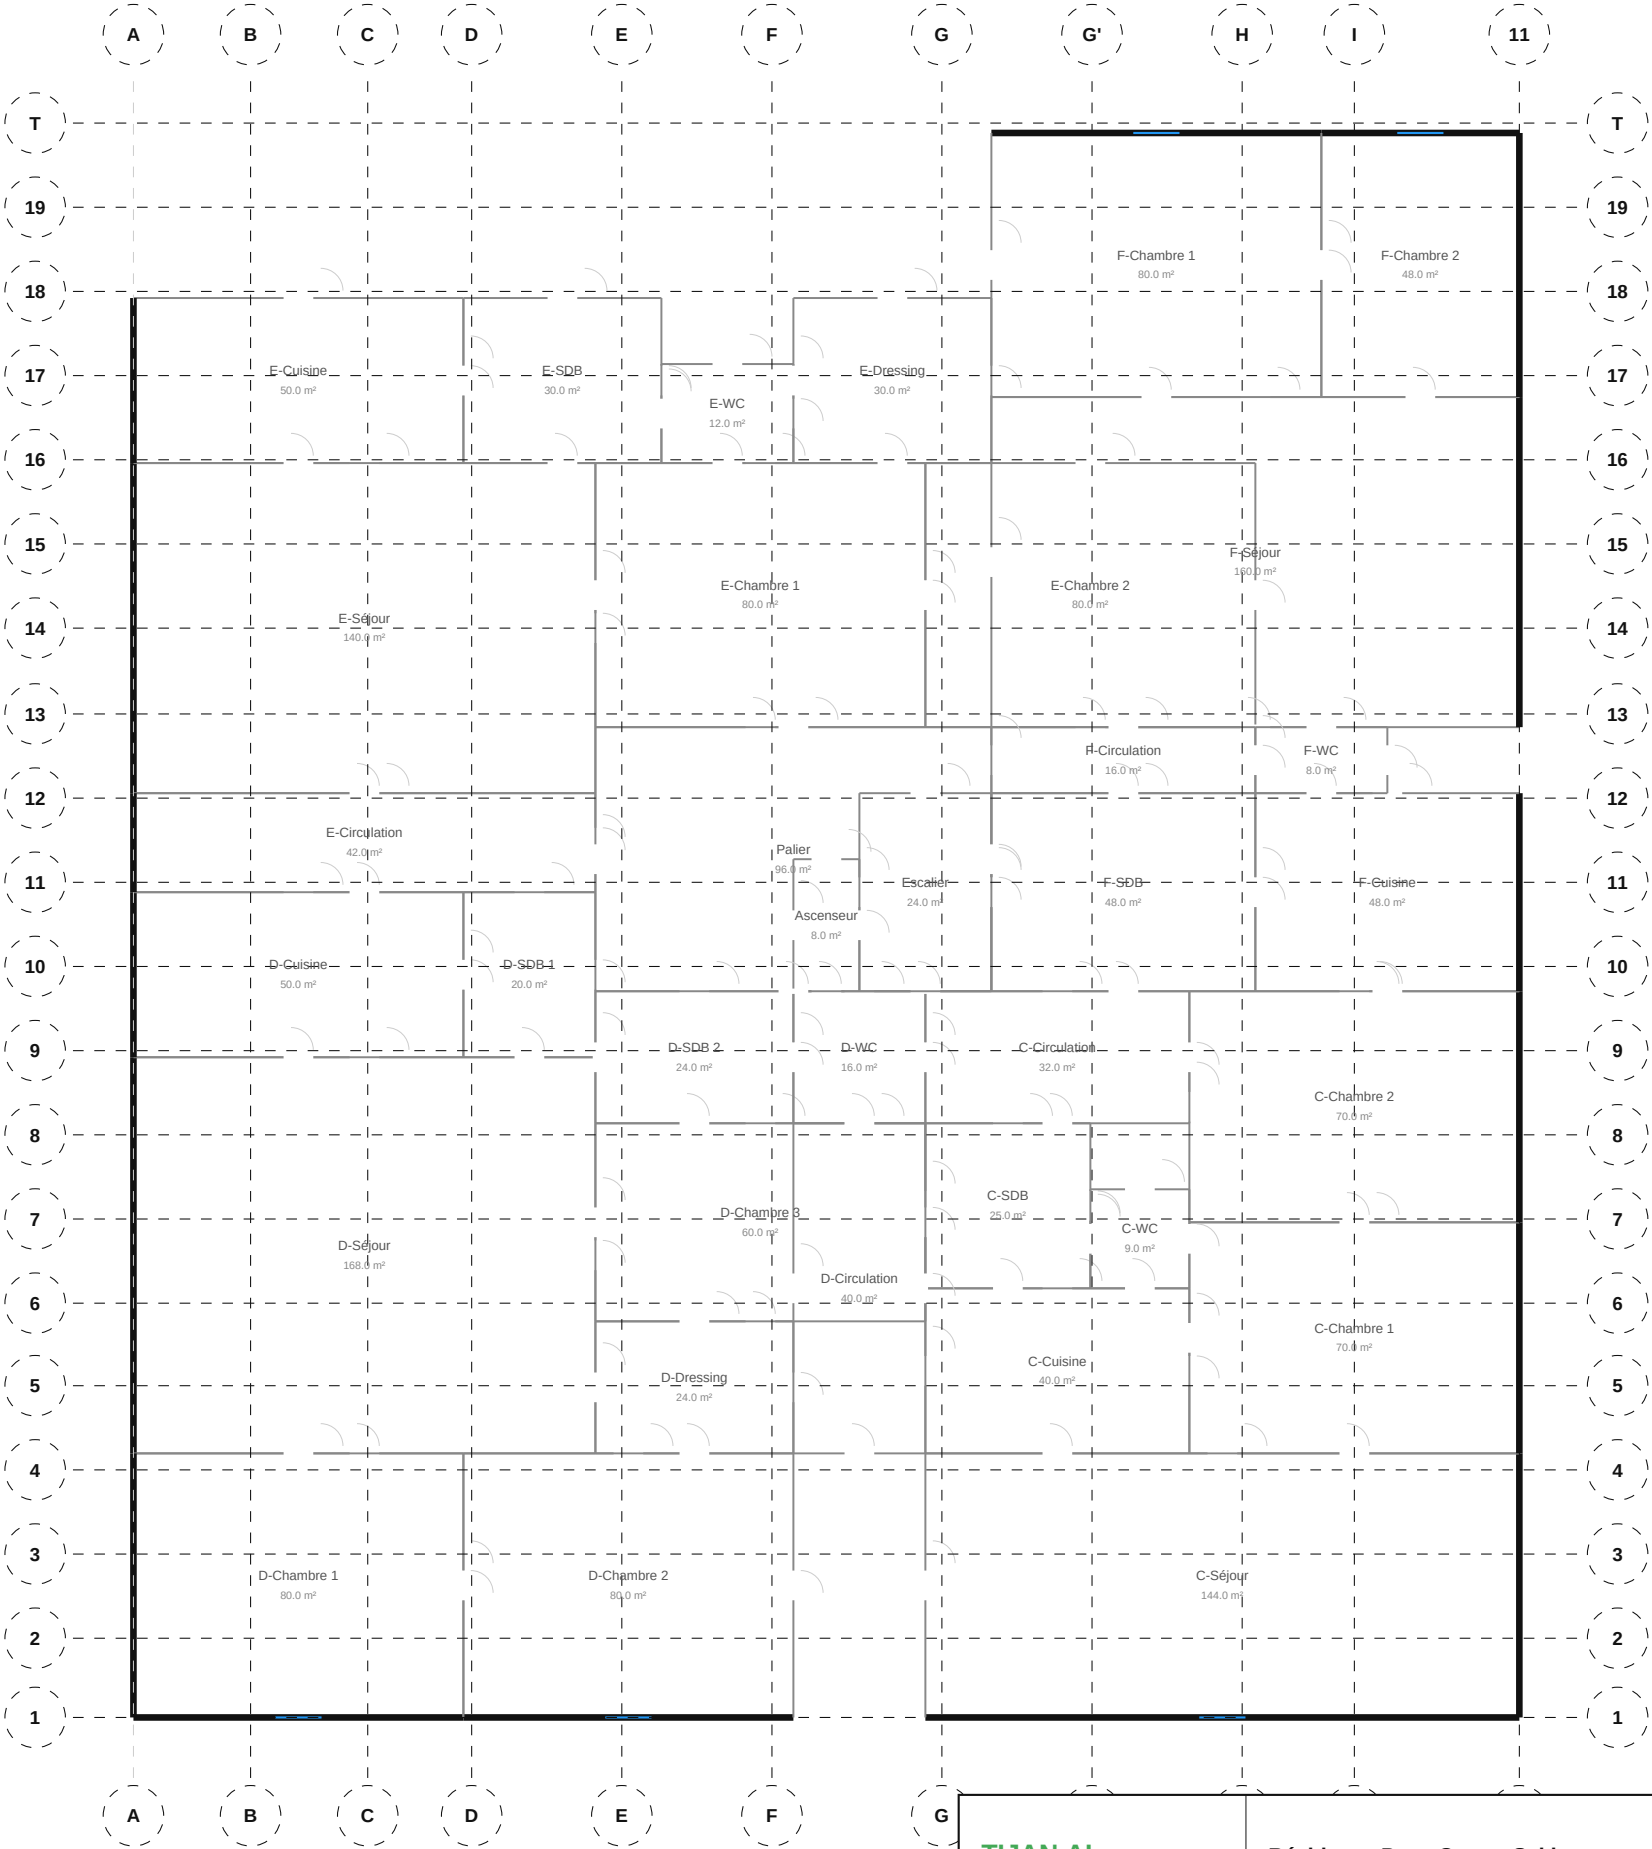


TIJAN AI Bureau d'Études Automatisé	Résidence Papa Oumar Sakho Dakar, Senegal	Éch: 1/100 Pl. 3/88
	Architecture — Étage 1	
Date: 06/05/2026	Réf: 1711	BIM vARC-003 Phase: APD

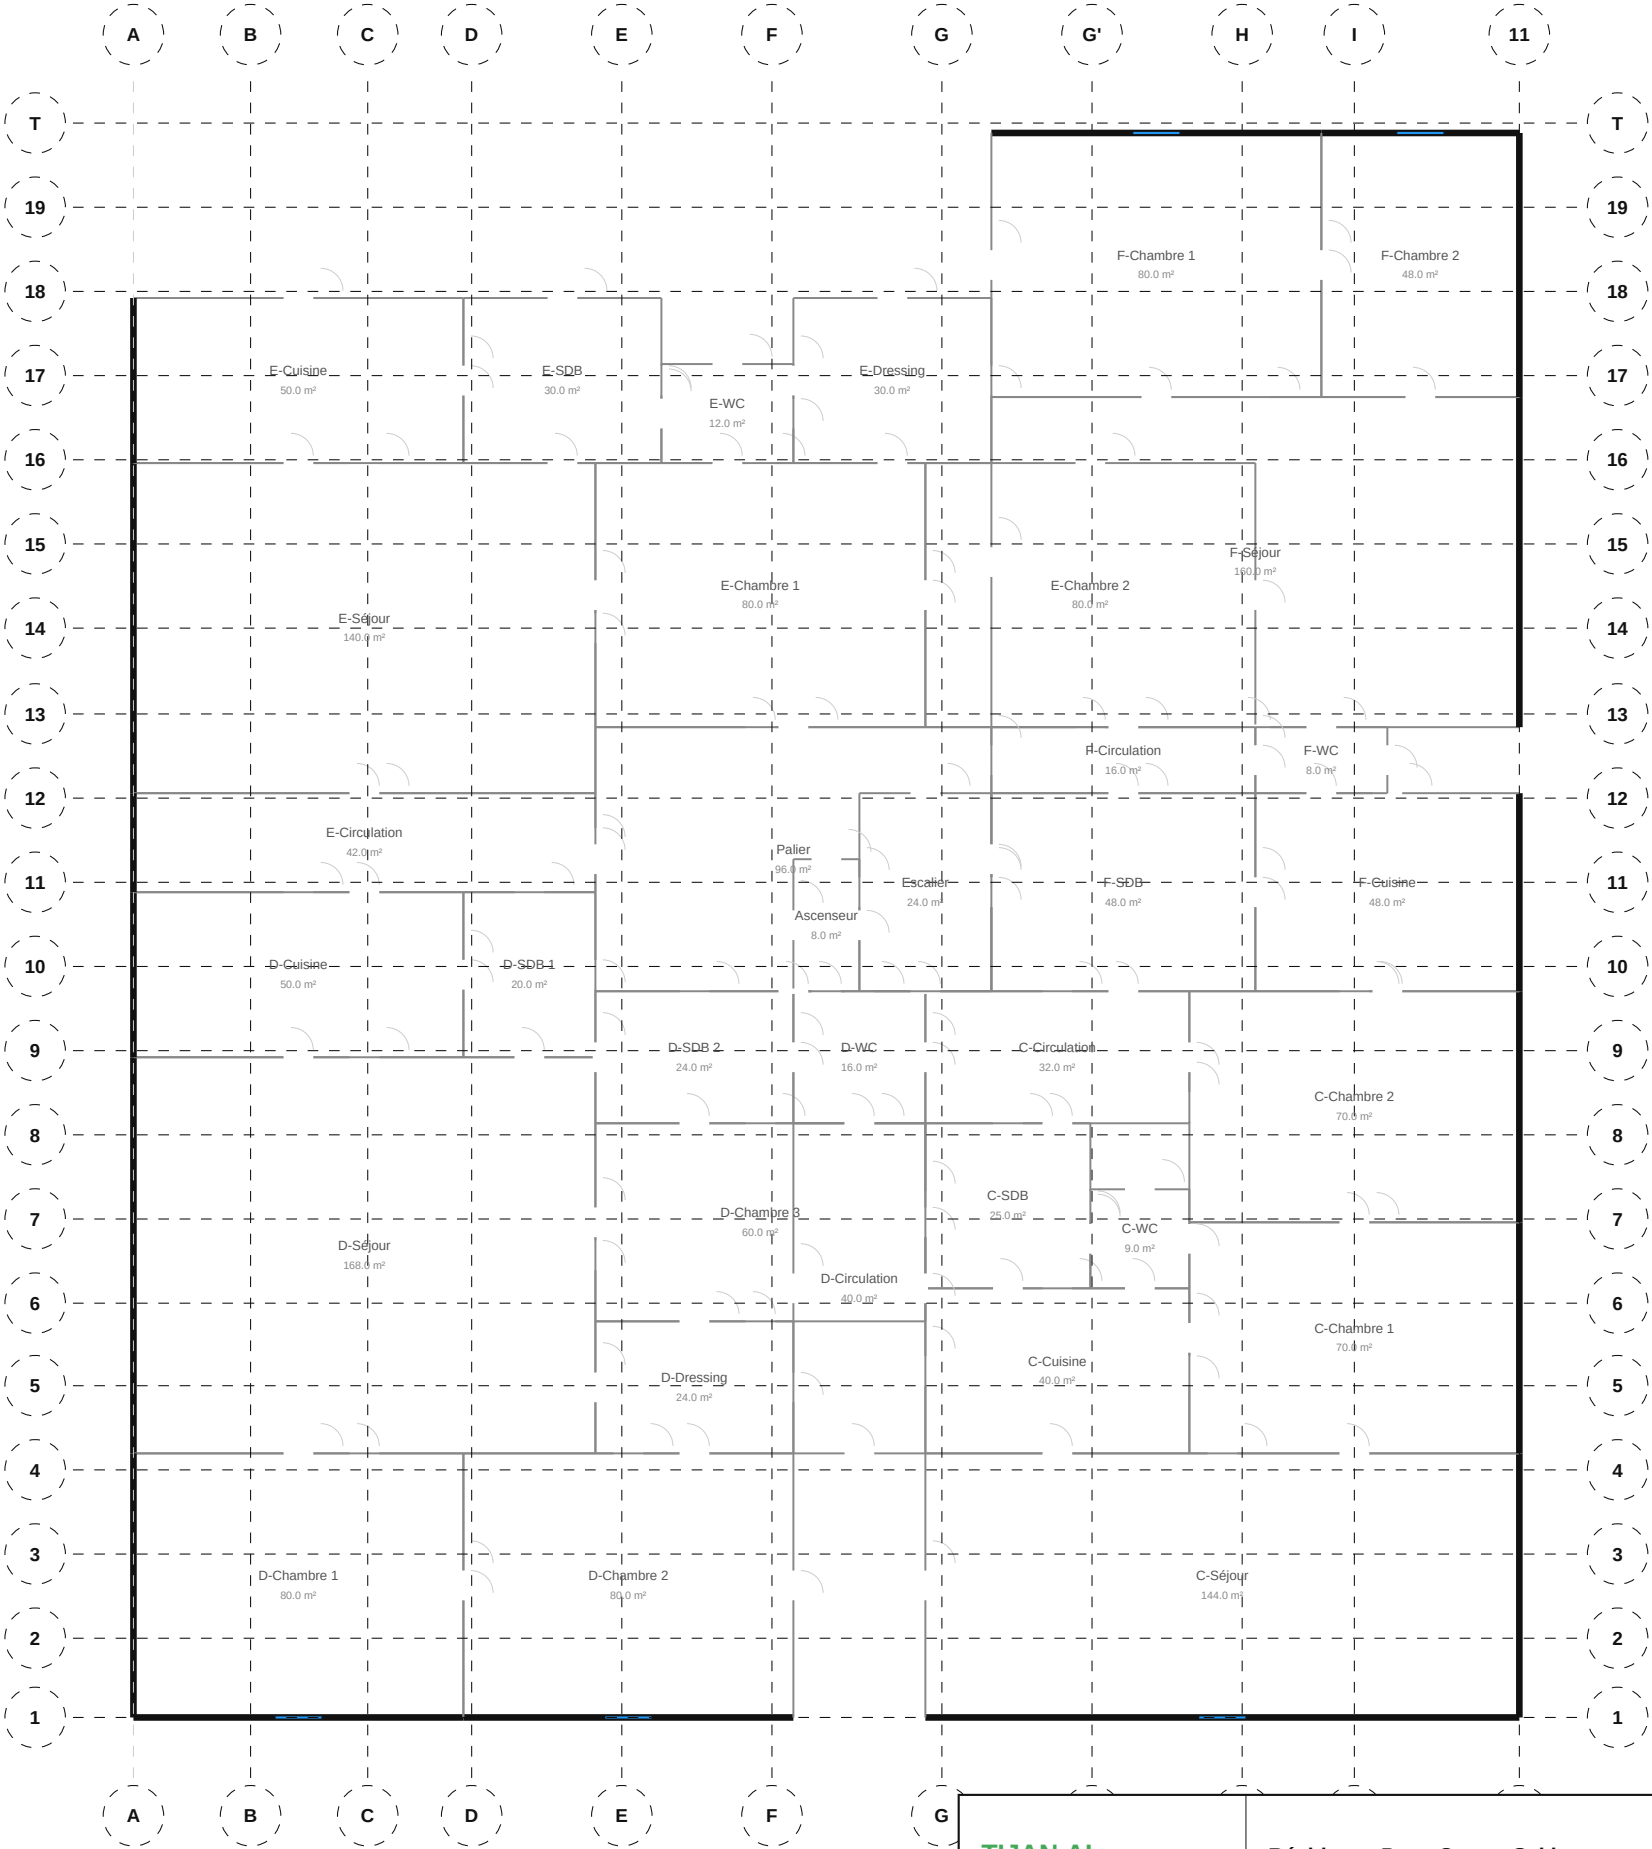


TIJAN AI Bureau d'Études Automatisé	Résidence Papa Oumar Sakho Dakar, Senegal	Éch: 1/100 Pl. 4/88
	Architecture — Étage 2	
	Date: 06/05/2026 Réf: 1711	BIM vARC-004 Phase: APD

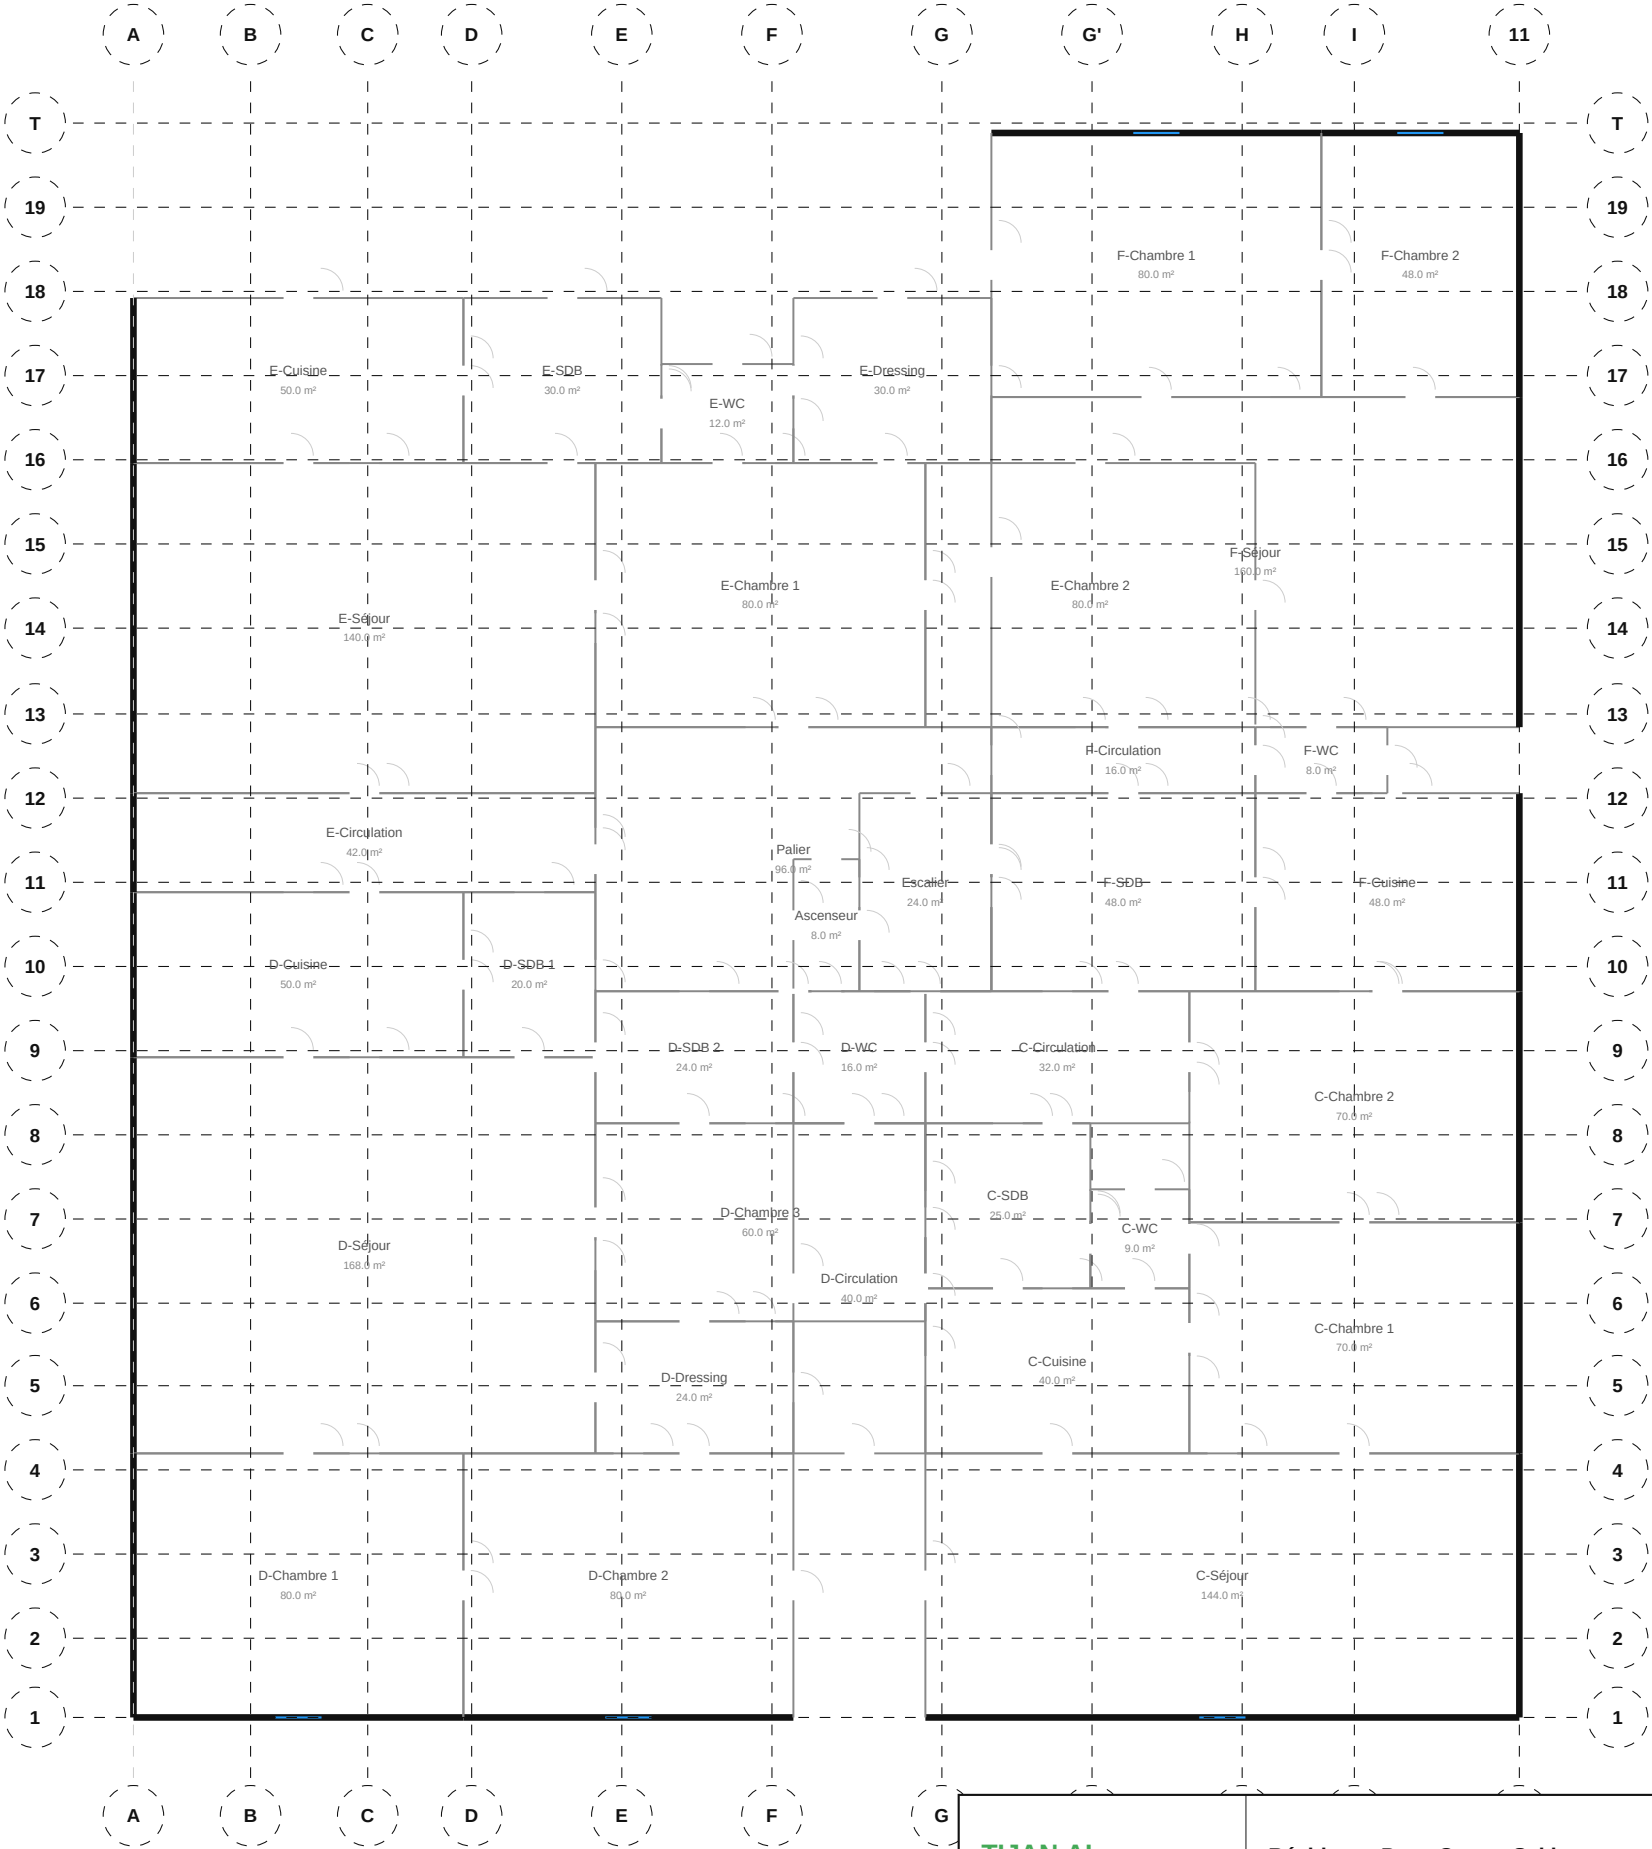


TIJAN AI Bureau d'Études Automatisé	Résidence Papa Oumar Sakho Dakar, Senegal	Éch: 1/100 Pl. 5/88
	Architecture — Étage 3	
	Date: 06/05/2026 Réf: 1711	BIM vARC-005 Phase: APD

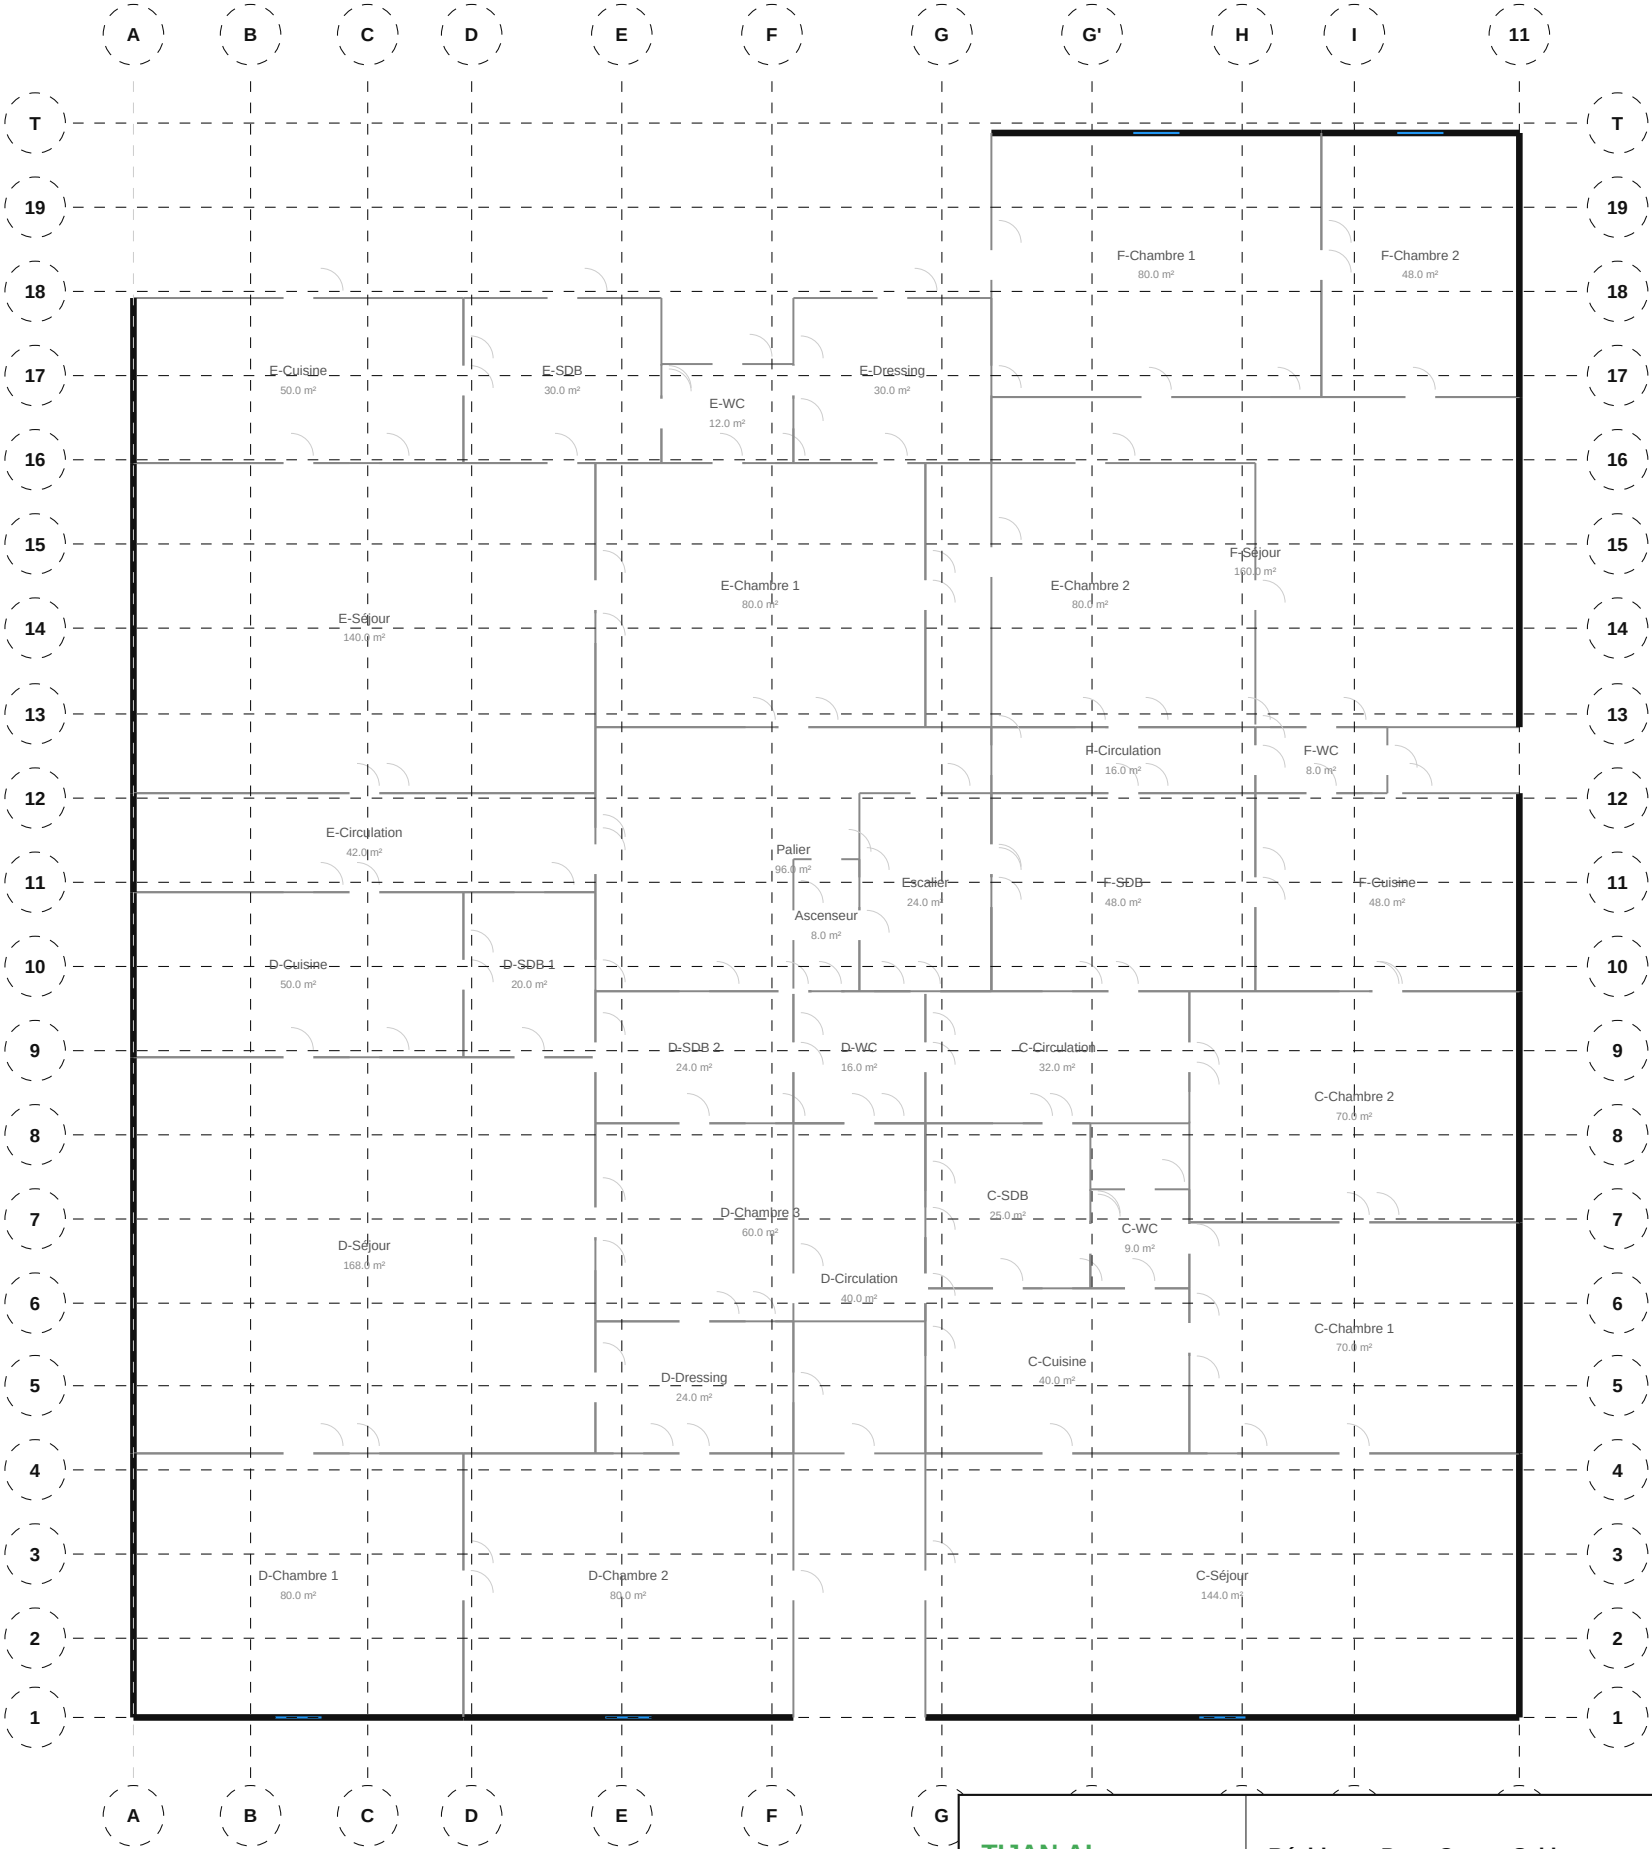


TIJAN AI Bureau d'Études Automatisé	Résidence Papa Oumar Sakho Dakar, Senegal	Éch: 1/100 Pl. 6/88
	Architecture — Étage 4	
	Date: 06/05/2026 Réf: 1711	BIM vARC-006 Phase: APD

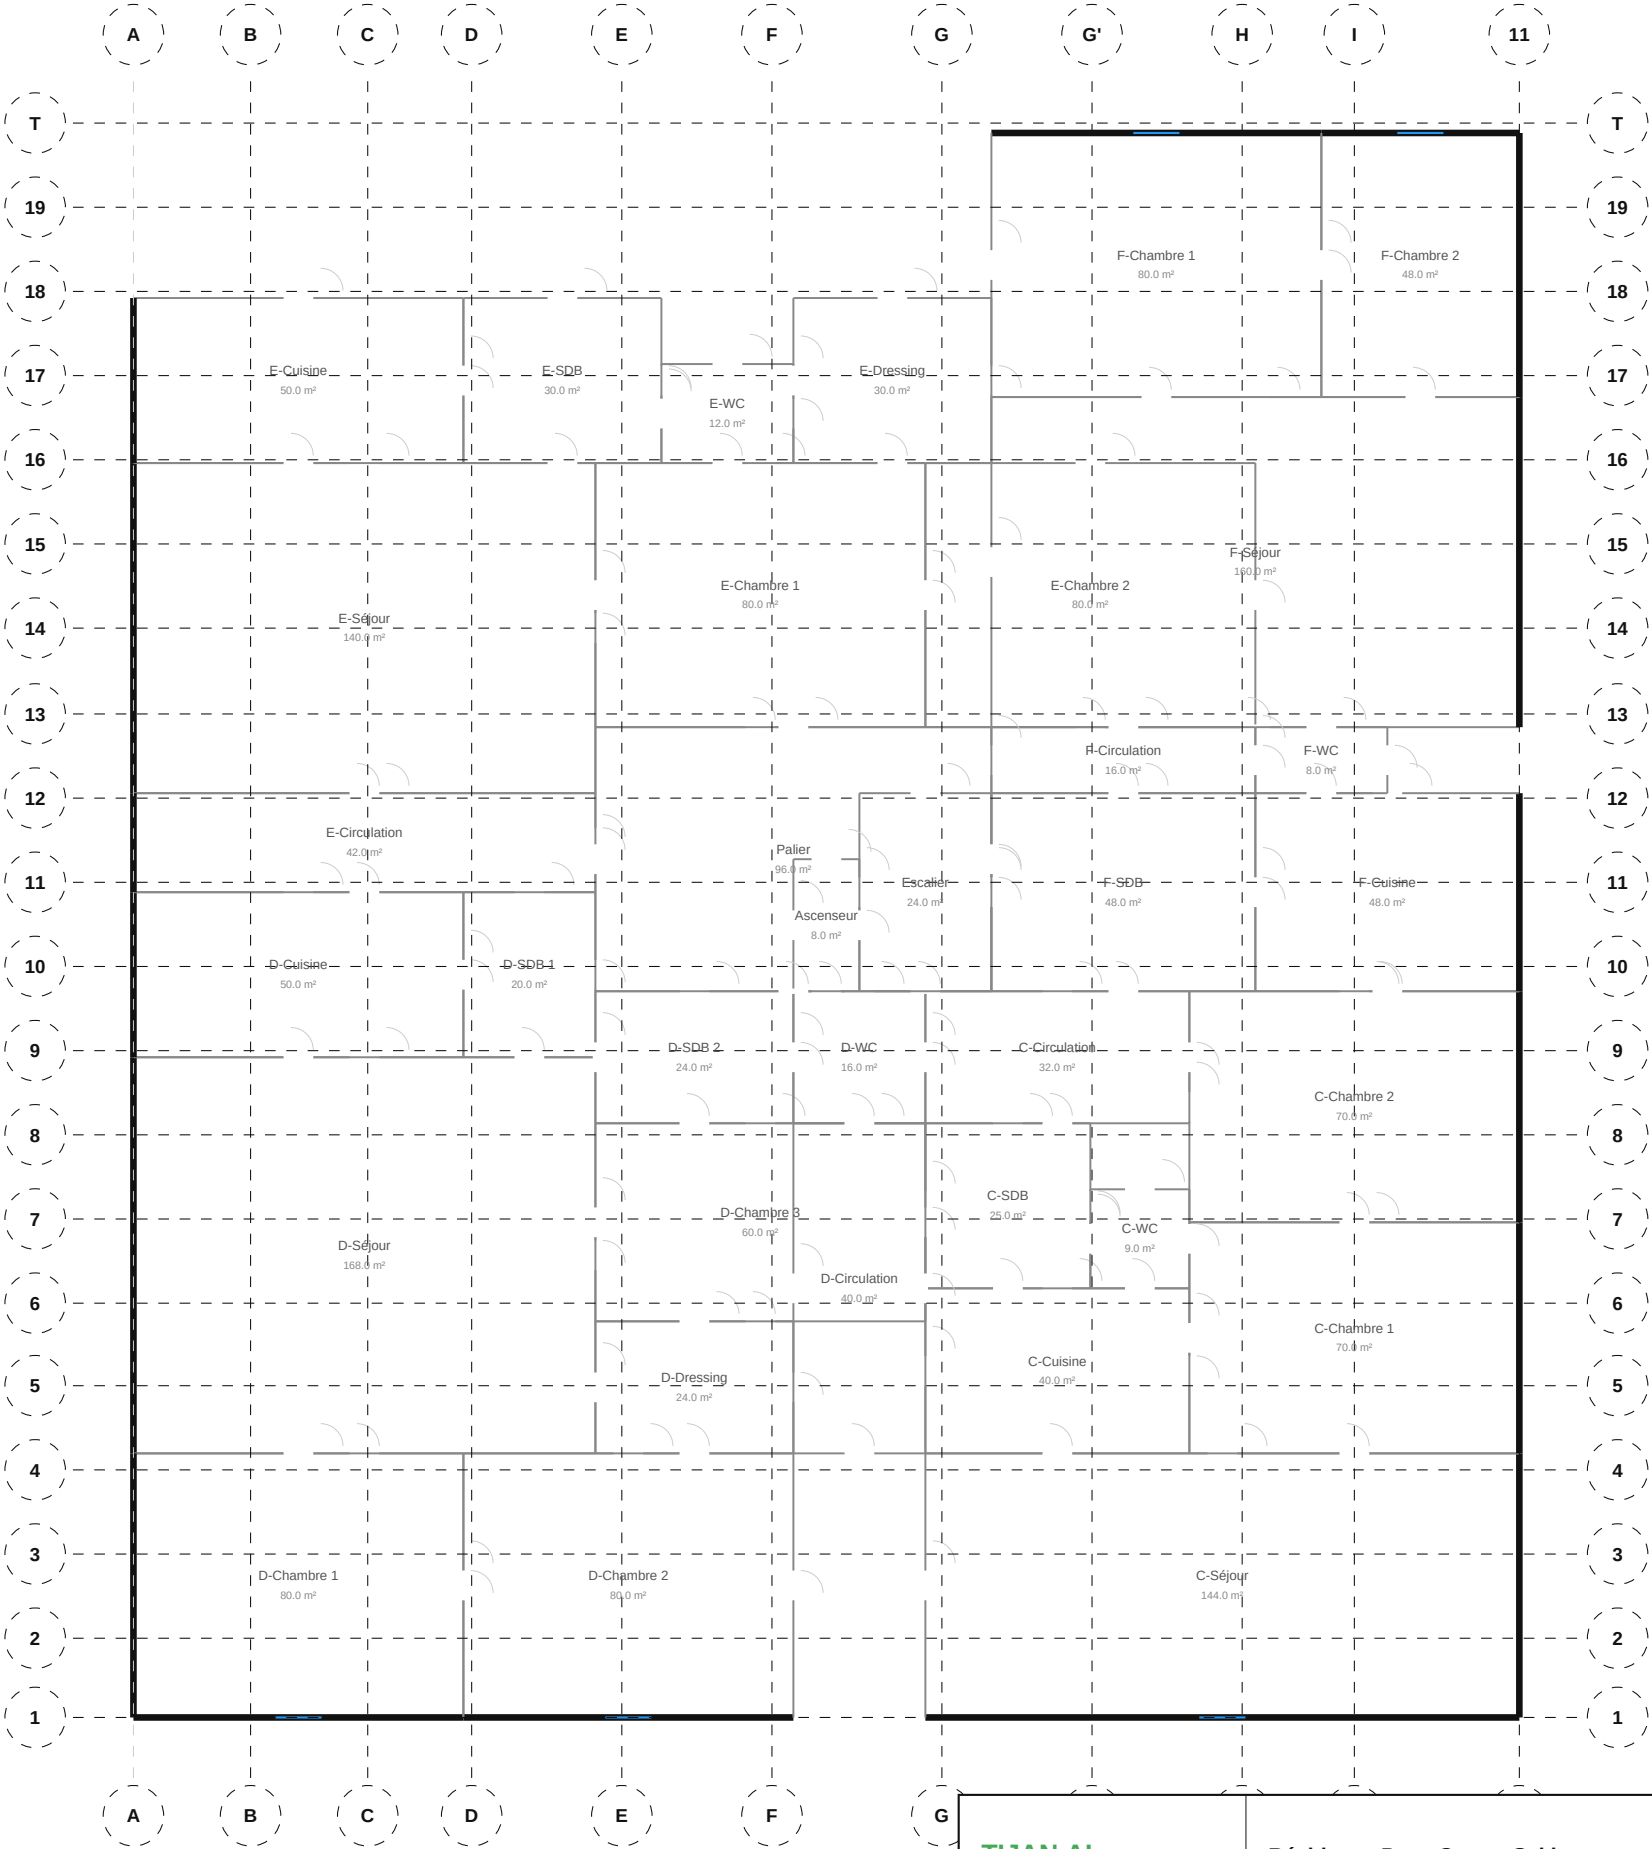


TIJAN AI Bureau d'Études Automatisé	Résidence Papa Oumar Sakho Dakar, Senegal	Éch: 1/100 Pl. 7/88
	Architecture — Étage 5	
	Date: 06/05/2026 Réf: 1711	BIM vARC-007 Phase: APD

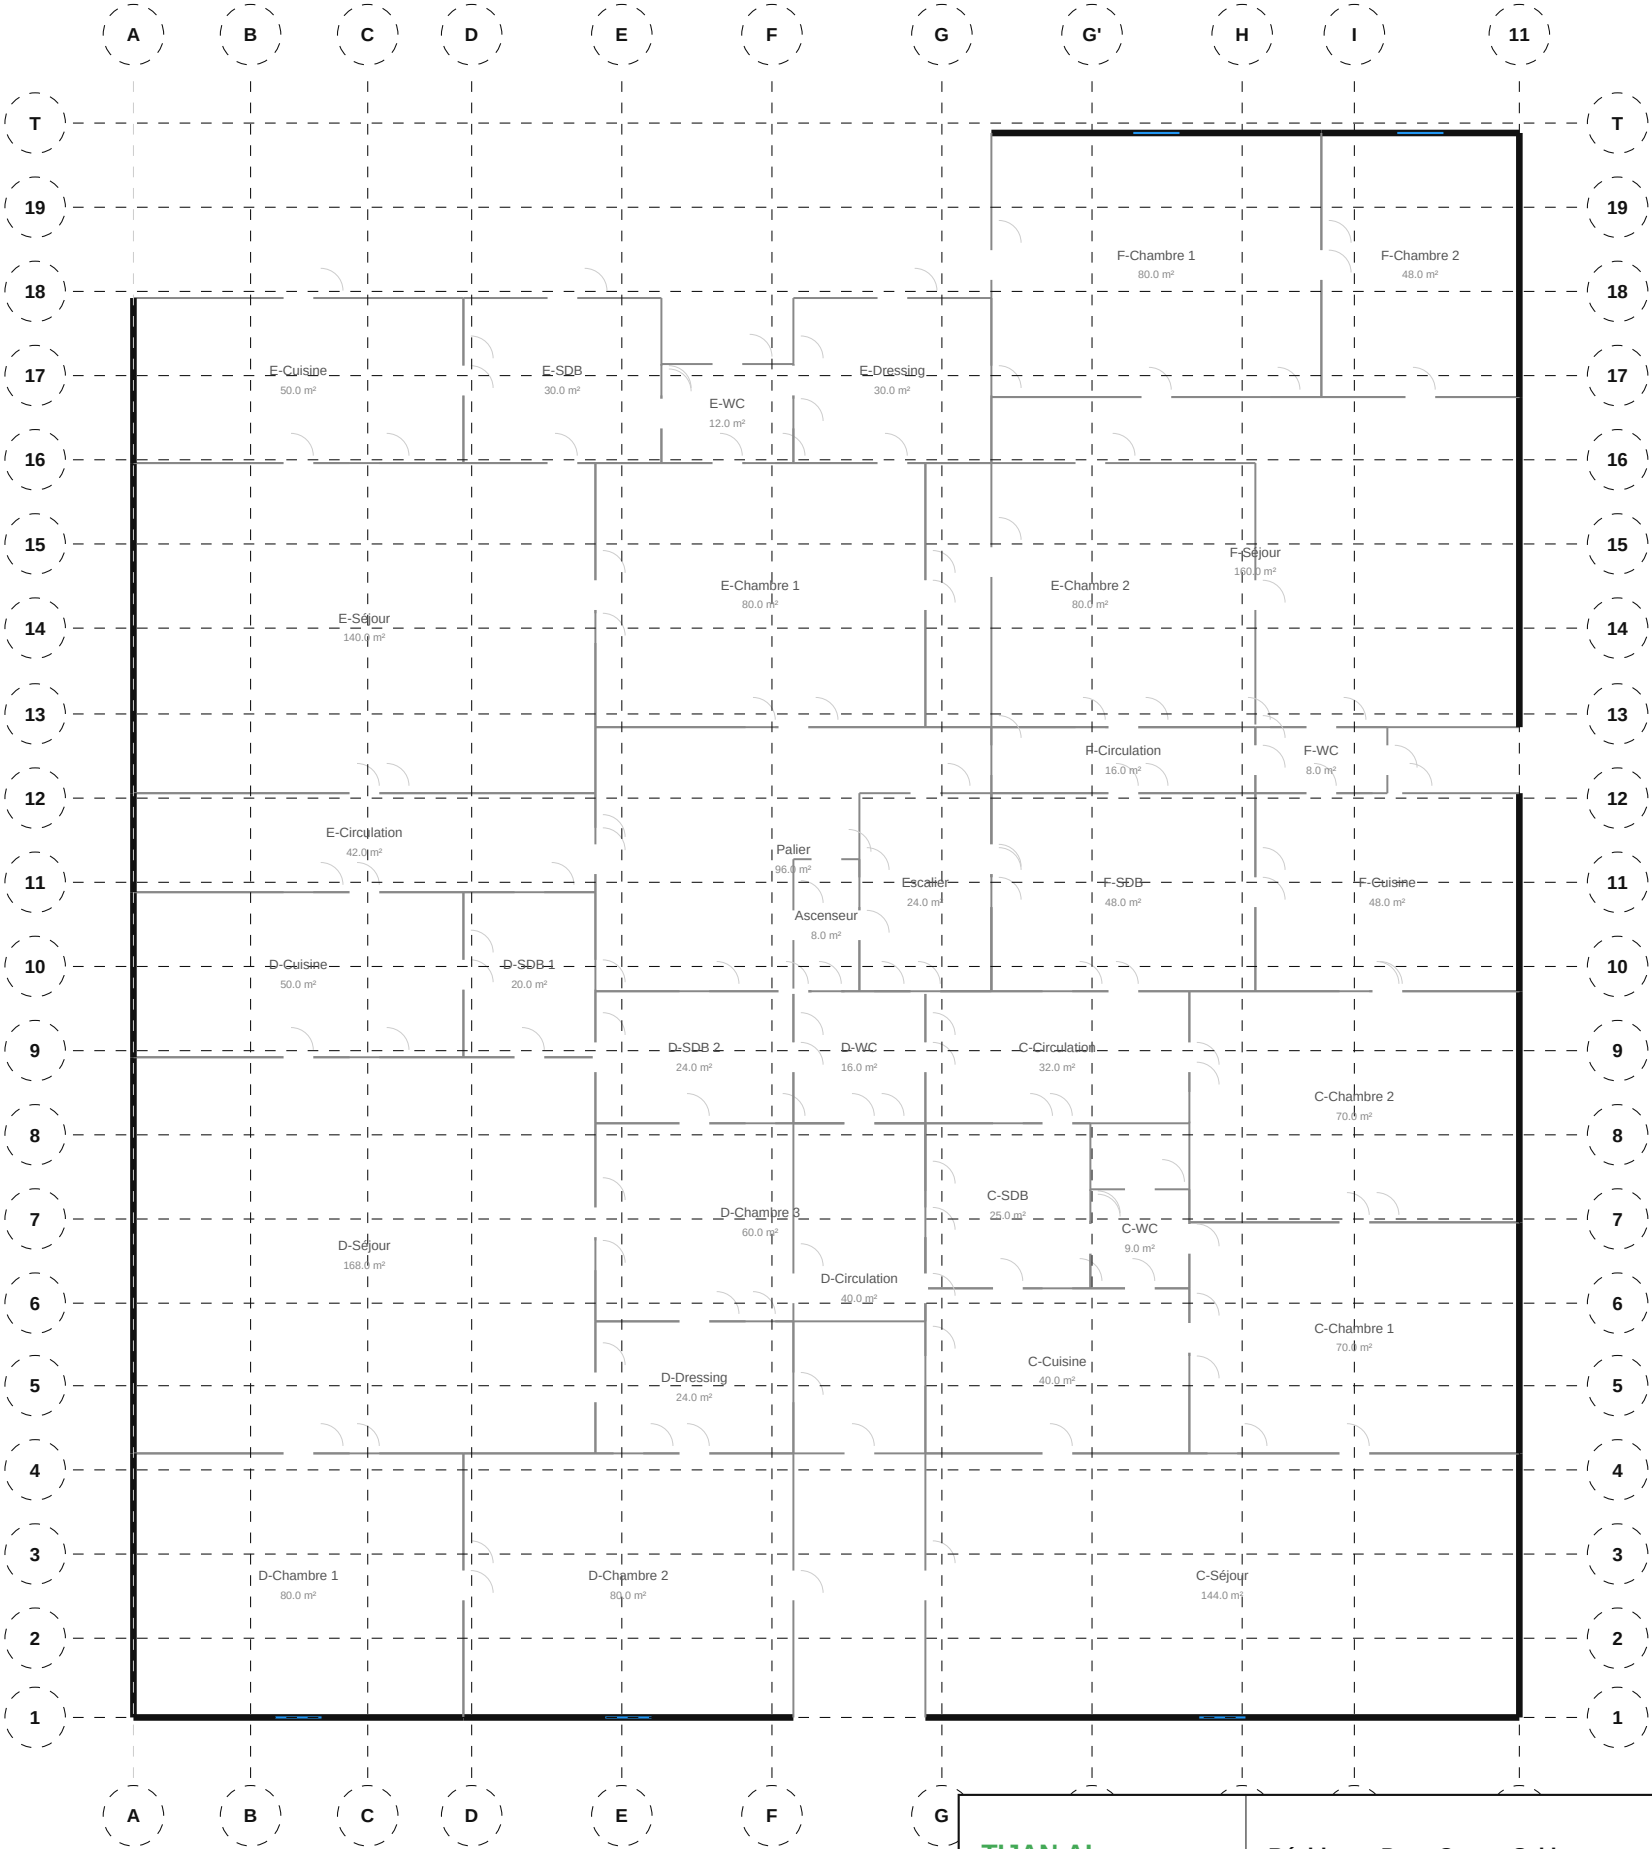


TIJAN AI Bureau d'Études Automatisé	Résidence Papa Oumar Sakho Dakar, Senegal	Éch: 1/100 Pl. 8/88
	Architecture — Étage 6	
	Date: 06/05/2026 Réf: 1711	BIM VARC-008 Phase: APD

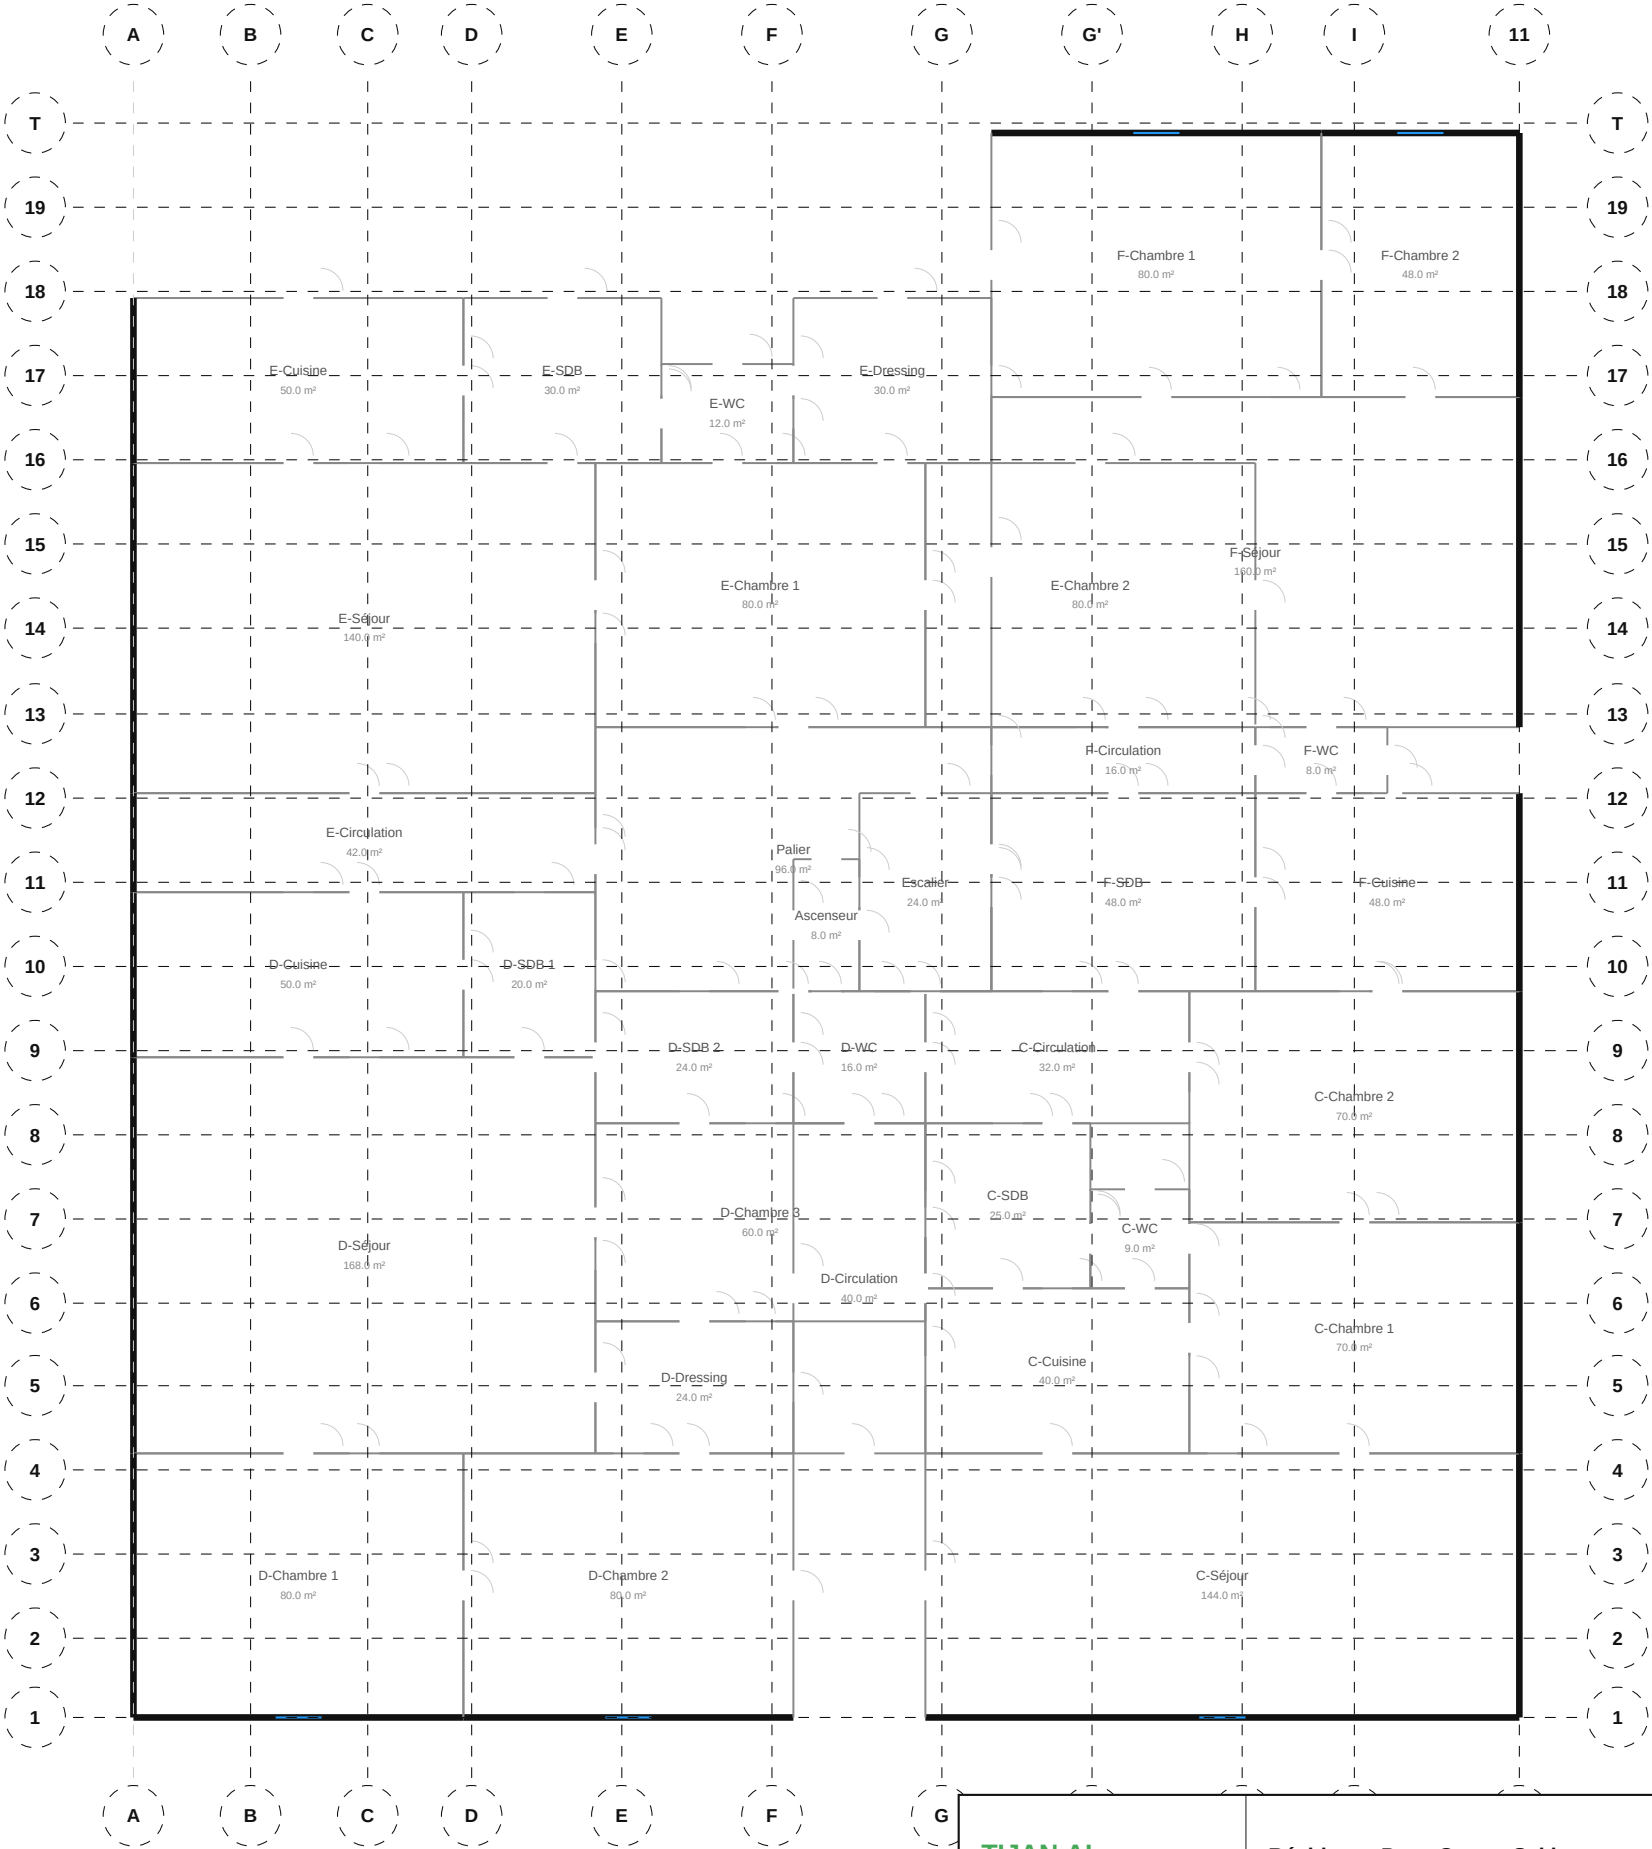


TIJAN AI Bureau d'Études Automatisé	Résidence Papa Oumar Sakho Dakar, Senegal	Éch: 1/100 Pl. 9/88
	Architecture — Étage 7	
	Date: 06/05/2026 Réf: 1711	BIM vARC-009 Phase: APD

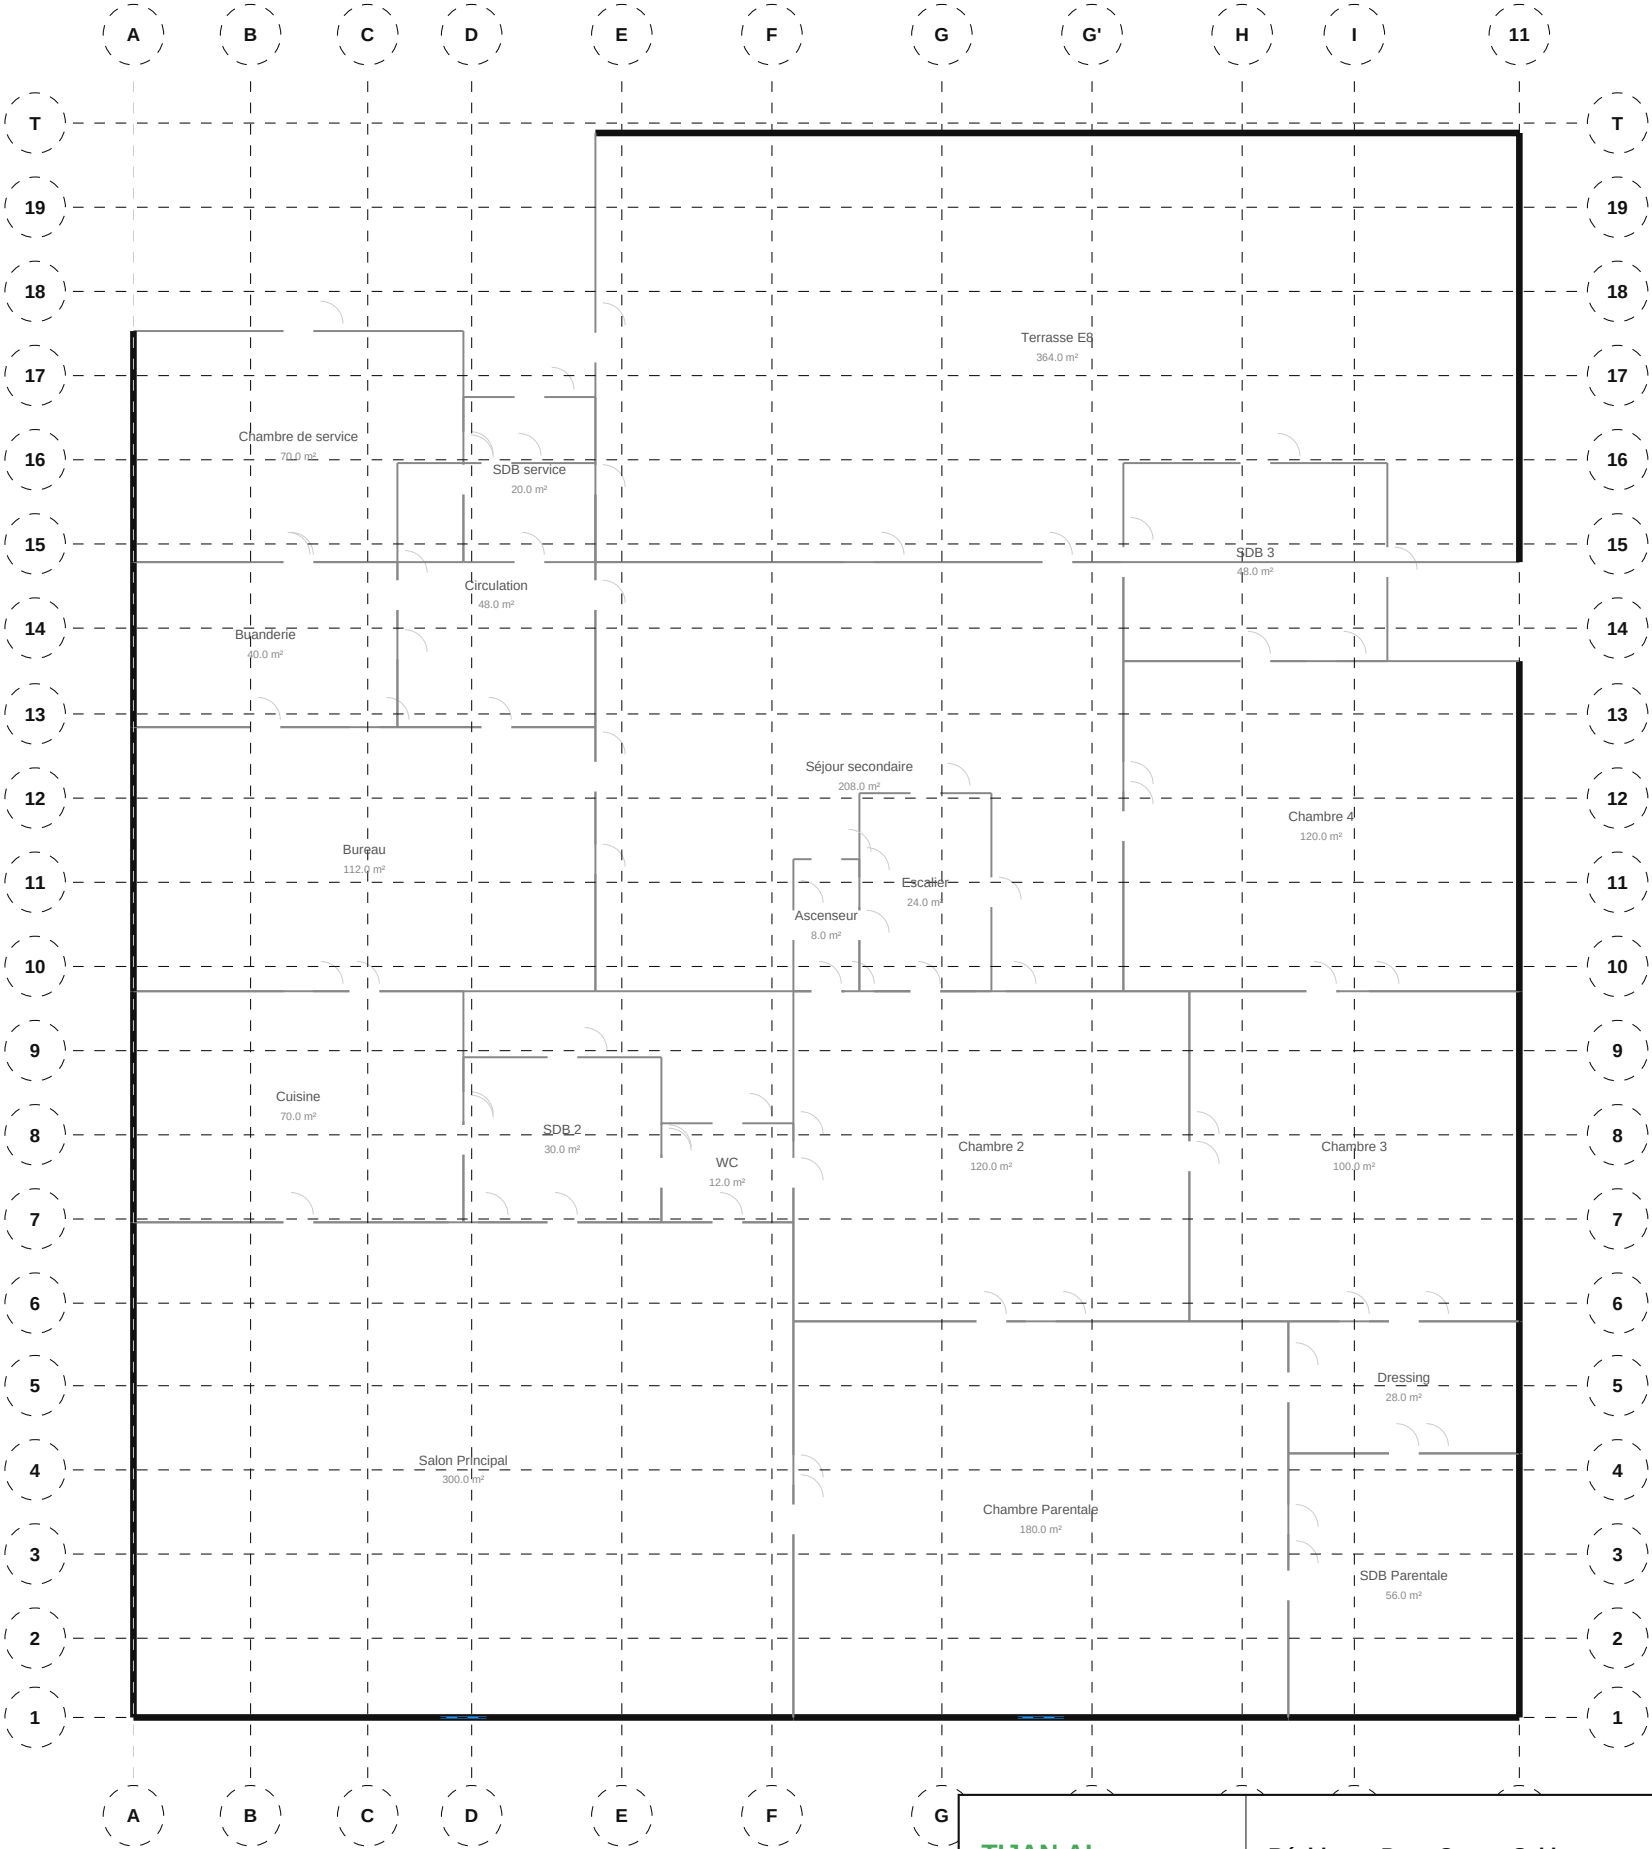

TIJAN AI Bureau d'Études Automatisé	Résidence Papa Oumar Sakho Dakar, Senegal	Éch: 1/100 Pl. 10/88
	Architecture — Étage 8	
Date: 06/05/2026	Réf: 1711	BIM VARC-010 Phase: APD

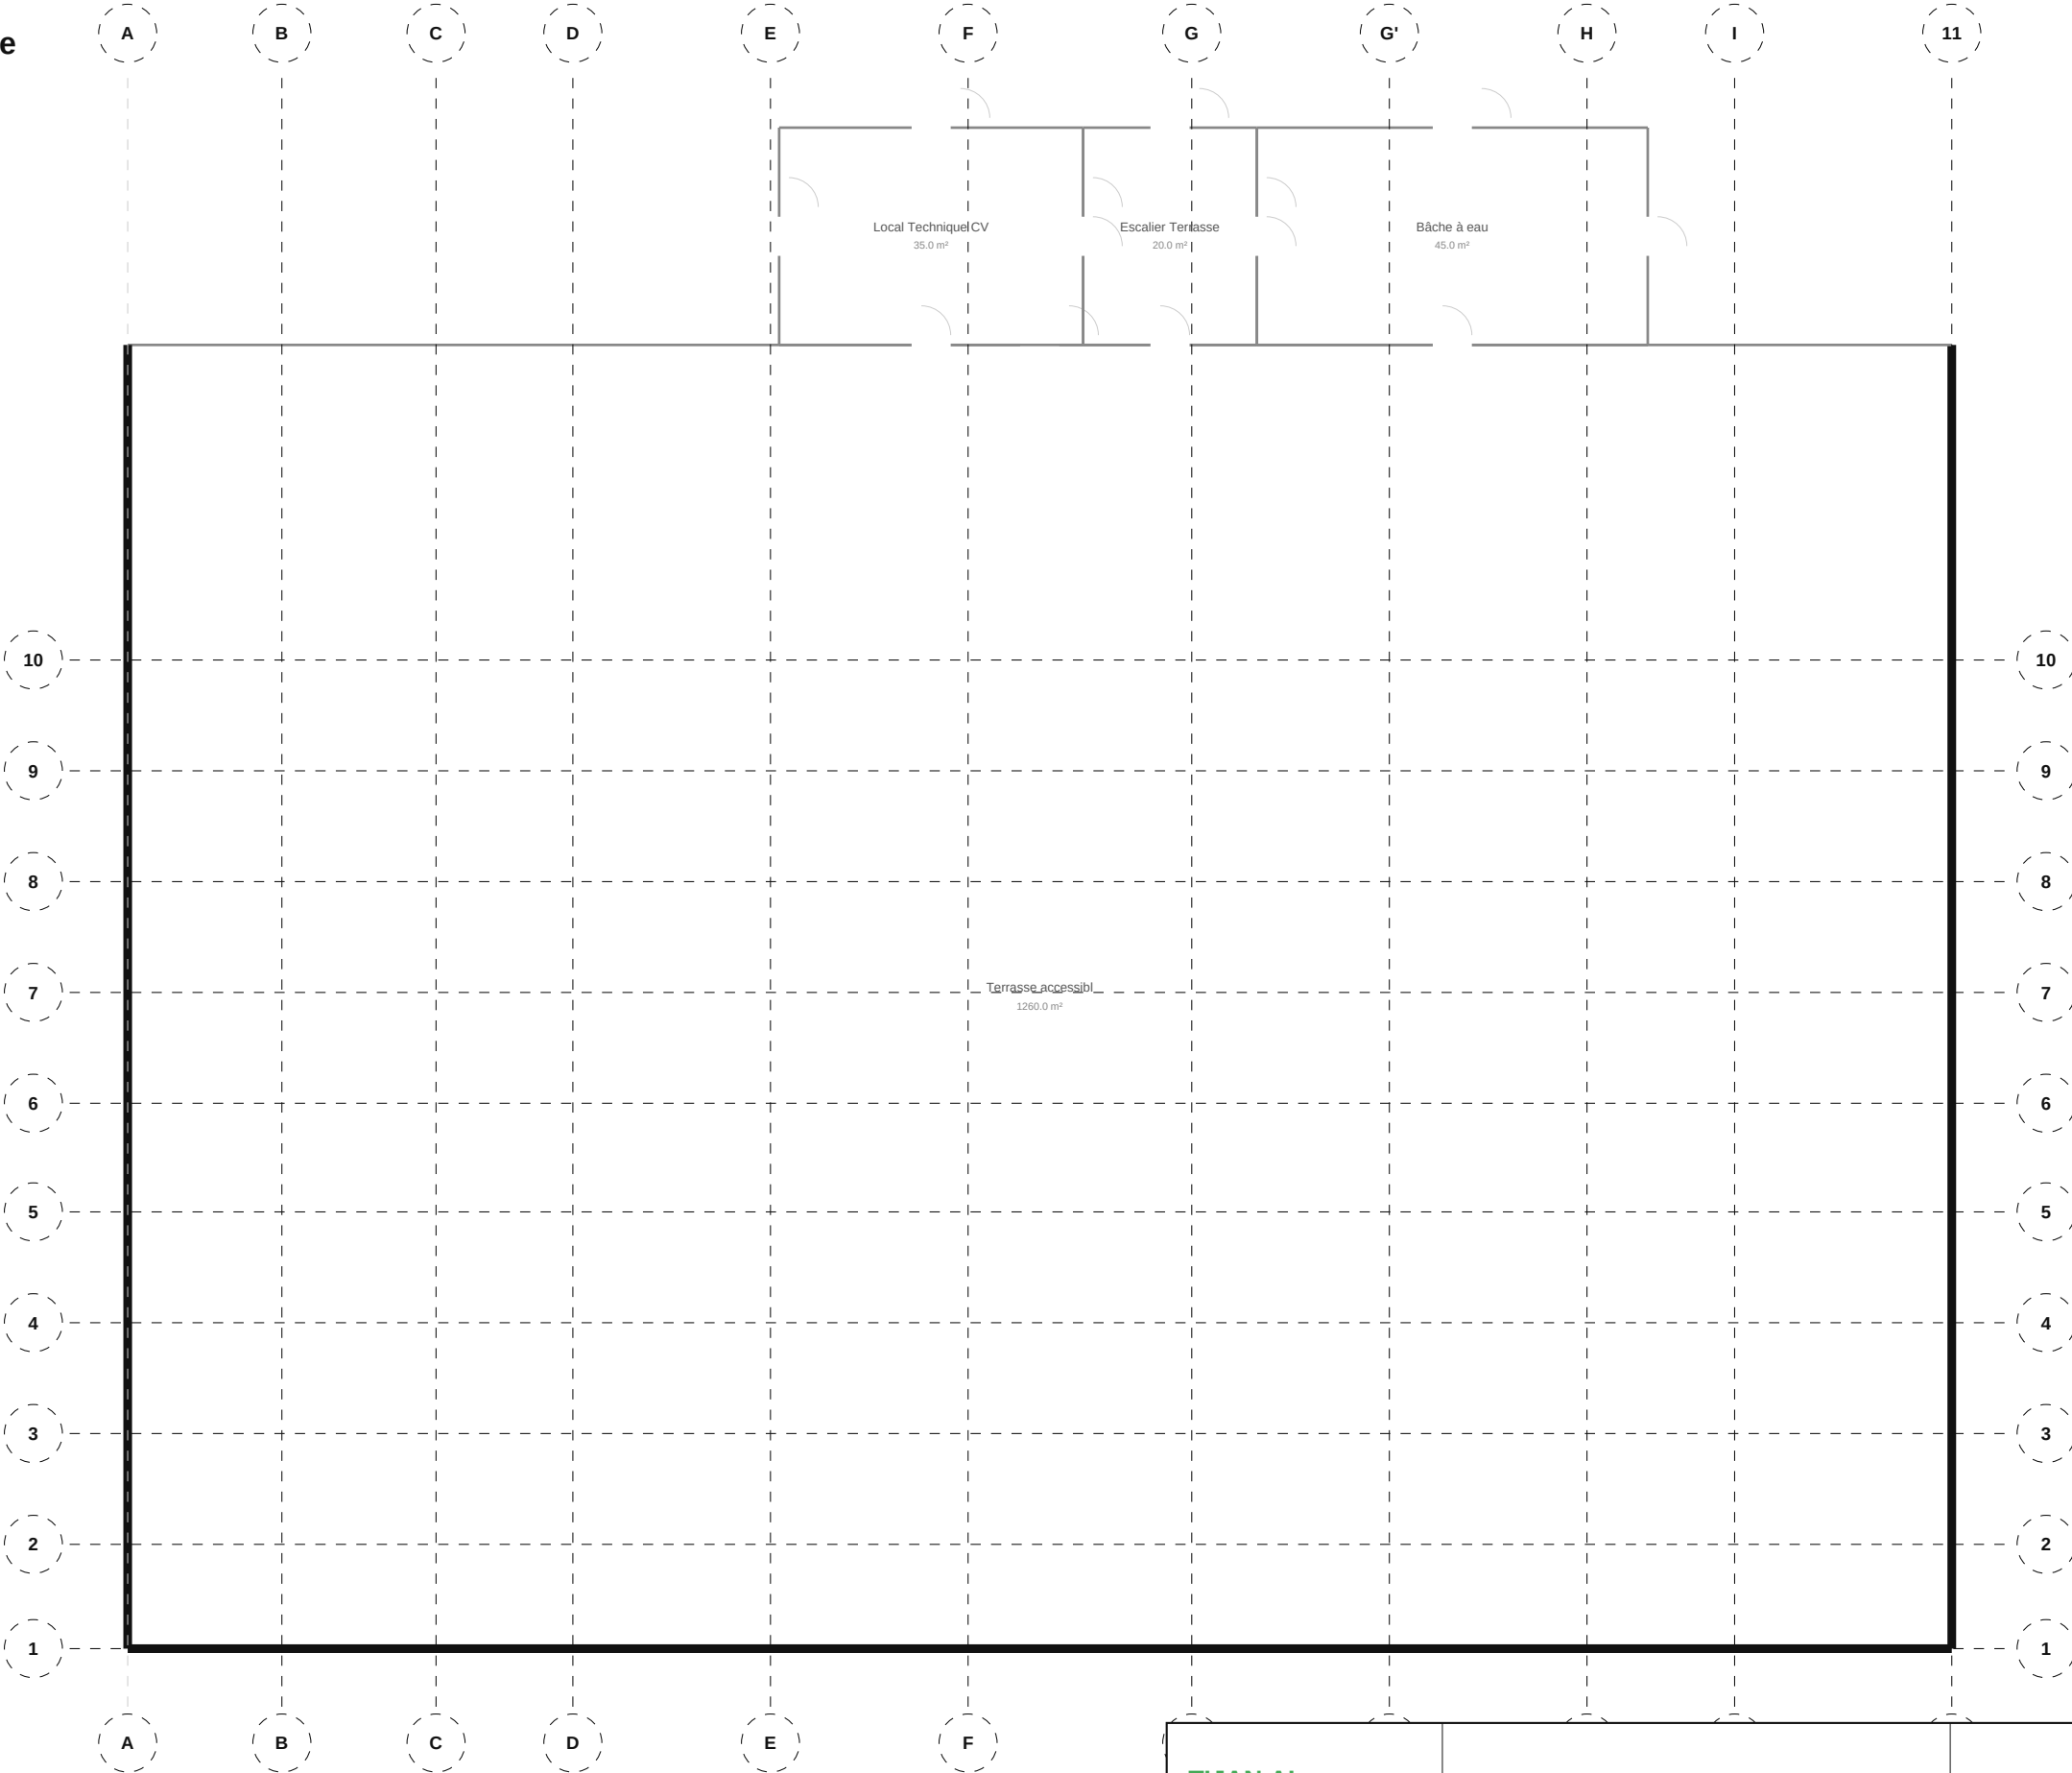


TIJAN AI Bureau d'Études Automatisé	Résidence Papa Oumar Sakho Dakar, Senegal	Éch: 1/100 Pl. 11/88
	Architecture — Terrasse	
Date: 06/05/2026	Réf: 1711	BIM vARC-011 Phase: APD

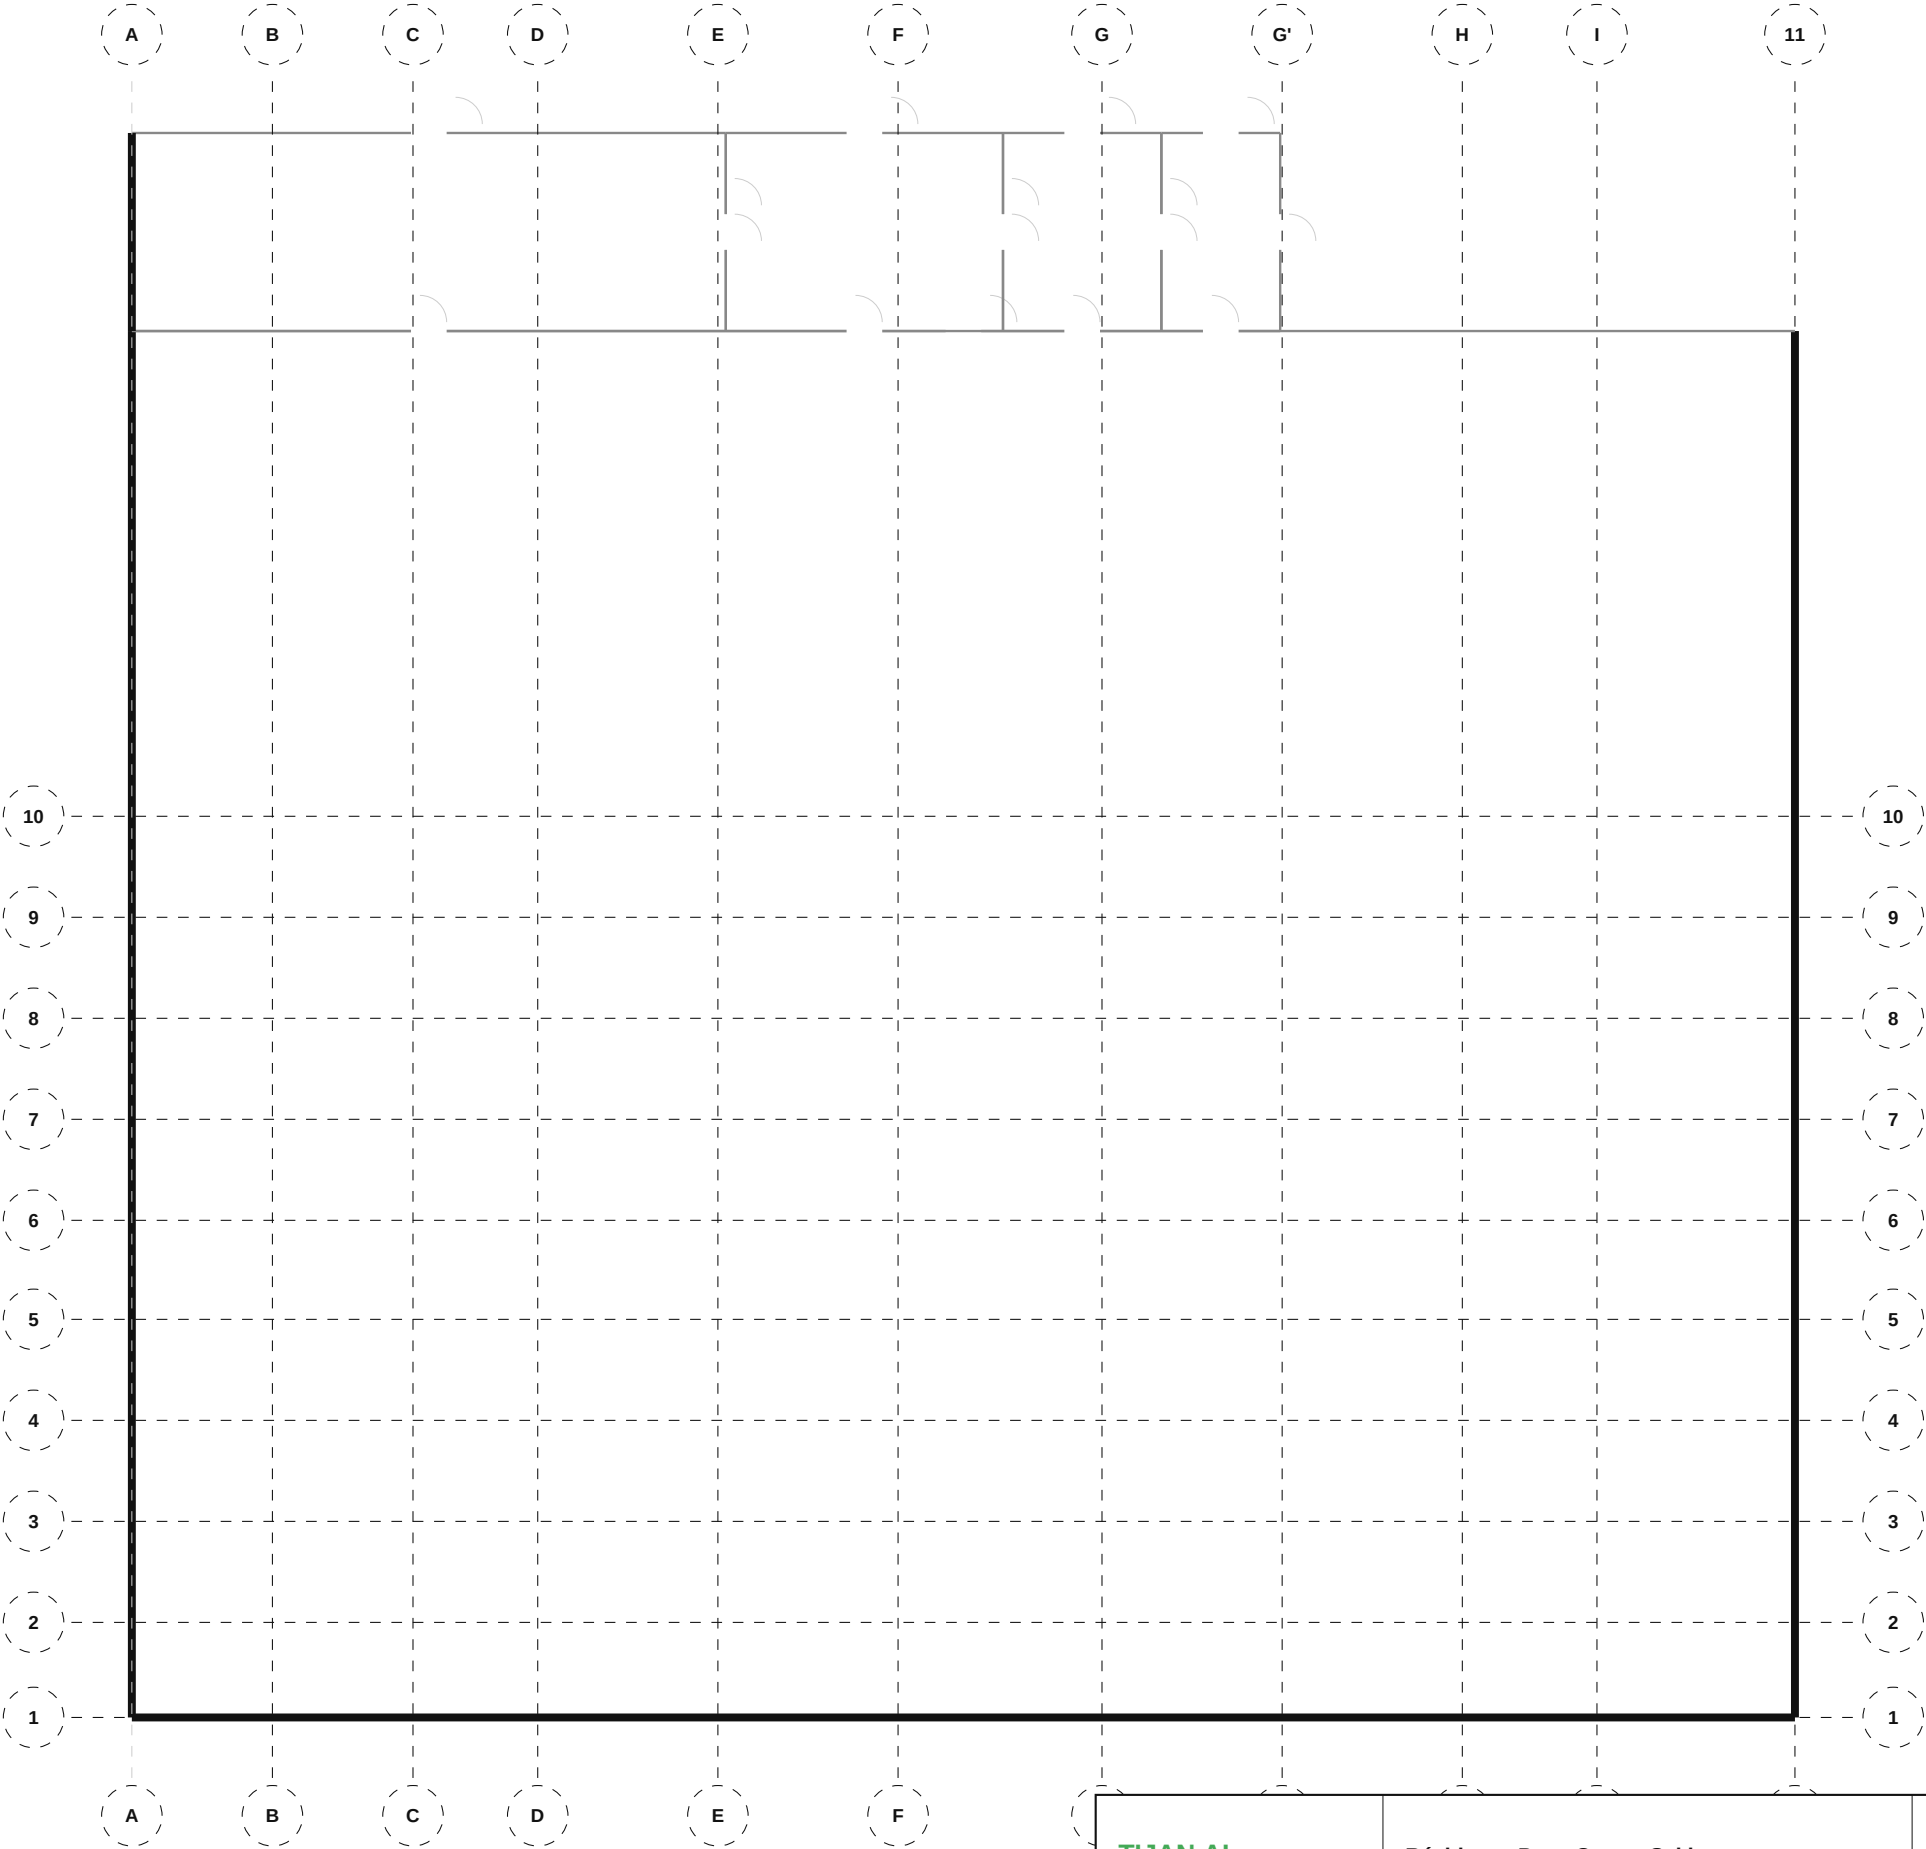


TIJAN AI Bureau d'Études Automatisé	Résidence Papa Oumar Sakho Dakar, Senegal	Éch: 1/100 Pl. 12/88
	Structure — Sous-Sol	
Date: 06/05/2026	Réf: 1711	BIM vSTR-012 Phase: APD


200 Structure — RDC

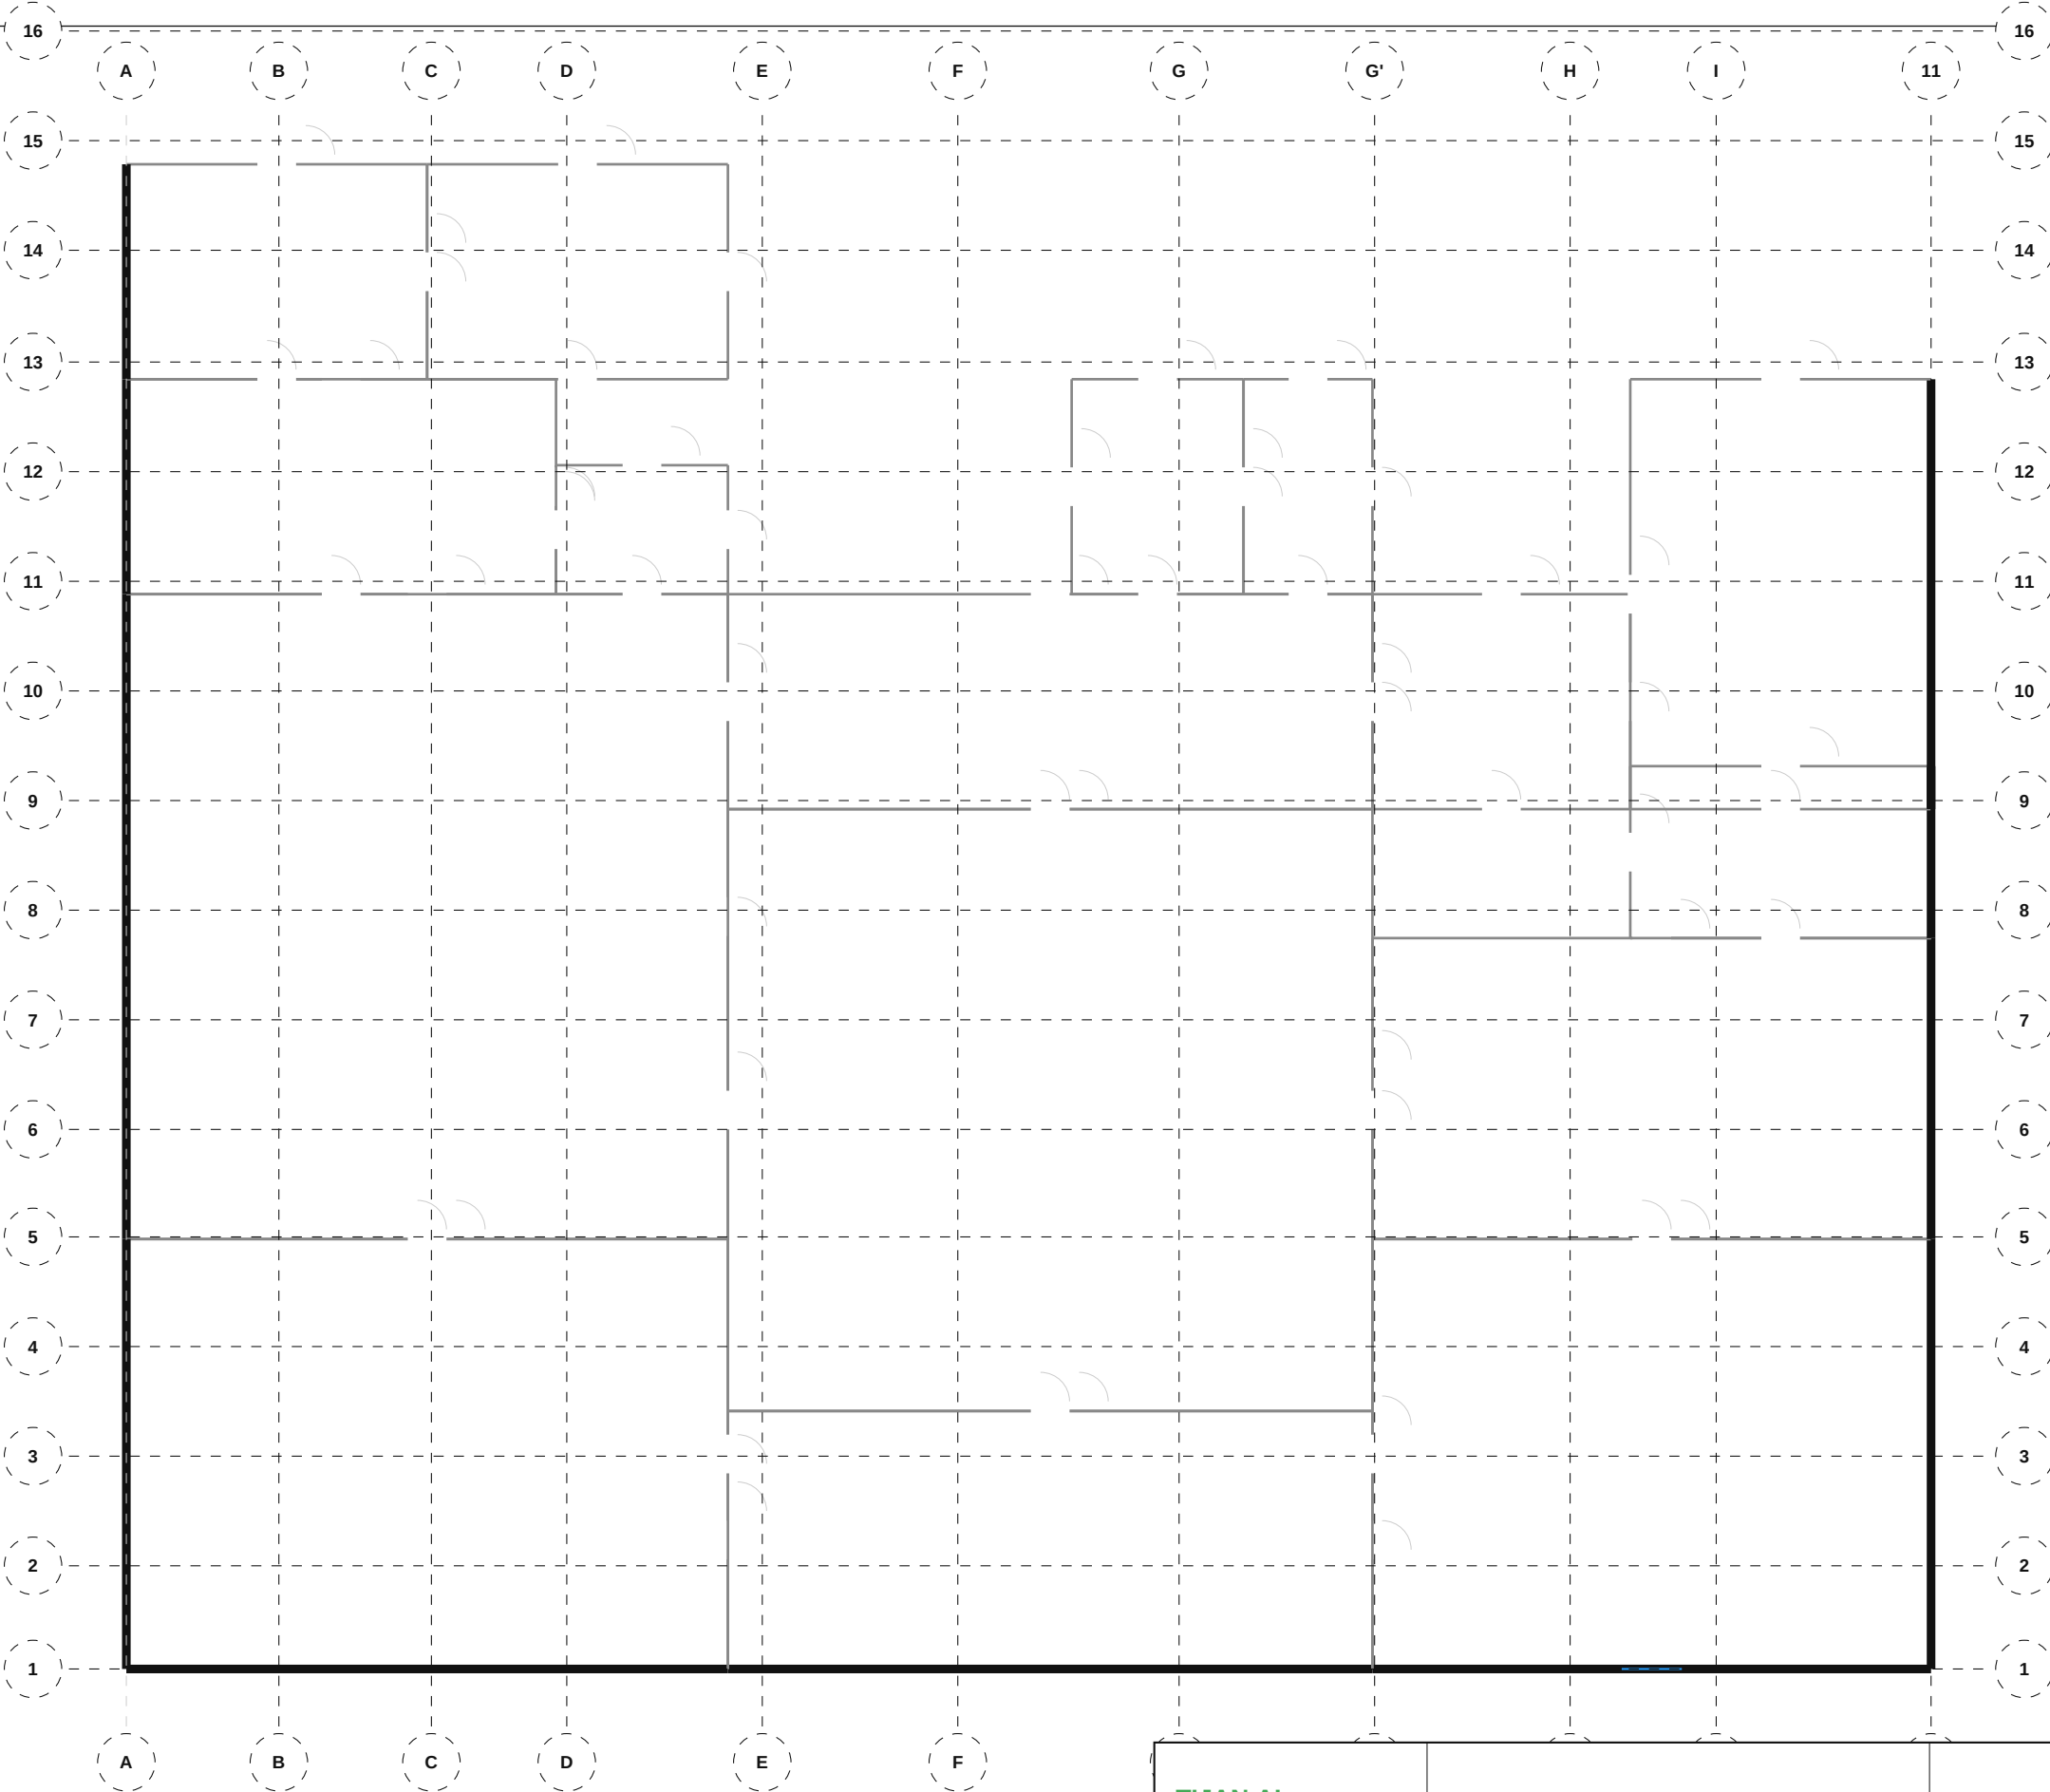


TIJAN AI Bureau d'Études Automatisé	Résidence Papa Oumar Sakho Dakar, Senegal	Éch: 1/100 Pl. 13/88
	Structure — RDC	
Date: 06/05/2026	Réf: 1711	BIM vSTR-013 Phase: APD

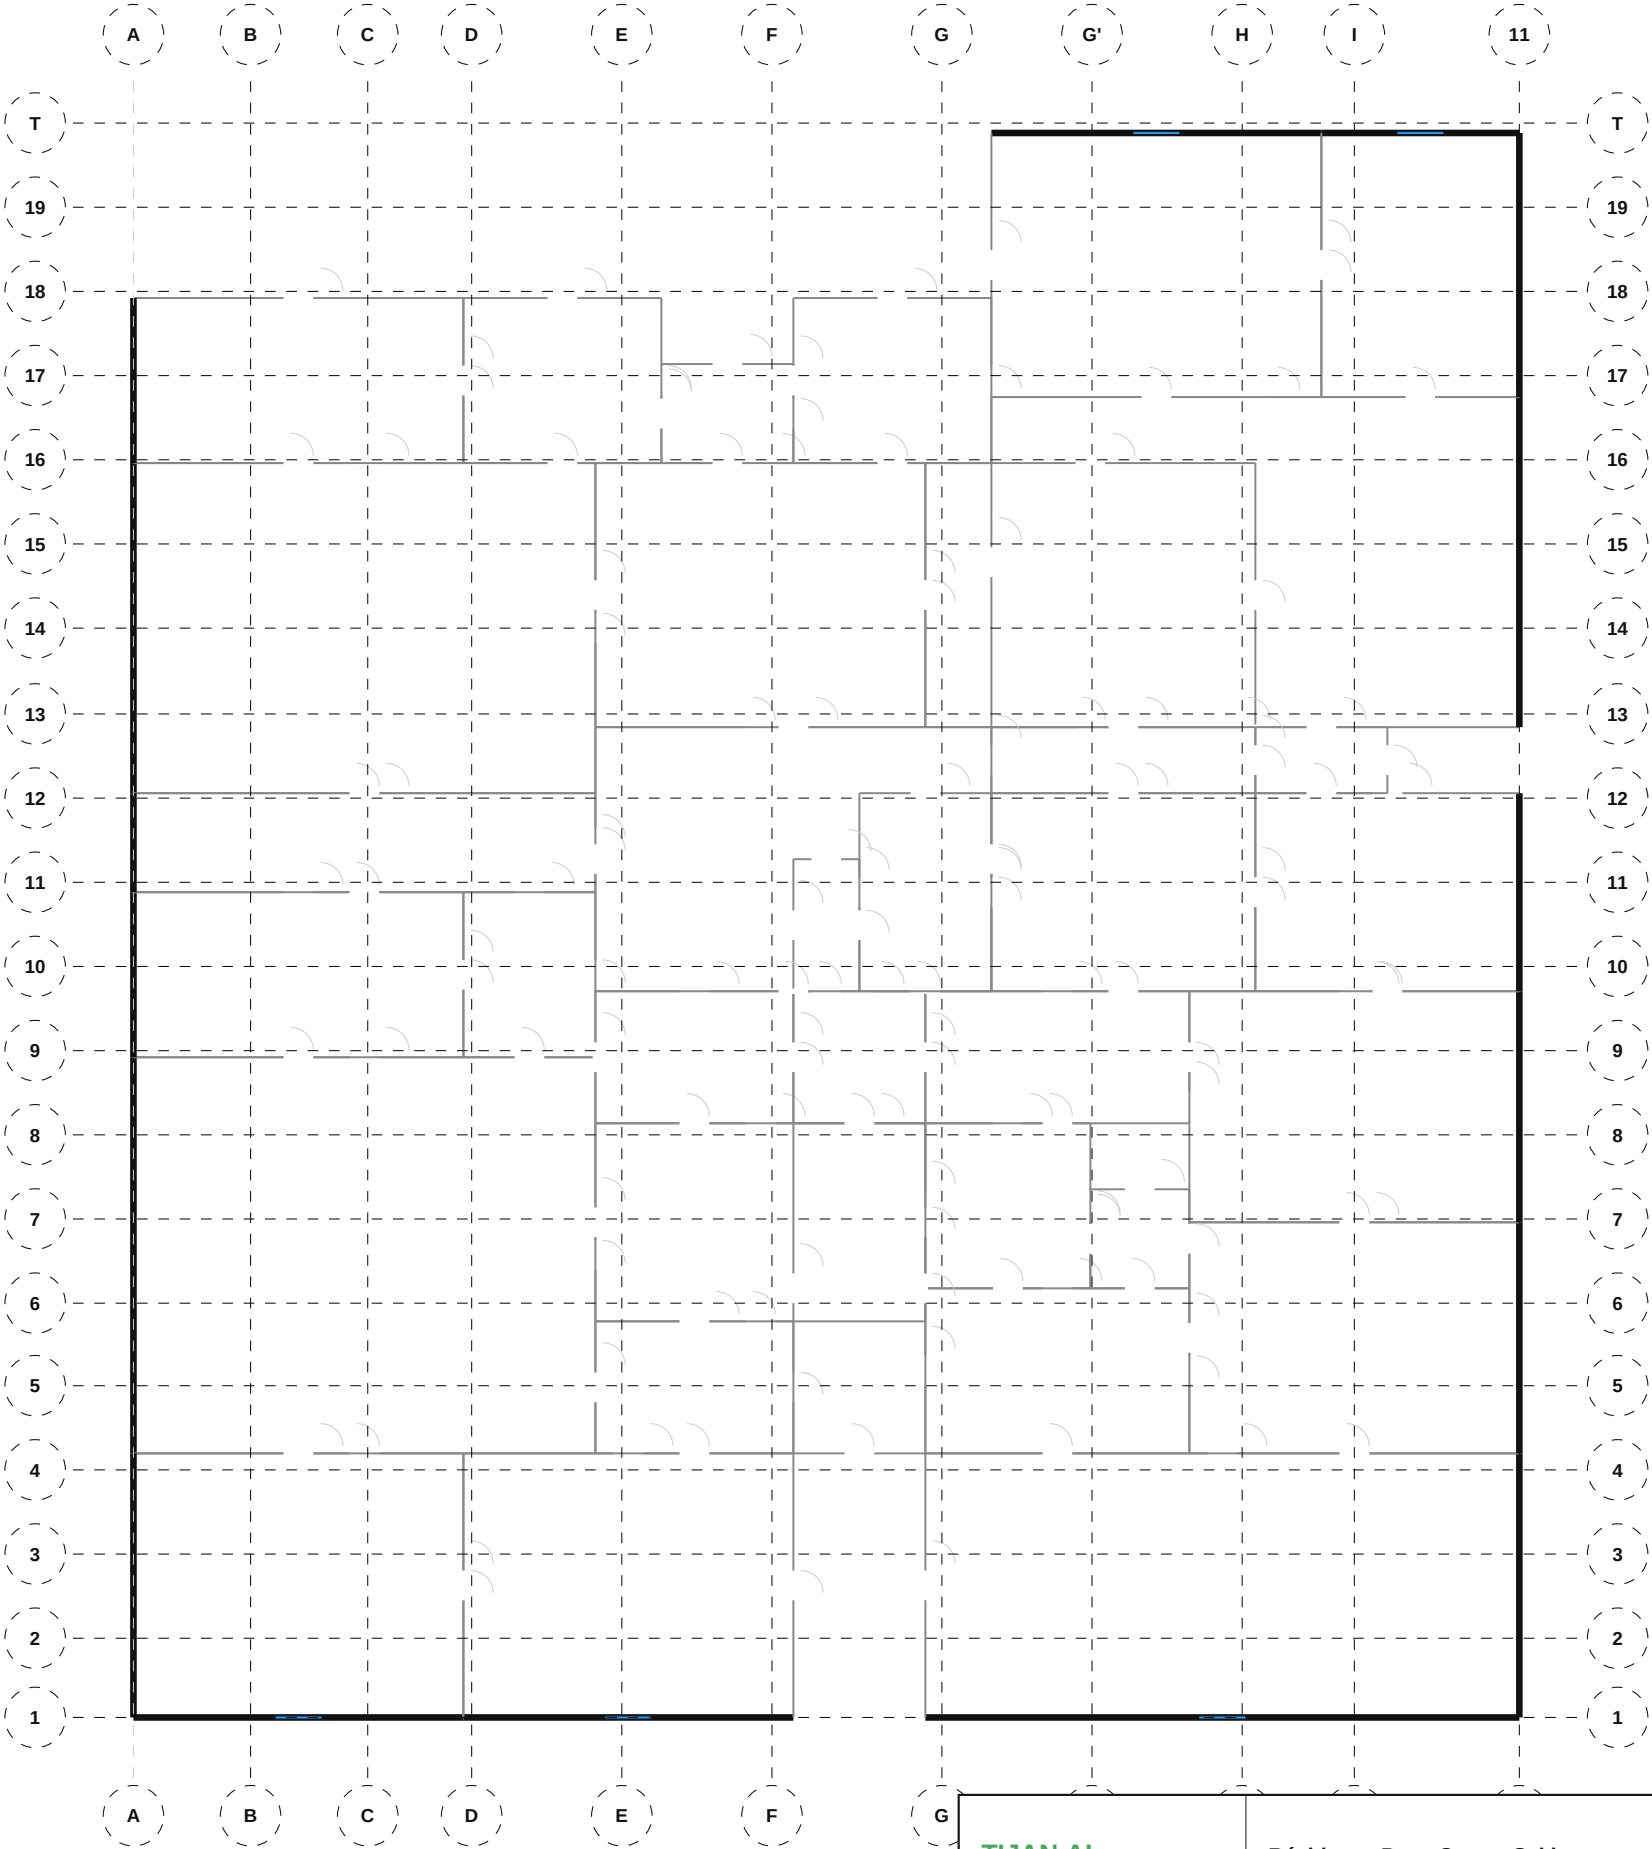


TIJAN AI Bureau d'Études Automatisé	Résidence Papa Oumar Sakho		Éch: 1/100
	Dakar, Senegal		Pl. 14/88
	Structure — Étage 1		
Date: 06/05/2026	Réf: 1711		BIM vSTR-014
			Phase: APD

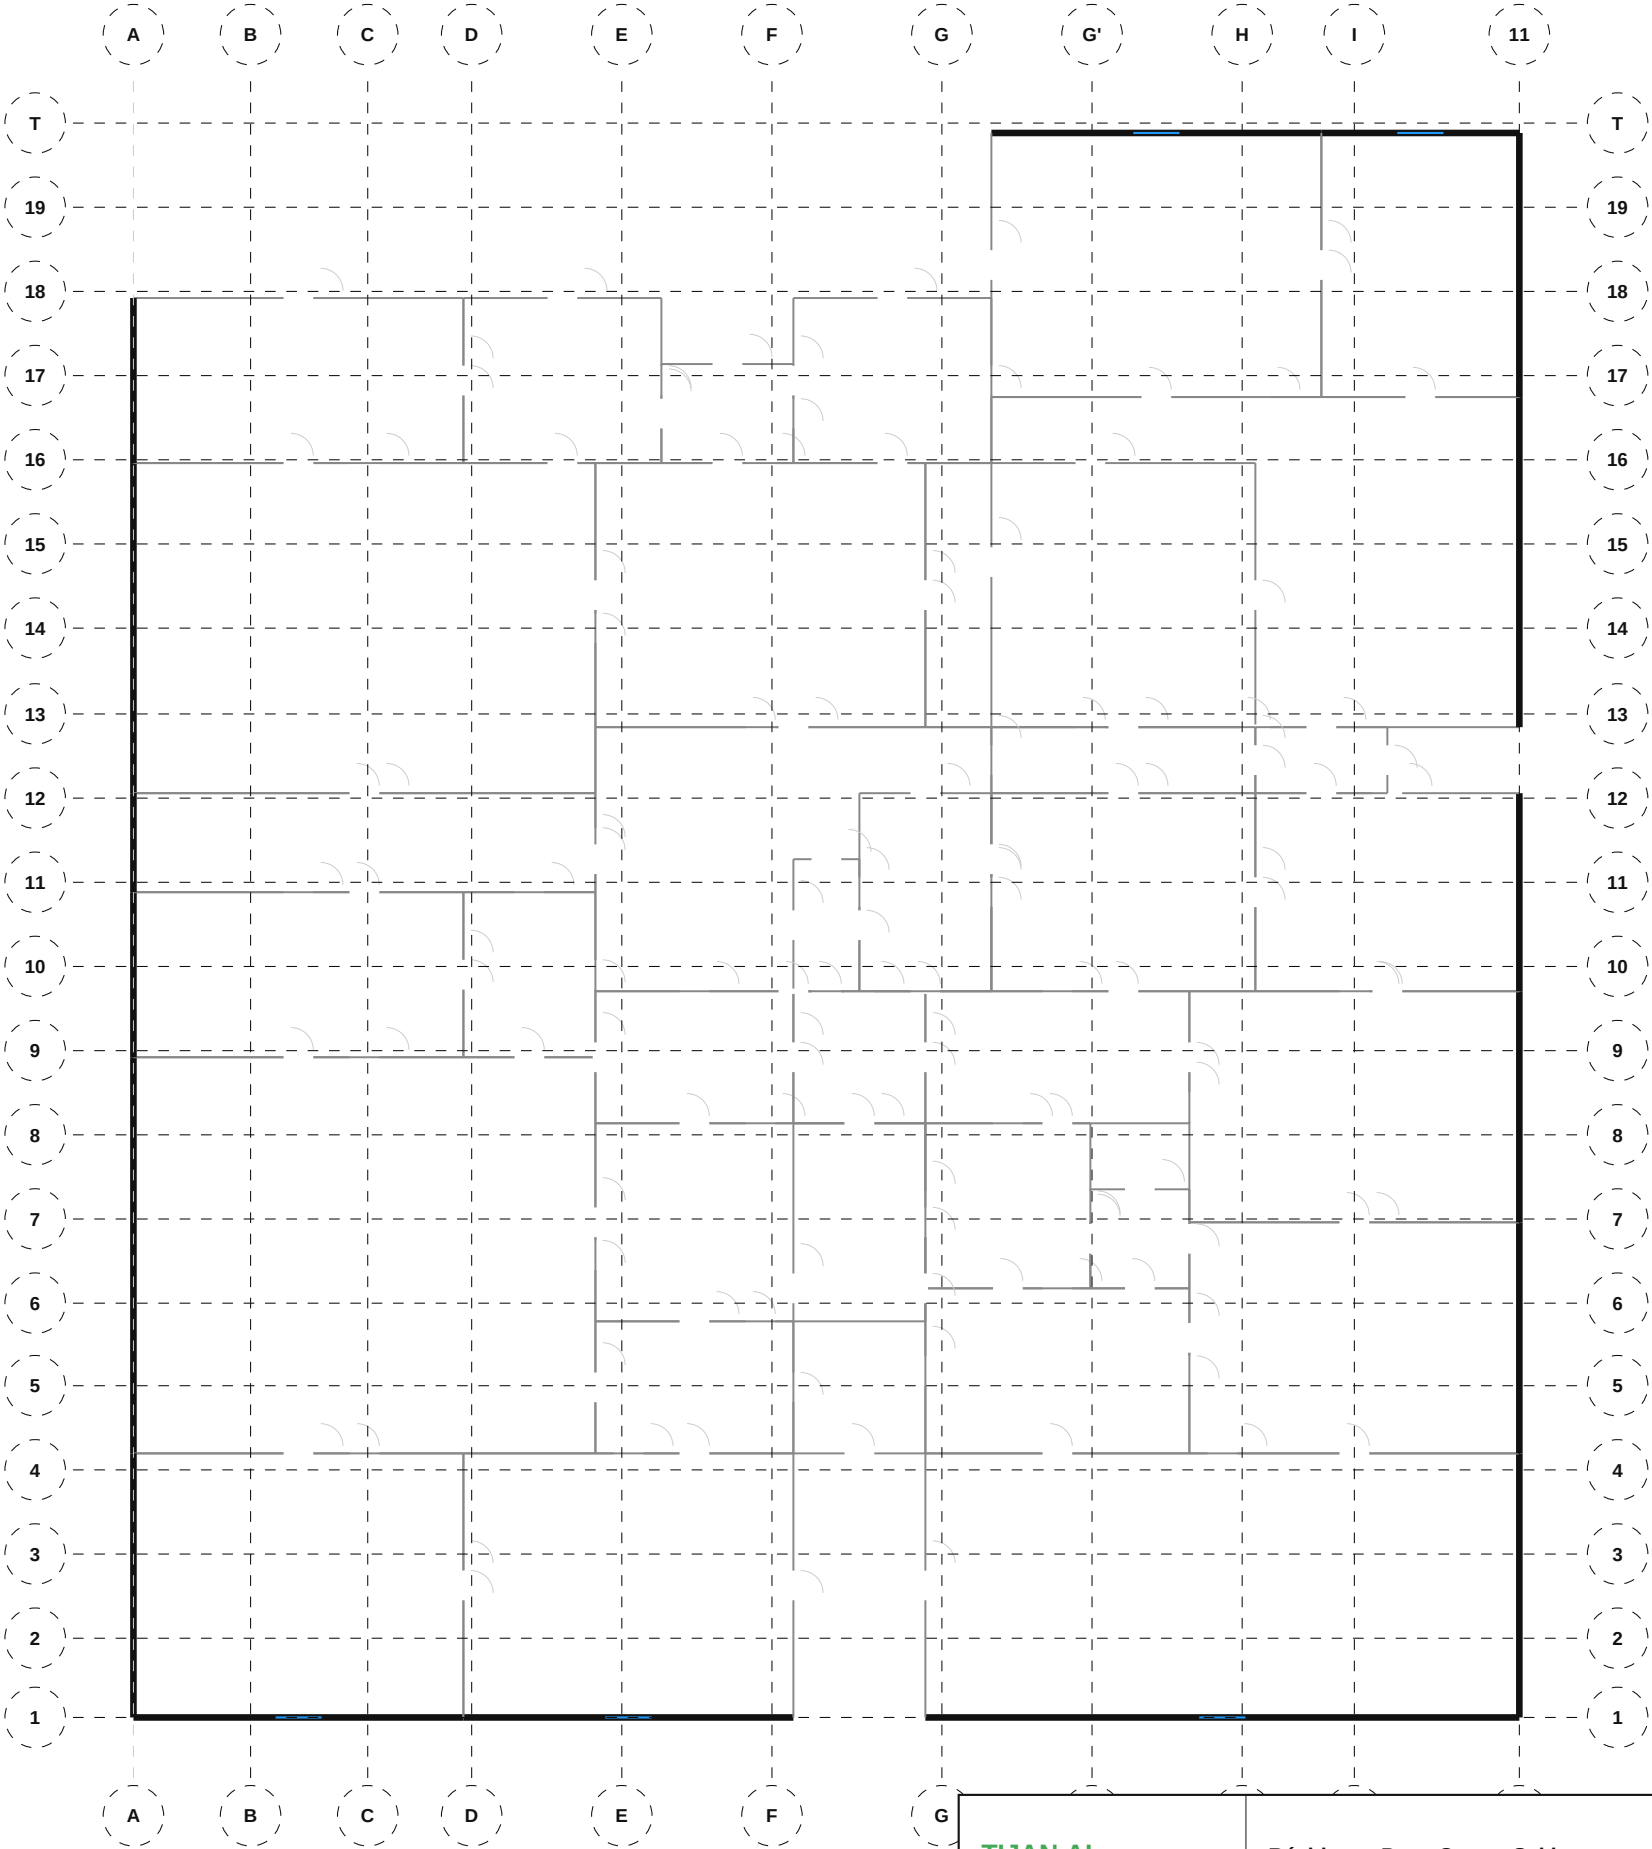


TIJAN AI Bureau d'Études Automatisé	Résidence Papa Oumar Sakho		Éch: 1/100
	Dakar, Senegal		Pl. 15/88
	Structure — Étage 2		
Date: 06/05/2026	Réf: 1711		BIM vSTR-015
			Phase: APD

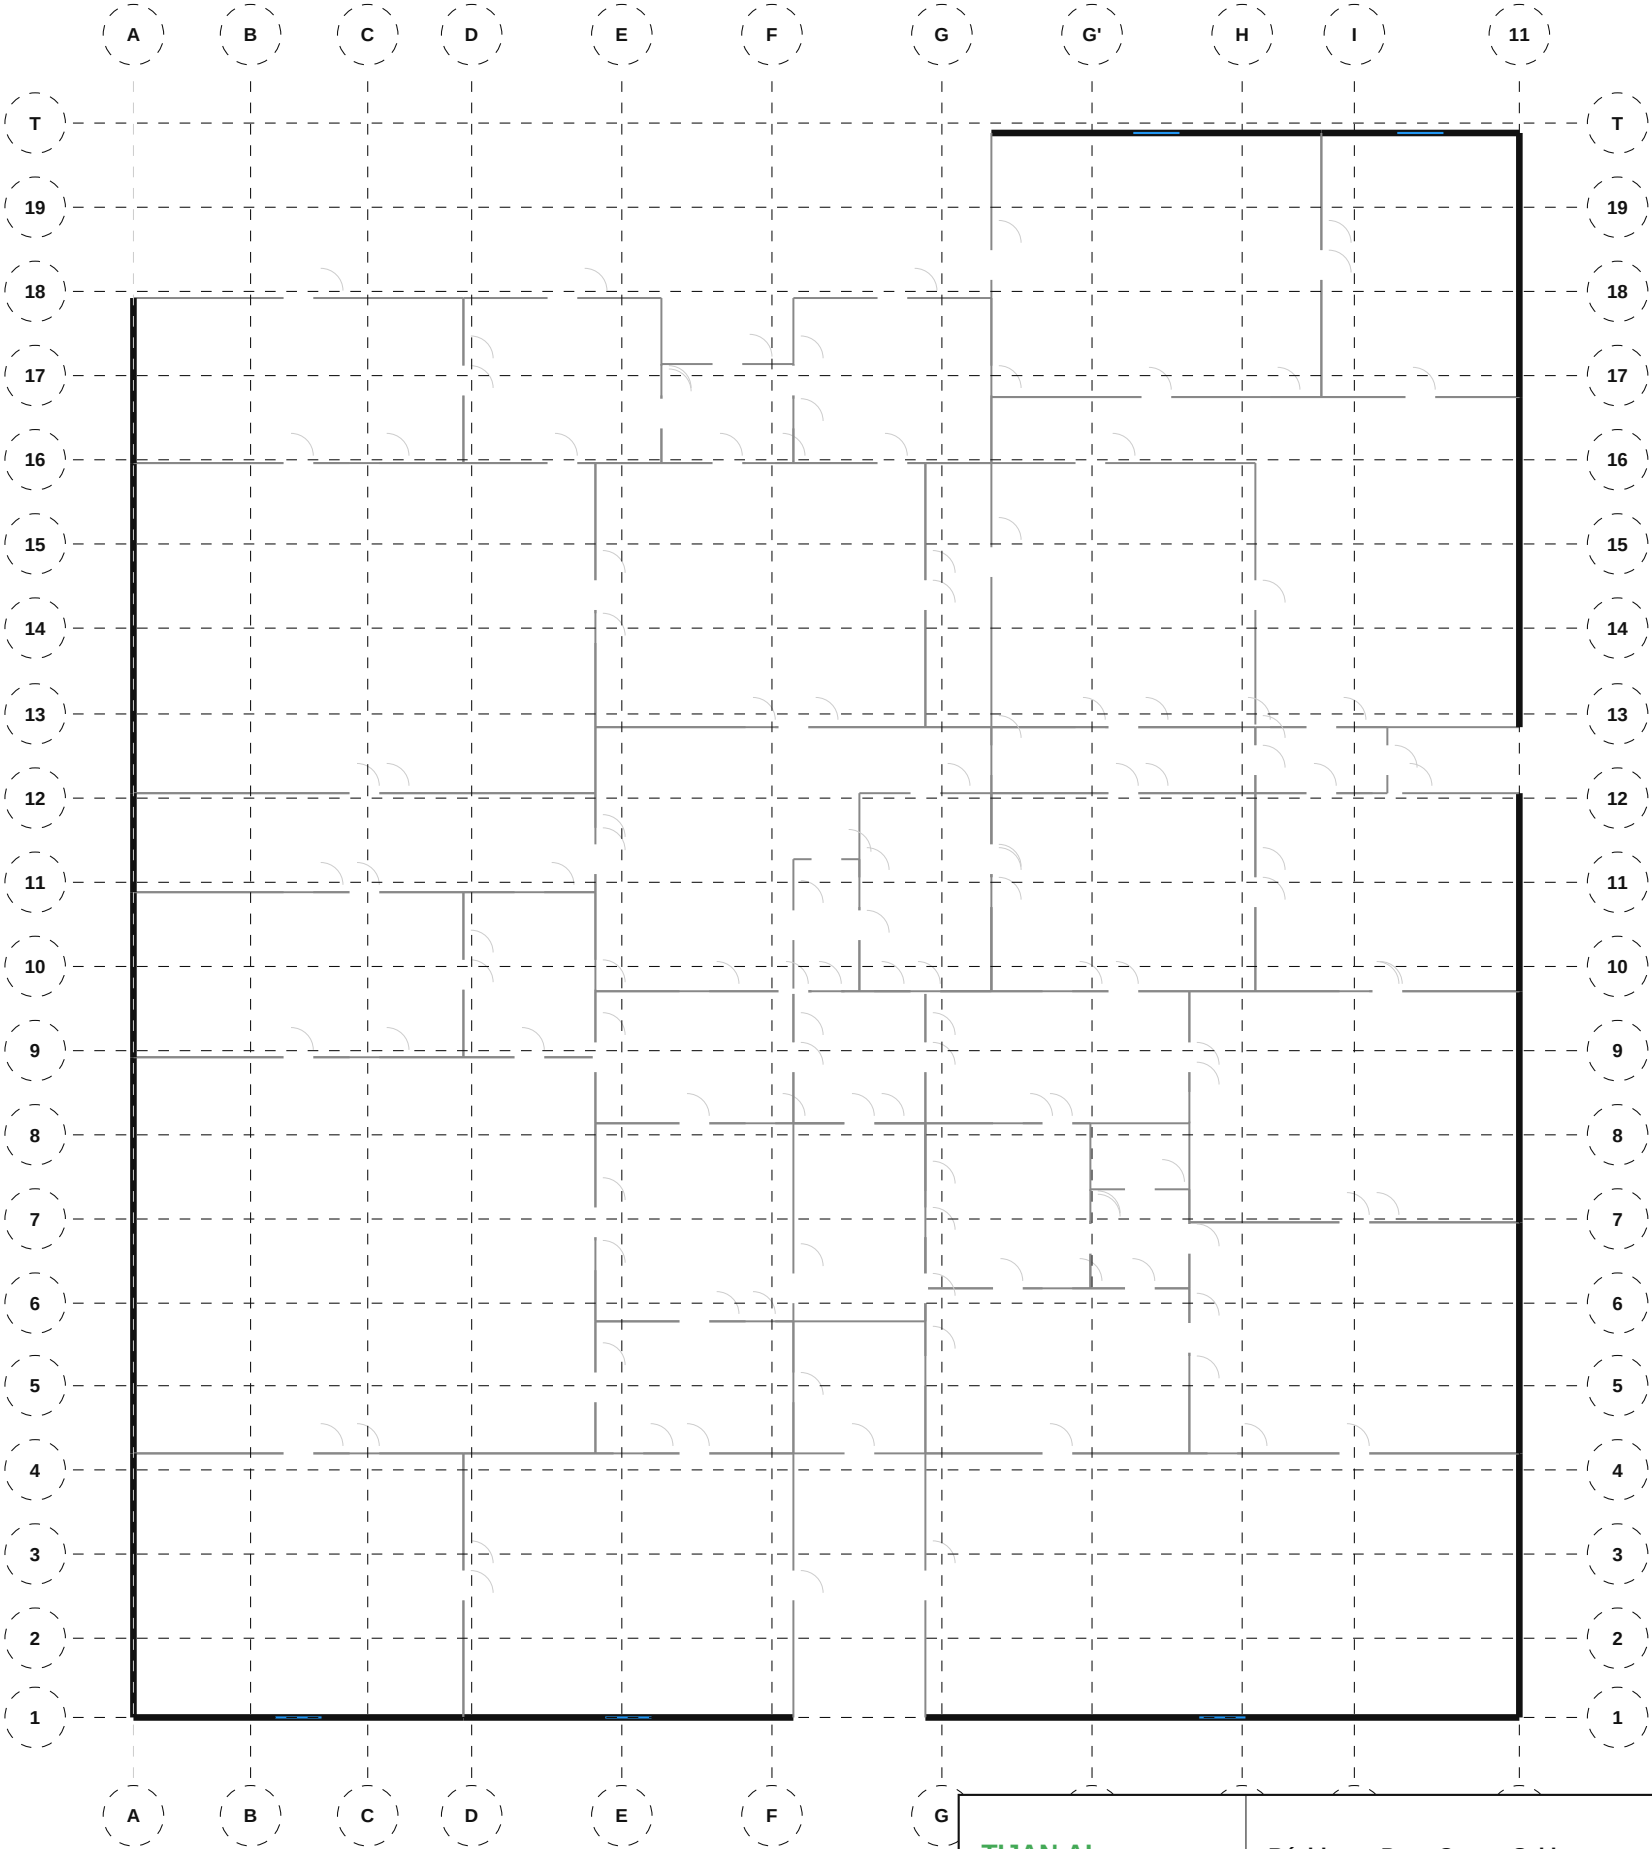


TIJAN AI Bureau d'Études Automatisé	Résidence Papa Oumar Sakho		Éch: 1/100
	Dakar, Senegal		Pl. 16/88
	Structure — Étage 3		
Date: 06/05/2026	Réf: 1711		BIM vSTR-016
			Phase: APD

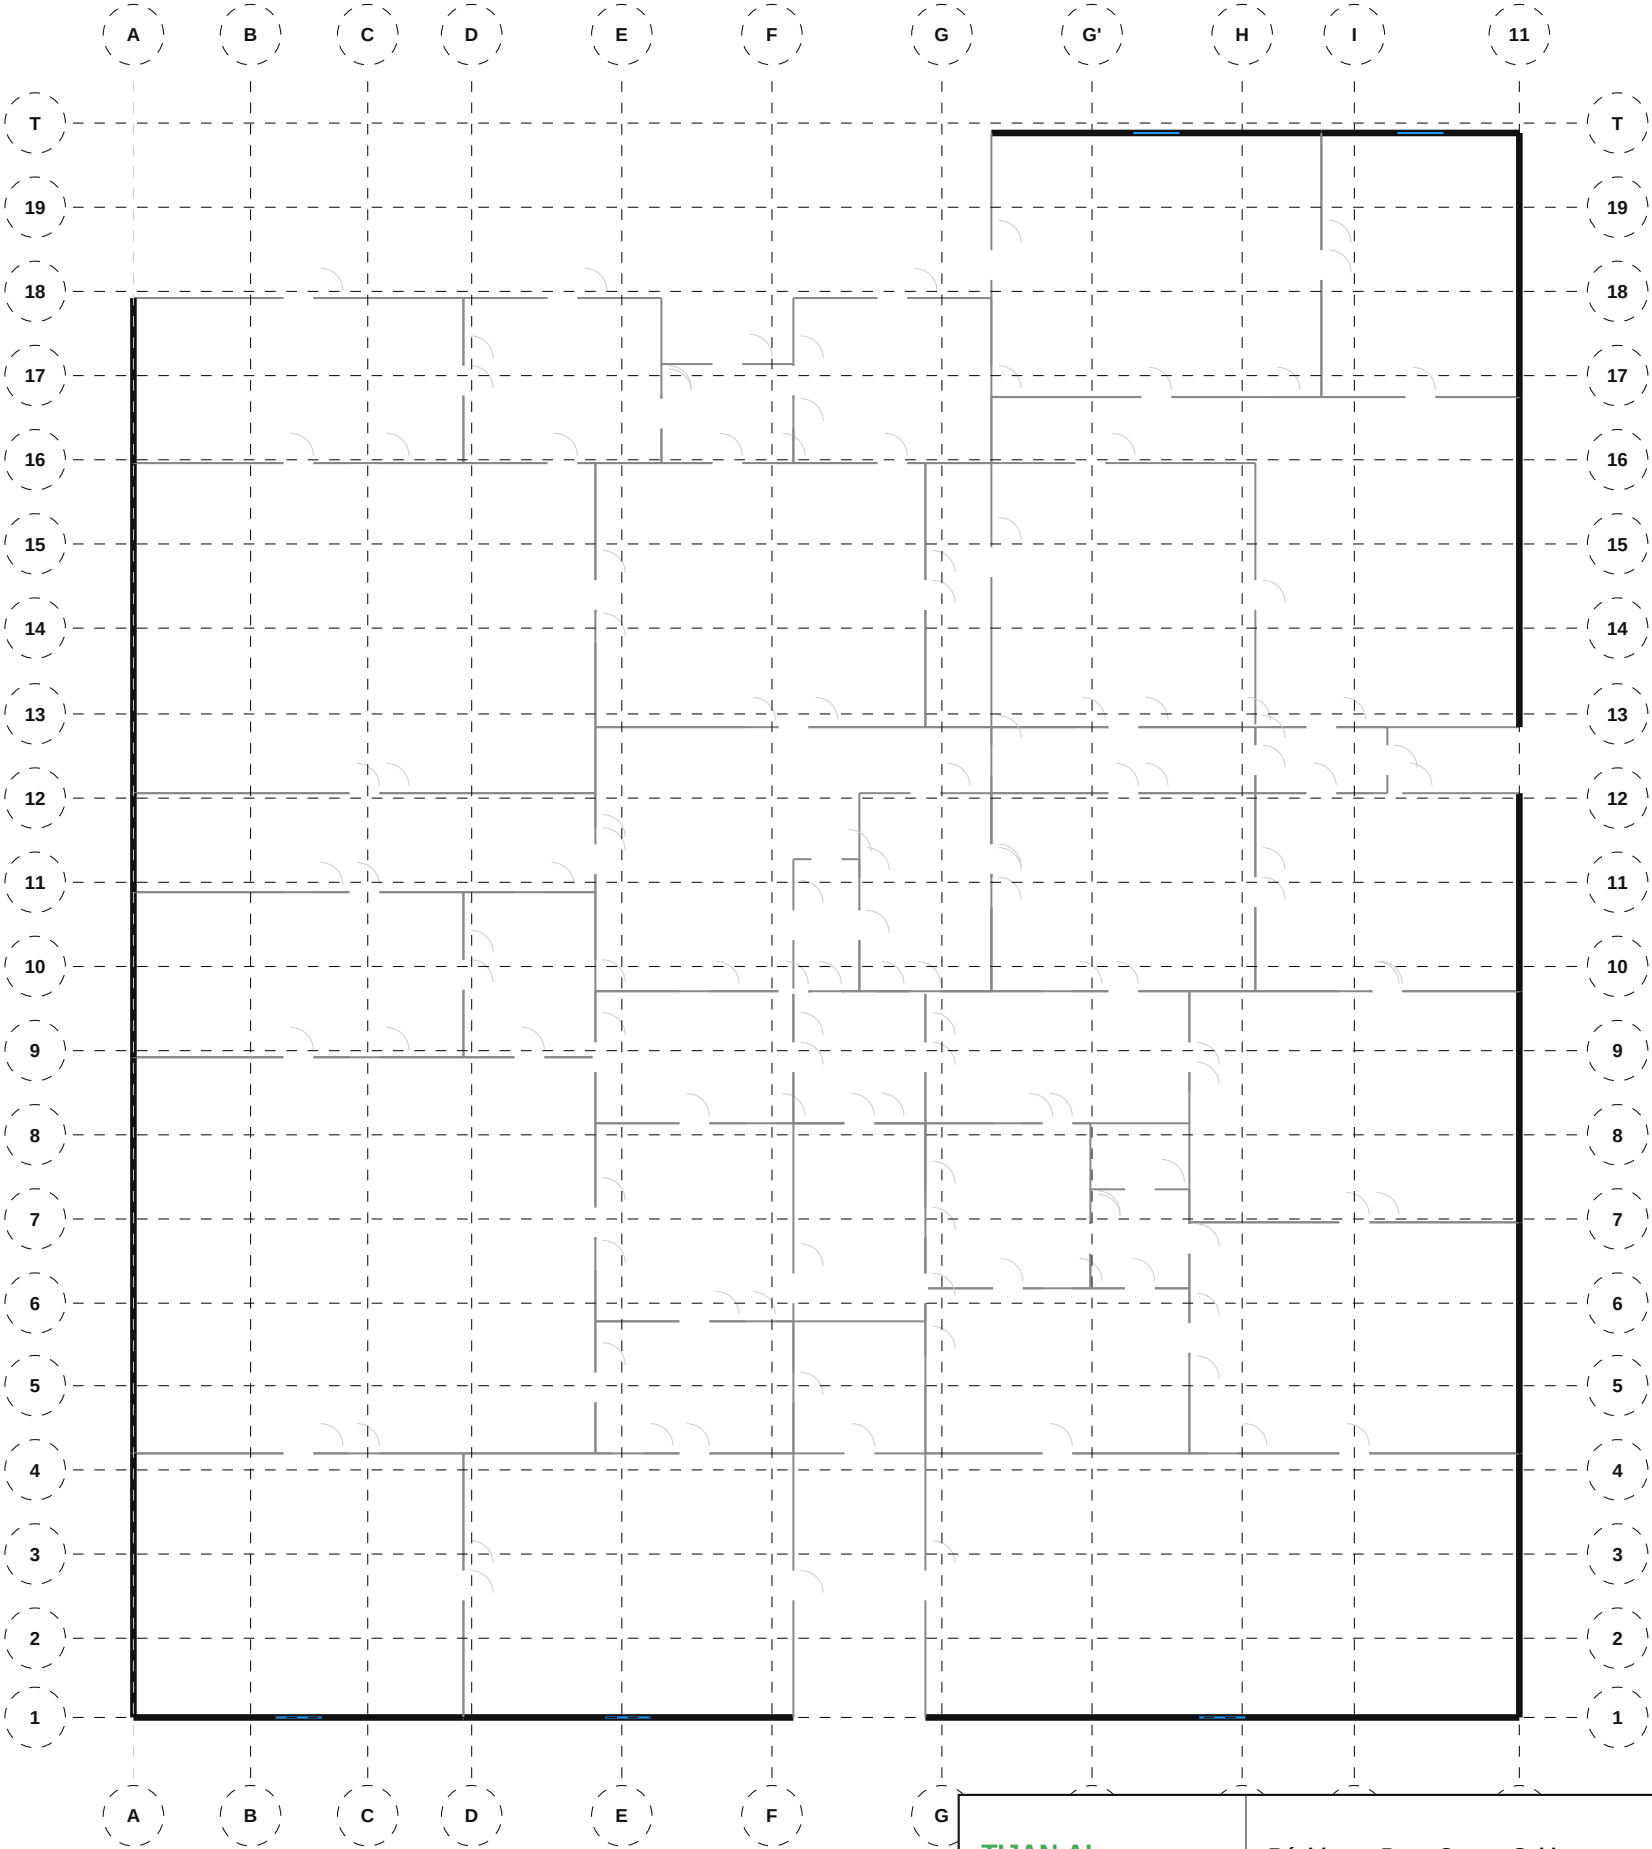


TIJAN AI Bureau d'Études Automatisé	Résidence Papa Oumar Sakho Dakar, Senegal		Éch: 1/100 Pl. 17/88
	Structure — Étage 4		
	Date: 06/05/2026	Réf: 1711	BIM vSTR-017 Phase: APD

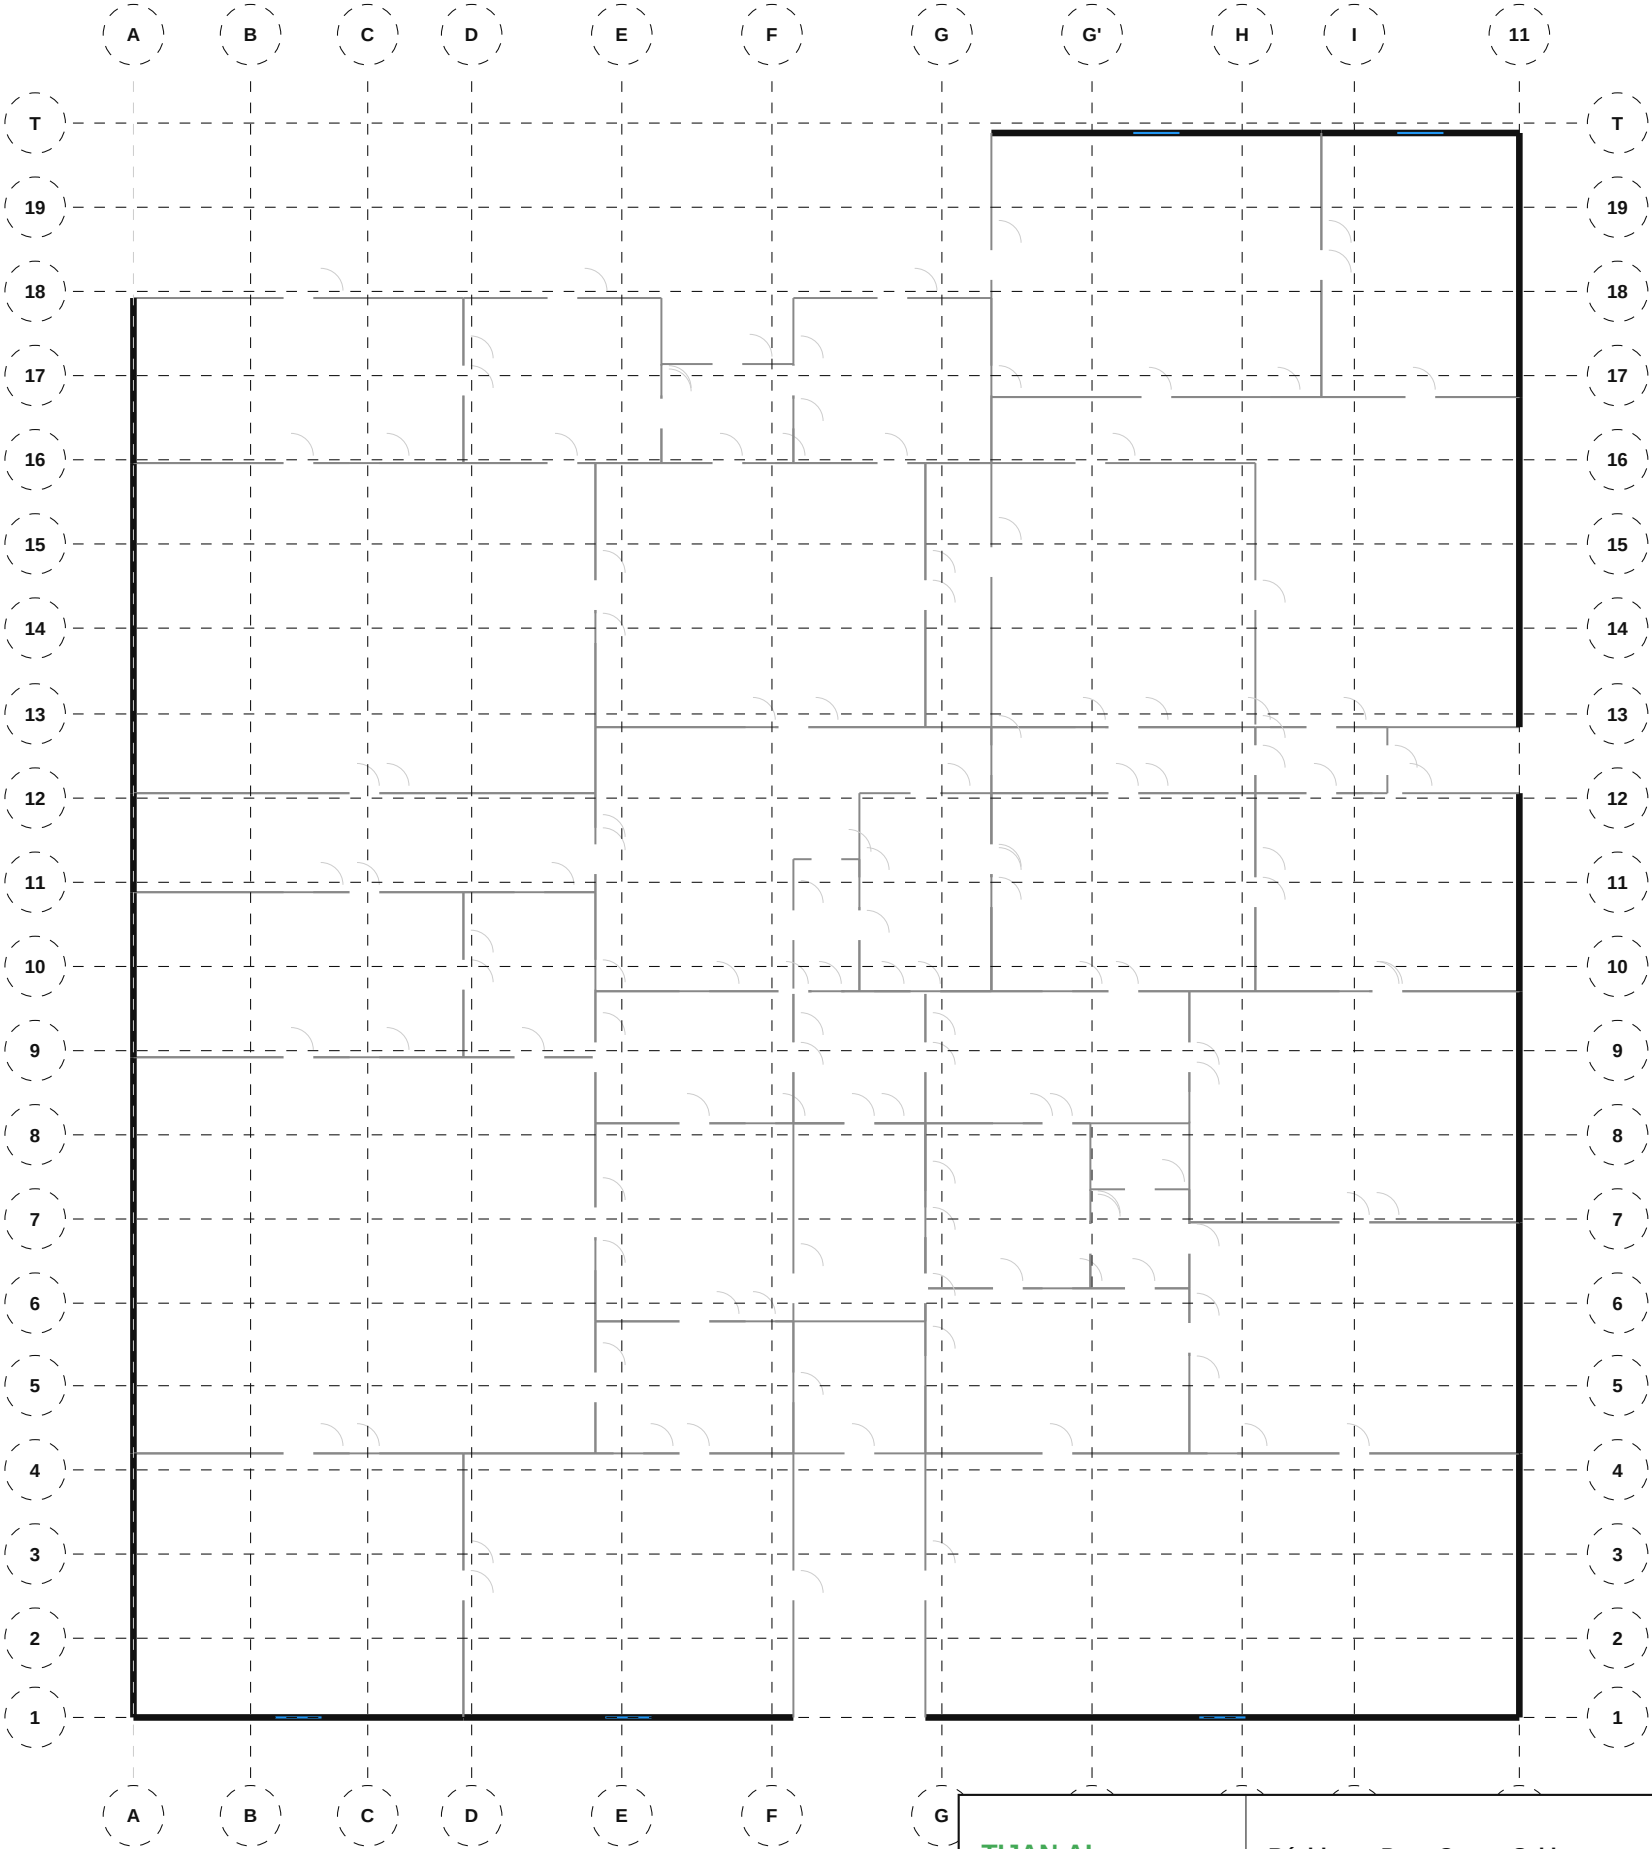


TIJAN AI Bureau d'Études Automatisé	Résidence Papa Oumar Sakho		Éch: 1/100
	Dakar, Senegal		Pl. 18/88
	Structure — Étage 5		
Date: 06/05/2026	Réf: 1711		BIM vSTR-018
			Phase: APD

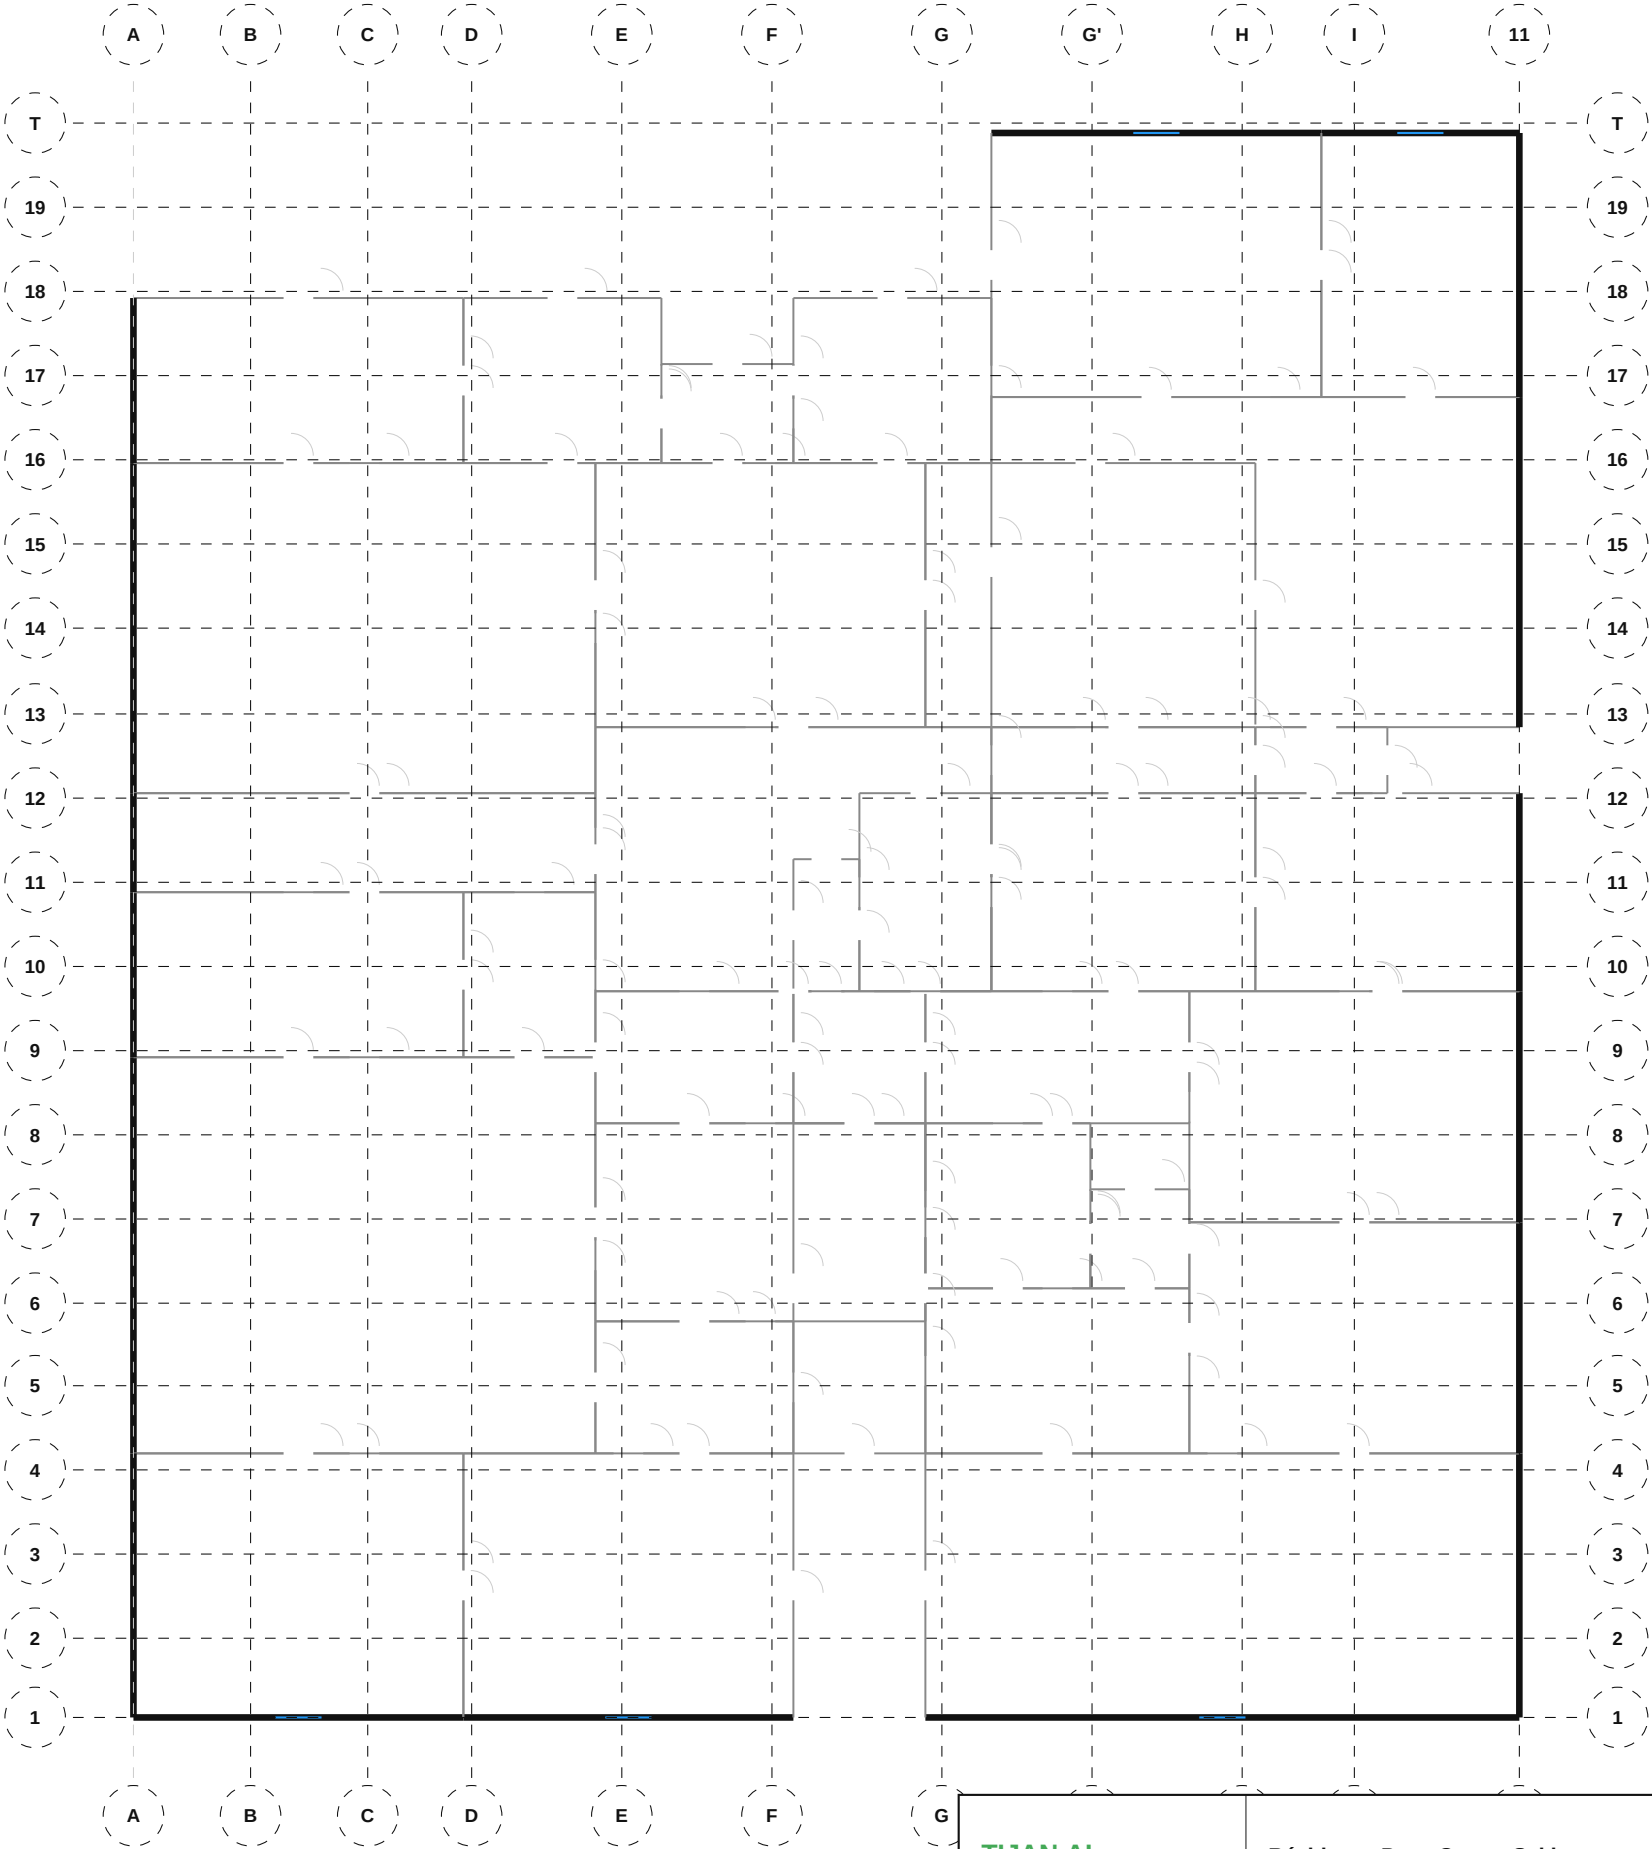


TIJAN AI Bureau d'Études Automatisé	Résidence Papa Oumar Sakho		Éch: 1/100
	Dakar, Senegal		Pl. 19/88
	Structure — Étage 6		
Date: 06/05/2026	Réf: 1711		BIM vSTR-019
		Phase: APD	

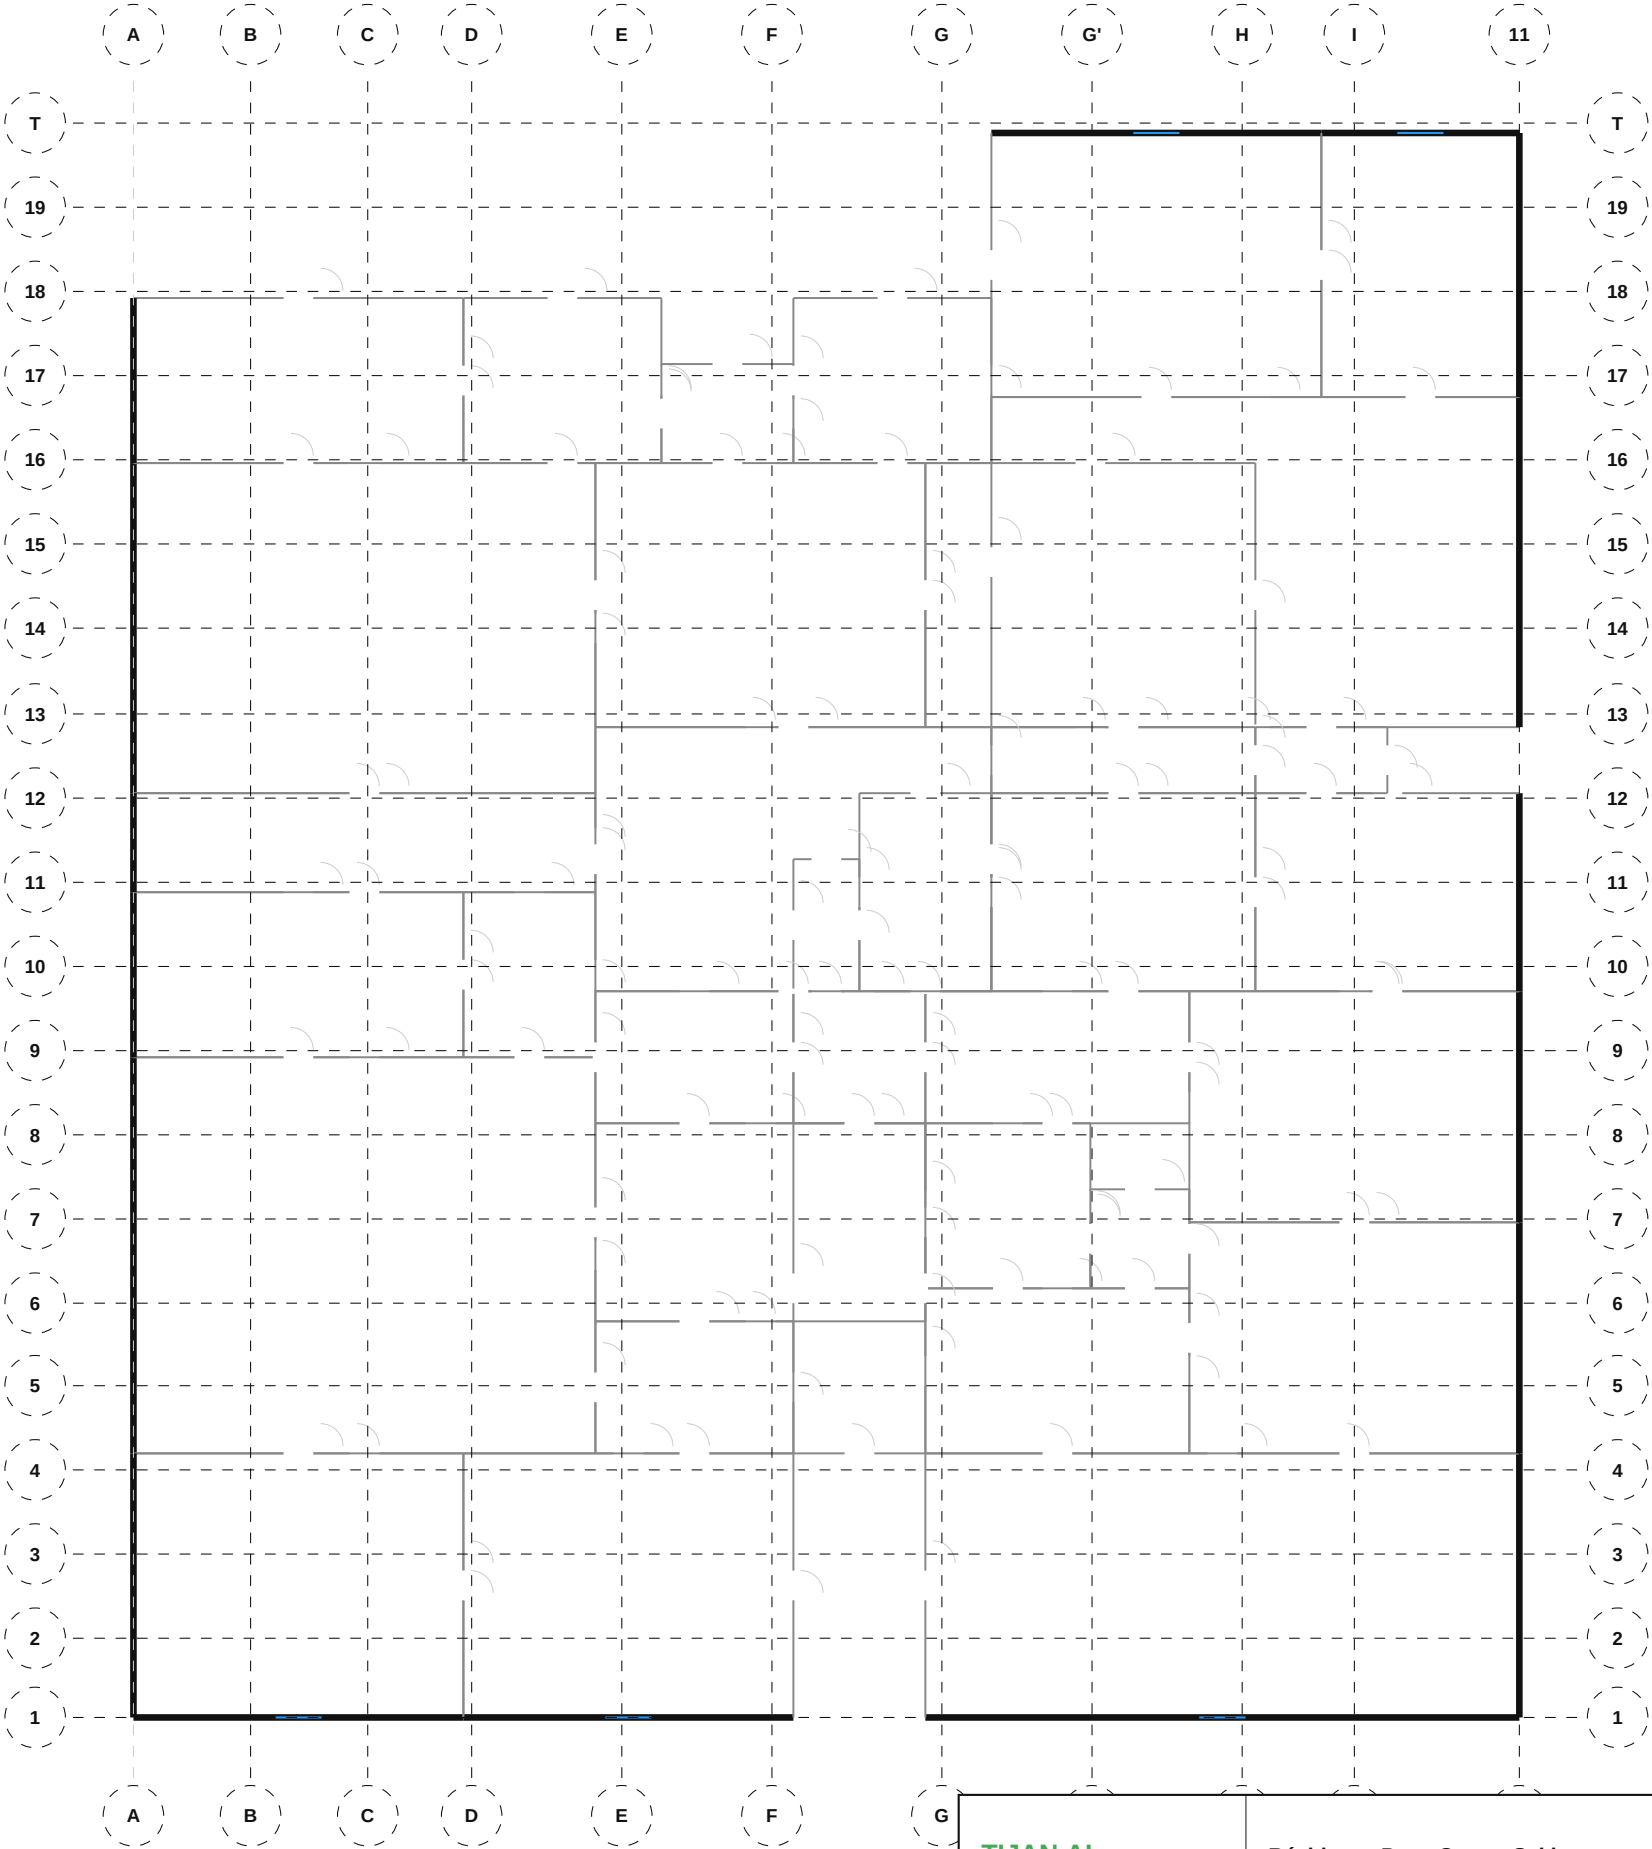


TIJAN AI Bureau d'Études Automatisé	Résidence Papa Oumar Sakho Dakar, Senegal		Éch: 1/100 Pl. 20/88
	Structure — Étage 7		
	Date: 06/05/2026	Réf: 1711	BIM vSTR-020 Phase: APD

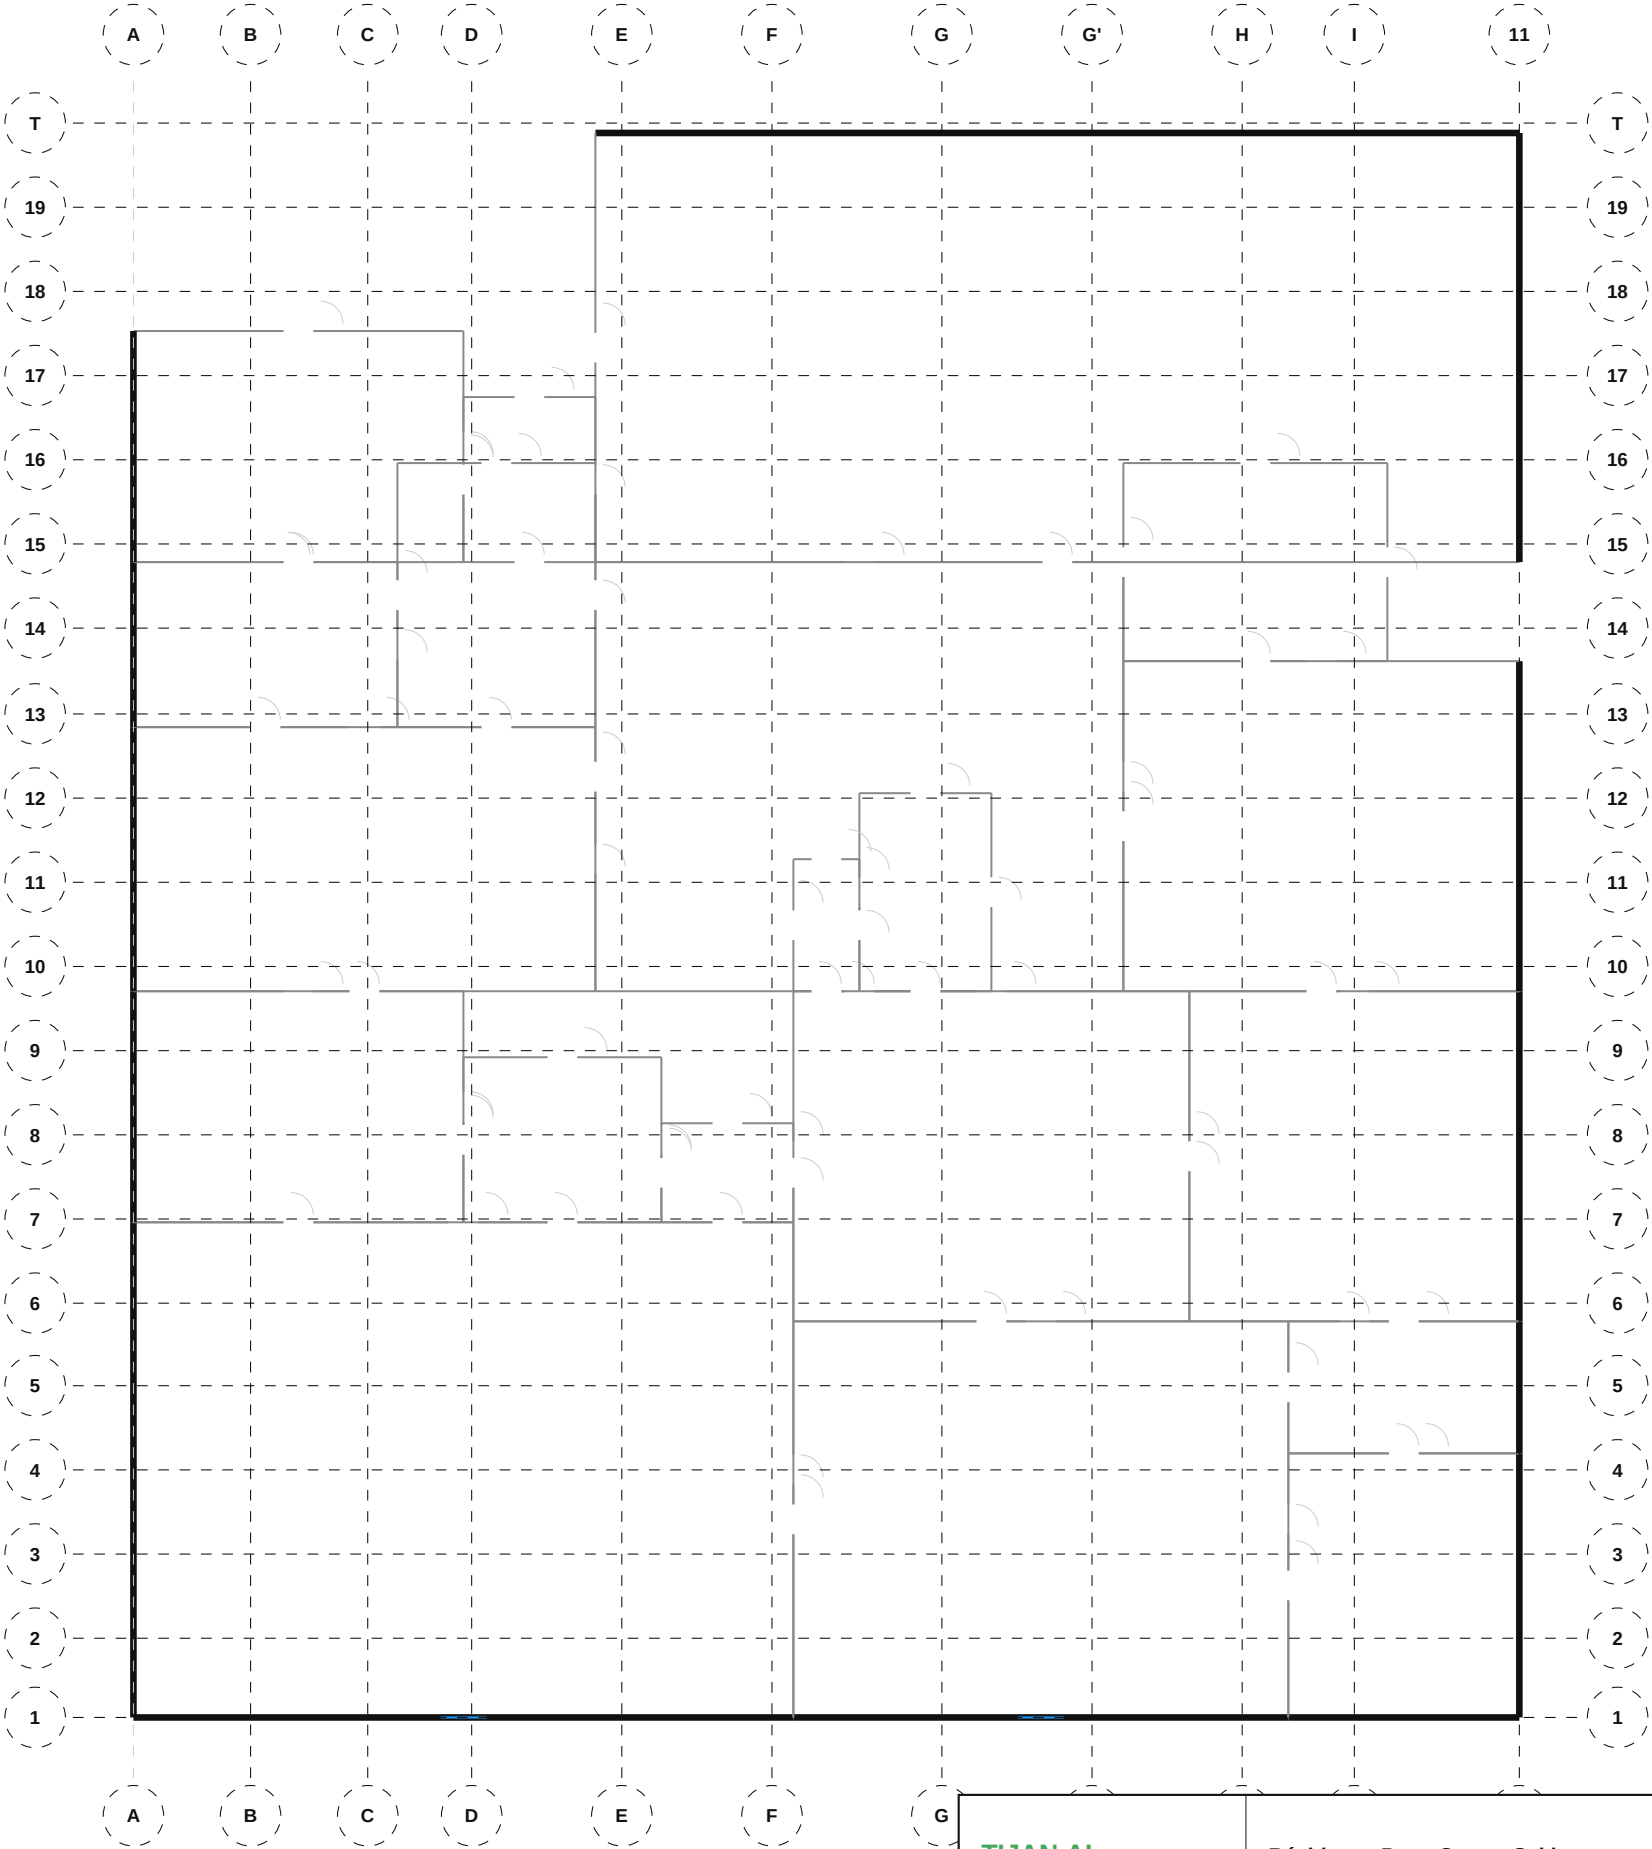

TIJAN AI Bureau d'Études Automatisé	Résidence Papa Oumar Sakho		Éch: 1/100
	Dakar, Senegal		Pl. 21/88
	Structure — Étage 8		
Date: 06/05/2026	Réf: 1711		BIM vSTR-021
			Phase: APD

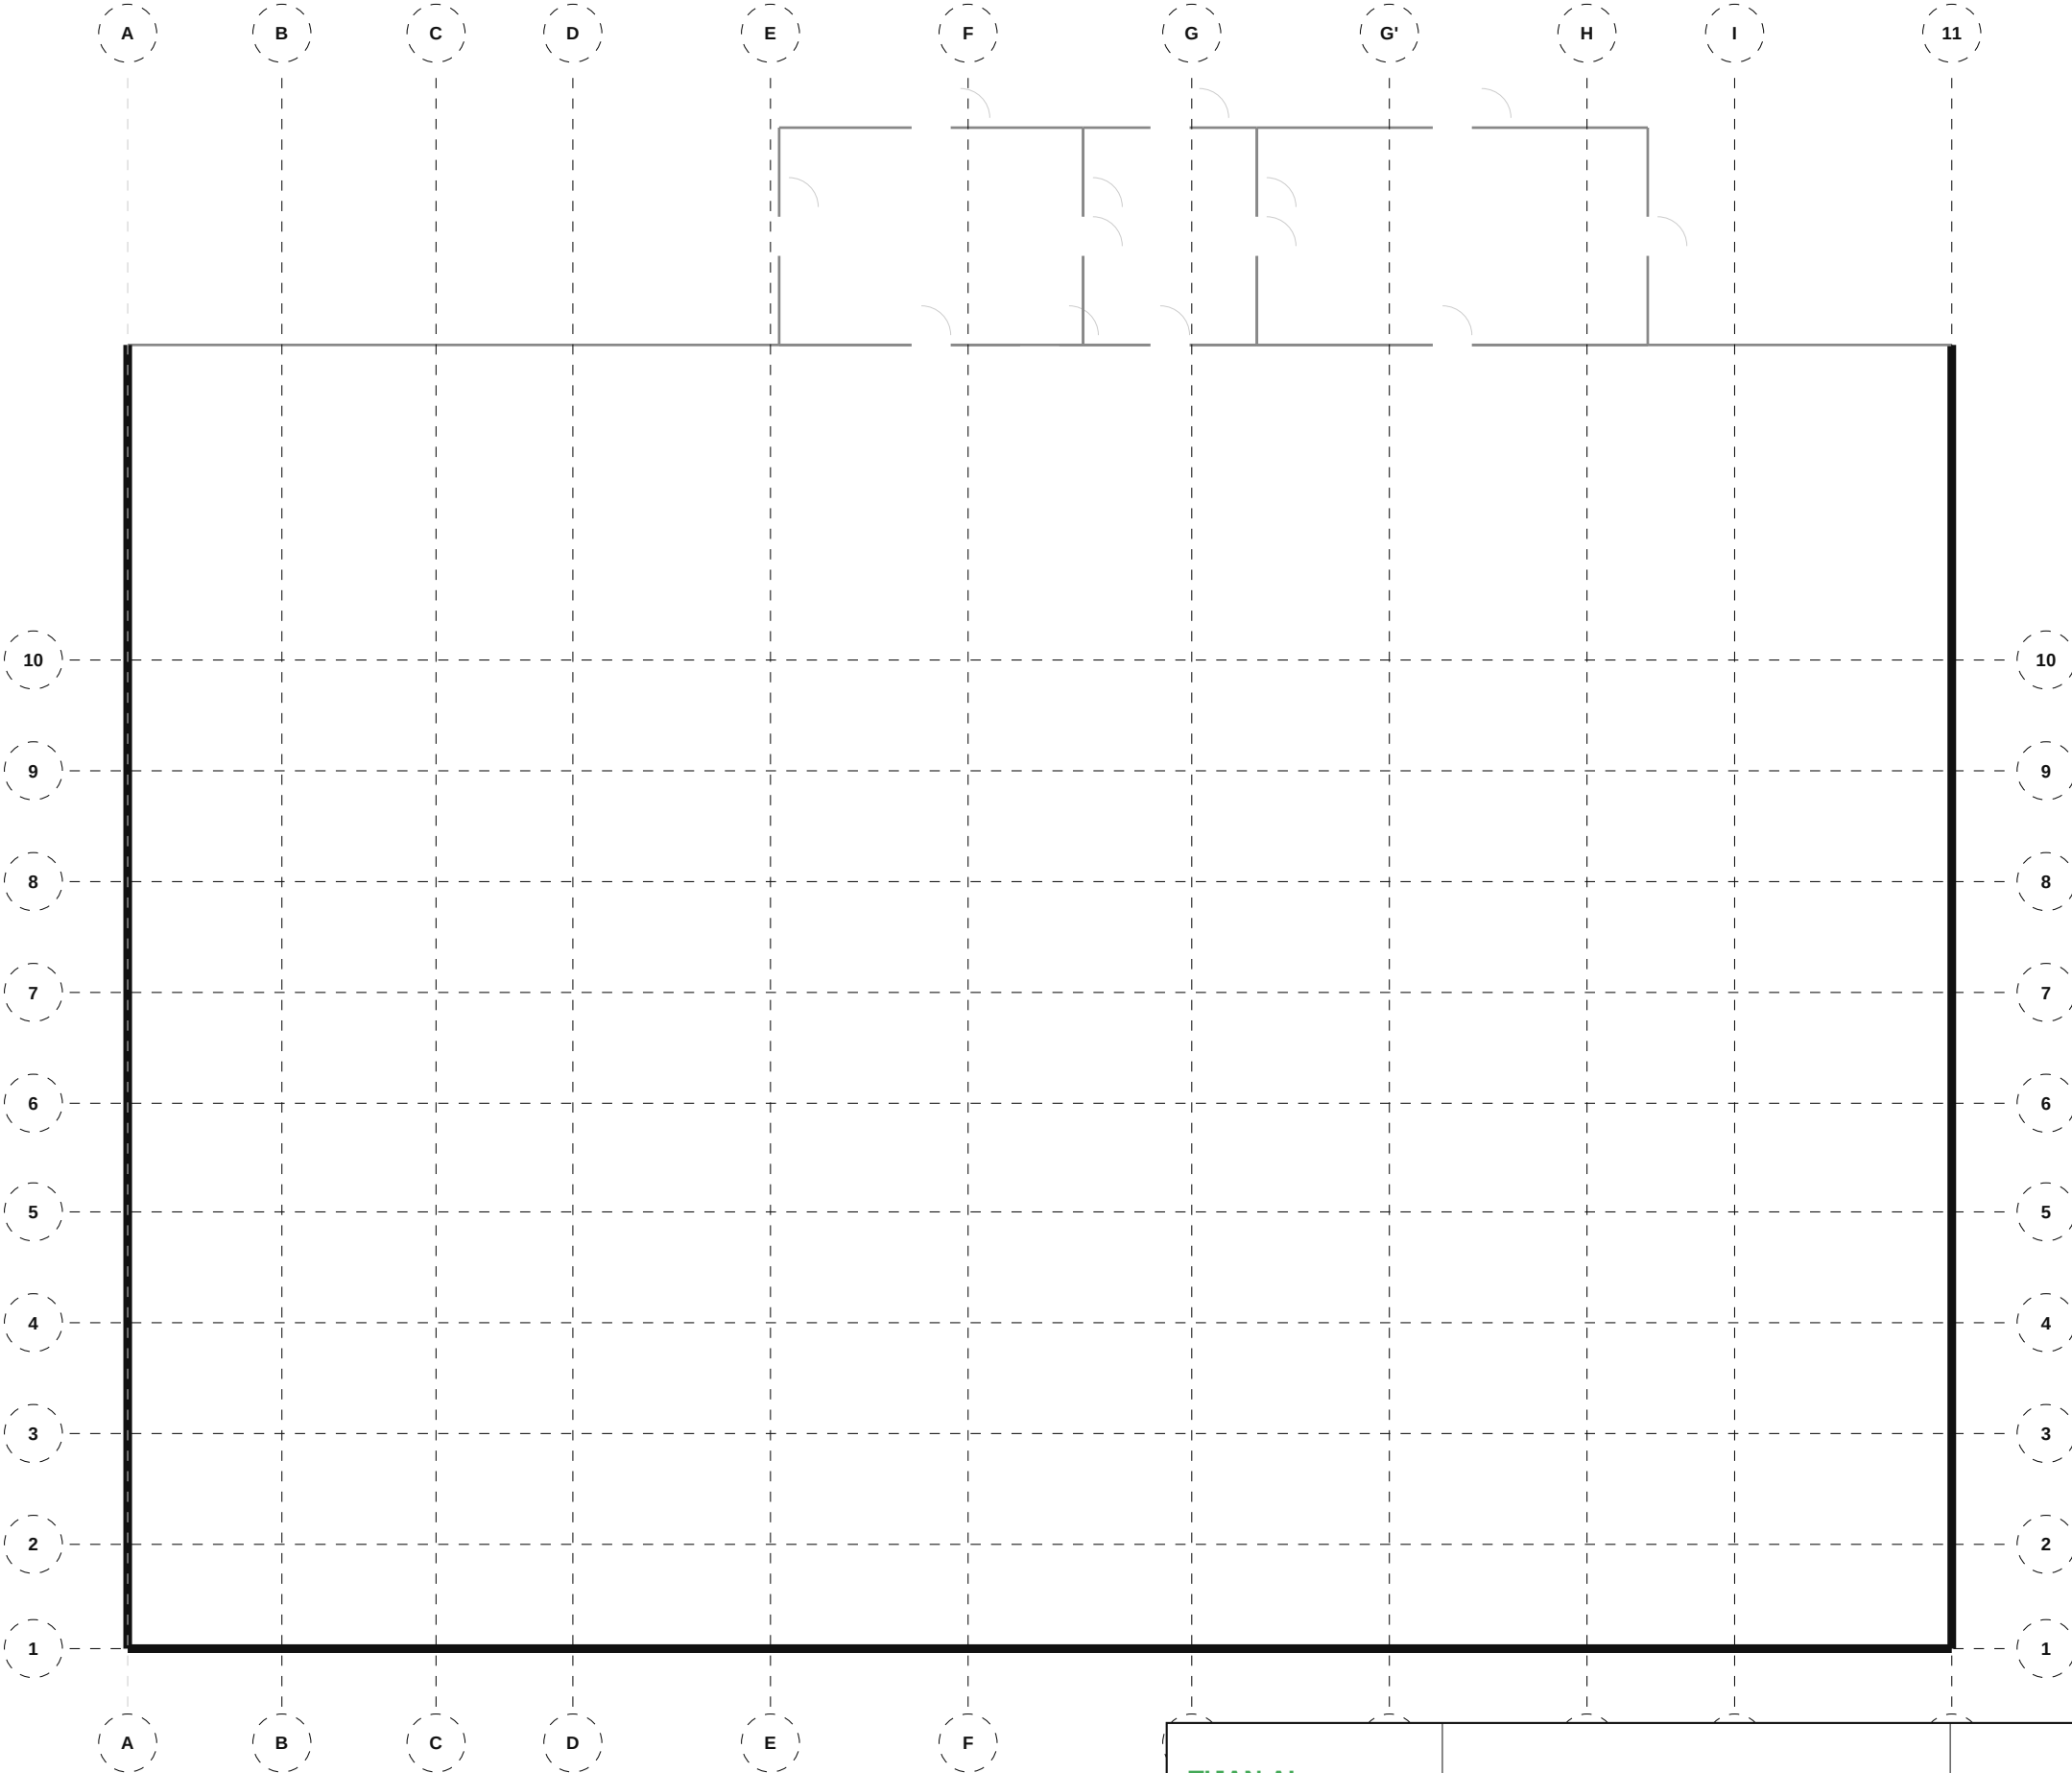


TIJAN AI Bureau d'Études Automatisé	Résidence Papa Oumar Sakho Dakar, Senegal	Éch: 1/100 Pl. 22/88
	Structure — Terrasse	
Date: 06/05/2026	Réf: 1711	BIM vSTR-022 Phase: APD

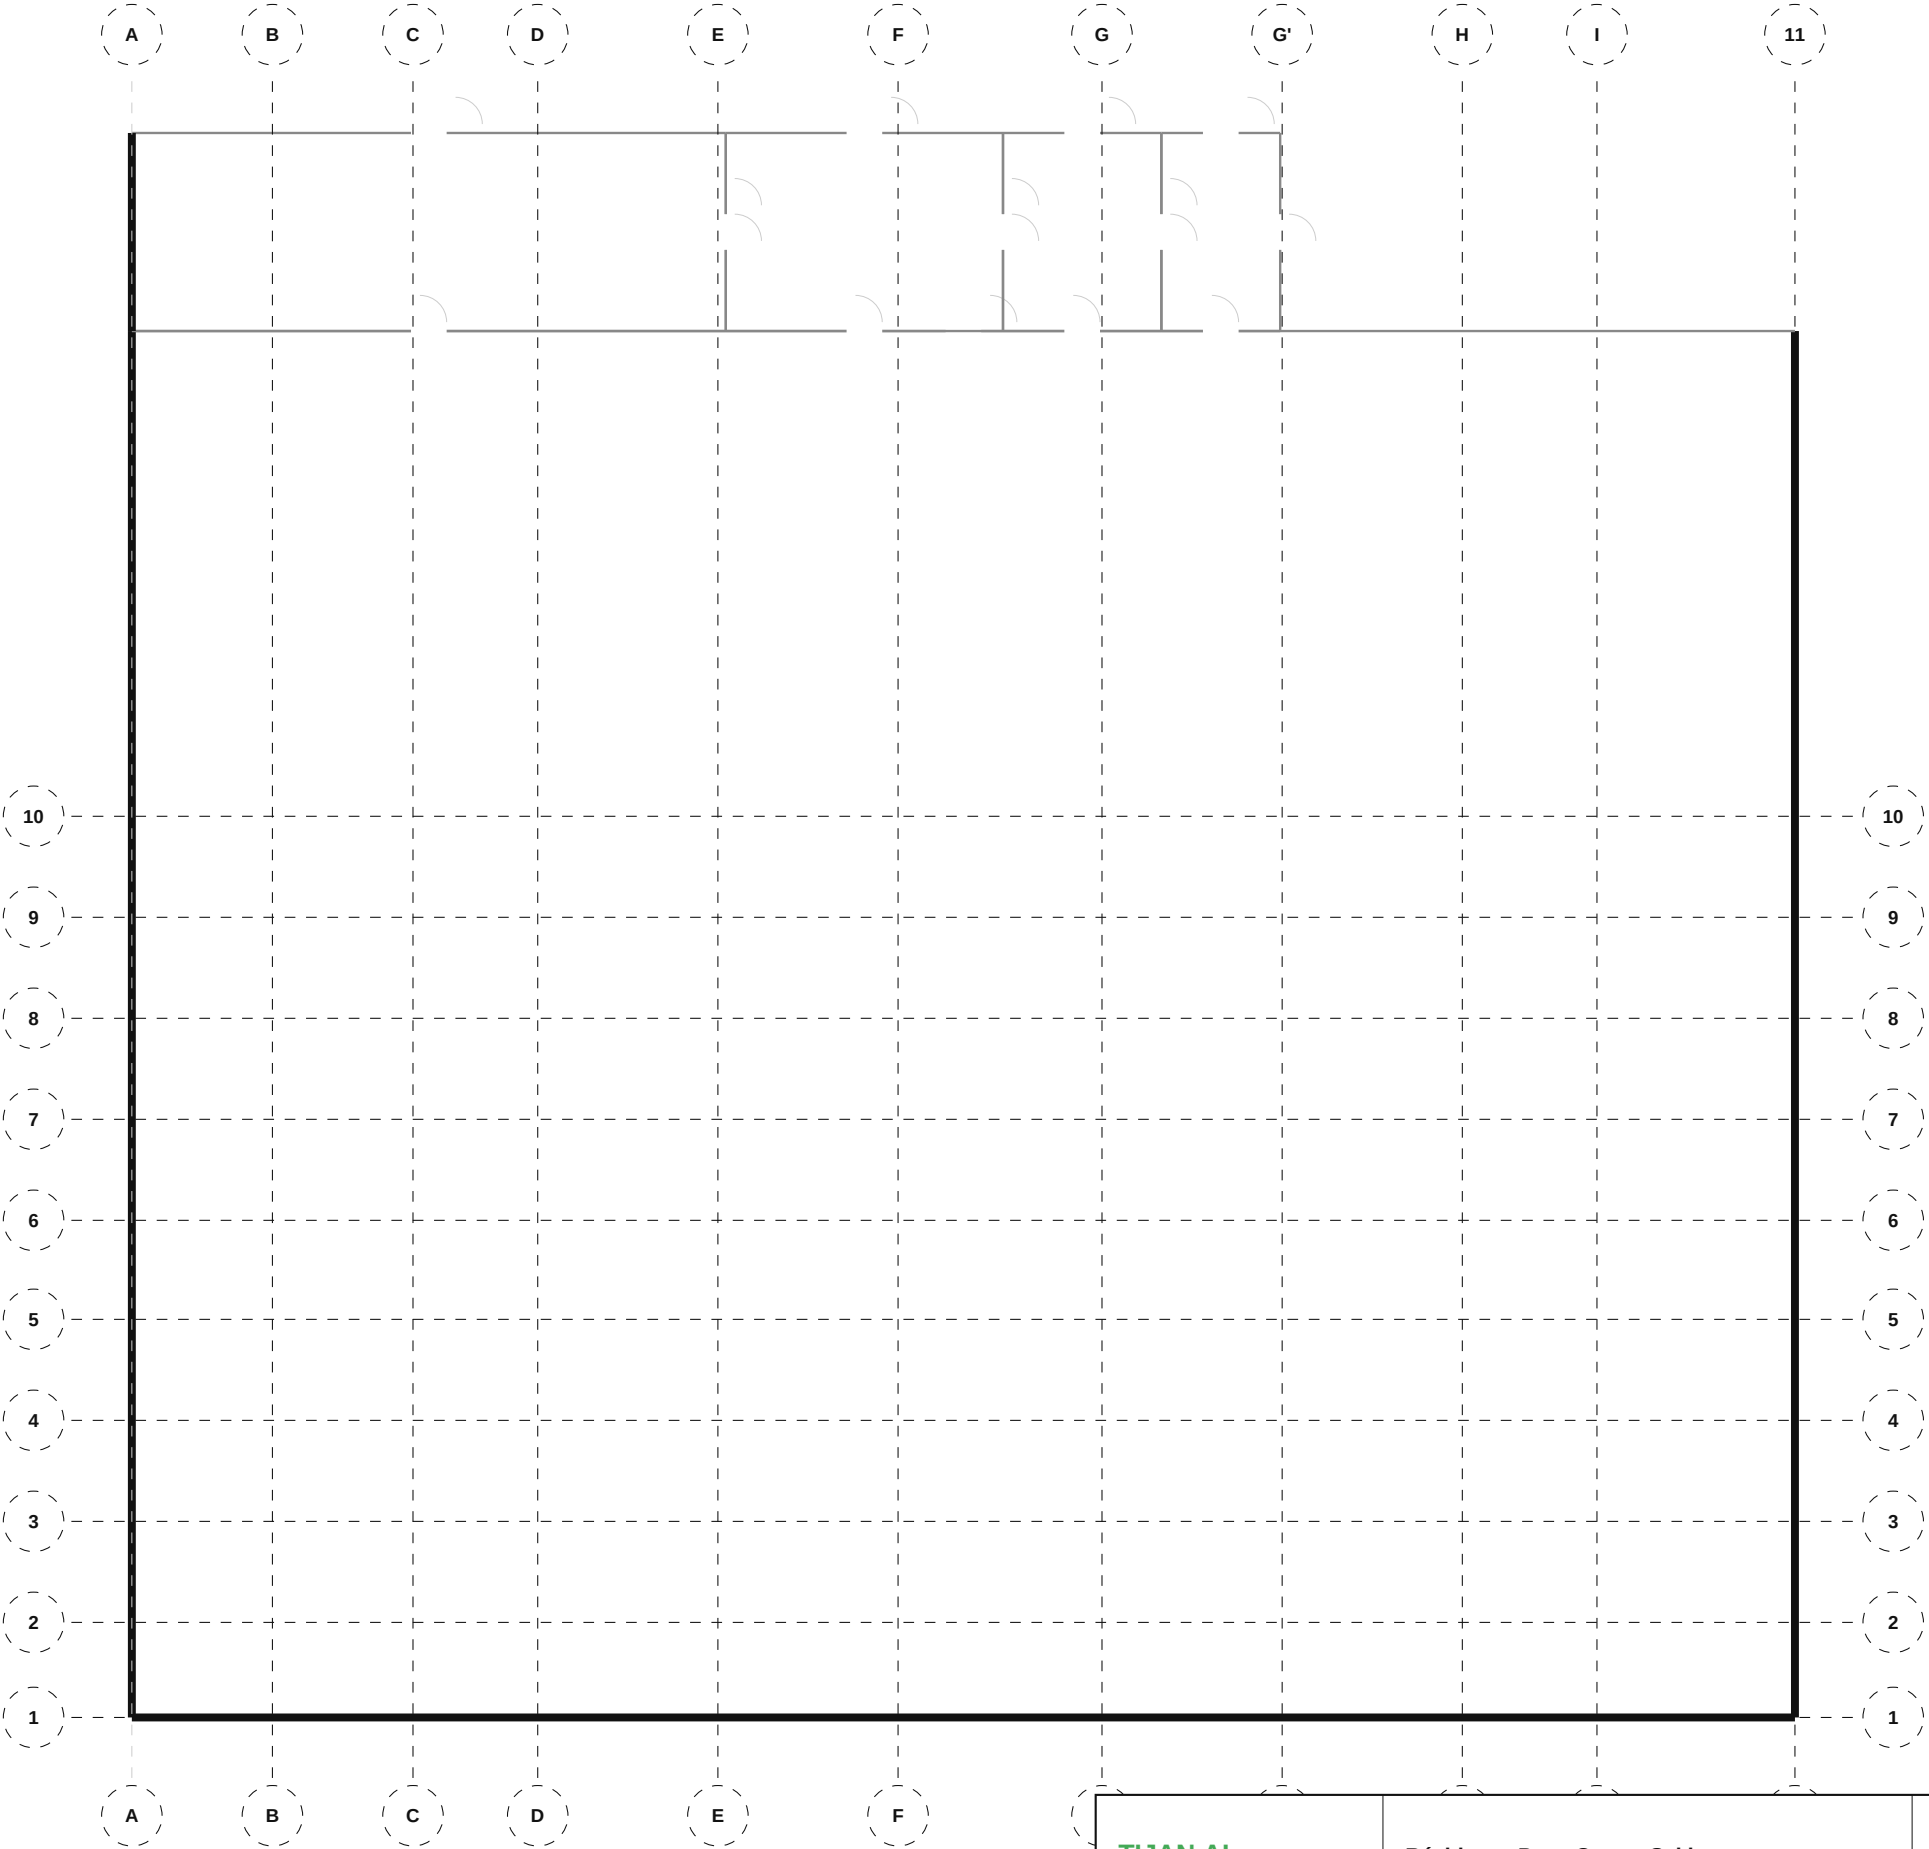


TIJAN AI Bureau d'Études Automatisé	Résidence Papa Oumar Sakho Dakar, Senegal	Éch: 1/100 Pl. 23/88
	Sécurité Incendie — Sous-Sol	
Date: 06/05/2026	Réf: 1711	BIM VFIF-023 Phase: APD

NOMENCLATURE — Sécurité Incendie

• Sprinkler: 11

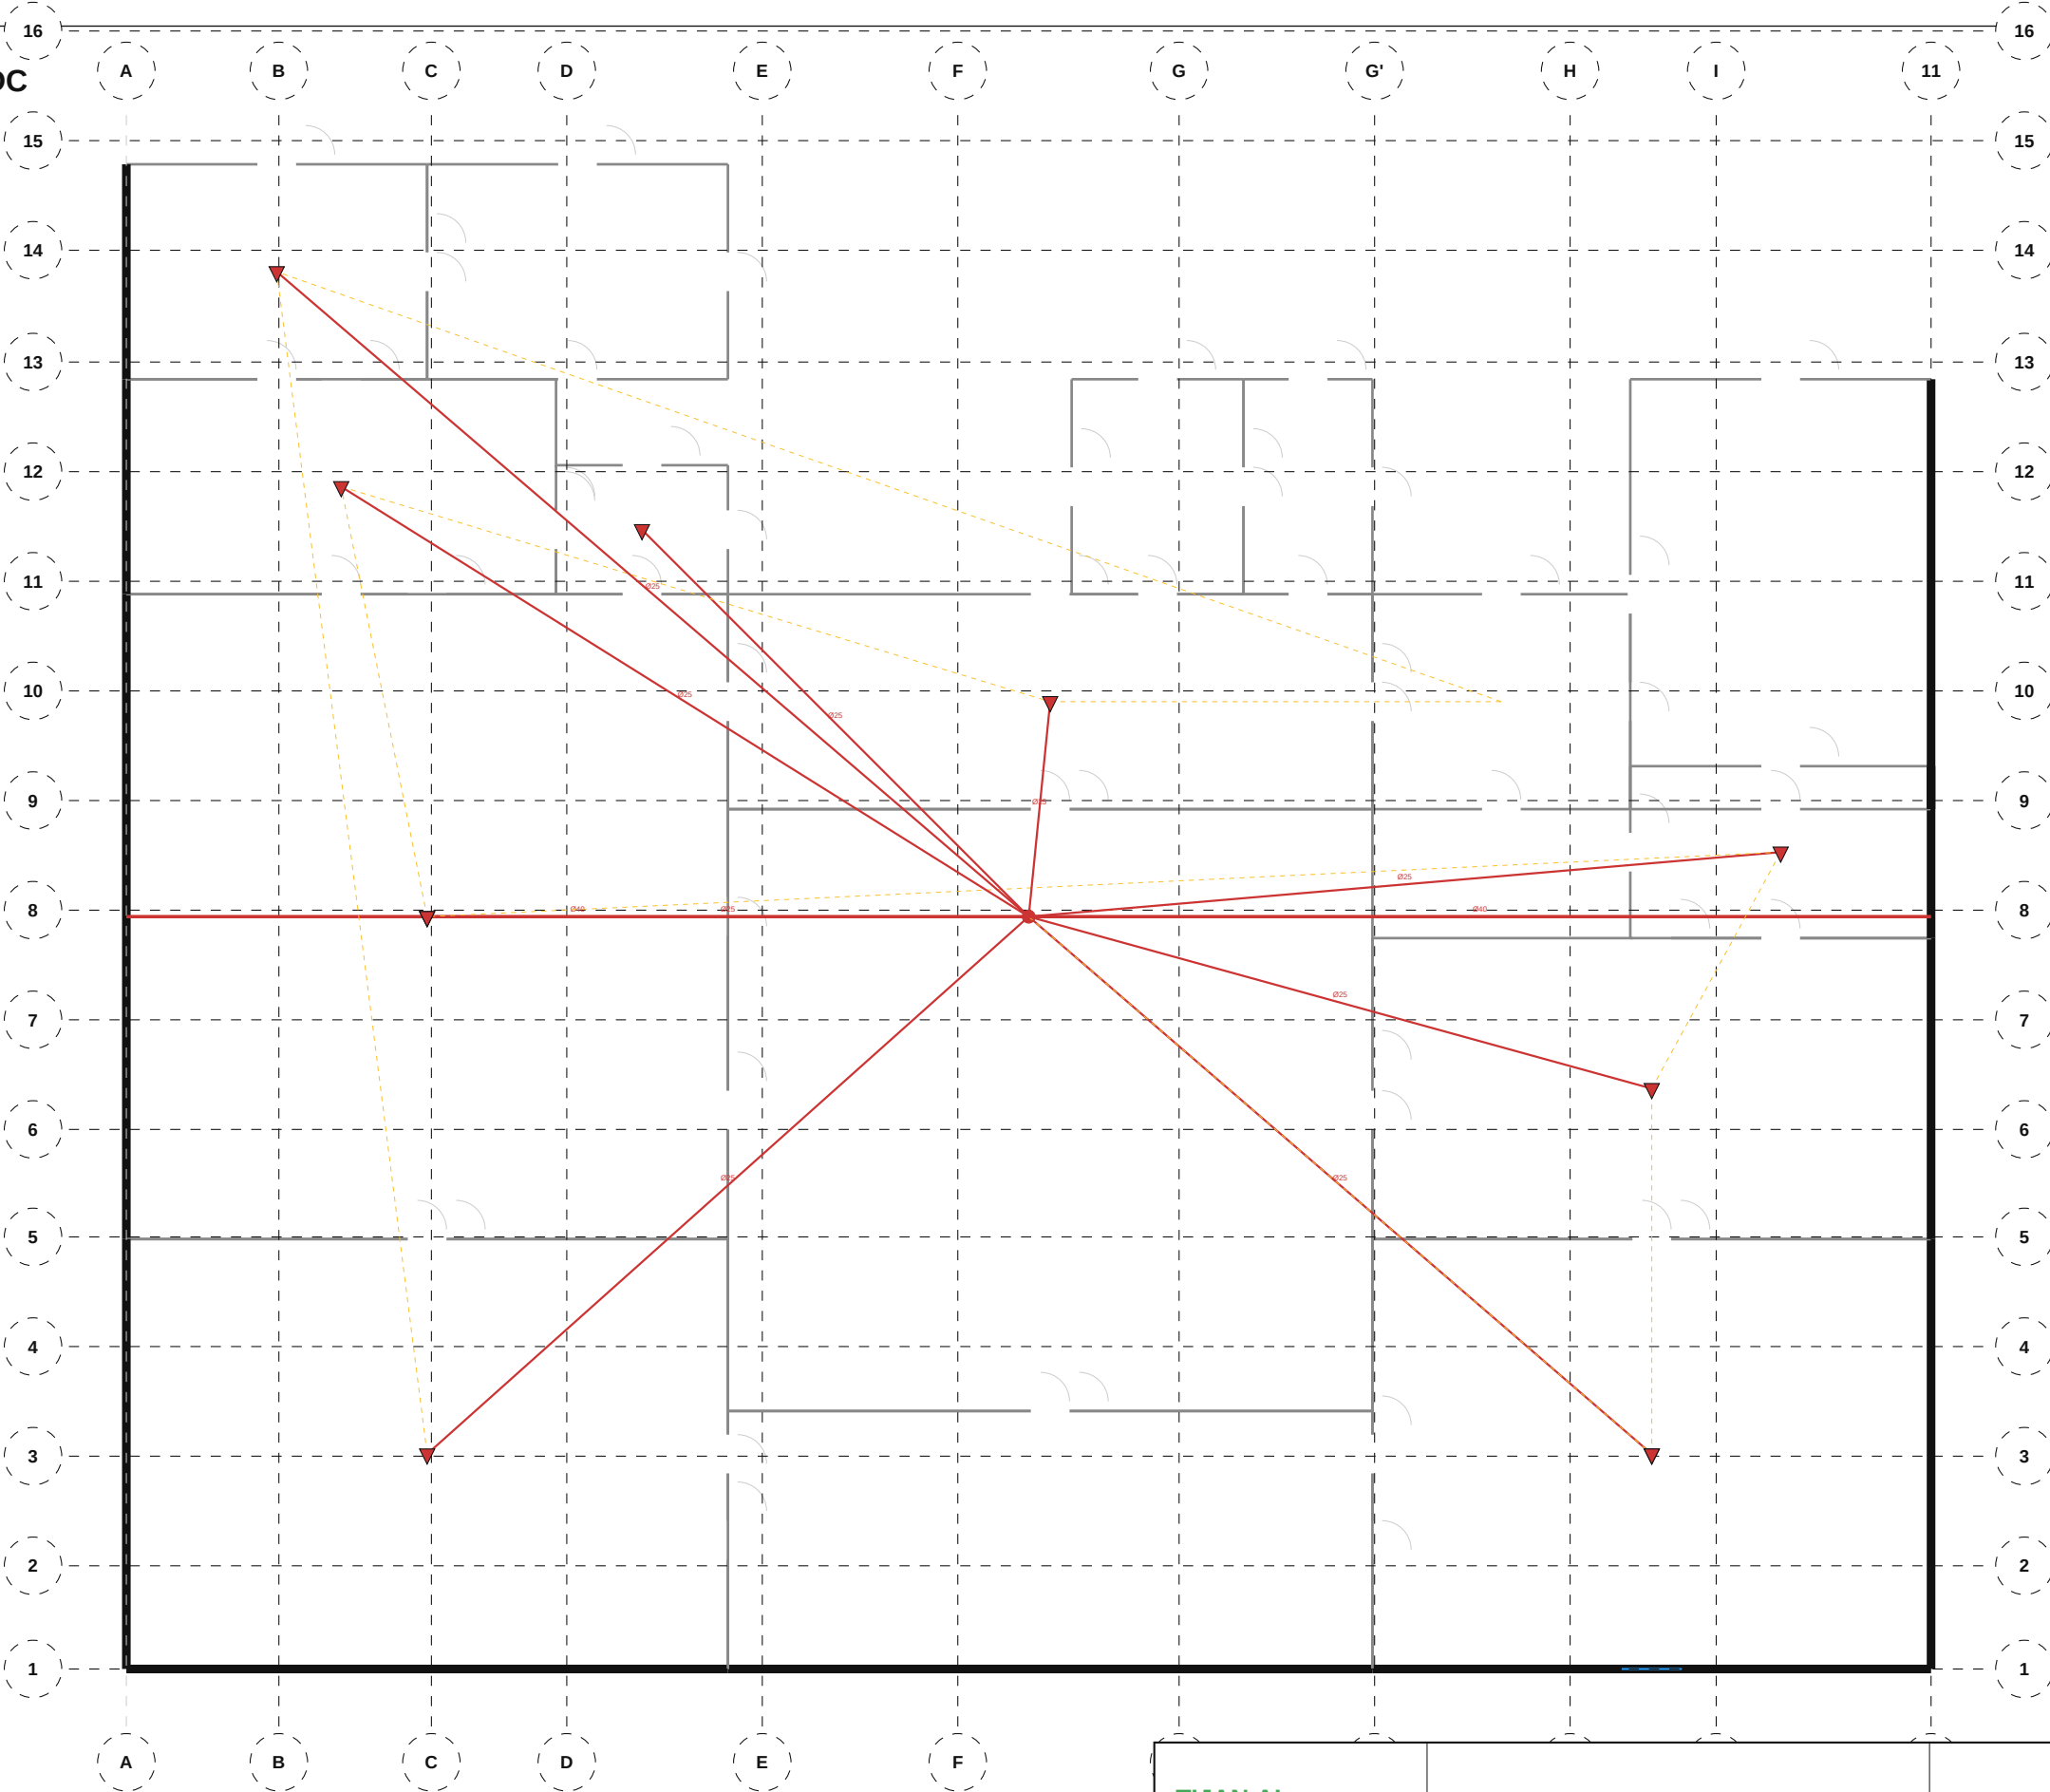


TIJAN AI Bureau d'Études Automatisé	Résidence Papa Oumar Sakho Dakar, Senegal	Éch: 1/100 Pl. 24/88
	Sécurité Incendie — RDC	
Date: 06/05/2026	Réf: 1711	BIM VFIF-024 Phase: APD

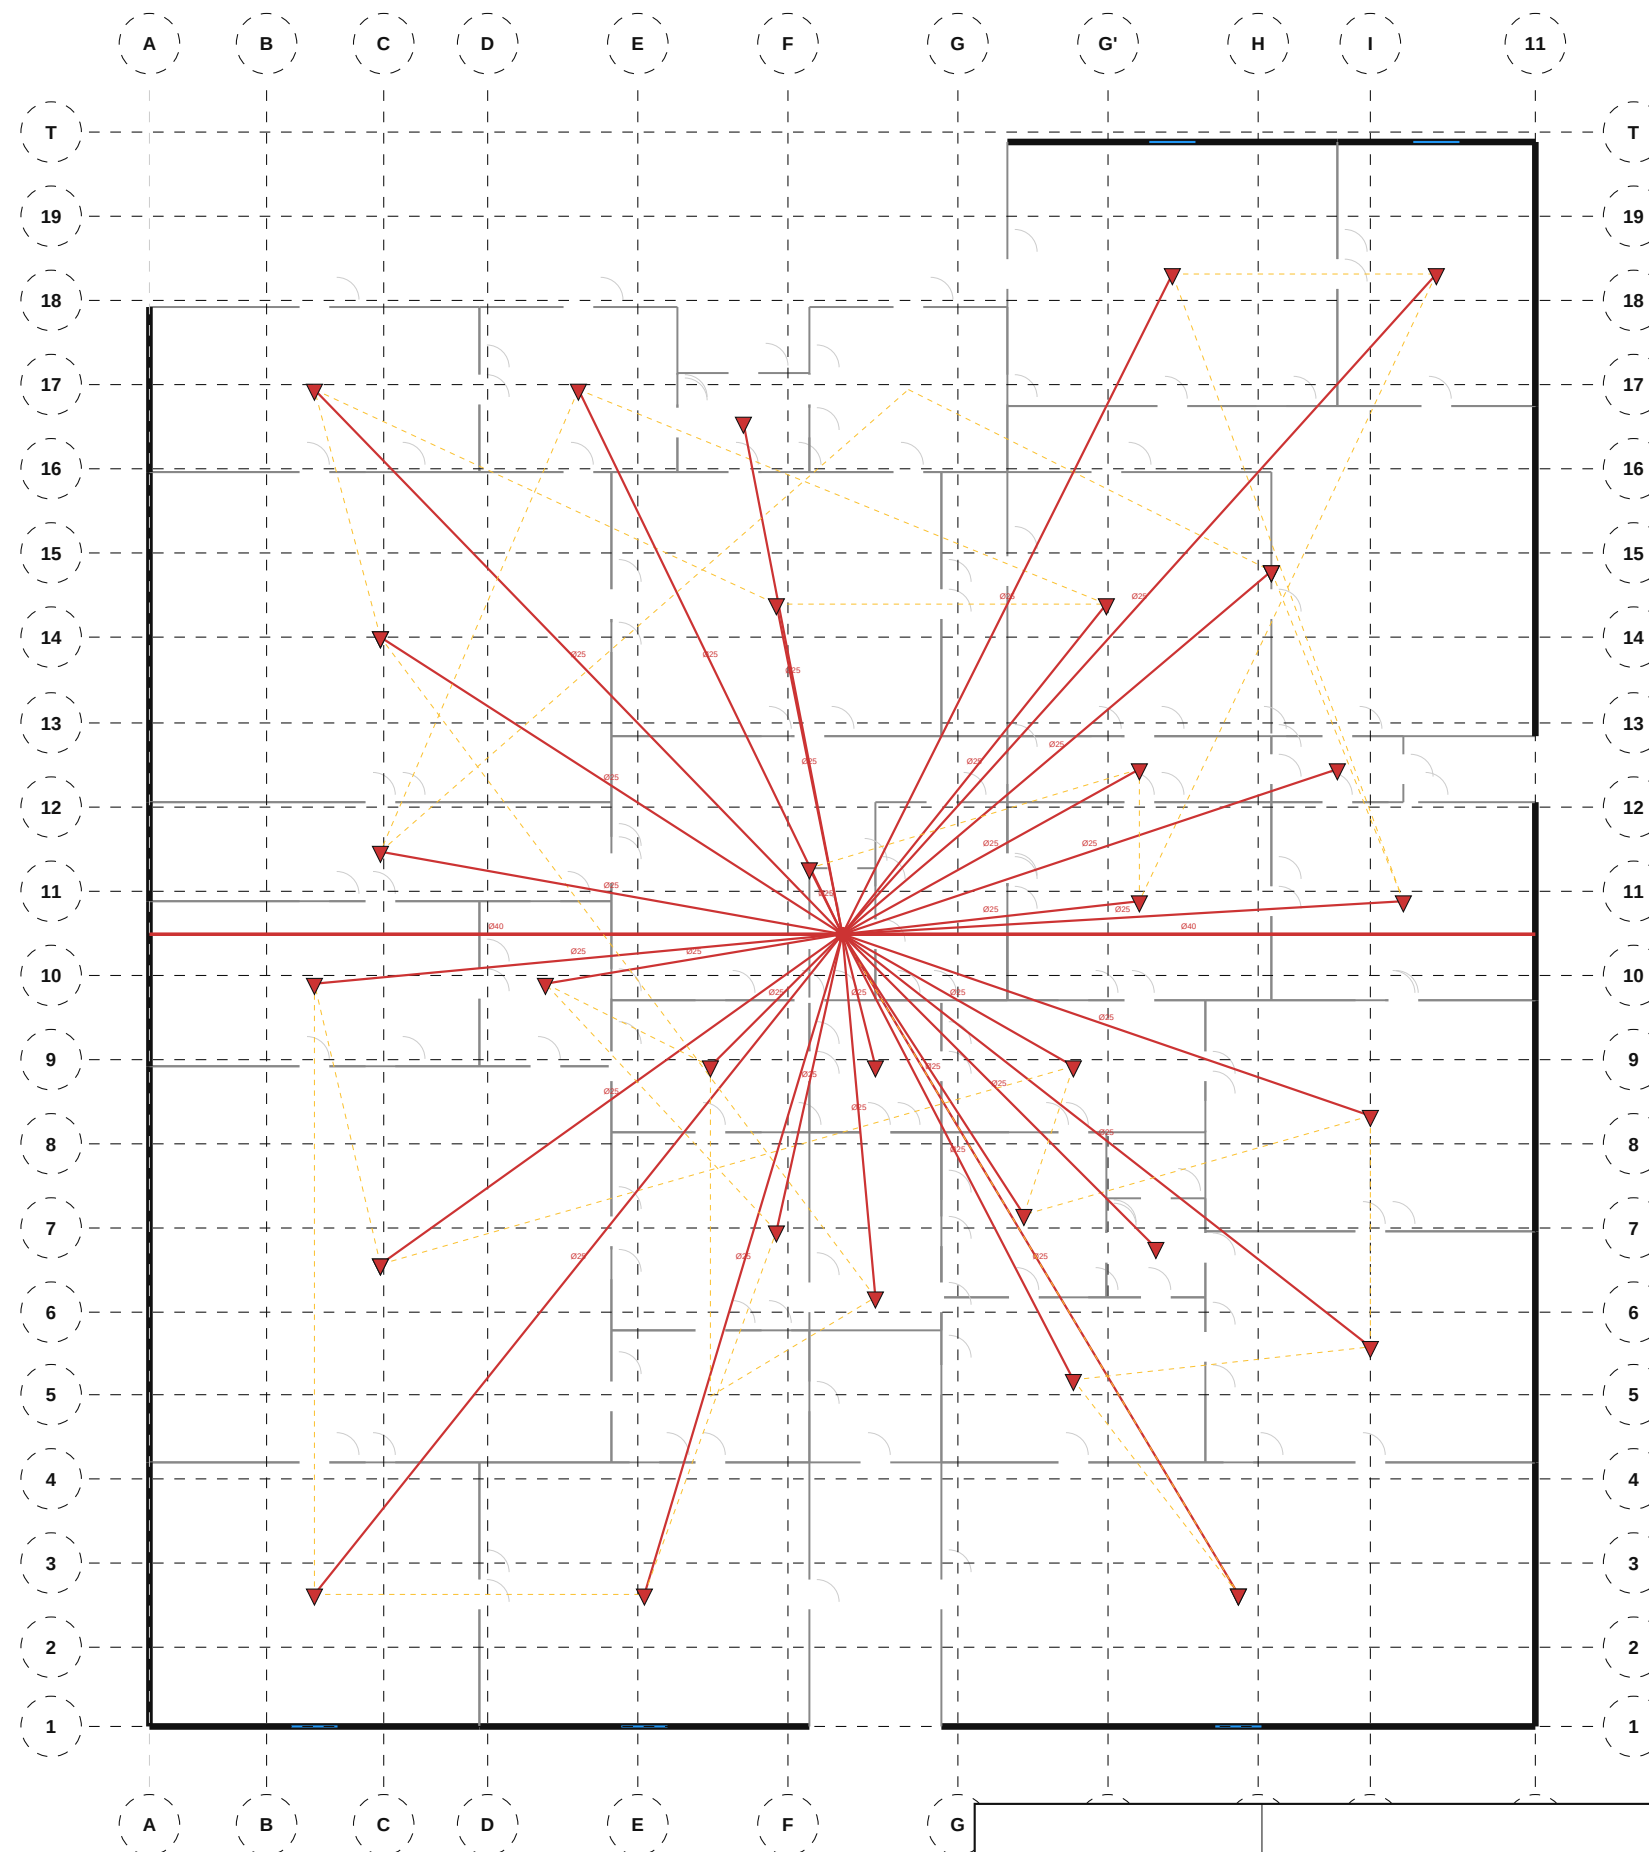

NOMENCLATURE — Sécurité Incendie

- Sprinkler: 35


TIJAN AI Bureau d'Études Automatisé	Résidence Papa Oumar Sakho Dakar, Senegal	Éch: 1/100 Pl. 25/88
	Sécurité Incendie — Étage 1	
Date: 06/05/2026	Réf: 1711	BIM vFIF-025 Phase: APD

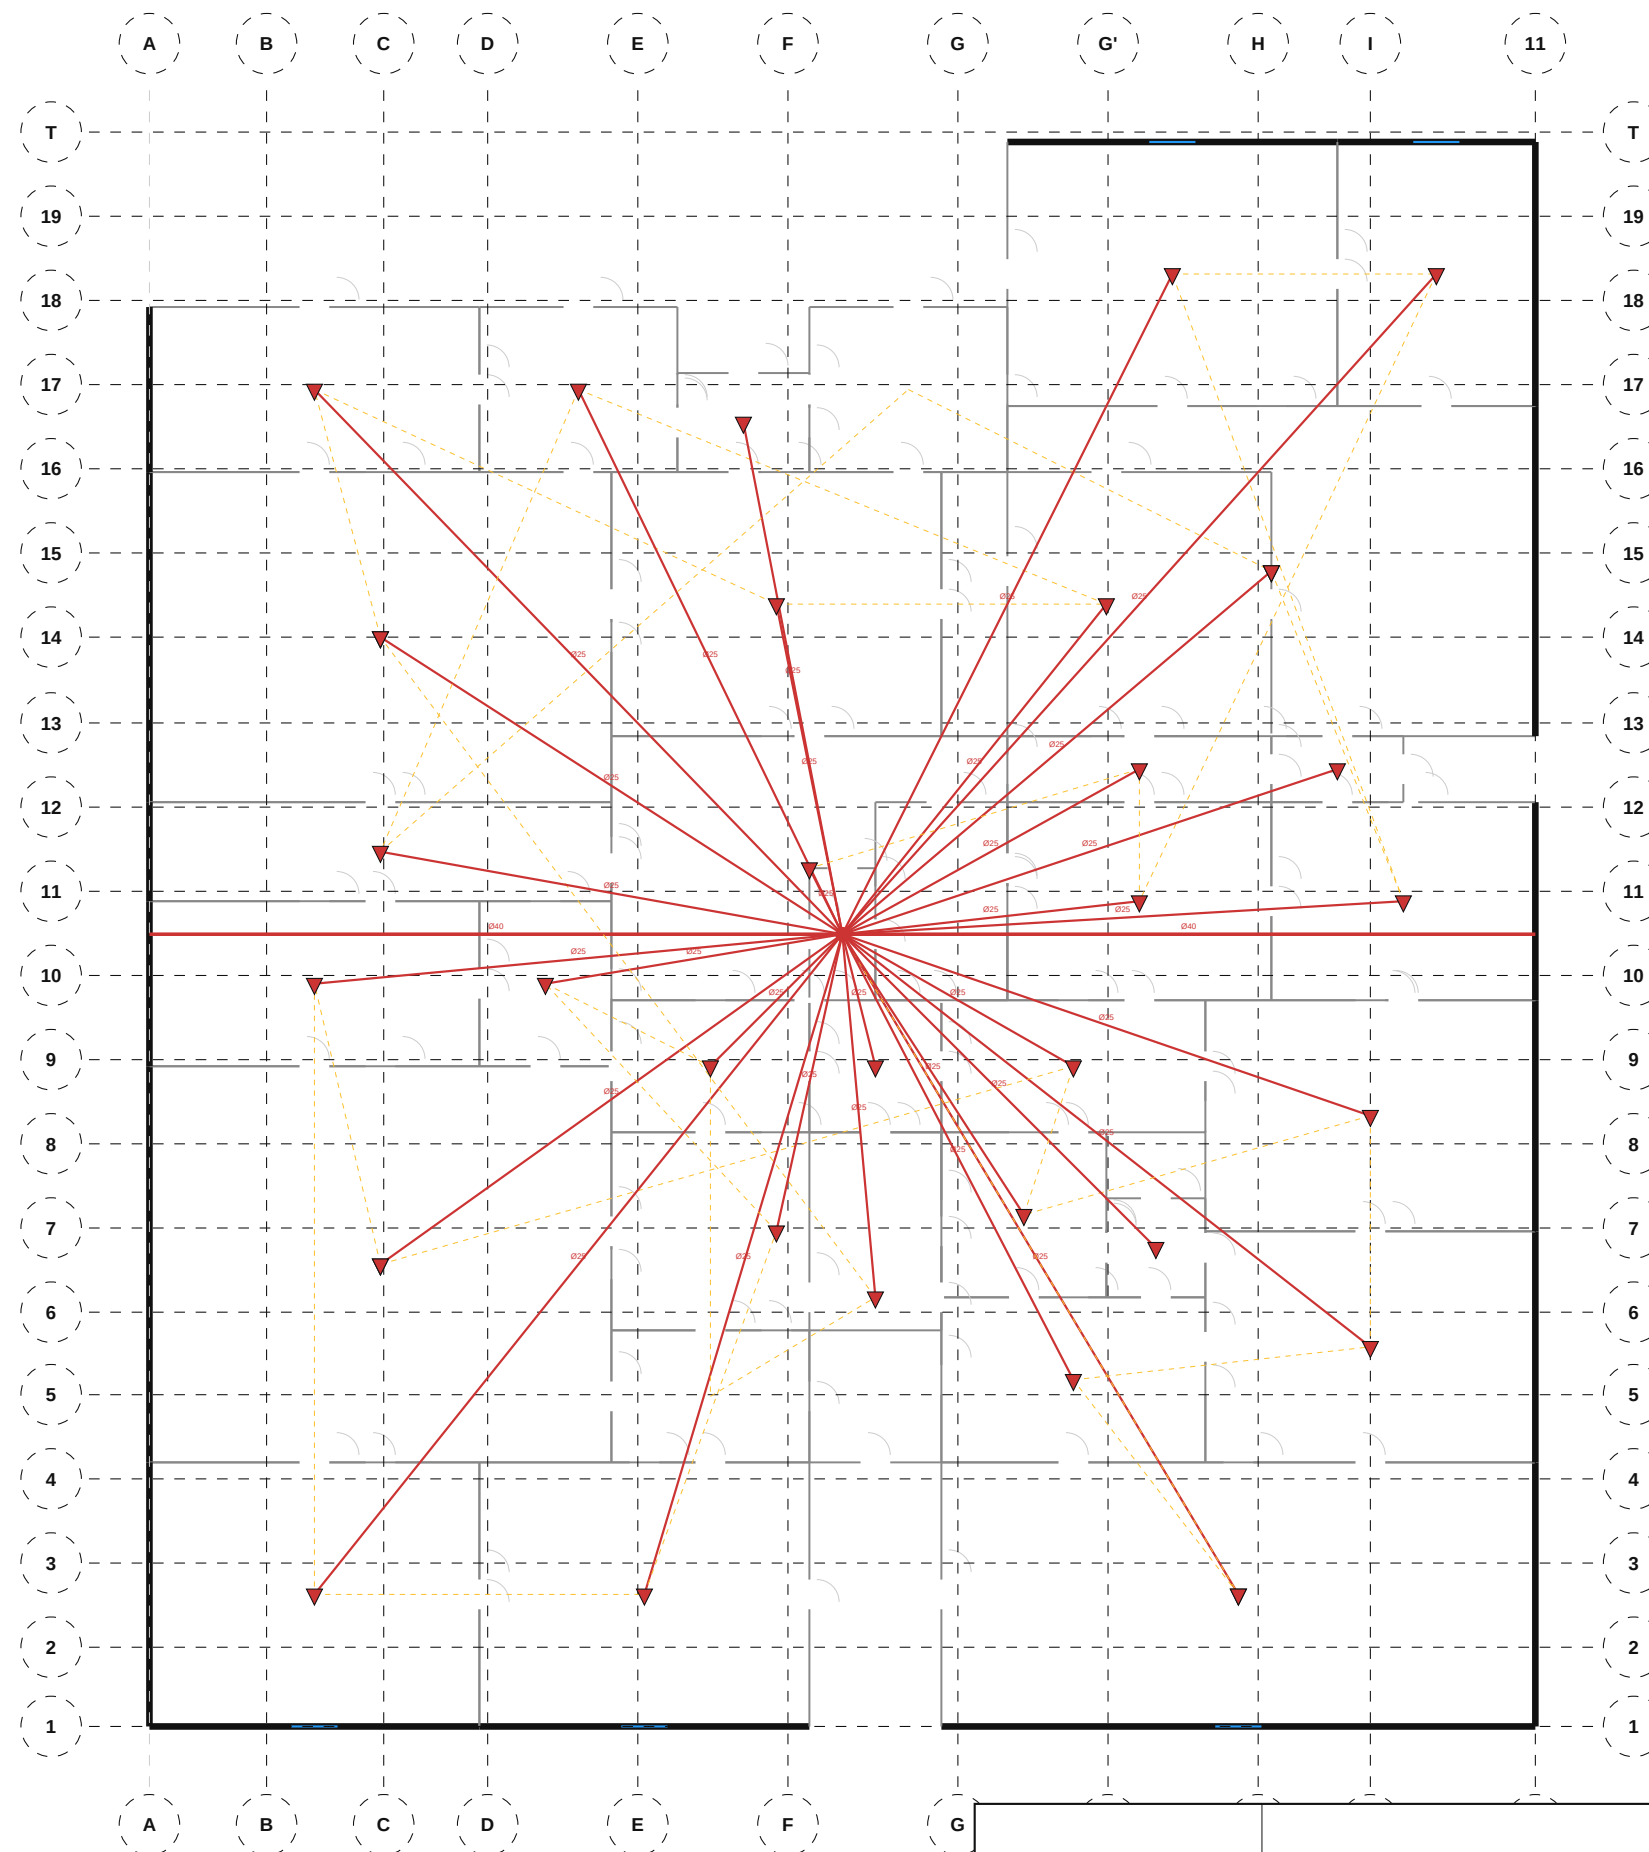

NOMENCLATURE — Sécurité Incendie

- Sprinkler: 35


TIJAN AI Bureau d'Études Automatisé	Résidence Papa Oumar Sakho Dakar, Senegal	Éch: 1/100 Pl. 26/88
	Sécurité Incendie — Étage 2	
Date: 06/05/2026	Réf: 1711	BIM vFIF-026 Phase: APD

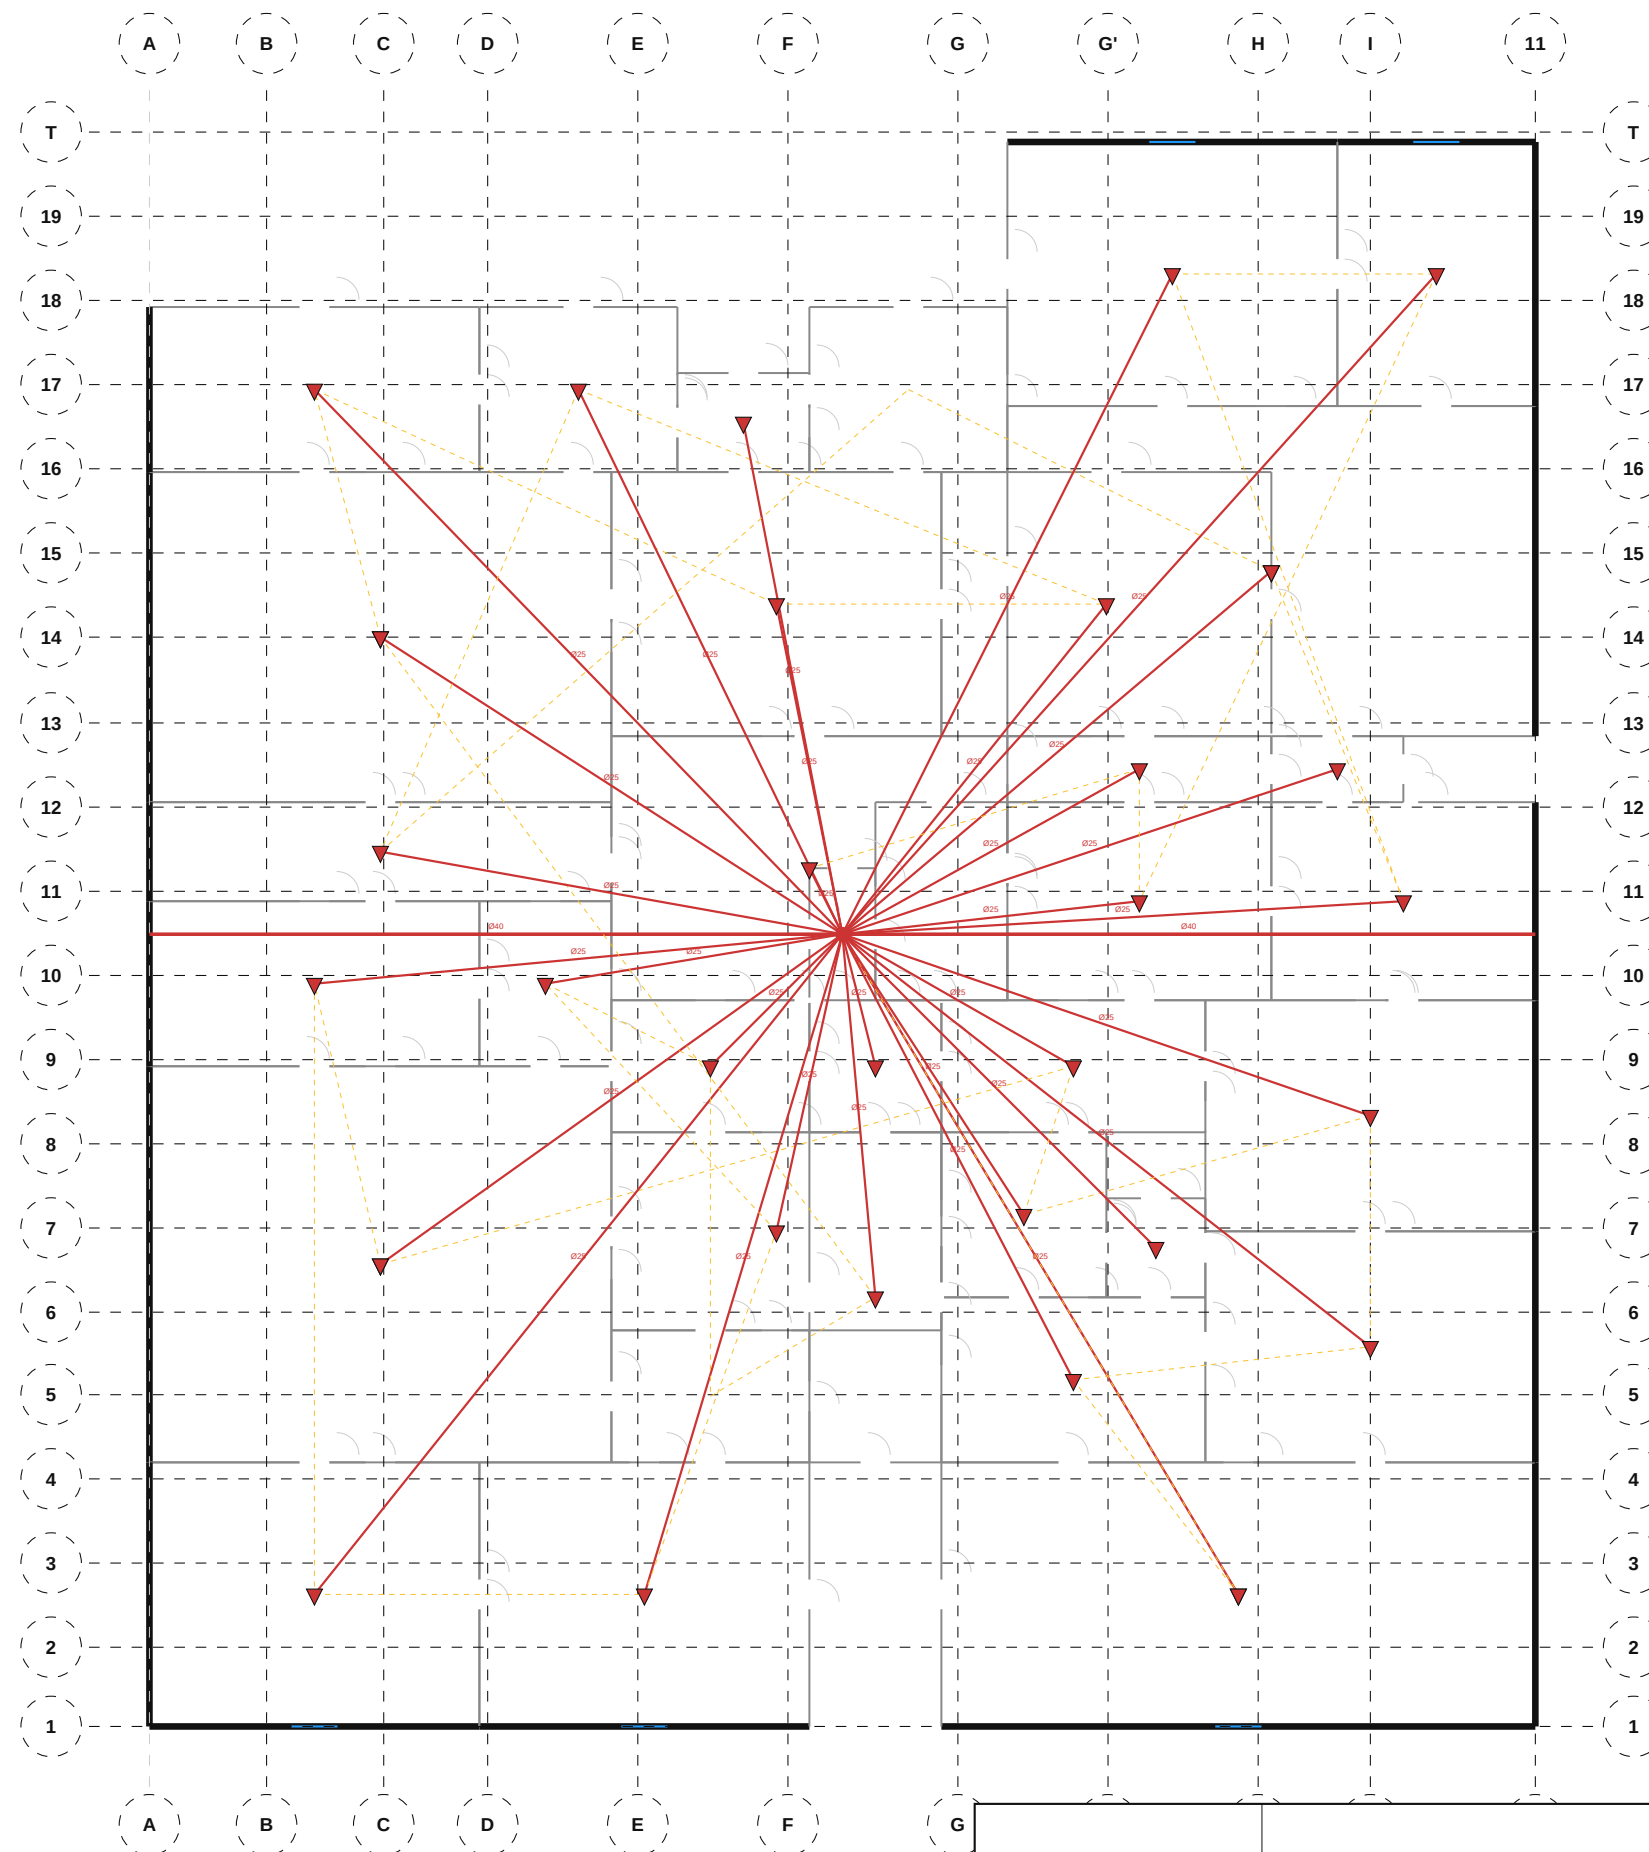

NOMENCLATURE — Sécurité Incendie

- Sprinkler: 35


TIJAN AI Bureau d'Études Automatisé	Résidence Papa Oumar Sakho Dakar, Senegal	Éch: 1/100 Pl. 27/88
	Sécurité Incendie — Étage 3	
Date: 06/05/2026	Réf: 1711	BIM vFIF-027 Phase: APD

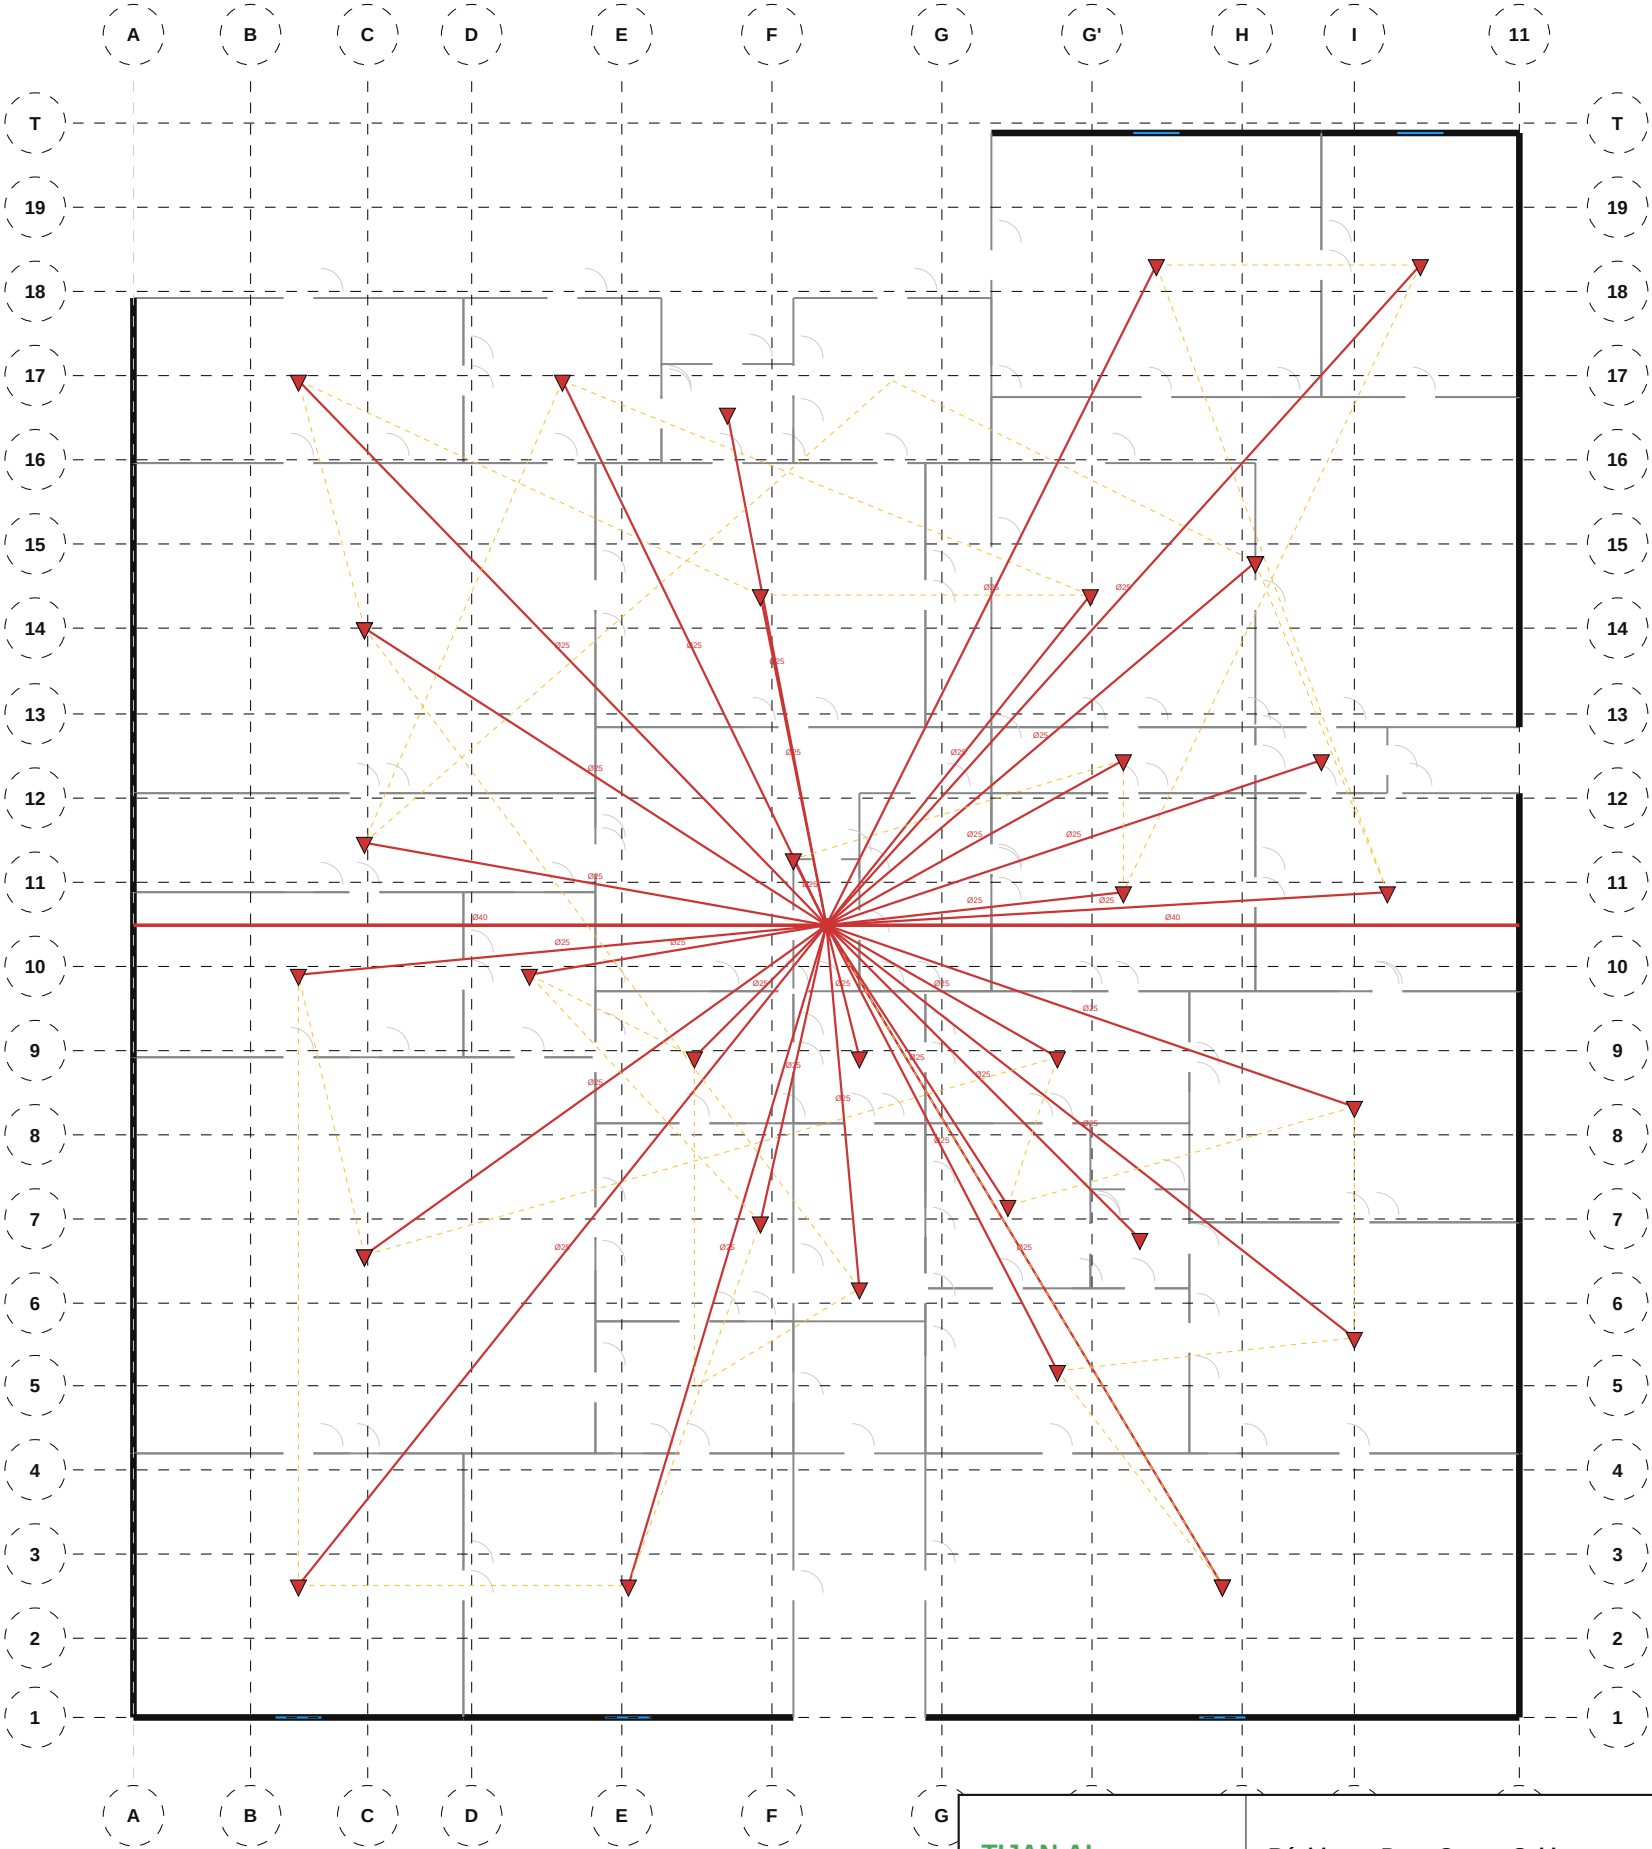

NOMENCLATURE — Sécurité Incendie

• Sprinkler: 35


TIJAN AI Bureau d'Études Automatisé	Résidence Papa Oumar Sakho Dakar, Senegal	Éch: 1/100 Pl. 28/88
	Sécurité Incendie — Étage 4	
Date: 06/05/2026	Réf: 1711	BIM VFIF-028 Phase: APD

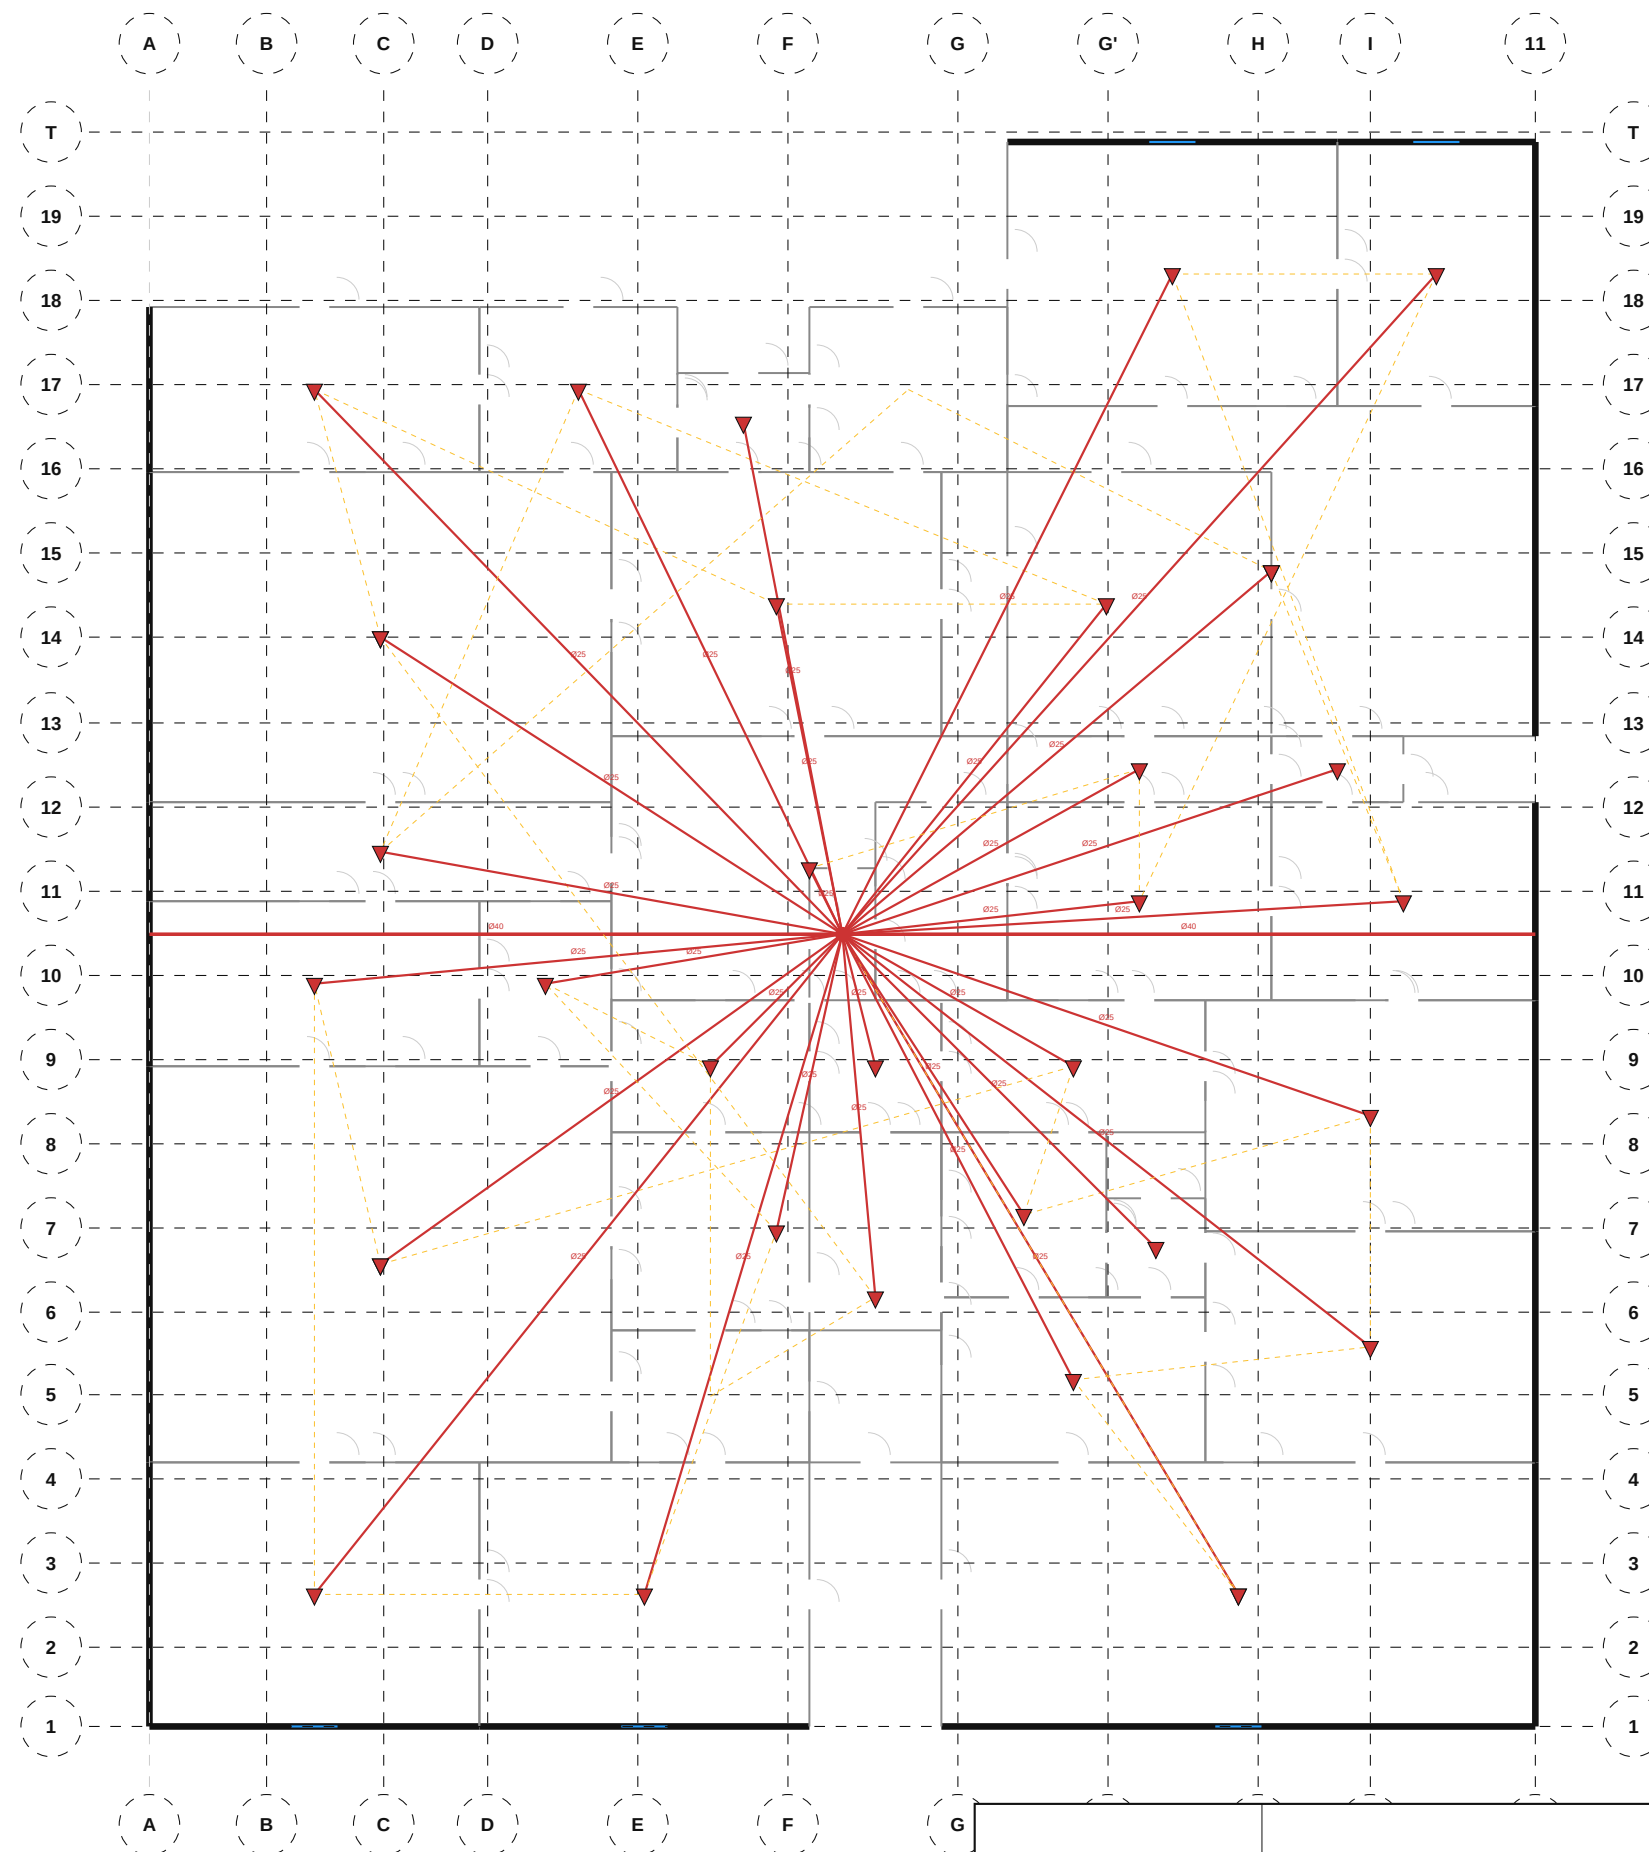

NOMENCLATURE — Sécurité Incendie

- Sprinkler: 35


TIJAN AI Bureau d'Études Automatisé	Résidence Papa Oumar Sakho Dakar, Senegal	Éch: 1/100 Pl. 29/88
	Sécurité Incendie — Étage 5	
Date: 06/05/2026	Réf: 1711	BIM vFIF-029 Phase: APD

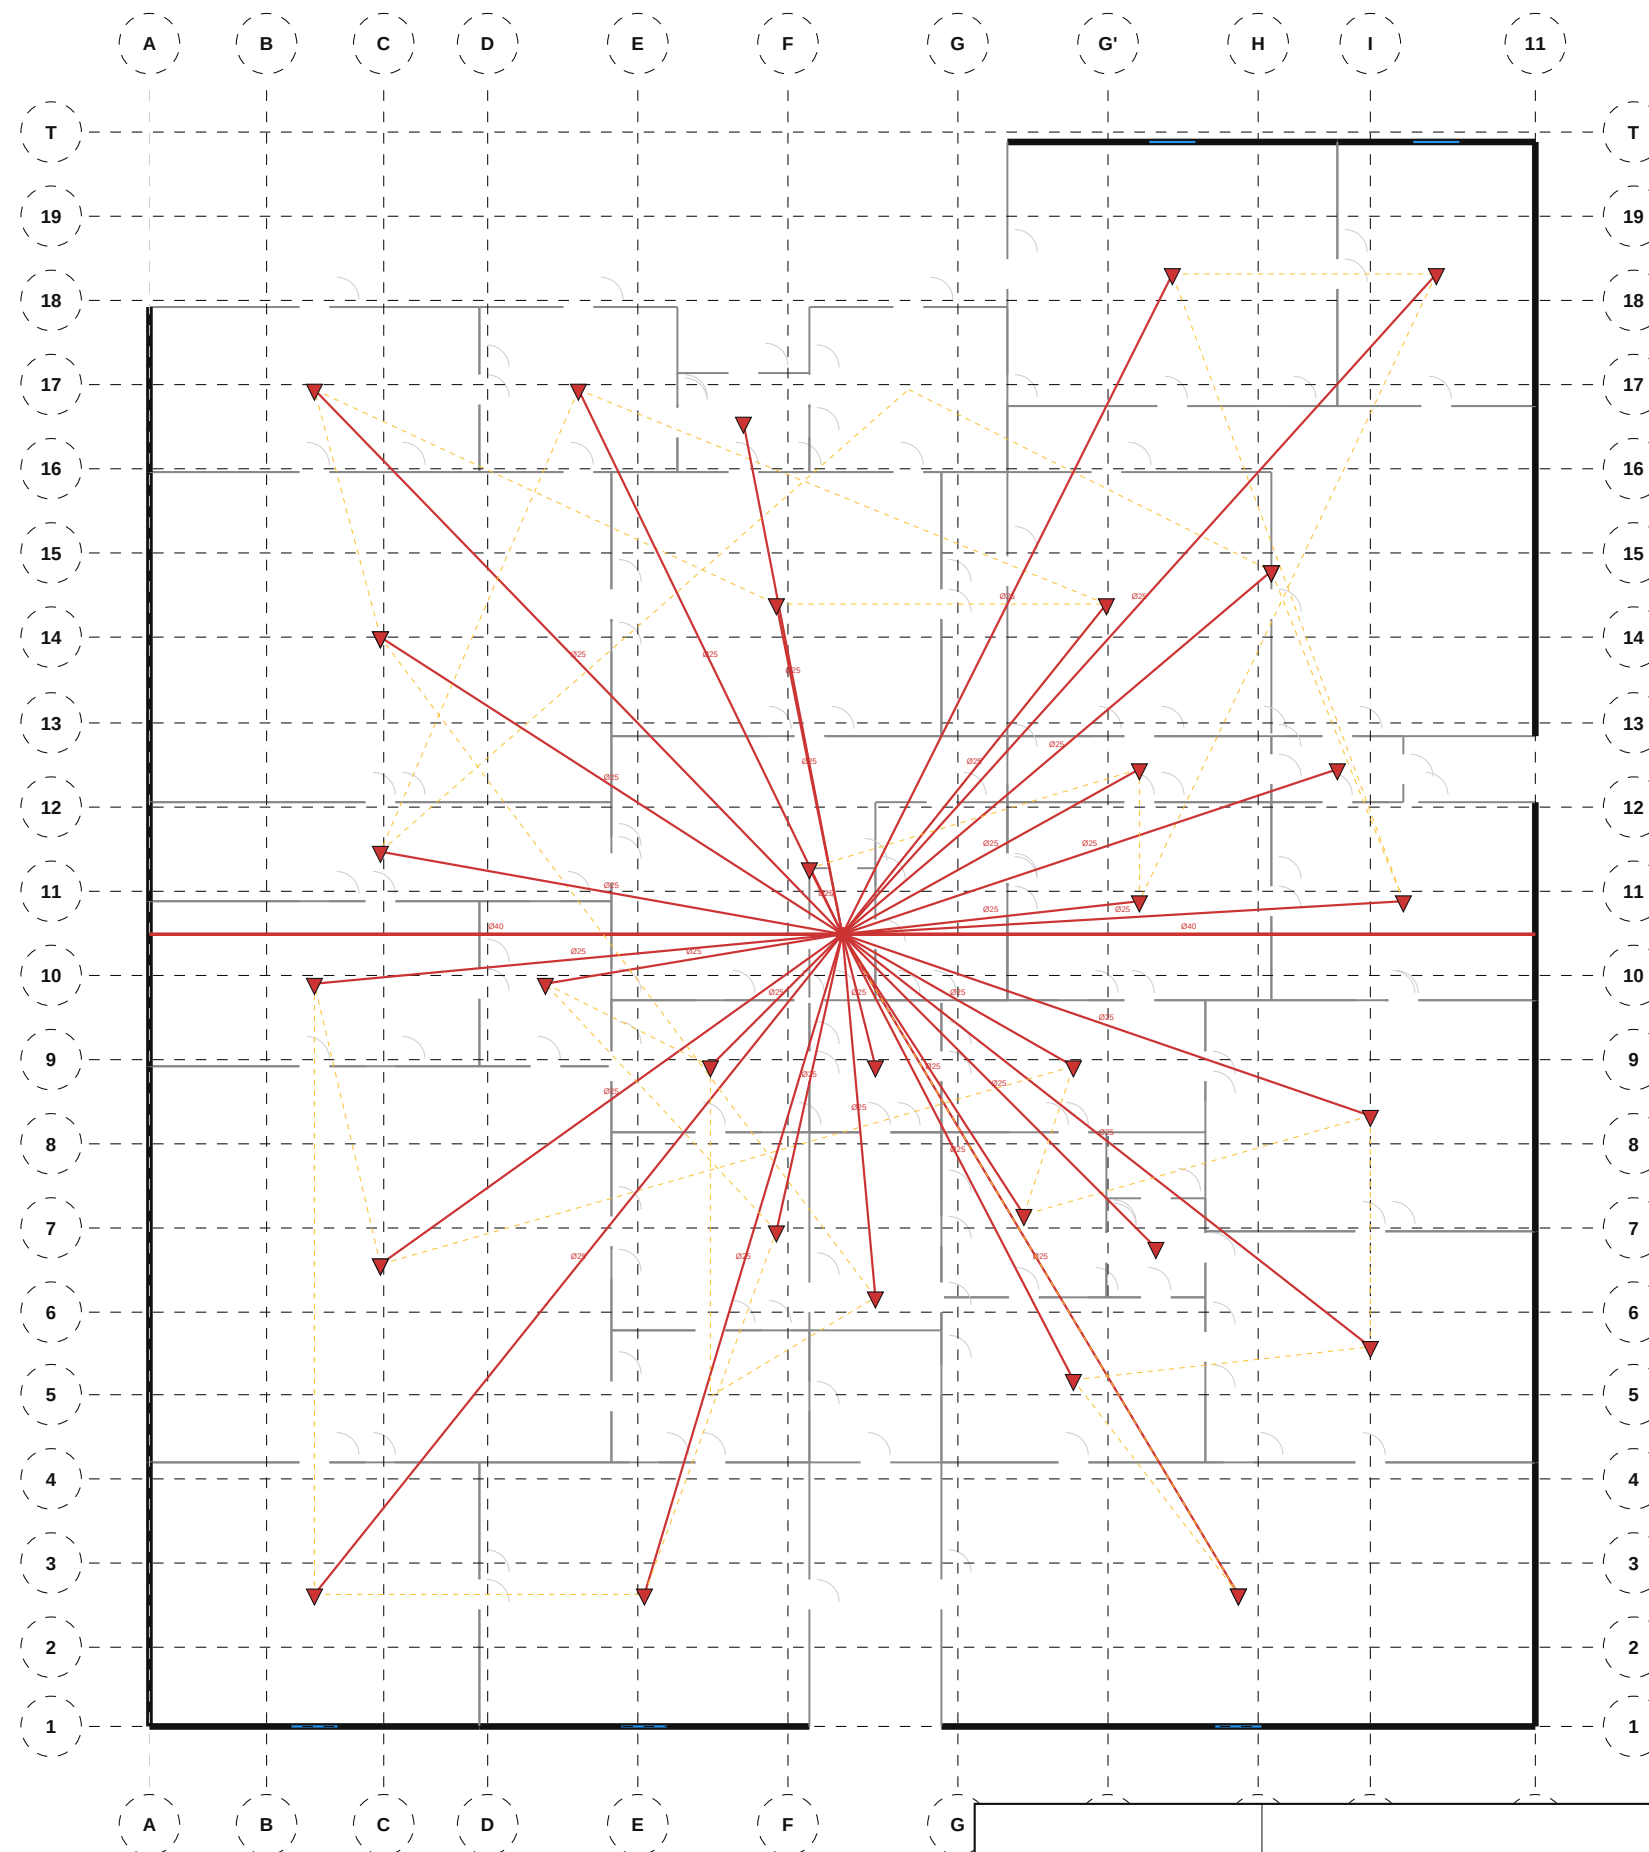

NOMENCLATURE — Sécurité Incendie

- Sprinkler: 35


TIJAN AI Bureau d'Études Automatisé	Résidence Papa Oumar Sakho Dakar, Senegal	Éch: 1/100 Pl. 30/88
	Sécurité Incendie — Étage 6	
Date: 06/05/2026	Réf: 1711	BIM vFIF-030 Phase: APD

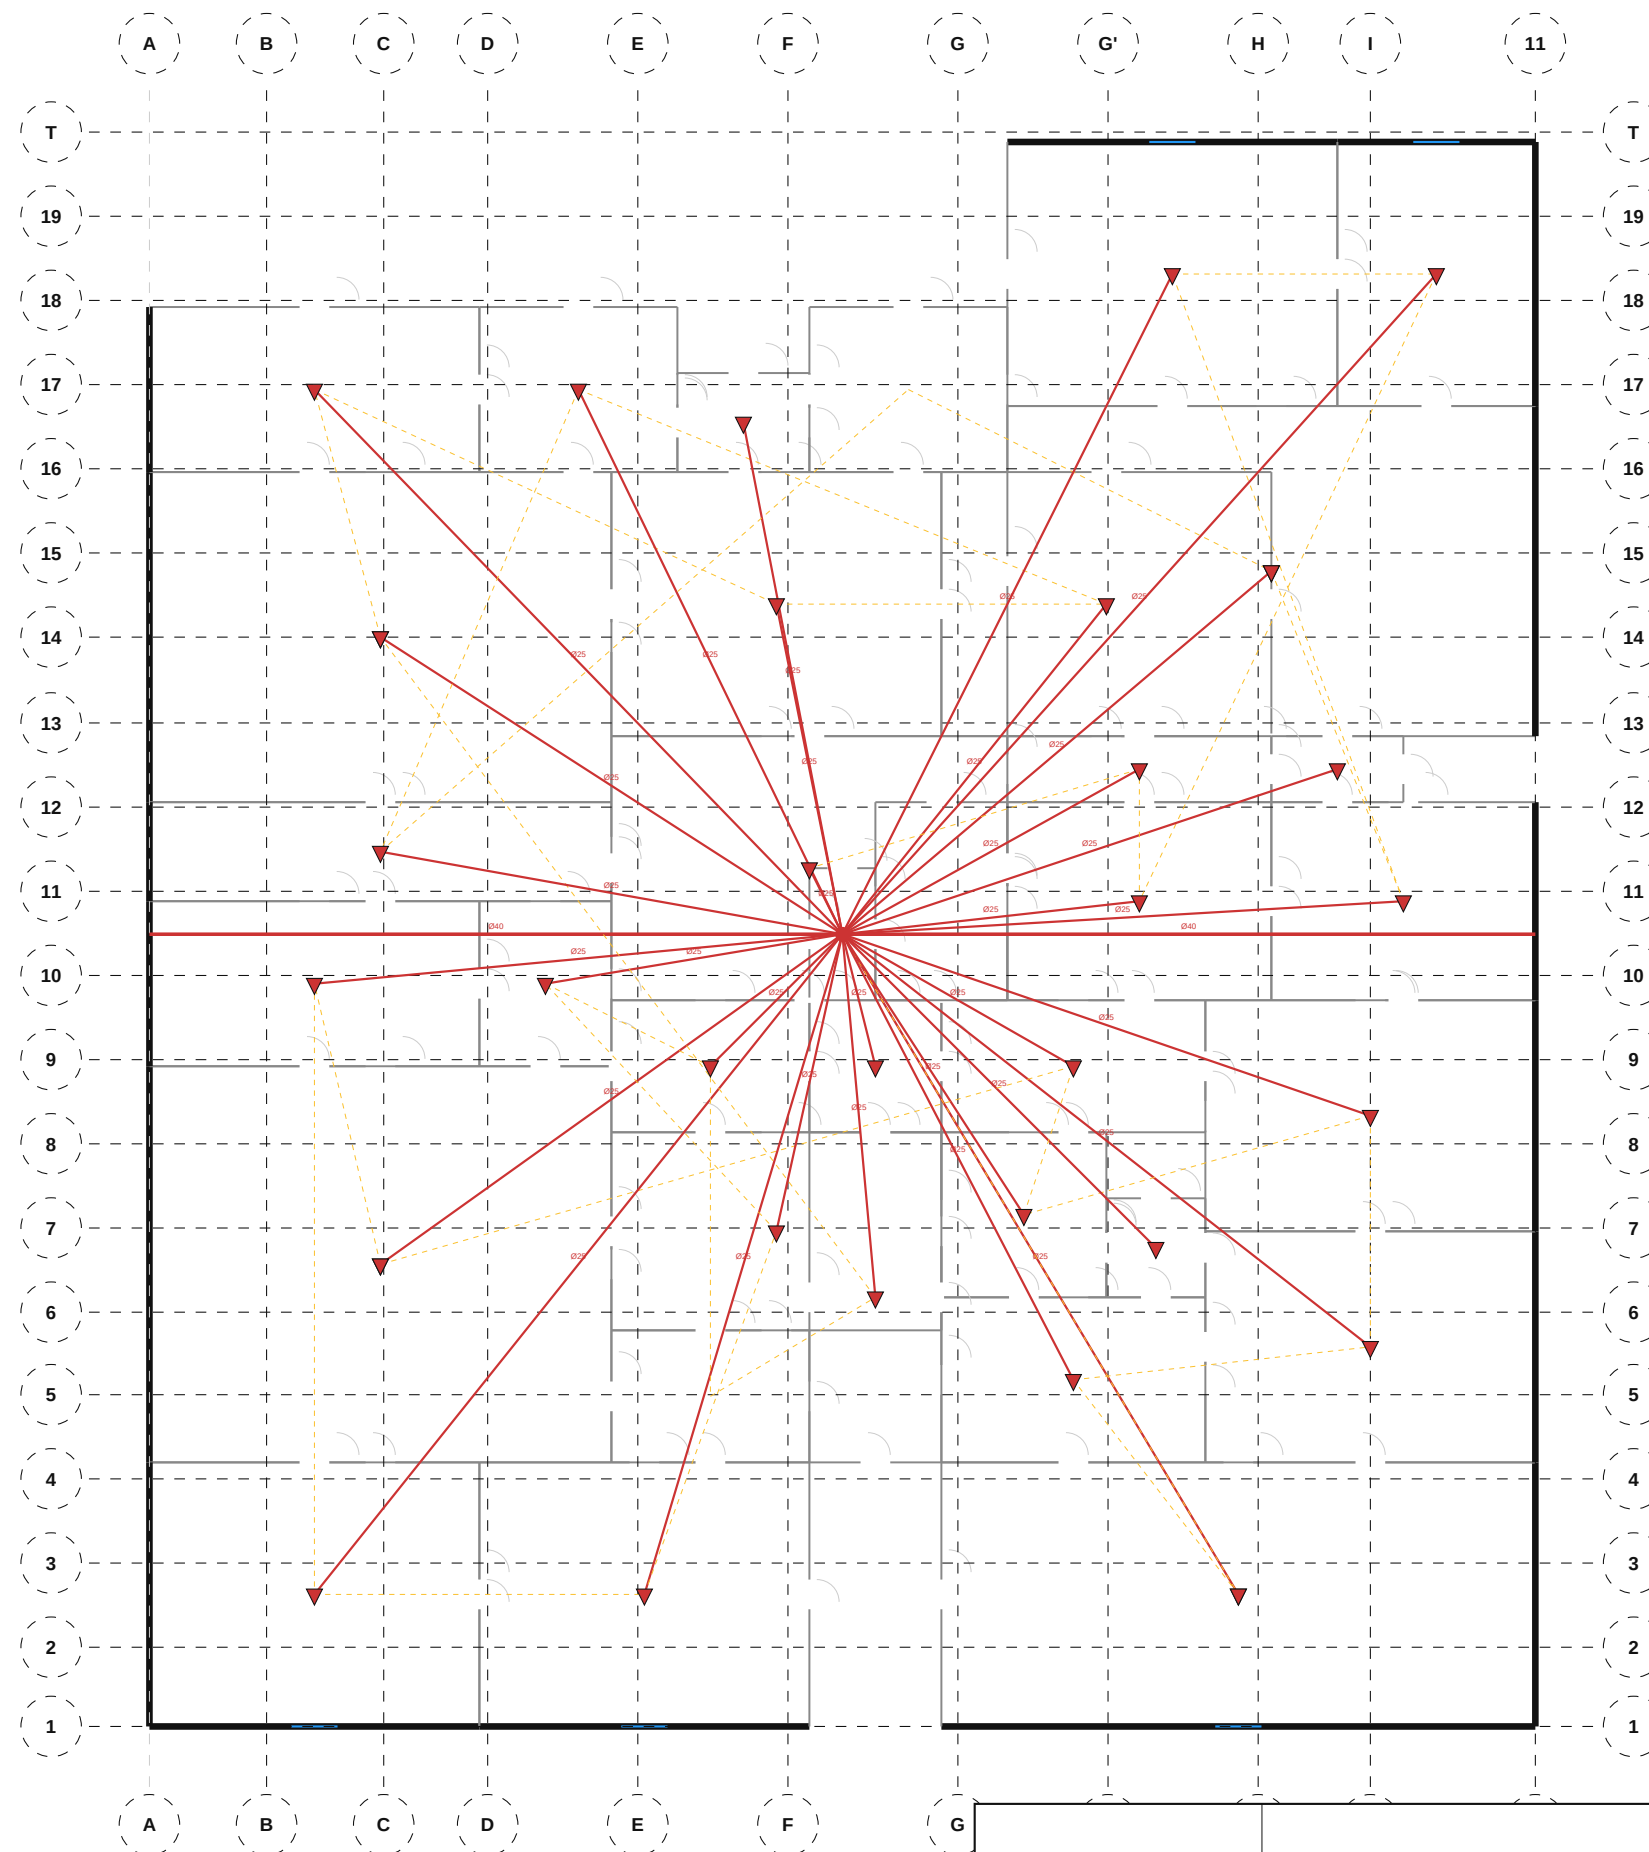

NOMENCLATURE — Sécurité Incendie

- Sprinkler: 35


TIJAN AI Bureau d'Études Automatisé	Résidence Papa Oumar Sakho Dakar, Senegal	Éch: 1/100 Pl. 31/88
	Sécurité Incendie — Étage 7	
Date: 06/05/2026	Réf: 1711	BIM vFIF-031 Phase: APD

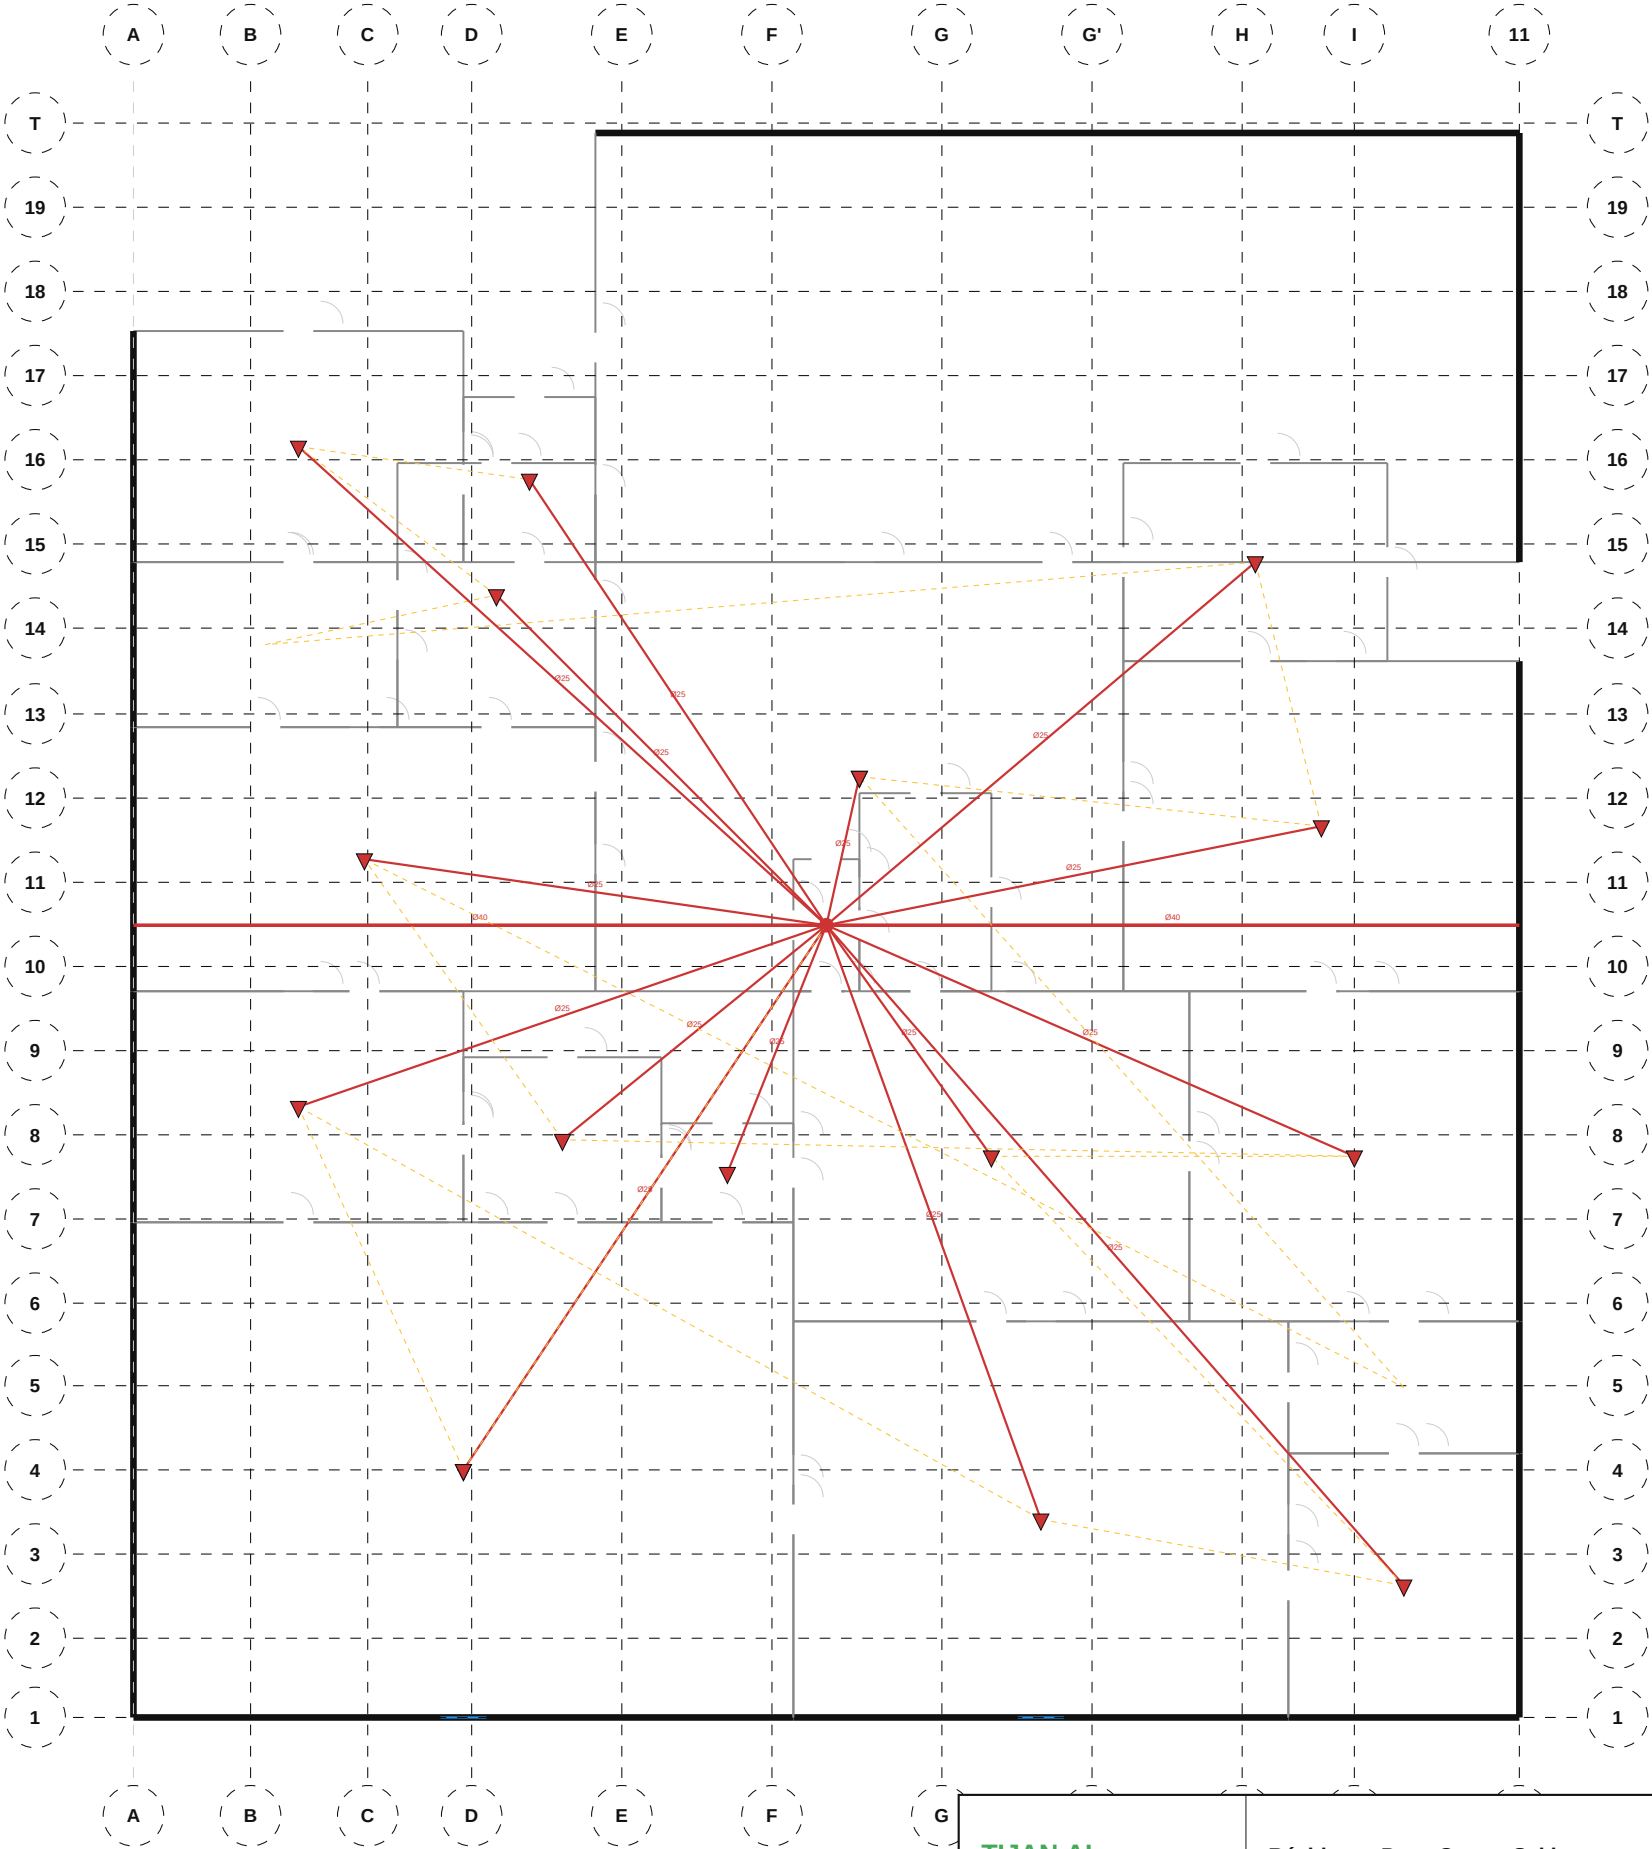


NOMENCLATURE — Sécurité Incendie

• Sprinkler: 17

TIJAN AI Bureau d'Études Automatisé	Résidence Papa Oumar Sakho Dakar, Senegal	Éch: 1/100 Pl. 32/88
	Sécurité Incendie — Étage 8	
Date: 06/05/2026	Réf: 1711	BIM VFIF-032 Phase: APD

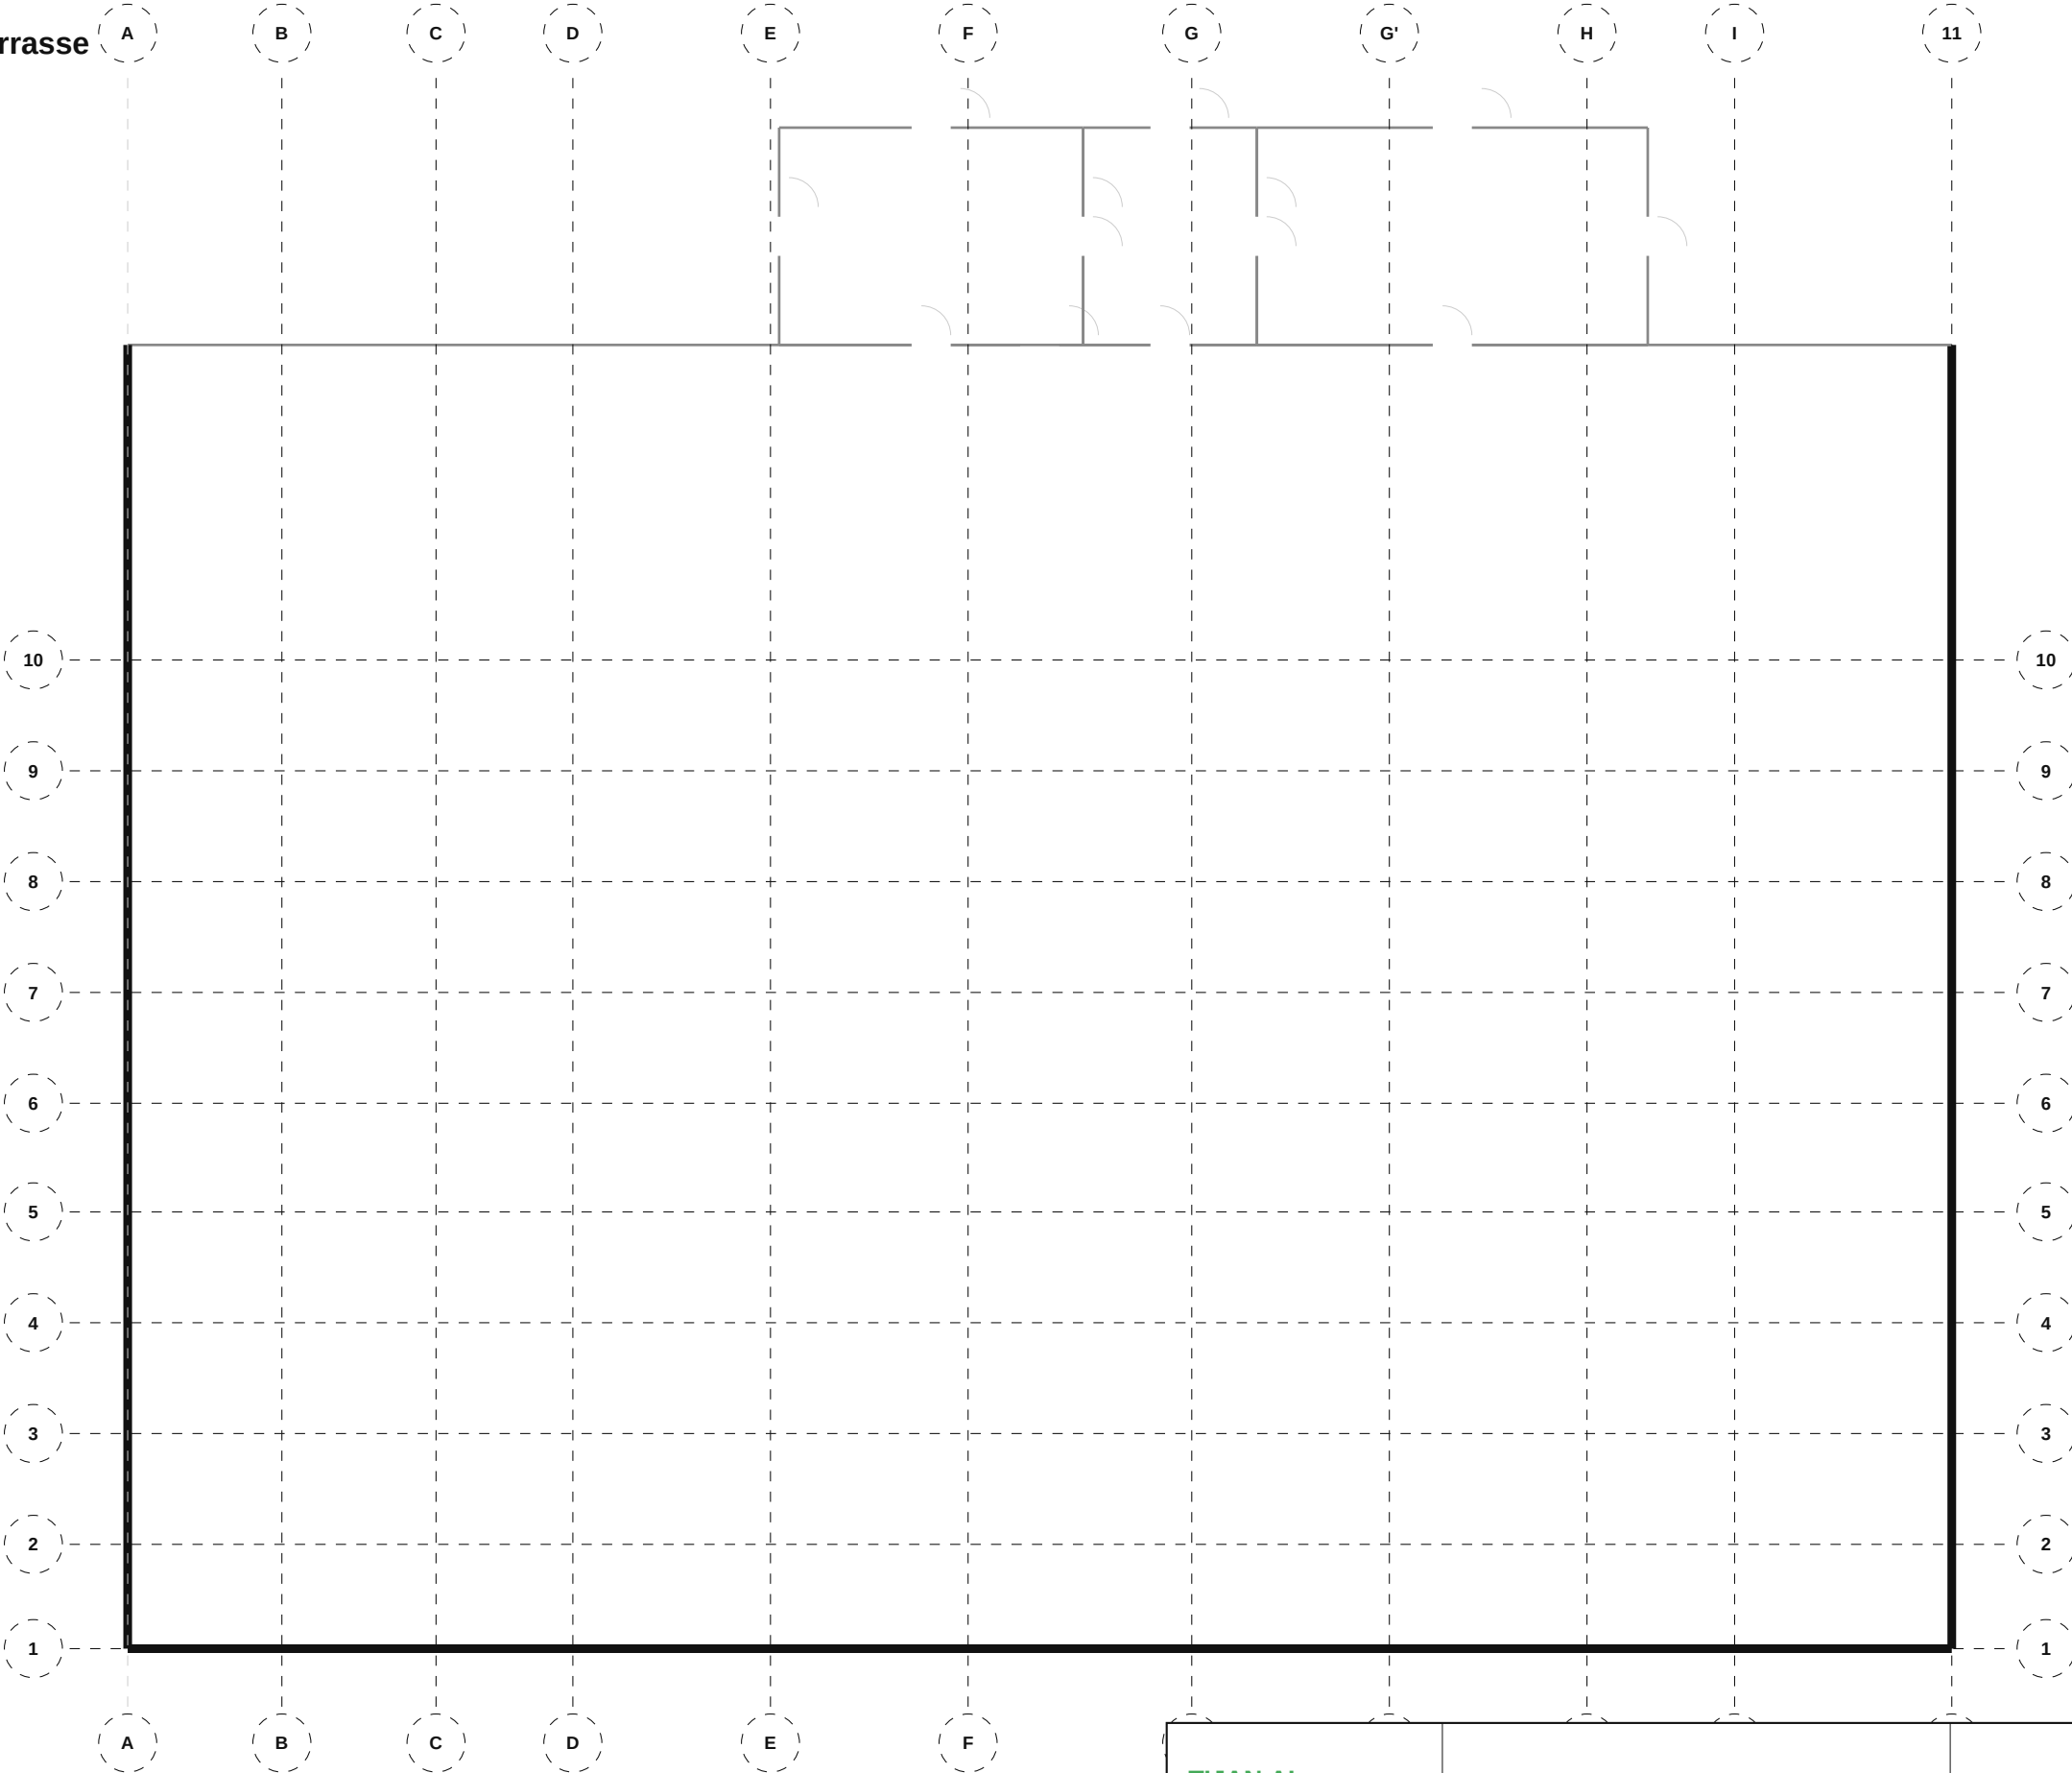

TIJAN AI Bureau d'Études Automatisé	Résidence Papa Oumar Sakho Dakar, Senegal	Éch: 1/100 Pl. 33/88
	Sécurité Incendie — Terrasse	
Date: 06/05/2026	Réf: 1711	BIM VFIF-033 Phase: APD

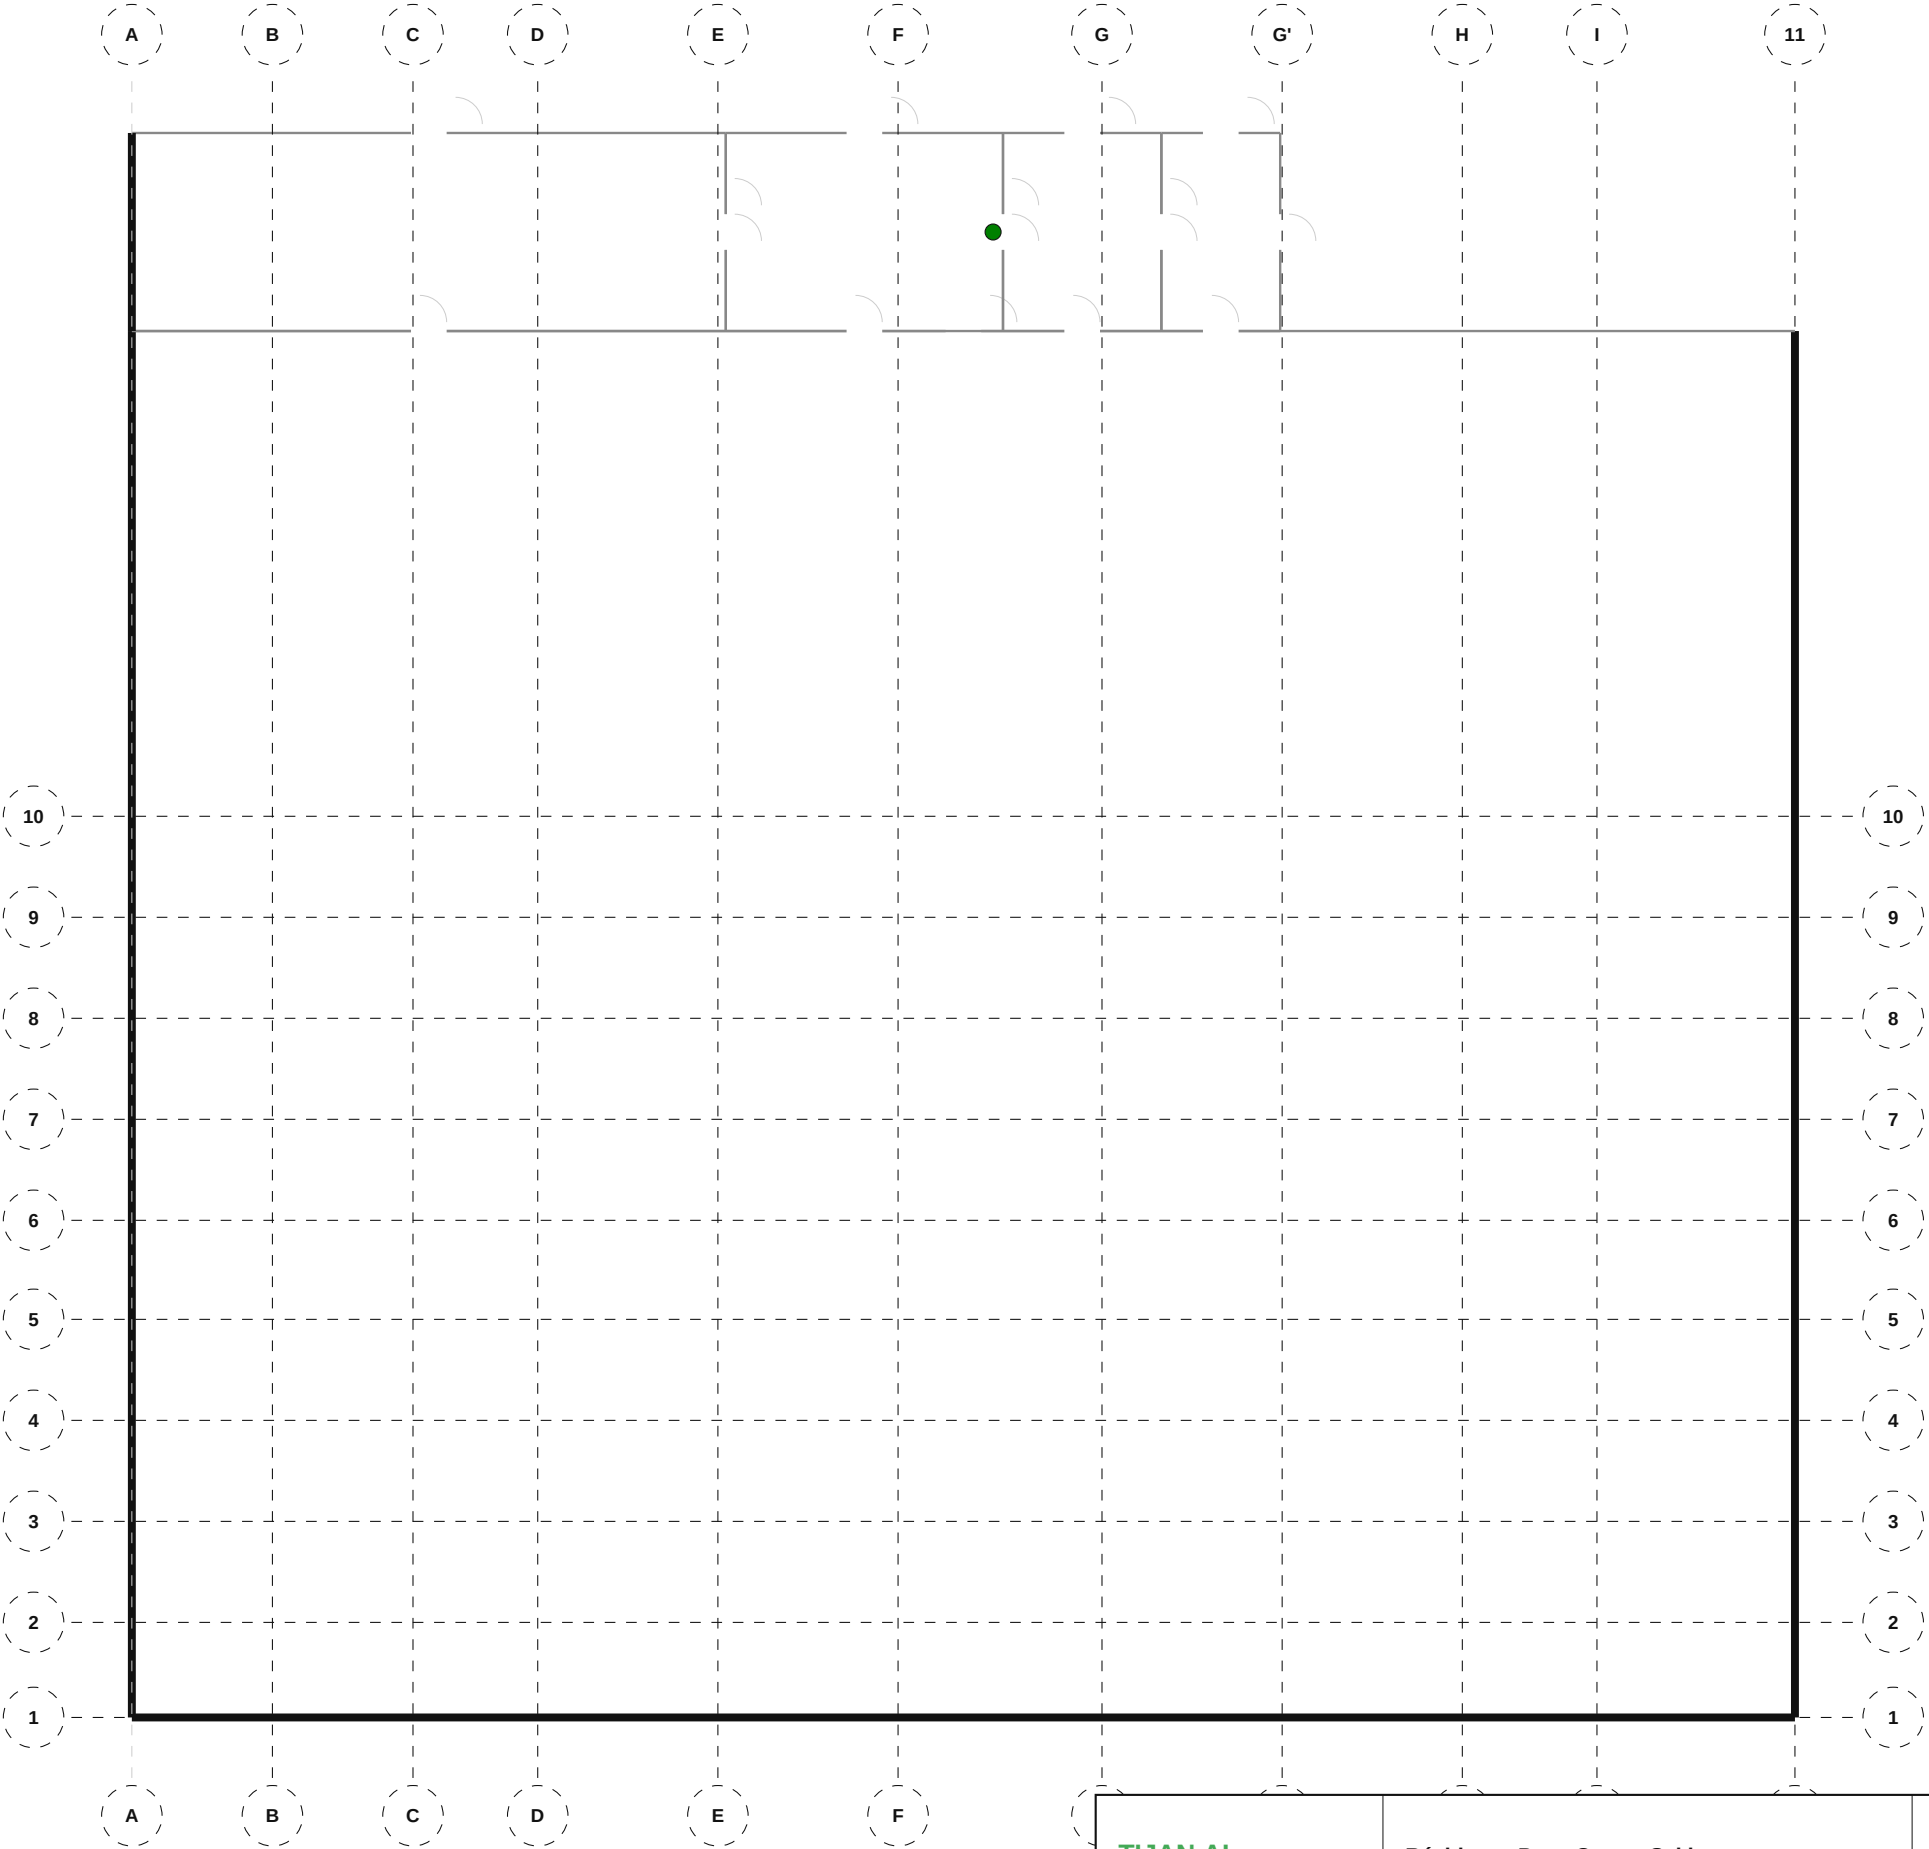

NOMENCLATURE — Plomberie


• Chauffe-eau: 1

TIJAN AI Bureau d'Études Automatisé	Résidence Papa Oumar Sakho Dakar, Senegal	Éch: 1/100 Pl. 34/88
	Plomberie — Sous-Sol	
Date: 06/05/2026	Réf: 1711	BIM vPLU-034 Phase: APD


410 Plomberie — RDC

NOMENCLATURE — Plomberie

- Chauffe-eau: 1
- Douche: 1
- Lavabo: 1
- Lave-mains: 1
- Lave-vaisselle: 1
- WC suspendu: 2
- Évier cuisine: 1

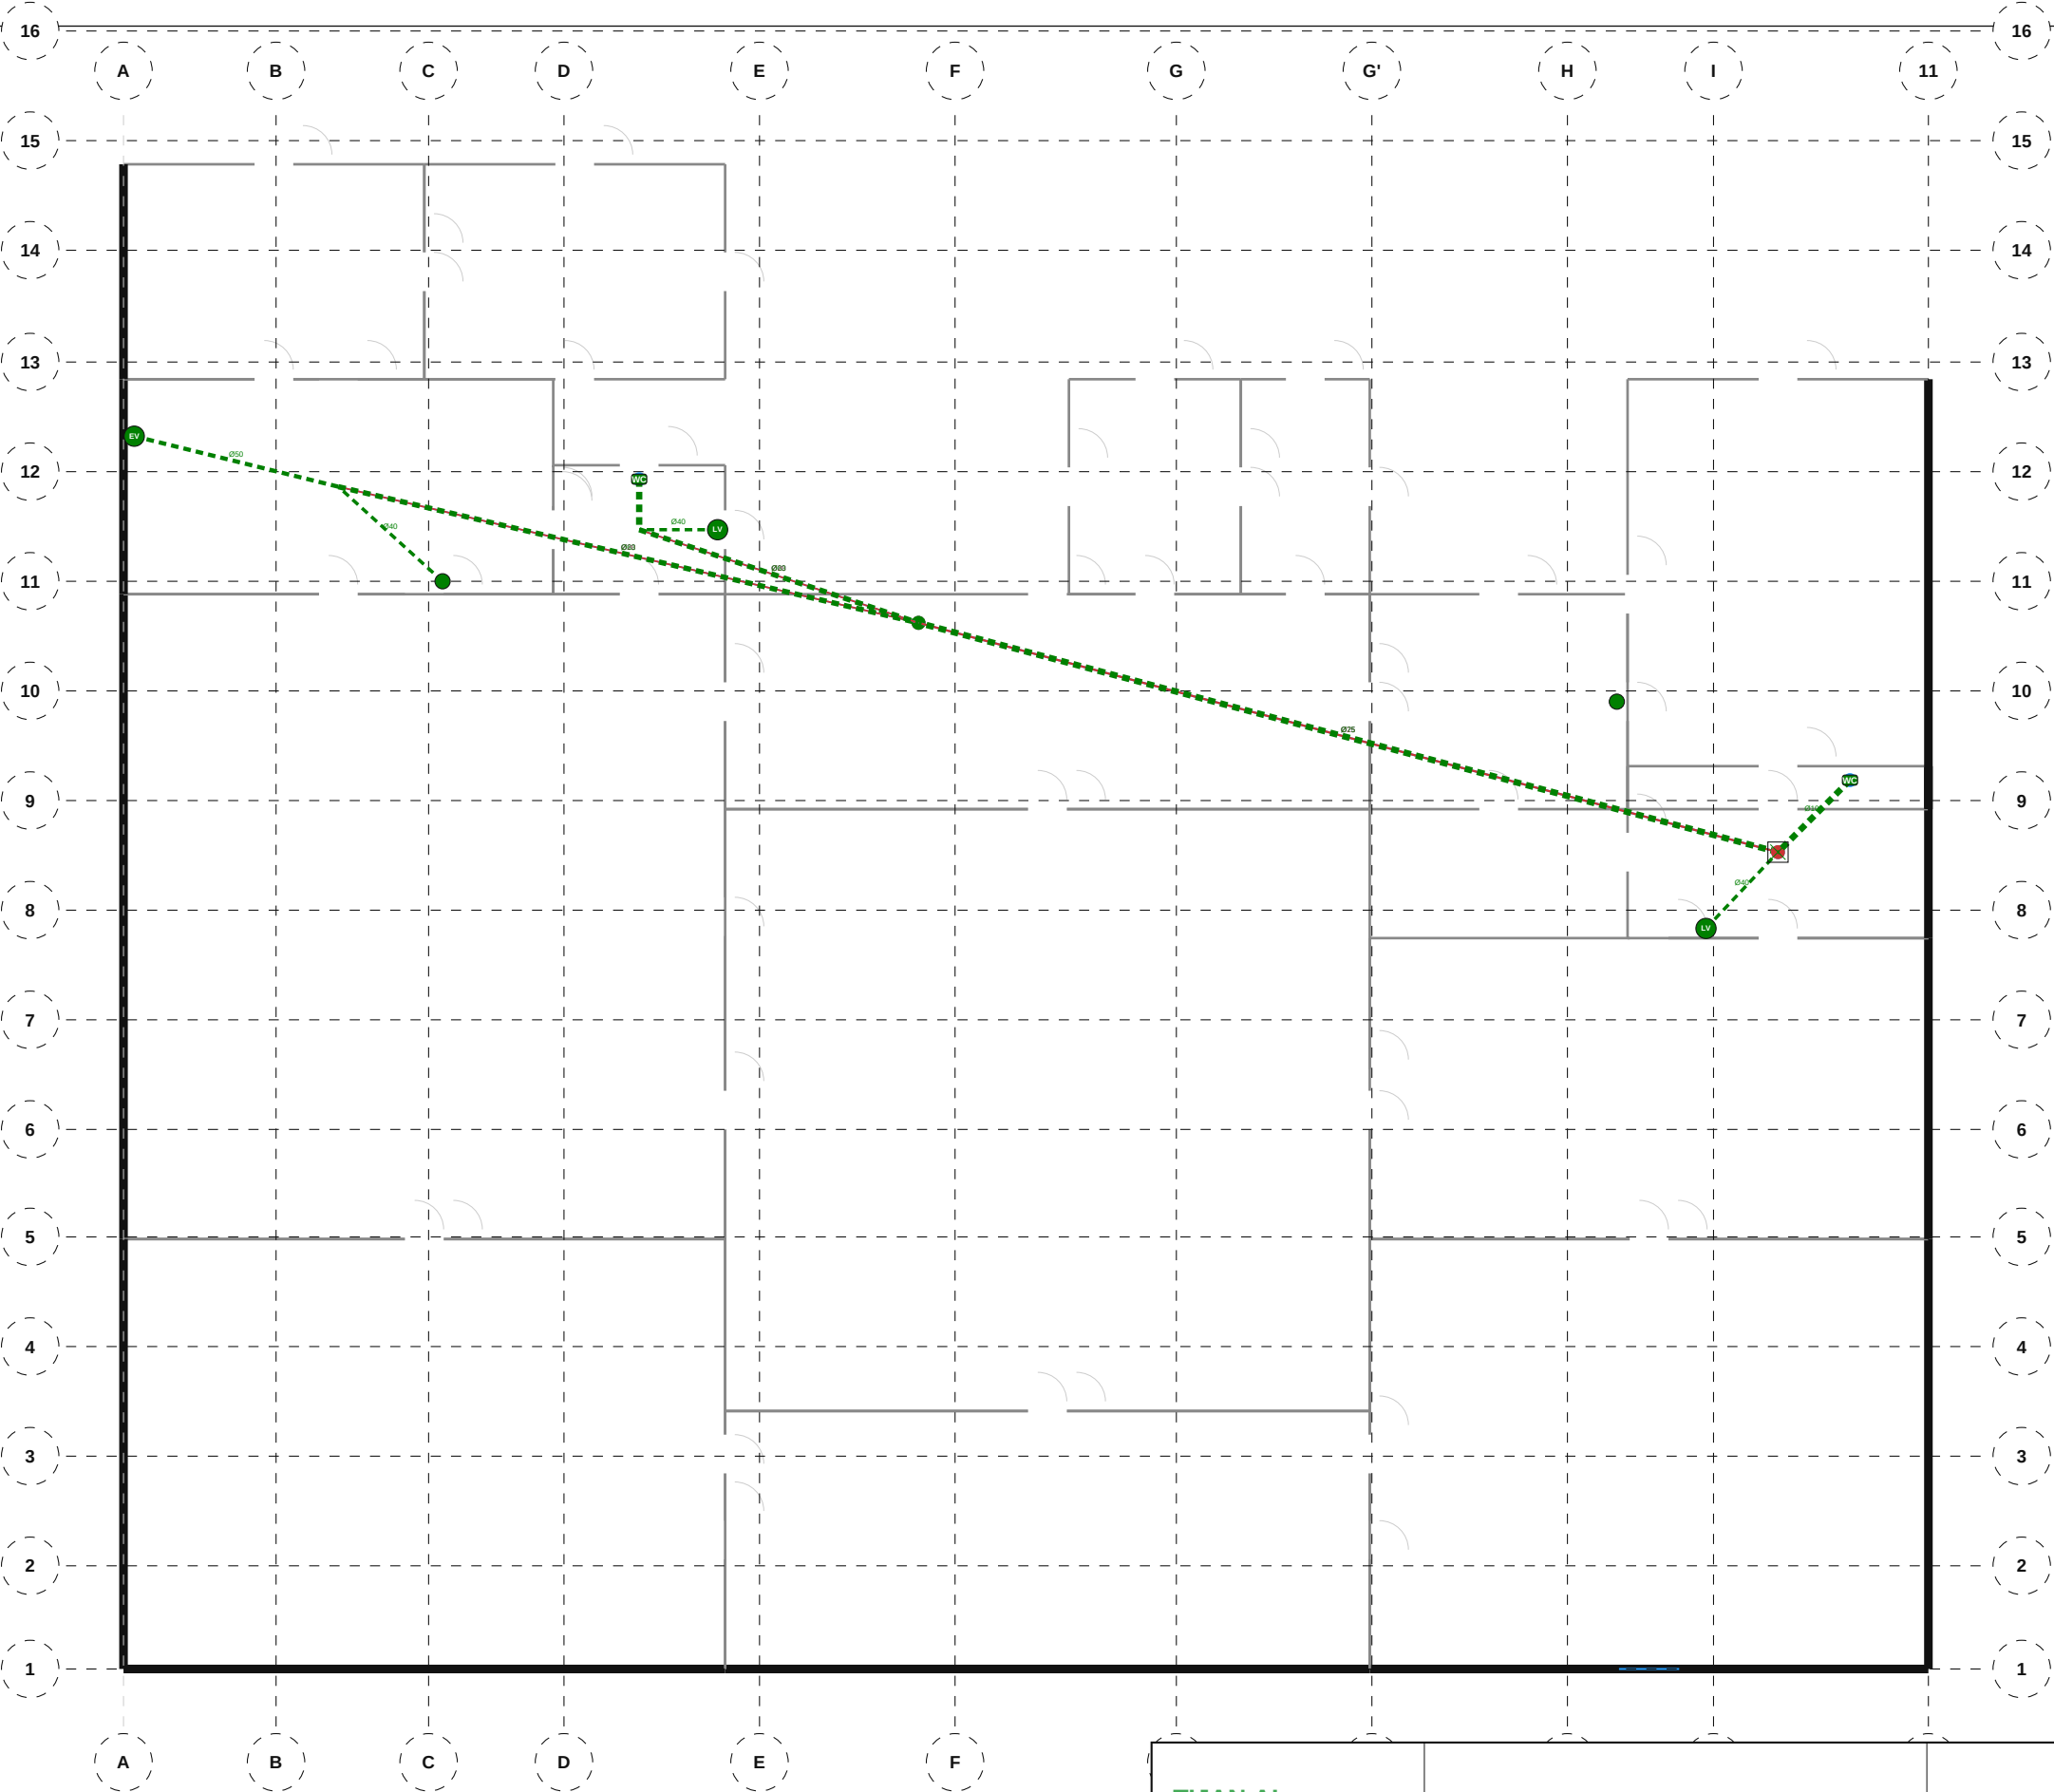


TIJAN AI Bureau d'Études Automatisé	Résidence Papa Oumar Sakho Dakar, Senegal	Éch: 1/100 Pl. 35/88
	Plomberie — RDC	
Date: 06/05/2026	Réf: 1711	BIM VPLU-035 Phase: APD

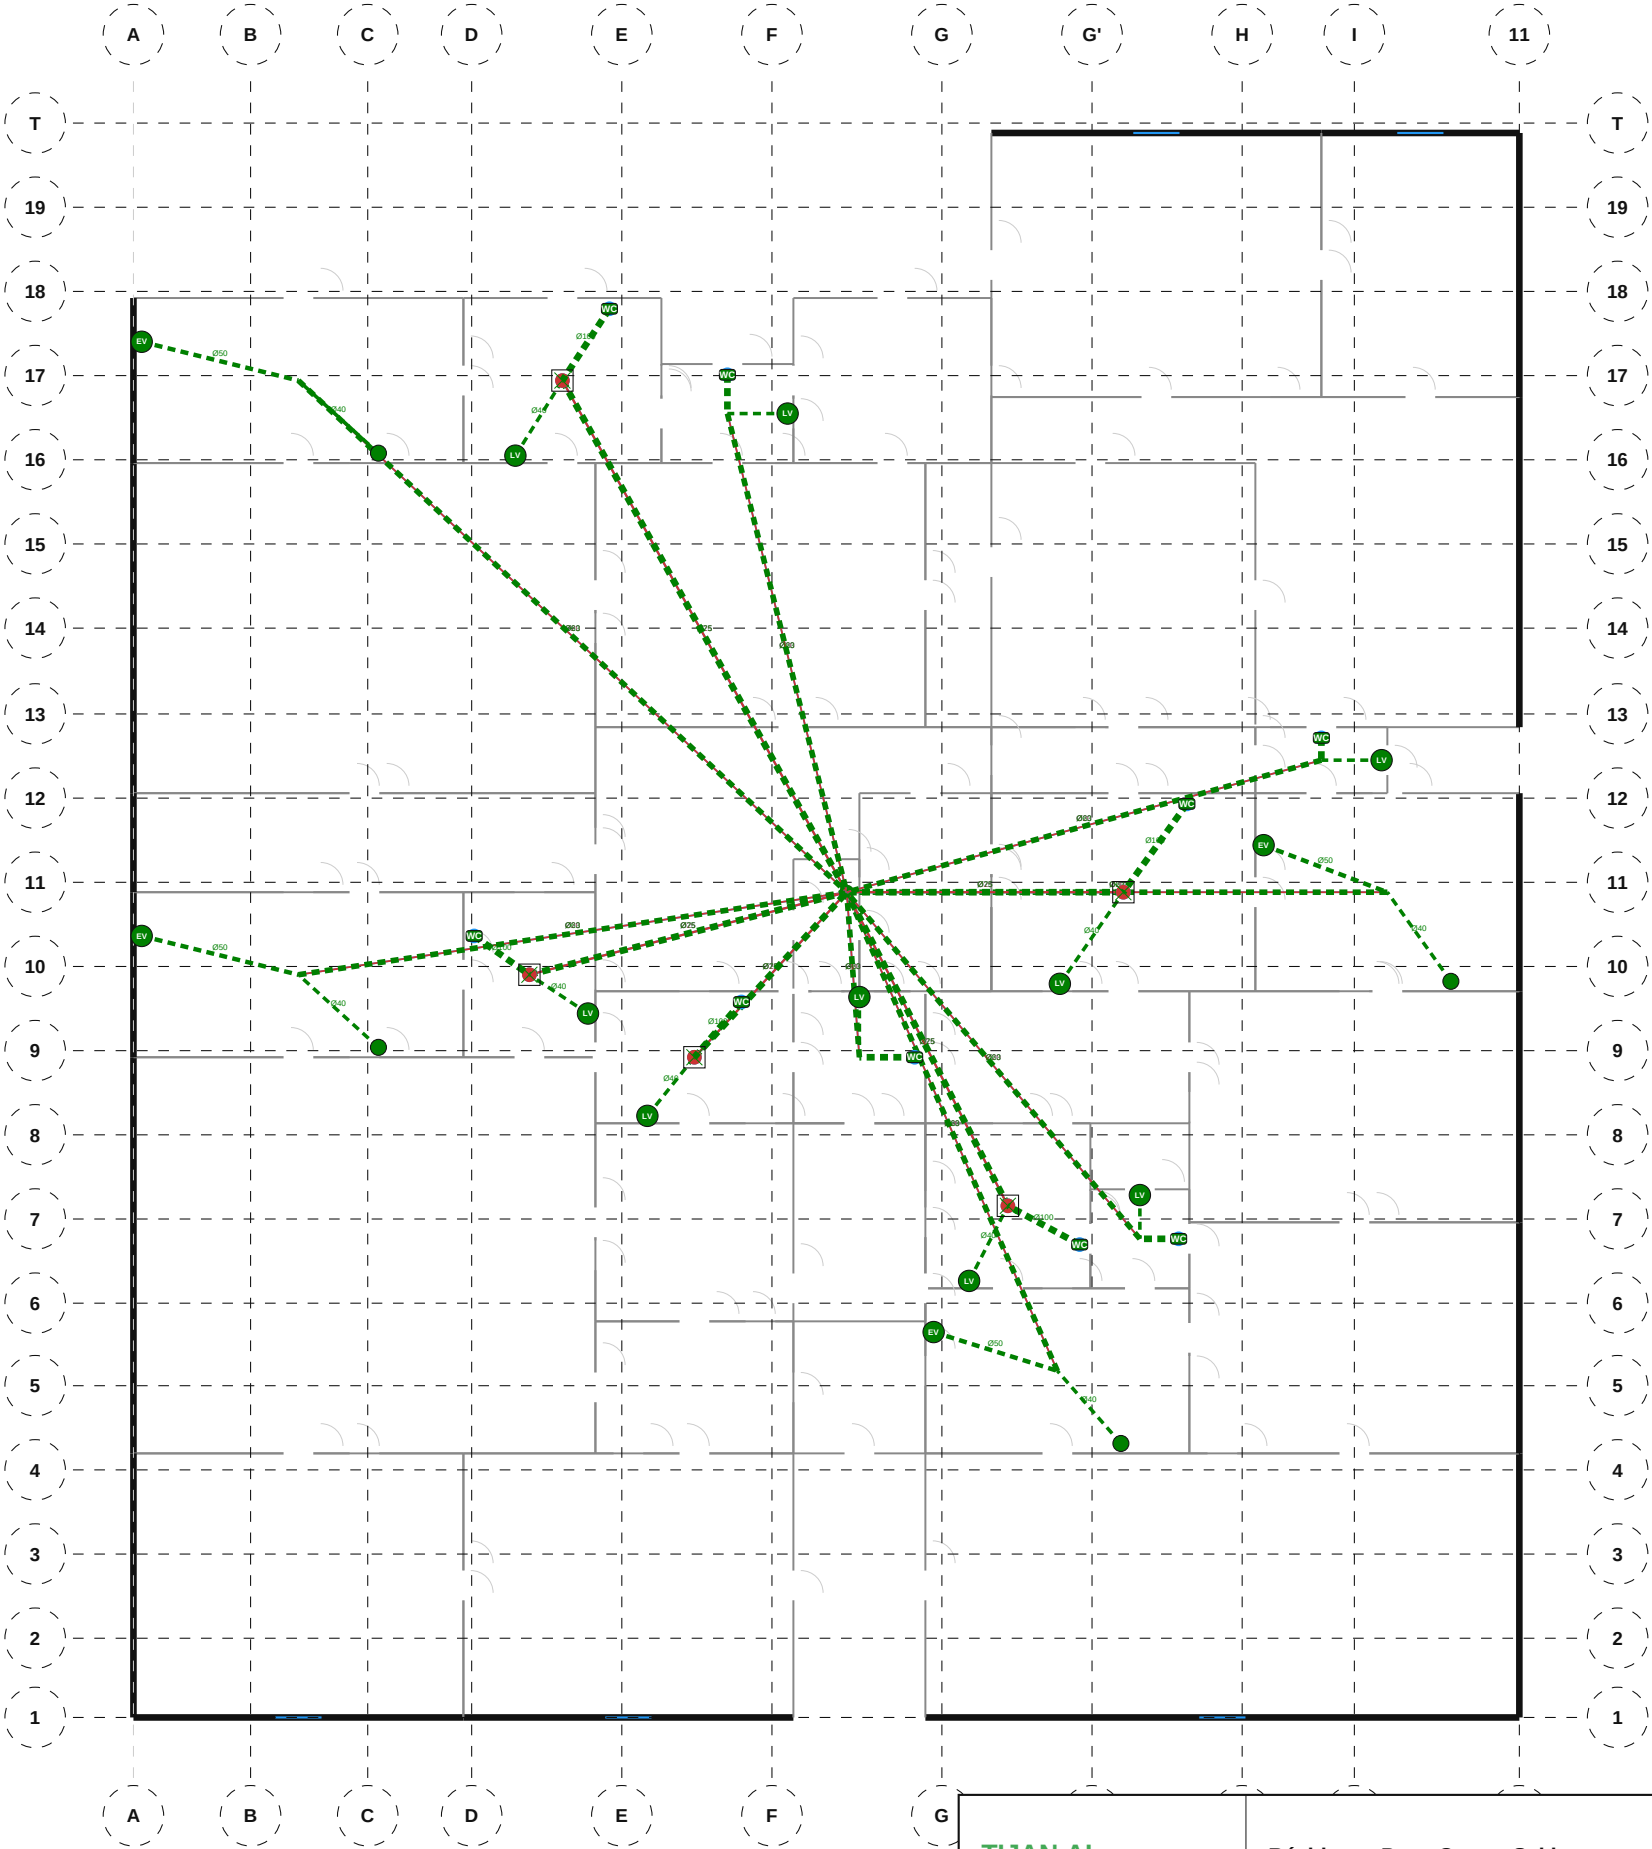

NOMENCLATURE — Plomberie

- Douche: 5
- Lavabo: 5
- Lave-mains: 4
- Lave-vaisselle: 4
- WC suspendu: 9
- Évier cuisine: 4


TIJAN AI Bureau d'Études Automatisé	Résidence Papa Oumar Sakho Dakar, Senegal	Éch: 1/100 Pl. 36/88
	Plomberie — Étage 1	
Date: 06/05/2026	Réf: 1711	BIM vPLU-036 Phase: APD

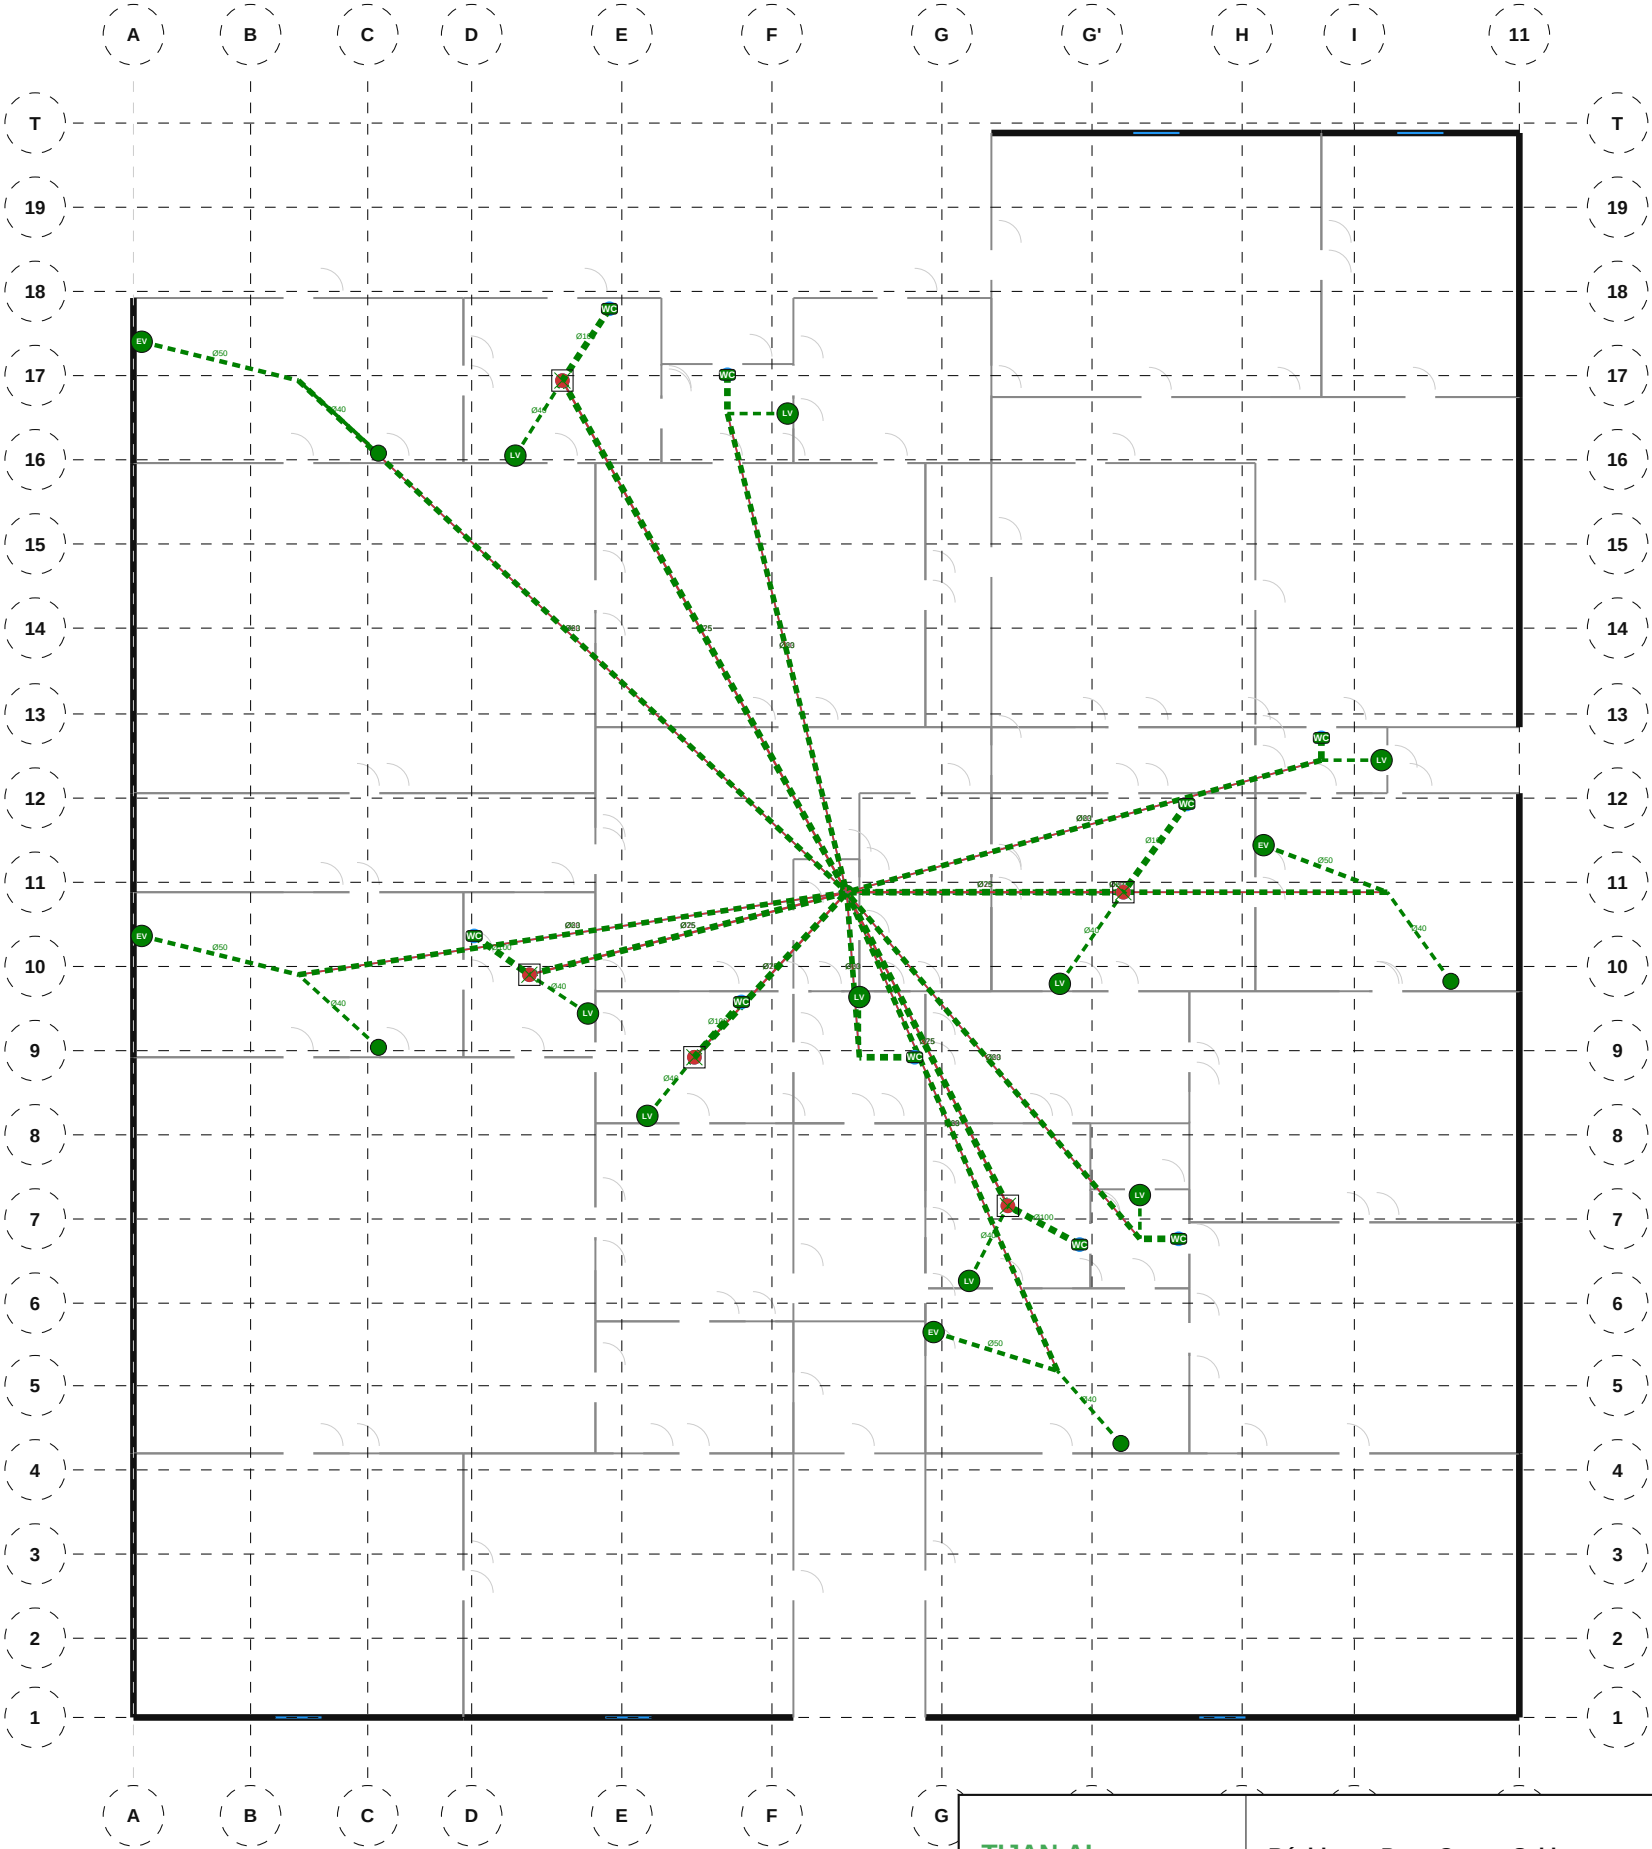

NOMENCLATURE — Plomberie

- Douche: 5
- Lavabo: 5
- Lave-mains: 4
- Lave-vaisselle: 4
- WC suspendu: 9
- Évier cuisine: 4


TIJAN AI Bureau d'Études Automatisé	Résidence Papa Oumar Sakho Dakar, Senegal	Éch: 1/100 Pl. 37/88
	Plomberie — Étage 2	
Date: 06/05/2026	Réf: 1711	BIM vPLU-037 Phase: APD

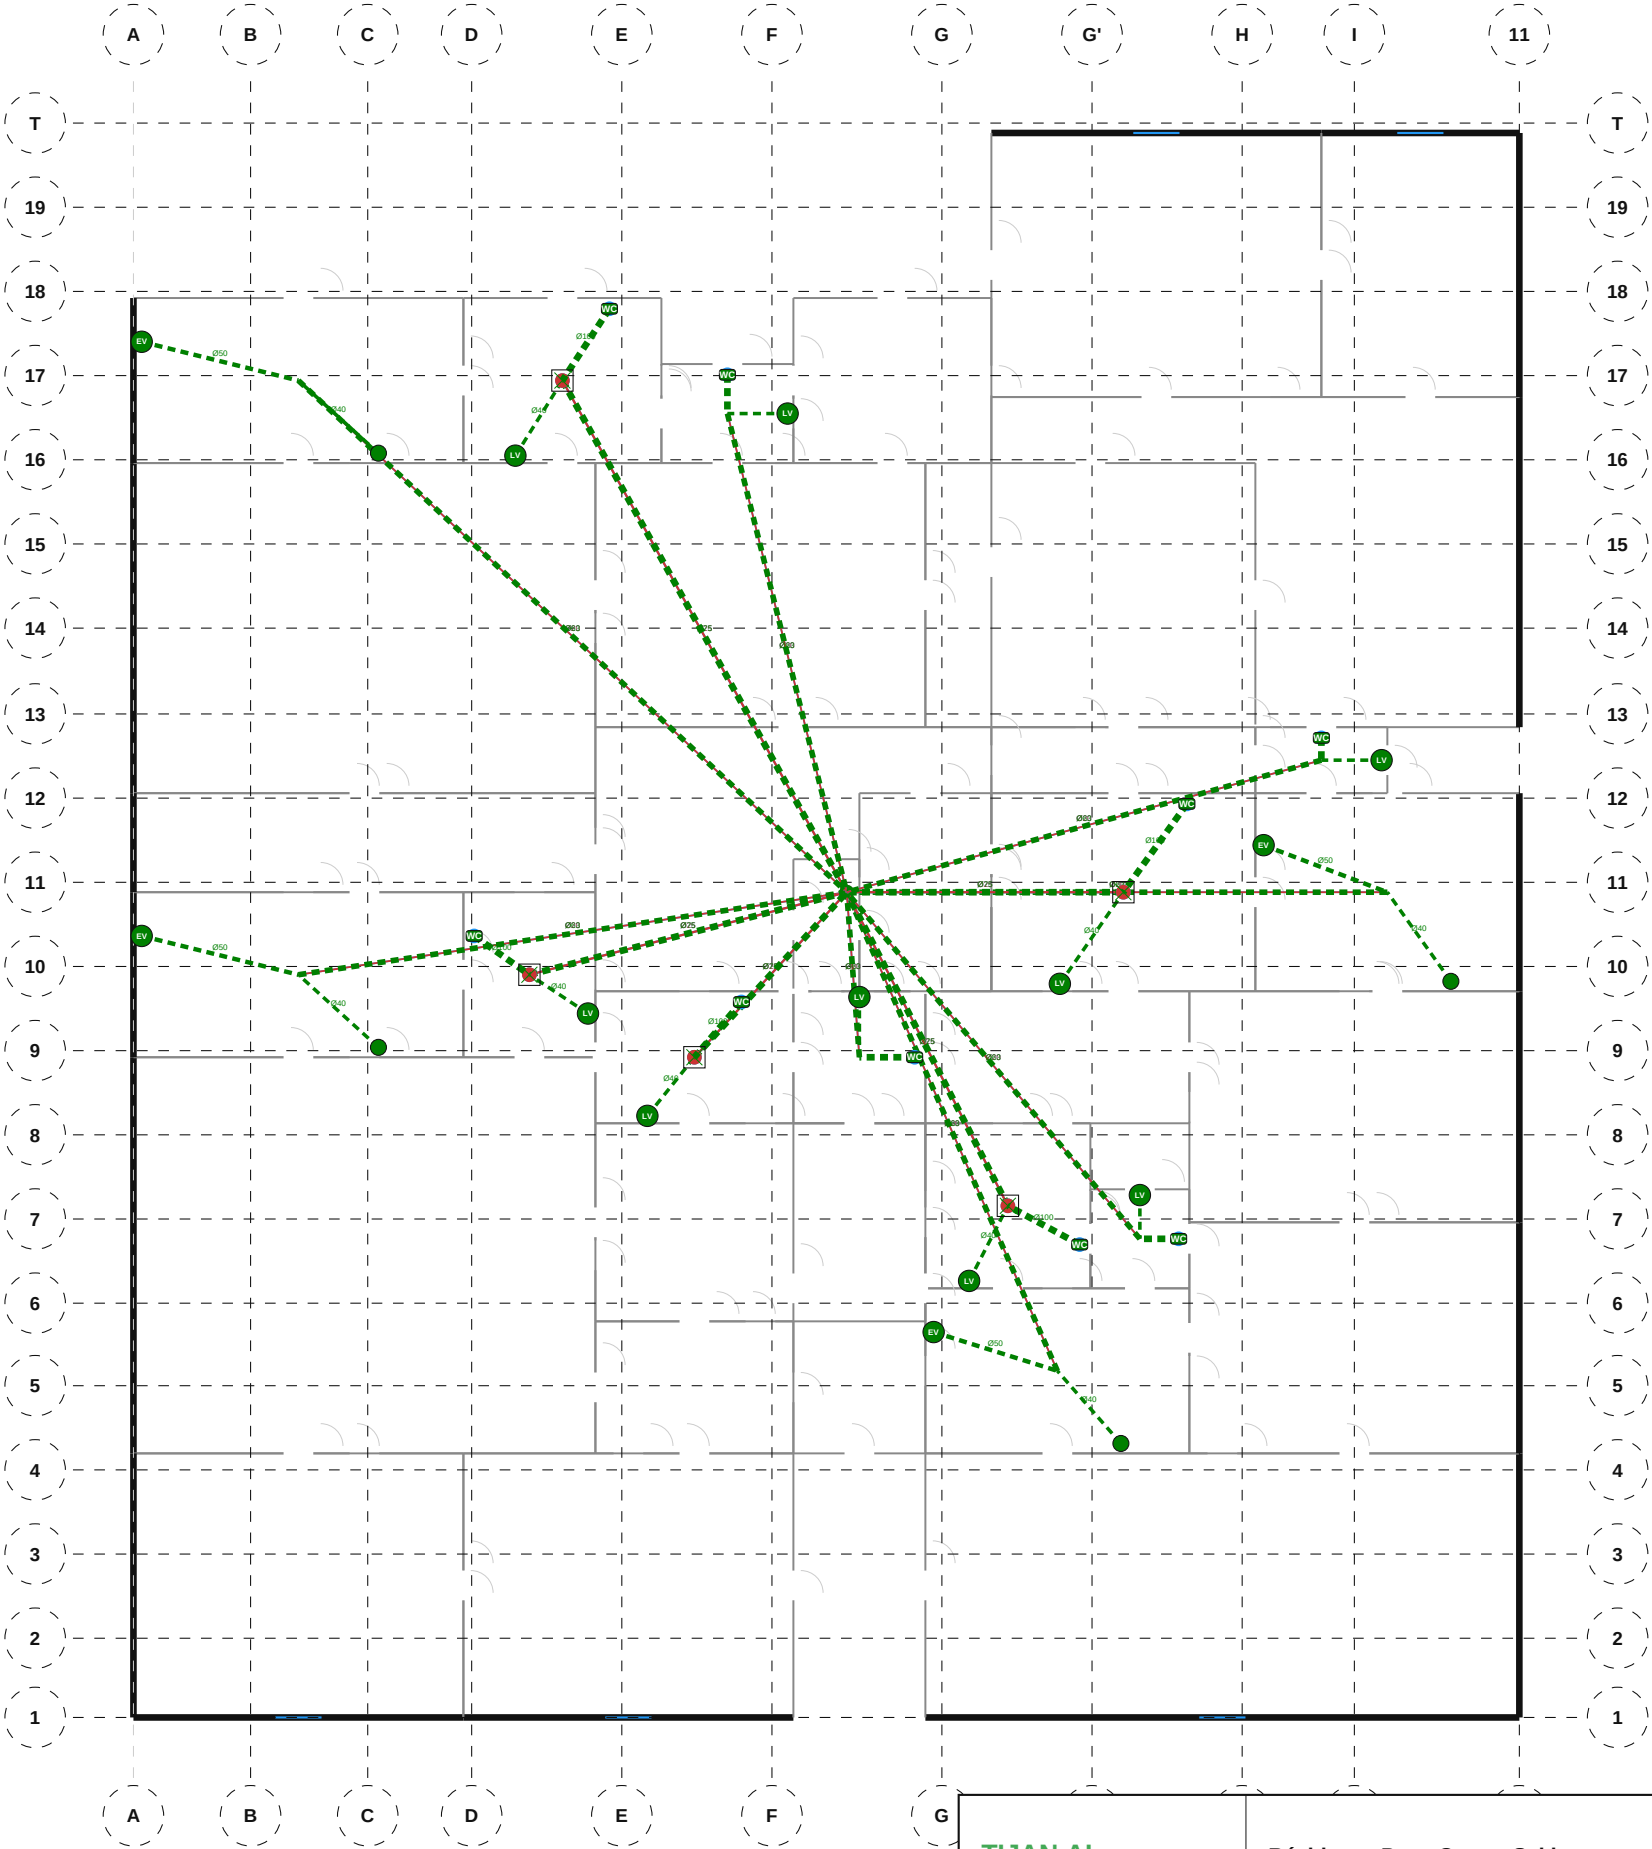

NOMENCLATURE — Plomberie

- Douche: 5
- Lavabo: 5
- Lave-mains: 4
- Lave-vaisselle: 4
- WC suspendu: 9
- Évier cuisine: 4


TIJAN AI Bureau d'Études Automatisé	Résidence Papa Oumar Sakho Dakar, Senegal	Éch: 1/100 Pl. 38/88
	Plomberie — Étage 3	
Date: 06/05/2026	Réf: 1711	BIM vPLU-038 Phase: APD

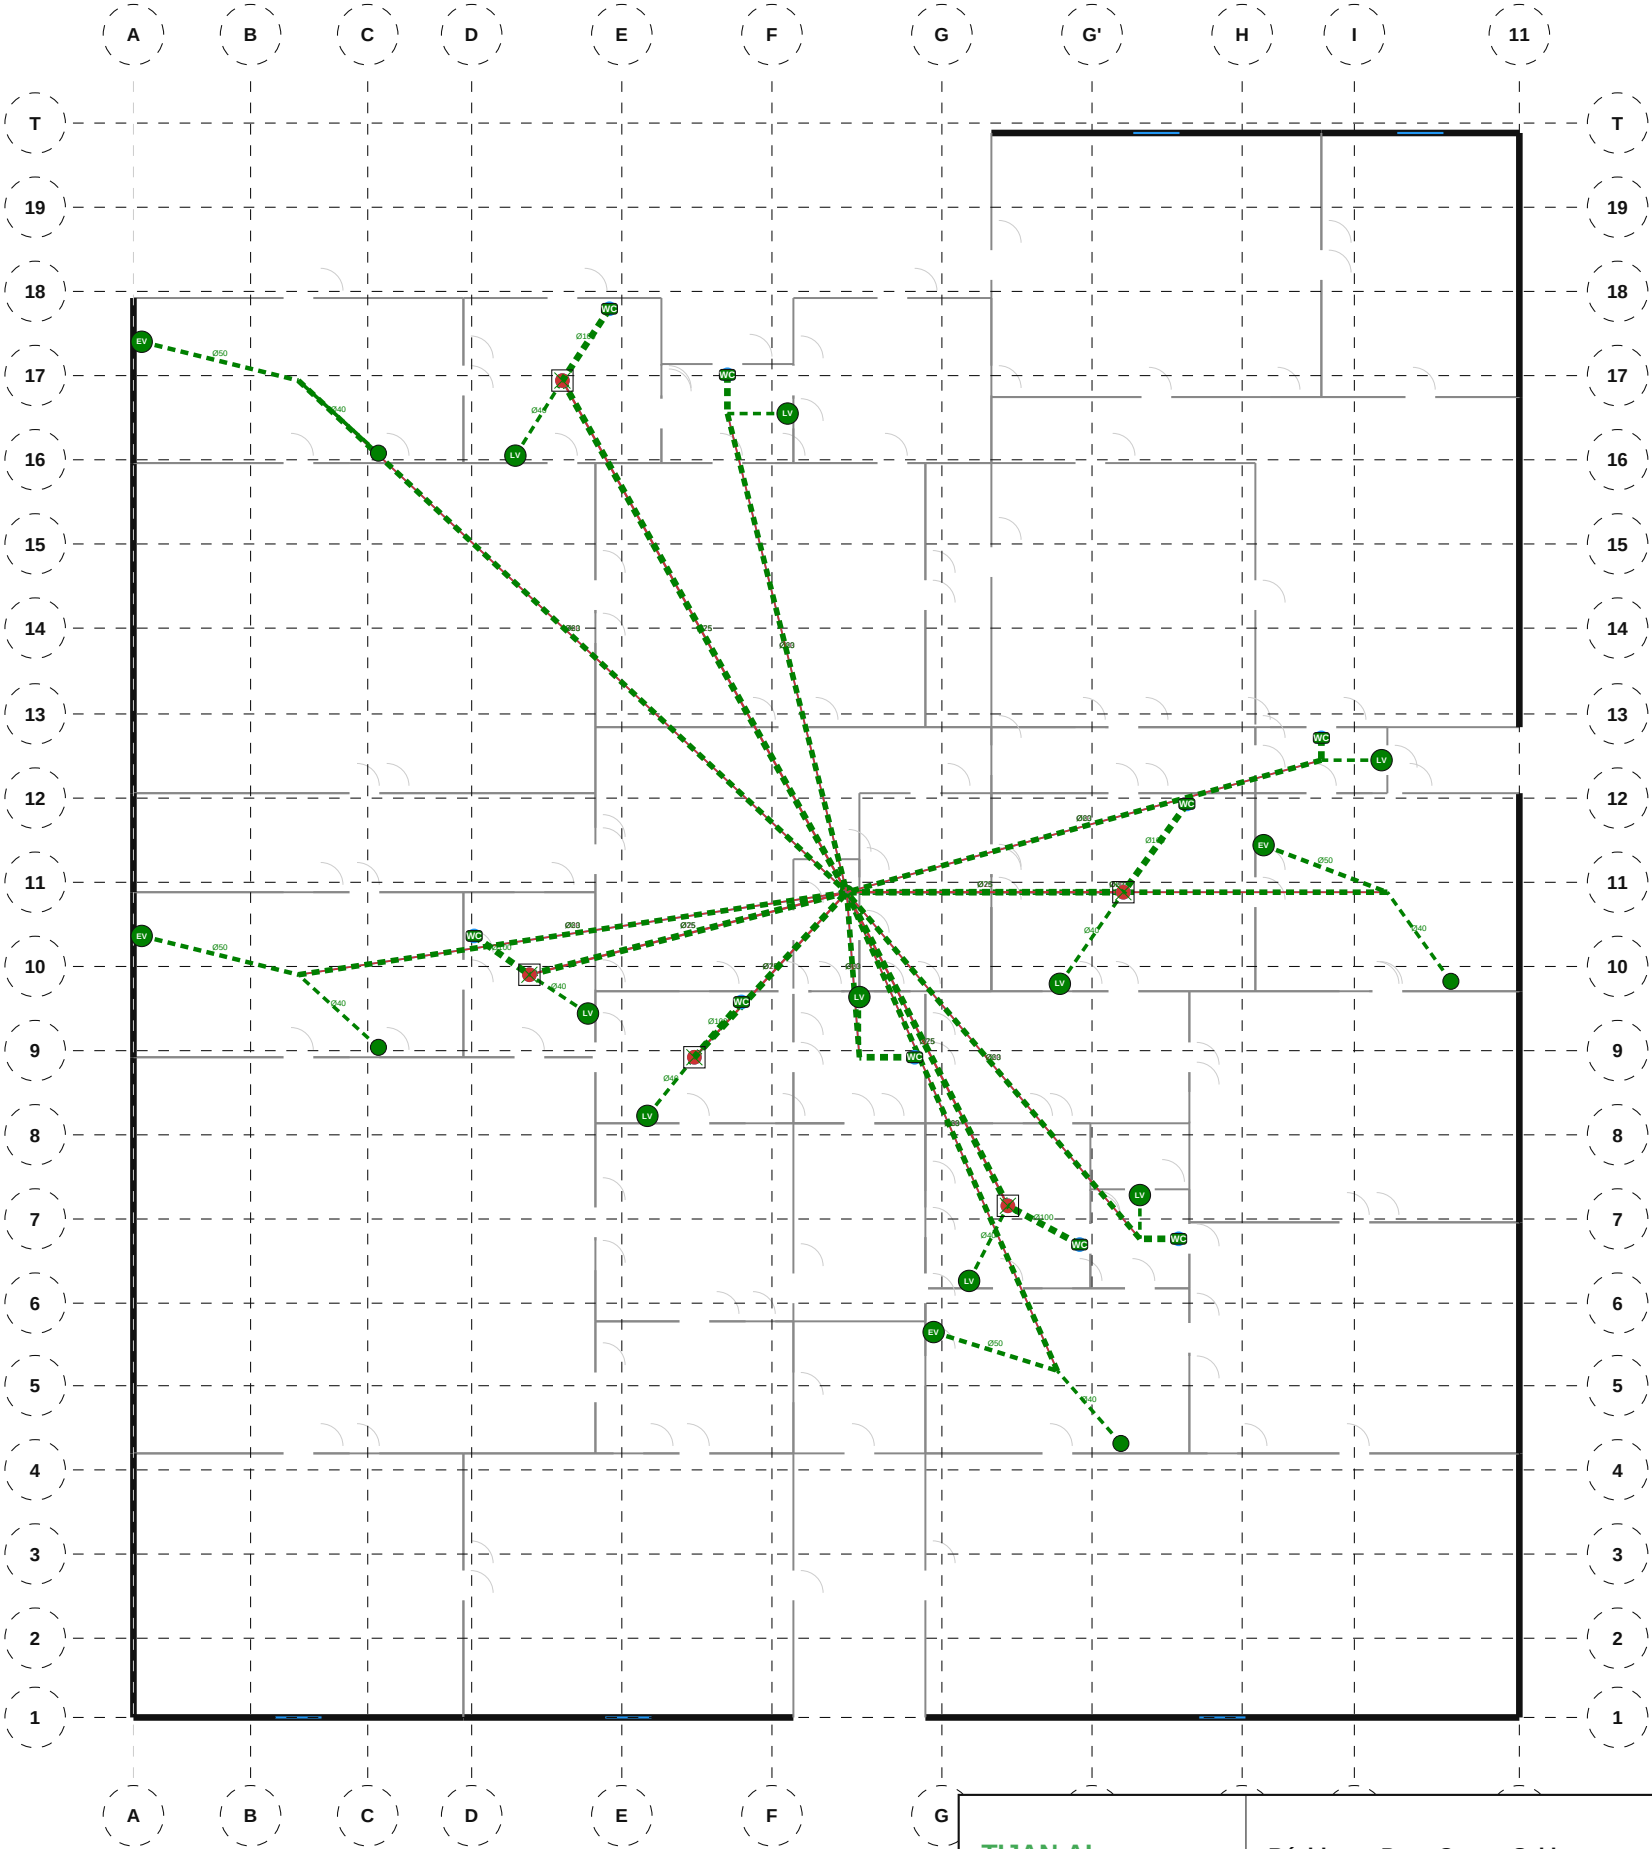

NOMENCLATURE — Plomberie

- Douche: 5
- Lavabo: 5
- Lave-mains: 4
- Lave-vaisselle: 4
- WC suspendu: 9
- Évier cuisine: 4


TIJAN AI Bureau d'Études Automatisé	Résidence Papa Oumar Sakho Dakar, Senegal	Éch: 1/100 Pl. 39/88
	Plomberie — Étage 4	
Date: 06/05/2026	Réf: 1711	BIM vPLU-039 Phase: APD

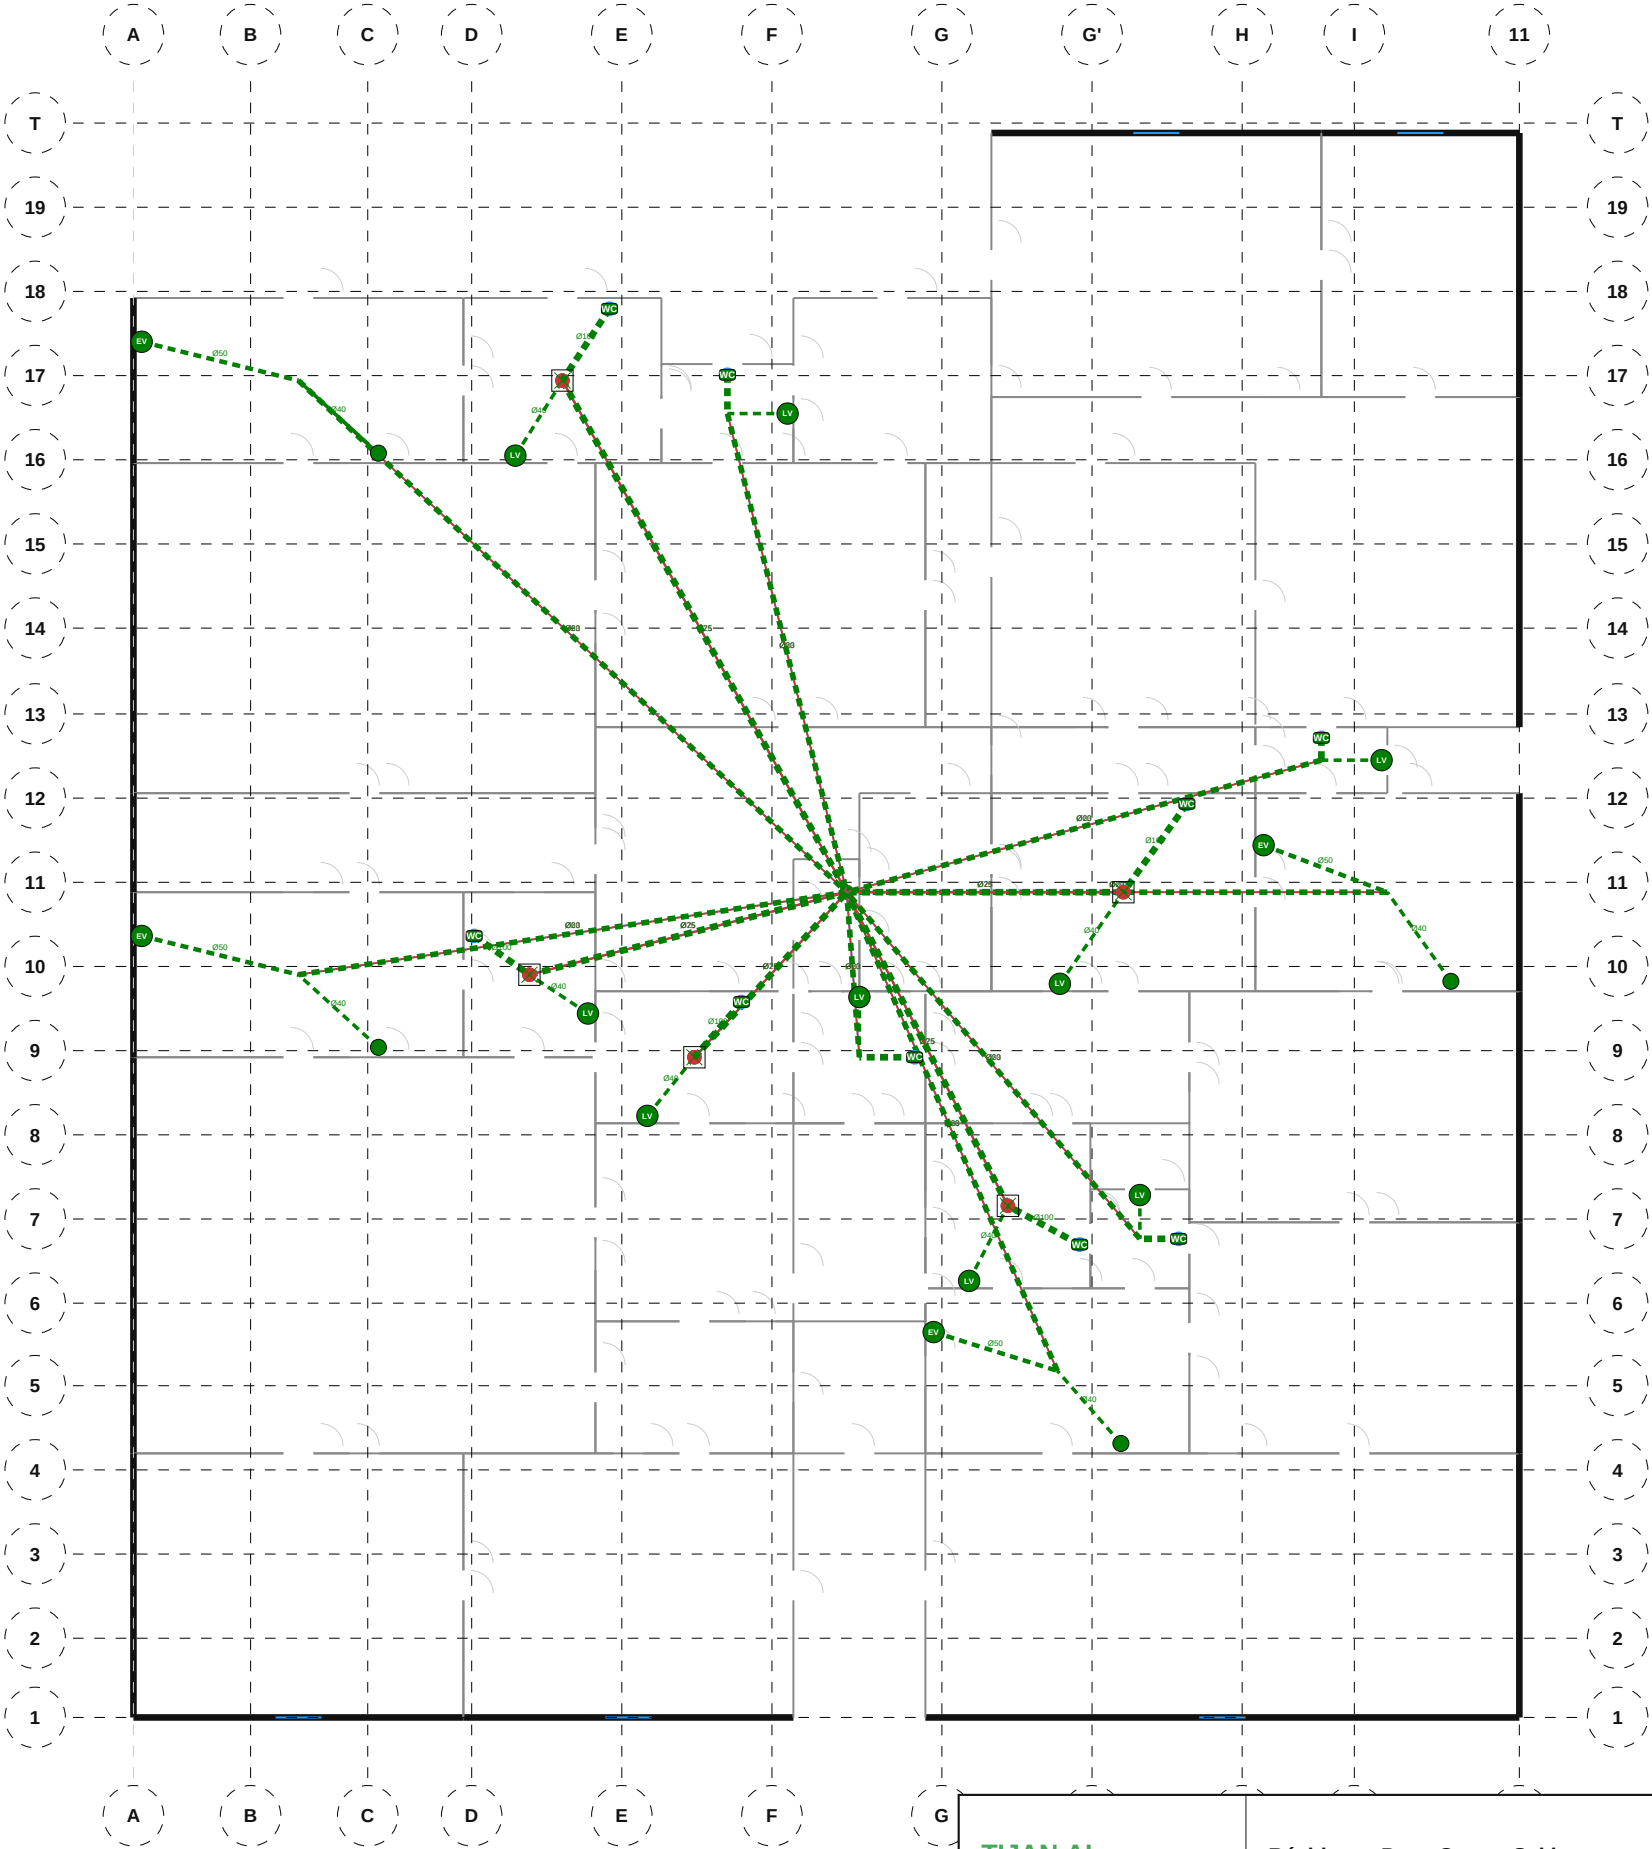

NOMENCLATURE — Plomberie

- Douche: 5
- Lavabo: 5
- Lave-mains: 4
- Lave-vaisselle: 4
- WC suspendu: 9
- Évier cuisine: 4


TIJAN AI Bureau d'Études Automatisé	Résidence Papa Oumar Sakho Dakar, Senegal	Éch: 1/100 Pl. 40/88
	Plomberie — Étage 5	
Date: 06/05/2026	Réf: 1711	BIM vPLU-040 Phase: APD

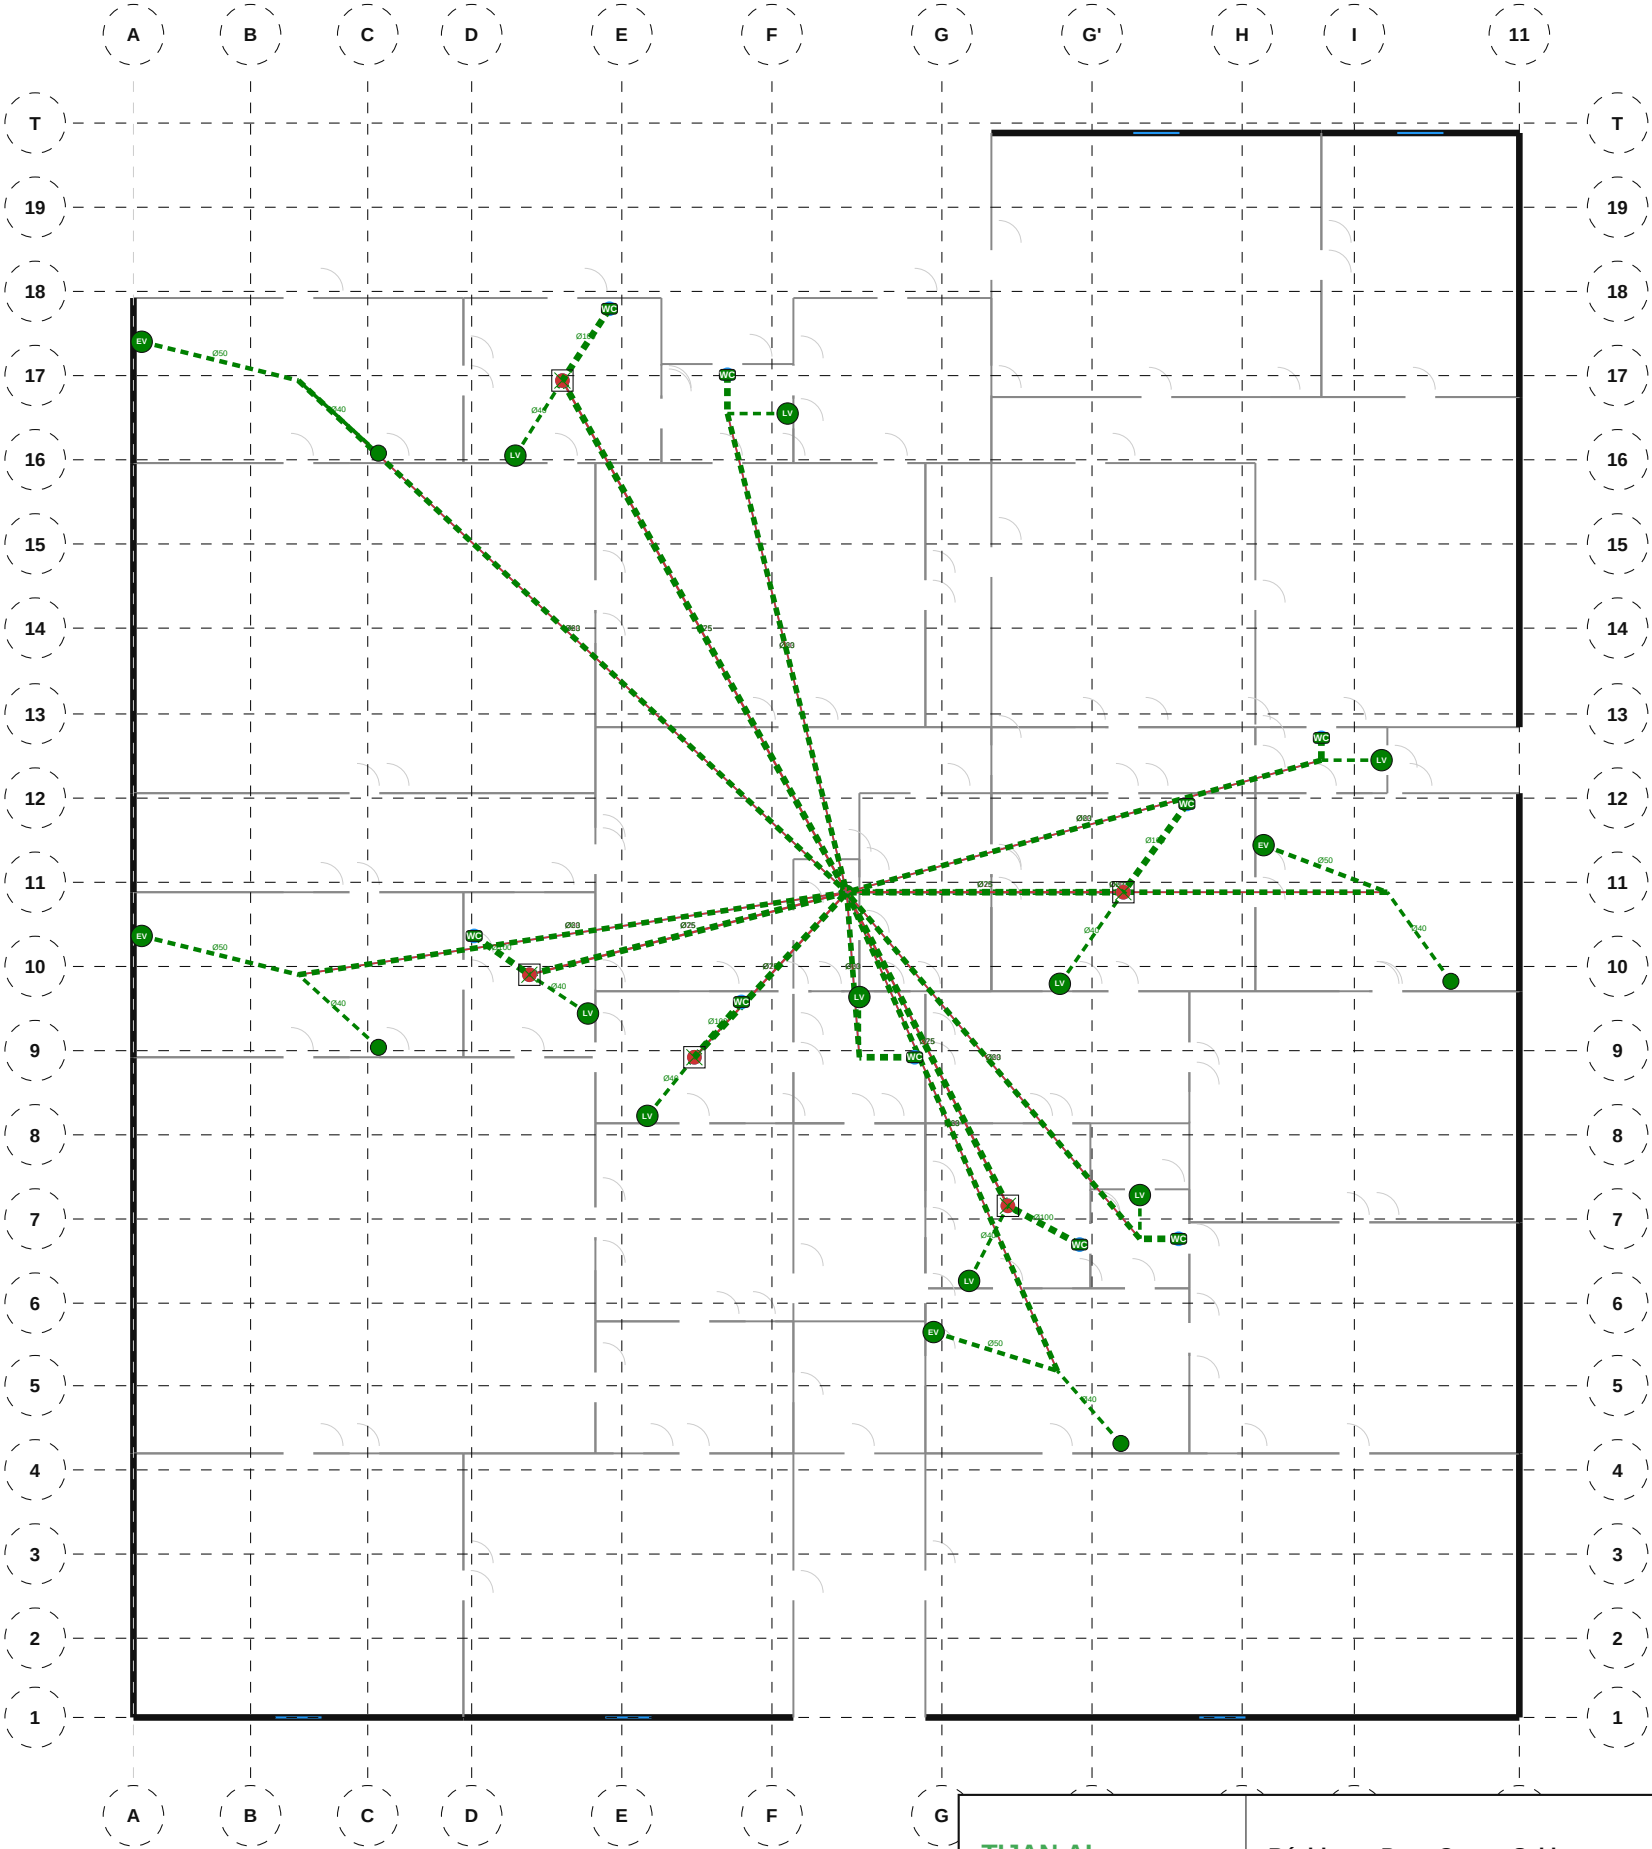

NOMENCLATURE — Plomberie

- Douche: 5
- Lavabo: 5
- Lave-mains: 4
- Lave-vaisselle: 4
- WC suspendu: 9
- Évier cuisine: 4


TIJAN AI Bureau d'Études Automatisé	Résidence Papa Oumar Sakho Dakar, Senegal	Éch: 1/100 Pl. 41/88
	Plomberie — Étage 6	
Date: 06/05/2026	Réf: 1711	BIM vPLU-041 Phase: APD

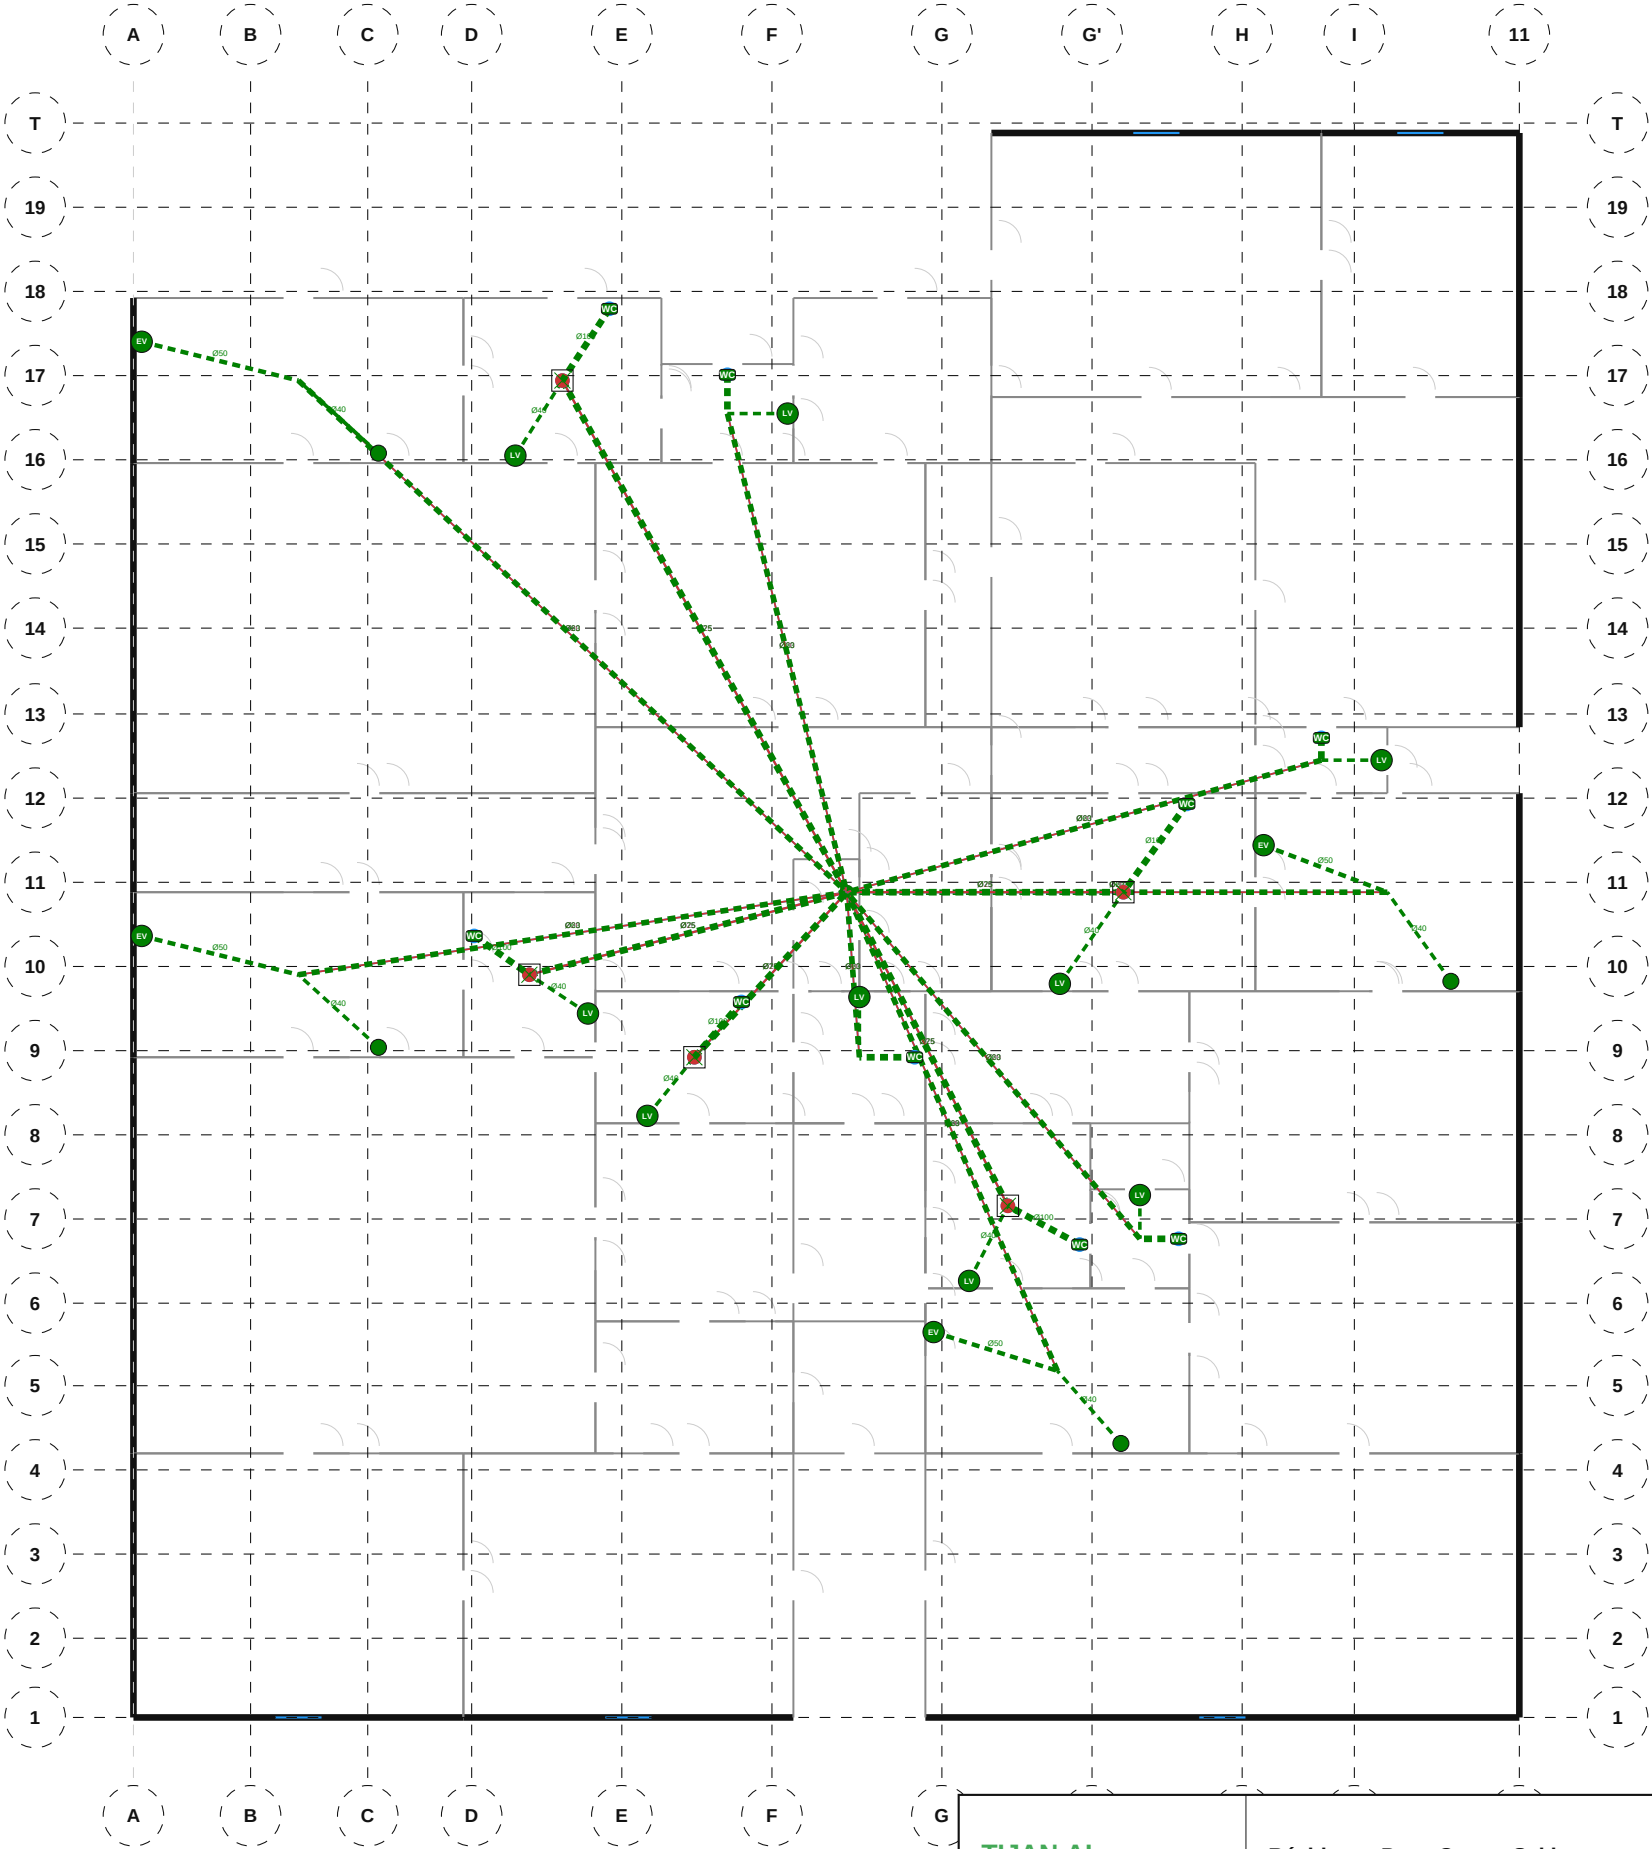

NOMENCLATURE — Plomberie

- Douche: 5
- Lavabo: 5
- Lave-mains: 4
- Lave-vaisselle: 4
- WC suspendu: 9
- Évier cuisine: 4


TIJAN AI Bureau d'Études Automatisé	Résidence Papa Oumar Sakho Dakar, Senegal	Éch: 1/100 Pl. 42/88
	Plomberie — Étage 7	
Date: 06/05/2026	Réf: 1711	BIM vPLU-042 Phase: APD

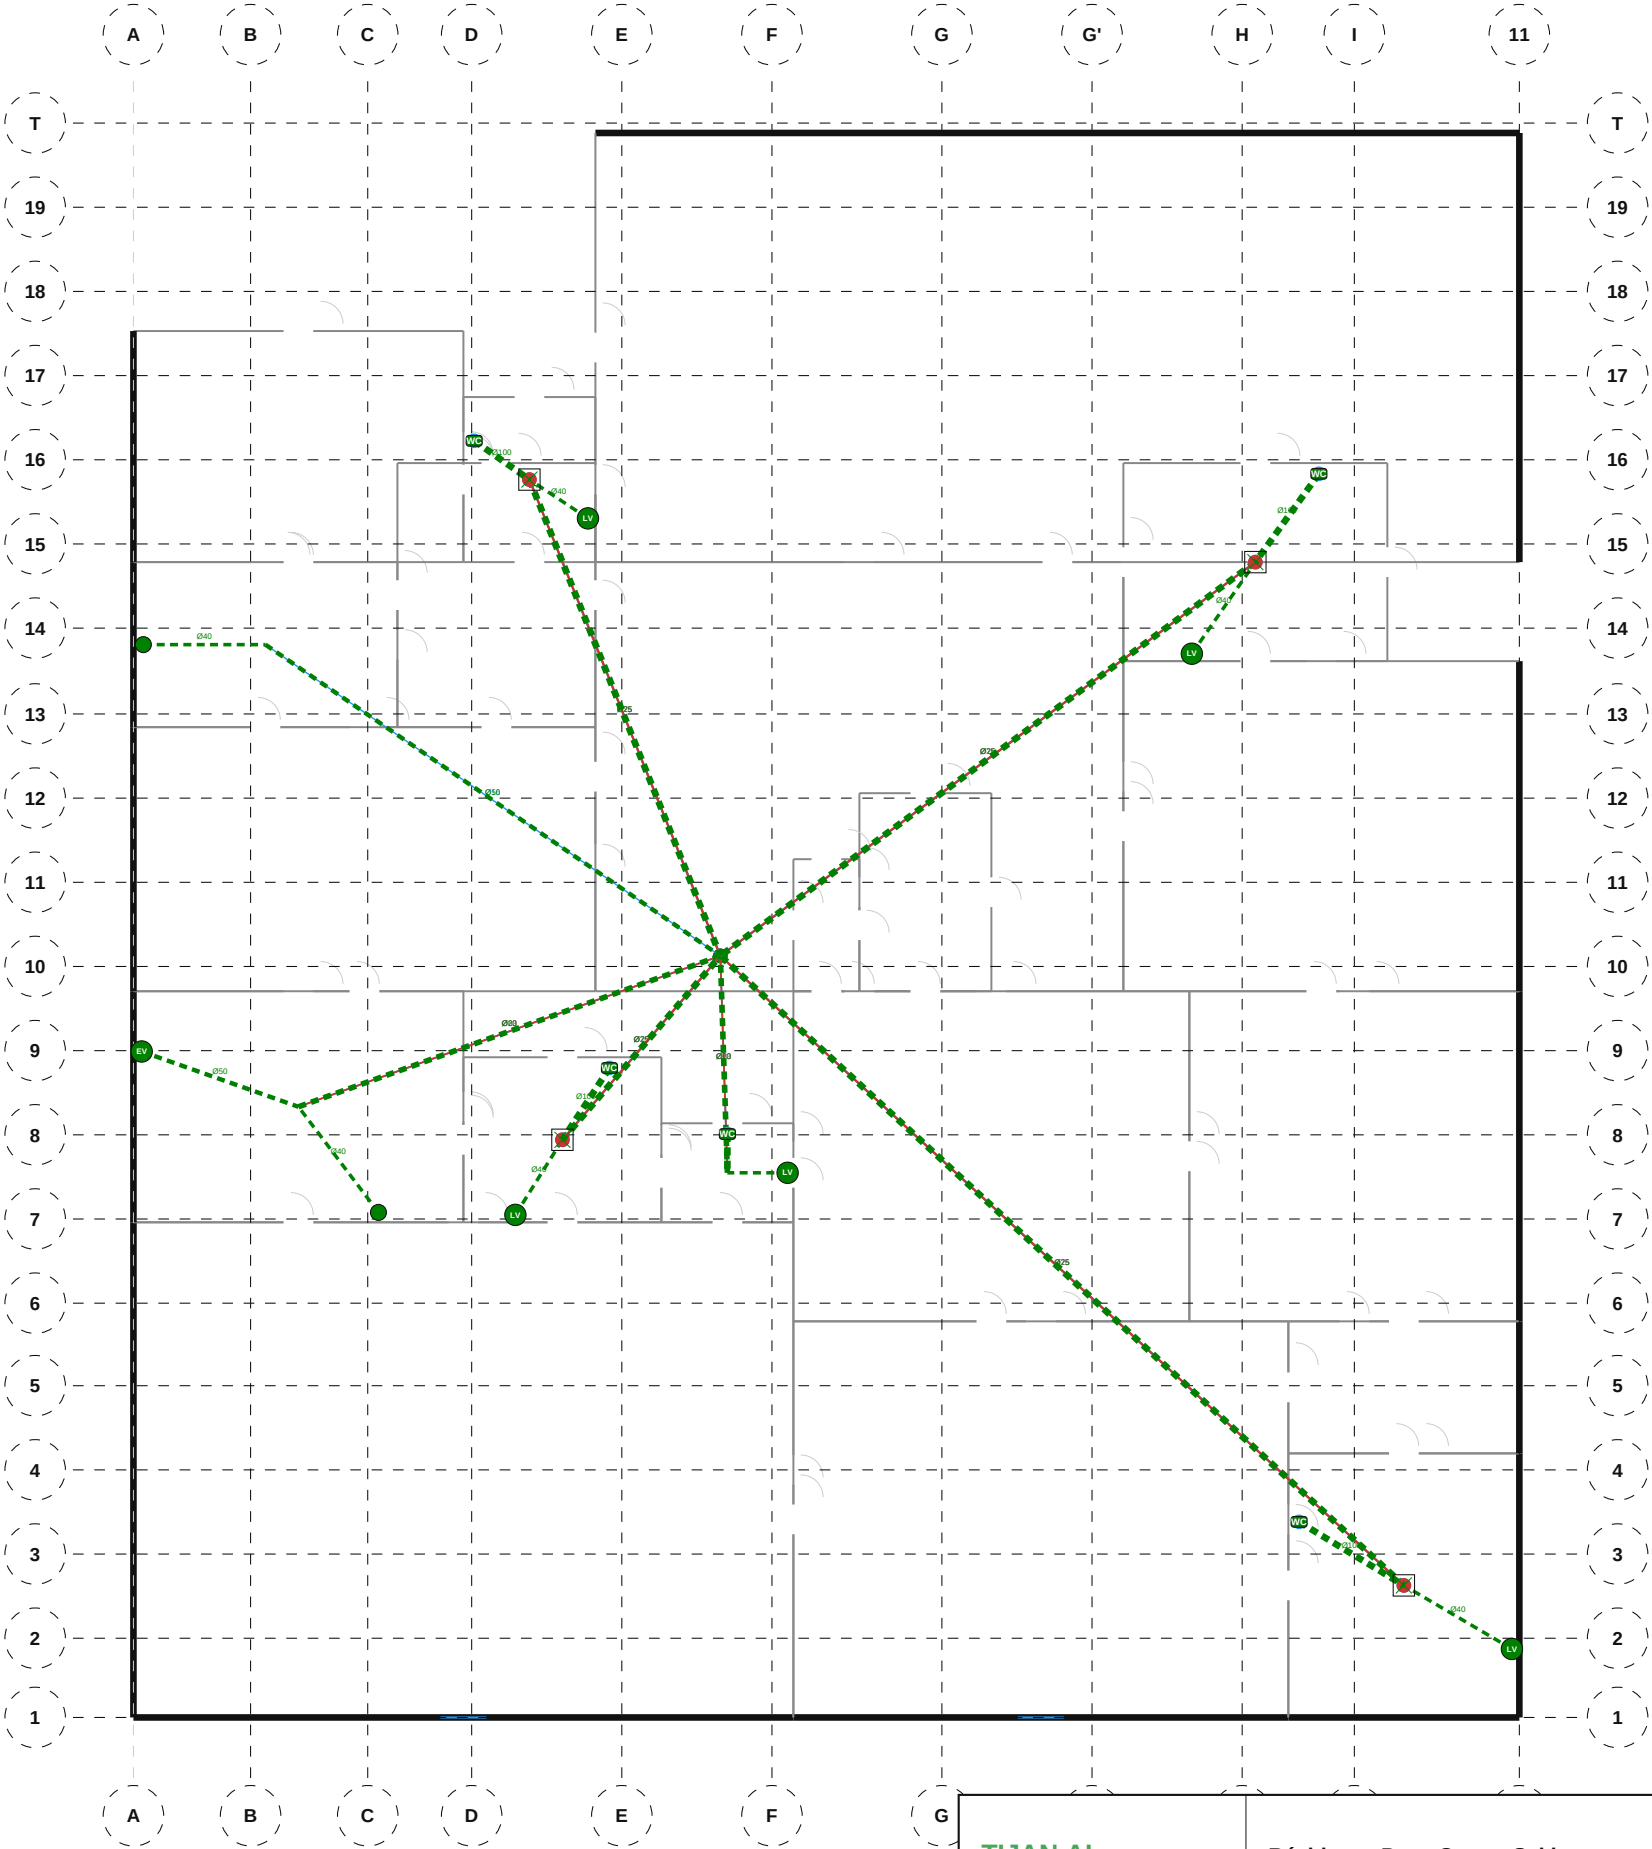

NOMENCLATURE — Plomberie

- Douche: 4
- Lavabo: 4
- Lave-linge: 1
- Lave-mains: 1
- Lave-vaisselle: 1
- WC suspendu: 5
- Évier cuisine: 1


TIJAN AI Bureau d'Études Automatisé	Résidence Papa Oumar Sakho Dakar, Senegal		Éch: 1/100 Pl. 43/88
	Plomberie — Étage 8		
	Date: 06/05/2026	Réf: 1711	BIM vPLU-043 Phase: APD

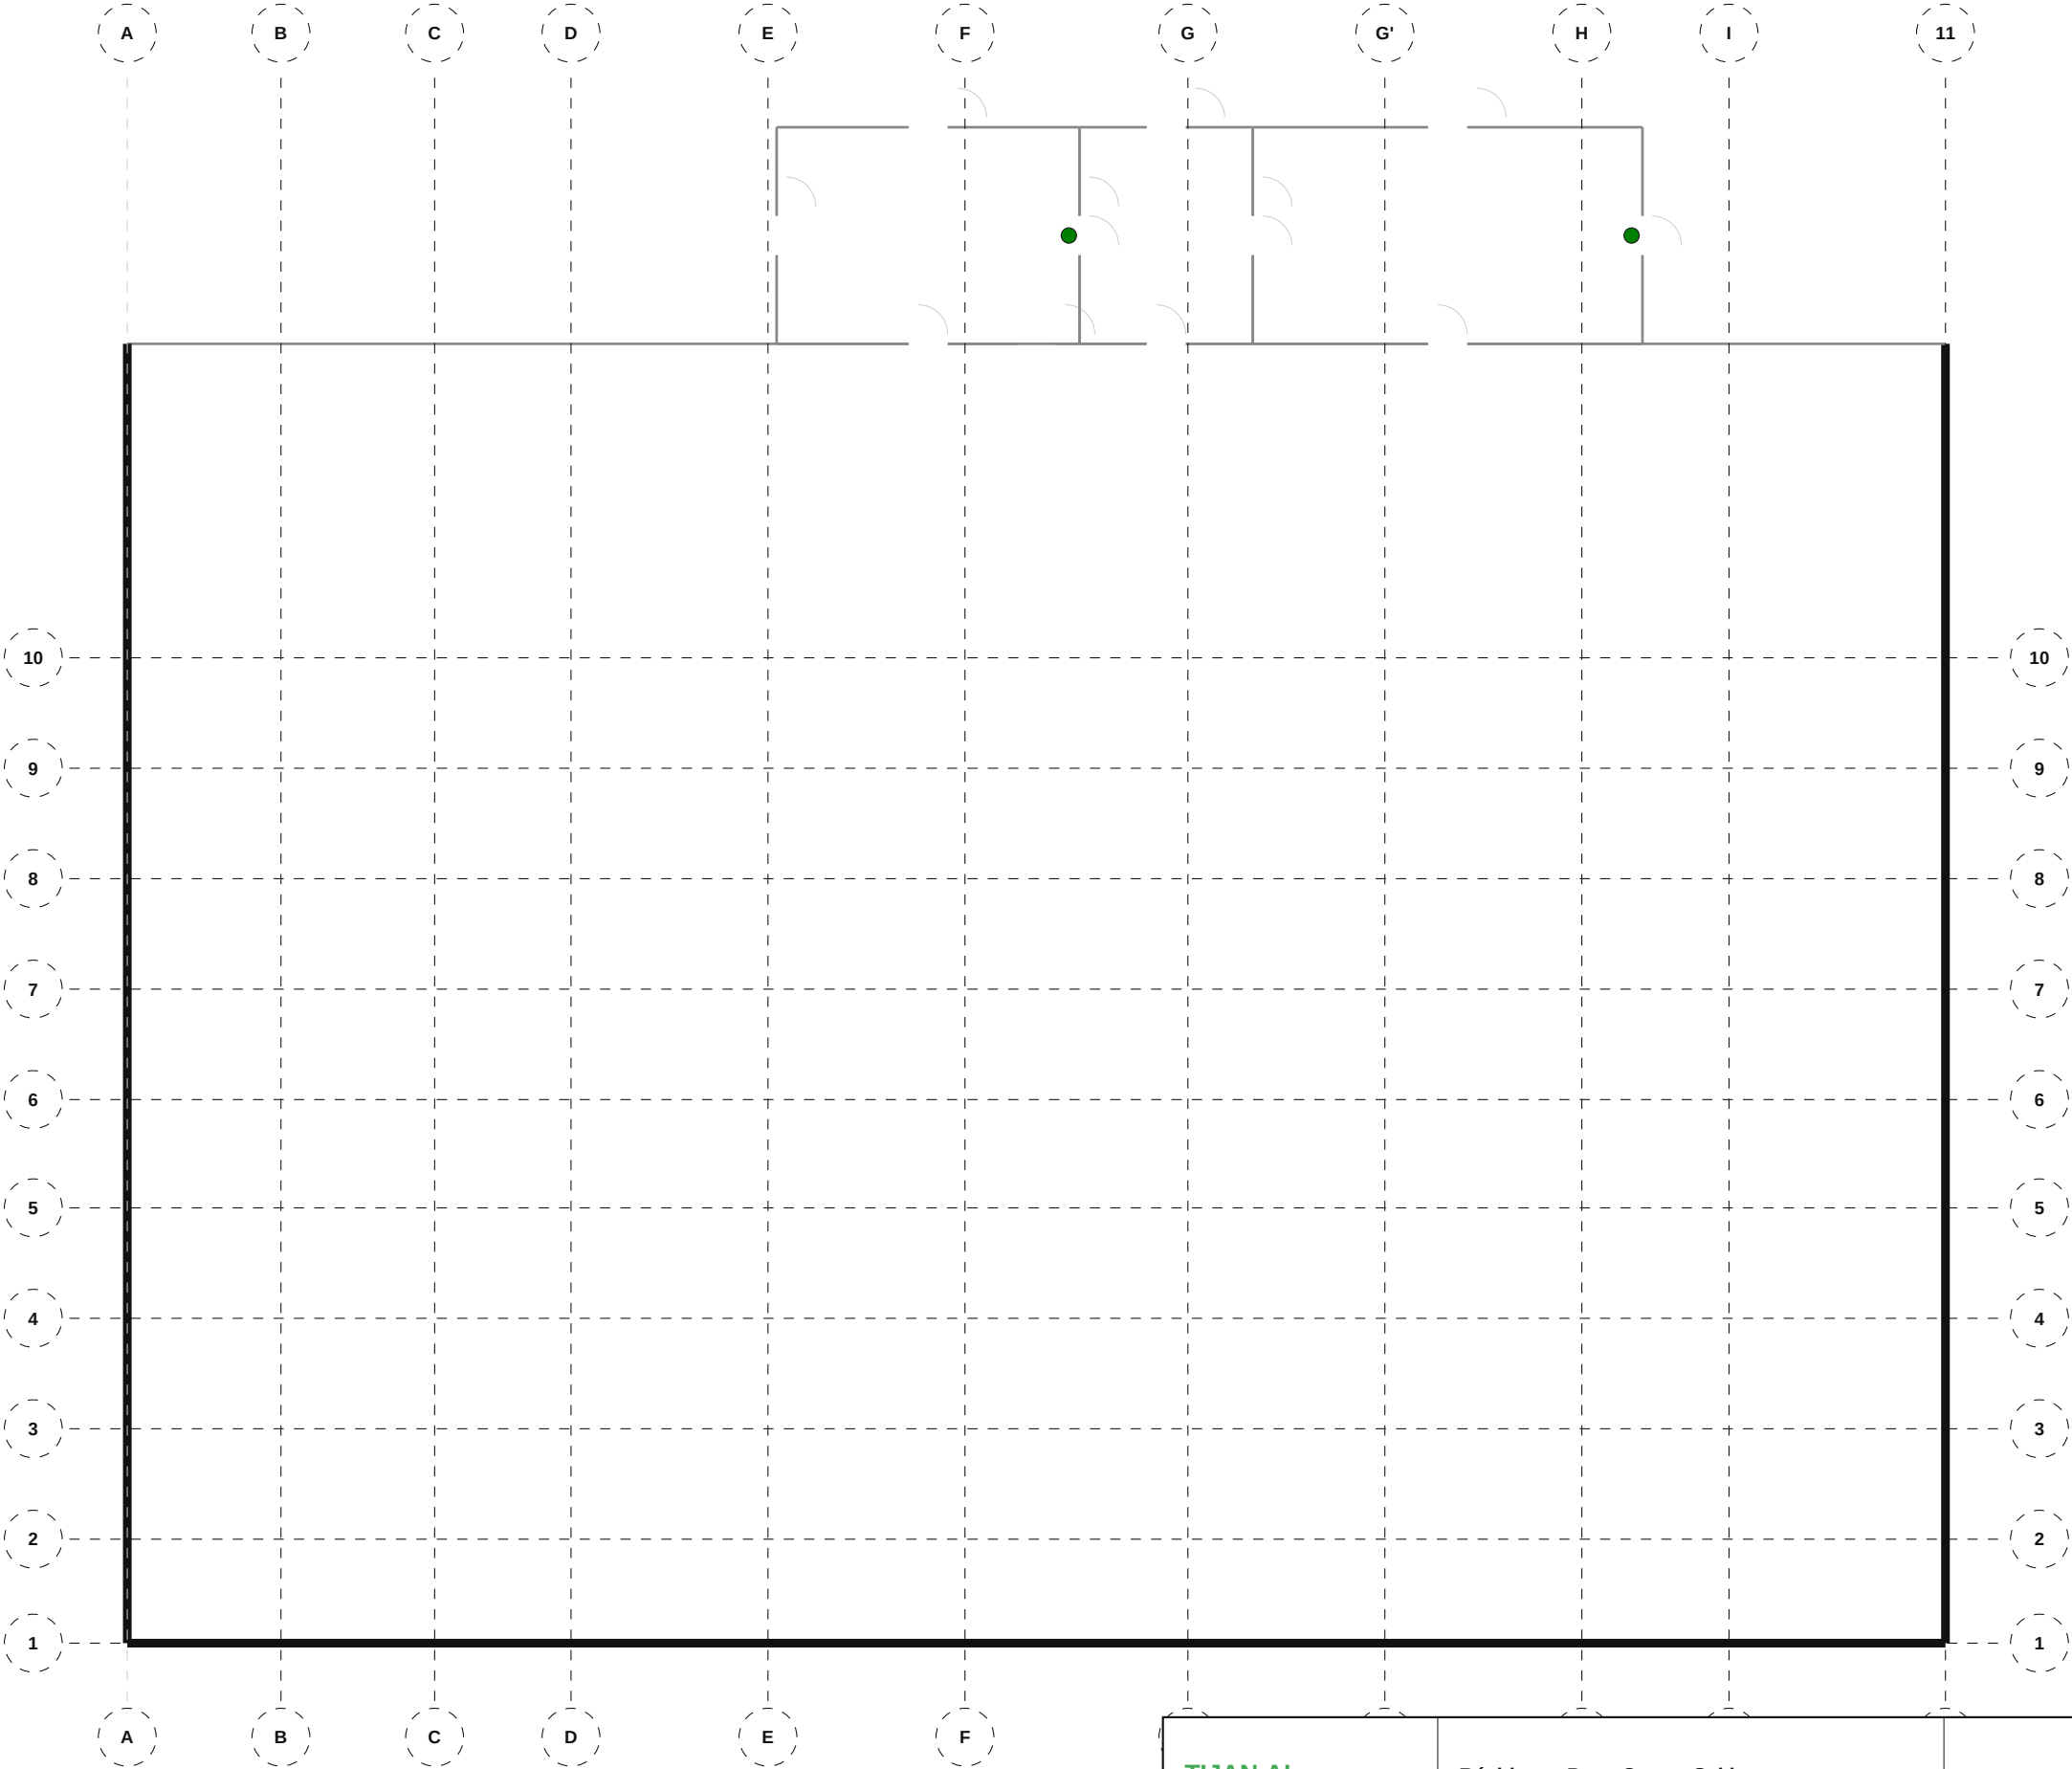

NOMENCLATURE — Plomberie

• Chauffe-eau: 2

TIJAN AI Bureau d'Études Automatisé	Résidence Papa Oumar Sakho Dakar, Senegal	Éch: 1/100 Pl. 44/88
	Plomberie — Terrasse	
Date: 06/05/2026	Réf: 1711	BIM vPLU-044 Phase: APD

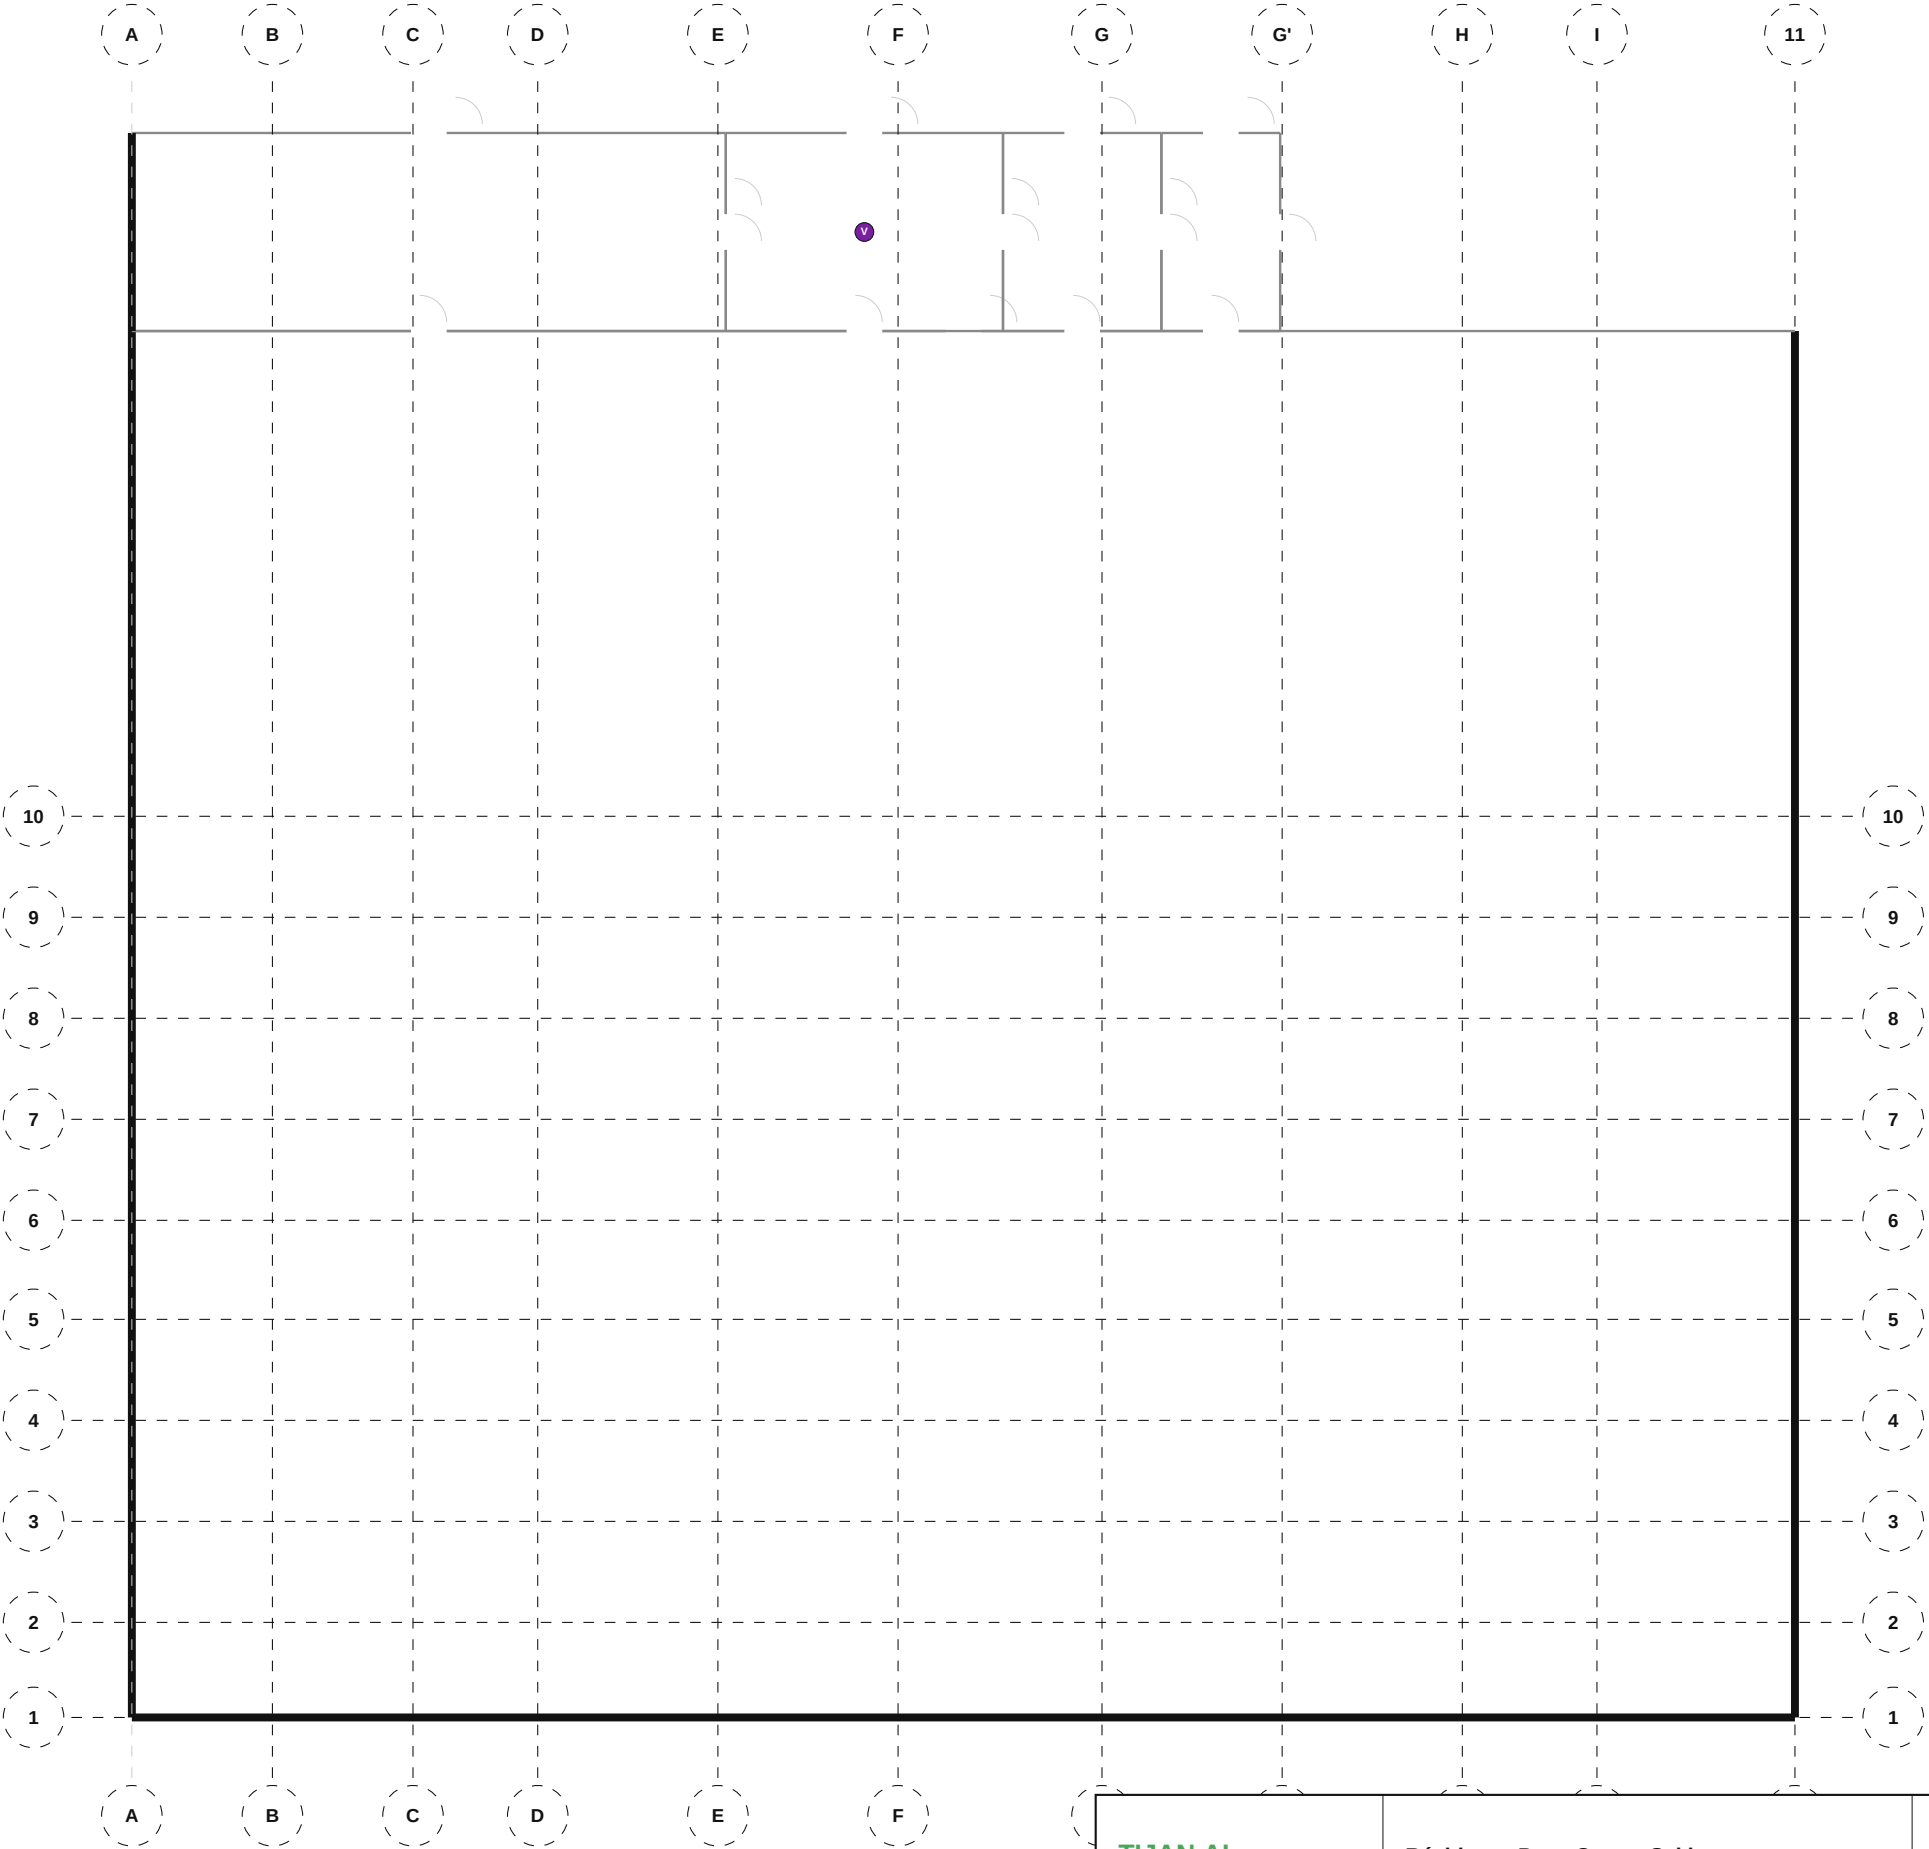


NOMENCLATURE — CVC / Ventilation

• Bouche VMC: 1

TIJAN AI Bureau d'Études Automatisé	Résidence Papa Oumar Sakho Dakar, Senegal	Éch: 1/100 Pl. 45/88
	CVC / Ventilation — Sous-Sol	
Date: 06/05/2026	Réf: 1711	BIM vHVC-045 Phase: APD


413 CVC / Ventilation — RDC

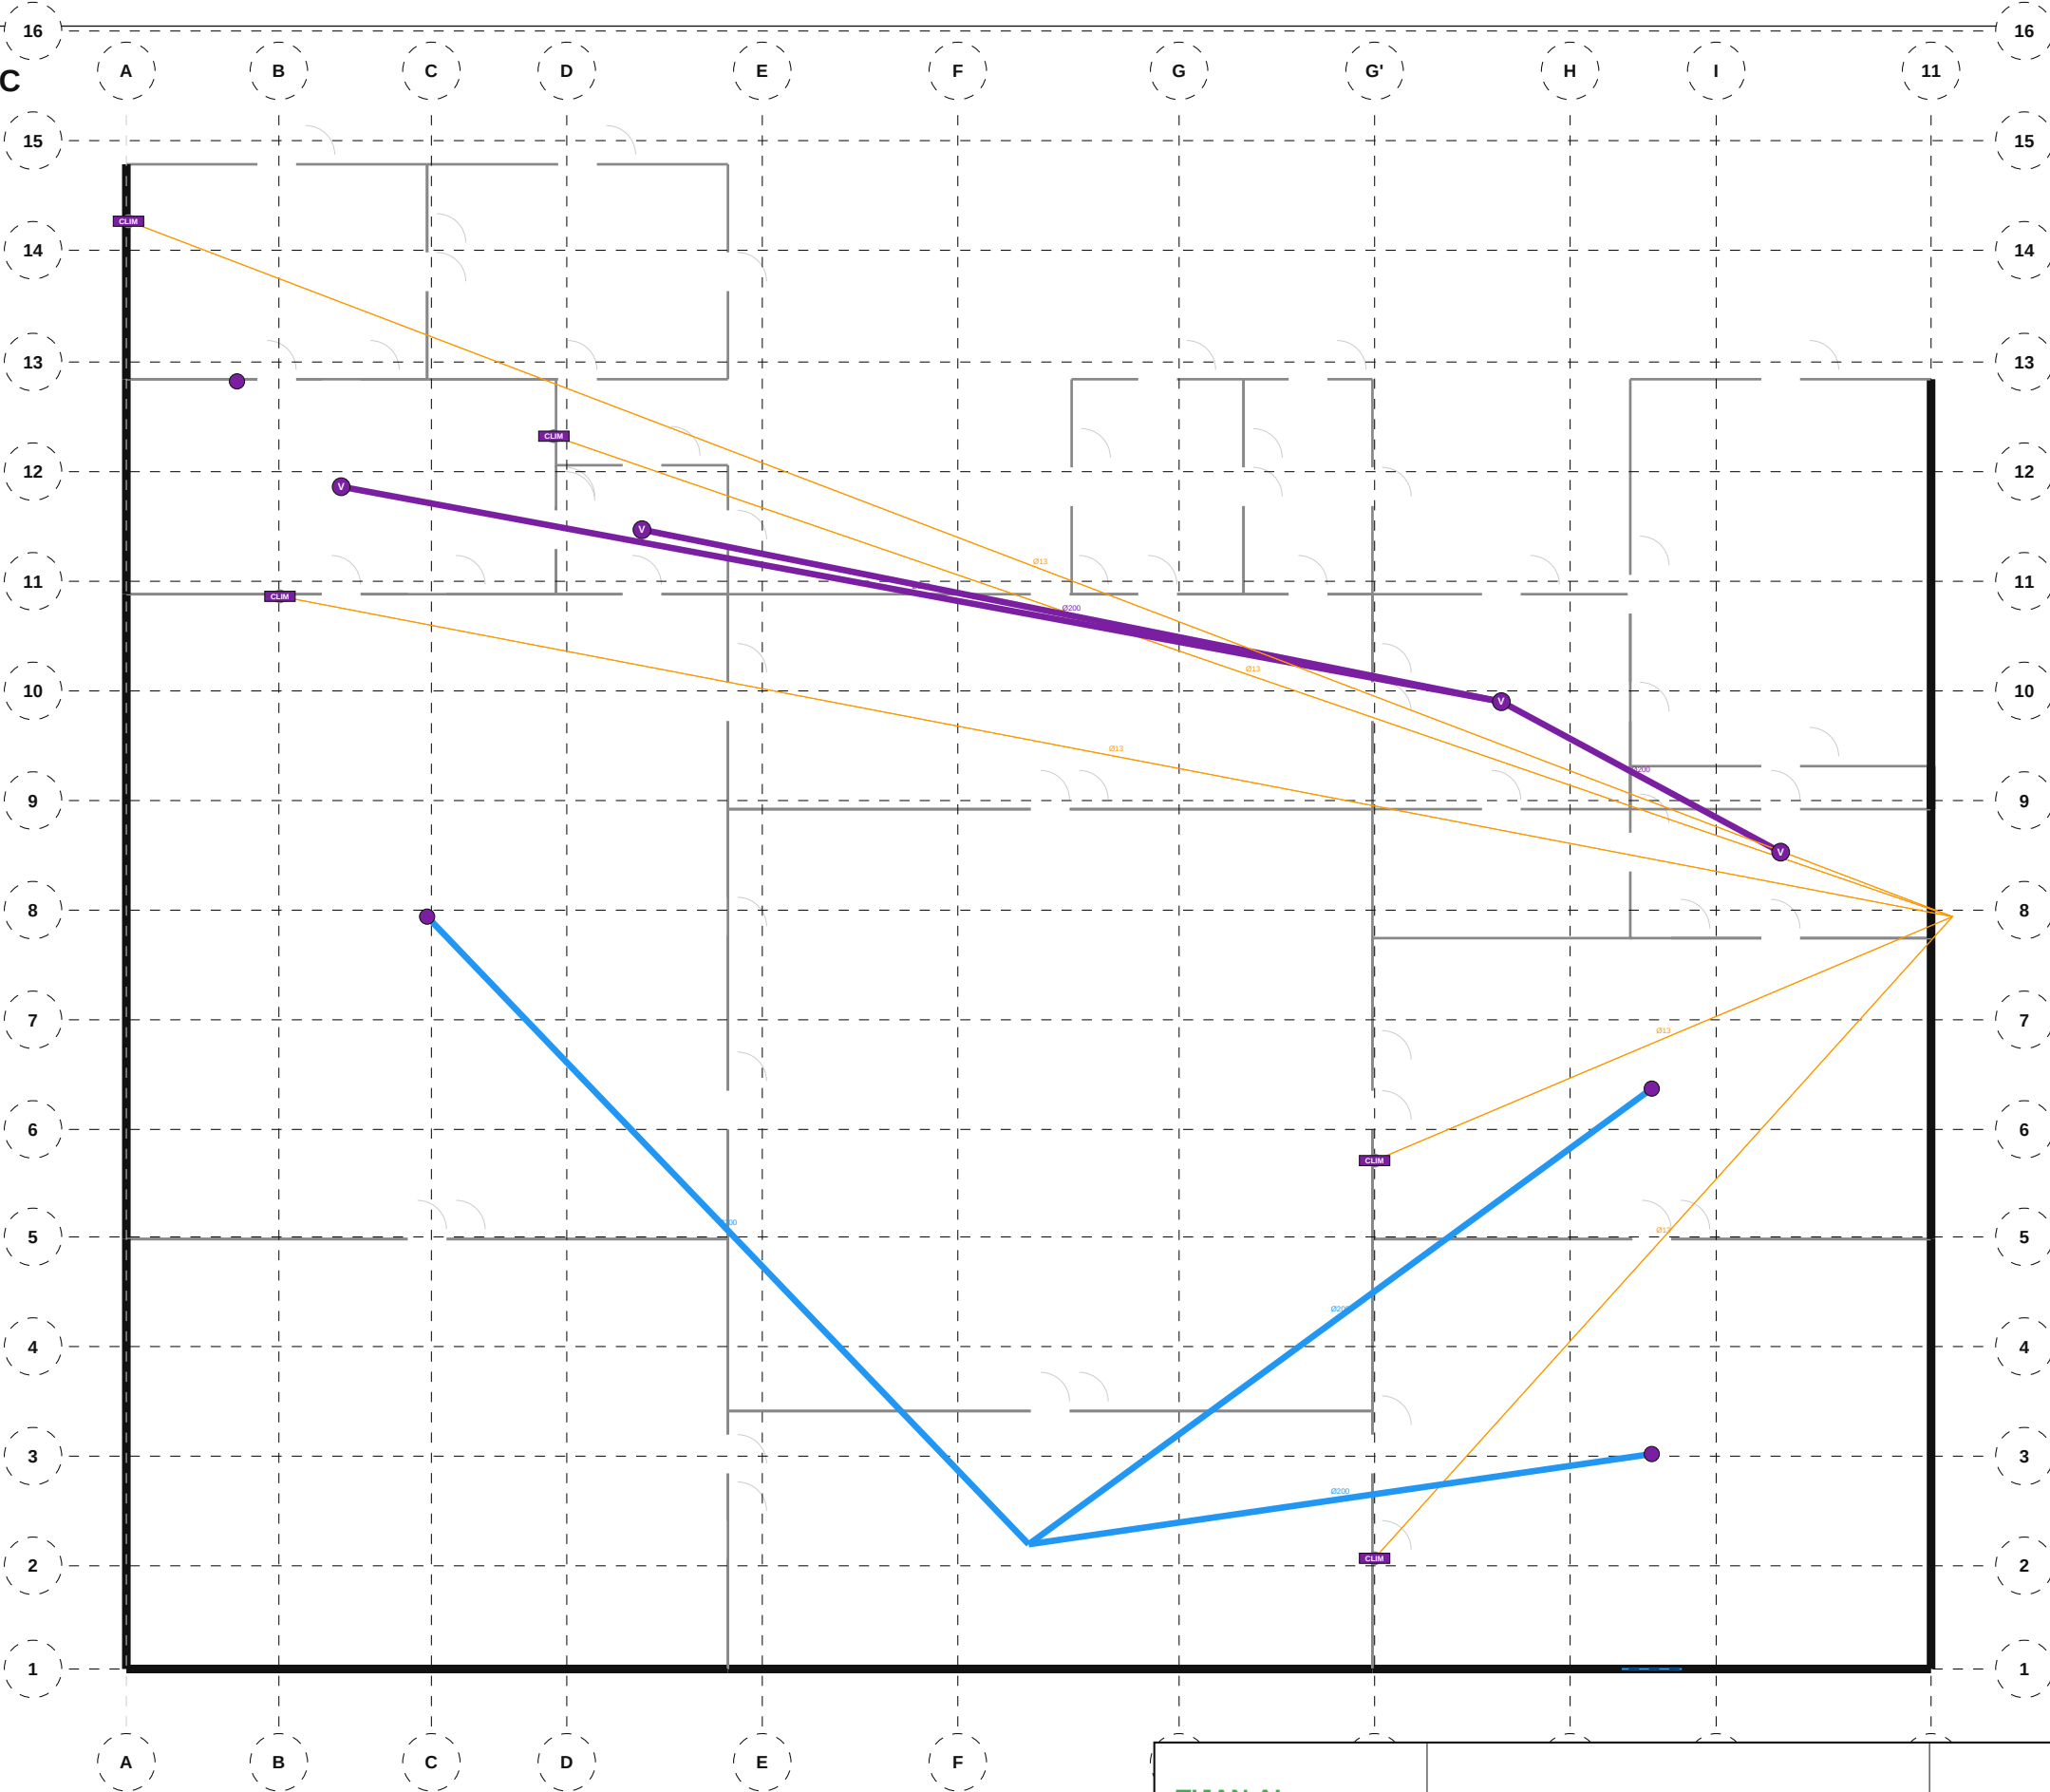

NOMENCLATURE — CVC / Ventilation

- Bouche VMC: 1
- Bouche VMC extraction: 3
- Grille soufflage: 3
- Hotte aspirante: 1
- Split climatiseur: 5


TIJAN AI Bureau d'Études Automatisé	Résidence Papa Oumar Sakho Dakar, Senegal	Éch: 1/100 Pl. 46/88
	CVC / Ventilation — RDC	
Date: 06/05/2026	Réf: 1711	BIM vHVC-046 Phase: APD

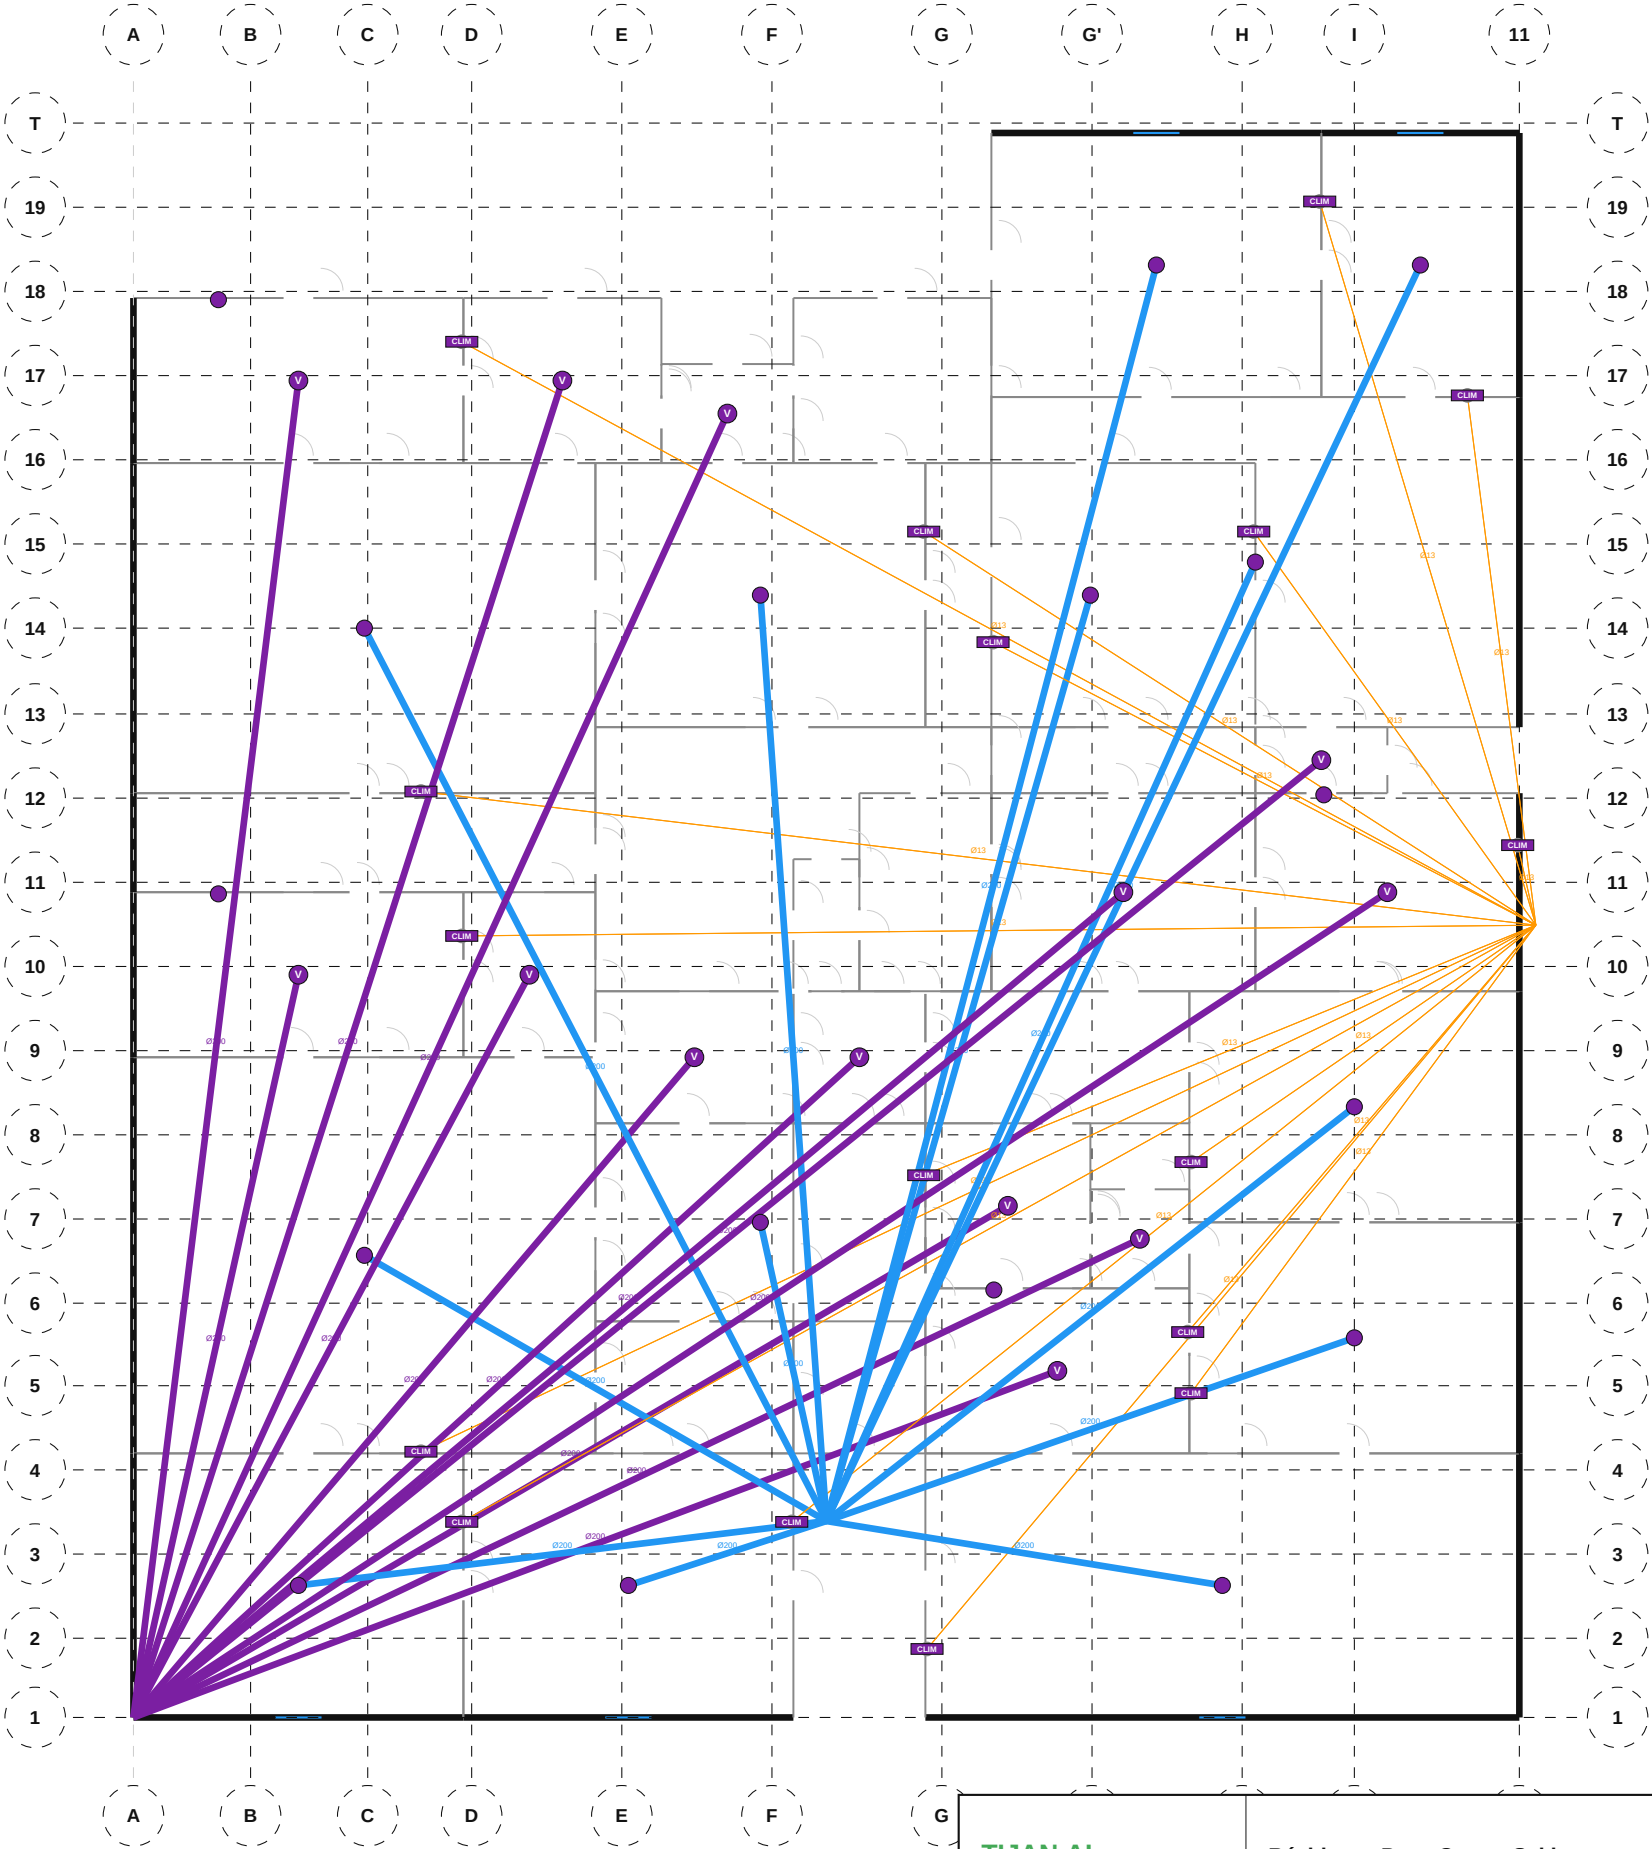

NOMENCLATURE — CVC / Ventilation

- Bouche VMC extraction: 13
- Grille soufflage: 13
- Hotte aspirante: 4
- Split climatiseur: 17


TIJAN AI Bureau d'Études Automatisé	Résidence Papa Oumar Sakho Dakar, Senegal	Éch: 1/100 Pl. 47/88
	CVC / Ventilation — Étage 1	
Date: 06/05/2026	Réf: 1711	BIM vHVC-047 Phase: APD

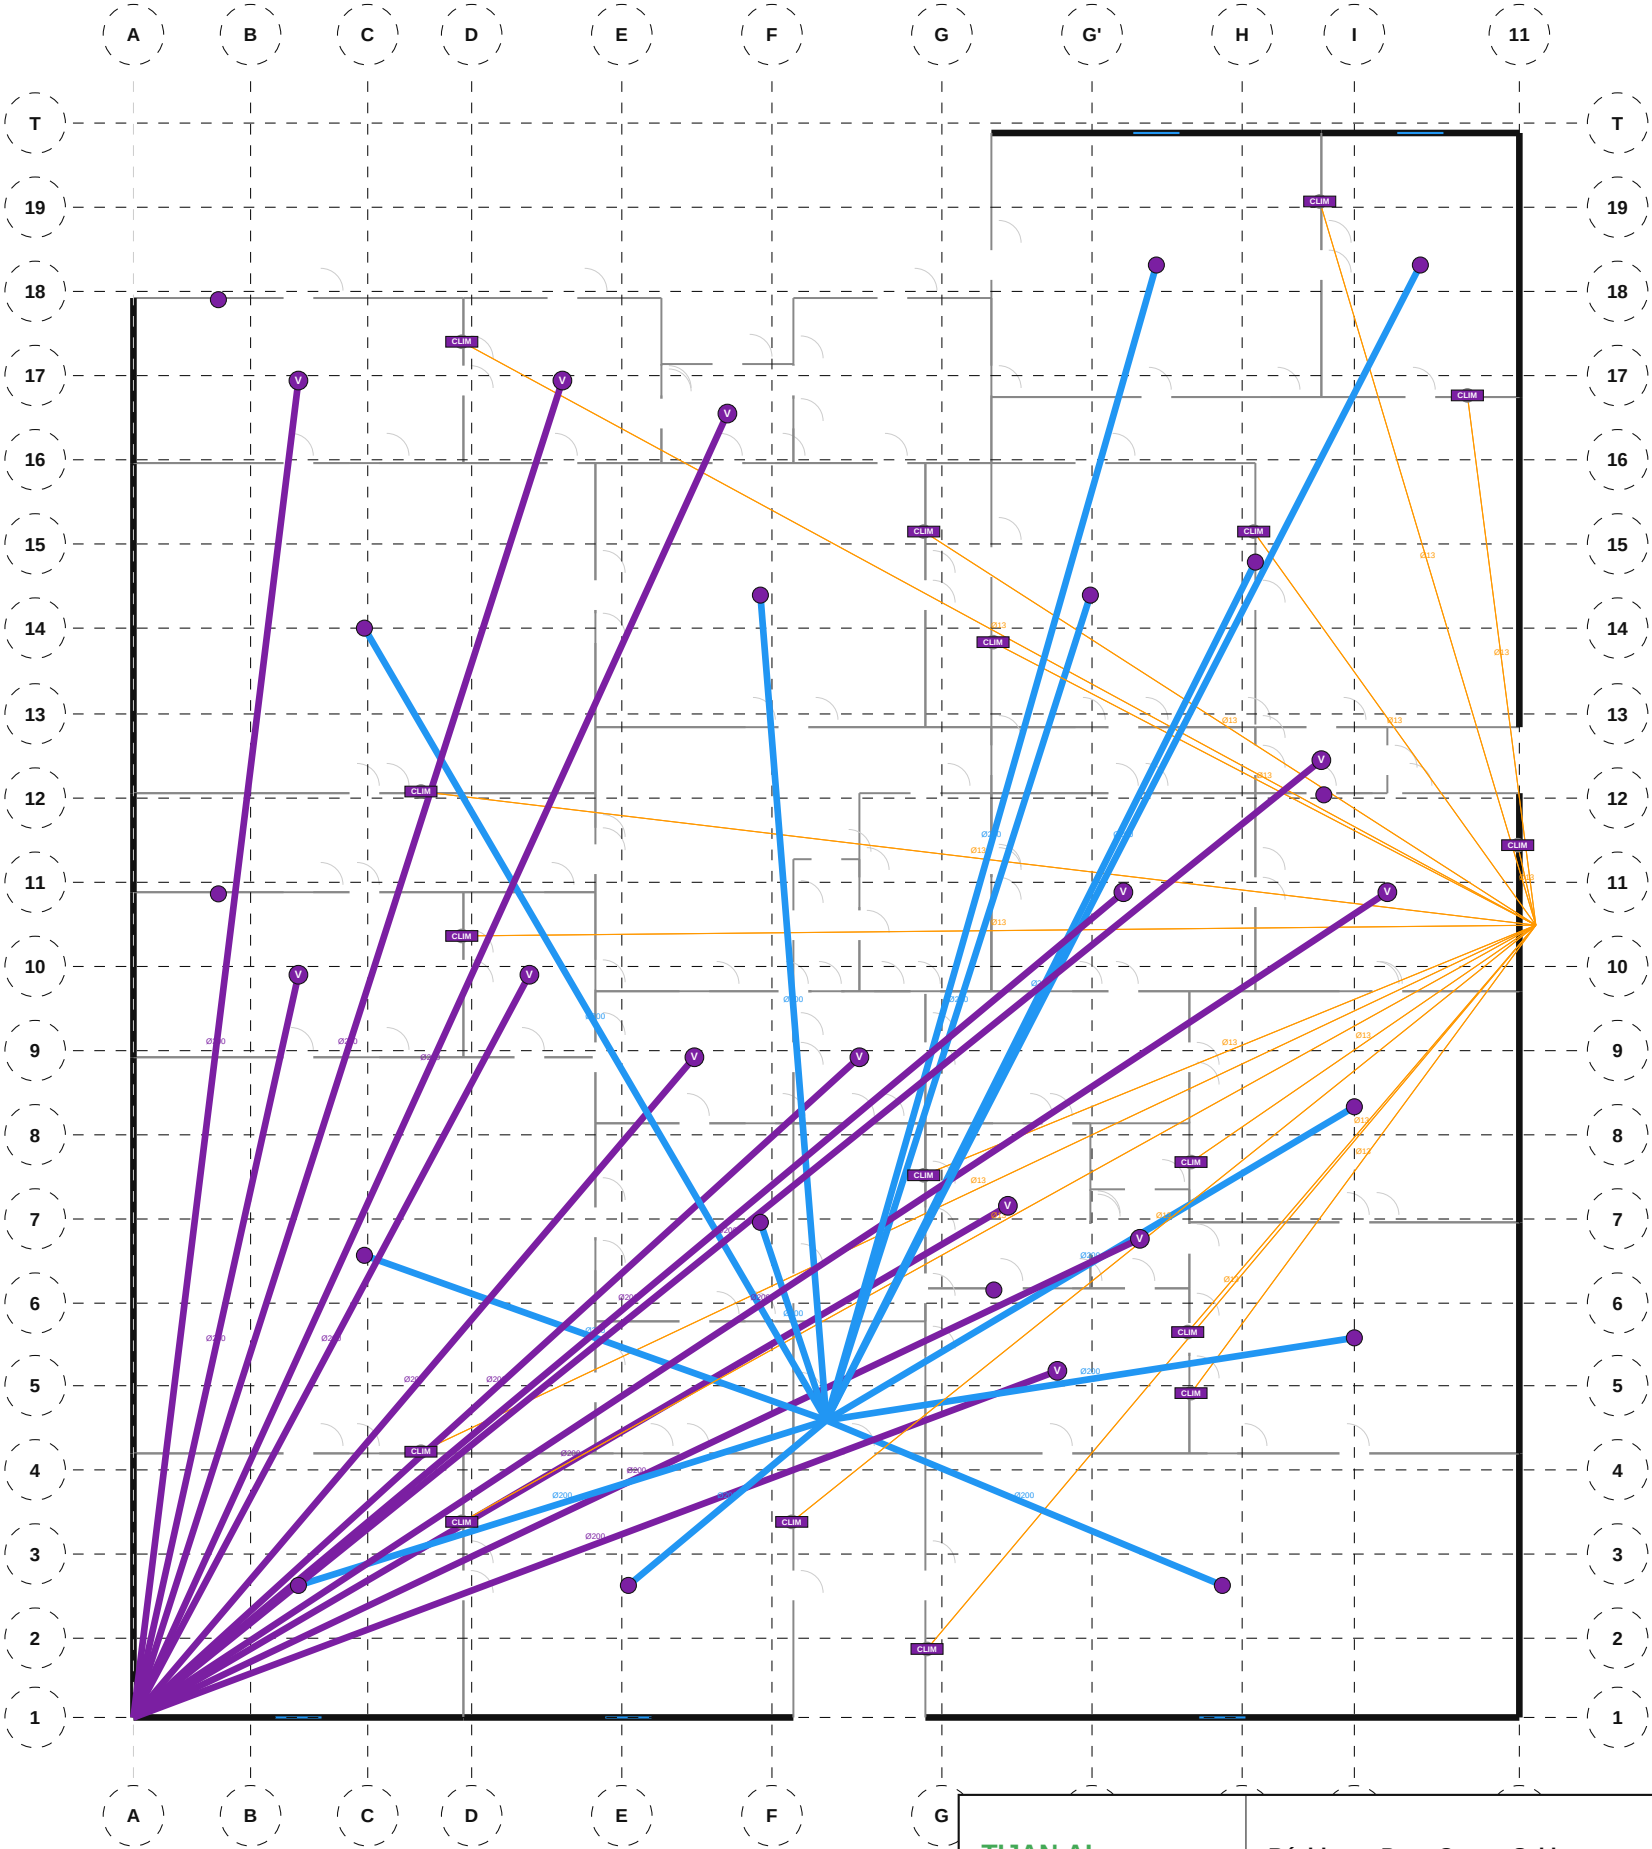

NOMENCLATURE — CVC / Ventilation

- Bouche VMC extraction: 13
- Grille soufflage: 13
- Hotte aspirante: 4
- Split climatiseur: 17


TIJAN AI Bureau d'Études Automatisé	Résidence Papa Oumar Sakho Dakar, Senegal	Éch: 1/100 Pl. 48/88
	CVC / Ventilation — Étage 2	
Date: 06/05/2026	Réf: 1711	BIM vHVC-048 Phase: APD

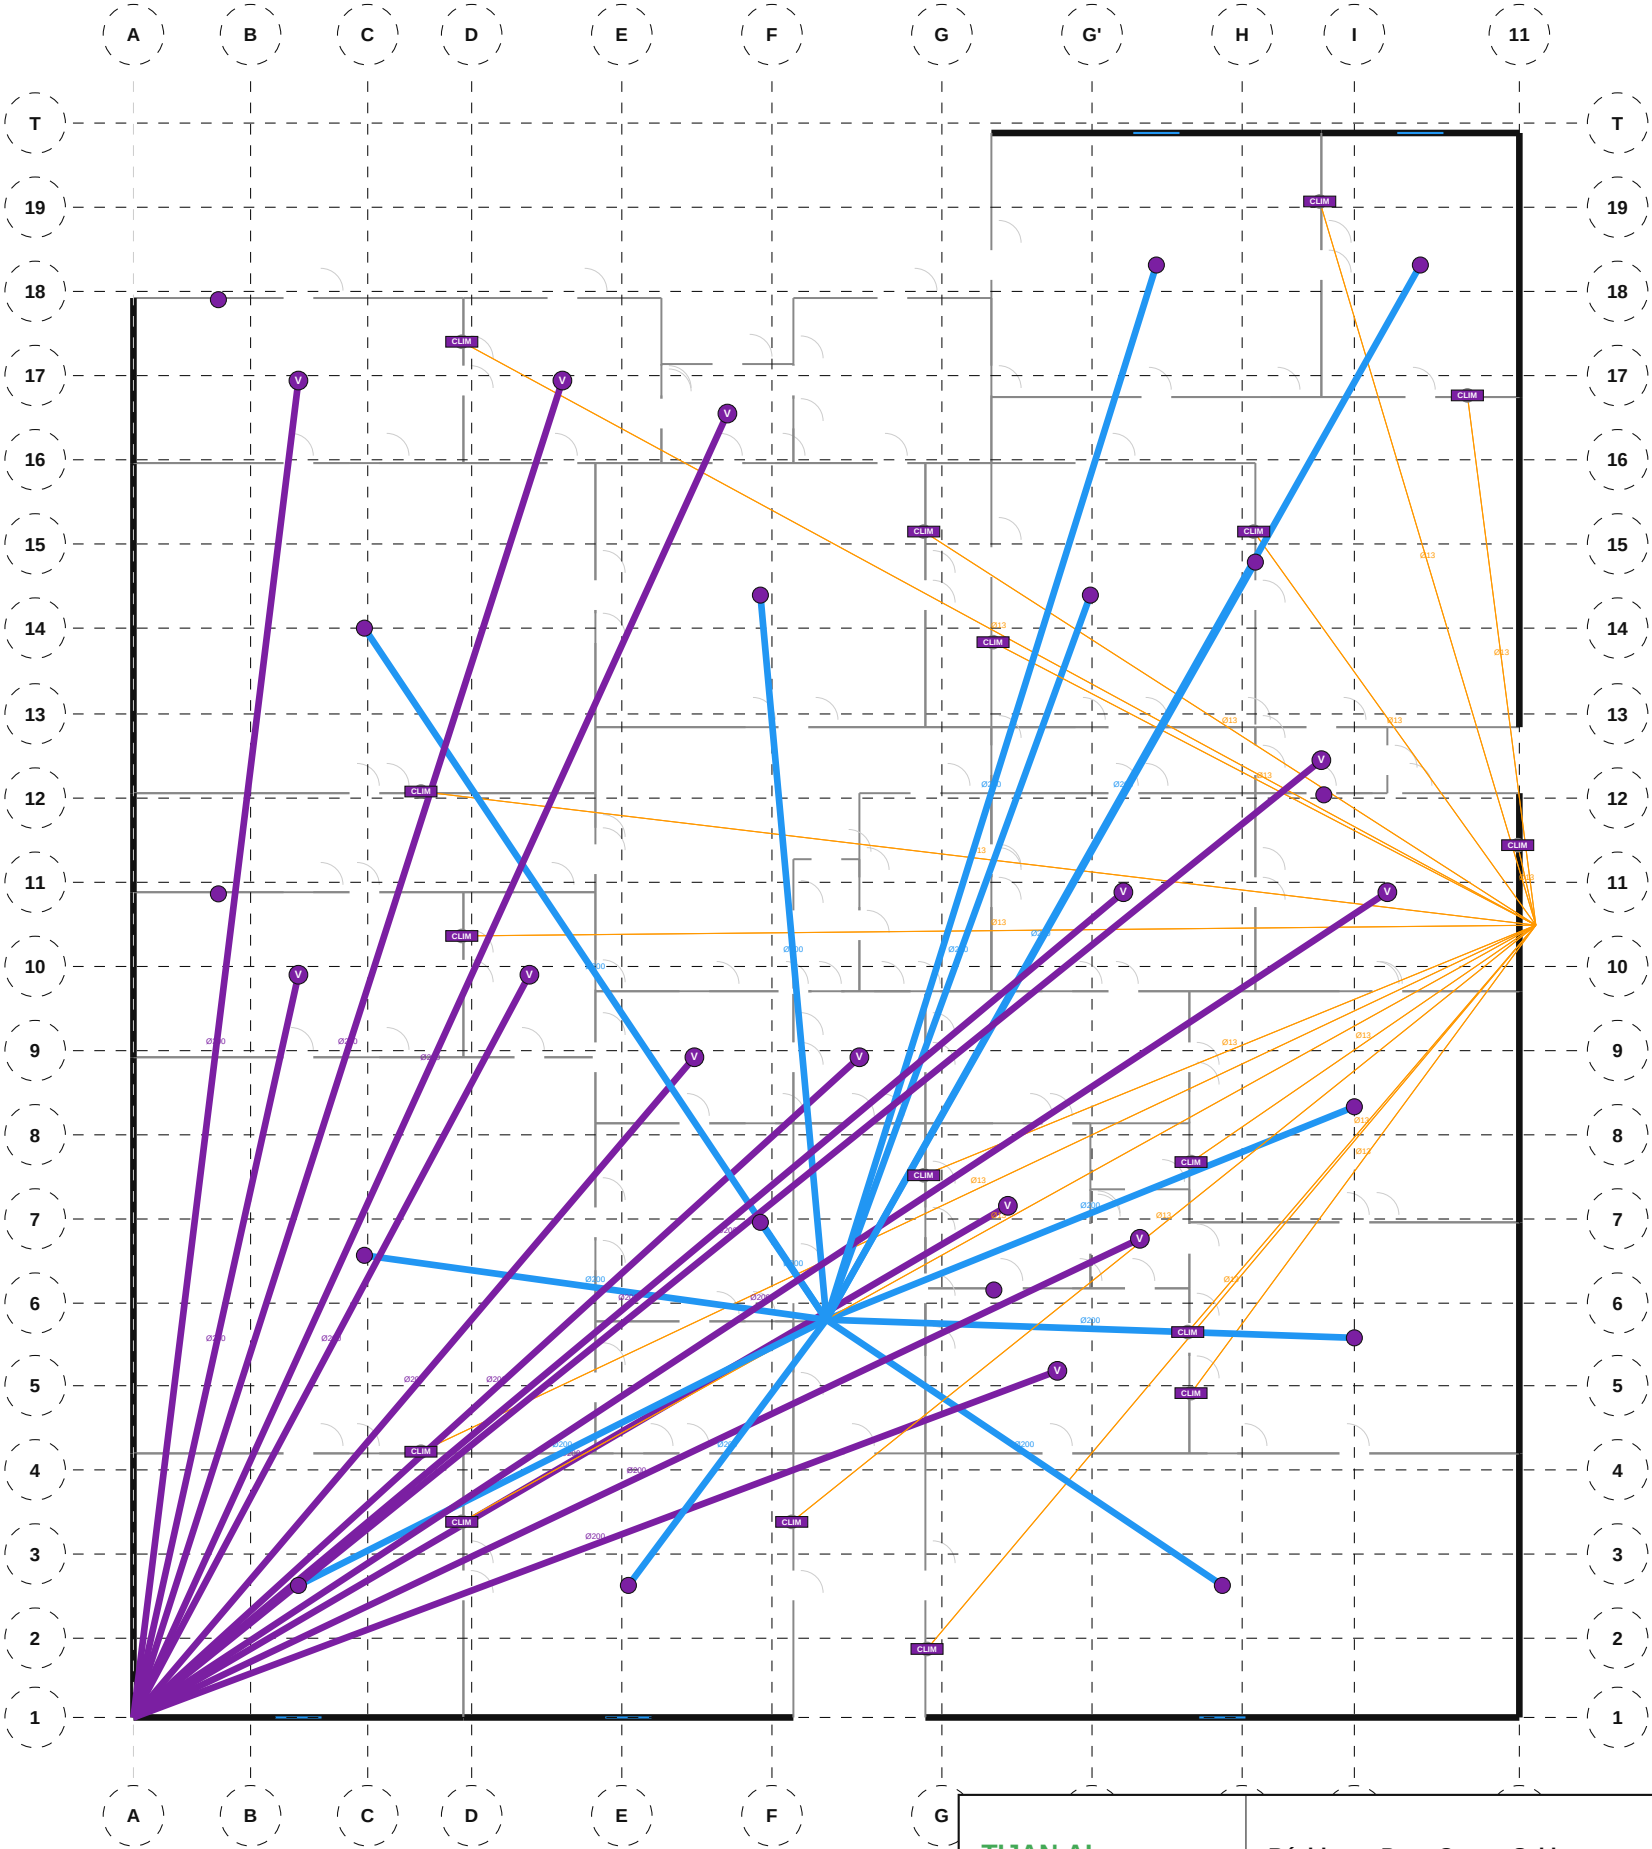

NOMENCLATURE — CVC / Ventilation

- Bouche VMC extraction: 13
- Grille soufflage: 13
- Hotte aspirante: 4
- Split climatiseur: 17


TIJAN AI Bureau d'Études Automatisé	Résidence Papa Oumar Sakho Dakar, Senegal	Éch: 1/100 Pl. 49/88
	CVC / Ventilation — Étage 3	
Date: 06/05/2026	Réf: 1711	BIM vHVC-049 Phase: APD

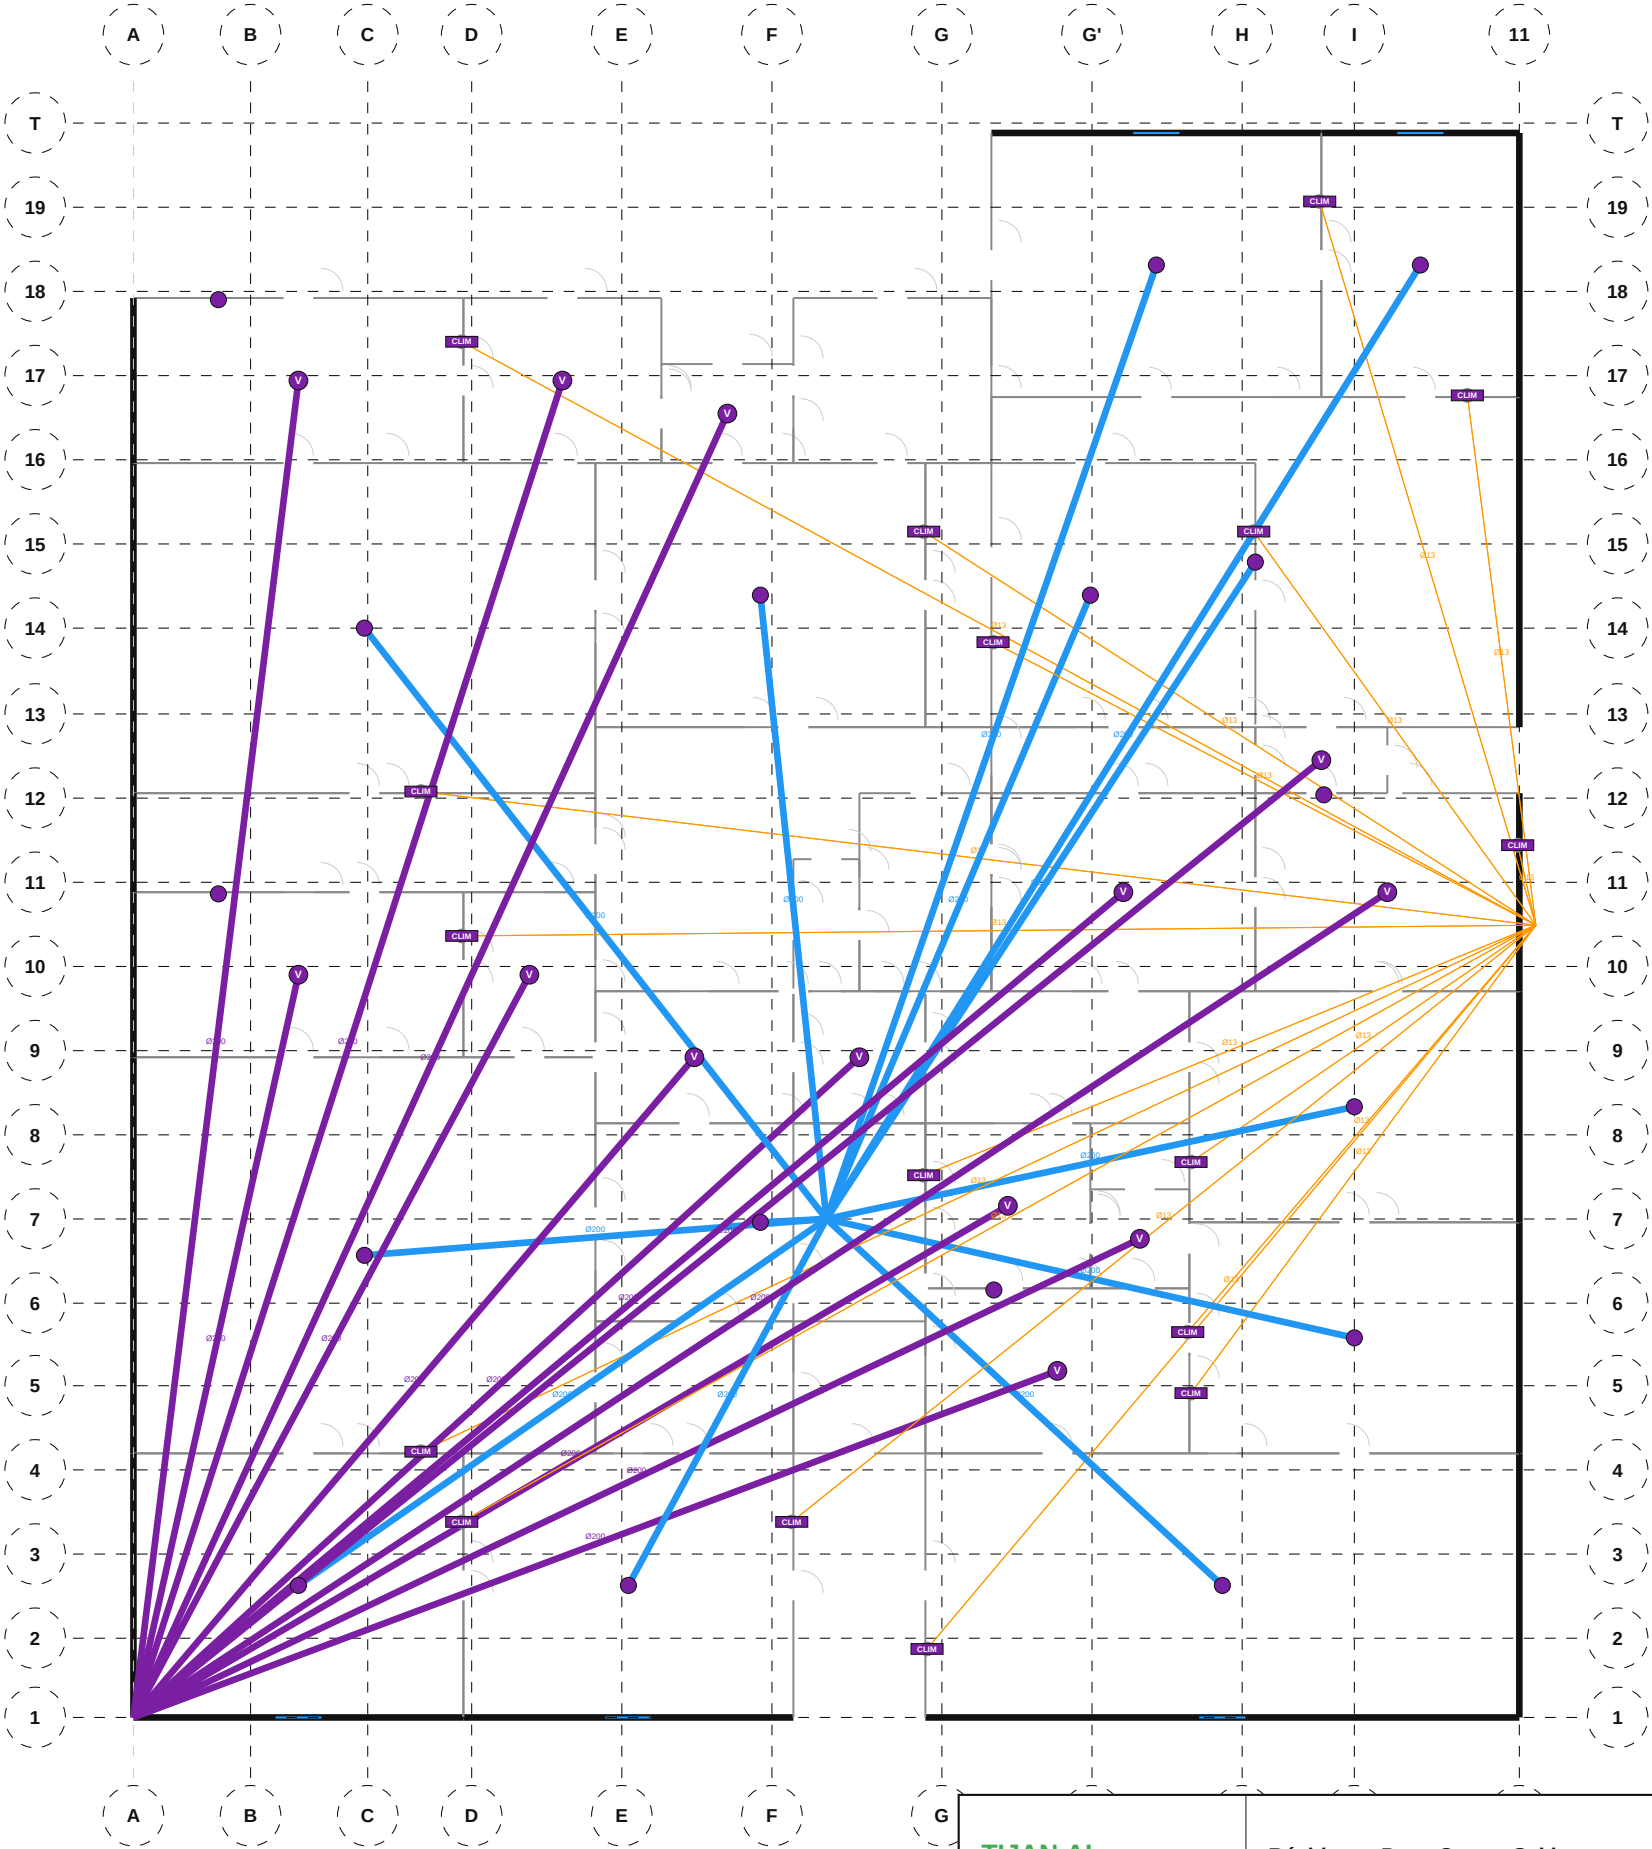

NOMENCLATURE — CVC / Ventilation

- Bouche VMC extraction: 13
- Grille soufflage: 13
- Hotte aspirante: 4
- Split climatiseur: 17


TIJAN AI Bureau d'Études Automatisé	Résidence Papa Oumar Sakho Dakar, Senegal	Éch: 1/100 Pl. 50/88
	CVC / Ventilation — Étage 4	
Date: 06/05/2026	Réf: 1711	BIM vHVC-050 Phase: APD

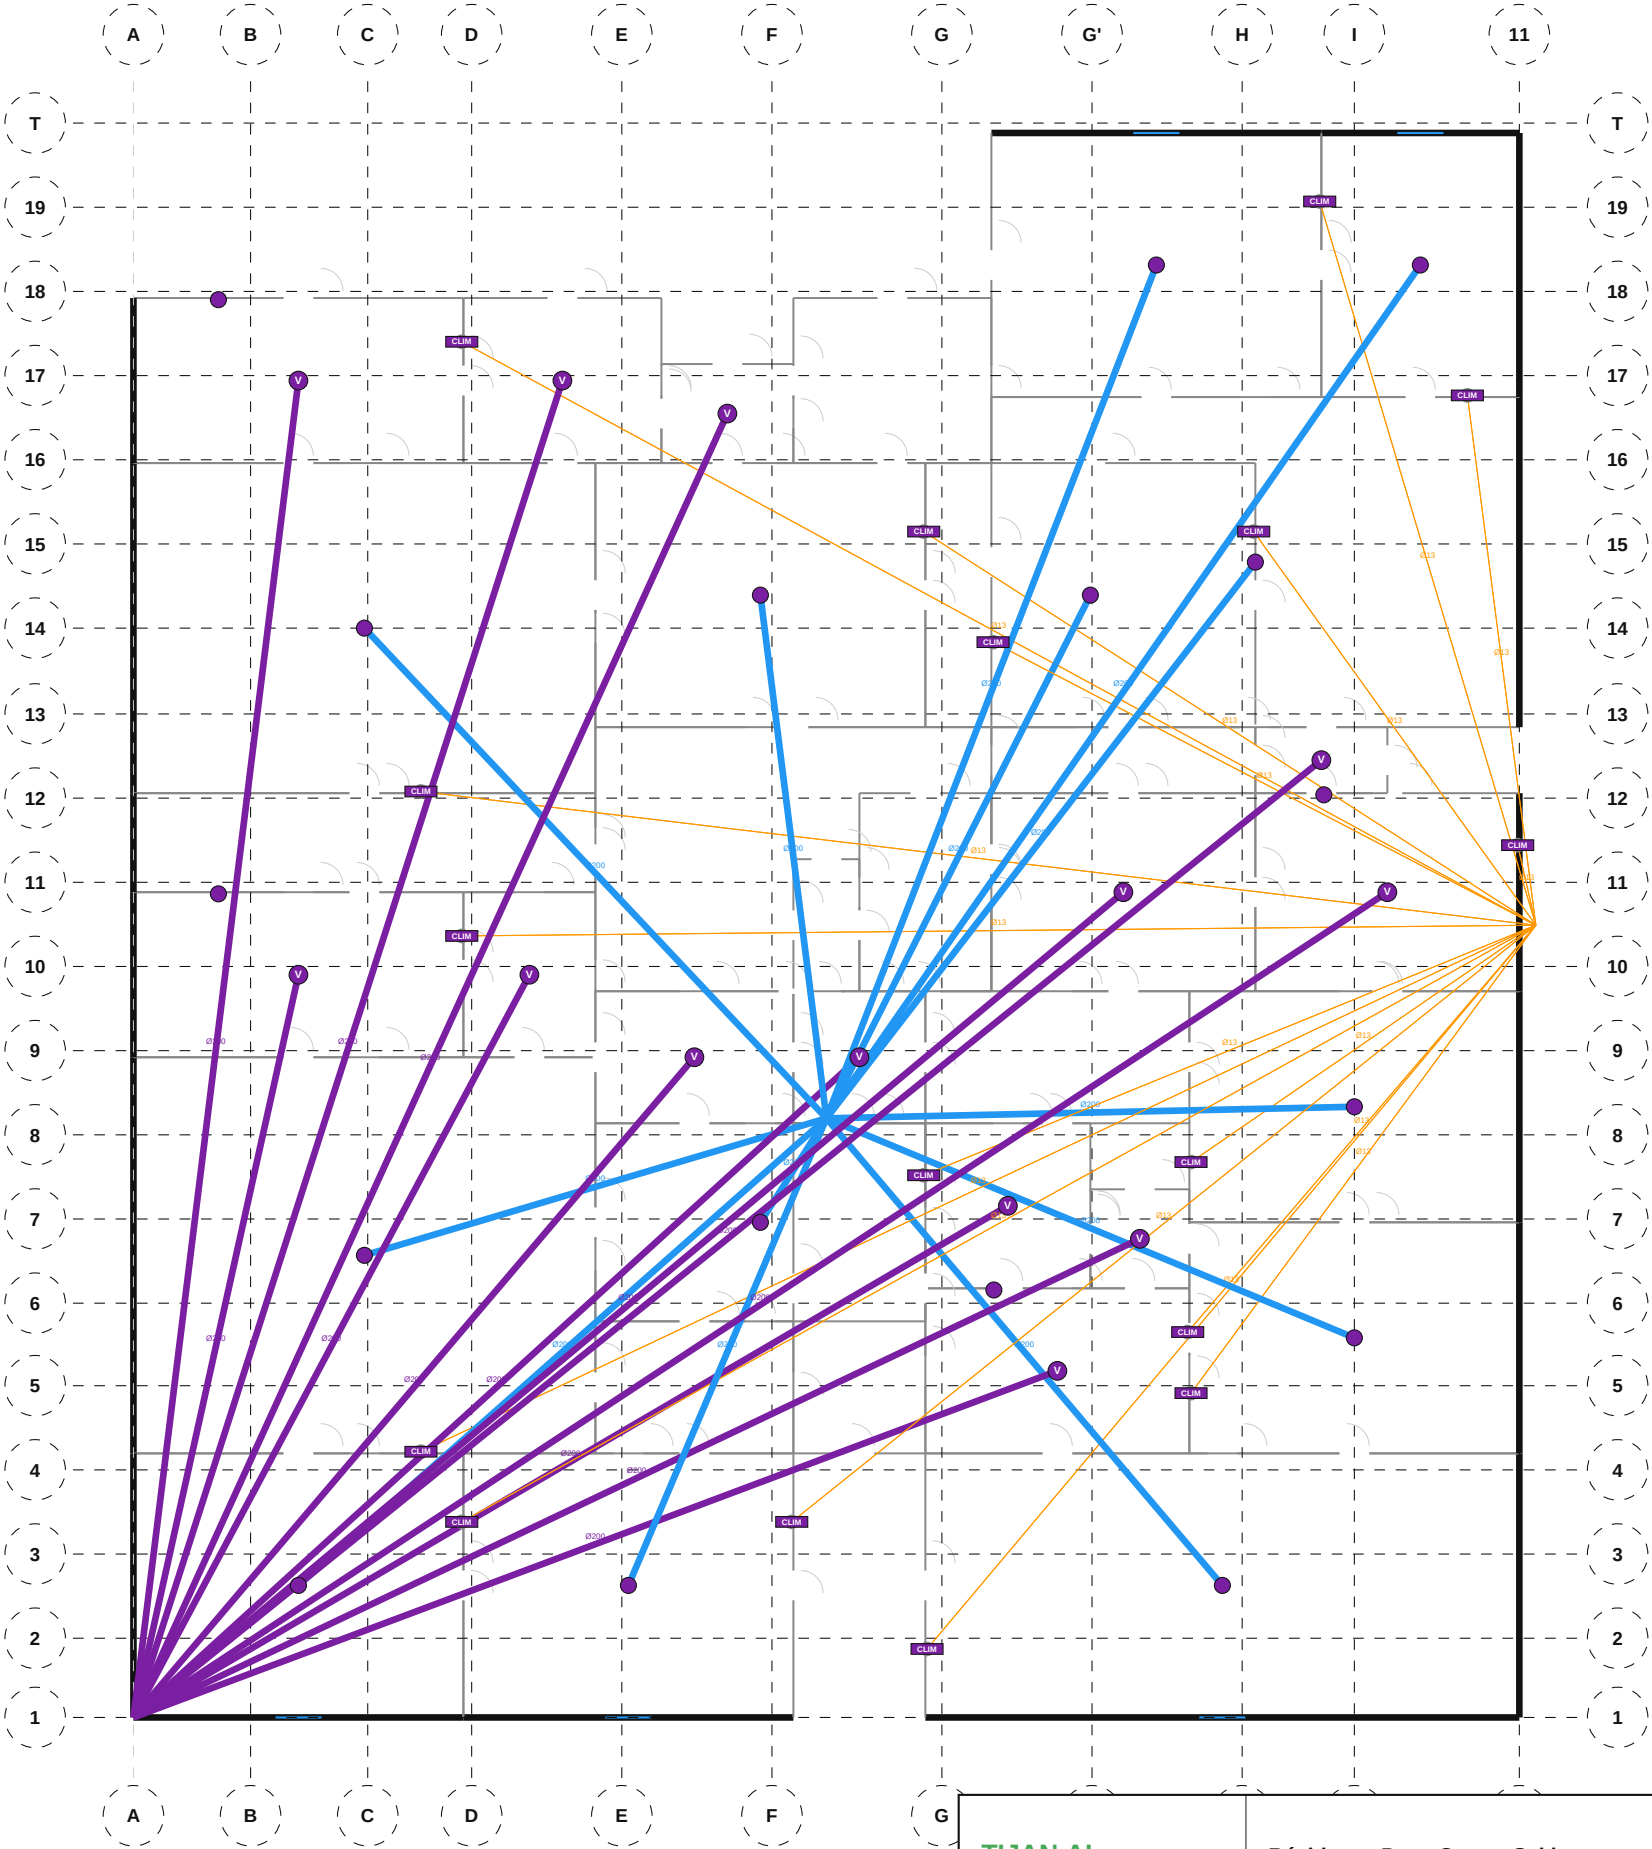

NOMENCLATURE — CVC / Ventilation

- Bouche VMC extraction: 13
- Grille soufflage: 13
- Hotte aspirante: 4
- Split climatiseur: 17


TIJAN AI Bureau d'Études Automatisé	Résidence Papa Oumar Sakho Dakar, Senegal	Éch: 1/100 Pl. 51/88	
		CVC / Ventilation — Étage 5	
	Date: 06/05/2026	Réf: 1711	BIM vHVC-051 Phase: APD

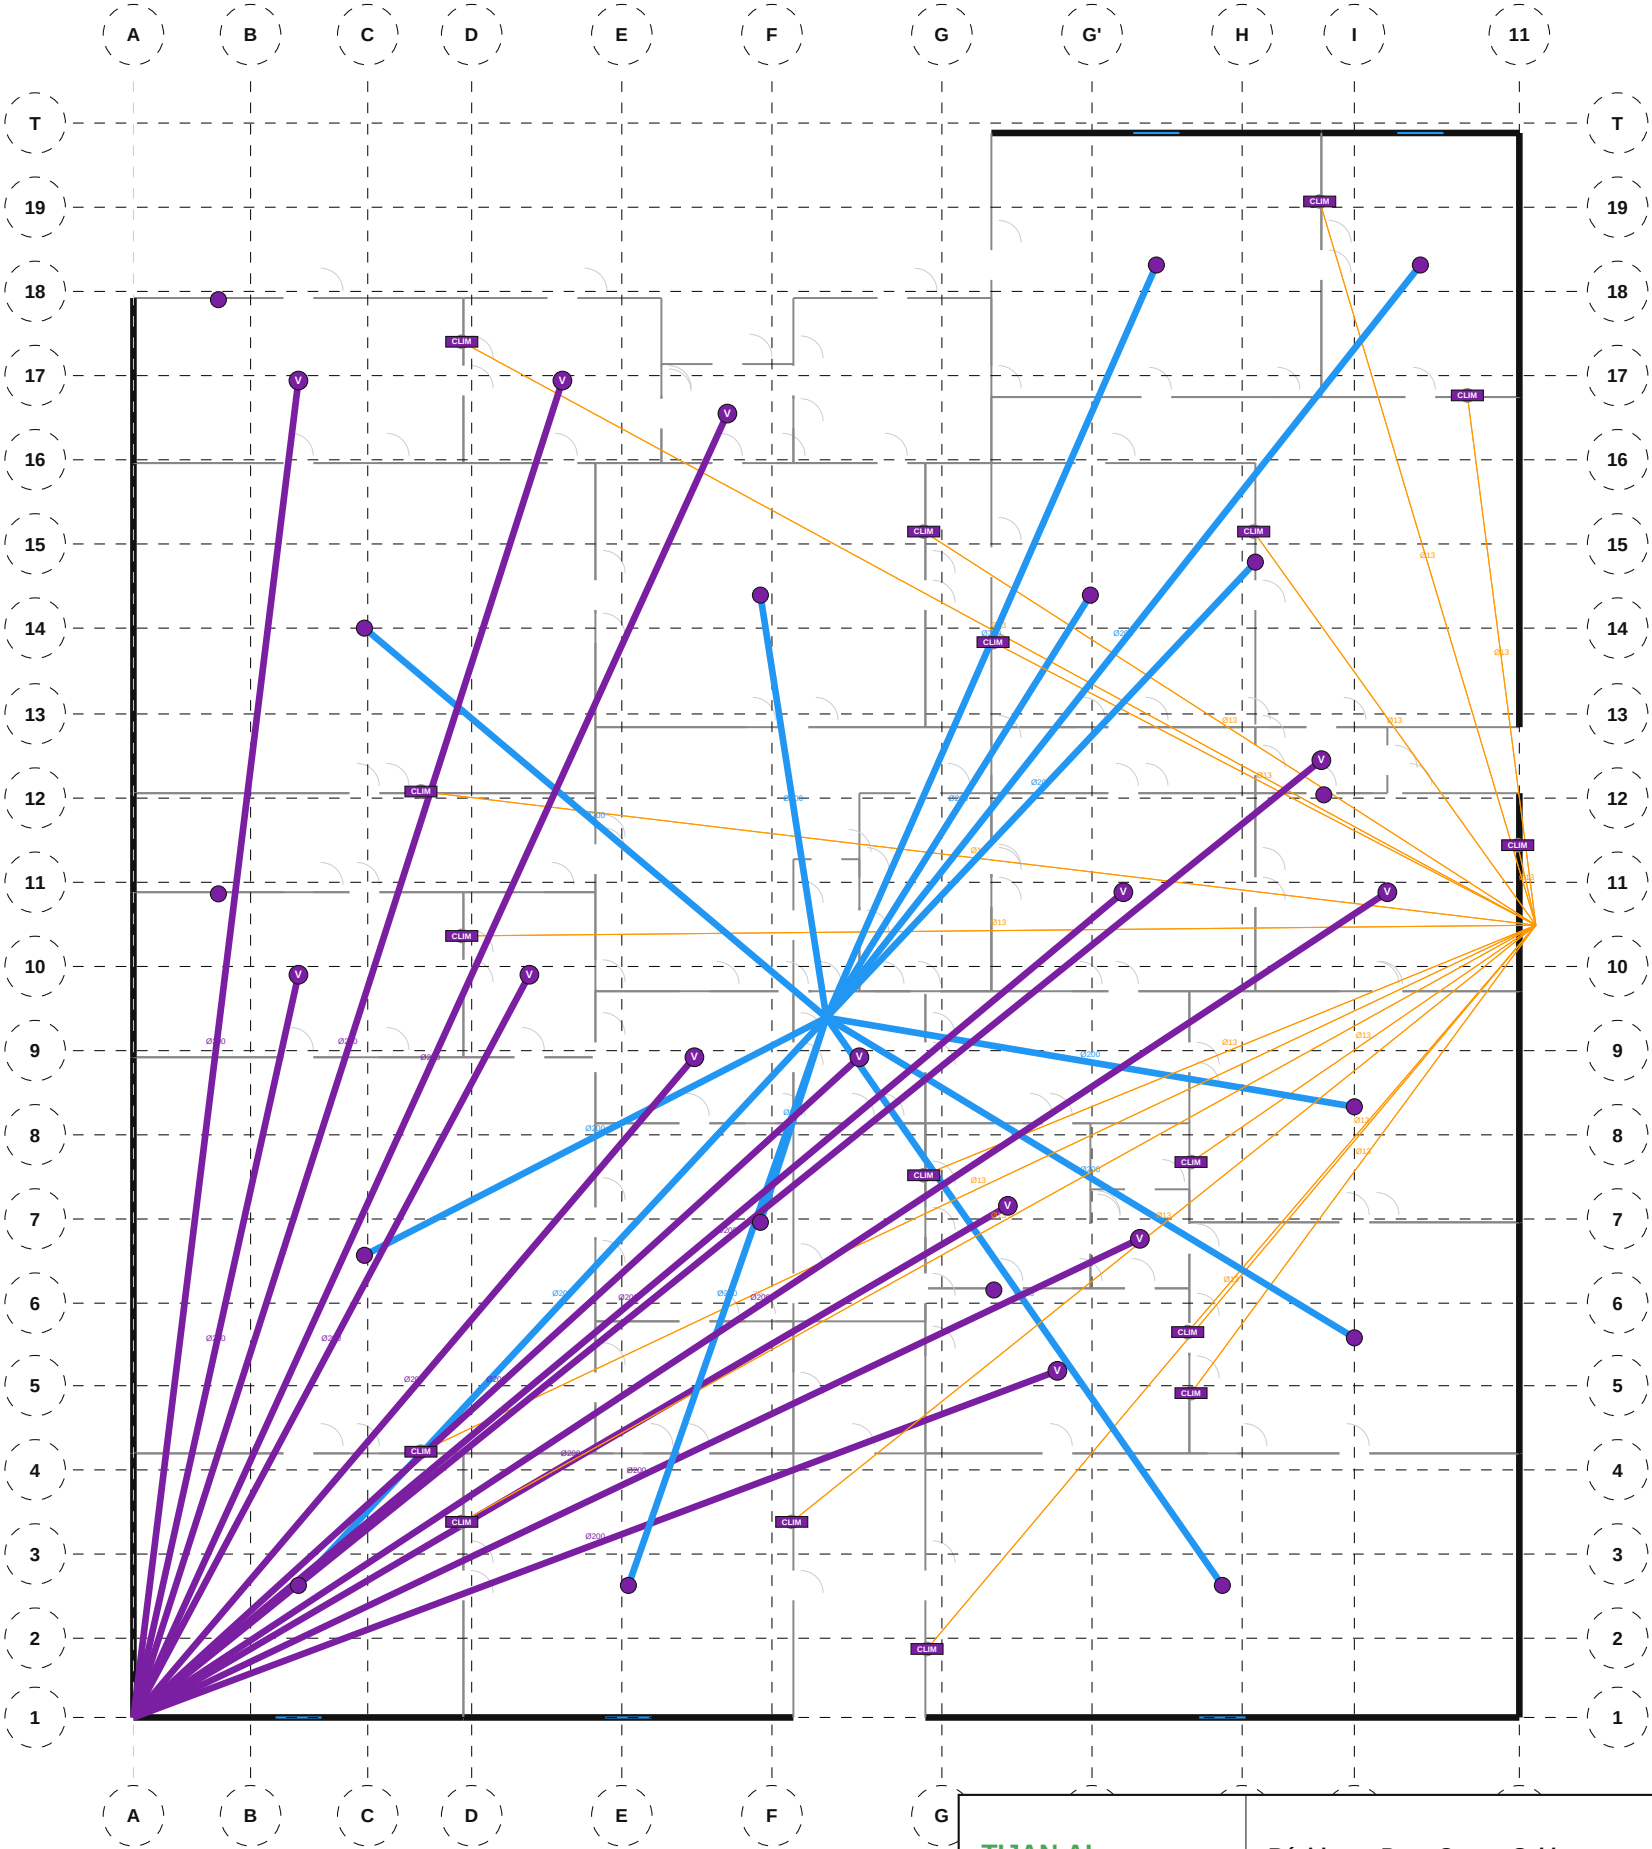

NOMENCLATURE — CVC / Ventilation

- Bouche VMC extraction: 13
- Grille soufflage: 13
- Hotte aspirante: 4
- Split climatiseur: 17


TIJAN AI Bureau d'Études Automatisé	Résidence Papa Oumar Sakho Dakar, Senegal	Éch: 1/100 Pl. 52/88
	CVC / Ventilation — Étage 6	
Date: 06/05/2026	Réf: 1711	BIM vHVC-052 Phase: APD

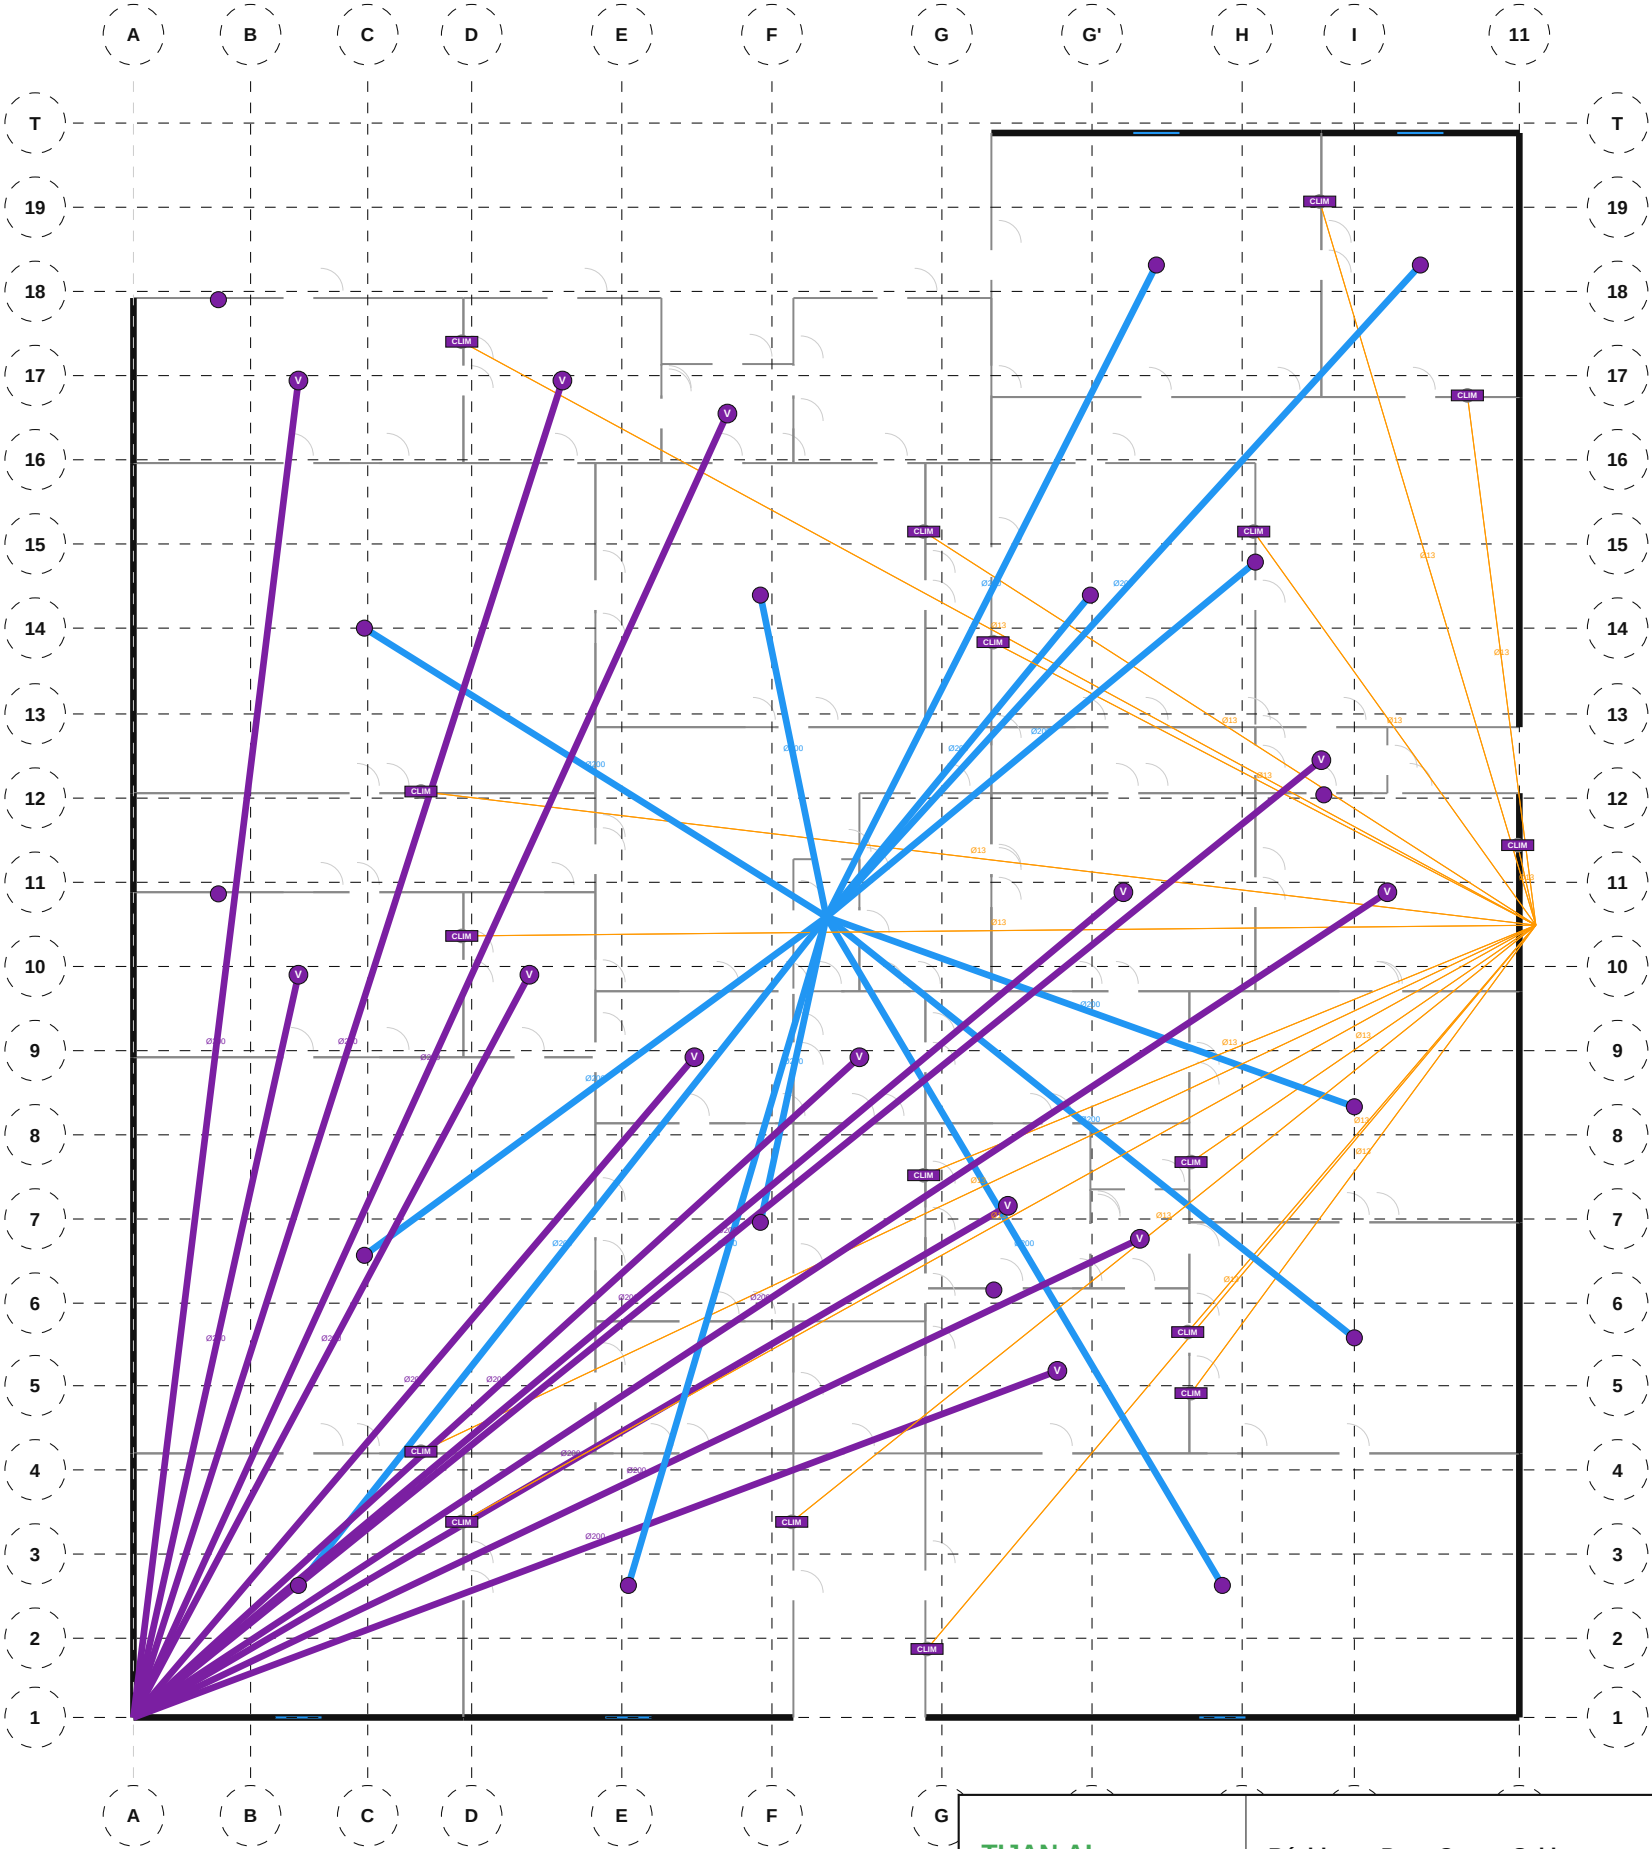

NOMENCLATURE — CVC / Ventilation

- Bouche VMC extraction: 13
- Grille soufflage: 13
- Hotte aspirante: 4
- Split climatiseur: 17


TIJAN AI Bureau d'Études Automatisé	Résidence Papa Oumar Sakho Dakar, Senegal	Éch: 1/100 Pl. 53/88
	CVC / Ventilation — Étage 7	
Date: 06/05/2026	Réf: 1711	BIM vHVC-053 Phase: APD

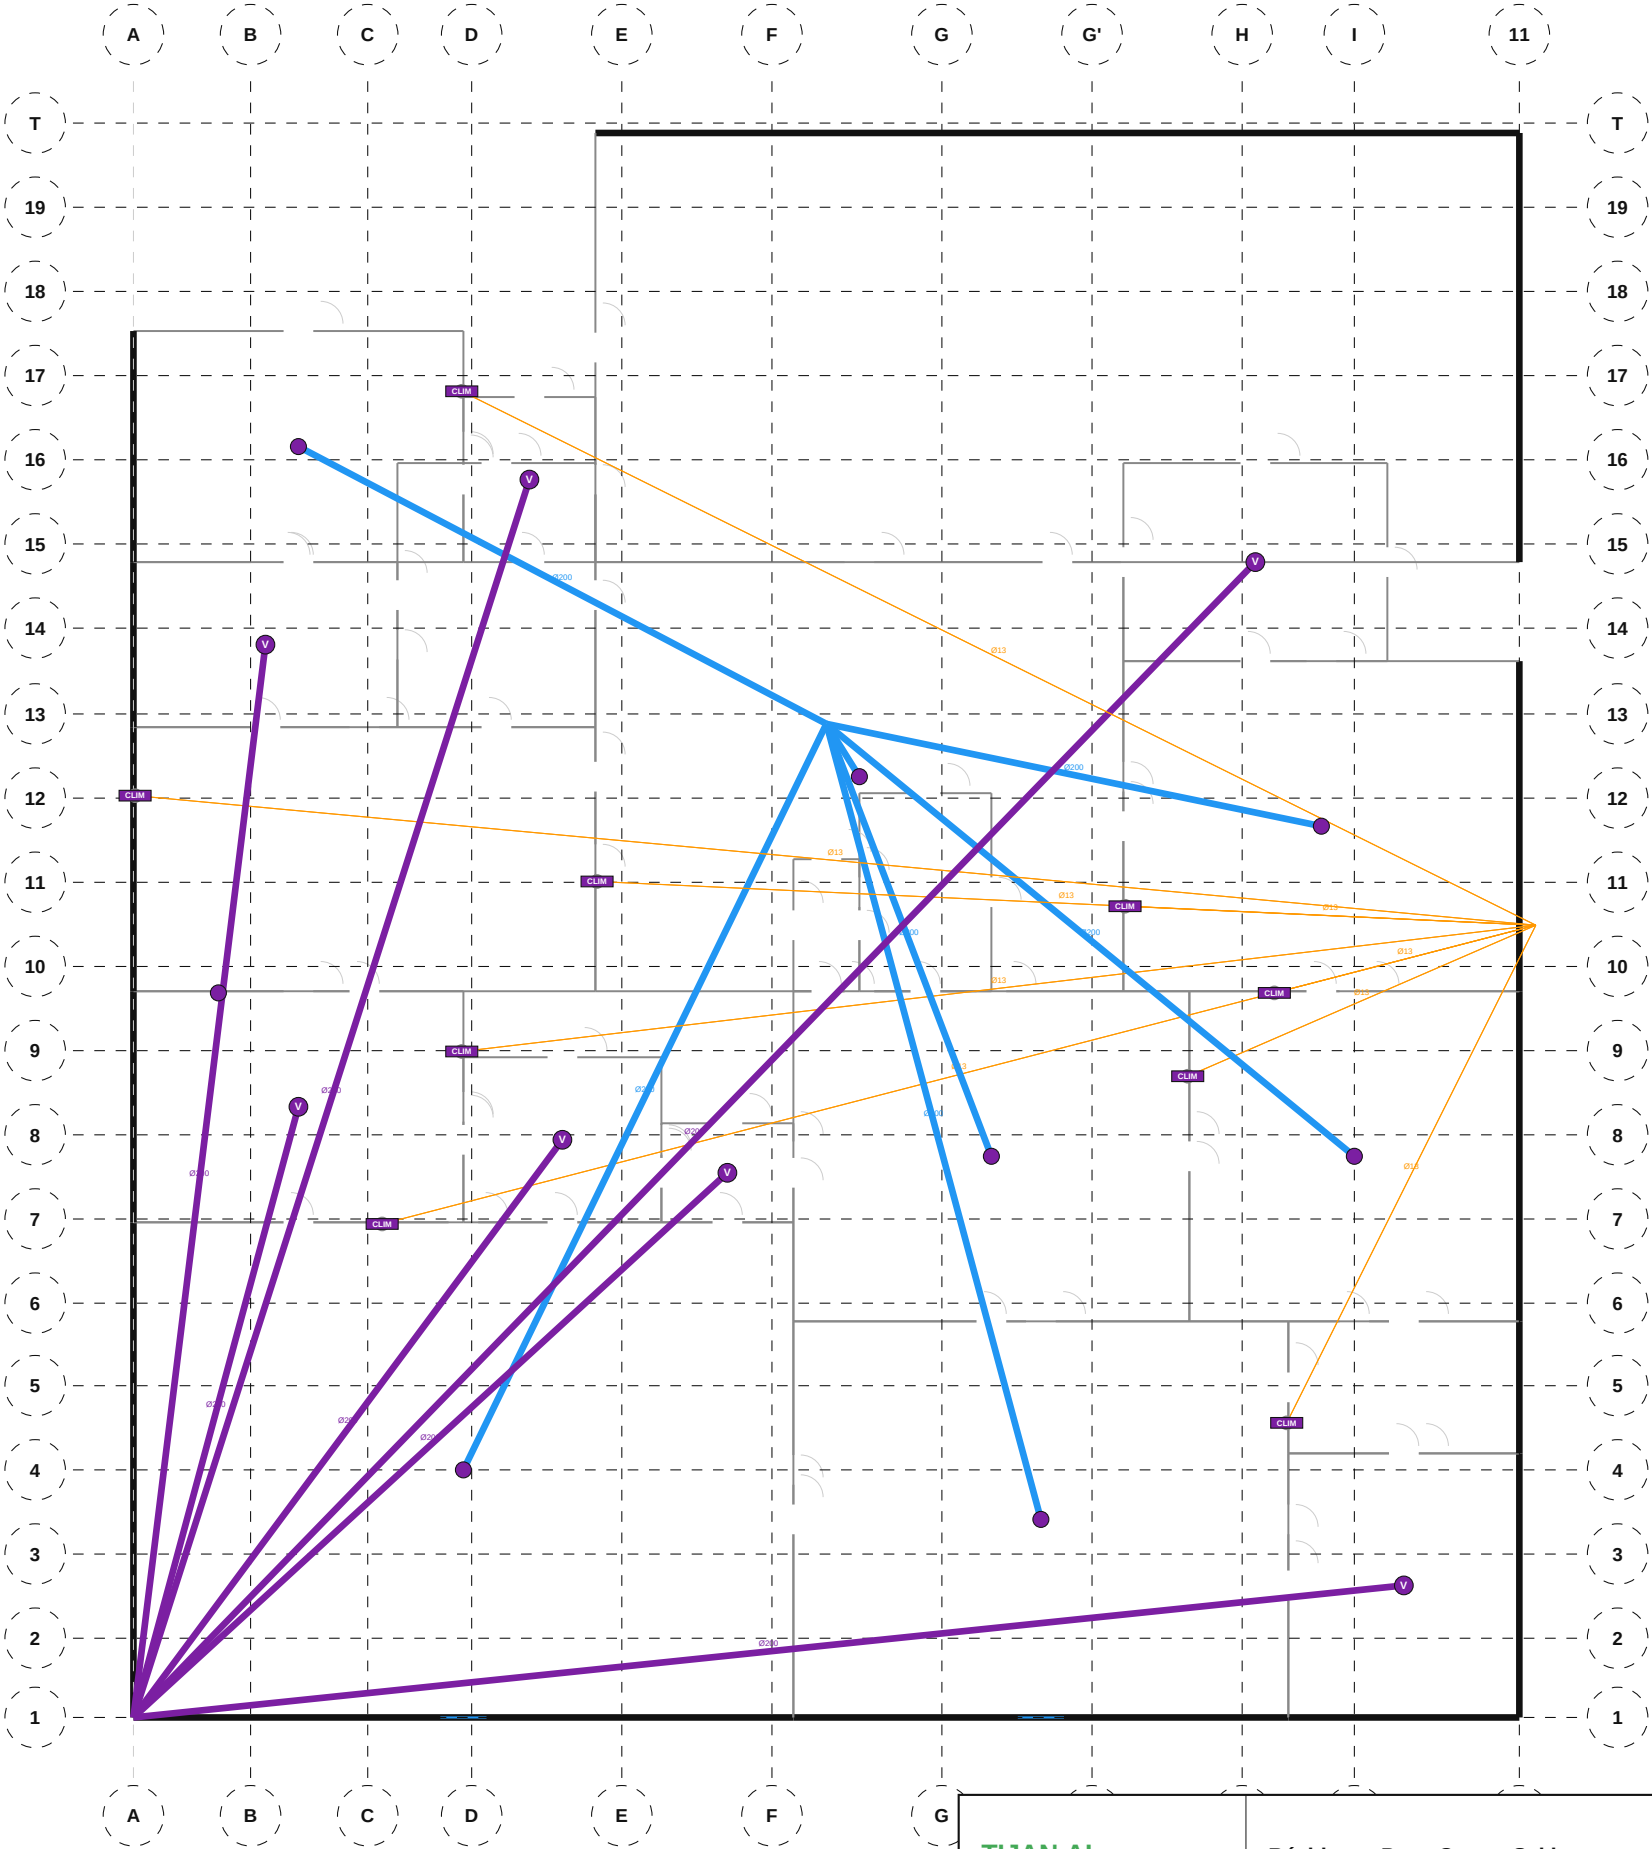

NOMENCLATURE — CVC / Ventilation

- Bouche VMC extraction: 7
- Grille soufflage: 7
- Hotte aspirante: 1
- Split climatiseur: 9

TIJAN AI Bureau d'Études Automatisé	Résidence Papa Oumar Sakho Dakar, Senegal	Éch: 1/100 Pl. 54/88
	CVC / Ventilation — Étage 8	
Date: 06/05/2026	Réf: 1711	BIM vHVC-054 Phase: APD

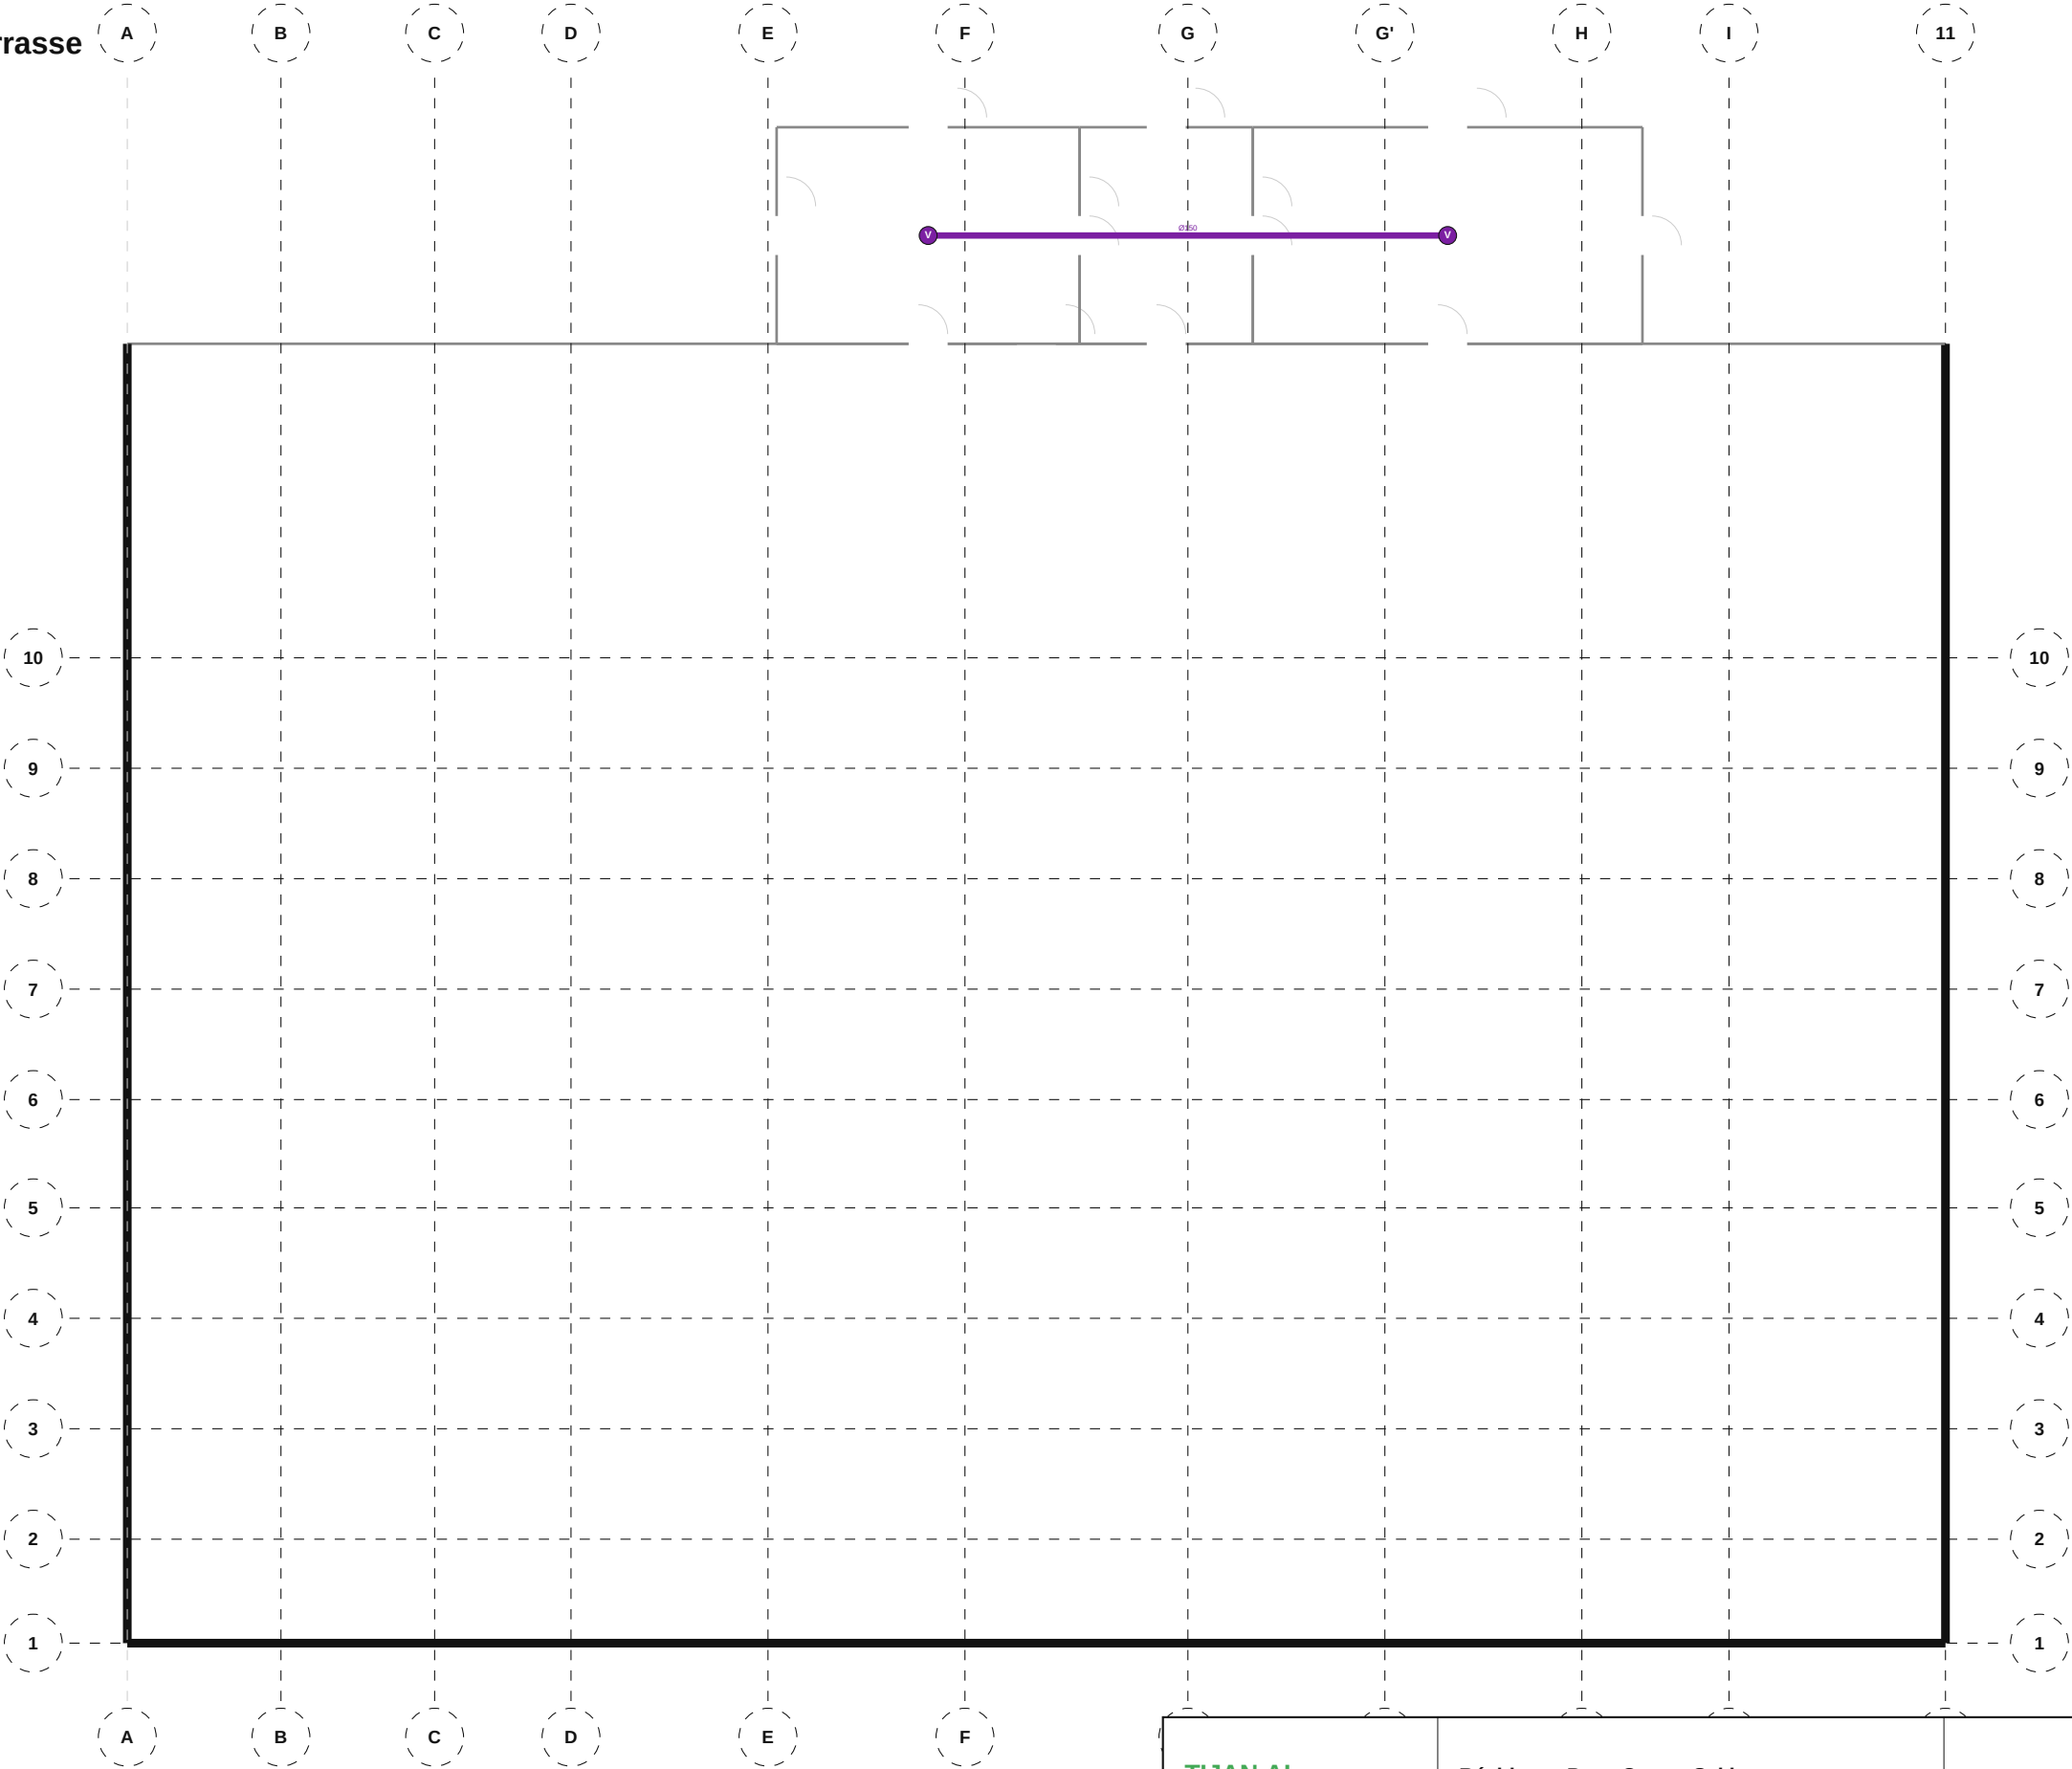


NOMENCLATURE — CVC / Ventilation

• Bouche VMC: 2

TIJAN AI Bureau d'Études Automatisé	Résidence Papa Oumar Sakho Dakar, Senegal	Éch: 1/100 Pl. 55/88
	CVC / Ventilation — Terrasse	
Date: 06/05/2026	Réf: 1711	BIM vHVC-055 Phase: APD

510 Courants Forts — Sous-Sol

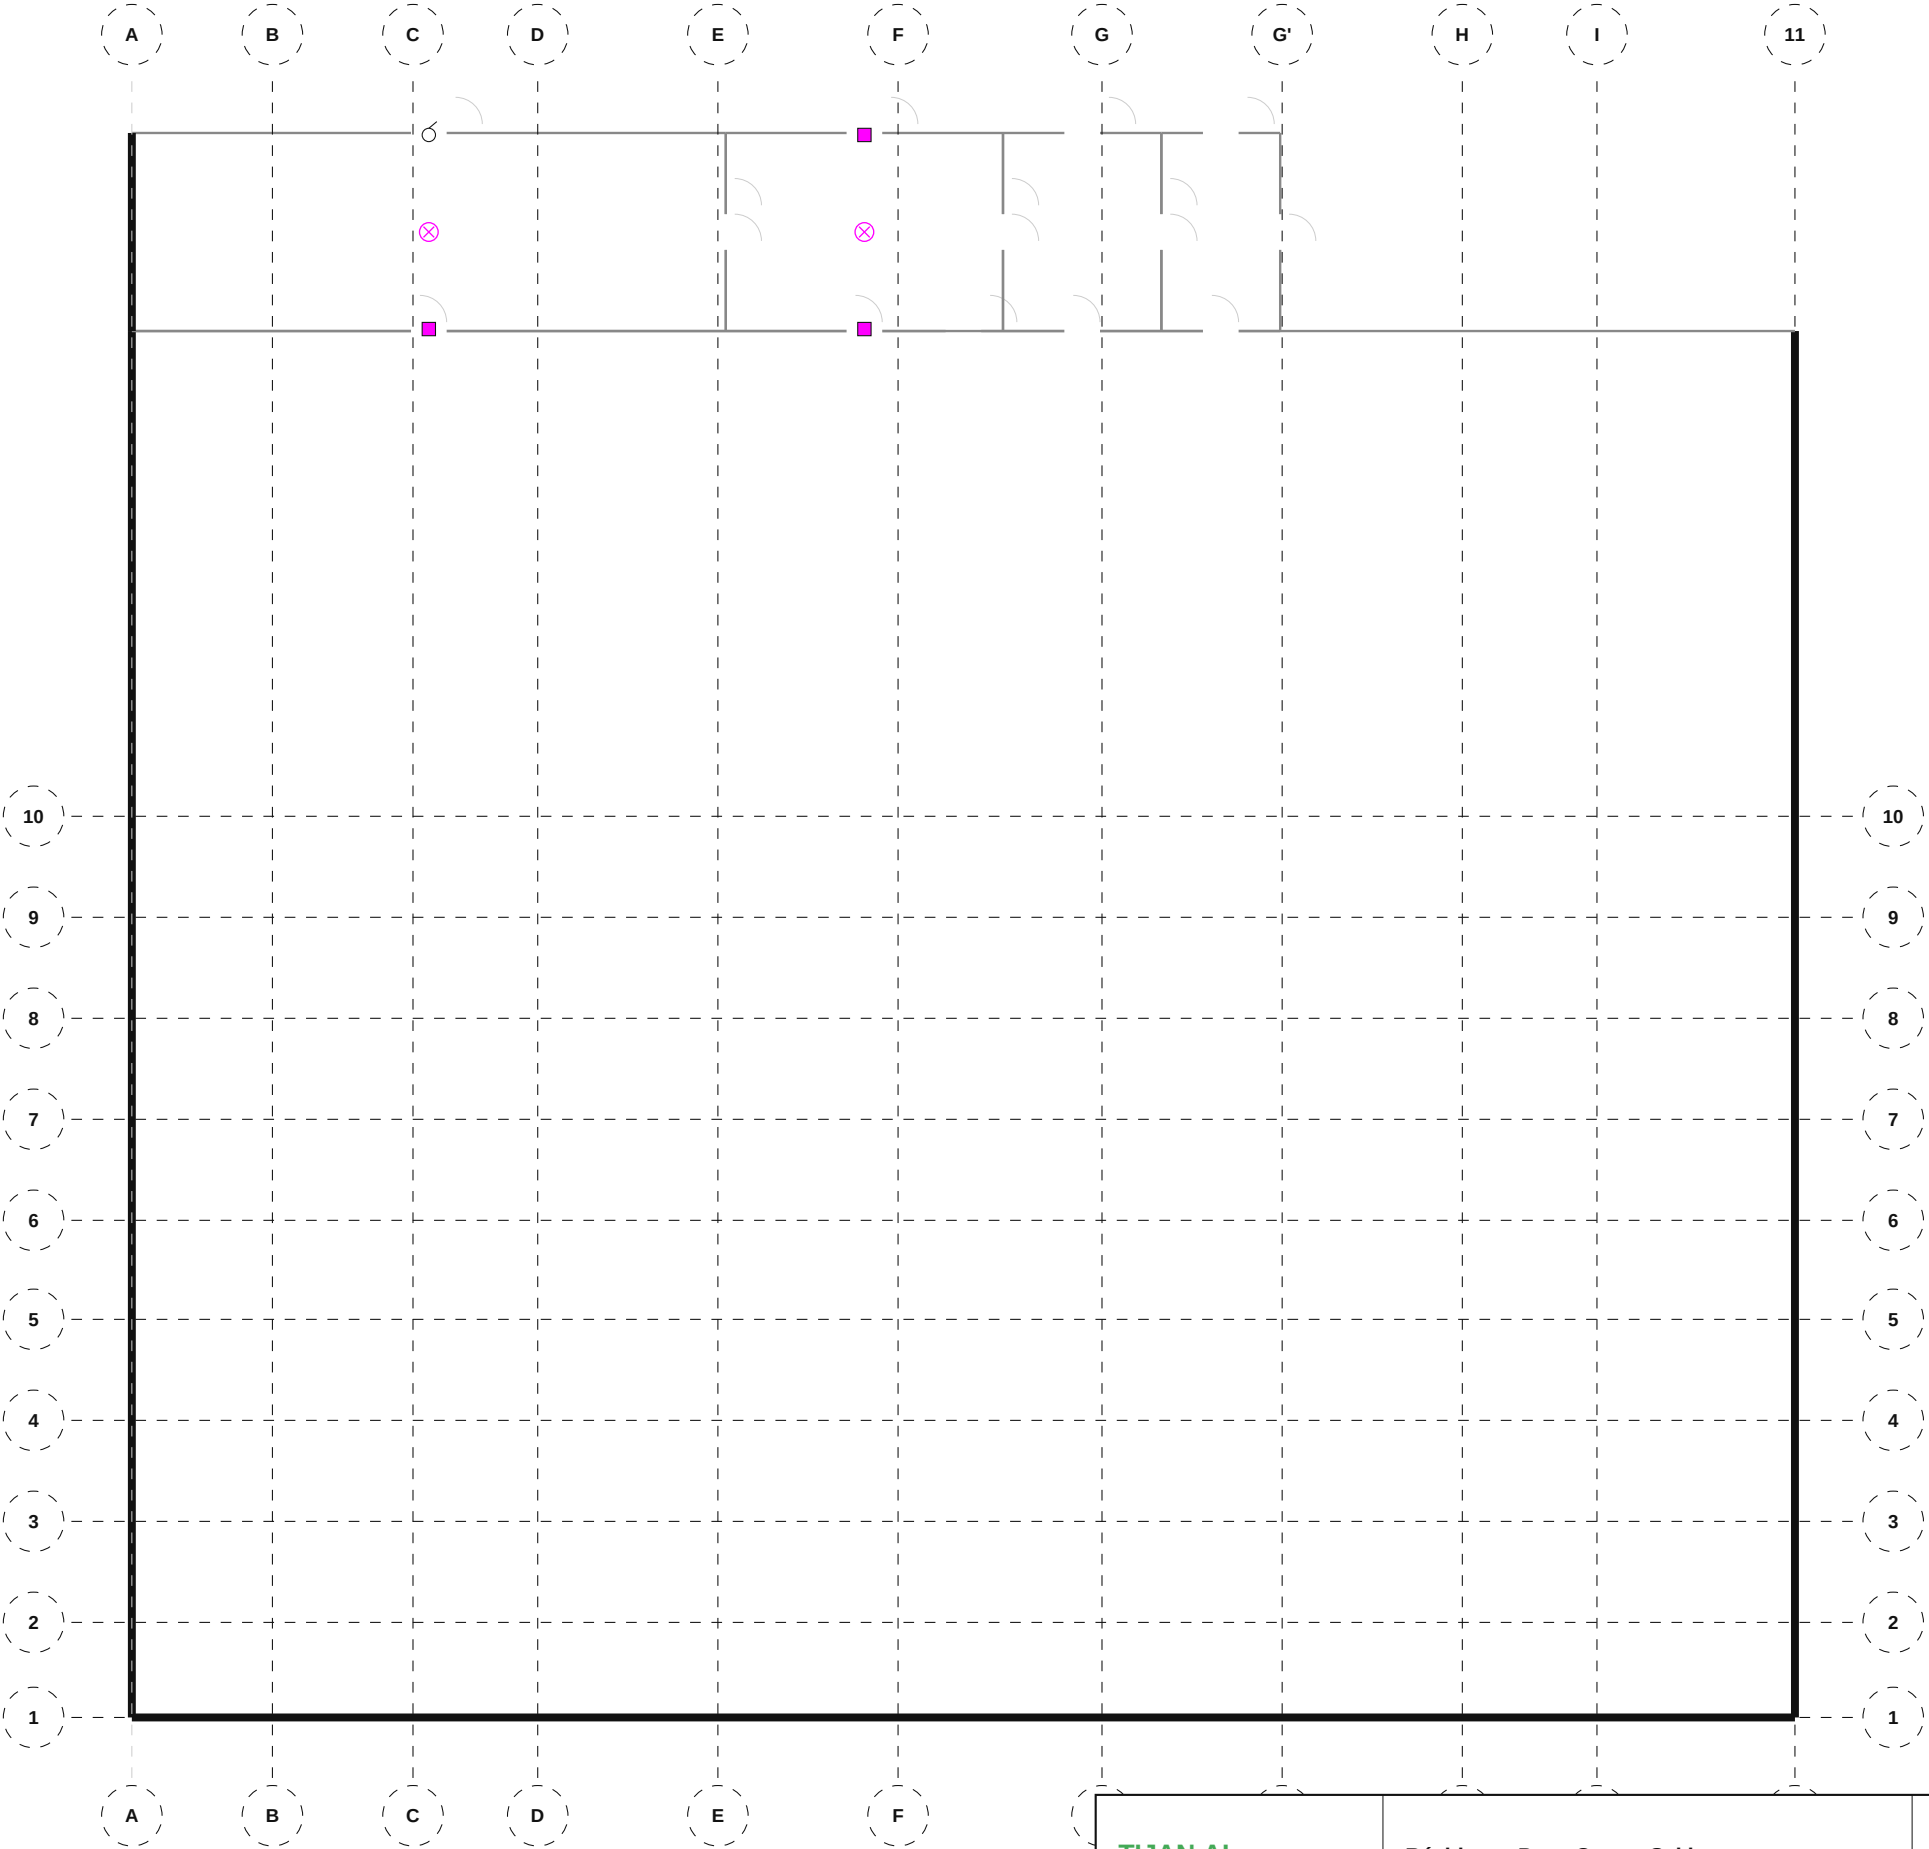


TIJAN AI Bureau d'Études Automatisé	Résidence Papa Oumar Sakho Dakar, Senegal	Éch: 1/100 Pl. 56/88
	Courants Forts — Sous-Sol	
Date: 06/05/2026	Réf: 1711	BIM vHCU-056 Phase: APD

510 Courants Forts — RDC


NOMENCLATURE — Courants Forts

- Applique miroir: 2
- Applique tête de lit: 2
- Interrupteur: 6
- Interrupteur va-et-vient: 8
- Plafonnier: 12
- Plafonnier IP44: 1
- Prise 2P+T: 1
- Prise 2P+T 16A: 25
- Prise plan de travail: 4
- Prise étanche 2P+T: 1
- Tableau électrique: 1

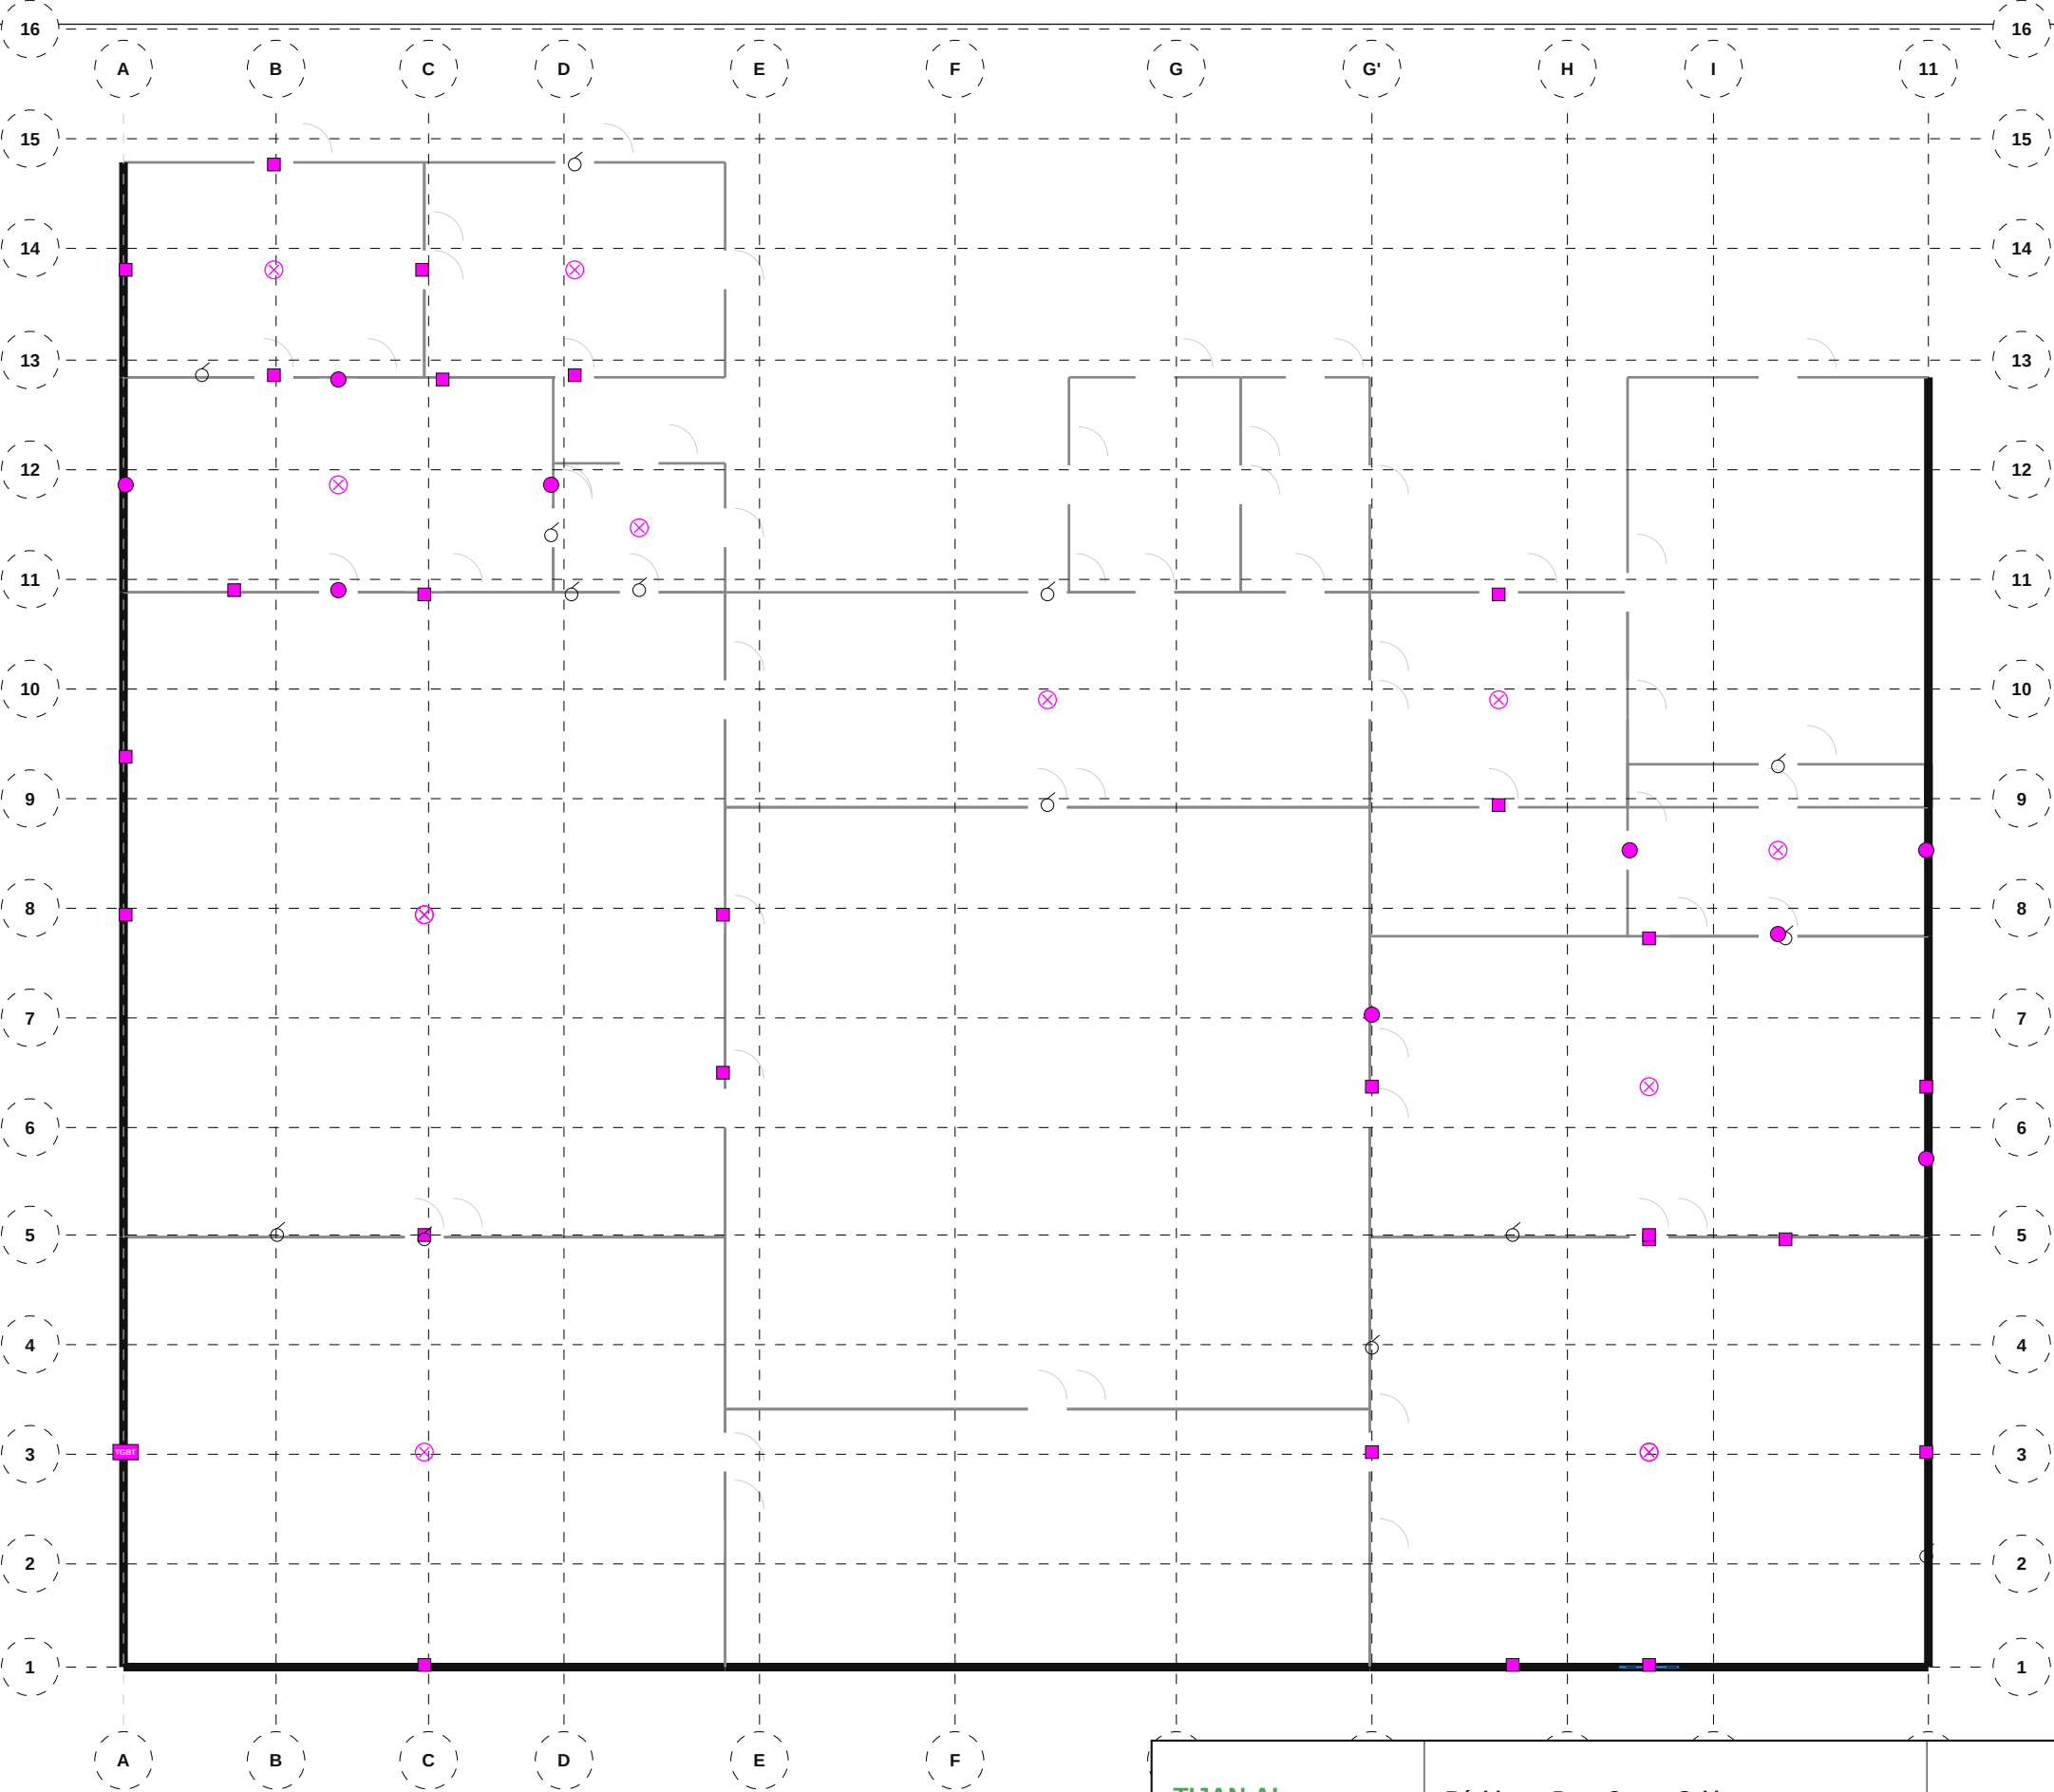

TIJAN AI Bureau d'Études Automatisé	Résidence Papa Oumar Sakho Dakar, Senegal	Éch: 1/100 Pl: 57/88
	Courants Forts — RDC	
Date: 06/05/2026	Réf: 1711	BIM vHCU-057 Phase: APD


510 Courants Forts — Étage 1

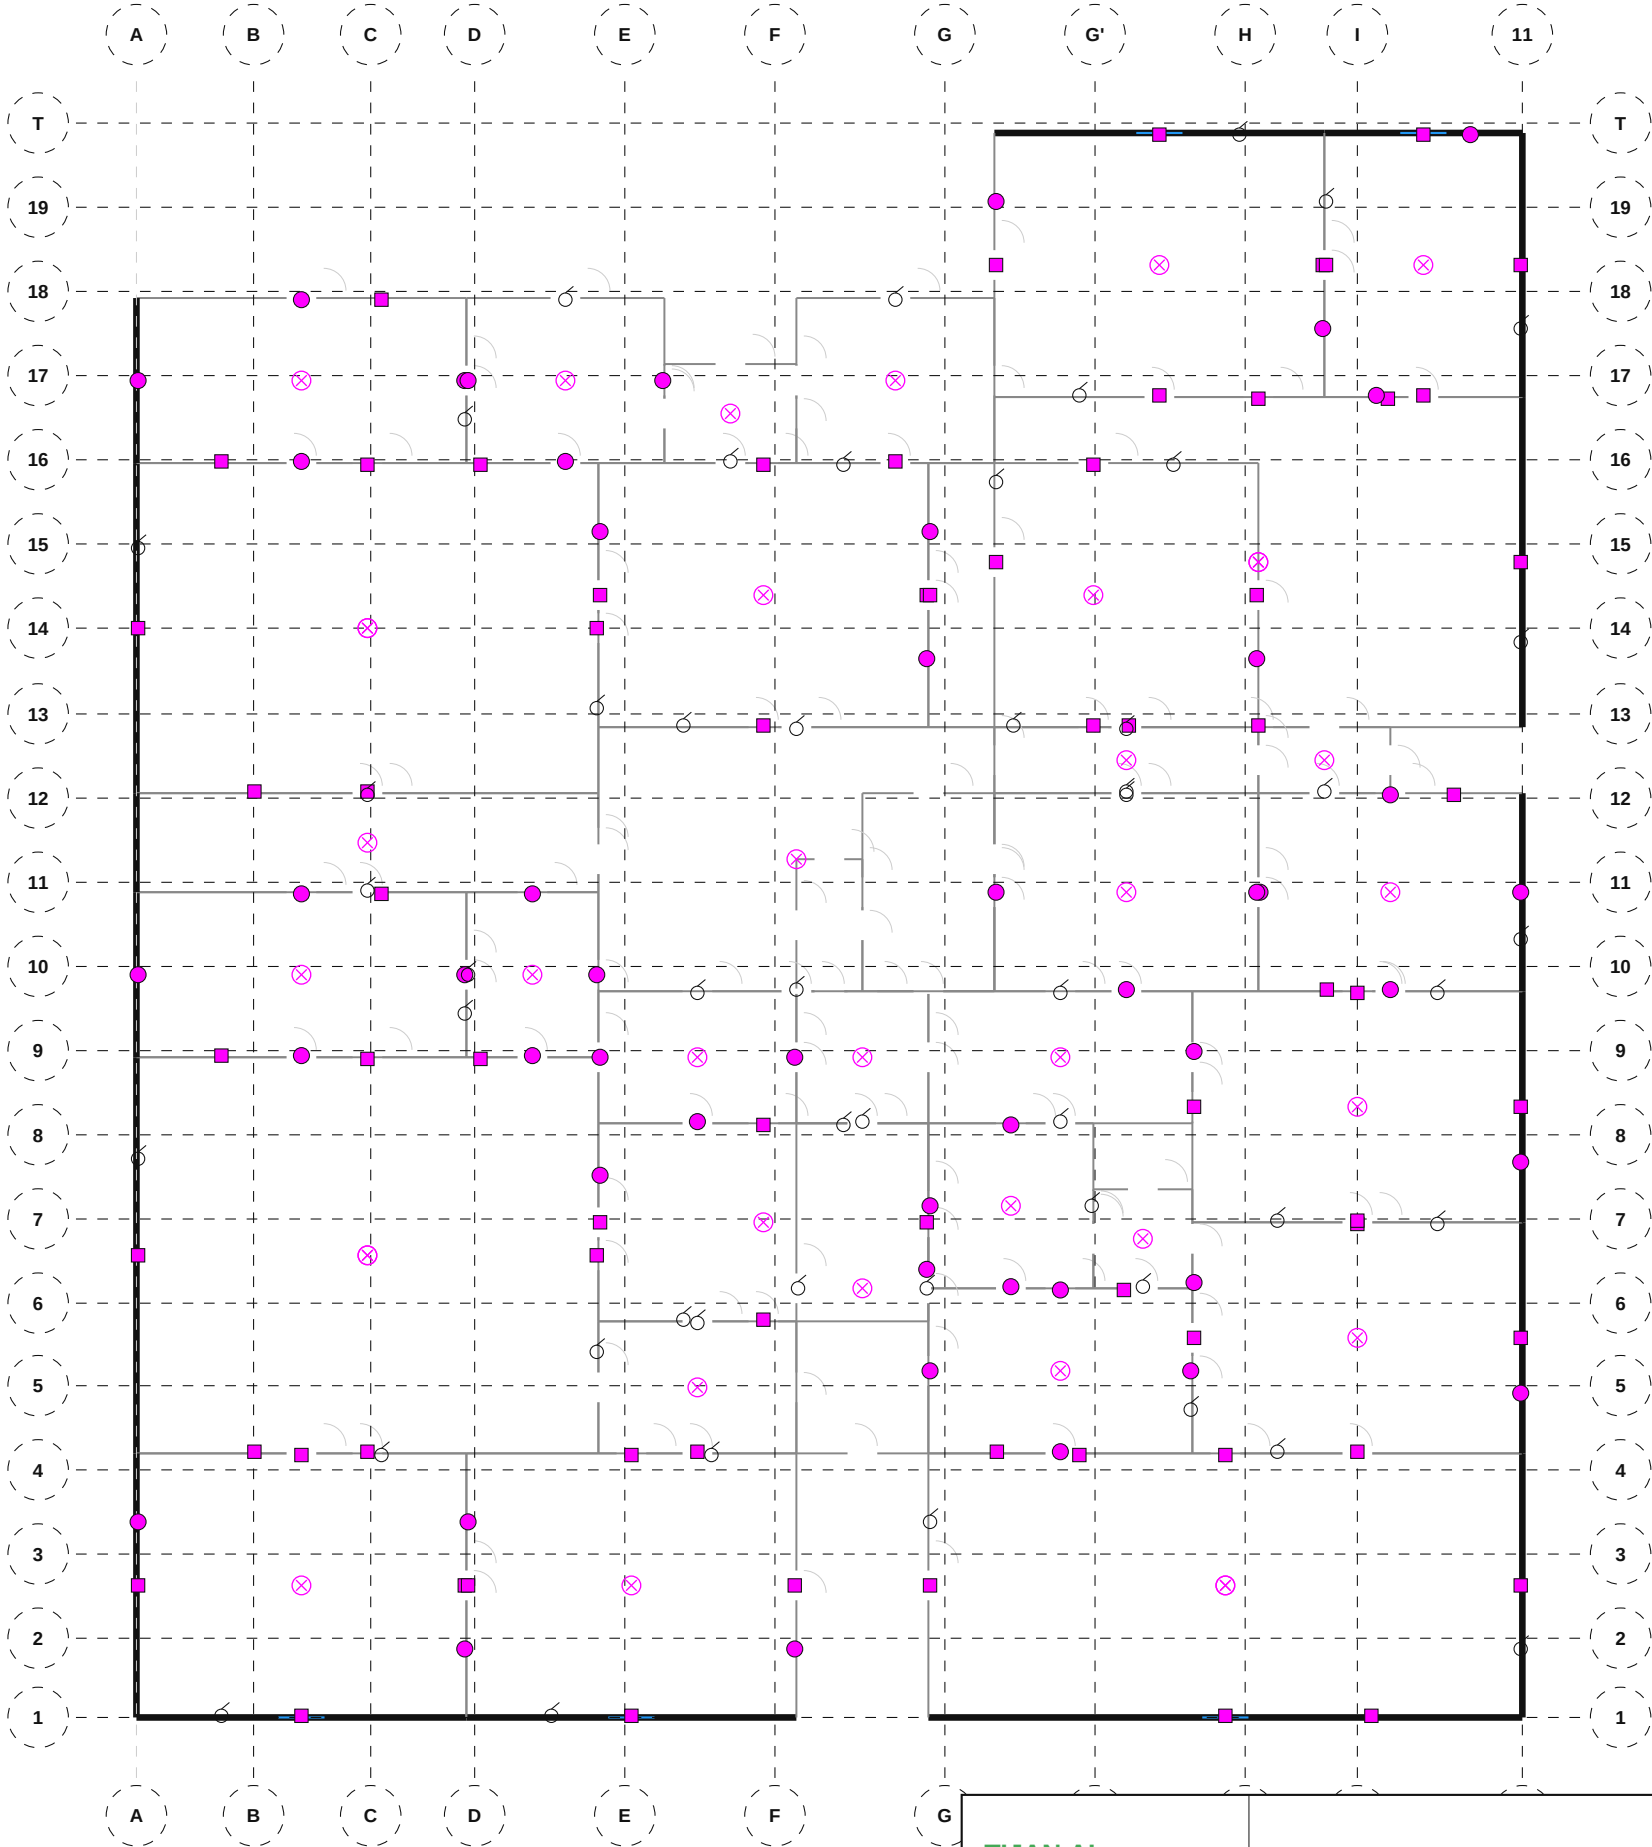

NOMENCLATURE — Courants Forts

- Applique miroir: 10
- Applique tête de lit: 18
- Interrupteur: 15
- Interrupteur va-et-vient: 36
- Plafonnier: 32
- Plafonnier IP44: 5
- Prise 2P+T 16A: 70
- Prise plan de travail: 16
- Prise étanche 2P+T: 5

TIJAN AI Bureau d'Études Automatisé	Résidence Papa Oumar Sakho Dakar, Senegal	Éch: 1/100 Pl: 58/88
	Courants Forts — Étage 1	
Date: 06/05/2026	Réf: 1711	BIM VHCU-058 Phase: APD

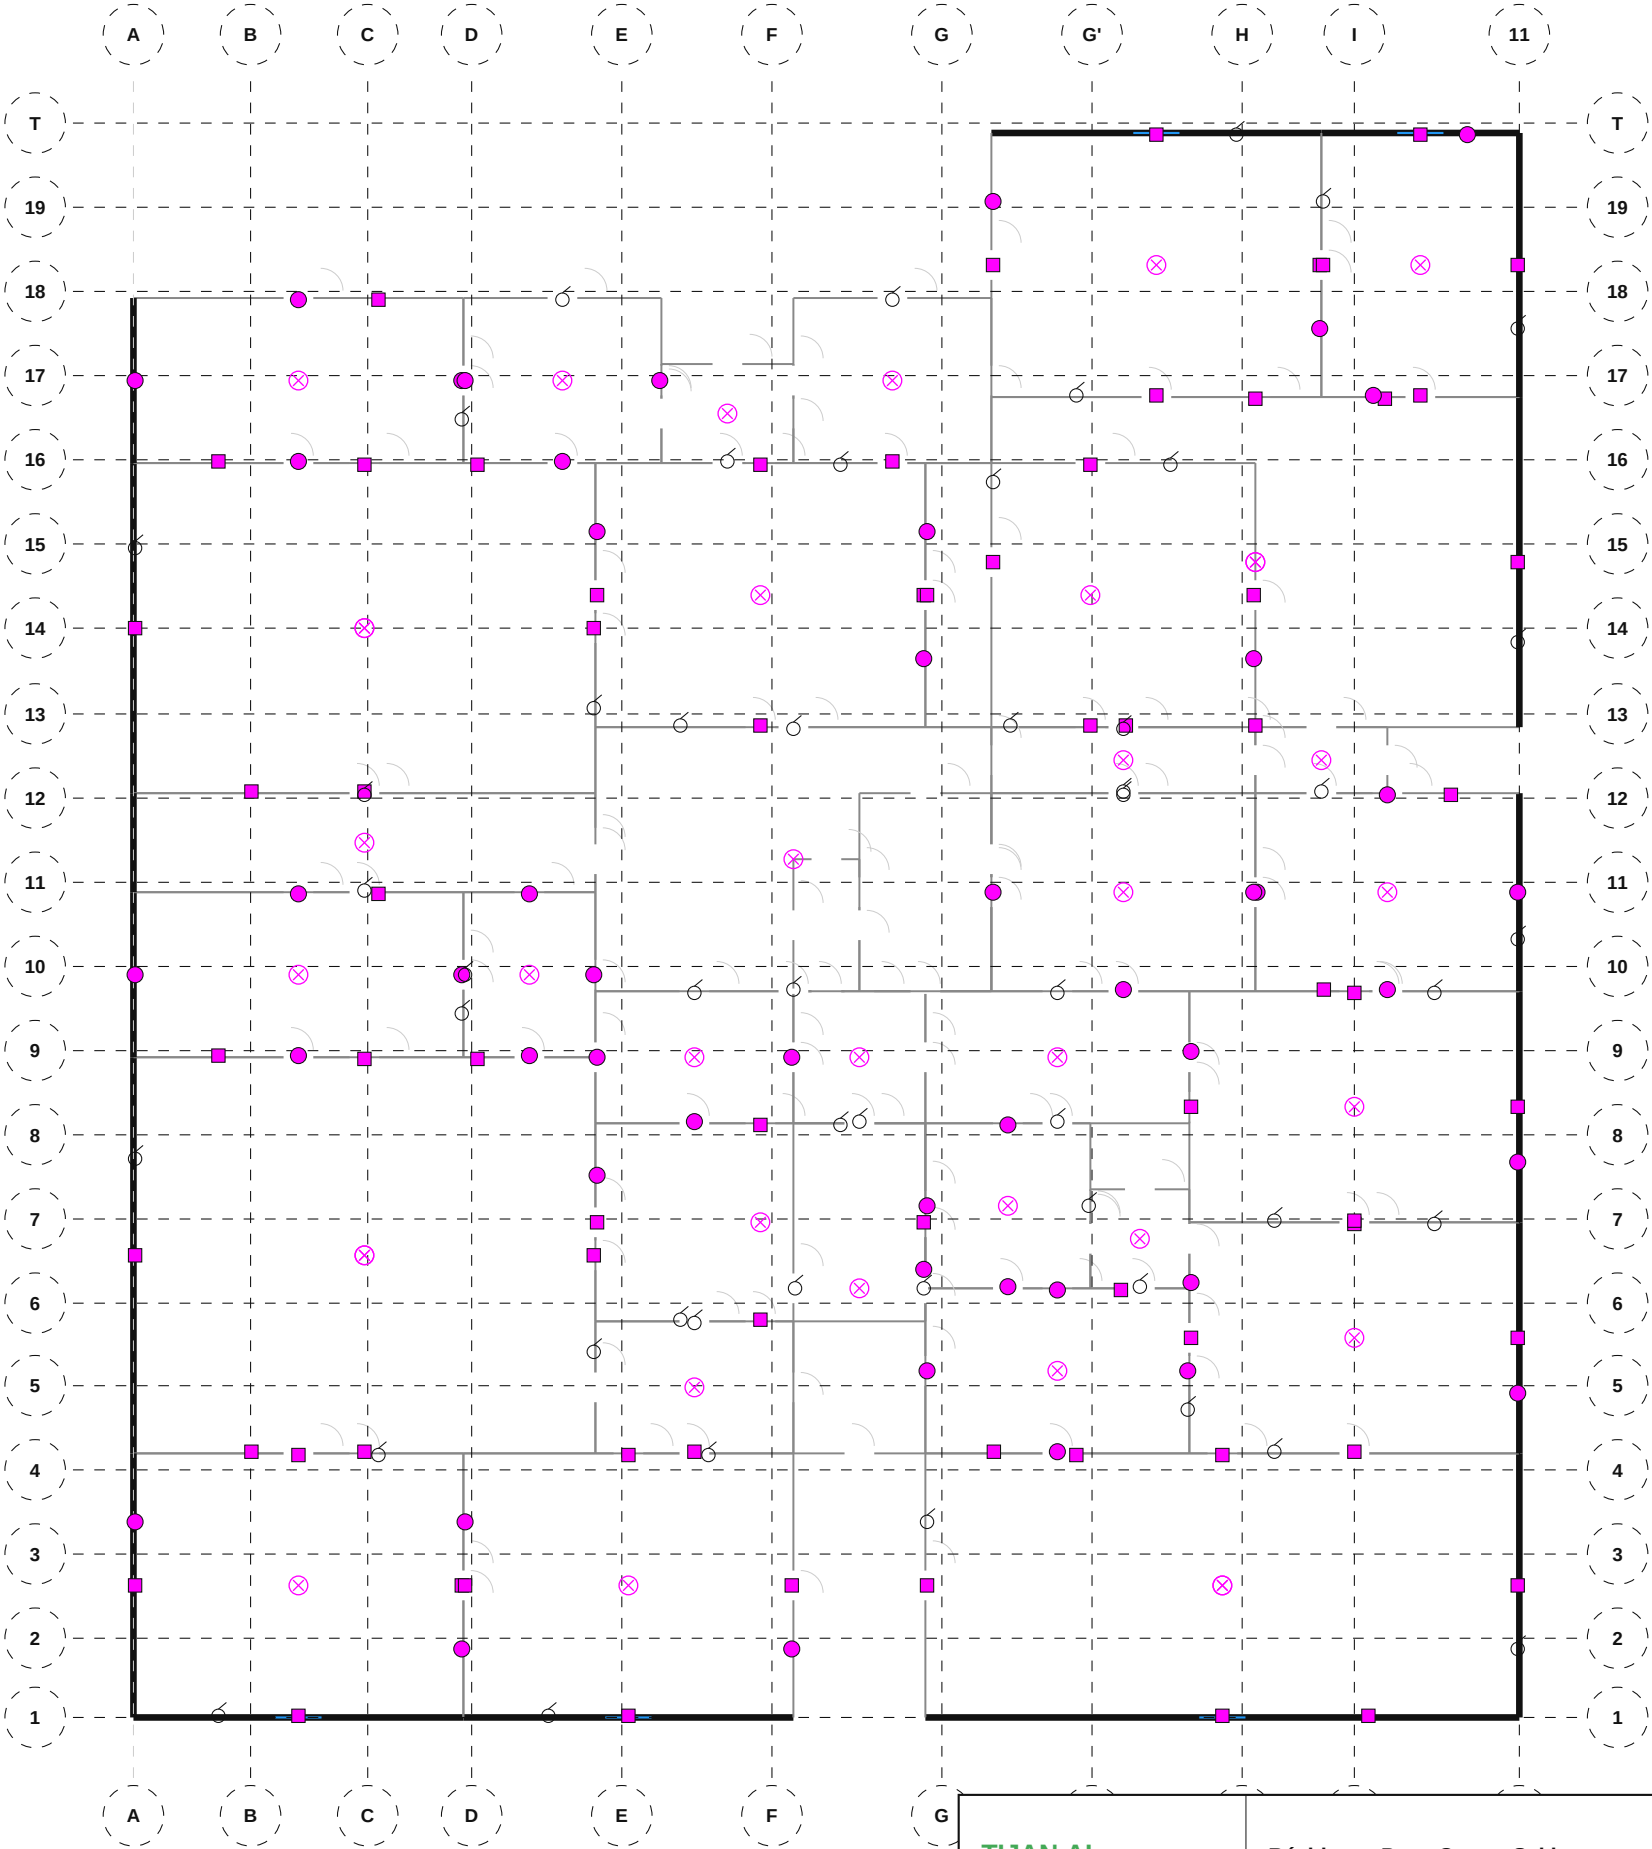


NOMENCLATURE — Courants Forts

- Applique miroir: 10
- Applique tête de lit: 18
- Interrupteur: 15
- Interrupteur va-et-vient: 36
- Plafonnier: 32
- Plafonnier IP44: 5
- Prise 2P+T 16A: 70
- Prise plan de travail: 16
- Prise étanche 2P+T: 5

TIJAN AI Bureau d'Études Automatisé	Résidence Papa Oumar Sakho Dakar, Senegal	Éch: 1/100 Pl. 59/88
	Courants Forts — Étage 2	
Date: 06/05/2026	Réf: 1711	BIM VHCU-059 Phase: APD


510 Courants Forts — Étage 3

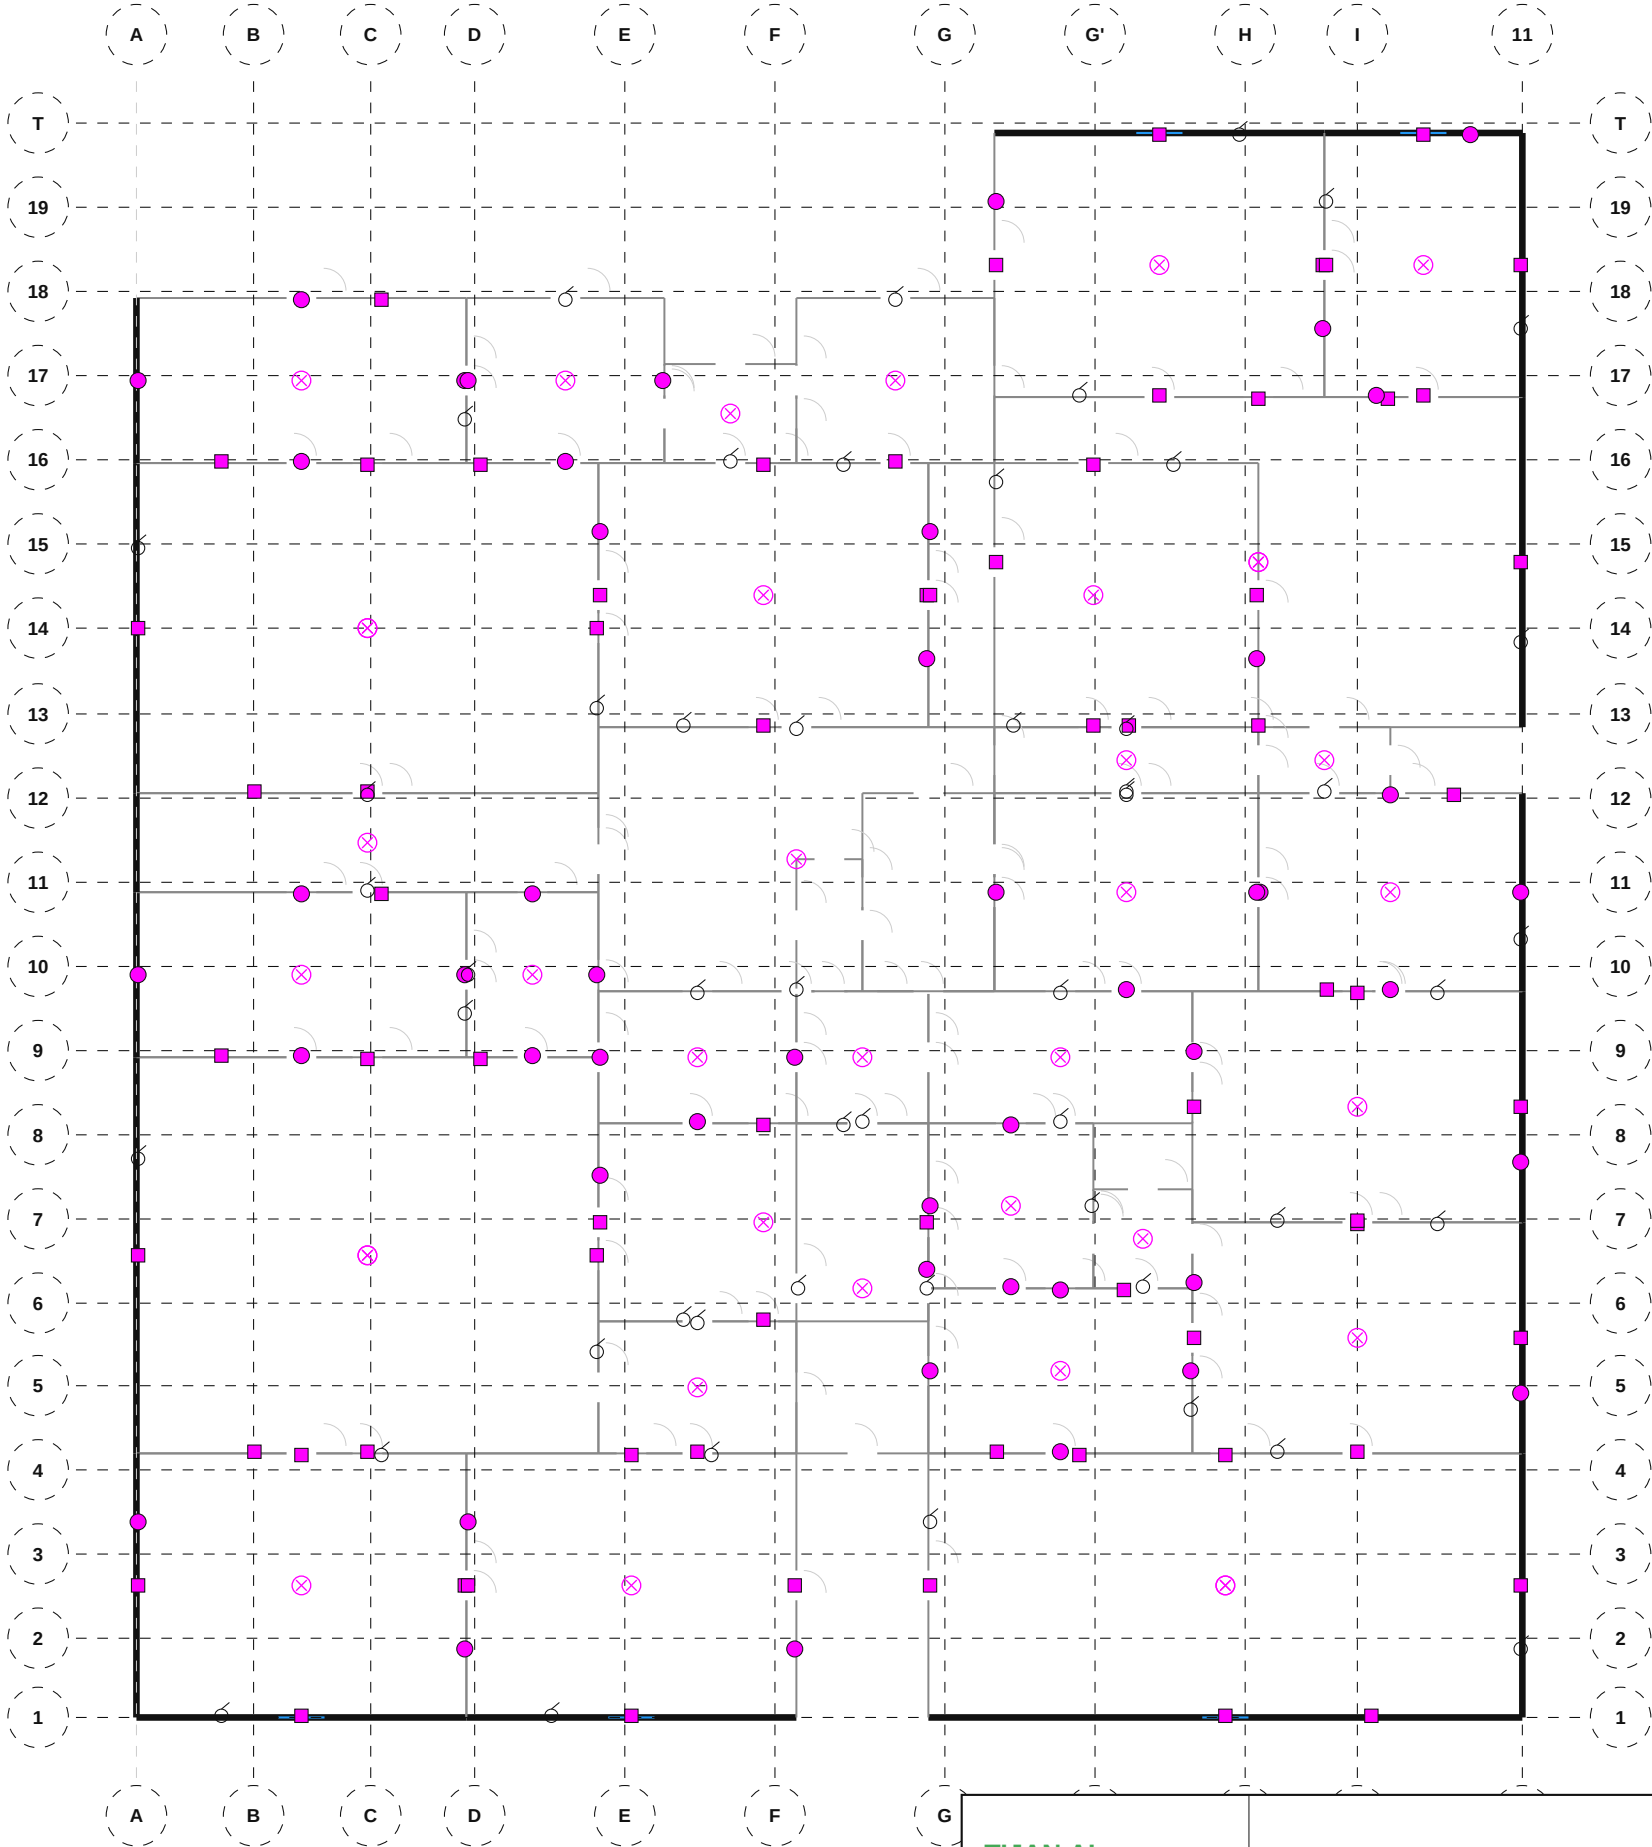

NOMENCLATURE — Courants Forts

- Applique miroir: 10
- Applique tête de lit: 18
- Interrupteur: 15
- Interrupteur va-et-vient: 36
- Plafonnier: 32
- Plafonnier IP44: 5
- Prise 2P+T 16A: 70
- Prise plan de travail: 16
- Prise étanche 2P+T: 5


TIJAN AI Bureau d'Études Automatisé	Résidence Papa Oumar Sakho Dakar, Senegal	Éch: 1/100 Pl. 60/88
	Courants Forts — Étage 3	
Date: 06/05/2026	Réf: 1711	BIM VHCU-060 Phase: APD

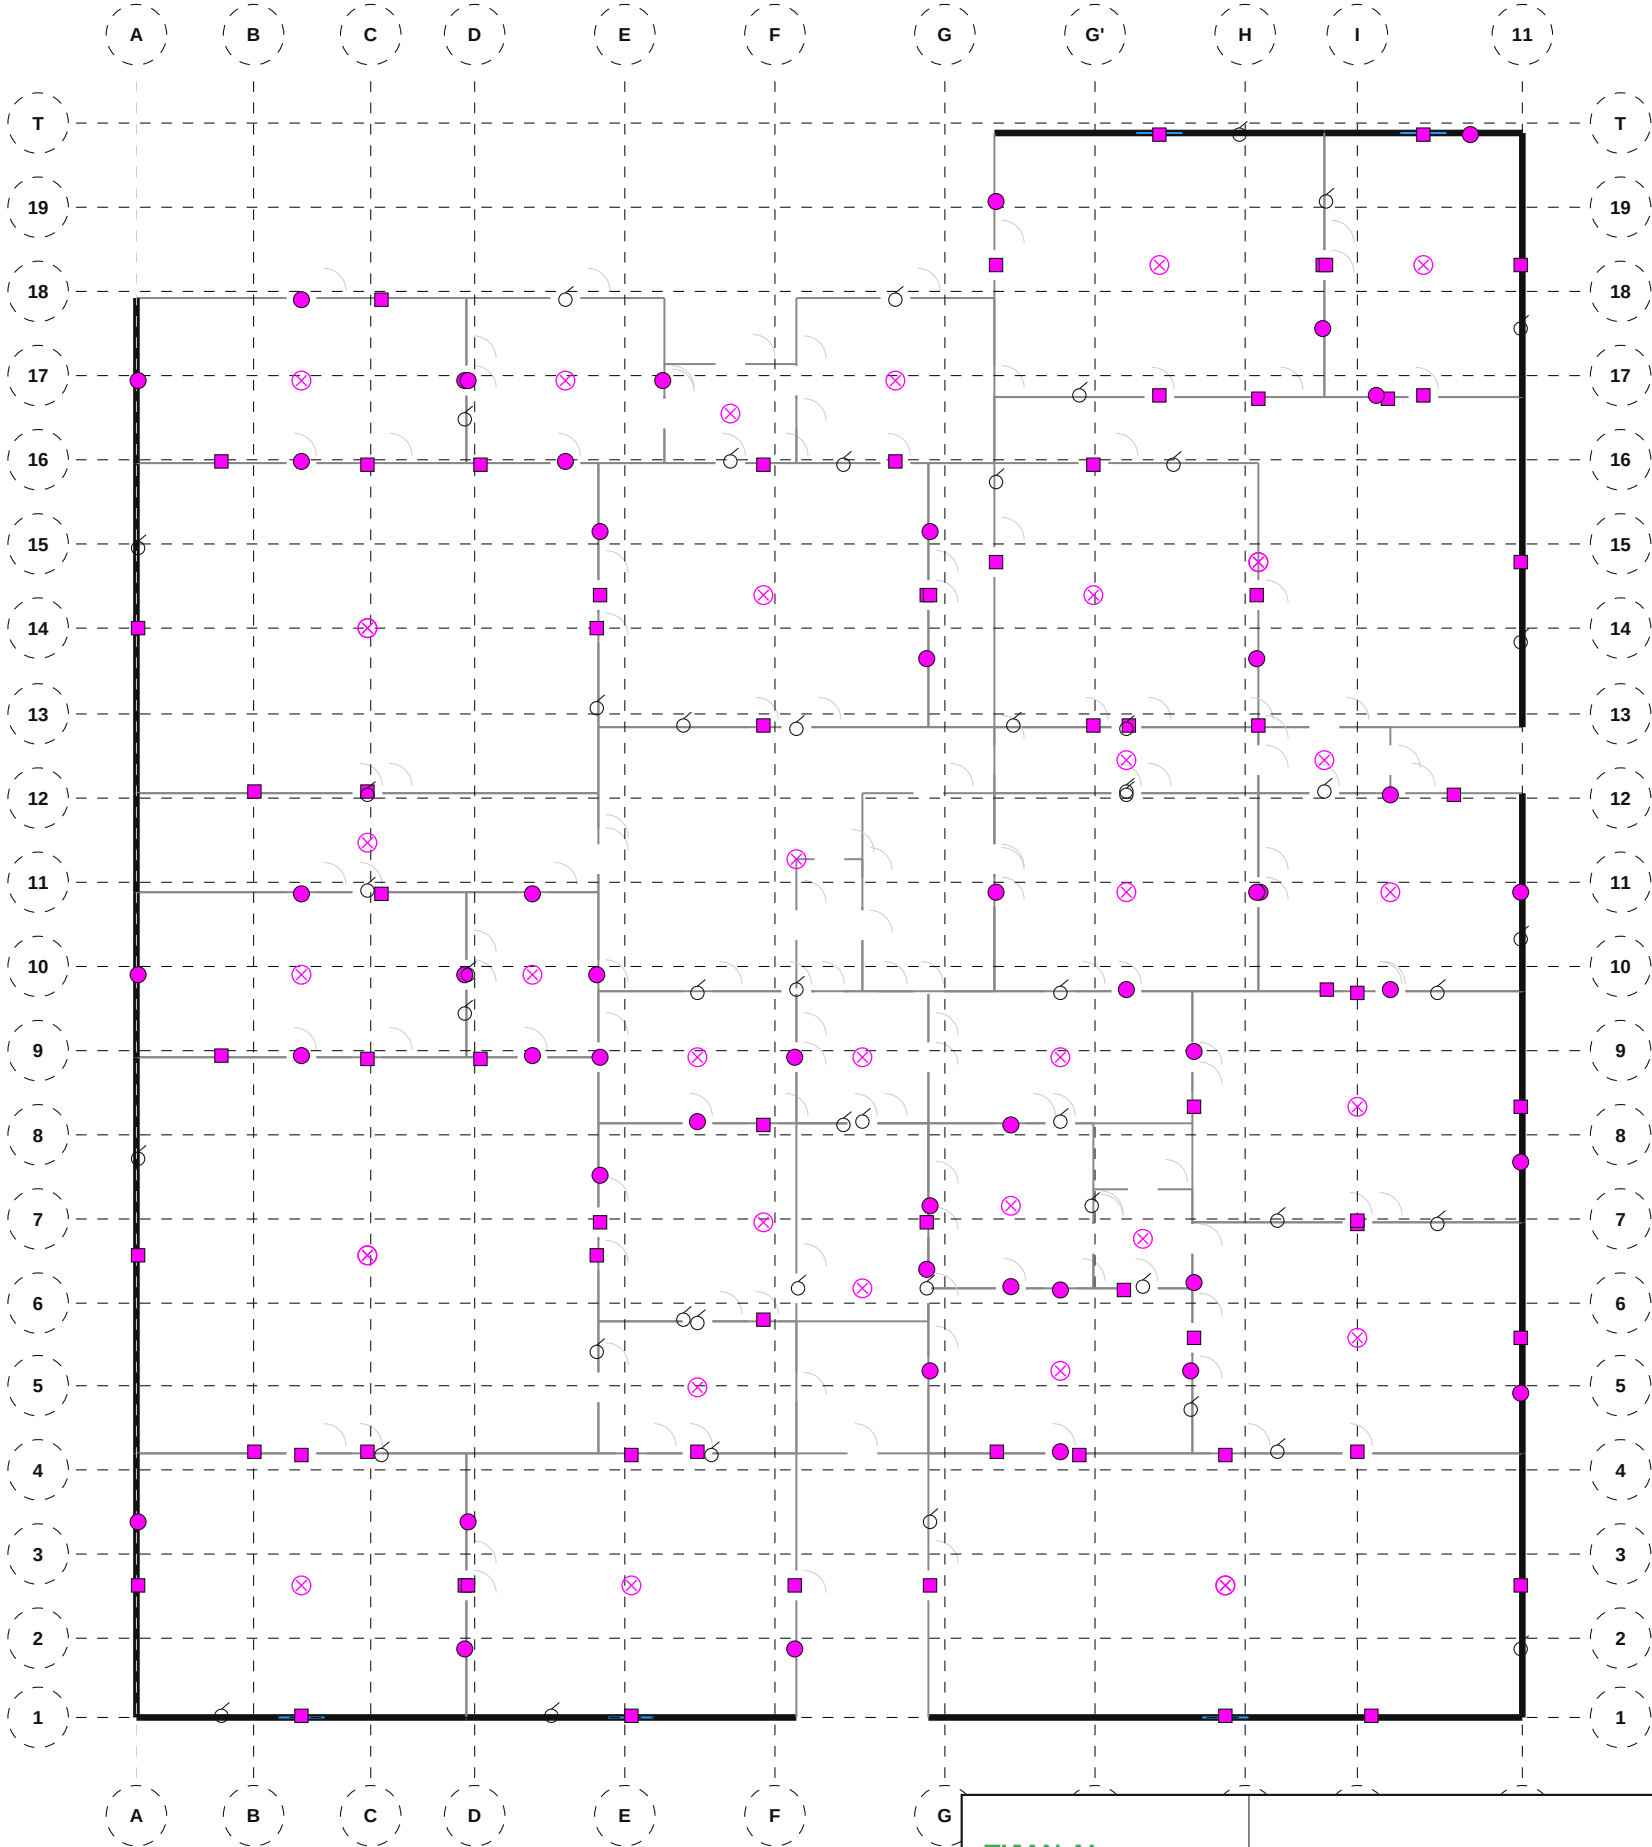

NOMENCLATURE — Courants Forts

- Applique miroir: 10
- Applique tête de lit: 18
- Interrupteur: 15
- Interrupteur va-et-vient: 36
- Plafonnier: 32
- Plafonnier IP44: 5
- Prise 2P+T 16A: 70
- Prise plan de travail: 16
- Prise étanche 2P+T: 5


TIJAN AI Bureau d'Études Automatisé	Résidence Papa Oumar Sakho Dakar, Senegal	Éch: 1/100 Pl. 61/88
	Courants Forts — Étage 4	
Date: 06/05/2026	Réf: 1711	BIM VHCU-061 Phase: APD

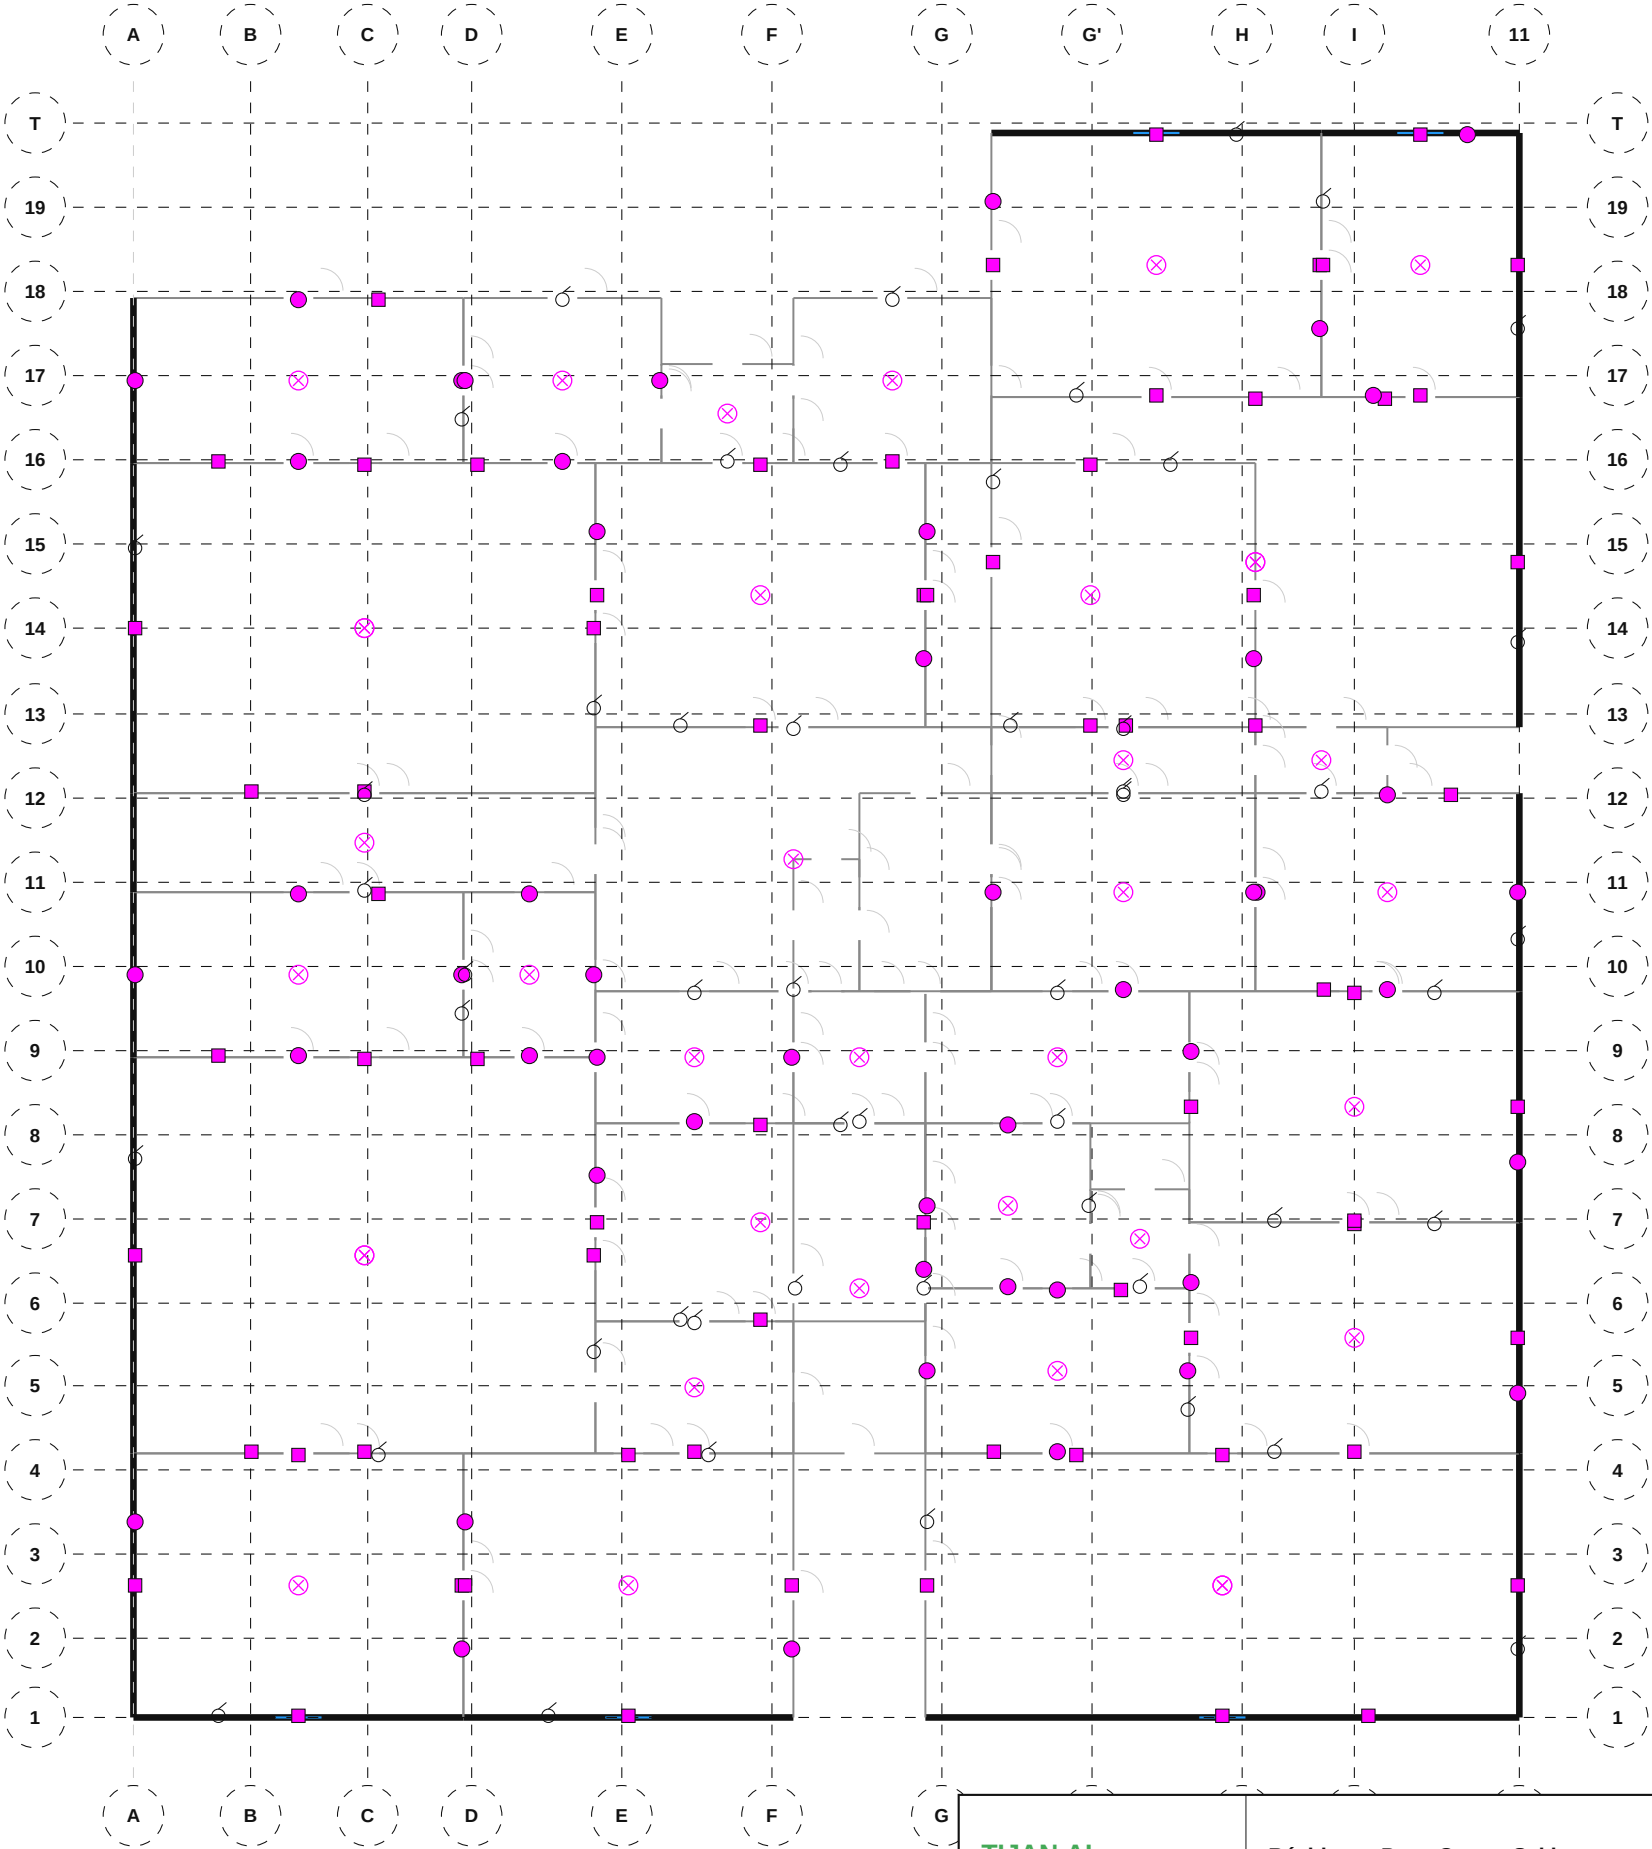

NOMENCLATURE — Courants Forts

- Applique miroir: 10
- Applique tête de lit: 18
- Interrupteur: 15
- Interrupteur va-et-vient: 36
- Plafonnier: 32
- Plafonnier IP44: 5
- Prise 2P+T 16A: 70
- Prise plan de travail: 16
- Prise étanche 2P+T: 5

TIJAN AI Bureau d'Études Automatisé	Résidence Papa Oumar Sakho Dakar, Senegal	Éch: 1/100 Pl. 62/88
	Courants Forts — Étage 5	
Date: 06/05/2026	Réf: 1711	BIM VHCU-062 Phase: APD

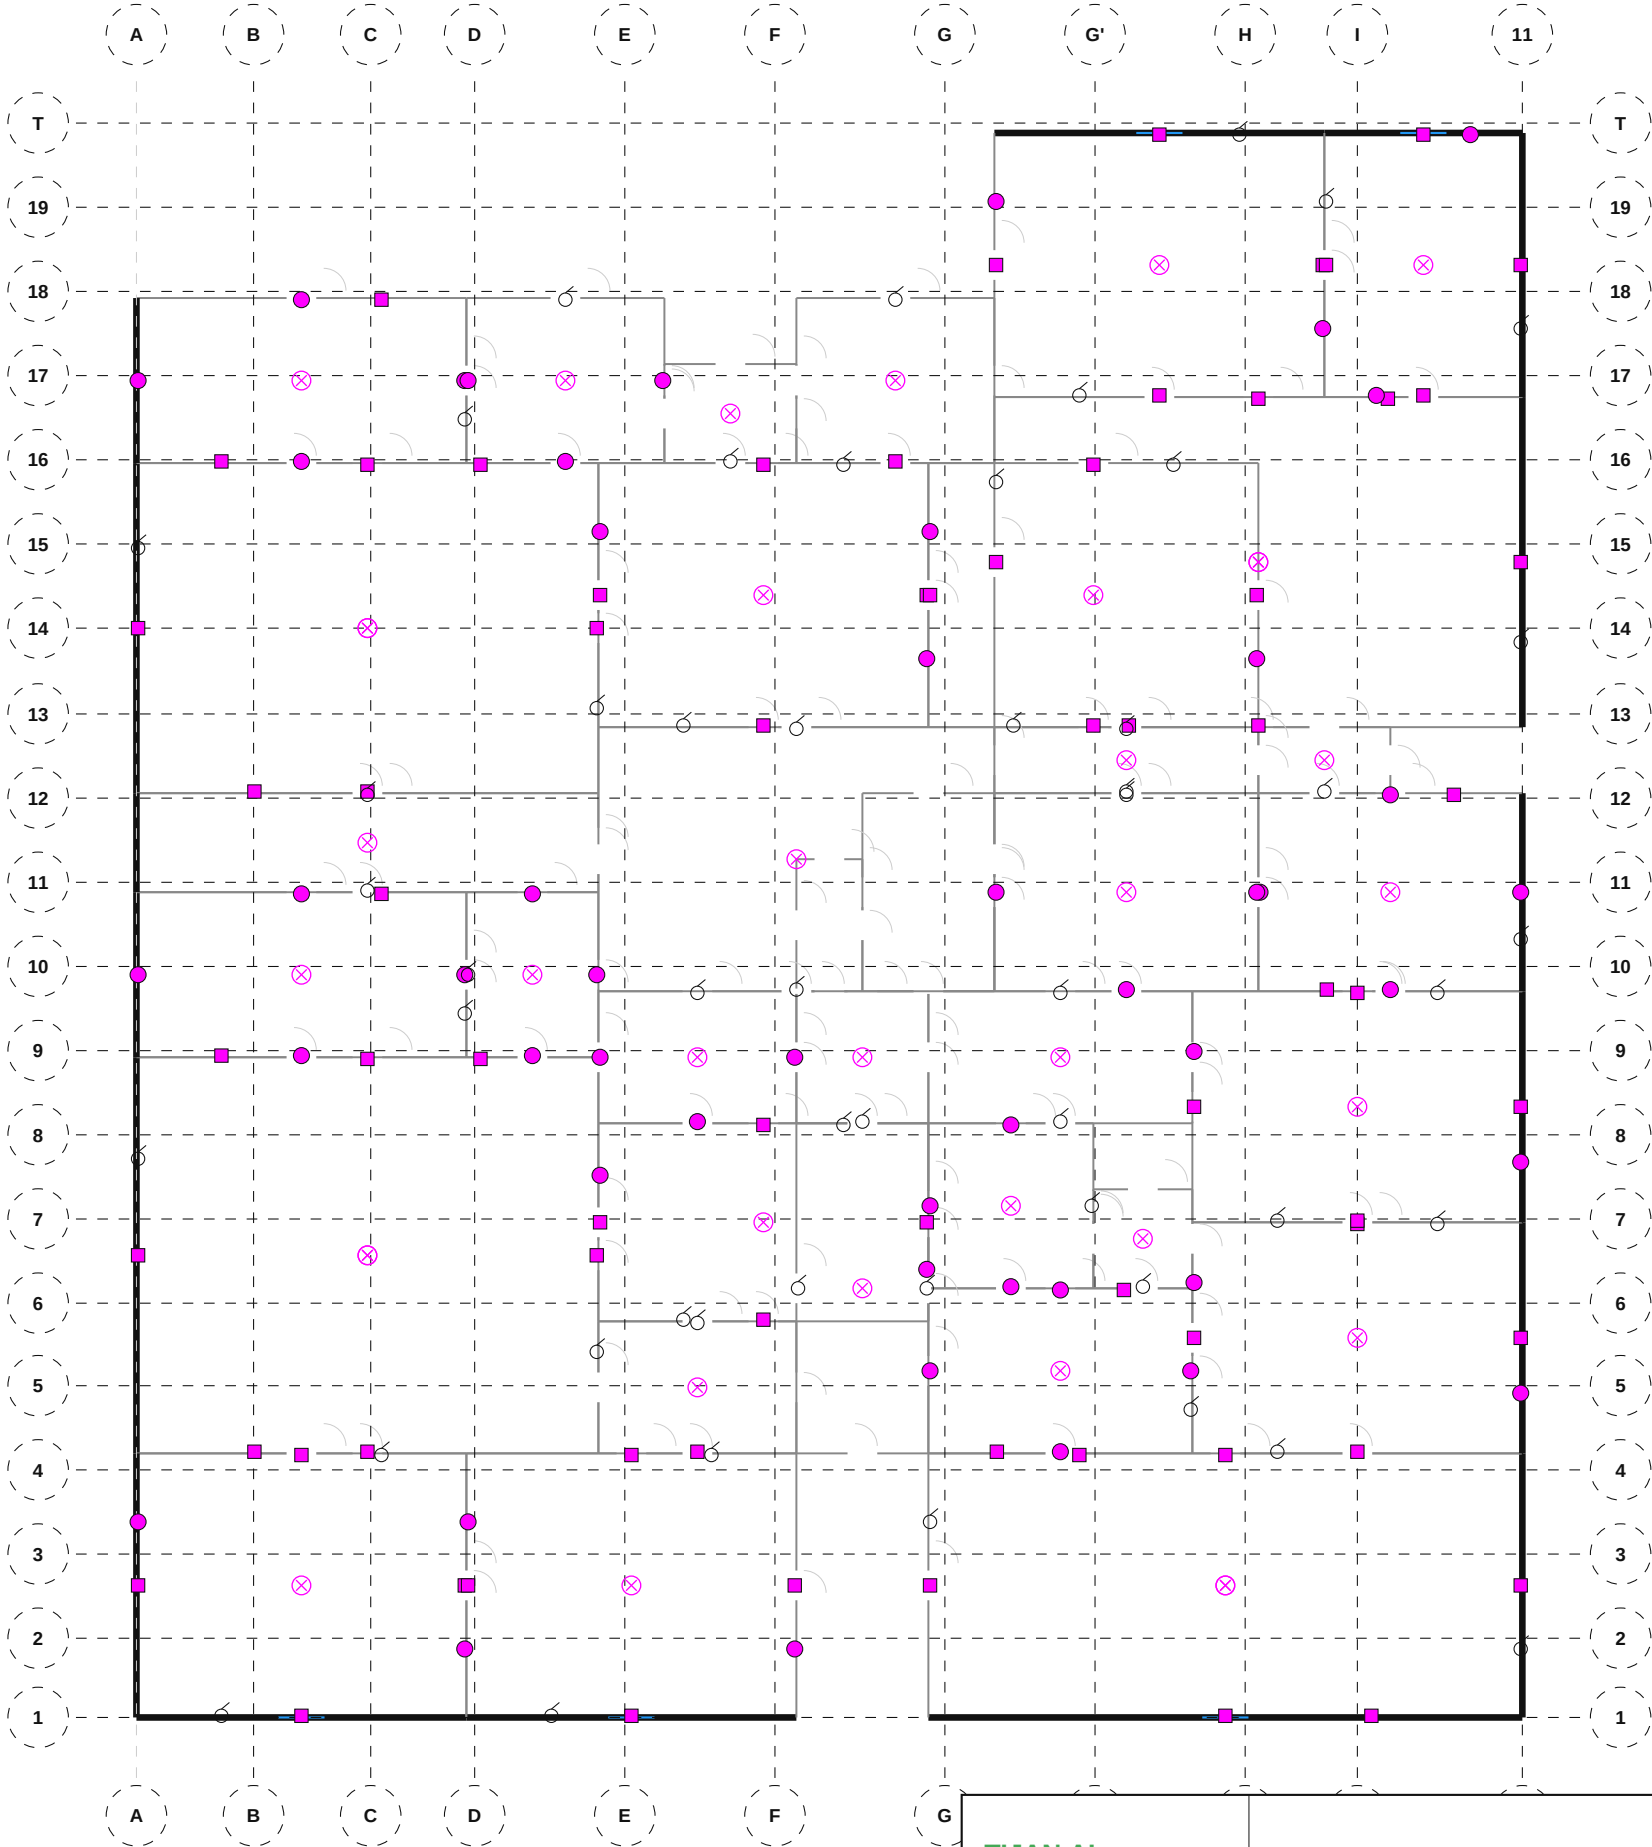


NOMENCLATURE — Courants Forts

- Applique miroir: 10
- Applique tête de lit: 18
- Interrupteur: 15
- Interrupteur va-et-vient: 36
- Plafonnier: 32
- Plafonnier IP44: 5
- Prise 2P+T 16A: 70
- Prise plan de travail: 16
- Prise étanche 2P+T: 5

TIJAN AI Bureau d'Études Automatisé	Résidence Papa Oumar Sakho Dakar, Senegal	Éch: 1/100 Pl. 63/88
	Courants Forts — Étage 6	
Date: 06/05/2026	Réf: 1711	BIM VHCU-063 Phase: APD

510 Courants Forts — Étage 7

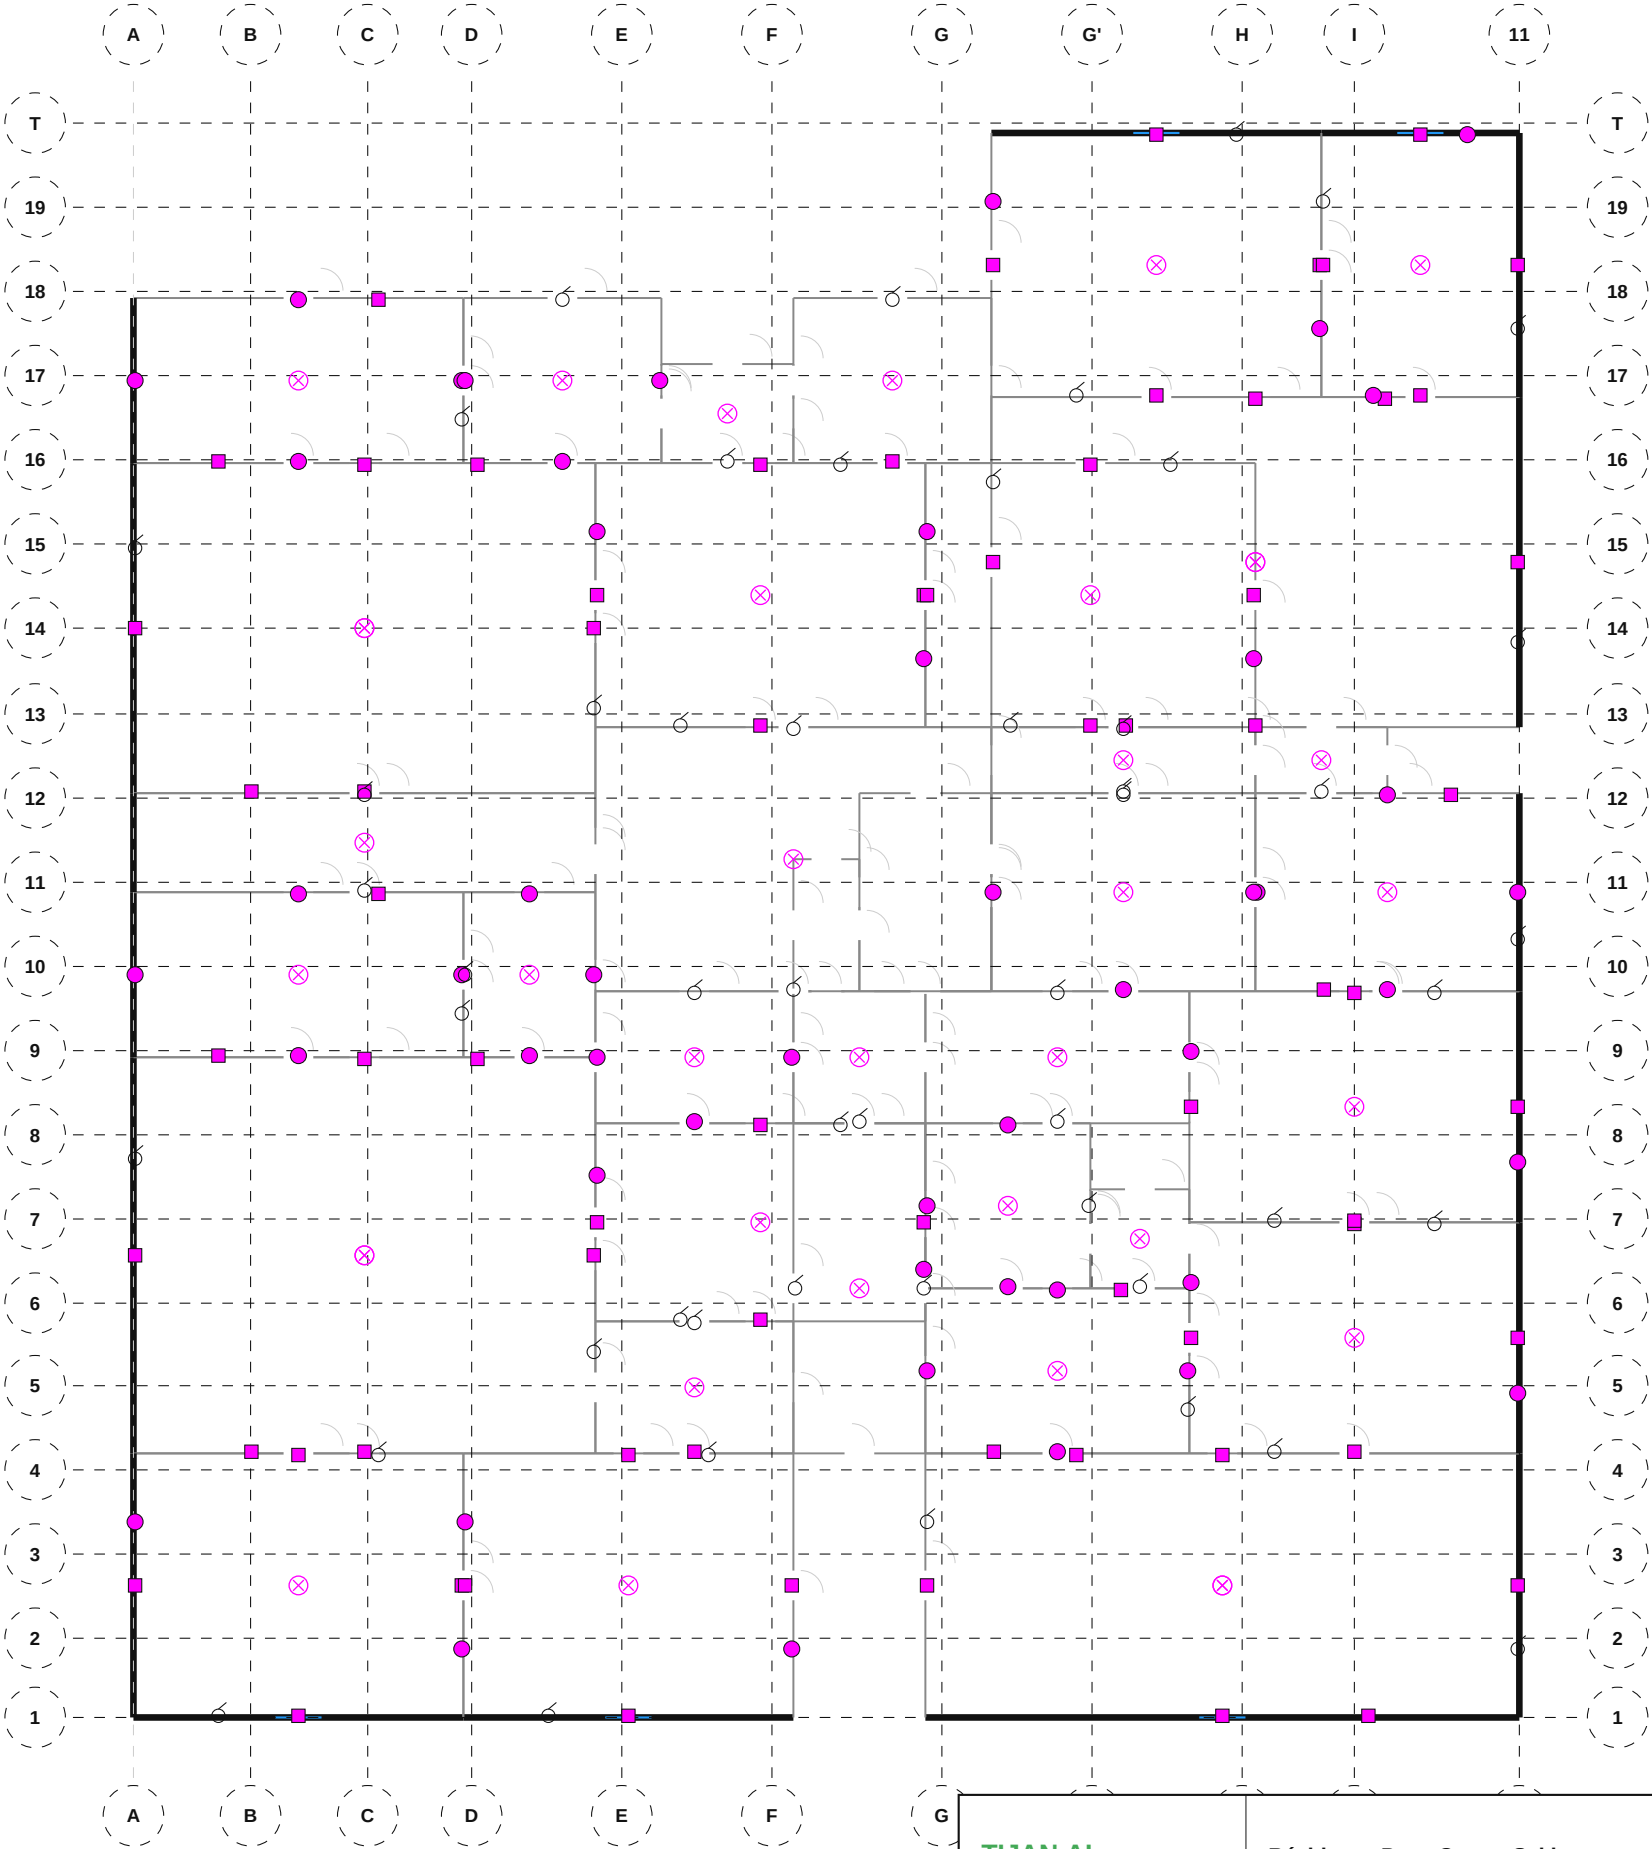


NOMENCLATURE — Courants Forts

- Applique miroir: 10
- Applique tête de lit: 18
- Interrupteur: 15
- Interrupteur va-et-vient: 36
- Plafonnier: 32
- Plafonnier IP44: 5
- Prise 2P+T 16A: 70
- Prise plan de travail: 16
- Prise étanche 2P+T: 5

TIJAN AI Bureau d'Études Automatisé	Résidence Papa Oumar Sakho Dakar, Senegal	Éch: 1/100 Pl. 64/88
	Courants Forts — Étage 7	
Date: 06/05/2026	Réf: 1711	BIM VHCU-064 Phase: APD

510 Courants Forts — Étage 8

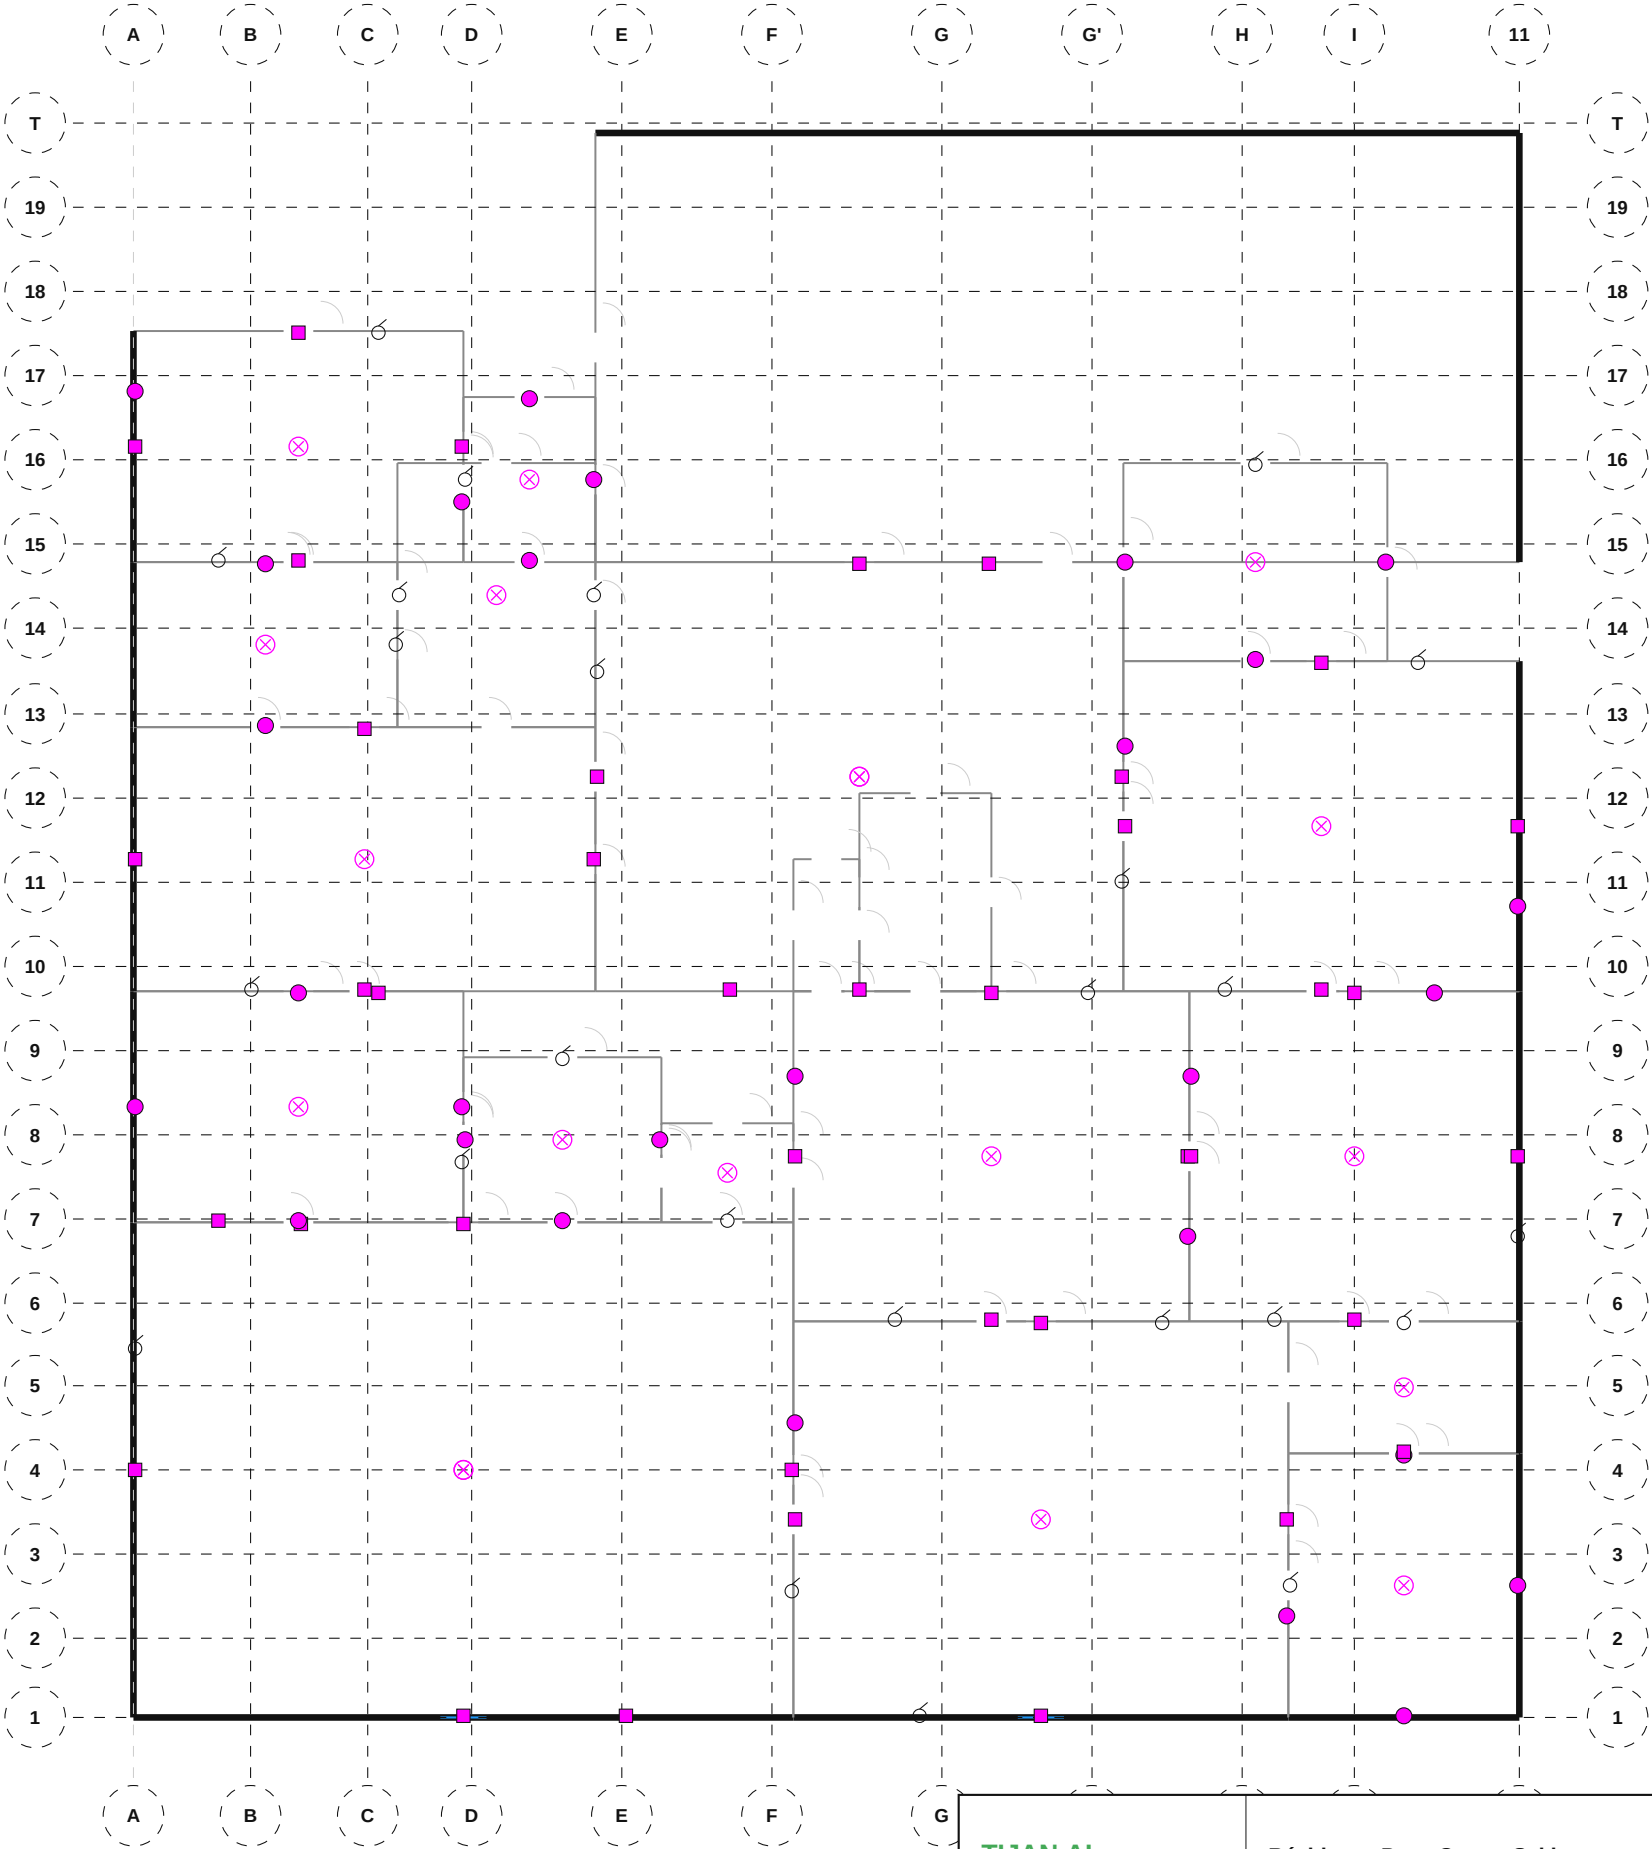


NOMENCLATURE — Courants Forts

- Applique miroir: 8
- Applique tête de lit: 10
- Interrupteur: 9
- Interrupteur va-et-vient: 16
- Plafonnier: 15
- Plafonnier IP44: 4
- Prise 2P+T 16A: 39
- Prise plan de travail: 4
- Prise étanche: 2
- Prise étanche 2P+T: 4

TIJAN AI Bureau d'Études Automatisé	Résidence Papa Oumar Sakho Dakar, Senegal	Éch: 1/100 Pl. 65/88
	Courants Forts — Étage 8	
Date: 06/05/2026	Réf: 1711	BIM VHCU-065 Phase: APD

510 Courants Forts — Terrasse

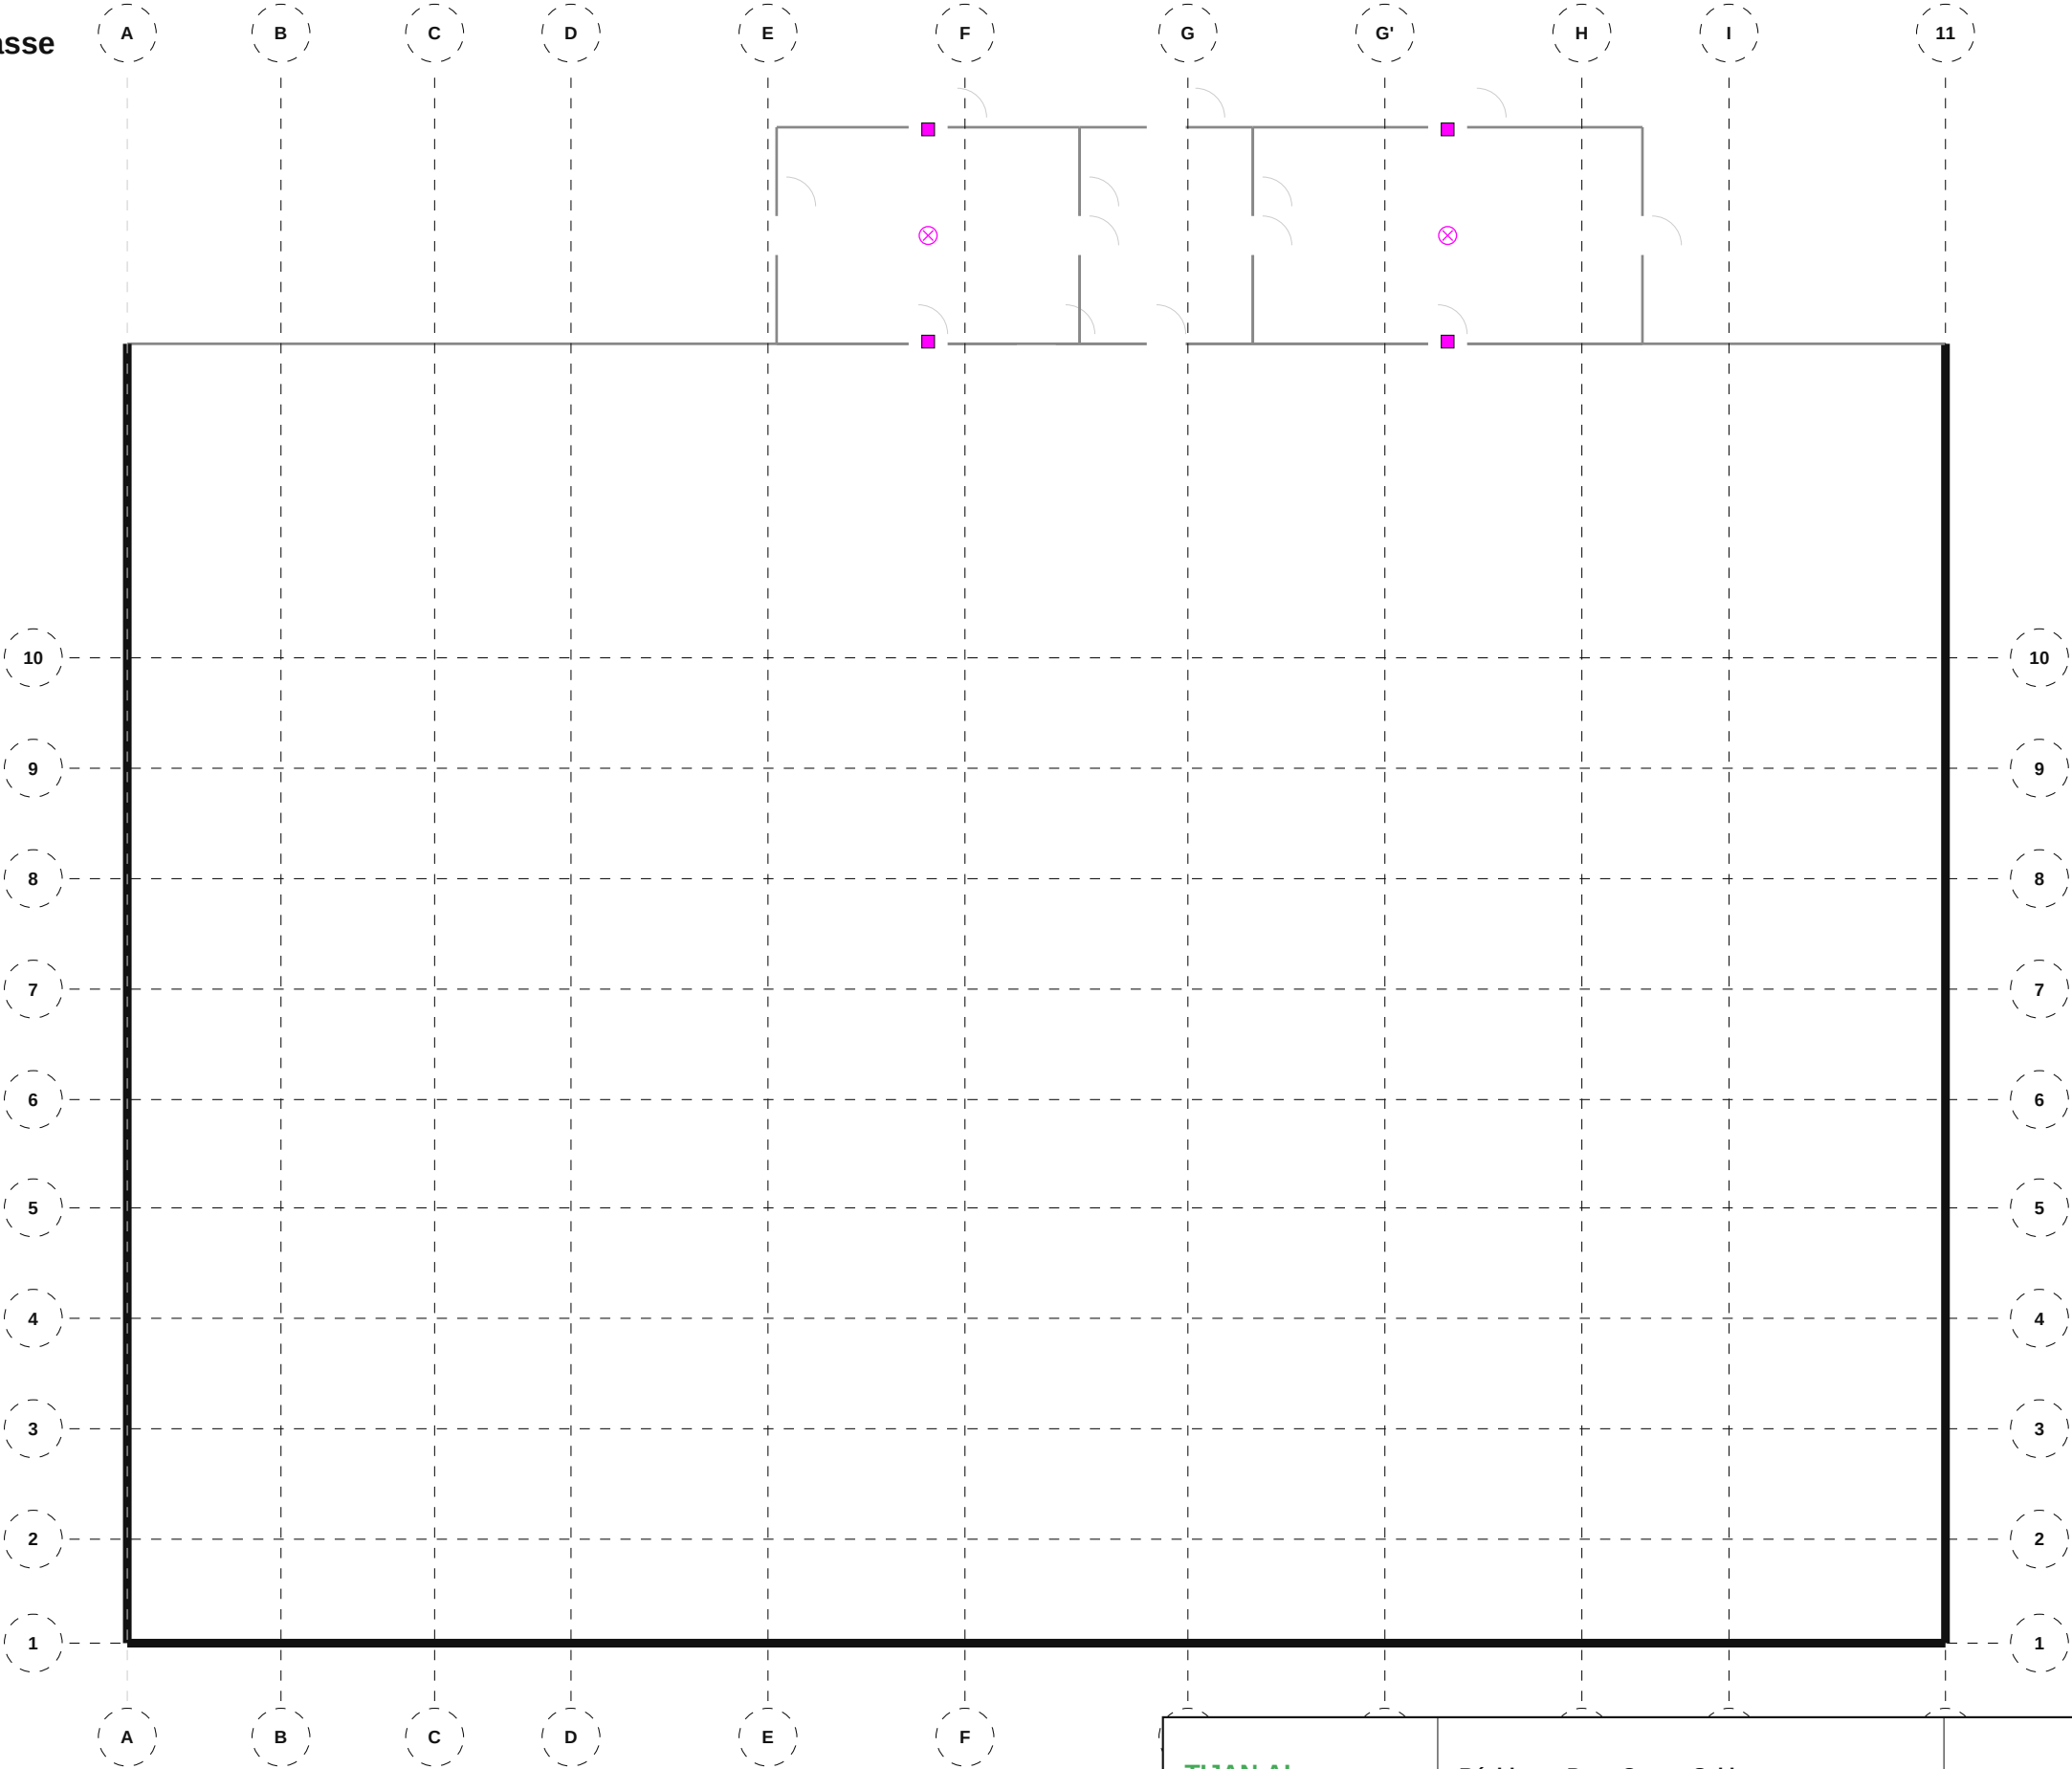


NOMENCLATURE — Courants Forts

- Plafonnier: 2
- Prise 2P+T 16A: 4

TIJAN AI Bureau d'Études Automatisé	Résidence Papa Oumar Sakho Dakar, Senegal	Éch: 1/100 Pl. 66/88
	Courants Forts — Terrasse	
Date: 06/05/2026	Réf: 1711	BIM vHCU-066 Phase: APD

520 Courants Faibles — Sous-Sol

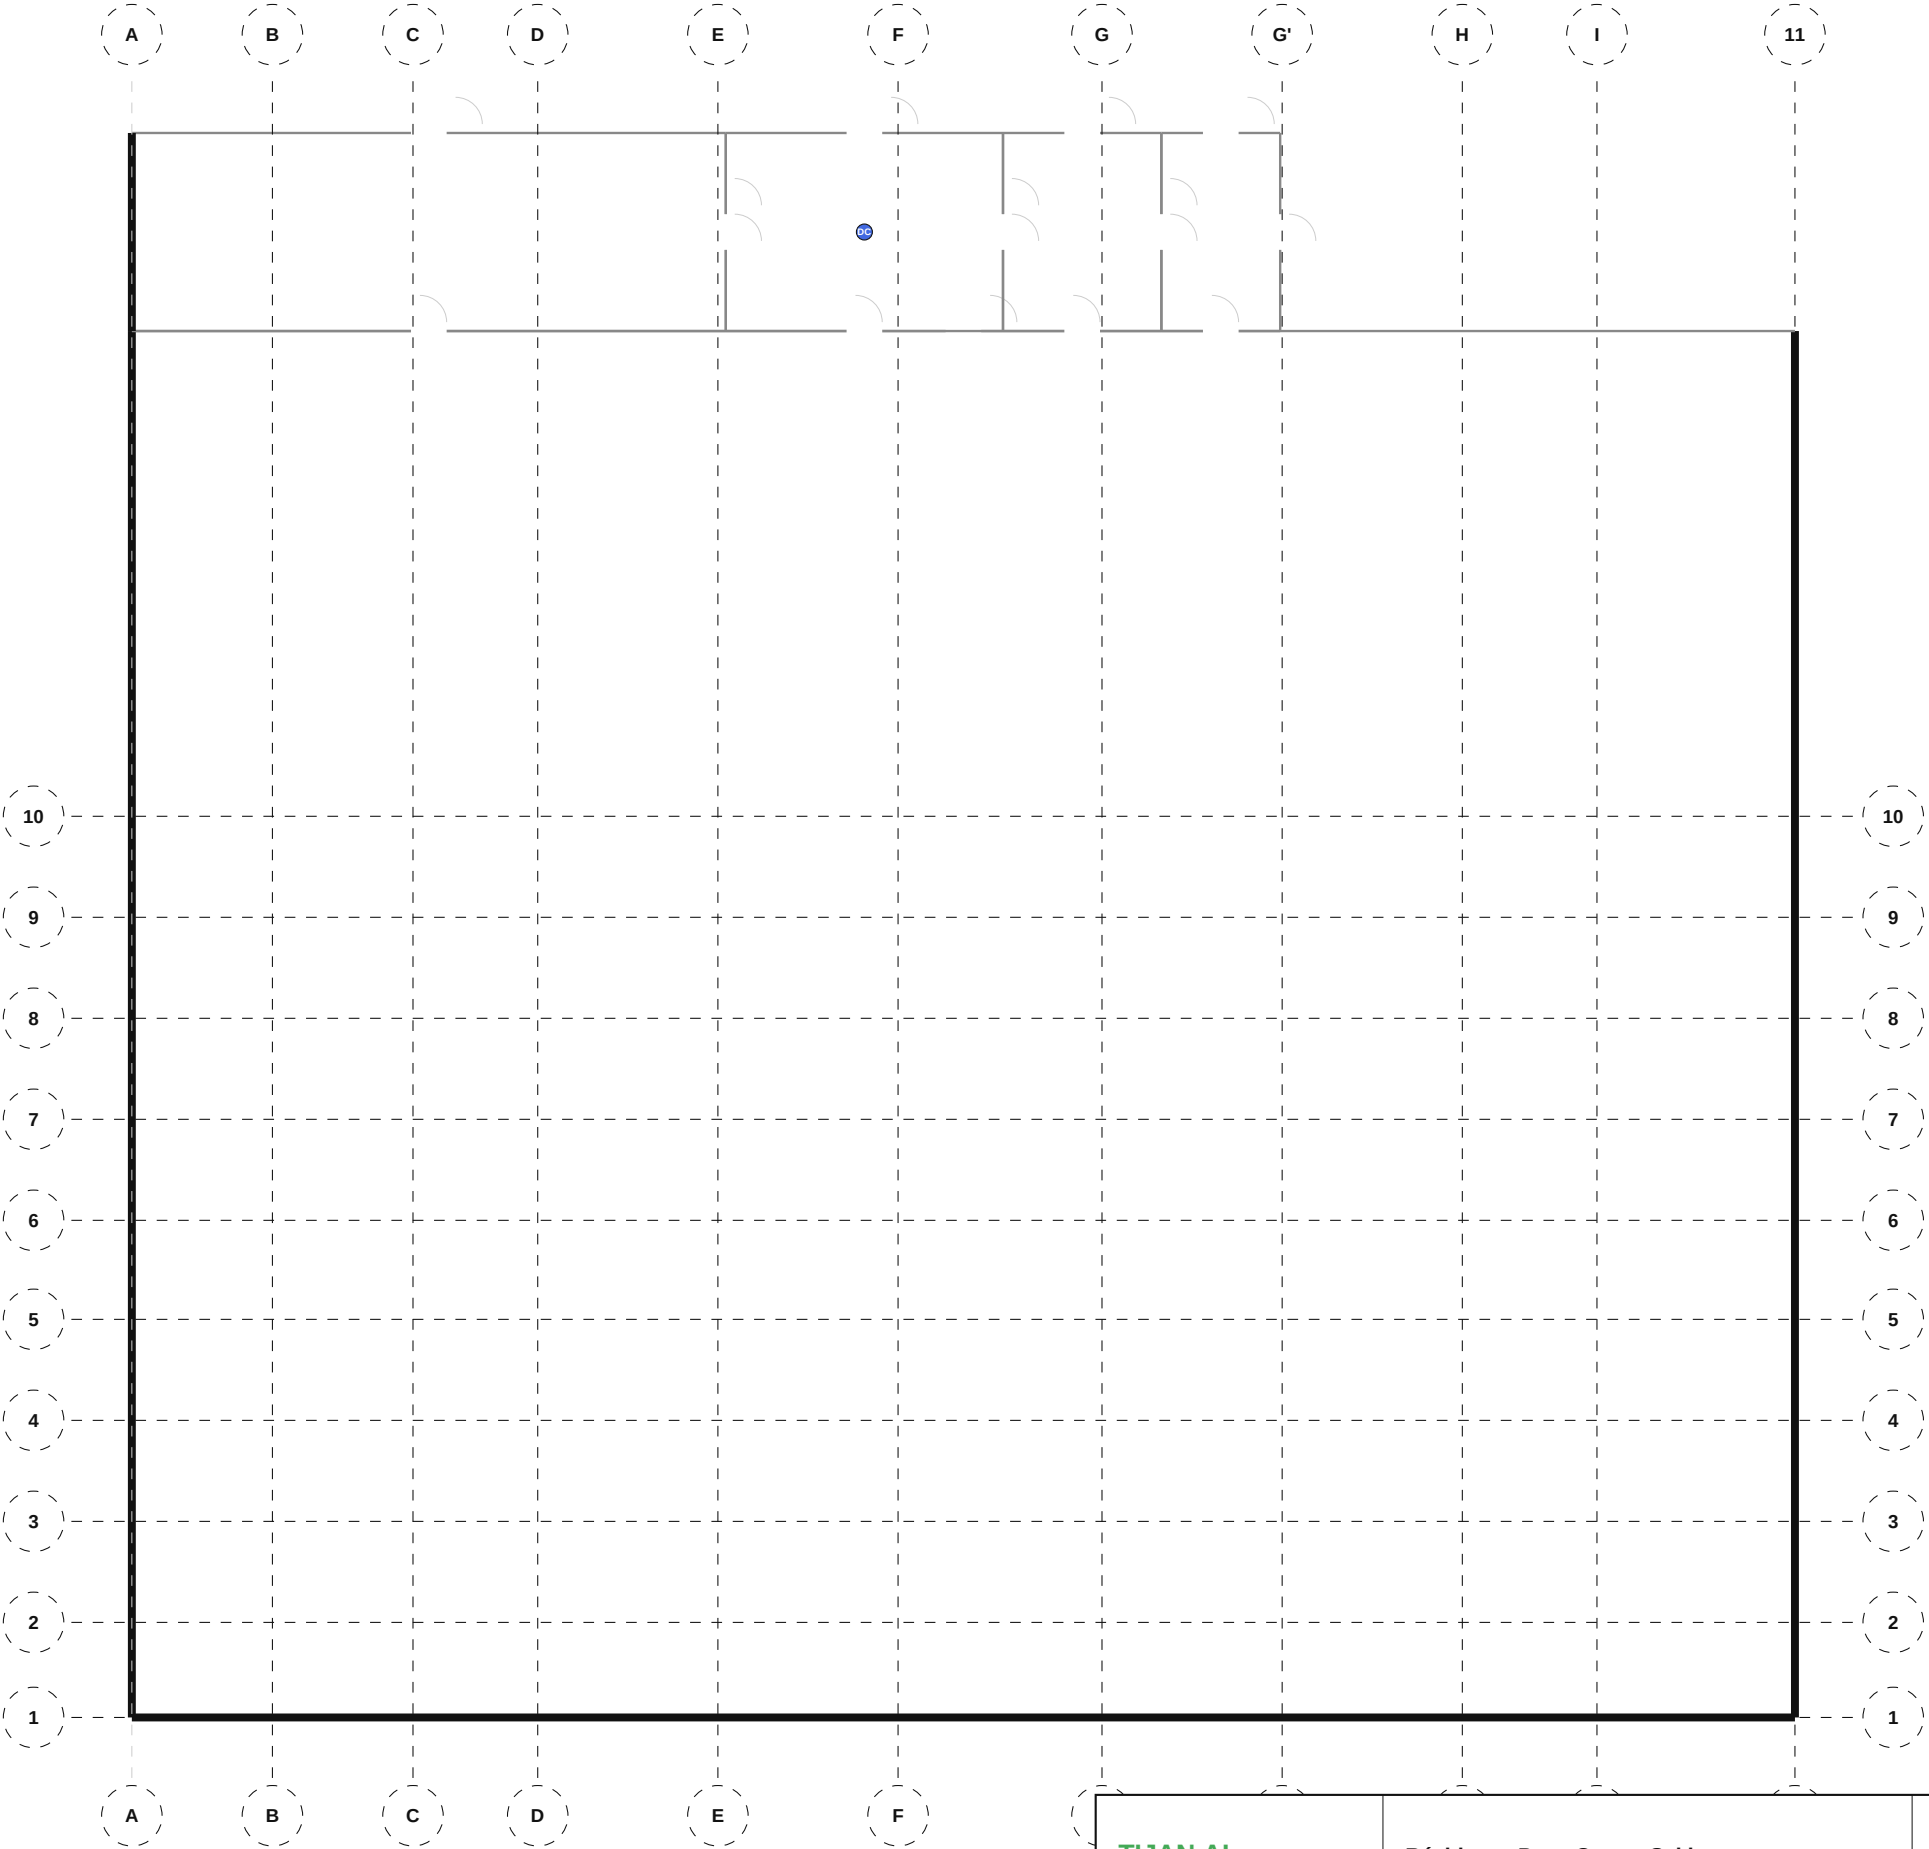

NOMENCLATURE — Courants Faibles


• Détecteur de chaleur: 1

TIJAN AI Bureau d'Études Automatisé	Résidence Papa Oumar Sakho Dakar, Senegal	Éch: 1/100 Pl. 67/88
	Courants Faibles — Sous-Sol	
Date: 06/05/2026	Réf: 1711	BIM V.LCU-067 Phase: APD

520 Courants Faibles — RDC


NOMENCLATURE — Courants Faibles

- Détecteur de chaleur: 2
- Détecteur de fumée: 7
- Interphone: 1
- Point d'accès WiFi: 2
- Prise RJ45: 7
- Prise TV: 3

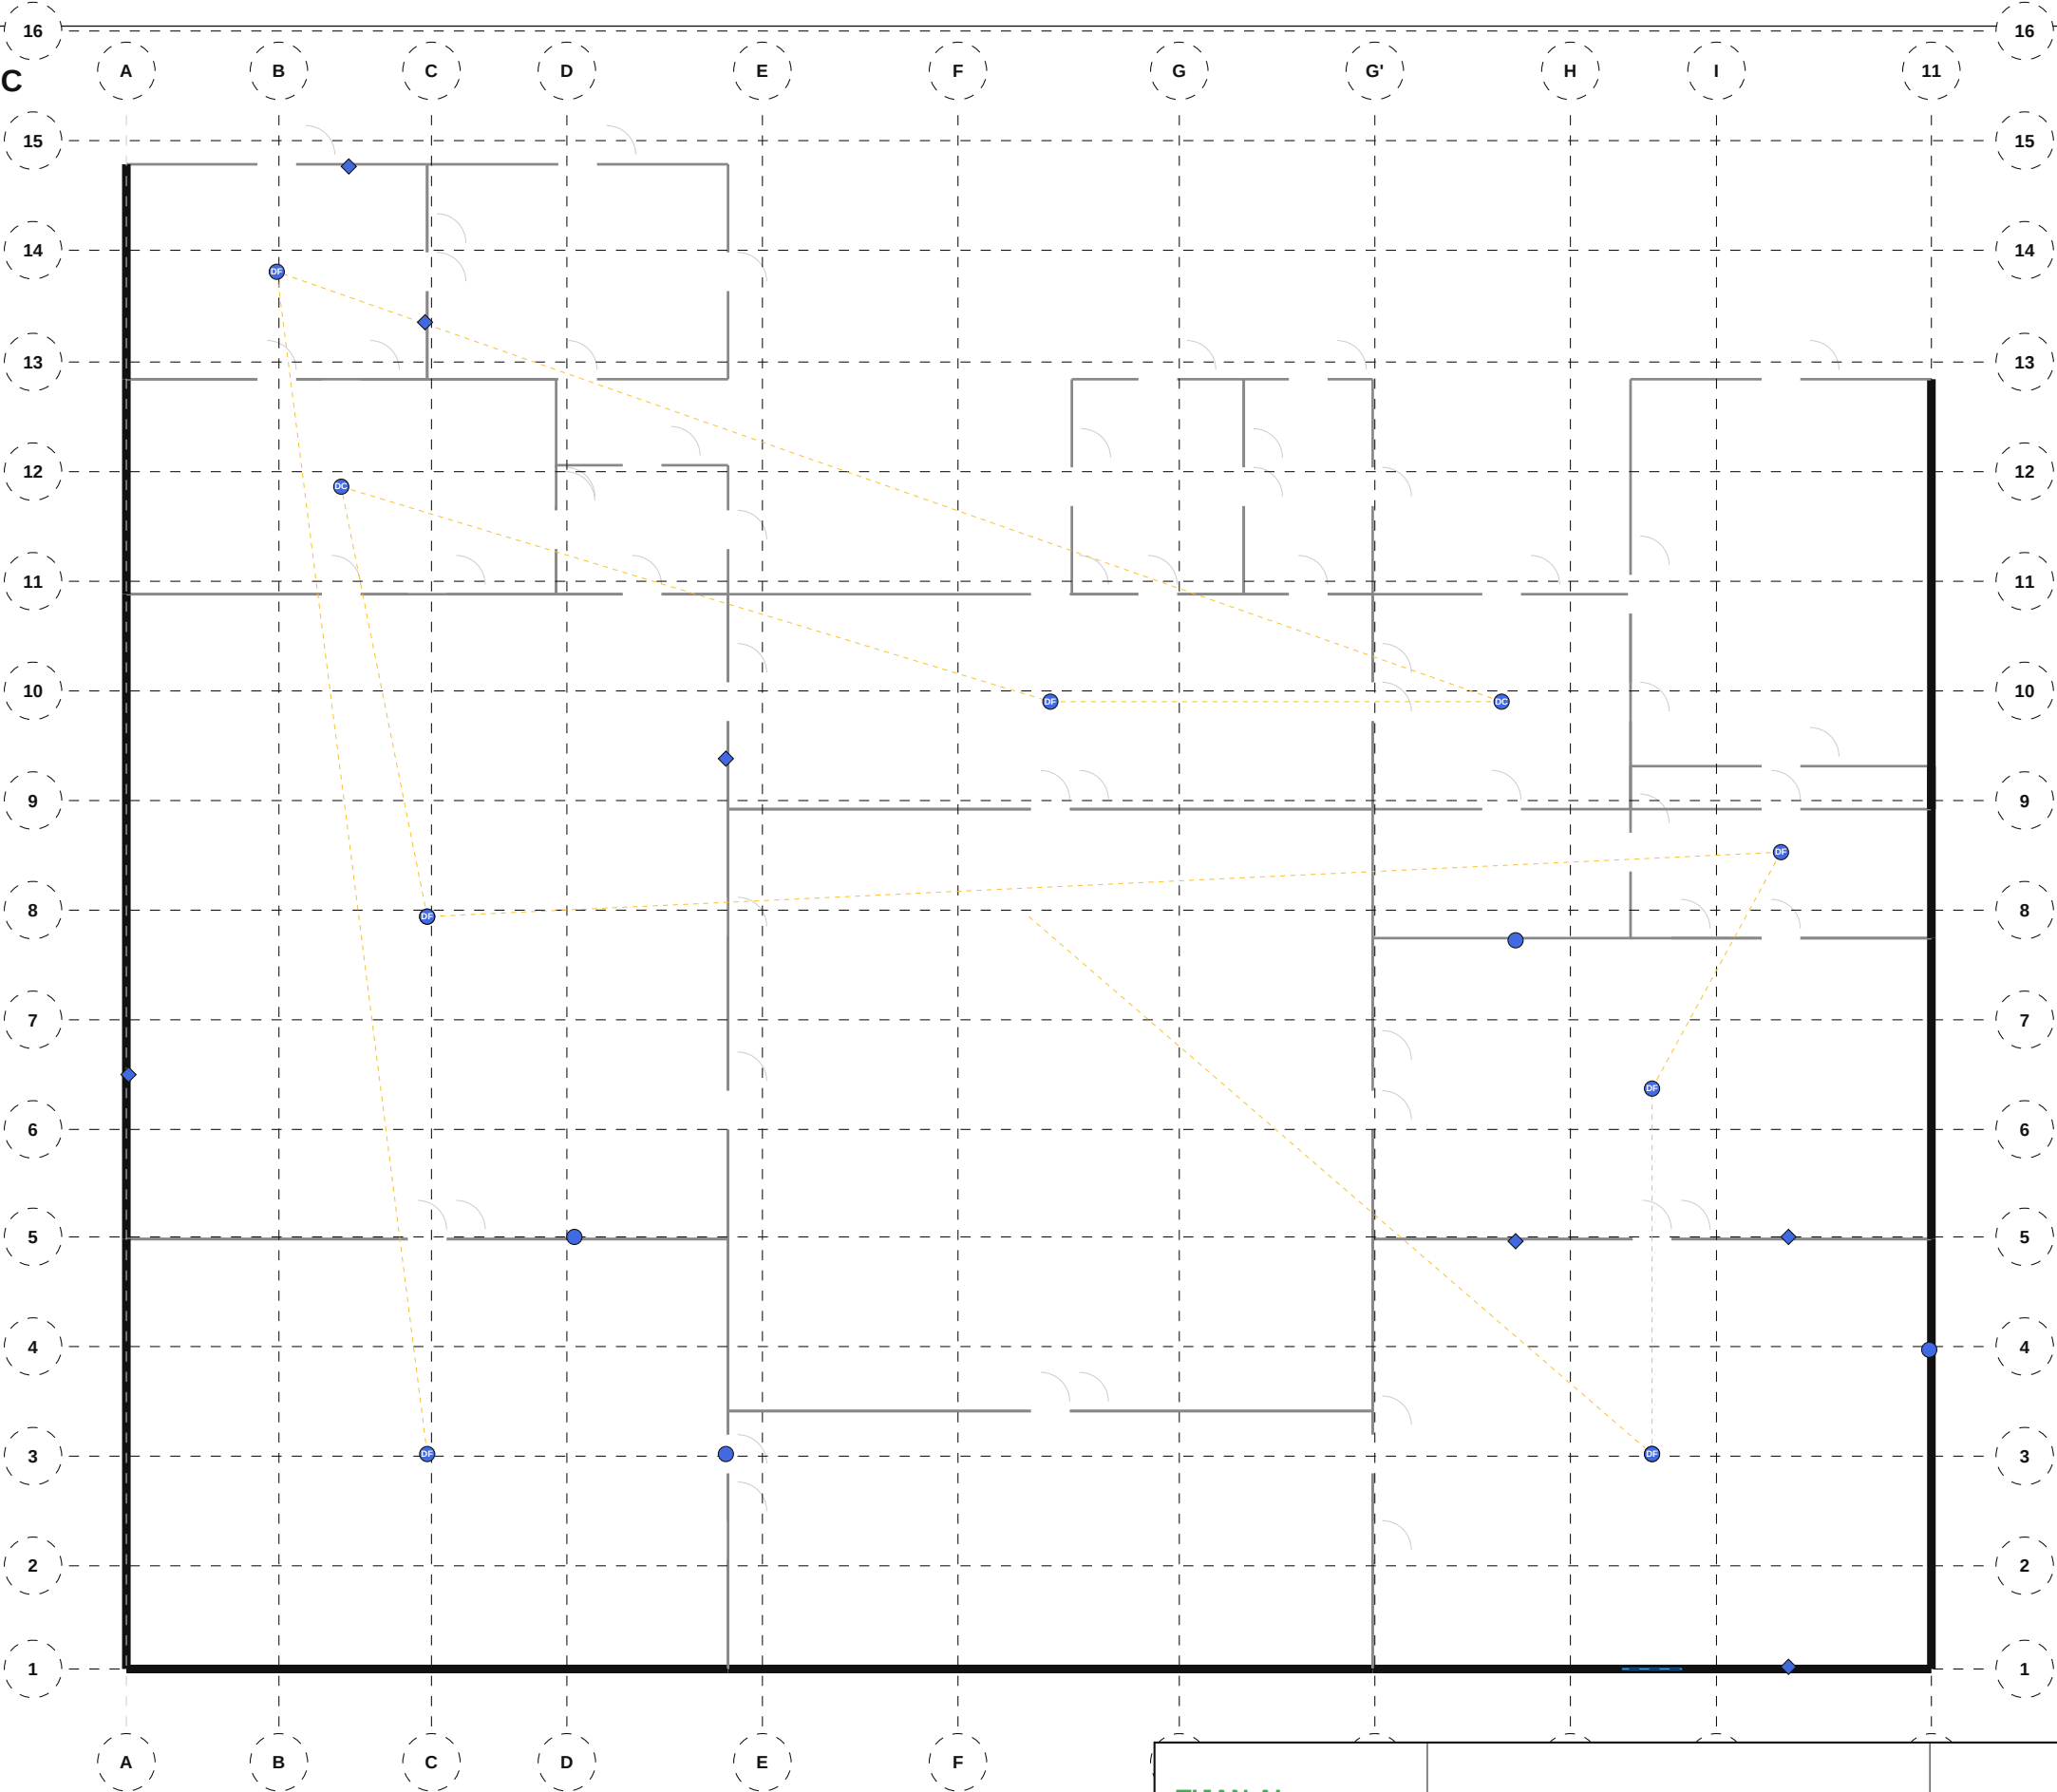

TIJAN AI Bureau d'Études Automatisé	Résidence Papa Oumar Sakho Dakar, Senegal	Éch: 1/100 Pl. 68/88
	Courants Faibles — RDC	
Date: 06/05/2026	Réf: 1711	BIM vLCU-068 Phase: APD

520 Courants Faibles — Étage 1

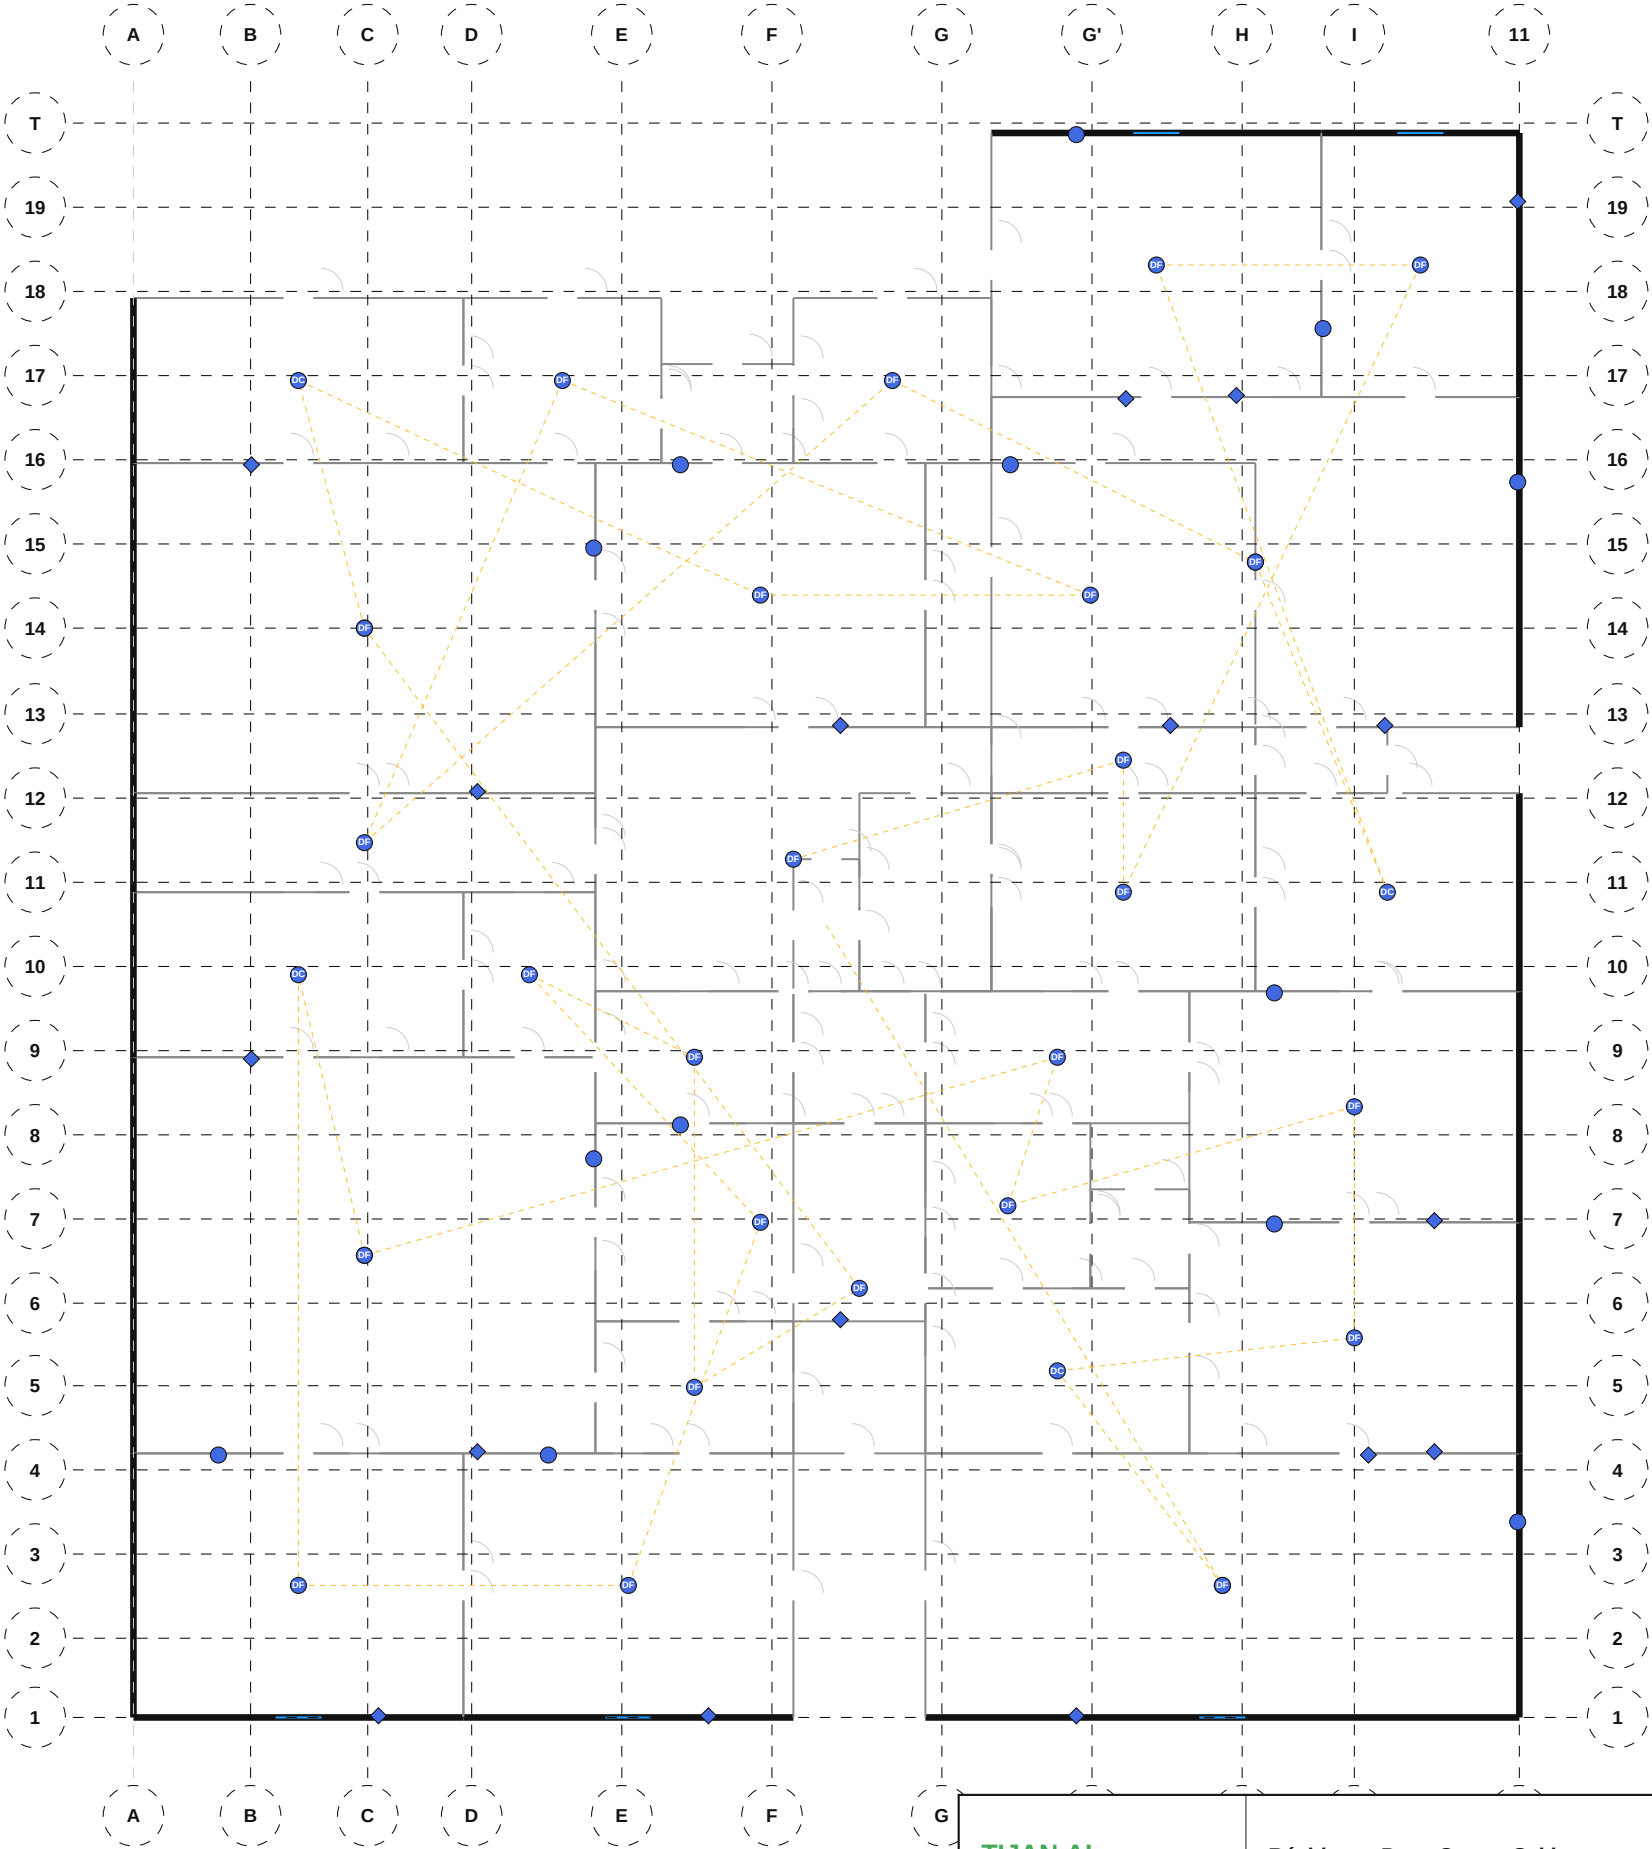


NOMENCLATURE — Courants Faibles

- Détecteur de chaleur: 4
- Détecteur de fumée: 25
- Point d'accès WiFi: 4
- Prise RJ45: 17
- Prise TV: 13

TIJAN AI Bureau d'Études Automatisé	Résidence Papa Oumar Sakho Dakar, Senegal	Éch: 1/100 Pl. 69/88
	Courants Faibles — Étage 1	
Date: 06/05/2026	Réf: 1711	BIM vLCU-069 Phase: APD

520 Courants Faibles — Étage 2

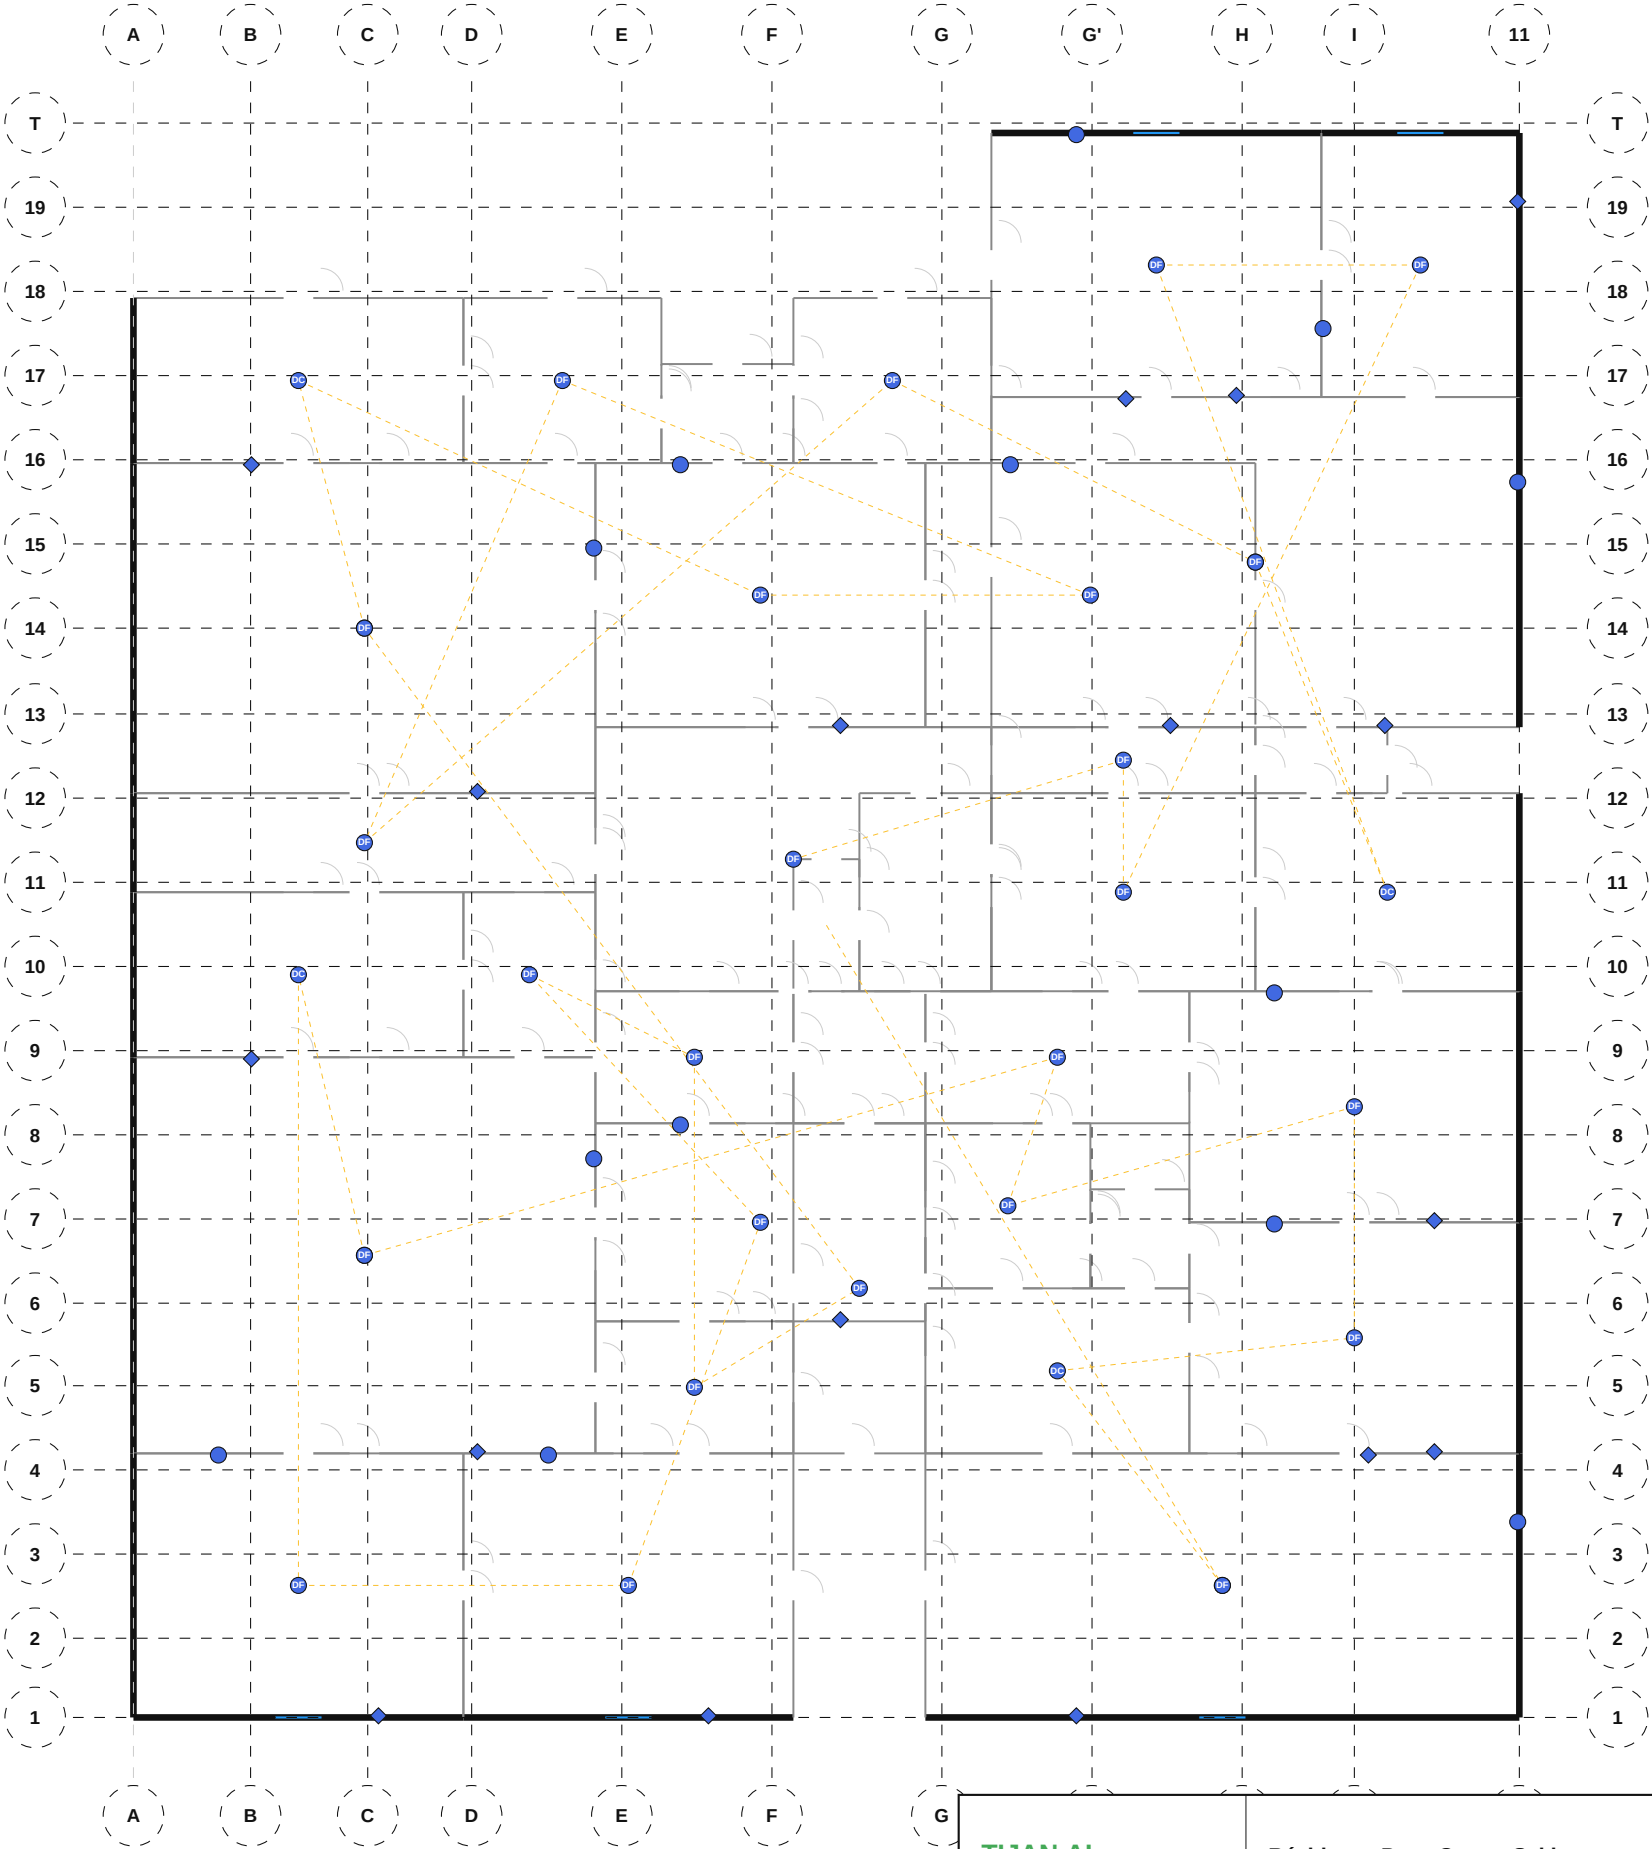


NOMENCLATURE — Courants Faibles

- Détecteur de chaleur: 4
- Détecteur de fumée: 25
- Point d'accès WiFi: 4
- Prise RJ45: 17
- Prise TV: 13

TIJAN AI Bureau d'Études Automatisé	Résidence Papa Oumar Sakho Dakar, Senegal	Éch: 1/100 Pl. 70/88
	Courants Faibles — Étage 2	
Date: 06/05/2026	Réf: 1711	BIM vLCU-070 Phase: APD

520 Courants Faibles — Étage 3

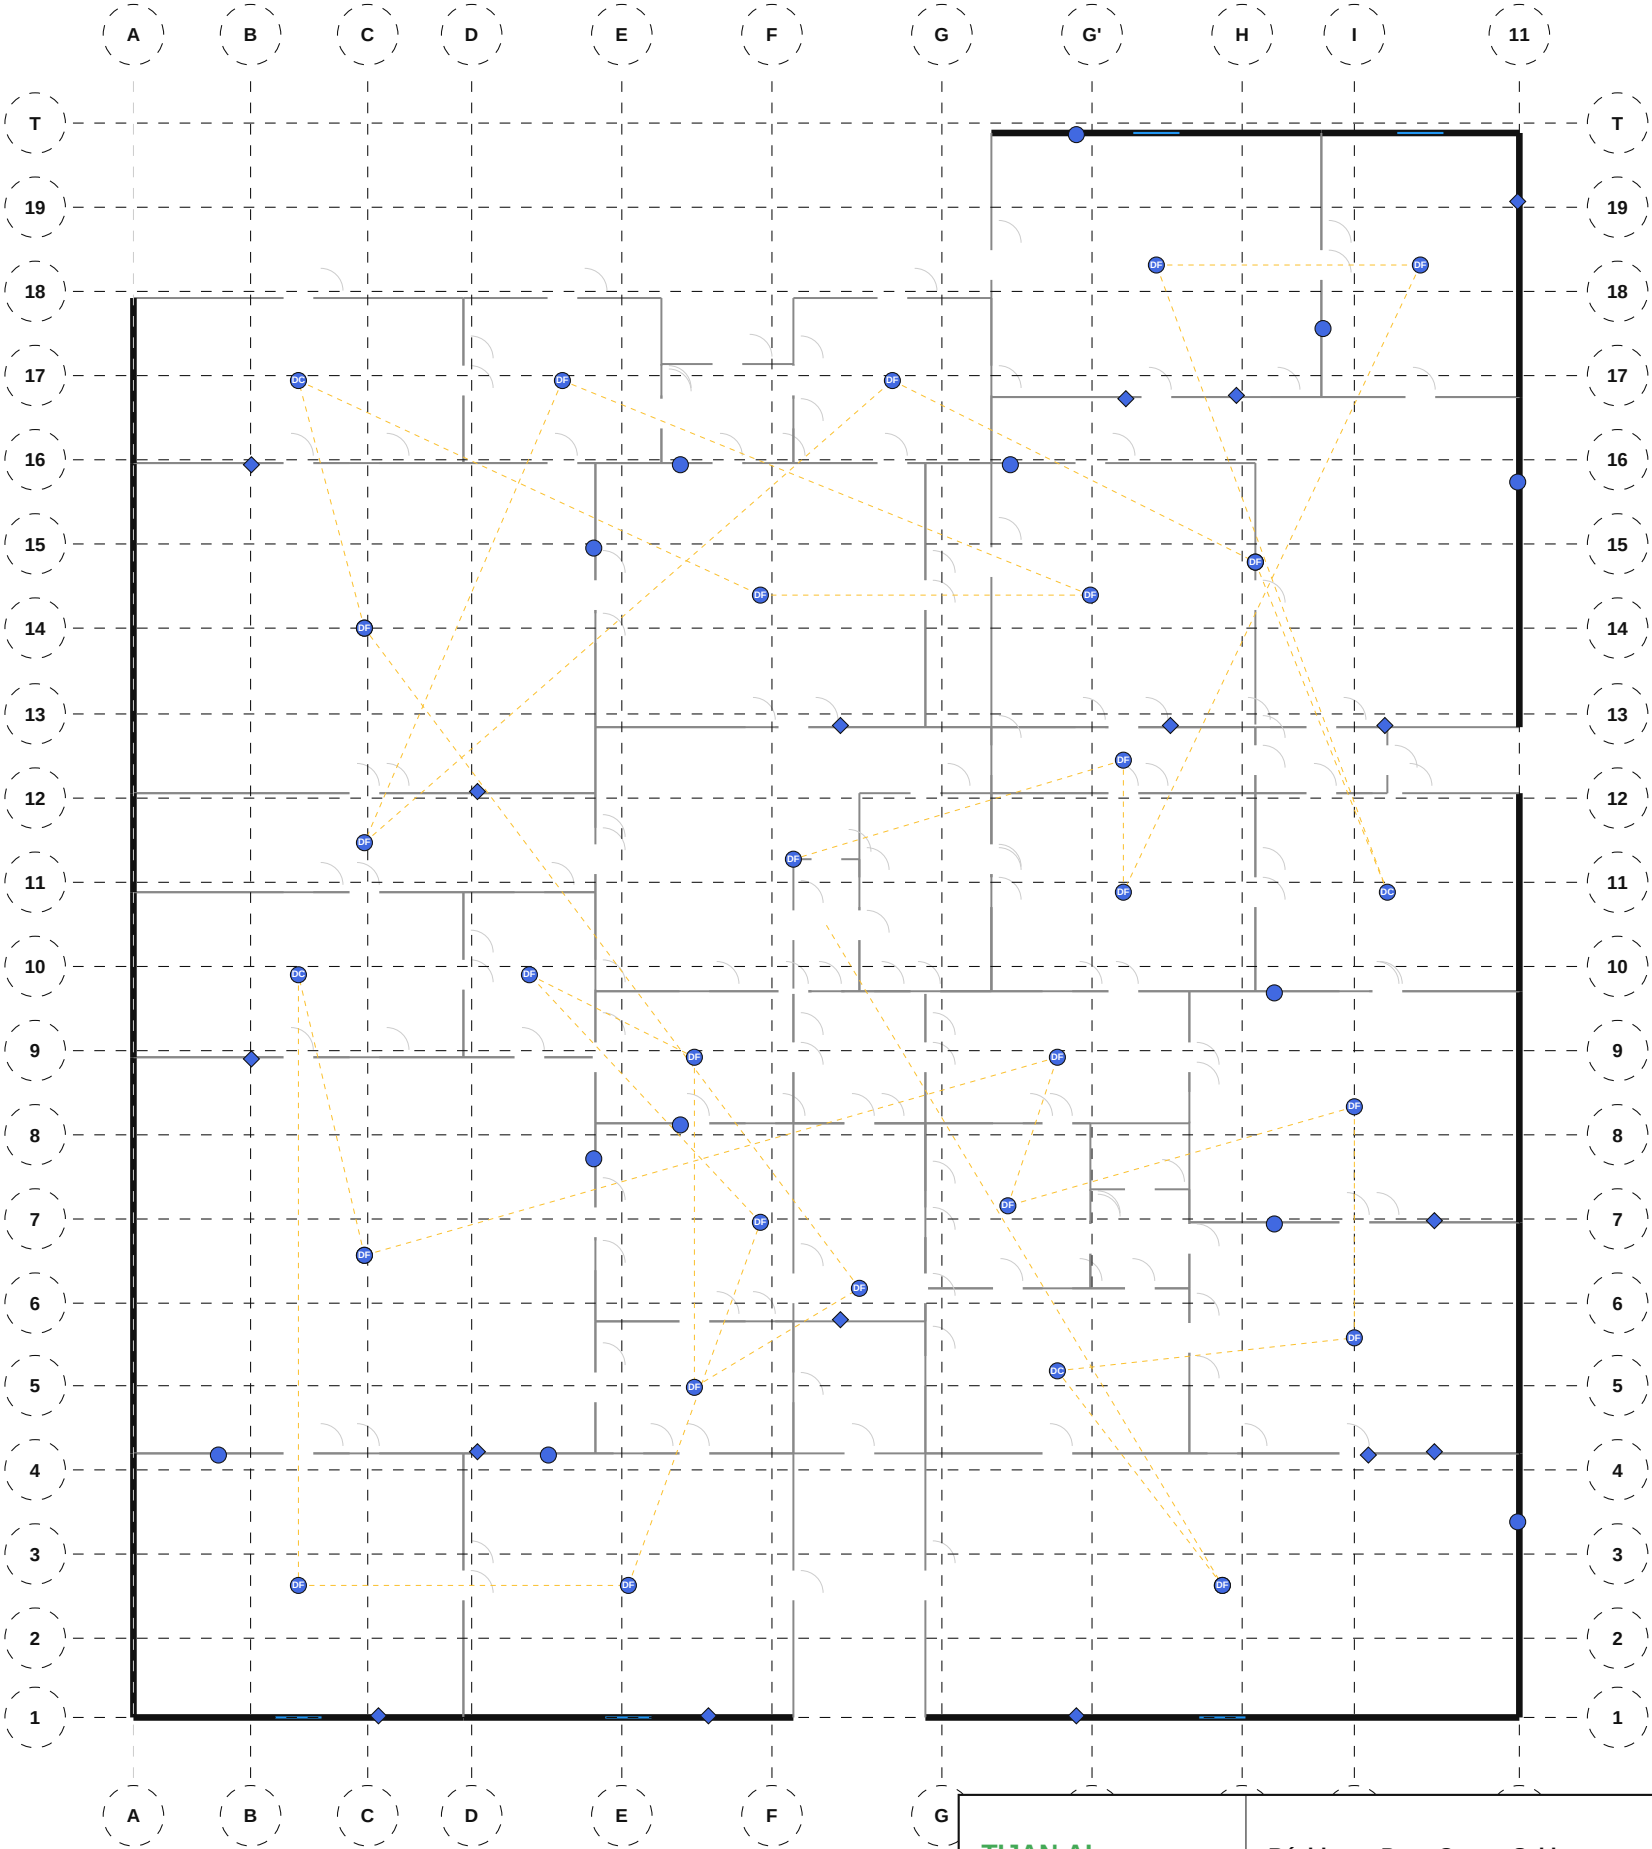


NOMENCLATURE — Courants Faibles

- Détecteur de chaleur: 4
- Détecteur de fumée: 25
- Point d'accès WiFi: 4
- Prise RJ45: 17
- Prise TV: 13

TIJAN AI Bureau d'Études Automatisé	Résidence Papa Oumar Sakho Dakar, Senegal	Éch: 1/100 Pl. 71/88
	Courants Faibles — Étage 3	
Date: 06/05/2026	Réf: 1711	BIM vLCU-071 Phase: APD

520 Courants Faibles — Étage 4

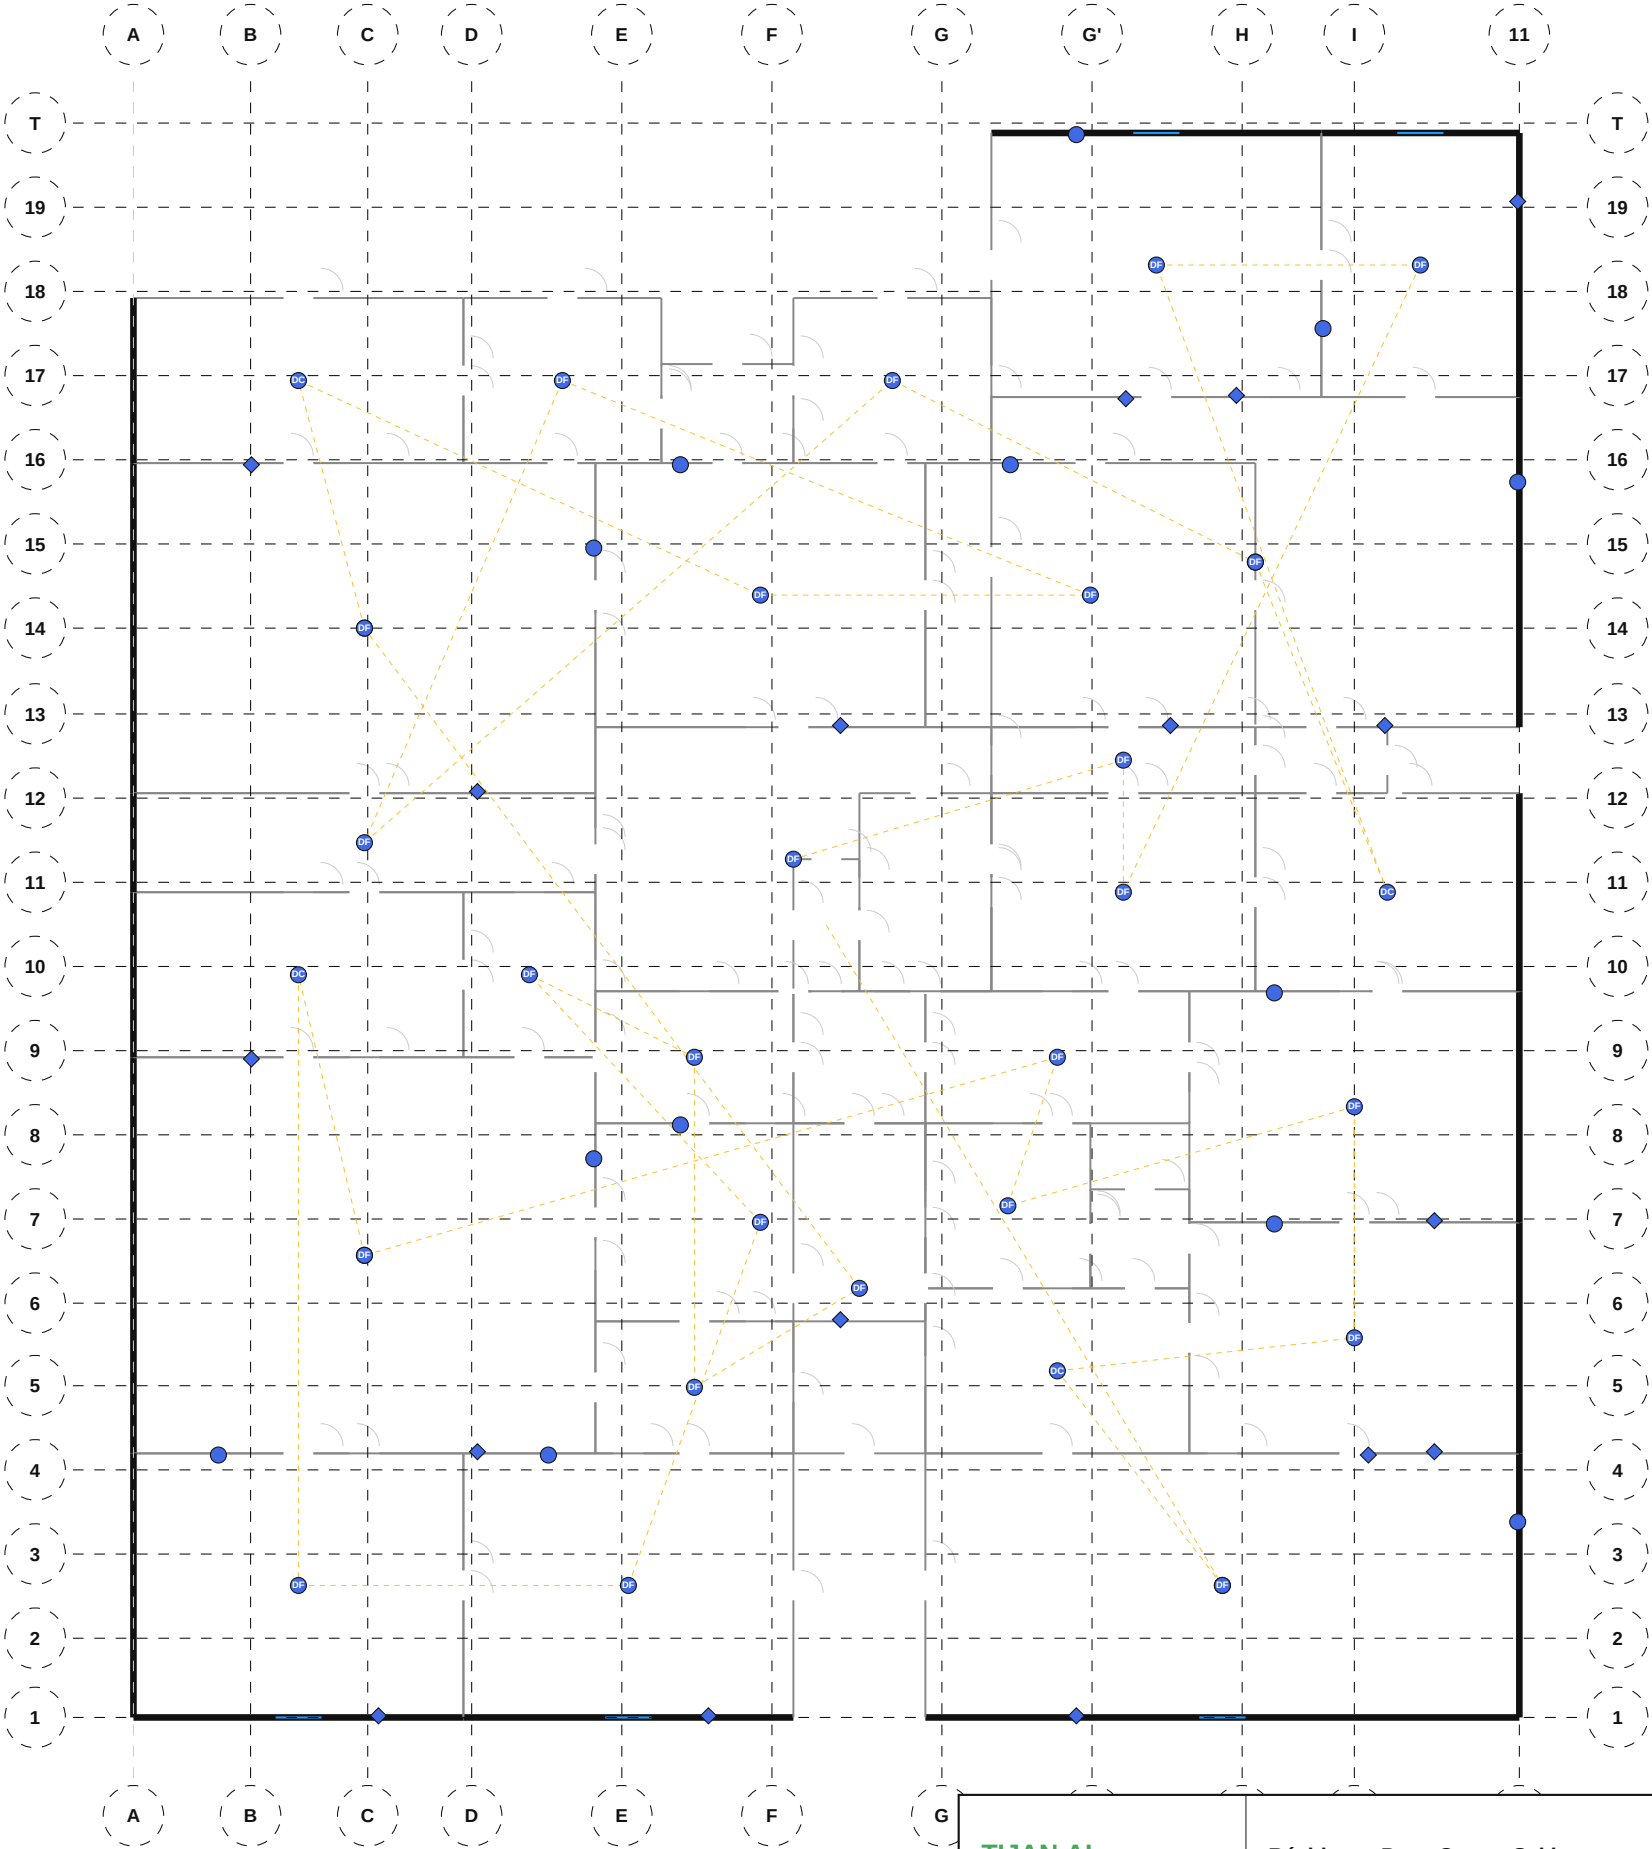


NOMENCLATURE — Courants Faibles

- Détecteur de chaleur: 4
- Détecteur de fumée: 25
- Point d'accès WiFi: 4
- Prise RJ45: 17
- Prise TV: 13

TIJAN AI Bureau d'Études Automatisé	Résidence Papa Oumar Sakho Dakar, Senegal	Éch: 1/100 Pl. 72/88
	Courants Faibles — Étage 4	
Date: 06/05/2026	Réf: 1711	BIM vLCU-072 Phase: APD

520 Courants Faibles — Étage 5

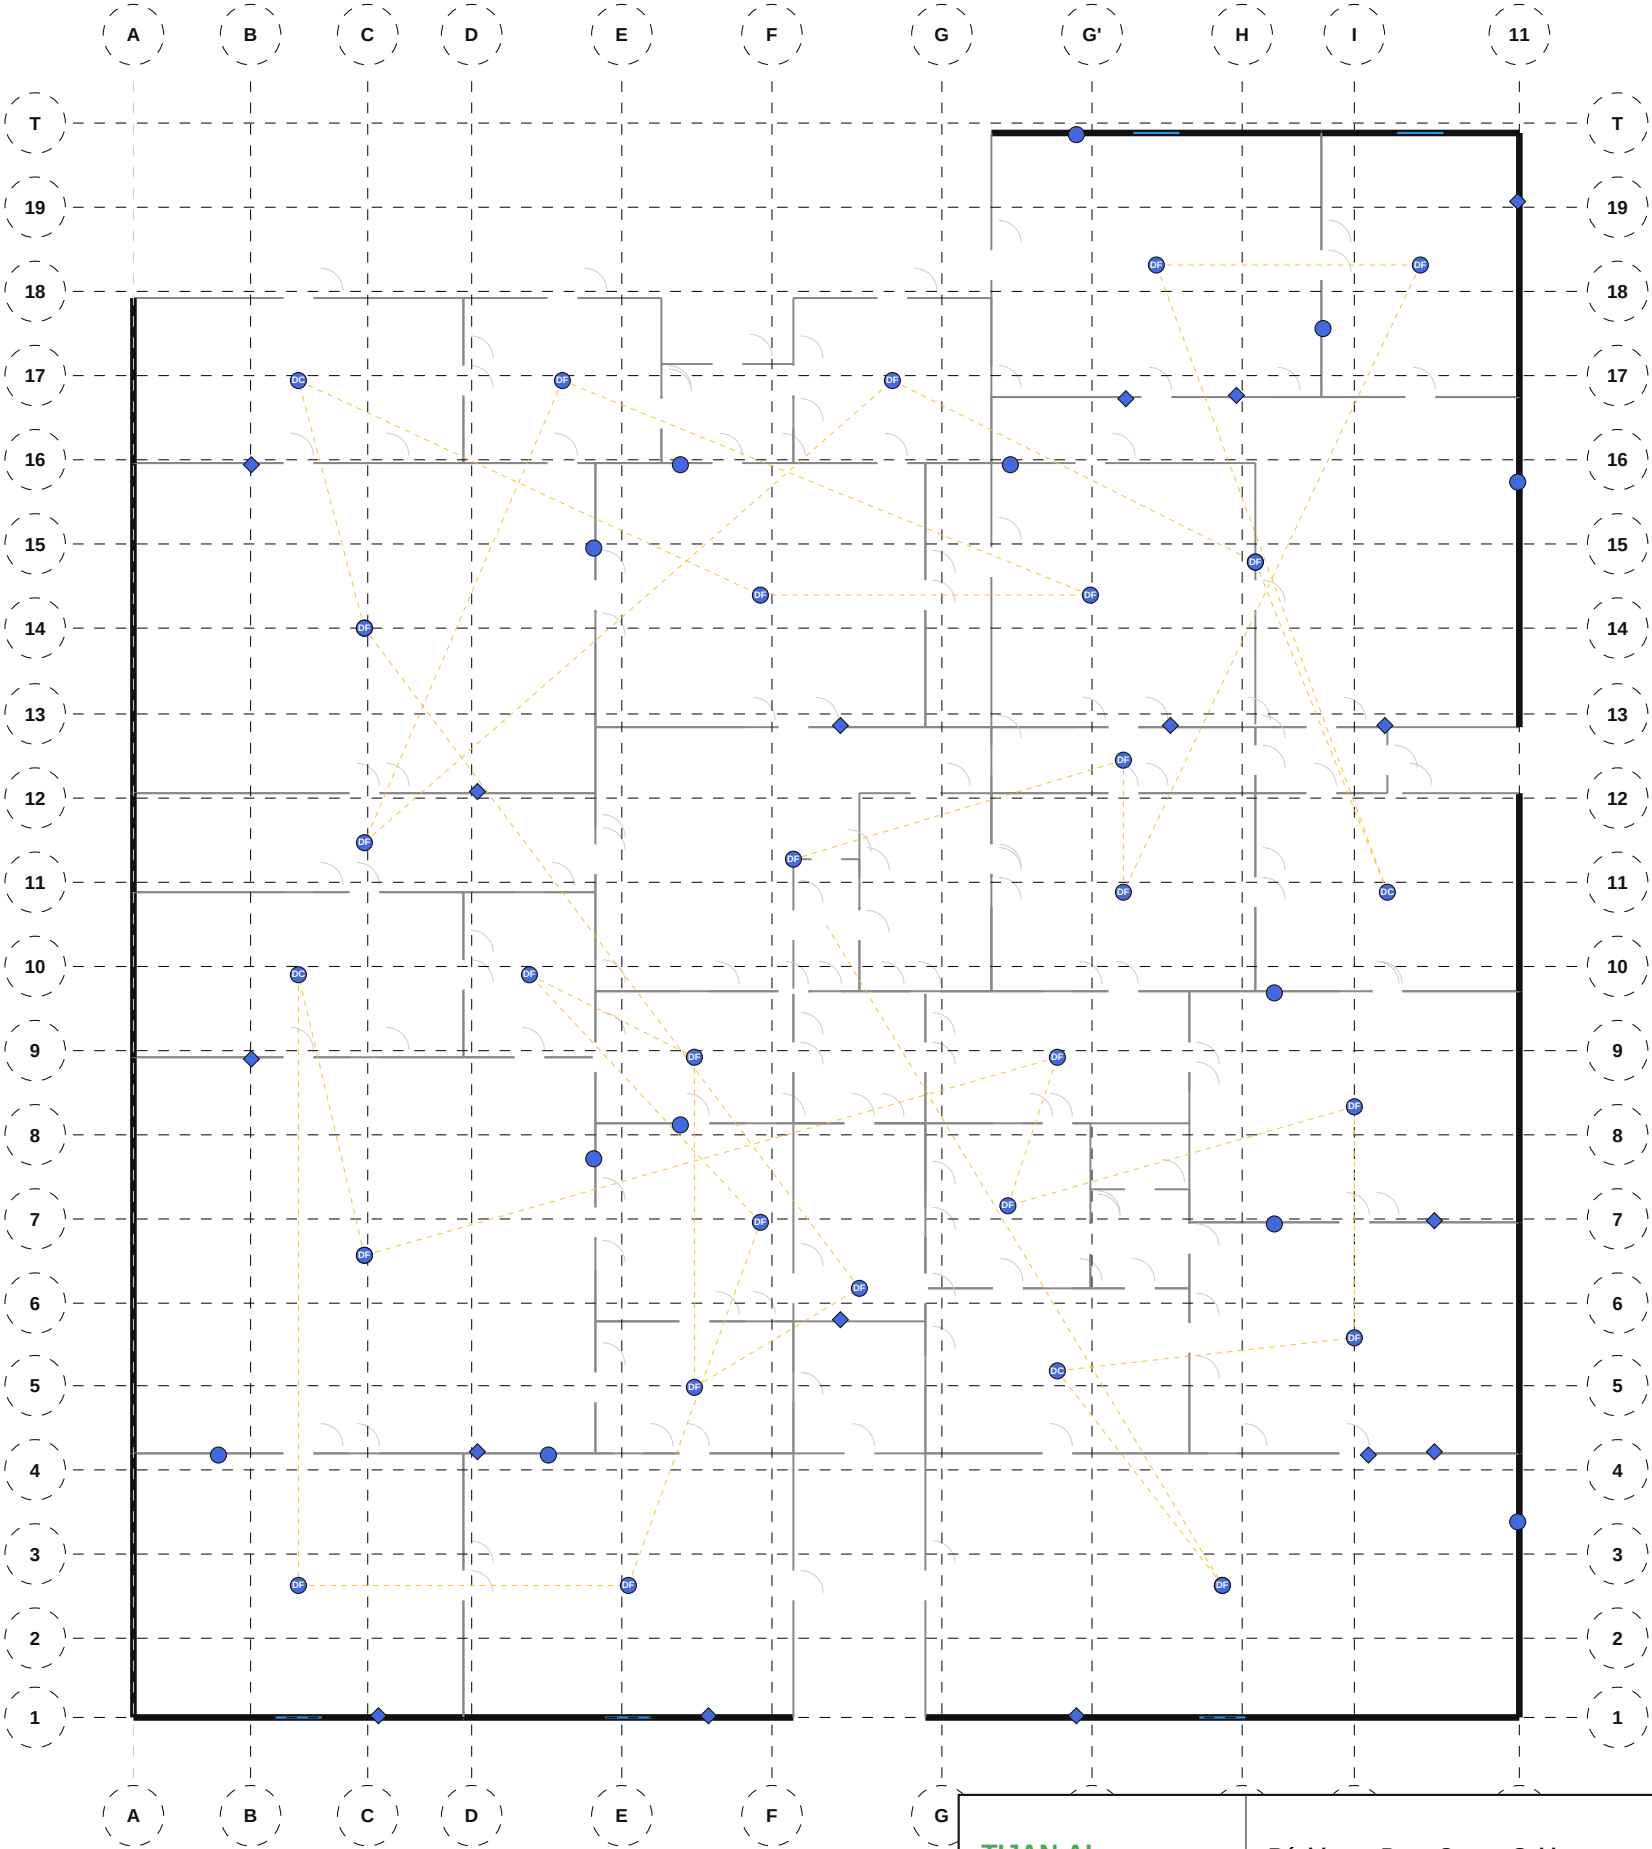


NOMENCLATURE — Courants Faibles

- Détecteur de chaleur: 4
- Détecteur de fumée: 25
- Point d'accès WiFi: 4
- Prise RJ45: 17
- Prise TV: 13

TIJAN AI Bureau d'Études Automatisé	Résidence Papa Oumar Sakho Dakar, Senegal	Éch: 1/100 Pl. 73/88
	Courants Faibles — Étage 5	
Date: 06/05/2026	Réf: 1711	BIM vLCU-073 Phase: APD

520 Courants Faibles — Étage 6

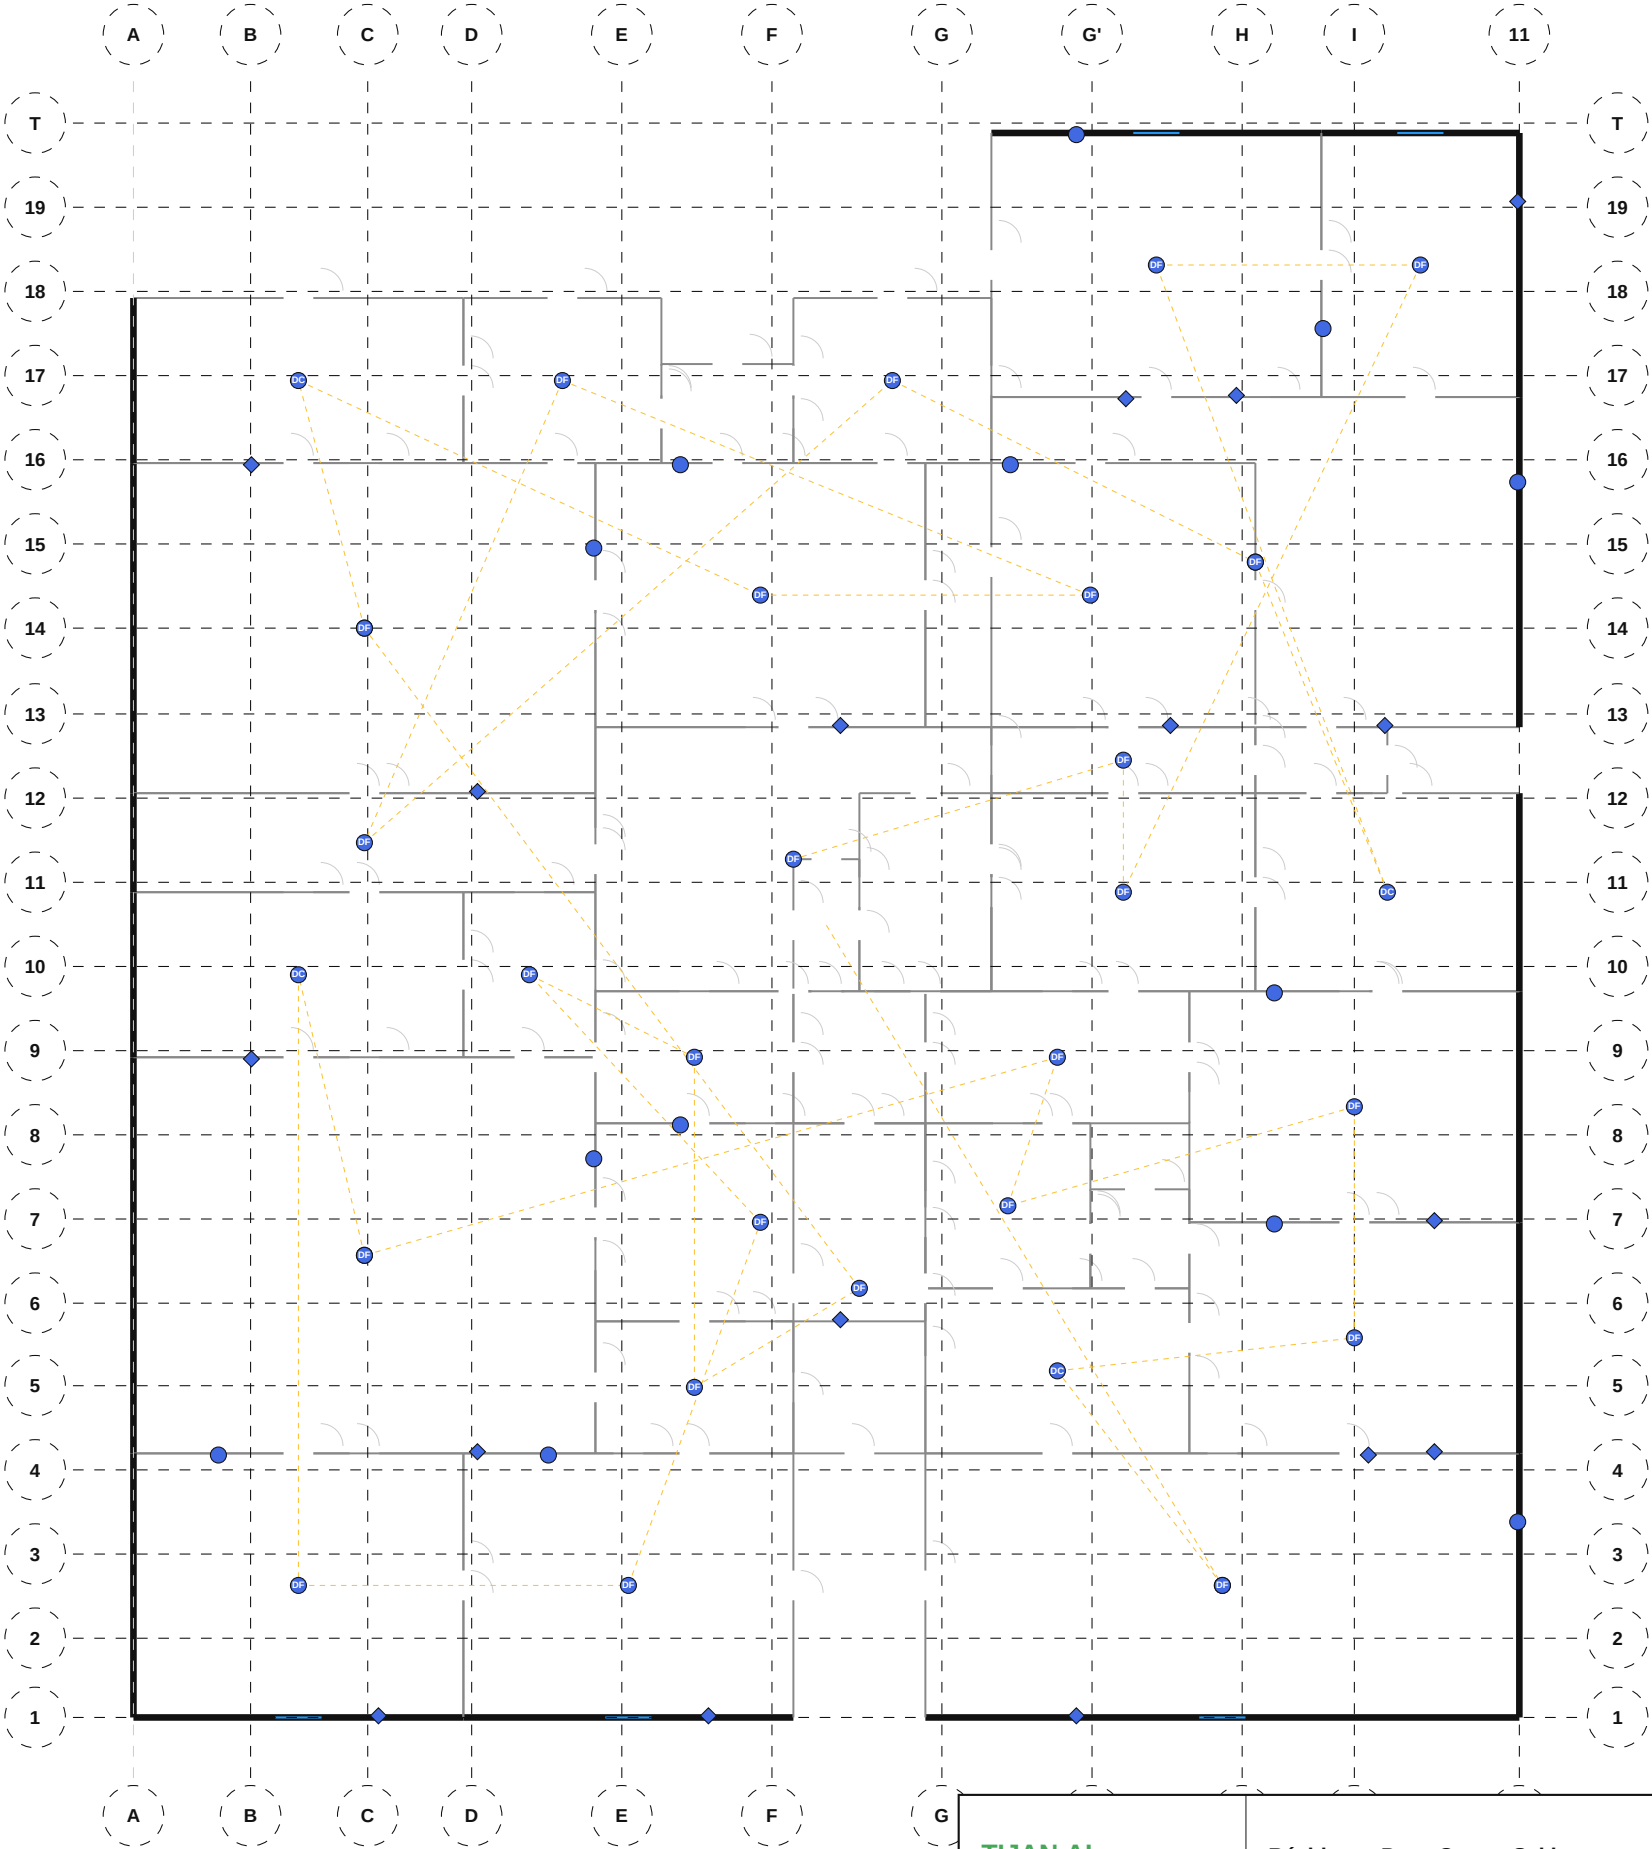


NOMENCLATURE — Courants Faibles

- Détecteur de chaleur: 4
- Détecteur de fumée: 25
- Point d'accès WiFi: 4
- Prise RJ45: 17
- Prise TV: 13

TIJAN AI Bureau d'Études Automatisé	Résidence Papa Oumar Sakho Dakar, Senegal	Éch: 1/100 Pl. 74/88
	Courants Faibles — Étage 6	
Date: 06/05/2026	Réf: 1711	BIM vLCU-074 Phase: APD


520 Courants Faibles — Étage 7

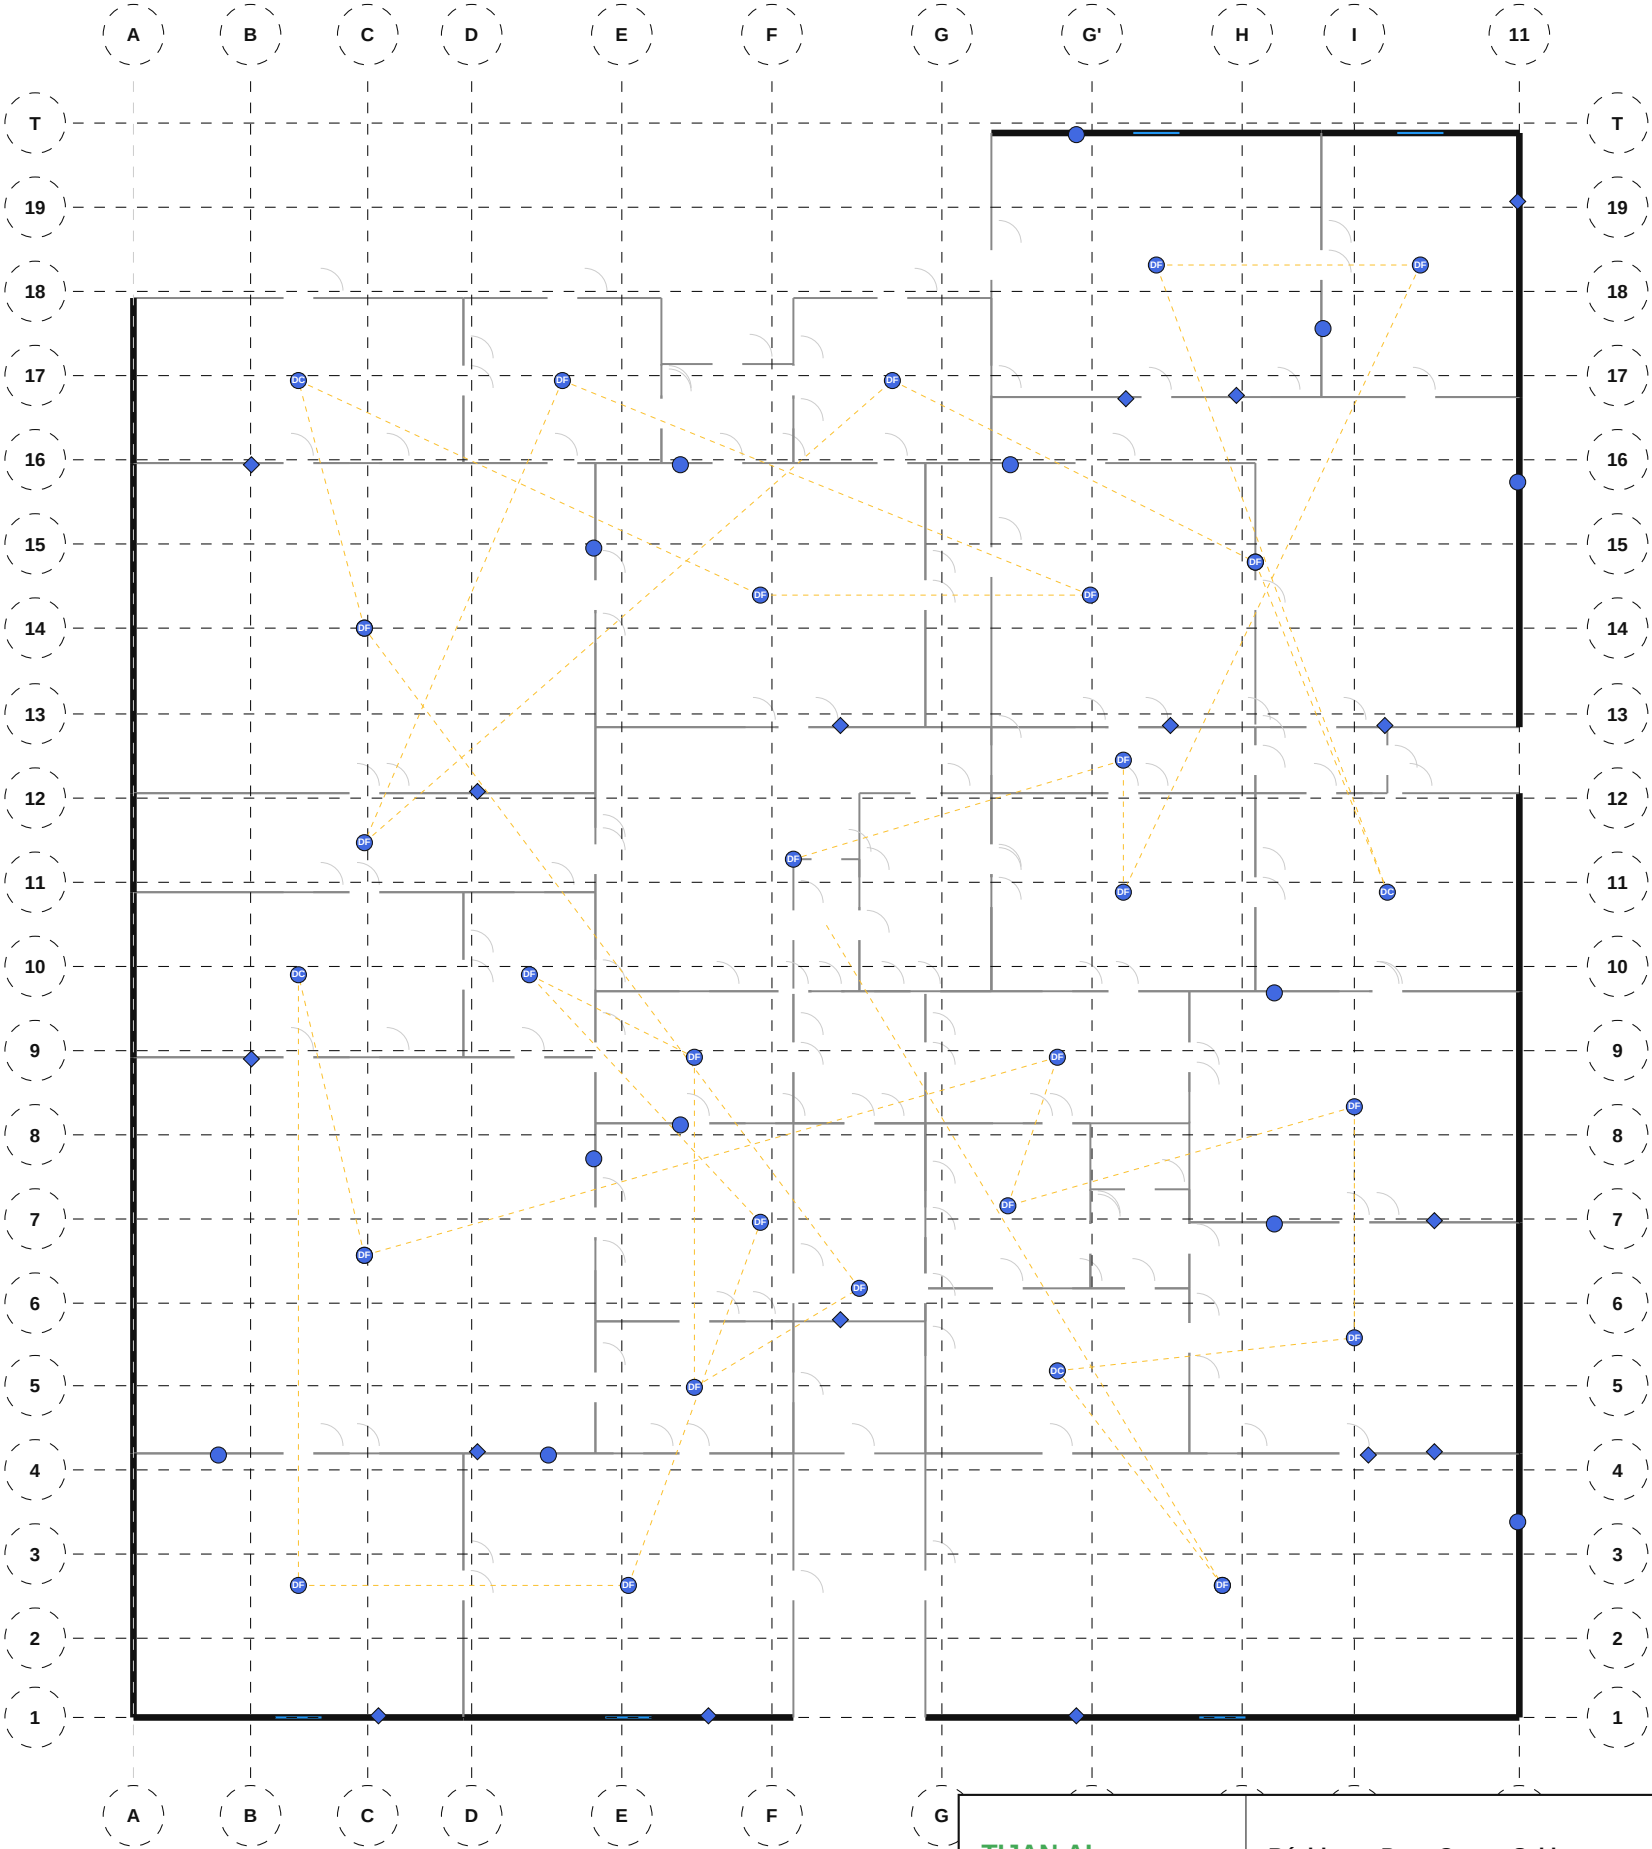

NOMENCLATURE — Courants Faibles

- Détecteur de chaleur: 4
- Détecteur de fumée: 25
- Point d'accès WiFi: 4
- Prise RJ45: 17
- Prise TV: 13

TIJAN AI Bureau d'Études Automatisé	Résidence Papa Oumar Sakho Dakar, Senegal	Éch: 1/100 Pl. 75/88
	Courants Faibles — Étage 7	
Date: 06/05/2026	Réf: 1711	BIM vLCU-075 Phase: APD

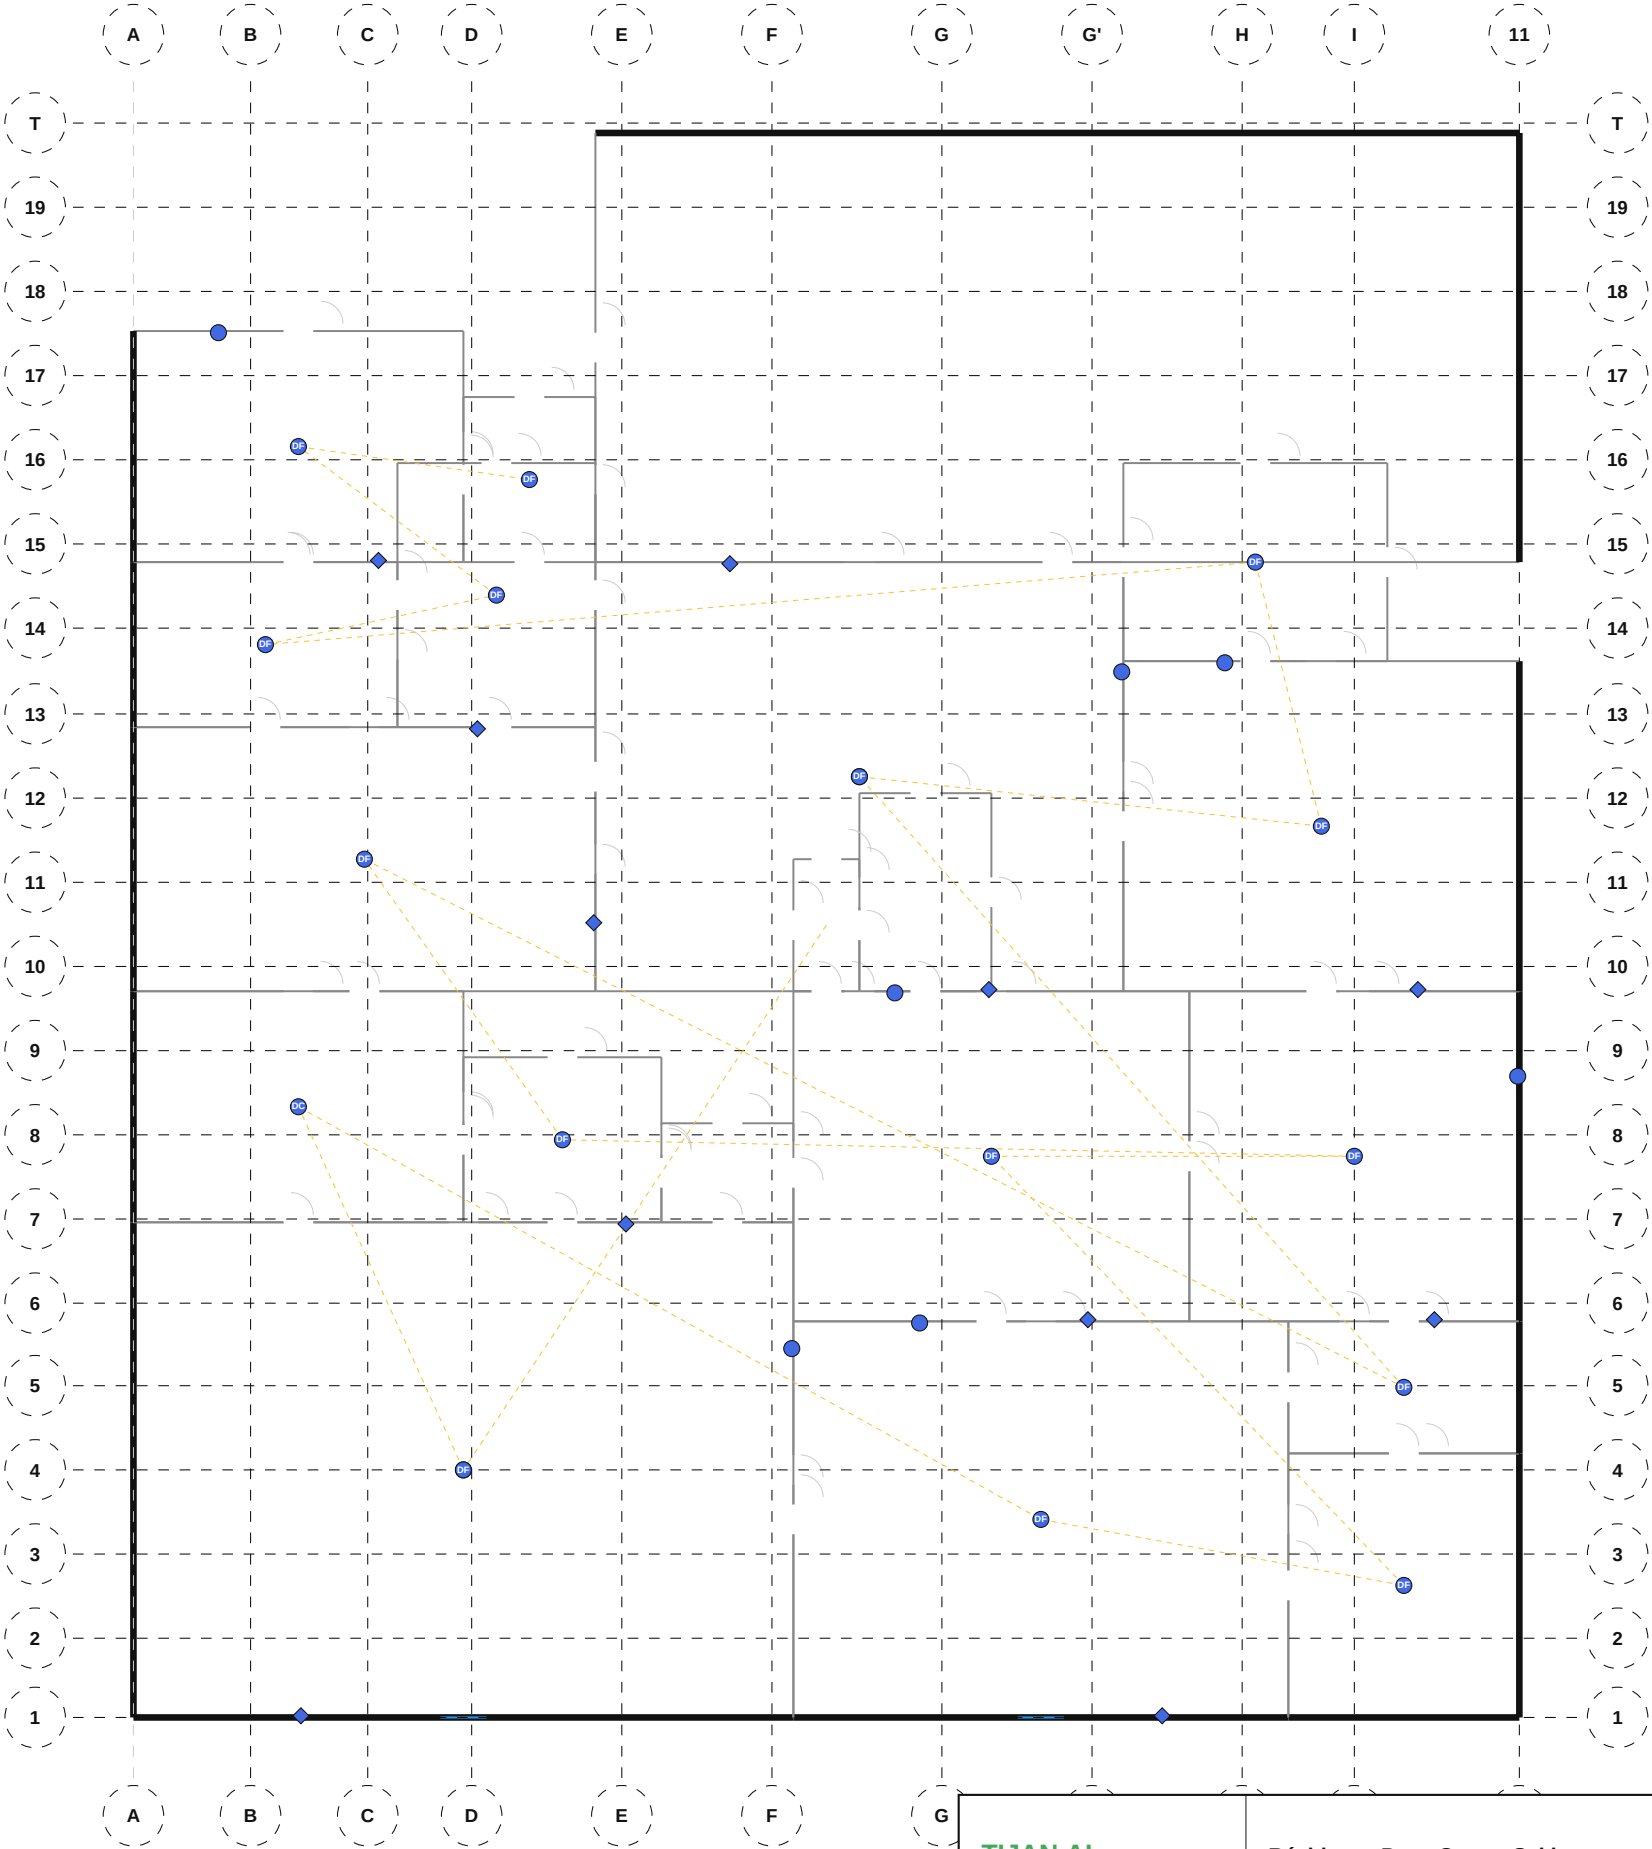


NOMENCLATURE — Courants Faibles

- Détecteur de chaleur: 1
- Détecteur de fumée: 15
- Point d'accès WiFi: 2
- Prise RJ45: 11
- Prise TV: 7

TIJAN AI Bureau d'Études Automatisé	Résidence Papa Oumar Sakho Dakar, Senegal	Éch: 1/100 Pl. 76/88
	Courants Faibles — Étage 8	
Date: 06/05/2026	Réf: 1711	BIM vLCU-076 Phase: APD

520 Courants Faibles — Terrasse

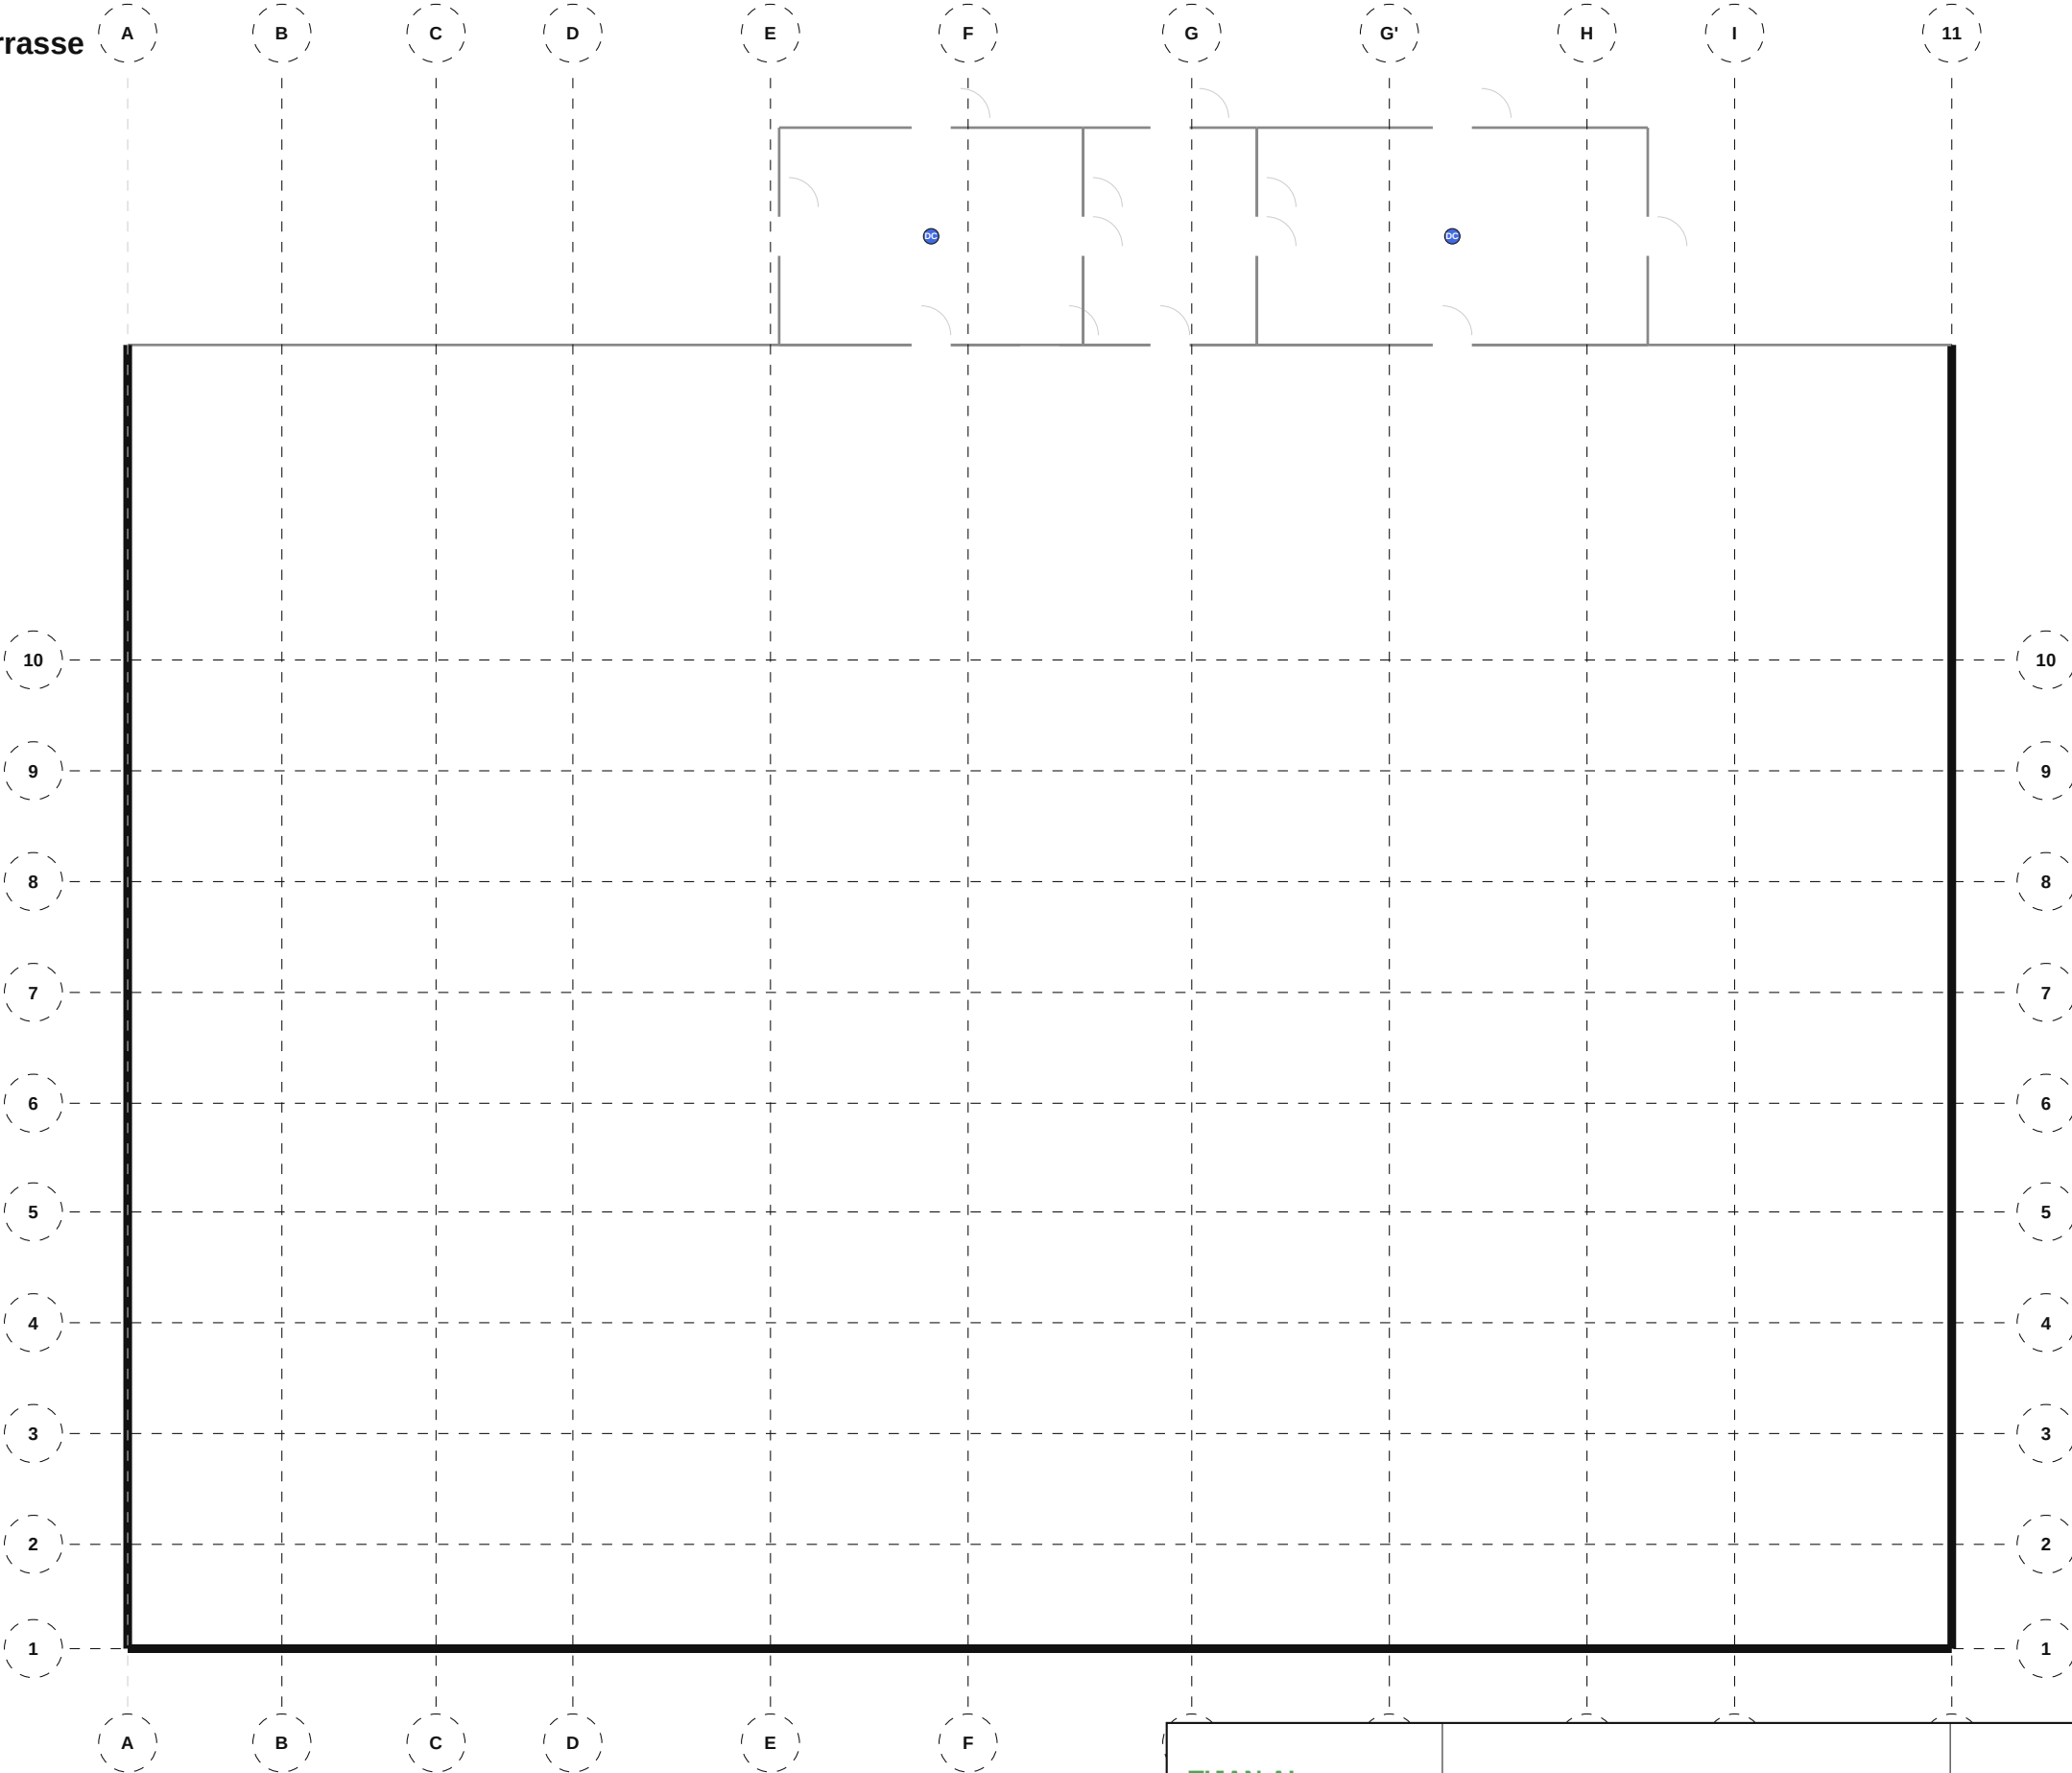

NOMENCLATURE — Courants Faibles


• Détecteur de chaleur: 2

TIJAN AI Bureau d'Études Automatisé	Résidence Papa Oumar Sakho Dakar, Senegal	Éch: 1/100 Pl. 77/88
	Courants Faibles — Terrasse	
Date: 06/05/2026	Réf: 1711	BIM vLCU-077 Phase: APD

001 Synthèse / Coordination — Sous-Sol

LÉGENDE RÉSEAUX

- EF — Eau Froide
- EC — Eau Chaude
- EU — Eaux Usées
- CLIM — Réfrigérant
- VMC — Extraction
- HCU — Courants Forts
- LCU — Courants Faibles
- SPK — Sprinkler

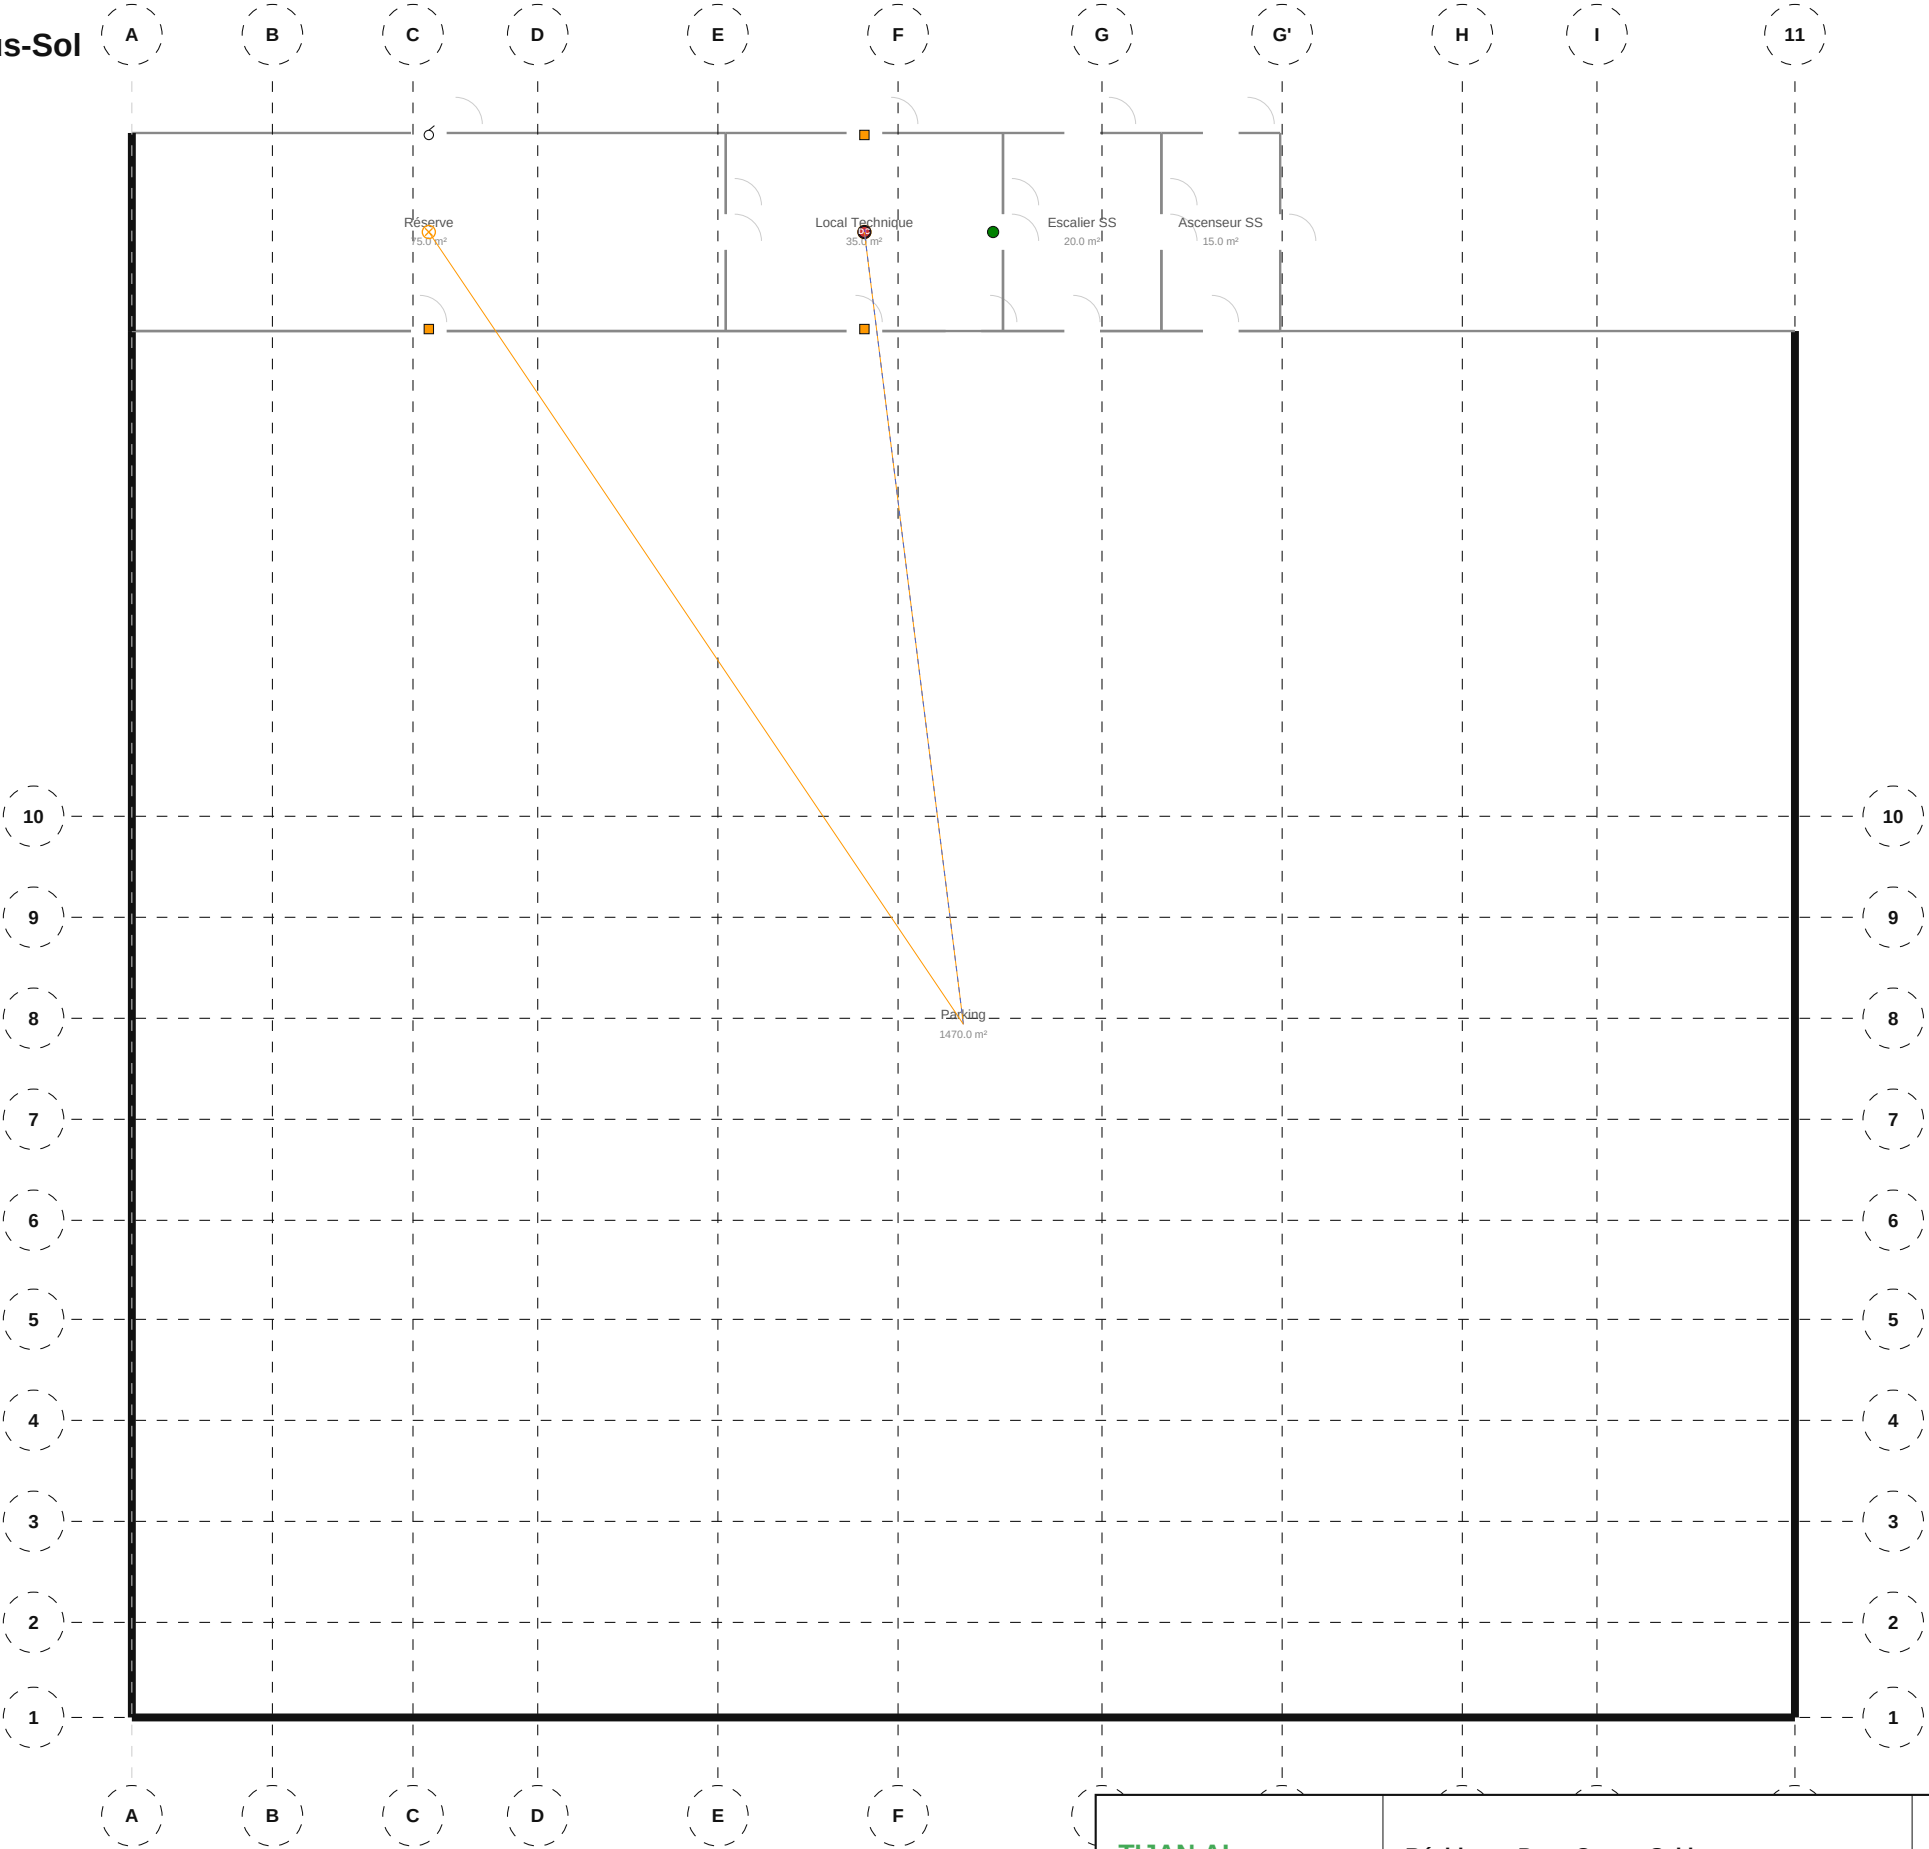


TIJAN AI Bureau d'Études Automatisé	Résidence Papa Oumar Sakho Dakar, Senegal	Éch: 1/100 Pl. 78/88
	Synthèse / Coordination — Sous-Sol	
Date: 06/05/2026	Réf: 1711	BIM vSYN-078 Phase: APD

001 Synthèse / Coordination — RD

LÉGENDE RÉSEAUX

- EF — Eau Froide
- EC — Eau Chaude
- EU — Eaux Usées
- CLIM — Réfrigérant
- VMC — Extraction
- HCU — Courants Forts
- LCU — Courants Faibles
- SPK — Sprinkler

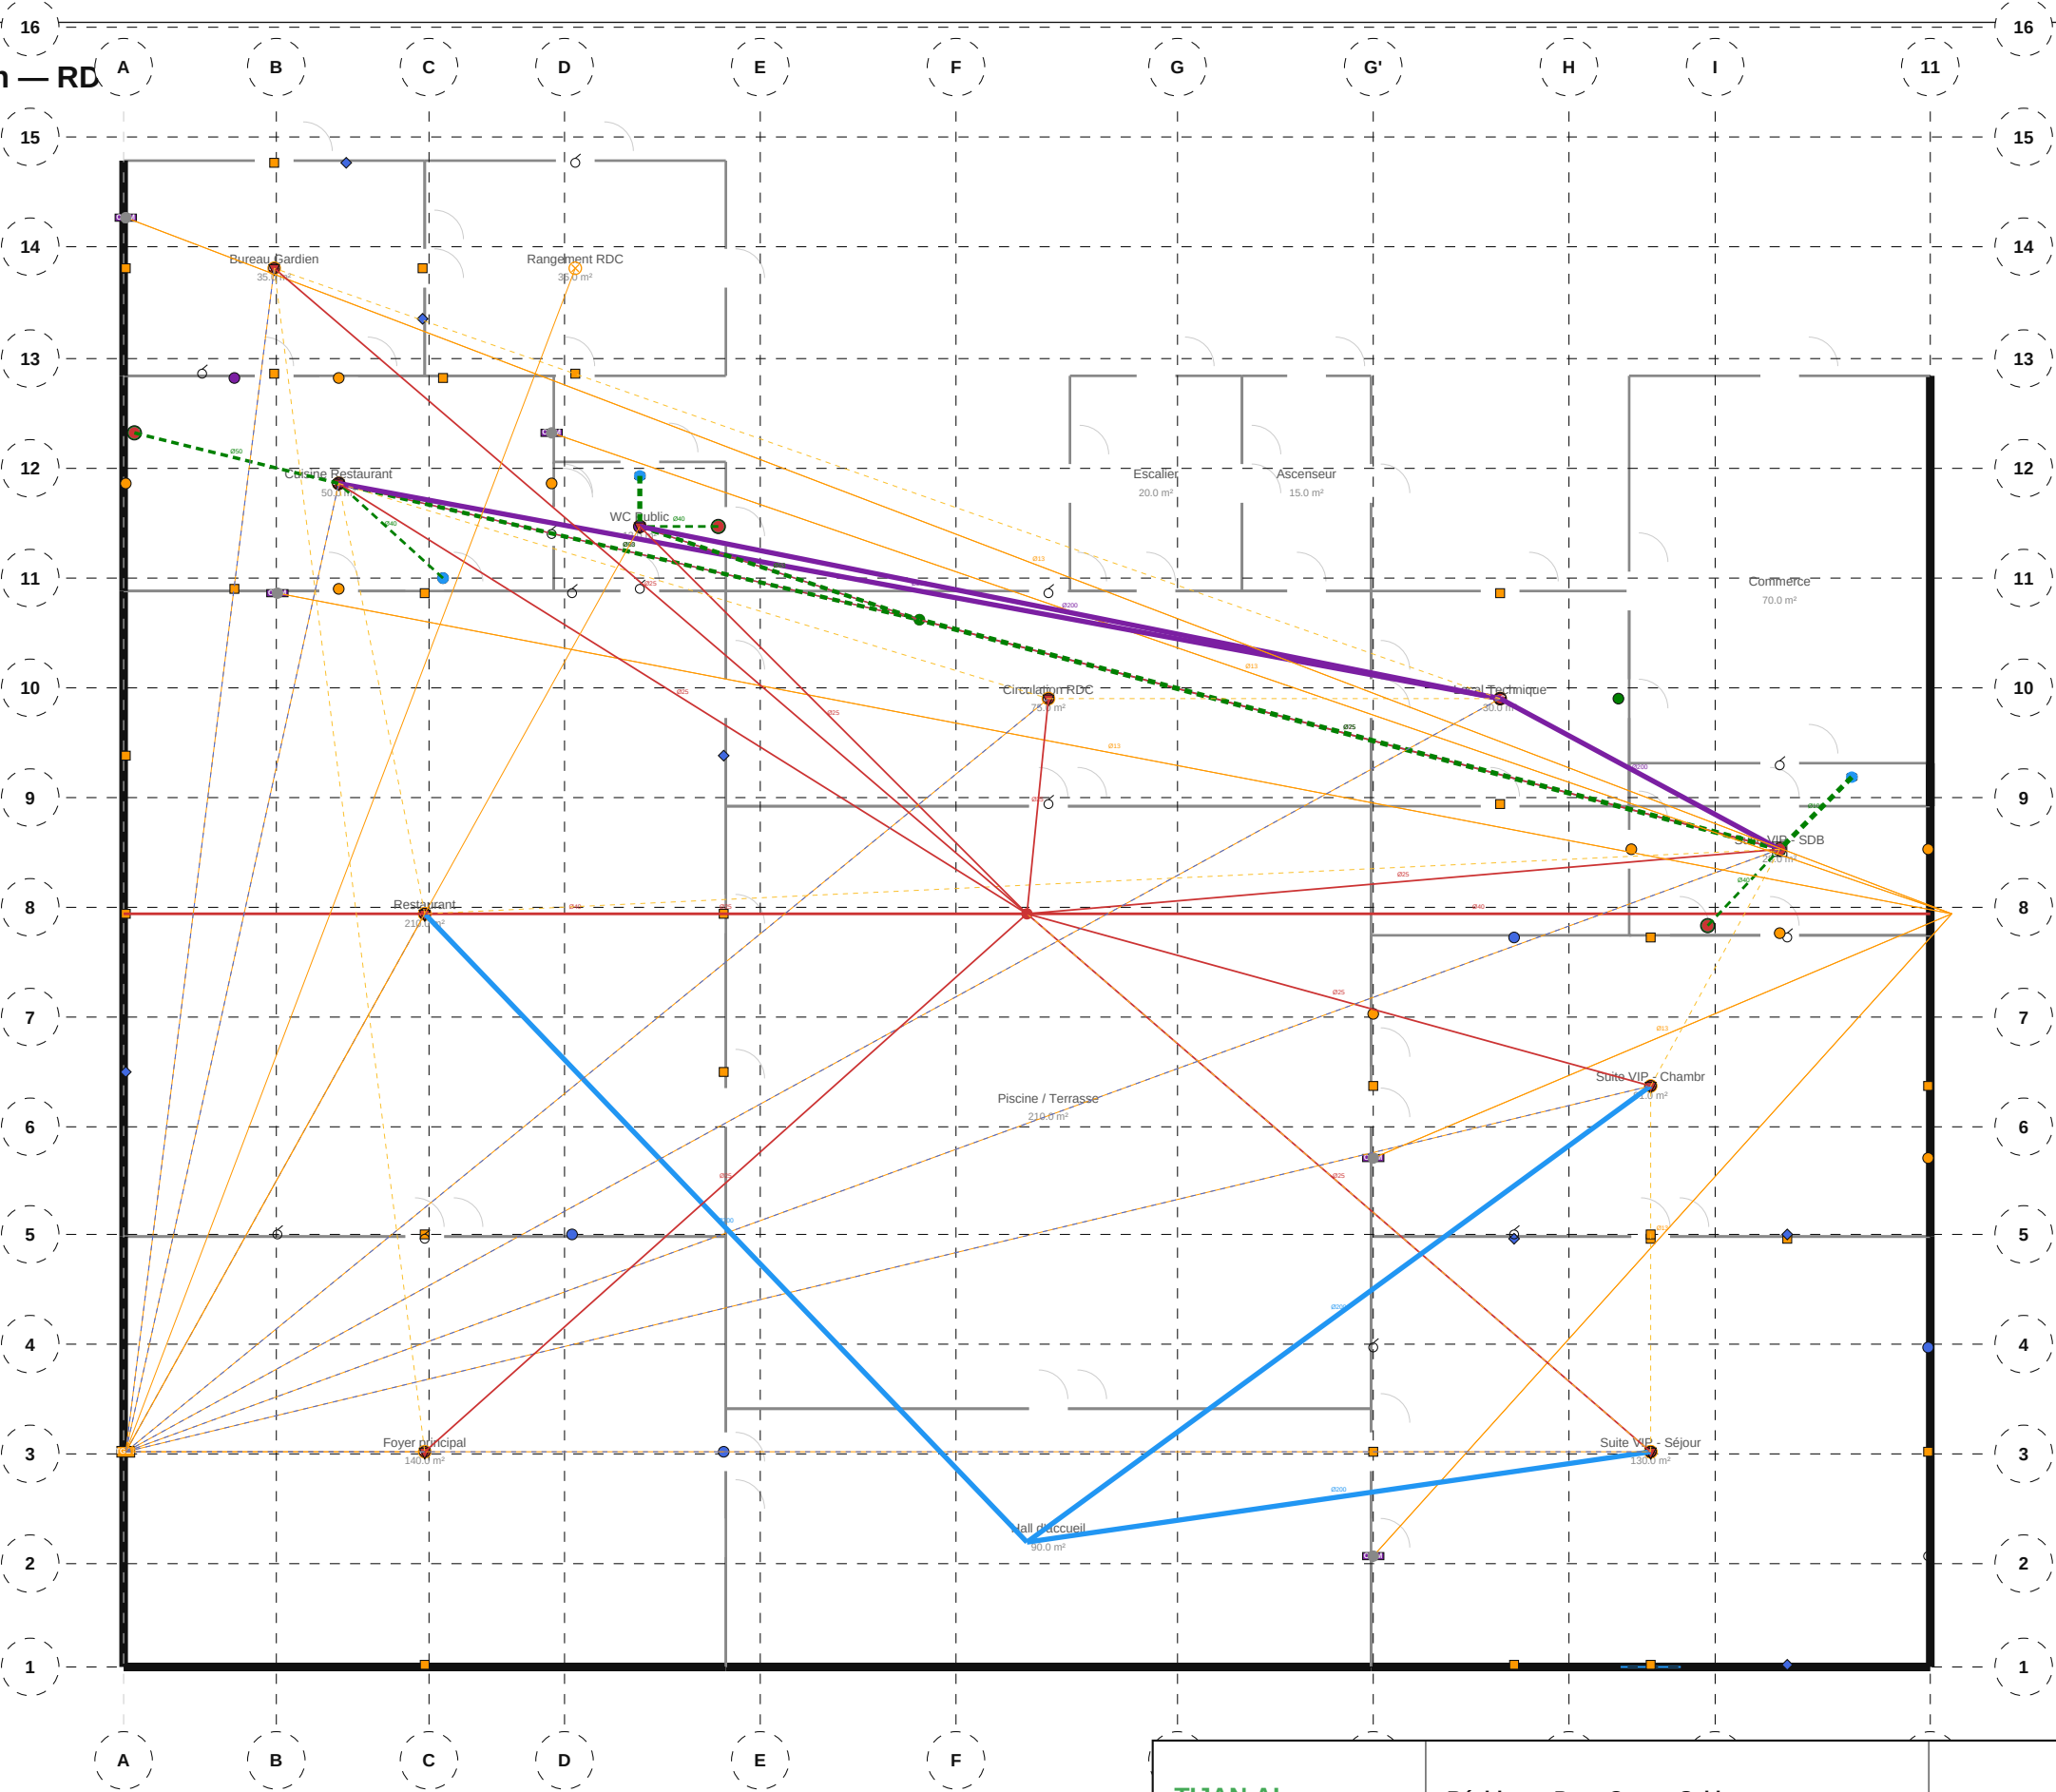

TIJAN AI

Bureau d'Études Automatisé

Résidence Papa Oumar Sakho

Dakar, Senegal

Éch: 1/100

Pl. 79/88

Synthèse / Coordination — RDC

Date: 06/05/2026

Réf: 1711


BIM vSYN-079

Phase: APD

001 Synthèse / Coordination — Étage 1

LÉGENDE RÉSEAUX

- EF — Eau Froide
- EC — Eau Chaude
- EU — Eaux Usées
- CLIM — Réfrigérant
- VMC — Extraction
- HCU — Courants Forts
- LCU — Courants Faibles
- SPK — Sprinkler

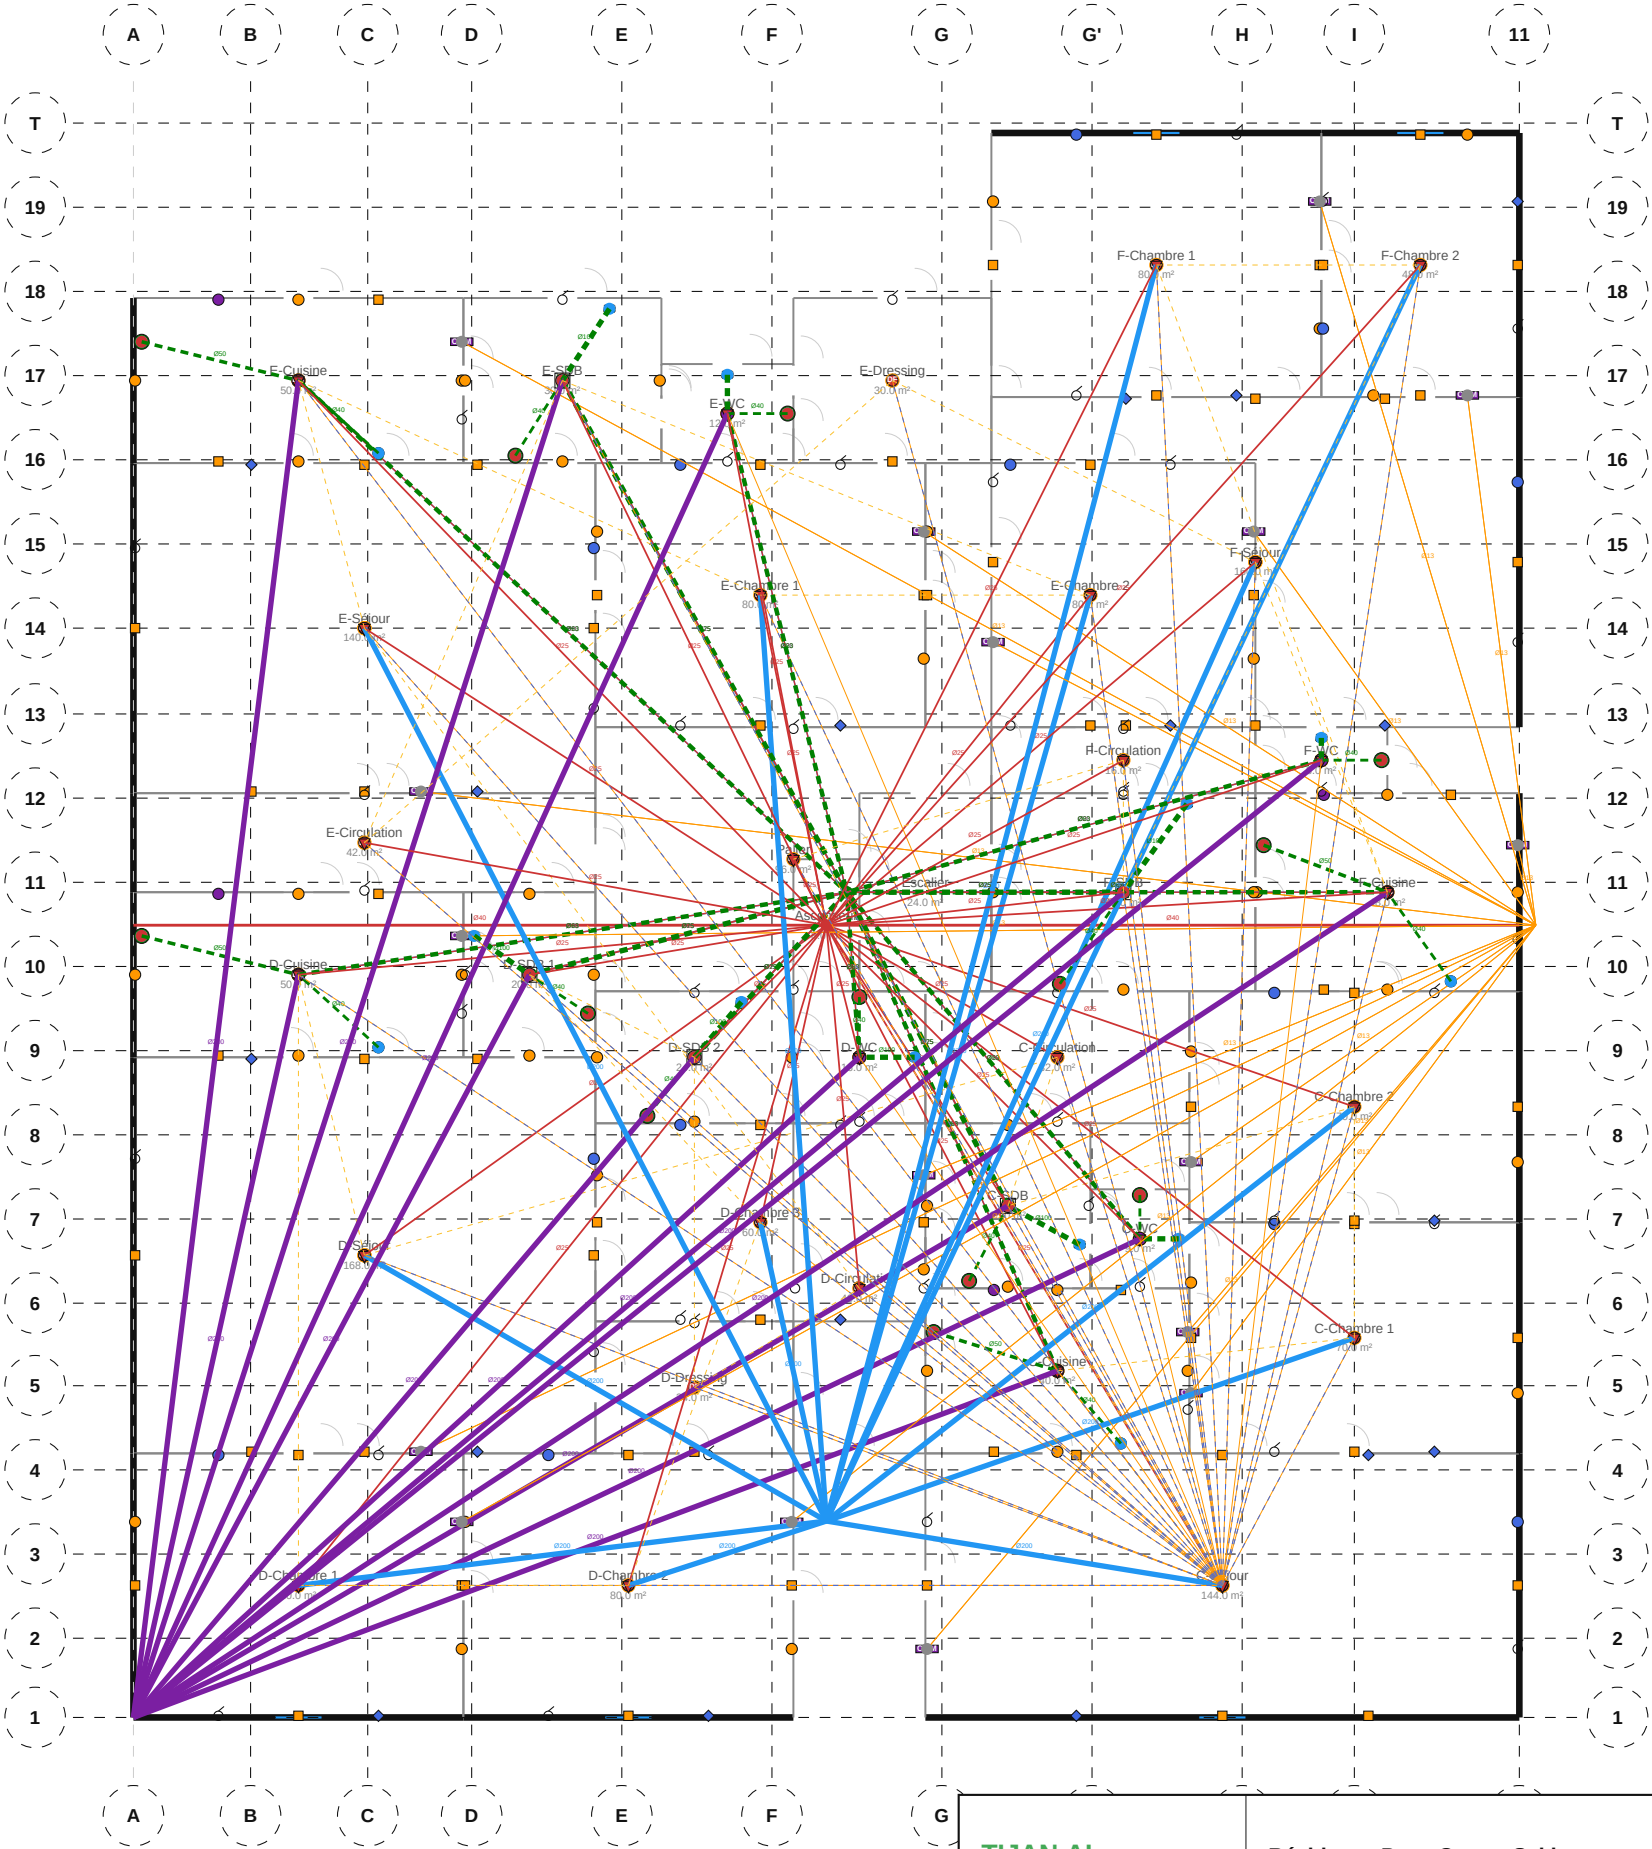


TIJAN AI Bureau d'Études Automatisé	Résidence Papa Oumar Sakho Dakar, Senegal	Éch: 1/100 Pl. 80/88
	Synthèse / Coordination — Étage 1	
Date: 06/05/2026	Réf: 1711	BIM vSYN-080 Phase: APD

001 Synthèse / Coordination — Étage 2

LÉGENDE RÉSEAUX

- EF — Eau Froide
- EC — Eau Chaude
- EU — Eaux Usées
- CLIM — Réfrigérant
- VMC — Extraction
- HCU — Courants Forts
- LCU — Courants Faibles
- SPK — Sprinkler

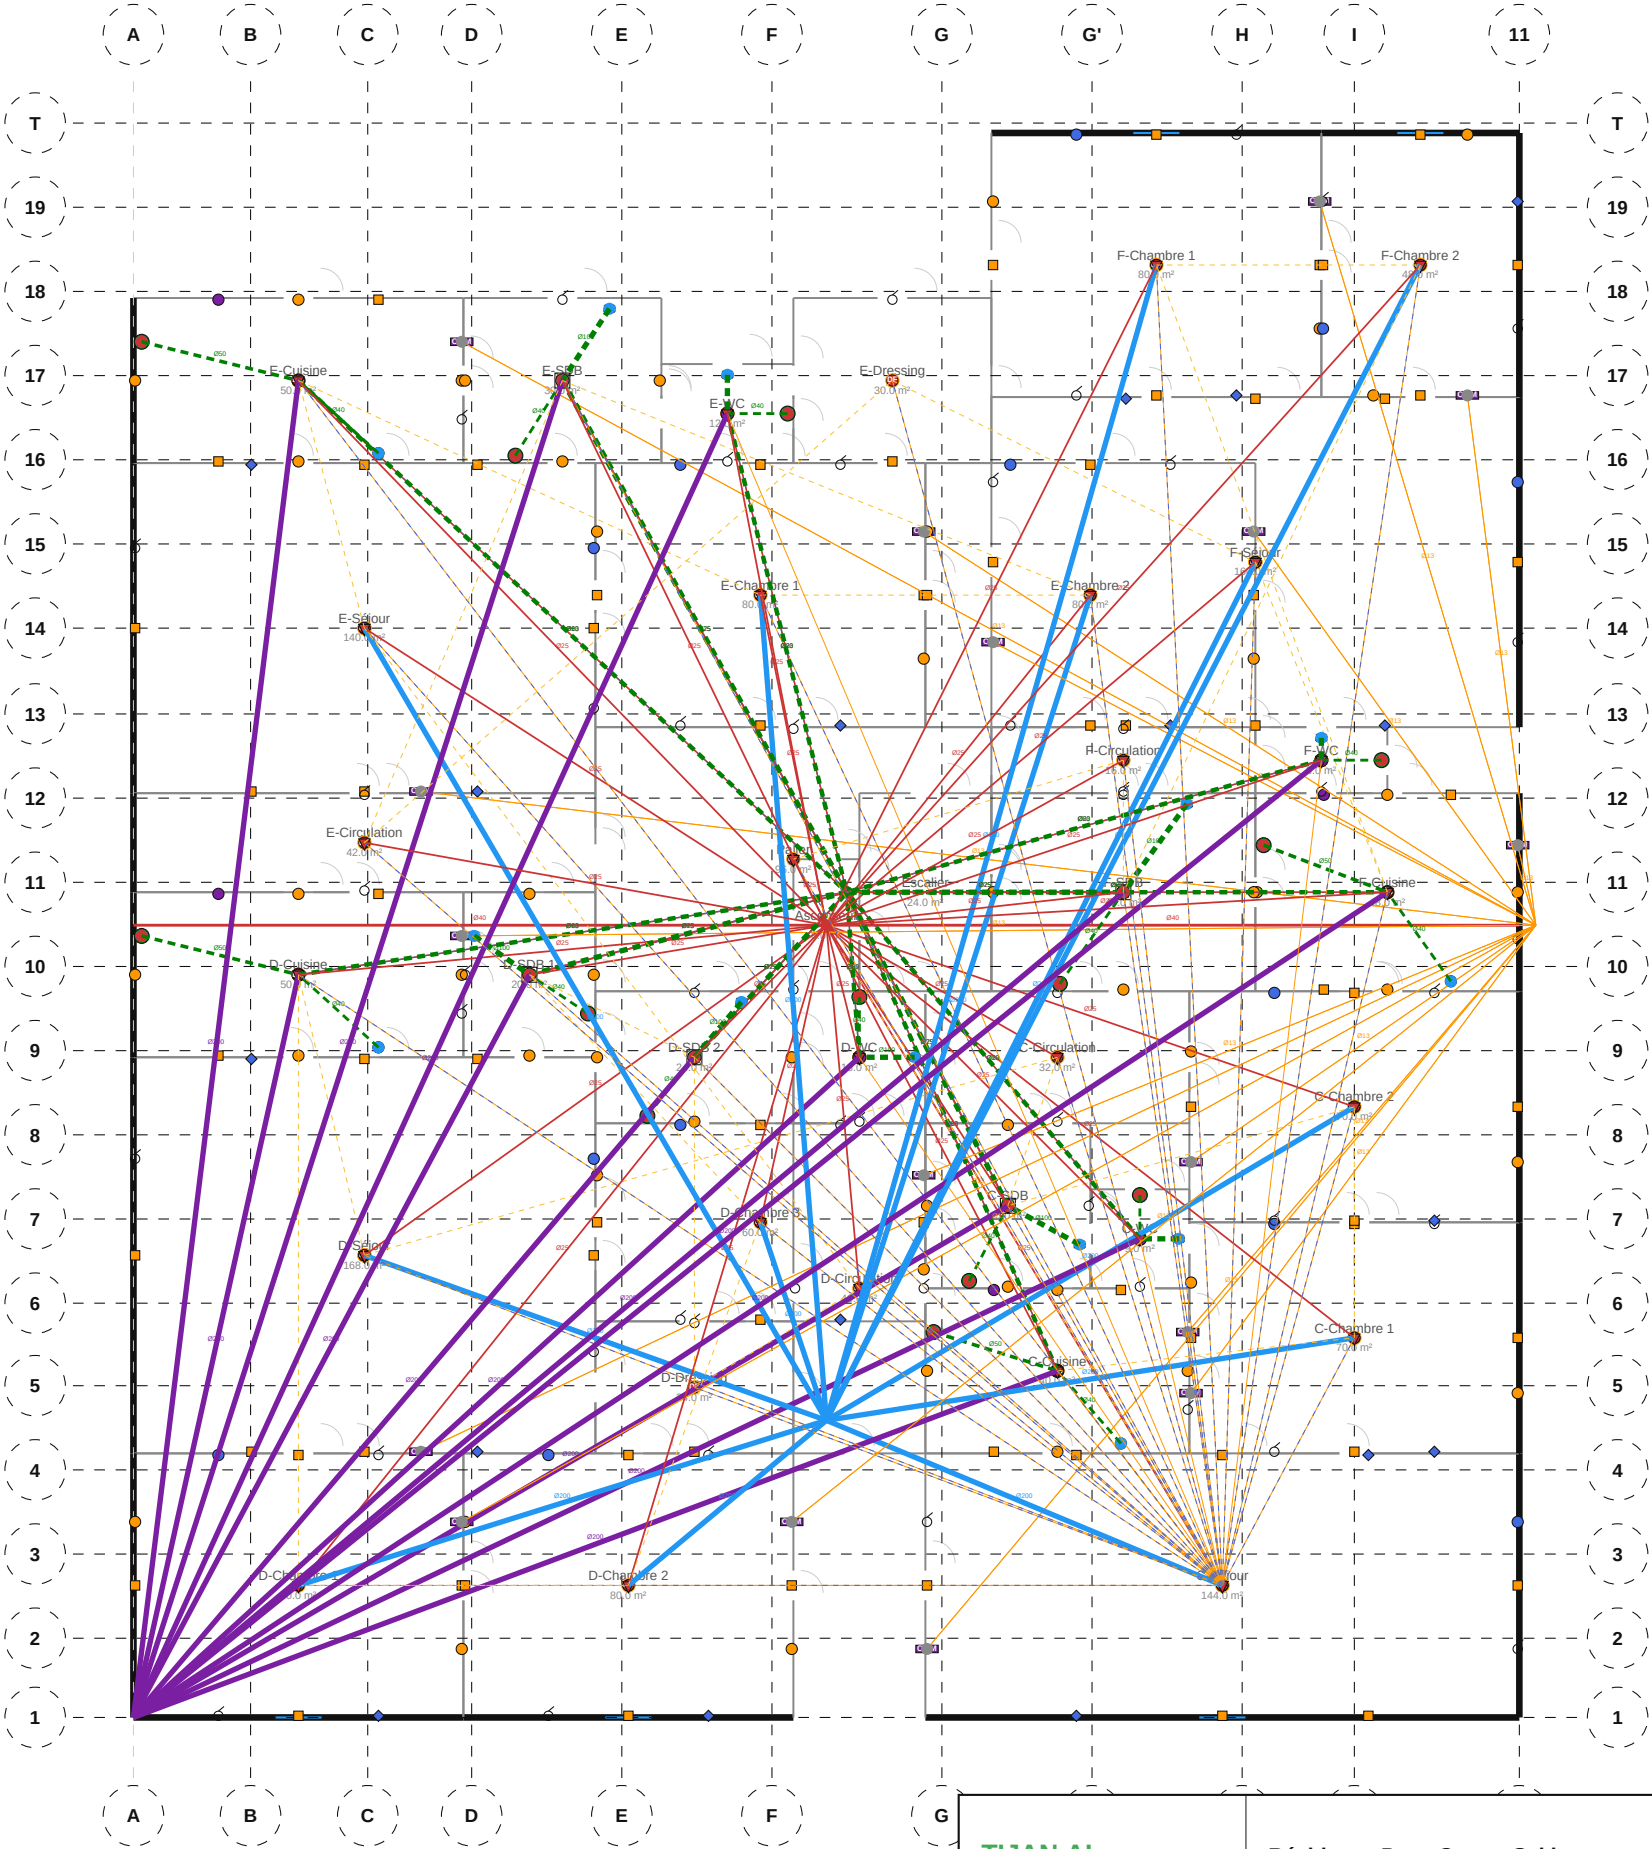


TIJAN AI Bureau d'Études Automatisé	Résidence Papa Oumar Sakho Dakar, Senegal	Éch: 1/100 Pl. 81/88
	Synthèse / Coordination — Étage 2	
Date: 06/05/2026	Réf: 1711	BIM vSYN-081 Phase: APD

001 Synthèse / Coordination — Étage 3

LÉGENDE RÉSEAUX

- EF — Eau Froide
- EC — Eau Chaude
- EU — Eaux Usées
- CLIM — Réfrigérant
- VMC — Extraction
- HCU — Courants Forts
- LCU — Courants Faibles
- SPK — Sprinkler

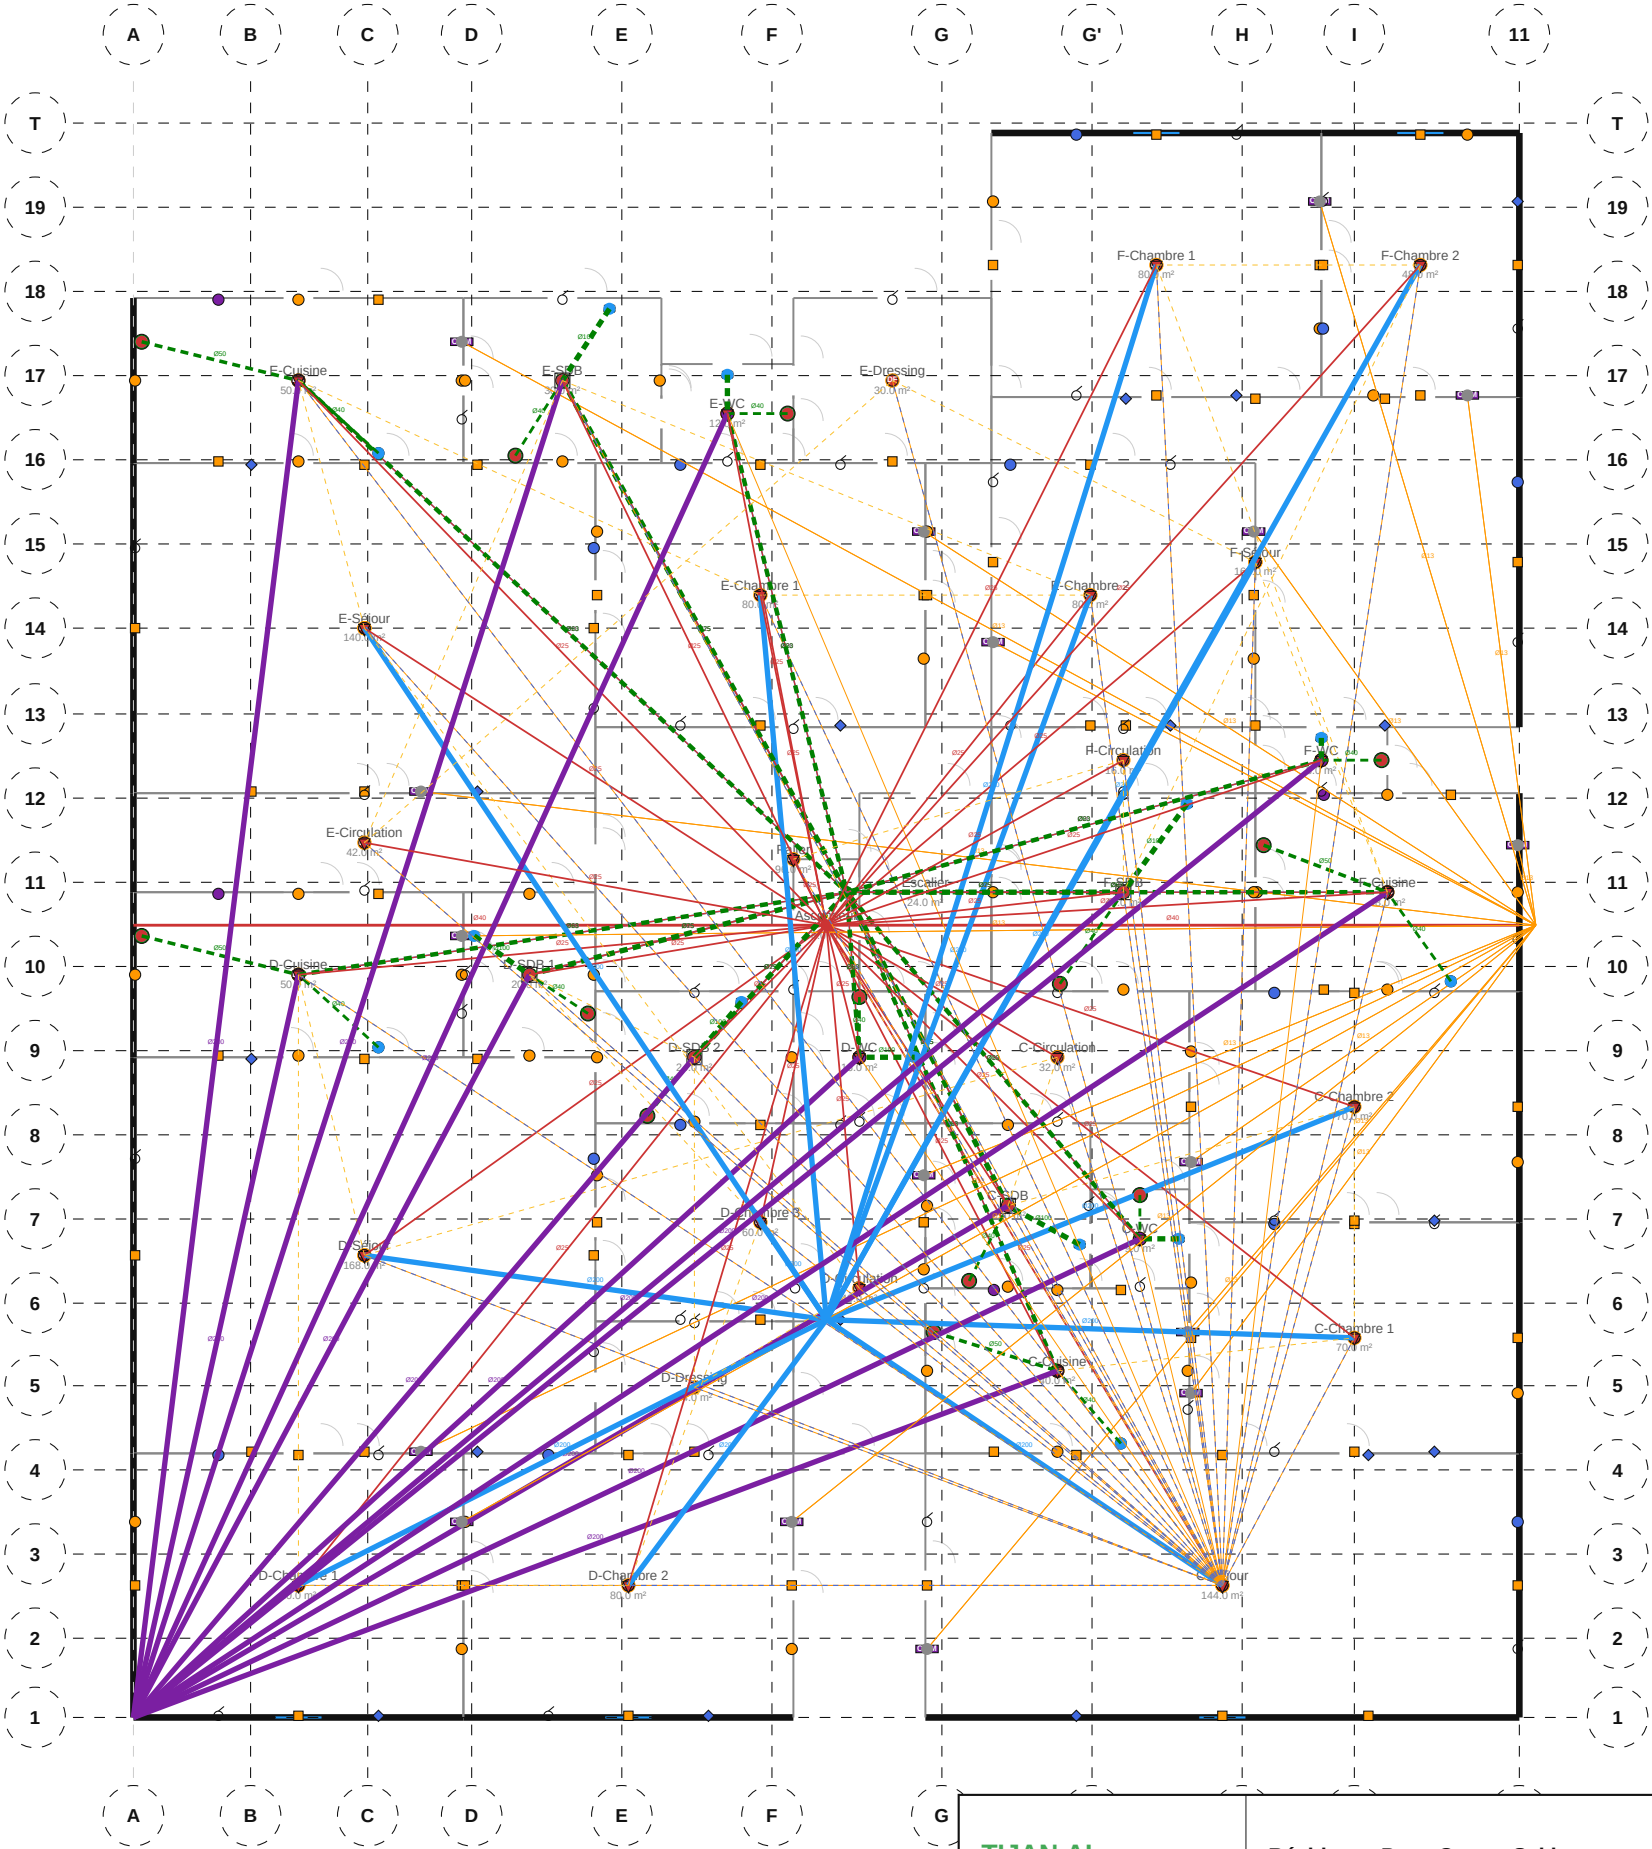


TIJAN AI Bureau d'Études Automatisé	Résidence Papa Oumar Sakho Dakar, Senegal	Éch: 1/100 Pl. 82/88
	Synthèse / Coordination — Étage 3	
Date: 06/05/2026	Réf: 1711	BIM vSYN-082 Phase: APD

001 Synthèse / Coordination — Étage 4

LÉGENDE RÉSEAUX

- EF — Eau Froide
- EC — Eau Chaude
- EU — Eaux Usées
- CLIM — Réfrigérant
- VMC — Extraction
- HCU — Courants Forts
- LCU — Courants Faibles
- SPK — Sprinkler

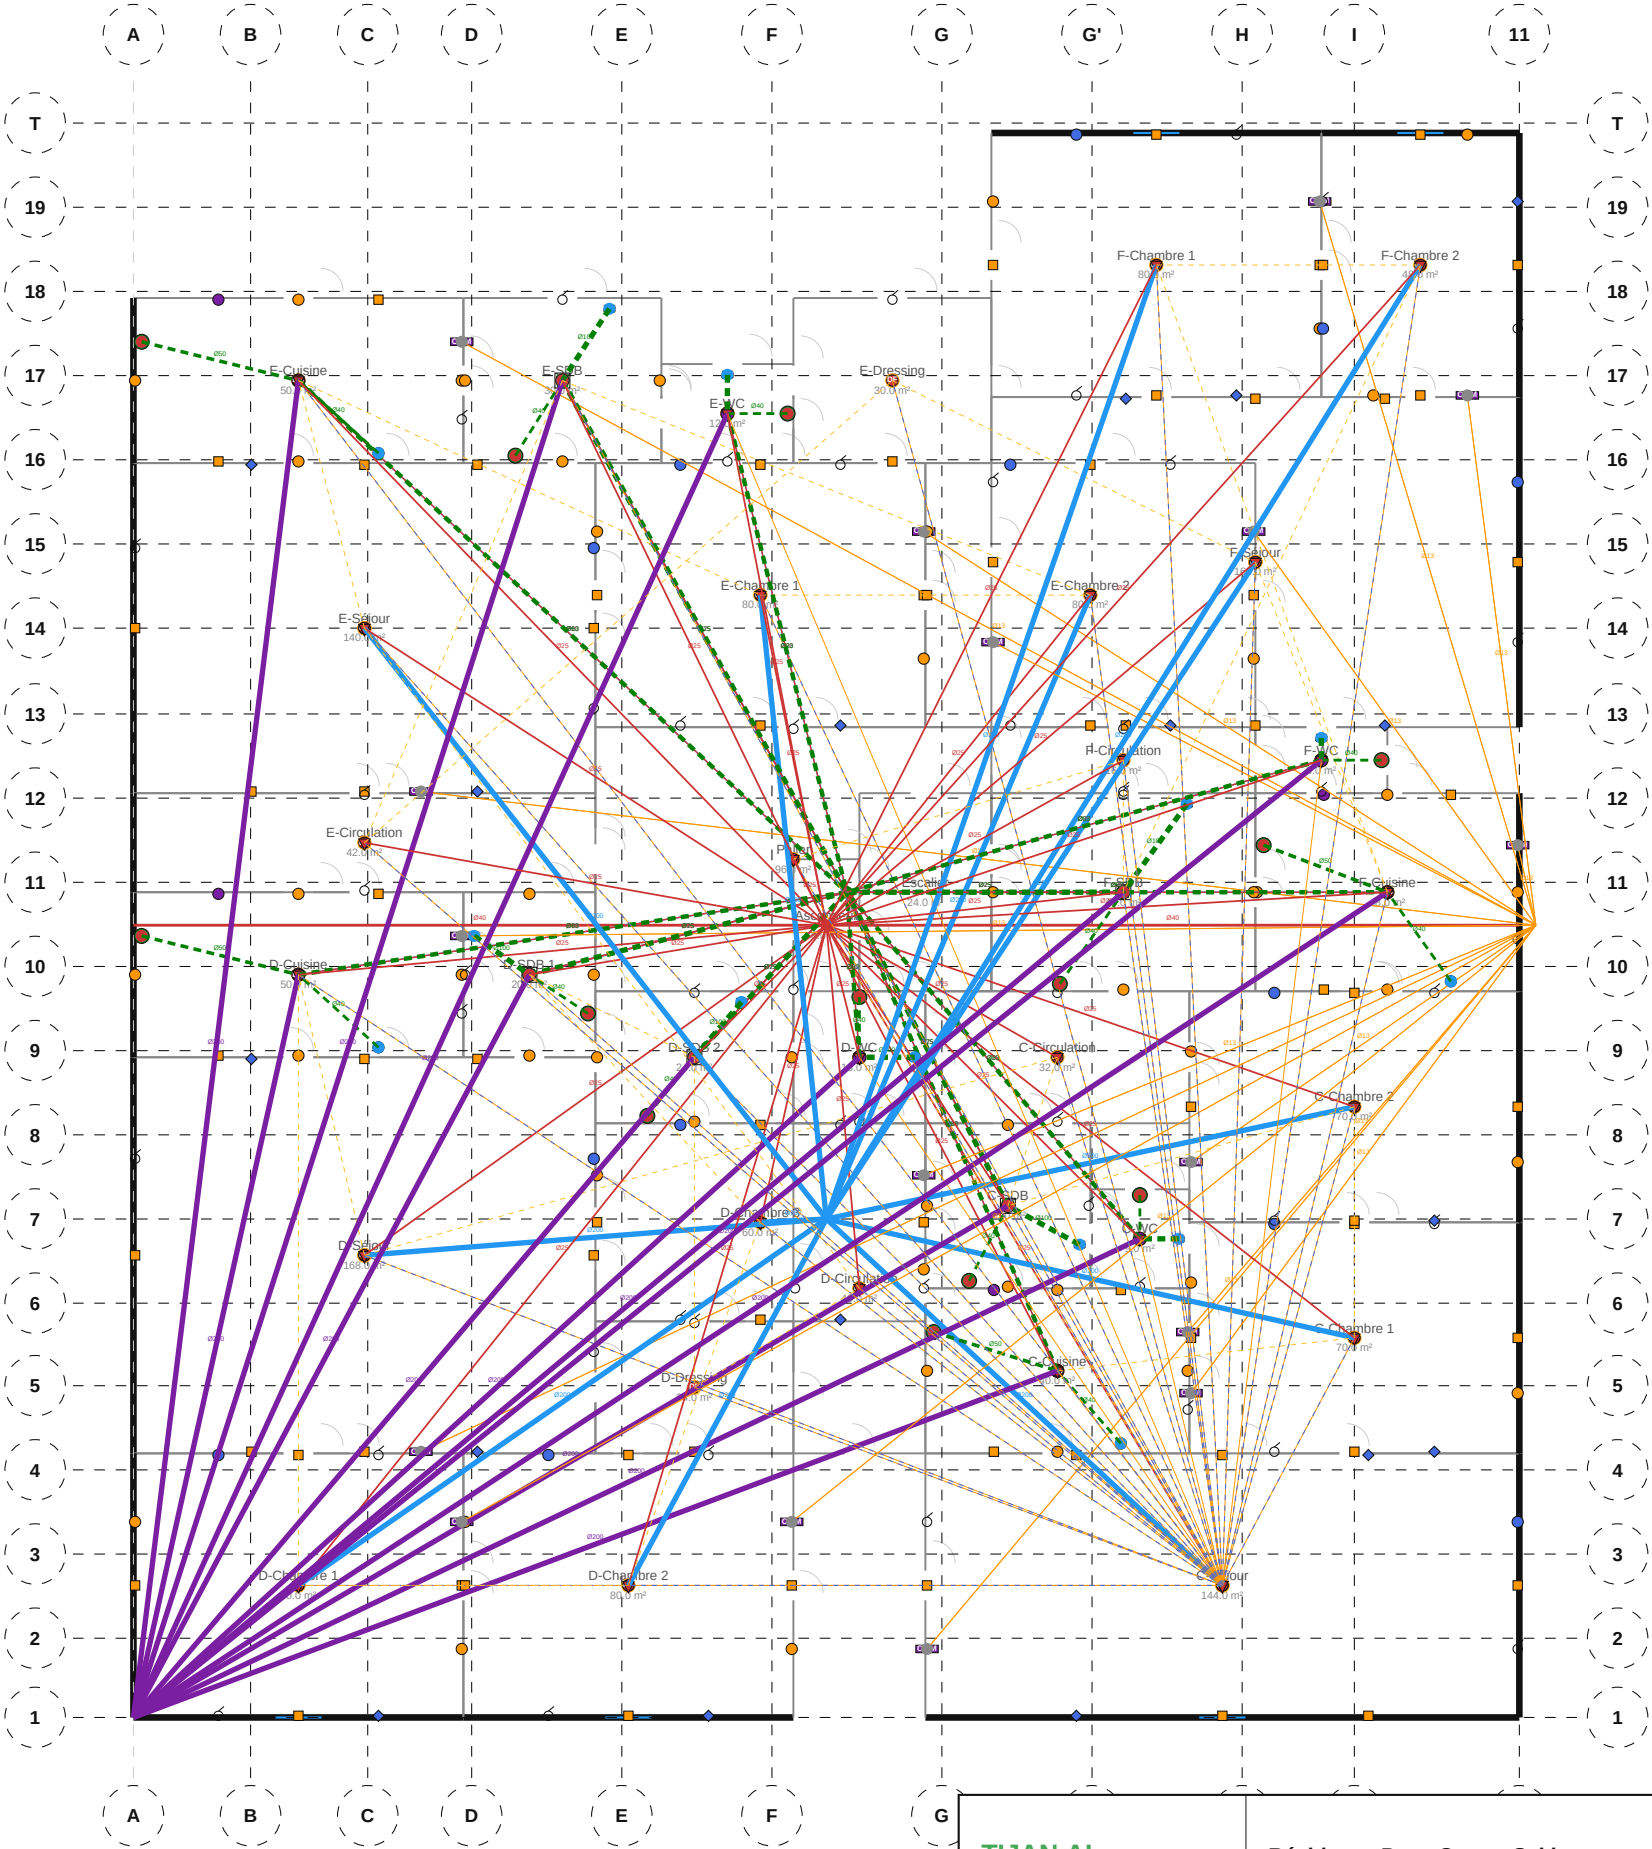


TIJAN AI Bureau d'Études Automatisé	Résidence Papa Oumar Sakho Dakar, Senegal	Éch: 1/100 Pl. 83/88
	Synthèse / Coordination — Étage 4	
Date: 06/05/2026	Réf: 1711	BIM vSYN-083 Phase: APD

001 Synthèse / Coordination — Étage 5

LÉGENDE RÉSEAUX

- EF — Eau Froide
- EC — Eau Chaude
- EU — Eaux Usées
- CLIM — Réfrigérant
- VMC — Extraction
- HCU — Courants Forts
- LCU — Courants Faibles
- SPK — Sprinkler

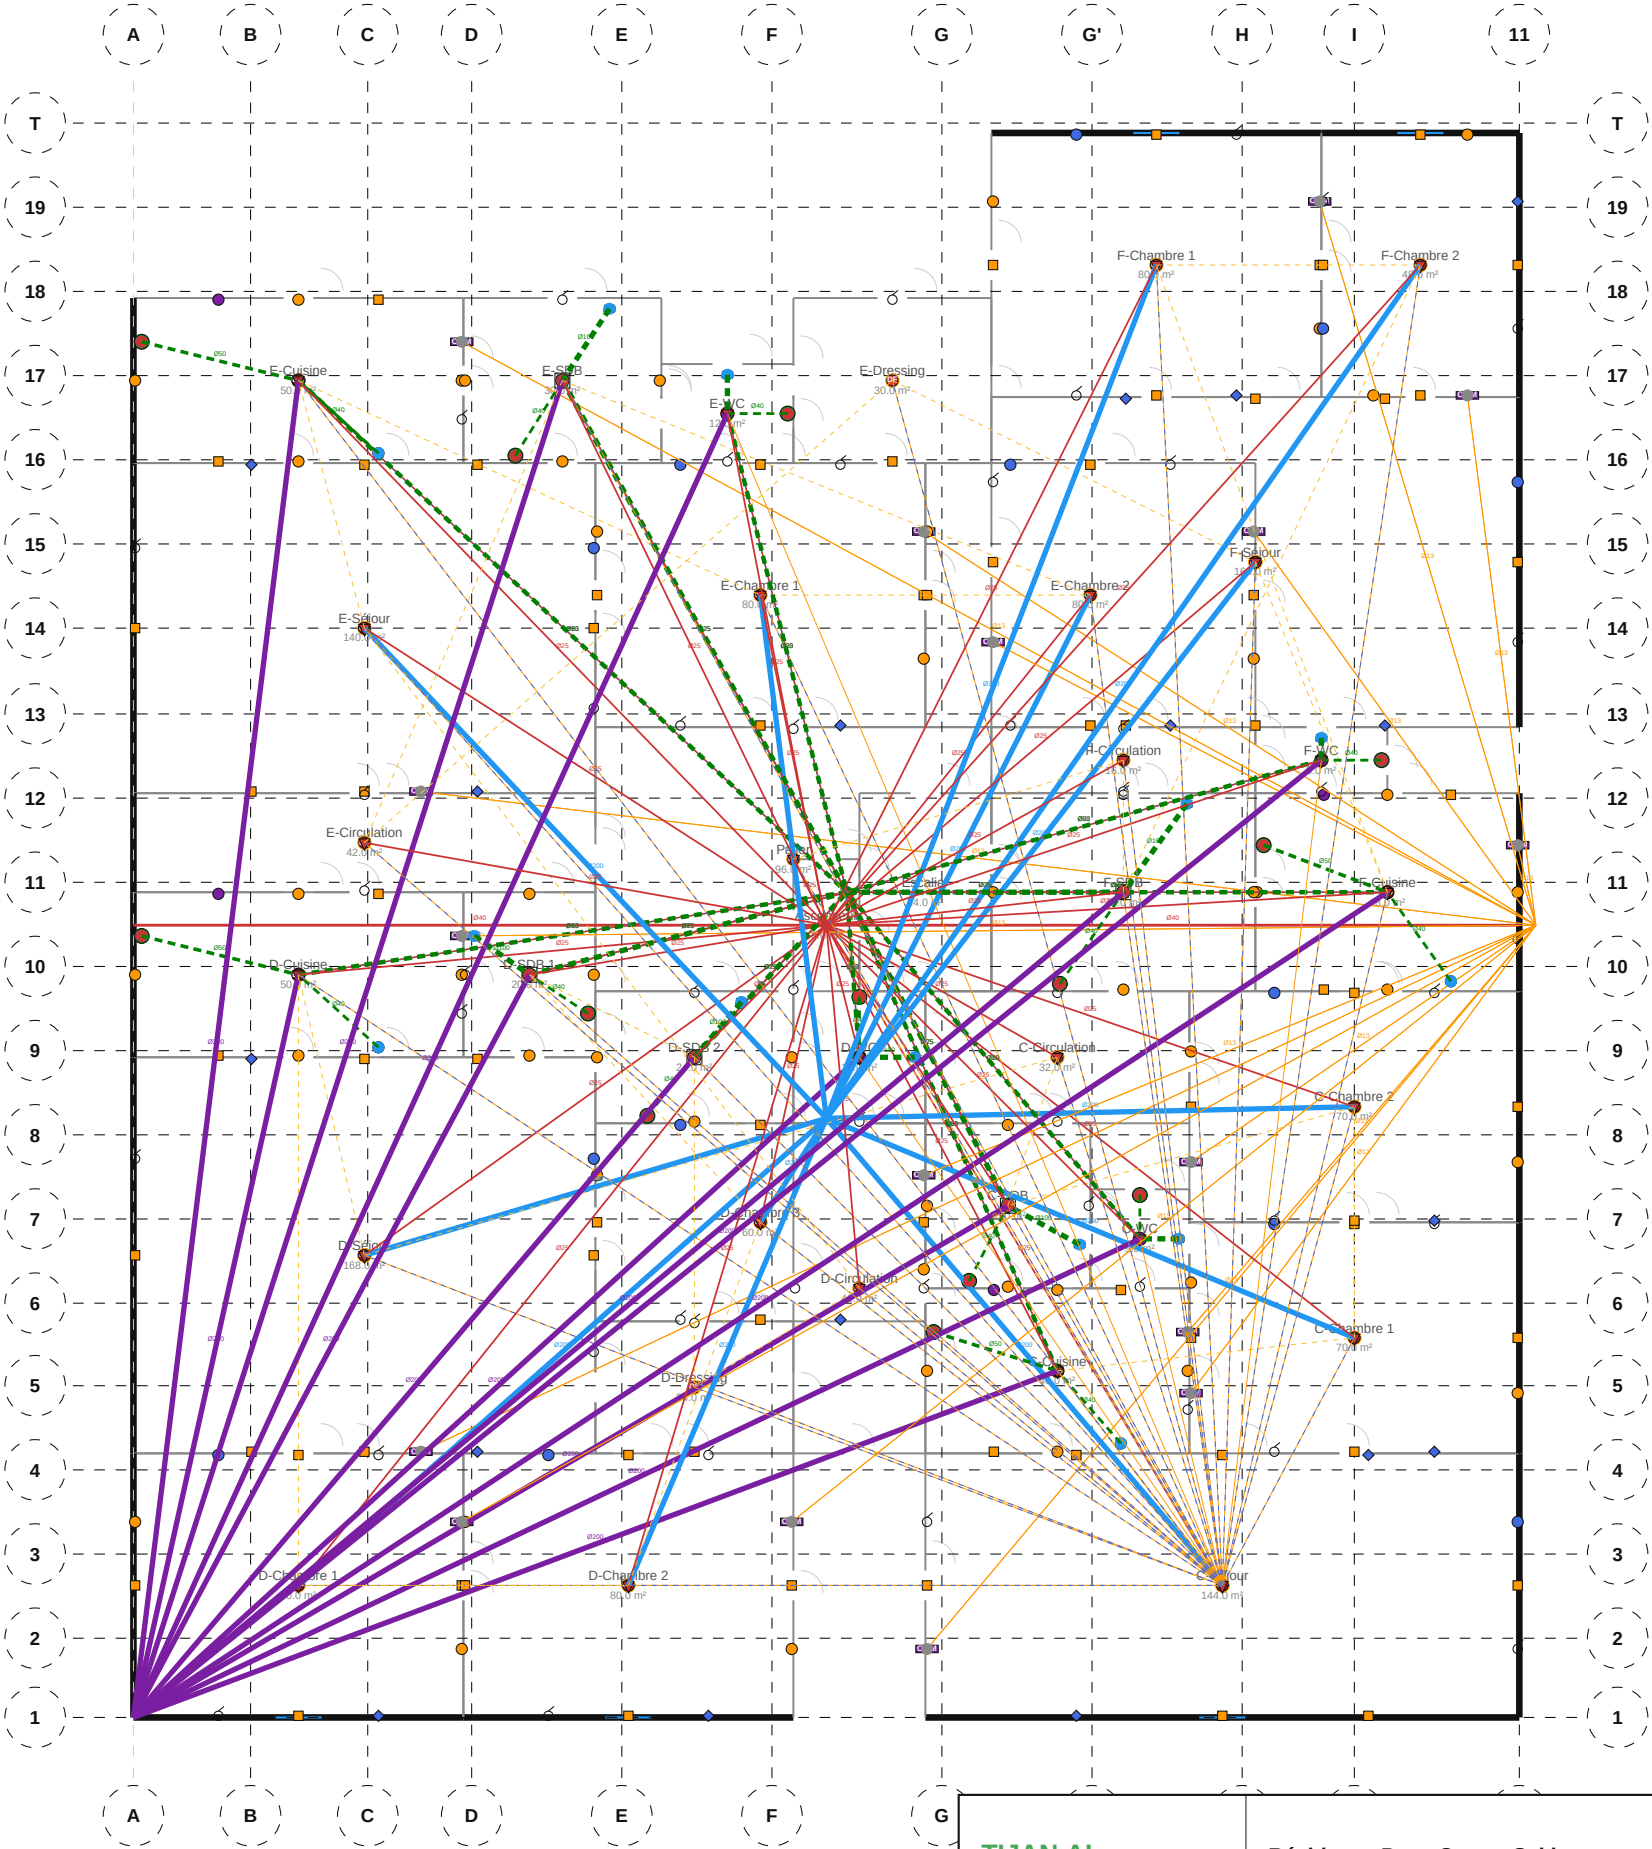


TIJAN AI Bureau d'Études Automatisé	Résidence Papa Oumar Sakho Dakar, Senegal	Éch: 1/100 Pl. 84/88
	Synthèse / Coordination — Étage 5	
Date: 06/05/2026	Réf: 1711	BIM vSYN-084 Phase: APD

001 Synthèse / Coordination — Étage 6

LÉGENDE RÉSEAUX

- EF — Eau Froide
- EC — Eau Chaude
- EU — Eaux Usées
- CLIM — Réfrigérant
- VMC — Extraction
- HCU — Courants Forts
- LCU — Courants Faibles
- SPK — Sprinkler

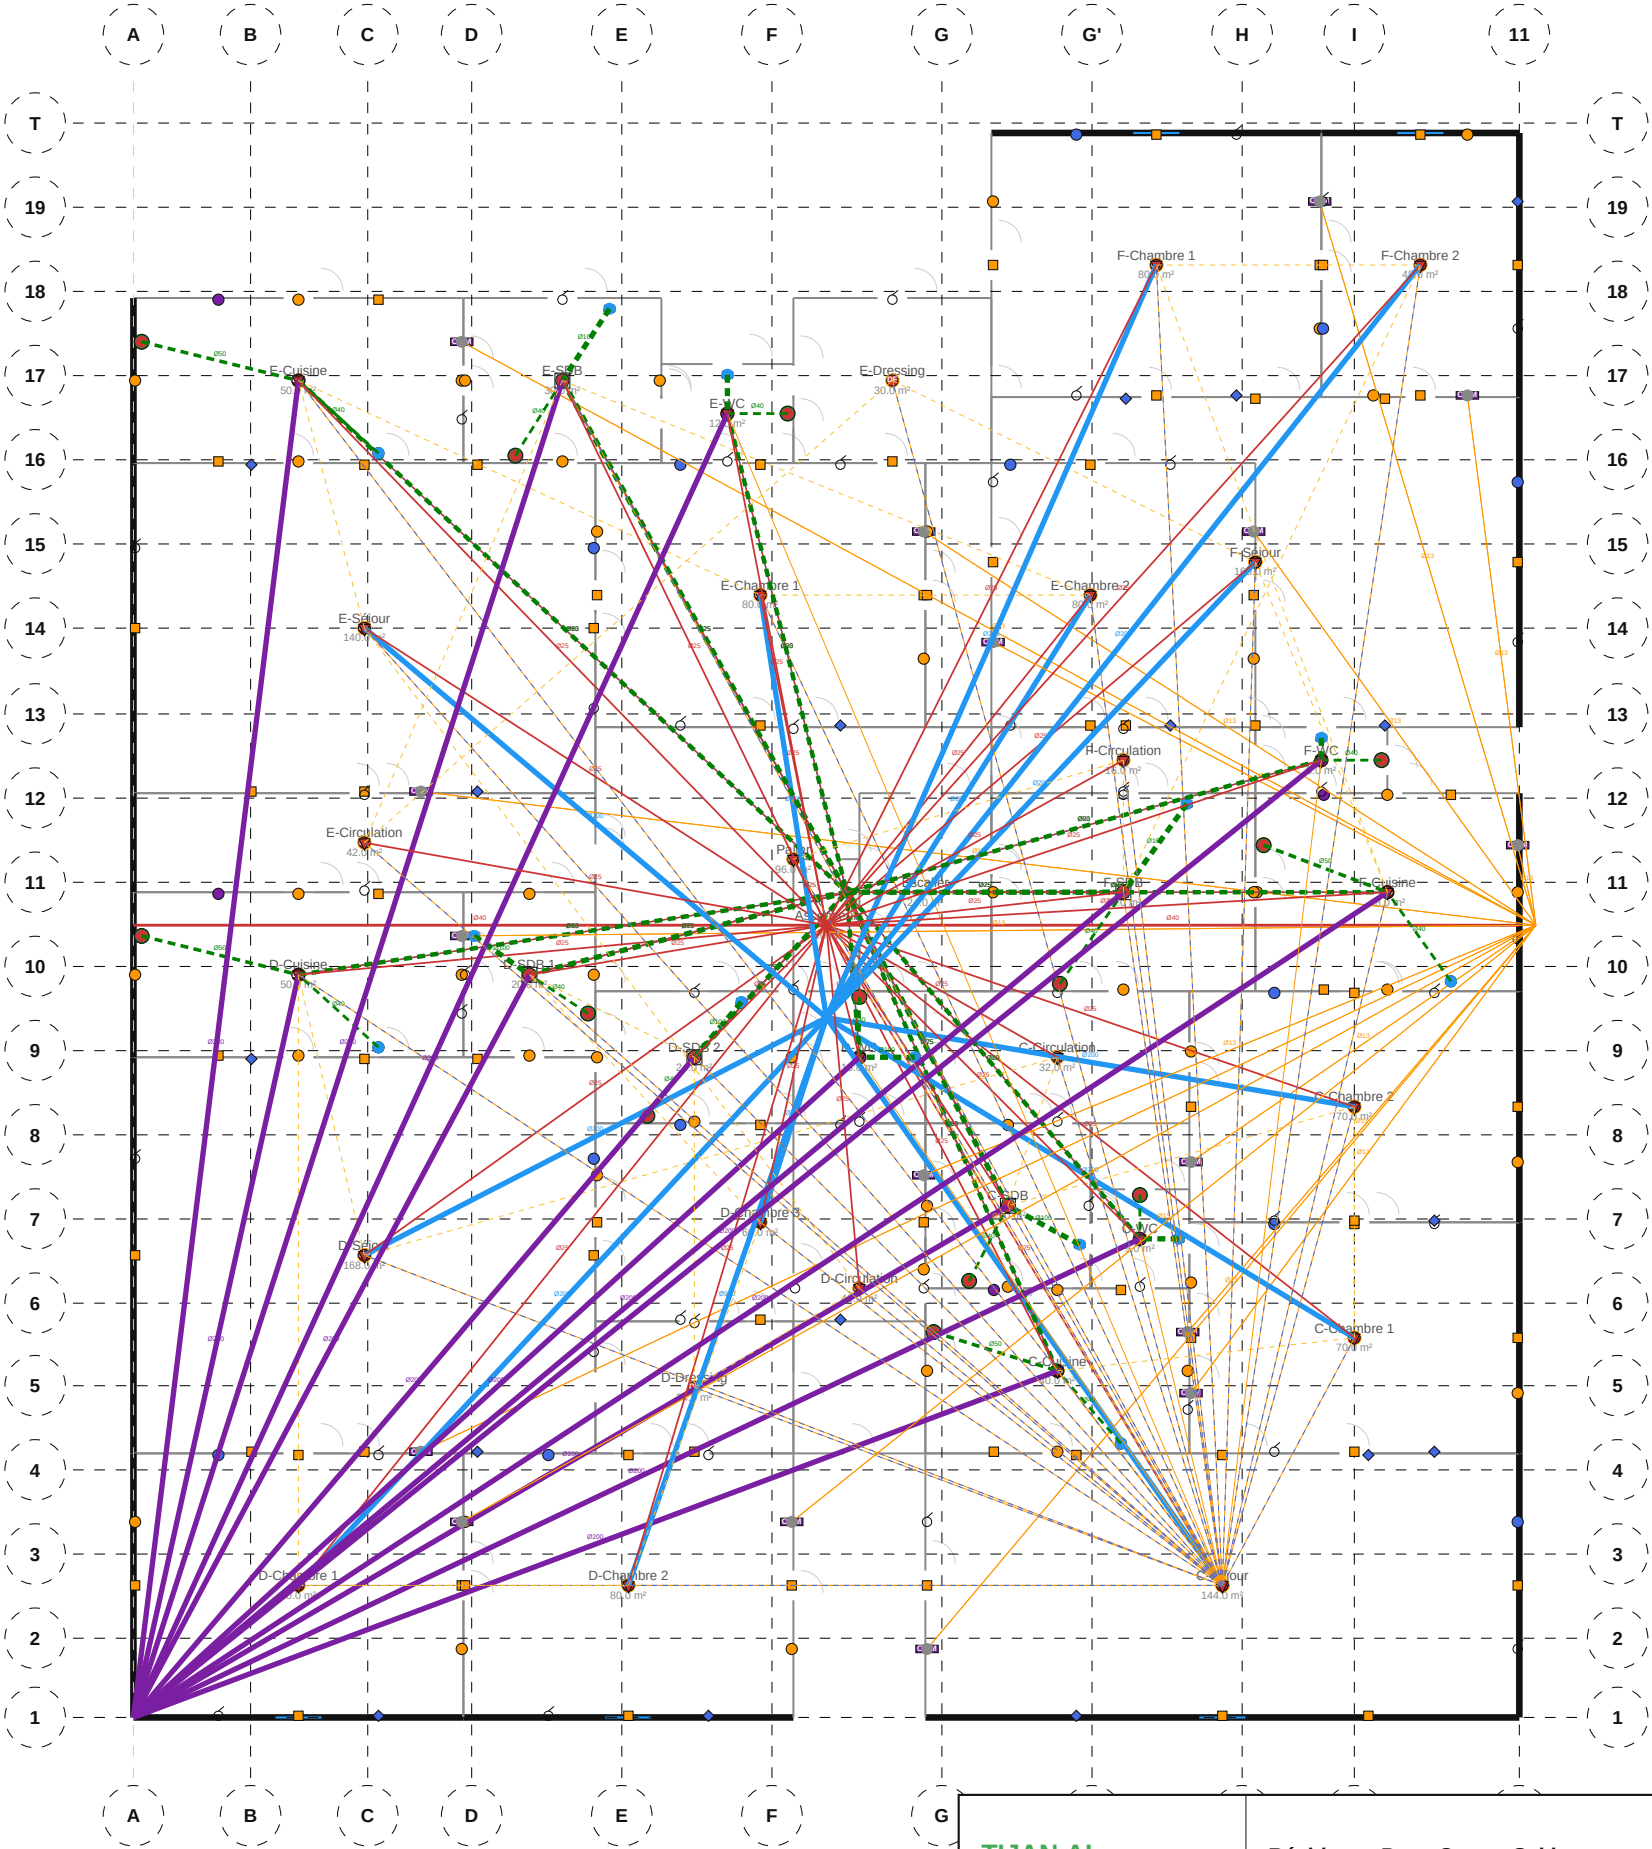


TIJAN AI Bureau d'Études Automatisé	Résidence Papa Oumar Sakho Dakar, Senegal	Éch: 1/100 Pl. 85/88
	Synthèse / Coordination — Étage 6	
Date: 06/05/2026	Réf: 1711	BIM vSYN-085 Phase: APD

001 Synthèse / Coordination — Étage 7

LÉGENDE RÉSEAUX

- EF — Eau Froide
- EC — Eau Chaude
- EU — Eaux Usées
- CLIM — Réfrigérant
- VMC — Extraction
- HCU — Courants Forts
- LCU — Courants Faibles
- SPK — Sprinkler

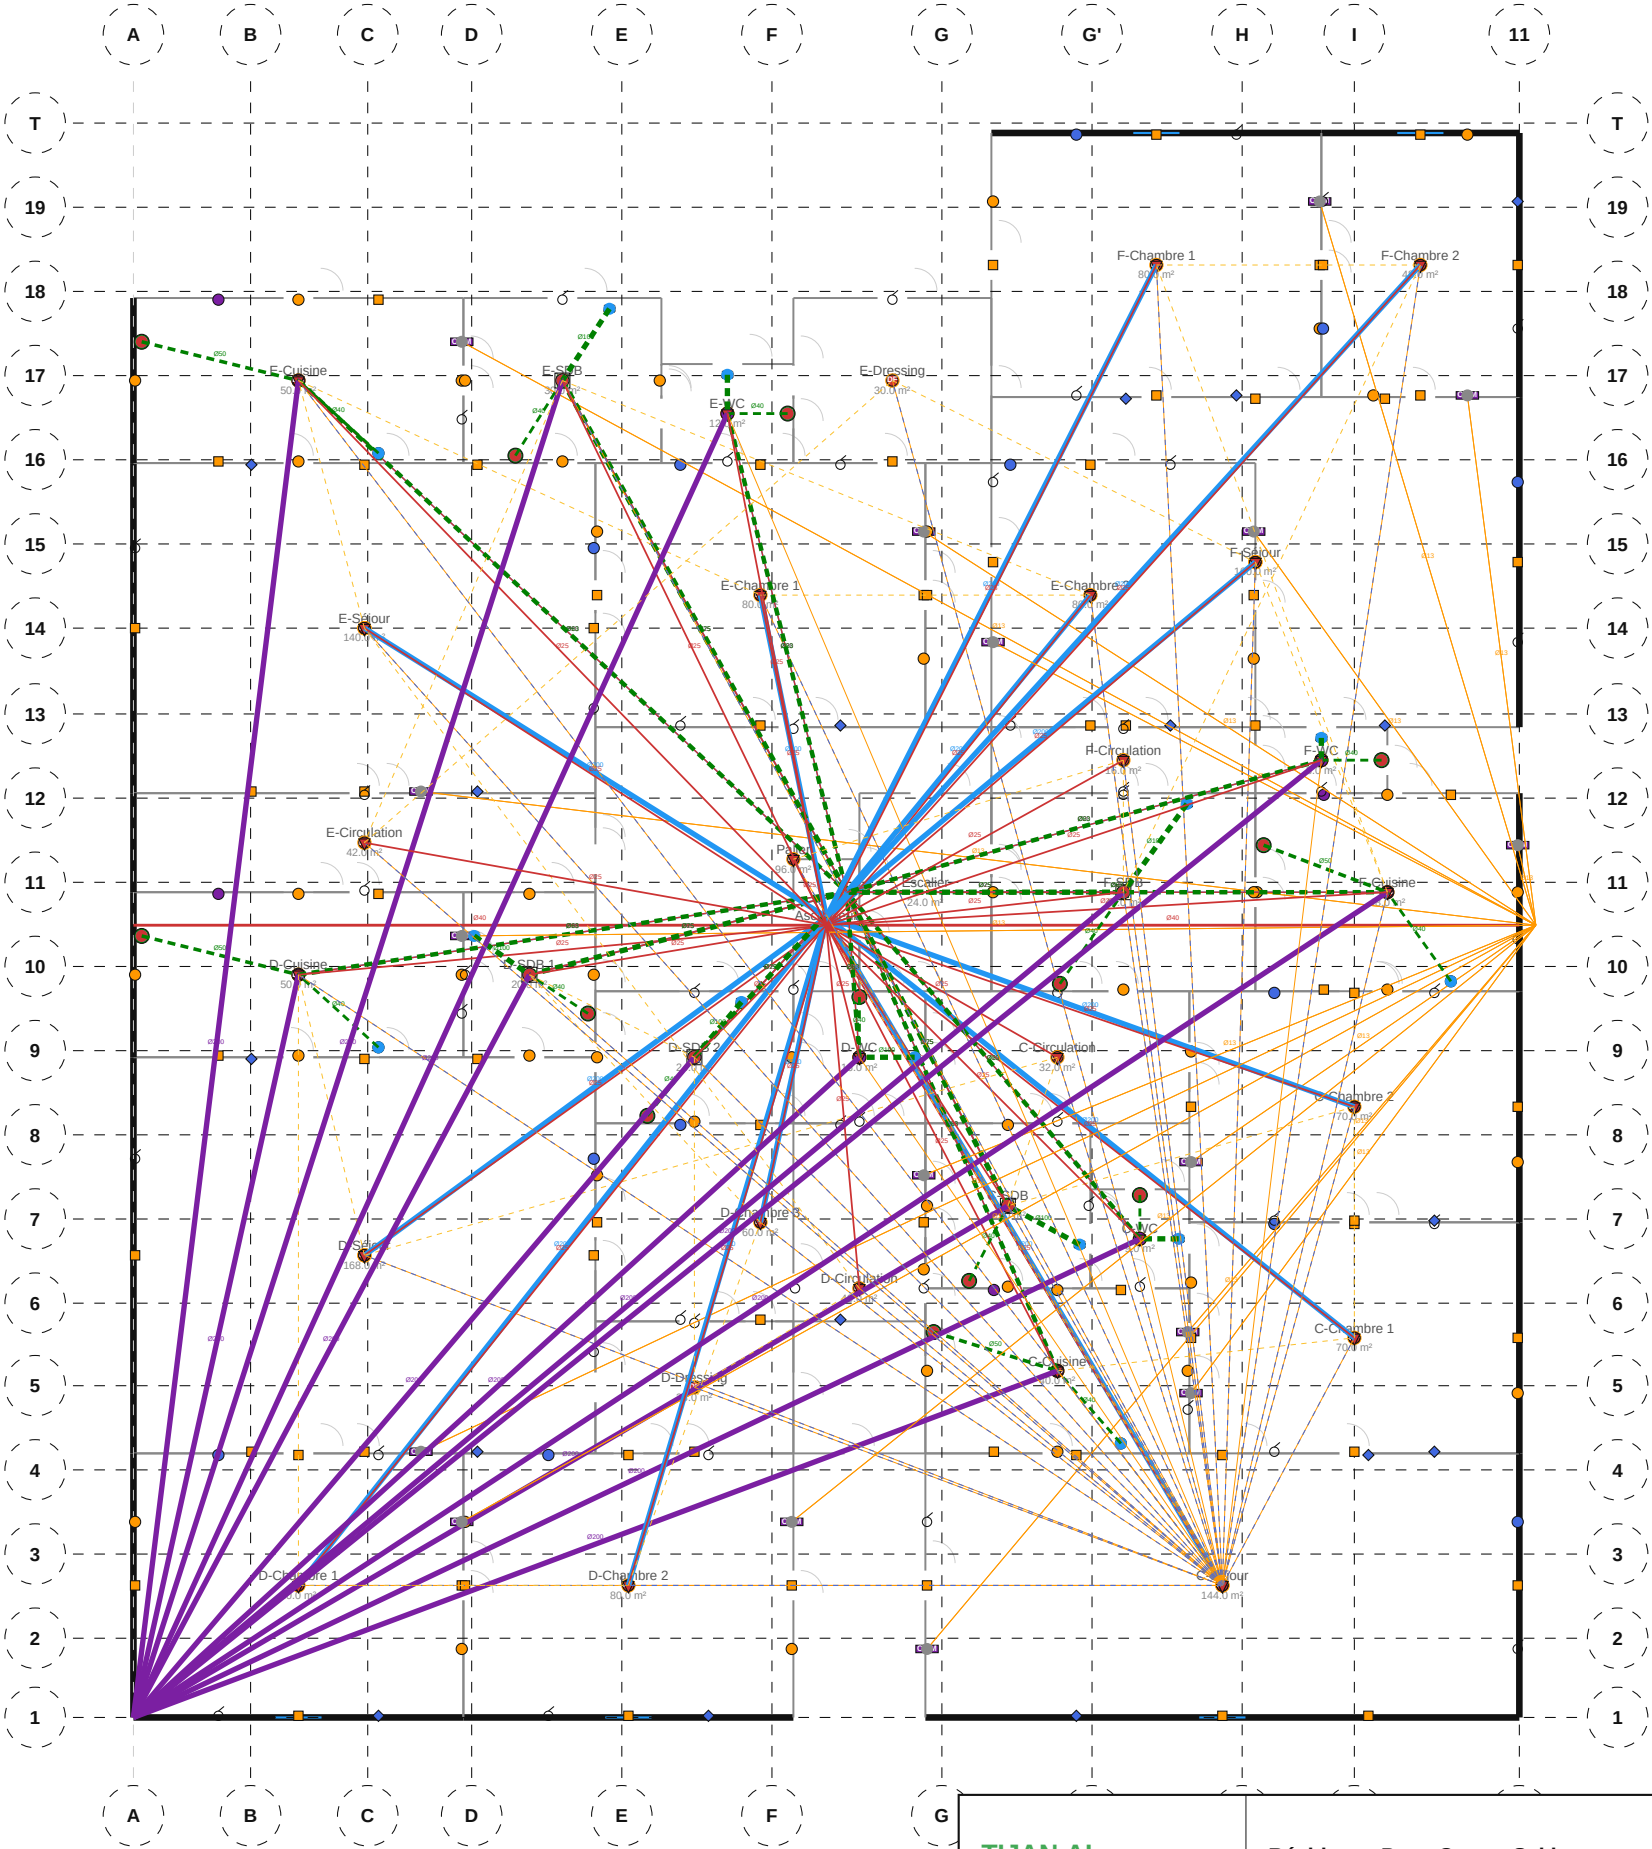


TIJAN AI Bureau d'Études Automatisé	Résidence Papa Oumar Sakho Dakar, Senegal	Éch: 1/100 Pl. 86/88
	Synthèse / Coordination — Étage 7	
Date: 06/05/2026	Réf: 1711	BIM vSYN-086 Phase: APD

001 Synthèse / Coordination — Étage 8

LÉGENDE RÉSEAUX

- EF — Eau Froide
- EC — Eau Chaude
- EU — Eaux Usées
- CLIM — Réfrigérant
- VMC — Extraction
- HCU — Courants Forts
- LCU — Courants Faibles
- SPK — Sprinkler

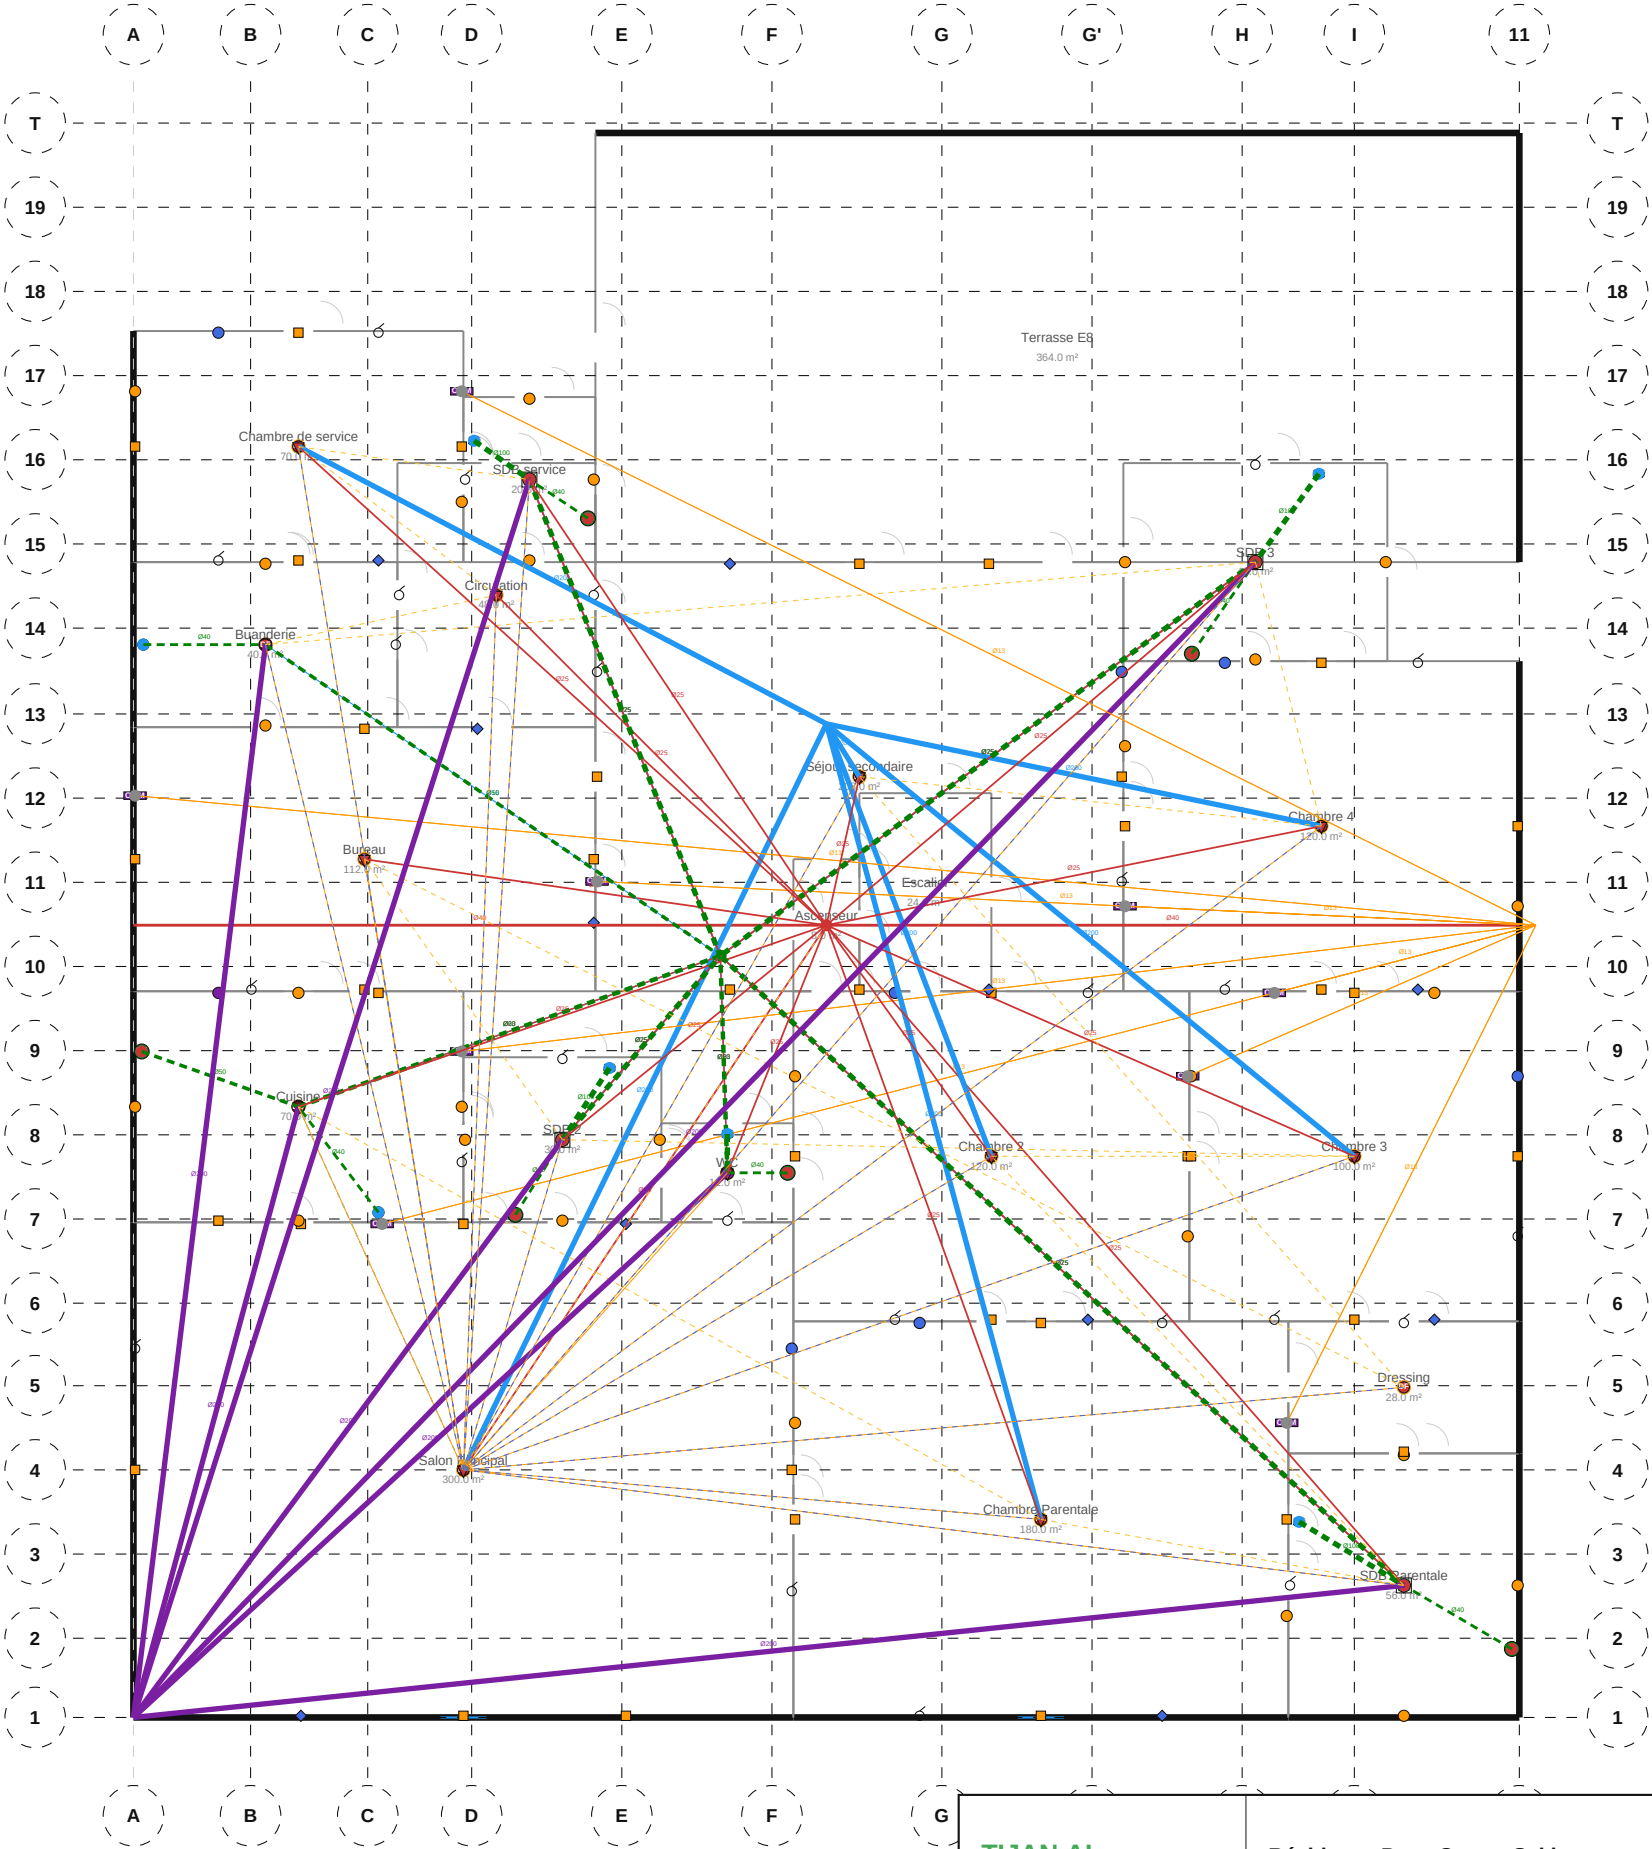

TIJAN AI

Bureau d'Études Automatisé

Résidence Papa Oumar Sakho

Dakar, Senegal

Éch: 1/100

Pl. 87/88

Synthèse / Coordination — Étage 8

Date: 06/05/2026

Réf: 1711


BIM vSYN-087

Phase: APD

001 Synthèse / Coordination — Terrasse

LÉGENDE RÉSEAUX

- EF — Eau Froide
- EC — Eau Chaude
- EU — Eaux Usées
- CLIM — Réfrigérant
- VMC — Extraction
- HCU — Courants Forts
- LCU — Courants Faibles
- SPK — Sprinkler

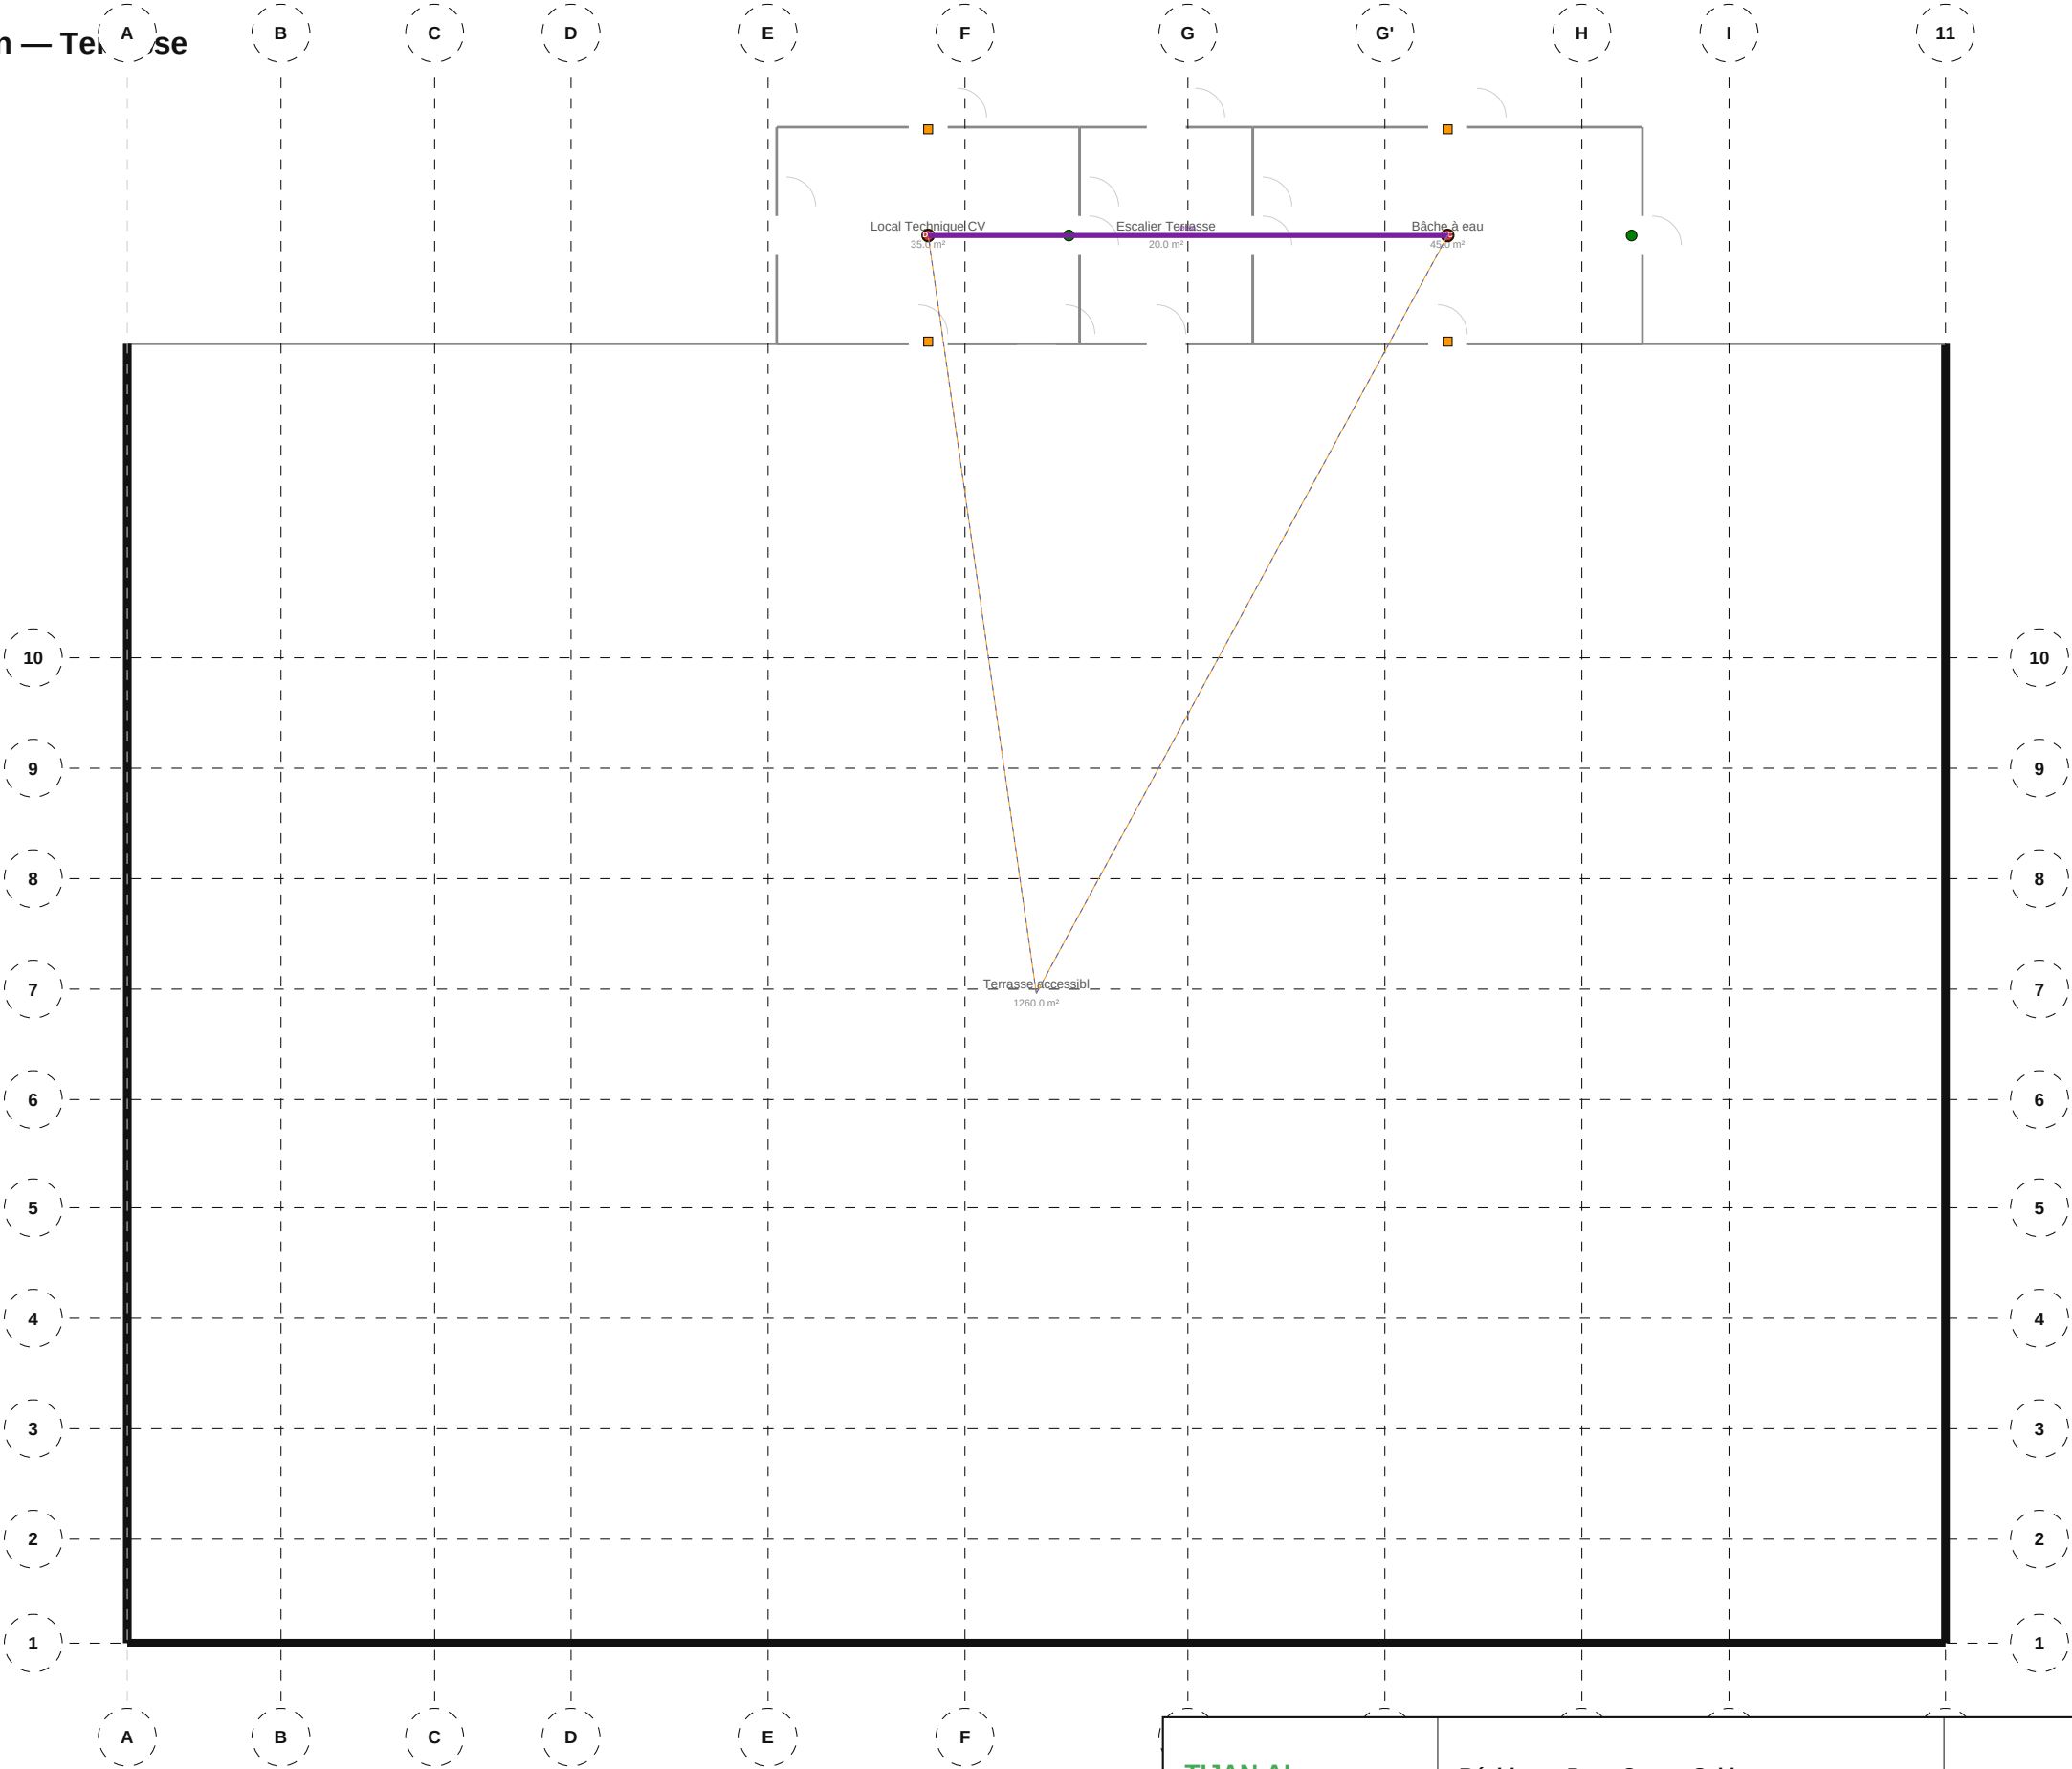

TIJAN AI Bureau d'Études Automatisé	Résidence Papa Oumar Sakho Dakar, Senegal	Éch: 1/100 Pl. 88/88
	Synthèse / Coordination — Terrasse	
Date: 06/05/2026	Réf: 1711	BIM vSYN-088 Phase: APD