



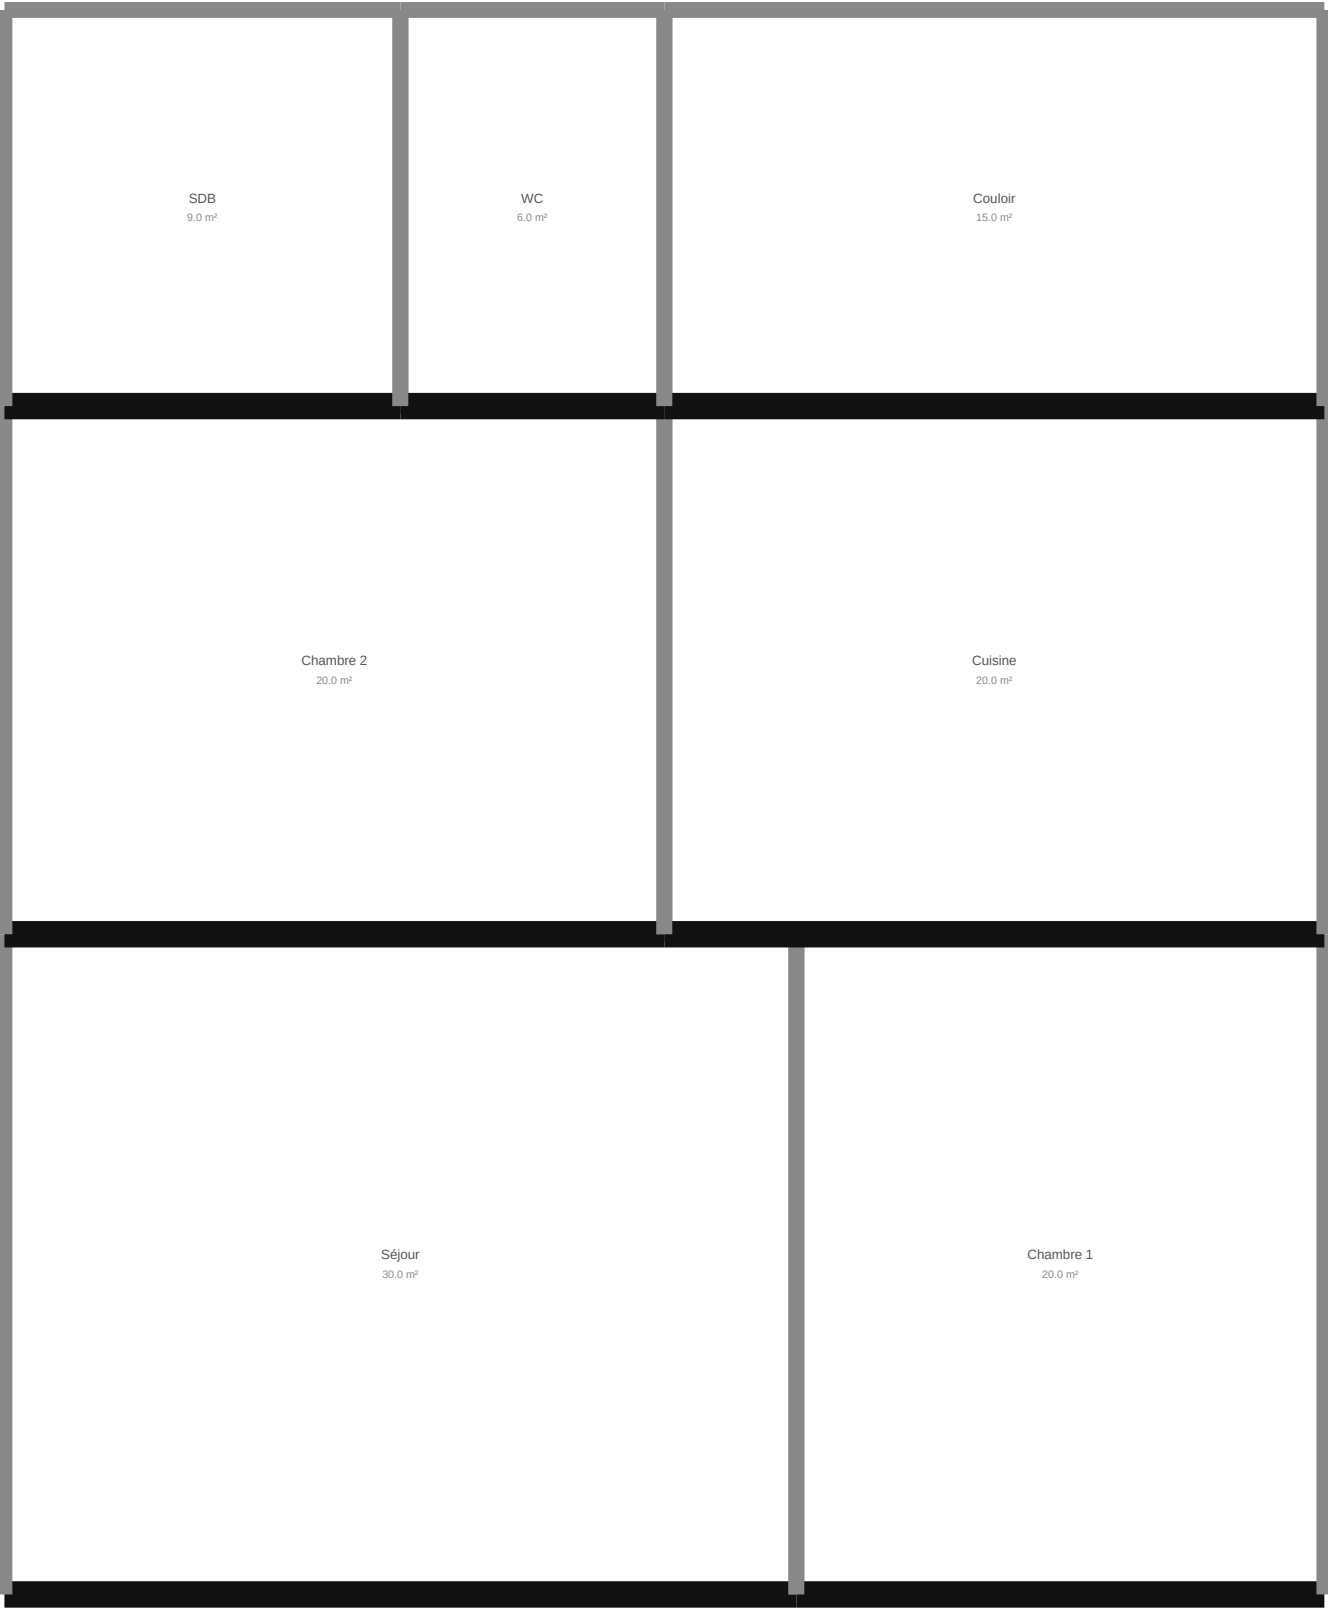

TIJAN AI Bureau d'Études Automatisé	Résidence Papa Oumar Sakho Dakar, Sénégal	Éch: 1/100 Pl. 1/70
	001 ARC — Architecture — RDC	
Date: 06/05/2026	Réf: 1711	BIM vARC-001 Phase: APD

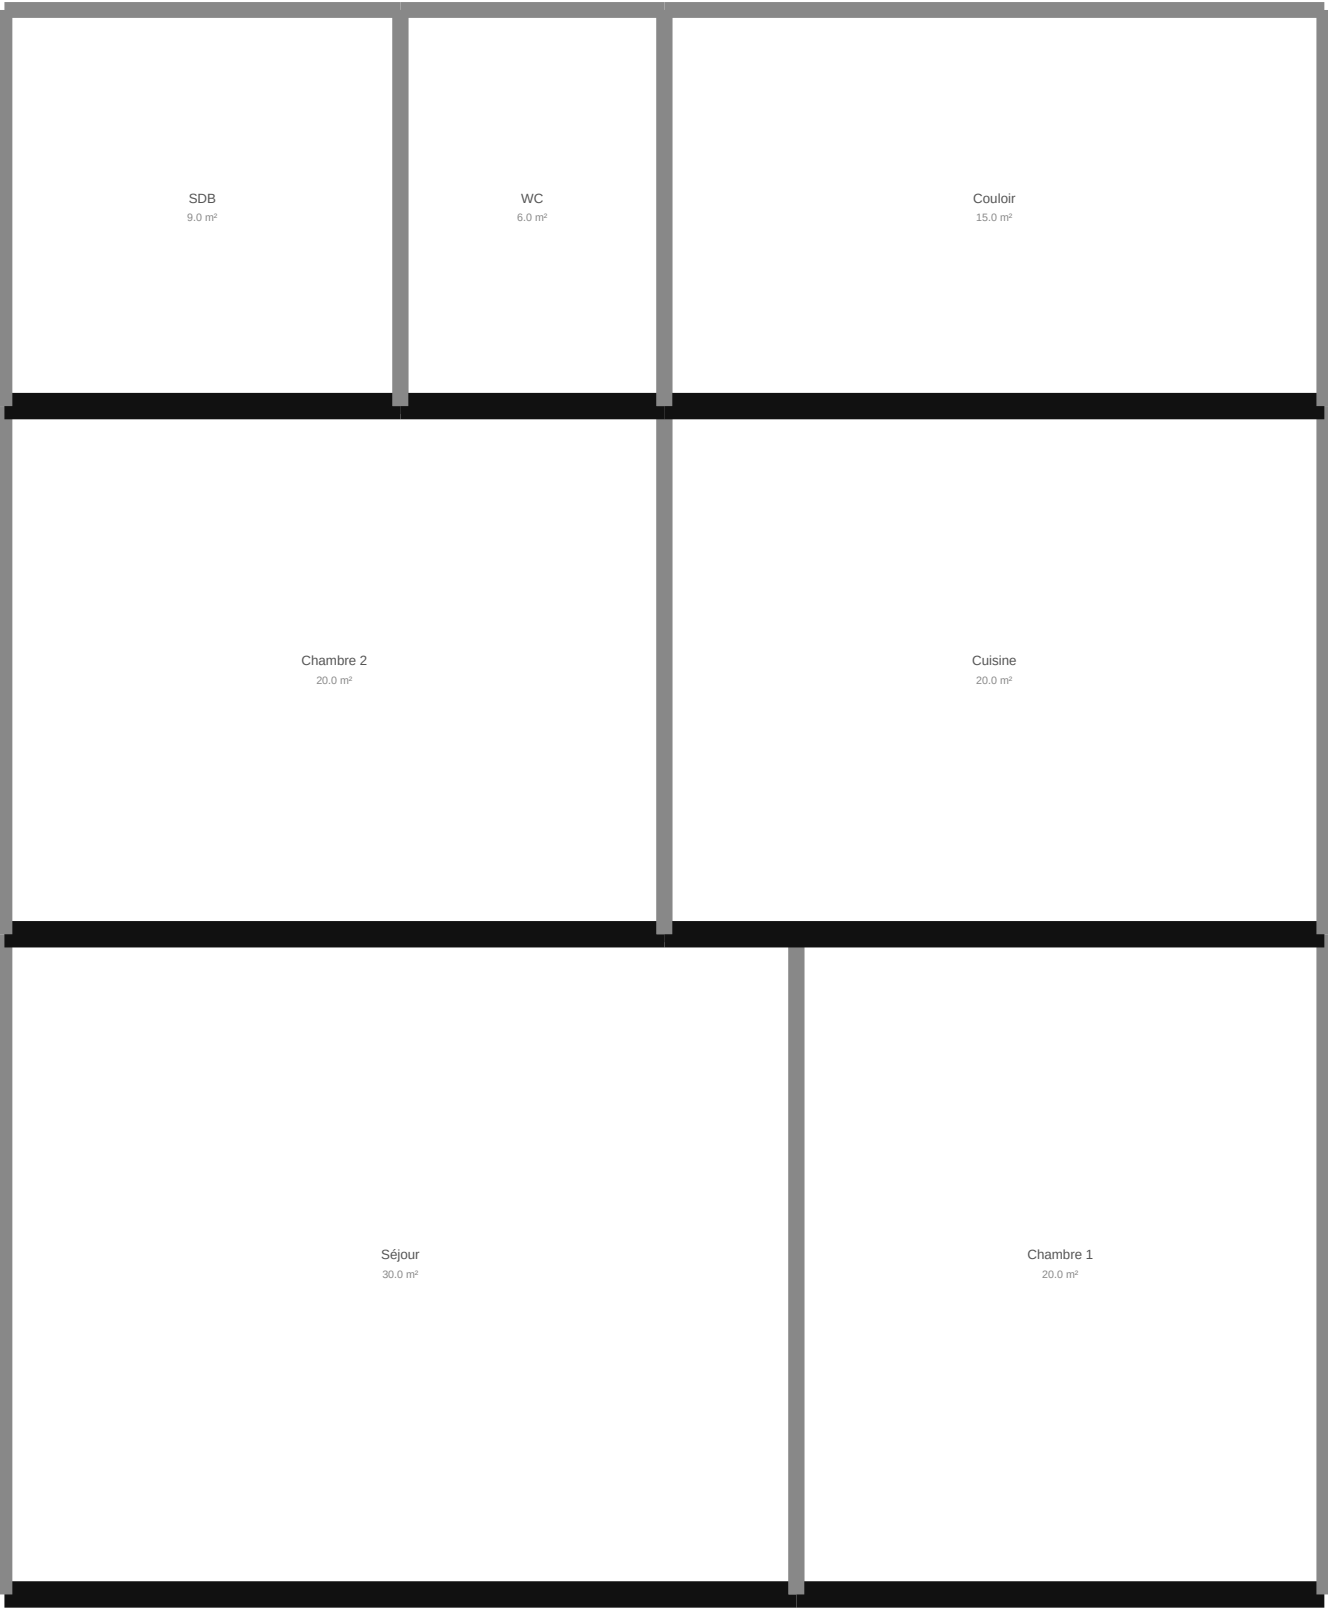

TIJAN AI Bureau d'Études Automatisé	Résidence Papa Oumar Sakho Dakar, Sénégal	Éch: 1/100 Pl. 2/70
	001 ARC — Architecture — R+1	
Date: 06/05/2026	Réf: 1711	BIM vARC-002 Phase: APD




TIJAN AI Bureau d'Études Automatisé	Résidence Papa Oumar Sakho Dakar, Sénégal	Éch: 1/100 Pl. 3/70
	001 ARC — Architecture — R+2	
Date: 06/05/2026	Réf: 1711	BIM vARC-003 Phase: APD




TIJAN AI Bureau d'Études Automatisé	Résidence Papa Oumar Sakho Dakar, Sénégal	Éch: 1/100 Pl. 4/70
	001 ARC — Architecture — R+3	
Date: 06/05/2026	Réf: 1711	BIM vARC-004 Phase: APD




TIJAN AI Bureau d'Études Automatisé	Résidence Papa Oumar Sakho Dakar, Sénégal	Éch: 1/100 Pl. 5/70
	001 ARC — Architecture — R+4	
Date: 06/05/2026	Réf: 1711	BIM vARC-005 Phase: APD

 


TIJAN AI Bureau d'Études Automatisé	Résidence Papa Oumar Sakho Dakar, Sénégal	Éch: 1/100 Pl. 6/70
	200 STR — Coffrage — RDC	
Date: 06/05/2026	Réf: 1711	BIM vSTR-006 Phase: APD

 


TIJAN AI Bureau d'Études Automatisé	Résidence Papa Oumar Sakho Dakar, Sénégal	Éch: 1/100 Pl. 7/70
	200 STR — Coffrage — R+1	
Date: 06/05/2026	Réf: 1711	BIM vSTR-007 Phase: APD

 

TIJAN AI Bureau d'Études Automatisé	Résidence Papa Oumar Sakho Dakar, Sénégal	Éch: 1/100 Pl. 8/70
	200 STR — Coffrage — R+2	
Date: 06/05/2026	Réf: 1711	BIM vSTR-008 Phase: APD

 


TIJAN AI Bureau d'Études Automatisé	Résidence Papa Oumar Sakho Dakar, Sénégal	Éch: 1/100 Pl. 9/70
	200 STR — Coffrage — R+3	
Date: 06/05/2026	Réf: 1711	BIM vSTR-009 Phase: APD

 

TIJAN AI Bureau d'Études Automatisé	Résidence Papa Oumar Sakho Dakar, Sénégal	Éch: 1/100 Pl. 10/70
	200 STR — Coffrage — R+4	
Date: 06/05/2026	Réf: 1711	BIM vSTR-010 Phase: APD


410 PLU — Eau Froide (EF) — RDC

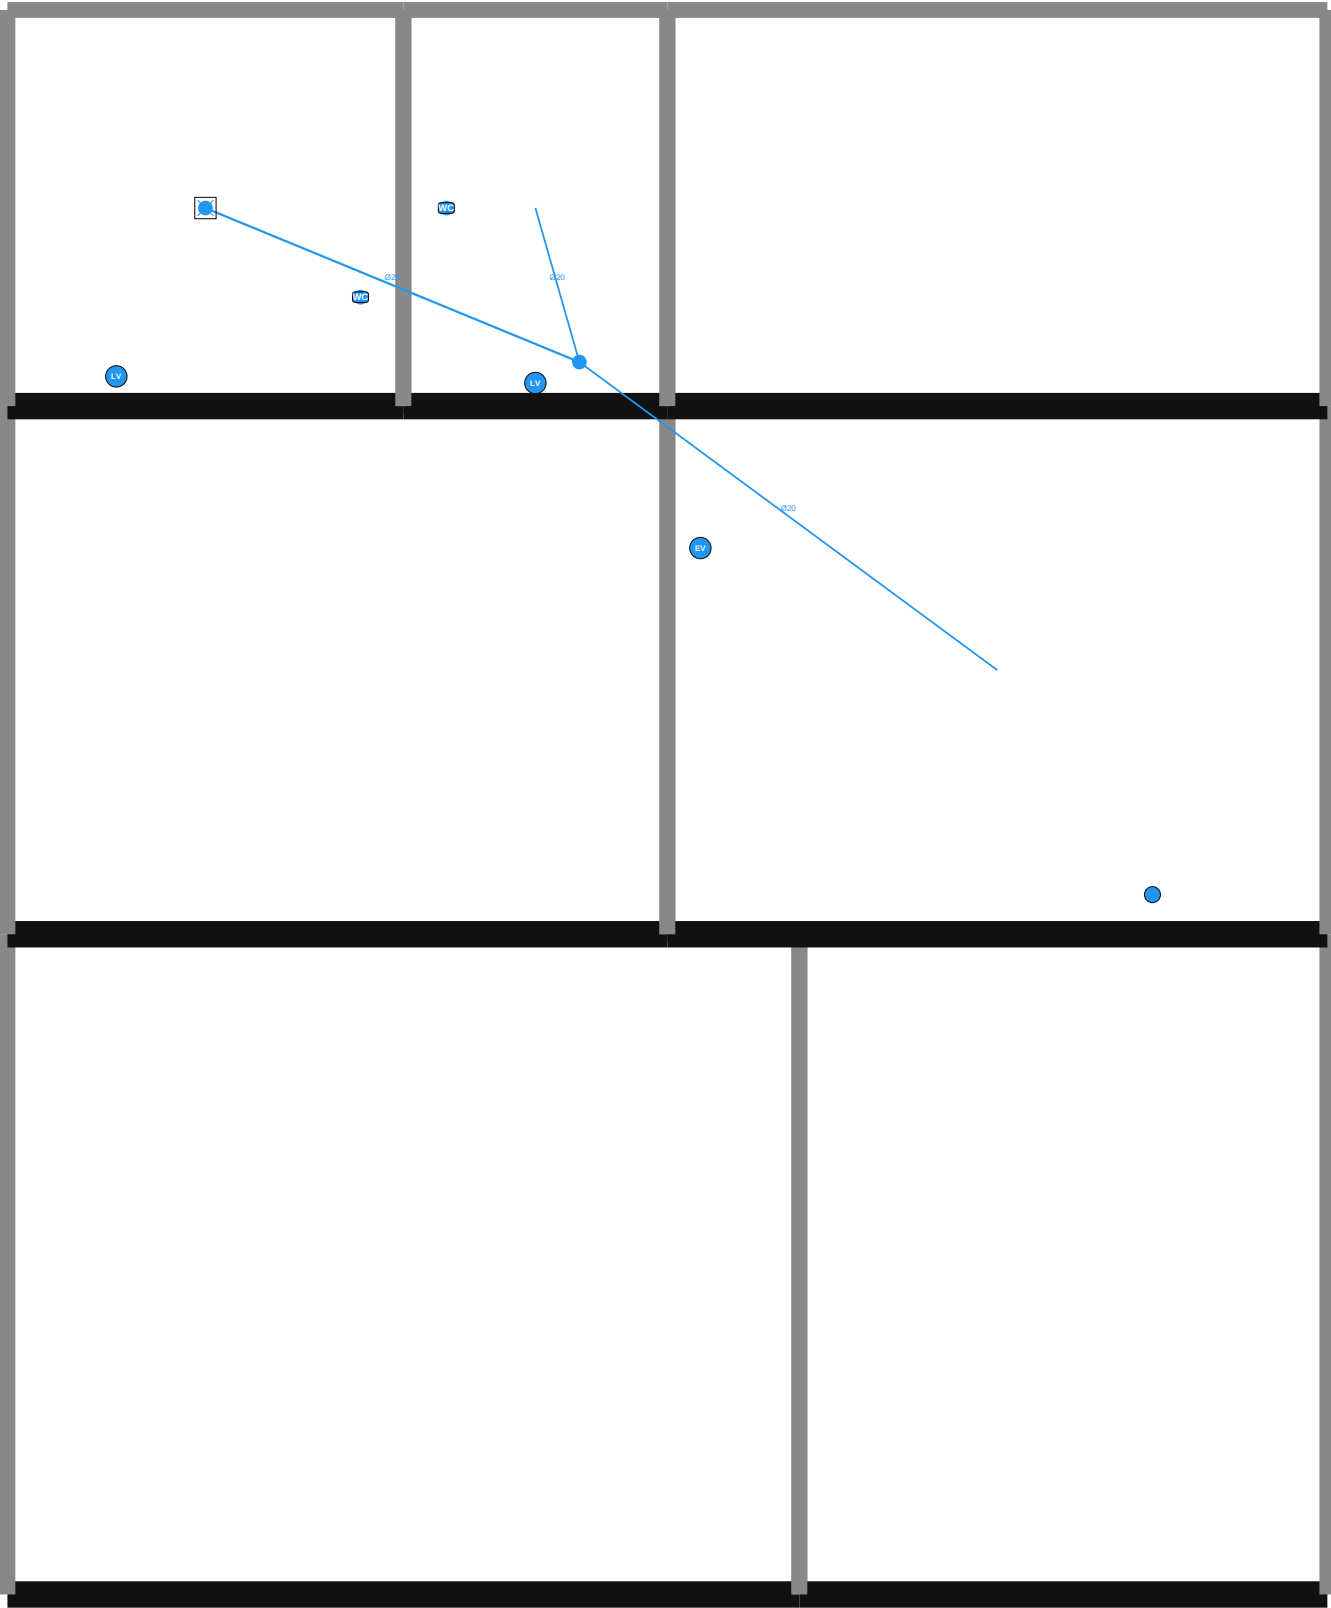

NOMENCLATURE — 410 PLU — Eau Froide (EF)

- WC suspendu: 2
- Évier cuisine: 1
- Lave-vaisselle: 1
- Lavabo: 1
- Douche: 1
- Lave-mains: 1


TIJAN AI Bureau d'Études Automatisé	Résidence Papa Oumar Sakho Dakar, Sénégal	Éch: 1/100 Pl. 11/70
	410 PLU — Eau Froide (EF) — RDC	
Date: 06/05/2026	Réf: 1711	BIM vPLU-011 Phase: APD

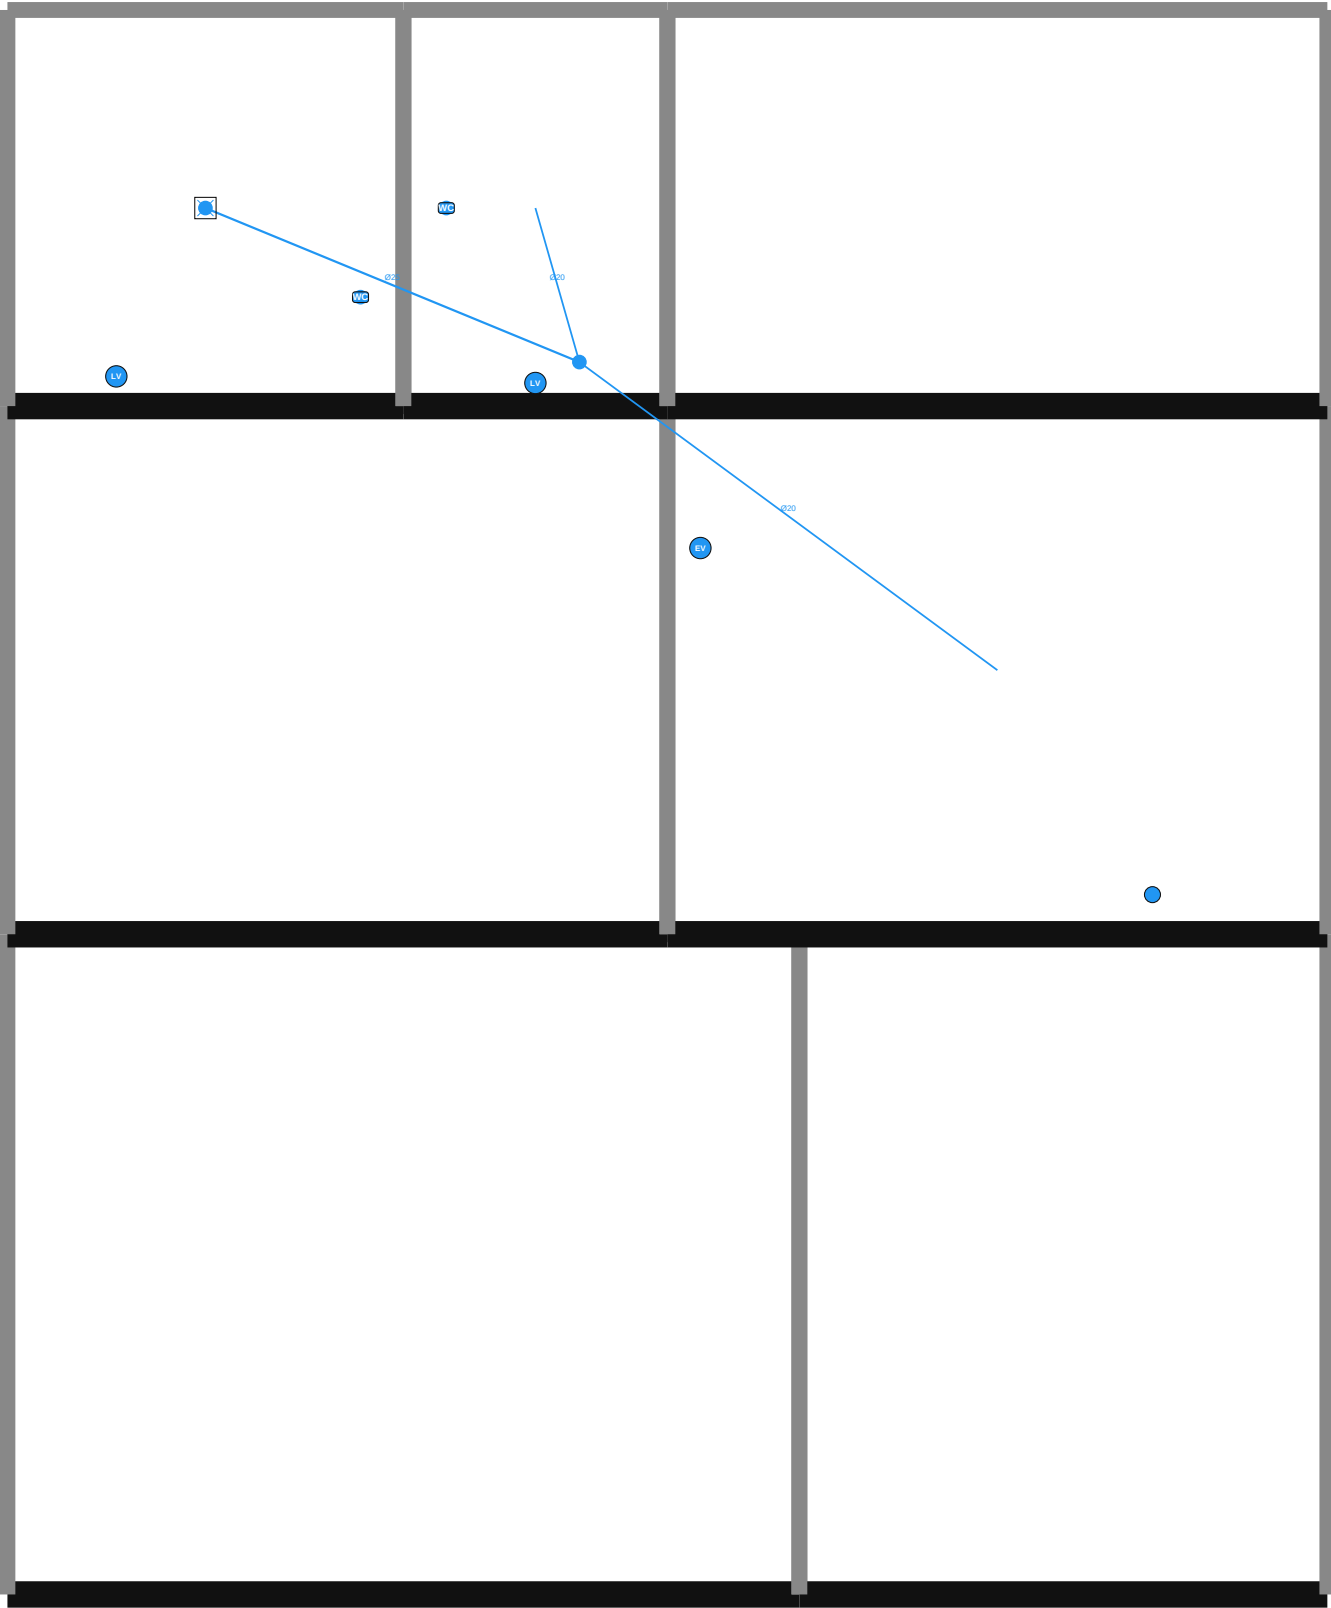

NOMENCLATURE — 410 PLU — Eau Froide (EF)

- WC suspendu: 2
- Évier cuisine: 1
- Lave-vaisselle: 1
- Lavabo: 1
- Douche: 1
- Lave-mains: 1


TIJAN AI Bureau d'Études Automatisé	Résidence Papa Oumar Sakho Dakar, Sénégal	Éch: 1/100 Pl. 12/70
	410 PLU — Eau Froide (EF) — R+1	
Date: 06/05/2026	Réf: 1711	BIM vPLU-012 Phase: APD

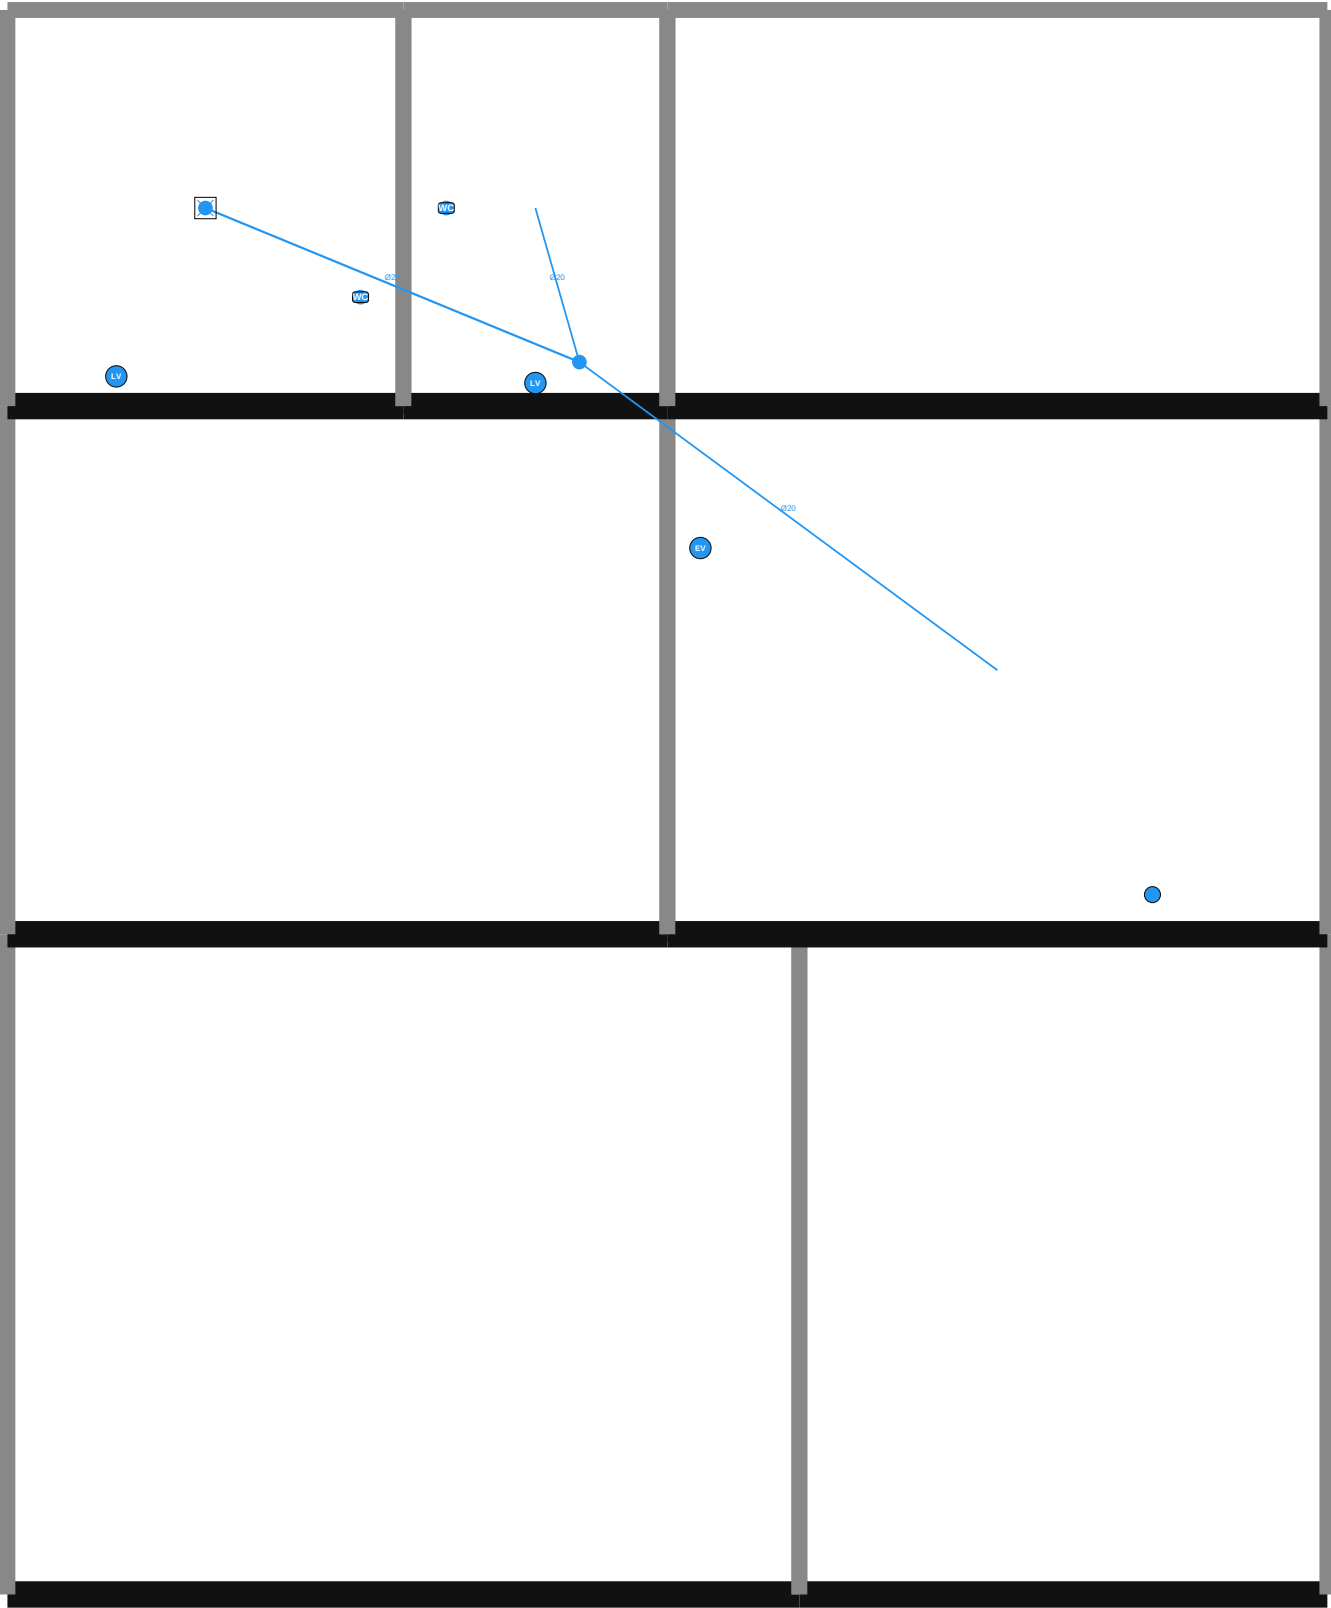

NOMENCLATURE — 410 PLU — Eau Froide (EF)

- WC suspendu: 2
- Évier cuisine: 1
- Lave-vaisselle: 1
- Lavabo: 1
- Douche: 1
- Lave-mains: 1


TIJAN AI Bureau d'Études Automatisé	Résidence Papa Oumar Sakho Dakar, Sénégal	Éch: 1/100 Pl. 13/70
	410 PLU — Eau Froide (EF) — R+2	
Date: 06/05/2026	Réf: 1711	BIM vPLU-013 Phase: APD

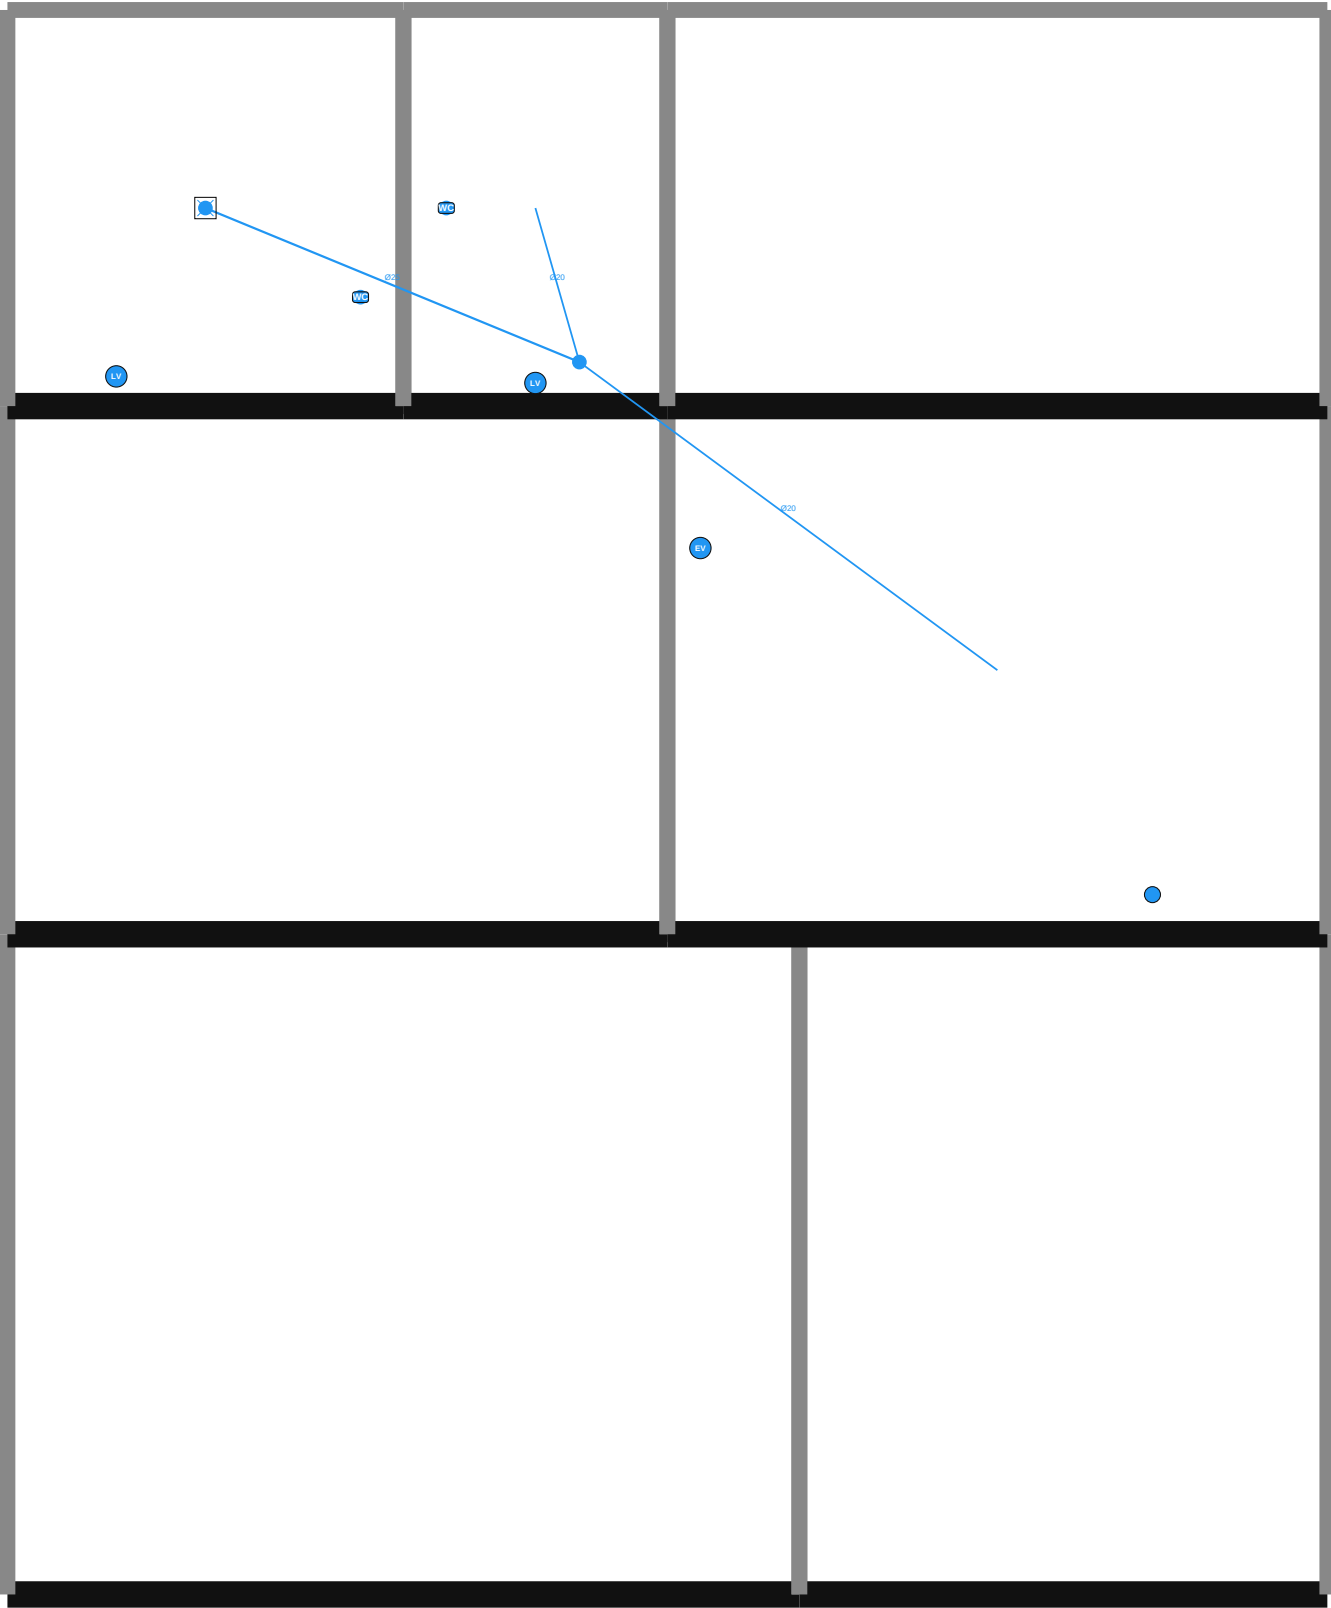

NOMENCLATURE — 410 PLU — Eau Froide (EF)

- WC suspendu: 2
- Évier cuisine: 1
- Lave-vaisselle: 1
- Lavabo: 1
- Douche: 1
- Lave-mains: 1


TIJAN AI Bureau d'Études Automatisé	Résidence Papa Oumar Sakho Dakar, Sénégal	Éch: 1/100 Pl. 14/70
	410 PLU — Eau Froide (EF) — R+3	
Date: 06/05/2026	Réf: 1711	BIM vPLU-014 Phase: APD

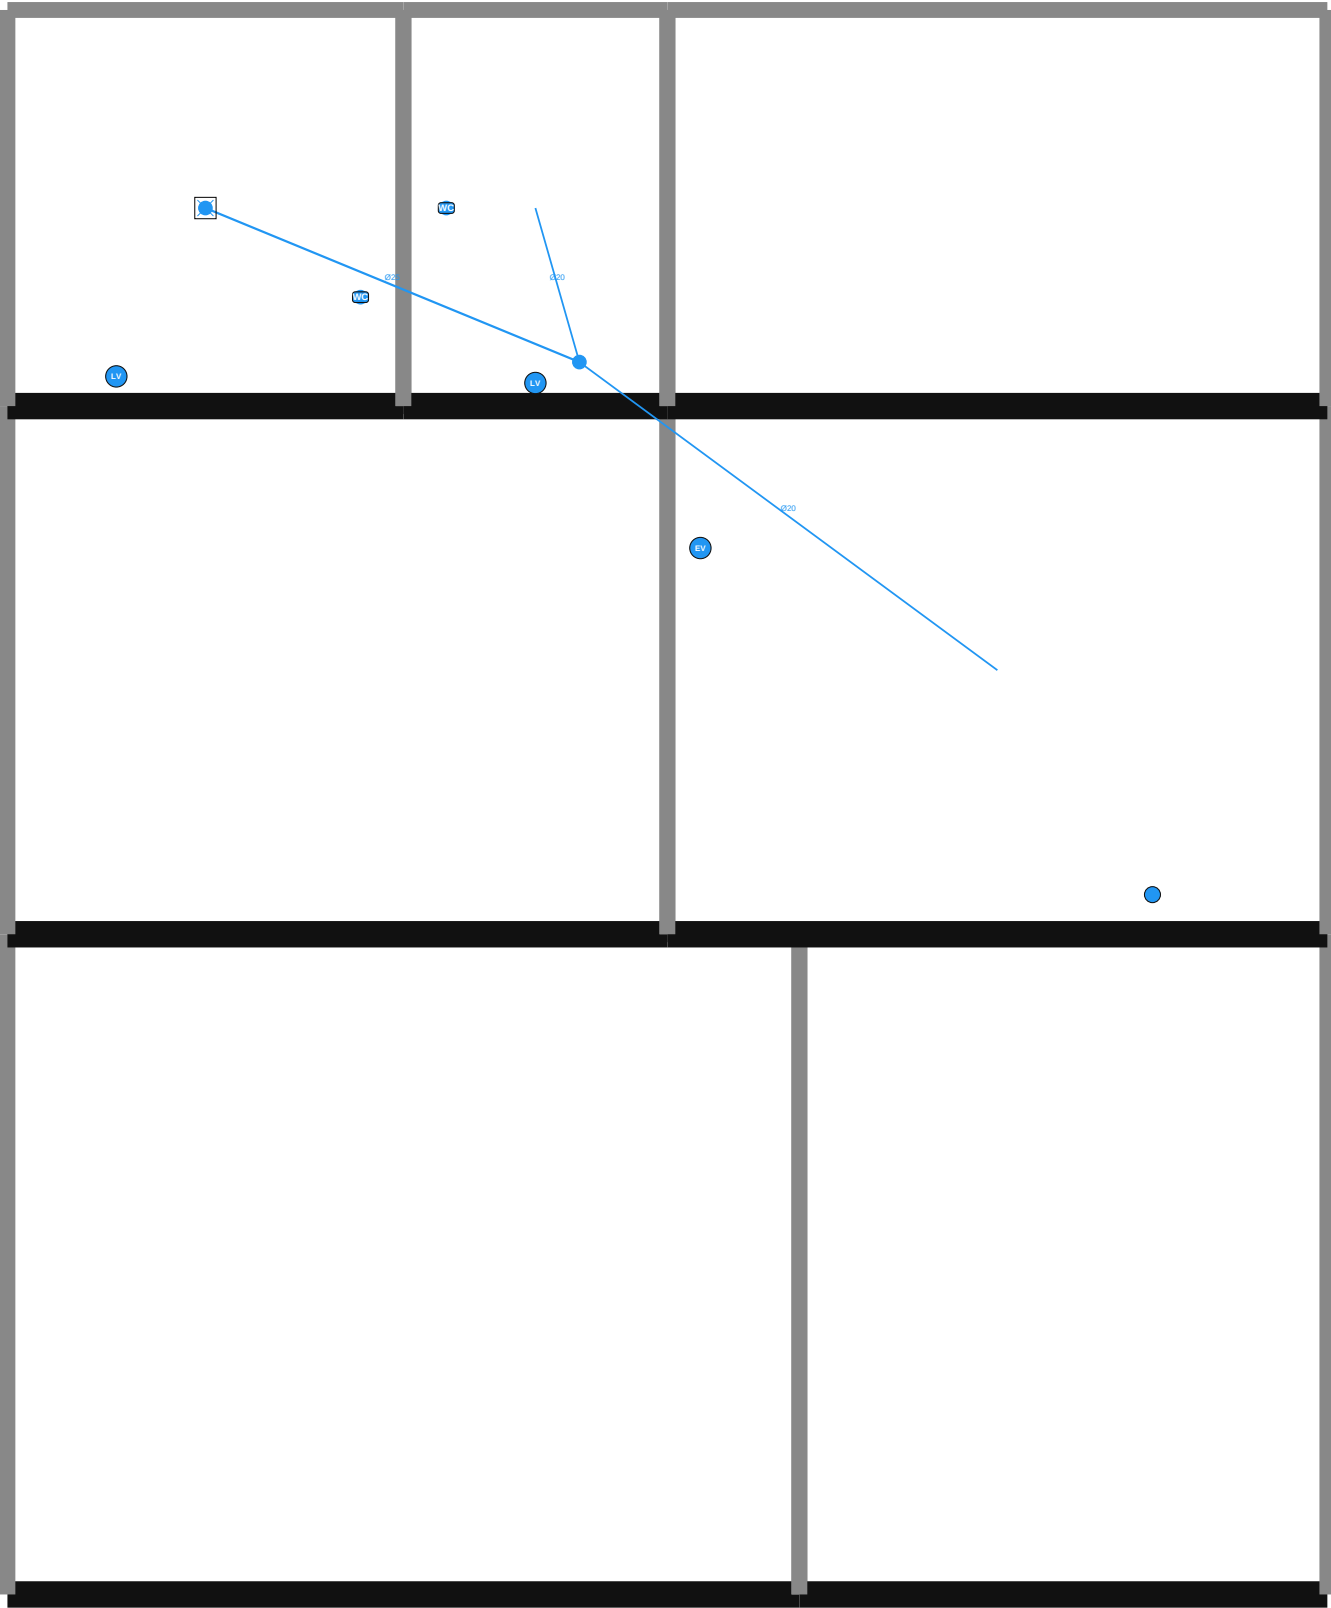

NOMENCLATURE — 410 PLU — Eau Froide (EF)

- WC suspendu: 2
- Évier cuisine: 1
- Lave-vaisselle: 1
- Lavabo: 1
- Douche: 1
- Lave-mains: 1


TIJAN AI Bureau d'Études Automatisé	Résidence Papa Oumar Sakho Dakar, Sénégal	Éch: 1/100 Pl. 15/70
	410 PLU — Eau Froide (EF) — R+4	
Date: 06/05/2026	Réf: 1711	BIM vPLU-015 Phase: APD

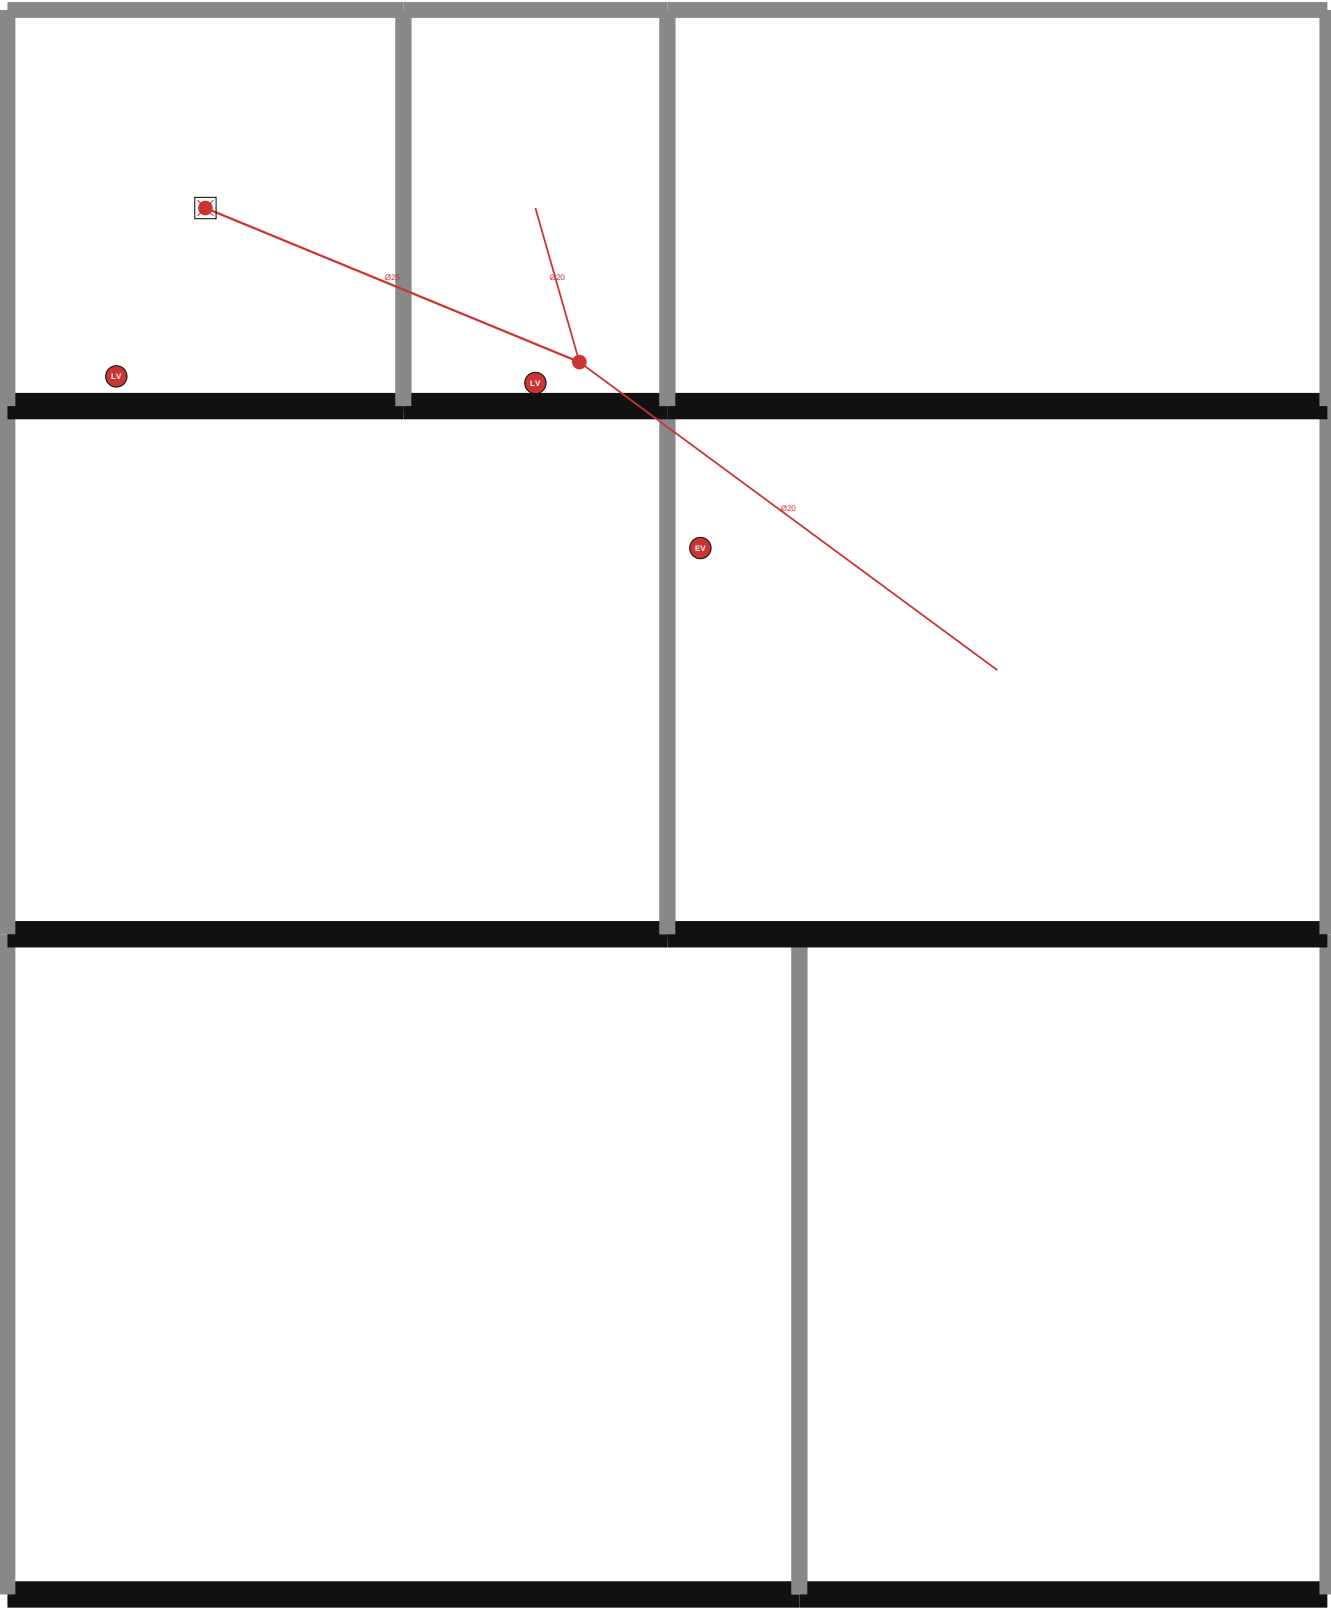

NOMENCLATURE — 410 PLU — Eau Chaude (EC)

- Évier cuisine: 1
- Lavabo: 1
- Douche: 1
- Lave-mains: 1


TIJAN AI Bureau d'Études Automatisé	Résidence Papa Oumar Sakho Dakar, Sénégal	Éch: 1/100 Pl. 16/70
	410 PLU — Eau Chaude (EC) — RDC	
Date: 06/05/2026	Réf: 1711	BIM vPLU-016 Phase: APD

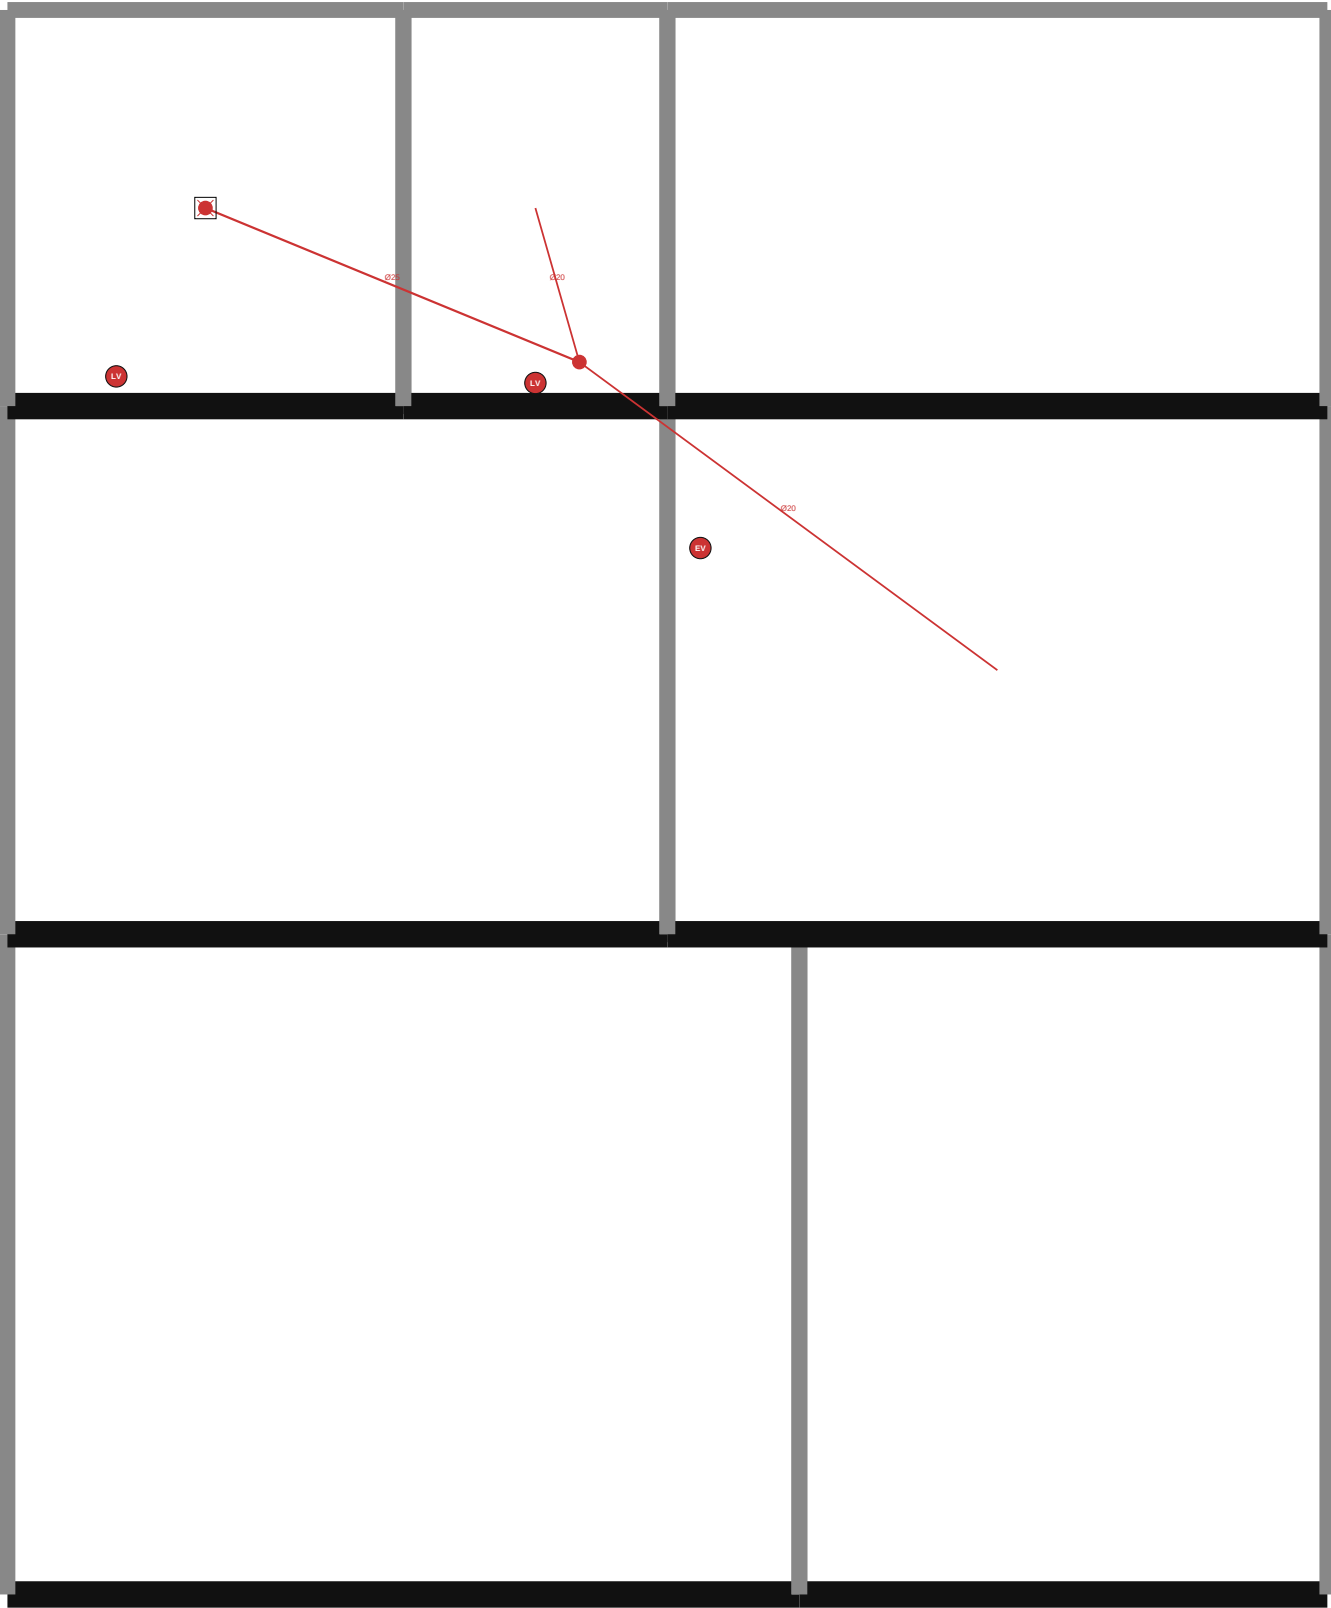

NOMENCLATURE — 410 PLU — Eau Chaude (EC)

- Évier cuisine: 1
- Lavabo: 1
- Douche: 1
- Lave-mains: 1

TIJAN AI Bureau d'Études Automatisé	Résidence Papa Oumar Sakho Dakar, Sénégal	Éch: 1/100 Pl. 17/70
	410 PLU — Eau Chaude (EC) — R+1	
Date: 06/05/2026	Réf: 1711	BIM vPLU-017 Phase: APD

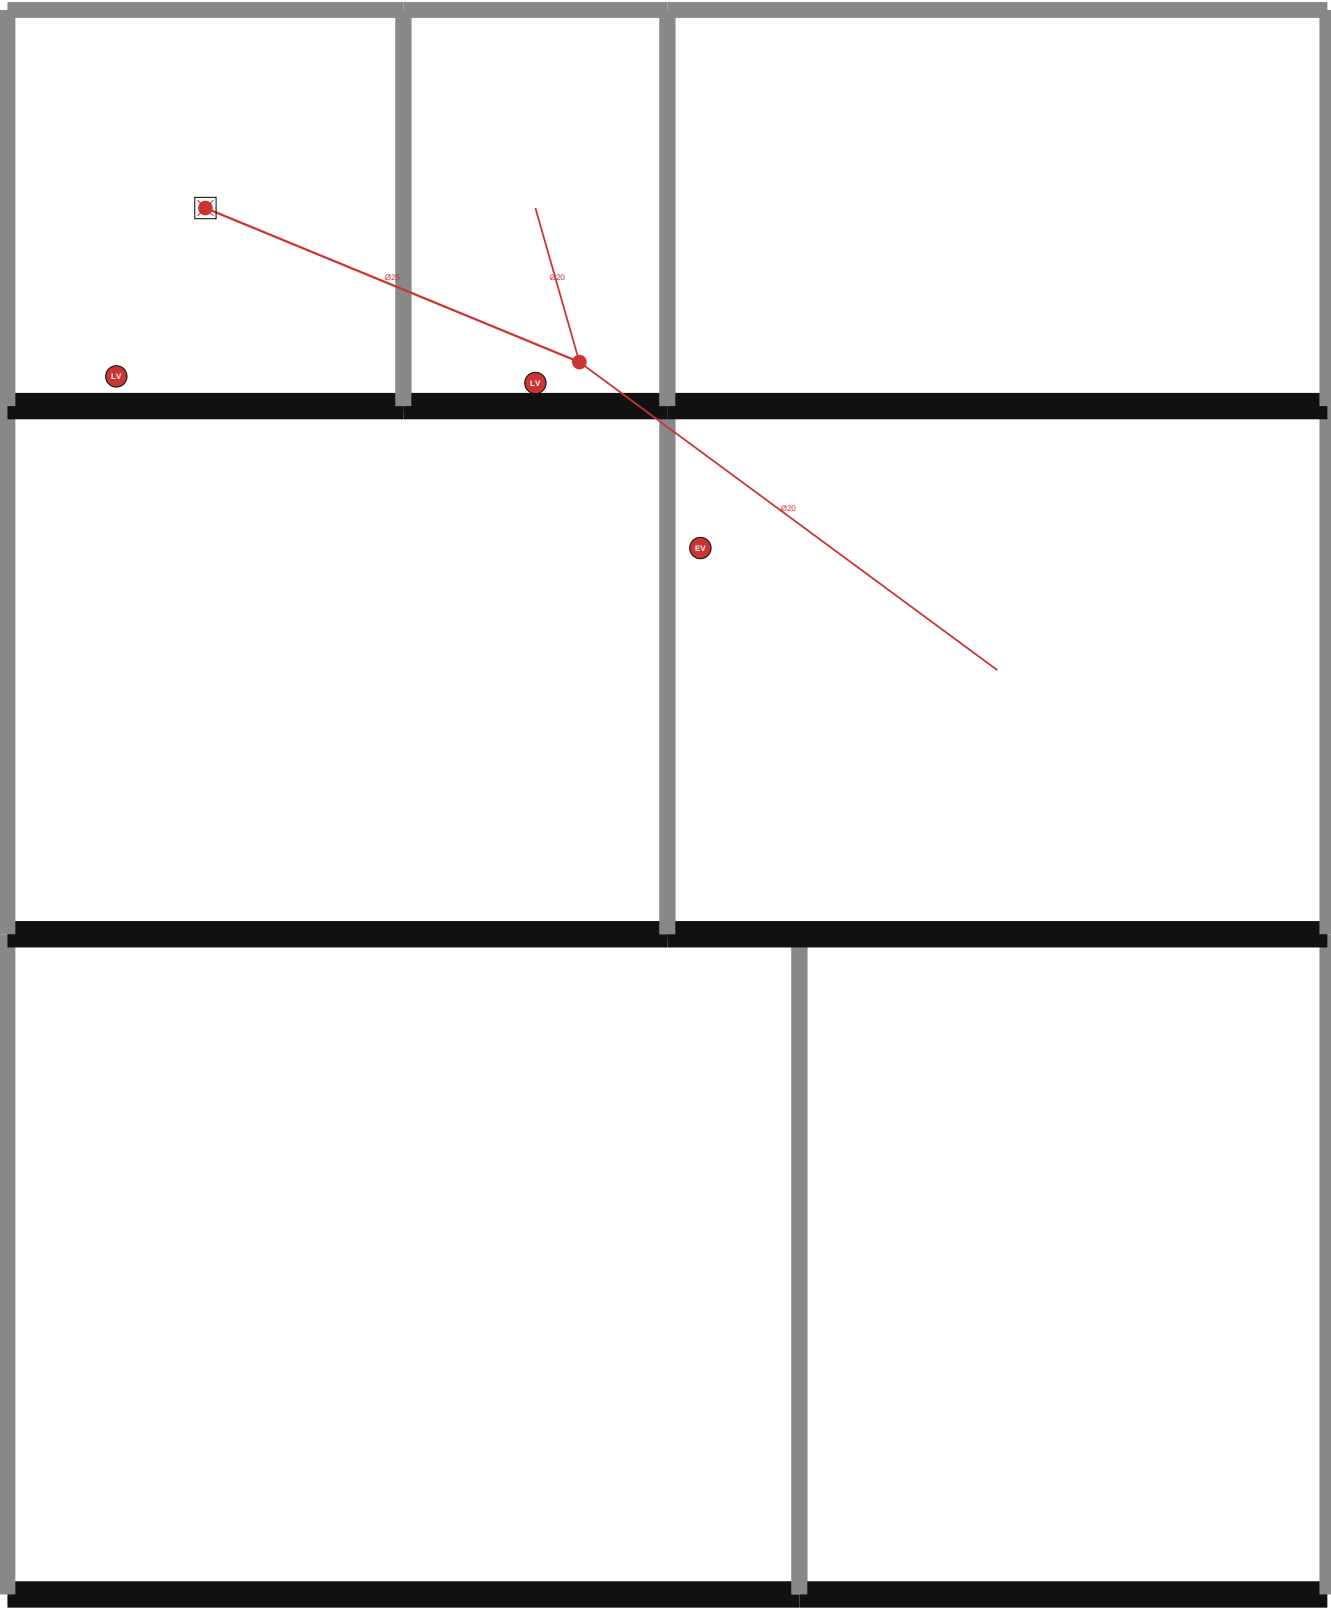

NOMENCLATURE — 410 PLU — Eau Chaude (EC)

- Évier cuisine: 1
- Lavabo: 1
- Douche: 1
- Lave-mains: 1

TIJAN AI

Bureau d'Études Automatisé

Résidence Papa Oumar Sakho

Dakar, Sénégal

Éch: 1/100

Pl. 18/70


410 PLU — Eau Chaude (EC) — R+2

Date: 06/05/2026

Réf: 1711

BIM vPLU-018


Phase: APD

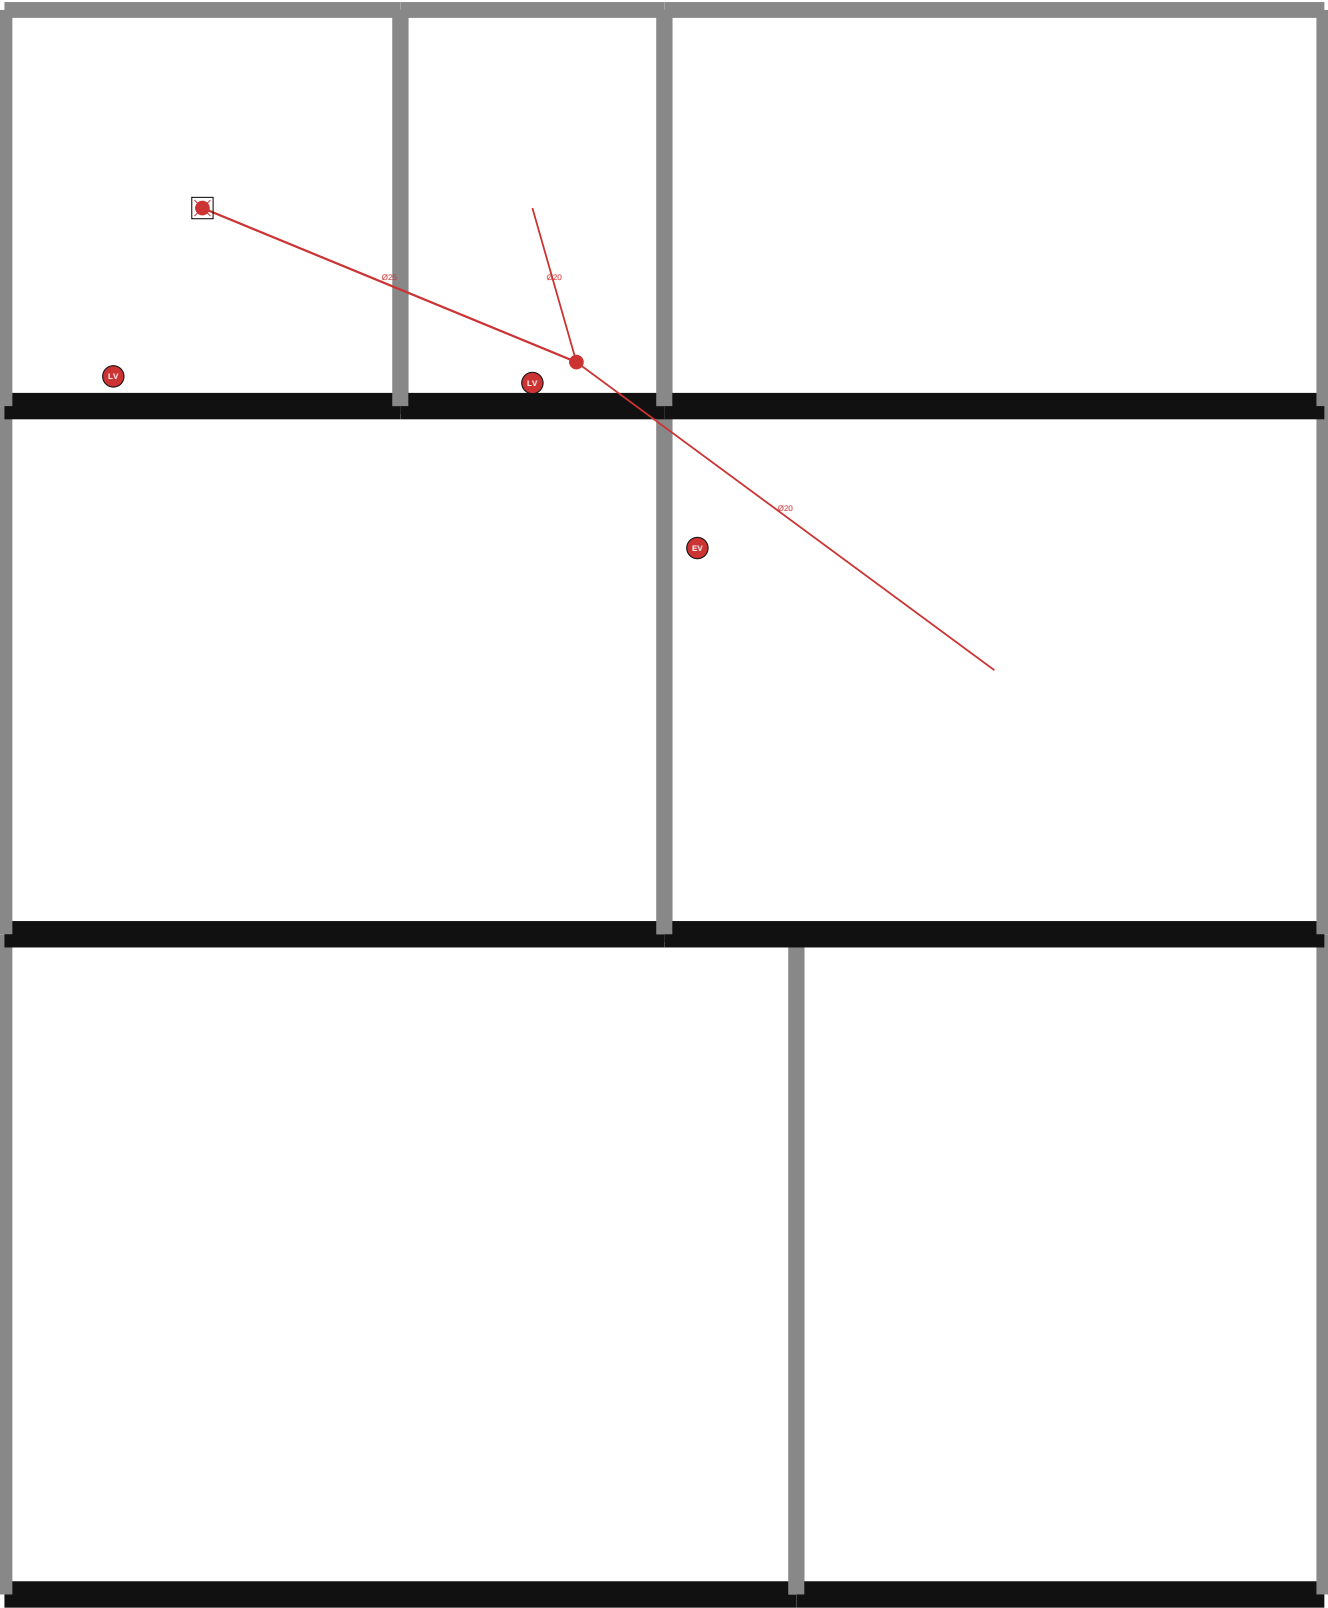

NOMENCLATURE — 410 PLU — Eau Chaude (EC)

- Évier cuisine: 1
- Lavabo: 1
- Douche: 1
- Lave-mains: 1


TIJAN AI Bureau d'Études Automatisé	Résidence Papa Oumar Sakho Dakar, Sénégal	Éch: 1/100 Pl. 19/70
	410 PLU — Eau Chaude (EC) — R+3	
Date: 06/05/2026	Réf: 1711	BIM vPLU-019 Phase: APD

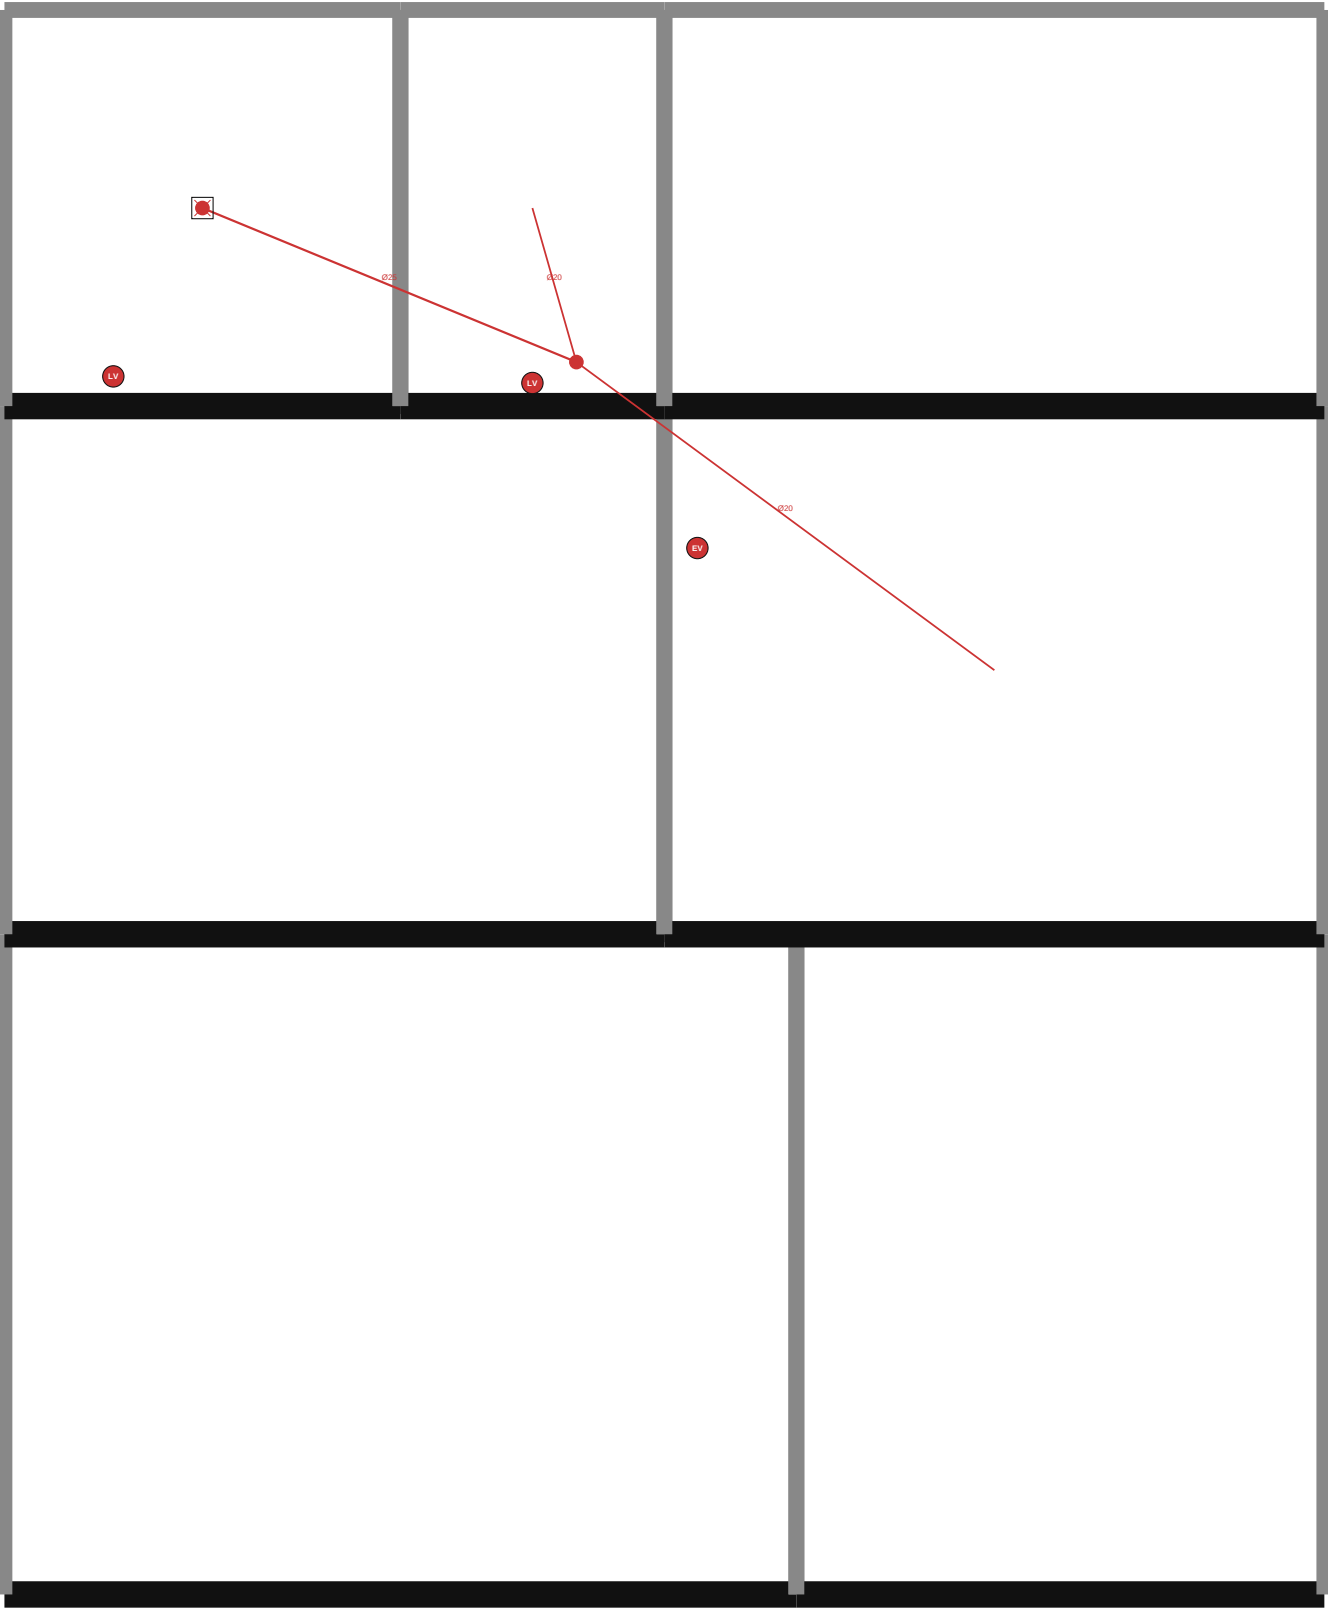

NOMENCLATURE — 410 PLU — Eau Chaude (EC)

- Évier cuisine: 1
- Lavabo: 1
- Douche: 1
- Lave-mains: 1


TIJAN AI Bureau d'Études Automatisé	Résidence Papa Oumar Sakho Dakar, Sénégal	Éch: 1/100 Pl. 20/70
	410 PLU — Eau Chaude (EC) — R+4	
Date: 06/05/2026	Réf: 1711	BIM vPLU-020 Phase: APD

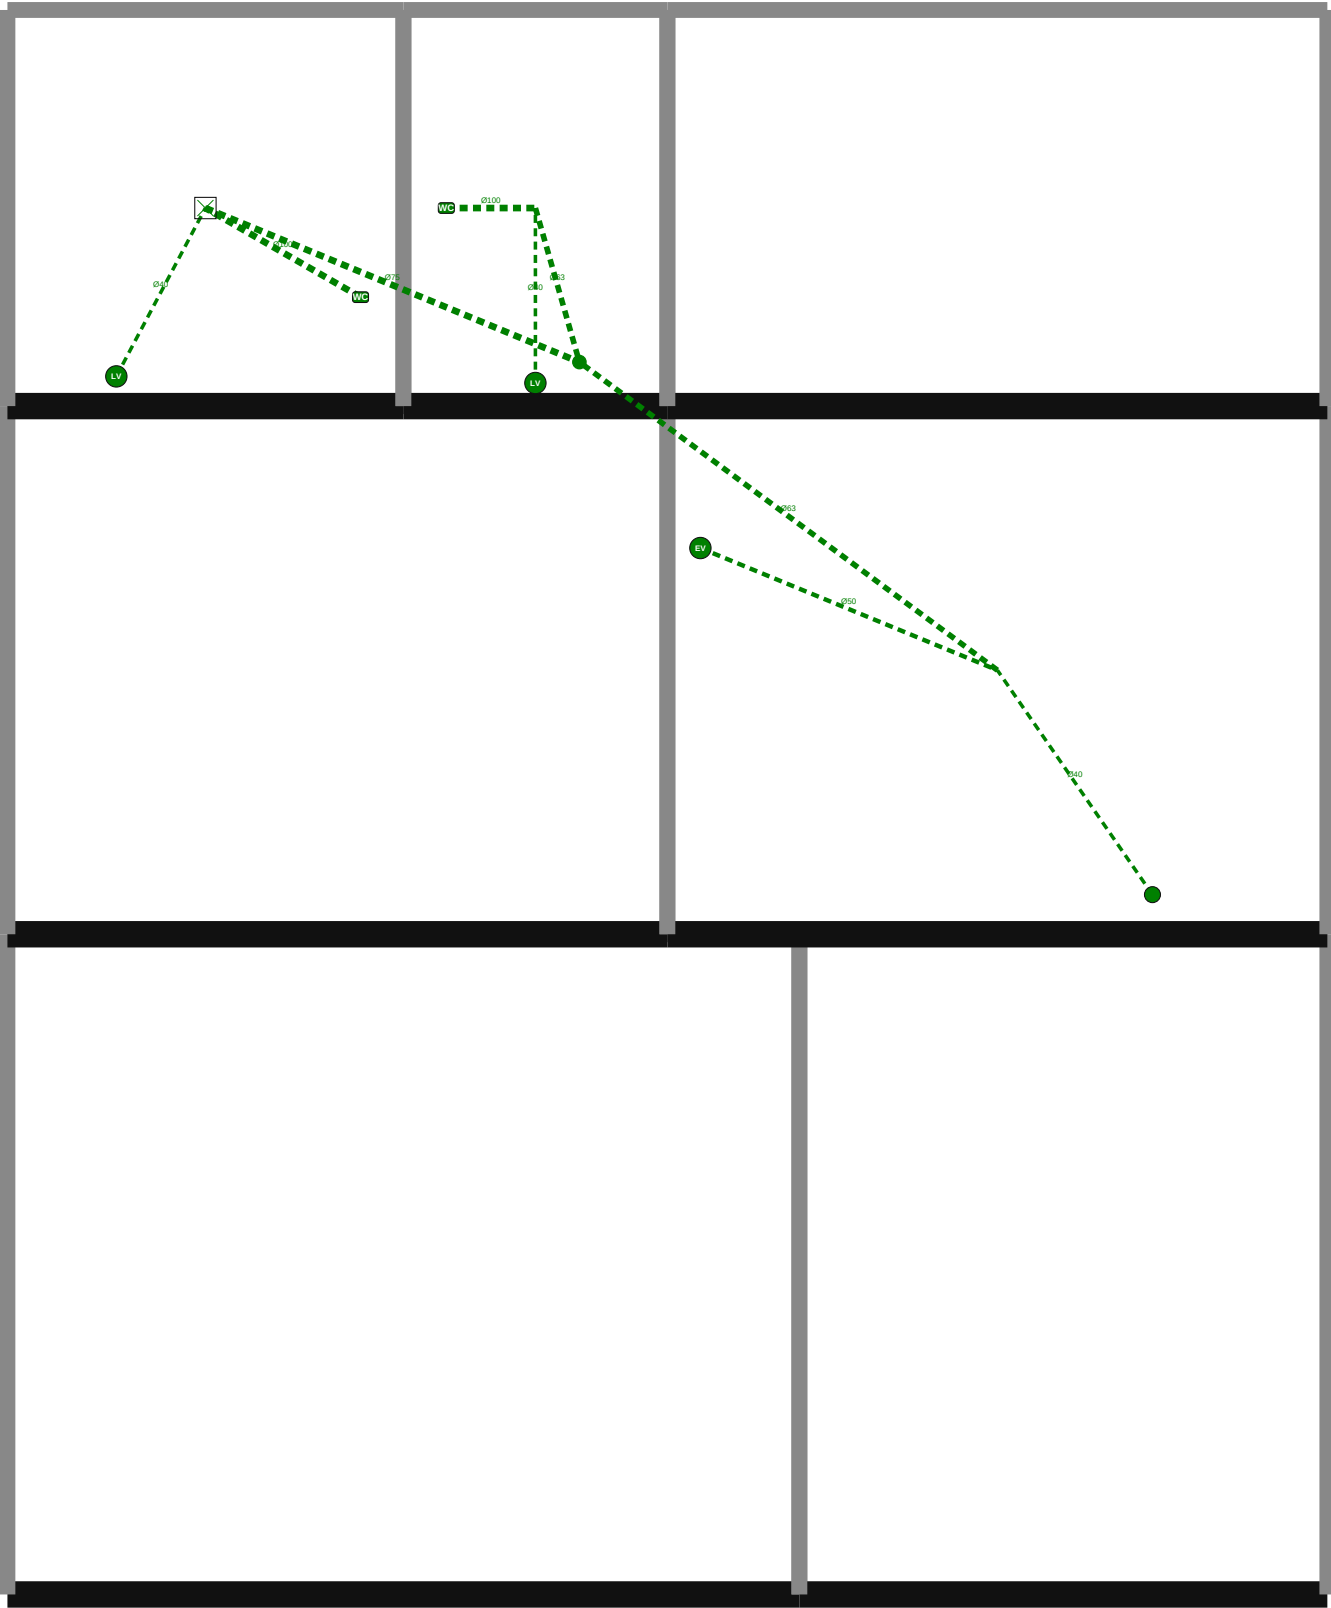

NOMENCLATURE — 410 PLU — Eaux Usées (EU)

- WC suspendu: 2
- Évier cuisine: 1
- Lave-vaisselle: 1
- Lavabo: 1
- Douche: 1
- Lave-mains: 1


TIJAN AI Bureau d'Études Automatisé	Résidence Papa Oumar Sakho Dakar, Sénégal	Éch: 1/100 Pl. 21/70
	410 PLU — Eaux Usées (EU) — RDC	
Date: 06/05/2026	Réf: 1711	BIM vPLU-021 Phase: APD

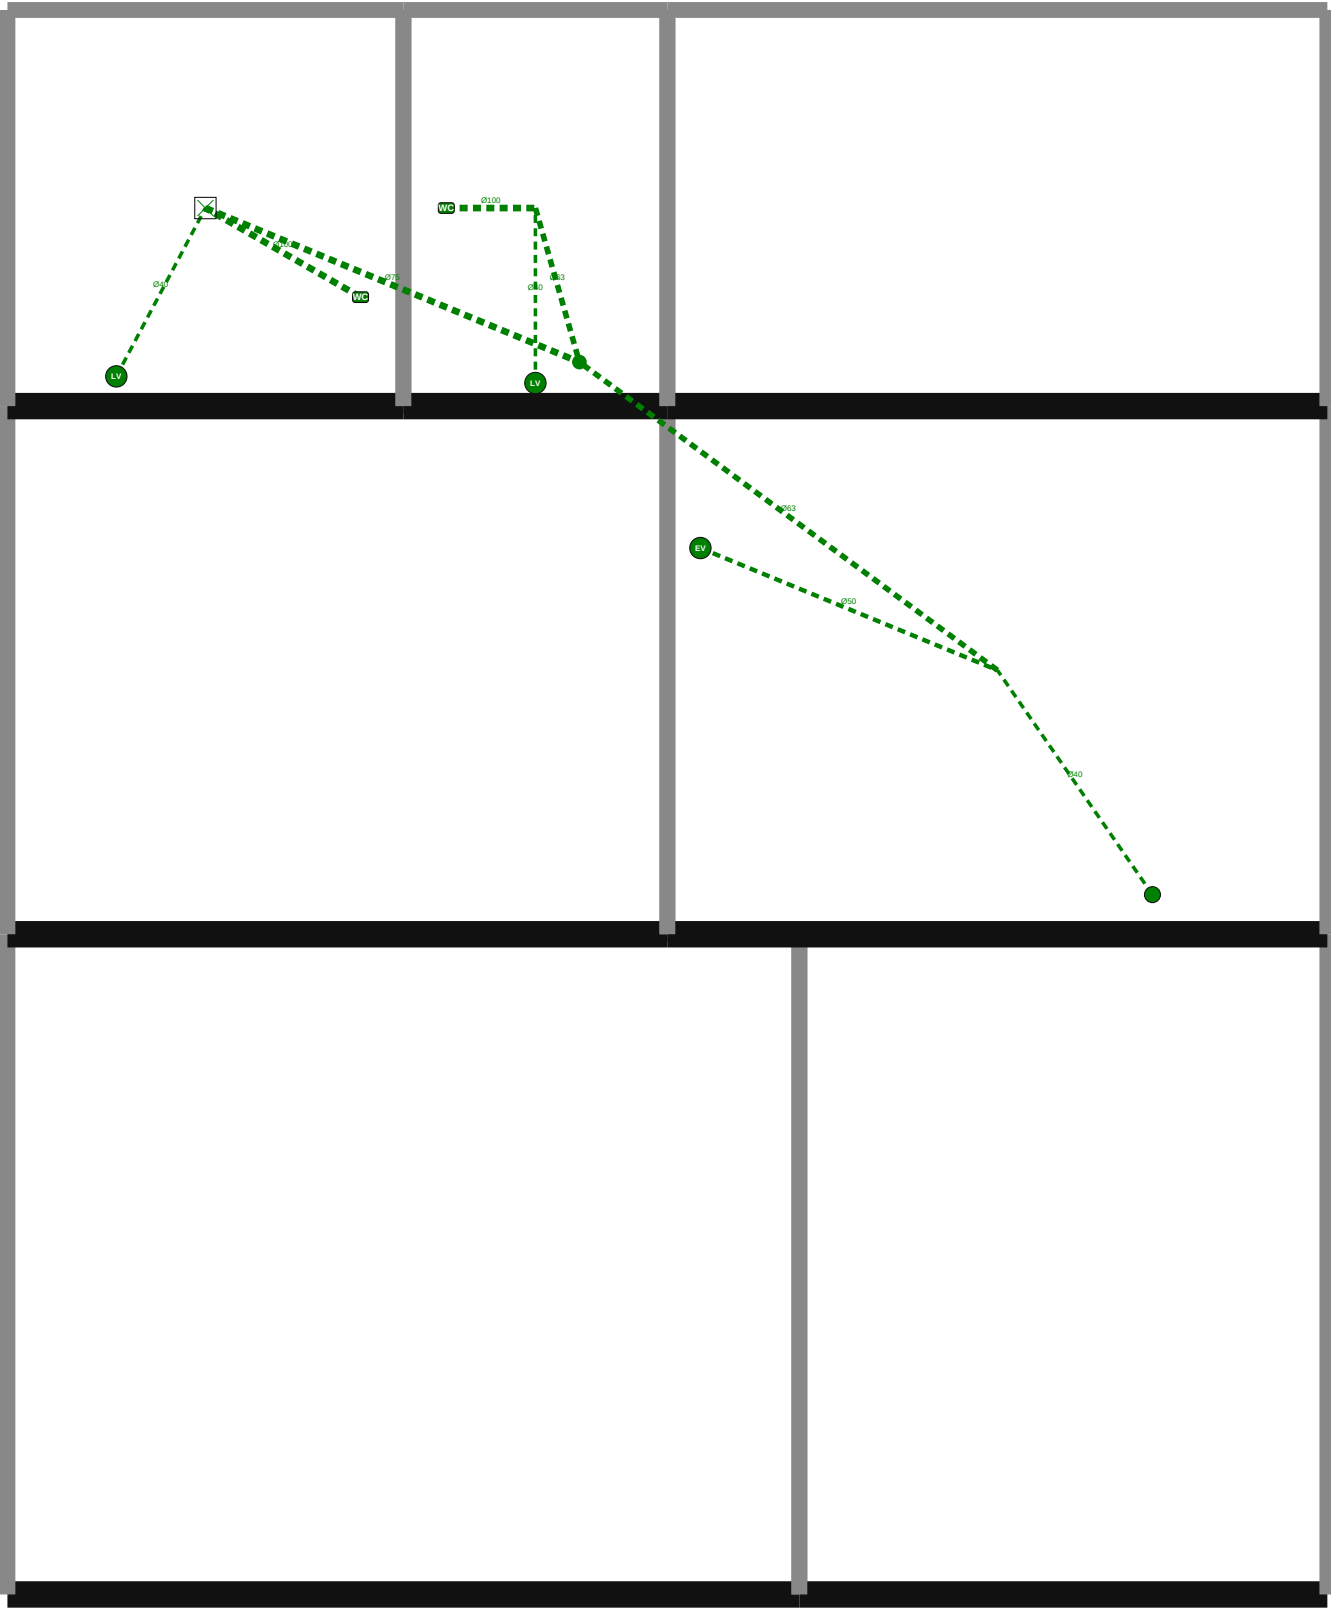

NOMENCLATURE — 410 PLU — Eaux Usées (EU)

- WC suspendu: 2
- Évier cuisine: 1
- Lave-vaisselle: 1
- Lavabo: 1
- Douche: 1
- Lave-mains: 1


TIJAN AI Bureau d'Études Automatisé	Résidence Papa Oumar Sakho Dakar, Sénégal	Éch: 1/100 Pl. 22/70
	410 PLU — Eaux Usées (EU) — R+1	
Date: 06/05/2026	Réf: 1711	BIM vPLU-022 Phase: APD

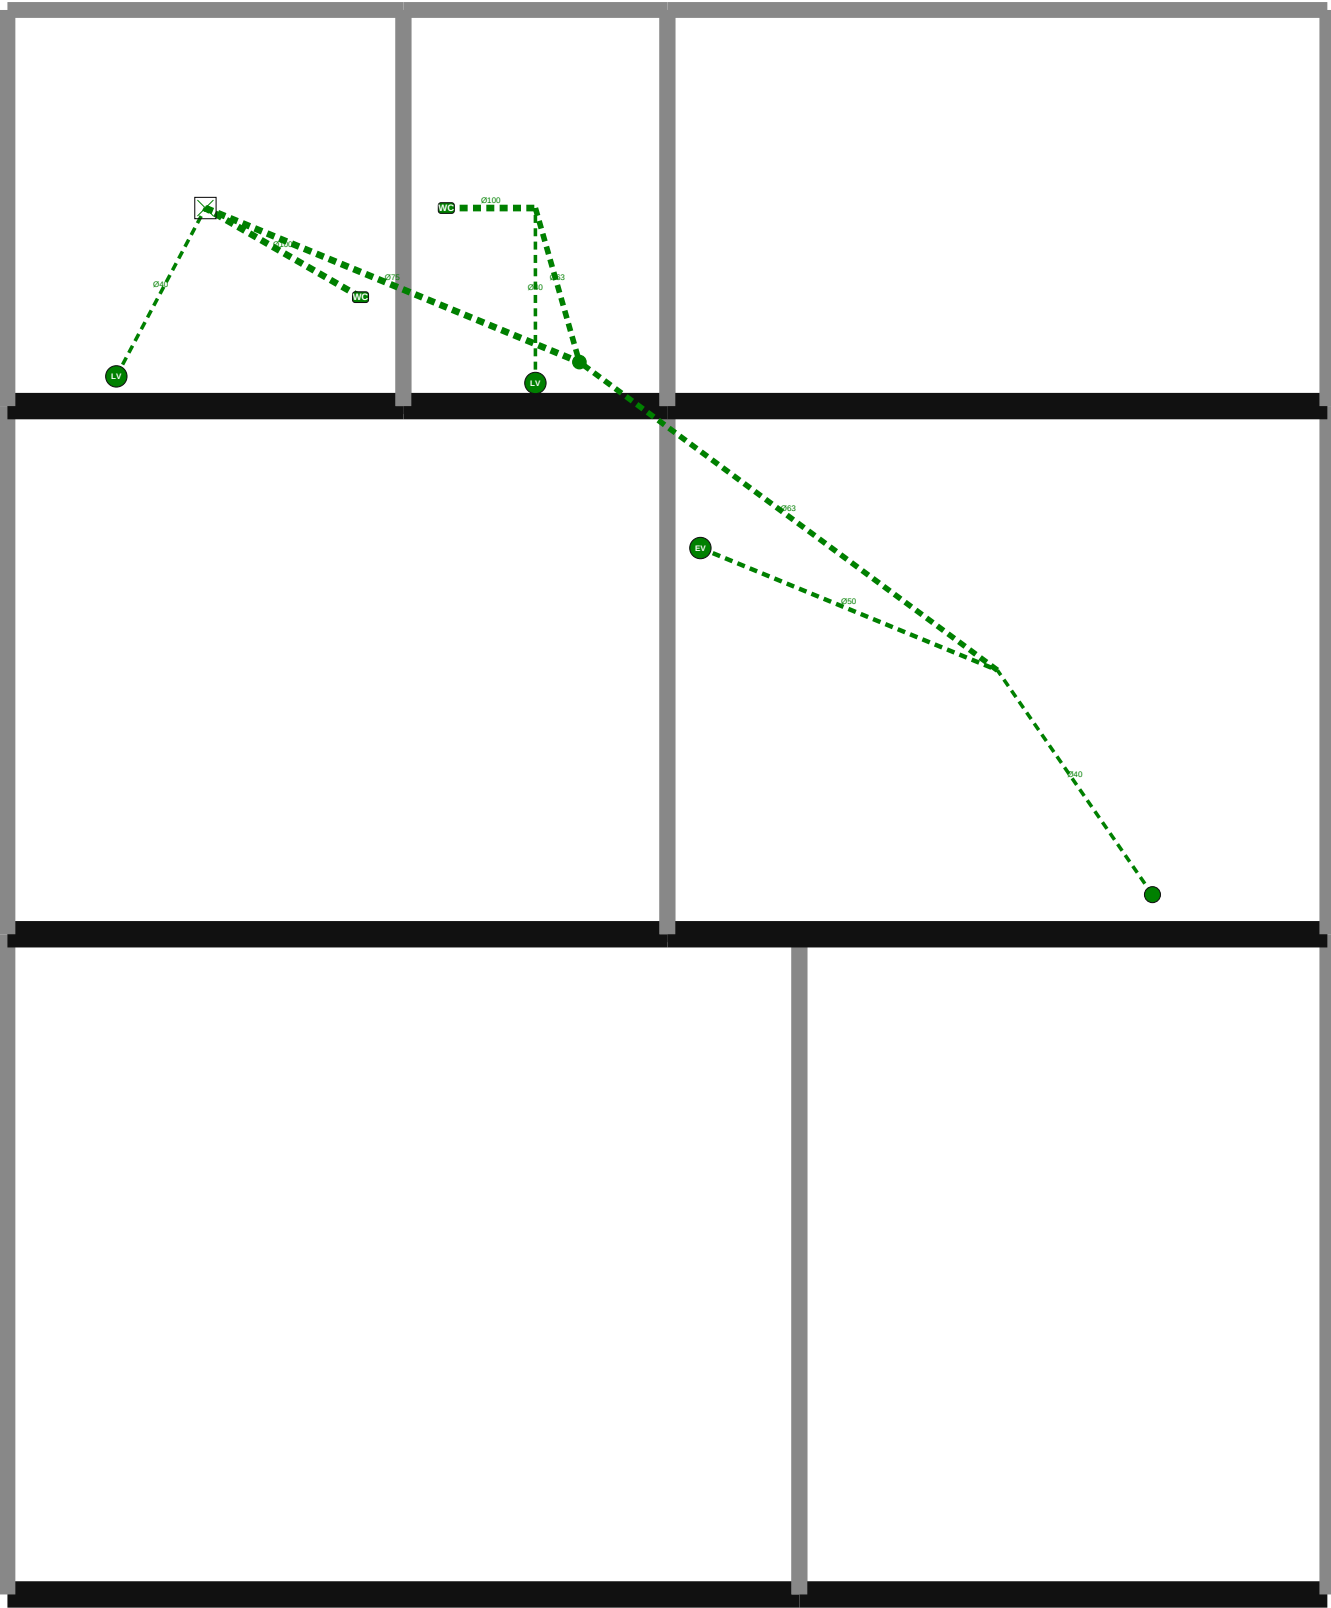

NOMENCLATURE — 410 PLU — Eaux Usées (EU)

- WC suspendu: 2
- Évier cuisine: 1
- Lave-vaisselle: 1
- Lavabo: 1
- Douche: 1
- Lave-mains: 1

TIJAN AI Bureau d'Études Automatisé	Résidence Papa Oumar Sakho Dakar, Sénégal	Éch: 1/100 Pl. 23/70
	410 PLU — Eaux Usées (EU) — R+2	
Date: 06/05/2026	Réf: 1711	BIM vPLU-023 Phase: APD

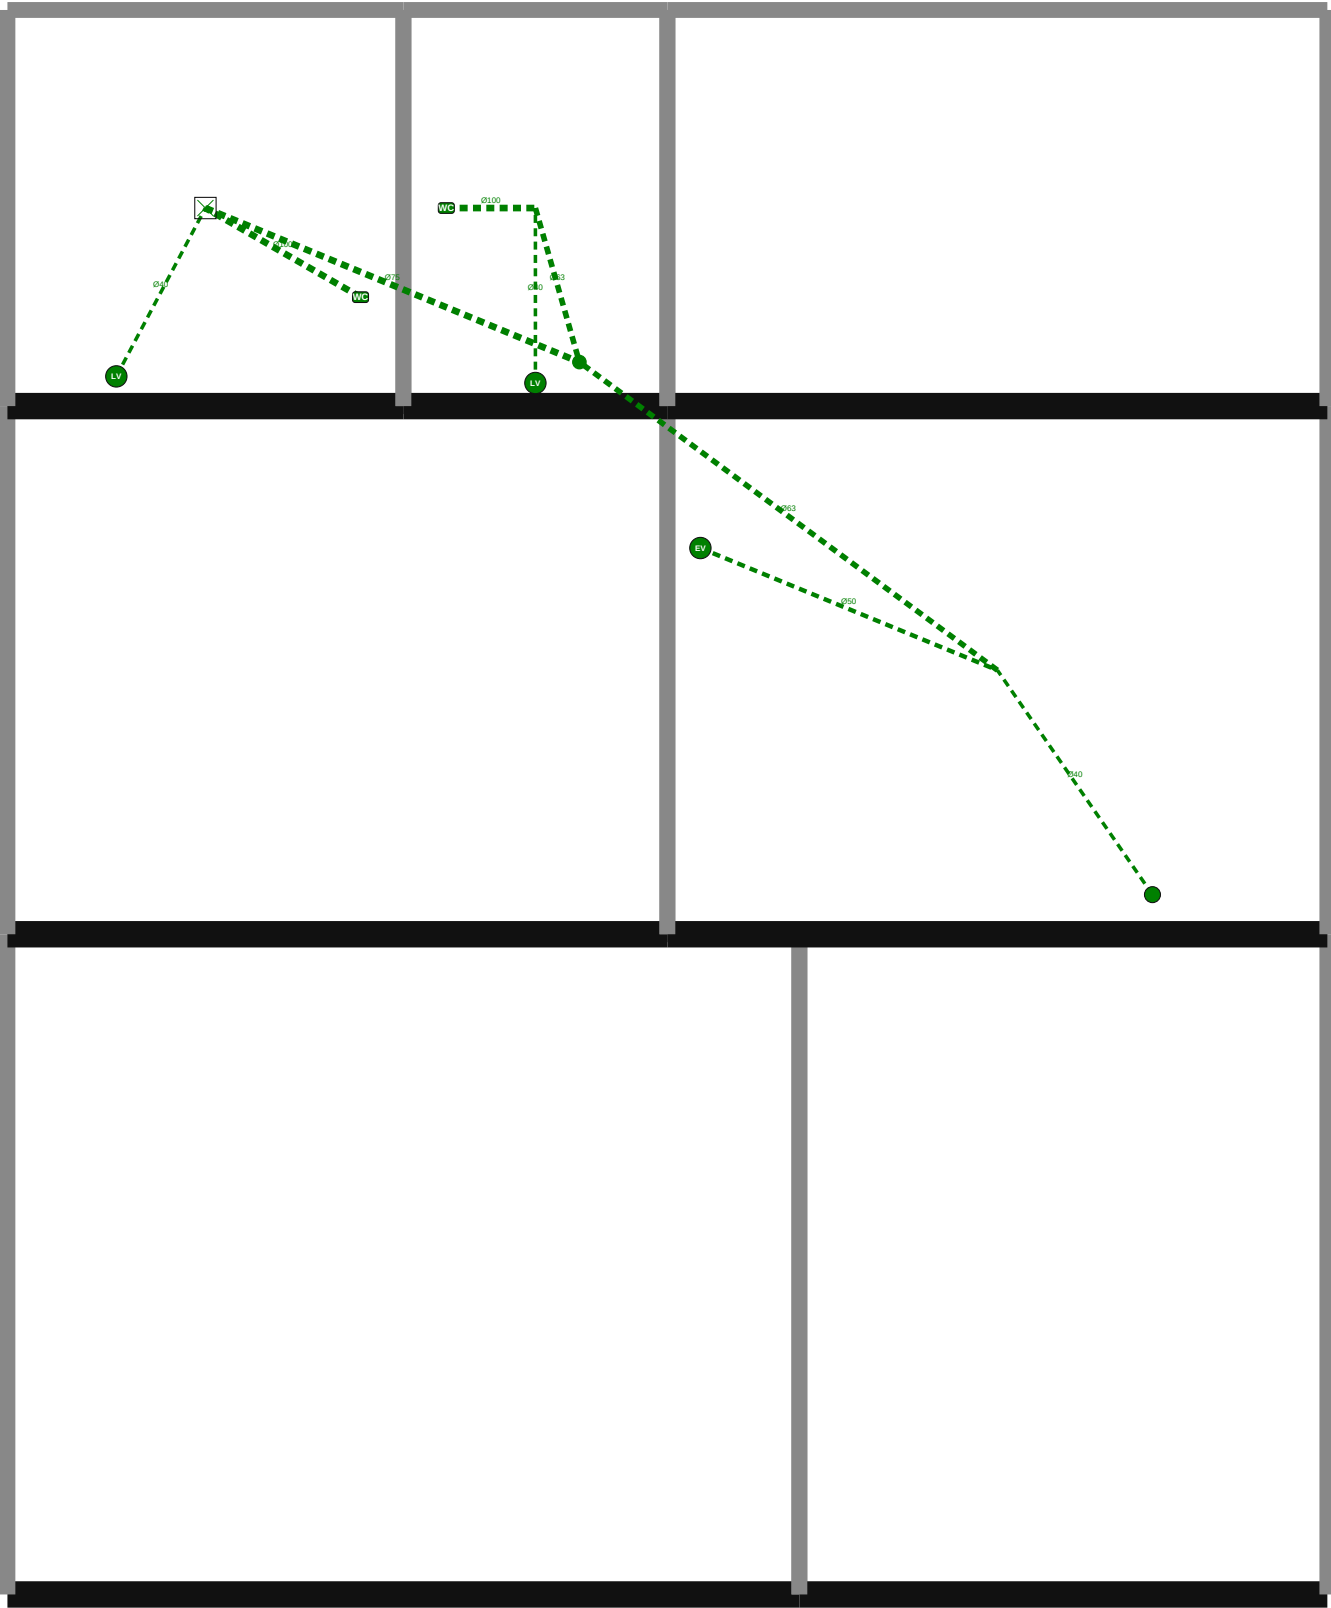


NOMENCLATURE — 410 PLU — Eaux Usées (EU)

- WC suspendu: 2
- Évier cuisine: 1
- Lave-vaisselle: 1
- Lavabo: 1
- Douche: 1
- Lave-mains: 1

TIJAN AI Bureau d'Études Automatisé	Résidence Papa Oumar Sakho Dakar, Sénégal	Éch: 1/100 Pl. 24/70
	410 PLU — Eaux Usées (EU) — R+3	
Date: 06/05/2026	Réf: 1711	BIM vPLU-024 Phase: APD


410 PLU — Eaux Usées (EU) — R+4

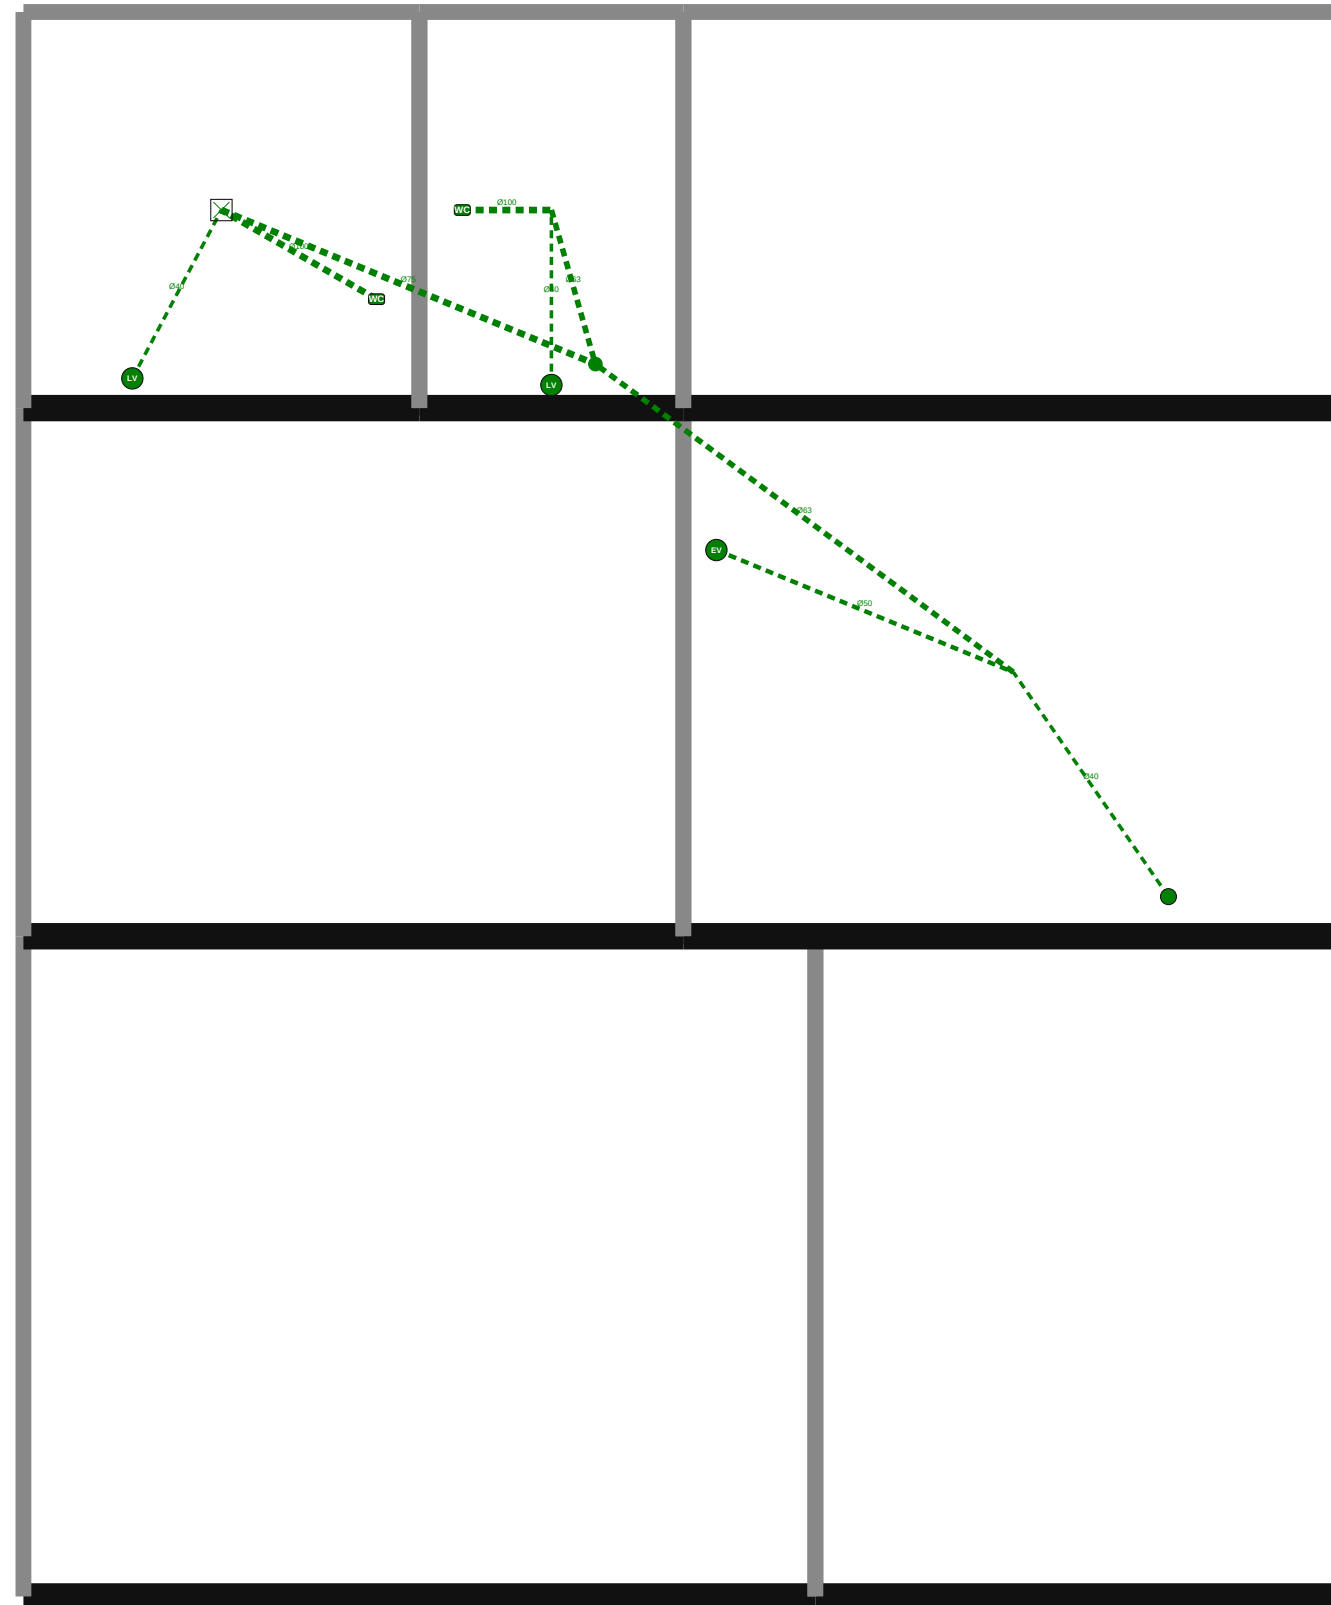

NOMENCLATURE — 410 PLU — Eaux Usées (EU)

- WC suspendu: 2
- Évier cuisine: 1
- Lave-vaisselle: 1
- Lavabo: 1
- Douche: 1
- Lave-mains: 1


TIJAN AI Bureau d'Études Automatisé	Résidence Papa Oumar Sakho Dakar, Sénégal	Éch: 1/100 Pl. 25/70
	410 PLU — Eaux Usées (EU) — R+4	
Date: 06/05/2026	Réf: 1711	BIM vPLU-025 Phase: APD

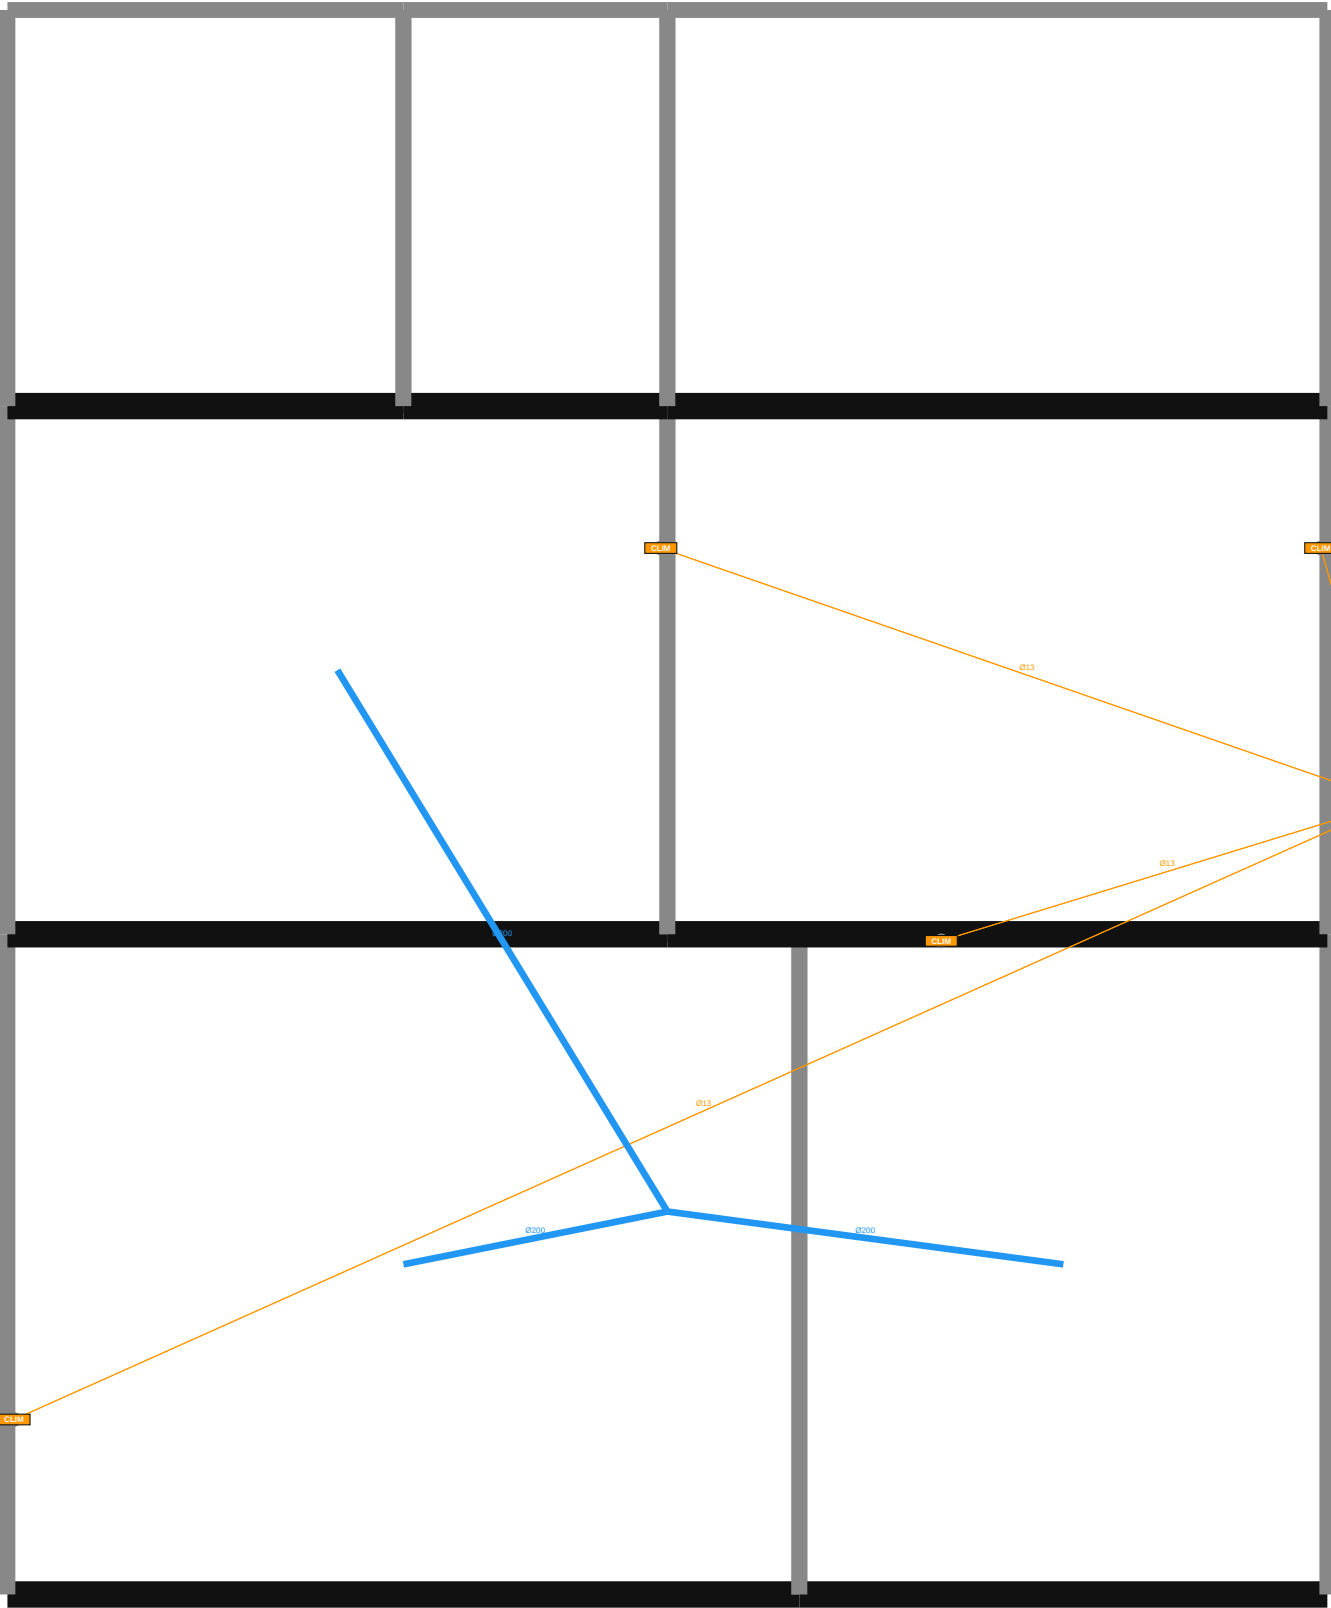

NOMENCLATURE — 413 HVC — Climatisation (CLIM)

• Split climatiseur: 4


TIJAN AI Bureau d'Études Automatisé	Résidence Papa Oumar Sakho Dakar, Sénégal	Éch: 1/100 Pl. 26/70
	413 HVC — Climatisation (CLIM) — RDC	
Date: 06/05/2026	Réf: 1711	BIM vHVC-026 Phase: APD

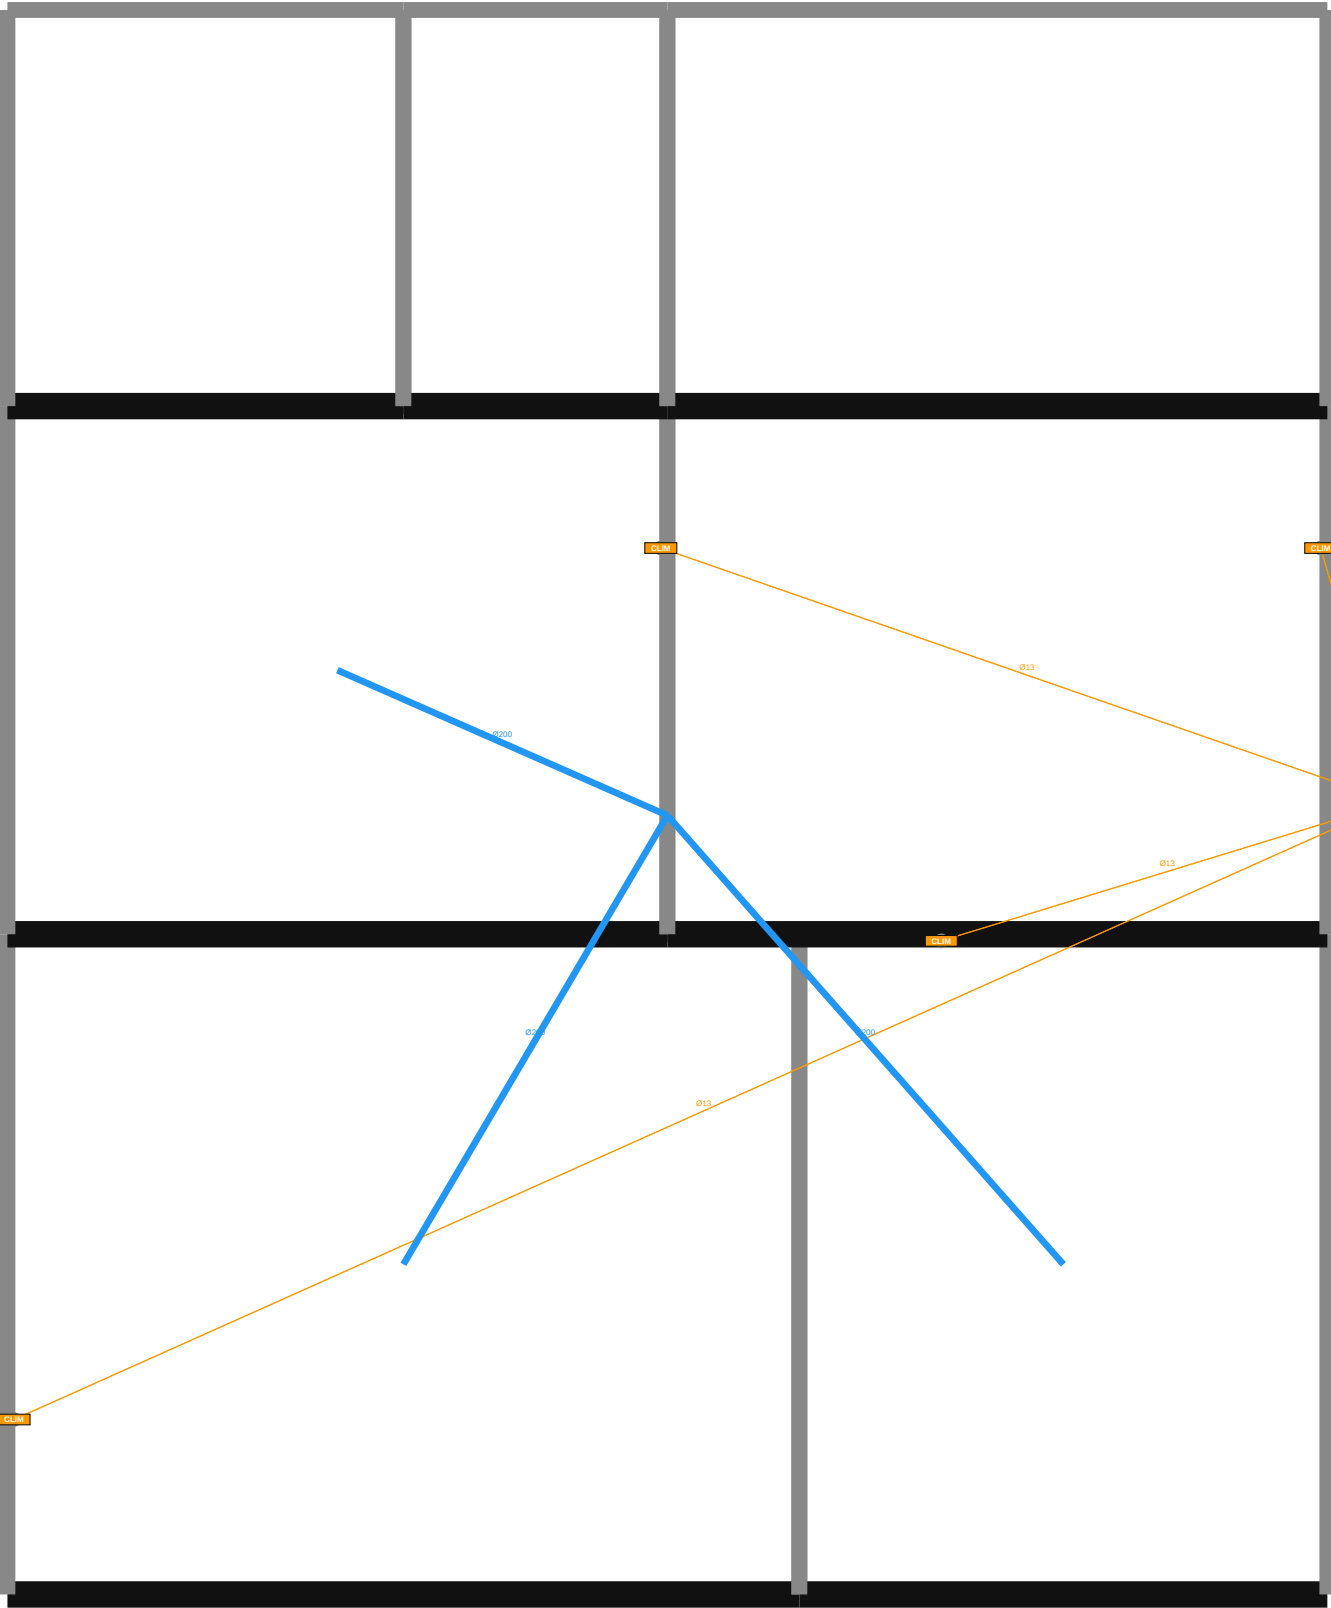

NOMENCLATURE — 413 HVC — Climatisation (CLIM)

• Split climatiseur: 4


TIJAN AI Bureau d'Études Automatisé	Résidence Papa Oumar Sakho Dakar, Sénégal	Éch: 1/100 Pl. 27/70
	413 HVC — Climatisation (CLIM) — R+1	
Date: 06/05/2026	Réf: 1711	BIM vHVC-027 Phase: APD

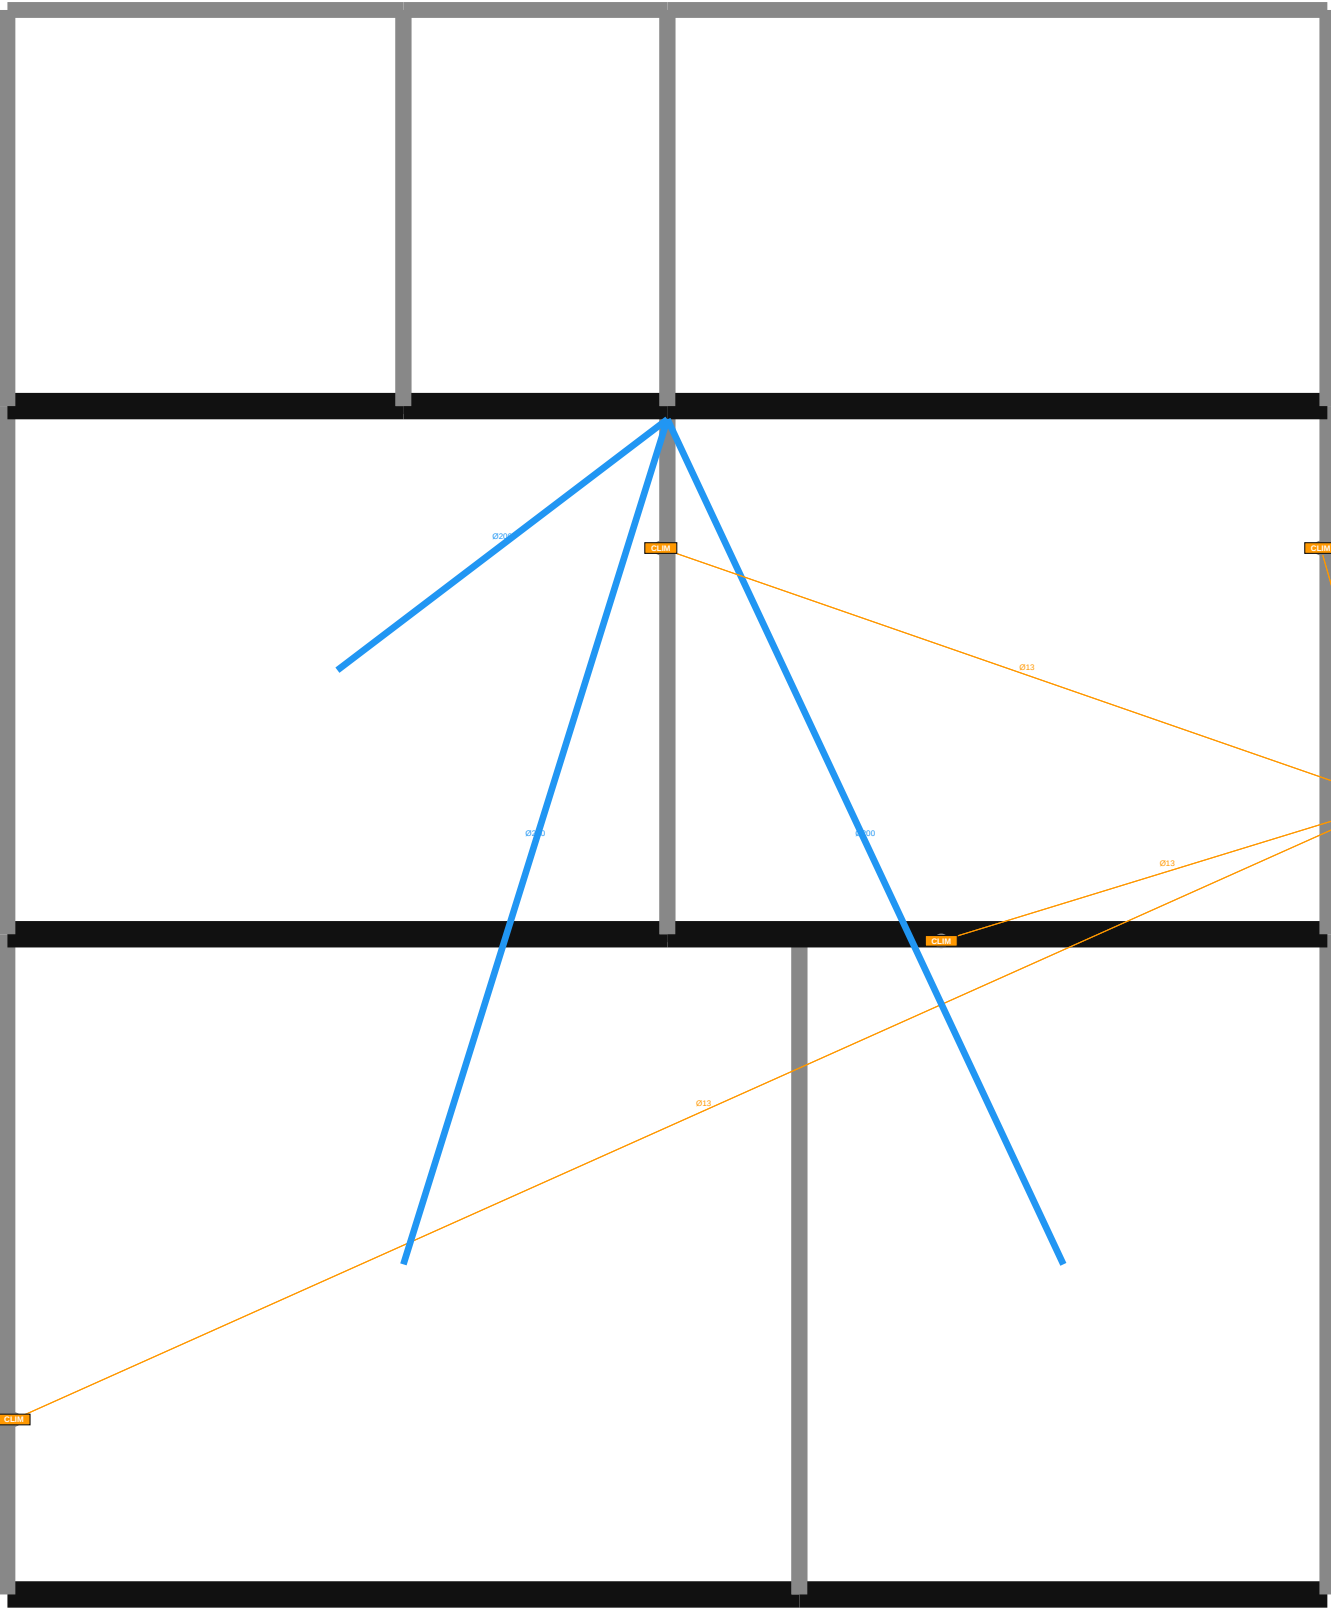

NOMENCLATURE — 413 HVC — Climatisation (CLIM)

• Split climatiseur: 4


TIJAN AI Bureau d'Études Automatisé	Résidence Papa Oumar Sakho Dakar, Sénégal	Éch: 1/100 Pl. 28/70
	413 HVC — Climatisation (CLIM) — R+2	
Date: 06/05/2026	Réf: 1711	BIM vHVC-028 Phase: APD

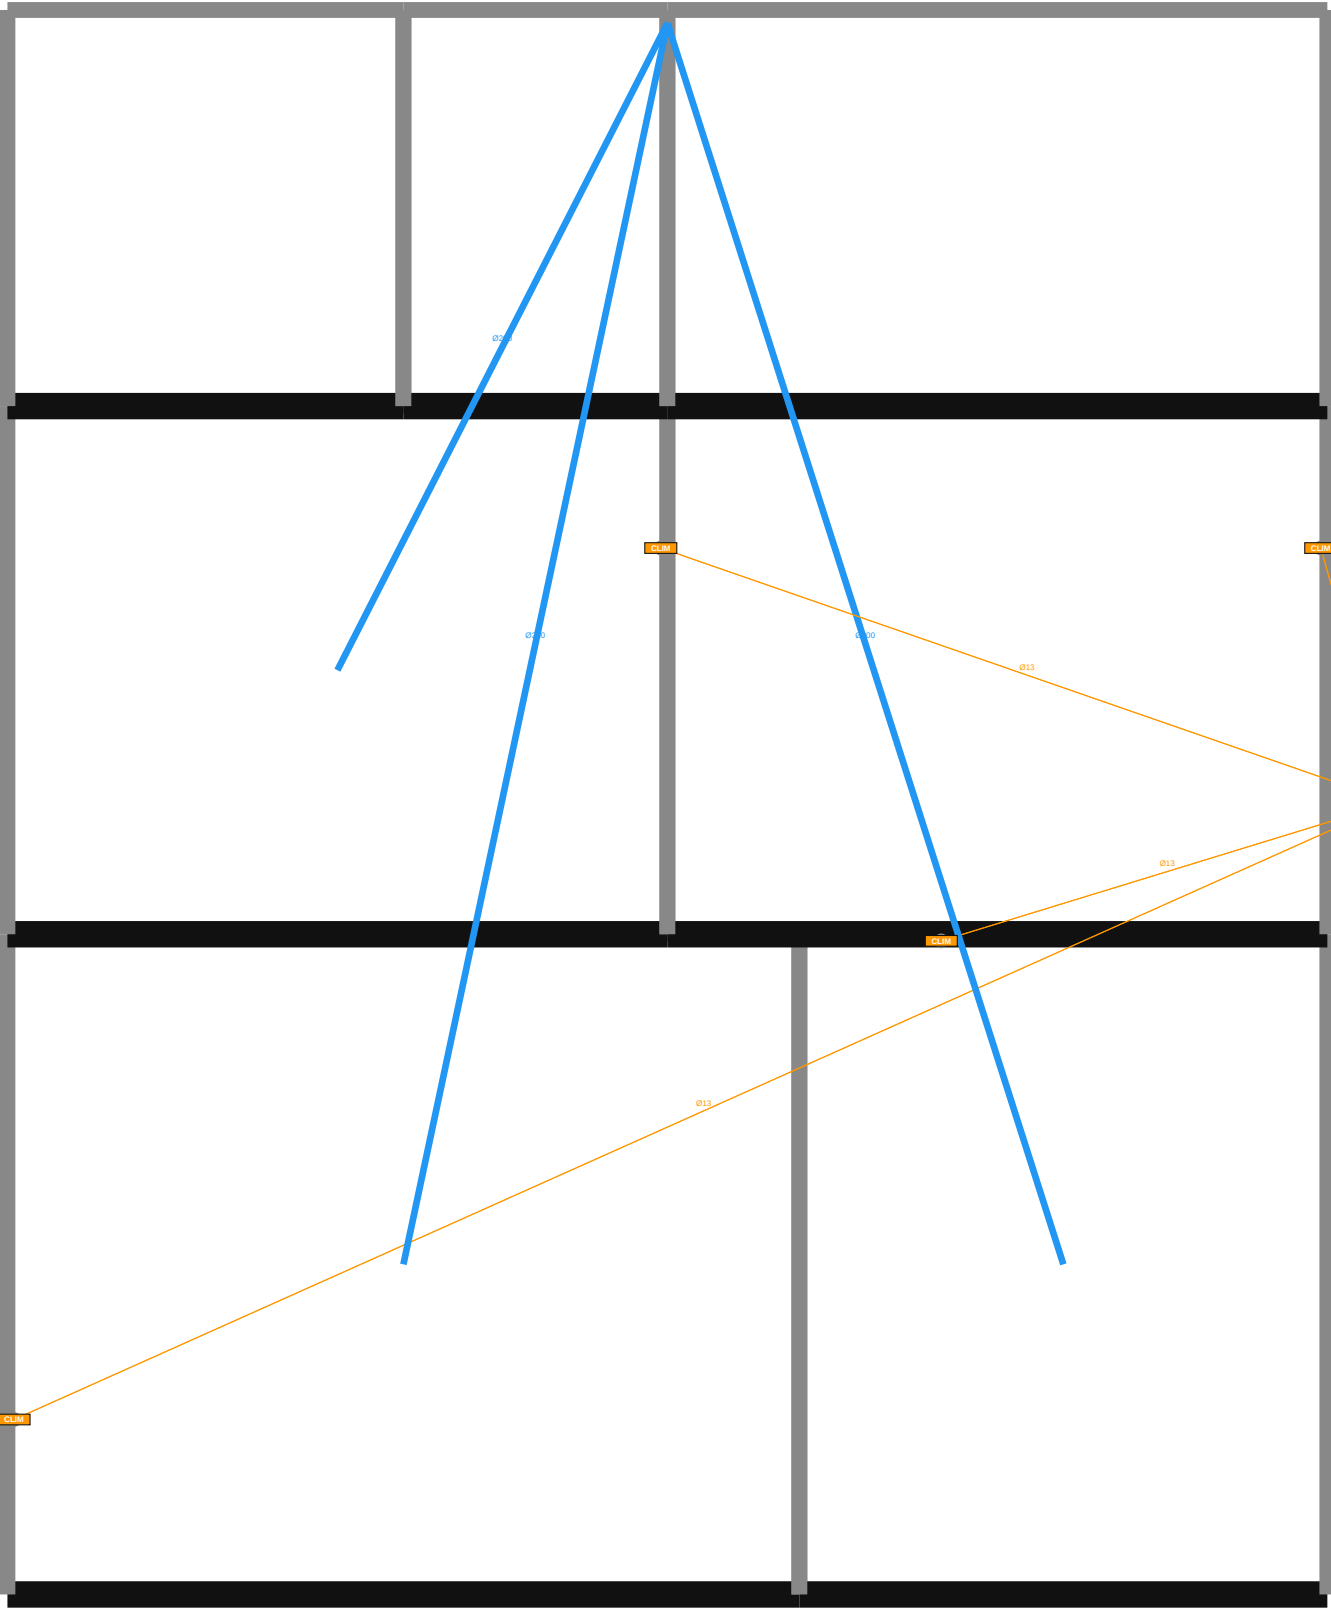

NOMENCLATURE — 413 HVC — Climatisation (CLIM)

• Split climatiseur: 4

TIJAN AI Bureau d'Études Automatisé	Résidence Papa Oumar Sakho Dakar, Sénégal	Éch: 1/100 Pl. 29/70
	413 HVC — Climatisation (CLIM) — R+3	
Date: 06/05/2026	Réf: 1711	BIM vHVC-029 Phase: APD

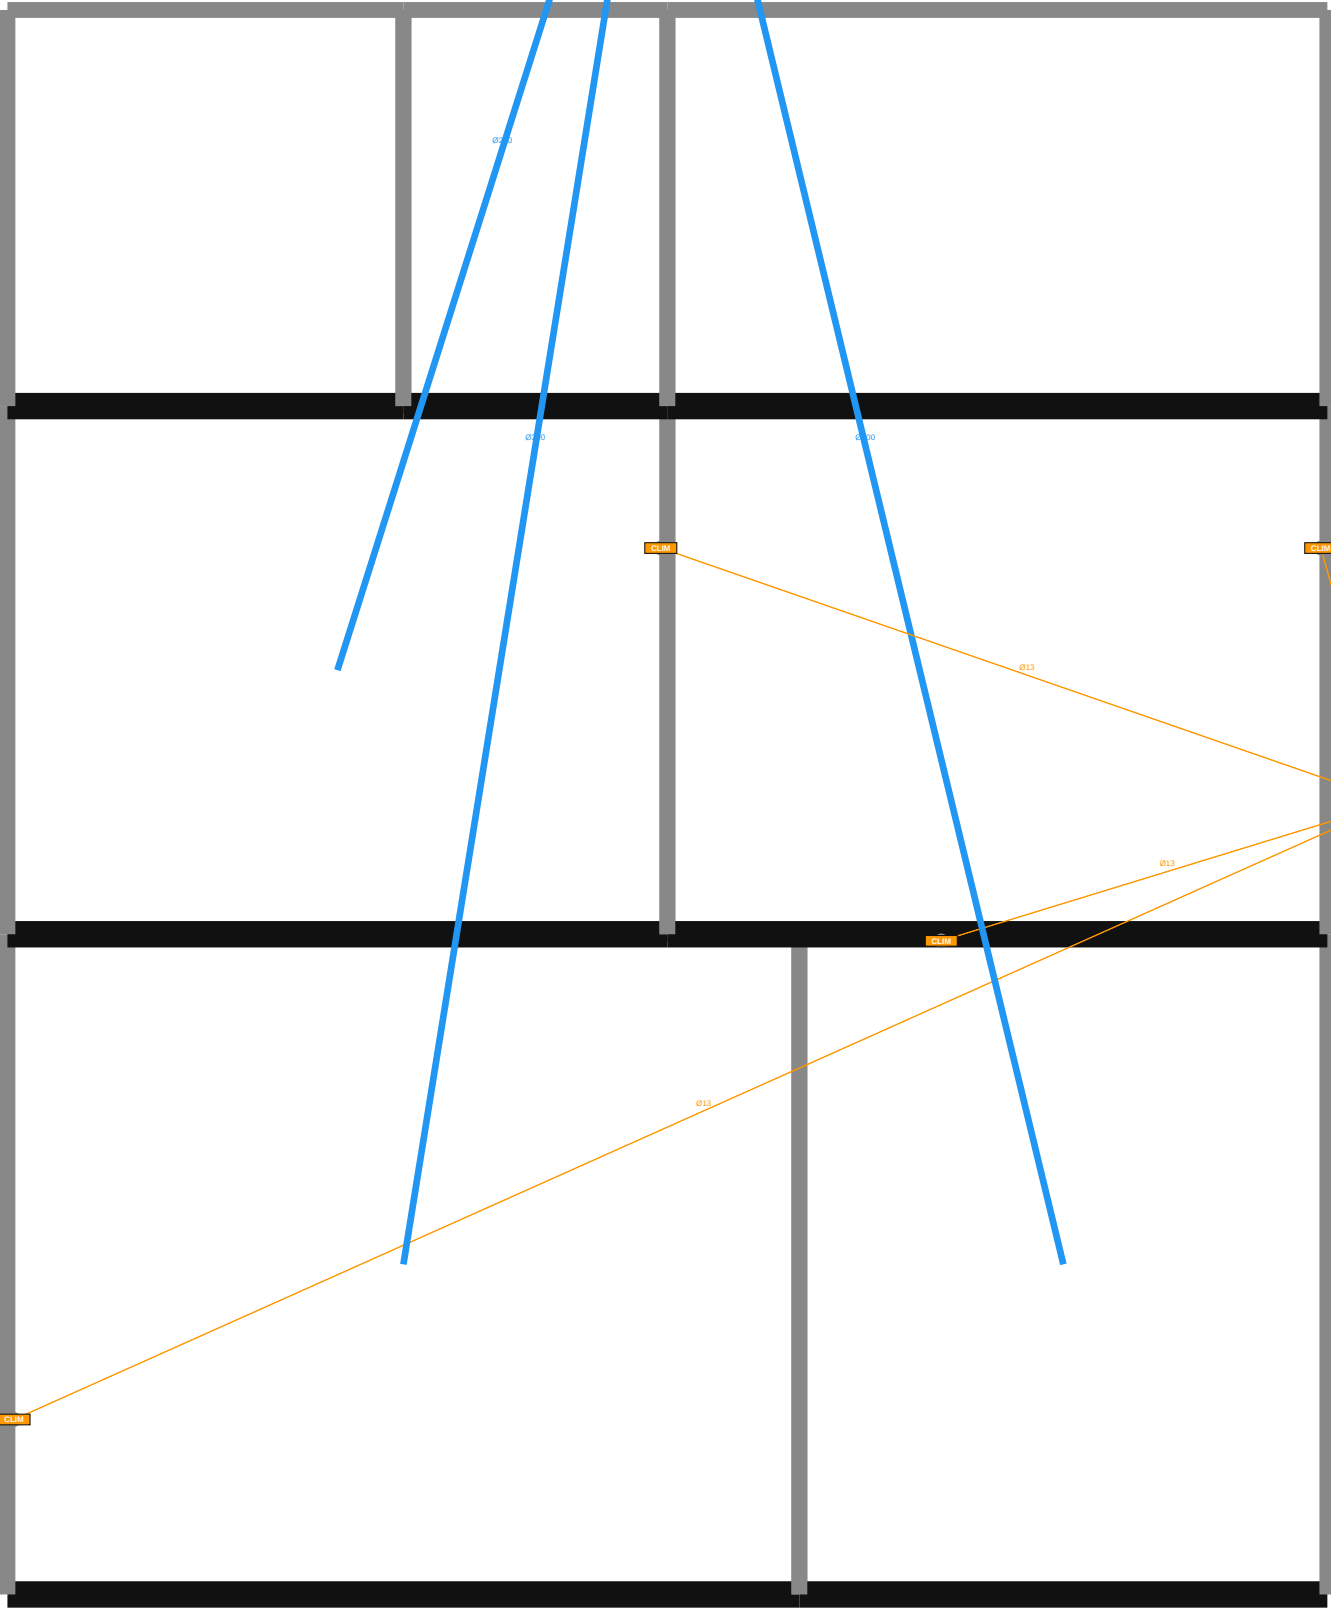

NOMENCLATURE — 413 HVC — Climatisation (CLIM)

• Split climatiseur: 4

TIJAN AI Bureau d'Études Automatisé	Résidence Papa Oumar Sakho Dakar, Sénégal	Éch: 1/100 Pl. 30/70
	413 HVC — Climatisation (CLIM) — R+4	
Date: 06/05/2026	Réf: 1711	BIM vHVC-030 Phase: APD



NOMENCLATURE — 413 HVC — Ventilation (VMC)

- Grille soufflage: 3
- Bouche VMC extraction: 3
- Hotte aspirante: 1

TIJAN AI Bureau d'Études Automatisé	Résidence Papa Oumar Sakho Dakar, Sénégal	Éch: 1/100 Pl. 31/70
	413 HVC — Ventilation (VMC) — RDC	
Date: 06/05/2026	Réf: 1711	BIM vHVC-031 Phase: APD



NOMENCLATURE — 413 HVC — Ventilation (VMC)

- Grille soufflage: 3
- Bouche VMC extraction: 3
- Hotte aspirante: 1

TIJAN AI Bureau d'Études Automatisé	Résidence Papa Oumar Sakho Dakar, Sénégal	Éch: 1/100 Pl. 32/70
	413 HVC — Ventilation (VMC) — R+1	
Date: 06/05/2026	Réf: 1711	BIM vHVC-032 Phase: APD



NOMENCLATURE — 413 HVC — Ventilation (VMC)

- Grille soufflage: 3
- Bouche VMC extraction: 3
- Hotte aspirante: 1

TIJAN AI Bureau d'Études Automatisé	Résidence Papa Oumar Sakho Dakar, Sénégal	Éch: 1/100 Pl. 33/70
	413 HVC — Ventilation (VMC) — R+2	
Date: 06/05/2026	Réf: 1711	BIM vHVC-033 Phase: APD



NOMENCLATURE — 413 HVC — Ventilation (VMC)

- Grille soufflage: 3
- Bouche VMC extraction: 3
- Hotte aspirante: 1


TIJAN AI Bureau d'Études Automatisé	Résidence Papa Oumar Sakho Dakar, Sénégal	Éch: 1/100 Pl. 34/70
	413 HVC — Ventilation (VMC) — R+3	
Date: 06/05/2026	Réf: 1711	BIM vHVC-034 Phase: APD



NOMENCLATURE — 413 HVC — Ventilation (VMC)

- Grille soufflage: 3
- Bouche VMC extraction: 3
- Hotte aspirante: 1


TIJAN AI Bureau d'Études Automatisé	Résidence Papa Oumar Sakho Dakar, Sénégal	Éch: 1/100 Pl. 35/70
	413 HVC — Ventilation (VMC) — R+4	
Date: 06/05/2026	Réf: 1711	BIM vHVC-035 Phase: APD

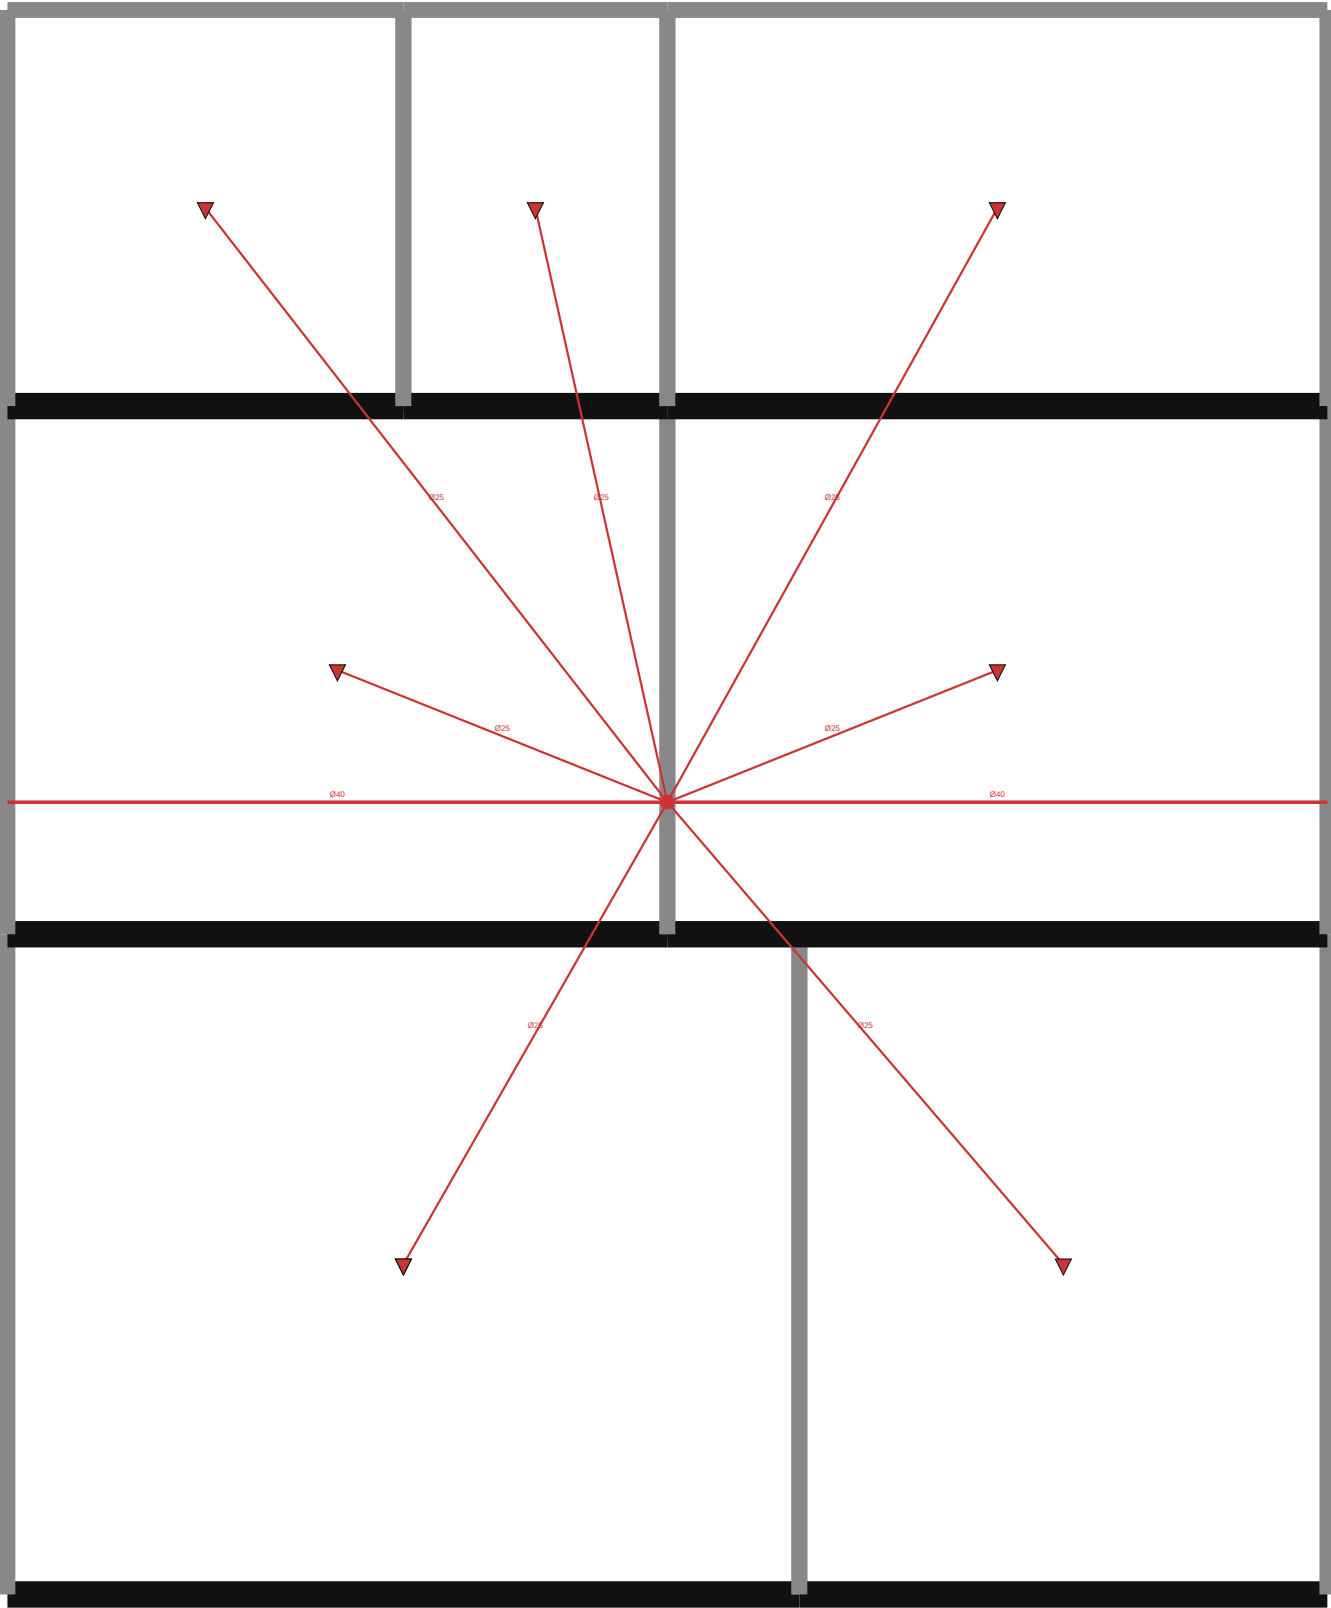

NOMENCLATURE — 400 FIF — Extinction (SPK)

• Sprinkler: 8


TIJAN AI Bureau d'Études Automatisé	Résidence Papa Oumar Sakho Dakar, Sénégal	Éch: 1/100 Pl. 36/70
	400 FIF — Extinction (SPK) — RDC	
Date: 06/05/2026	Réf: 1711	BIM vFIF-036 Phase: APD

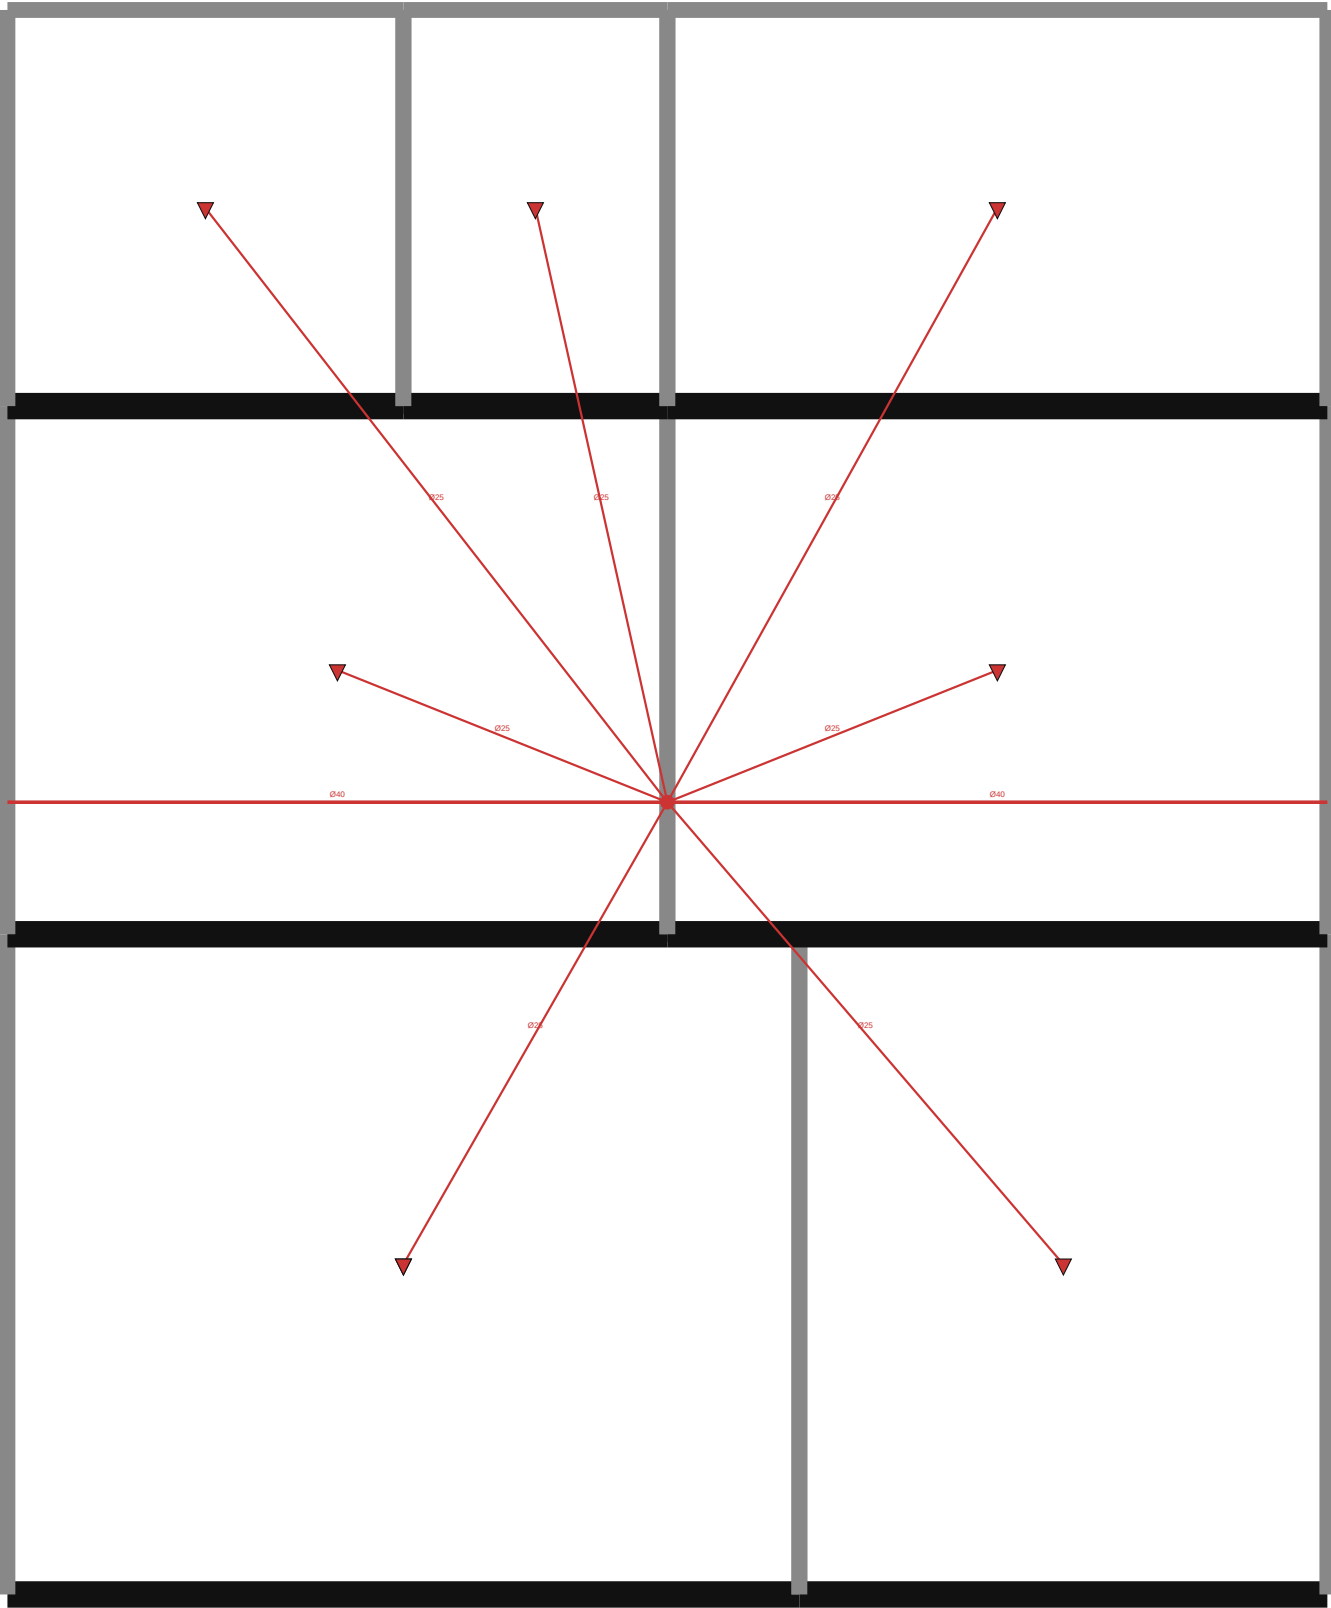

NOMENCLATURE — 400 FIF — Extinction (SPK)

• Sprinkler: 8


TIJAN AI Bureau d'Études Automatisé	Résidence Papa Oumar Sakho Dakar, Sénégal	Éch: 1/100 Pl. 37/70
	400 FIF — Extinction (SPK) — R+1	
Date: 06/05/2026	Réf: 1711	BIM VFIF-037 Phase: APD

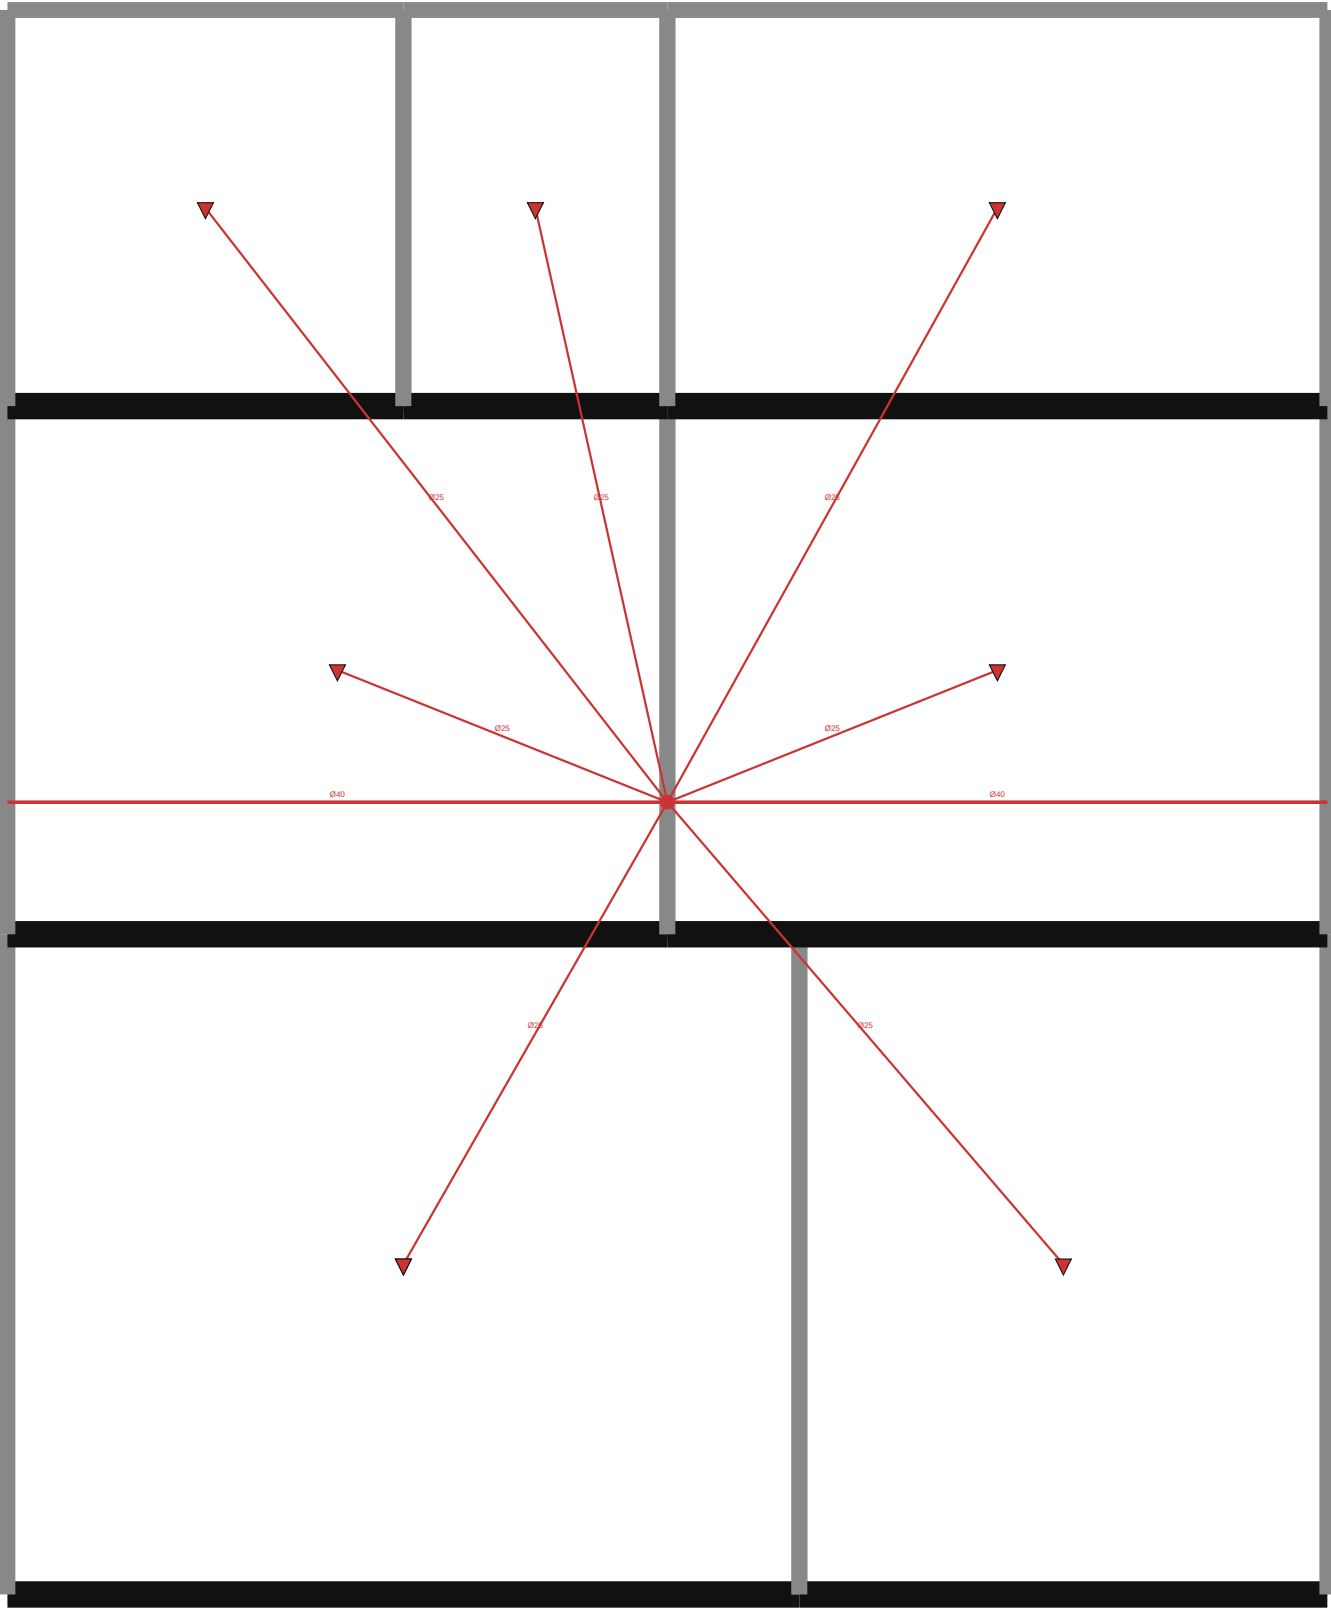

NOMENCLATURE — 400 FIF — Extinction (SPK)

• Sprinkler: 8


TIJAN AI Bureau d'Études Automatisé	Résidence Papa Oumar Sakho Dakar, Sénégal	Éch: 1/100 Pl. 38/70
	400 FIF — Extinction (SPK) — R+2	
Date: 06/05/2026	Réf: 1711	BIM vFIF-038 Phase: APD

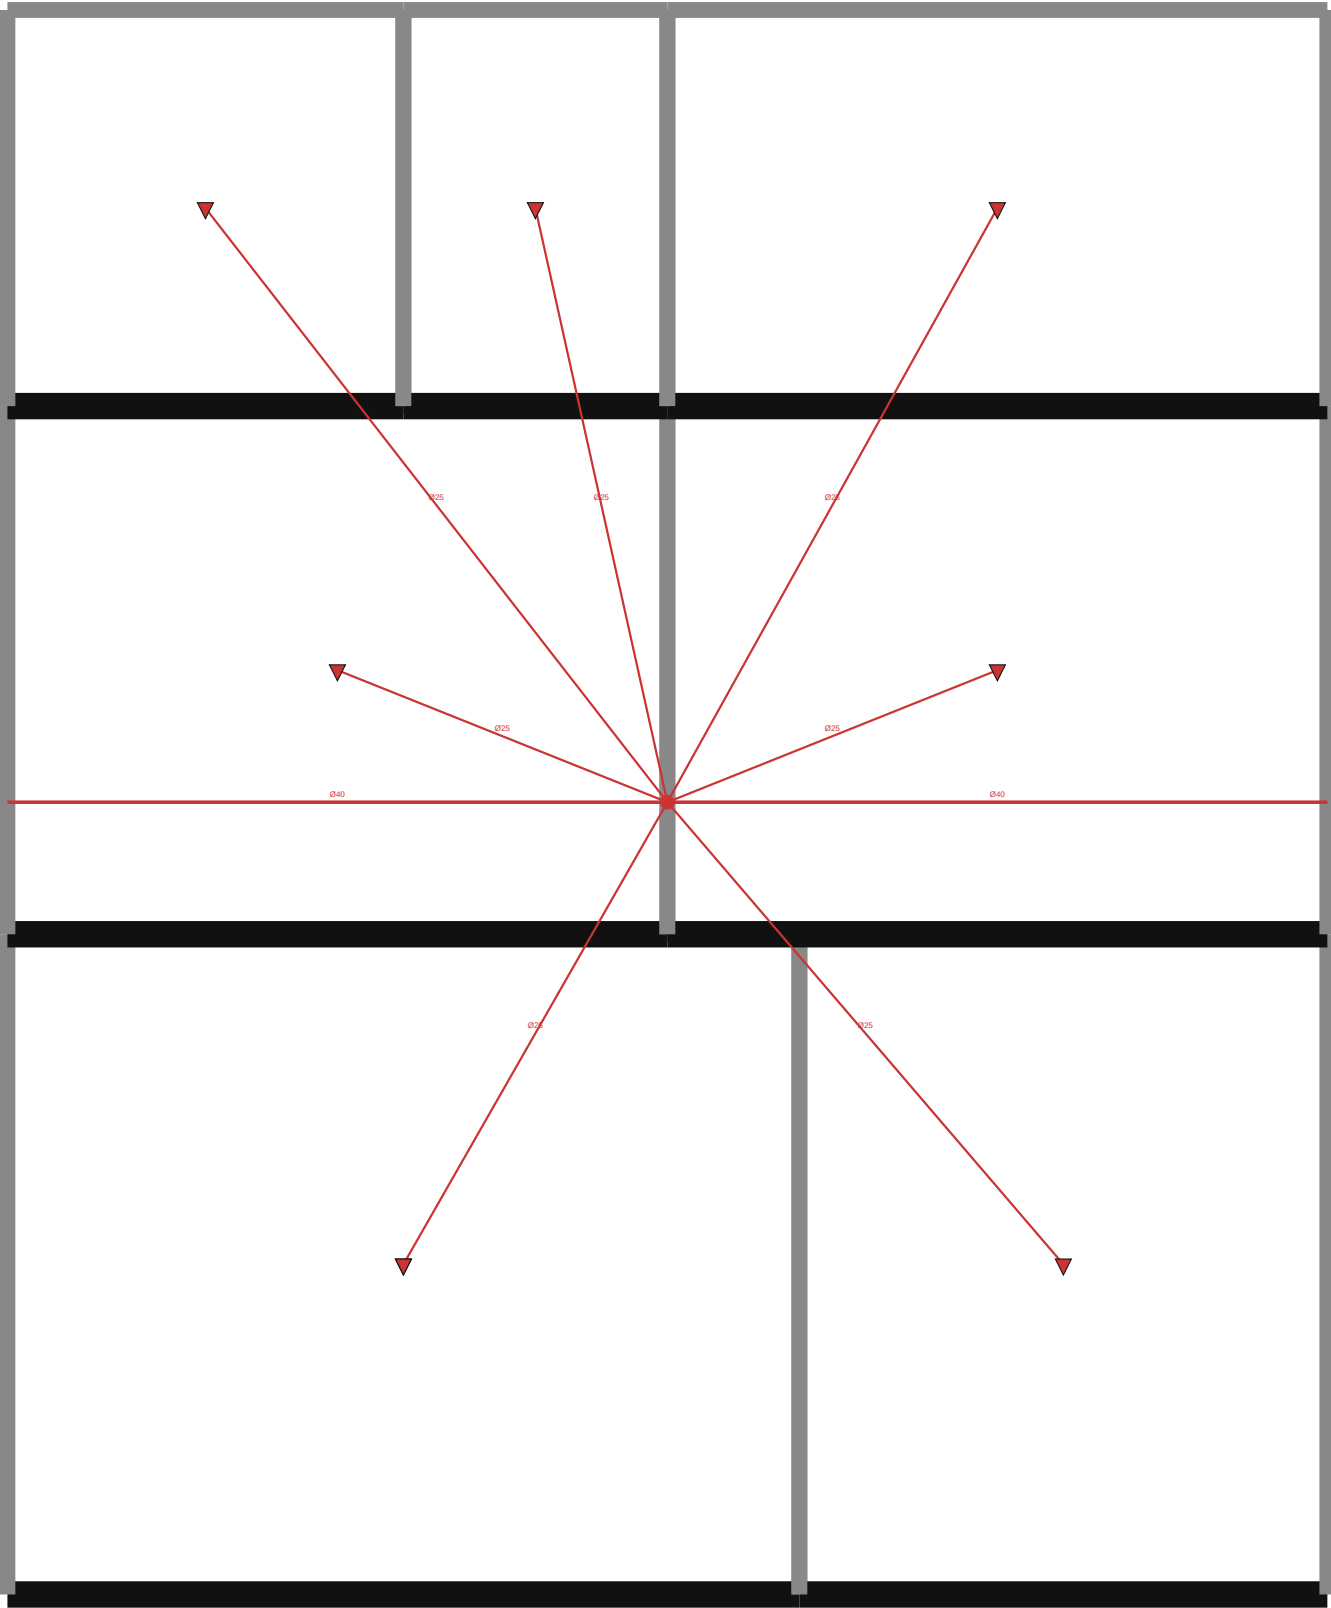

NOMENCLATURE — 400 FIF — Extinction (SPK)

• Sprinkler: 8

TIJAN AI Bureau d'Études Automatisé	Résidence Papa Oumar Sakho Dakar, Sénégal	Éch: 1/100 Pl. 39/70
	400 FIF — Extinction (SPK) — R+3	
Date: 06/05/2026	Réf: 1711	BIM vFIF-039 Phase: APD

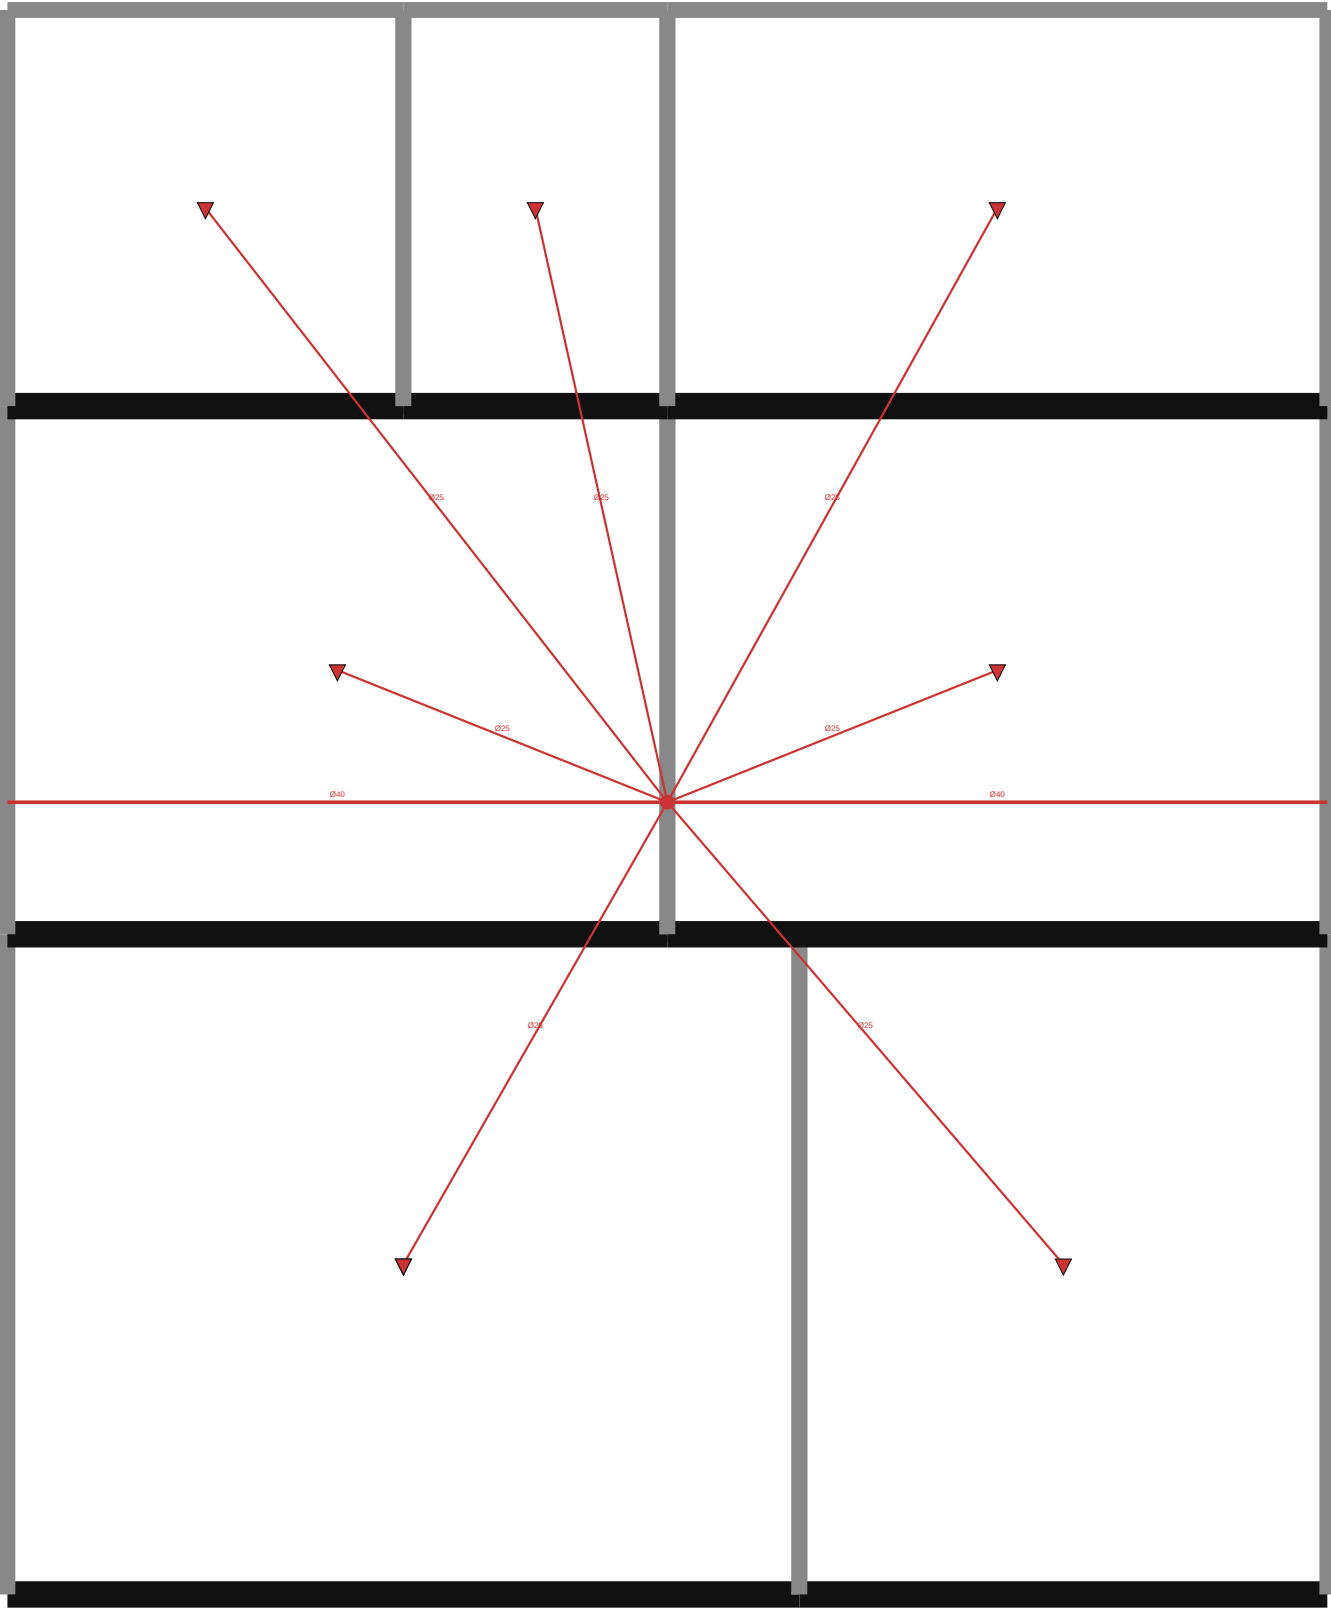


NOMENCLATURE — 400 FIF — Extinction (SPK)

• Sprinkler: 8

TIJAN AI Bureau d'Études Automatisé	Résidence Papa Oumar Sakho Dakar, Sénégal	Éch: 1/100 Pl. 40/70
	400 FIF — Extinction (SPK) — R+4	
Date: 06/05/2026	Réf: 1711	BIM vFIF-040 Phase: APD


400 FIF — Détection (DET) — RDC

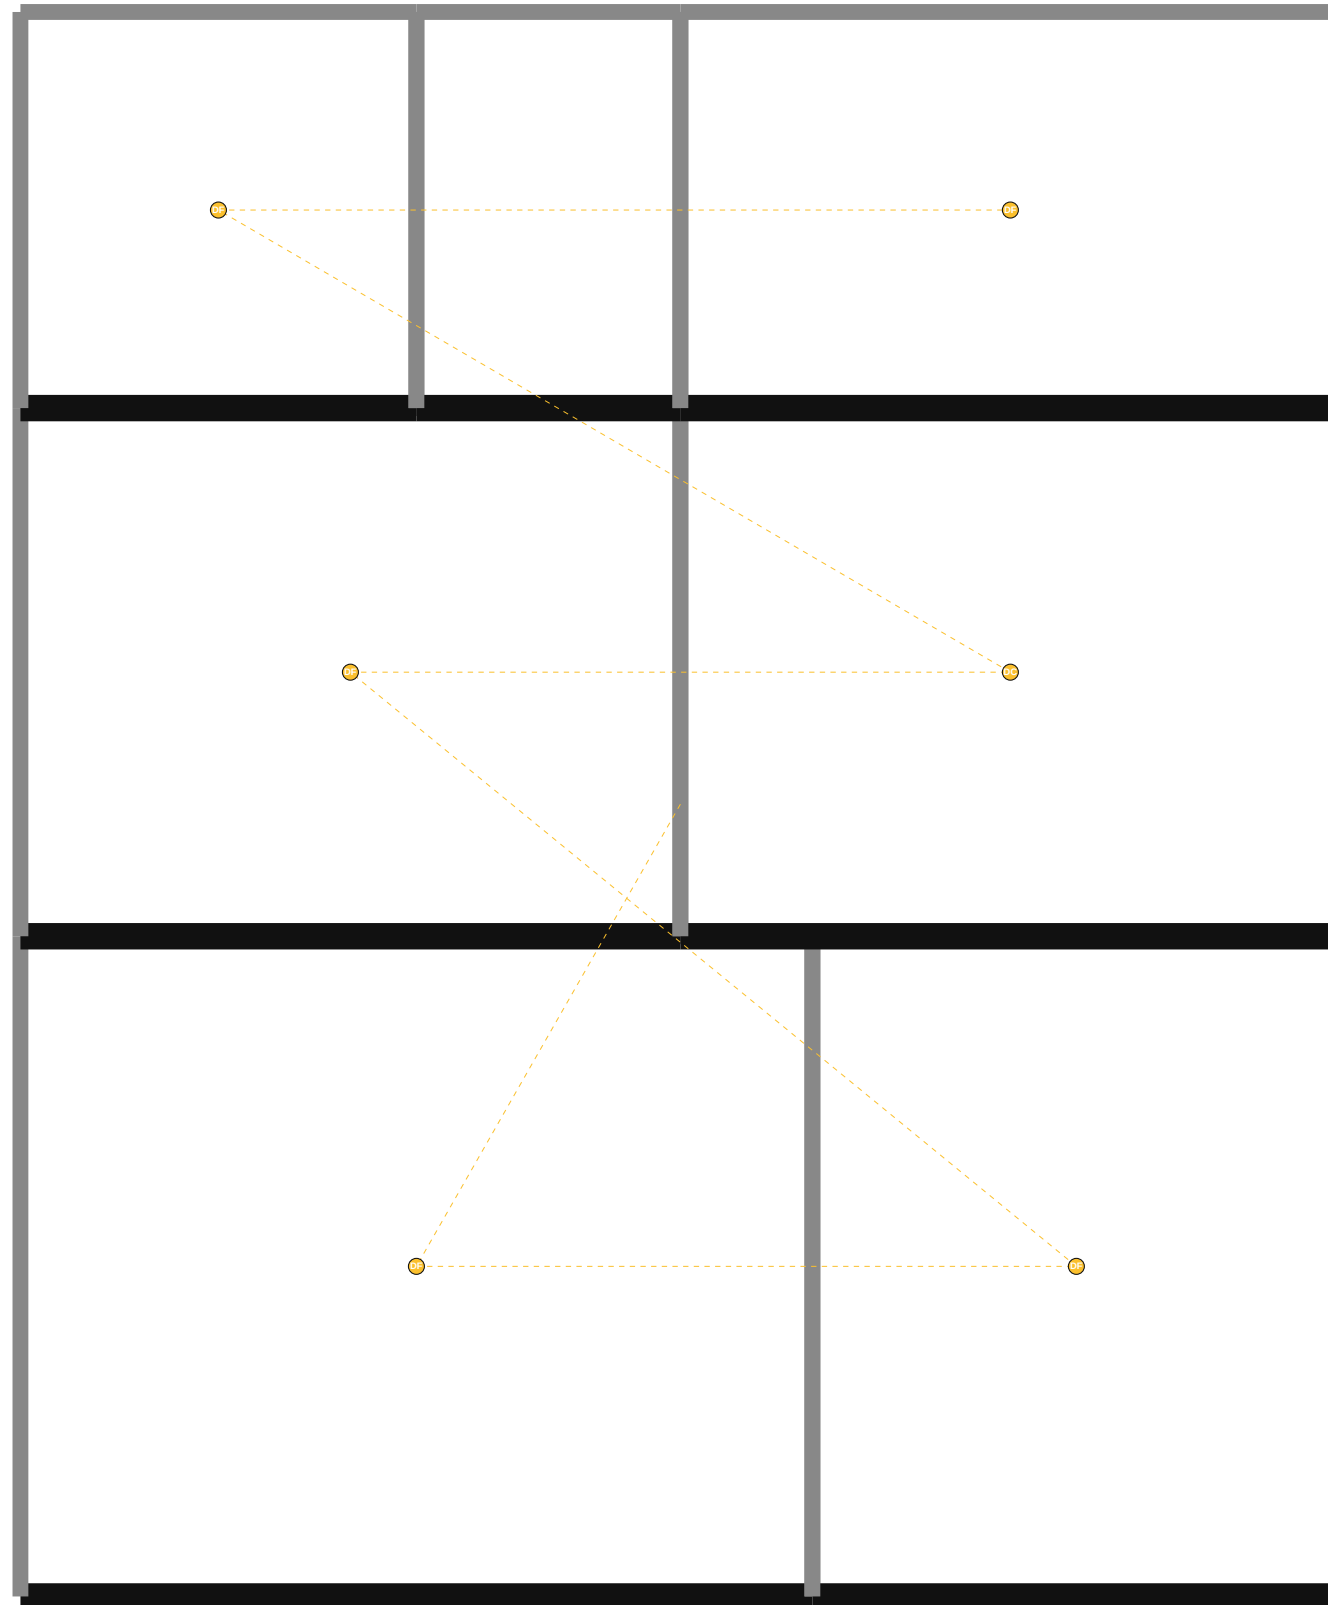

NOMENCLATURE — 400 FIF — Détection (DET)

- Détecteur de fumée: 5
- Détecteur de chaleur: 1


TIJAN AI Bureau d'Études Automatisé	Résidence Papa Oumar Sakho Dakar, Sénégal	Éch: 1/100 Pl. 41/70
	400 FIF — Détection (DET) — RDC	
Date: 06/05/2026	Réf: 1711	BIM vFIF-041 Phase: APD

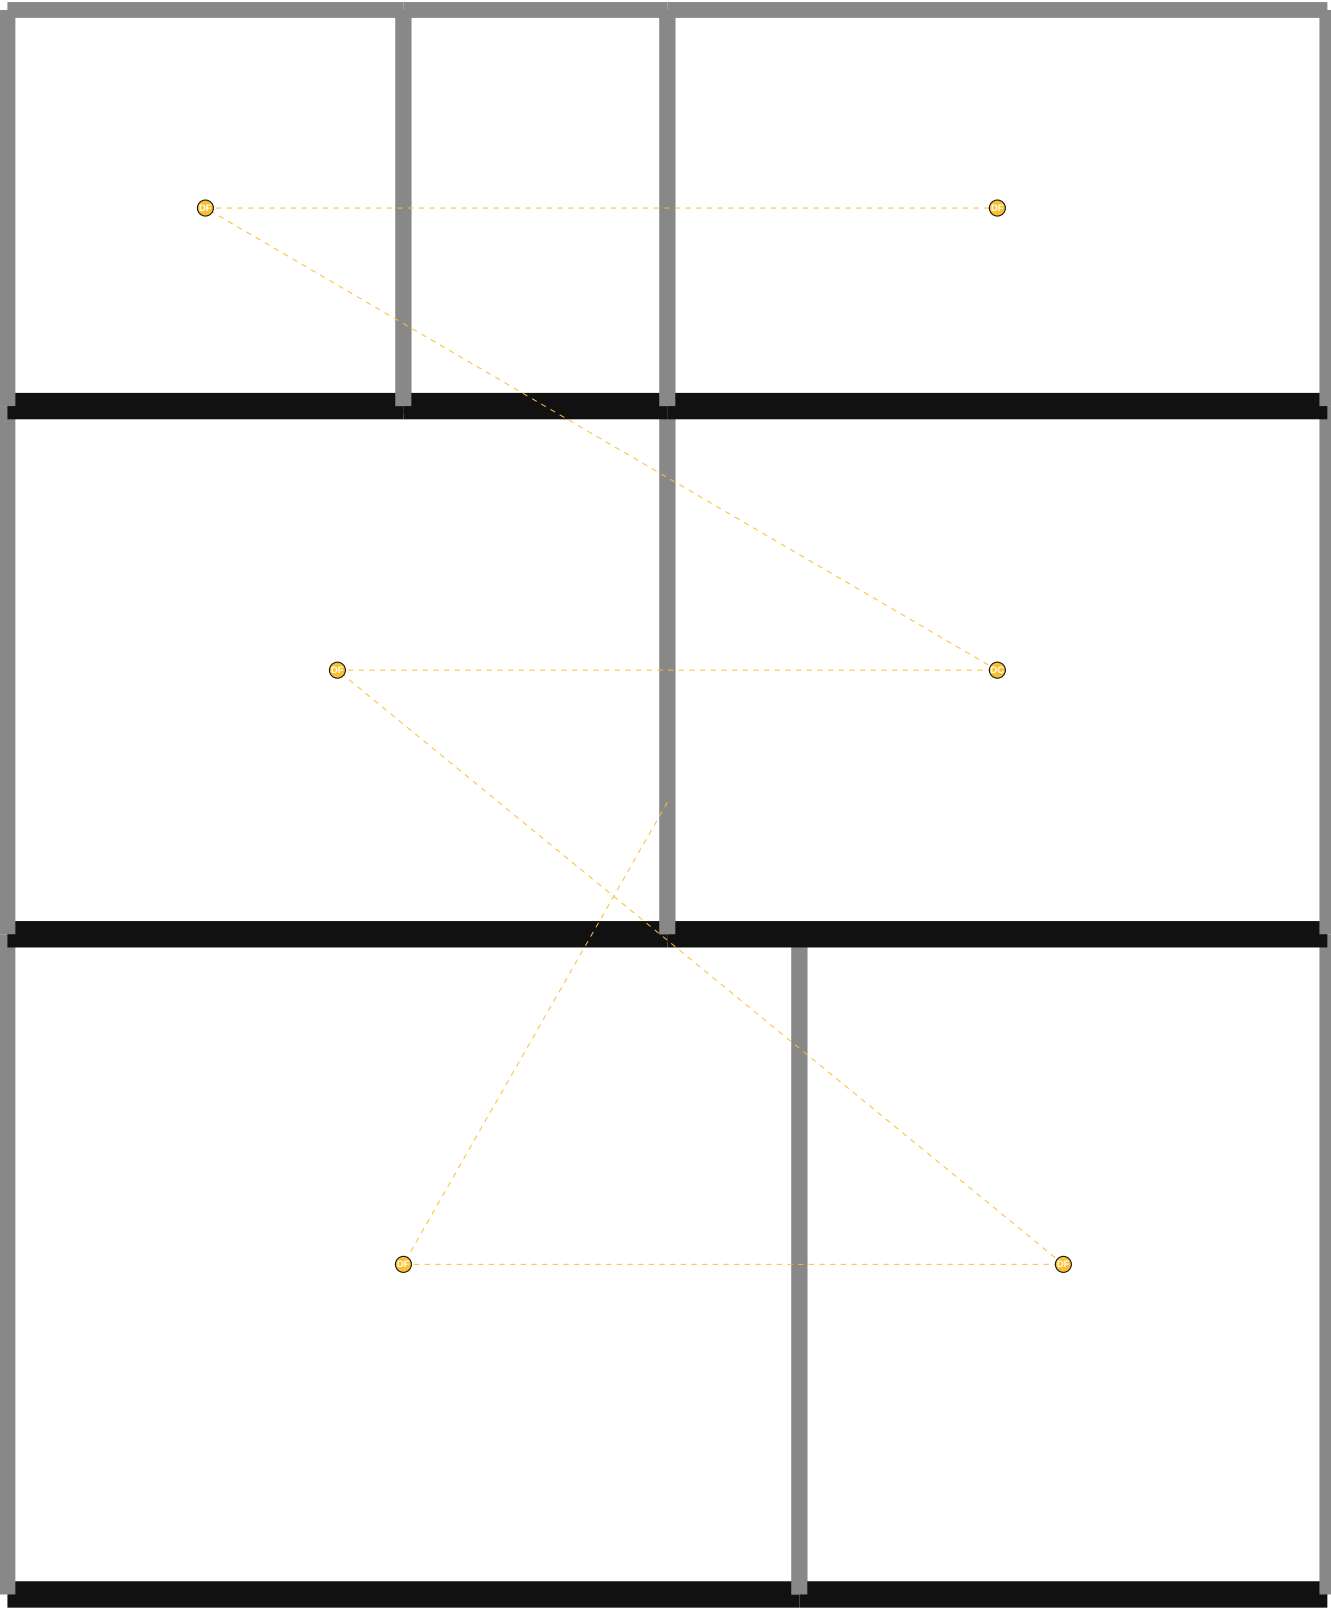

NOMENCLATURE — 400 FIF — Détection (DET)

- Détecteur de fumée: 5
- Détecteur de chaleur: 1


TIJAN AI Bureau d'Études Automatisé	Résidence Papa Oumar Sakho Dakar, Sénégal	Éch: 1/100 Pl. 42/70
	400 FIF — Détection (DET) — R+1	
Date: 06/05/2026	Réf: 1711	BIM vFIF-042 Phase: APD

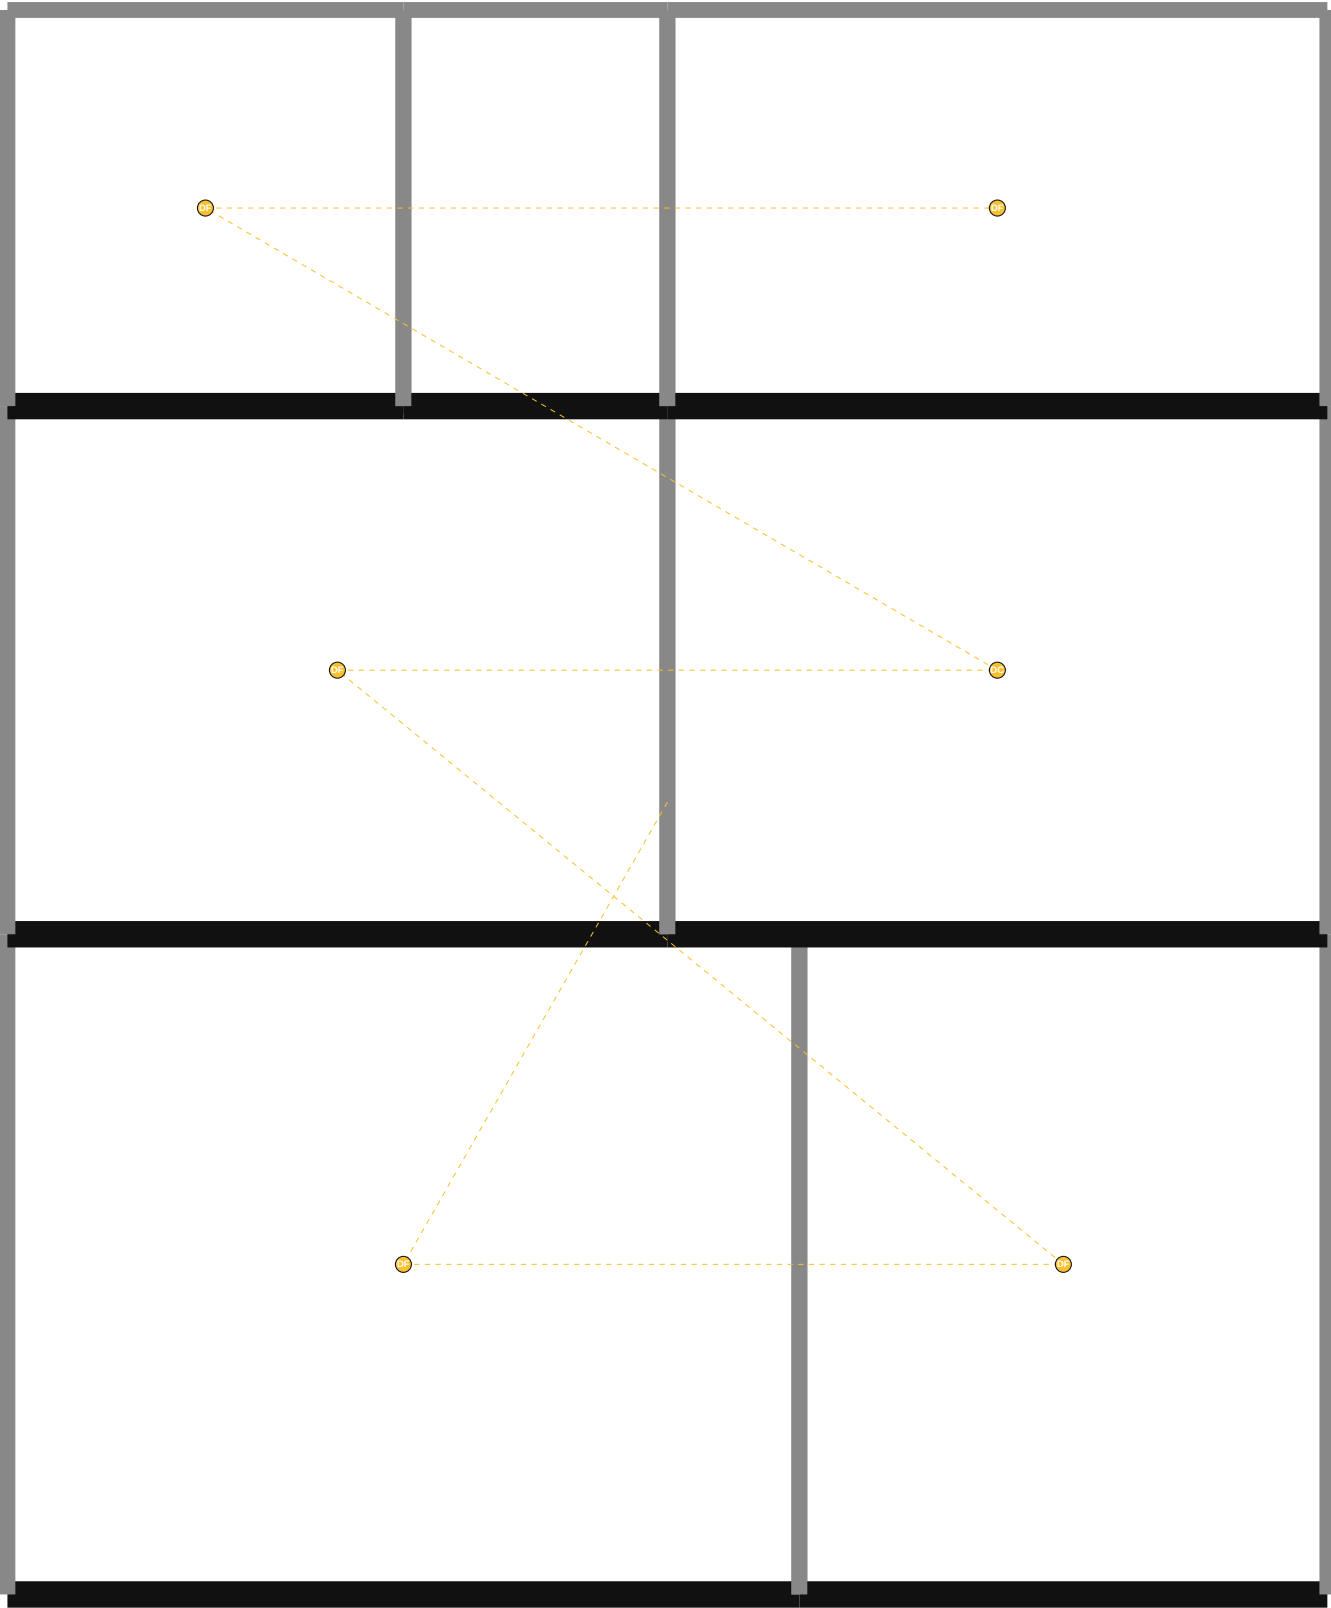

NOMENCLATURE — 400 FIF — Détection (DET)

- Détecteur de fumée: 5
- Détecteur de chaleur: 1


TIJAN AI Bureau d'Études Automatisé	Résidence Papa Oumar Sakho Dakar, Sénégal	Éch: 1/100 Pl. 43/70
	400 FIF — Détection (DET) — R+2	
Date: 06/05/2026	Réf: 1711	BIM vFIF-043 Phase: APD

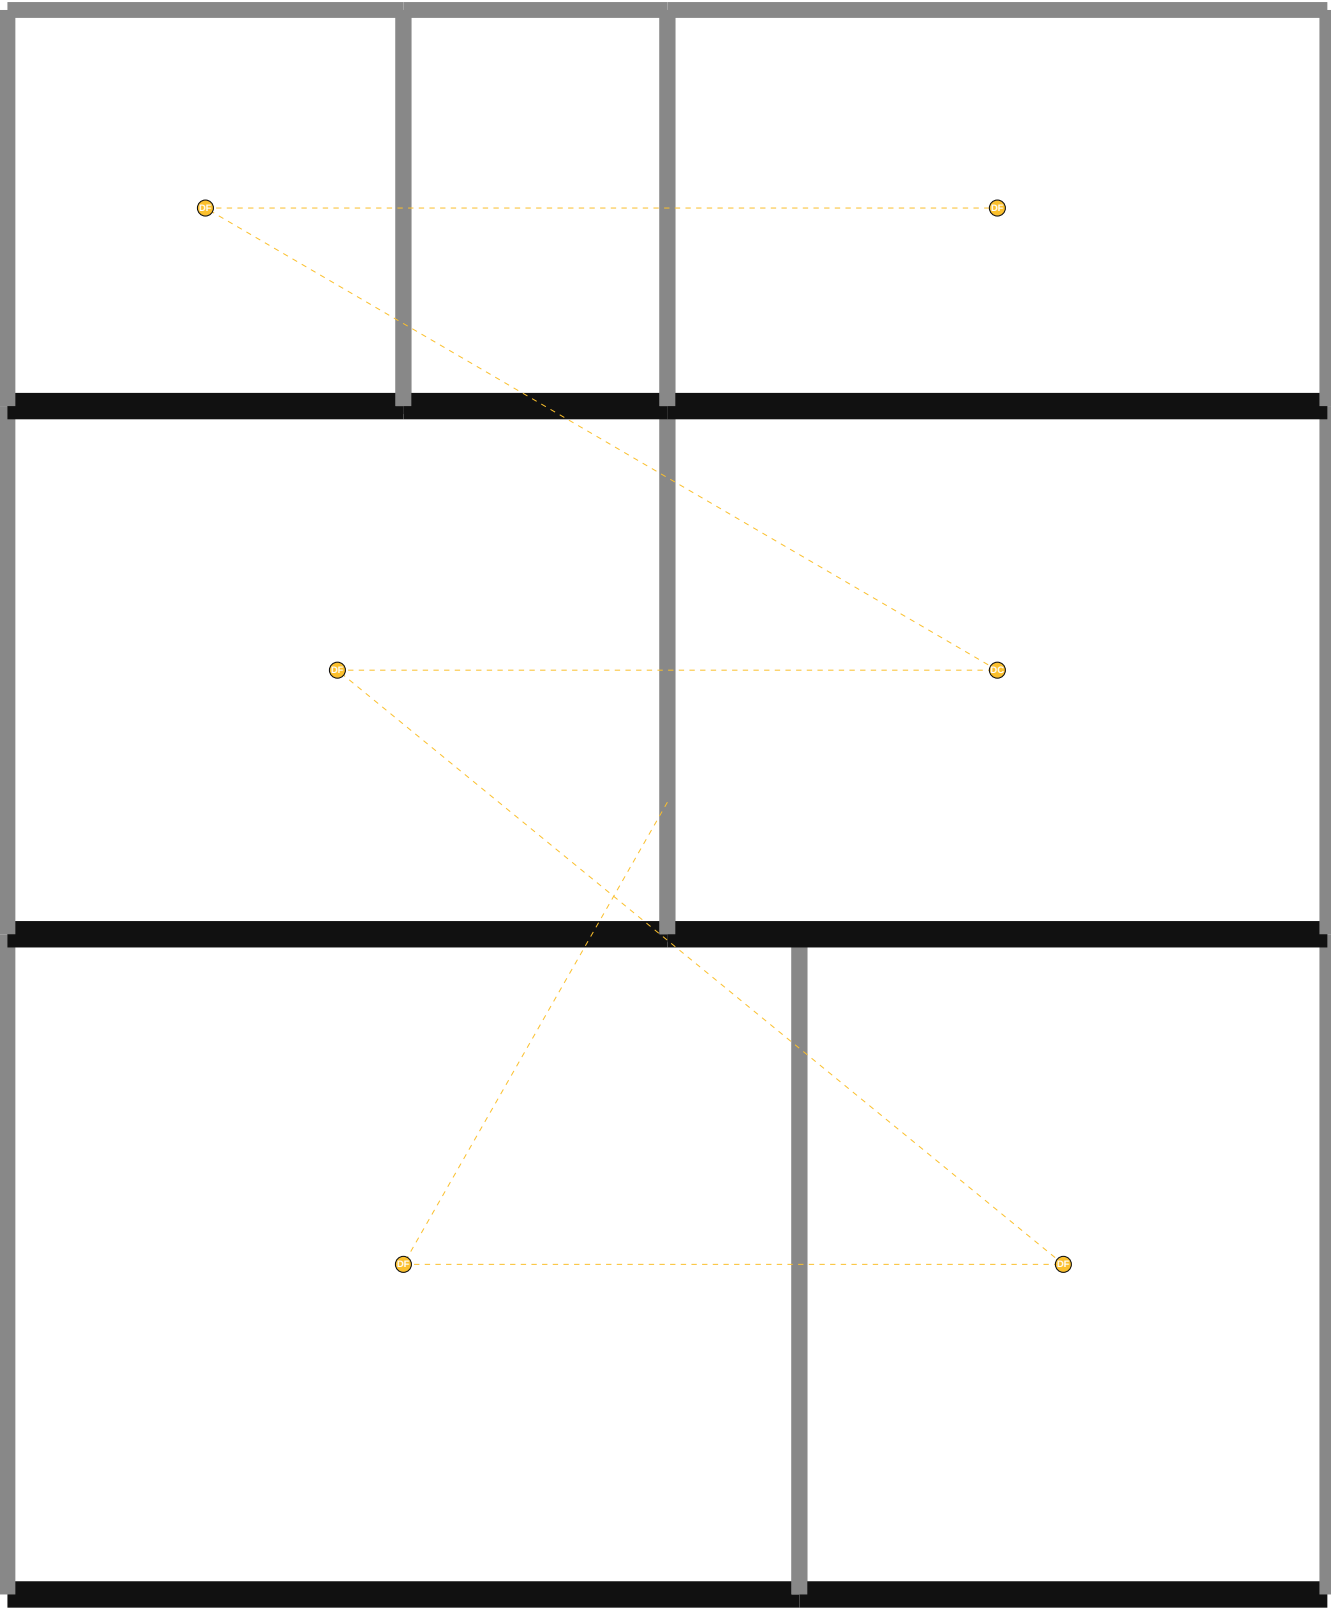

NOMENCLATURE — 400 FIF — Détection (DET)

- Détecteur de fumée: 5
- Détecteur de chaleur: 1


TIJAN AI Bureau d'Études Automatisé	Résidence Papa Oumar Sakho Dakar, Sénégal	Éch: 1/100 Pl. 44/70
	400 FIF — Détection (DET) — R+3	
Date: 06/05/2026	Réf: 1711	BIM vFIF-044 Phase: APD

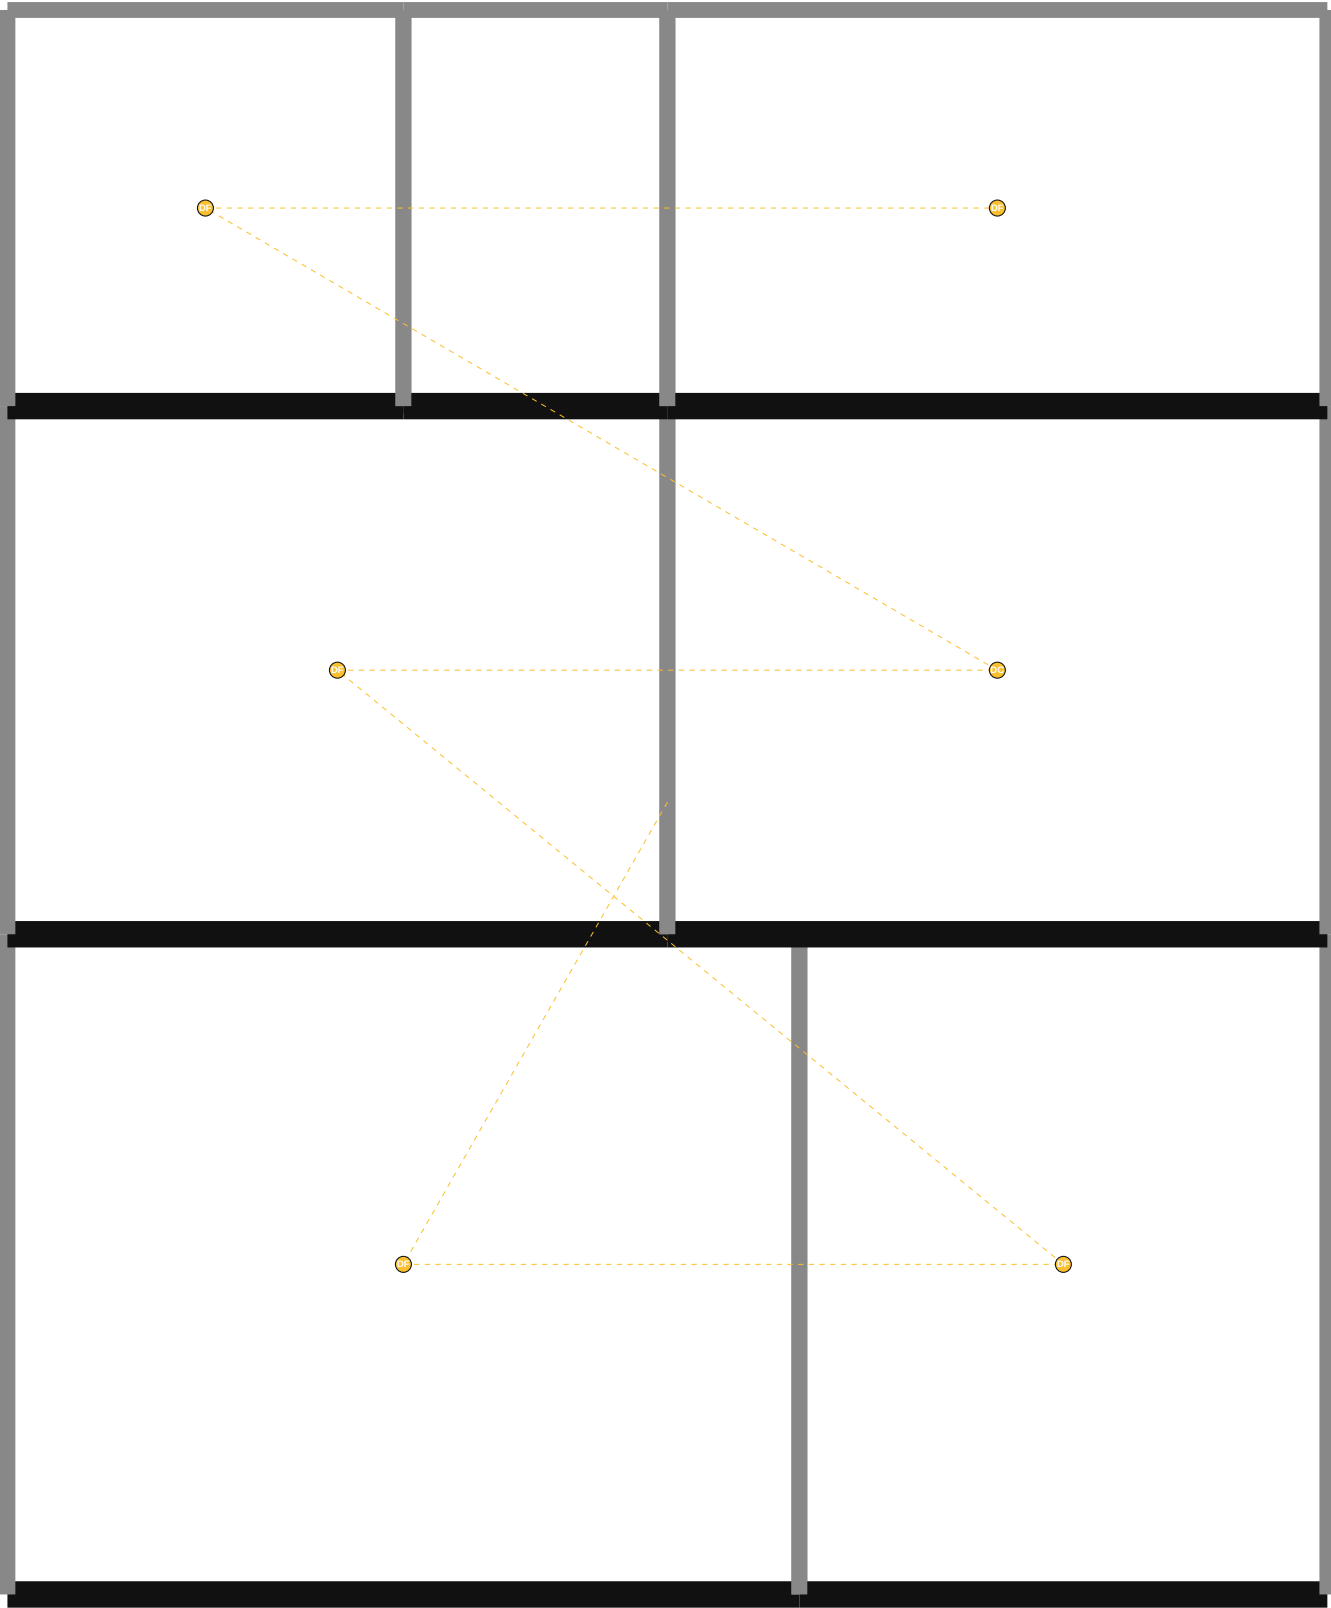

NOMENCLATURE — 400 FIF — Détection (DET)

- Détecteur de fumée: 5
- Détecteur de chaleur: 1


TIJAN AI Bureau d'Études Automatisé	Résidence Papa Oumar Sakho Dakar, Sénégal	Éch: 1/100 Pl. 45/70
	400 FIF — Détection (DET) — R+4	
Date: 06/05/2026	Réf: 1711	BIM vFIF-045 Phase: APD

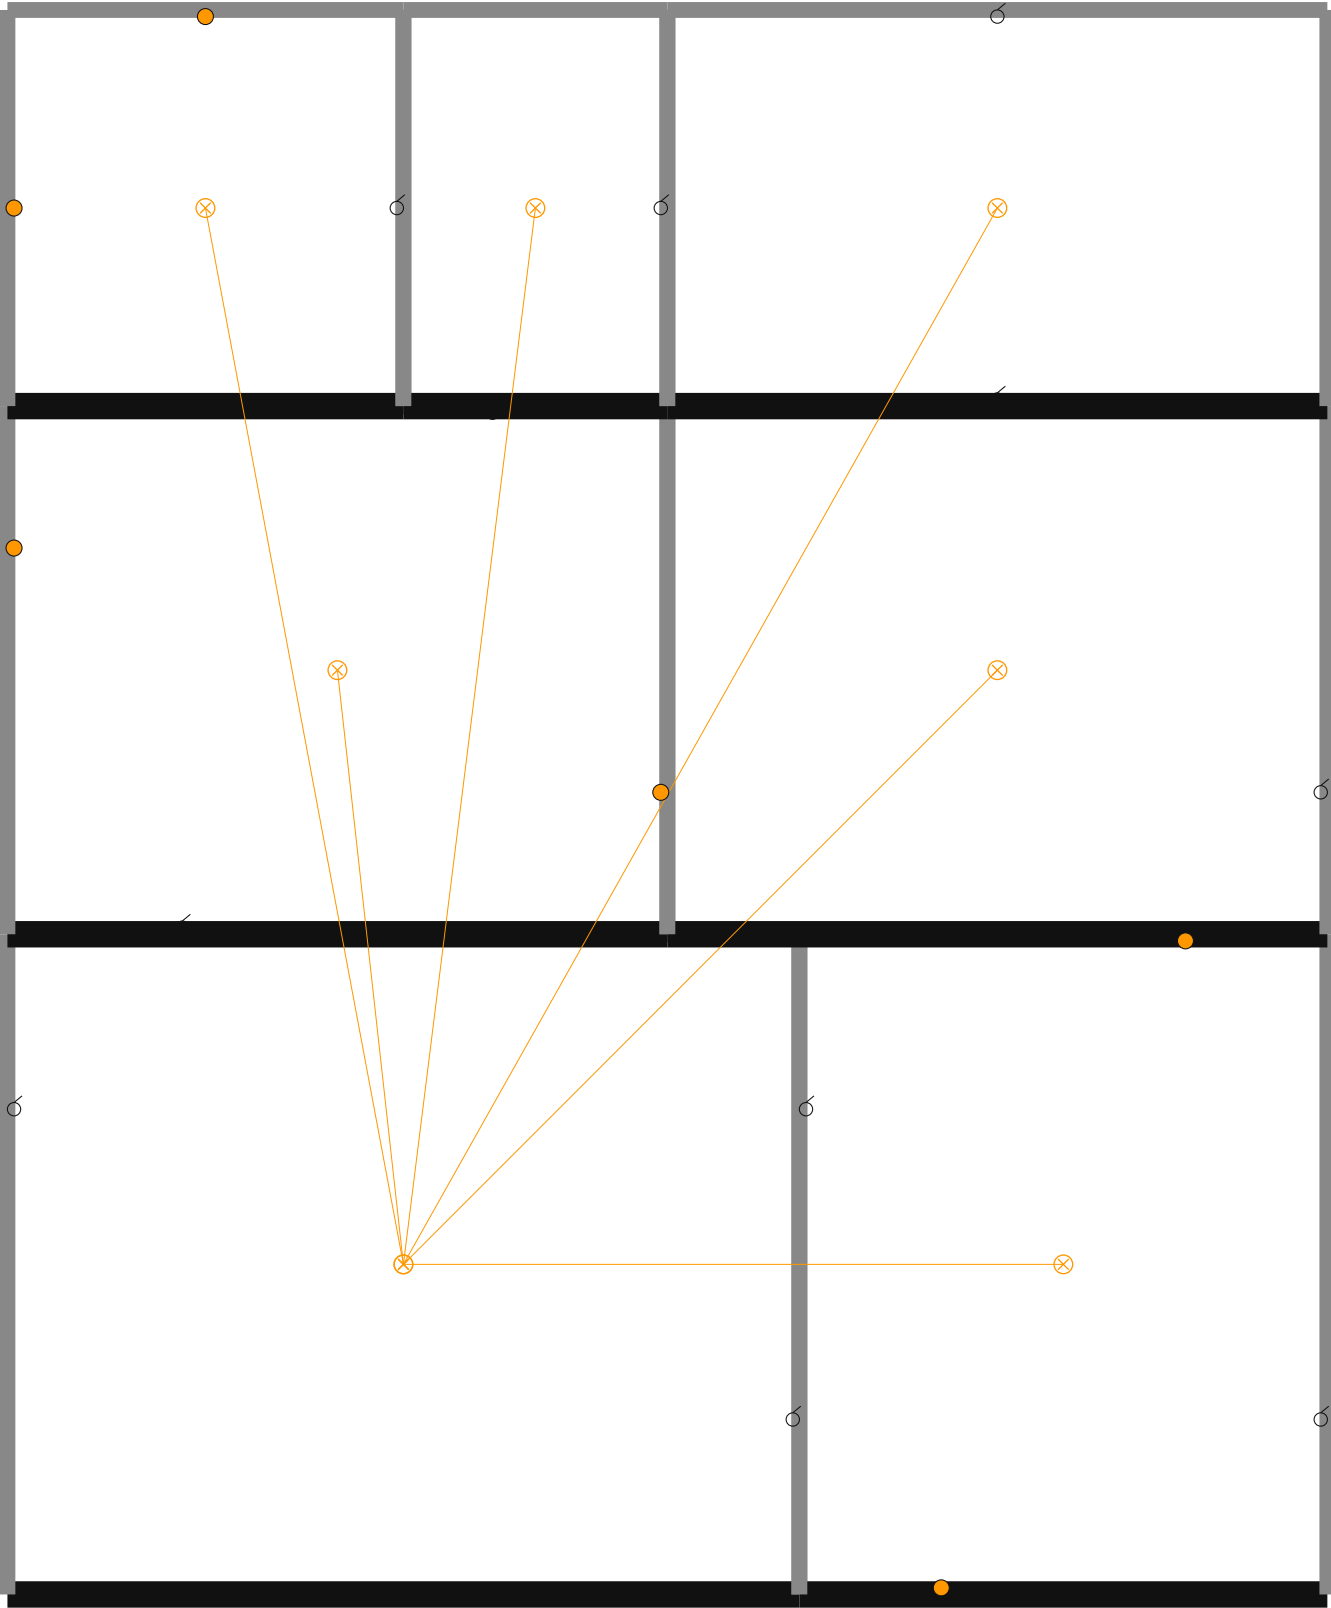

NOMENCLATURE — 510 HCU — Éclairage (ECL)

- Interrupteur va-et-vient: 8
- Plafonnier: 7
- Applique tête de lit: 4
- Interrupteur: 3
- Applique miroir: 2
- Plafonnier IP44: 1

TIJAN AI Bureau d'Études Automatisé	Résidence Papa Oumar Sakho Dakar, Sénégal	Éch: 1/100 Pl. 46/70
	510 HCU — Éclairage (ECL) — RDC	
Date: 06/05/2026	Réf: 1711	BIM vHCU-046 Phase: APD

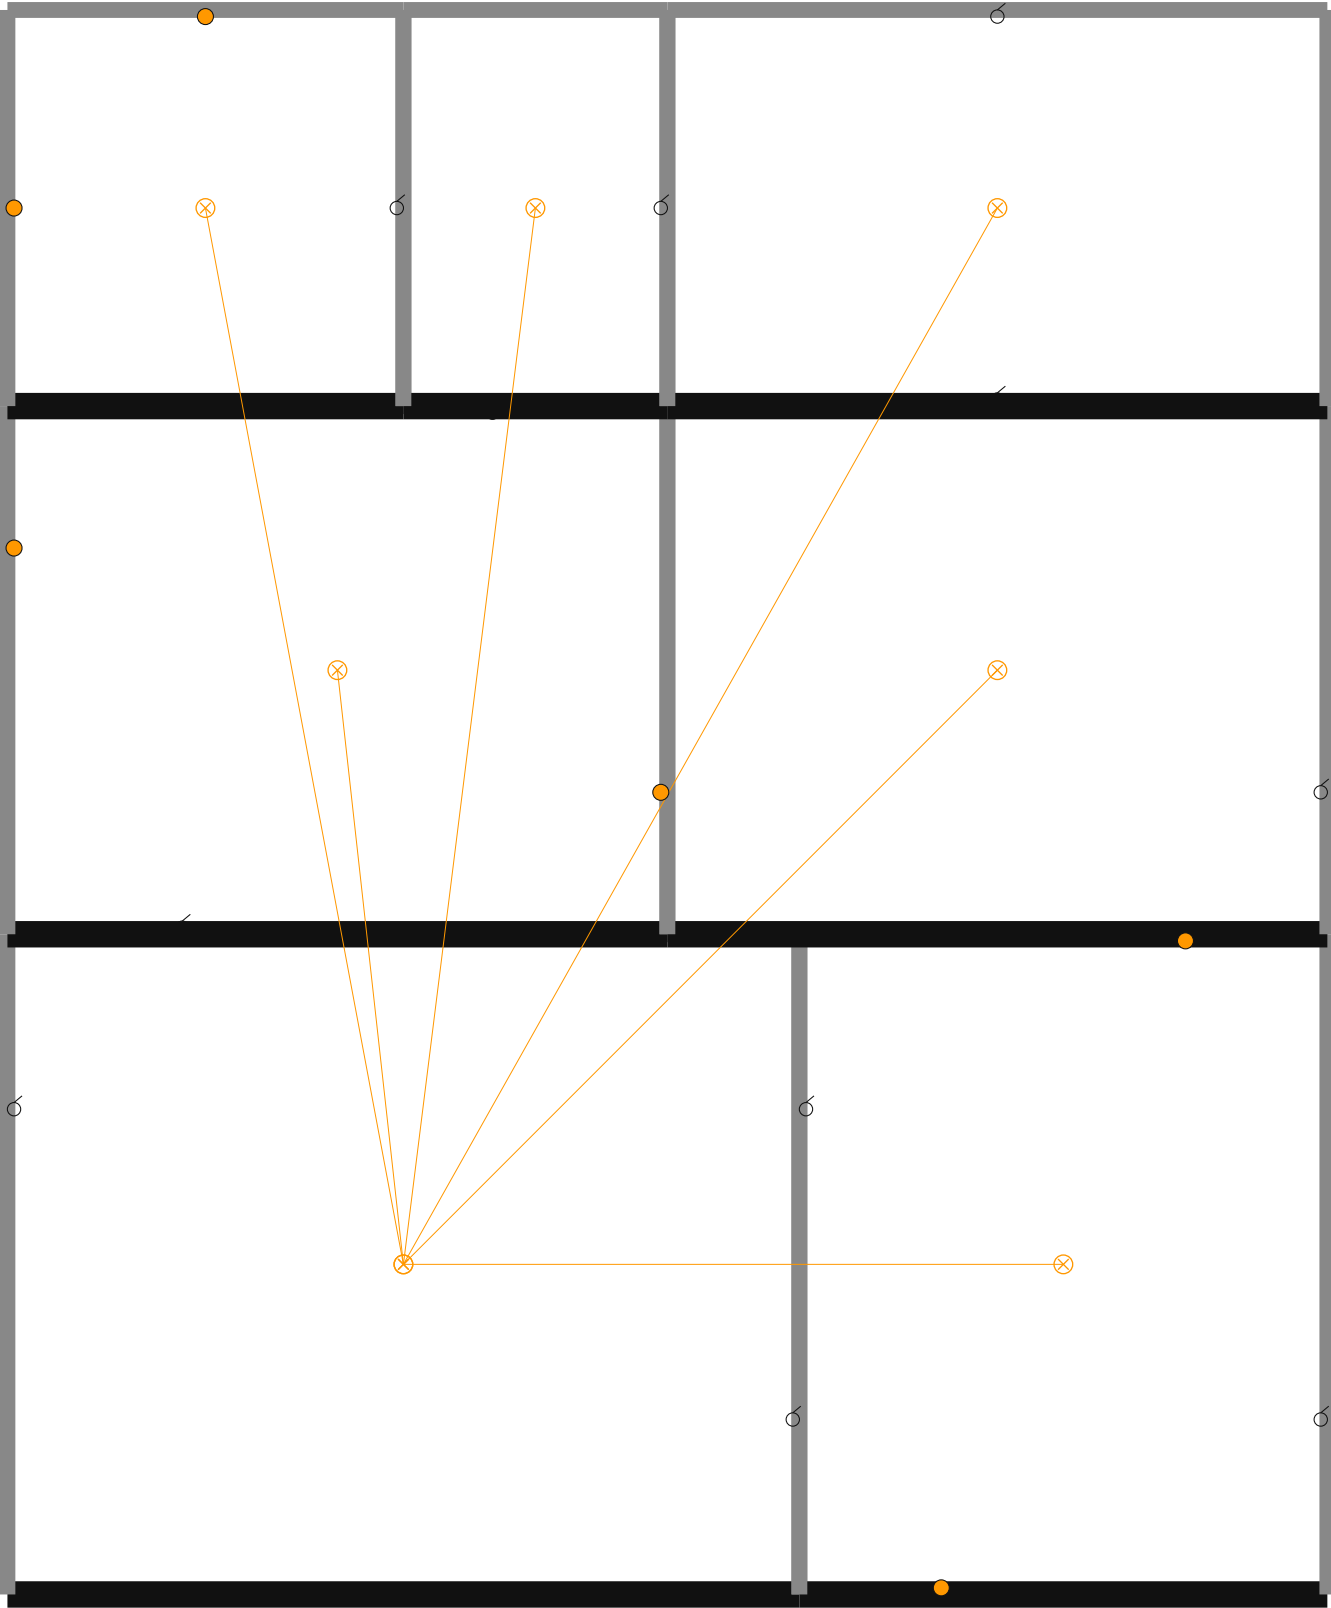


NOMENCLATURE — 510 HCU — Éclairage (ECL)

- Interrupteur va-et-vient: 8
- Plafonnier: 7
- Applique tête de lit: 4
- Interrupteur: 3
- Applique miroir: 2
- Plafonnier IP44: 1

TIJAN AI Bureau d'Études Automatisé	Résidence Papa Oumar Sakho Dakar, Sénégal	Éch: 1/100 Pl. 47/70
	510 HCU — Éclairage (ECL) — R+1	
Date: 06/05/2026	Réf: 1711	BIM vHCU-047 Phase: APD


510 HCU — Éclairage (ECL) — R+2

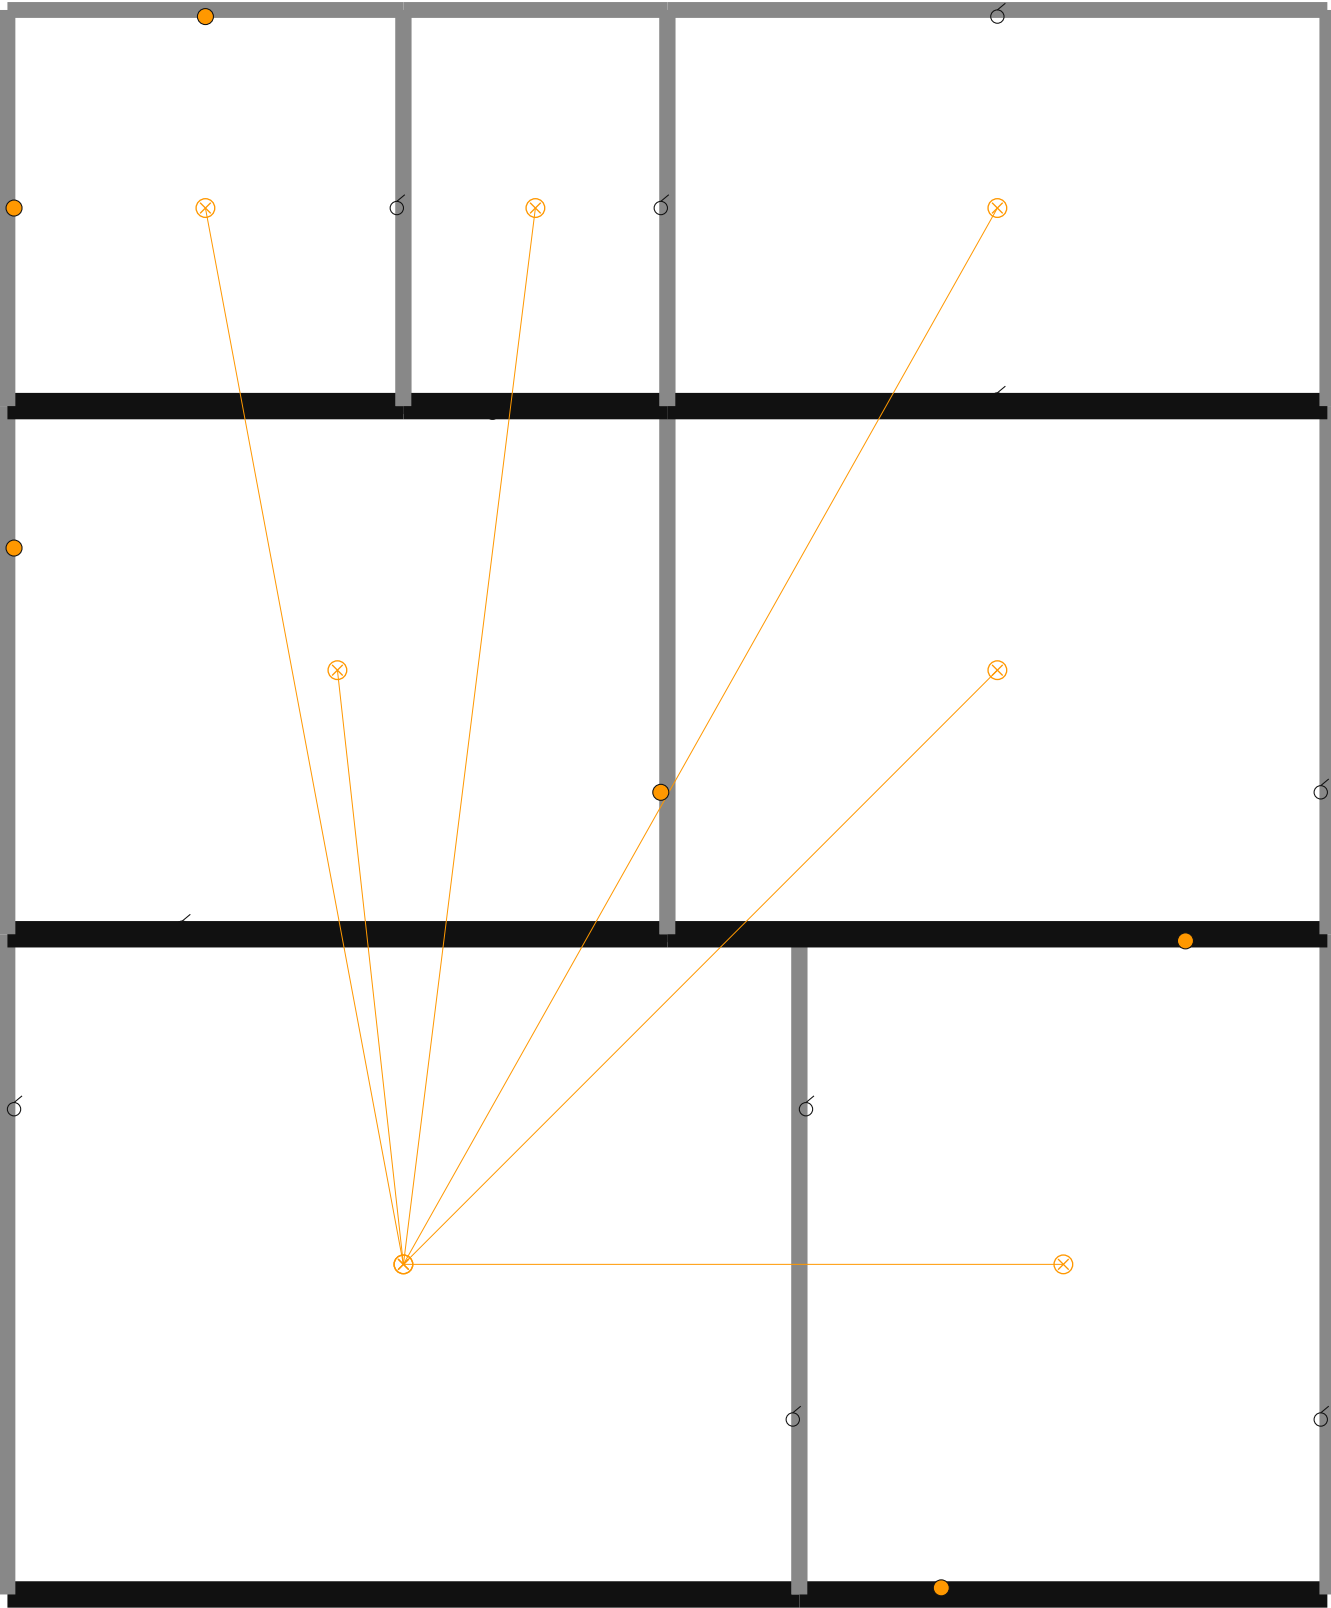

NOMENCLATURE — 510 HCU — Éclairage (ECL)

- Interrupteur va-et-vient: 8
- Plafonnier: 7
- Applique tête de lit: 4
- Interrupteur: 3
- Applique miroir: 2
- Plafonnier IP44: 1


TIJAN AI Bureau d'Études Automatisé	Résidence Papa Oumar Sakho Dakar, Sénégal	Éch: 1/100 Pl. 48/70
	510 HCU — Éclairage (ECL) — R+2	
Date: 06/05/2026	Réf: 1711	BIM vHCU-048 Phase: APD

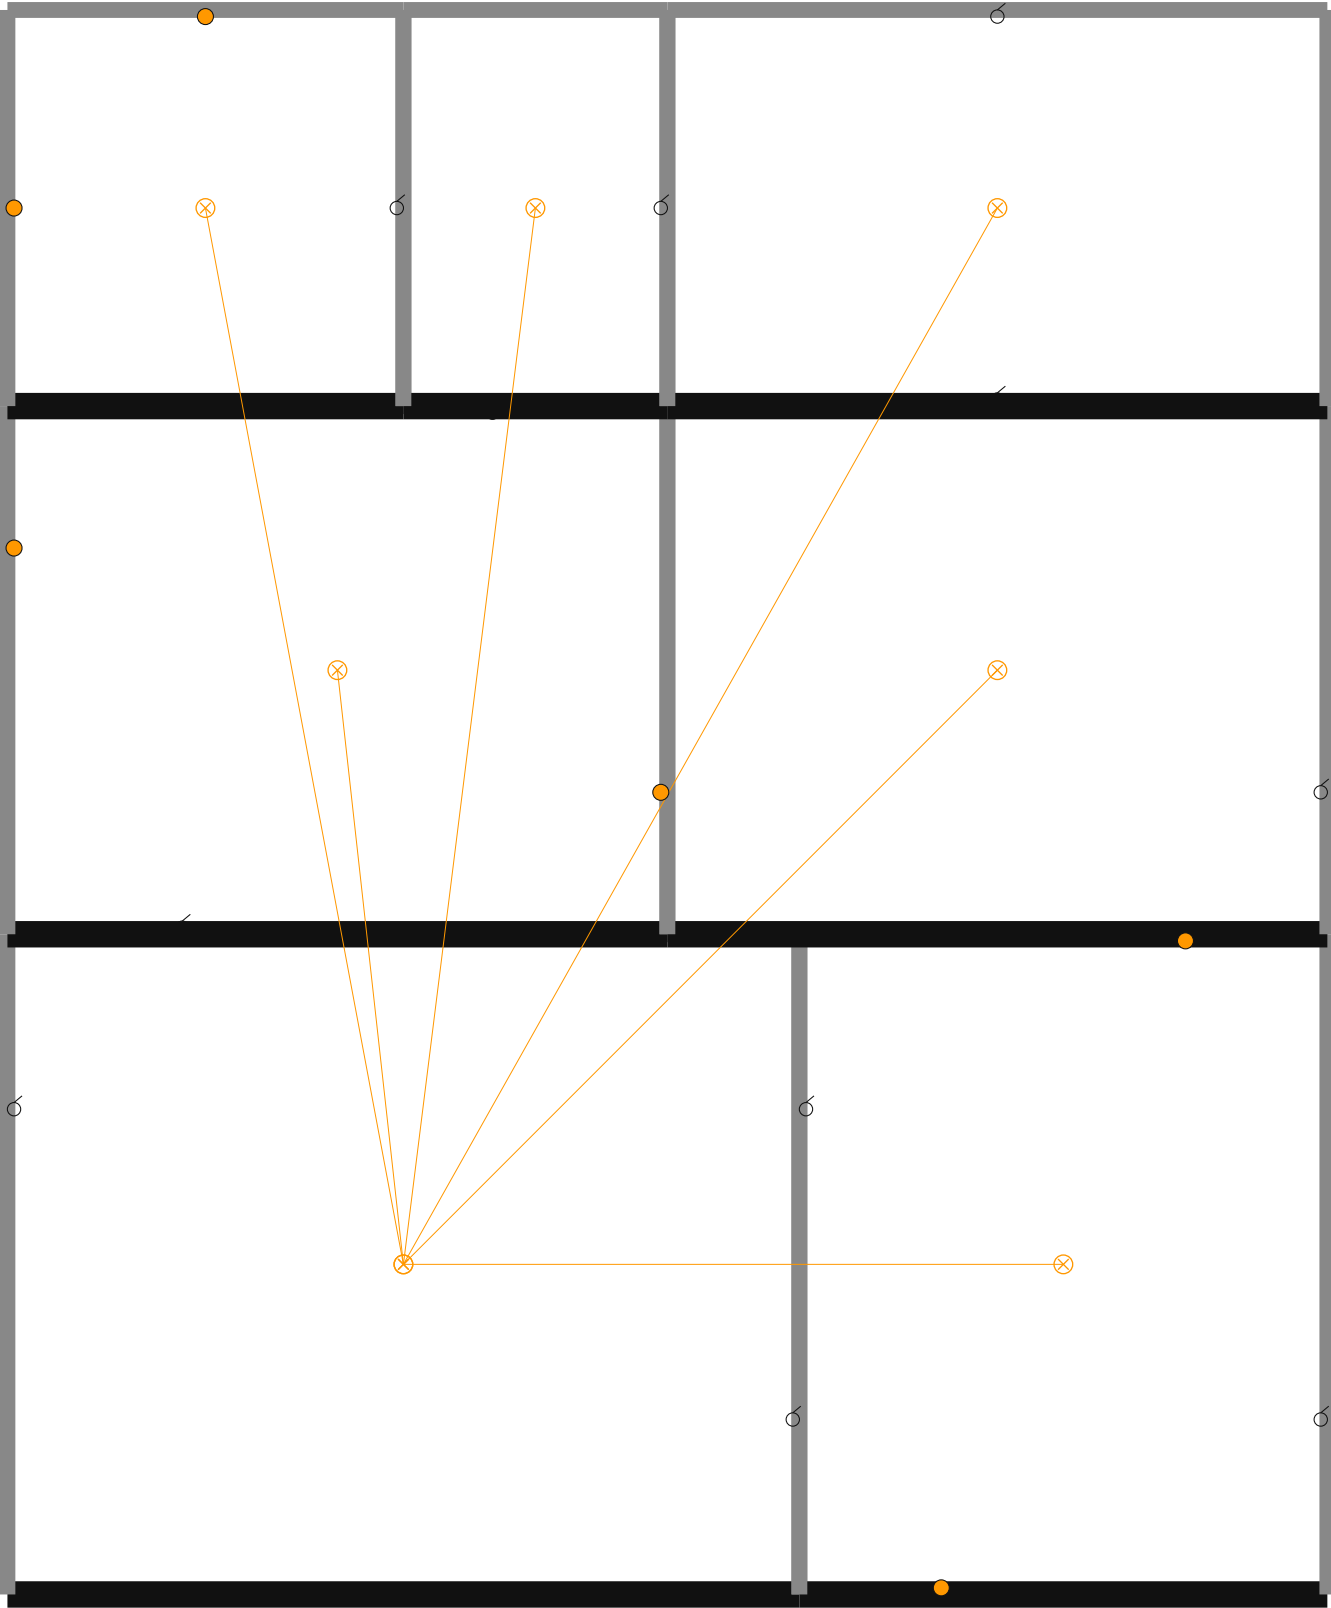

NOMENCLATURE — 510 HCU — Éclairage (ECL)

- Interrupteur va-et-vient: 8
- Plafonnier: 7
- Applique tête de lit: 4
- Interrupteur: 3
- Applique miroir: 2
- Plafonnier IP44: 1


TIJAN AI Bureau d'Études Automatisé	Résidence Papa Oumar Sakho Dakar, Sénégal	Éch: 1/100 Pl. 49/70
	510 HCU — Éclairage (ECL) — R+3	
Date: 06/05/2026	Réf: 1711	BIM vHCU-049 Phase: APD

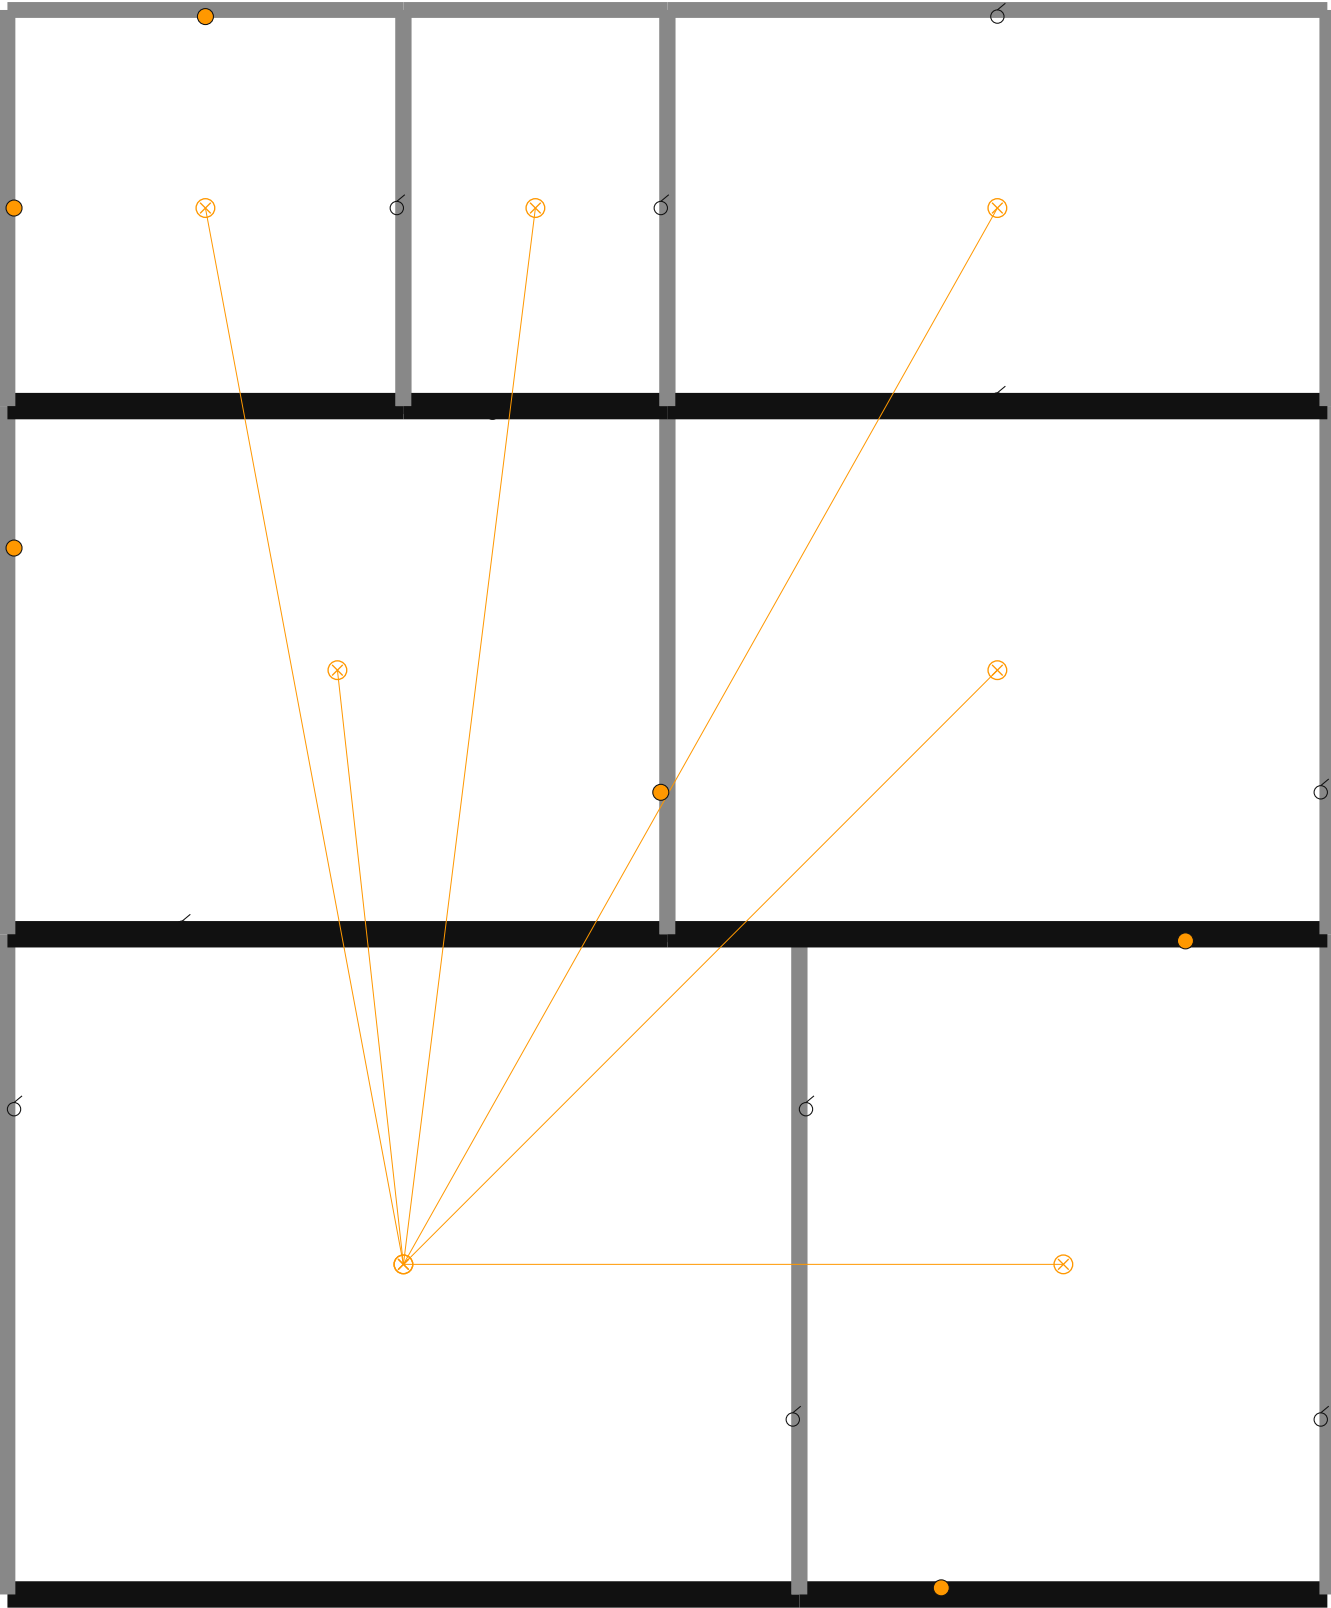

NOMENCLATURE — 510 HCU — Éclairage (ECL)

- Interrupteur va-et-vient: 8
- Plafonnier: 7
- Applique tête de lit: 4
- Interrupteur: 3
- Applique miroir: 2
- Plafonnier IP44: 1

TIJAN AI Bureau d'Études Automatisé	Résidence Papa Oumar Sakho Dakar, Sénégal	Éch: 1/100 Pl. 50/70
	510 HCU — Éclairage (ECL) — R+4	
Date: 06/05/2026	Réf: 1711	BIM vHCU-050 Phase: APD

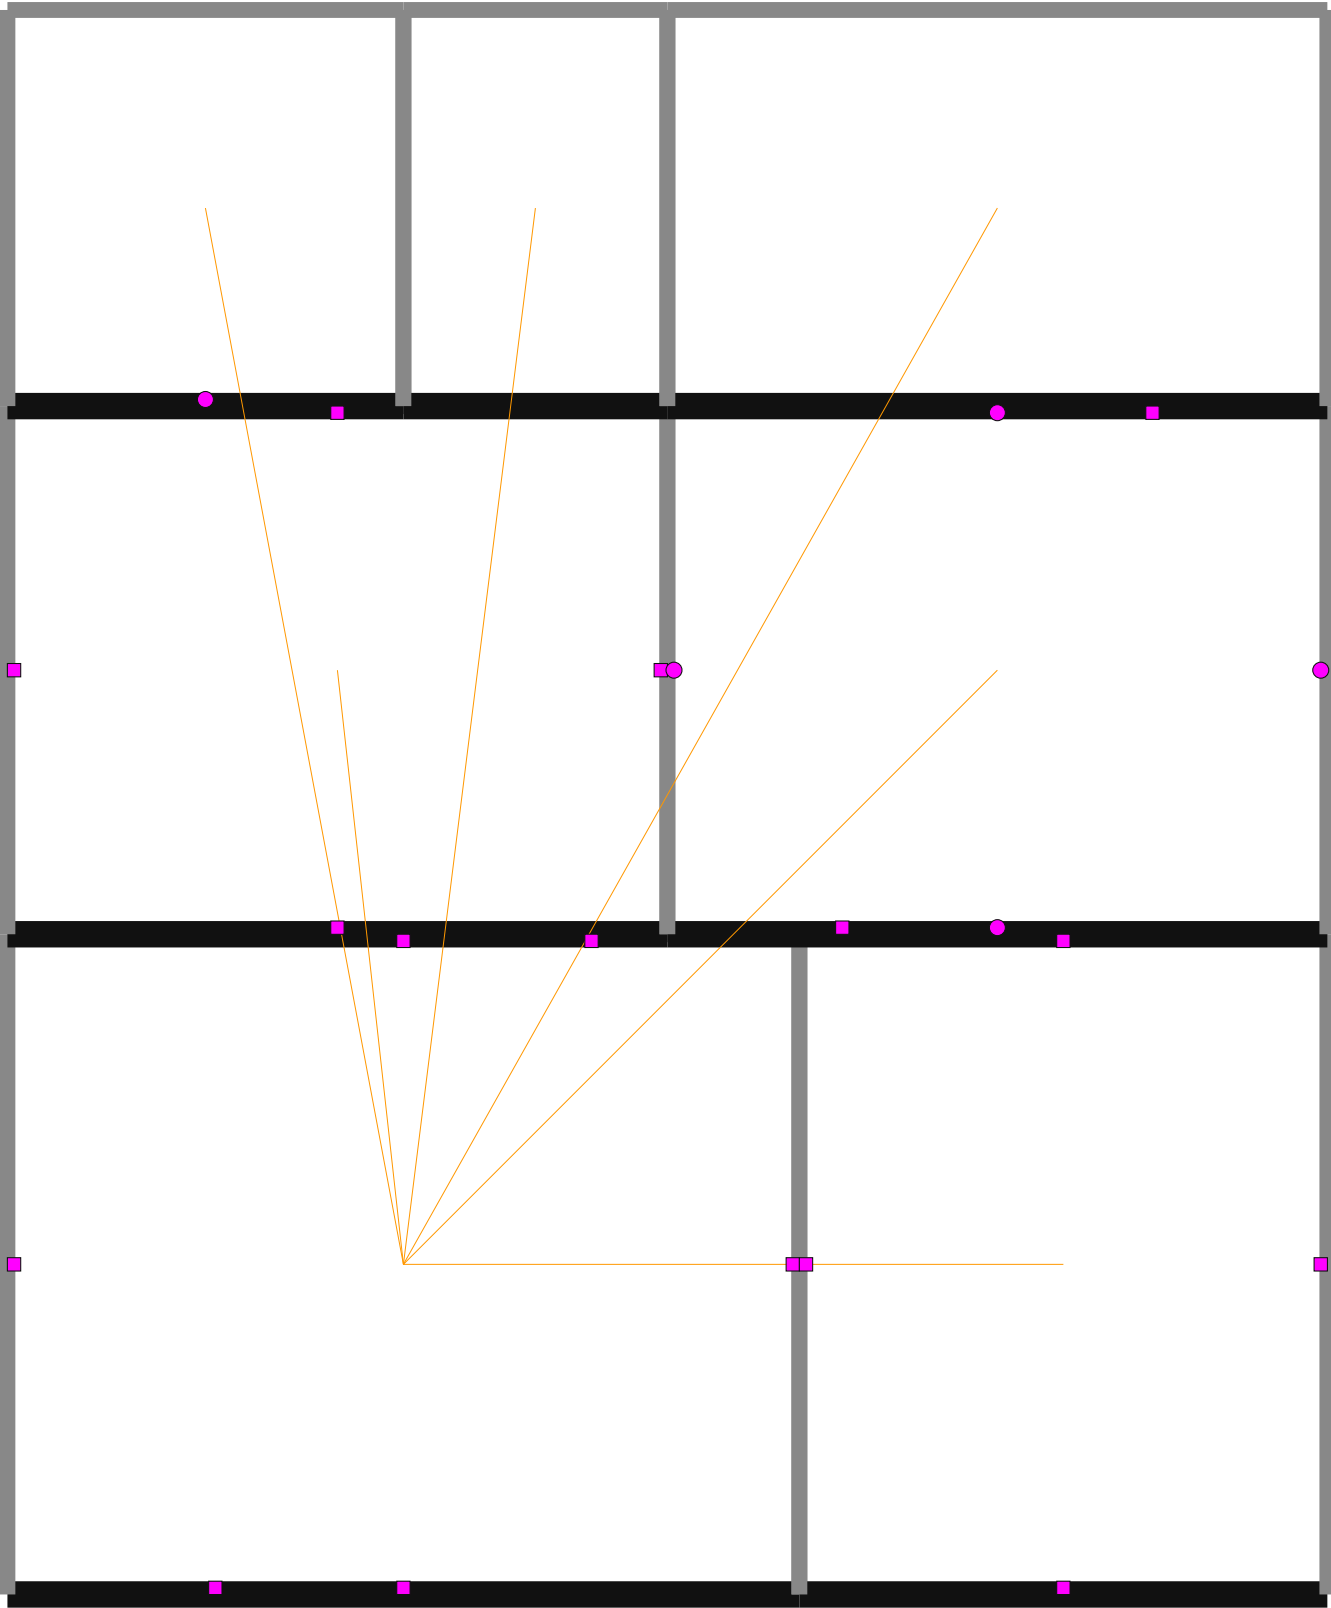


NOMENCLATURE — 510 HCU — Prises de Courant (PC)

- Prise 2P+T 16A: 16
- Prise plan de travail: 4
- Prise étanche 2P+T: 1

TIJAN AI Bureau d'Études Automatisé	Résidence Papa Oumar Sakho Dakar, Sénégal	Éch: 1/100 Pl. 51/70
	510 HCU — Prises de Courant (PC) — RDC	
Date: 06/05/2026	Réf: 1711	BIM vHCU-051 Phase: APD


510 HCU — Prises de Courant (PC) — R+1

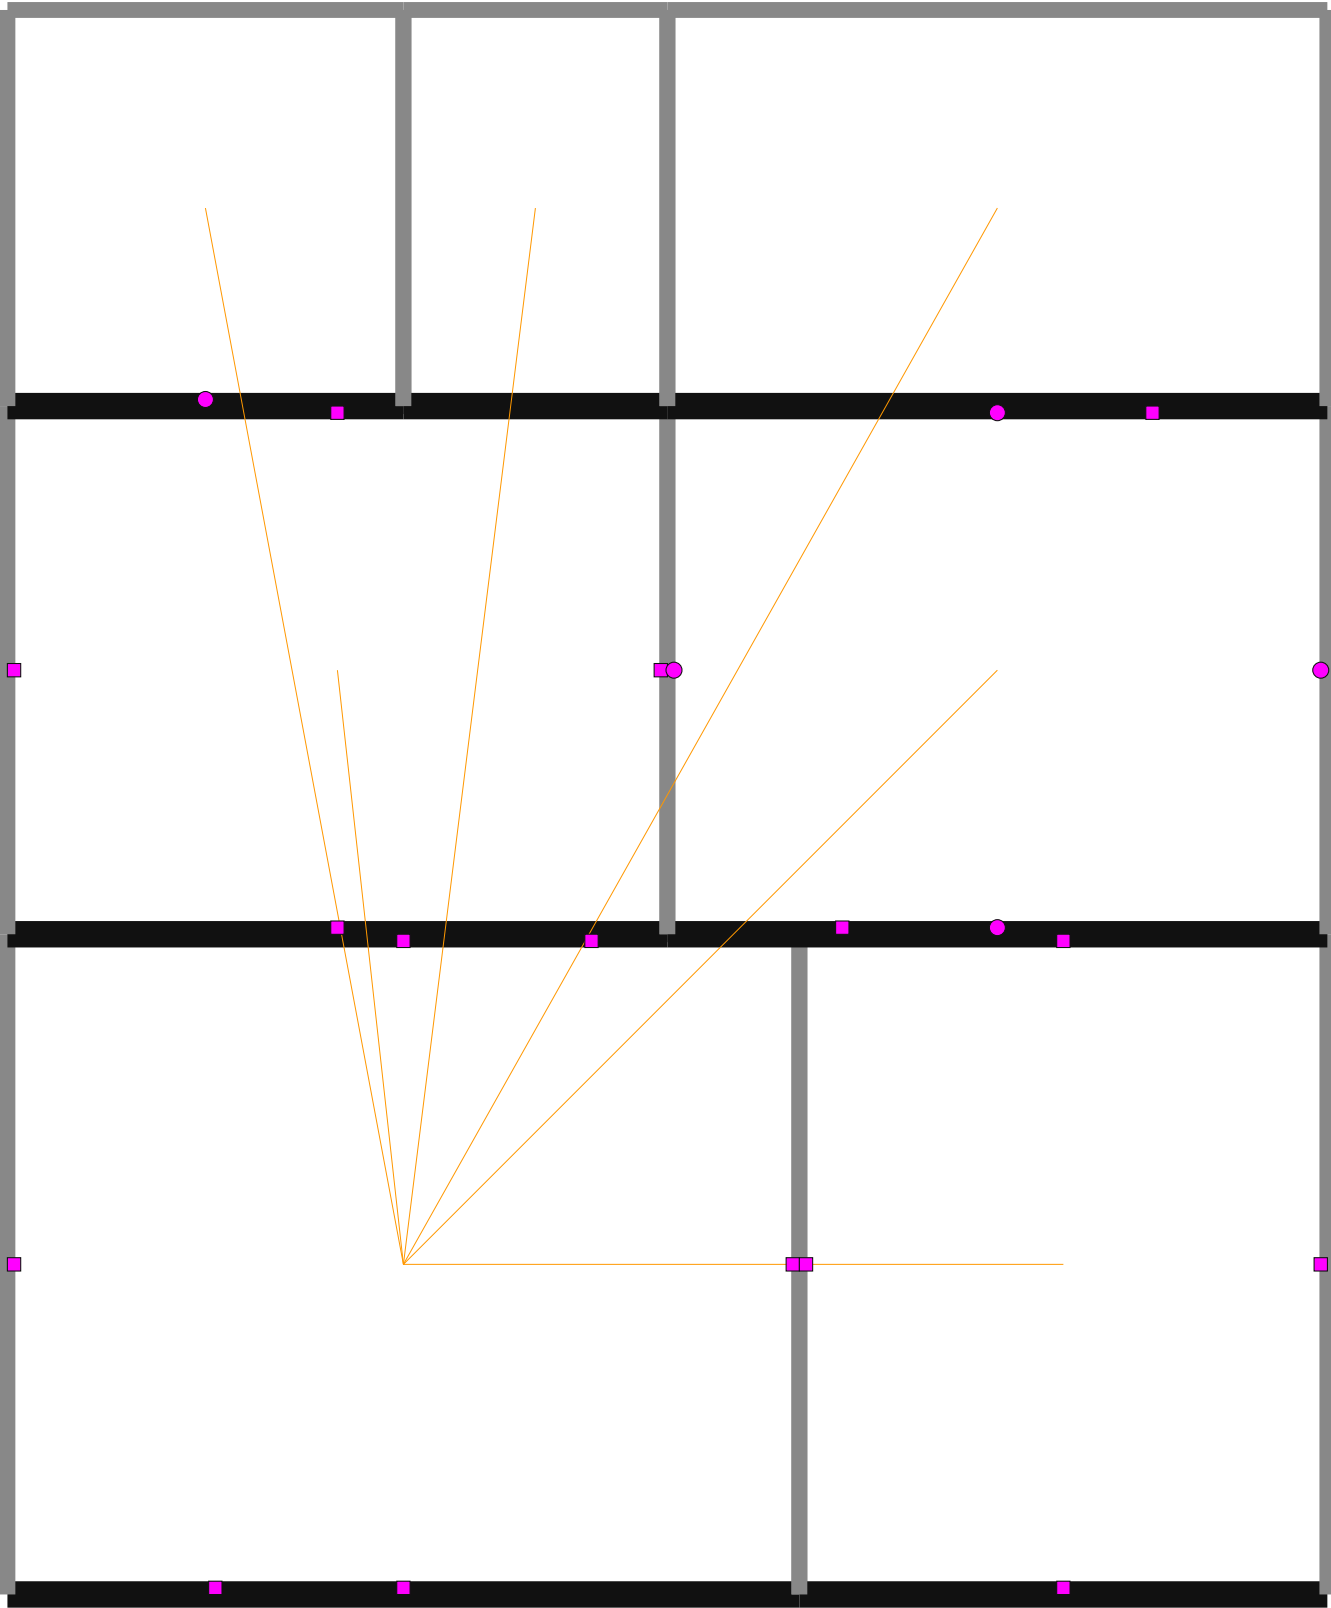

NOMENCLATURE — 510 HCU — Prises de Courant (PC)

- Prise 2P+T 16A: 16
- Prise plan de travail: 4
- Prise étanche 2P+T: 1


TIJAN AI Bureau d'Études Automatisé	Résidence Papa Oumar Sakho Dakar, Sénégal	Éch: 1/100 Pl. 52/70
	510 HCU — Prises de Courant (PC) — R+1	
Date: 06/05/2026	Réf: 1711	BIM vHCU-052 Phase: APD

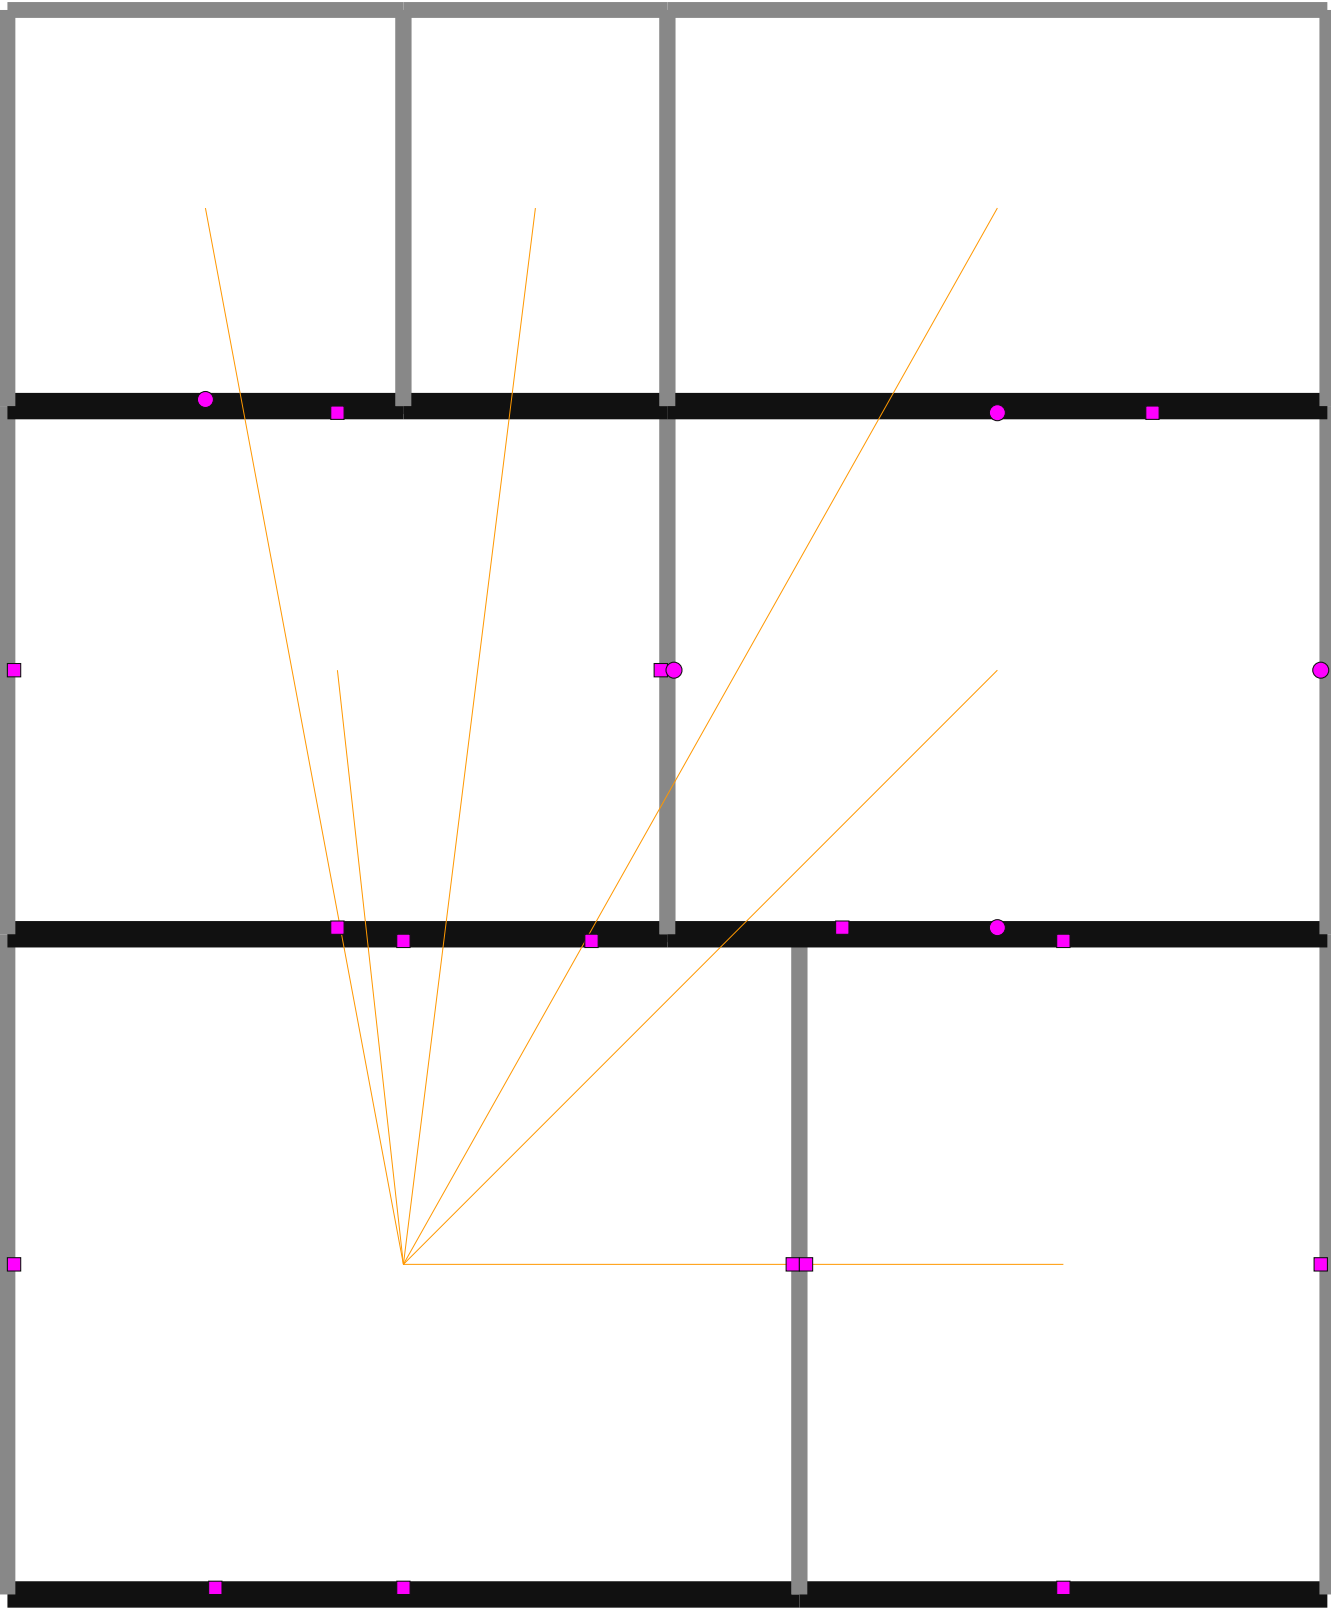

NOMENCLATURE — 510 HCU — Prises de Courant (PC)

- Prise 2P+T 16A: 16
- Prise plan de travail: 4
- Prise étanche 2P+T: 1


TIJAN AI Bureau d'Études Automatisé	Résidence Papa Oumar Sakho Dakar, Sénégal	Éch: 1/100 Pl. 53/70
	510 HCU — Prises de Courant (PC) — R+2	
Date: 06/05/2026	Réf: 1711	BIM vHCU-053 Phase: APD

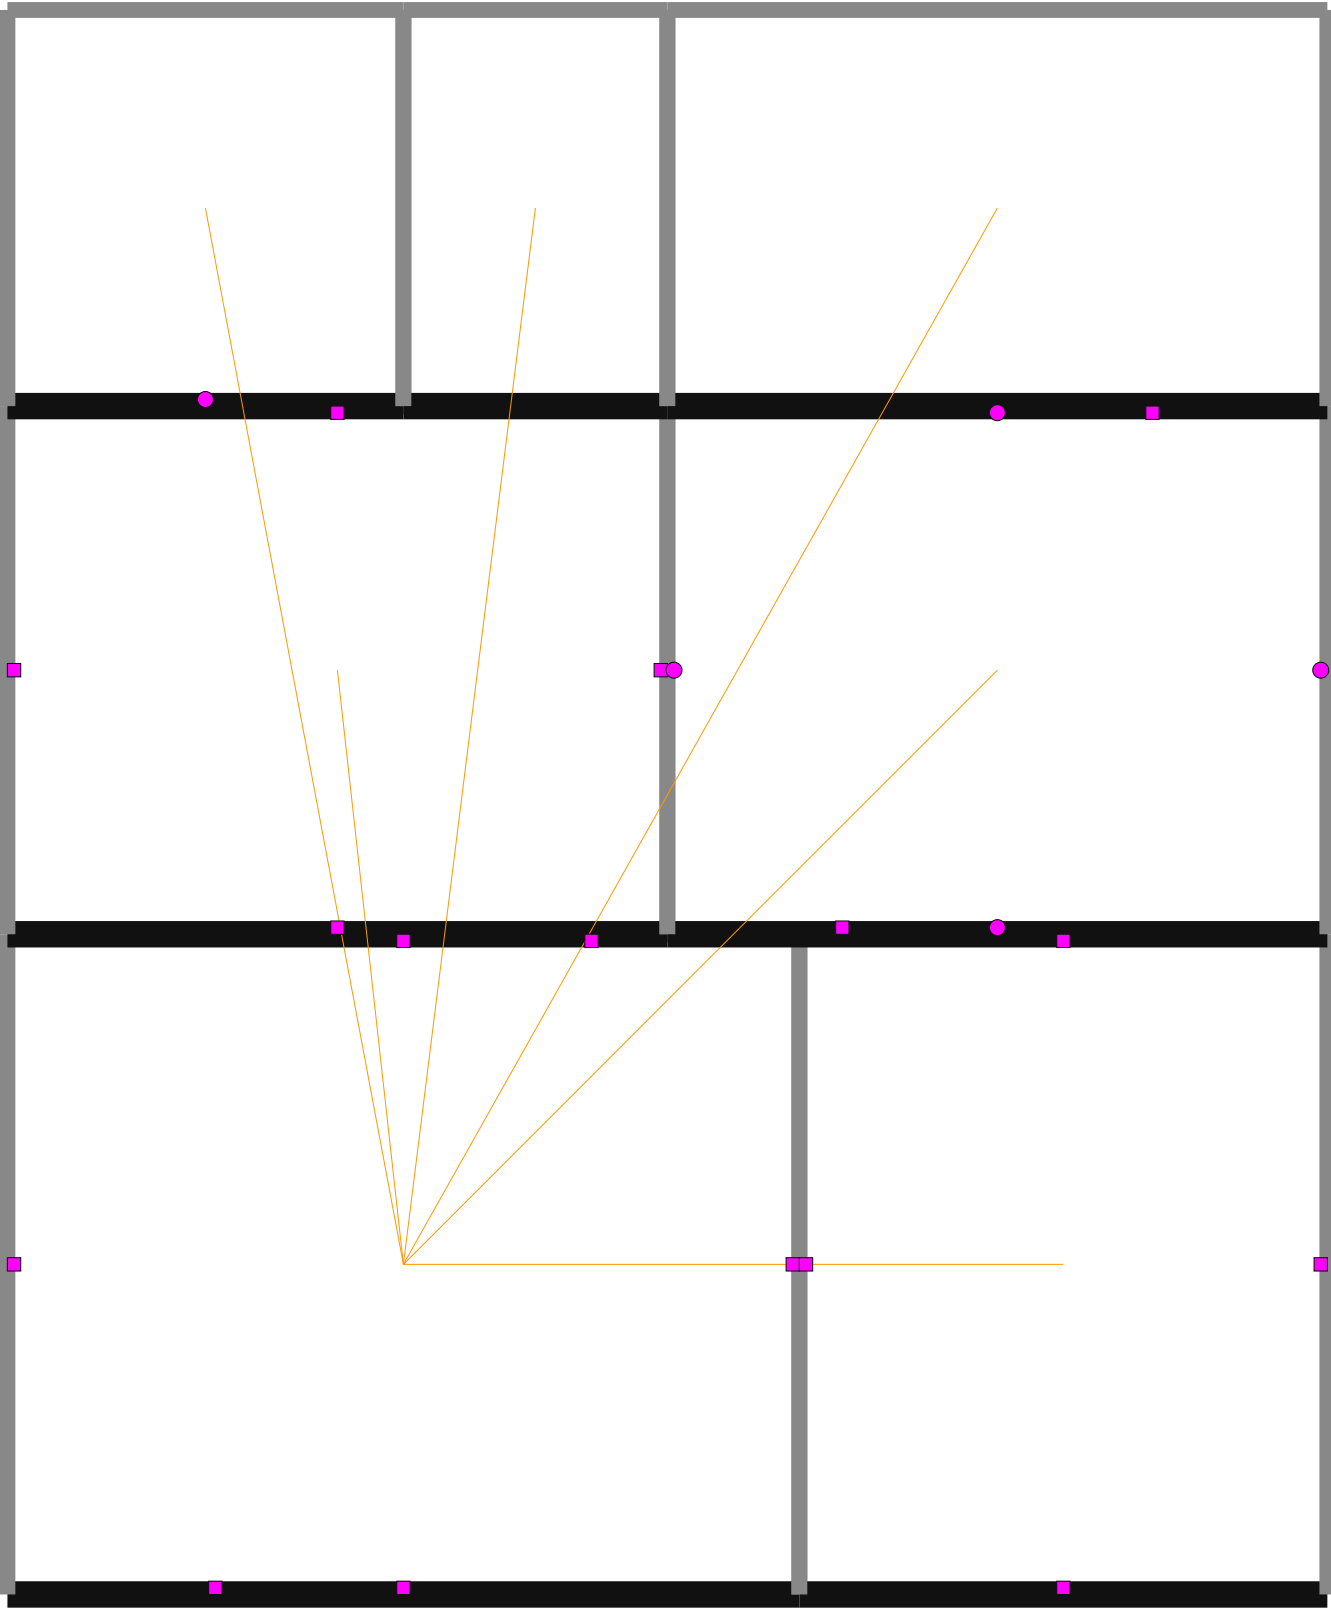

NOMENCLATURE — 510 HCU — Prises de Courant (PC)

- Prise 2P+T 16A: 16
- Prise plan de travail: 4
- Prise étanche 2P+T: 1


TIJAN AI Bureau d'Études Automatisé	Résidence Papa Oumar Sakho Dakar, Sénégal	Éch: 1/100 Pl. 54/70
	510 HCU — Prises de Courant (PC) — R+3	
Date: 06/05/2026	Réf: 1711	BIM vHCU-054 Phase: APD

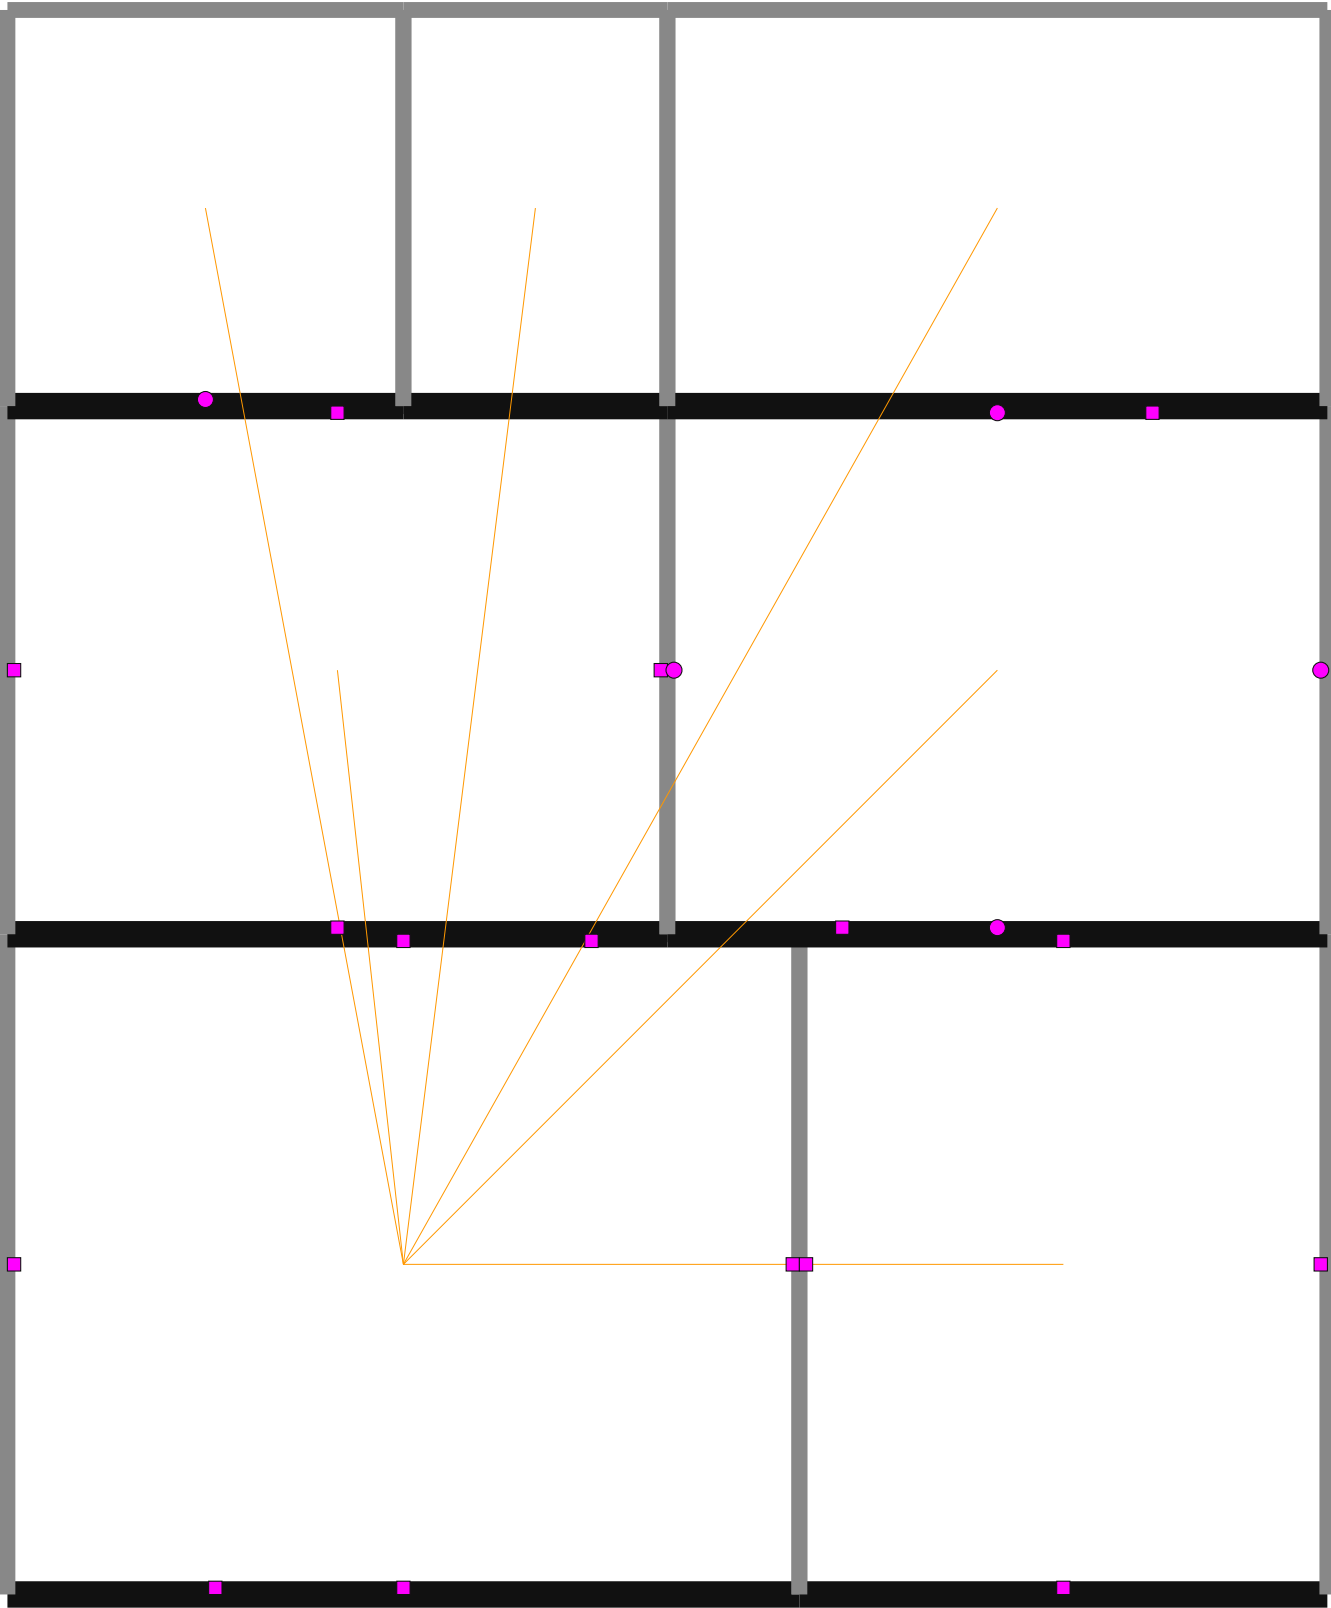

NOMENCLATURE — 510 HCU — Prises de Courant (PC)

- Prise 2P+T 16A: 16
- Prise plan de travail: 4
- Prise étanche 2P+T: 1


TIJAN AI Bureau d'Études Automatisé	Résidence Papa Oumar Sakho Dakar, Sénégal	Éch: 1/100 Pl. 55/70
	510 HCU — Prises de Courant (PC) — R+4	
Date: 06/05/2026	Réf: 1711	BIM vHCU-055 Phase: APD

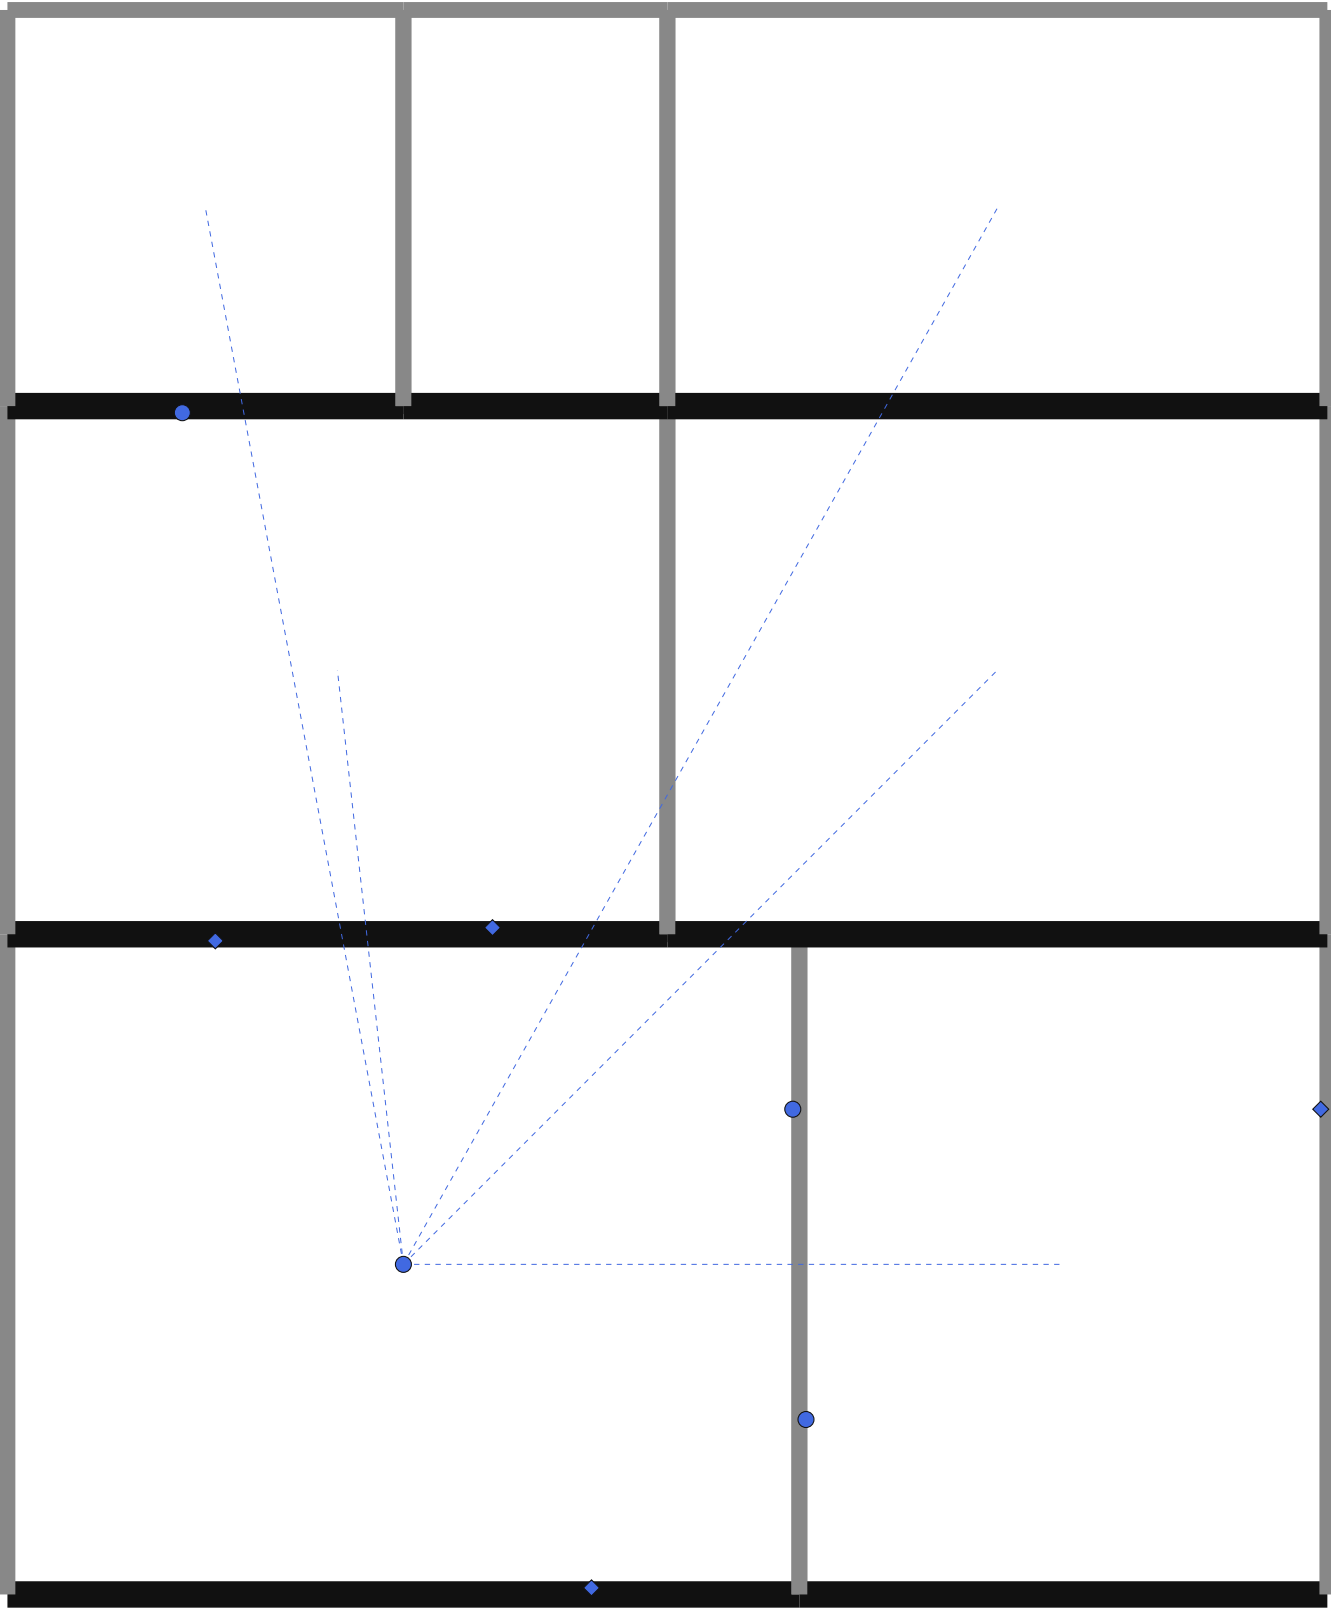

NOMENCLATURE — 520 LCU — Courants Faibles

- Prise RJ45: 4
- Prise TV: 3
- Point d'accès WiFi: 1


TIJAN AI Bureau d'Études Automatisé	Résidence Papa Oumar Sakho Dakar, Sénégal	Éch: 1/100 Pl. 56/70
	520 LCU — Courants Faibles — RDC	
Date: 06/05/2026	Réf: 1711	BIM v.LCU-056 Phase: APD

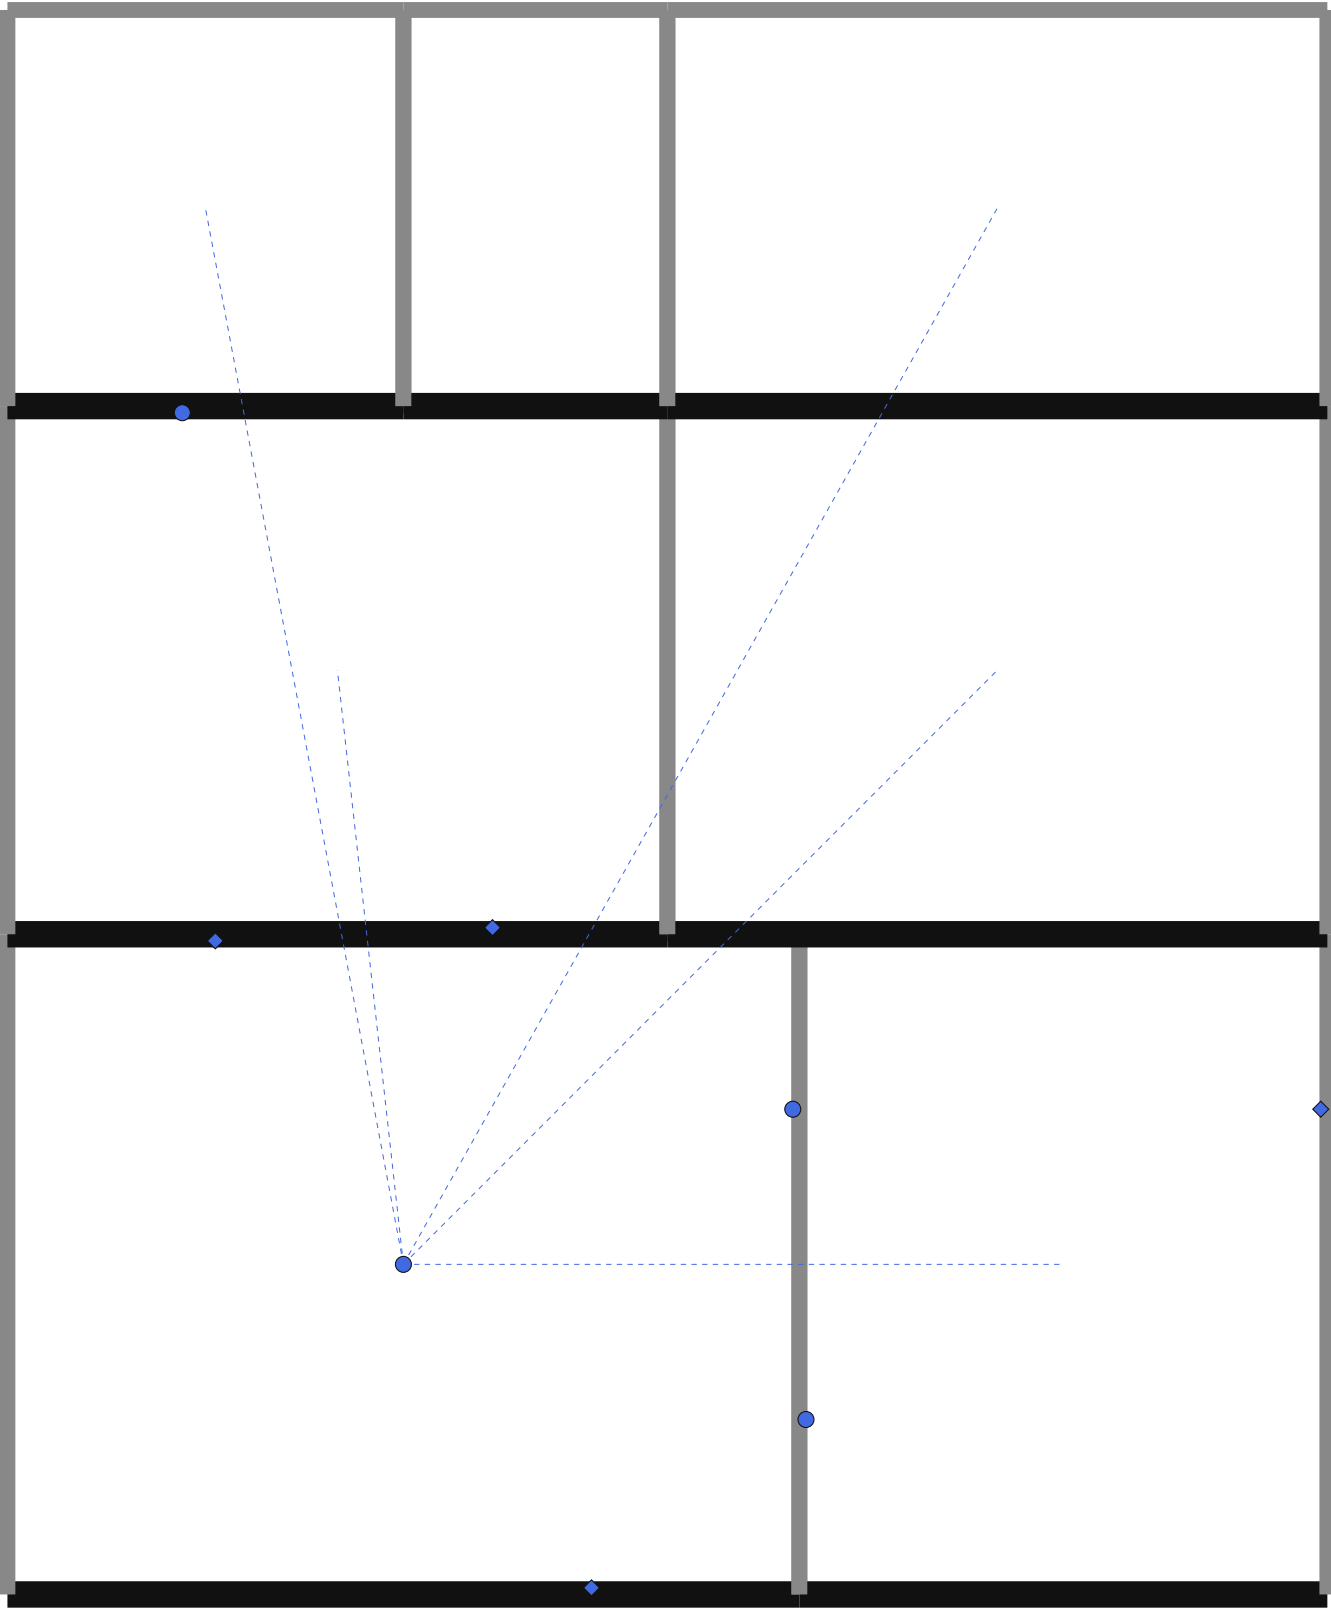

NOMENCLATURE — 520 LCU — Courants Faibles

- Prise RJ45: 4
- Prise TV: 3
- Point d'accès WiFi: 1


TIJAN AI Bureau d'Études Automatisé	Résidence Papa Oumar Sakho Dakar, Sénégal	Éch: 1/100 Pl. 57/70
	520 LCU — Courants Faibles — R+1	
Date: 06/05/2026	Réf: 1711	BIM v.LCU-057 Phase: APD

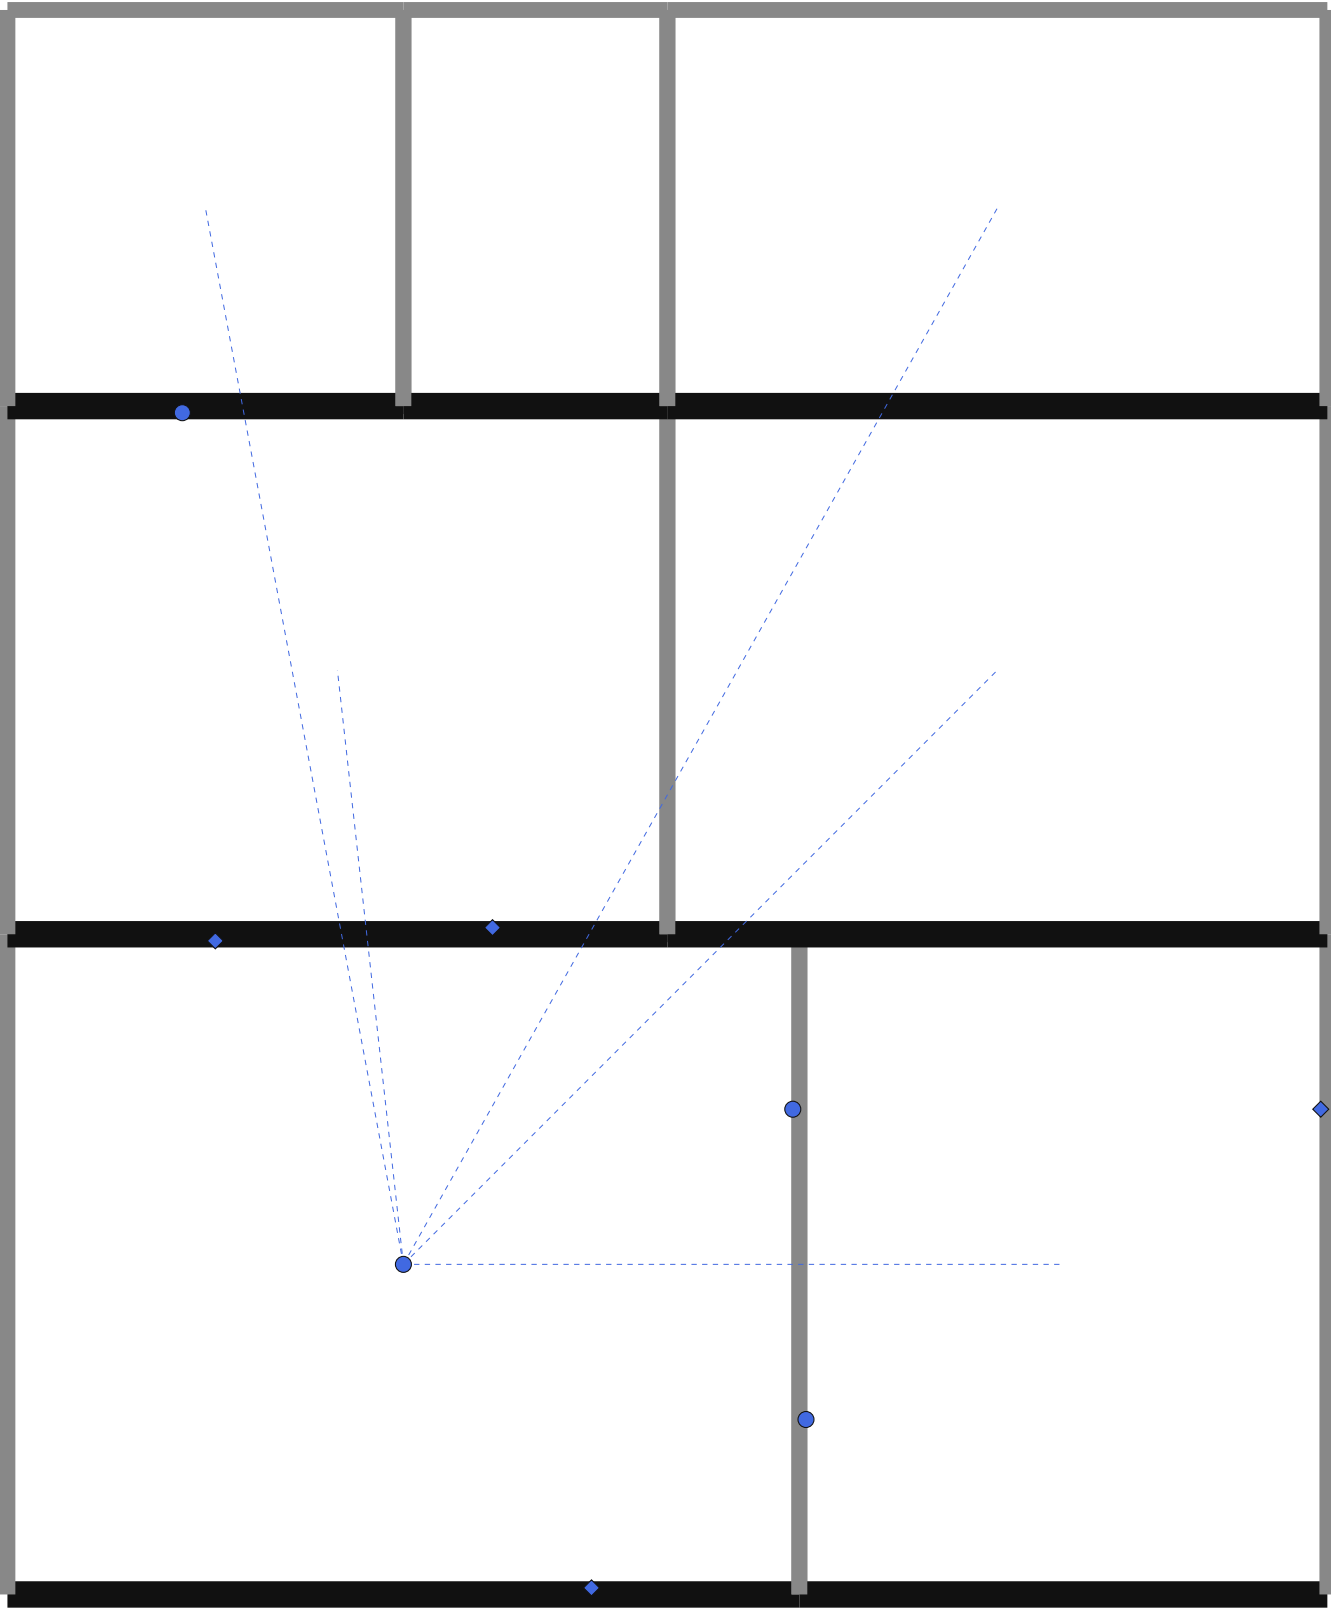

NOMENCLATURE — 520 LCU — Courants Faibles

- Prise RJ45: 4
- Prise TV: 3
- Point d'accès WiFi: 1


TIJAN AI Bureau d'Études Automatisé	Résidence Papa Oumar Sakho Dakar, Sénégal	Éch: 1/100 Pl. 58/70
	520 LCU — Courants Faibles — R+2	
Date: 06/05/2026	Réf: 1711	BIM v.LCU-058 Phase: APD

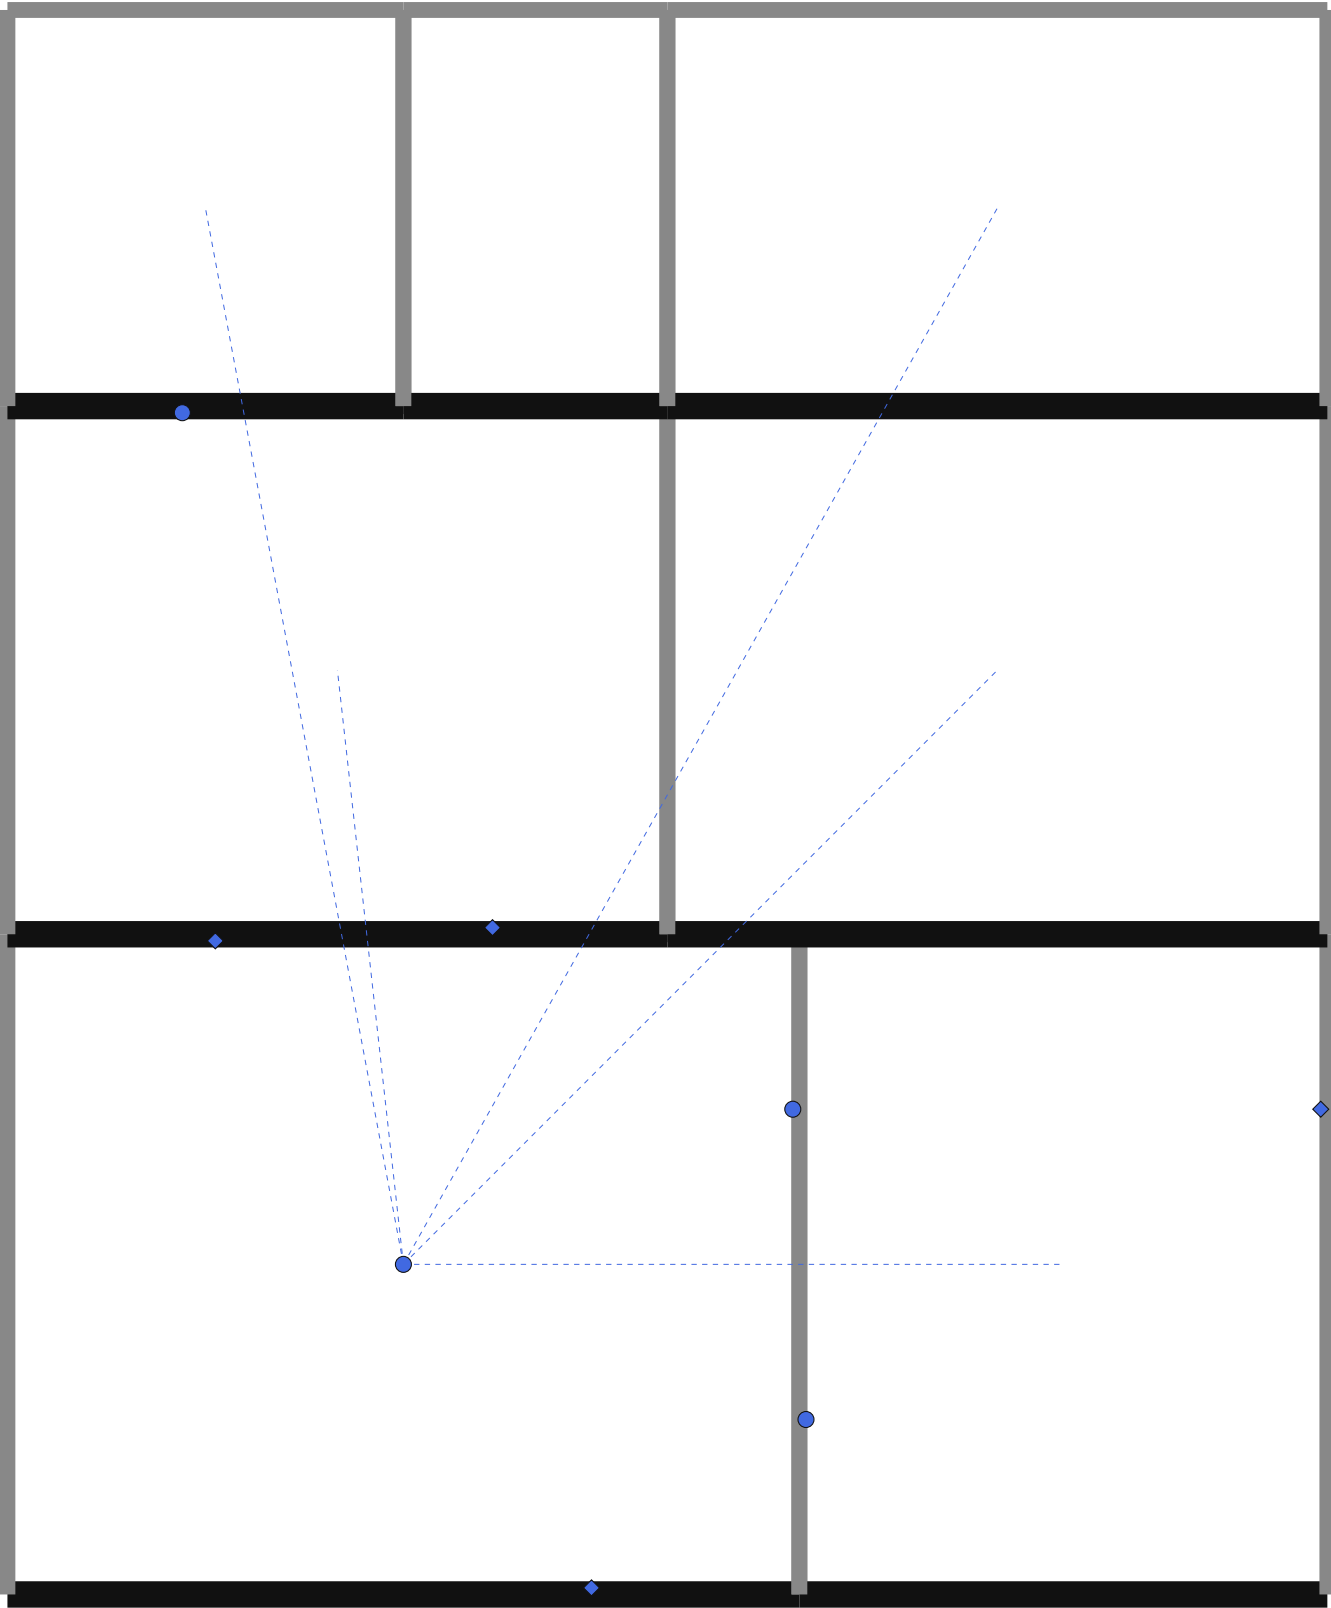

NOMENCLATURE — 520 LCU — Courants Faibles

- Prise RJ45: 4
- Prise TV: 3
- Point d'accès WiFi: 1


TIJAN AI Bureau d'Études Automatisé	Résidence Papa Oumar Sakho Dakar, Sénégal	Éch: 1/100 Pl. 59/70
	520 LCU — Courants Faibles — R+3	
Date: 06/05/2026	Réf: 1711	BIM v.LCU-059 Phase: APD

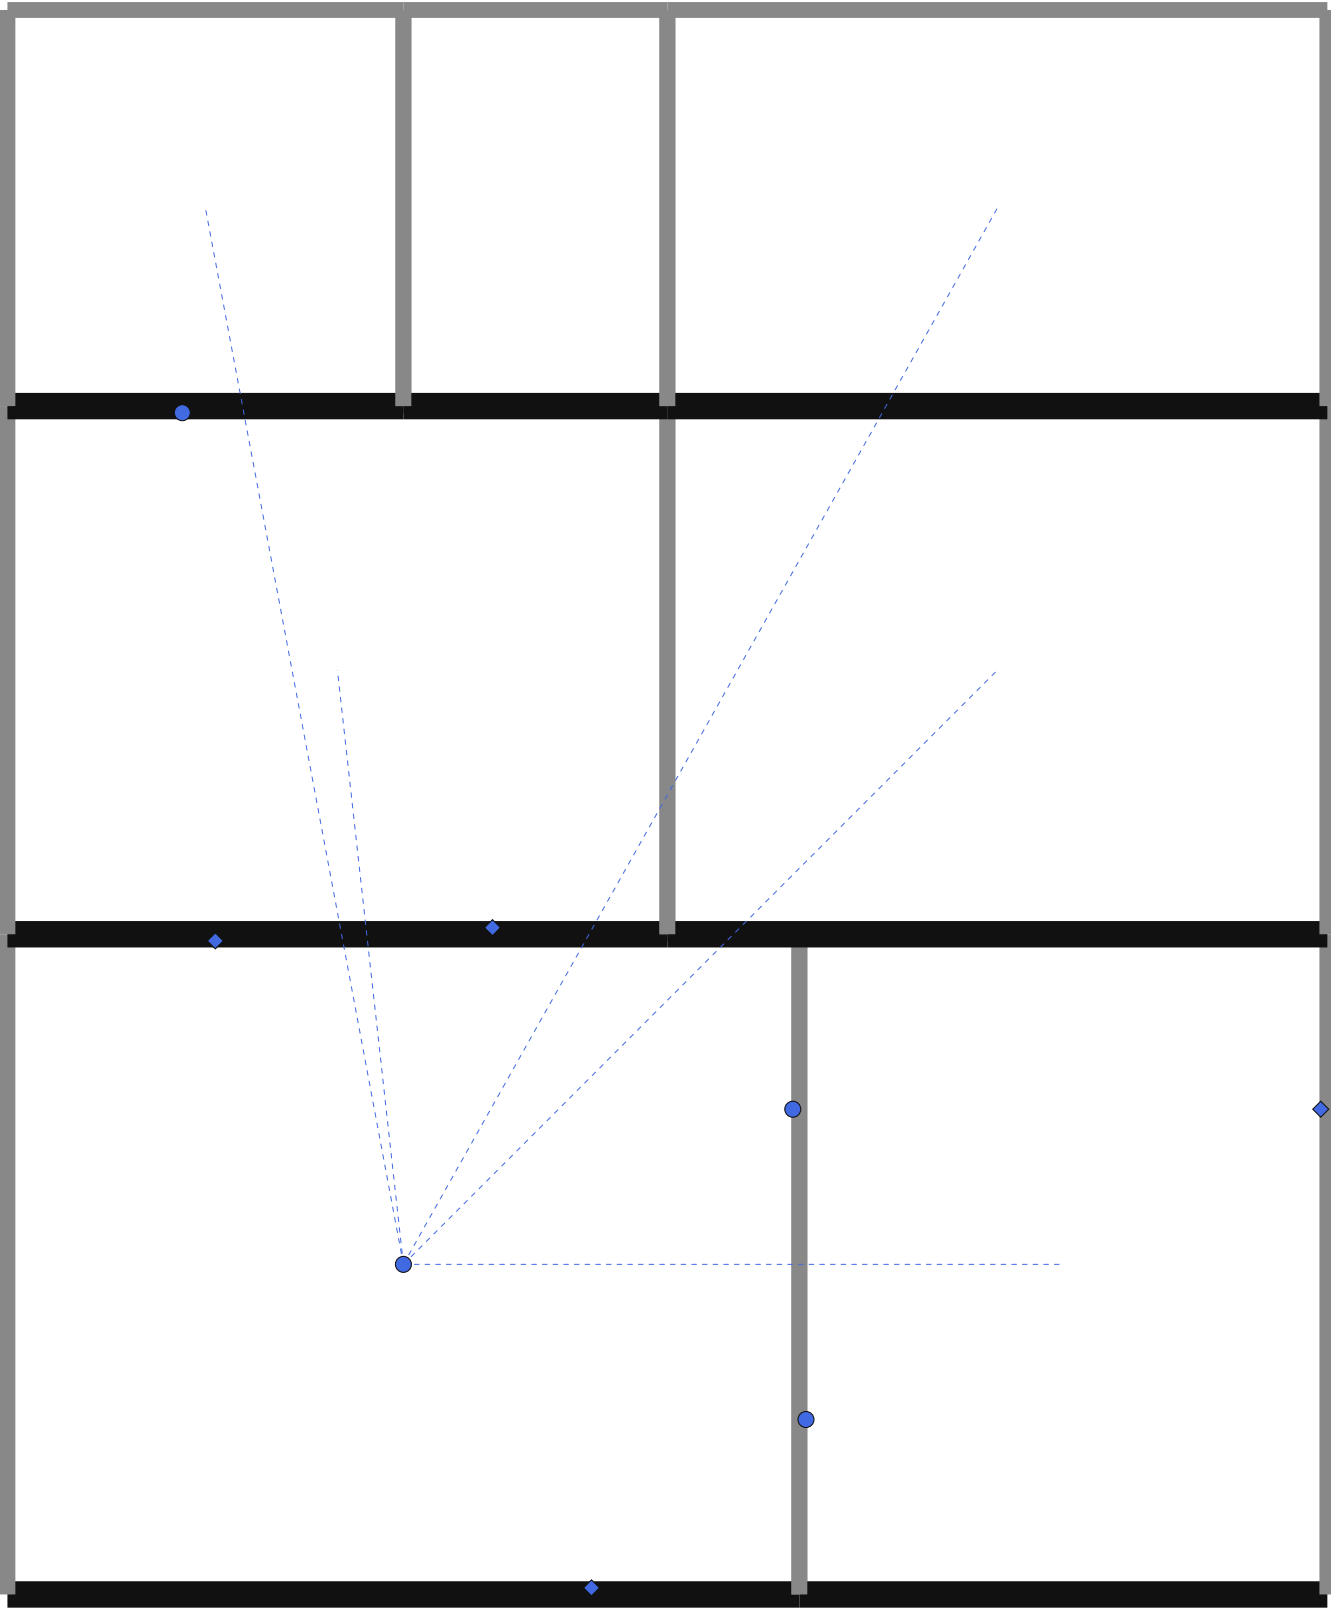


NOMENCLATURE — 520 LCU — Courants Faibles

- Prise RJ45: 4
- Prise TV: 3
- Point d'accès WiFi: 1

TIJAN AI Bureau d'Études Automatisé	Résidence Papa Oumar Sakho Dakar, Sénégal	Éch: 1/100 Pl. 60/70
	520 LCU — Courants Faibles — R+4	
Date: 06/05/2026	Réf: 1711	BIM v.LCU-060 Phase: APD

 

TIJAN AI Bureau d'Études Automatisé	Résidence Papa Oumar Sakho Dakar, Sénégal	Éch: 1/100 Pl. 61/70
	113 RC — Faux Plafond — RDC	
Date: 06/05/2026	Réf: 1711	BIM VRC-061 Phase: APD

 

TIJAN AI

Bureau d'Études Automatisé

Résidence Papa Oumar Sakho

Dakar, Sénégal

Éch: 1/100

Pl. 62/70


113 RC — Faux Plafond — R+1

Date: 06/05/2026


Réf: 1711

BIM VRC-062


Phase: APD

 

TIJAN AI Bureau d'Études Automatisé	Résidence Papa Oumar Sakho Dakar, Sénégal	Éch: 1/100 Pl. 63/70
	113 RC — Faux Plafond — R+2	
Date: 06/05/2026	Réf: 1711	BIM VRC-063 Phase: APD

 

TIJAN AI Bureau d'Études Automatisé	Résidence Papa Oumar Sakho Dakar, Sénégal	Éch: 1/100 Pl. 64/70
	113 RC — Faux Plafond — R+3	
Date: 06/05/2026	Réf: 1711	BIM VRC-064 Phase: APD

 


TIJAN AI Bureau d'Études Automatisé	Résidence Papa Oumar Sakho Dakar, Sénégal	Éch: 1/100 Pl. 65/70
	113 RC — Faux Plafond — R+4	
Date: 06/05/2026	Réf: 1711	BIM VRC-065 Phase: APD

001 SYN — Synthèse — RDC

LÉGENDE RÉSEAUX

- EF — Eau Froide
- EC — Eau Chaude
- EU — Eaux Usées
- CLIM — Réfrigérant
- VMC — Extraction
- HCU — Courants Forts
- LCU — Courants Faibles
- SPK — Sprinkler

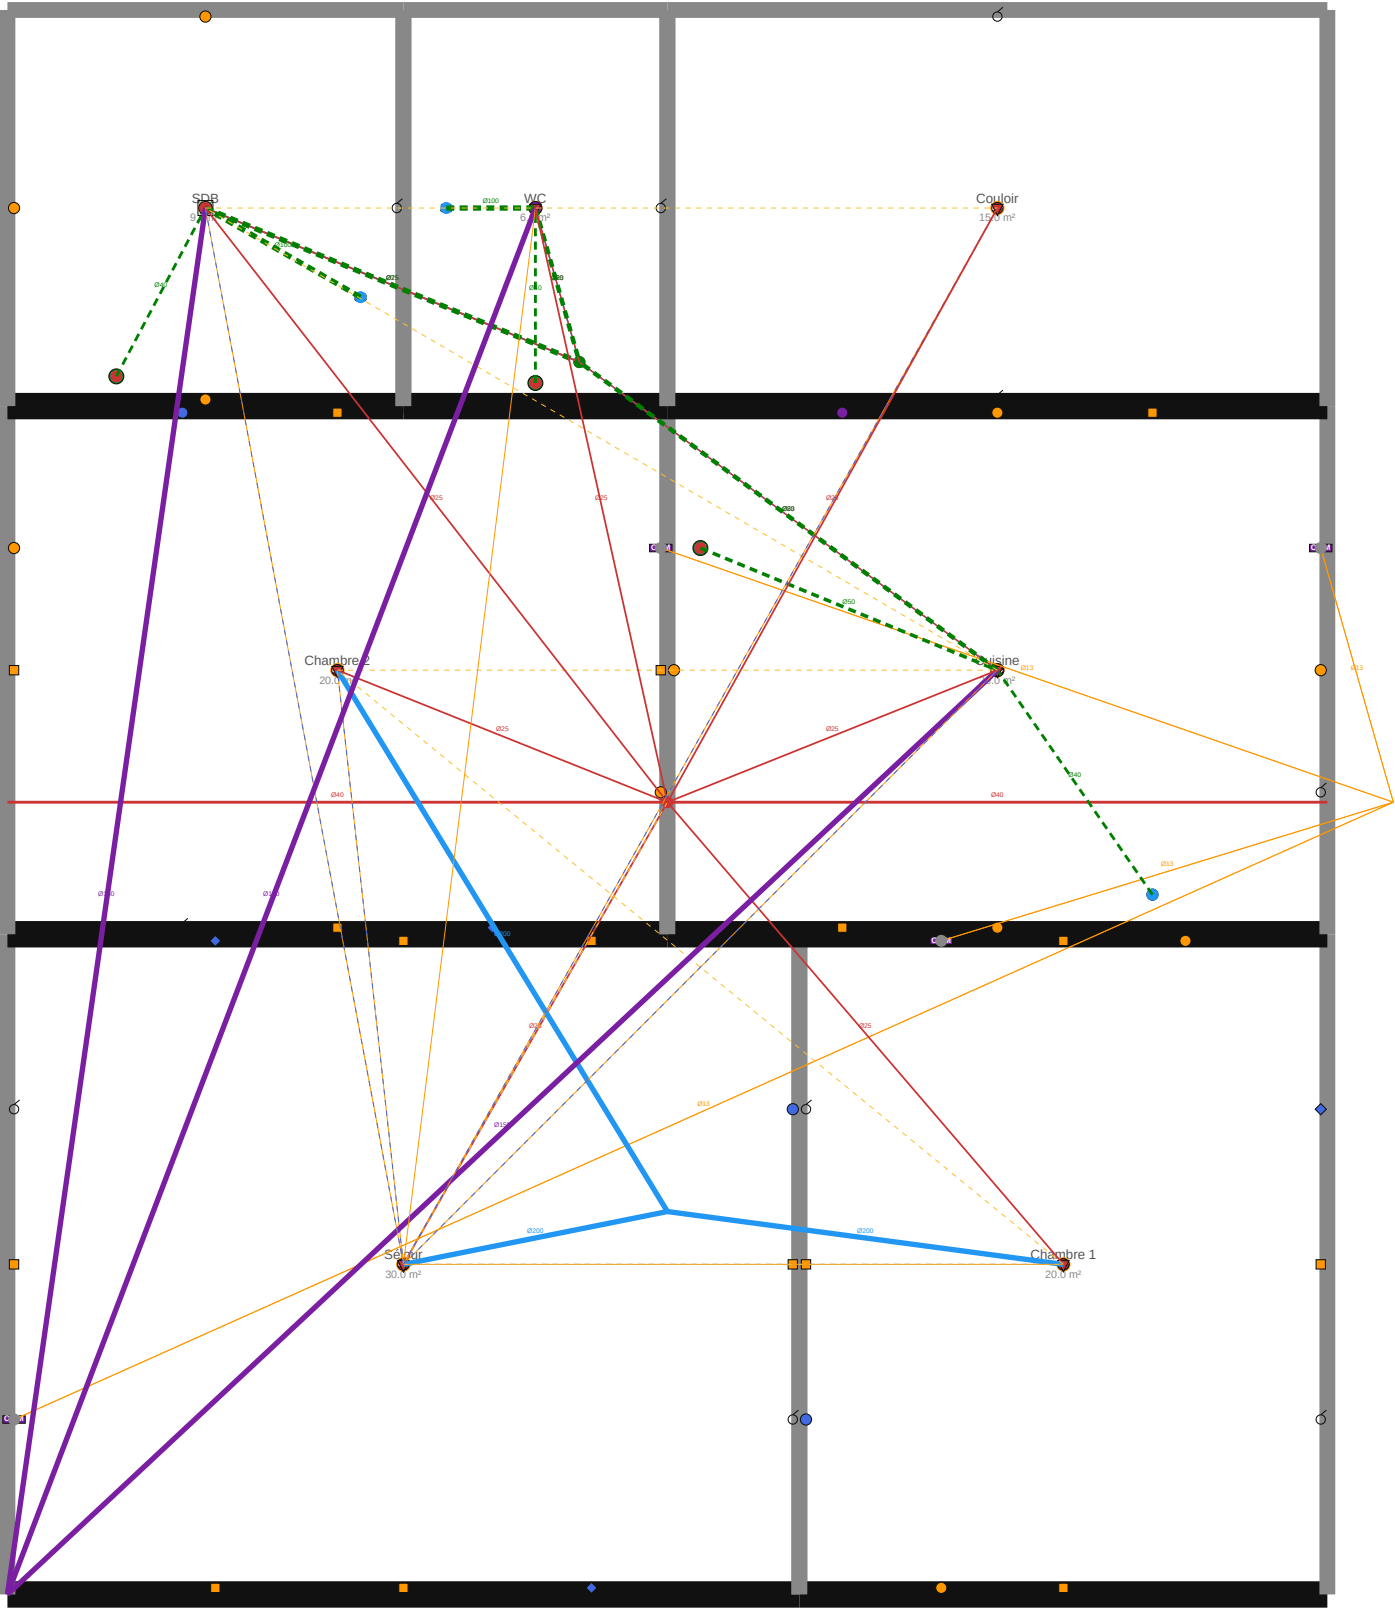

TIJAN AI Bureau d'Études Automatisé	Résidence Papa Oumar Sakho Dakar, Sénégal	Éch: 1/100 Pl. 66/70
	001 SYN — Synthèse — RDC	
Date: 06/05/2026	Réf: 1711	BIM vSYN-066 Phase: APD

001 SYN — Synthèse — R+1

LÉGENDE RÉSEAUX

- EF — Eau Froide
- EC — Eau Chaude
- EU — Eaux Usées
- CLIM — Réfrigérant
- VMC — Extraction
- HCU — Courants Forts
- LCU — Courants Faibles
- SPK — Sprinkler




TIJAN AI Bureau d'Études Automatisé	Résidence Papa Oumar Sakho Dakar, Sénégal	Éch: 1/100 Pl. 67/70
	001 SYN — Synthèse — R+1	
Date: 06/05/2026	Réf: 1711	BIM vSYN-067 Phase: APD

001 SYN — Synthèse — R+2

LÉGENDE RÉSEAUX

- EF — Eau Froide
- EC — Eau Chaude
- EU — Eaux Usées
- CLIM — Réfrigérant
- VMC — Extraction
- HCU — Courants Forts
- LCU — Courants Faibles
- SPK — Sprinkler

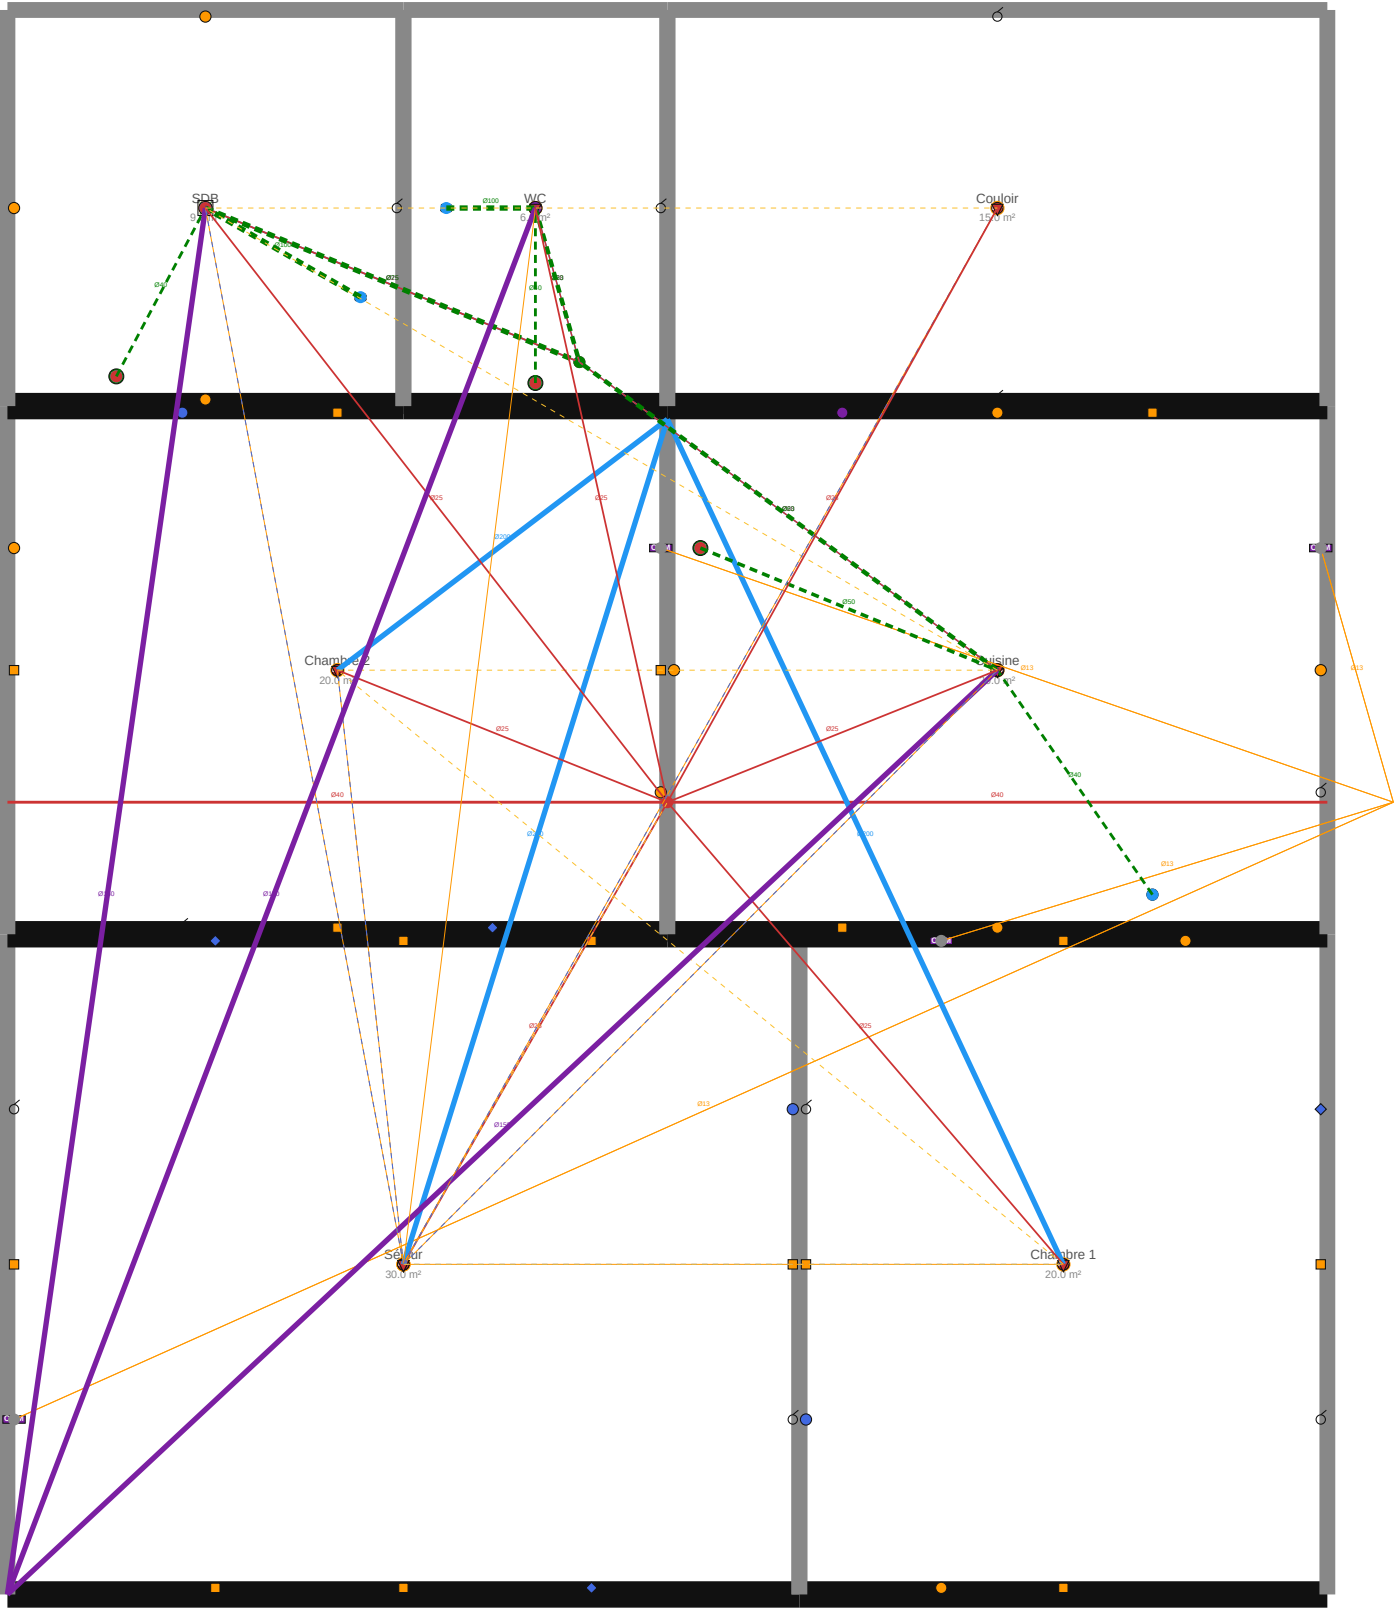


TIJAN AI Bureau d'Études Automatisé	Résidence Papa Oumar Sakho Dakar, Sénégal	Éch: 1/100 Pl. 68/70
	001 SYN — Synthèse — R+2	
Date: 06/05/2026	Réf: 1711	BIM vSYN-068 Phase: APD

001 SYN — Synthèse — R+3

LÉGENDE RÉSEAUX

- EF — Eau Froide
- EC — Eau Chaude
- EU — Eaux Usées
- CLIM — Réfrigérant
- VMC — Extraction
- HCU — Courants Forts
- LCU — Courants Faibles
- SPK — Sprinkler

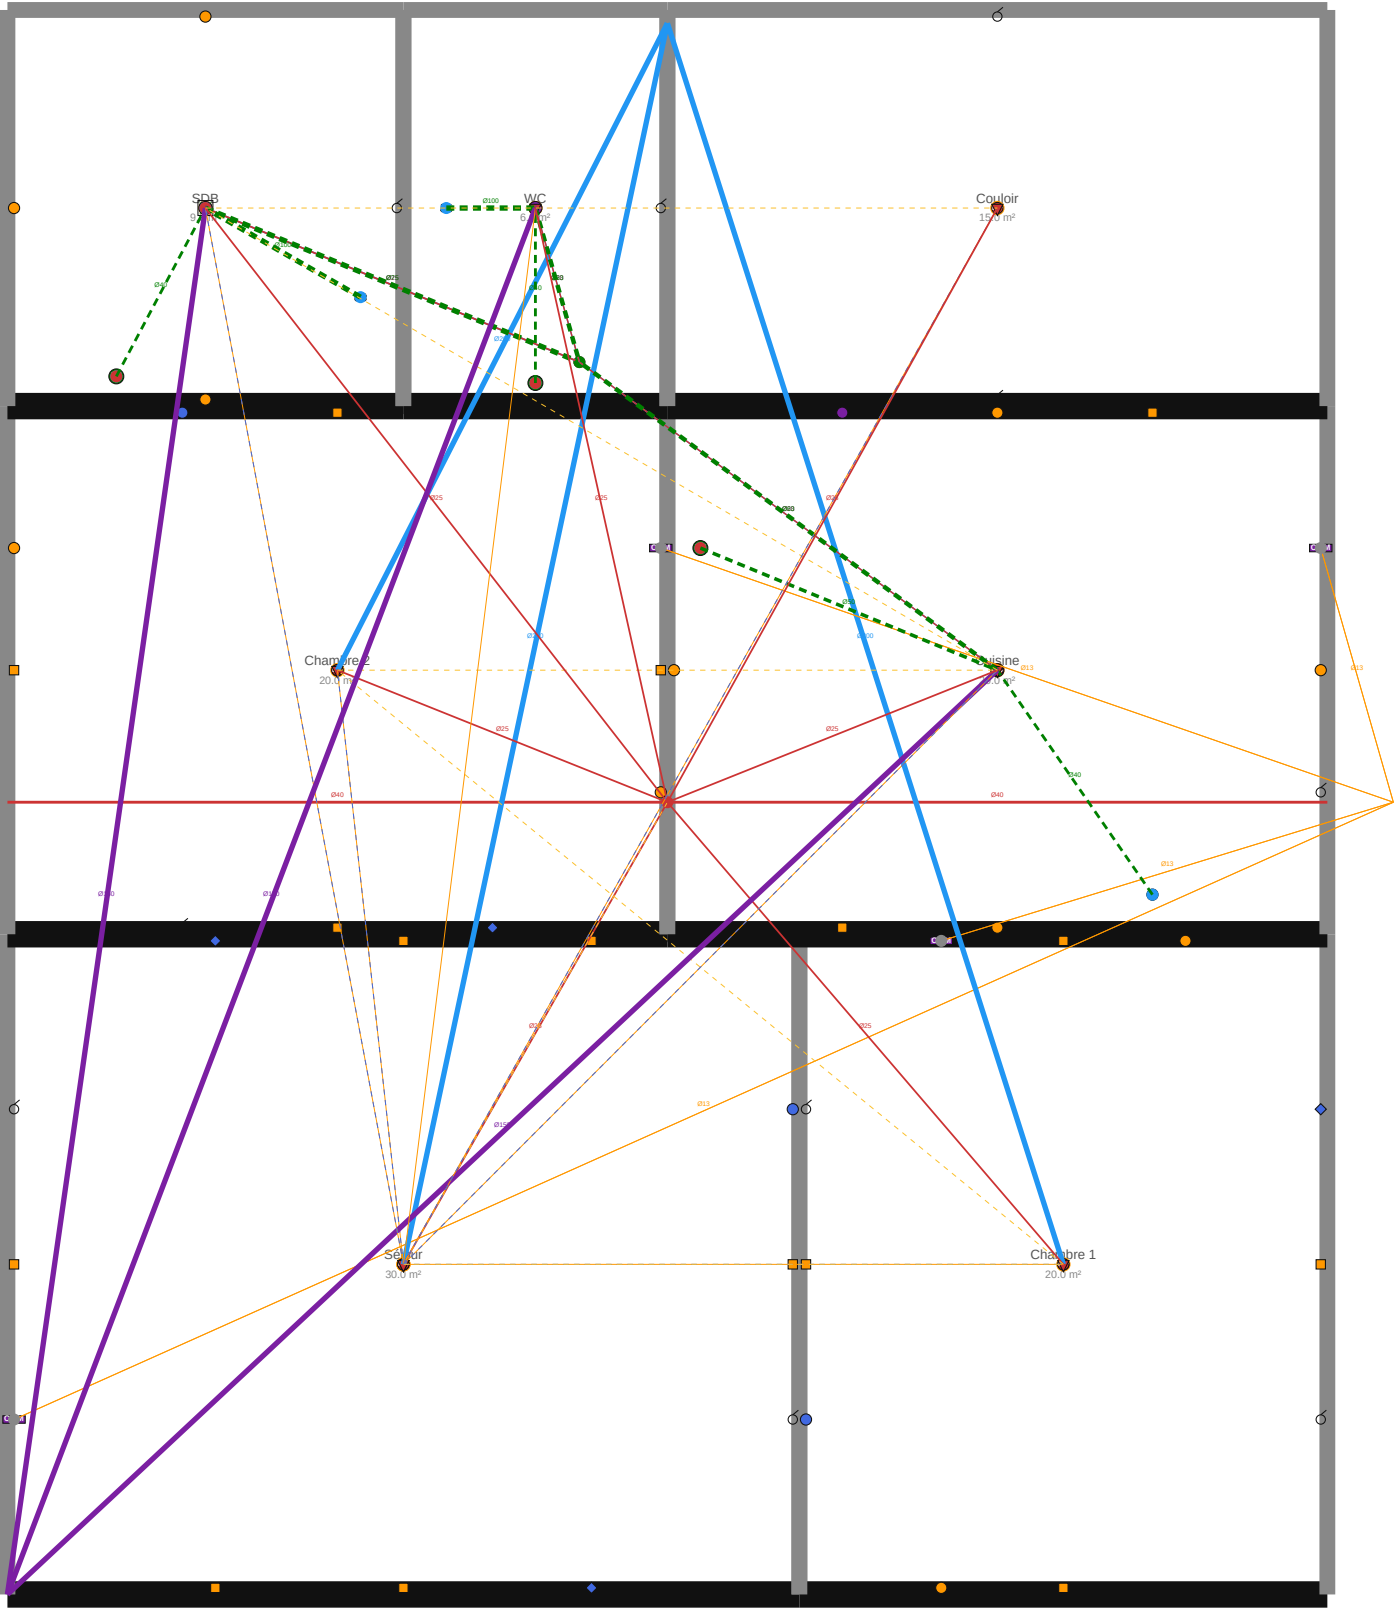


TIJAN AI Bureau d'Études Automatisé	Résidence Papa Oumar Sakho Dakar, Sénégal	Éch: 1/100 Pl. 69/70
	001 SYN — Synthèse — R+3	
Date: 06/05/2026	Réf: 1711	BIM vSYN-069 Phase: APD

001 SYN — Synthèse — R+4

LÉGENDE RÉSEAUX

- EF — Eau Froide
- EC — Eau Chaude
- EU — Eaux Usées
- CLIM — Réfrigérant
- VMC — Extraction
- HCU — Courants Forts
- LCU — Courants Faibles
- SPK — Sprinkler

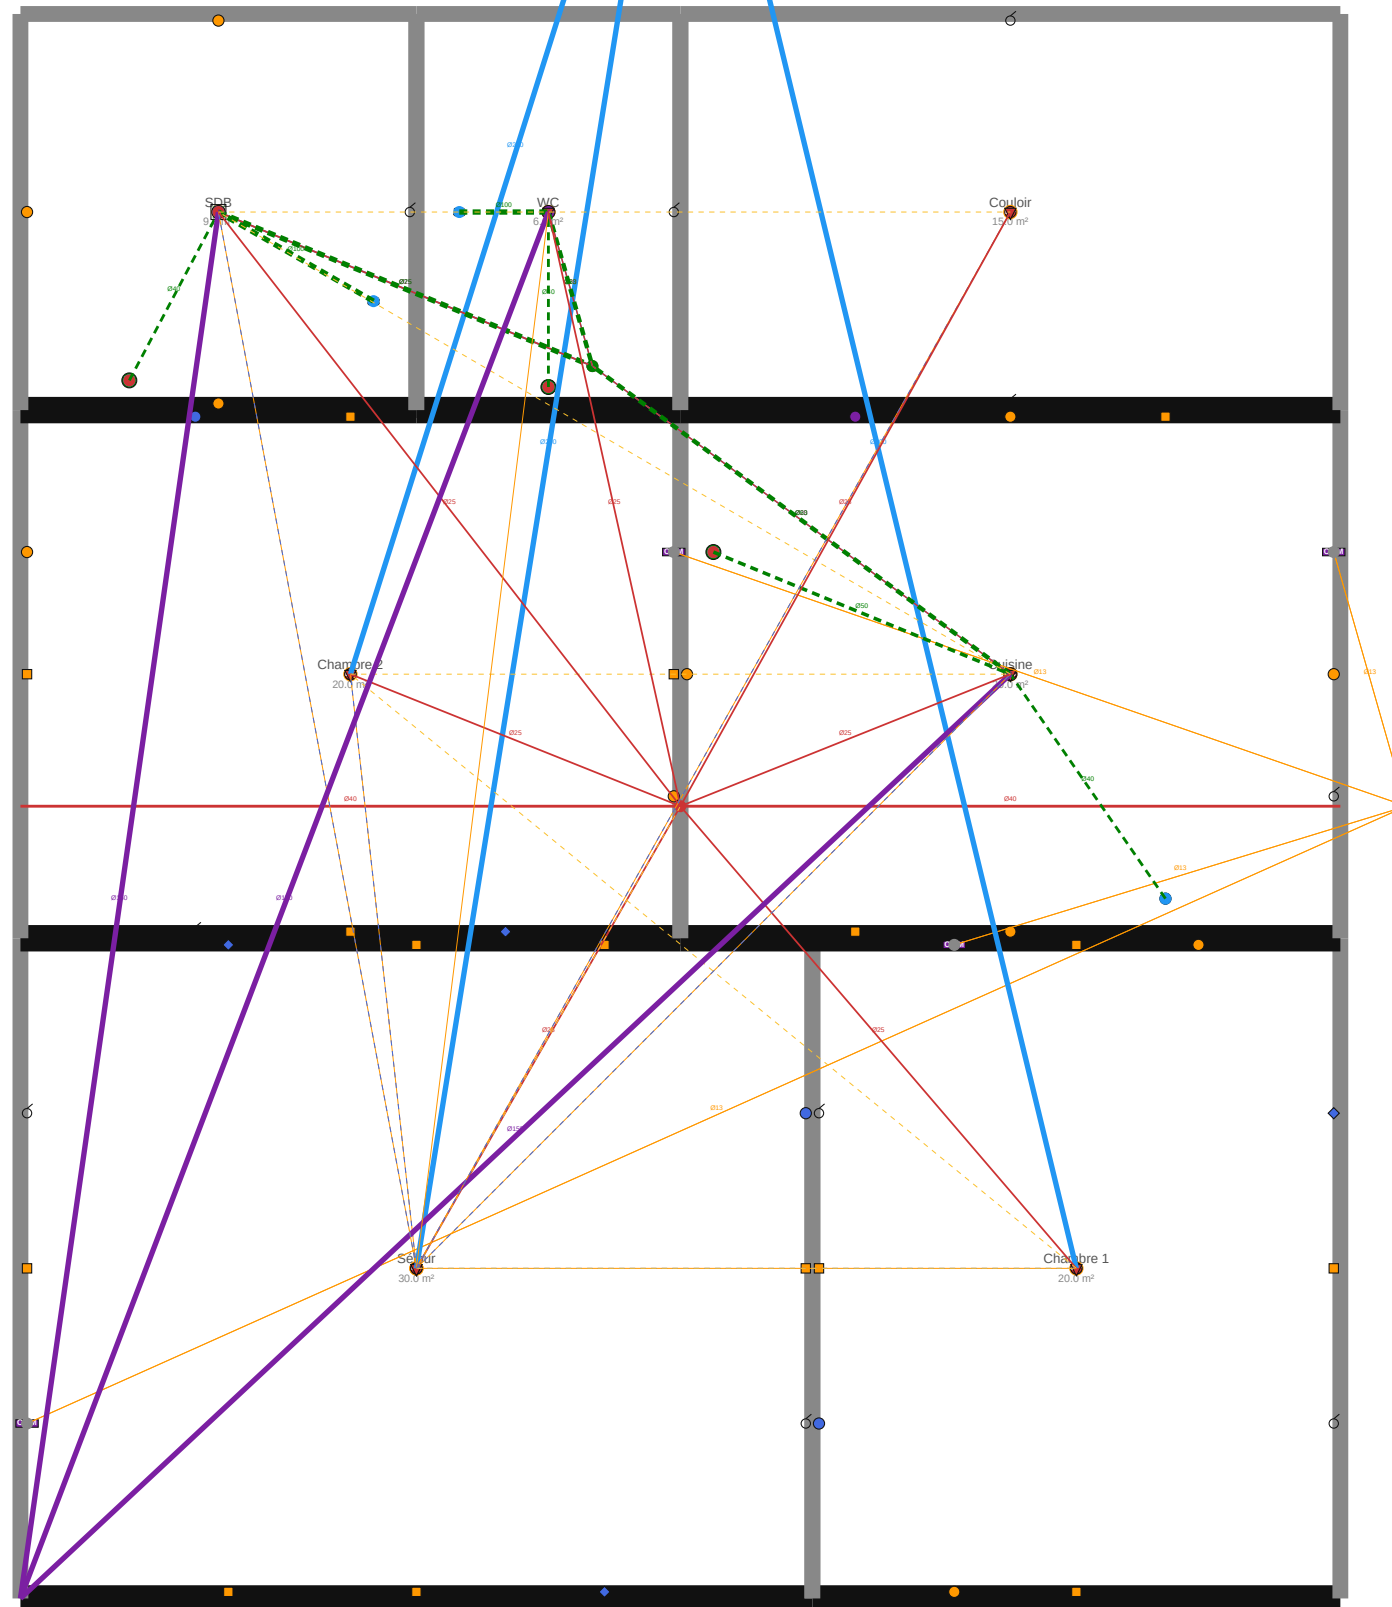

TIJAN AI Bureau d'Études Automatisé	Résidence Papa Oumar Sakho Dakar, Sénégal	Éch: 1/100 Pl. 70/70
	001 SYN — Synthèse — R+4	
Date: 06/05/2026	Réf: 1711	BIM vSYN-070 Phase: APD