




 

TIJAN AI Bureau d'Études Automatisé	Résidence Papa Oumar Sakho Dakar, Sénégal	Éch: 1/100 Pl. 1/137
	001 ARC — Architecture — Sous-Sol	
Date: 06/05/2026	Réf: 1711	BIM vARC-001 Phase: APD

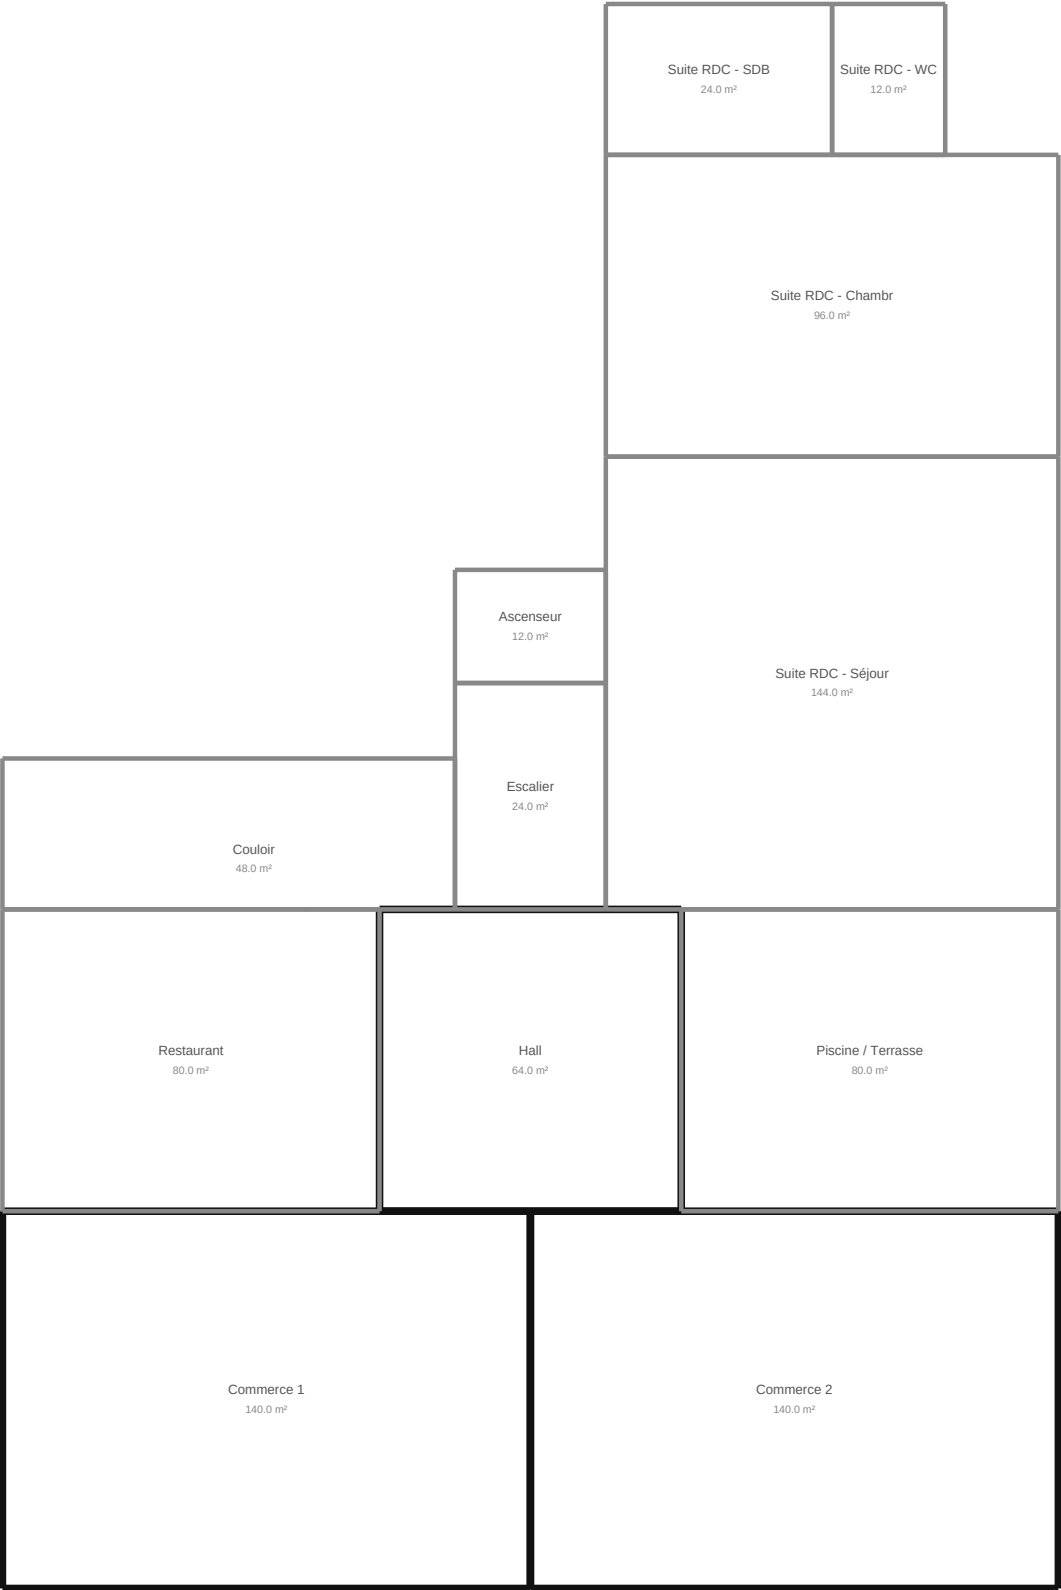

TIJAN AI Bureau d'Études Automatisé	Résidence Papa Oumar Sakho Dakar, Sénégal	Éch: 1/100 Pl. 2/137
	001 ARC — Architecture — RDC	
Date: 06/05/2026	Réf: 1711	BIM vARC-002 Phase: APD

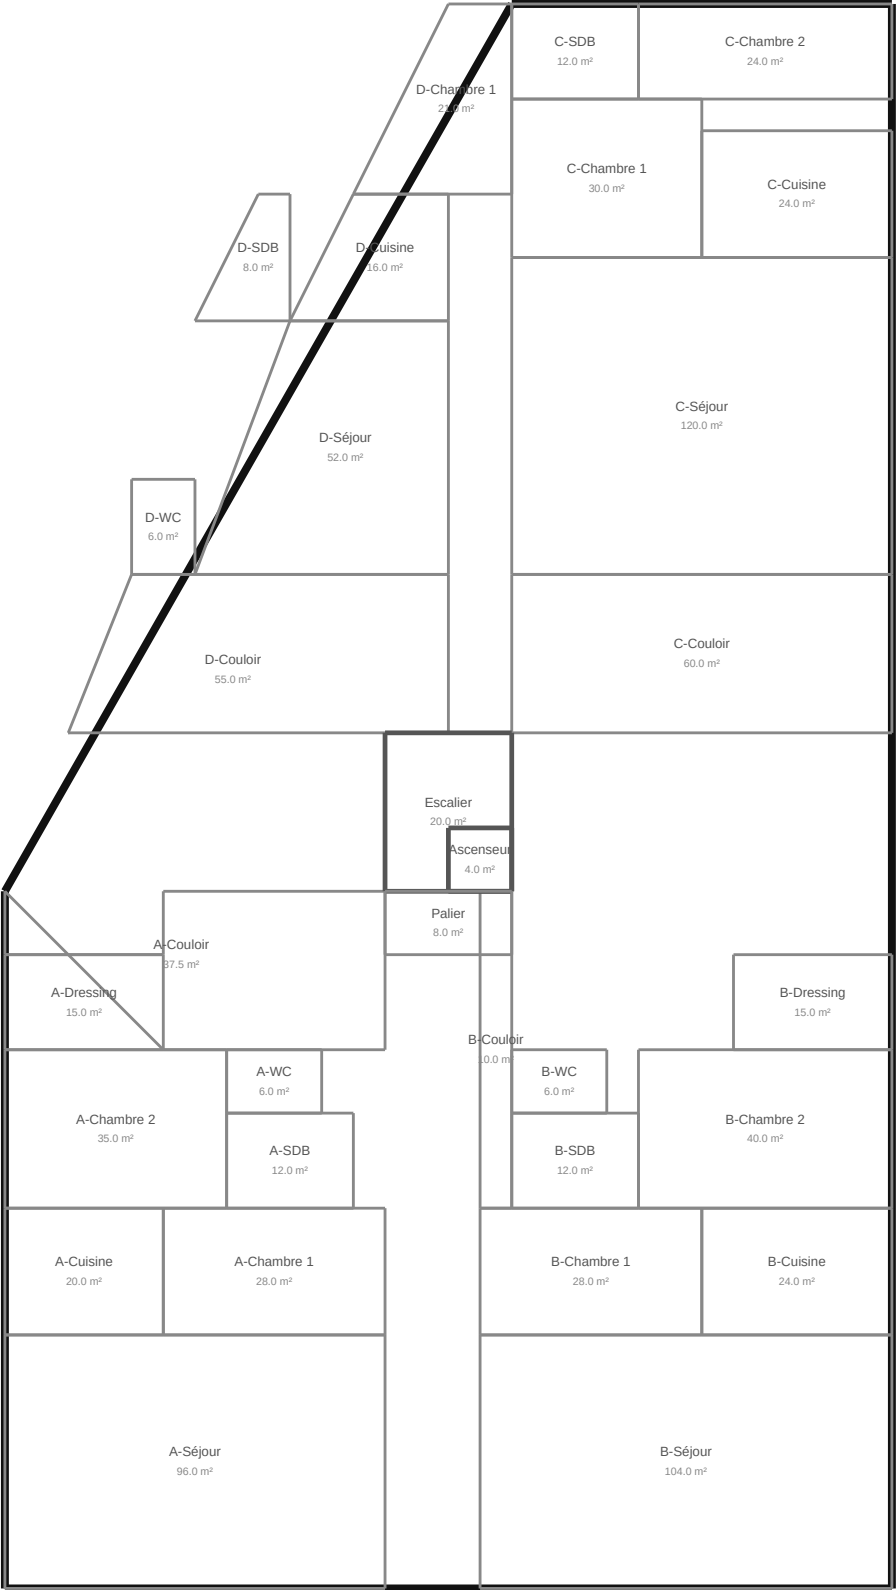

TIJAN AI

Bureau d'Études Automatisé

Résidence Papa Oumar Sakho

Dakar, Sénégal

Éch: 1/100

Pl. 3/137


001 ARC — Architecture — R+1

Date: 06/05/2026

Réf: 1711

BIM vARC-003

Phase: APD

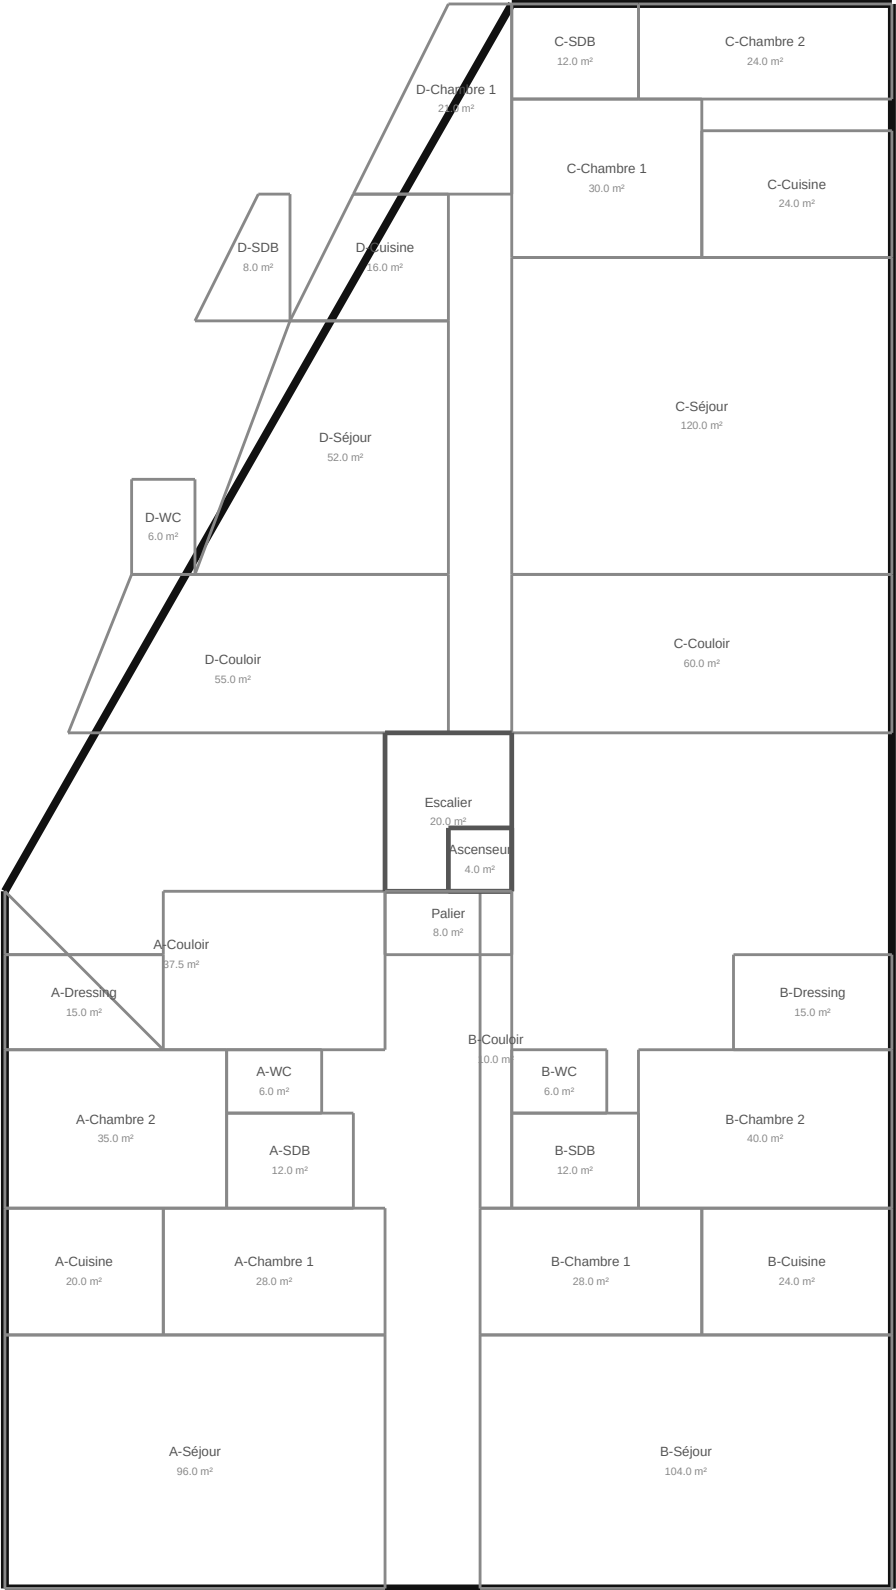

TIJAN AI

Bureau d'Études Automatisé

Résidence Papa Oumar Sakho

Dakar, Sénégal

Éch: 1/100

Pl. 4/137


001 ARC — Architecture — R+2

Date: 06/05/2026

Réf: 1711

BIM vARC-004

Phase: APD

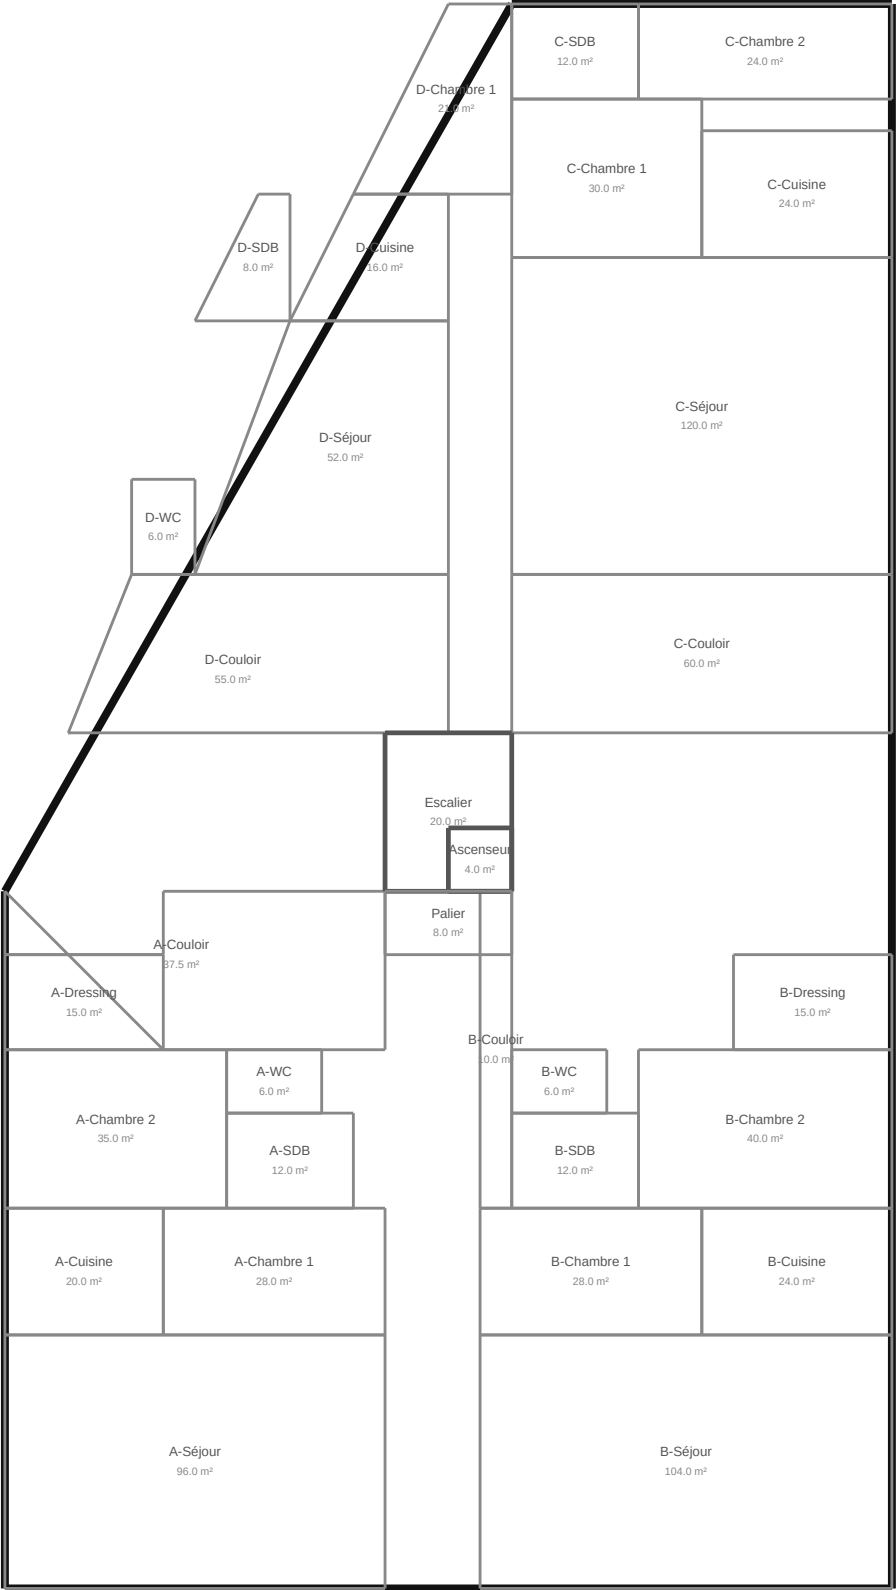

TIJAN AI

Bureau d'Études Automatisé

Résidence Papa Oumar Sakho

Dakar, Sénégal

Éch: 1/100

Pl. 5/137


001 ARC — Architecture — R+3

Date: 06/05/2026

Réf: 1711

BIM vARC-005

Phase: APD

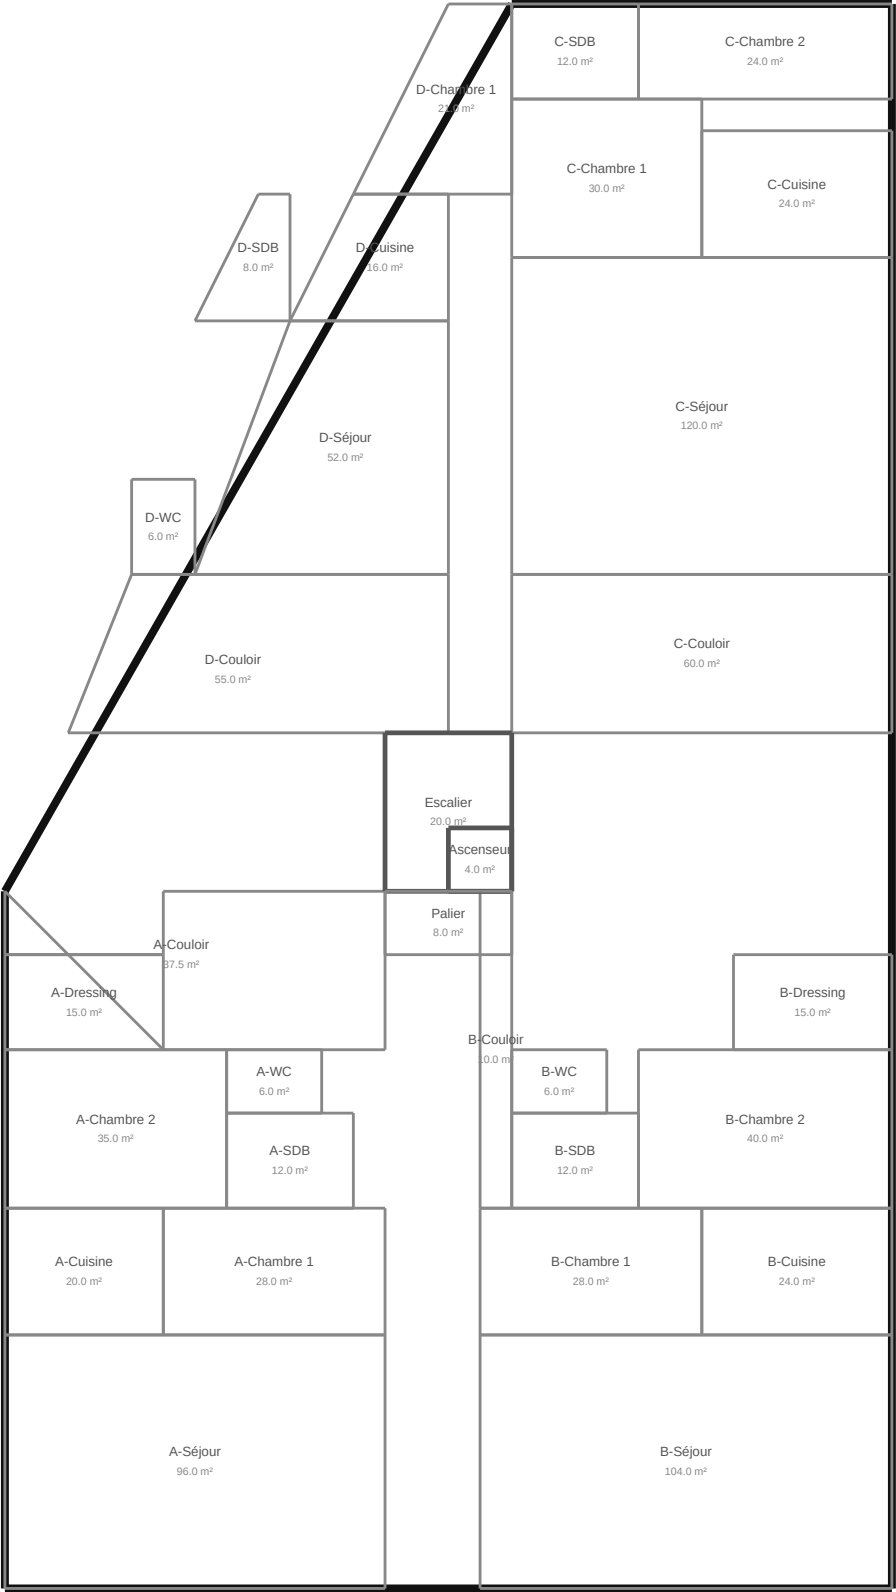

TIJAN AI

Bureau d'Études Automatisé

Résidence Papa Oumar Sakho

Dakar, Sénégal

Éch: 1/100

Pl. 6/137


001 ARC — Architecture — R+4

Date: 06/05/2026

Réf: 1711

BIM vARC-006

Phase: APD

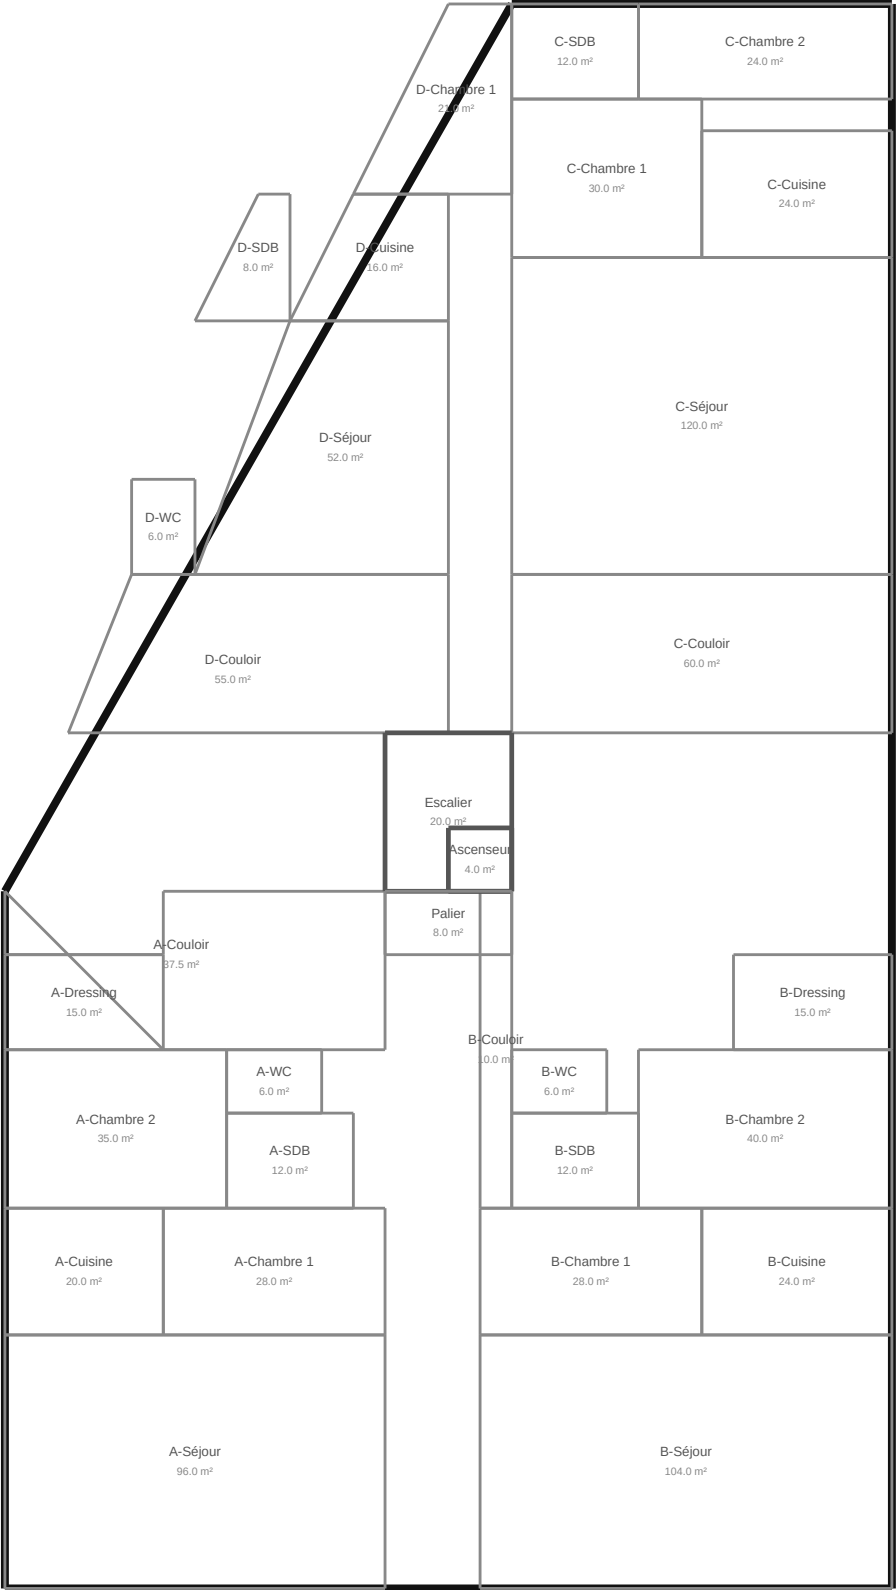

TIJAN AI

Bureau d'Études Automatisé

Résidence Papa Oumar Sakho

Dakar, Sénégal

Éch: 1/100

Pl. 7/137


001 ARC — Architecture — R+5

Date: 06/05/2026

Réf: 1711

BIM vARC-007

Phase: APD

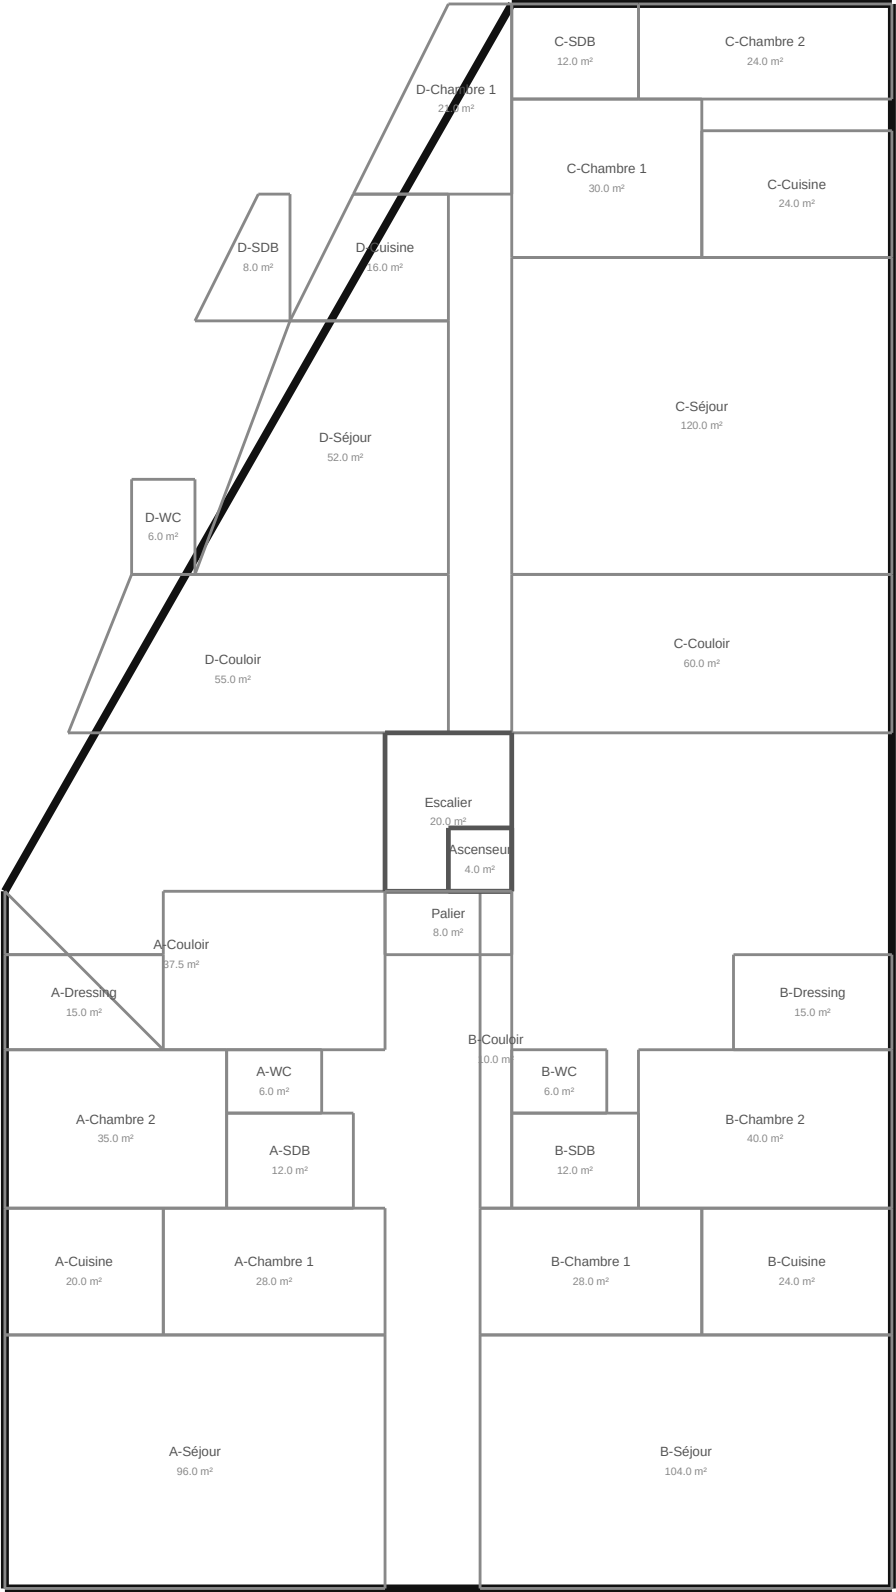

TIJAN AI

Bureau d'Études Automatisé

Résidence Papa Oumar Sakho

Dakar, Sénégal

Éch: 1/100

Pl. 8/137


001 ARC — Architecture — R+6

Date: 06/05/2026

Réf: 1711

BIM vARC-008

Phase: APD

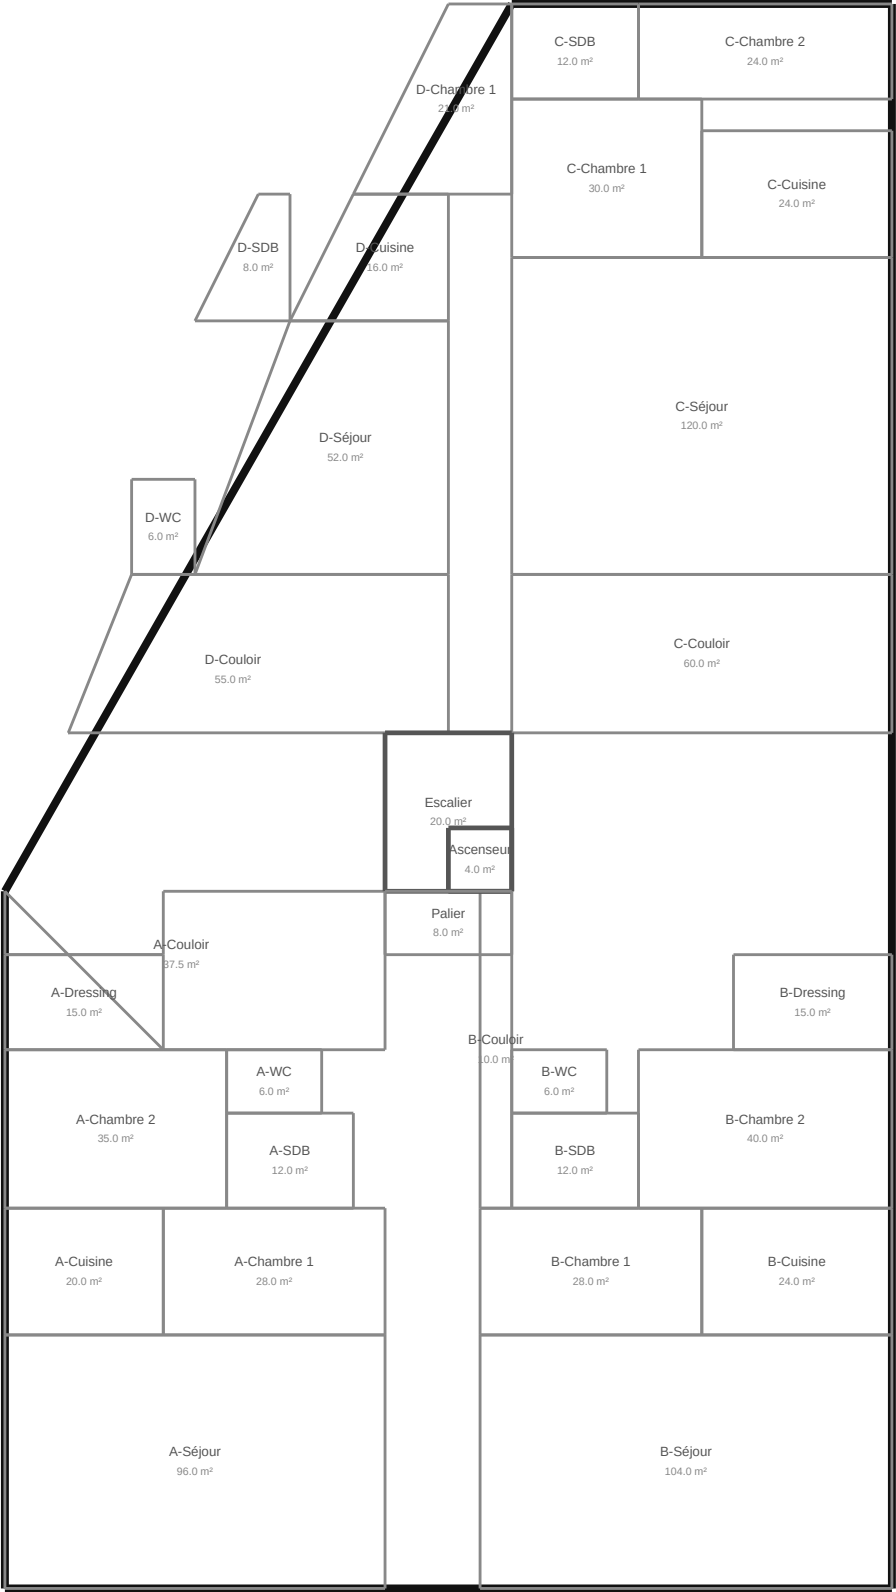

TIJAN AI

Bureau d'Études Automatisé

Résidence Papa Oumar Sakho

Dakar, Sénégal

Éch: 1/100

Pl. 9/137


001 ARC — Architecture — R+7

Date: 06/05/2026


Réf: 1711

BIM vARC-009


Phase: APD

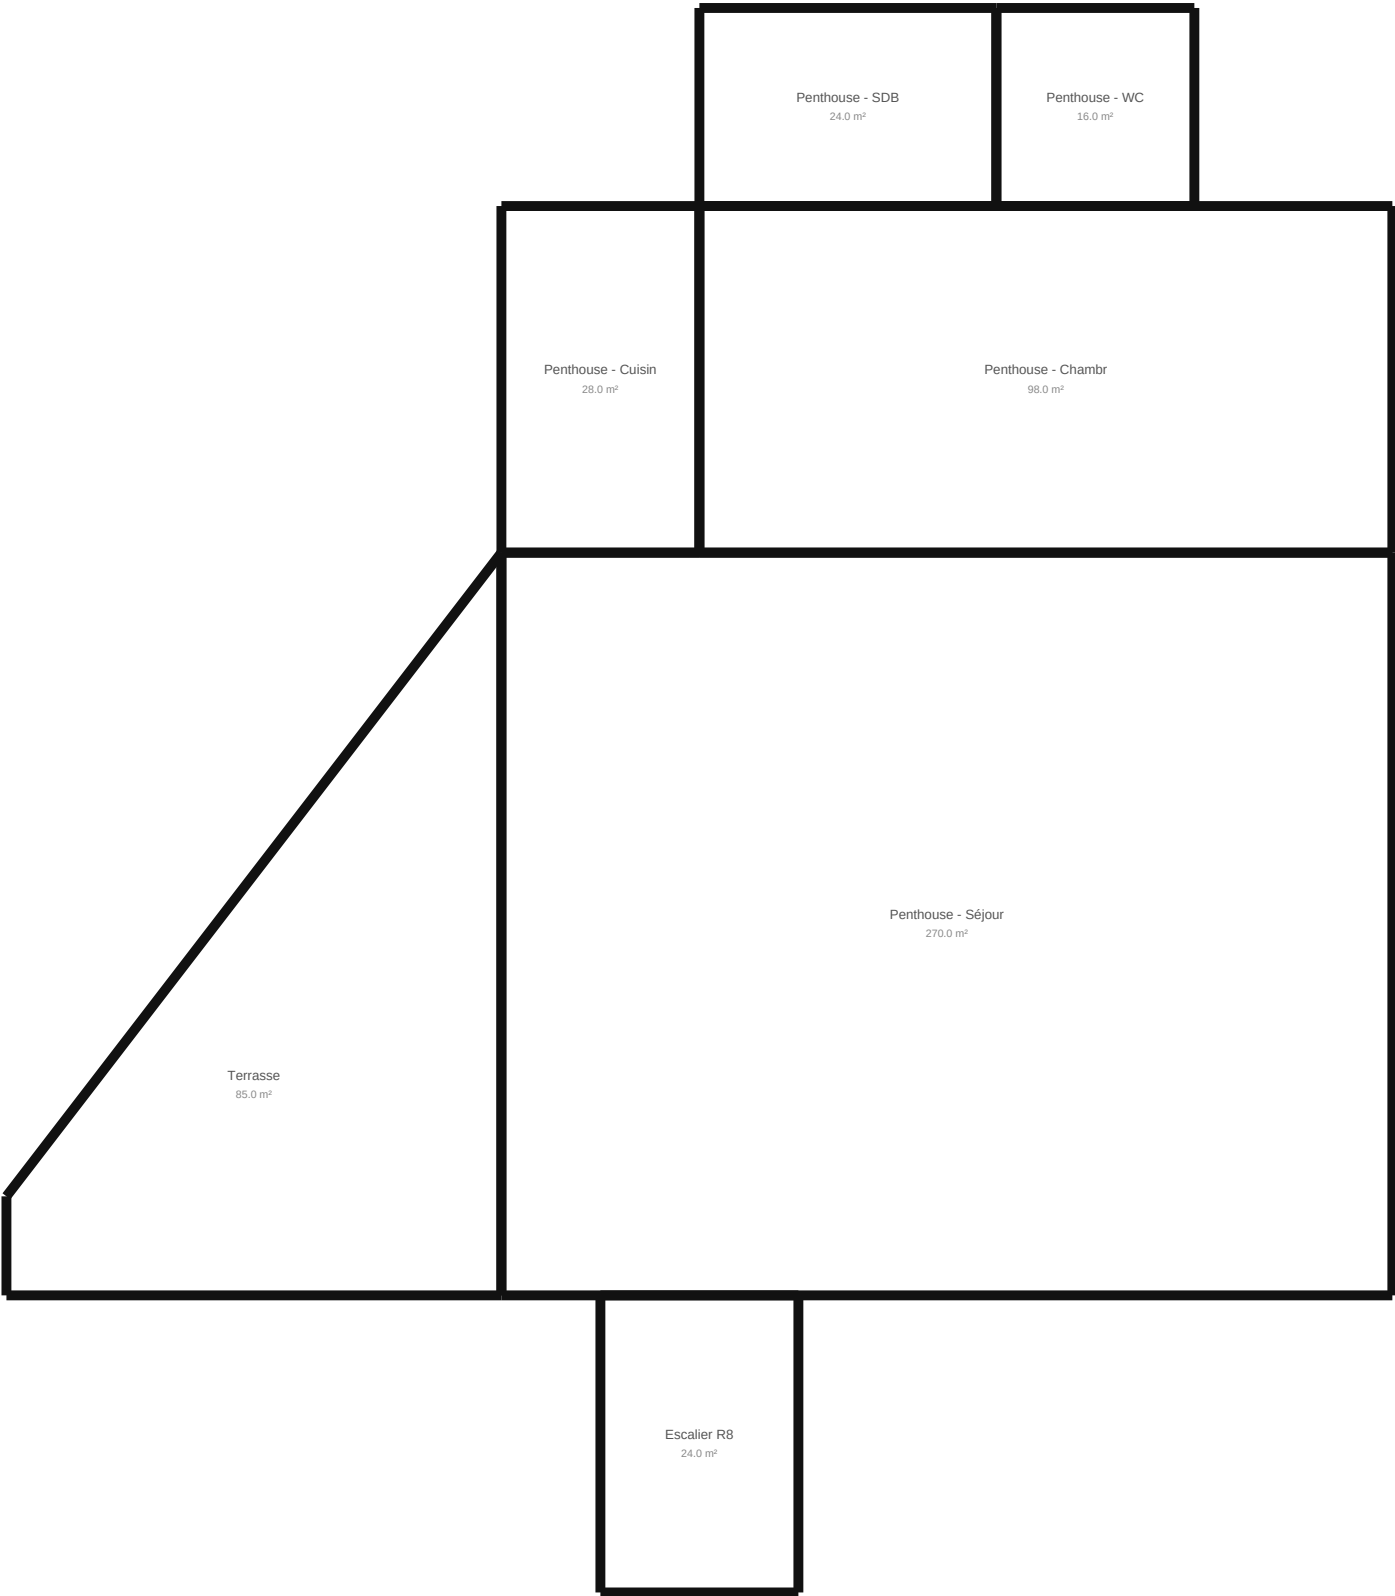


TIJAN AI Bureau d'Études Automatisé	Résidence Papa Oumar Sakho Dakar, Sénégal	Éch: 1/100 Pl. 10/137
	001 ARC — Architecture — R+8	
Date: 06/05/2026	Réf: 1711	BIM vARC-010 Phase: APD

 

TIJAN AI Bureau d'Études Automatisé	Résidence Papa Oumar Sakho Dakar, Sénégal	Éch: 1/100 Pl. 11/137
	200 STR — Coffrage — Sous-Sol	
Date: 06/05/2026	Réf: 1711	BIM vSTR-011 Phase: APD

 

TIJAN AI Bureau d'Études Automatisé	Résidence Papa Oumar Sakho Dakar, Sénégal	Éch: 1/100 Pl. 12/137
	200 STR — Coffrage — RDC	
Date: 06/05/2026	Réf: 1711	BIM vSTR-012 Phase: APD

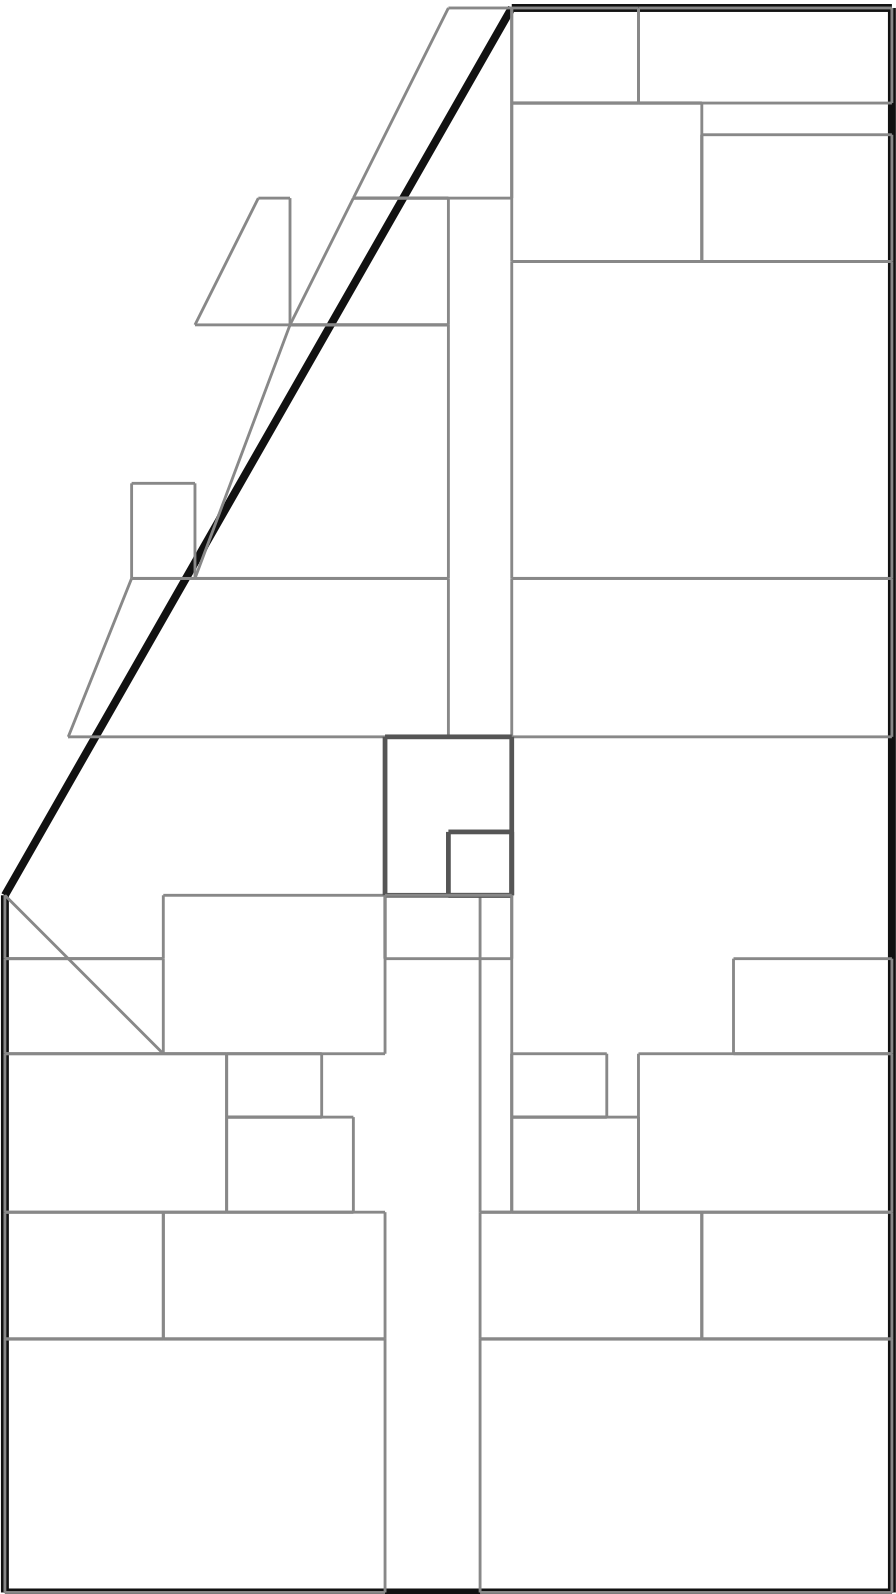

TIJAN AI

Bureau d'Études Automatisé

Résidence Papa Oumar Sakho

Dakar, Sénégal

Éch: 1/100

Pl. 13/137


200 STR — Coffrage — R+1

Date: 06/05/2026


Réf: 1711

BIM vSTR-013


Phase: APD

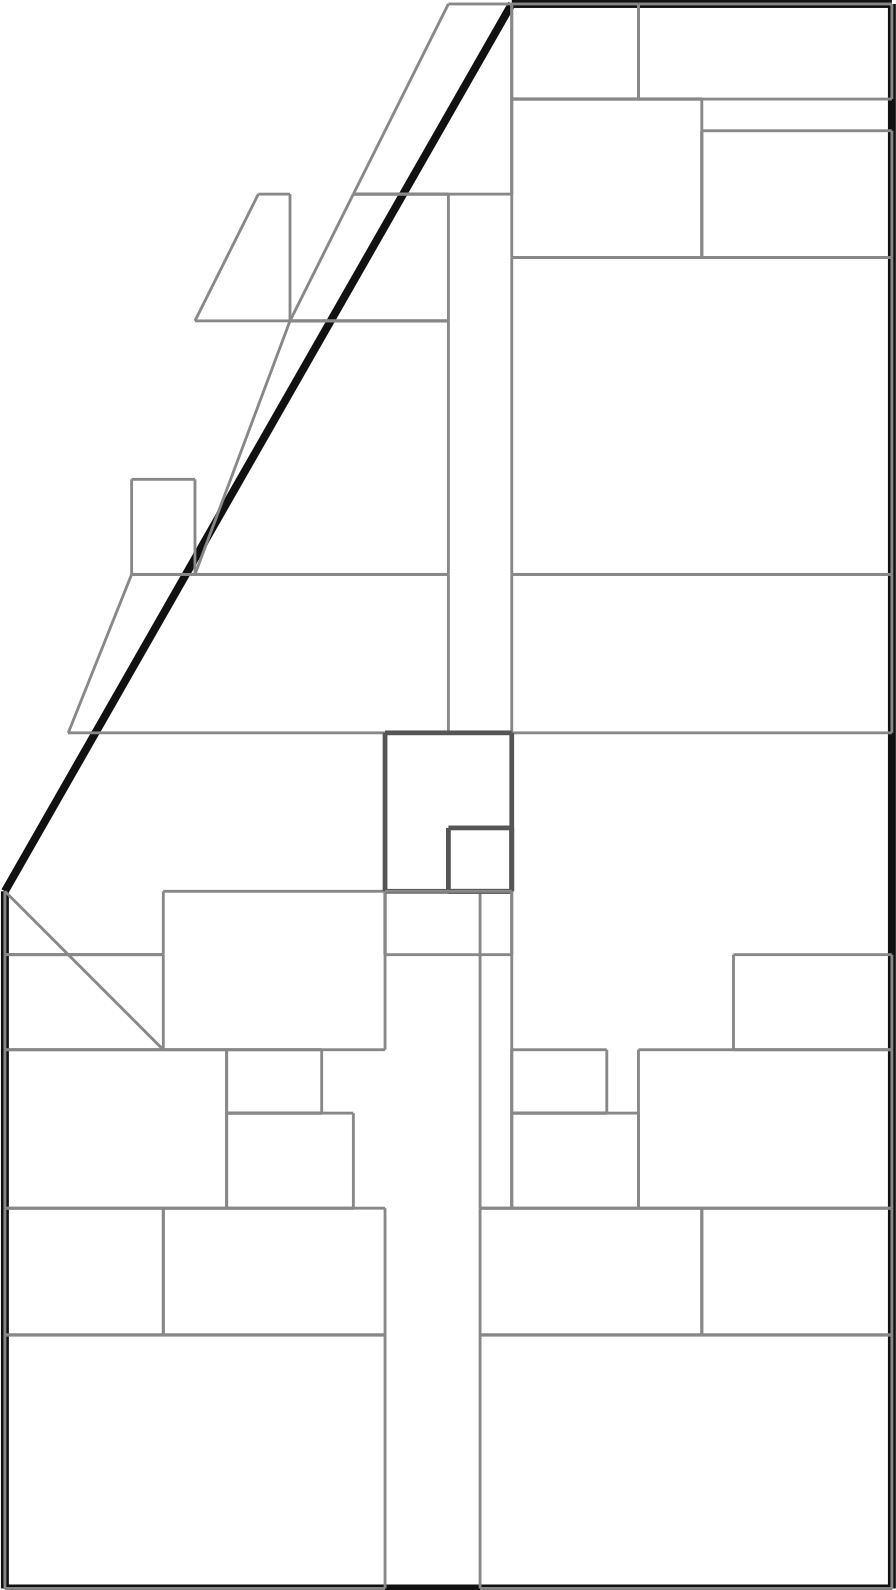


TIJAN AI Bureau d'Études Automatisé	Résidence Papa Oumar Sakho Dakar, Sénégal	Éch: 1/100 Pl. 14/137
	200 STR — Coffrage — R+2	
Date: 06/05/2026	Réf: 1711	BIM vSTR-014 Phase: APD

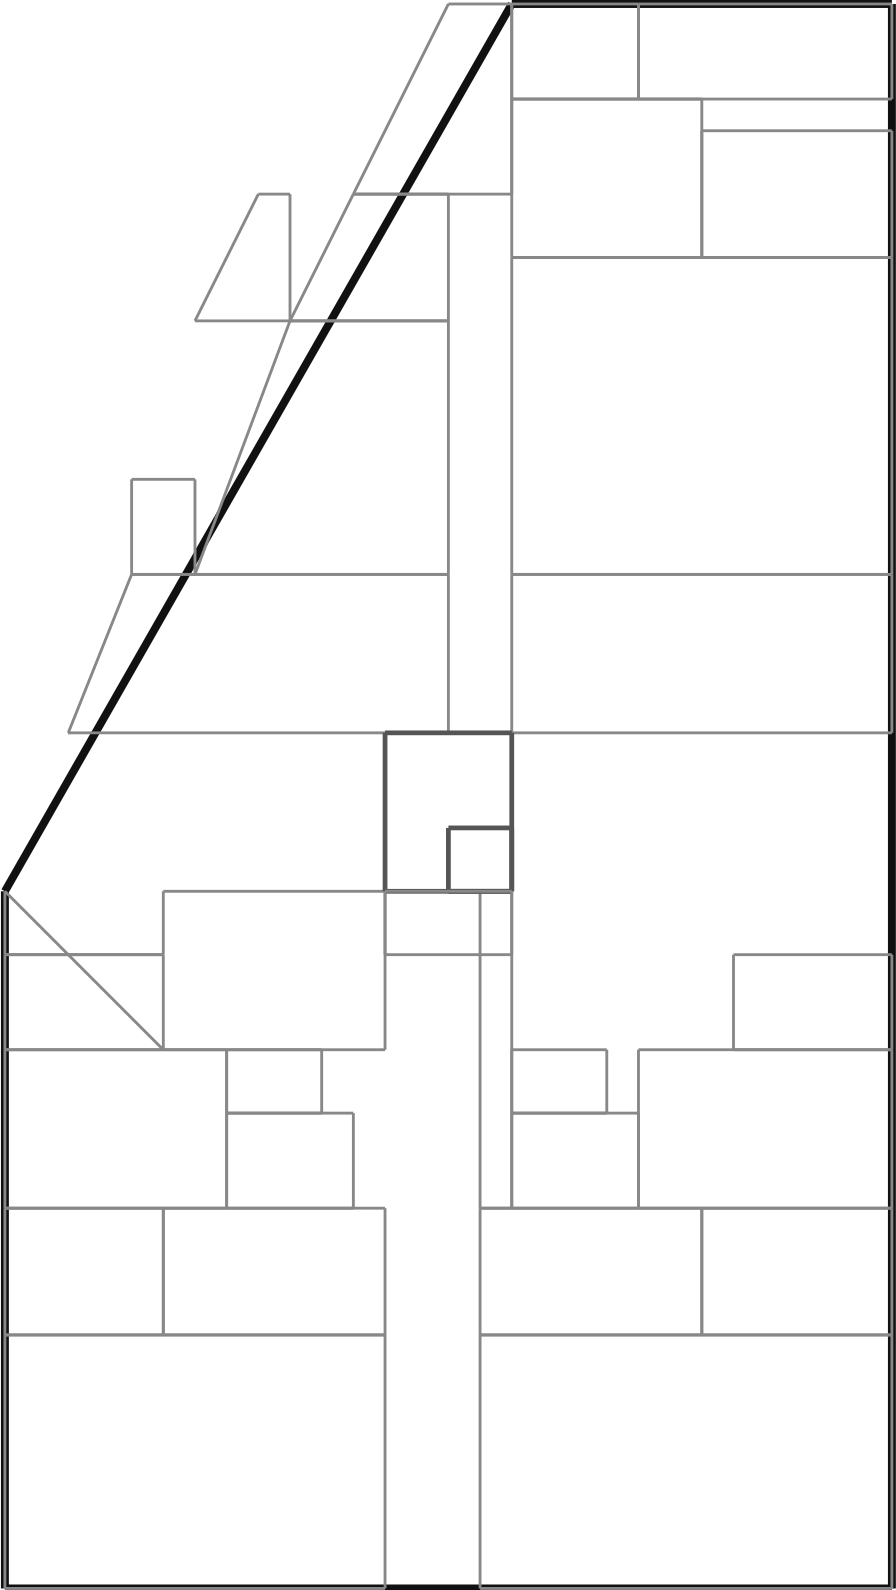


TIJAN AI Bureau d'Études Automatisé	Résidence Papa Oumar Sakho Dakar, Sénégal	Éch: 1/100 Pl. 15/137
	200 STR — Coffrage — R+3	
Date: 06/05/2026	Réf: 1711	BIM vSTR-015 Phase: APD

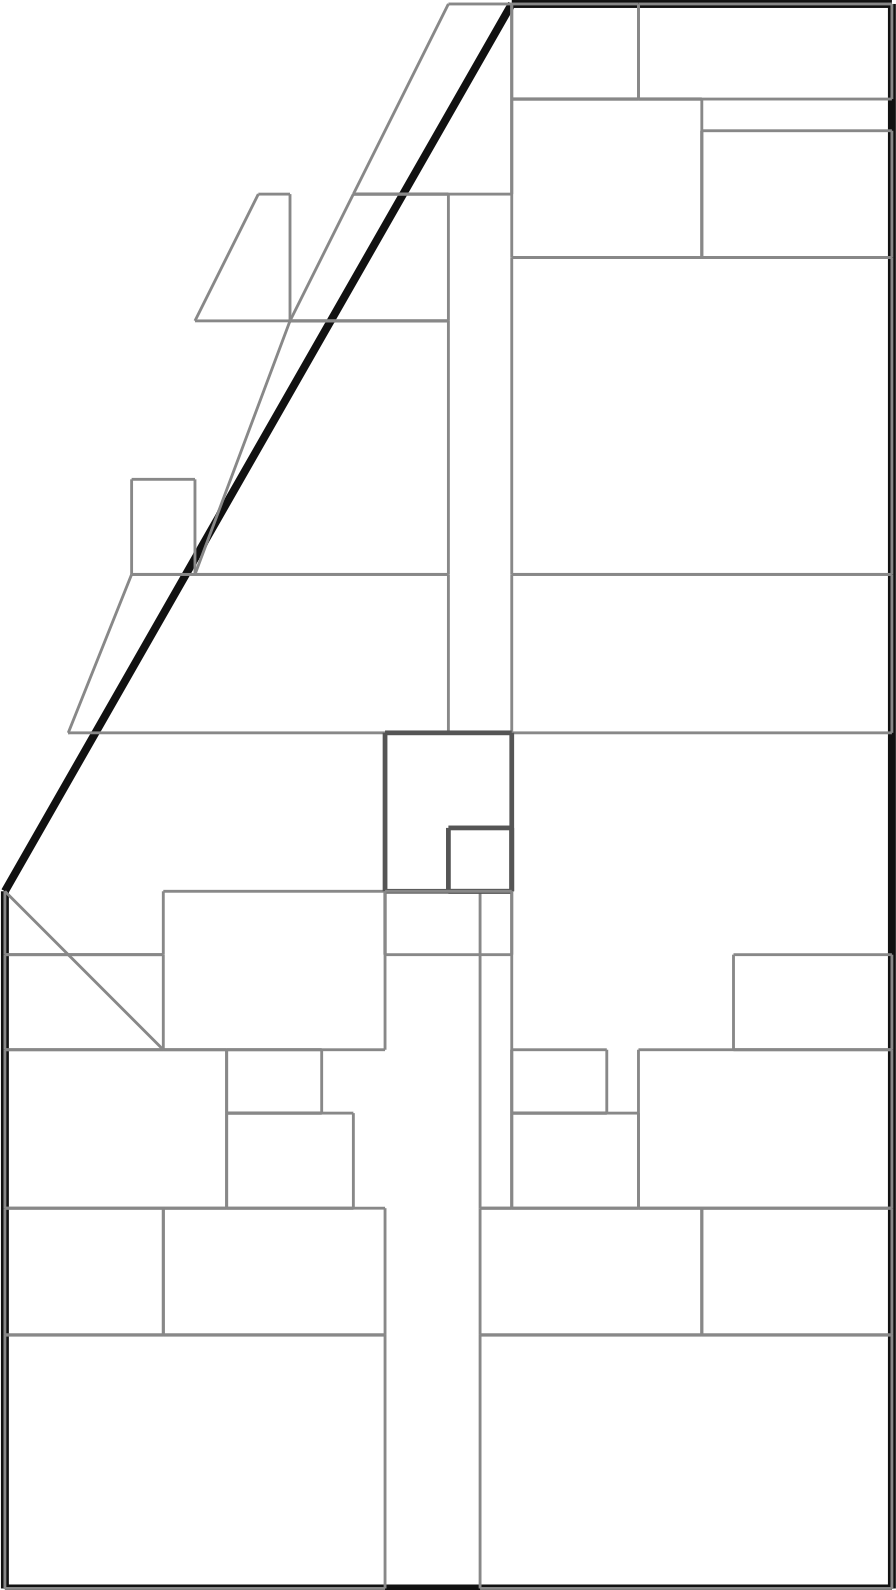


TIJAN AI Bureau d'Études Automatisé	Résidence Papa Oumar Sakho Dakar, Sénégal	Éch: 1/100 Pl. 16/137
	200 STR — Coffrage — R+4	
Date: 06/05/2026	Réf: 1711	BIM vSTR-016 Phase: APD

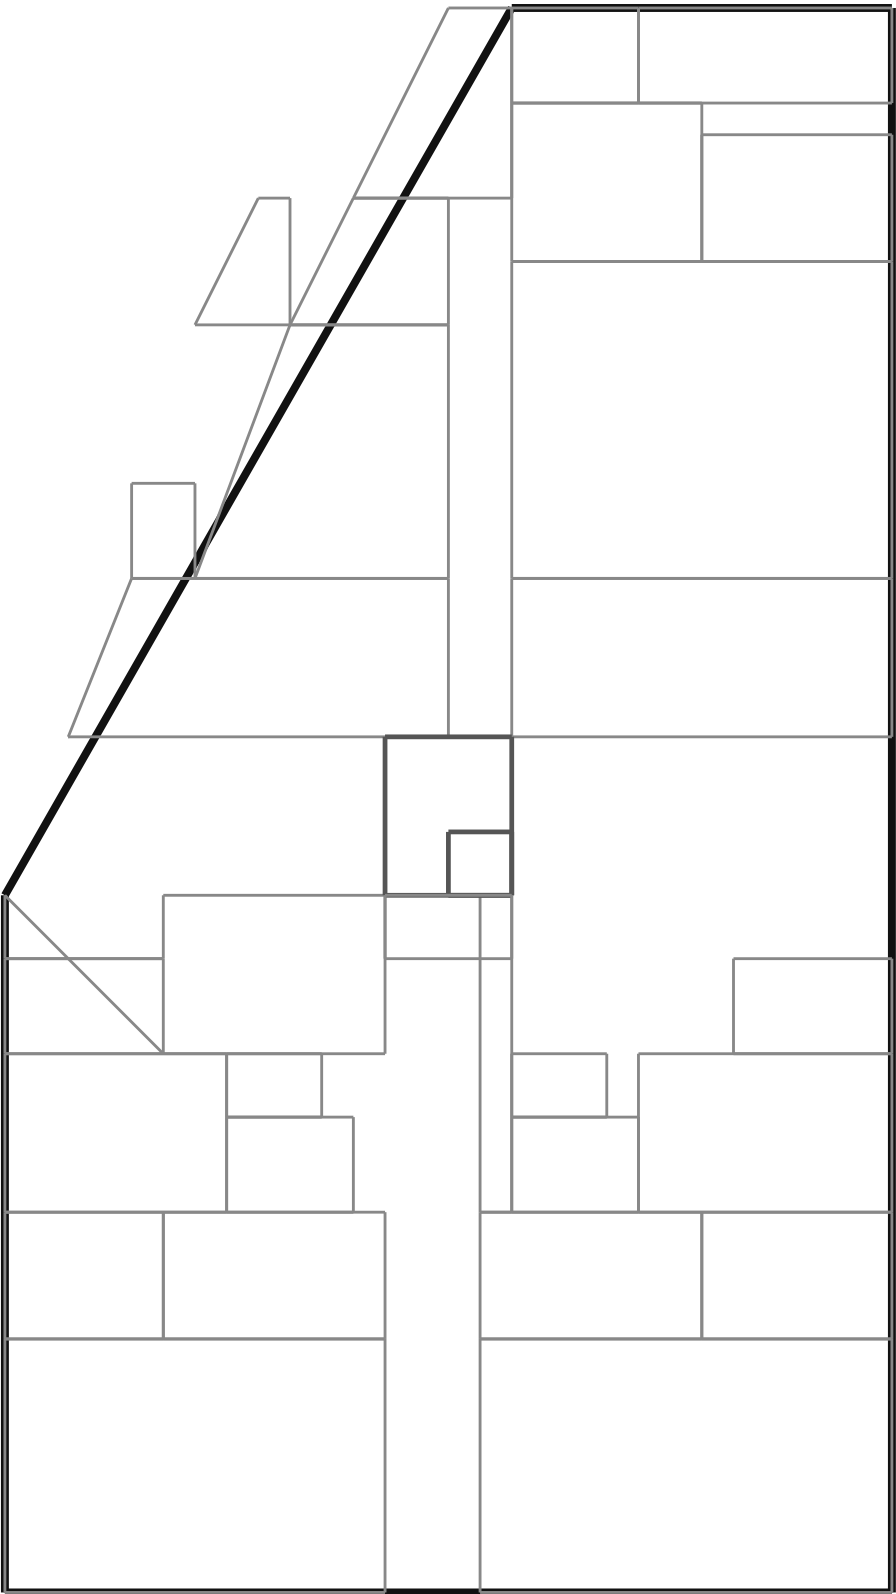

TIJAN AI Bureau d'Études Automatisé	Résidence Papa Oumar Sakho Dakar, Sénégal	Éch: 1/100 Pl. 17/137
	200 STR — Coffrage — R+5	
Date: 06/05/2026	Réf: 1711	BIM vSTR-017 Phase: APD

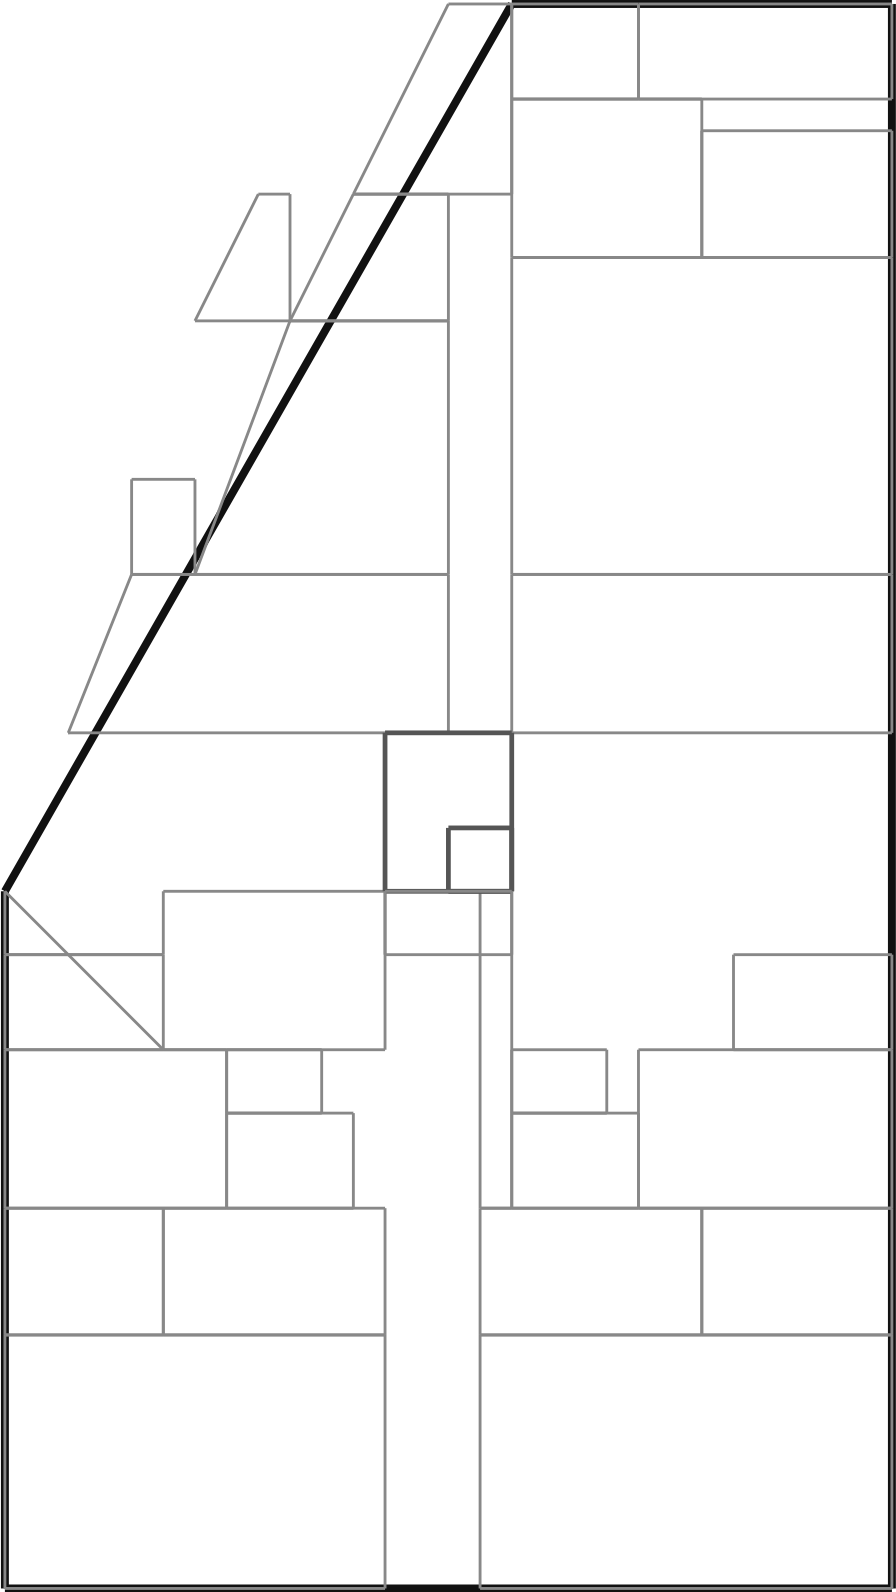

TIJAN AI Bureau d'Études Automatisé	Résidence Papa Oumar Sakho Dakar, Sénégal	Éch: 1/100 Pl. 18/137
	200 STR — Coffrage — R+6	
Date: 06/05/2026	Réf: 1711	BIM vSTR-018 Phase: APD

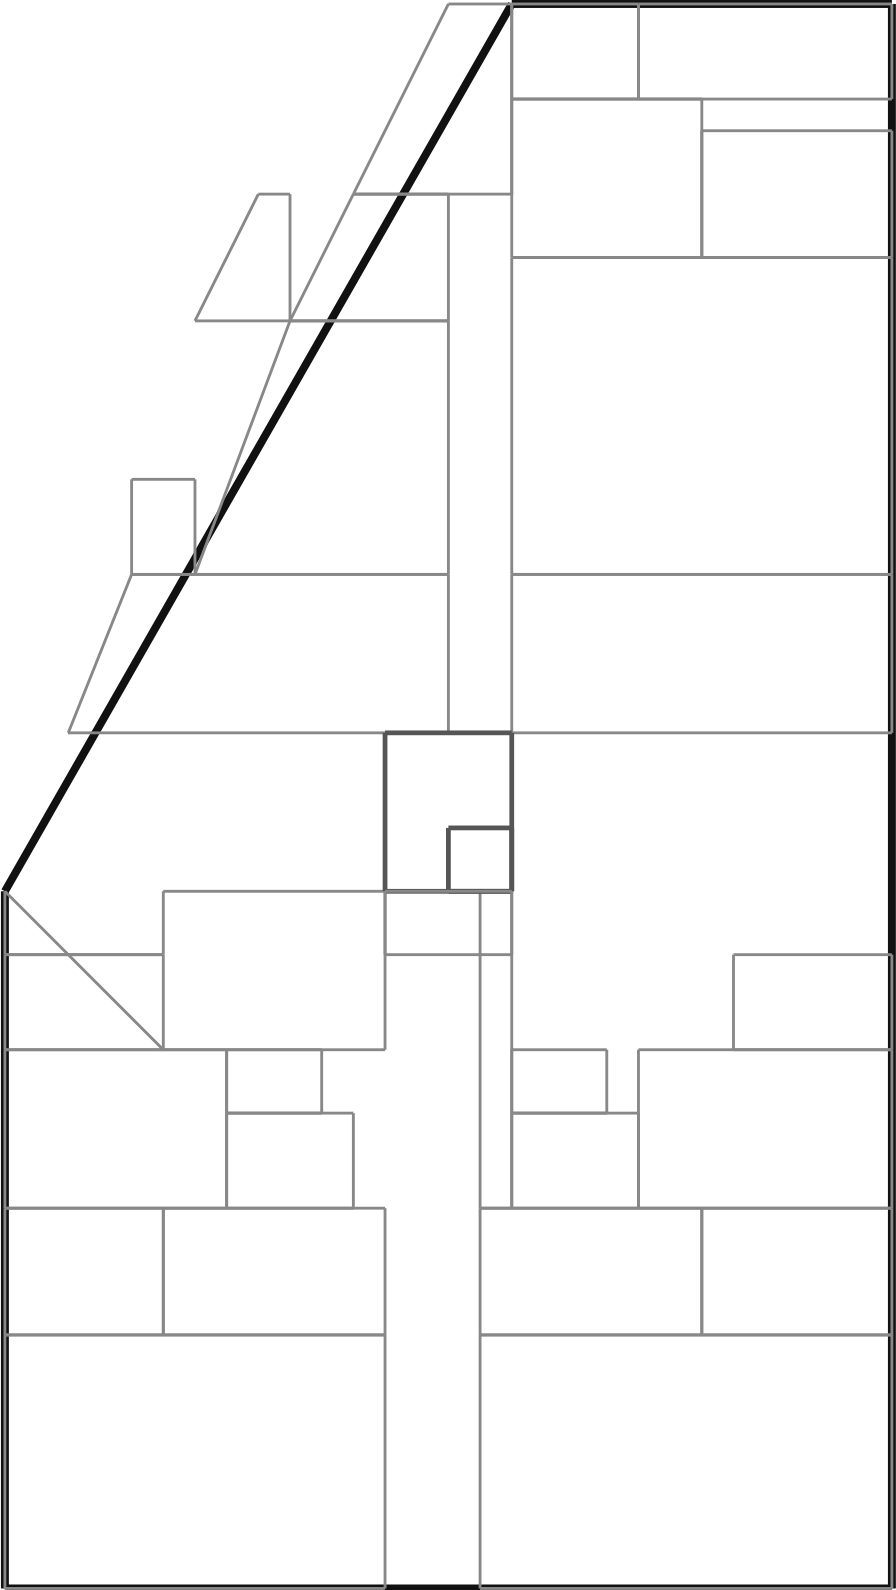

TIJAN AI

Bureau d'Études Automatisé

Résidence Papa Oumar Sakho

Dakar, Sénégal

Éch: 1/100

Pl. 19/137


200 STR — Coffrage — R+7

Date: 06/05/2026


Réf: 1711

BIM vSTR-019

Phase: APD

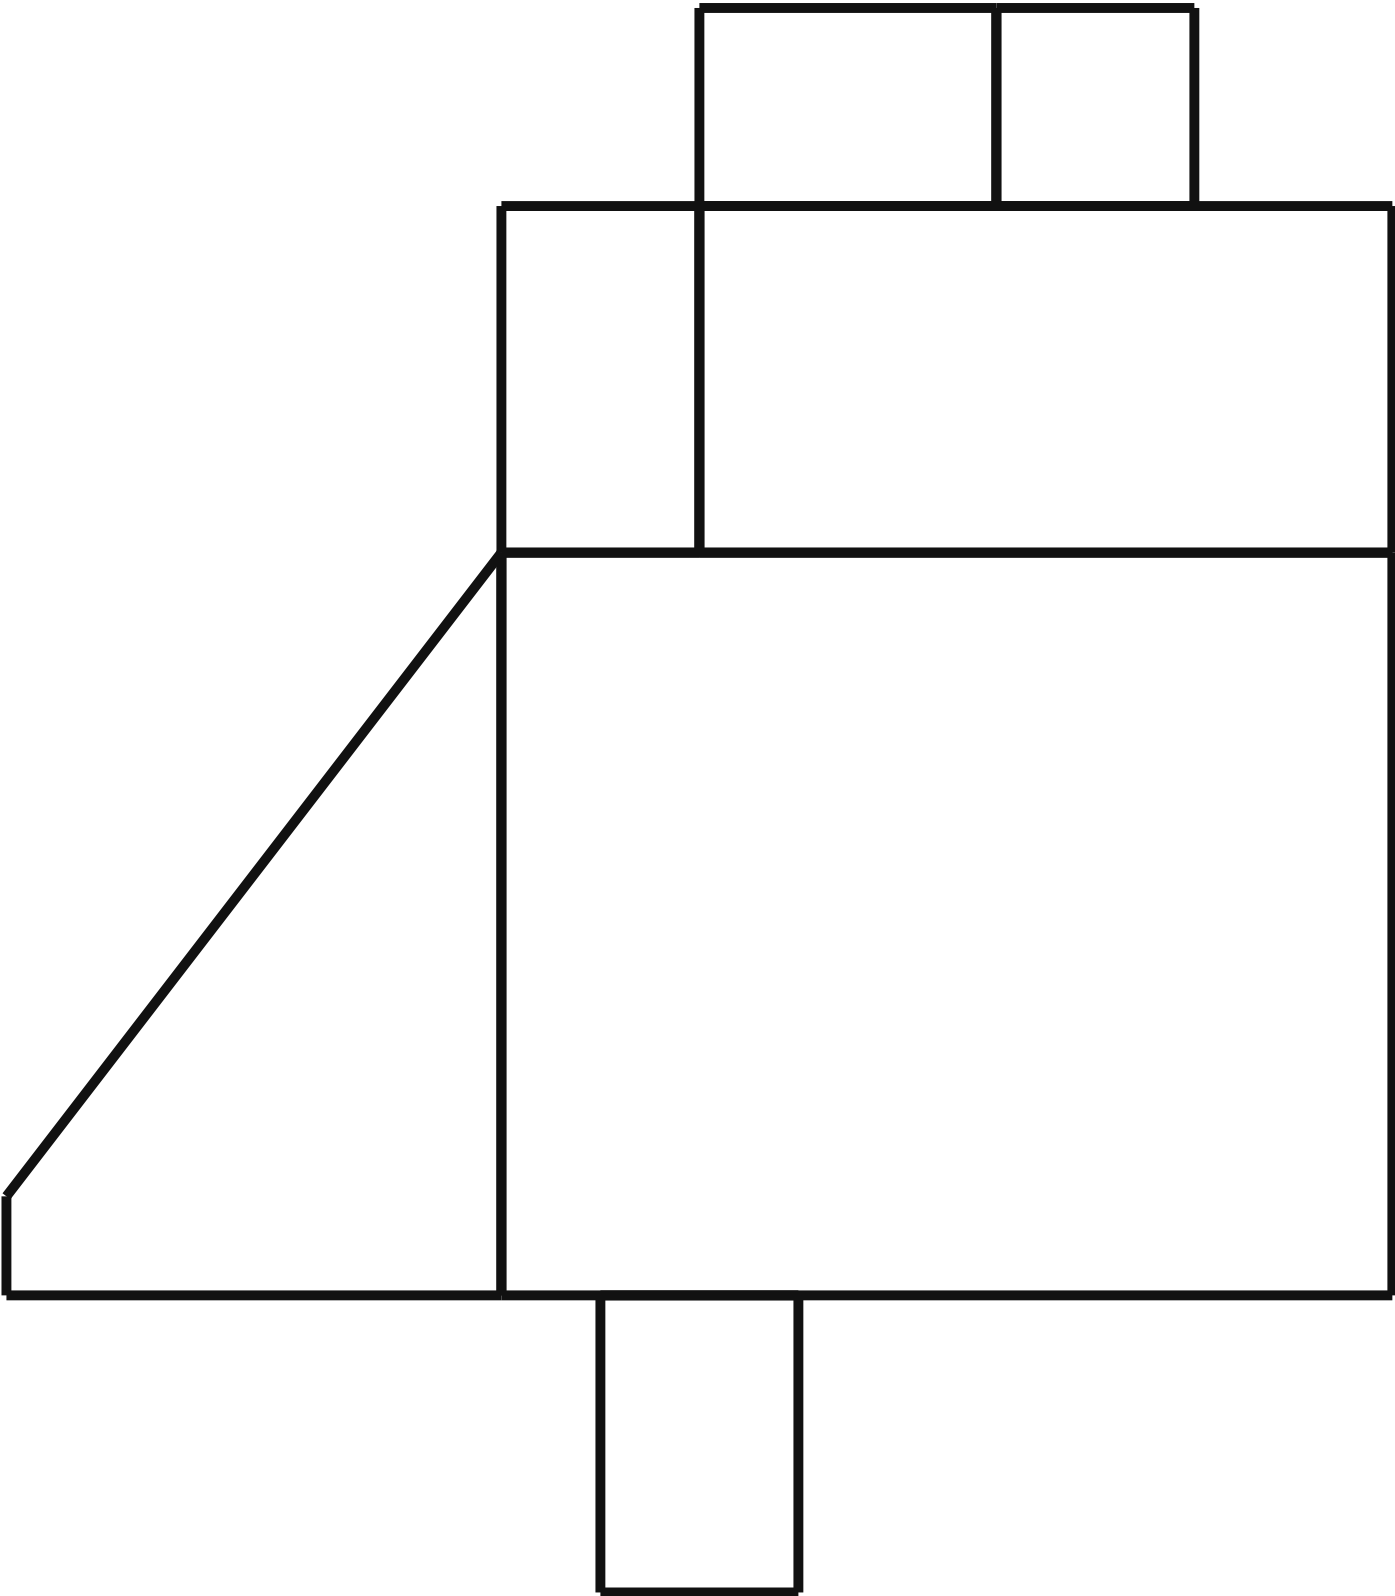


TIJAN AI Bureau d'Études Automatisé	Résidence Papa Oumar Sakho Dakar, Sénégal	Éch: 1/100 Pl. 20/137
	200 STR — Coffrage — R+8	
Date: 06/05/2026	Réf: 1711	BIM vSTR-020 Phase: APD

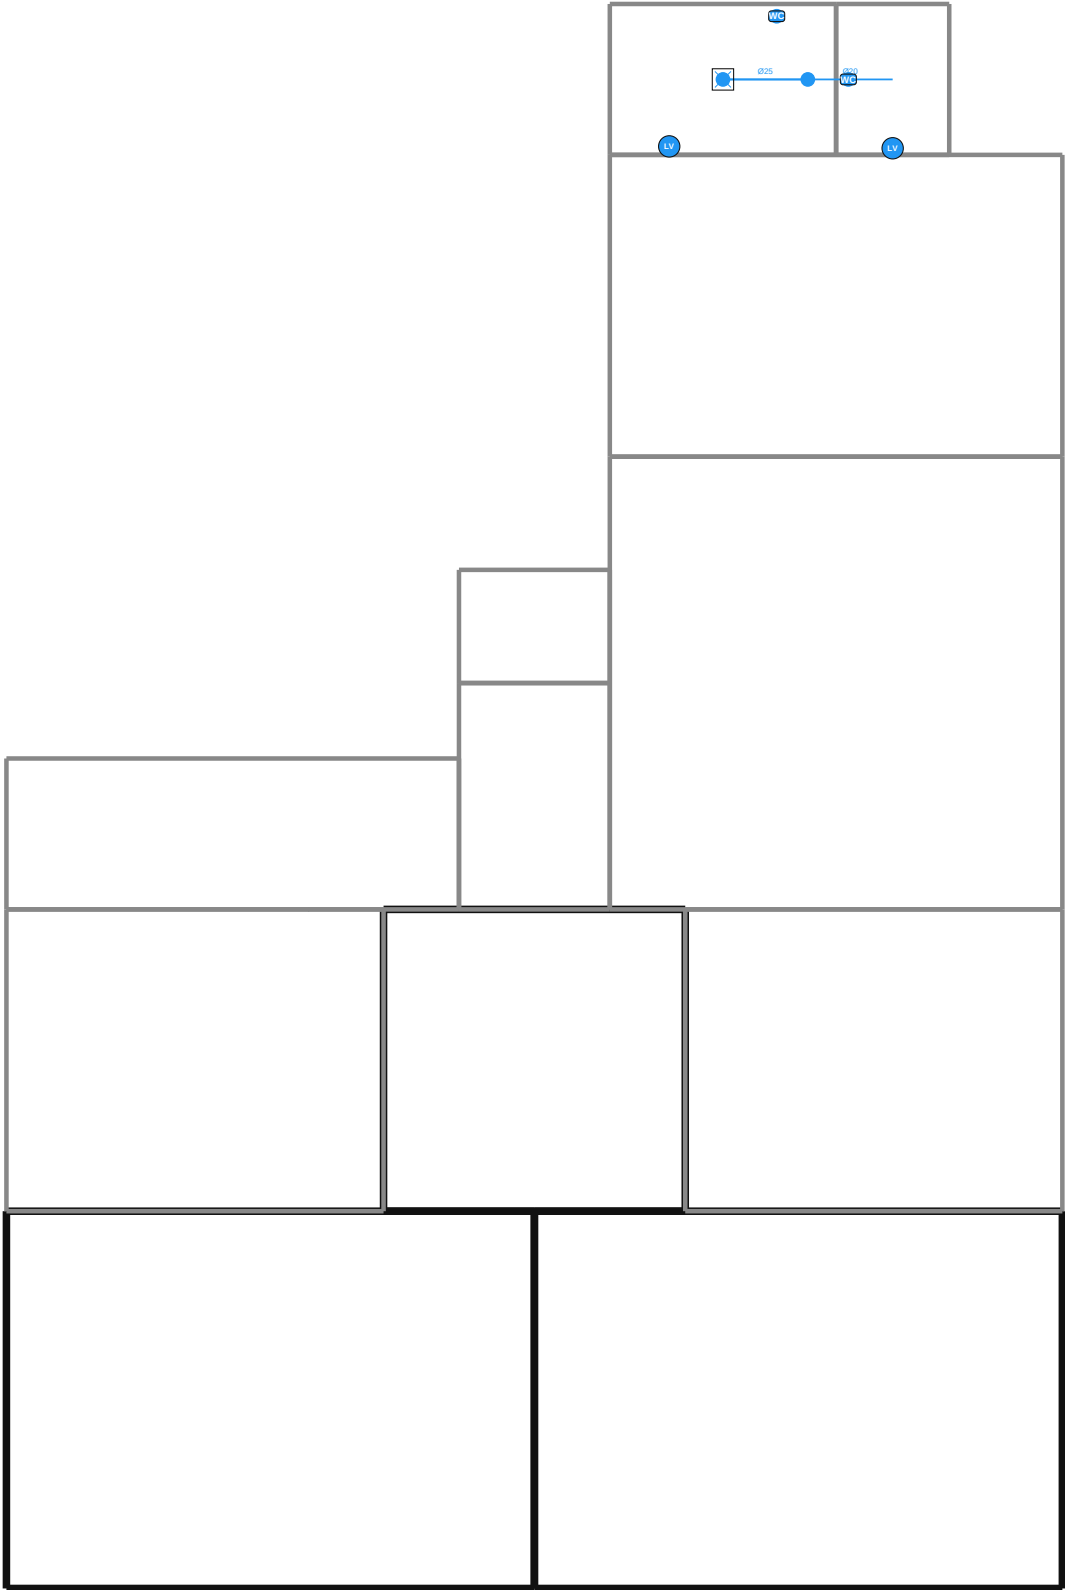

NOMENCLATURE — 410 PLU — Eau Froide (EF)

- WC suspendu: 2
- Lavabo: 1
- Douche: 1
- Lave-mains: 1


TIJAN AI Bureau d'Études Automatisé	Résidence Papa Oumar Sakho Dakar, Sénégal	Éch: 1/100 Pl. 21/137
	410 PLU — Eau Froide (EF) — RDC	
Date: 06/05/2026	Réf: 1711	BIM vPLU-021 Phase: APD

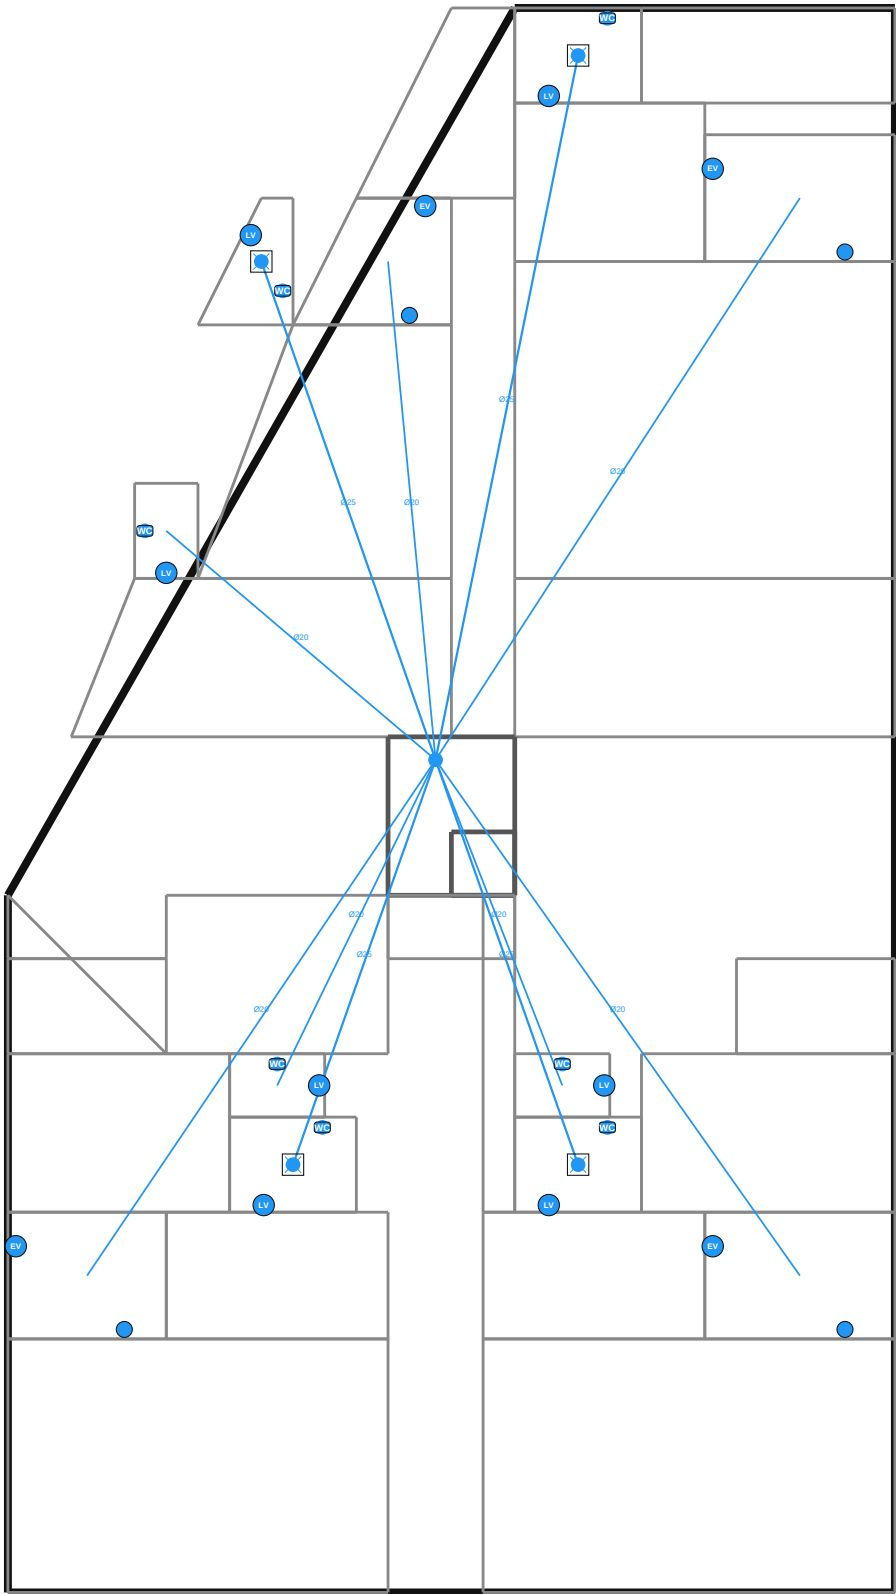

NOMENCLATURE — 410 PLU — Eau Froide (EF)

- WC suspendu: 7
- Évier cuisine: 4
- Lave-vaisselle: 4
- Lavabo: 4
- Douche: 4
- Lave-mains: 3


TIJAN AI Bureau d'Études Automatisé	Résidence Papa Oumar Sakho Dakar, Sénégal	Éch: 1/100 Pl. 22/137
	410 PLU — Eau Froide (EF) — R+1	
Date: 06/05/2026	Réf: 1711	BIM vPLU-022 Phase: APD

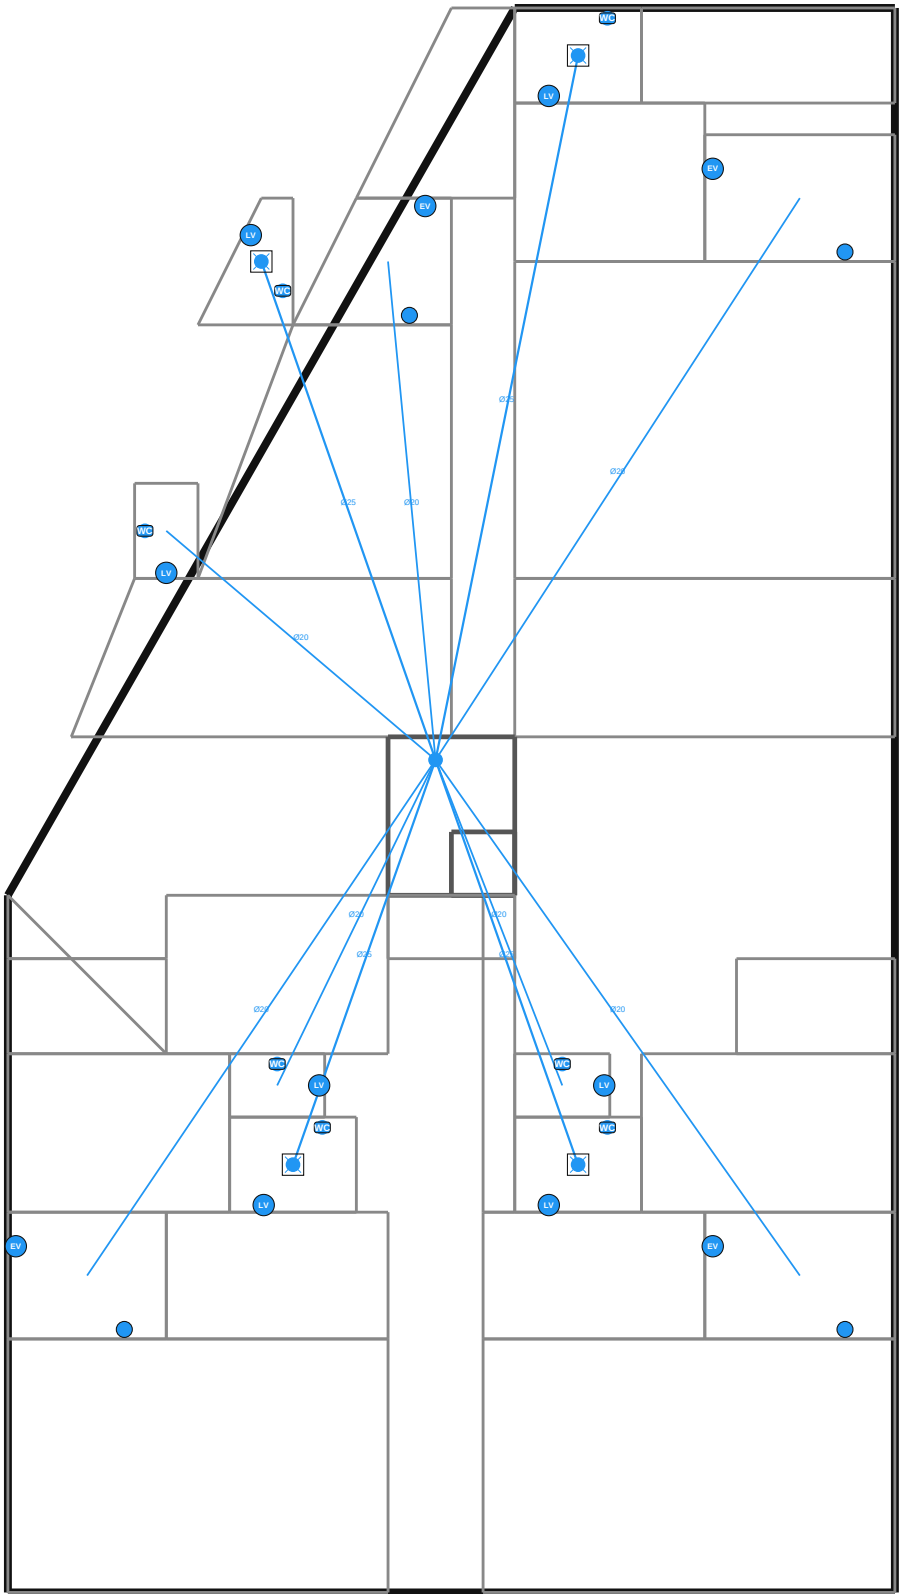

NOMENCLATURE — 410 PLU — Eau Froide (EF)

- WC suspendu: 7
- Évier cuisine: 4
- Lave-vaisselle: 4
- Lavabo: 4
- Douche: 4
- Lave-mains: 3


TIJAN AI Bureau d'Études Automatisé	Résidence Papa Oumar Sakho Dakar, Sénégal	Éch: 1/100 Pl. 23/137
	410 PLU — Eau Froide (EF) — R+2	
Date: 06/05/2026	Réf: 1711	BIM vPLU-023 Phase: APD

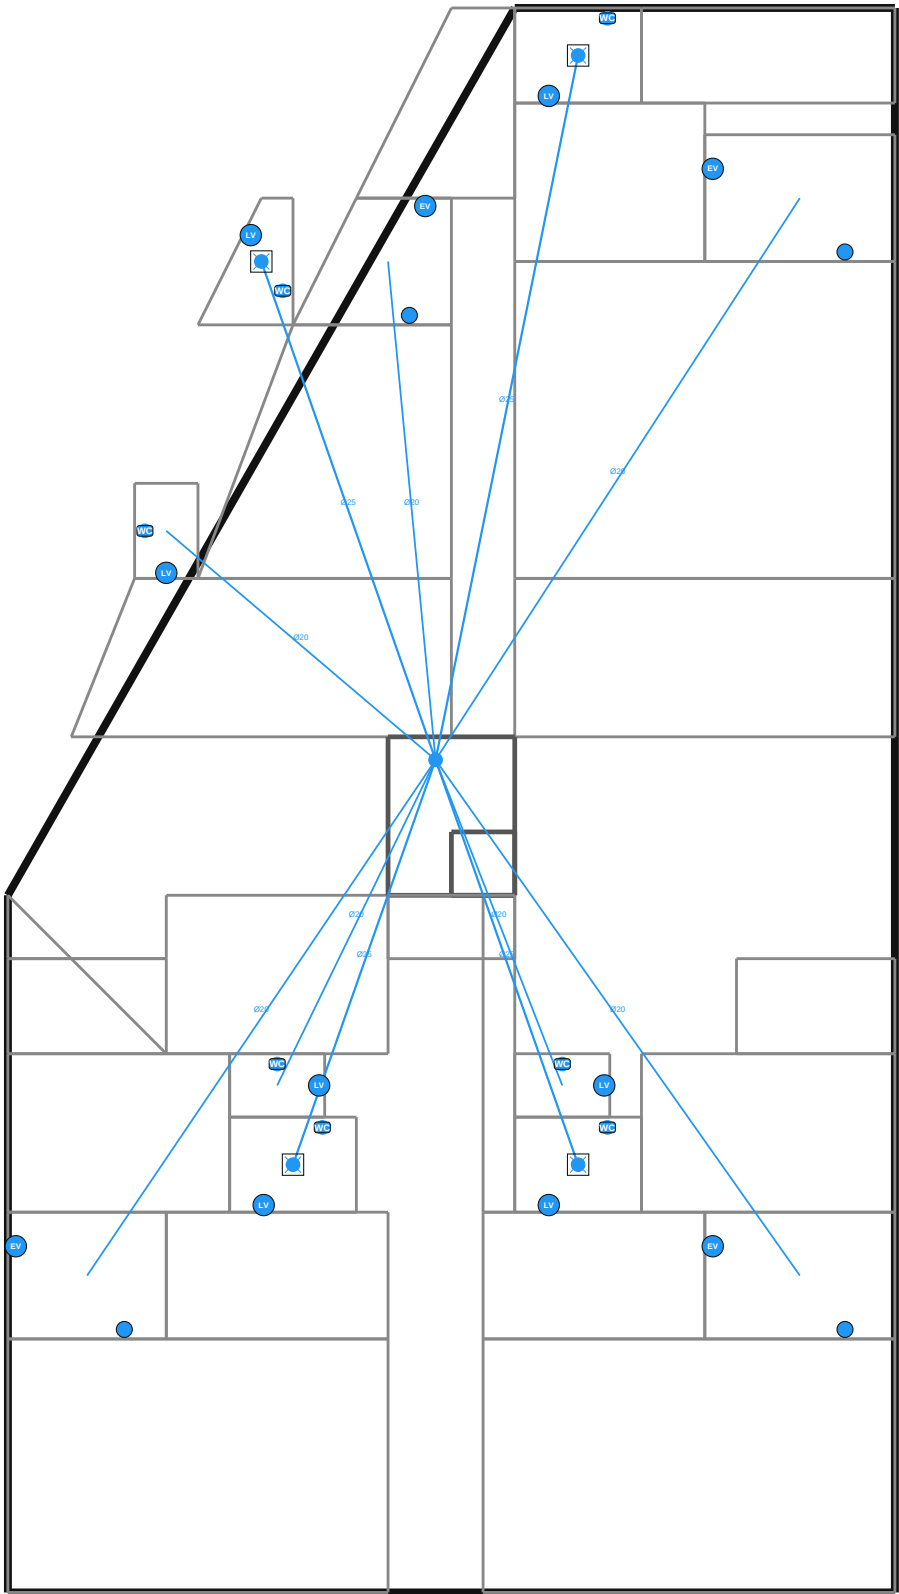

NOMENCLATURE — 410 PLU — Eau Froide (EF)

- WC suspendu: 7
- Évier cuisine: 4
- Lave-vaisselle: 4
- Lavabo: 4
- Douche: 4
- Lave-mains: 3


TIJAN AI Bureau d'Études Automatisé	Résidence Papa Oumar Sakho Dakar, Sénégal	Éch: 1/100 Pl. 24/137
	410 PLU — Eau Froide (EF) — R+3	
Date: 06/05/2026	Réf: 1711	BIM vPLU-024 Phase: APD

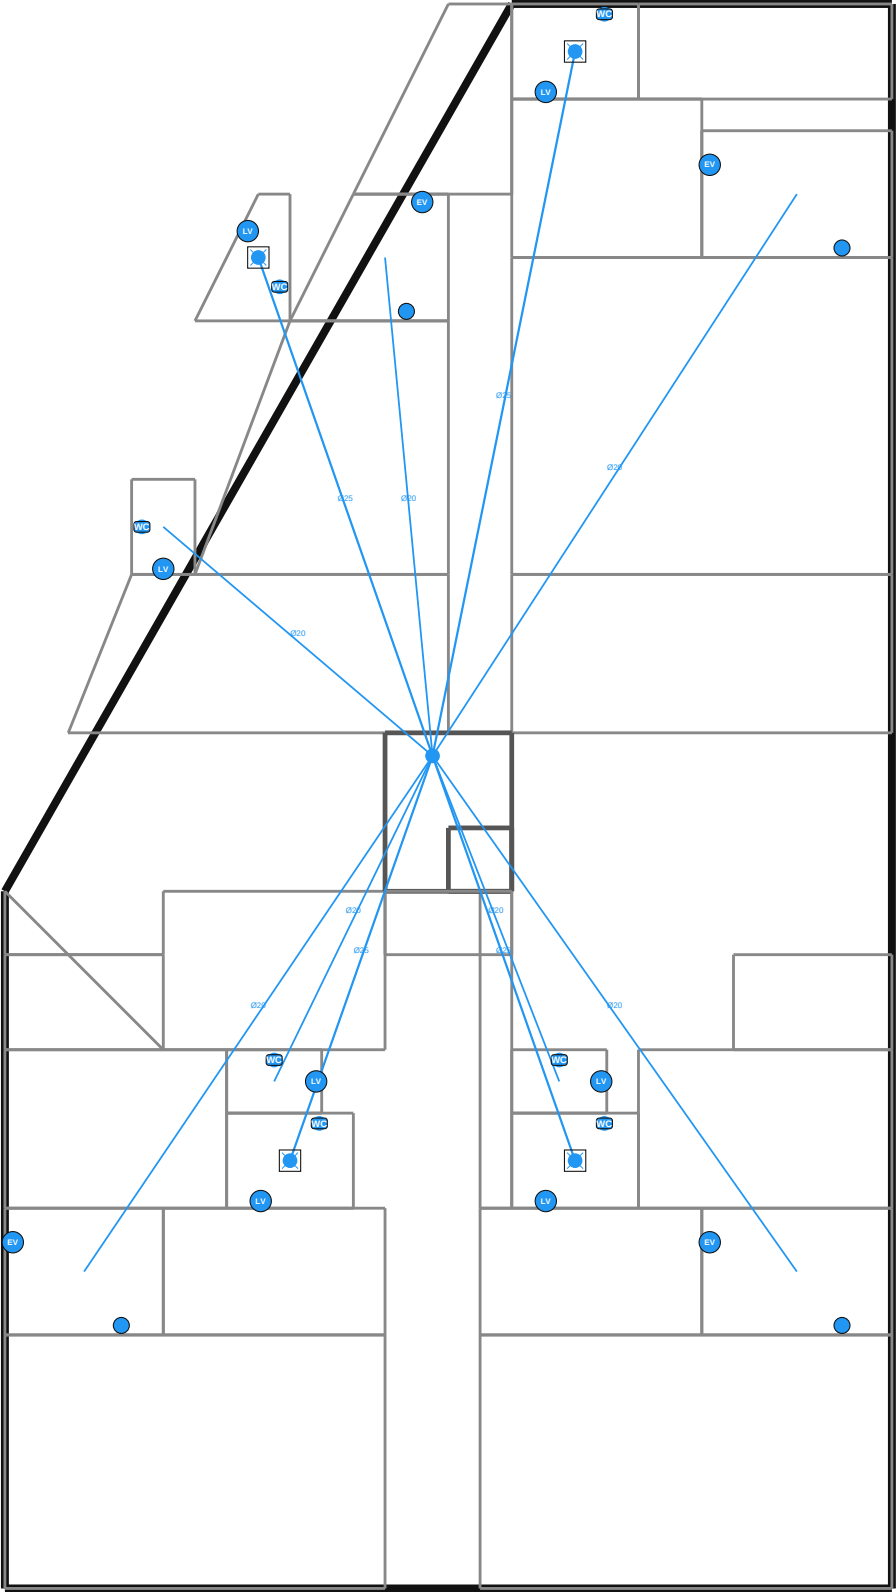

NOMENCLATURE — 410 PLU — Eau Froide (EF)

- WC suspendu: 7
- Évier cuisine: 4
- Lave-vaisselle: 4
- Lavabo: 4
- Douche: 4
- Lave-mains: 3


TIJAN AI Bureau d'Études Automatisé	Résidence Papa Oumar Sakho Dakar, Sénégal	Éch: 1/100 Pl. 25/137
	410 PLU — Eau Froide (EF) — R+4	
Date: 06/05/2026	Réf: 1711	BIM vPLU-025 Phase: APD

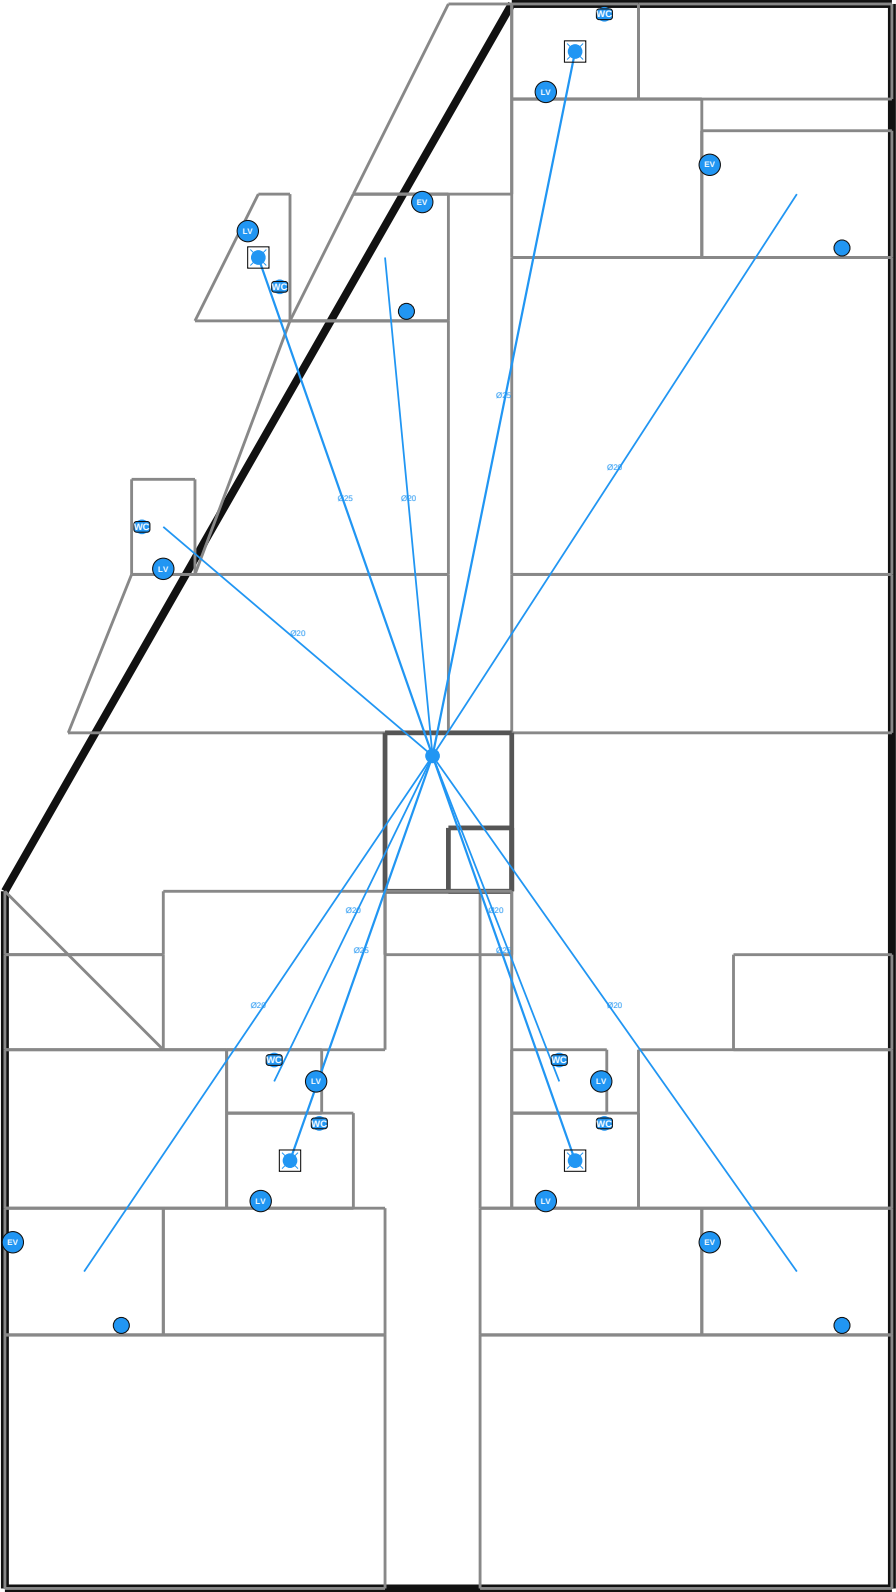

NOMENCLATURE — 410 PLU — Eau Froide (EF)

- WC suspendu: 7
- Évier cuisine: 4
- Lave-vaisselle: 4
- Lavabo: 4
- Douche: 4
- Lave-mains: 3


TIJAN AI Bureau d'Études Automatisé	Résidence Papa Oumar Sakho Dakar, Sénégal	Éch: 1/100 Pl. 26/137
	410 PLU — Eau Froide (EF) — R+5	
Date: 06/05/2026	Réf: 1711	BIM vPLU-026 Phase: APD

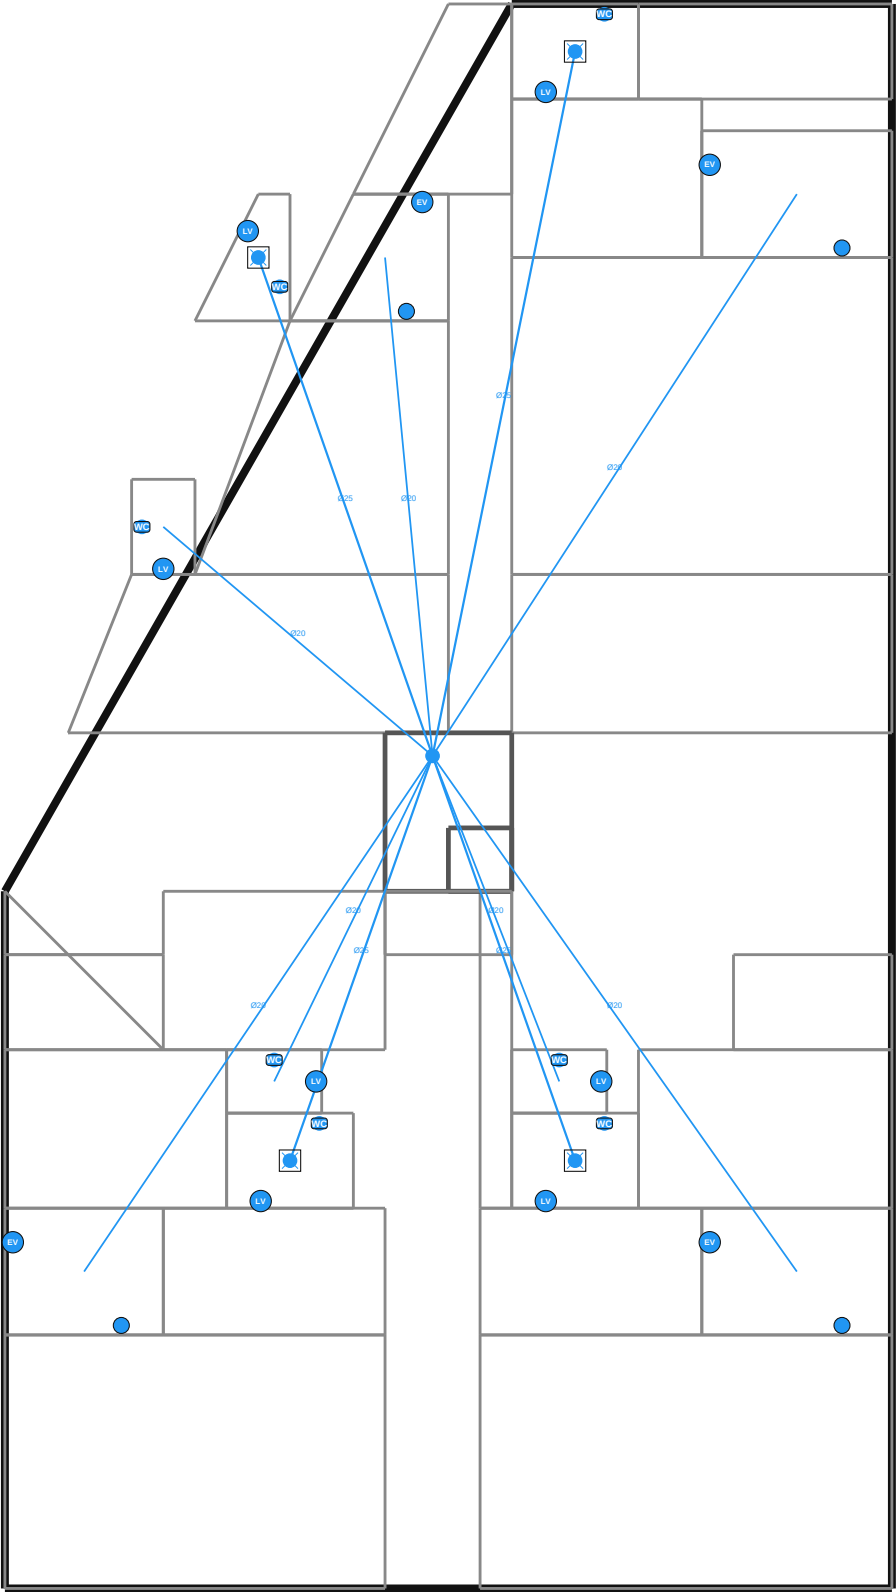

NOMENCLATURE — 410 PLU — Eau Froide (EF)

- WC suspendu: 7
- Évier cuisine: 4
- Lave-vaisselle: 4
- Lavabo: 4
- Douche: 4
- Lave-mains: 3


TIJAN AI Bureau d'Études Automatisé	Résidence Papa Oumar Sakho Dakar, Sénégal	Éch: 1/100 Pl. 27/137
	410 PLU — Eau Froide (EF) — R+6	
Date: 06/05/2026	Réf: 1711	BIM vPLU-027 Phase: APD

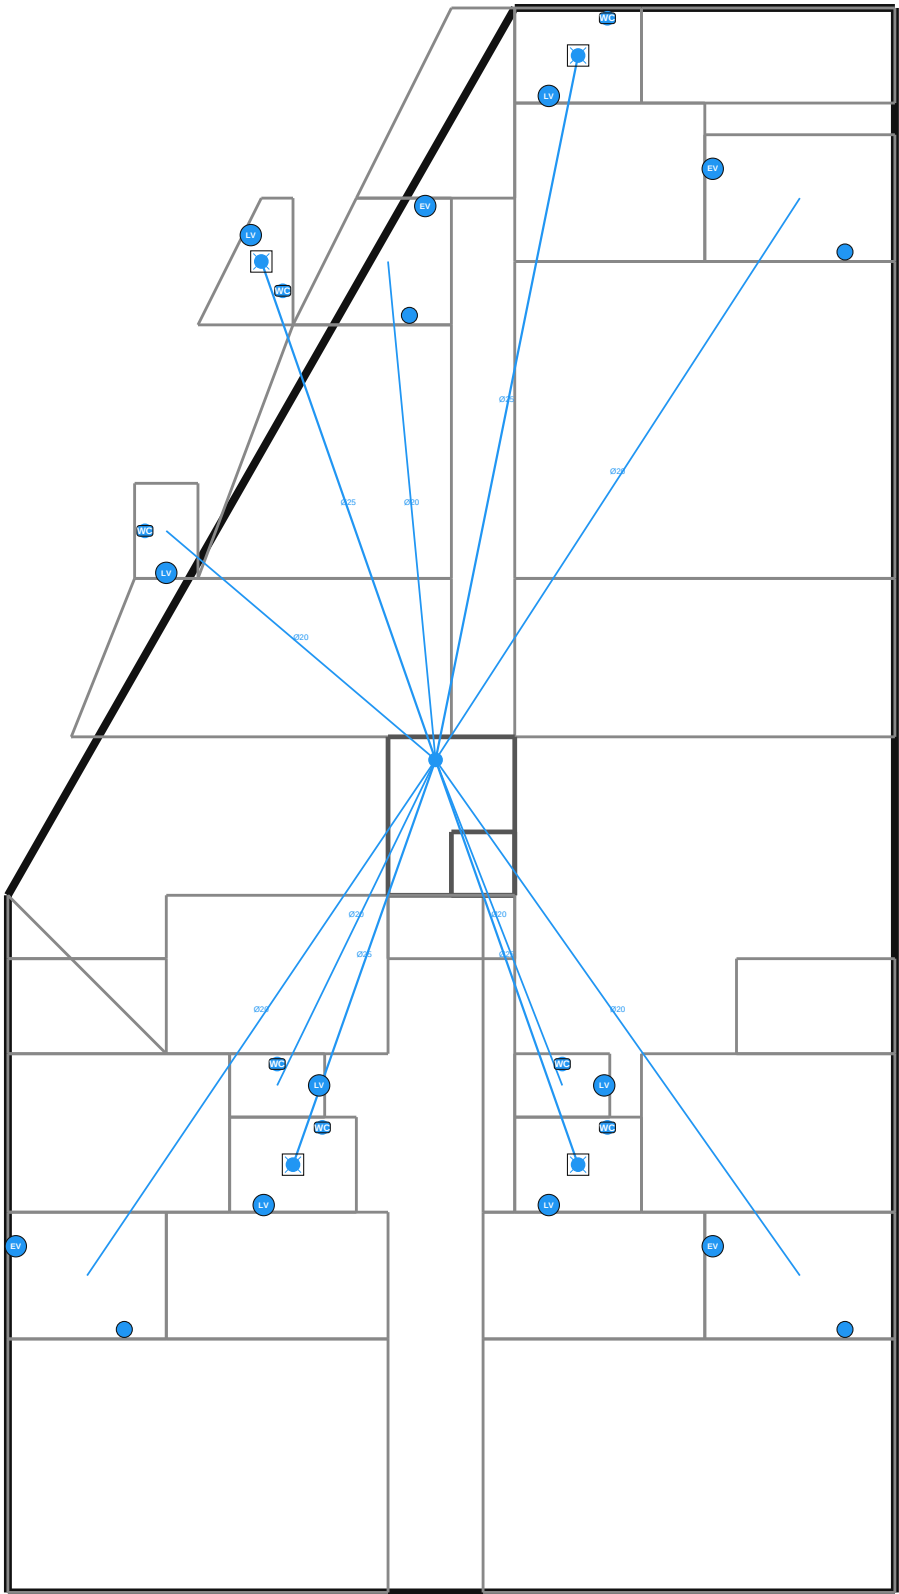

NOMENCLATURE — 410 PLU — Eau Froide (EF)

- WC suspendu: 7
- Évier cuisine: 4
- Lave-vaisselle: 4
- Lavabo: 4
- Douche: 4
- Lave-mains: 3


TIJAN AI Bureau d'Études Automatisé	Résidence Papa Oumar Sakho Dakar, Sénégal	Éch: 1/100 Pl. 28/137
	410 PLU — Eau Froide (EF) — R+7	
Date: 06/05/2026	Réf: 1711	BIM vPLU-028 Phase: APD

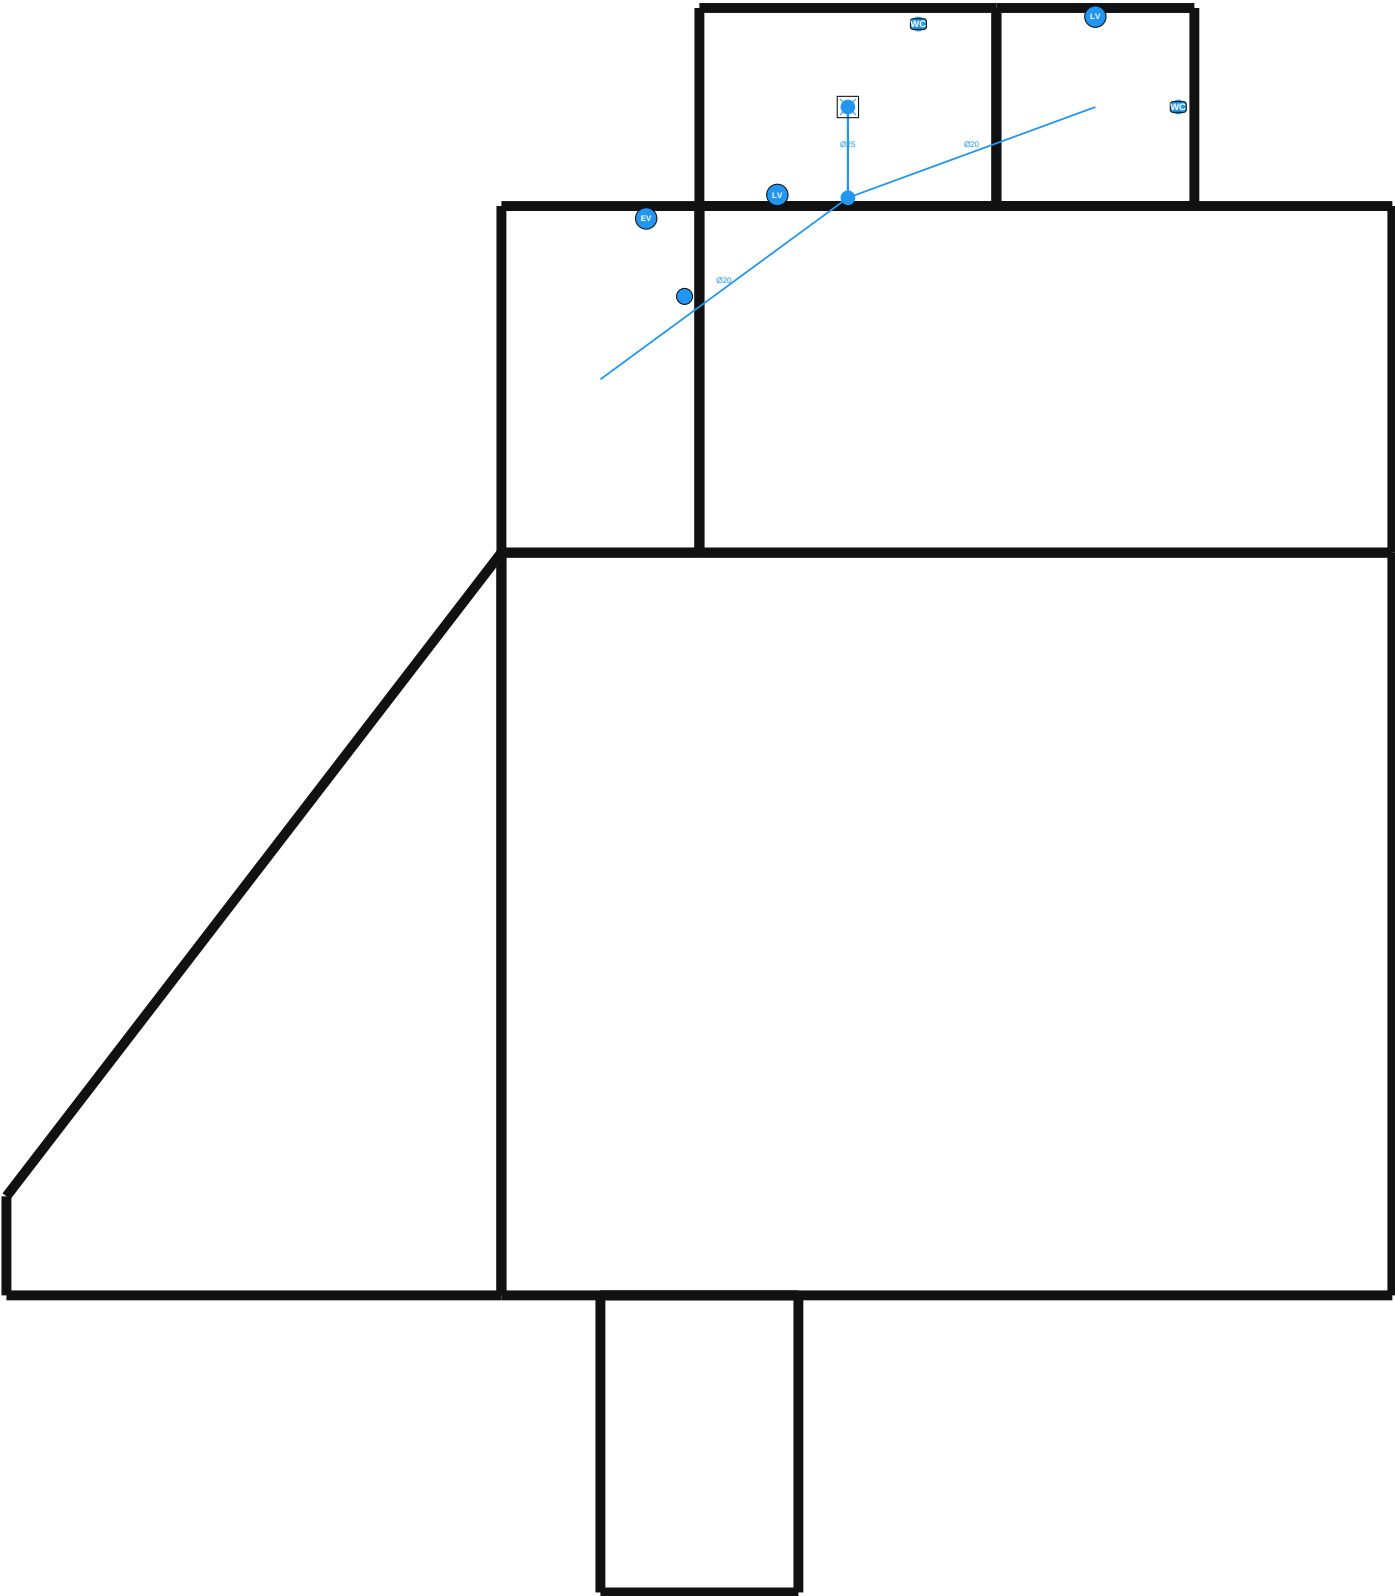

NOMENCLATURE — 410 PLU — Eau Froide (EF)

- WC suspendu: 2
- Évier cuisine: 1
- Lave-vaisselle: 1
- Lavabo: 1
- Douche: 1
- Lave-mains: 1


TIJAN AI Bureau d'Études Automatisé	Résidence Papa Oumar Sakho Dakar, Sénégal	Éch: 1/100 Pl. 29/137
	410 PLU — Eau Froide (EF) — R+8	
Date: 06/05/2026	Réf: 1711	BIM vPLU-029 Phase: APD

 

NOMENCLATURE — 410 PLU — Eau Chaude (EC)

• Chauffe-eau: 1


TIJAN AI Bureau d'Études Automatisé	Résidence Papa Oumar Sakho Dakar, Sénégal	Éch: 1/100 Pl. 30/137
	410 PLU — Eau Chaude (EC) — Sous-Sol	
Date: 06/05/2026	Réf: 1711	BIM vPLU-030 Phase: APD

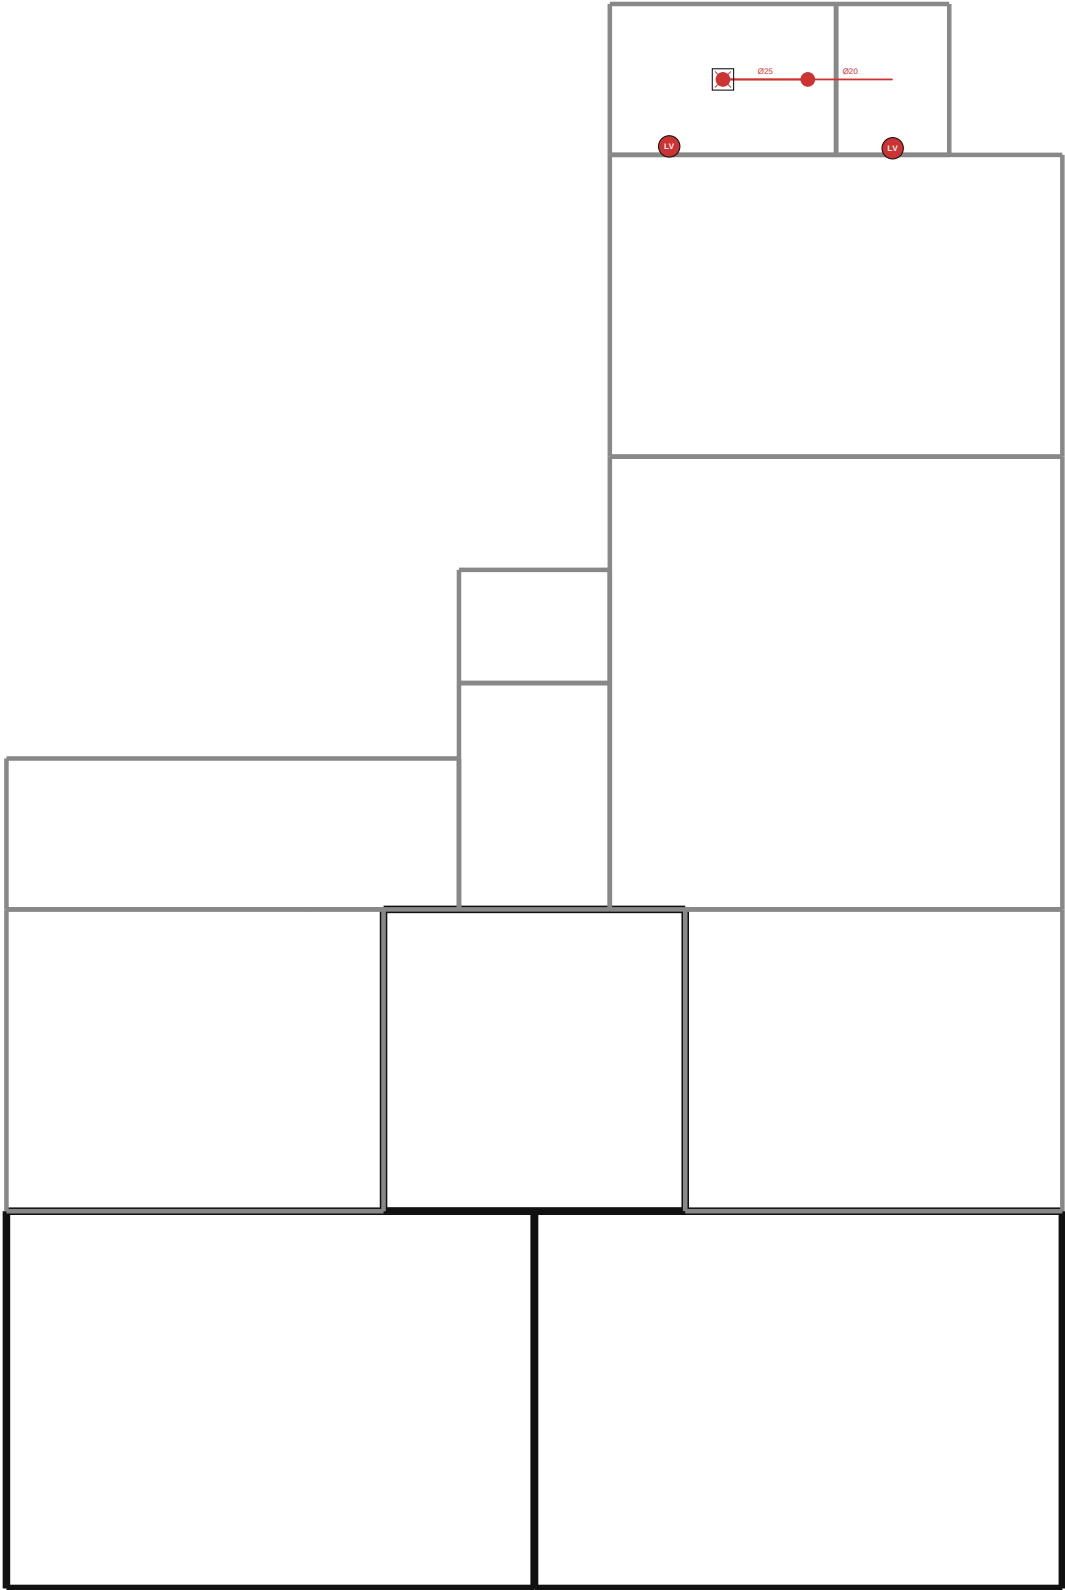

NOMENCLATURE — 410 PLU — Eau Chaude (EC)

- Lavabo: 1
- Douche: 1
- Lave-mains: 1

TIJAN AI Bureau d'Études Automatisé	Résidence Papa Oumar Sakho Dakar, Sénégal	Éch: 1/100 Pl. 31/137
	410 PLU — Eau Chaude (EC) — RDC	
Date: 06/05/2026	Réf: 1711	BIM vPLU-031 Phase: APD

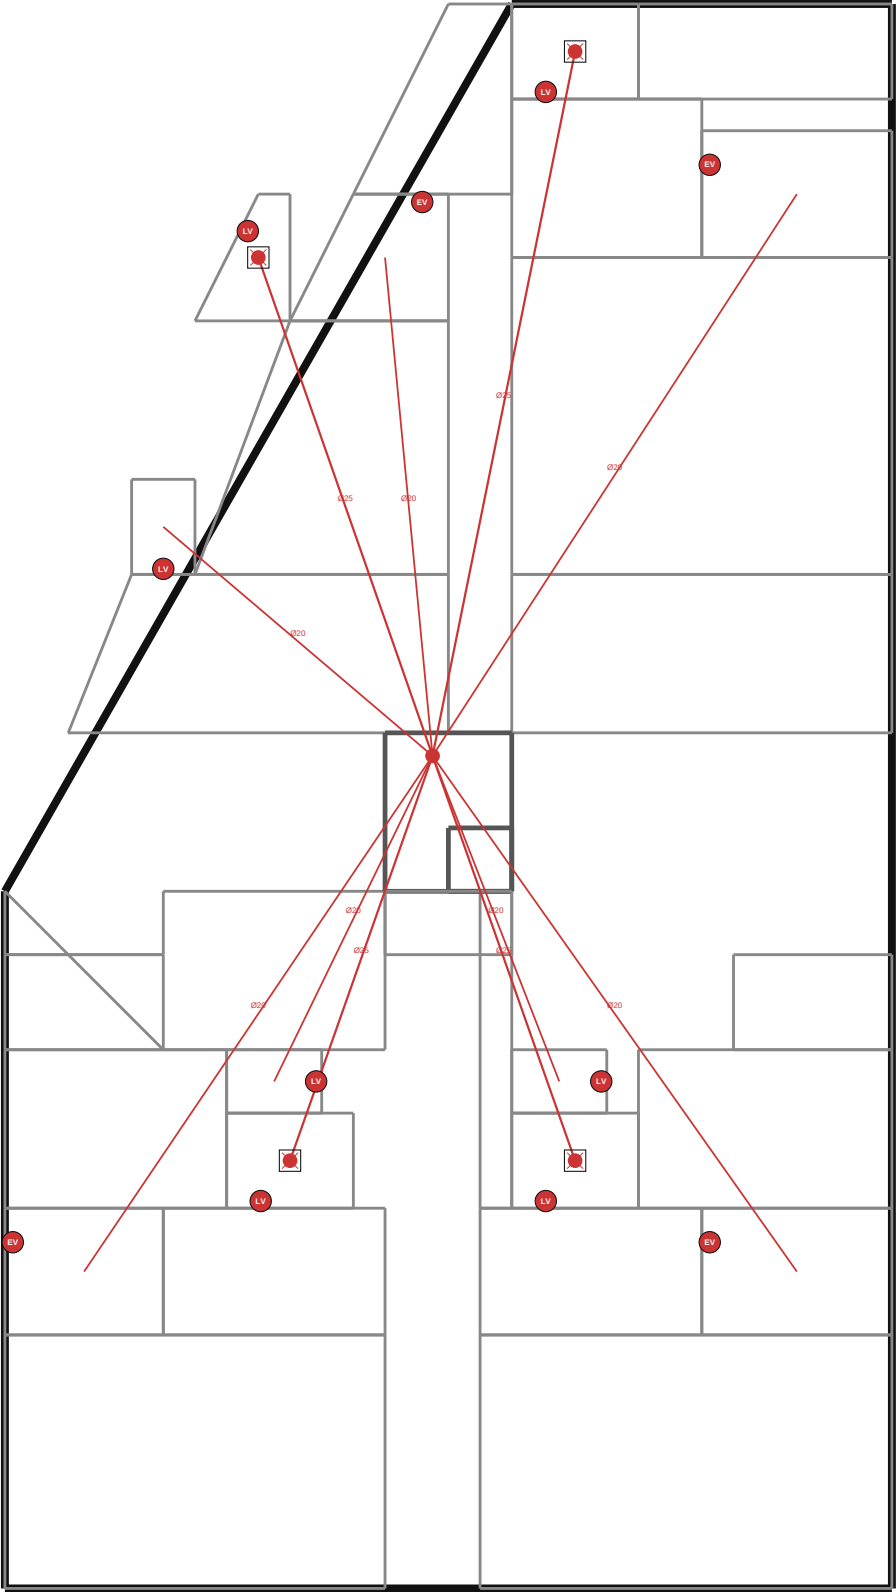

NOMENCLATURE — 410 PLU — Eau Chaude (EC)

- Évier cuisine: 4
- Lavabo: 4
- Douche: 4
- Lave-mains: 3

TIJAN AI

Bureau d'Études Automatisé

Résidence Papa Oumar Sakho

Dakar, Sénégal

Éch: 1/100

Pl. 32/137


410 PLU — Eau Chaude (EC) — R+1

Date: 06/05/2026

Réf: 1711

BIM vPLU-032


Phase: APD

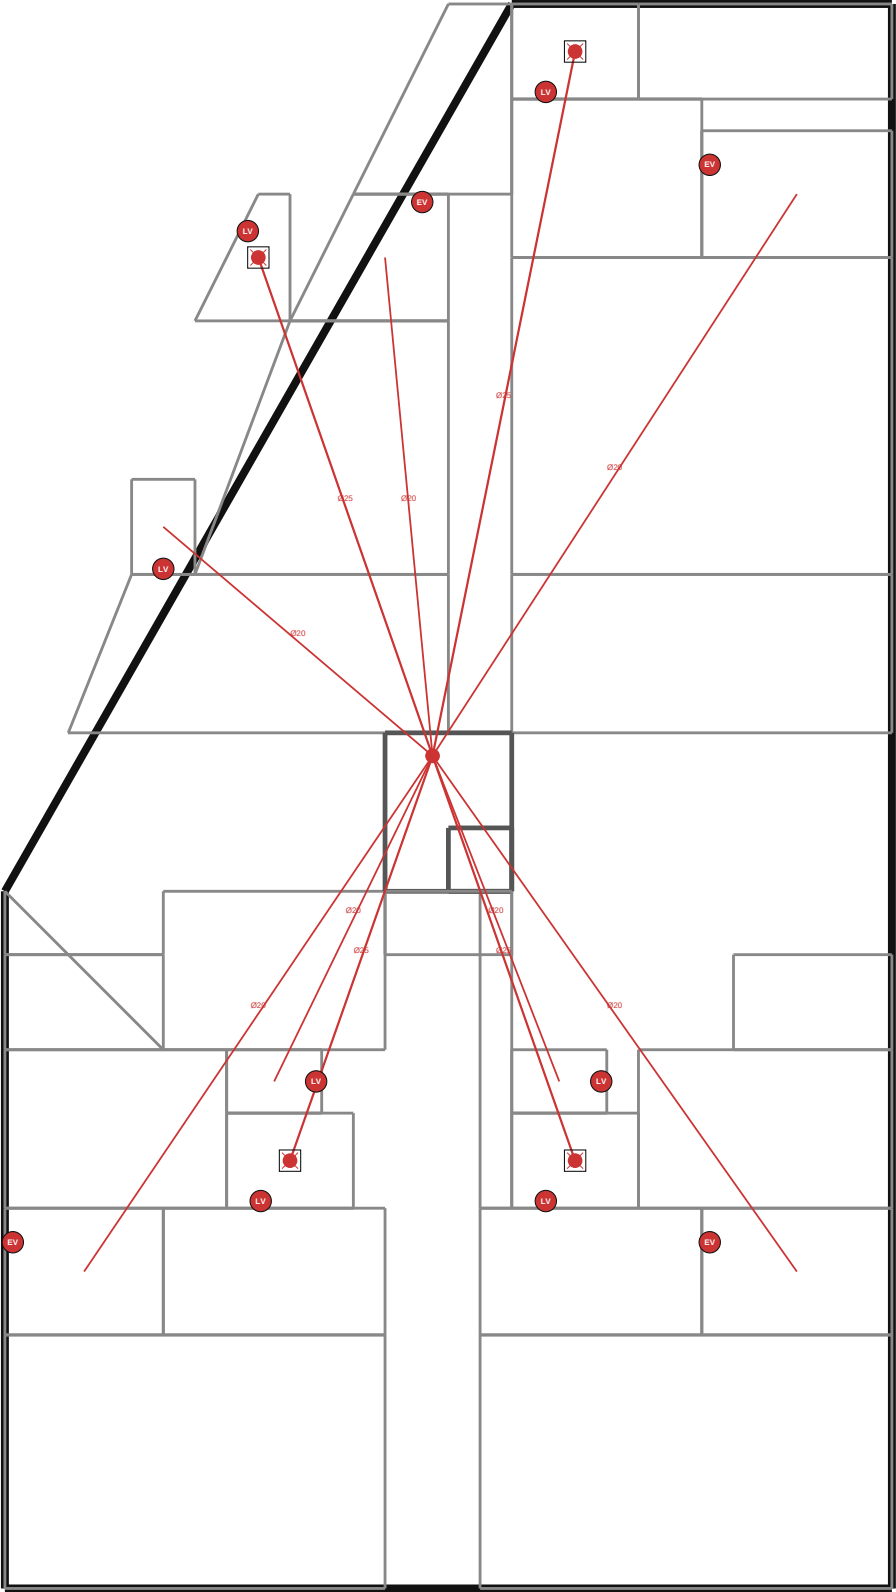

NOMENCLATURE — 410 PLU — Eau Chaude (EC)

- Évier cuisine: 4
- Lavabo: 4
- Douche: 4
- Lave-mains: 3


TIJAN AI Bureau d'Études Automatisé	Résidence Papa Oumar Sakho Dakar, Sénégal	Éch: 1/100 Pl. 33/137
	410 PLU — Eau Chaude (EC) — R+2	
Date: 06/05/2026	Réf: 1711	BIM vPLU-033 Phase: APD

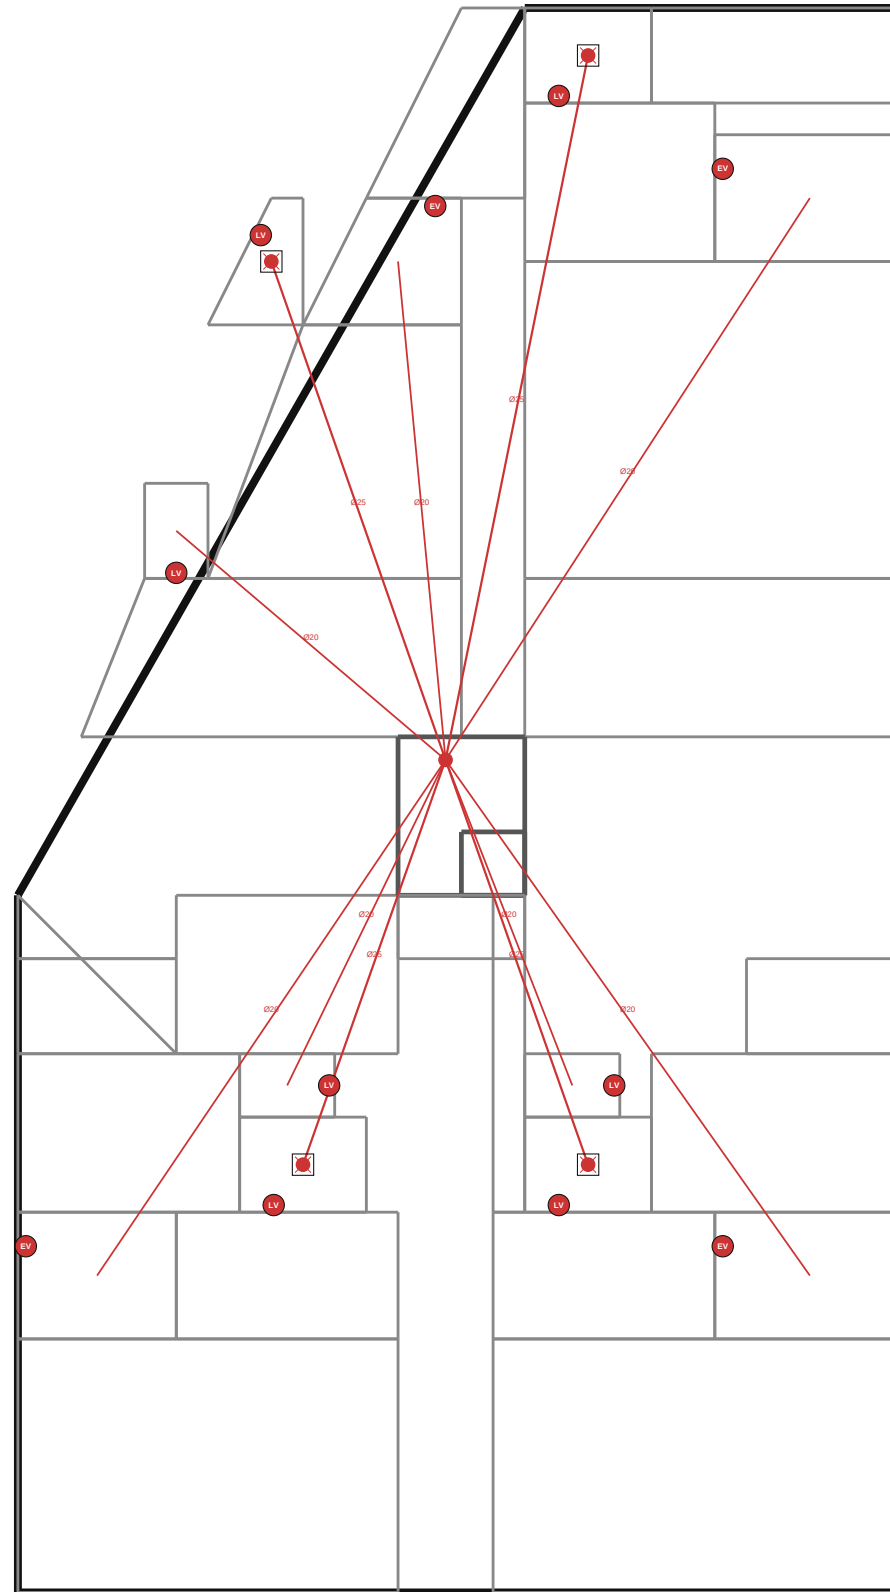

NOMENCLATURE — 410 PLU — Eau Chaude (EC)

- Évier cuisine: 4
- Lavabo: 4
- Douche: 4
- Lave-mains: 3


TIJAN AI Bureau d'Études Automatisé	Résidence Papa Oumar Sakho Dakar, Sénégal	Éch: 1/100 Pl. 34/137
	410 PLU — Eau Chaude (EC) — R+3	
Date: 06/05/2026	Réf: 1711	BIM vPLU-034 Phase: APD

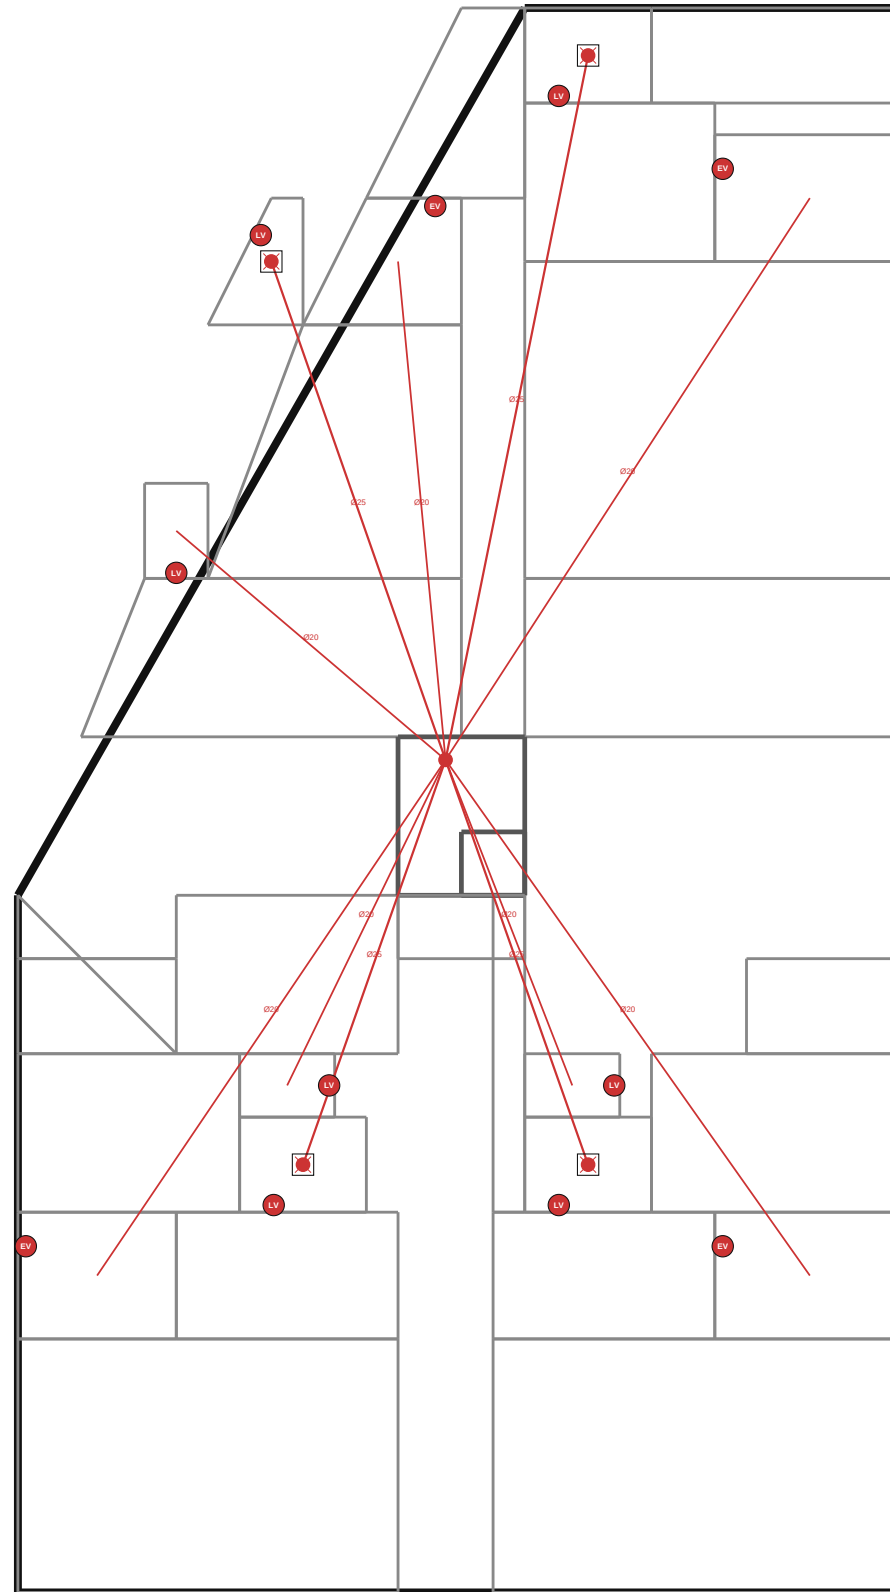

NOMENCLATURE — 410 PLU — Eau Chaude (EC)

- Évier cuisine: 4
- Lavabo: 4
- Douche: 4
- Lave-mains: 3


TIJAN AI Bureau d'Études Automatisé	Résidence Papa Oumar Sakho Dakar, Sénégal	Éch: 1/100 Pl. 35/137
	410 PLU — Eau Chaude (EC) — R+4	
Date: 06/05/2026	Réf: 1711	BIM vPLU-035 Phase: APD

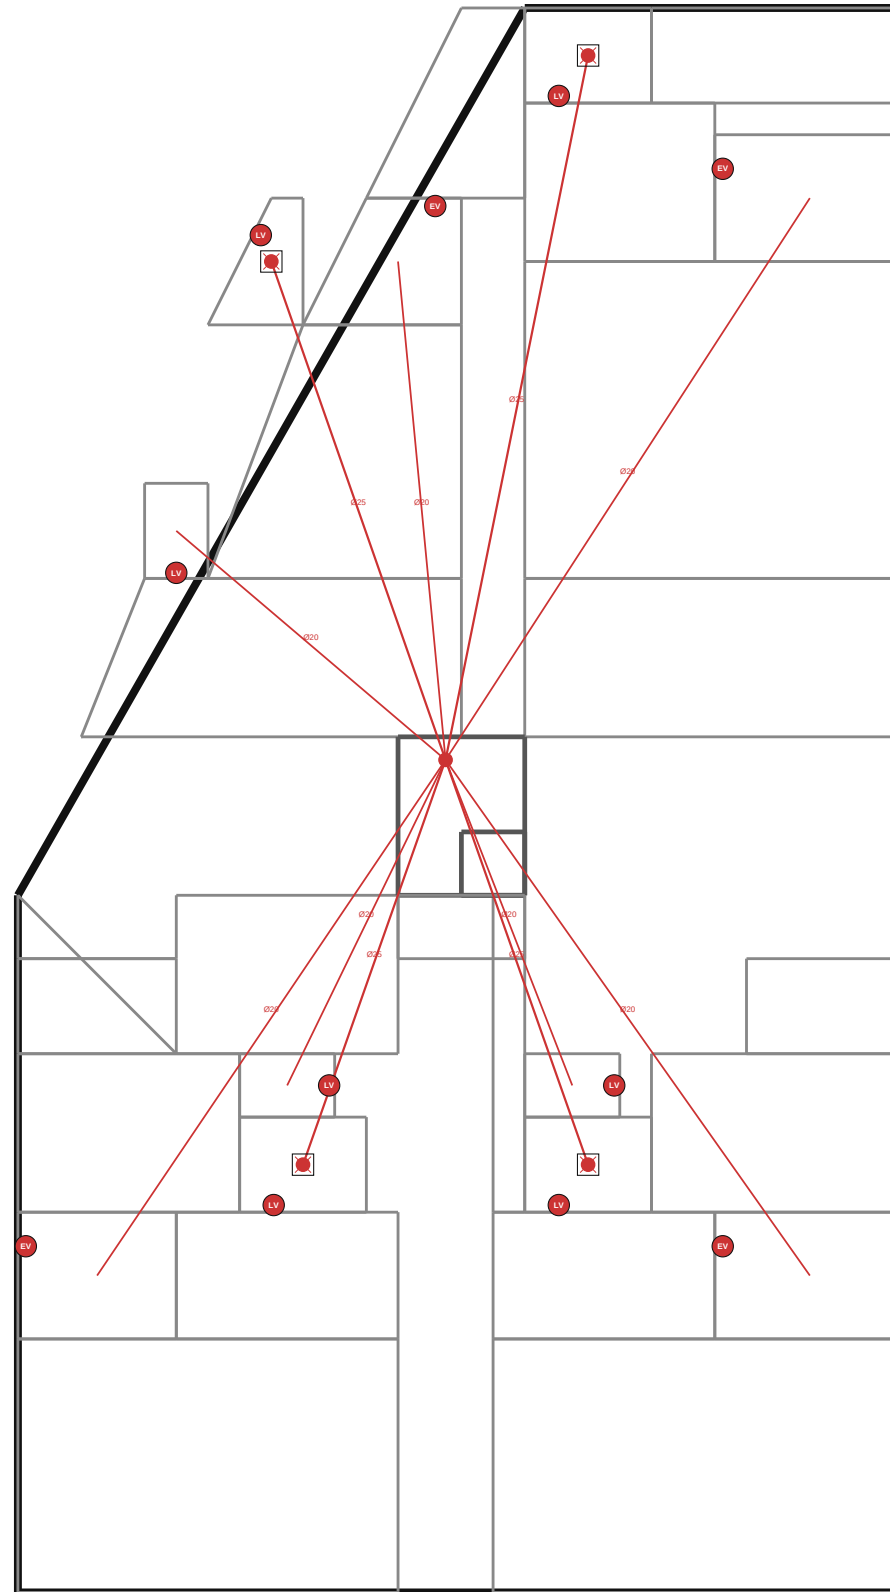

NOMENCLATURE — 410 PLU — Eau Chaude (EC)

- Évier cuisine: 4
- Lavabo: 4
- Douche: 4
- Lave-mains: 3


TIJAN AI Bureau d'Études Automatisé	Résidence Papa Oumar Sakho Dakar, Sénégal	Éch: 1/100 Pl. 36/137
	410 PLU — Eau Chaude (EC) — R+5	
Date: 06/05/2026	Réf: 1711	BIM vPLU-036 Phase: APD

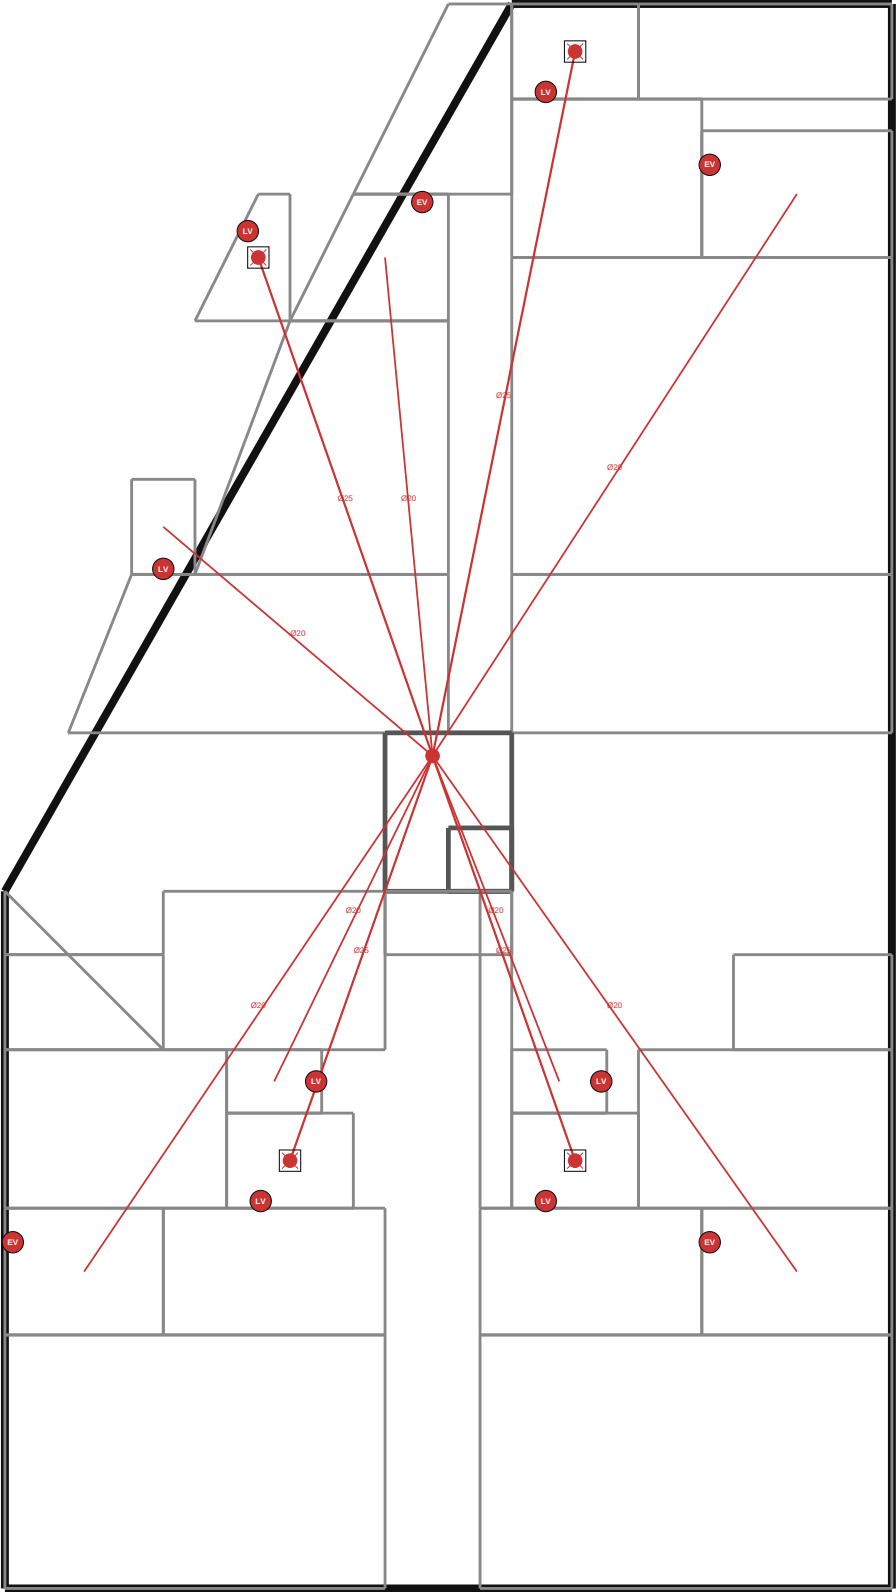

NOMENCLATURE — 410 PLU — Eau Chaude (EC)

- Évier cuisine: 4
- Lavabo: 4
- Douche: 4
- Lave-mains: 3

TIJAN AI Bureau d'Études Automatisé	Résidence Papa Oumar Sakho Dakar, Sénégal	Éch: 1/100 Pl. 37/137
	410 PLU — Eau Chaude (EC) — R+6	
Date: 06/05/2026	Réf: 1711	BIM vPLU-037 Phase: APD

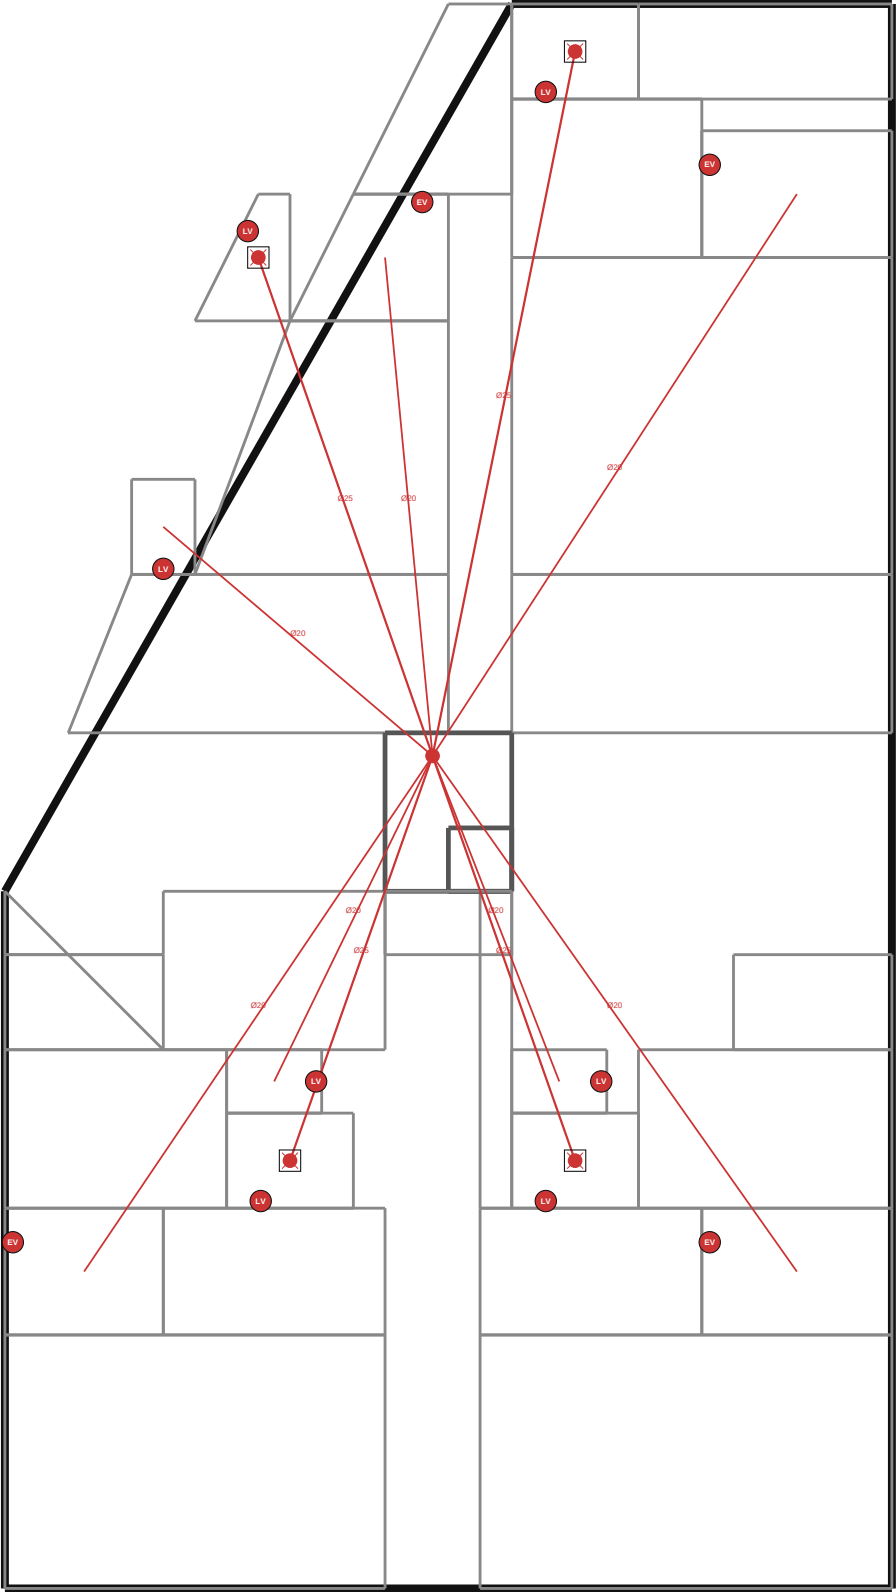

NOMENCLATURE — 410 PLU — Eau Chaude (EC)

- Évier cuisine: 4
- Lavabo: 4
- Douche: 4
- Lave-mains: 3

TIJAN AI

Bureau d'Études Automatisé

Résidence Papa Oumar Sakho

Dakar, Sénégal

Éch: 1/100

Pl. 38/137


410 PLU — Eau Chaude (EC) — R+7

Date: 06/05/2026

Réf: 1711

BIM vPLU-038


Phase: APD

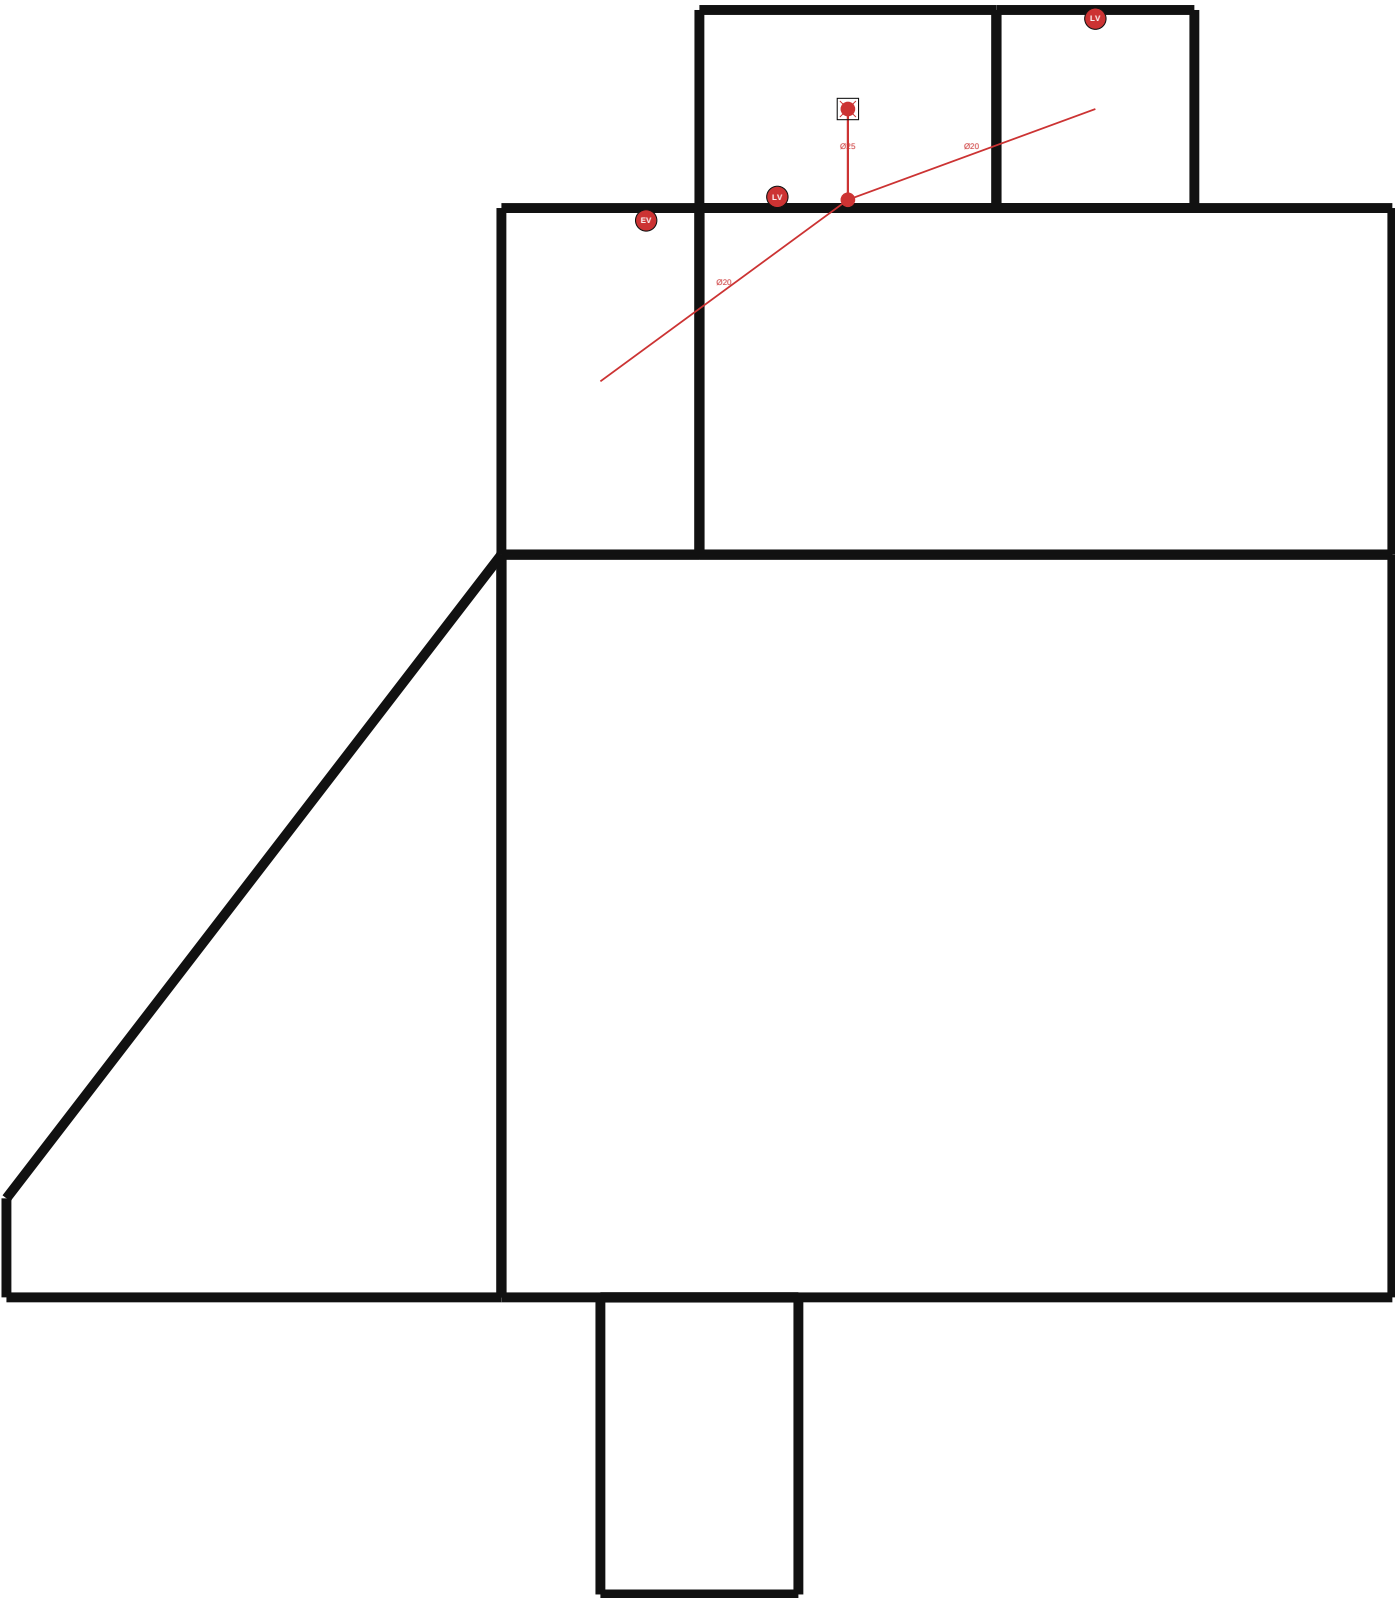

NOMENCLATURE — 410 PLU — Eau Chaude (EC)

- Évier cuisine: 1
- Lavabo: 1
- Douche: 1
- Lave-mains: 1


TIJAN AI Bureau d'Études Automatisé	Résidence Papa Oumar Sakho Dakar, Sénégal	Éch: 1/100 Pl. 39/137
	410 PLU — Eau Chaude (EC) — R+8	
Date: 06/05/2026	Réf: 1711	BIM vPLU-039 Phase: APD

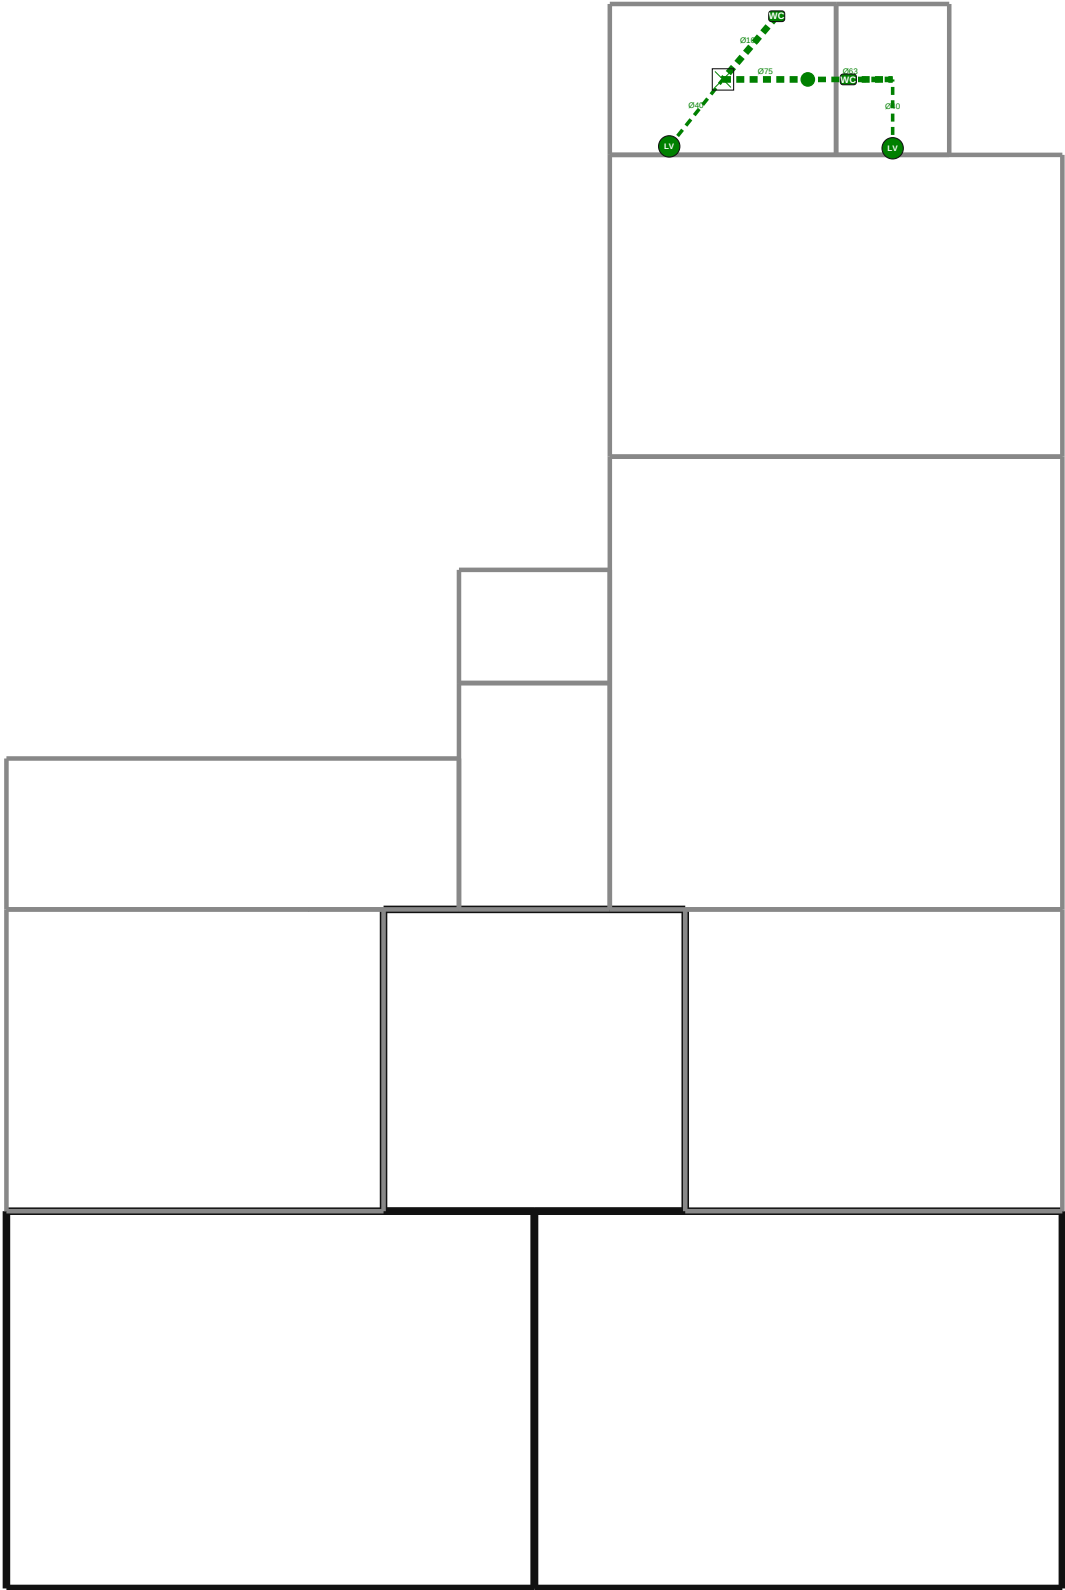

NOMENCLATURE — 410 PLU — Eaux Usées (EU)

- WC suspendu: 2
- Lavabo: 1
- Douche: 1
- Lave-mains: 1


TIJAN AI Bureau d'Études Automatisé	Résidence Papa Oumar Sakho Dakar, Sénégal	Éch: 1/100 Pl. 40/137
	410 PLU — Eaux Usées (EU) — RDC	
Date: 06/05/2026	Réf: 1711	BIM vPLU-040 Phase: APD

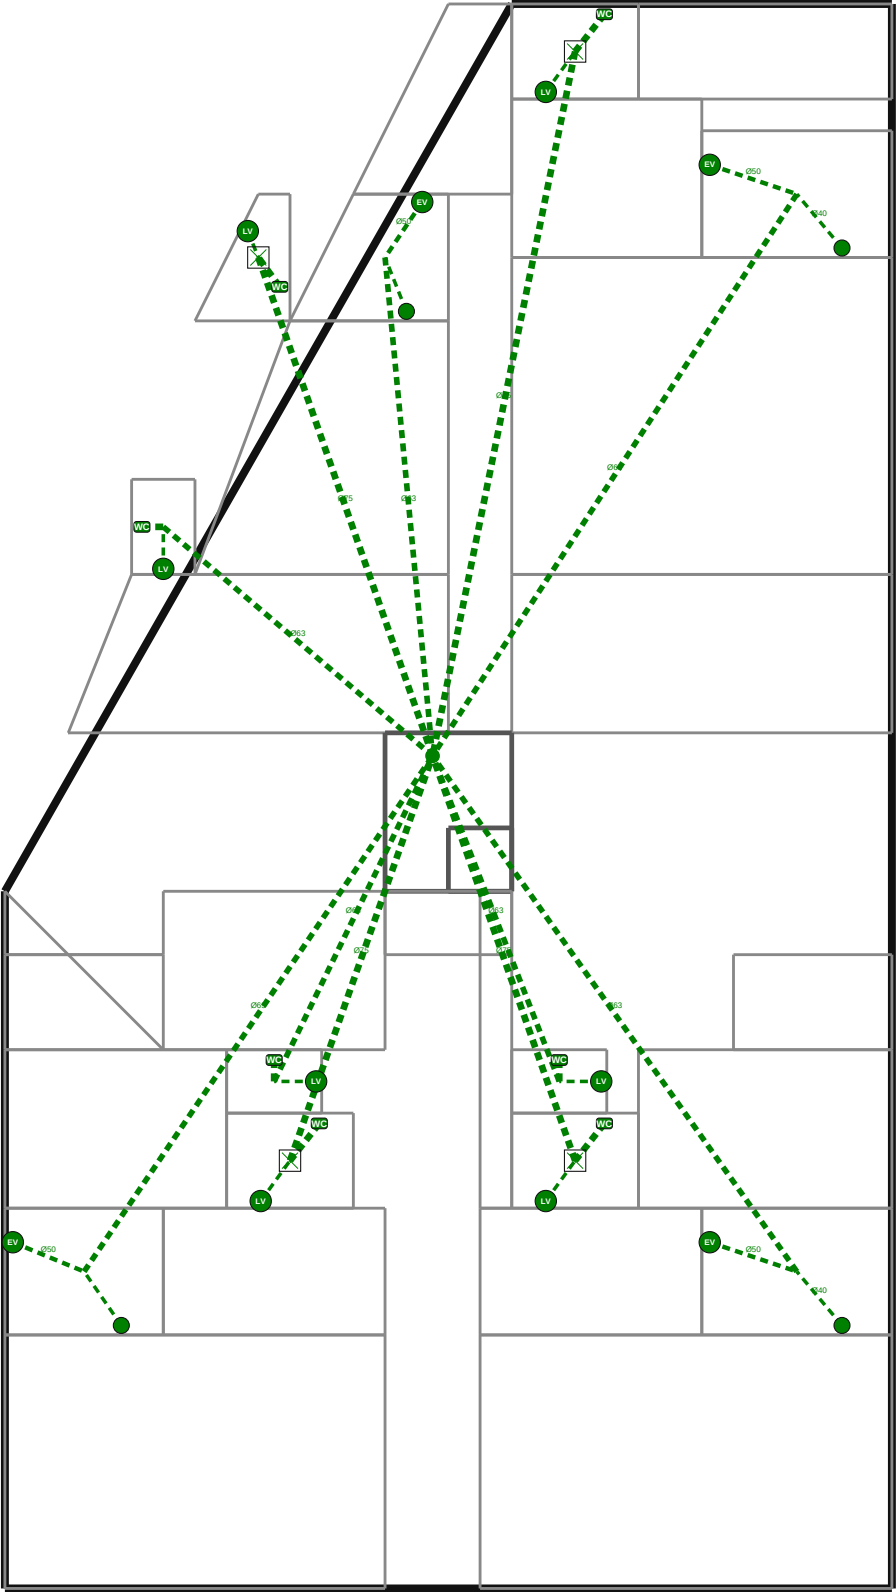

NOMENCLATURE — 410 PLU — Eaux Usées (EU)

- WC suspendu: 7
- Évier cuisine: 4
- Lave-vaisselle: 4
- Lavabo: 4
- Douche: 4
- Lave-mains: 3


TIJAN AI Bureau d'Études Automatisé	Résidence Papa Oumar Sakho Dakar, Sénégal	Éch: 1/100 Pl. 41/137
	410 PLU — Eaux Usées (EU) — R+1	
Date: 06/05/2026	Réf: 1711	BIM vPLU-041 Phase: APD

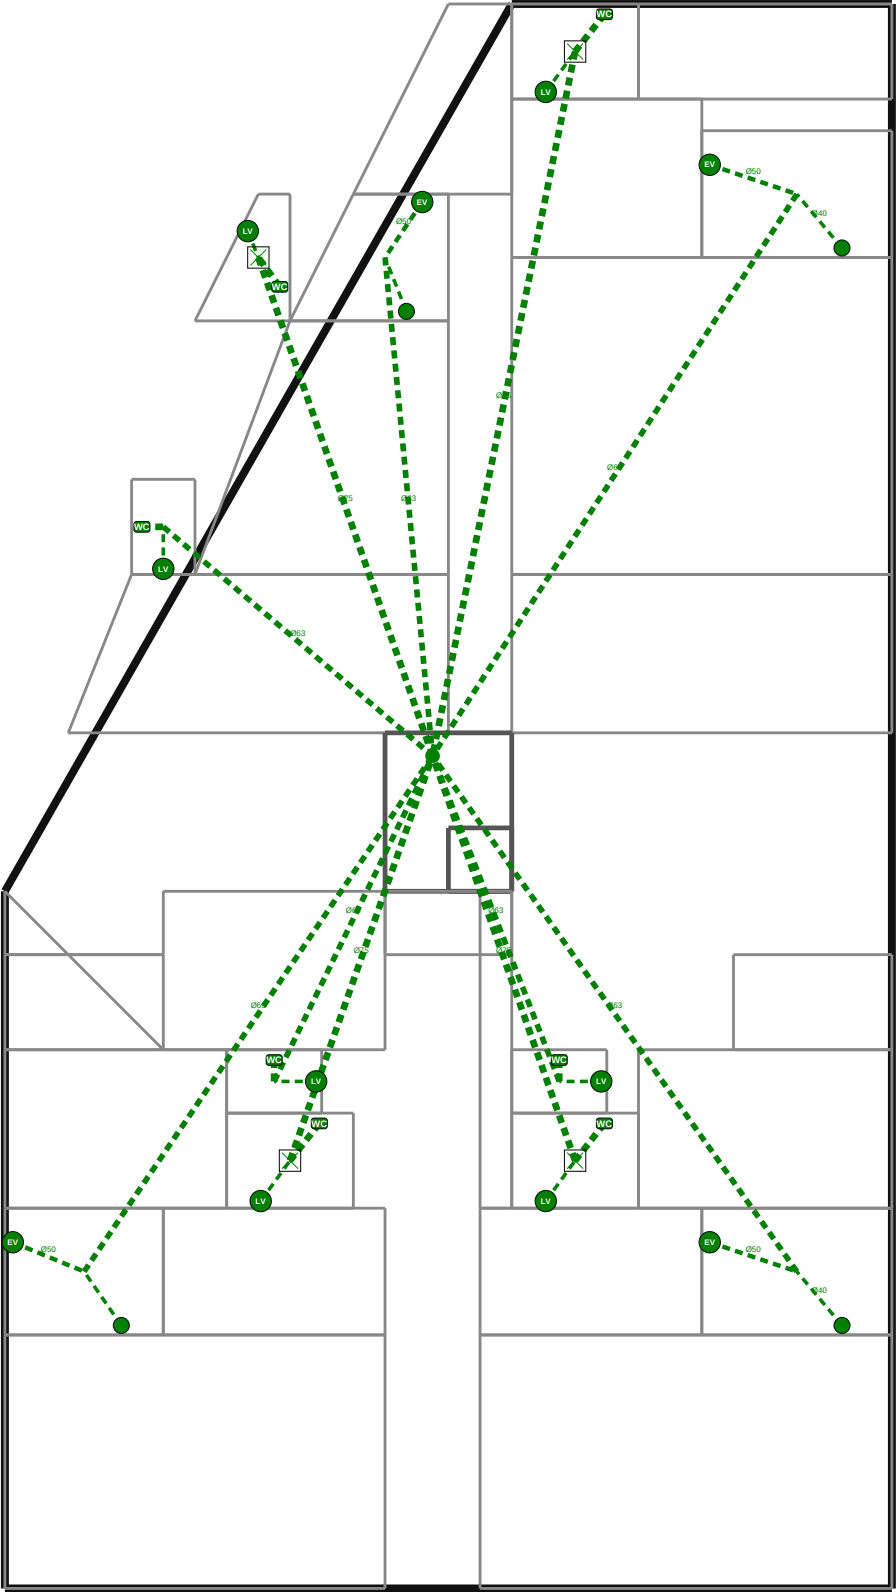

NOMENCLATURE — 410 PLU — Eaux Usées (EU)

- WC suspendu: 7
- Évier cuisine: 4
- Lave-vaisselle: 4
- Lavabo: 4
- Douche: 4
- Lave-mains: 3


TIJAN AI Bureau d'Études Automatisé	Résidence Papa Oumar Sakho Dakar, Sénégal	Éch: 1/100 Pl. 42/137
	410 PLU — Eaux Usées (EU) — R+2	
Date: 06/05/2026	Réf: 1711	BIM vPLU-042 Phase: APD

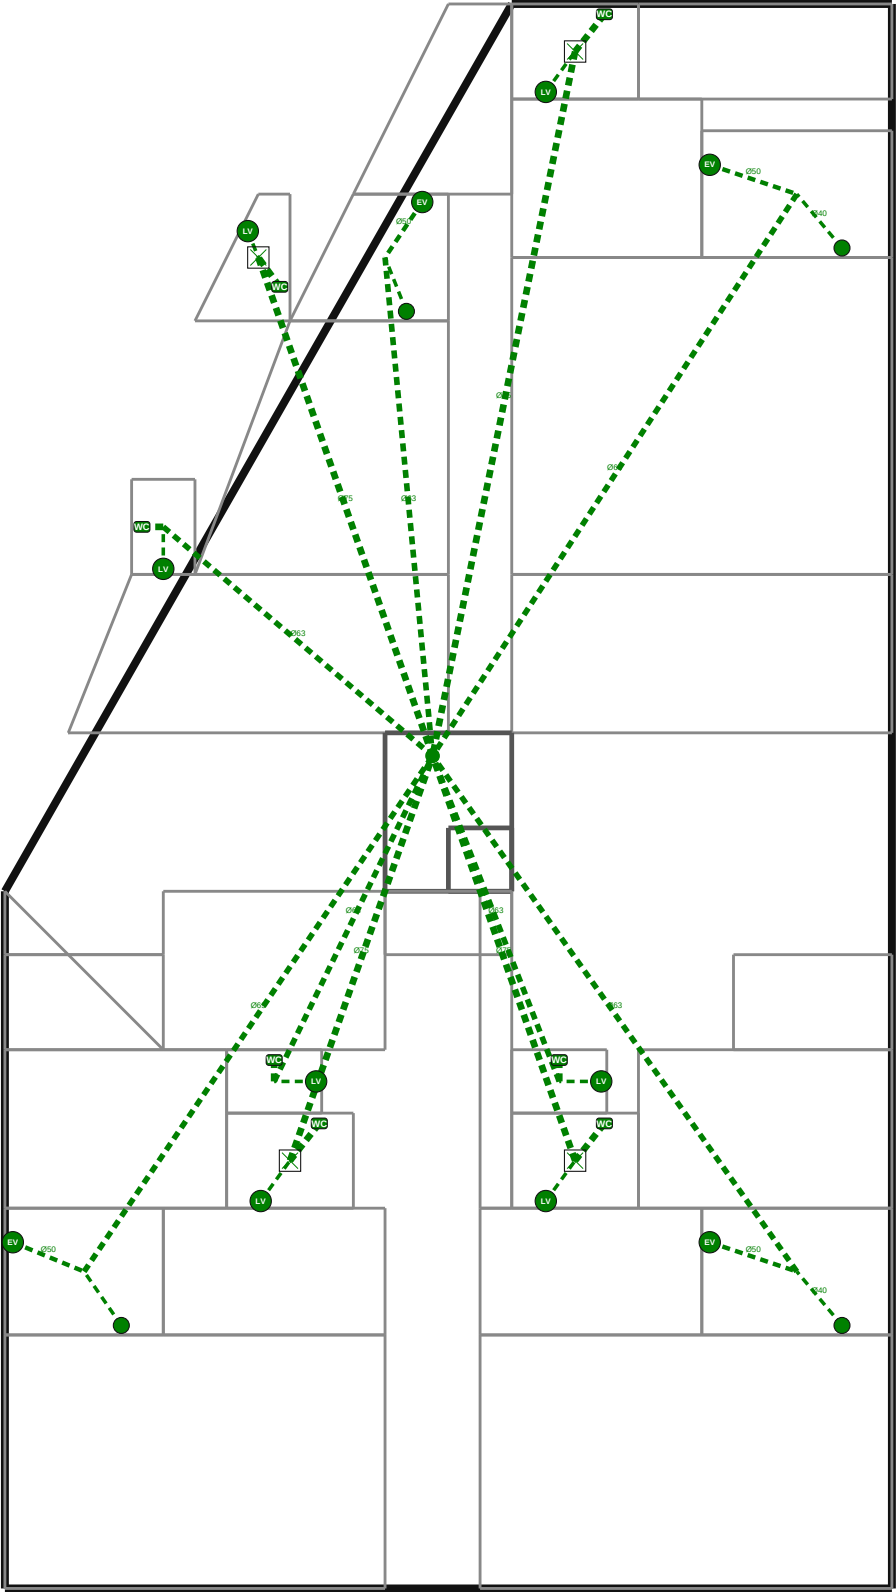

NOMENCLATURE — 410 PLU — Eaux Usées (EU)

- WC suspendu: 7
- Évier cuisine: 4
- Lave-vaisselle: 4
- Lavabo: 4
- Douche: 4
- Lave-mains: 3


TIJAN AI Bureau d'Études Automatisé	Résidence Papa Oumar Sakho Dakar, Sénégal	Éch: 1/100 Pl. 43/137
	410 PLU — Eaux Usées (EU) — R+3	
Date: 06/05/2026	Réf: 1711	BIM vPLU-043 Phase: APD

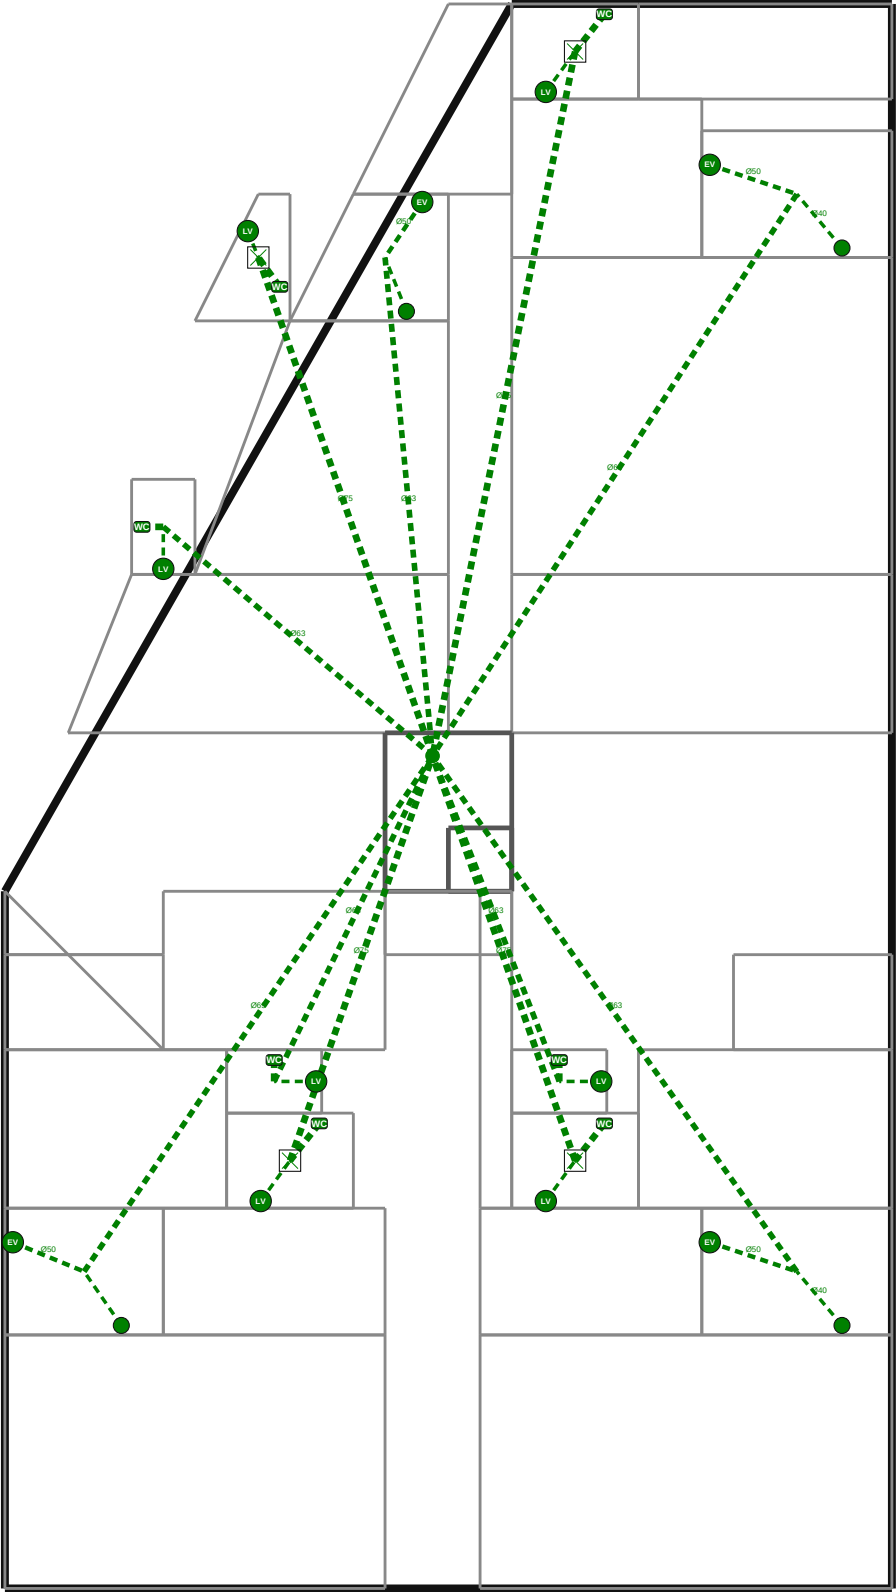

NOMENCLATURE — 410 PLU — Eaux Usées (EU)

- WC suspendu: 7
- Évier cuisine: 4
- Lave-vaisselle: 4
- Lavabo: 4
- Douche: 4
- Lave-mains: 3


TIJAN AI Bureau d'Études Automatisé	Résidence Papa Oumar Sakho Dakar, Sénégal	Éch: 1/100 Pl. 44/137
	410 PLU — Eaux Usées (EU) — R+4	
Date: 06/05/2026	Réf: 1711	BIM vPLU-044 Phase: APD

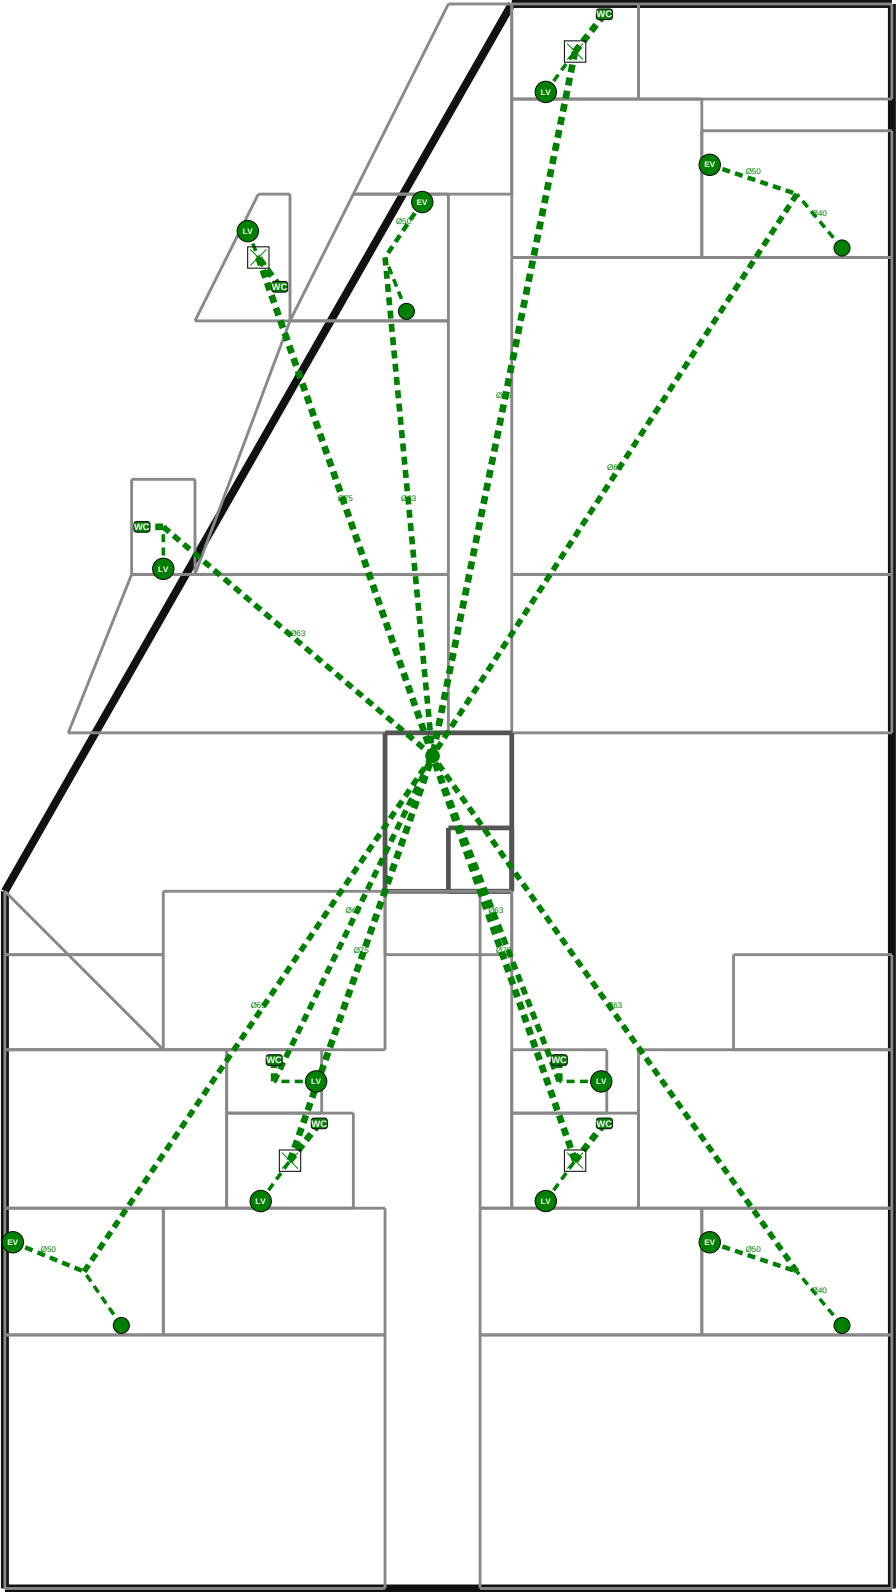

NOMENCLATURE — 410 PLU — Eaux Usées (EU)

- WC suspendu: 7
- Évier cuisine: 4
- Lave-vaisselle: 4
- Lavabo: 4
- Douche: 4
- Lave-mains: 3


TIJAN AI Bureau d'Études Automatisé	Résidence Papa Oumar Sakho Dakar, Sénégal	Éch: 1/100 Pl. 45/137
	410 PLU — Eaux Usées (EU) — R+5	
Date: 06/05/2026	Réf: 1711	BIM vPLU-045 Phase: APD

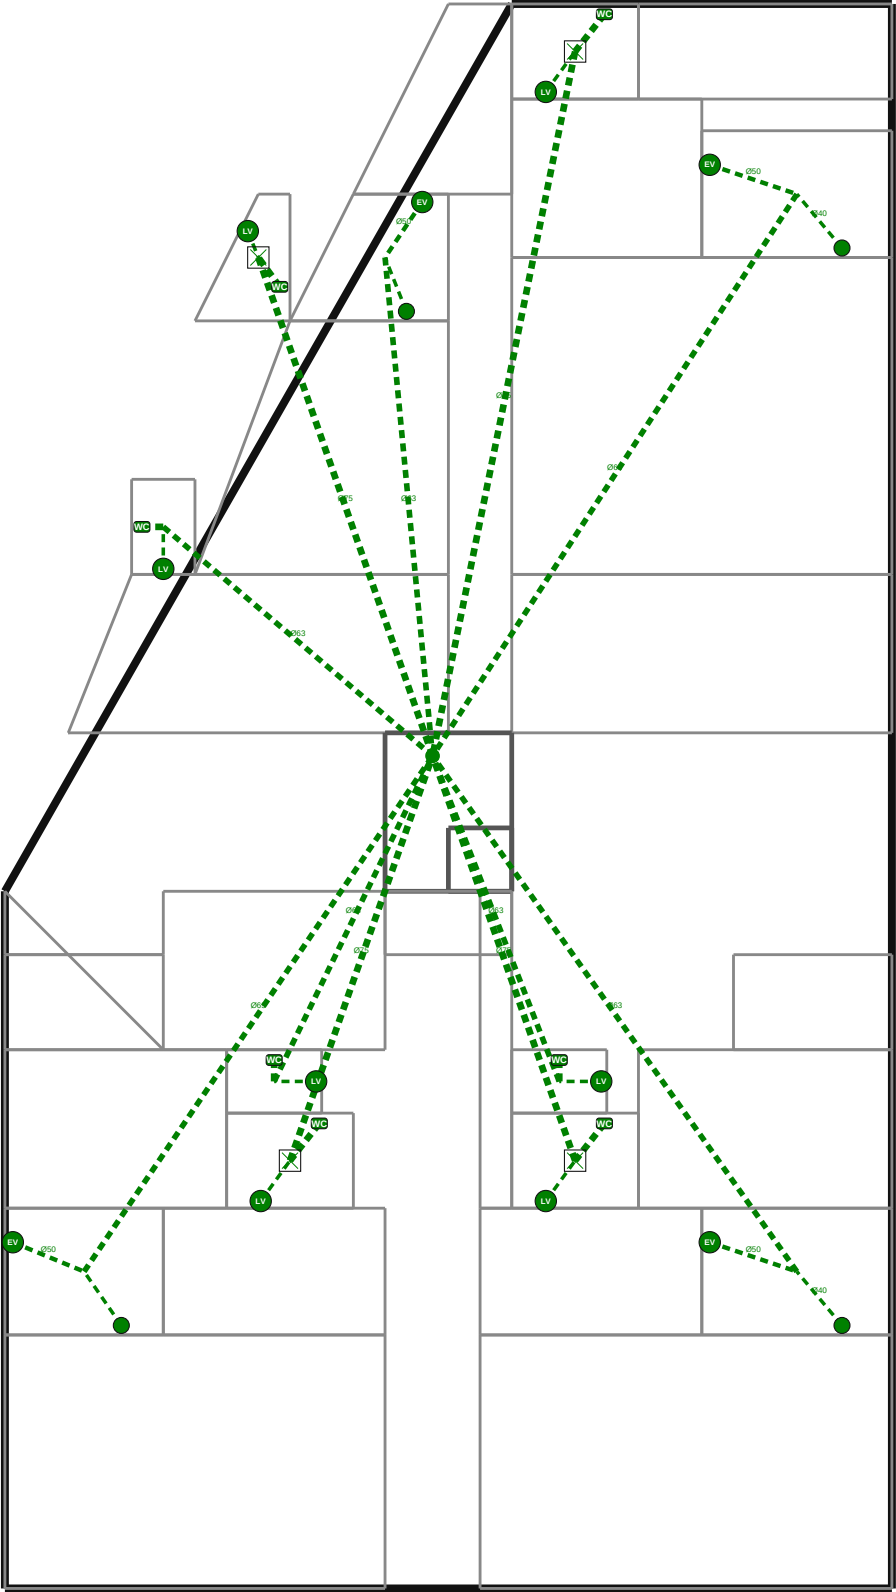

NOMENCLATURE — 410 PLU — Eaux Usées (EU)

- WC suspendu: 7
- Évier cuisine: 4
- Lave-vaisselle: 4
- Lavabo: 4
- Douche: 4
- Lave-mains: 3


TIJAN AI Bureau d'Études Automatisé	Résidence Papa Oumar Sakho Dakar, Sénégal	Éch: 1/100 Pl. 46/137
	410 PLU — Eaux Usées (EU) — R+6	
Date: 06/05/2026	Réf: 1711	BIM vPLU-046 Phase: APD

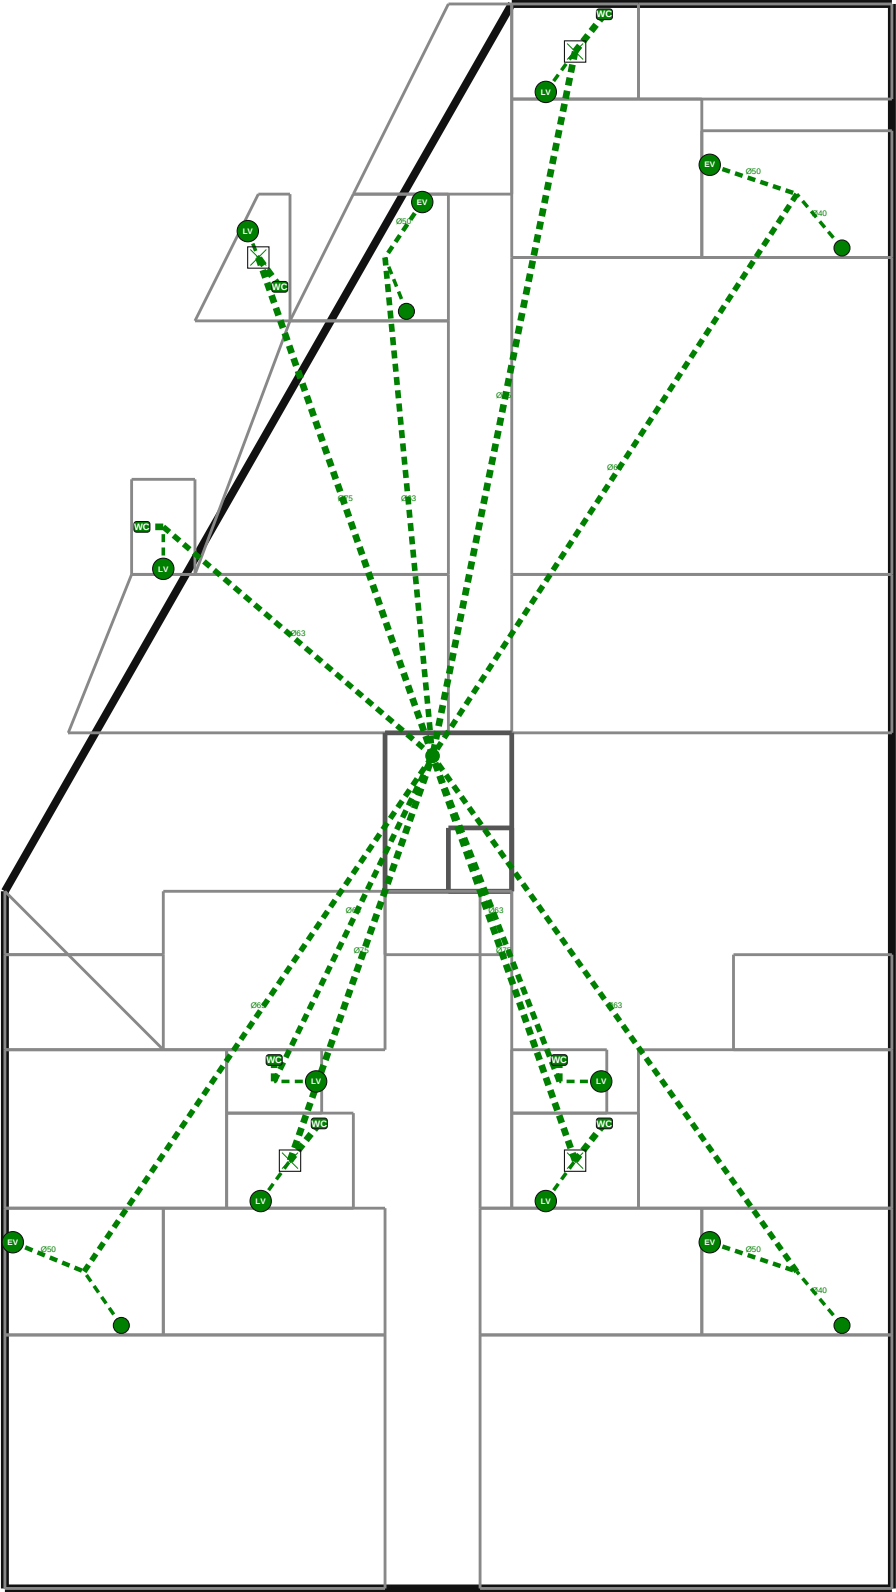

NOMENCLATURE — 410 PLU — Eaux Usées (EU)

- WC suspendu: 7
- Évier cuisine: 4
- Lave-vaisselle: 4
- Lavabo: 4
- Douche: 4
- Lave-mains: 3

TIJAN AI Bureau d'Études Automatisé	Résidence Papa Oumar Sakho Dakar, Sénégal	Éch: 1/100 Pl. 47/137
	410 PLU — Eaux Usées (EU) — R+7	
Date: 06/05/2026	Réf: 1711	BIM vPLU-047 Phase: APD

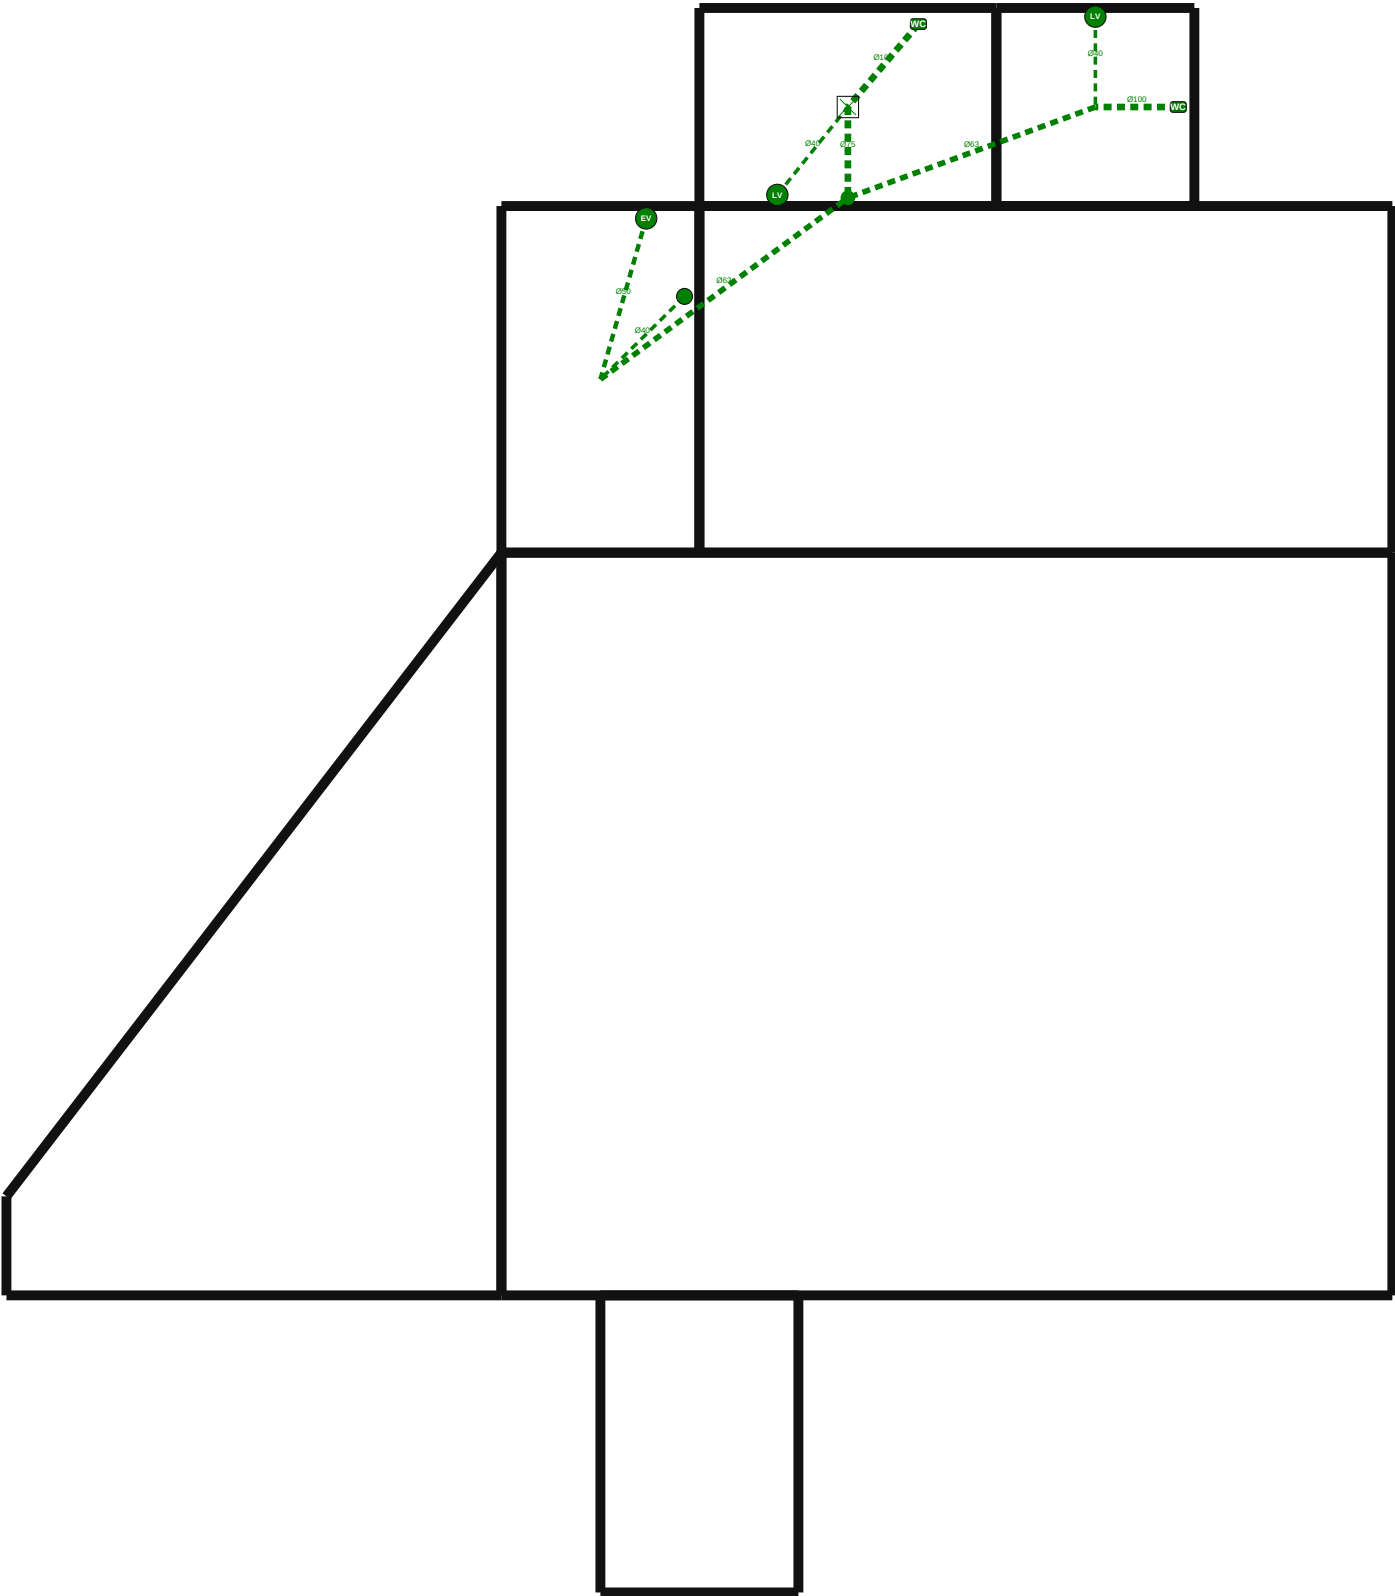


NOMENCLATURE — 410 PLU — Eaux Usées (EU)

- WC suspendu: 2
- Évier cuisine: 1
- Lave-vaisselle: 1
- Lavabo: 1
- Douche: 1
- Lave-mains: 1


TIJAN AI Bureau d'Études Automatisé	Résidence Papa Oumar Sakho Dakar, Sénégal	Éch: 1/100 Pl. 48/137
	410 PLU — Eaux Usées (EU) — R+8	
Date: 06/05/2026	Réf: 1711	BIM vPLU-048 Phase: APD

NOMENCLATURE — 413 HVC — Climatisation (CLIM)

• Split climatiseur: 3

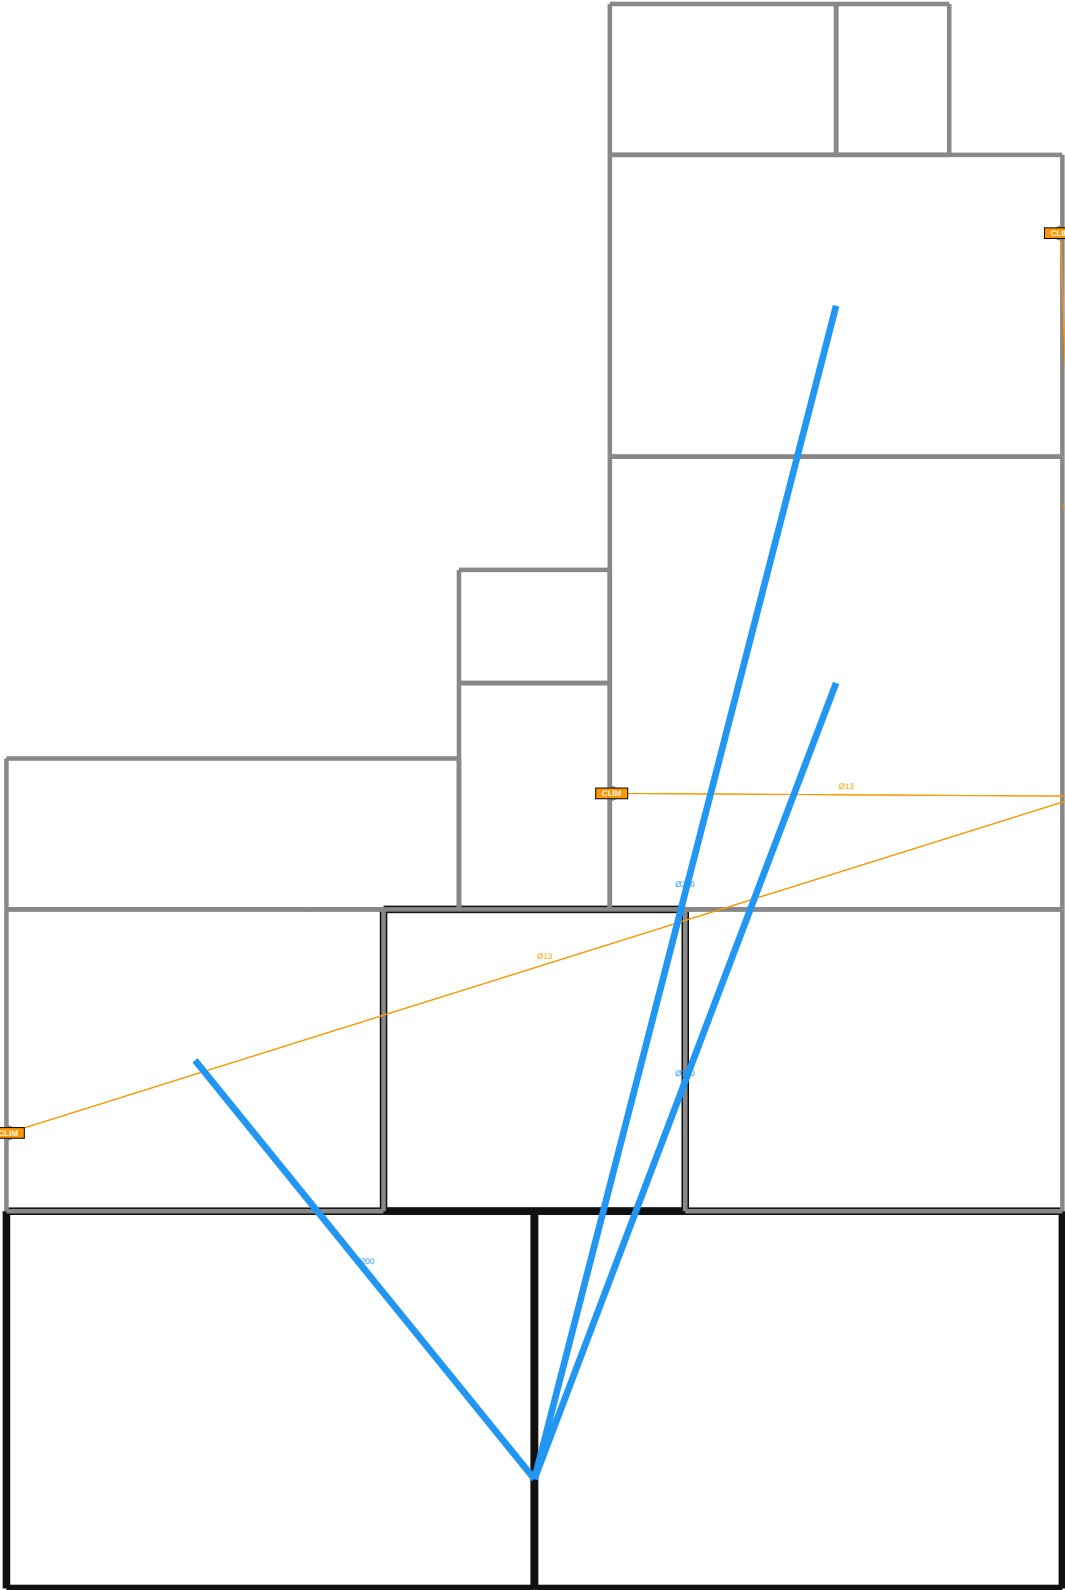


TIJAN AI Bureau d'Études Automatisé	Résidence Papa Oumar Sakho Dakar, Sénégal	Éch: 1/100 Pl. 49/137
	413 HVC — Climatisation (CLIM) — RDC	
Date: 06/05/2026	Réf: 1711	BIM vHVC-049 Phase: APD

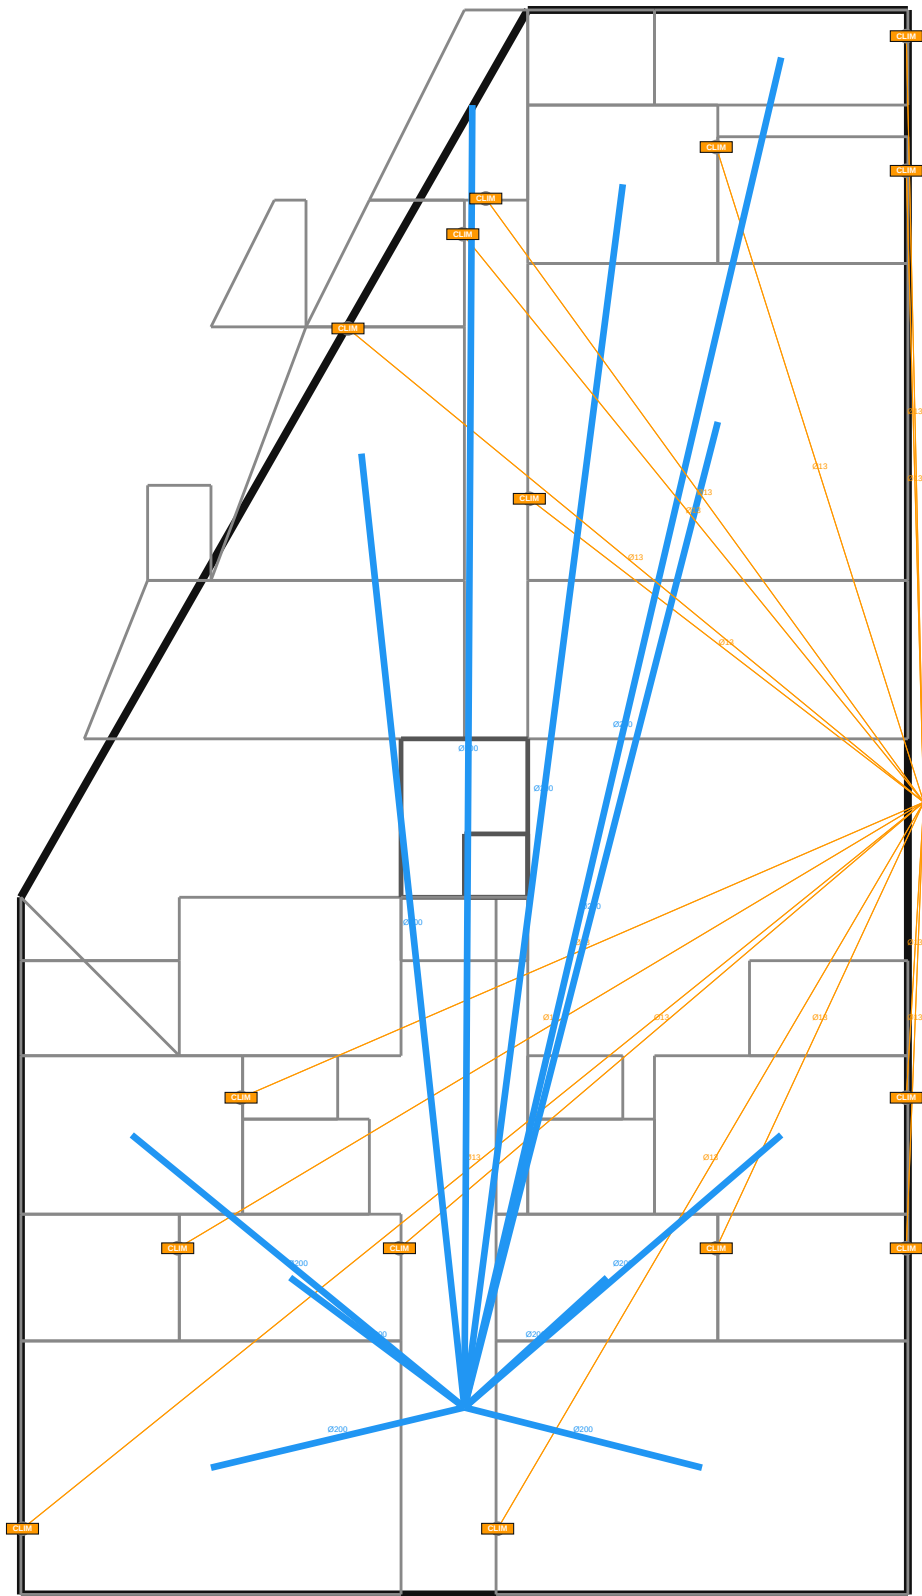

NOMENCLATURE — 413 HVC — Climatisation (CLIM)

• Split climatiseur: 15


TIJAN AI Bureau d'Études Automatisé	Résidence Papa Oumar Sakho Dakar, Sénégal	Éch: 1/100 Pl. 50/137
	413 HVC — Climatisation (CLIM) — R+1	
Date: 06/05/2026	Réf: 1711	BIM vHVC-050 Phase: APD

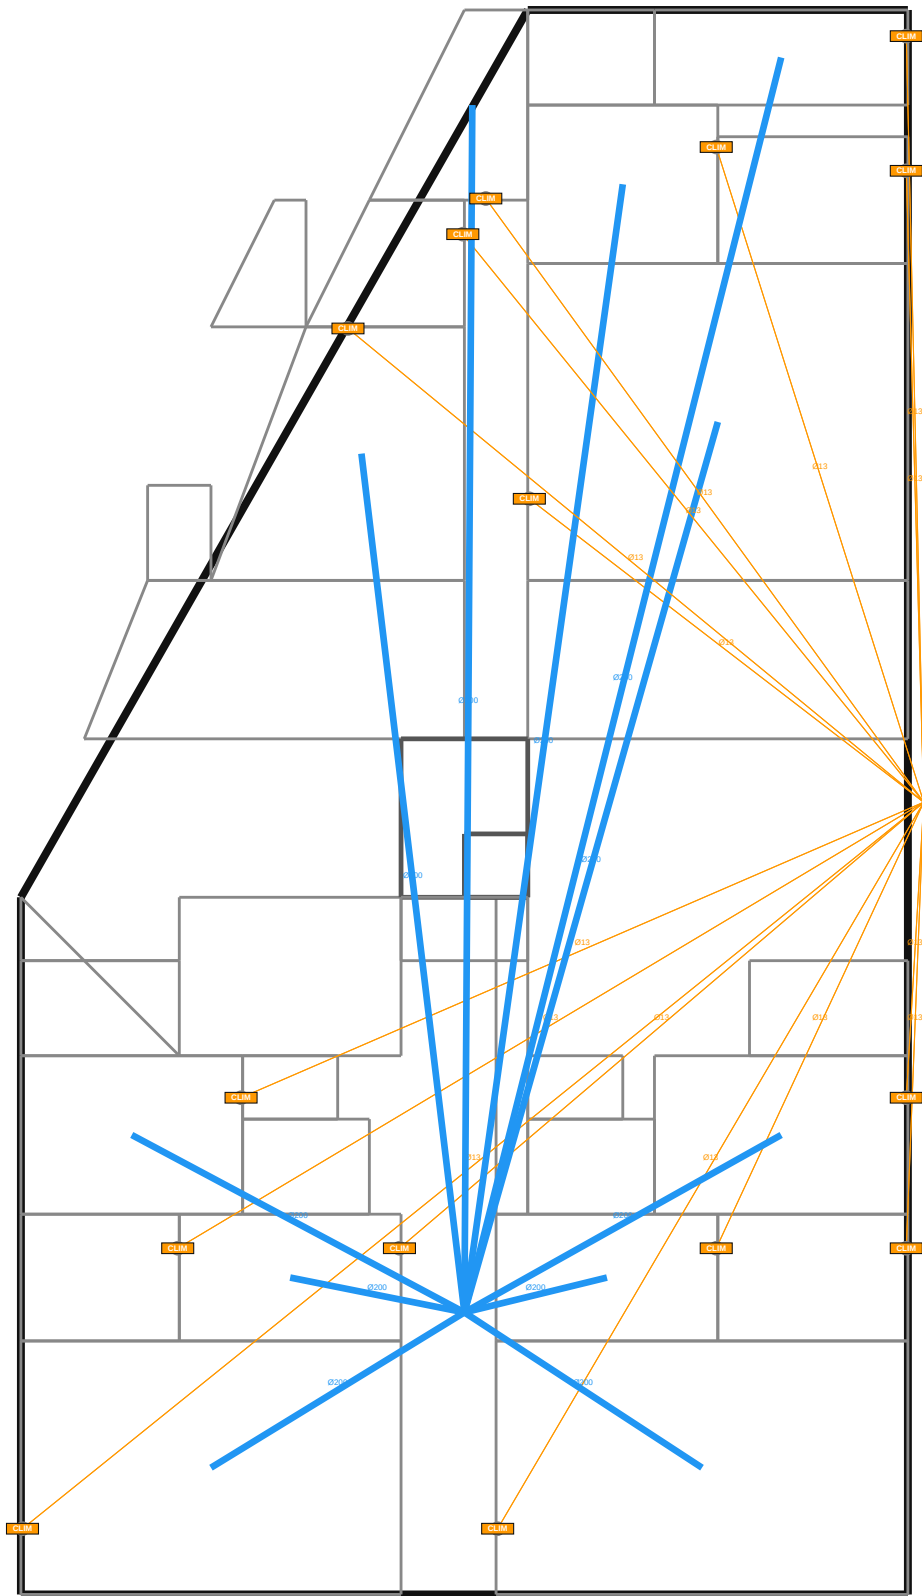

NOMENCLATURE — 413 HVC — Climatisation (CLIM)

• Split climatiseur: 15


TIJAN AI Bureau d'Études Automatisé	Résidence Papa Oumar Sakho Dakar, Sénégal	Éch: 1/100 Pl. 51/137
	413 HVC — Climatisation (CLIM) — R+2	
Date: 06/05/2026	Réf: 1711	BIM vHVC-051 Phase: APD

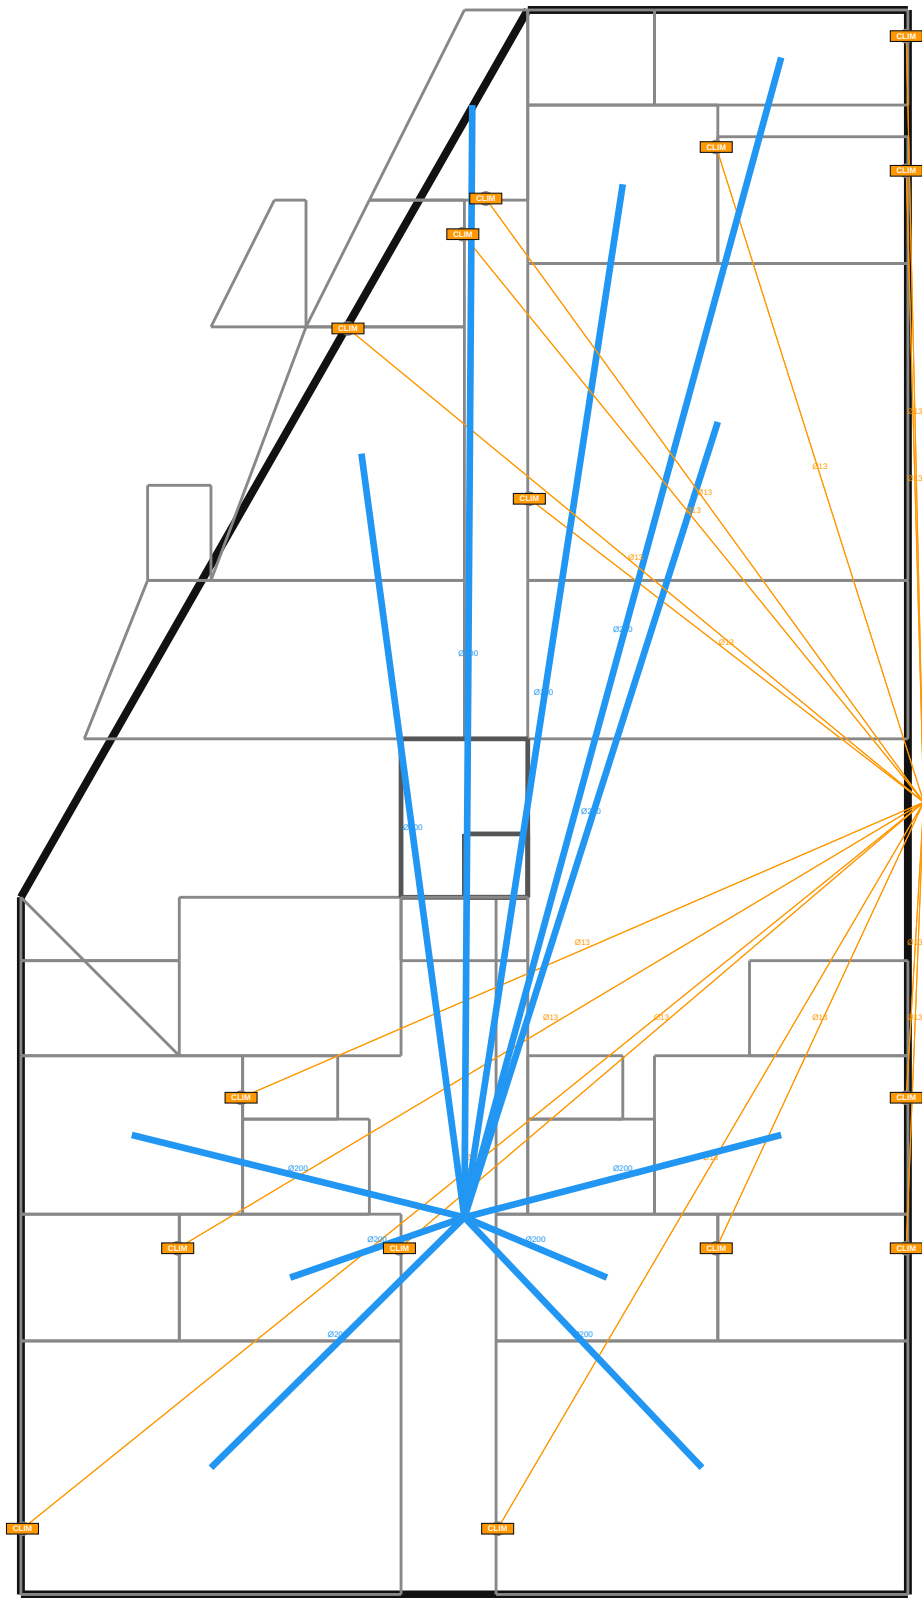

NOMENCLATURE — 413 HVC — Climatisation (CLIM)

• Split climatiseur: 15

TIJAN AI Bureau d'Études Automatisé	Résidence Papa Oumar Sakho Dakar, Sénégal	Éch: 1/100 Pl. 52/137
	413 HVC — Climatisation (CLIM) — R+3	
Date: 06/05/2026	Réf: 1711	BIM vHVC-052 Phase: APD

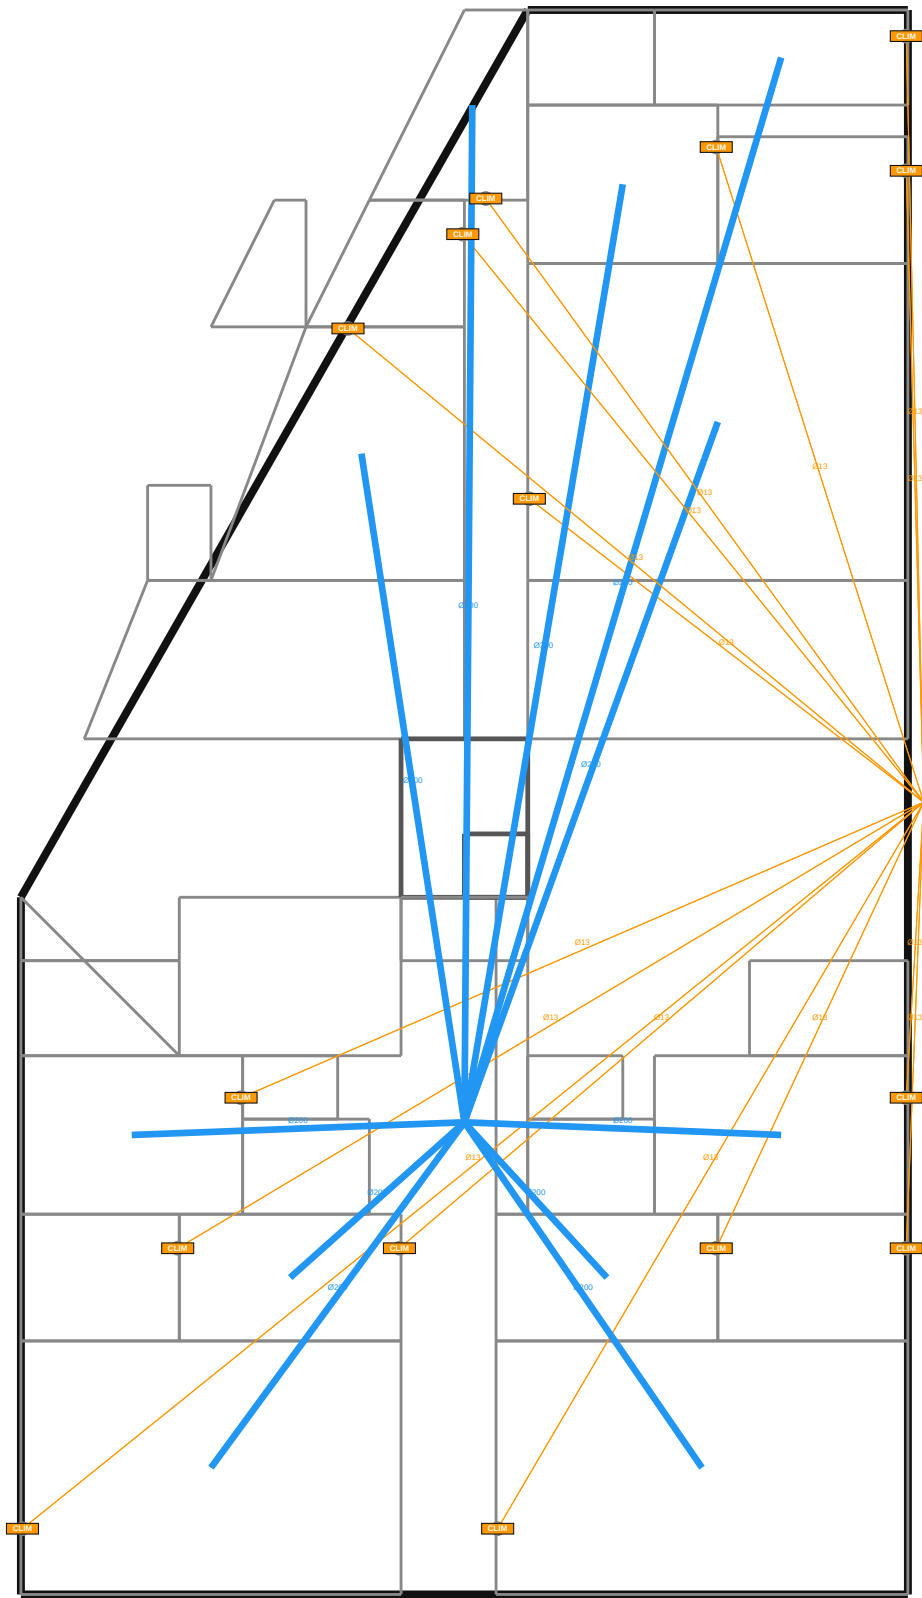

NOMENCLATURE — 413 HVC — Climatisation (CLIM)

• Split climatiseur: 15

TIJAN AI

Bureau d'Études Automatisé

Résidence Papa Oumar Sakho

Dakar, Sénégal

Éch: 1/100

Pl. 53/137


413 HVC — Climatisation (CLIM) — R+4

Date: 06/05/2026

Réf: 1711

BIM vHVC-053


Phase: APD

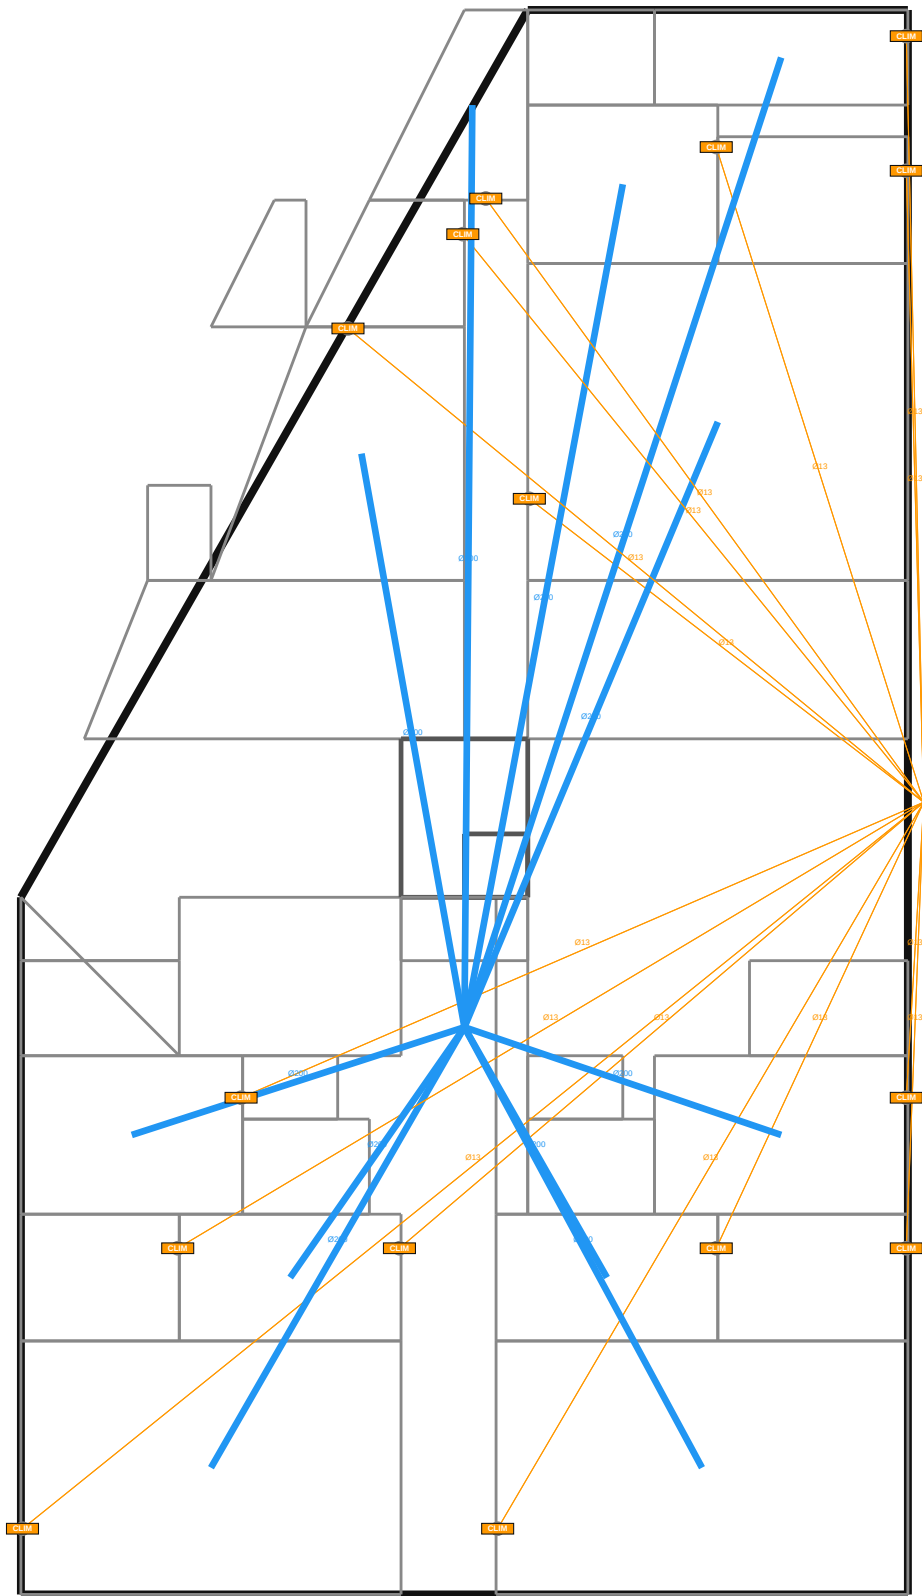

NOMENCLATURE — 413 HVC — Climatisation (CLIM)

• Split climatiseur: 15


TIJAN AI Bureau d'Études Automatisé	Résidence Papa Oumar Sakho Dakar, Sénégal	Éch: 1/100 Pl. 54/137
	413 HVC — Climatisation (CLIM) — R+5	
Date: 06/05/2026	Réf: 1711	BIM vHVC-054 Phase: APD

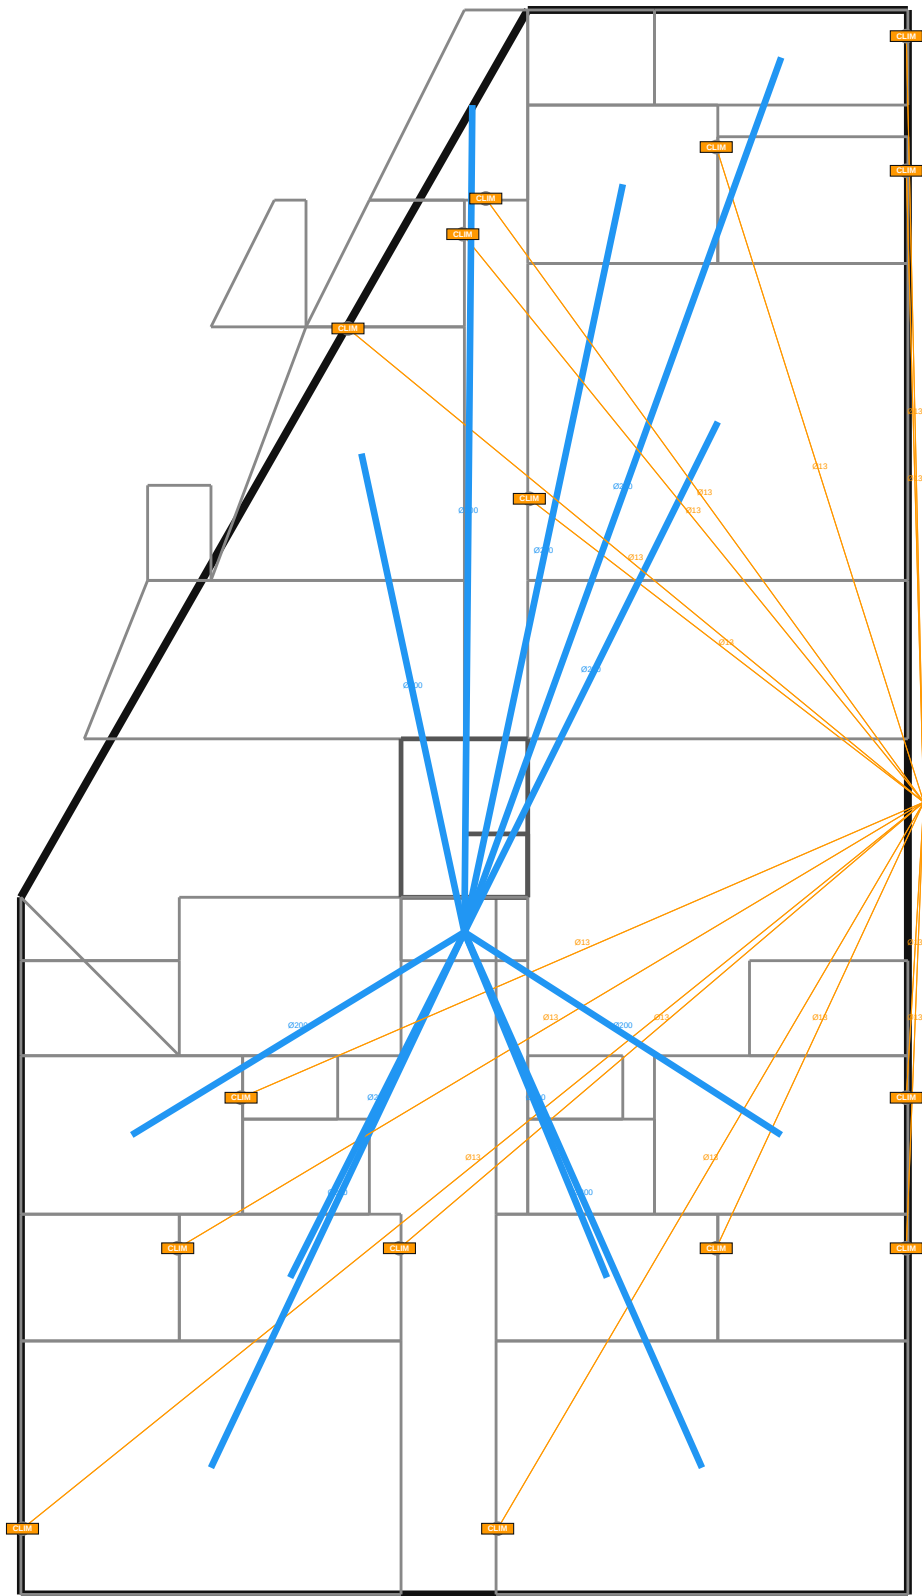

NOMENCLATURE — 413 HVC — Climatisation (CLIM)

• Split climatiseur: 15


TIJAN AI Bureau d'Études Automatisé	Résidence Papa Oumar Sakho Dakar, Sénégal	Éch: 1/100 Pl. 55/137
	413 HVC — Climatisation (CLIM) — R+6	
Date: 06/05/2026	Réf: 1711	BIM vHVC-055 Phase: APD

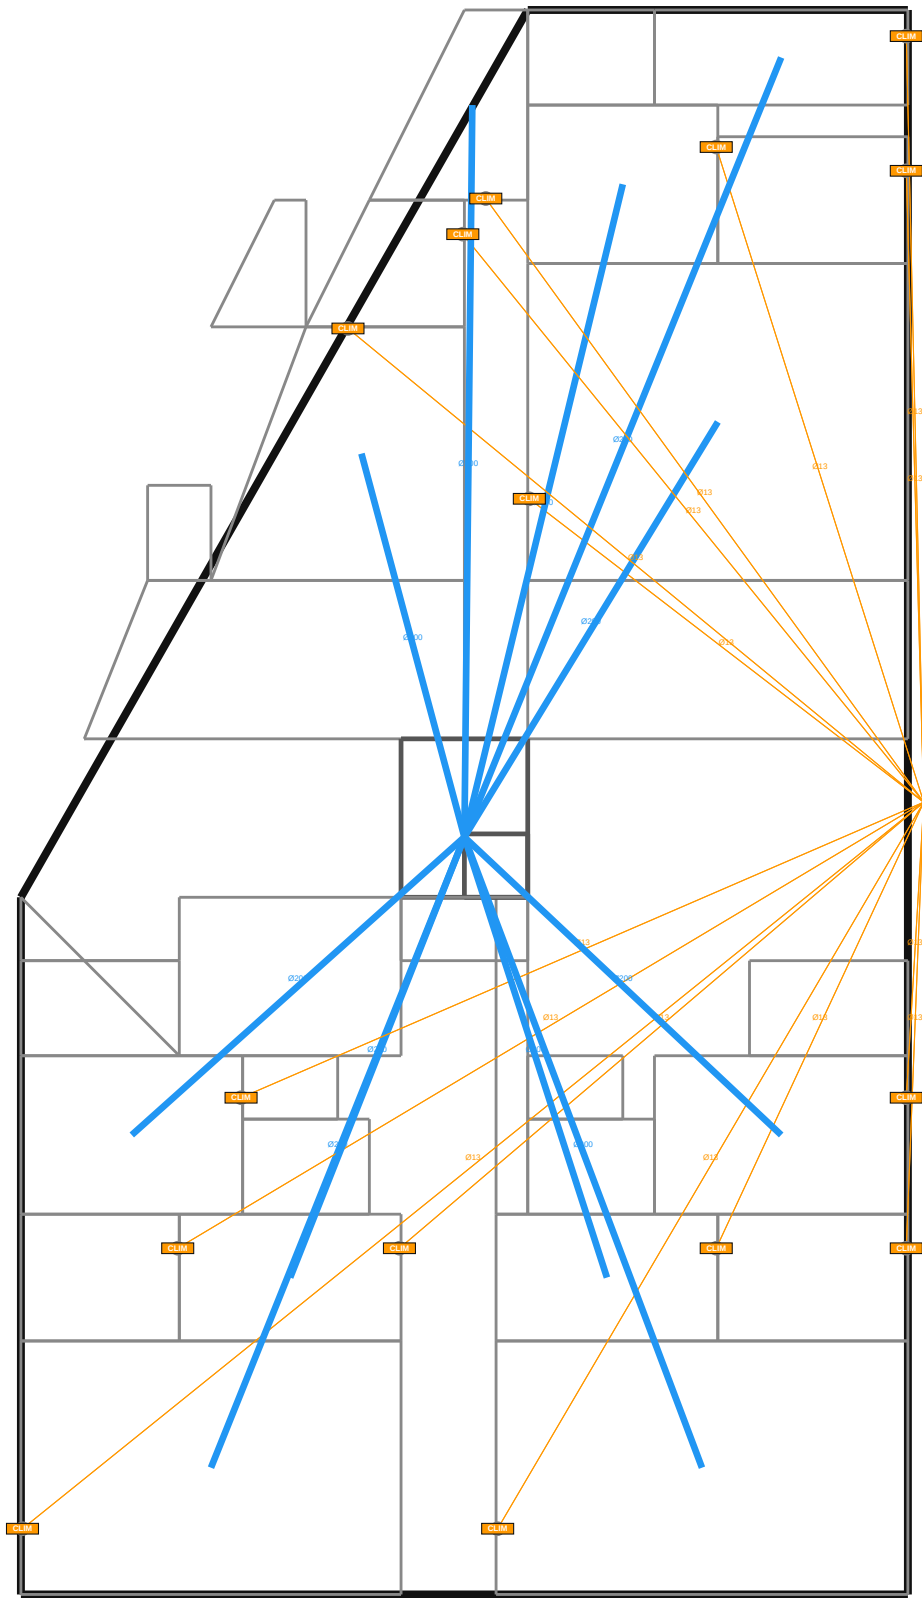

NOMENCLATURE — 413 HVC — Climatisation (CLIM)

• Split climatiseur: 15

TIJAN AI Bureau d'Études Automatisé	Résidence Papa Oumar Sakho Dakar, Sénégal	Éch: 1/100 Pl. 56/137
	413 HVC — Climatisation (CLIM) — R+7	
Date: 06/05/2026	Réf: 1711	BIM vHVC-056 Phase: APD

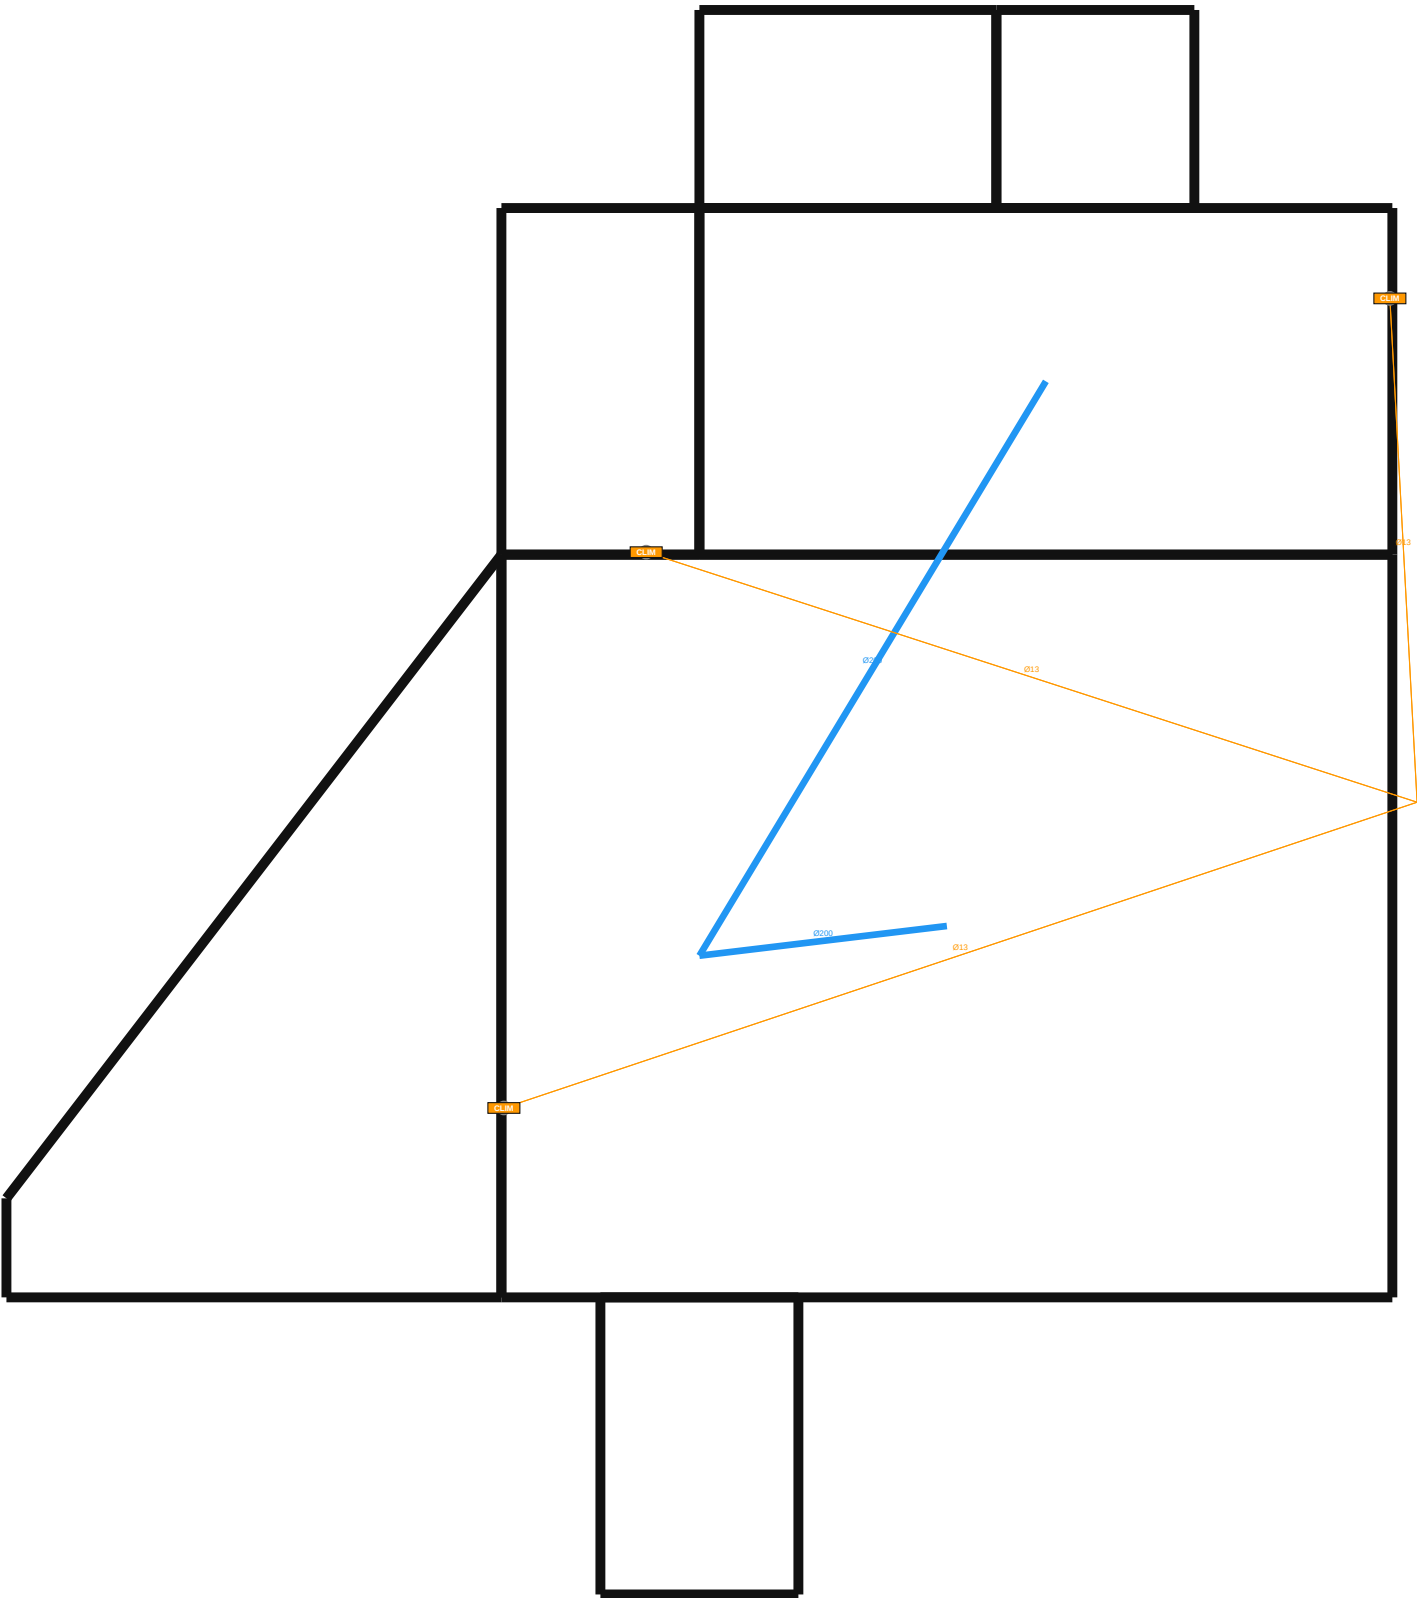


NOMENCLATURE — 413 HVC — Climatisation (CLIM)

• Split climatiseur: 3

TIJAN AI Bureau d'Études Automatisé	Résidence Papa Oumar Sakho Dakar, Sénégal	Éch: 1/100 Pl. 57/137
	413 HVC — Climatisation (CLIM) — R+8	
Date: 06/05/2026	Réf: 1711	BIM vHVC-057 Phase: APD


413 HVC — Ventilation (VMC) — Sous-Sol

 

NOMENCLATURE — 413 HVC — Ventilation (VMC)

• Bouche VMC: 1


TIJAN AI Bureau d'Études Automatisé	Résidence Papa Oumar Sakho Dakar, Sénégal	Éch: 1/100 Pl. 58/137
	413 HVC — Ventilation (VMC) — Sous-Sol	
Date: 06/05/2026	Réf: 1711	BIM vHVC-058 Phase: APD

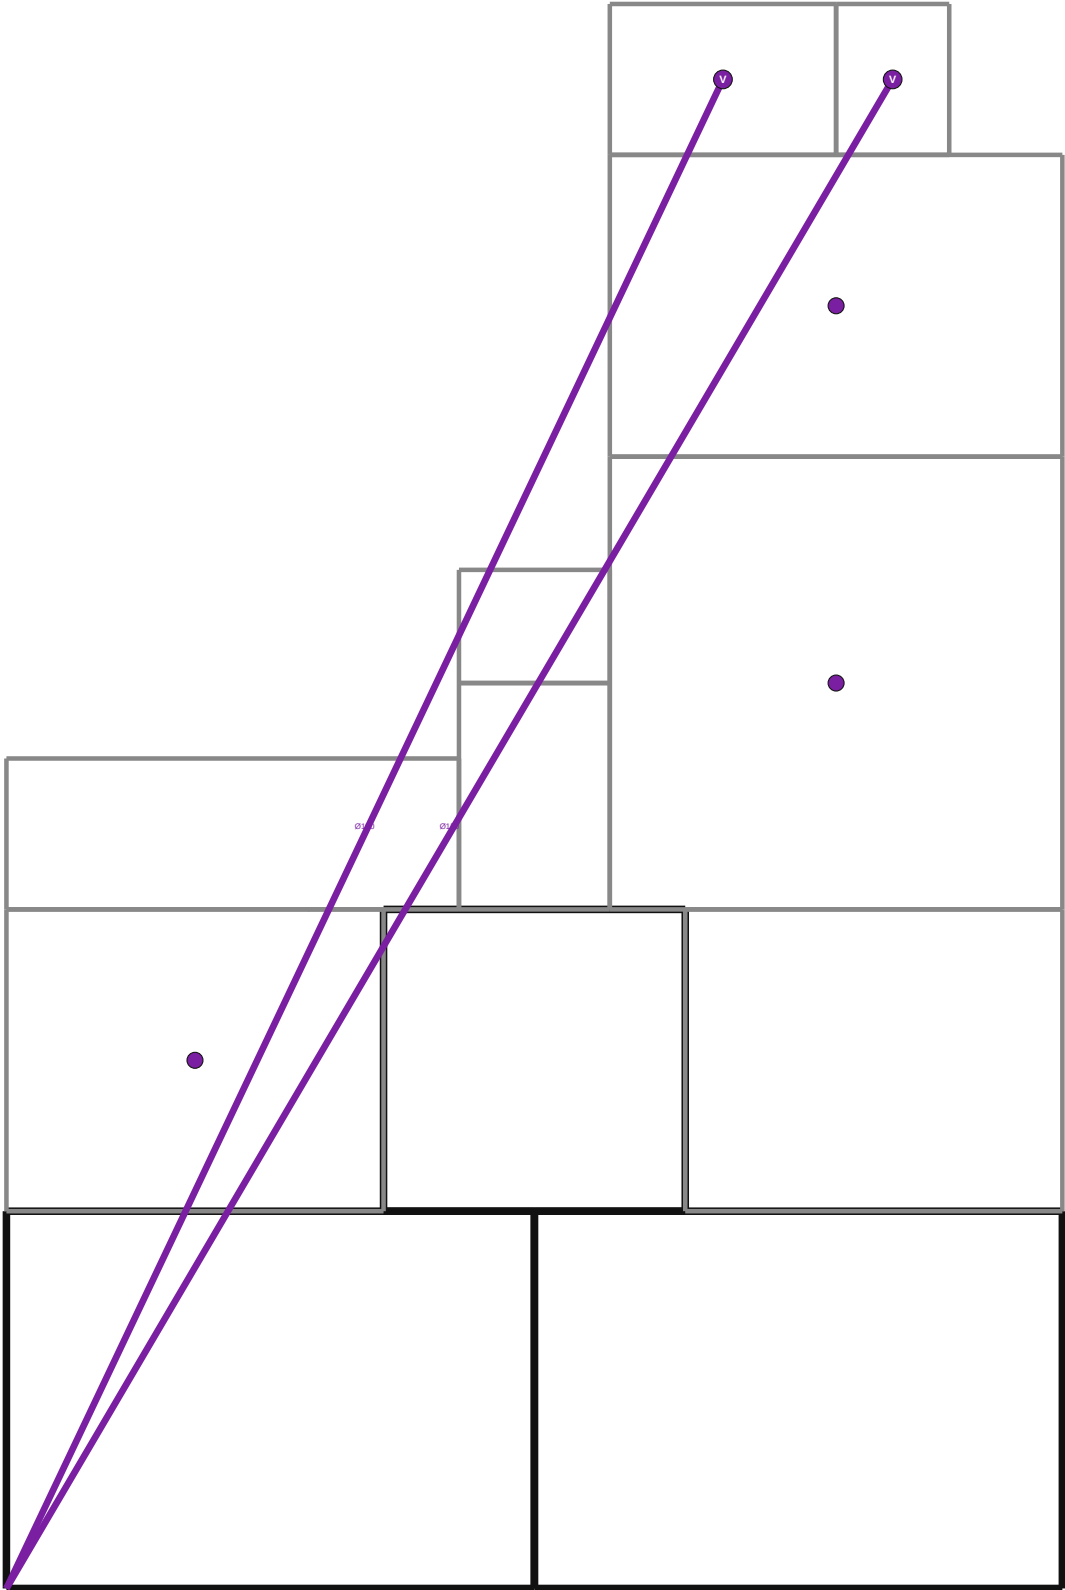

NOMENCLATURE — 413 HVC — Ventilation (VMC)

- Grille soufflage: 3
- Bouche VMC extraction: 2


TIJAN AI Bureau d'Études Automatisé	Résidence Papa Oumar Sakho Dakar, Sénégal	Éch: 1/100 Pl. 59/137
	413 HVC — Ventilation (VMC) — RDC	
Date: 06/05/2026	Réf: 1711	BIM vHVC-059 Phase: APD

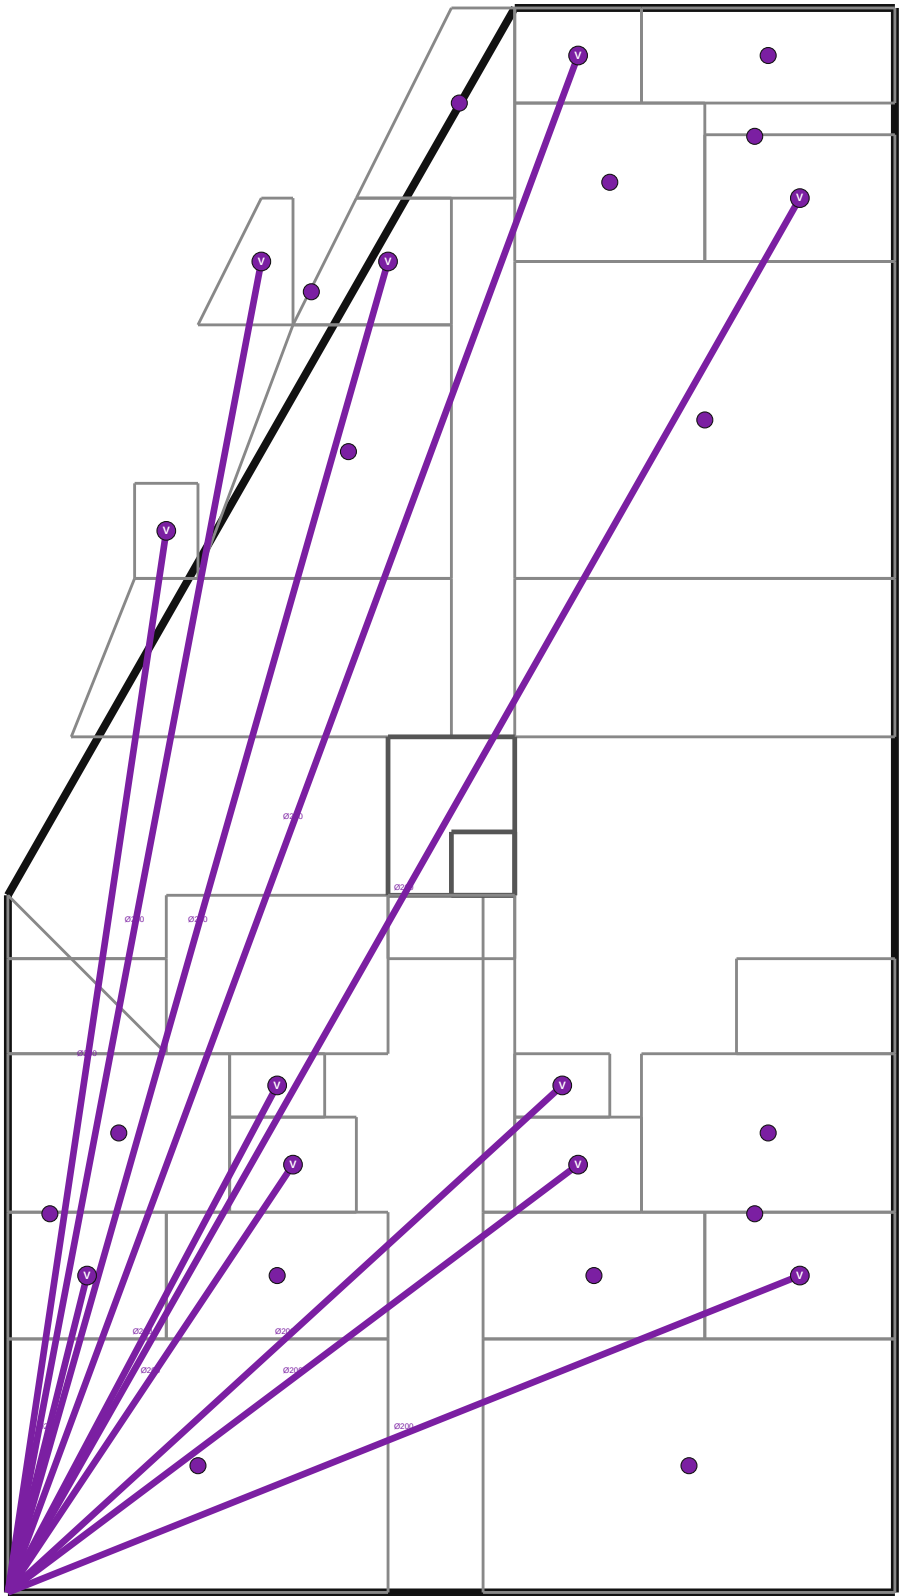

NOMENCLATURE — 413 HVC — Ventilation (VMC)

- Grille soufflage: 11
- Bouche VMC extraction: 11
- Hotte aspirante: 4


TIJAN AI Bureau d'Études Automatisé	Résidence Papa Oumar Sakho Dakar, Sénégal	Éch: 1/100 Pl. 60/137
	413 HVC — Ventilation (VMC) — R+1	
Date: 06/05/2026	Réf: 1711	BIM vHVC-060 Phase: APD

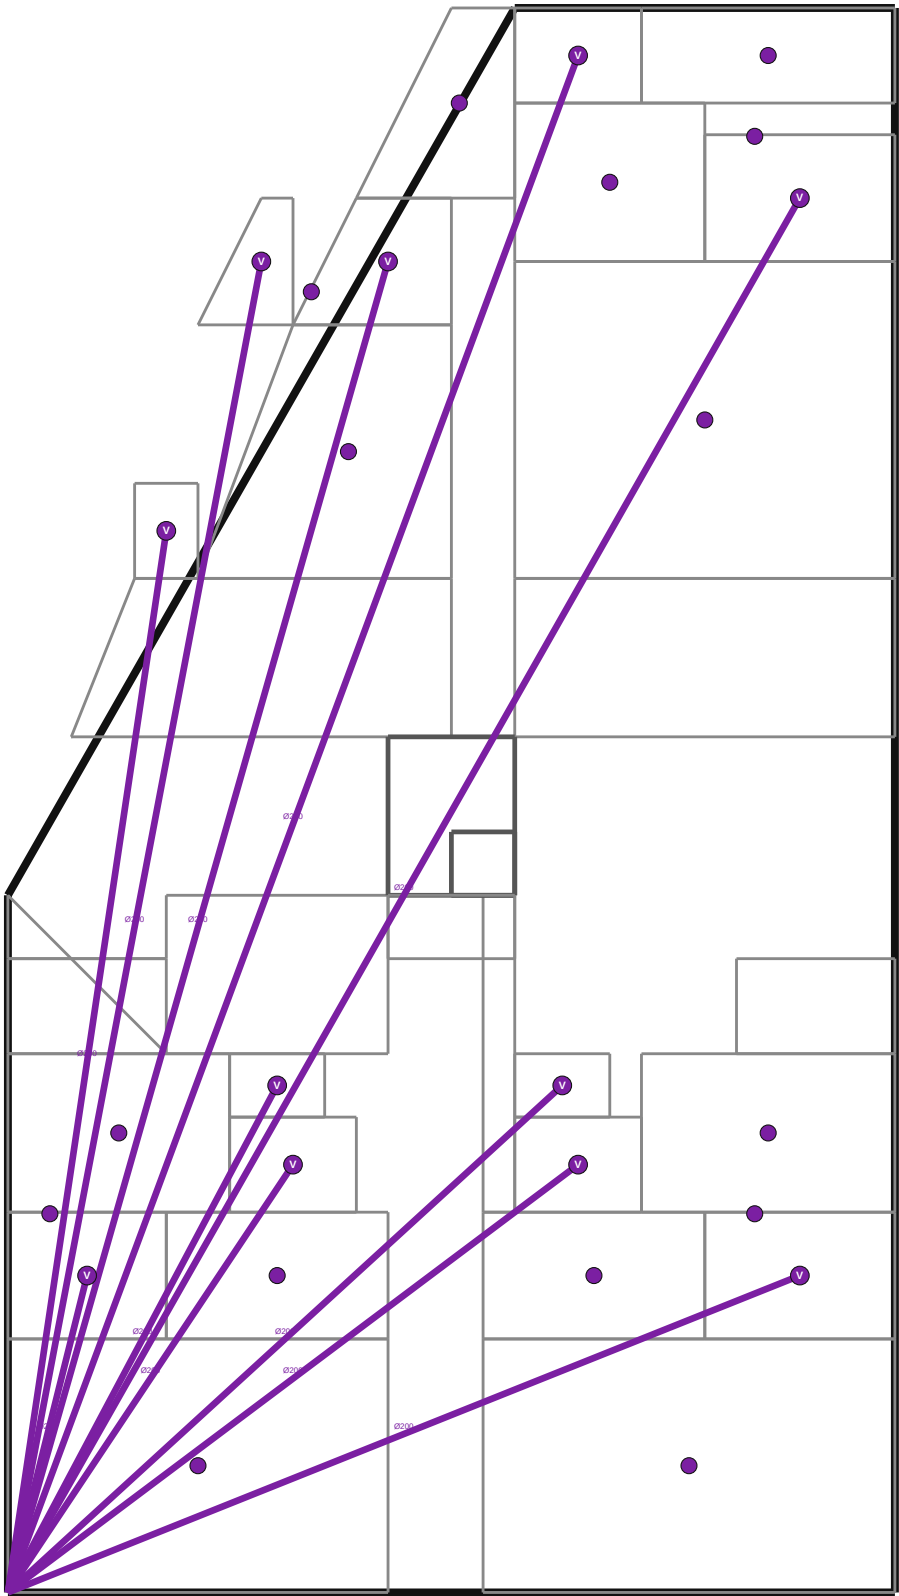

NOMENCLATURE — 413 HVC — Ventilation (VMC)

- Grille soufflage: 11
- Bouche VMC extraction: 11
- Hotte aspirante: 4


TIJAN AI Bureau d'Études Automatisé	Résidence Papa Oumar Sakho Dakar, Sénégal	Éch: 1/100 Pl. 61/137
	413 HVC — Ventilation (VMC) — R+2	
Date: 06/05/2026	Réf: 1711	BIM vHVC-061 Phase: APD

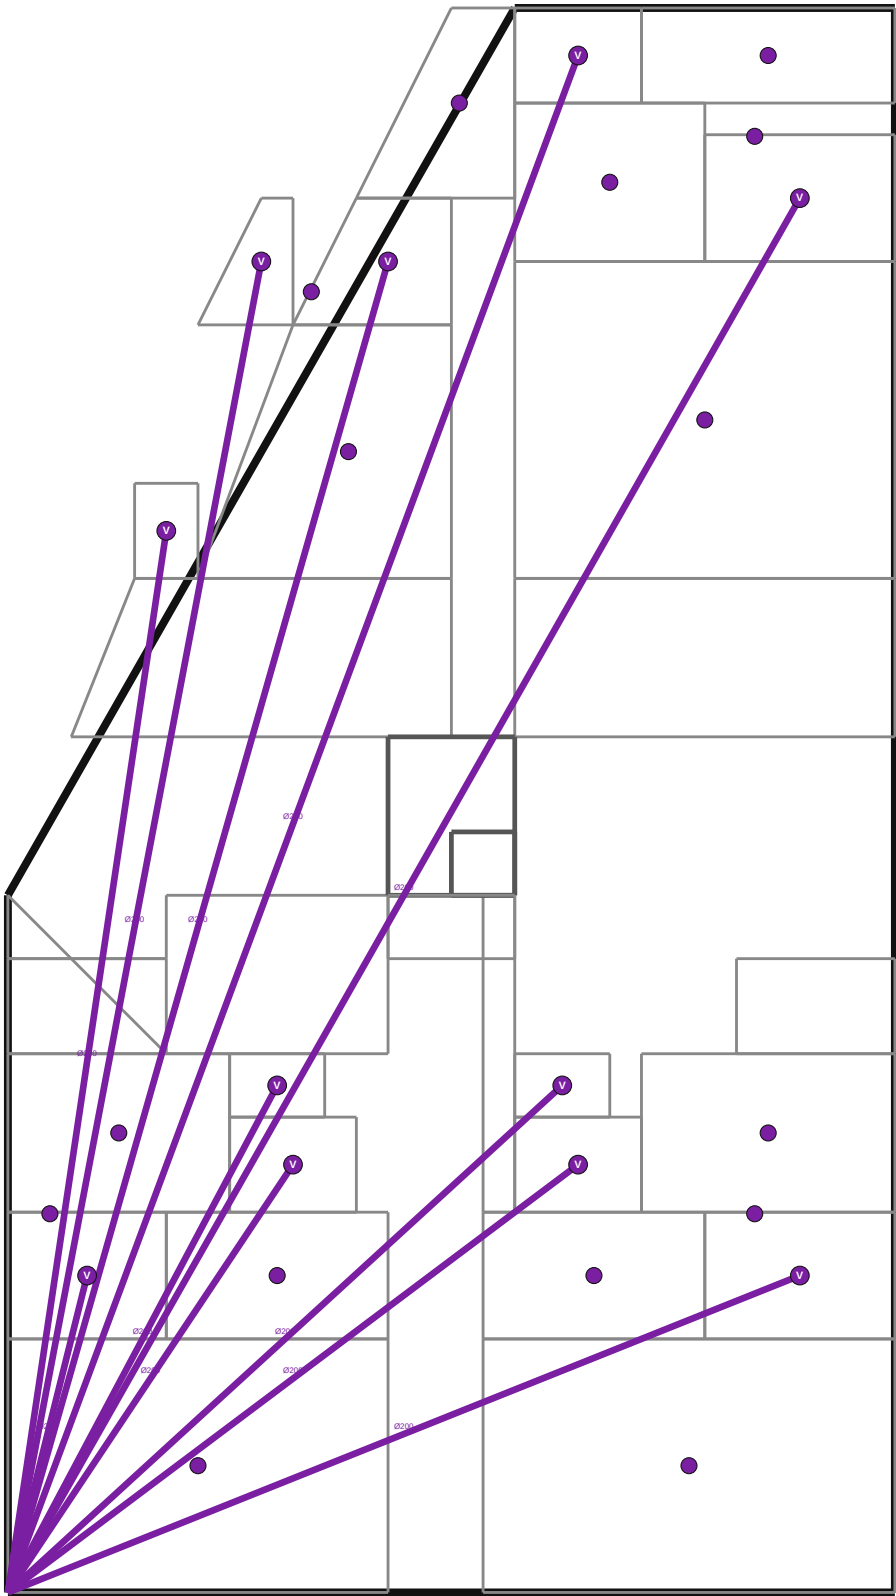

NOMENCLATURE — 413 HVC — Ventilation (VMC)

- Grille soufflage: 11
- Bouche VMC extraction: 11
- Hotte aspirante: 4


TIJAN AI Bureau d'Études Automatisé	Résidence Papa Oumar Sakho Dakar, Sénégal	Éch: 1/100 Pl. 62/137
	413 HVC — Ventilation (VMC) — R+3	
Date: 06/05/2026	Réf: 1711	BIM vHVC-062 Phase: APD

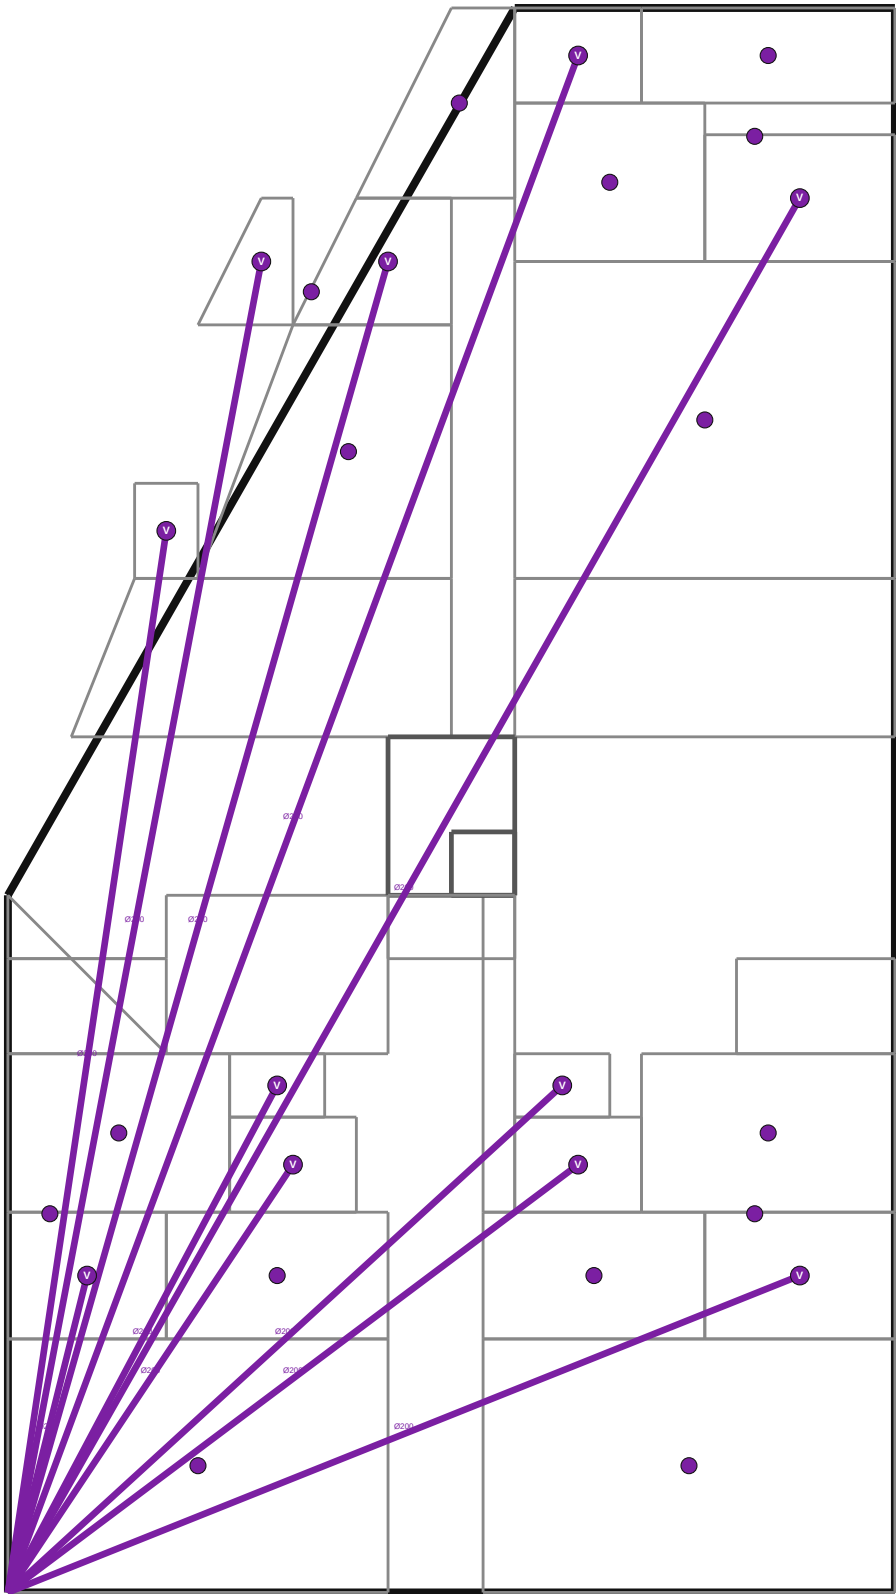

NOMENCLATURE — 413 HVC — Ventilation (VMC)

- Grille soufflage: 11
- Bouche VMC extraction: 11
- Hotte aspirante: 4


TIJAN AI Bureau d'Études Automatisé	Résidence Papa Oumar Sakho Dakar, Sénégal	Éch: 1/100 Pl. 63/137
	413 HVC — Ventilation (VMC) — R+4	
Date: 06/05/2026	Réf: 1711	BIM vHVC-063 Phase: APD

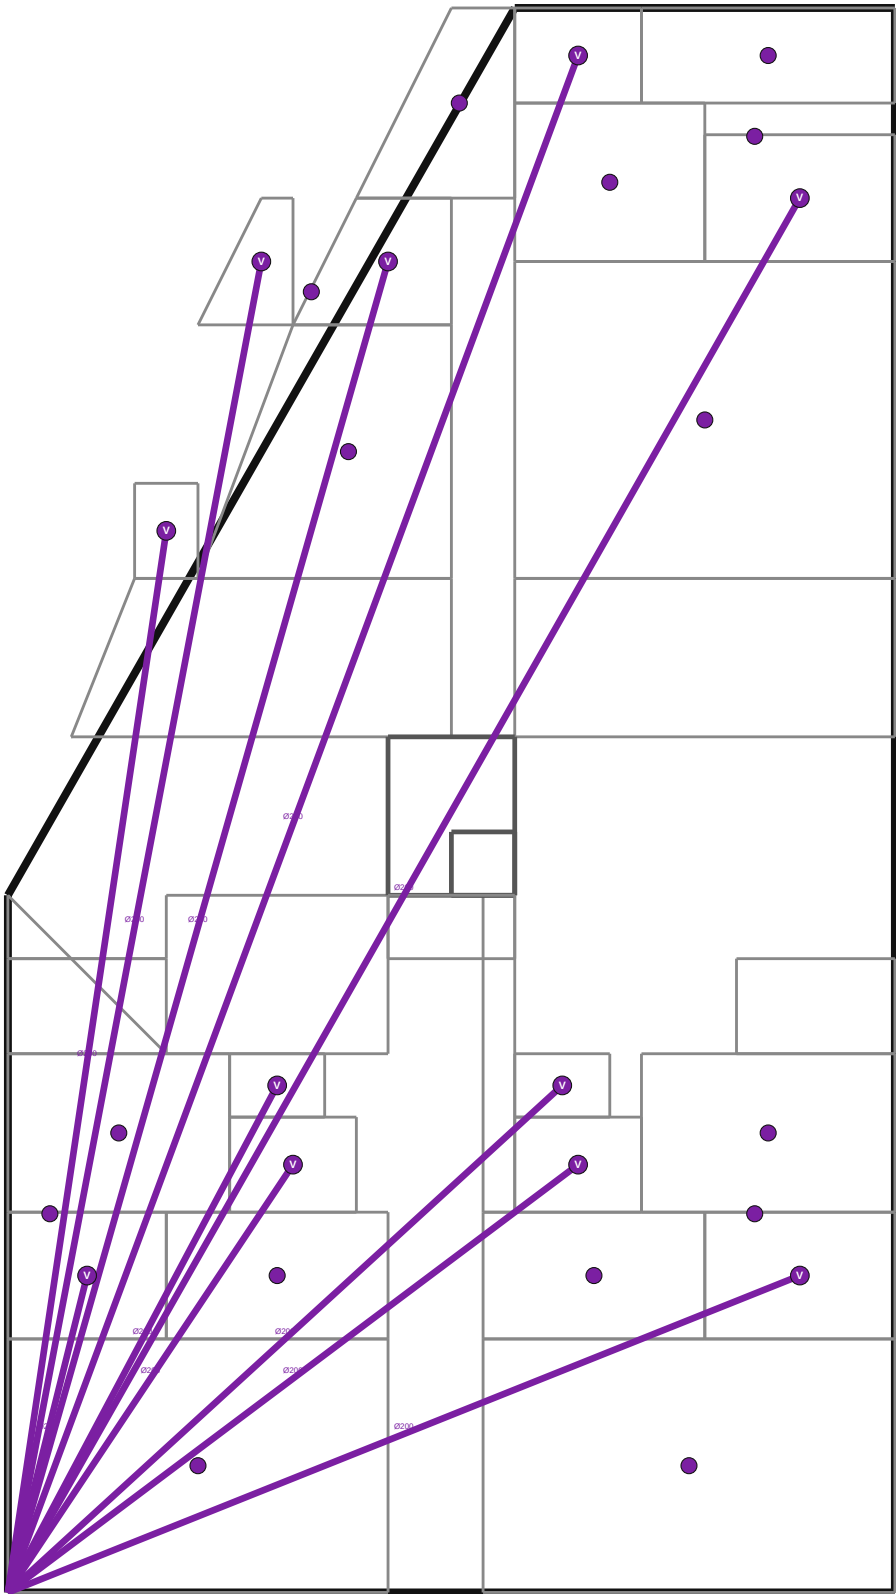

NOMENCLATURE — 413 HVC — Ventilation (VMC)

- Grille soufflage: 11
- Bouche VMC extraction: 11
- Hotte aspirante: 4

TIJAN AI Bureau d'Études Automatisé	Résidence Papa Oumar Sakho Dakar, Sénégal	Éch: 1/100 Pl. 64/137
	413 HVC — Ventilation (VMC) — R+5	
Date: 06/05/2026	Réf: 1711	BIM vHVC-064 Phase: APD

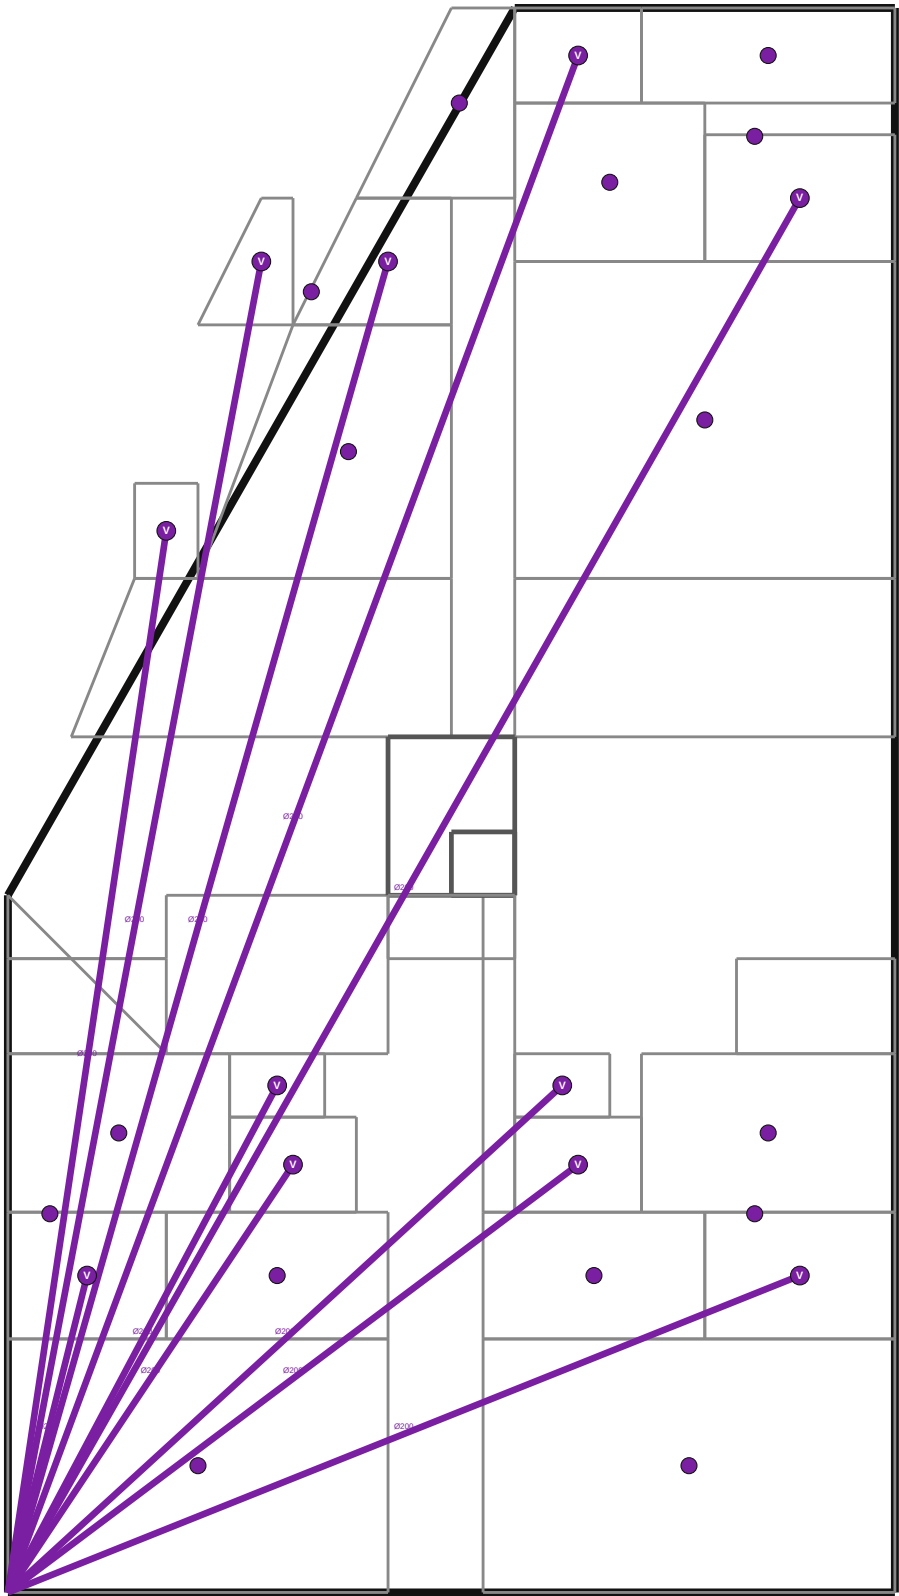


NOMENCLATURE — 413 HVC — Ventilation (VMC)

- Grille soufflage: 11
- Bouche VMC extraction: 11
- Hotte aspirante: 4

TIJAN AI Bureau d'Études Automatisé	Résidence Papa Oumar Sakho Dakar, Sénégal	Éch: 1/100 Pl. 65/137
	413 HVC — Ventilation (VMC) — R+6	
Date: 06/05/2026	Réf: 1711	BIM vHVC-065 Phase: APD


413 HVC — Ventilation (VMC) — R+7

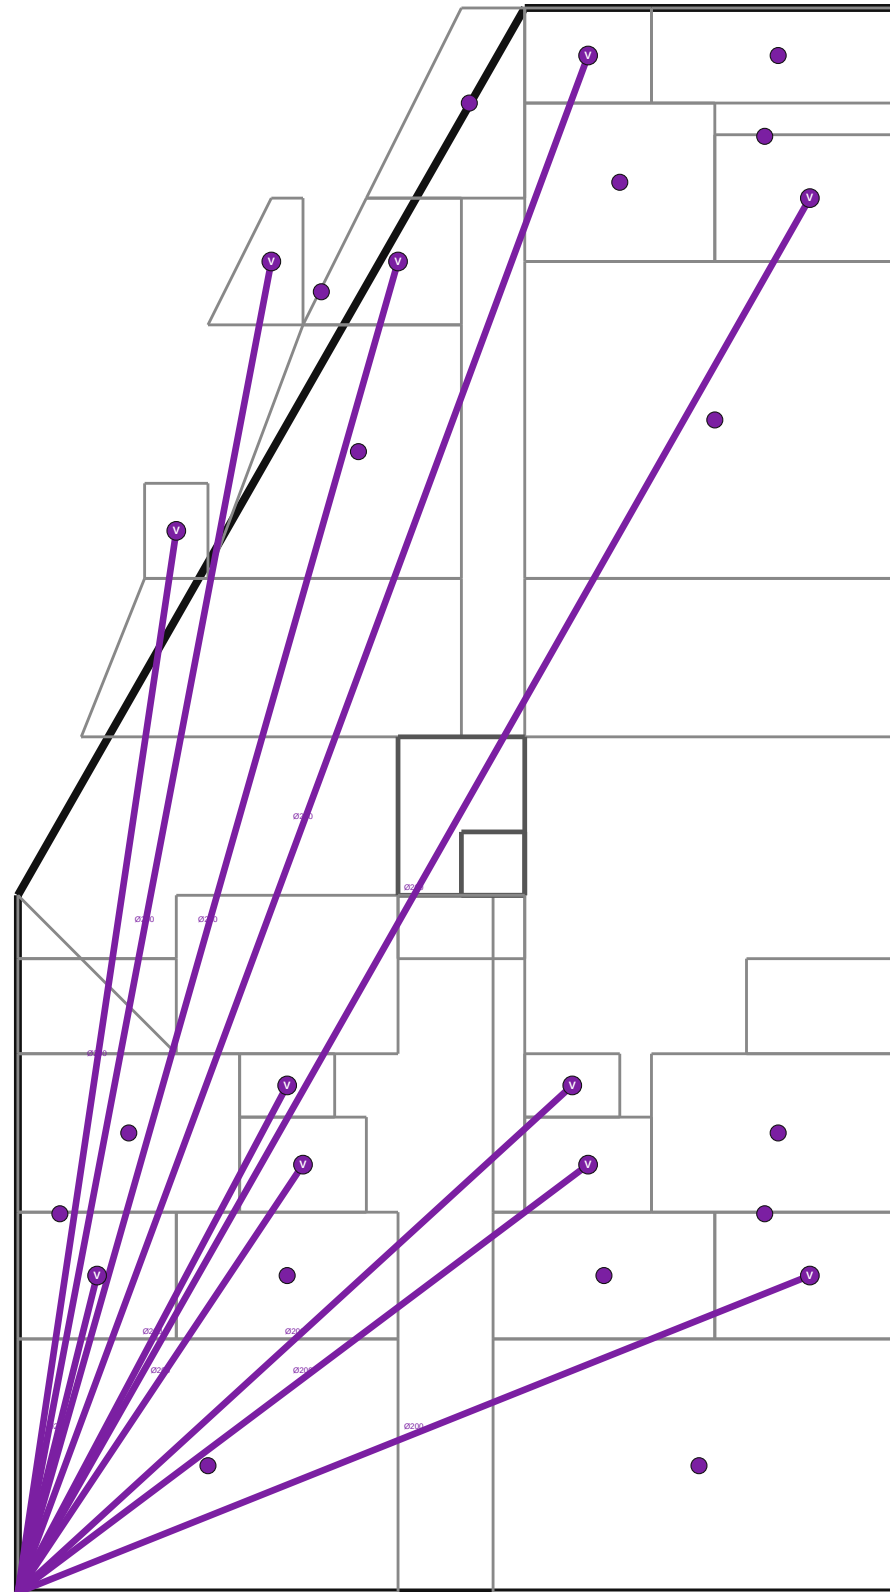

NOMENCLATURE — 413 HVC — Ventilation (VMC)

- Grille soufflage: 11
- Bouche VMC extraction: 11
- Hotte aspirante: 4


TIJAN AI Bureau d'Études Automatisé	Résidence Papa Oumar Sakho Dakar, Sénégal	Éch: 1/100 Pl. 66/137
	413 HVC — Ventilation (VMC) — R+7	
Date: 06/05/2026	Réf: 1711	BIM vHVC-066 Phase: APD

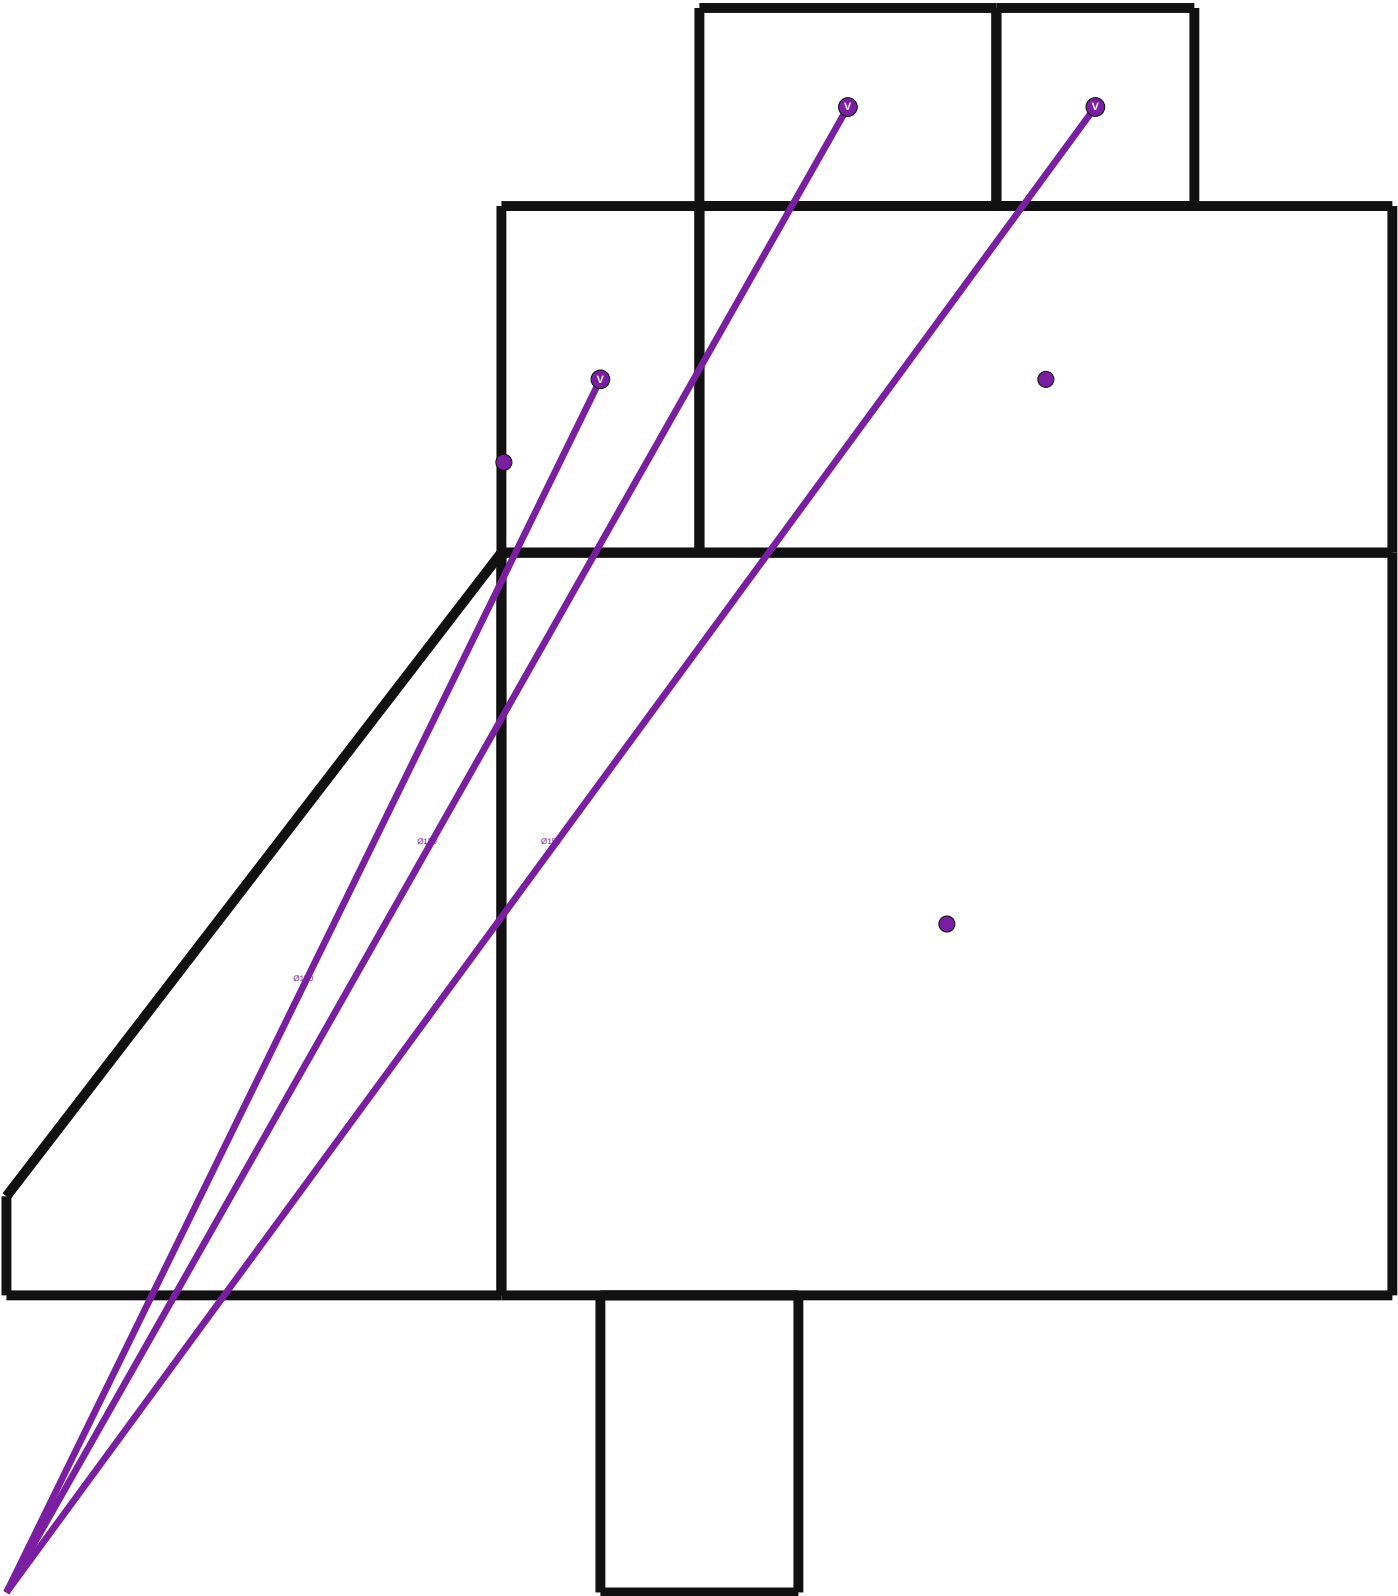

NOMENCLATURE — 413 HVC — Ventilation (VMC)

- Bouche VMC extraction: 3
- Grille soufflage: 2
- Hotte aspirante: 1


TIJAN AI Bureau d'Études Automatisé	Résidence Papa Oumar Sakho Dakar, Sénégal	Éch: 1/100 Pl. 67/137
	413 HVC — Ventilation (VMC) — R+8	
Date: 06/05/2026	Réf: 1711	BIM vHVC-067 Phase: APD

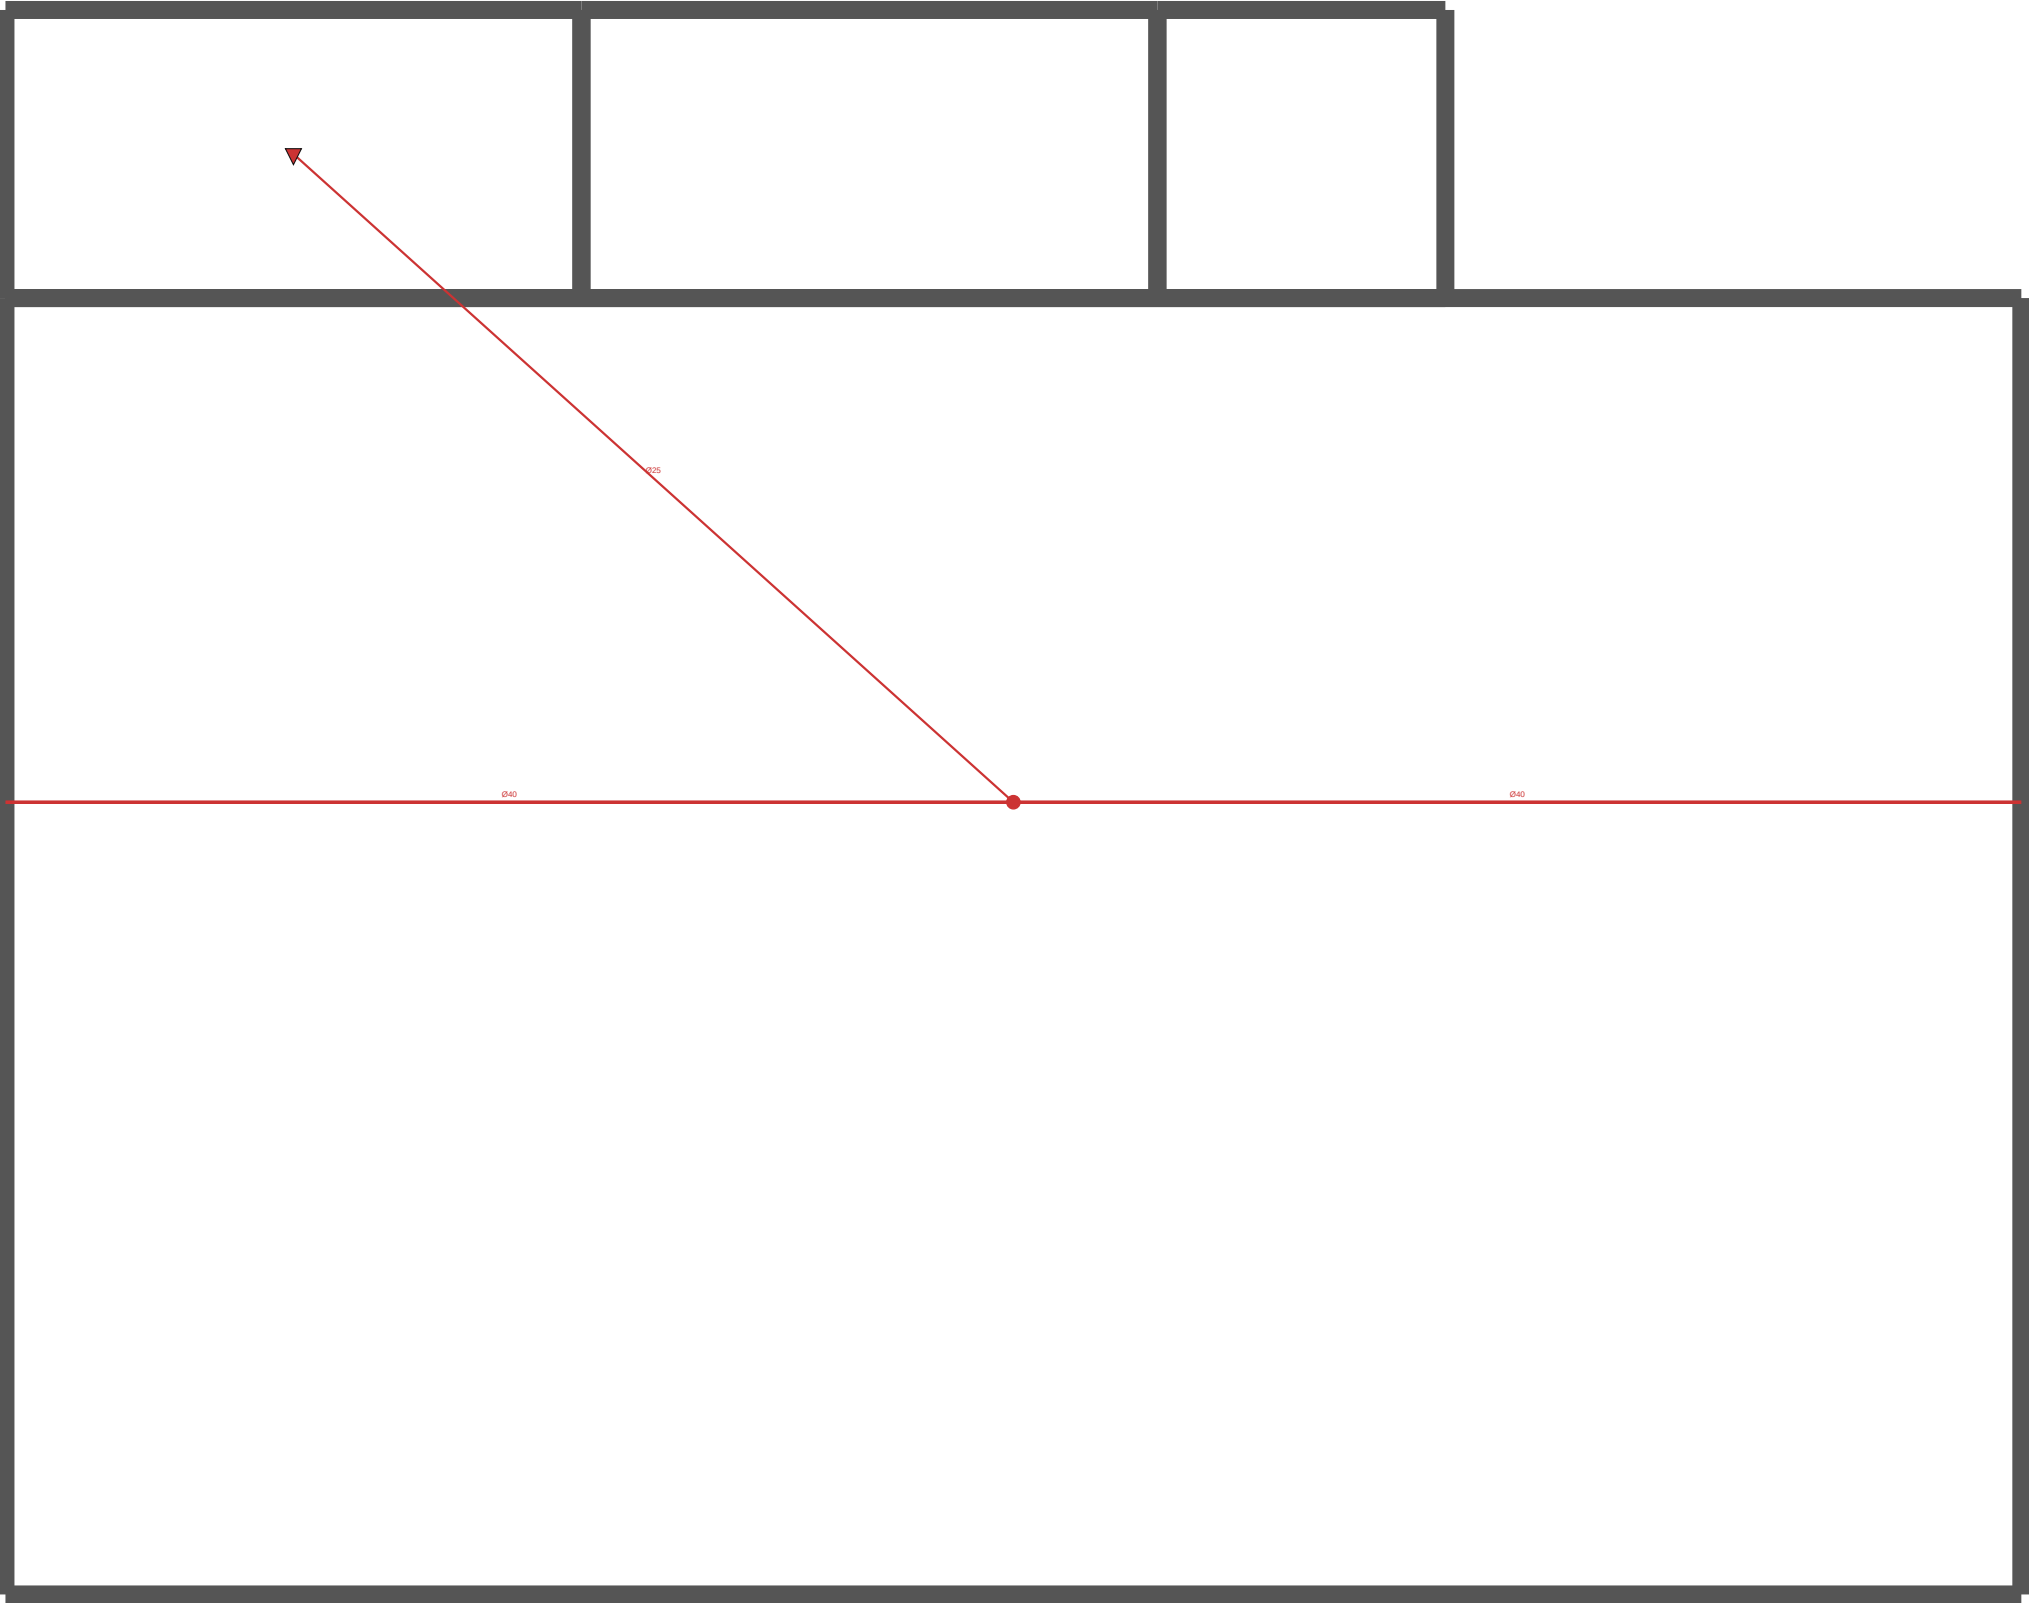

NOMENCLATURE — 400 FIF — Extinction (SPK)

• Sprinkler: 1


TIJAN AI Bureau d'Études Automatisé	Résidence Papa Oumar Sakho Dakar, Sénégal	Éch: 1/100 Pl. 68/137
	400 FIF — Extinction (SPK) — Sous-Sol	
Date: 06/05/2026	Réf: 1711	BIM vFIF-068 Phase: APD

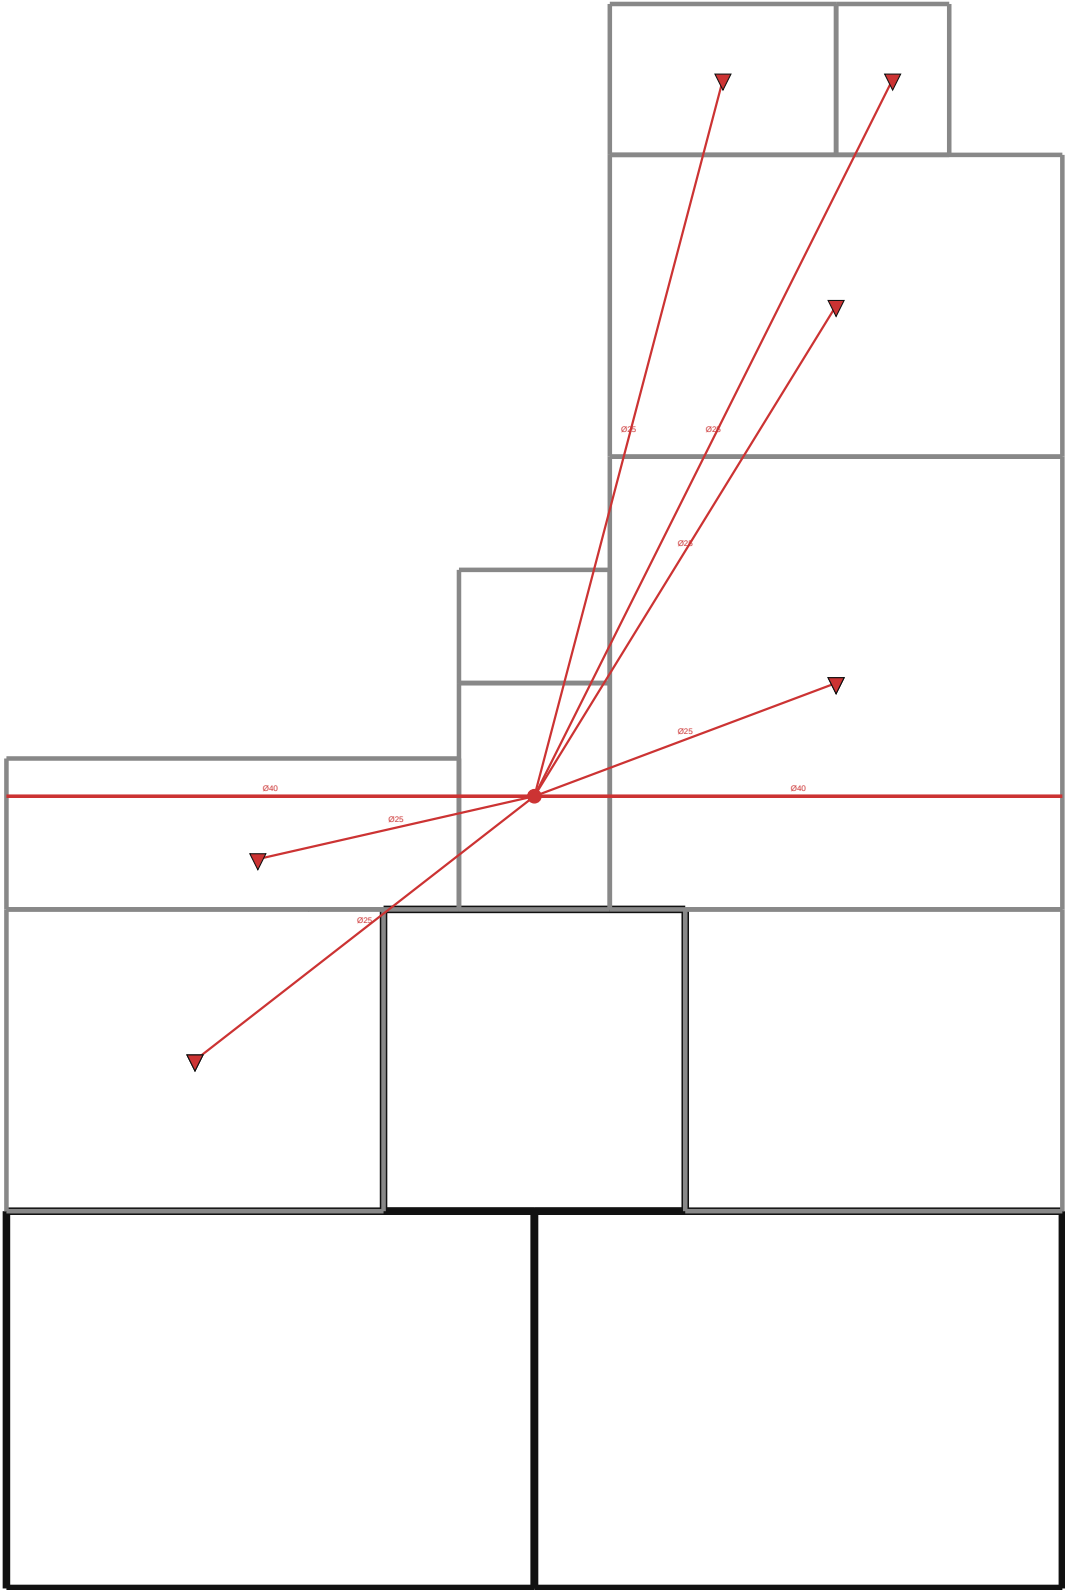

NOMENCLATURE — 400 FIF — Extinction (SPK)

• Sprinkler: 8

TIJAN AI Bureau d'Études Automatisé	Résidence Papa Oumar Sakho Dakar, Sénégal	Éch: 1/100 Pl. 69/137
	400 FIF — Extinction (SPK) — RDC	
Date: 06/05/2026	Réf: 1711	BIM VFIF-069 Phase: APD

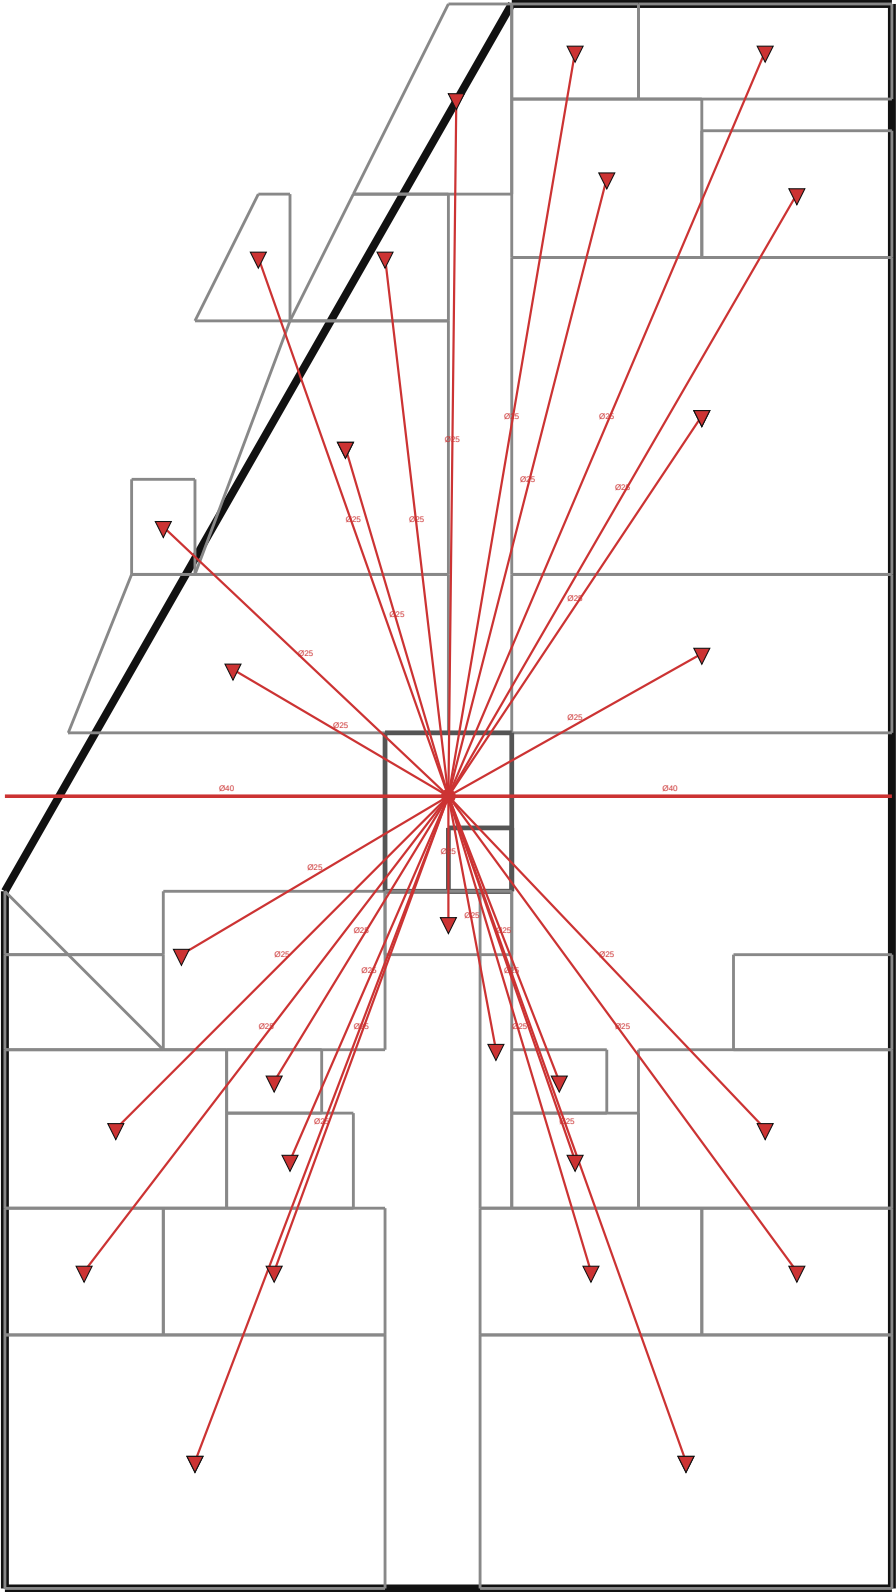


NOMENCLATURE — 400 FIF — Extinction (SPK)

• Sprinkler: 31

TIJAN AI Bureau d'Études Automatisé	Résidence Papa Oumar Sakho Dakar, Sénégal	Éch: 1/100 Pl. 70/137
	400 FIF — Extinction (SPK) — R+1	
Date: 06/05/2026	Réf: 1711	BIM vFIF-070 Phase: APD


400 FIF — Extinction (SPK) — R+2

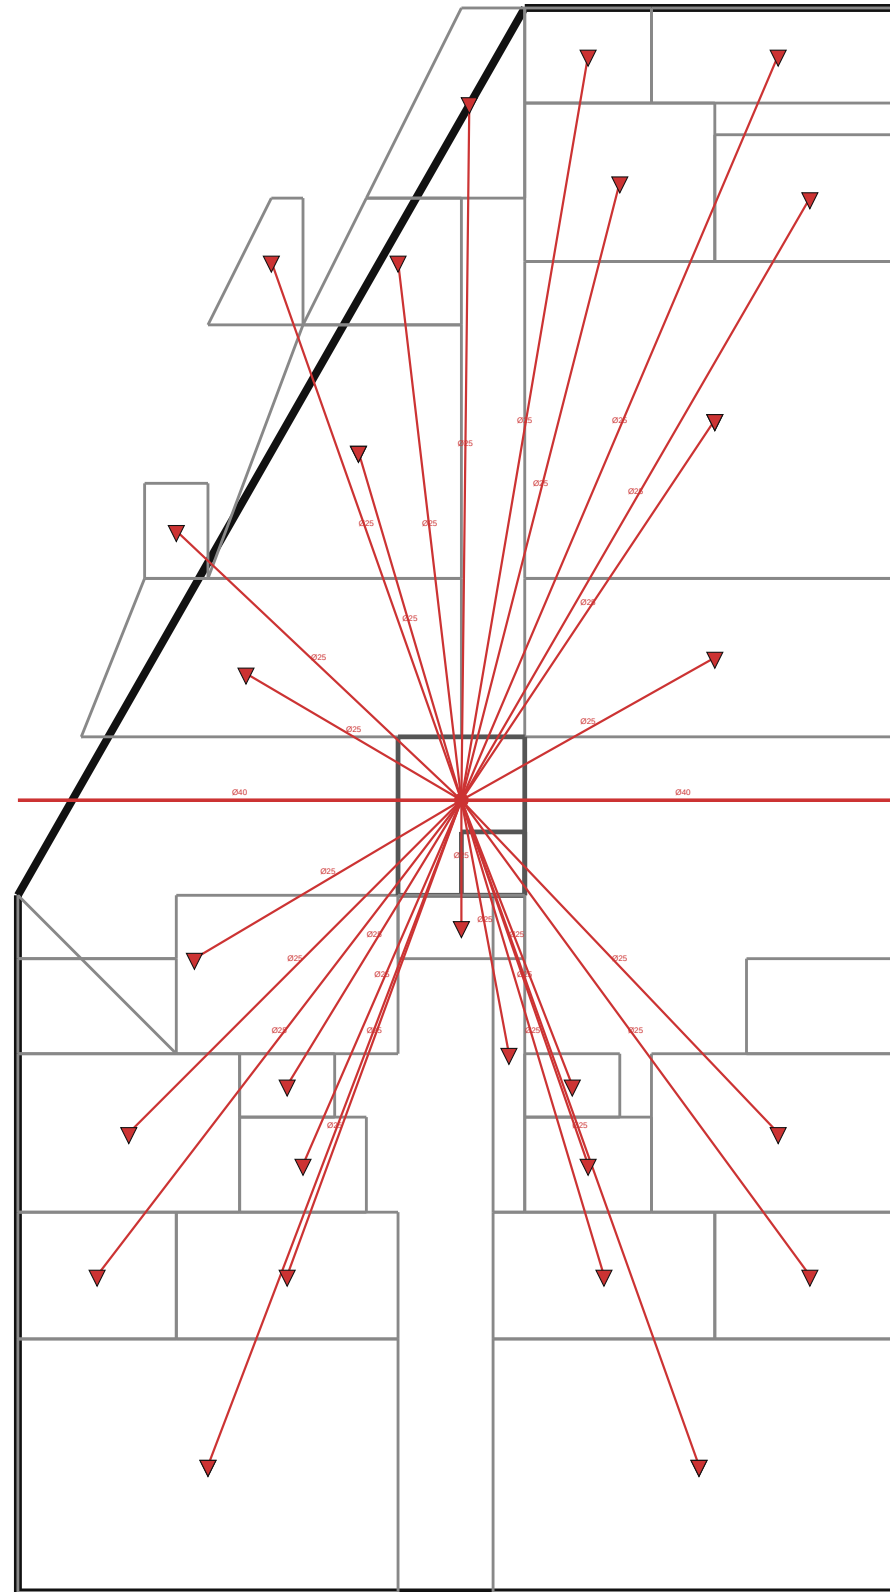

NOMENCLATURE — 400 FIF — Extinction (SPK)

- Sprinkler: 31


TIJAN AI Bureau d'Études Automatisé	Résidence Papa Oumar Sakho Dakar, Sénégal	Éch: 1/100 Pl. 71/137
	400 FIF — Extinction (SPK) — R+2	
Date: 06/05/2026	Réf: 1711	BIM VFIF-071 Phase: APD

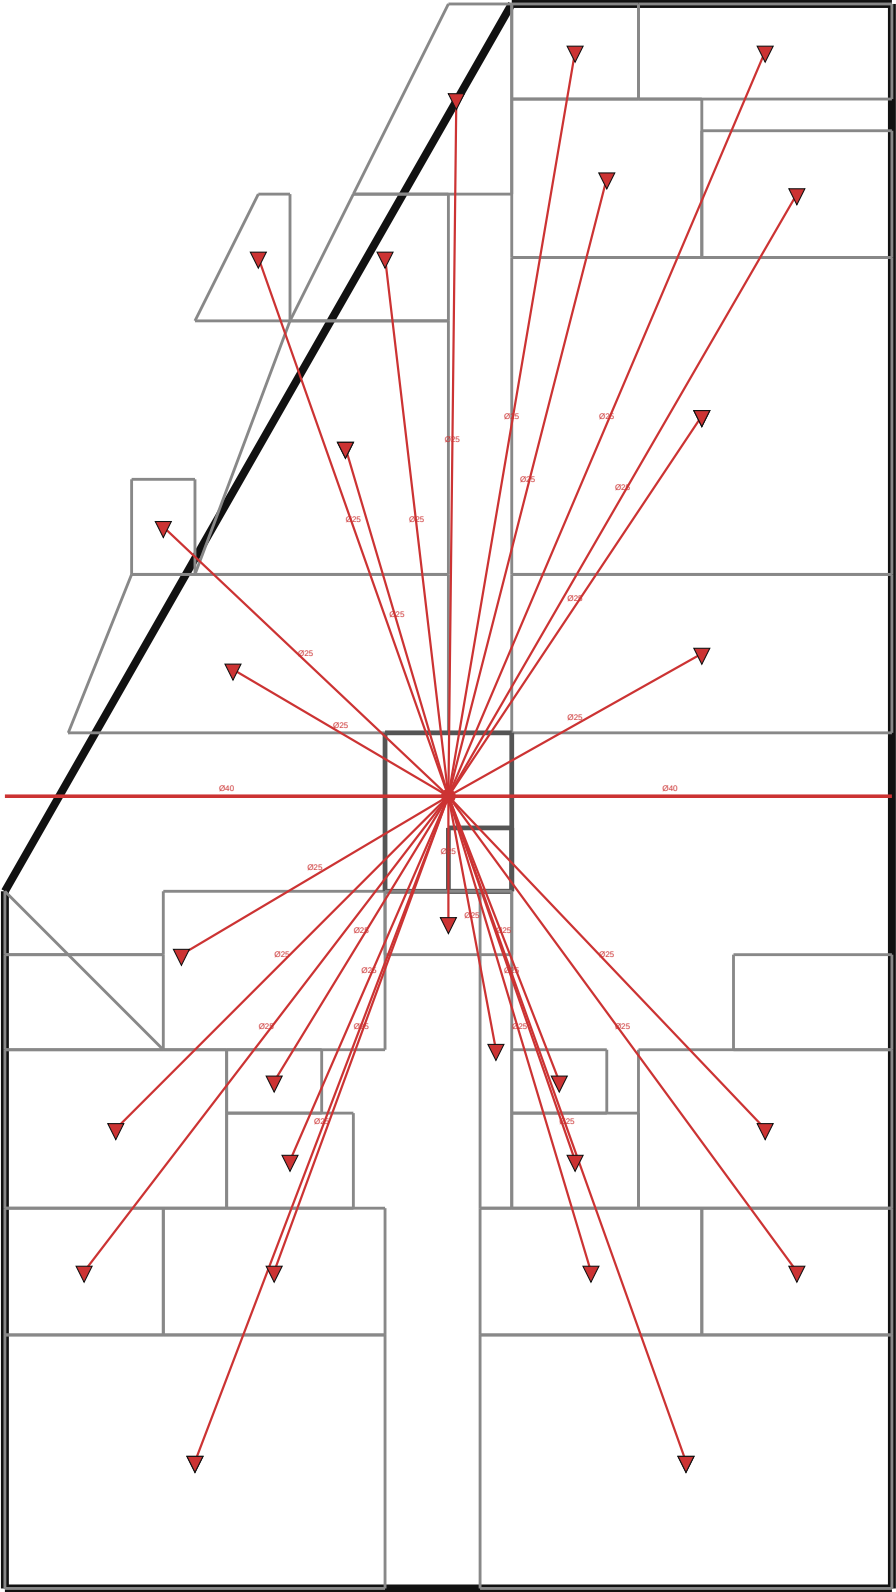

NOMENCLATURE — 400 FIF — Extinction (SPK)

• Sprinkler: 31


TIJAN AI Bureau d'Études Automatisé	Résidence Papa Oumar Sakho Dakar, Sénégal	Éch: 1/100 Pl. 72/137
	400 FIF — Extinction (SPK) — R+3	
Date: 06/05/2026	Réf: 1711	BIM vFIF-072 Phase: APD

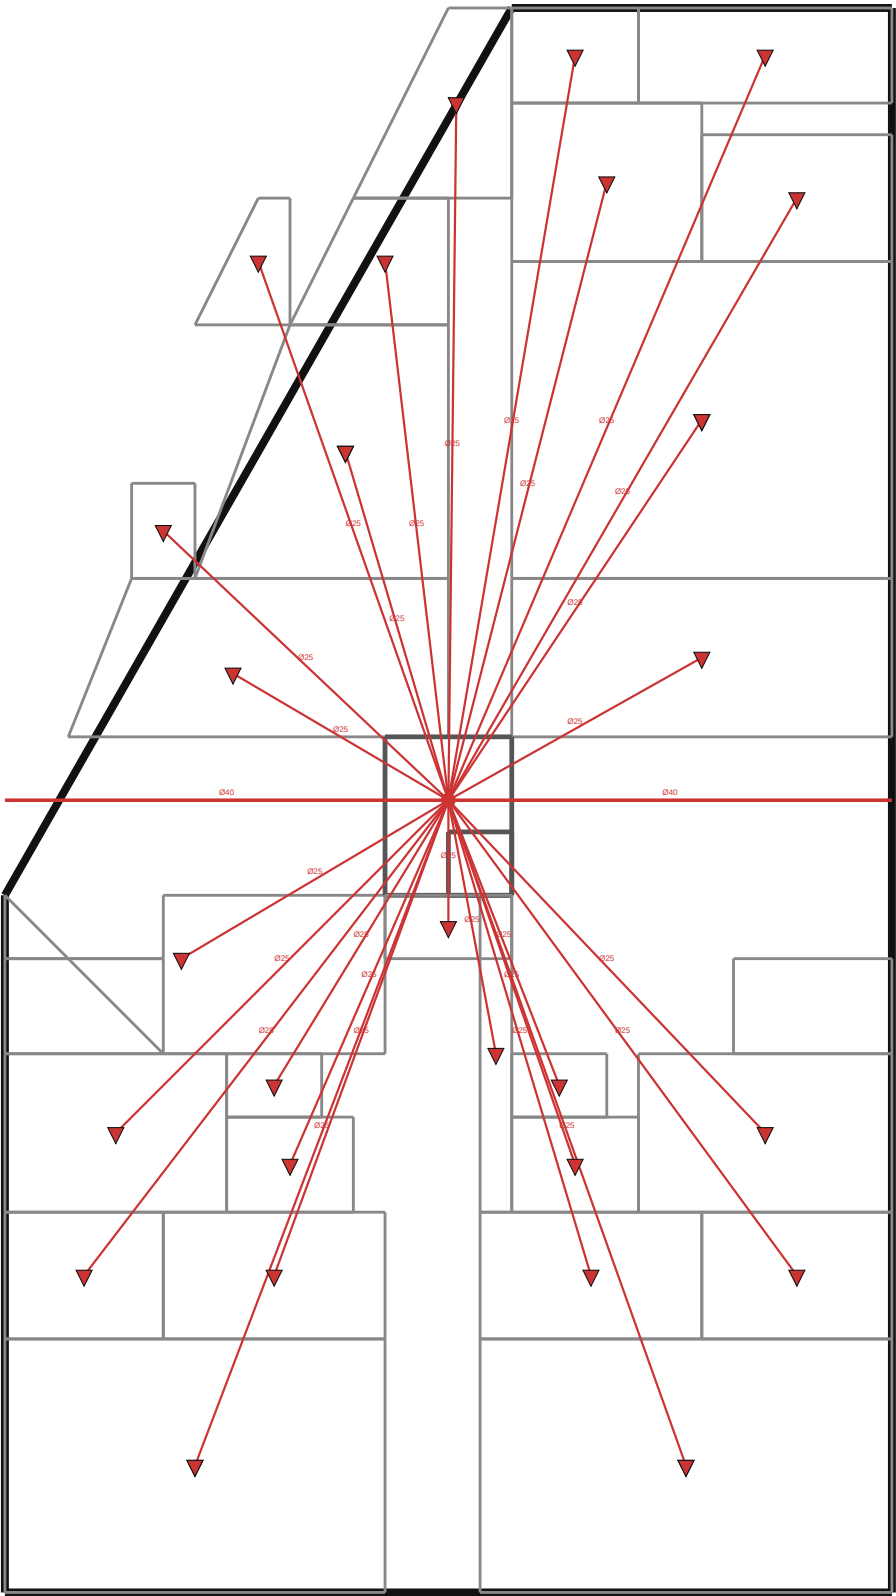

NOMENCLATURE — 400 FIF — Extinction (SPK)

• Sprinkler: 31


TIJAN AI Bureau d'Études Automatisé	Résidence Papa Oumar Sakho Dakar, Sénégal	Éch: 1/100 Pl. 73/137
	400 FIF — Extinction (SPK) — R+4	
Date: 06/05/2026	Réf: 1711	BIM vFIF-073 Phase: APD

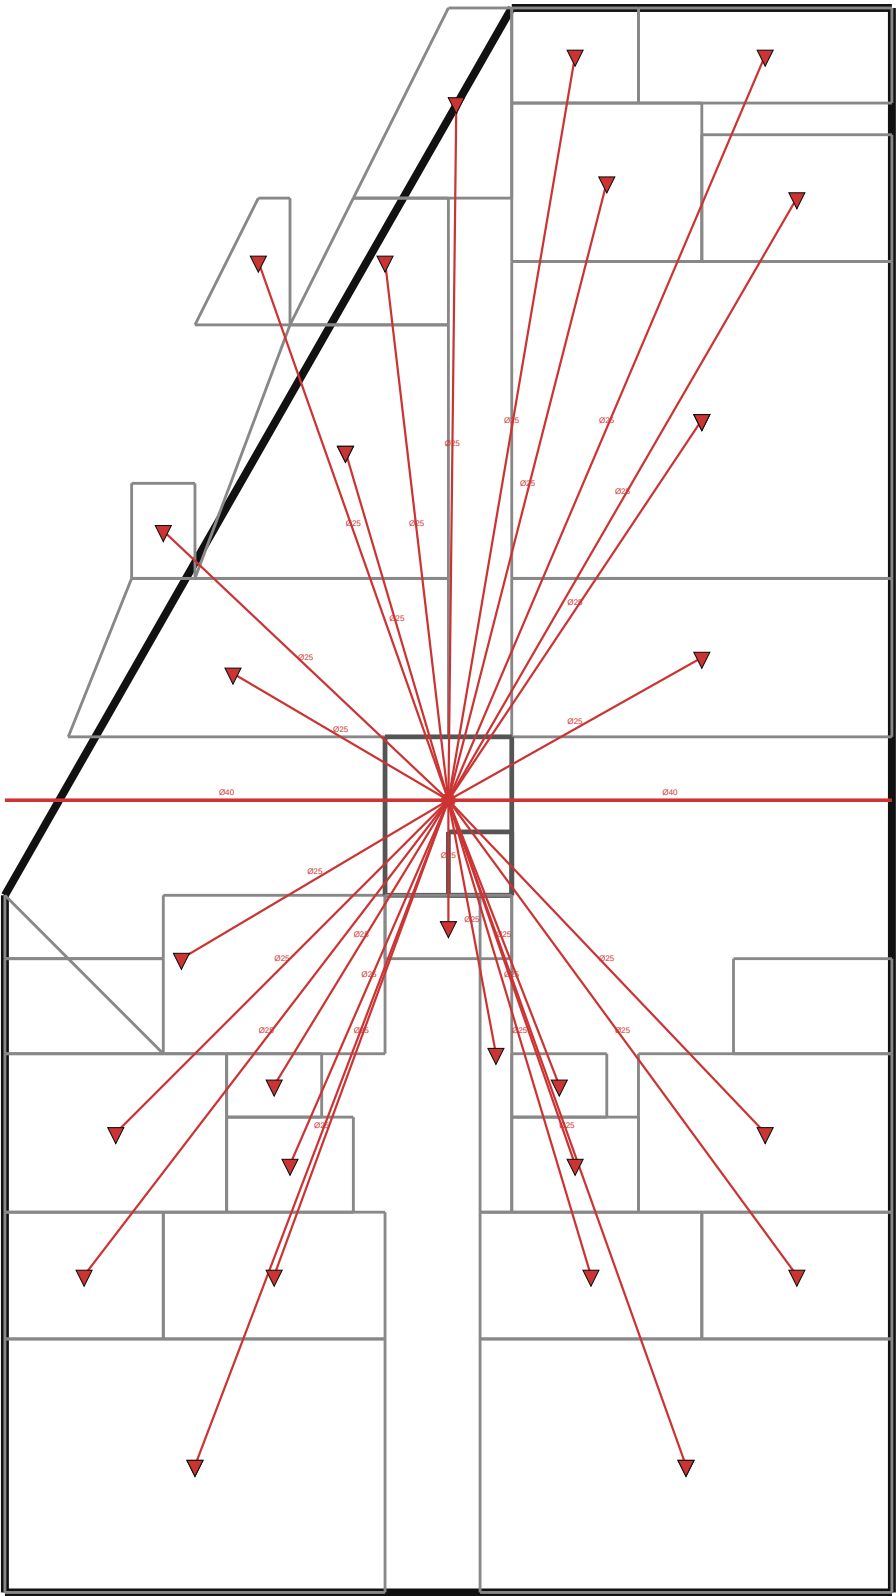

NOMENCLATURE — 400 FIF — Extinction (SPK)

• Sprinkler: 31


TIJAN AI Bureau d'Études Automatisé	Résidence Papa Oumar Sakho Dakar, Sénégal	Éch: 1/100 Pl. 74/137
	400 FIF — Extinction (SPK) — R+5	
Date: 06/05/2026	Réf: 1711	BIM vFIF-074 Phase: APD

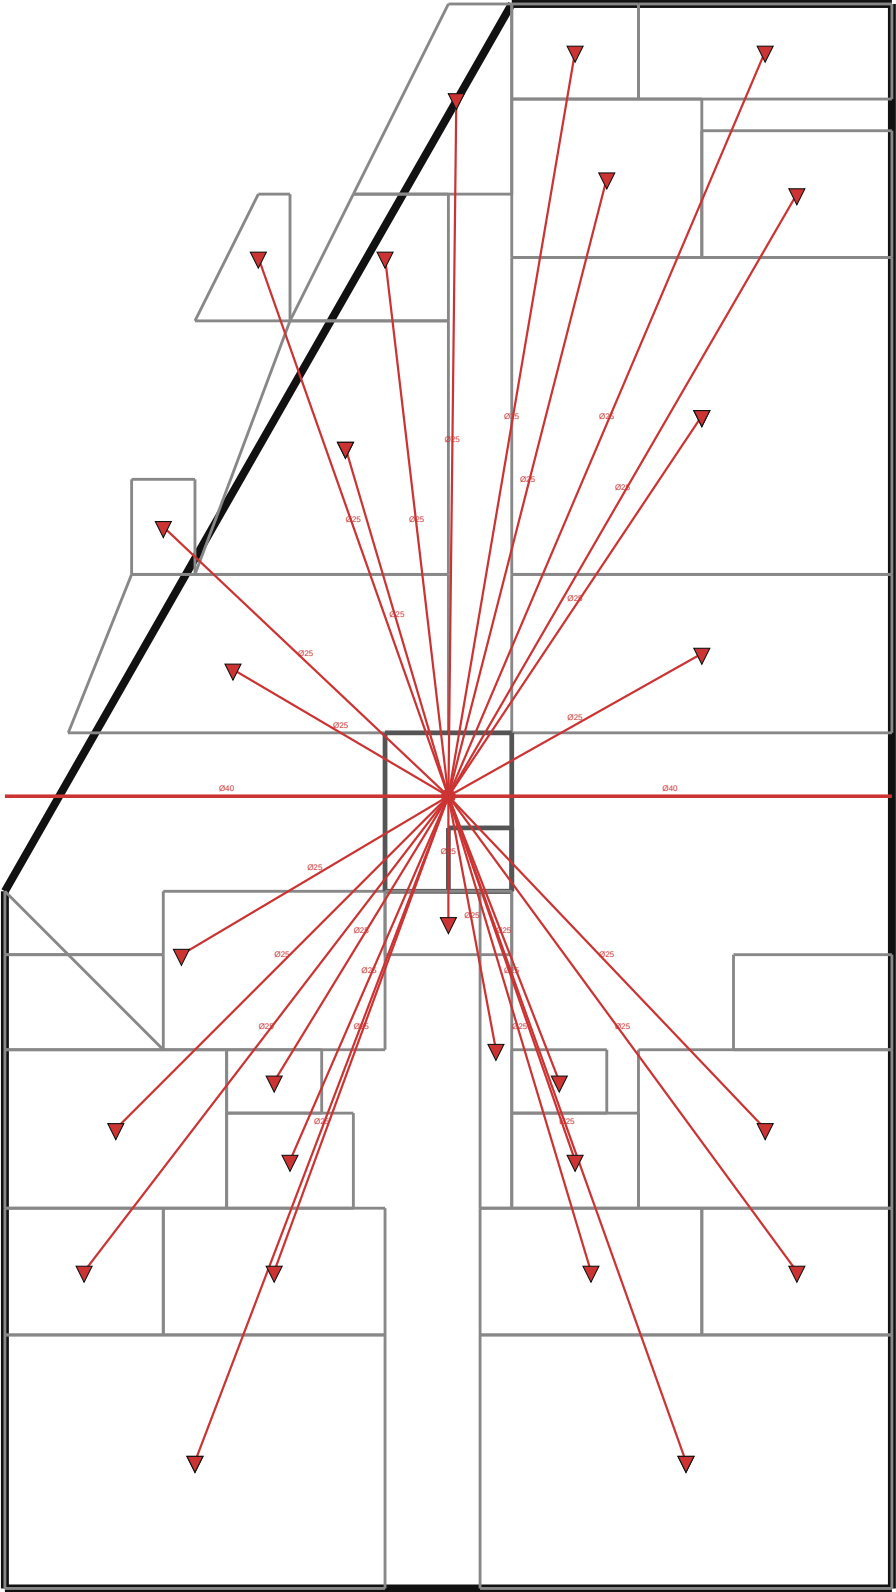

NOMENCLATURE — 400 FIF — Extinction (SPK)

• Sprinkler: 31


TIJAN AI Bureau d'Études Automatisé	Résidence Papa Oumar Sakho Dakar, Sénégal	Éch: 1/100 Pl. 75/137
	400 FIF — Extinction (SPK) — R+6	
Date: 06/05/2026	Réf: 1711	BIM vFIF-075 Phase: APD

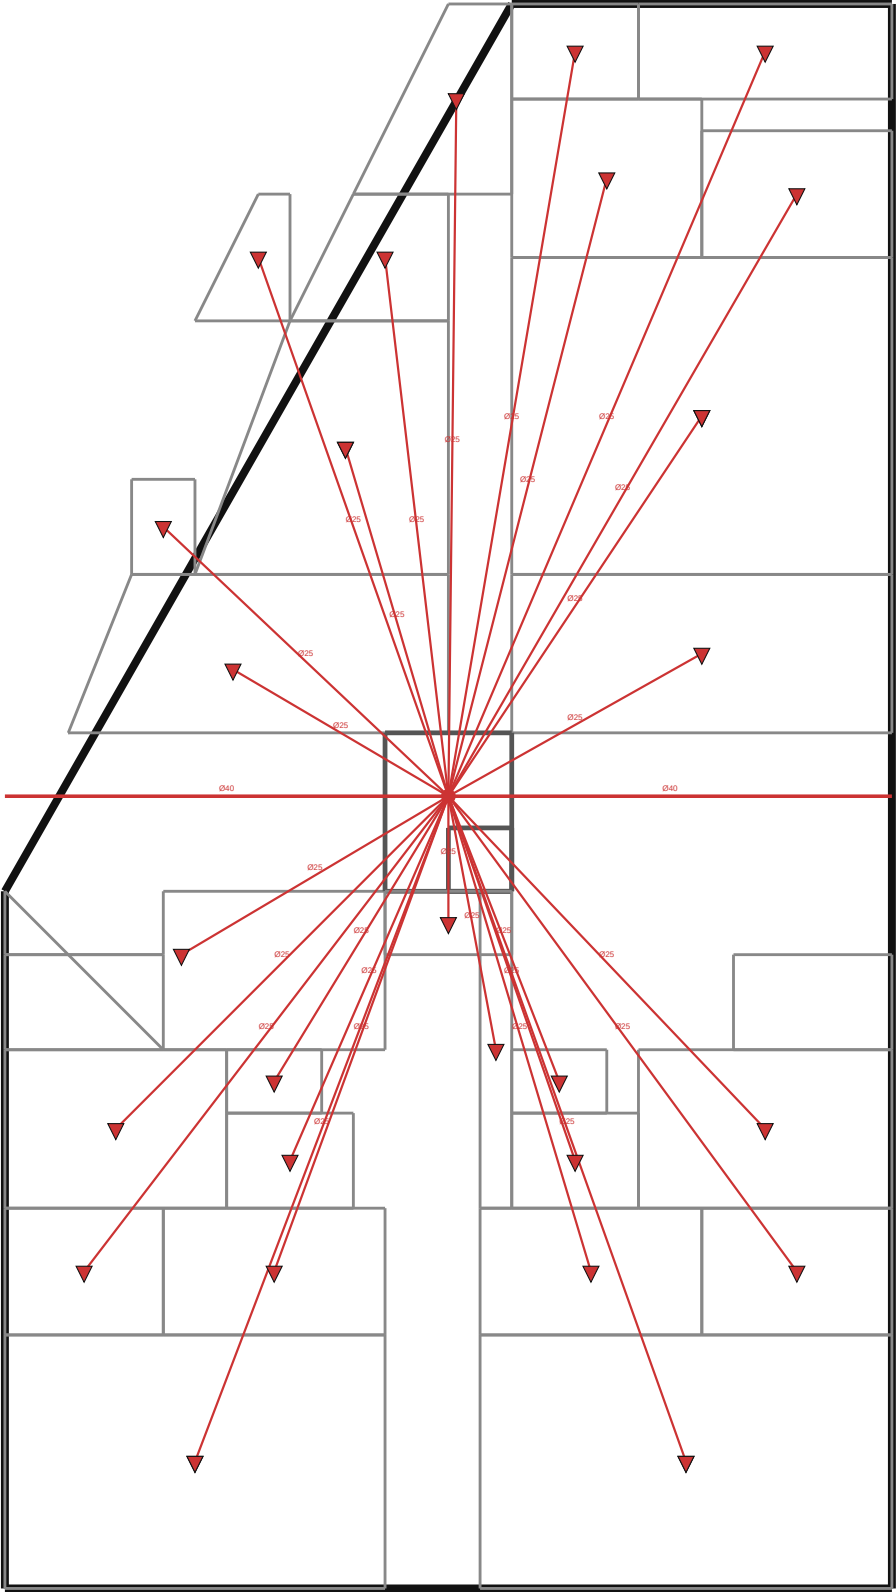

NOMENCLATURE — 400 FIF — Extinction (SPK)

• Sprinkler: 31

TIJAN AI Bureau d'Études Automatisé	Résidence Papa Oumar Sakho Dakar, Sénégal	Éch: 1/100 Pl. 76/137
	400 FIF — Extinction (SPK) — R+7	
Date: 06/05/2026	Réf: 1711	BIM vFIF-076 Phase: APD

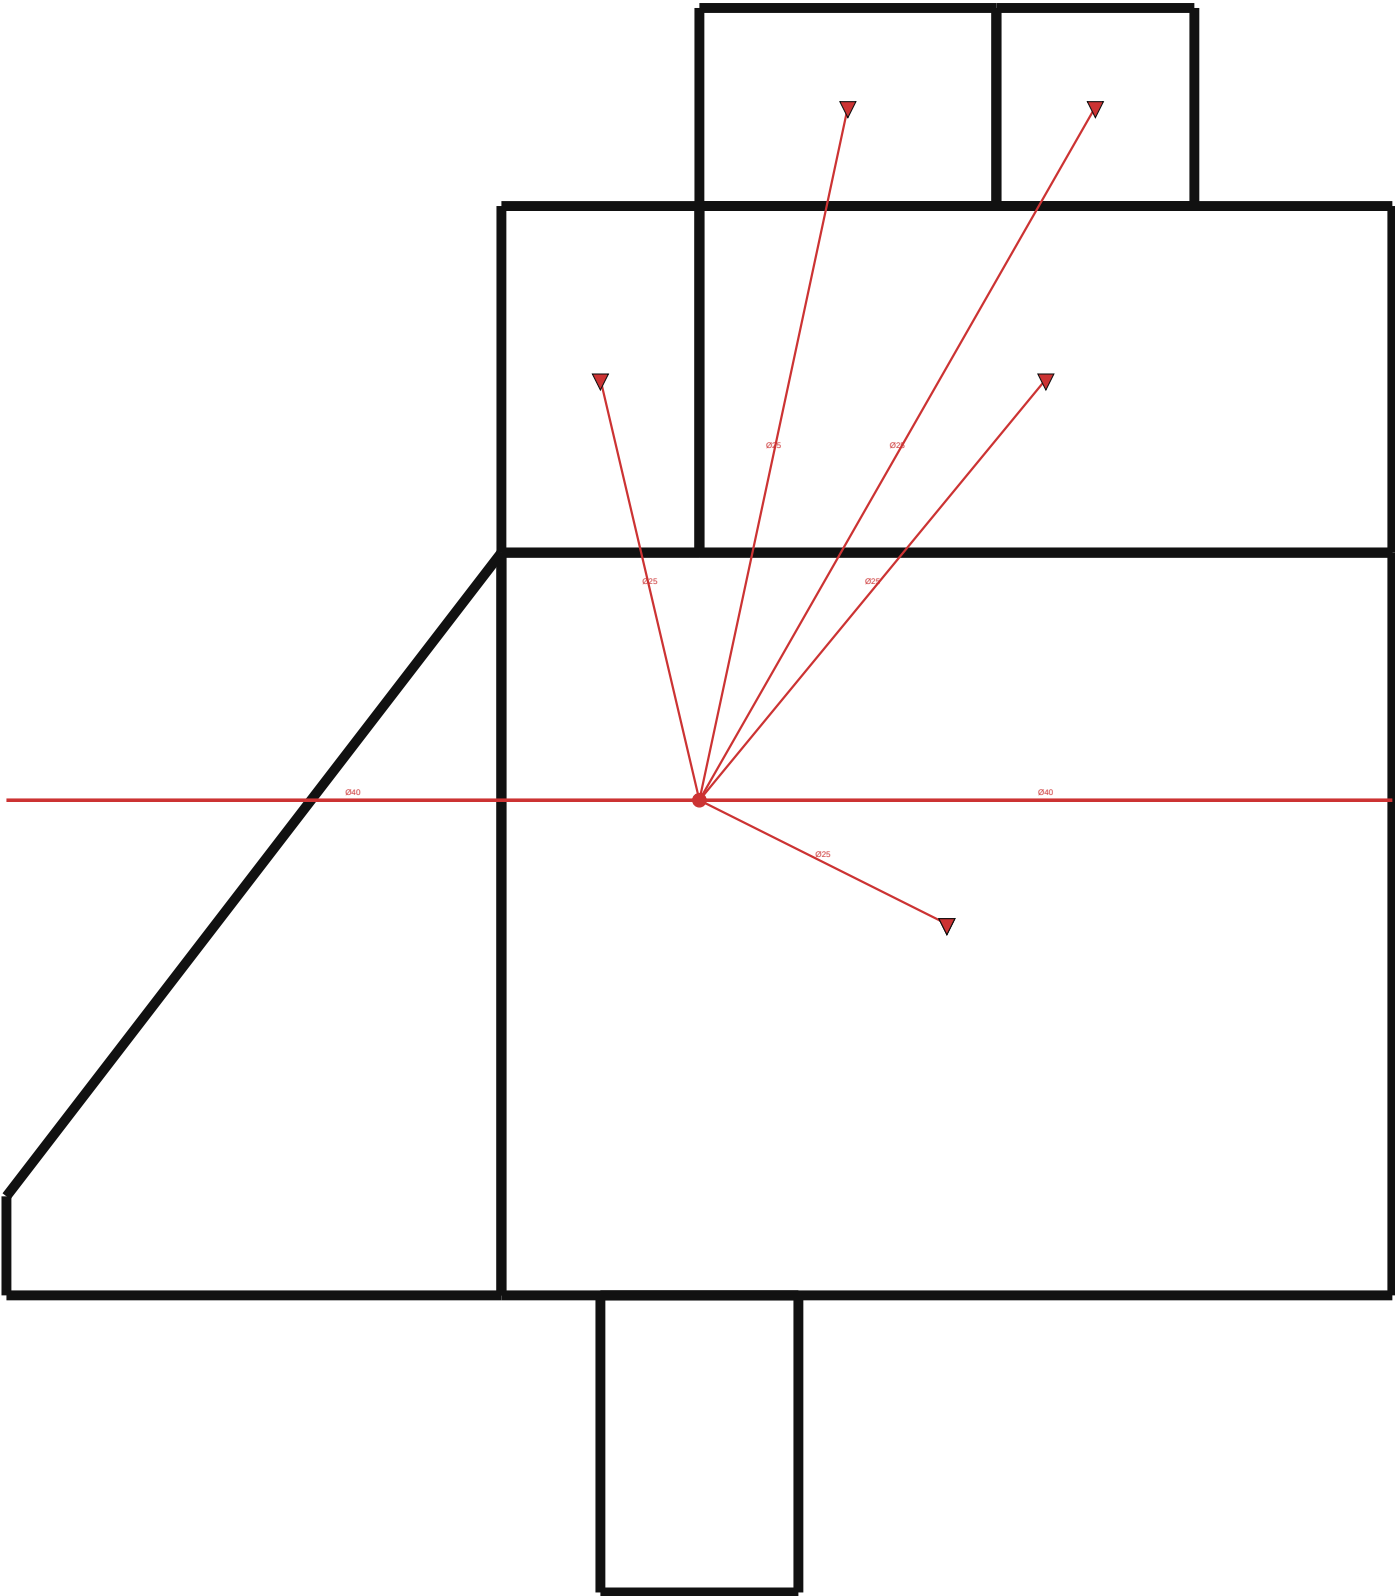

NOMENCLATURE — 400 FIF — Extinction (SPK)

• Sprinkler: 6


TIJAN AI Bureau d'Études Automatisé	Résidence Papa Oumar Sakho Dakar, Sénégal	Éch: 1/100 Pl. 77/137
	400 FIF — Extinction (SPK) — R+8	
Date: 06/05/2026	Réf: 1711	BIM vFIF-077 Phase: APD



NOMENCLATURE — 400 FIF — Détection (DET)

- Détecteur de fumée: 1
- Détecteur de chaleur: 1


TIJAN AI Bureau d'Études Automatisé	Résidence Papa Oumar Sakho Dakar, Sénégal	Éch: 1/100 Pl. 78/137
	400 FIF — Détection (DET) — Sous-Sol	
Date: 06/05/2026	Réf: 1711	BIM vFIF-078 Phase: APD

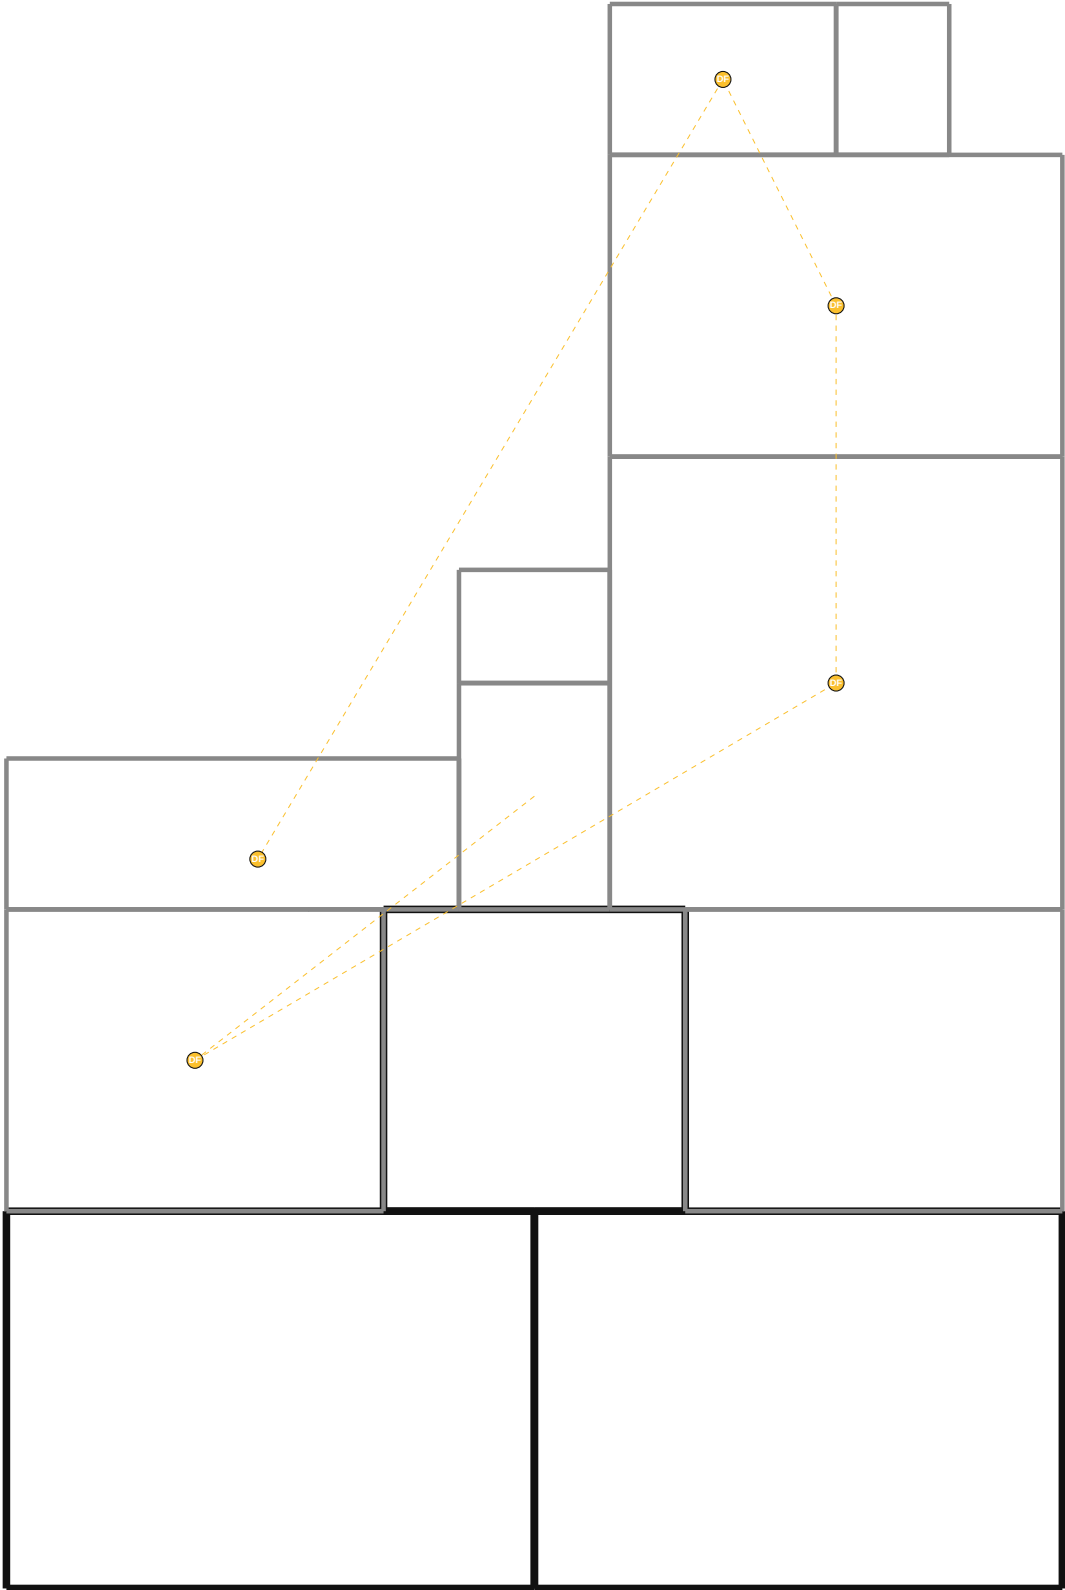

NOMENCLATURE — 400 FIF — Détection (DET)

• Détecteur de fumée: 5


TIJAN AI Bureau d'Études Automatisé	Résidence Papa Oumar Sakho Dakar, Sénégal	Éch: 1/100 Pl. 79/137
	400 FIF — Détection (DET) — RDC	
Date: 06/05/2026	Réf: 1711	BIM vFIF-079 Phase: APD

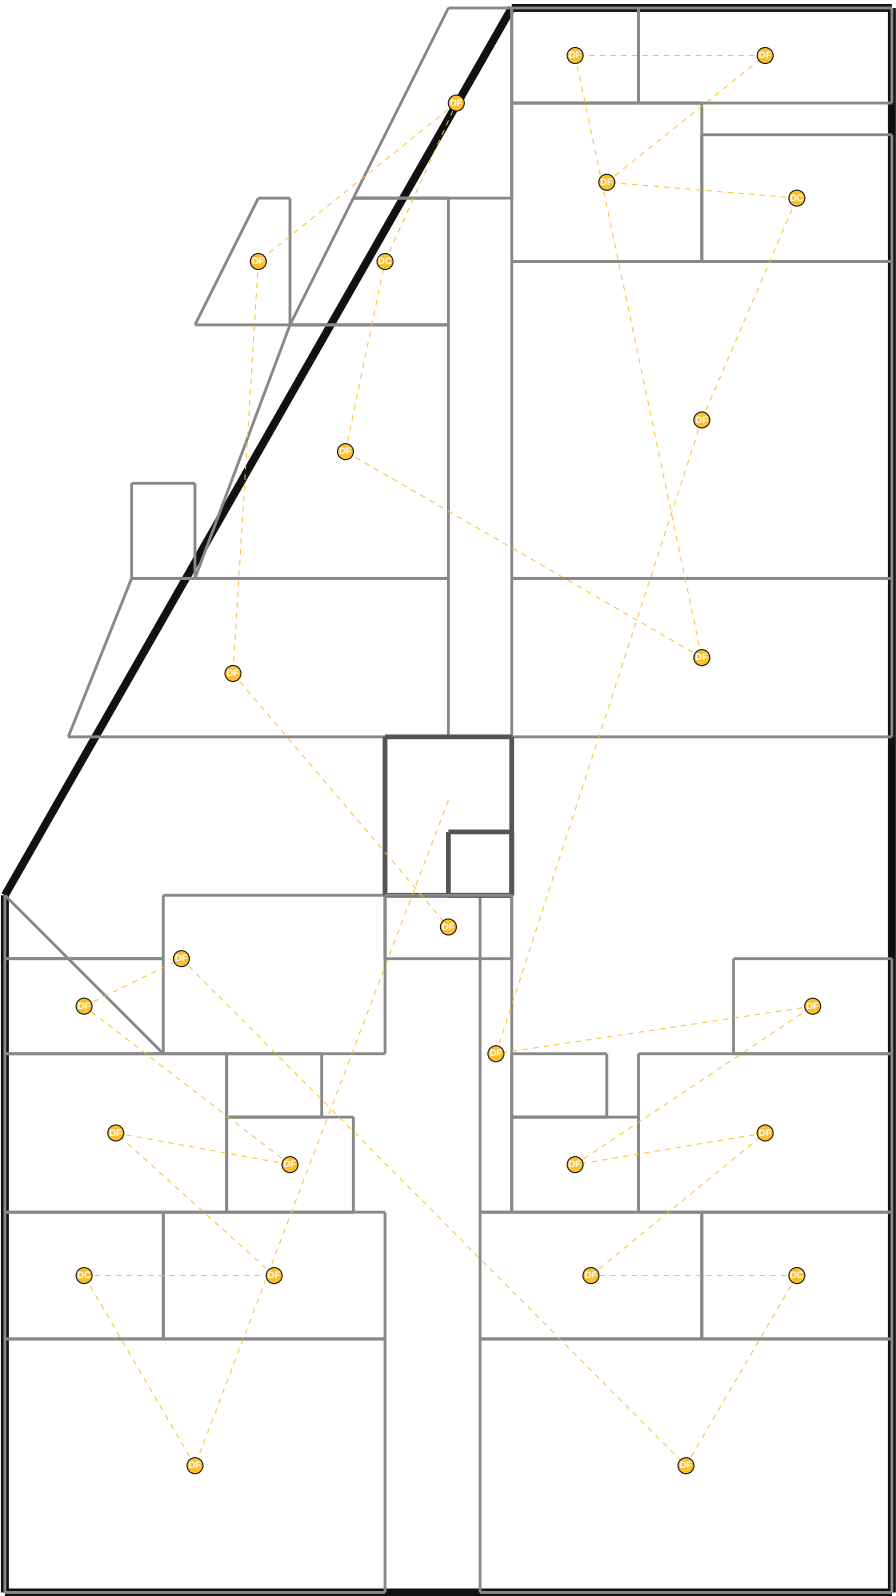

NOMENCLATURE — 400 FIF — Détection (DET)

- Détecteur de fumée: 22
- Détecteur de chaleur: 4


TIJAN AI Bureau d'Études Automatisé	Résidence Papa Oumar Sakho Dakar, Sénégal	Éch: 1/100 Pl. 80/137
	400 FIF — Détection (DET) — R+1	
Date: 06/05/2026	Réf: 1711	BIM vFIF-080 Phase: APD

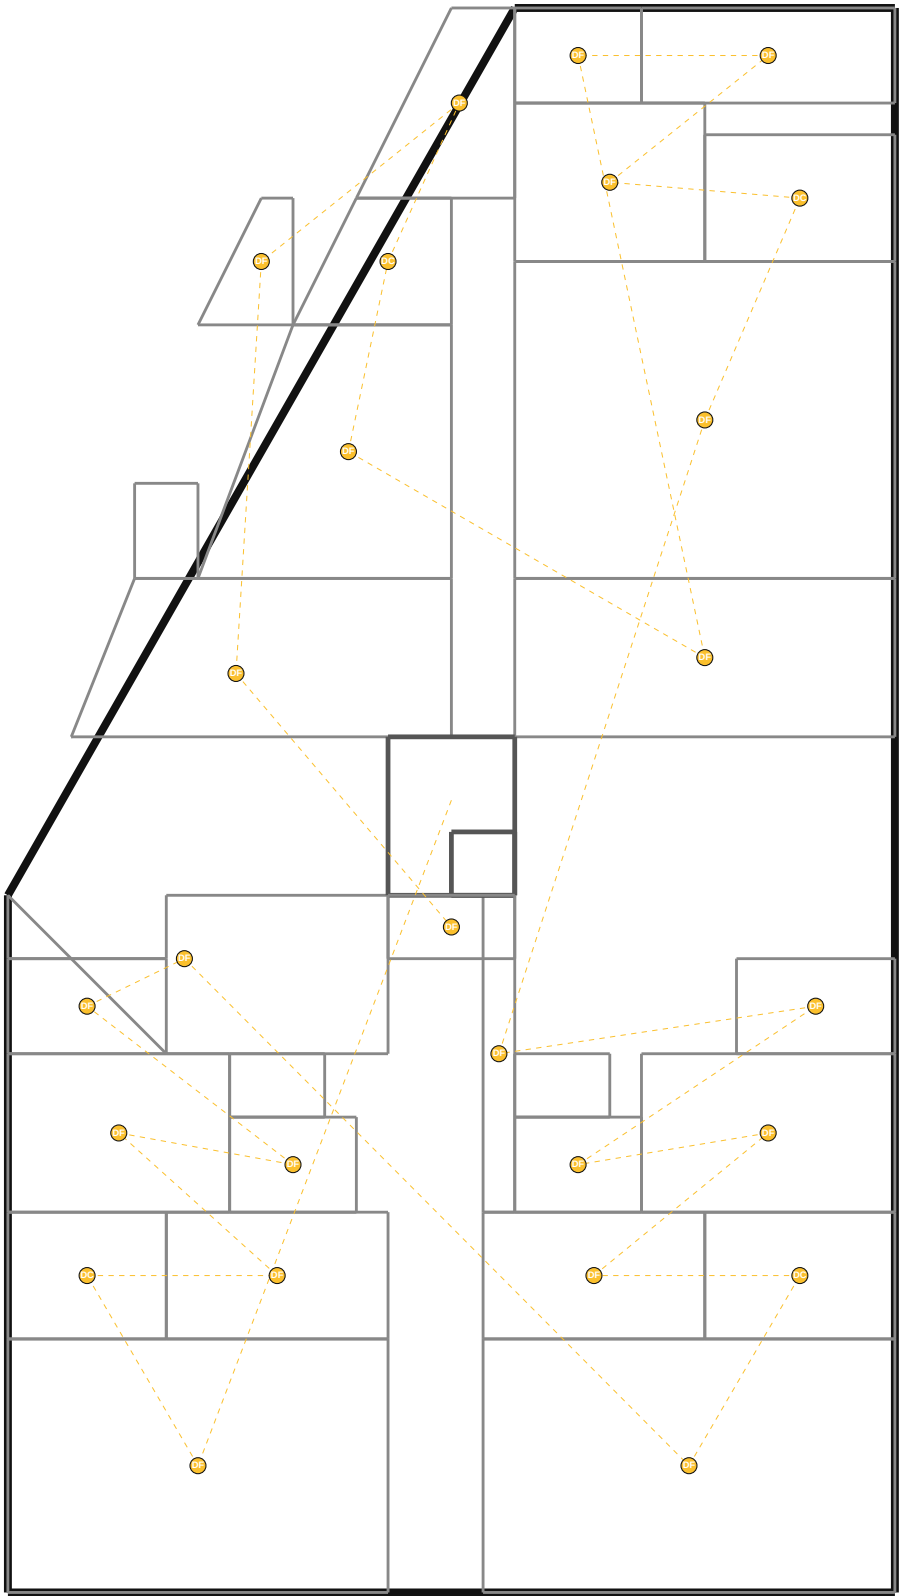

NOMENCLATURE — 400 FIF — Détection (DET)

- Détecteur de fumée: 22
- Détecteur de chaleur: 4


TIJAN AI Bureau d'Études Automatisé	Résidence Papa Oumar Sakho Dakar, Sénégal	Éch: 1/100 Pl. 81/137
	400 FIF — Détection (DET) — R+2	
Date: 06/05/2026	Réf: 1711	BIM vFIF-081 Phase: APD

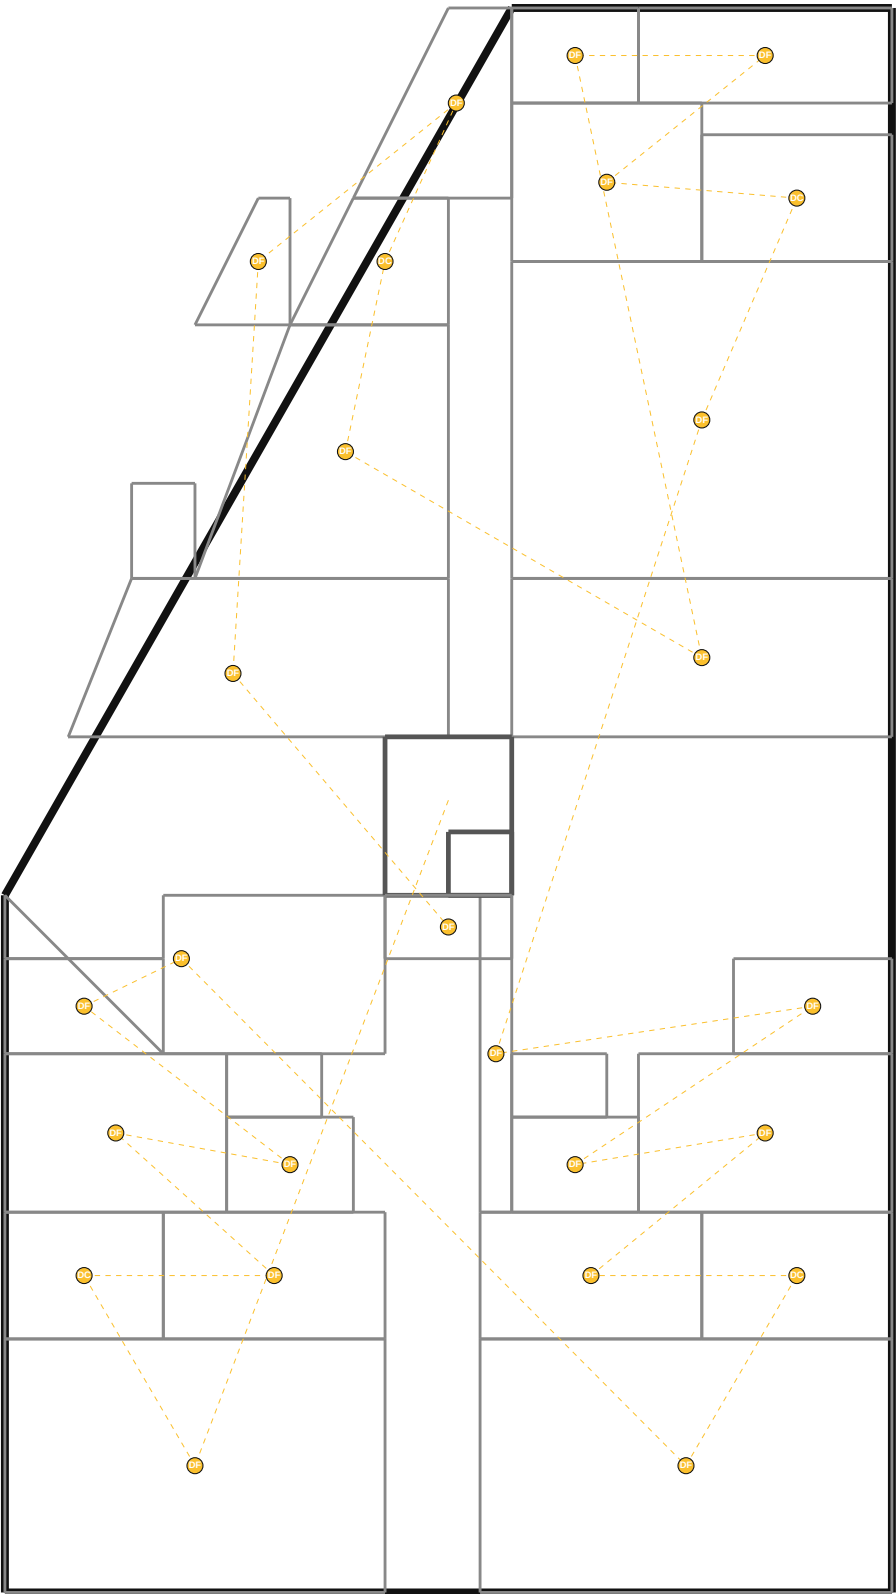

NOMENCLATURE — 400 FIF — Détection (DET)

- Détecteur de fumée: 22
- Détecteur de chaleur: 4


TIJAN AI Bureau d'Études Automatisé	Résidence Papa Oumar Sakho Dakar, Sénégal	Éch: 1/100 Pl. 82/137
	400 FIF — Détection (DET) — R+3	
Date: 06/05/2026	Réf: 1711	BIM vFIF-082 Phase: APD

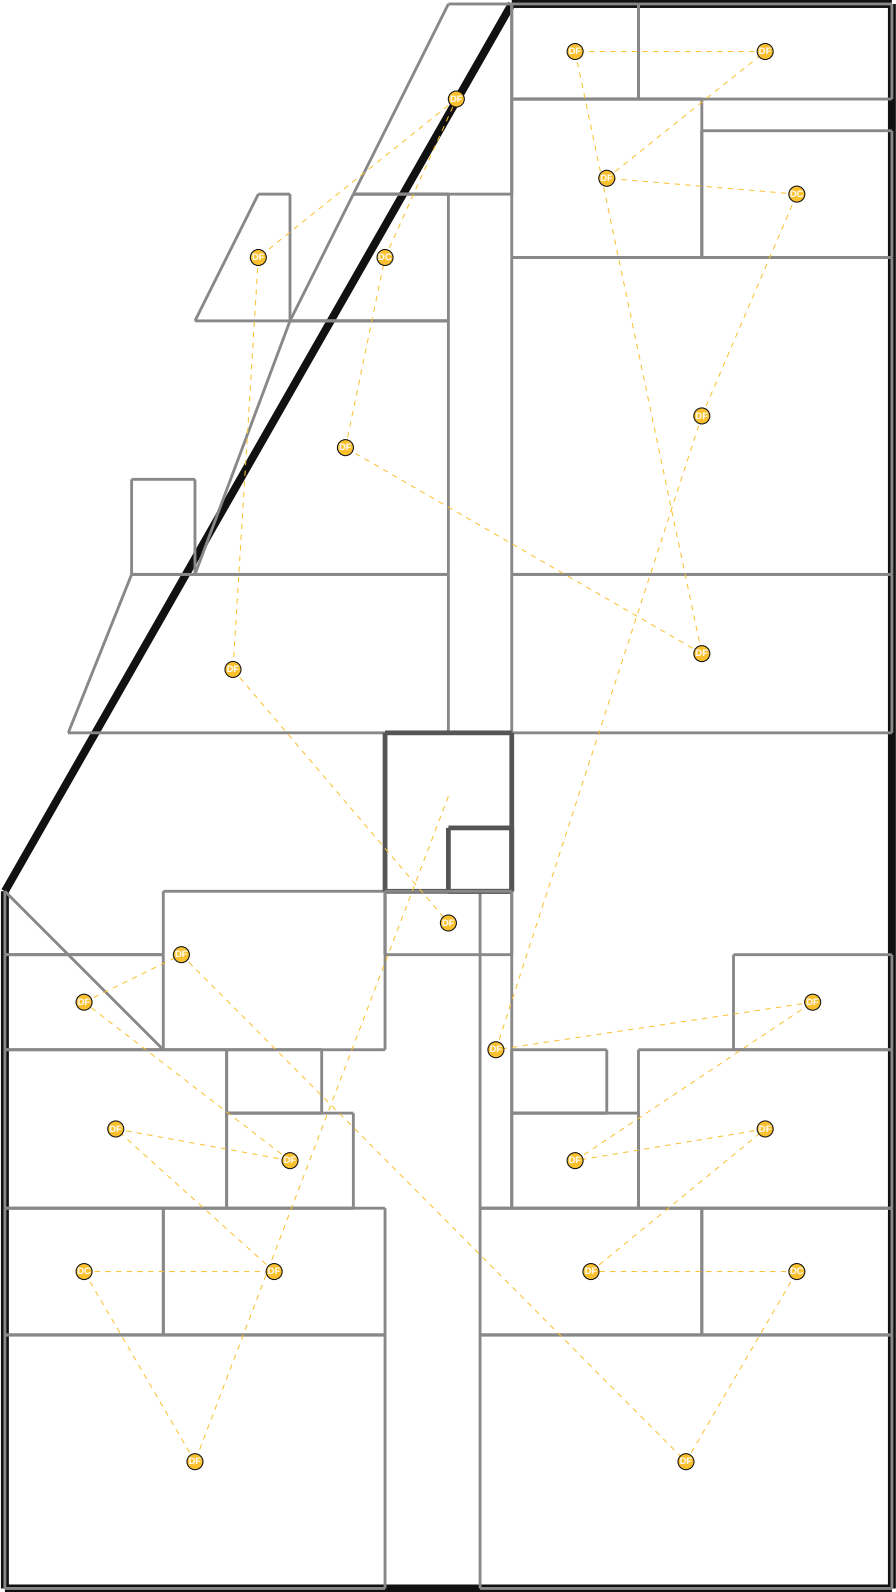

NOMENCLATURE — 400 FIF — Détection (DET)

- Détecteur de fumée: 22
- Détecteur de chaleur: 4


TIJAN AI Bureau d'Études Automatisé	Résidence Papa Oumar Sakho Dakar, Sénégal	Éch: 1/100 Pl. 83/137
	400 FIF — Détection (DET) — R+4	
Date: 06/05/2026	Réf: 1711	BIM vFIF-083 Phase: APD

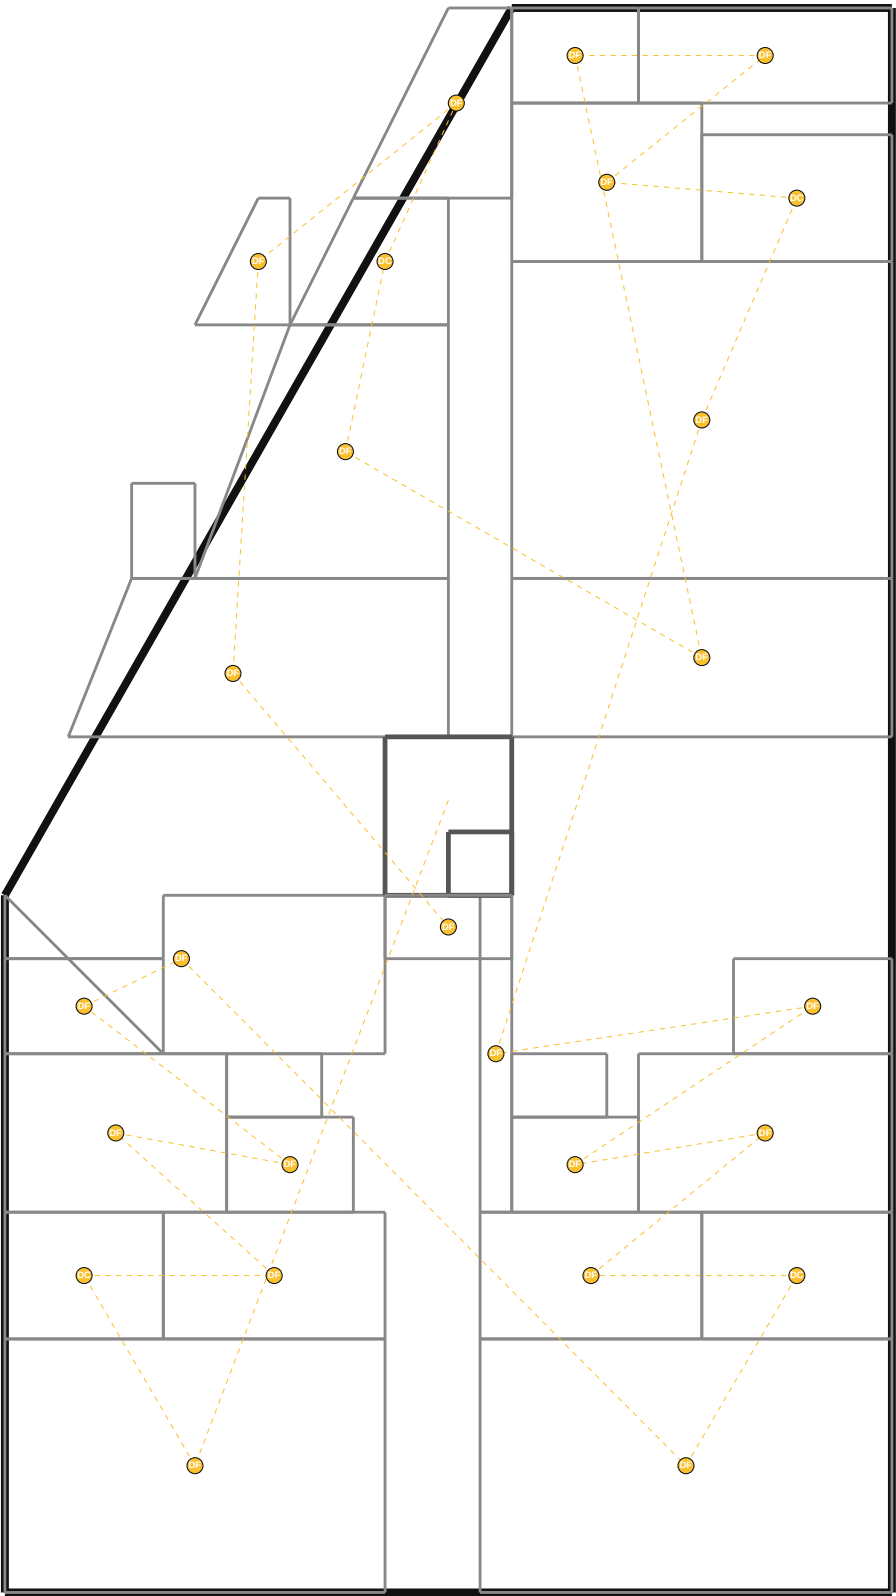

NOMENCLATURE — 400 FIF — Détection (DET)

- Détecteur de fumée: 22
- Détecteur de chaleur: 4


TIJAN AI Bureau d'Études Automatisé	Résidence Papa Oumar Sakho Dakar, Sénégal	Éch: 1/100 Pl. 84/137
	400 FIF — Détection (DET) — R+5	
Date: 06/05/2026	Réf: 1711	BIM vFIF-084 Phase: APD

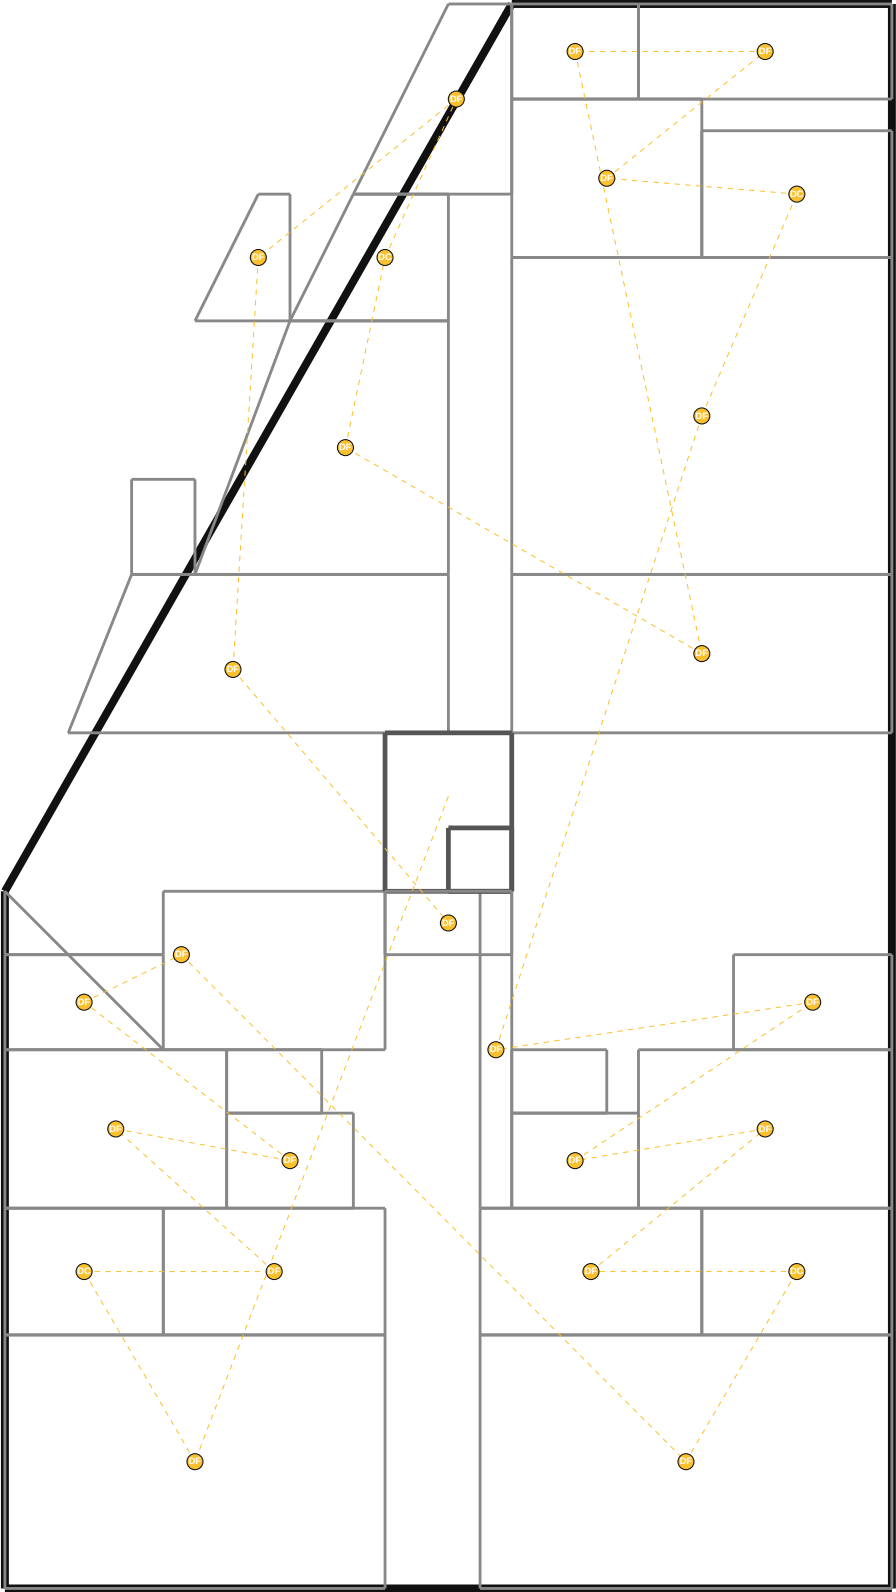

NOMENCLATURE — 400 FIF — Détection (DET)

- Détecteur de fumée: 22
- Détecteur de chaleur: 4


TIJAN AI Bureau d'Études Automatisé	Résidence Papa Oumar Sakho Dakar, Sénégal	Éch: 1/100 Pl. 85/137
	400 FIF — Détection (DET) — R+6	
Date: 06/05/2026	Réf: 1711	BIM vFIF-085 Phase: APD

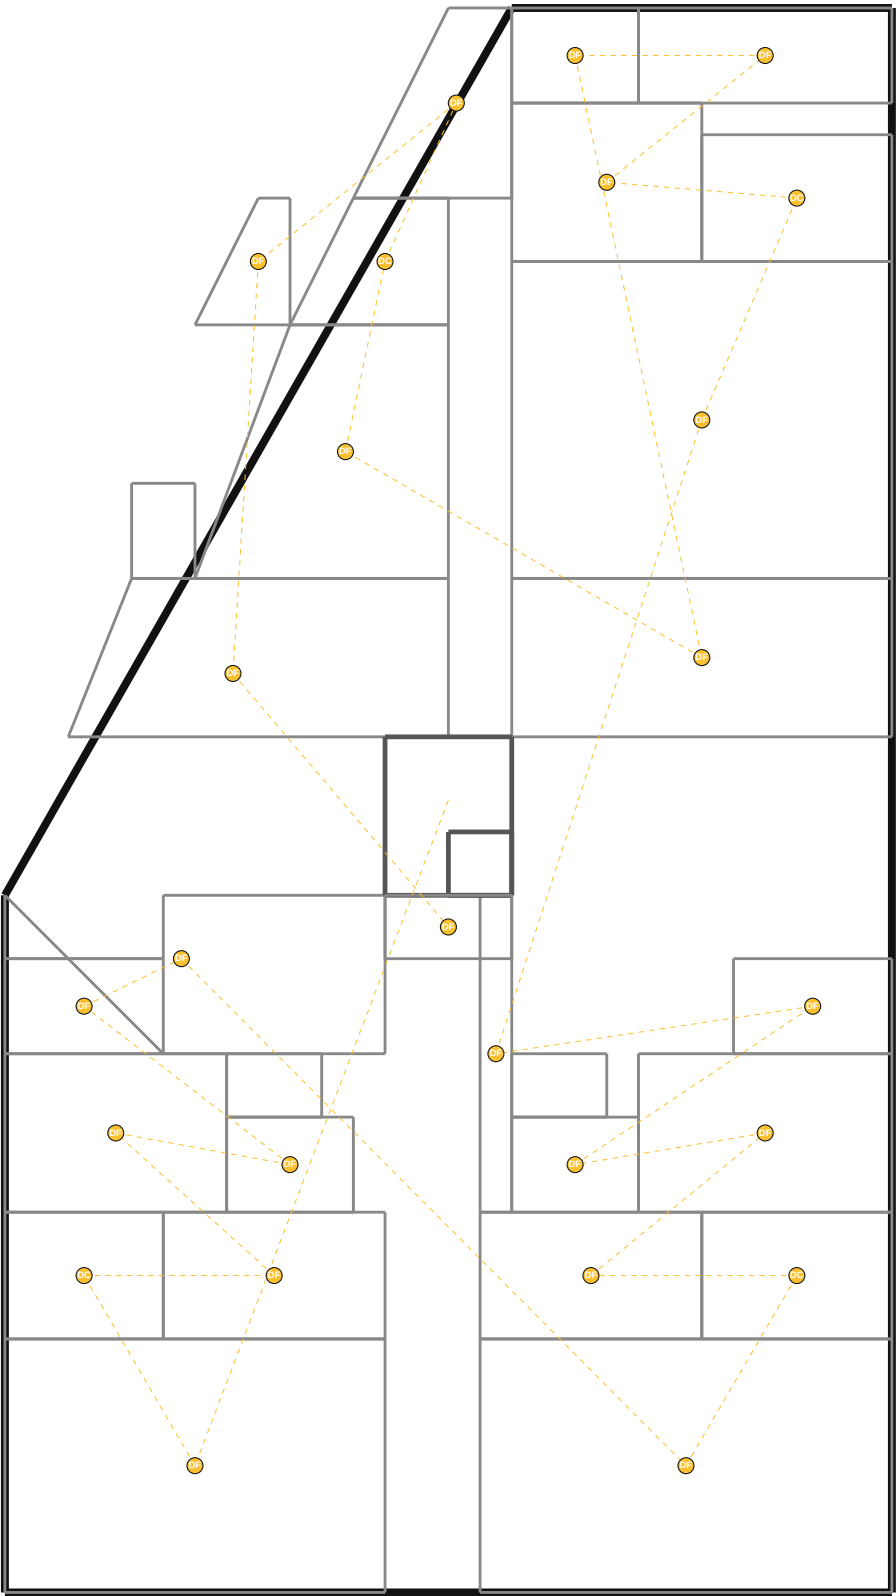

NOMENCLATURE — 400 FIF — Détection (DET)

- Détecteur de fumée: 22
- Détecteur de chaleur: 4

TIJAN AI Bureau d'Études Automatisé	Résidence Papa Oumar Sakho Dakar, Sénégal	Éch: 1/100 Pl. 86/137
	400 FIF — Détection (DET) — R+7	
Date: 06/05/2026	Réf: 1711	BIM vFIF-086 Phase: APD

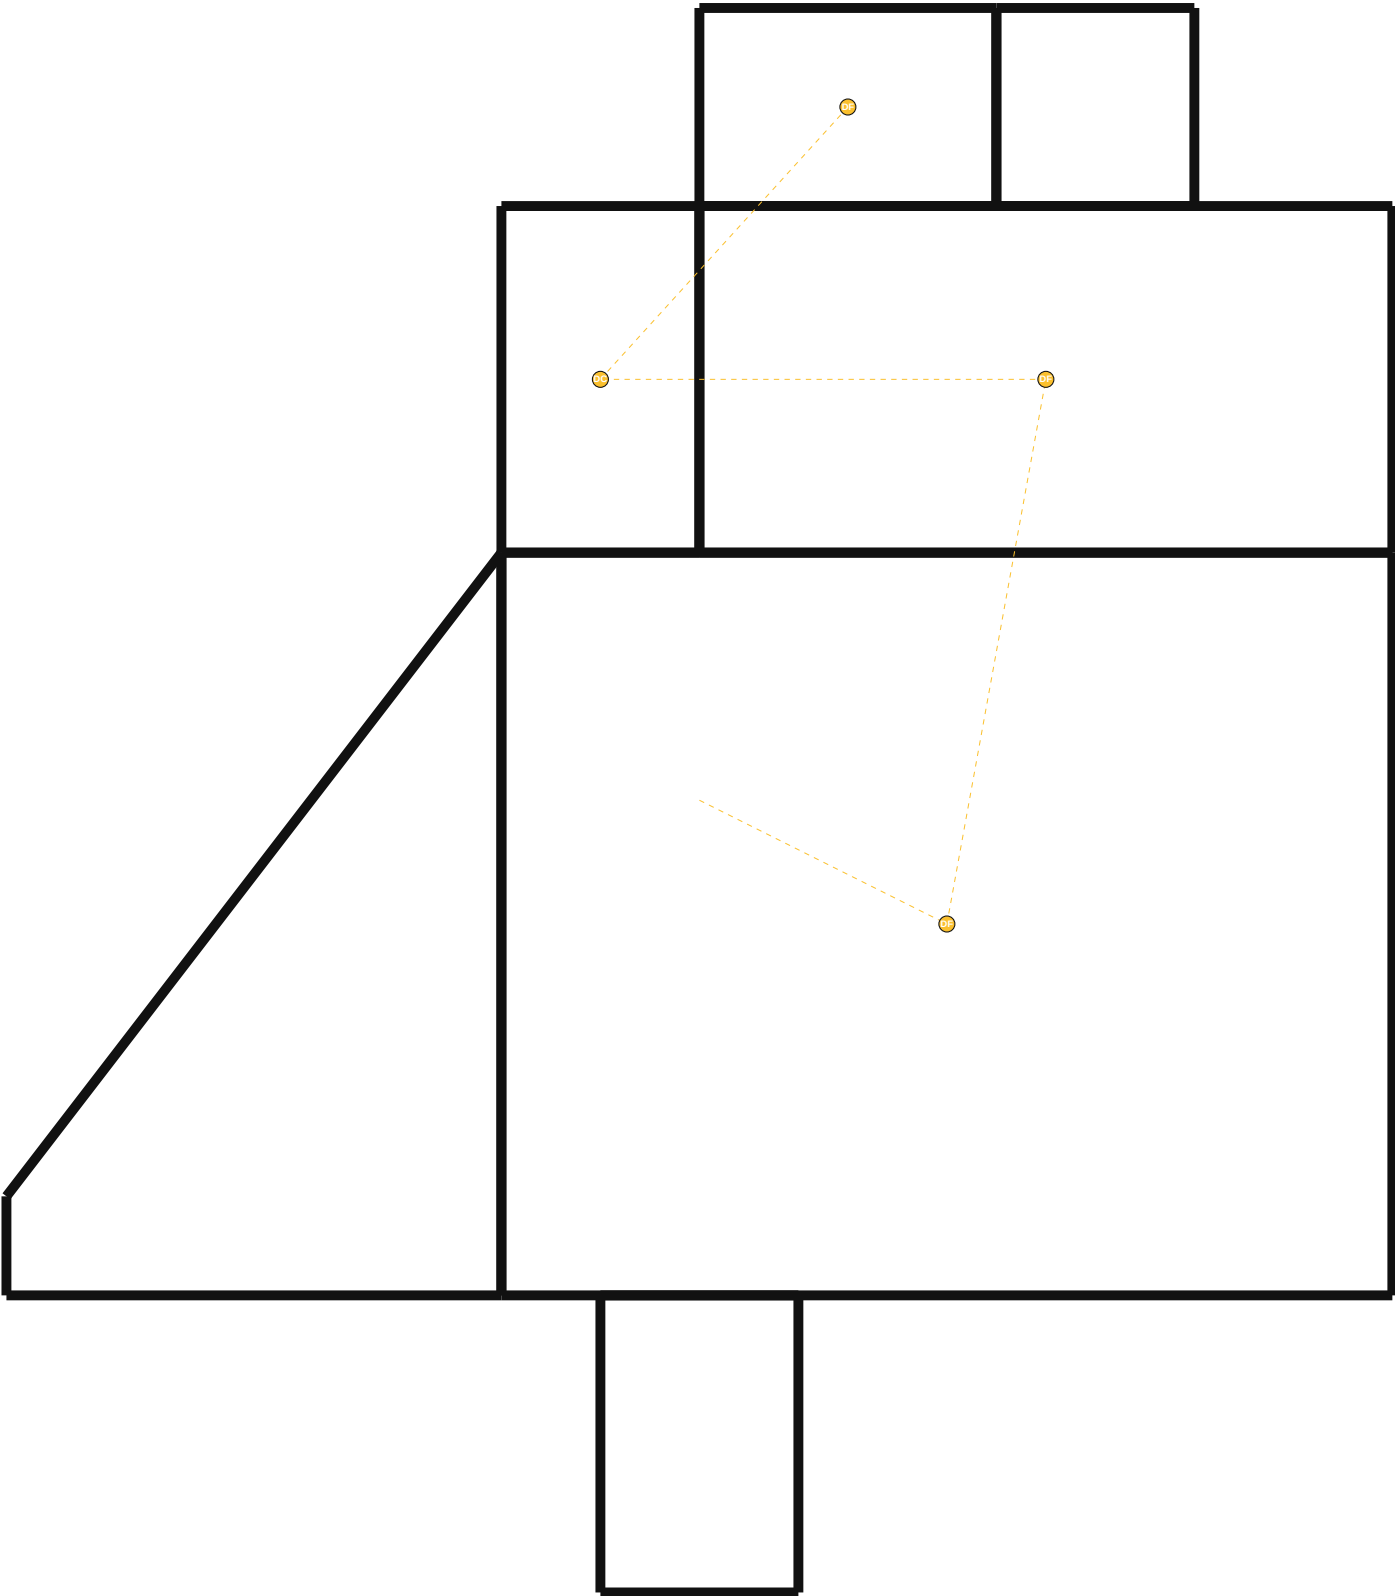


NOMENCLATURE — 400 FIF — Détection (DET)

- Détecteur de fumée: 3
- Détecteur de chaleur: 1

TIJAN AI Bureau d'Études Automatisé	Résidence Papa Oumar Sakho Dakar, Sénégal	Éch: 1/100 Pl. 87/137
	400 FIF — Détection (DET) — R+8	
Date: 06/05/2026	Réf: 1711	BIM vFIF-087 Phase: APD

510 HCU — Éclairage (ECL) — Sous-Sol

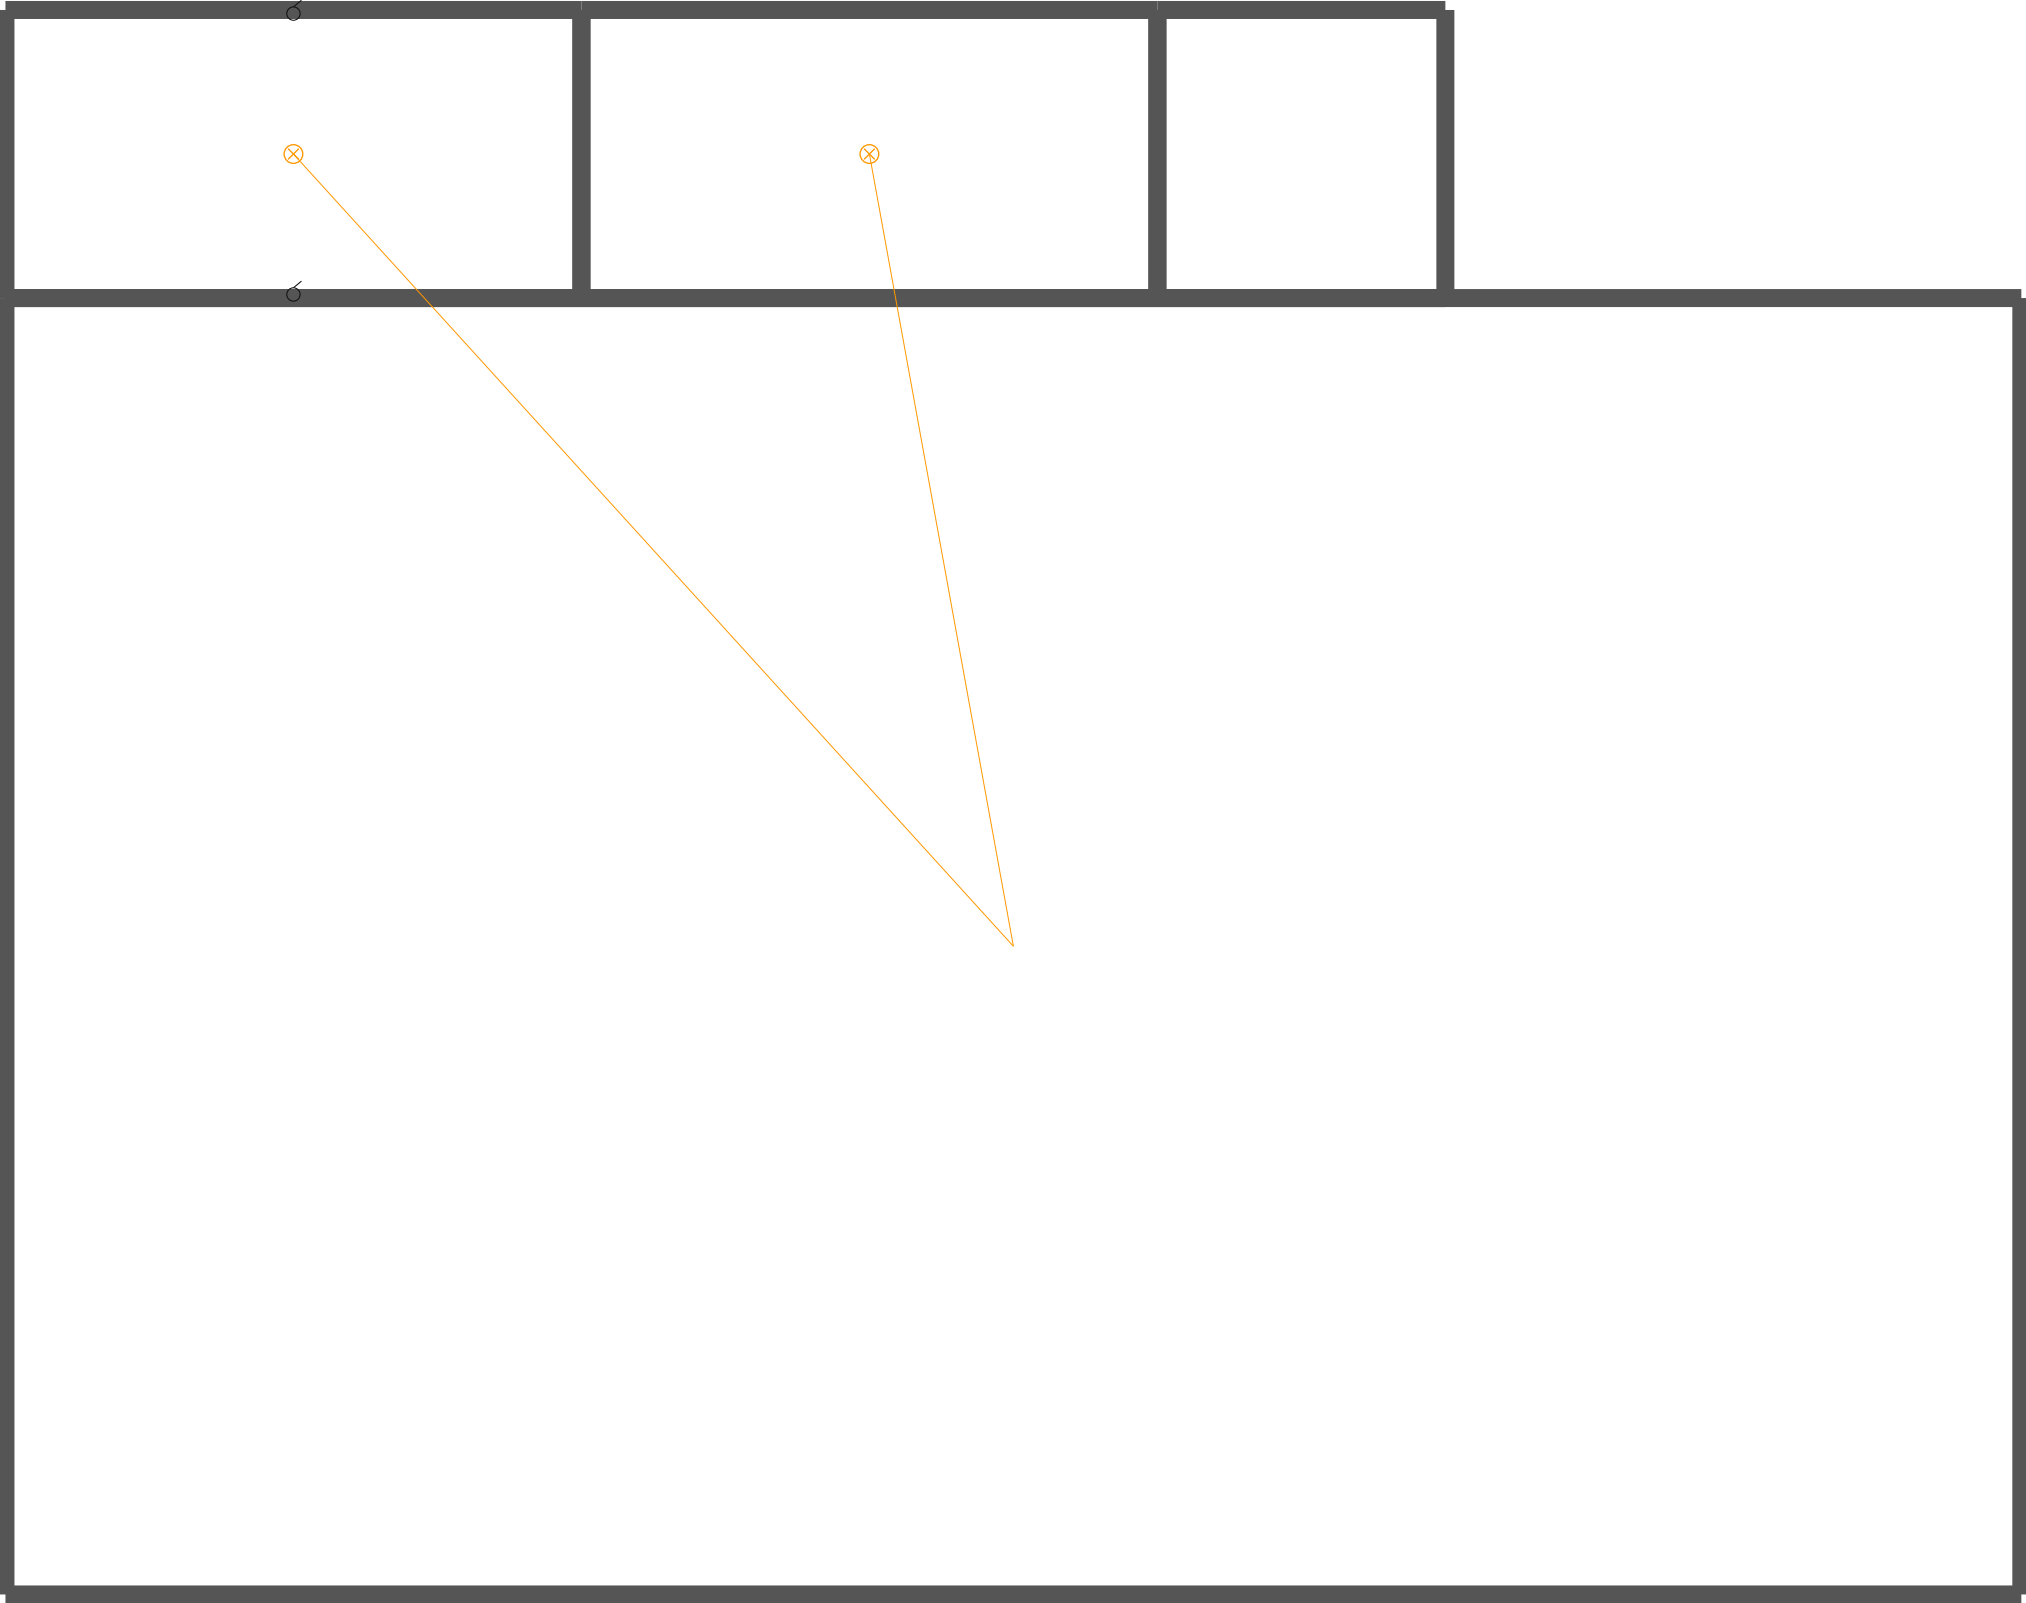


NOMENCLATURE — 510 HCU — Éclairage (ECL)

- Interrupteur va-et-vient: 2
- Plafonnier: 2

TIJAN AI Bureau d'Études Automatisé	Résidence Papa Oumar Sakho Dakar, Sénégal	Éch: 1/100 Pl. 88/137
	510 HCU — Éclairage (ECL) — Sous-Sol	
Date: 06/05/2026	Réf: 1711	BIM vHCU-088 Phase: APD


510 HCU — Éclairage (ECL) — RDC

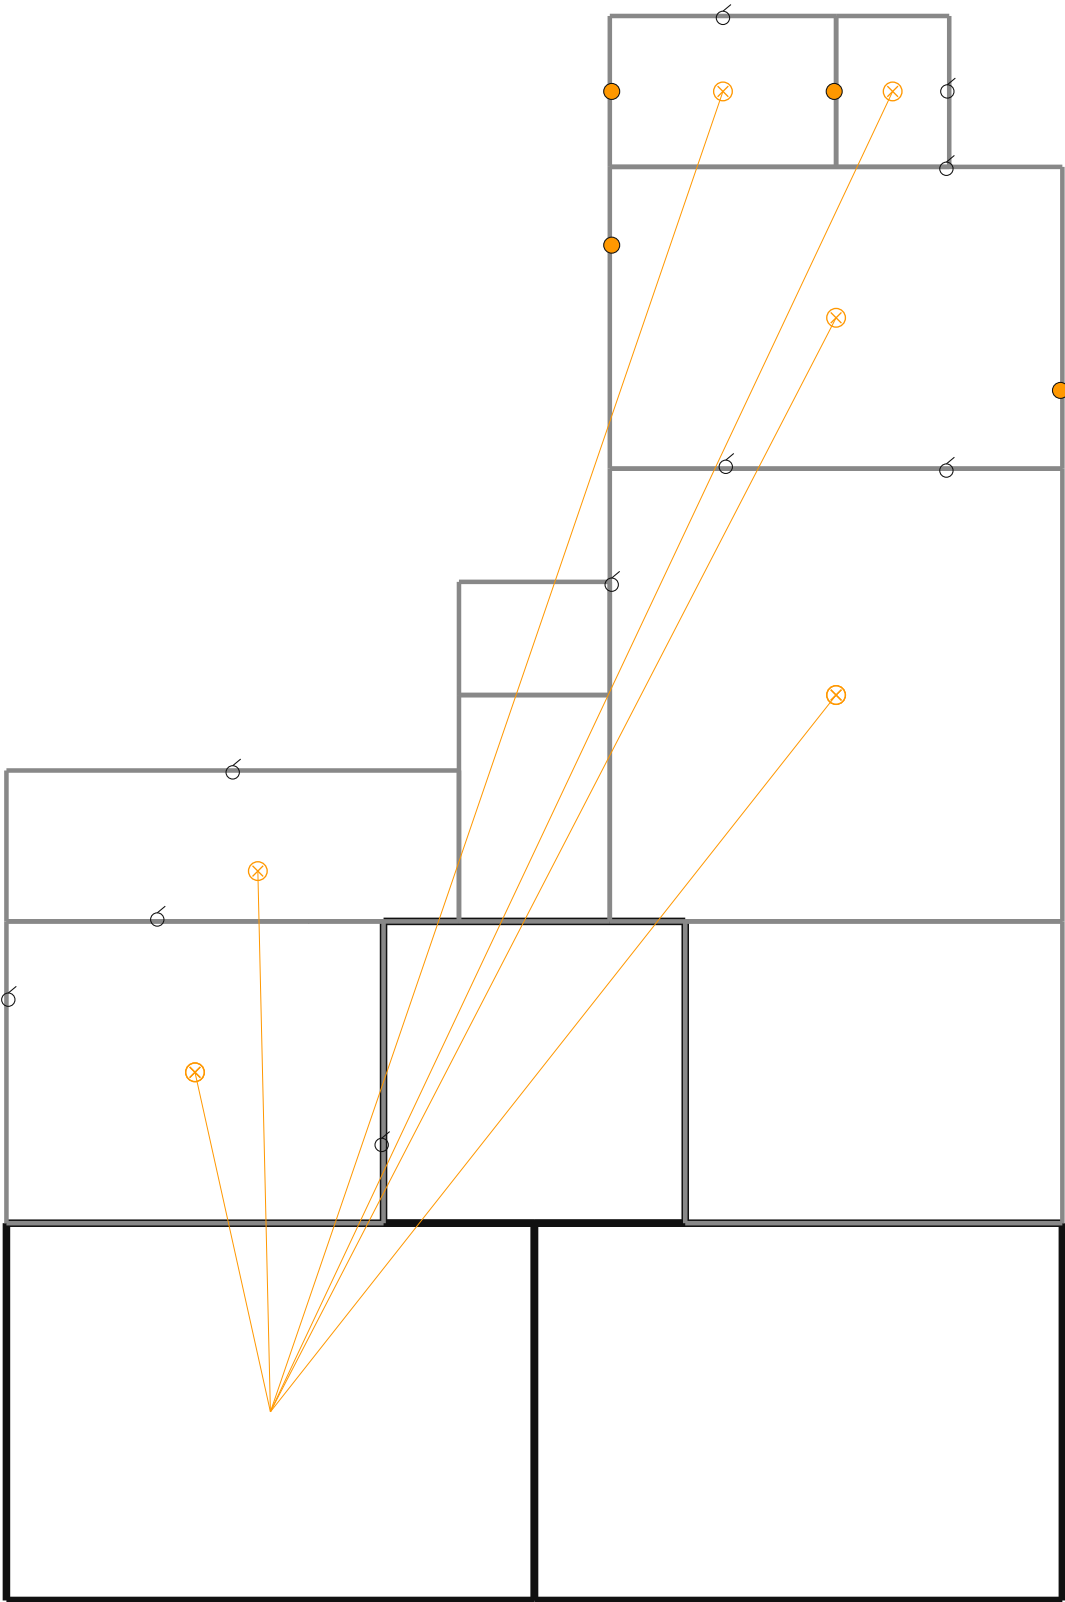

NOMENCLATURE — 510 HCU — Éclairage (ECL)

- Interrupteur va-et-vient: 8
- Plafonnier: 7
- Applique tête de lit: 2
- Interrupteur: 2
- Applique miroir: 2
- Plafonnier IP44: 1


TIJAN AI Bureau d'Études Automatisé	Résidence Papa Oumar Sakho Dakar, Sénégal	Éch: 1/100 Pl. 89/137
	510 HCU — Éclairage (ECL) — RDC	
Date: 06/05/2026	Réf: 1711	BIM vHCU-089 Phase: APD

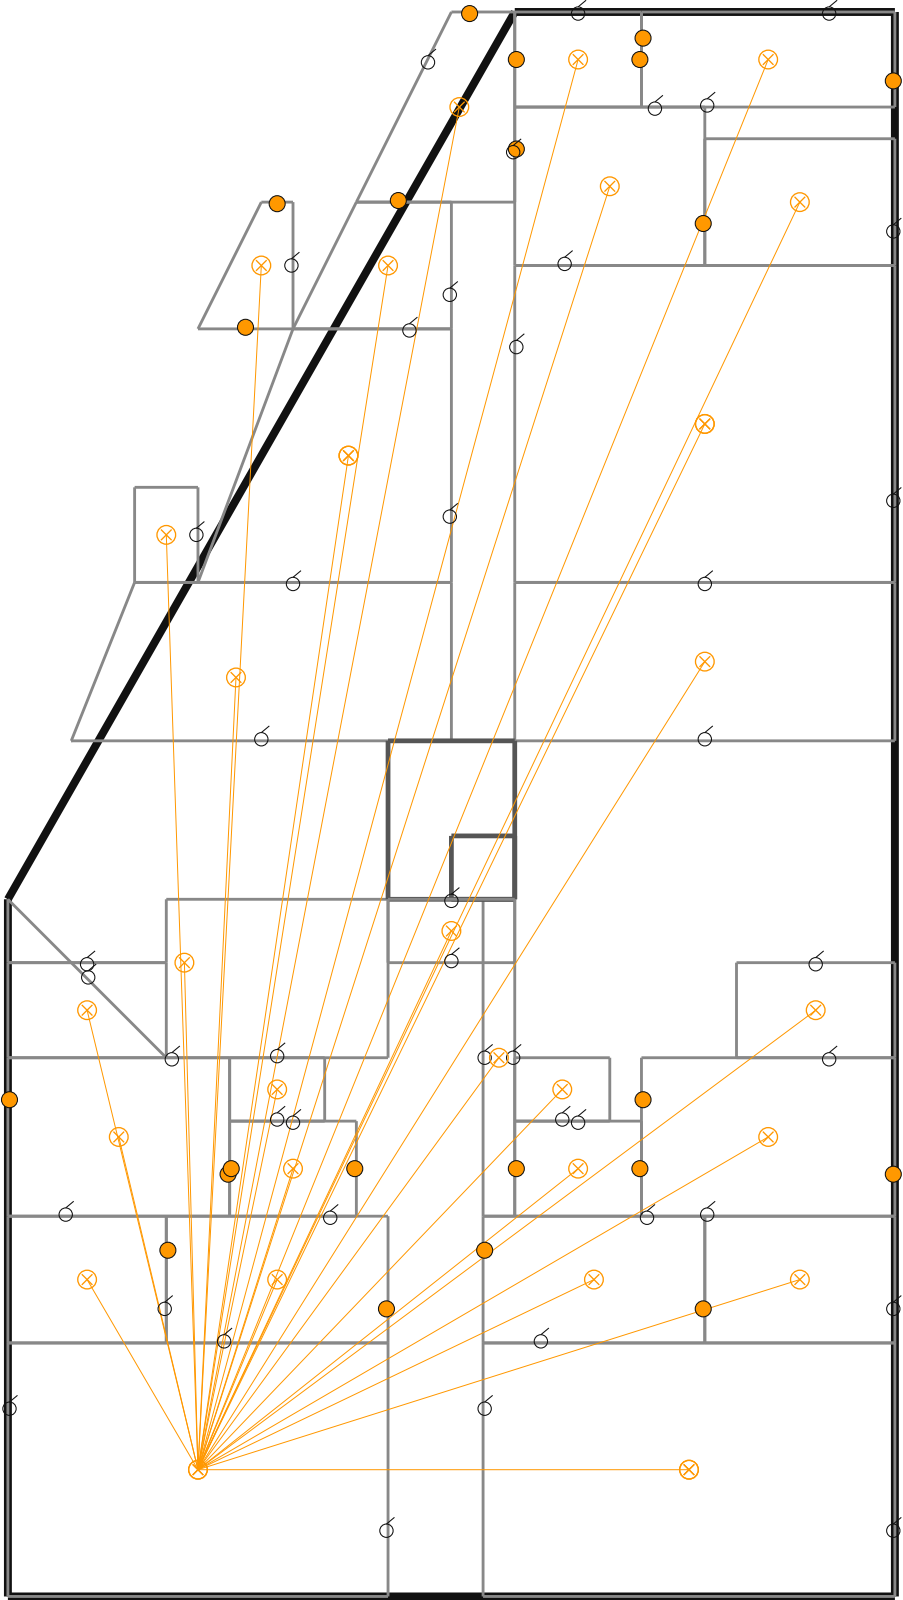

NOMENCLATURE — 510 HCU — Éclairage (ECL)

- Interrupteur va-et-vient: 32
- Plafonnier: 29
- Applique tête de lit: 14
- Interrupteur: 13
- Applique miroir: 8
- Plafonnier IP44: 4


TIJAN AI Bureau d'Études Automatisé	Résidence Papa Oumar Sakho Dakar, Sénégal	Éch: 1/100 Pl. 90/137
	510 HCU — Éclairage (ECL) — R+1	
Date: 06/05/2026	Réf: 1711	BIM vHCU-090 Phase: APD

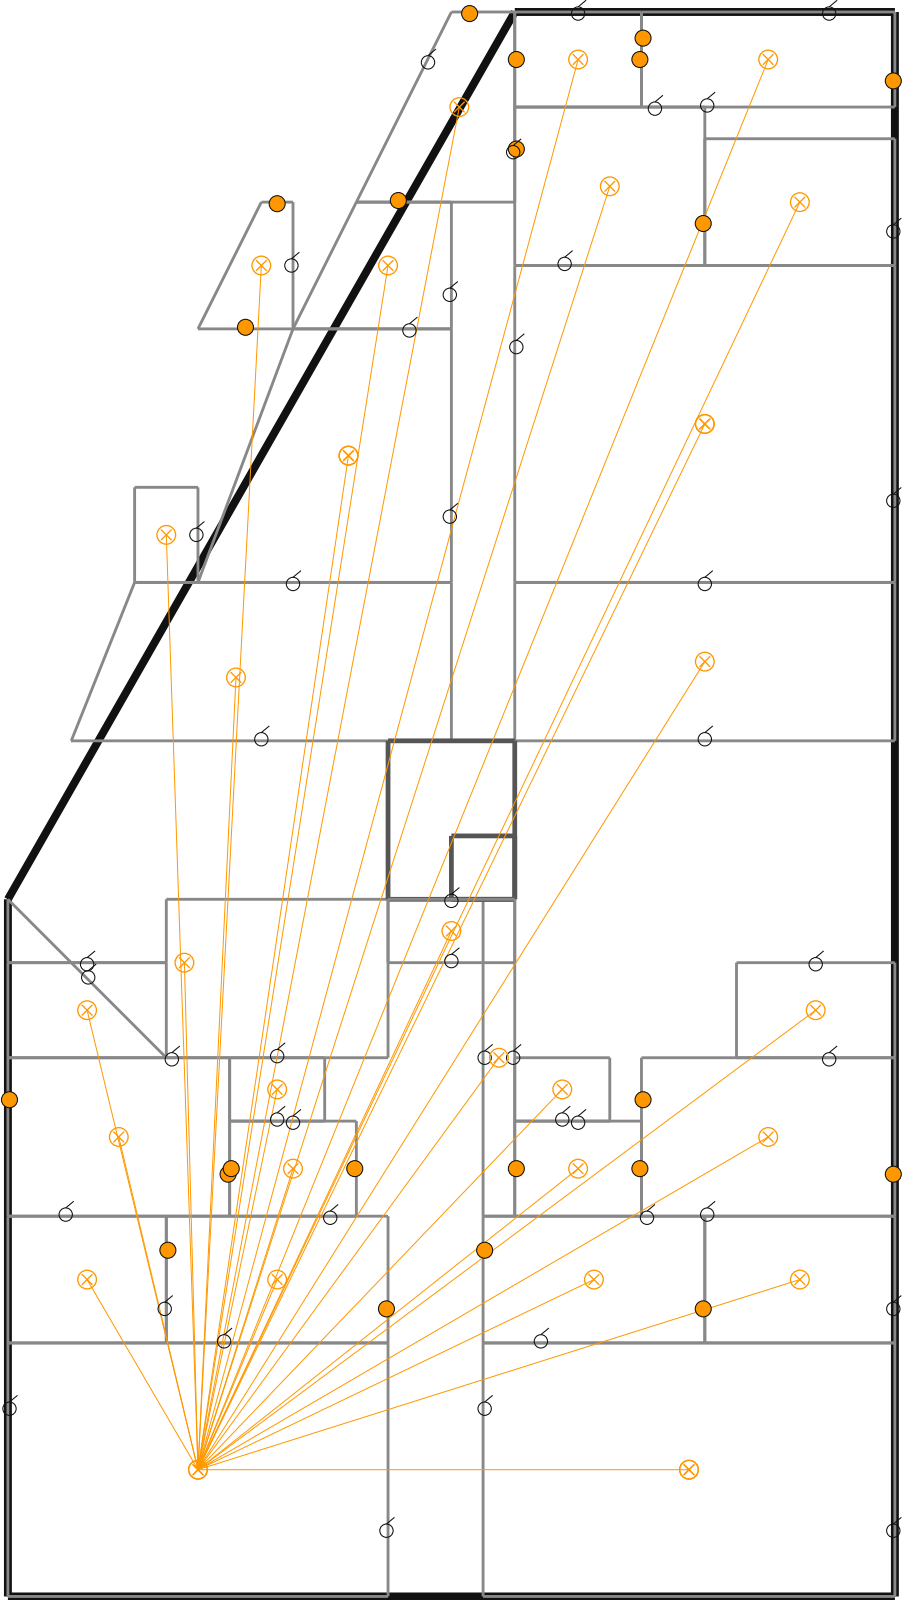

NOMENCLATURE — 510 HCU — Éclairage (ECL)

- Interrupteur va-et-vient: 32
- Plafonnier: 29
- Applique tête de lit: 14
- Interrupteur: 13
- Applique miroir: 8
- Plafonnier IP44: 4


TIJAN AI Bureau d'Études Automatisé	Résidence Papa Oumar Sakho Dakar, Sénégal	Éch: 1/100 Pl. 91/137
	510 HCU — Éclairage (ECL) — R+2	
Date: 06/05/2026	Réf: 1711	BIM vHCU-091 Phase: APD

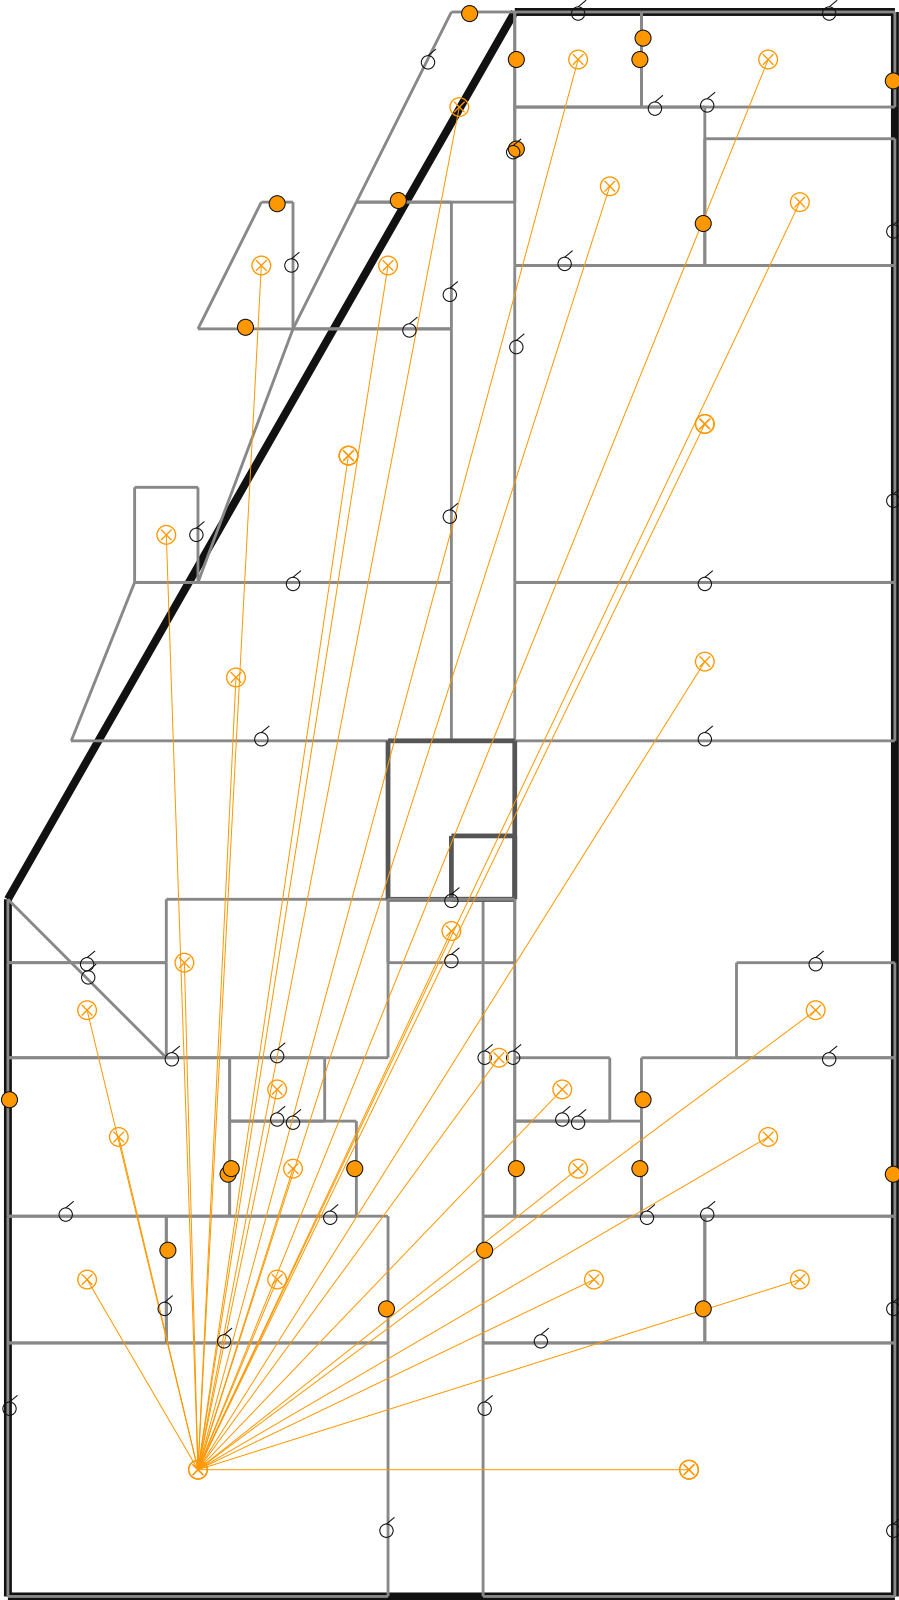

NOMENCLATURE — 510 HCU — Éclairage (ECL)

- Interrupteur va-et-vient: 32
- Plafonnier: 29
- Applique tête de lit: 14
- Interrupteur: 13
- Applique miroir: 8
- Plafonnier IP44: 4


TIJAN AI Bureau d'Études Automatisé	Résidence Papa Oumar Sakho Dakar, Sénégal	Éch: 1/100 Pl. 92/137
	510 HCU — Éclairage (ECL) — R+3	
Date: 06/05/2026	Réf: 1711	BIM vHCU-092 Phase: APD

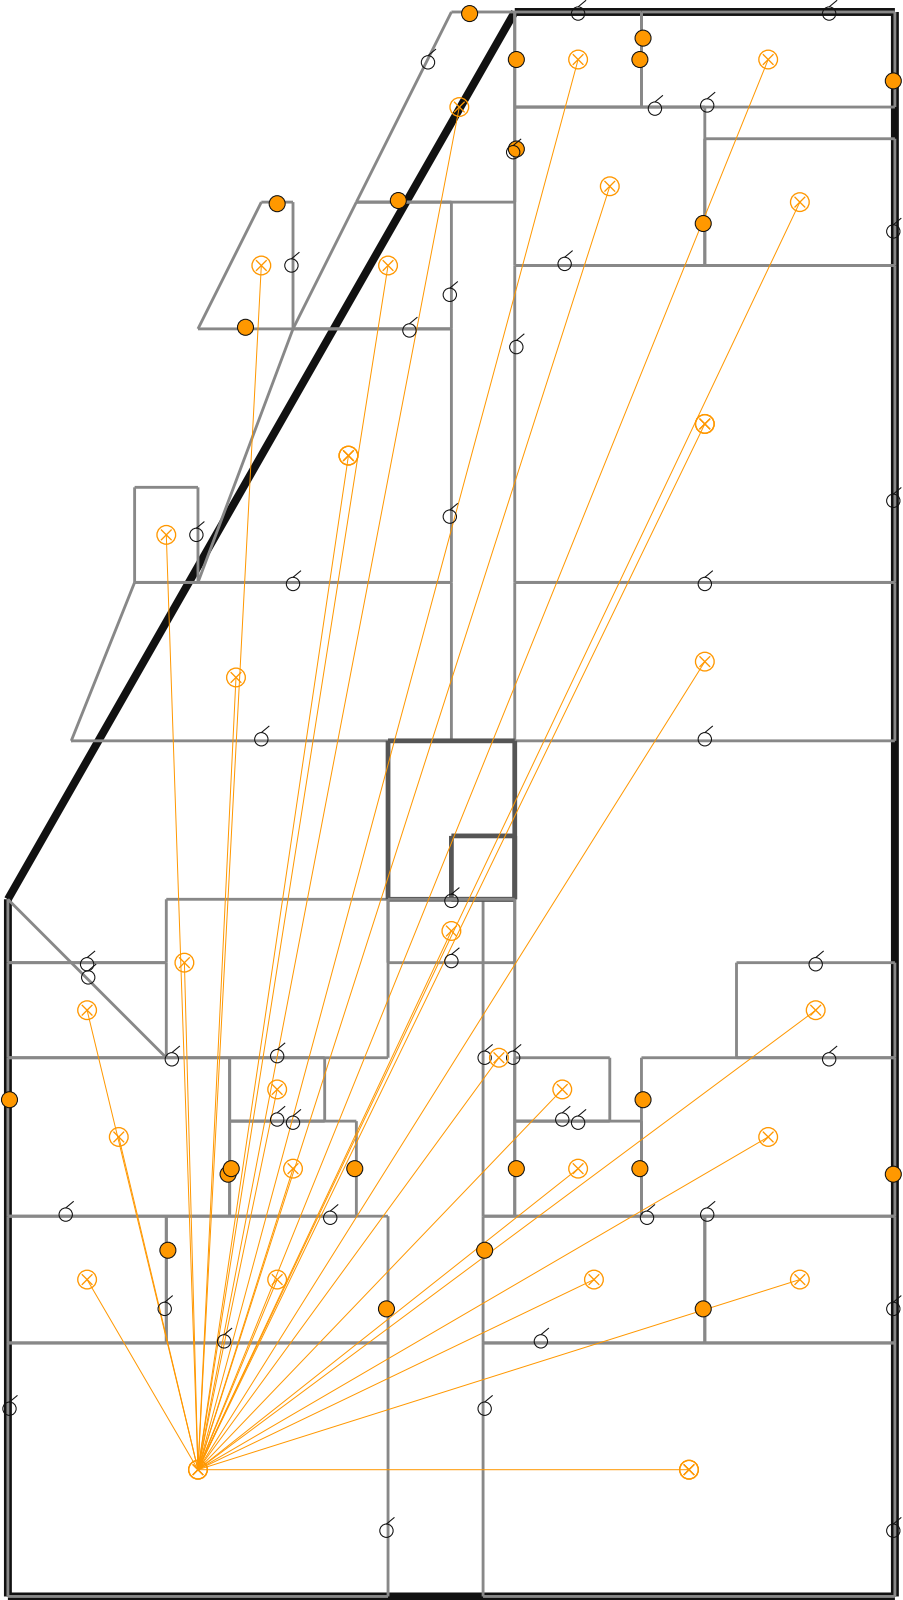

NOMENCLATURE — 510 HCU — Éclairage (ECL)

- Interrupteur va-et-vient: 32
- Plafonnier: 29
- Applique tête de lit: 14
- Interrupteur: 13
- Applique miroir: 8
- Plafonnier IP44: 4


TIJAN AI Bureau d'Études Automatisé	Résidence Papa Oumar Sakho Dakar, Sénégal	Éch: 1/100 Pl. 93/137
	510 HCU — Éclairage (ECL) — R+4	
Date: 06/05/2026	Réf: 1711	BIM vHCU-093 Phase: APD

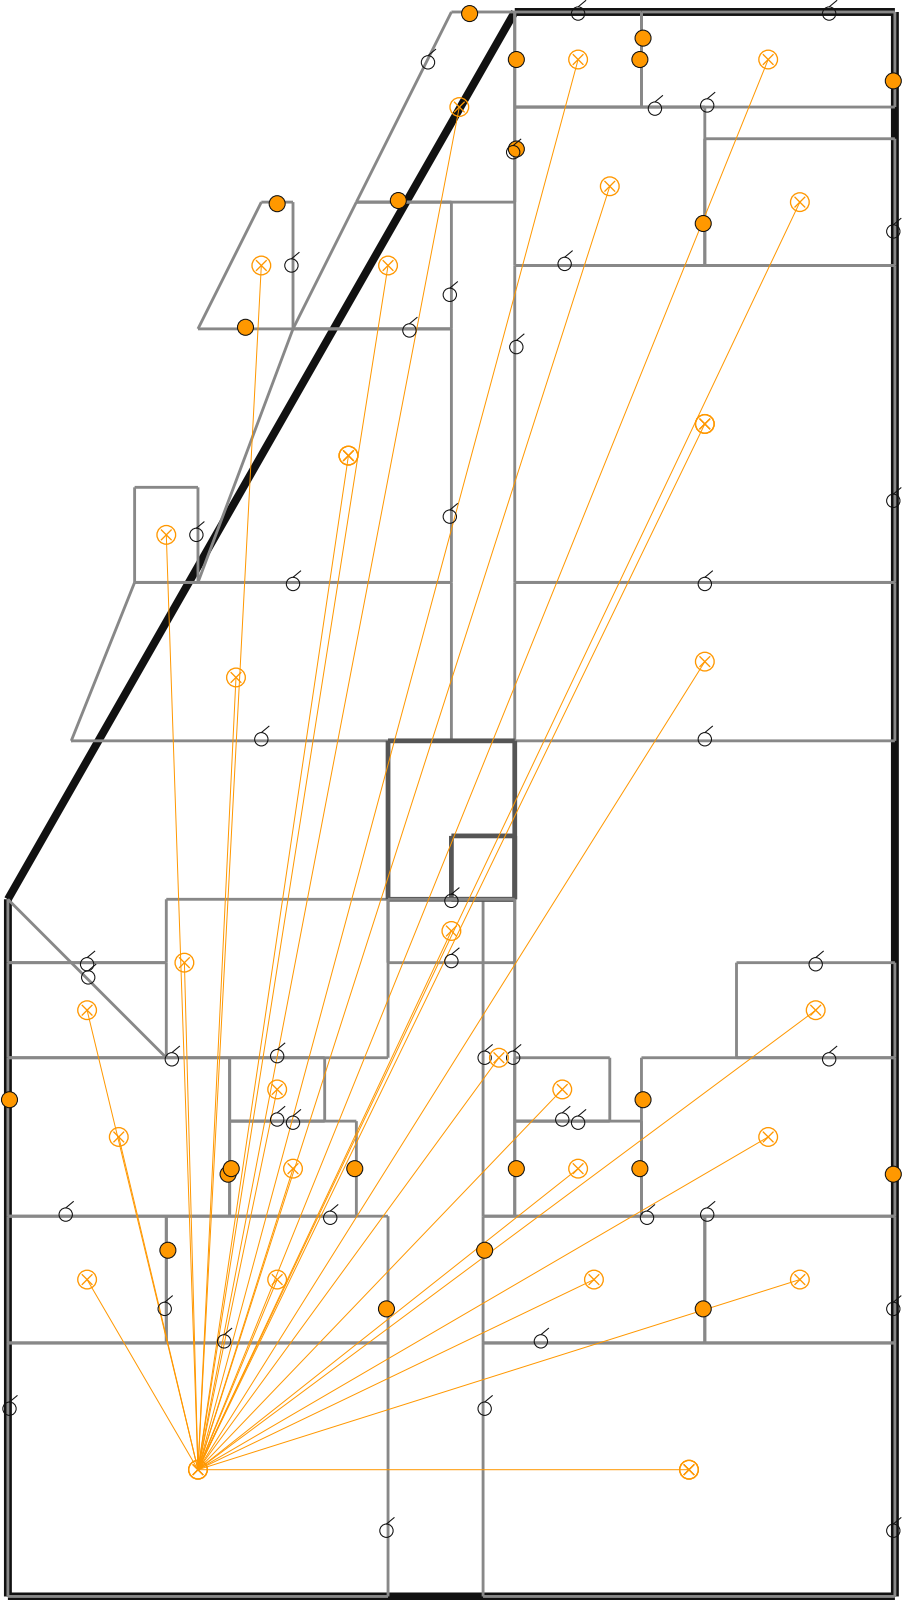

NOMENCLATURE — 510 HCU — Éclairage (ECL)

- Interrupteur va-et-vient: 32
- Plafonnier: 29
- Applique tête de lit: 14
- Interrupteur: 13
- Applique miroir: 8
- Plafonnier IP44: 4


TIJAN AI Bureau d'Études Automatisé	Résidence Papa Oumar Sakho Dakar, Sénégal	Éch: 1/100 Pl. 94/137
	510 HCU — Éclairage (ECL) — R+5	
Date: 06/05/2026	Réf: 1711	BIM vHCU-094 Phase: APD

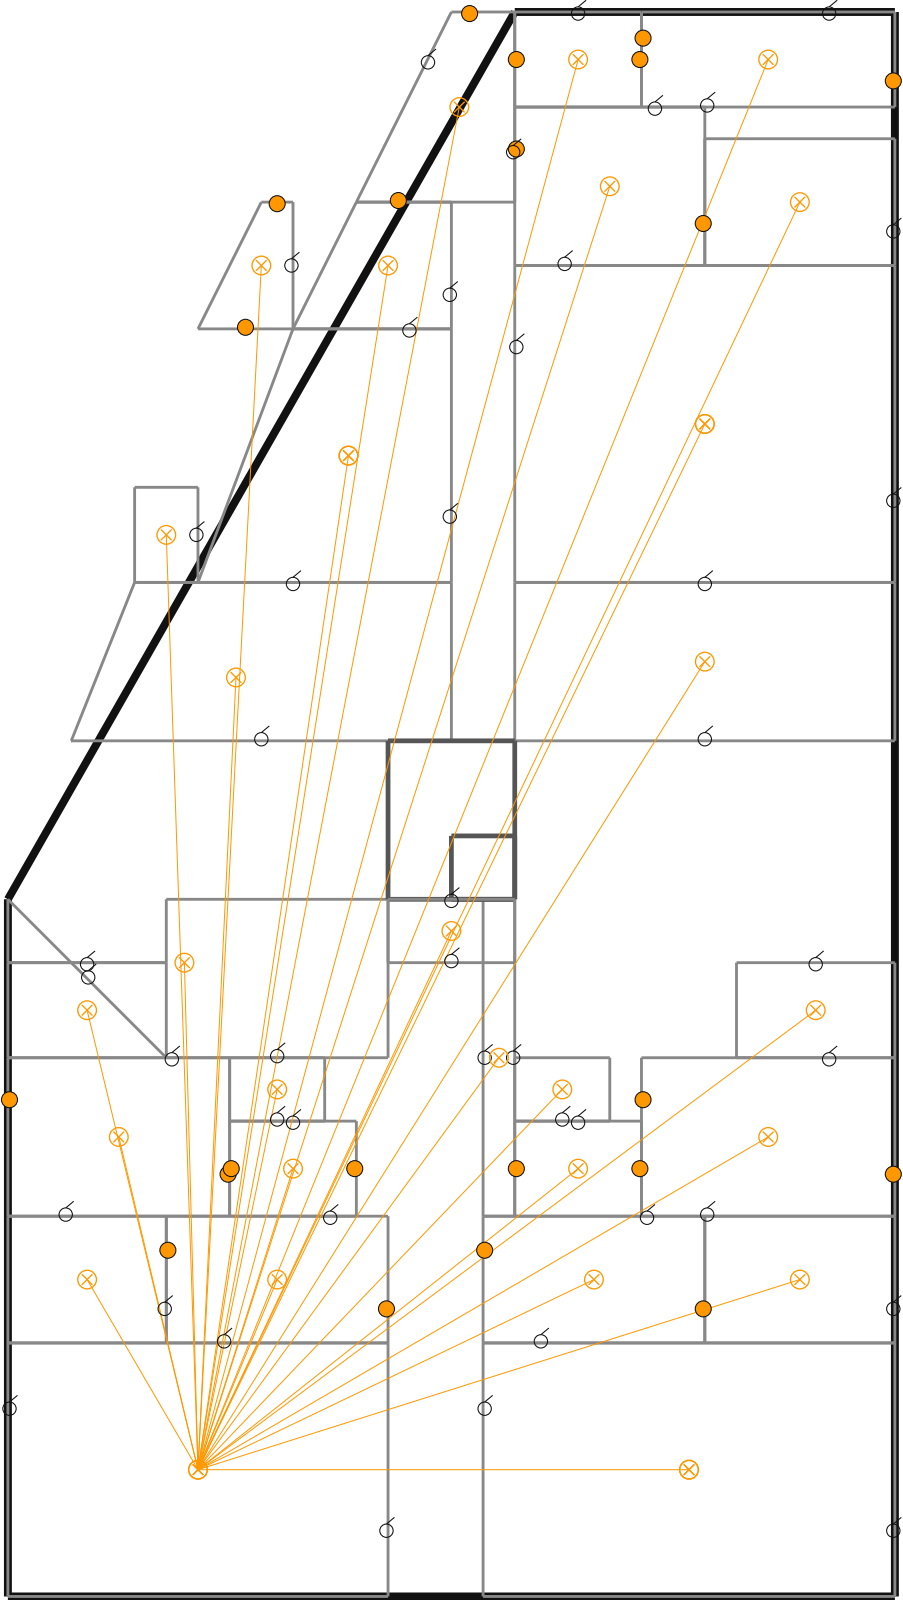

NOMENCLATURE — 510 HCU — Éclairage (ECL)

- Interrupteur va-et-vient: 32
- Plafonnier: 29
- Applique tête de lit: 14
- Interrupteur: 13
- Applique miroir: 8
- Plafonnier IP44: 4


TIJAN AI Bureau d'Études Automatisé	Résidence Papa Oumar Sakho Dakar, Sénégal	Éch: 1/100 Pl. 95/137
	510 HCU — Éclairage (ECL) — R+6	
Date: 06/05/2026	Réf: 1711	BIM vHCU-095 Phase: APD

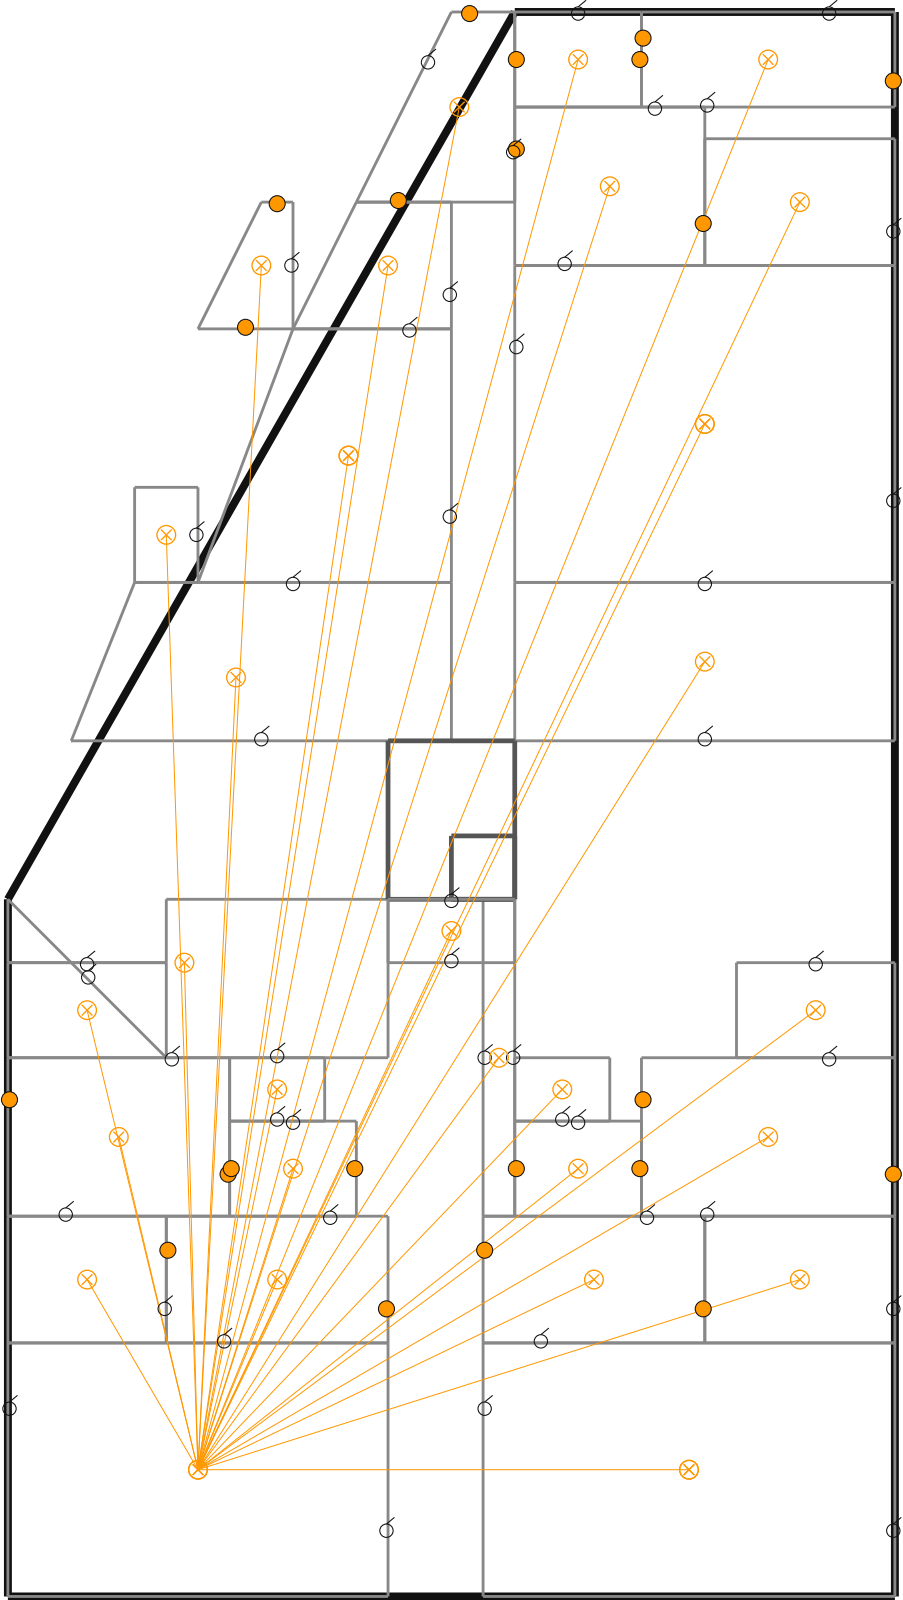

NOMENCLATURE — 510 HCU — Éclairage (ECL)

- Interrupteur va-et-vient: 32
- Plafonnier: 29
- Applique tête de lit: 14
- Interrupteur: 13
- Applique miroir: 8
- Plafonnier IP44: 4


TIJAN AI Bureau d'Études Automatisé	Résidence Papa Oumar Sakho Dakar, Sénégal	Éch: 1/100 Pl. 96/137
	510 HCU — Éclairage (ECL) — R+7	
Date: 06/05/2026	Réf: 1711	BIM vHCU-096 Phase: APD

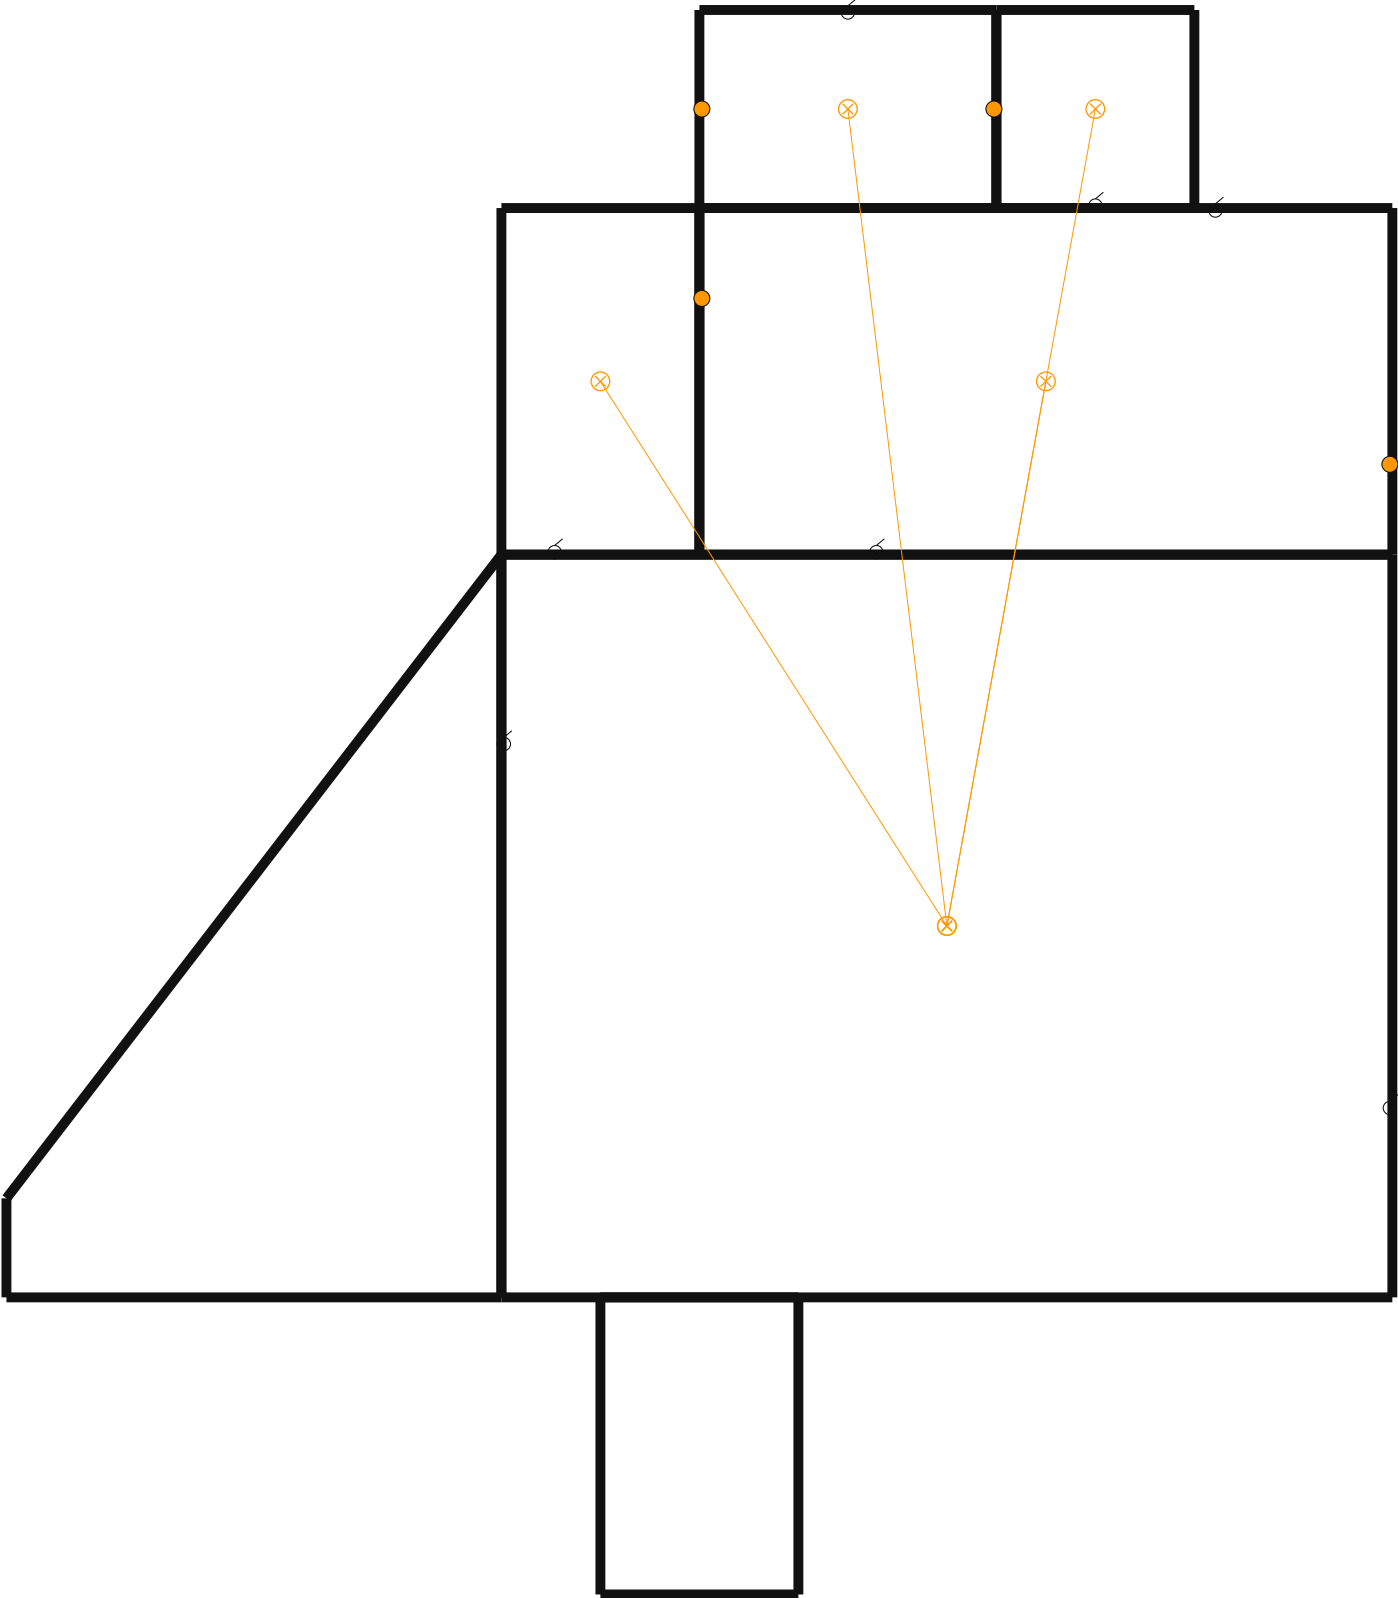

NOMENCLATURE — 510 HCU — Éclairage (ECL)

- Plafonnier: 5
- Interrupteur va-et-vient: 4
- Interrupteur: 3
- Applique tête de lit: 2
- Applique miroir: 2
- Plafonnier IP44: 1


TIJAN AI Bureau d'Études Automatisé	Résidence Papa Oumar Sakho Dakar, Sénégal	Éch: 1/100 Pl. 97/137
	510 HCU — Éclairage (ECL) — R+8	
Date: 06/05/2026	Réf: 1711	BIM vHCU-097 Phase: APD

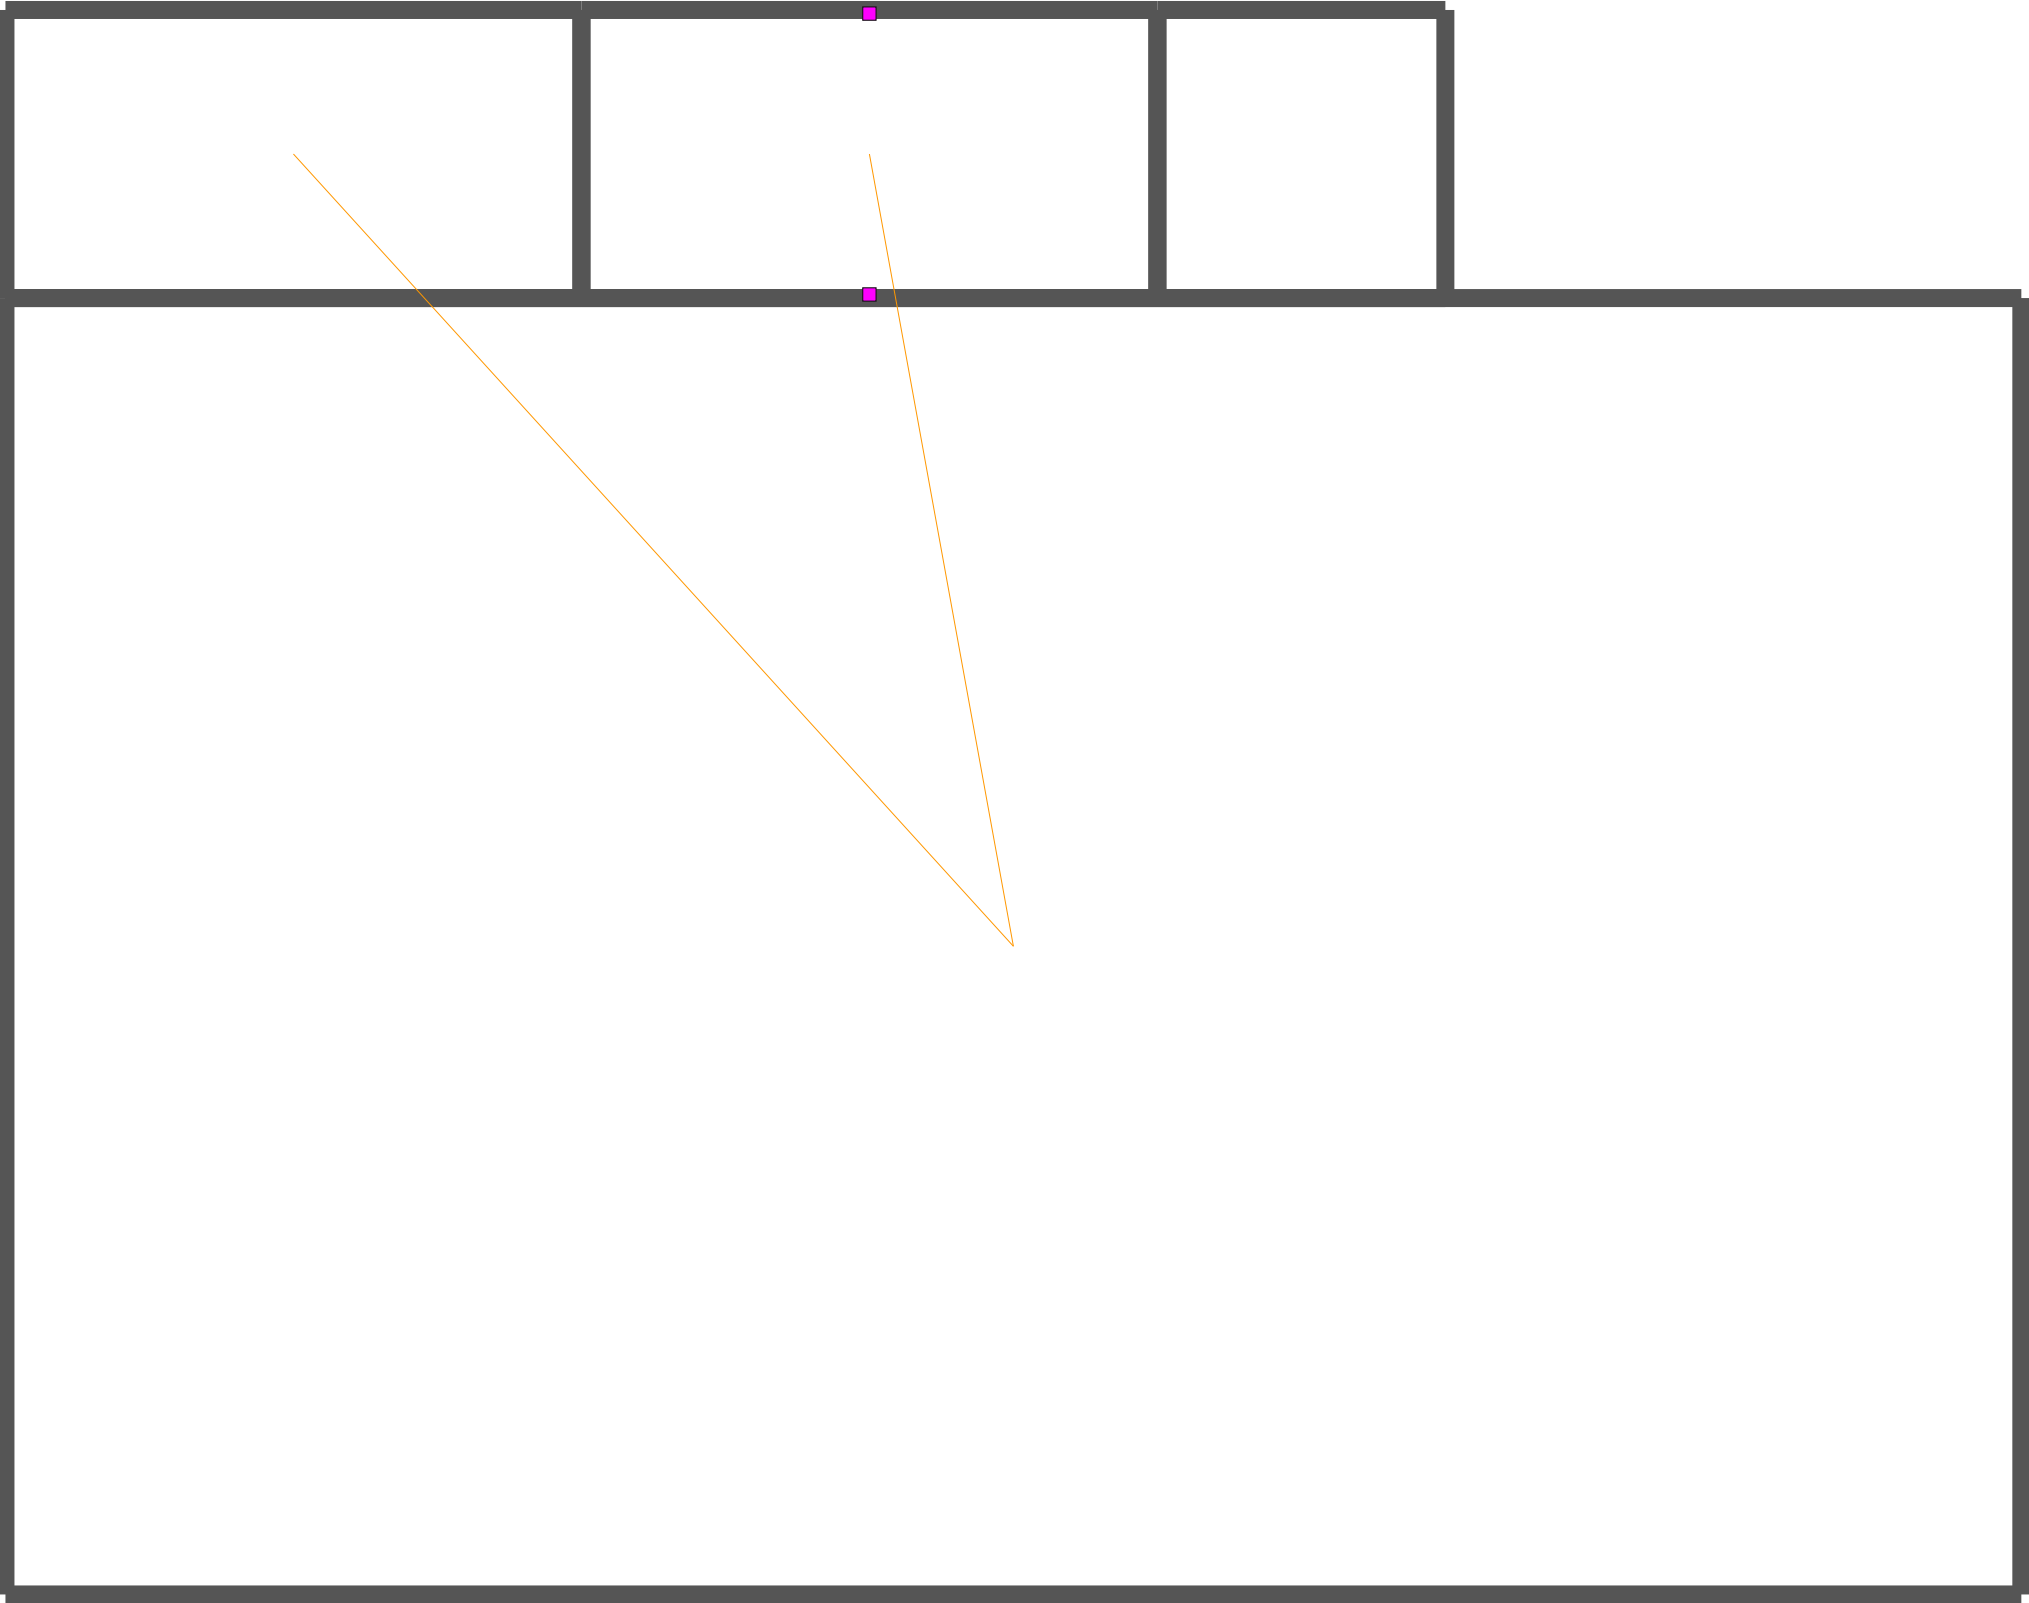

NOMENCLATURE — 510 HCU — Prises de Courant (PC)

• Prise 2P+T 16A: 2


TIJAN AI Bureau d'Études Automatisé	Résidence Papa Oumar Sakho Dakar, Sénégal	Éch: 1/100 Pl. 98/137
	510 HCU — Prises de Courant (PC) — Sous-Sol	
Date: 06/05/2026	Réf: 1711	BIM vHCU-098 Phase: APD

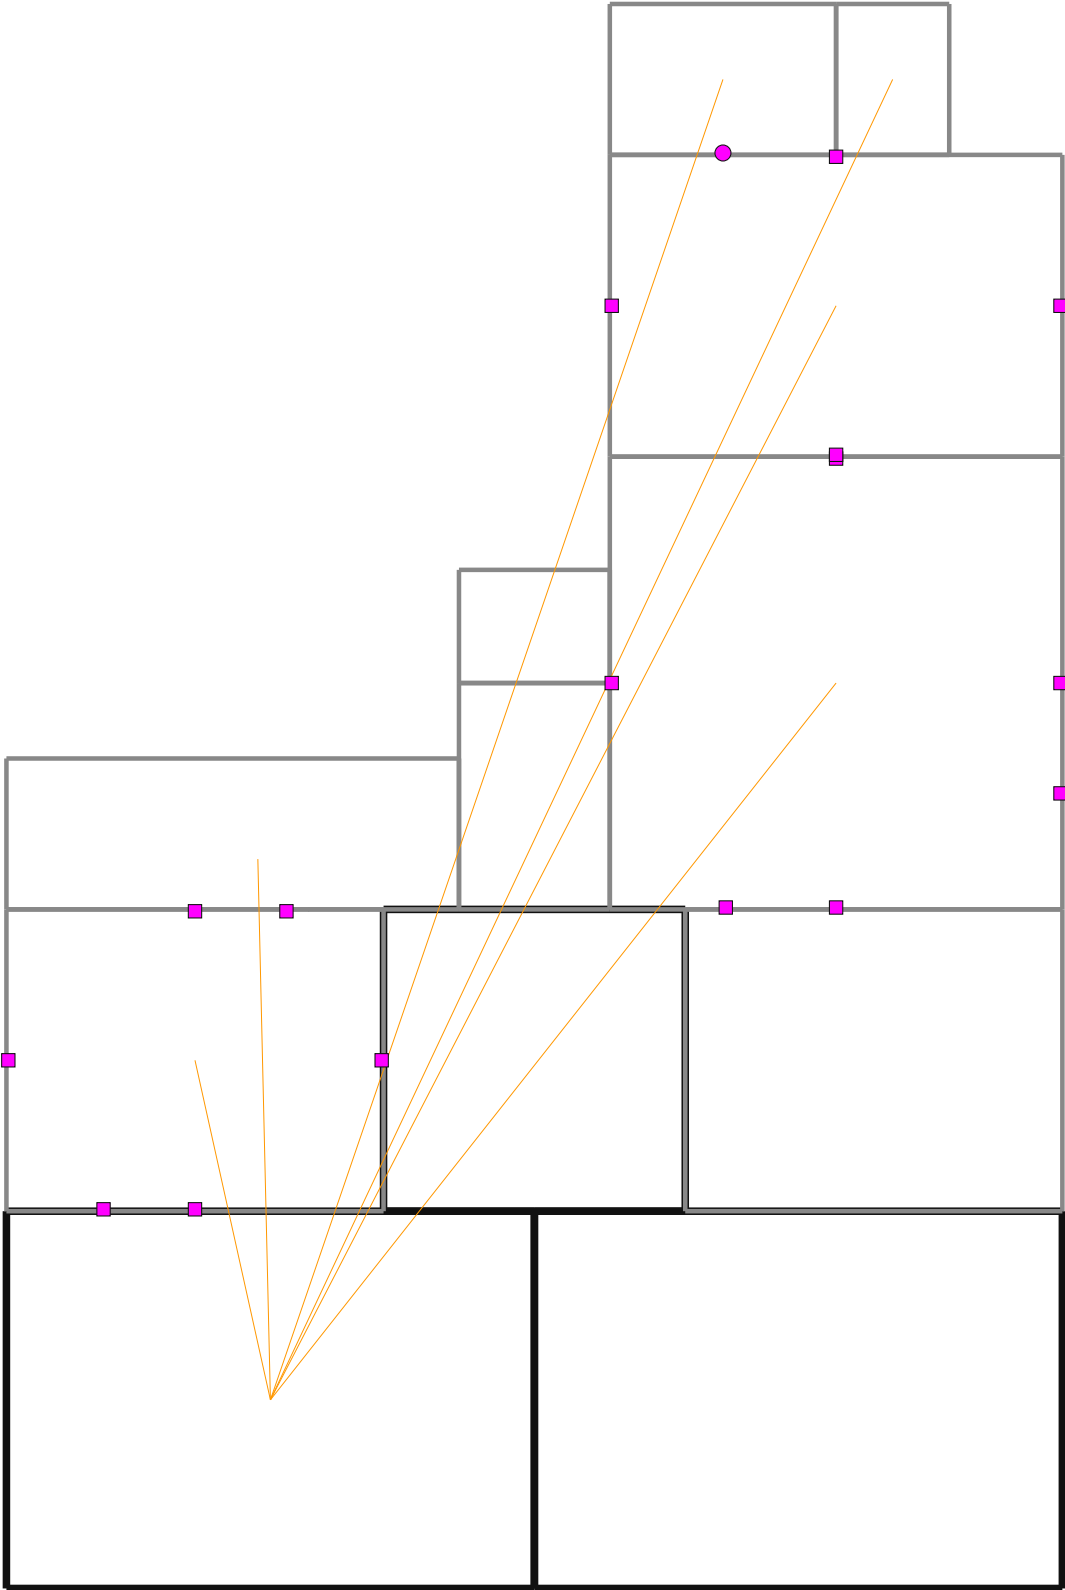

NOMENCLATURE — 510 HCU — Prises de Courant (PC)

- Prise 2P+T 16A: 16
- Prise étanche 2P+T: 1


TIJAN AI Bureau d'Études Automatisé	Résidence Papa Oumar Sakho Dakar, Sénégal	Éch: 1/100 Pl. 99/137
	510 HCU — Prises de Courant (PC) — RDC	
Date: 06/05/2026	Réf: 1711	BIM vHCU-099 Phase: APD

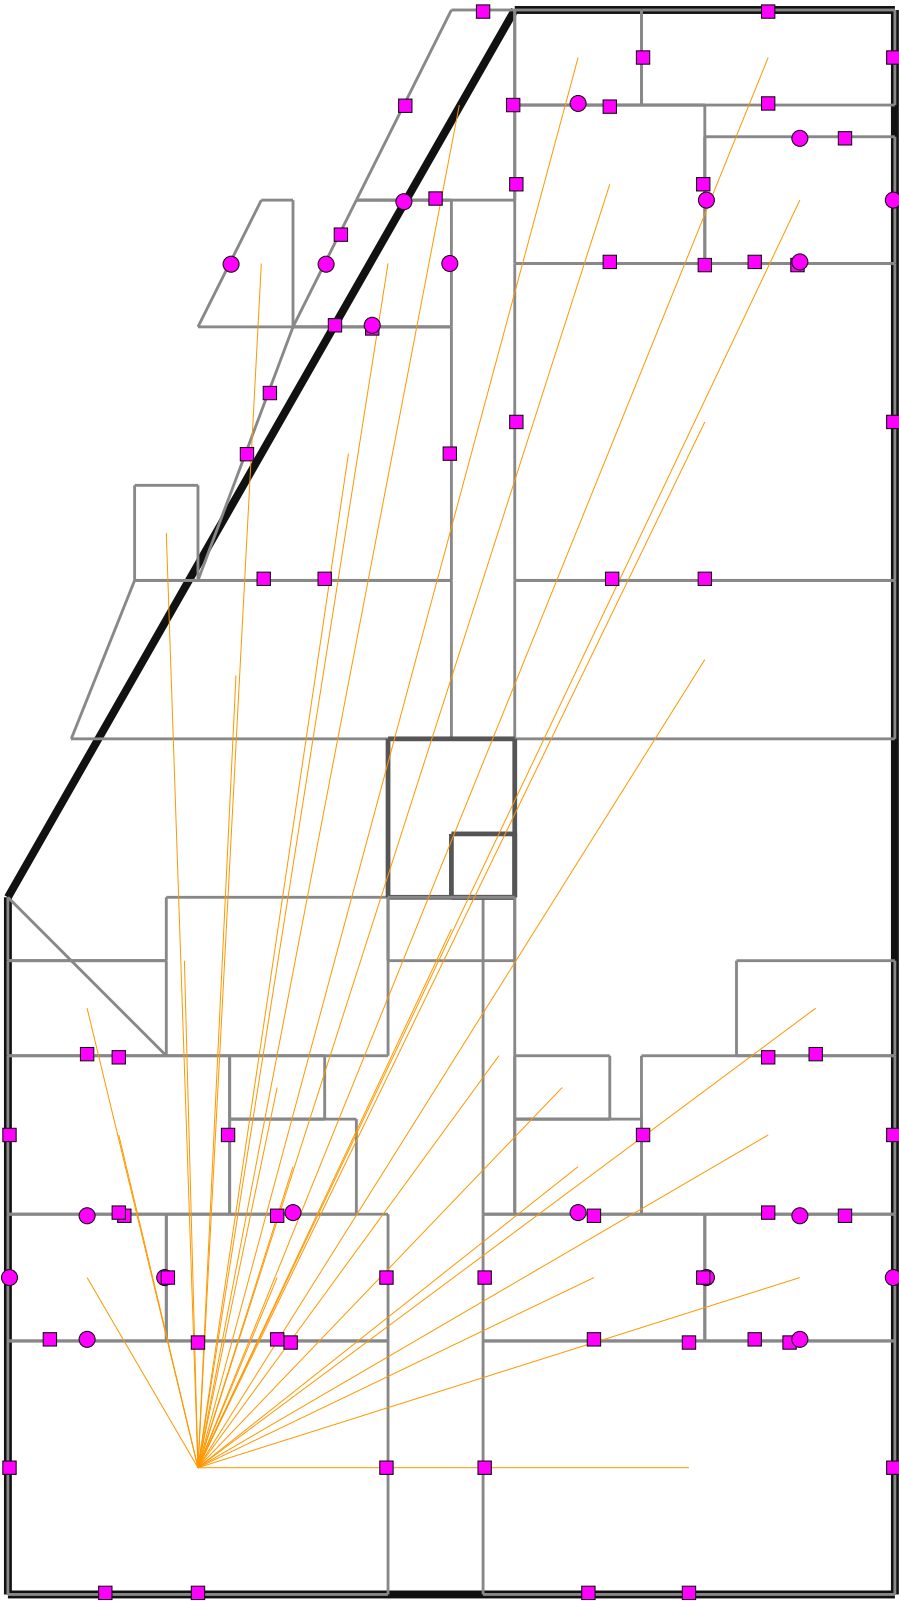

NOMENCLATURE — 510 HCU — Prises de Courant (PC)

- Prise 2P+T 16A: 62
- Prise plan de travail: 16
- Prise étanche 2P+T: 4


TIJAN AI Bureau d'Études Automatisé	Résidence Papa Oumar Sakho Dakar, Sénégal	Éch: 1/100 Pl. 100/137
	510 HCU — Prises de Courant (PC) — R+1	
Date: 06/05/2026	Réf: 1711	BIM vHCU-100 Phase: APD

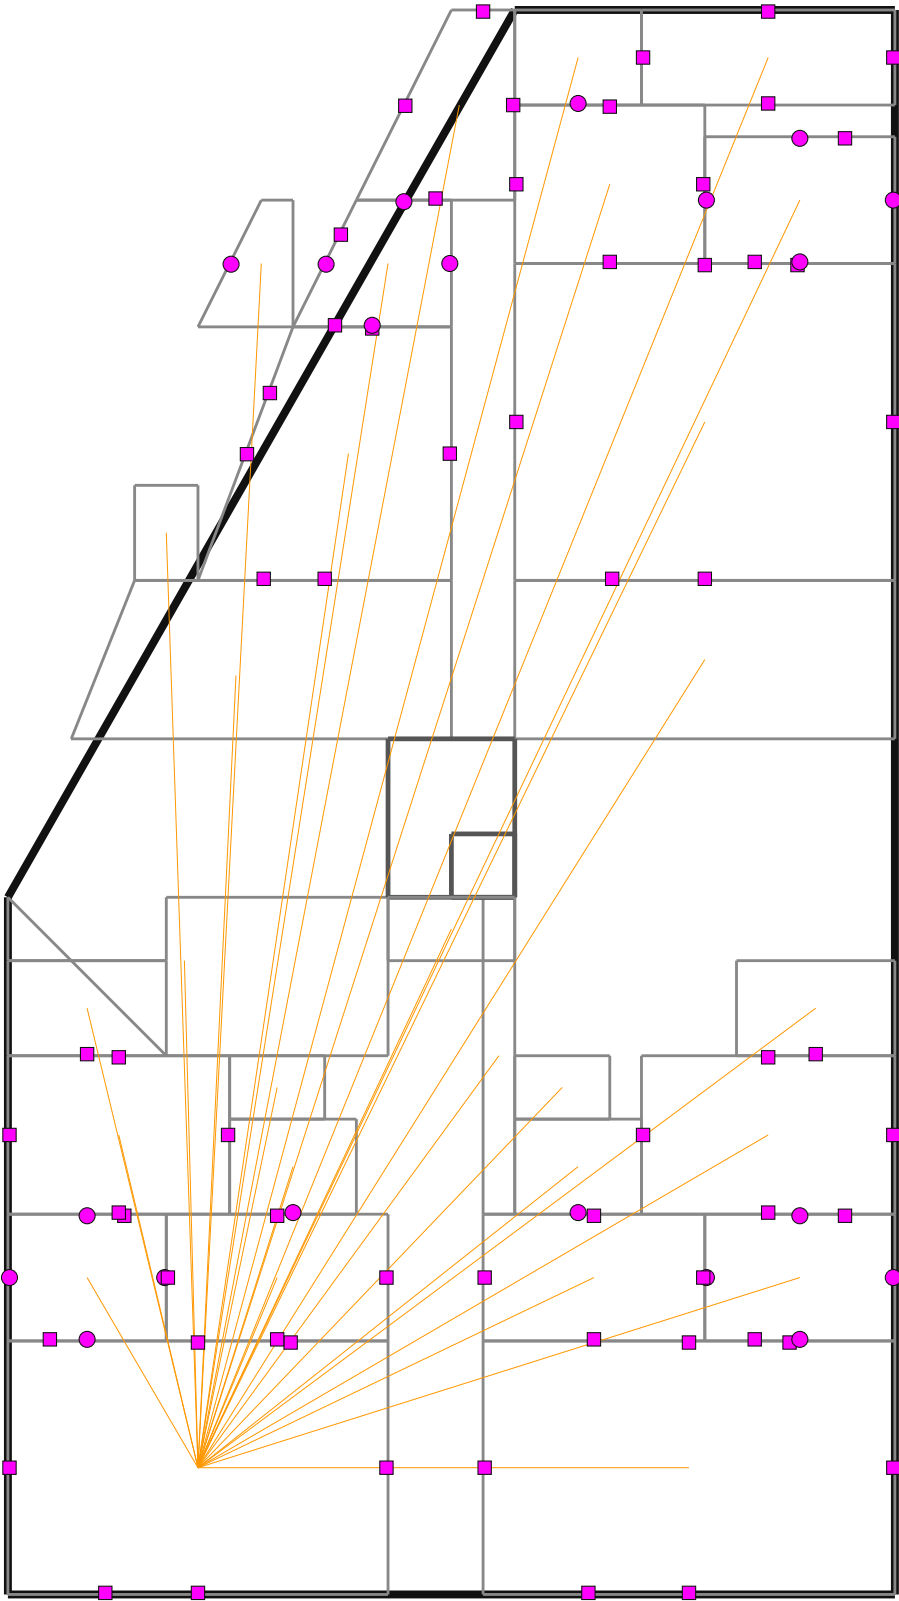

NOMENCLATURE — 510 HCU — Prises de Courant (PC)

- Prise 2P+T 16A: 62
- Prise plan de travail: 16
- Prise étanche 2P+T: 4

TIJAN AI Bureau d'Études Automatisé	Résidence Papa Oumar Sakho Dakar, Sénégal	Éch: 1/100 Pl. 101/137
	510 HCU — Prises de Courant (PC) — R+2	
Date: 06/05/2026	Réf: 1711	BIM vHCU-101 Phase: APD

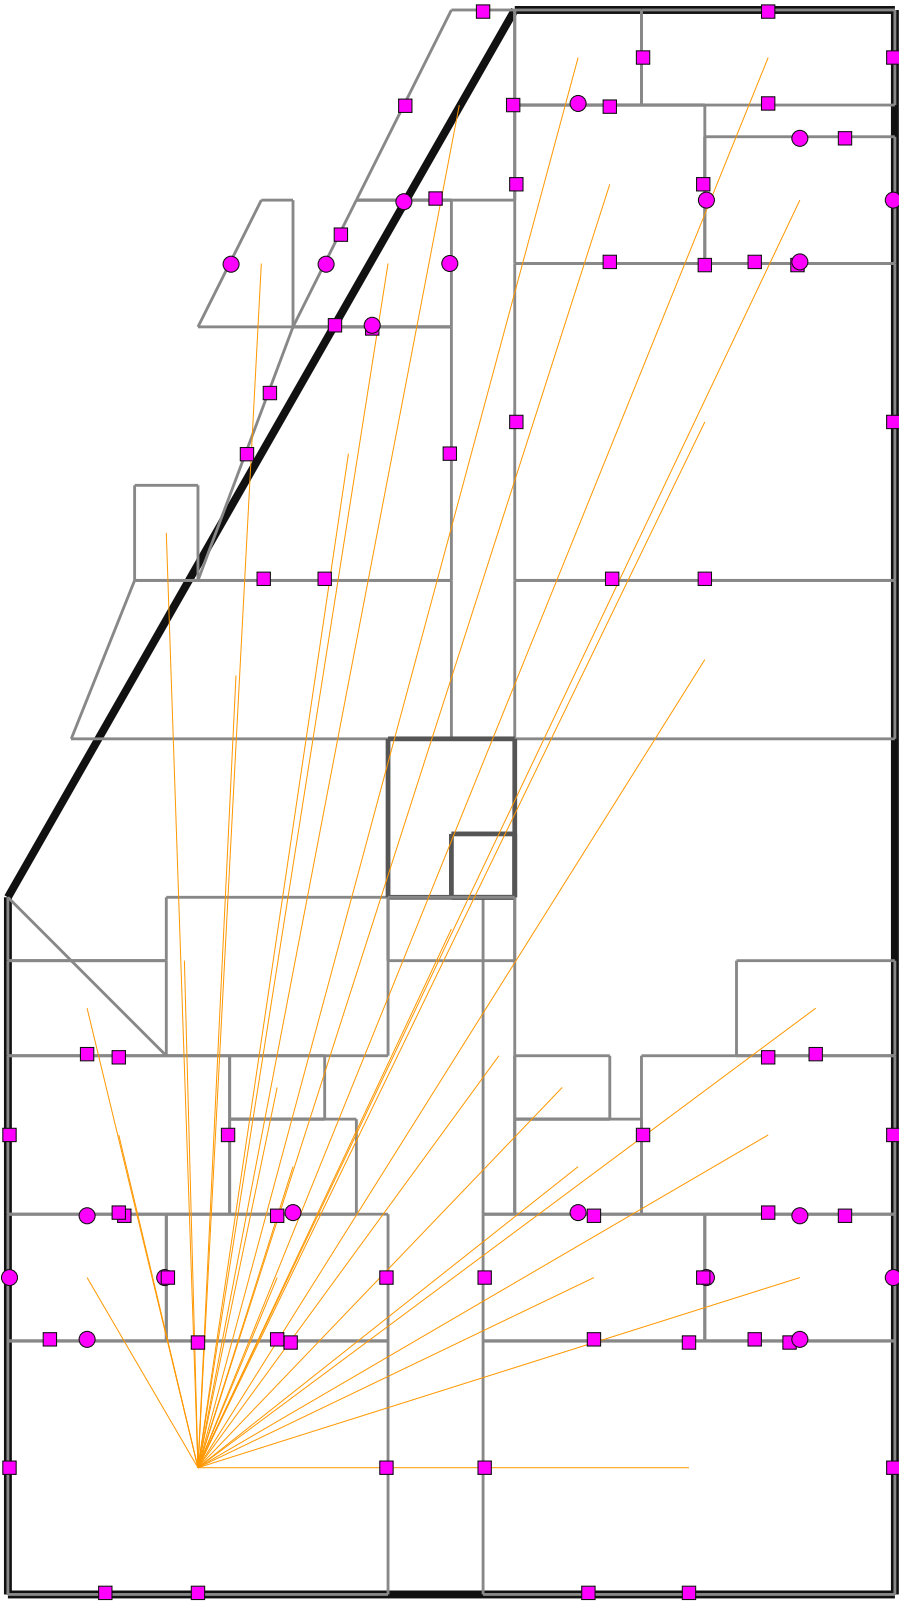

NOMENCLATURE — 510 HCU — Prises de Courant (PC)

- Prise 2P+T 16A: 62
- Prise plan de travail: 16
- Prise étanche 2P+T: 4

TIJAN AI

Bureau d'Études Automatisé

Résidence Papa Oumar Sakho

Dakar, Sénégal

Éch: 1/100

Pl. 102/137


510 HCU — Prises de Courant (PC) — R+3

Date: 06/05/2026

Réf: 1711

BIM vHCU-102


Phase: APD

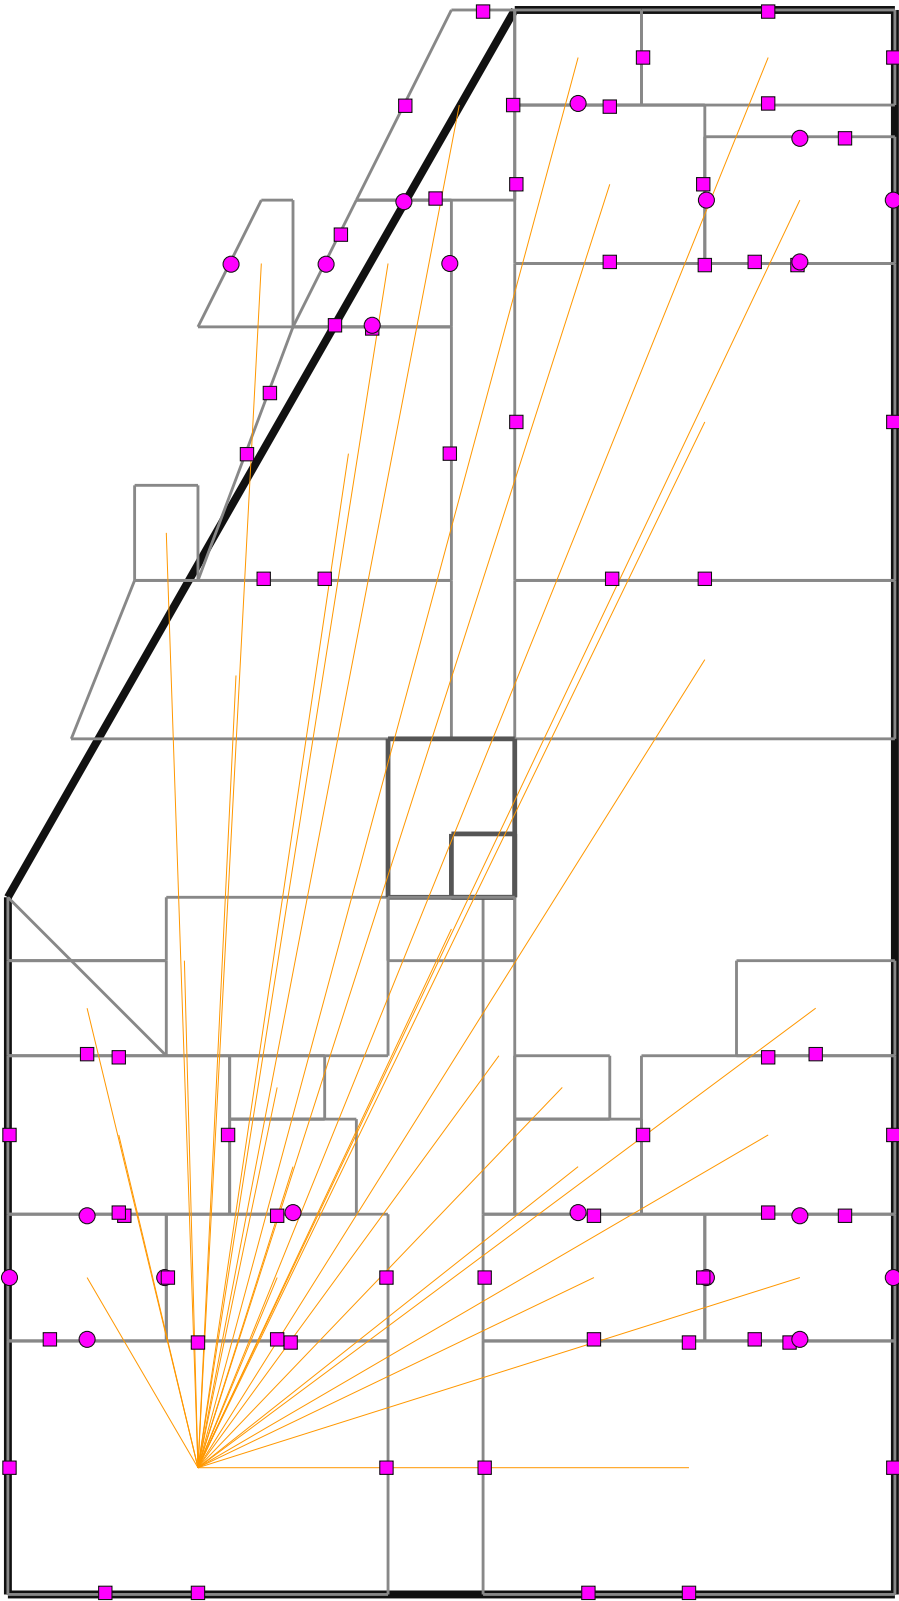

NOMENCLATURE — 510 HCU — Prises de Courant (PC)

- Prise 2P+T 16A: 62
- Prise plan de travail: 16
- Prise étanche 2P+T: 4

TIJAN AI Bureau d'Études Automatisé	Résidence Papa Oumar Sakho Dakar, Sénégal	Éch: 1/100 Pl. 103/137
	510 HCU — Prises de Courant (PC) — R+4	
Date: 06/05/2026	Réf: 1711	BIM vHCU-103 Phase: APD

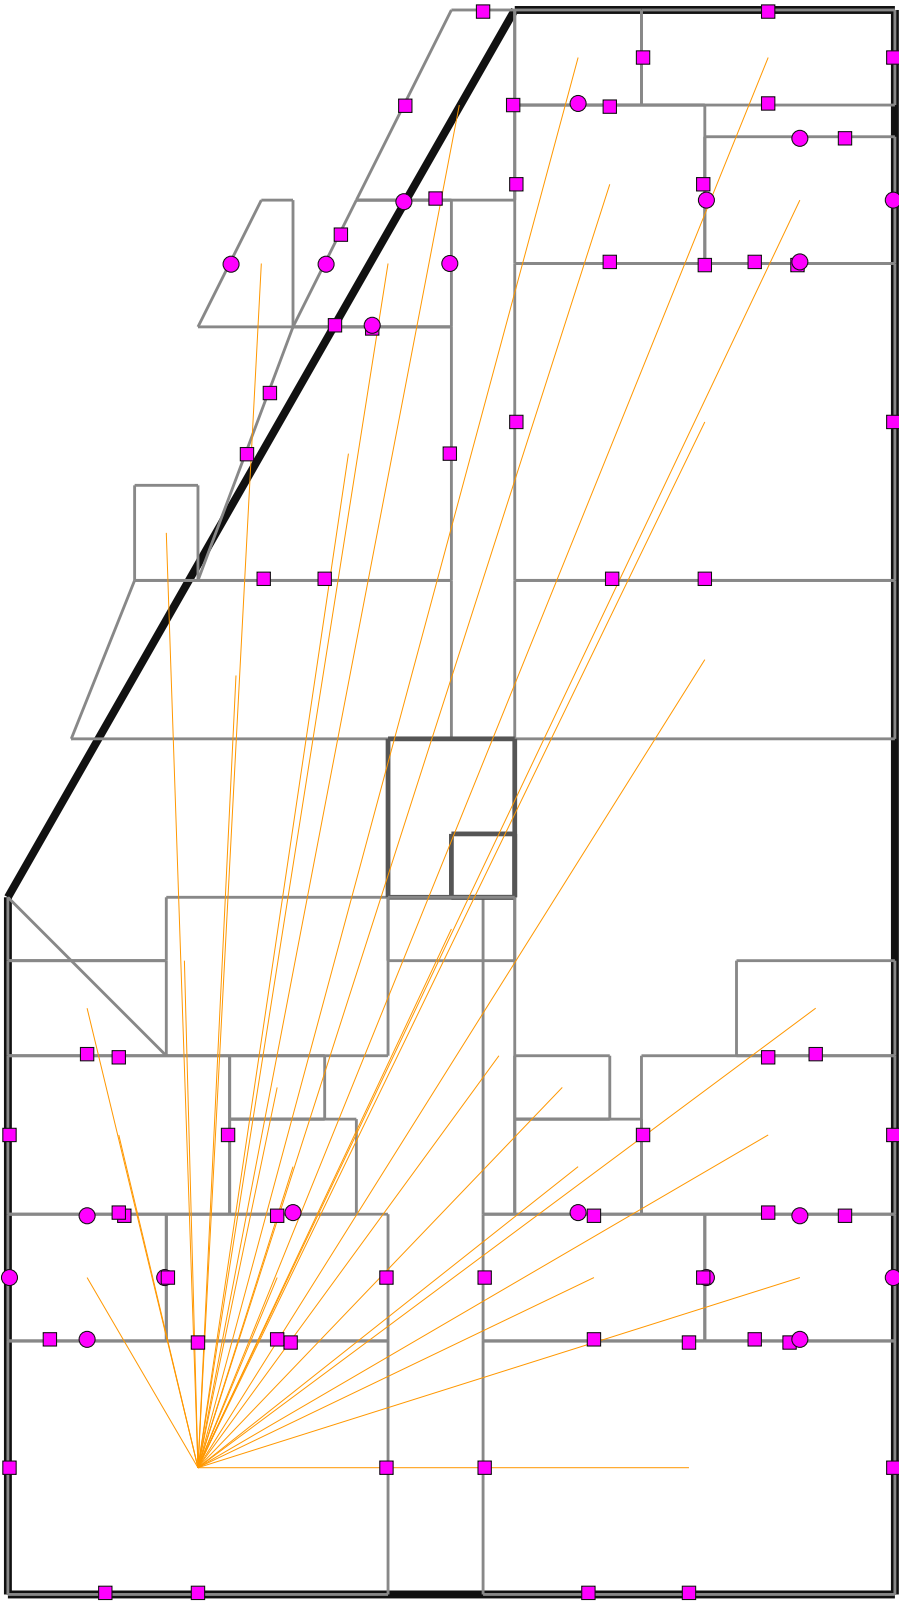

NOMENCLATURE — 510 HCU — Prises de Courant (PC)

- Prise 2P+T 16A: 62
- Prise plan de travail: 16
- Prise étanche 2P+T: 4

TIJAN AI

Bureau d'Études Automatisé

Résidence Papa Oumar Sakho

Dakar, Sénégal

Éch: 1/100

Pl. 104/137


510 HCU — Prises de Courant (PC) — R+5

Date: 06/05/2026

Réf: 1711

BIM vHCU-104


Phase: APD

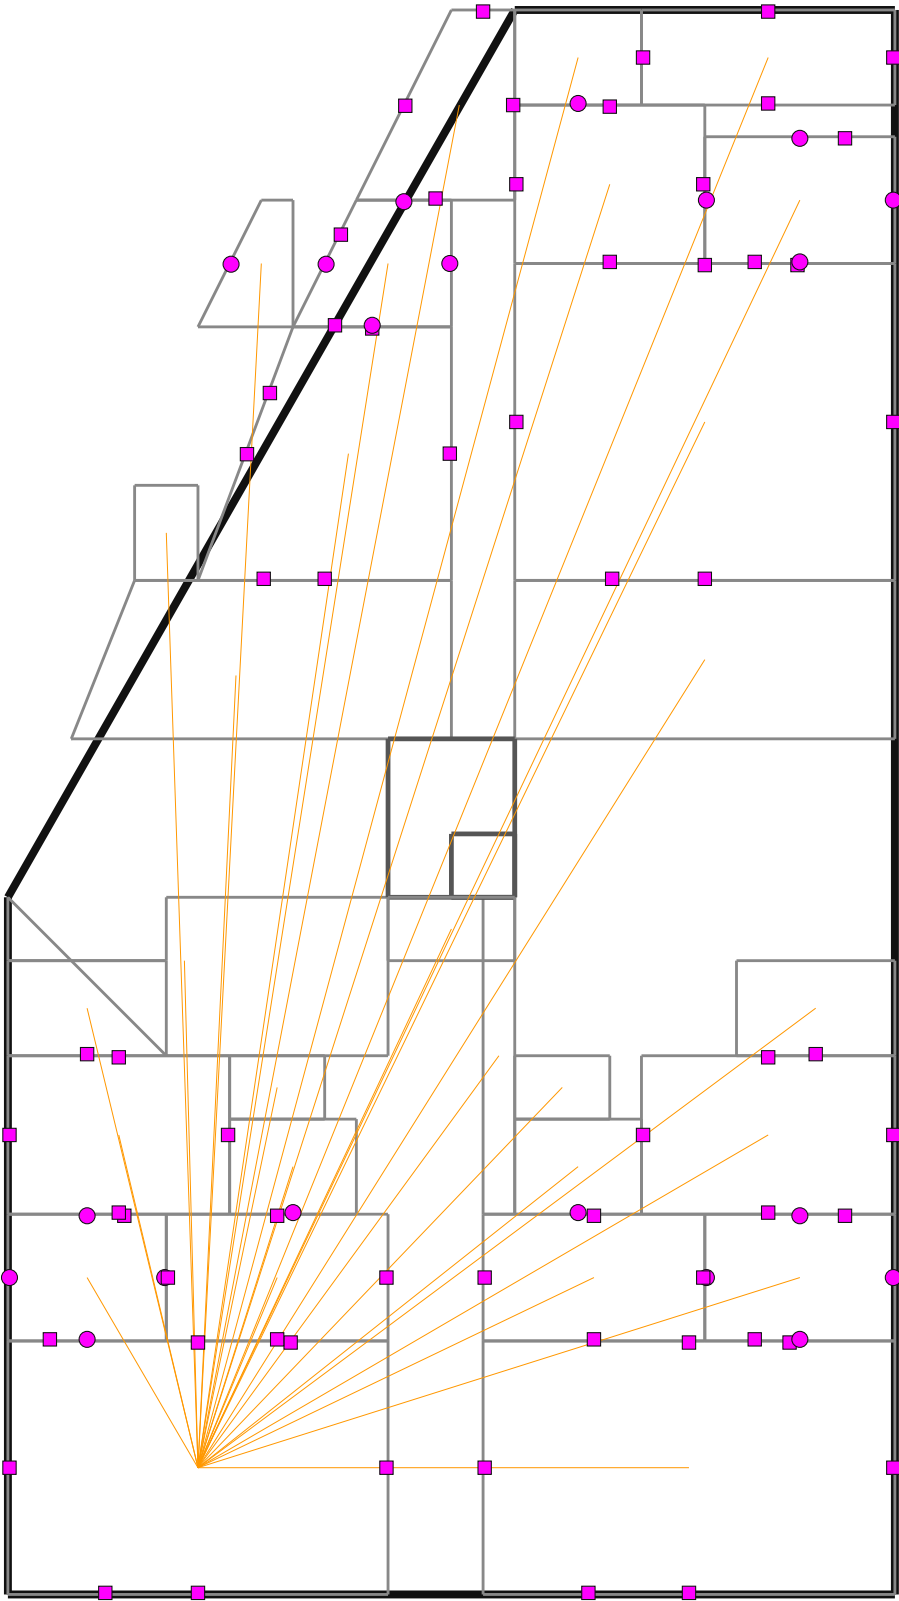

NOMENCLATURE — 510 HCU — Prises de Courant (PC)

- Prise 2P+T 16A: 62
- Prise plan de travail: 16
- Prise étanche 2P+T: 4


TIJAN AI Bureau d'Études Automatisé	Résidence Papa Oumar Sakho Dakar, Sénégal	Éch: 1/100 Pl. 105/137
	510 HCU — Prises de Courant (PC) — R+6	
Date: 06/05/2026	Réf: 1711	BIM vHCU-105 Phase: APD

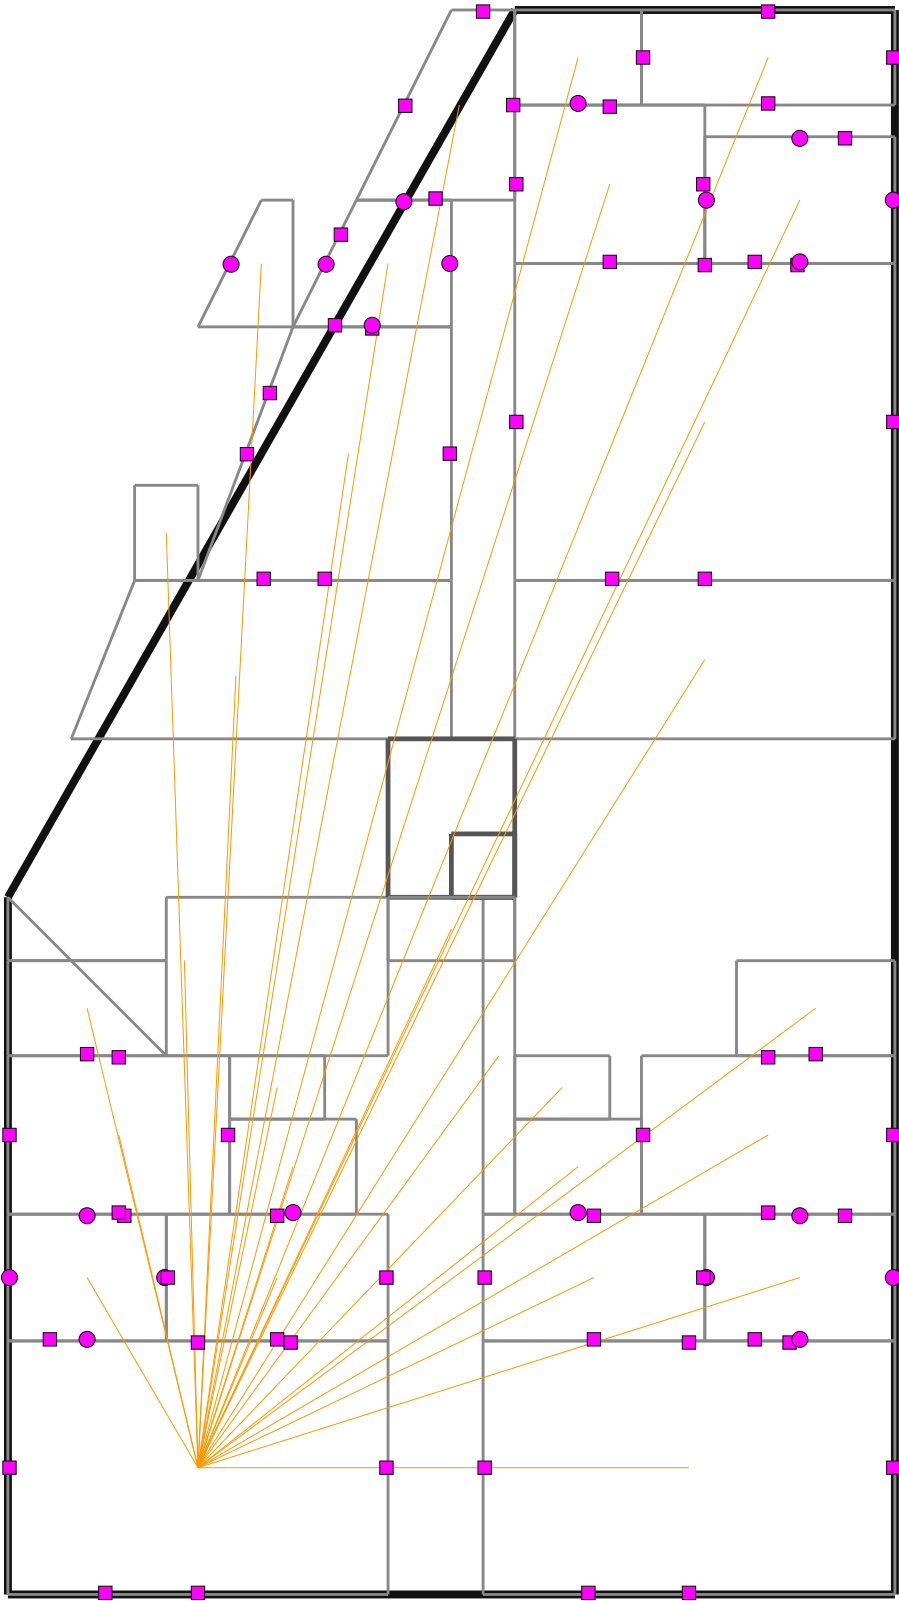

NOMENCLATURE — 510 HCU — Prises de Courant (PC)

- Prise 2P+T 16A: 62
- Prise plan de travail: 16
- Prise étanche 2P+T: 4


TIJAN AI Bureau d'Études Automatisé	Résidence Papa Oumar Sakho Dakar, Sénégal	Éch: 1/100 Pl. 106/137
	510 HCU — Prises de Courant (PC) — R+7	
Date: 06/05/2026	Réf: 1711	BIM vHCU-106 Phase: APD

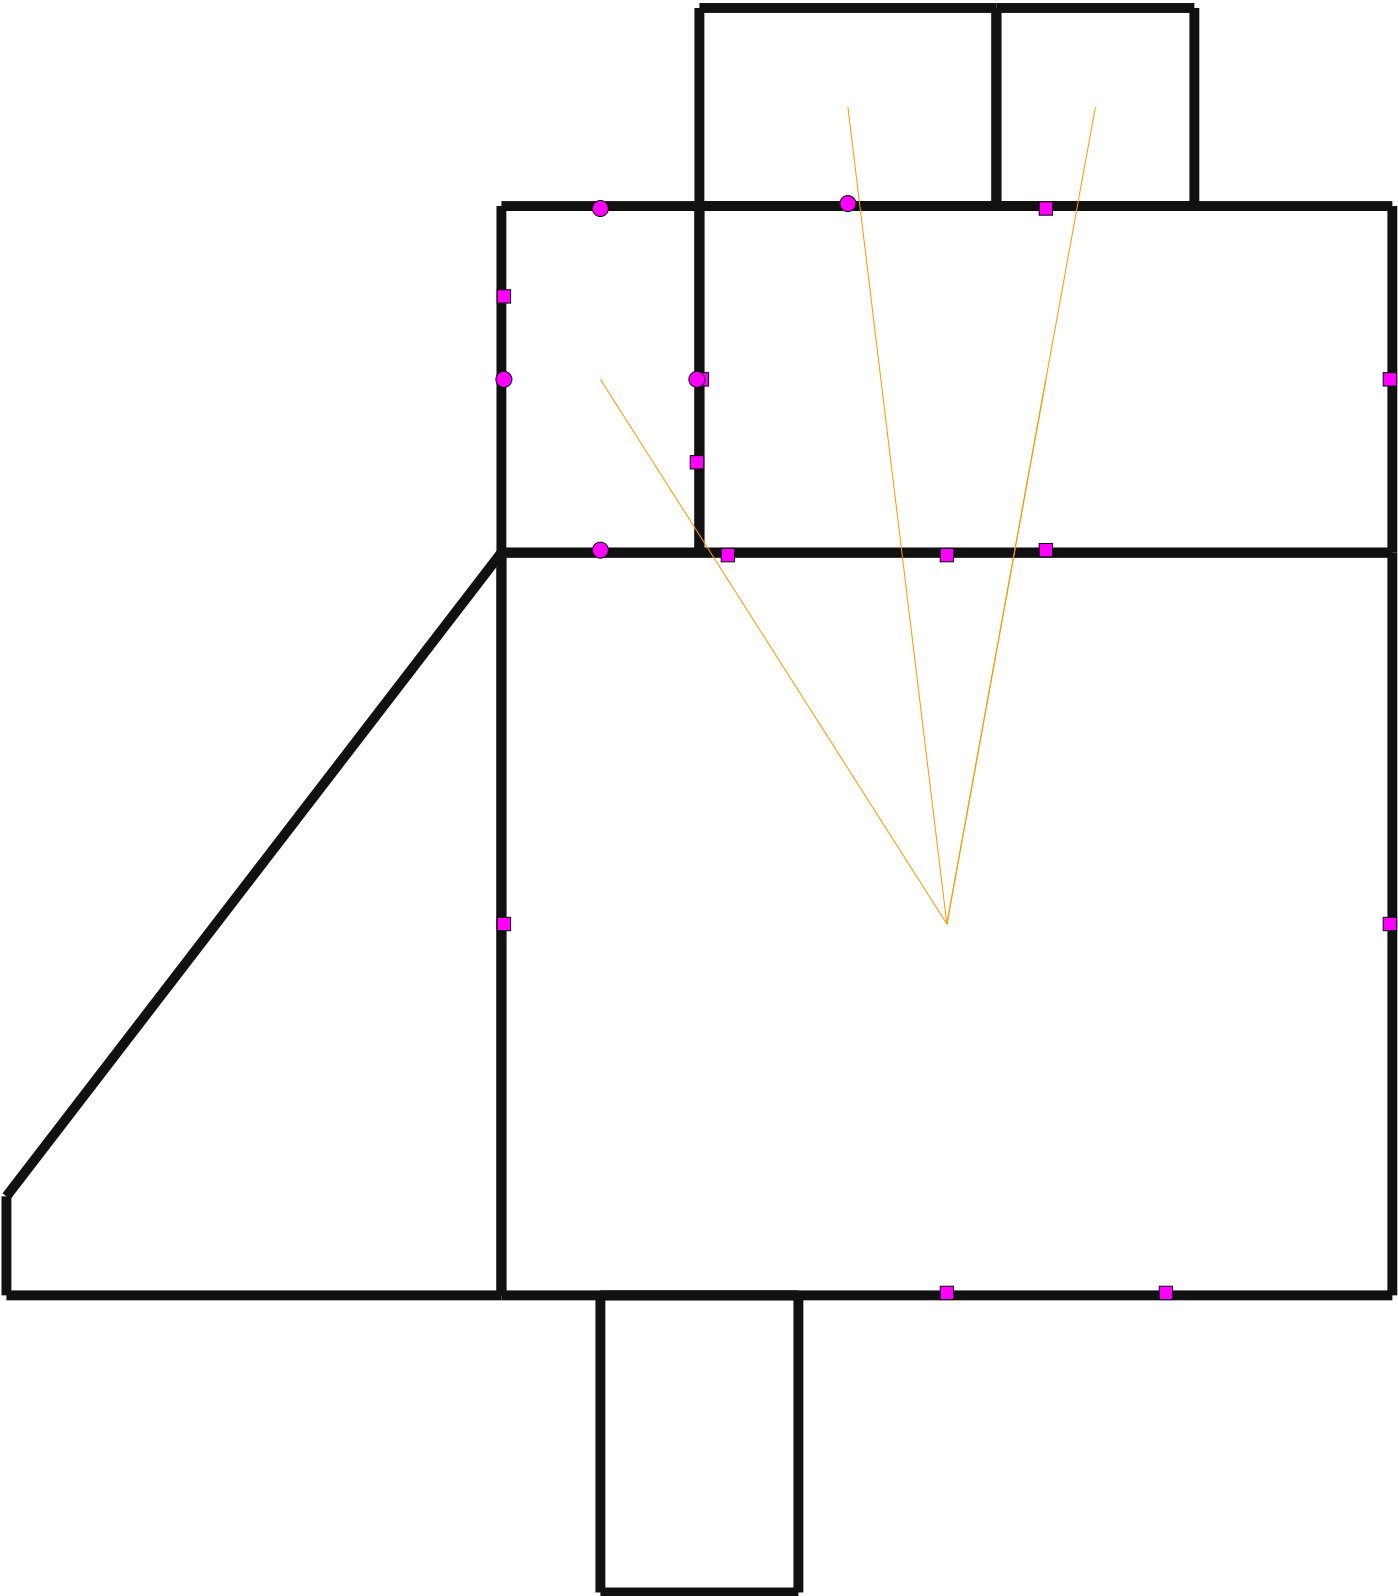

NOMENCLATURE — 510 HCU — Prises de Courant (PC)

- Prise 2P+T 16A: 12
- Prise plan de travail: 4
- Prise étanche 2P+T: 1

TIJAN AI Bureau d'Études Automatisé	Résidence Papa Oumar Sakho Dakar, Sénégal	Éch: 1/100 Pl. 107/137
	510 HCU — Prises de Courant (PC) — R+8	
Date: 06/05/2026	Réf: 1711	BIM vHCU-107 Phase: APD

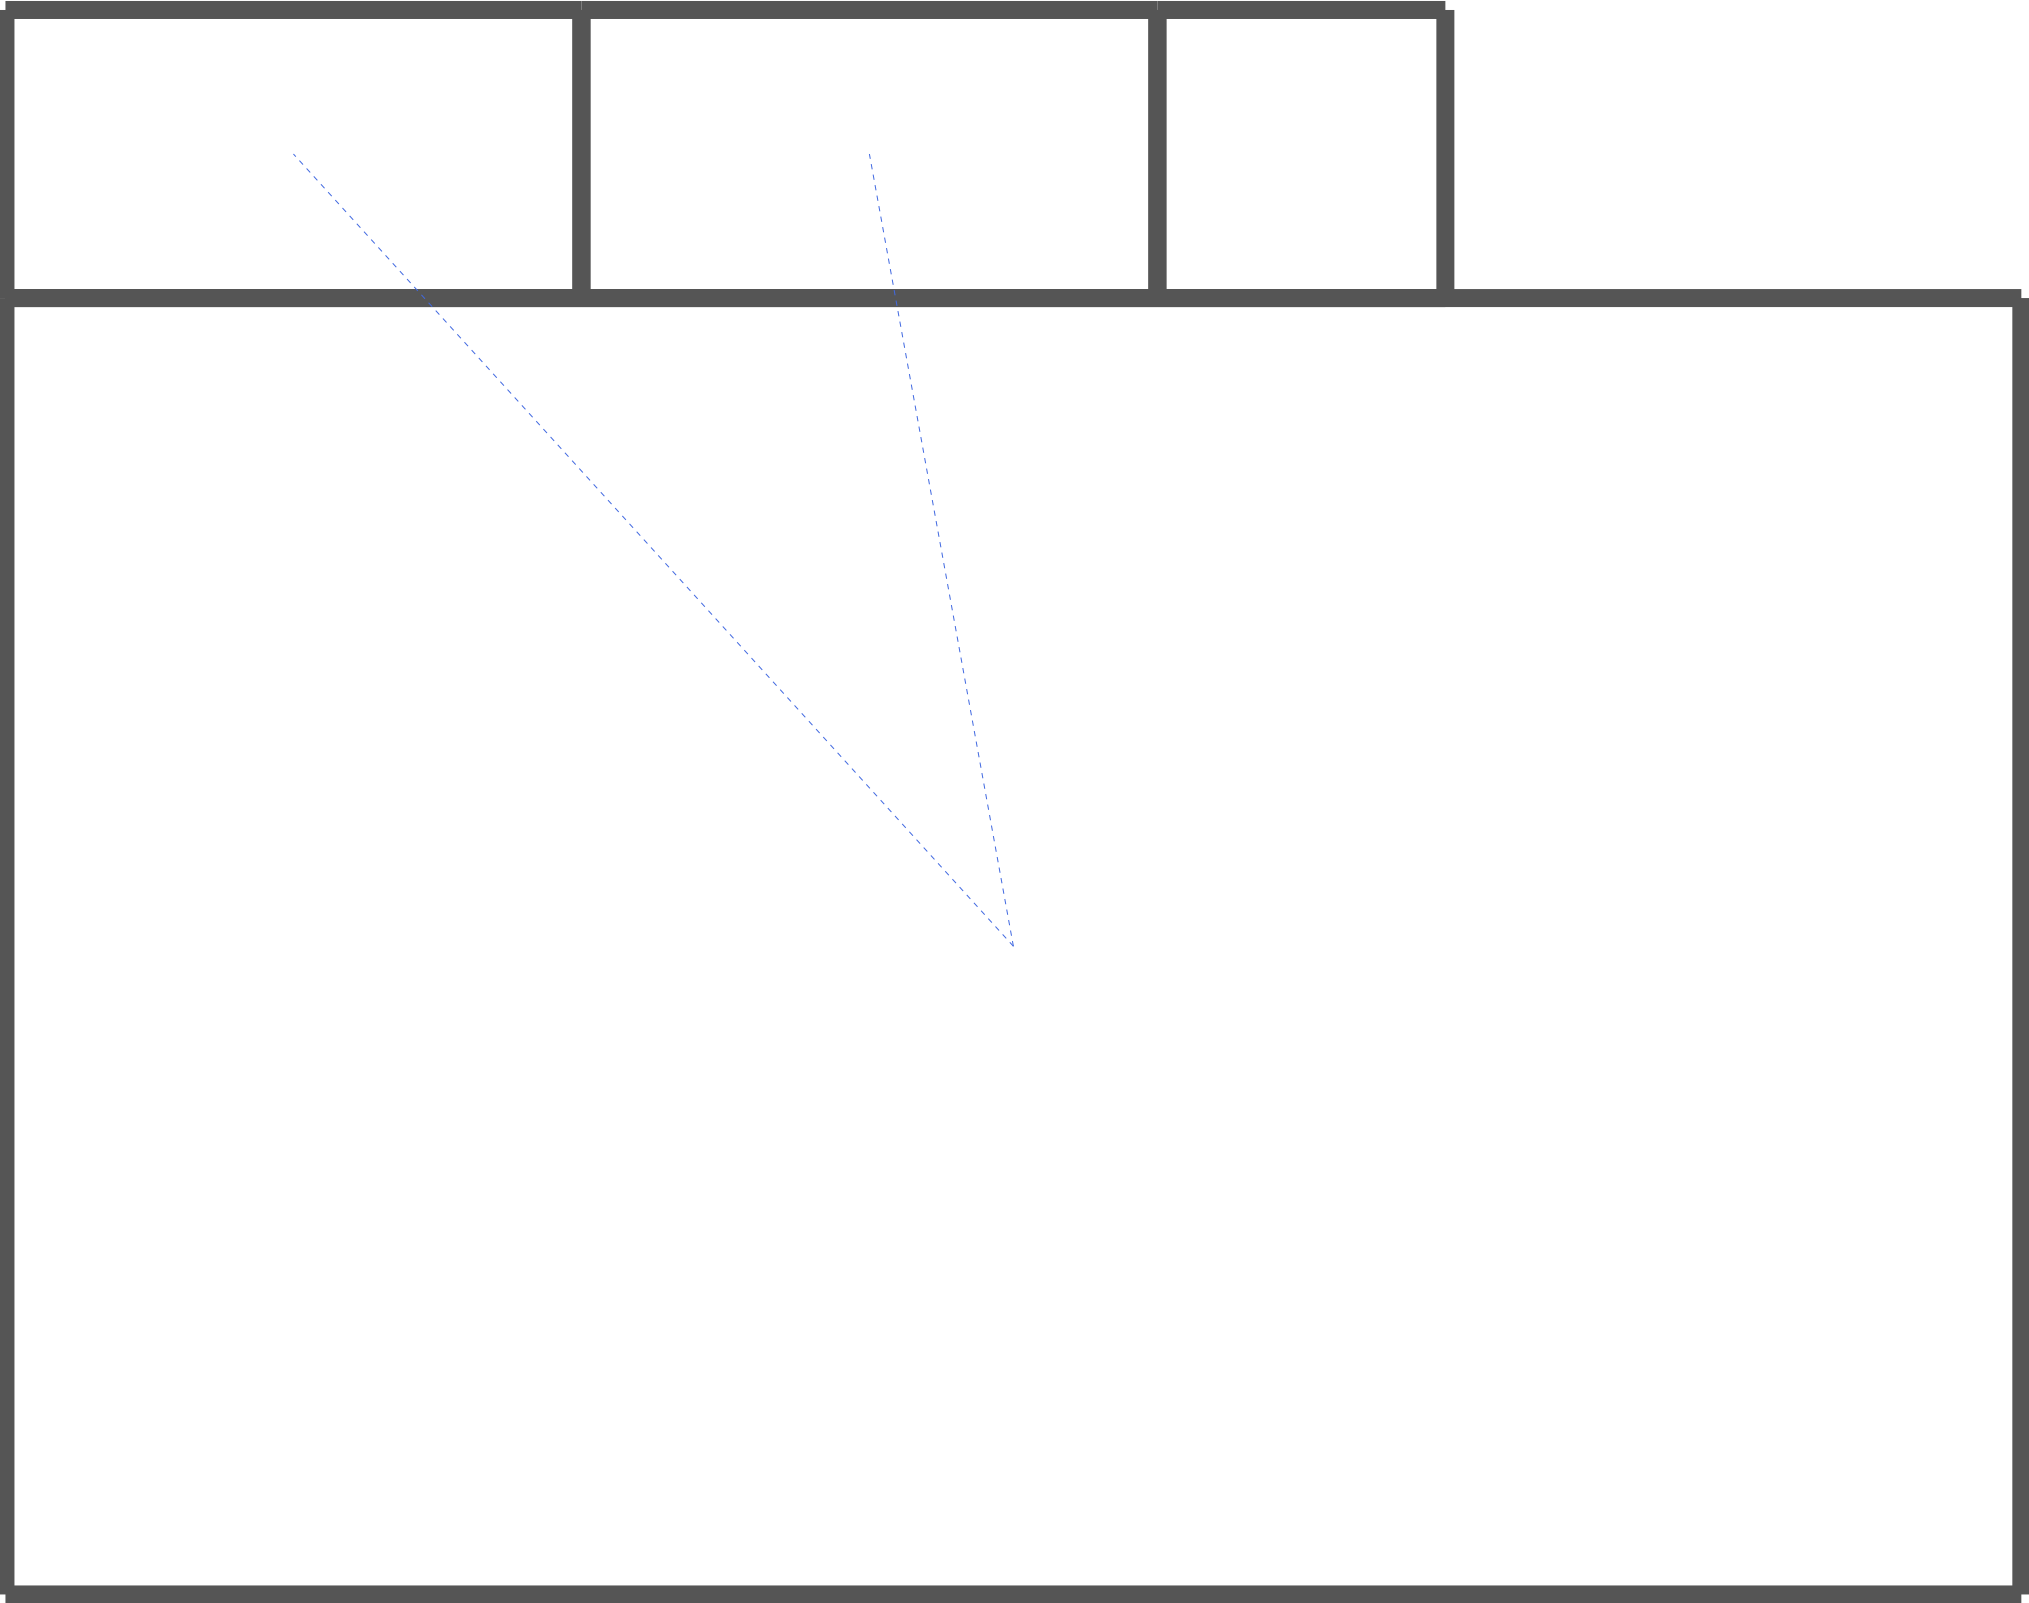

TIJAN AI

Bureau d'Études Automatisé

Résidence Papa Oumar Sakho

Dakar, Sénégal

Éch: 1/100

Pl. 108/137


520 LCU — Courants Faibles — Sous-Sol

Date: 06/05/2026

Réf: 1711

BIM v.LCU-108


Phase: APD

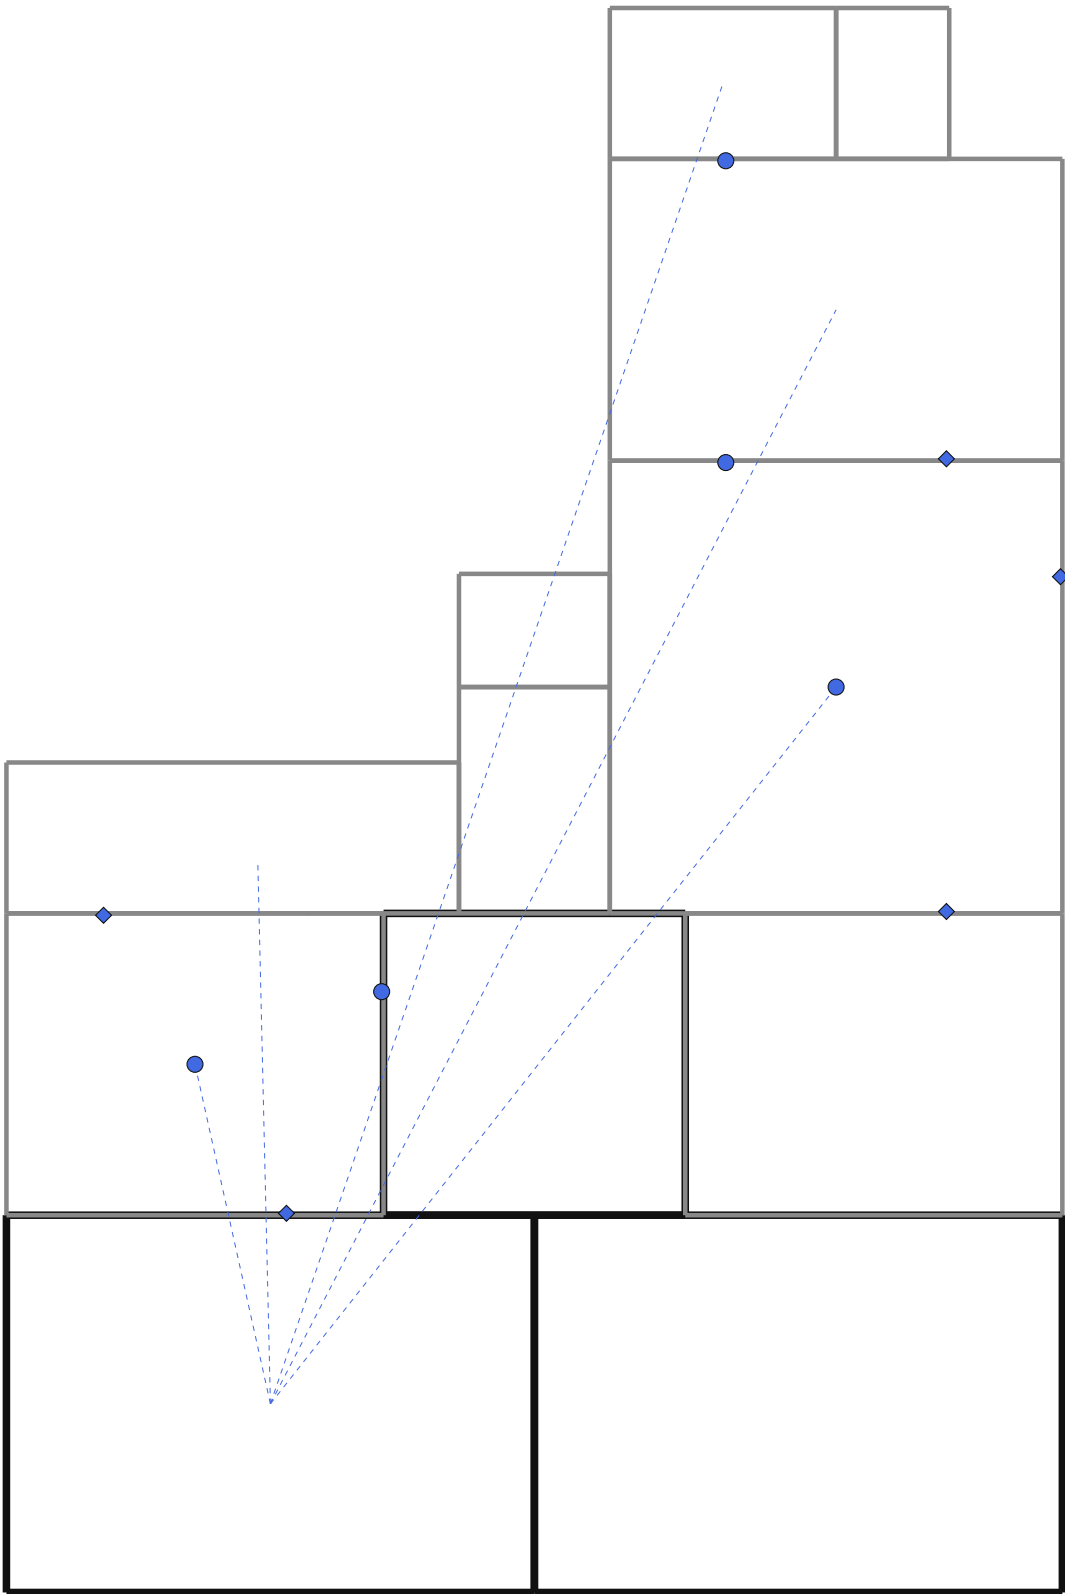

NOMENCLATURE — 520 LCU — Courants Faibles

- Prise RJ45: 5
- Prise TV: 3
- Point d'accès WiFi: 2


TIJAN AI Bureau d'Études Automatisé	Résidence Papa Oumar Sakho Dakar, Sénégal	Éch: 1/100 Pl. 109/137
	520 LCU — Courants Faibles — RDC	
Date: 06/05/2026	Réf: 1711	BIM v.LCU-109 Phase: APD

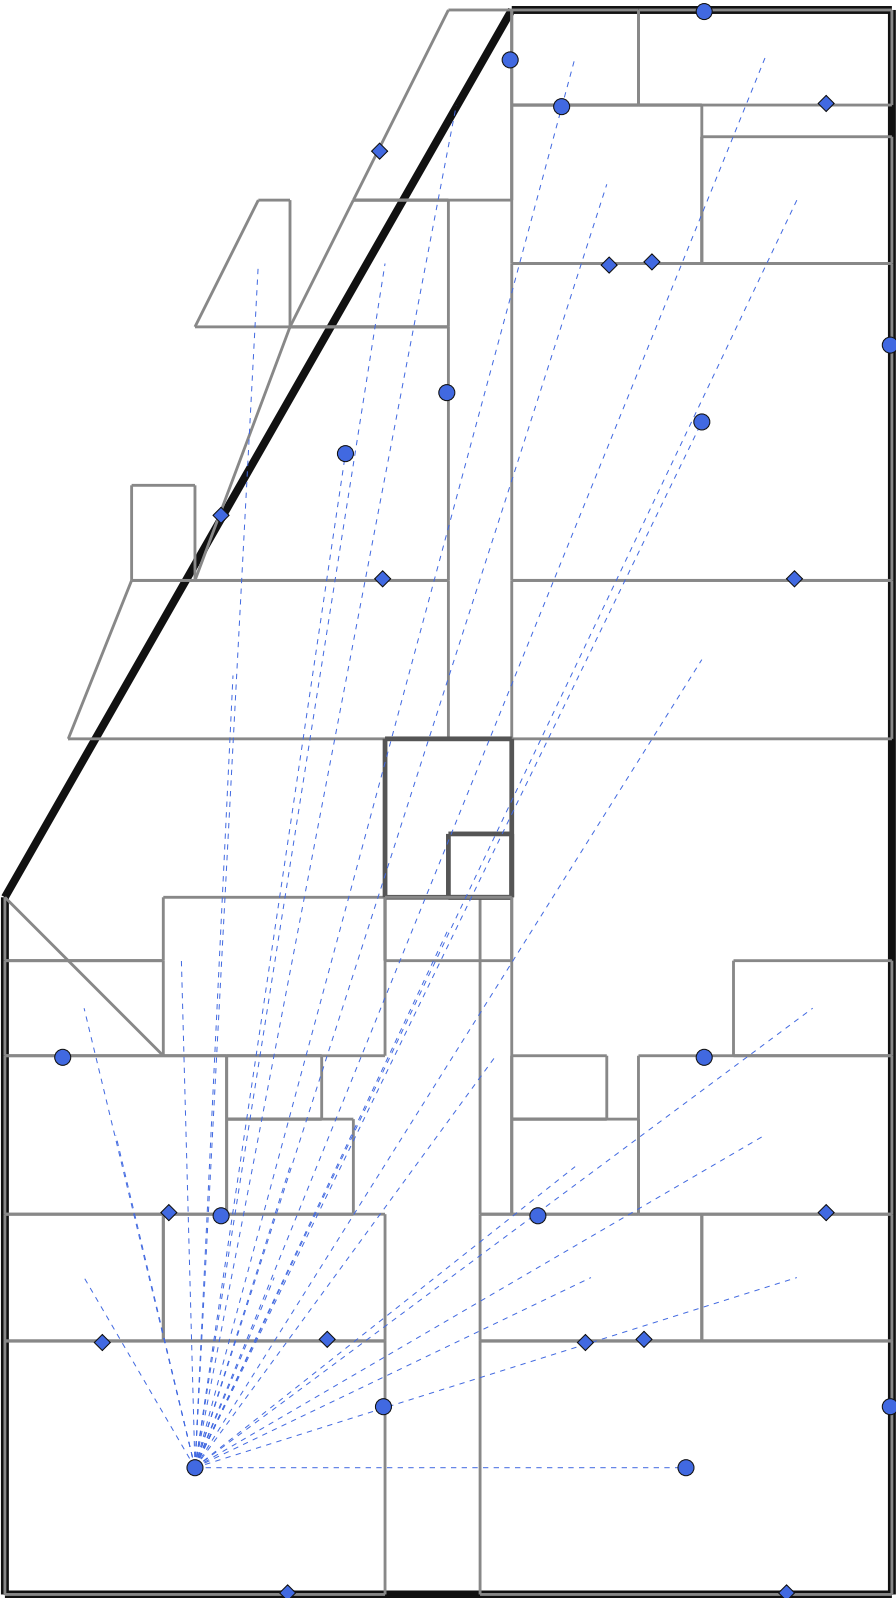

NOMENCLATURE — 520 LCU — Courants Faibles

- Prise RJ45: 15
- Prise TV: 11
- Point d'accès WiFi: 4


TIJAN AI Bureau d'Études Automatisé	Résidence Papa Oumar Sakho Dakar, Sénégal	Éch: 1/100 Pl. 110/137
	520 LCU — Courants Faibles — R+1	
Date: 06/05/2026	Réf: 1711	BIM vLCU-110 Phase: APD

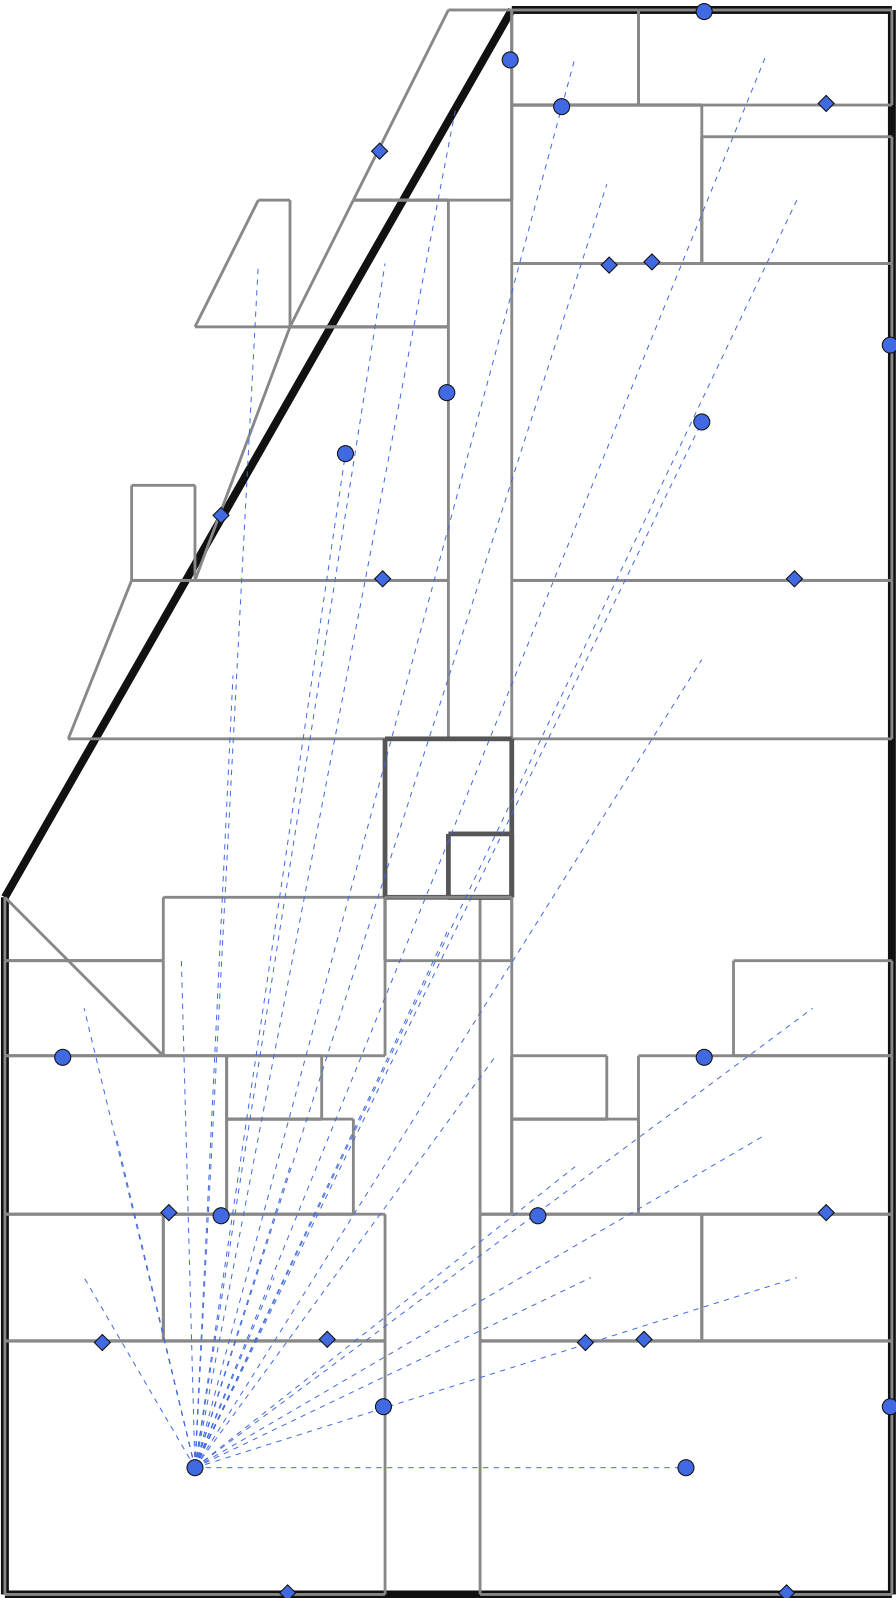

NOMENCLATURE — 520 LCU — Courants Faibles

- Prise RJ45: 15
- Prise TV: 11
- Point d'accès WiFi: 4


TIJAN AI Bureau d'Études Automatisé	Résidence Papa Oumar Sakho Dakar, Sénégal	Éch: 1/100 Pl. 111/137
	520 LCU — Courants Faibles — R+2	
Date: 06/05/2026	Réf: 1711	BIM vLCU-111 Phase: APD

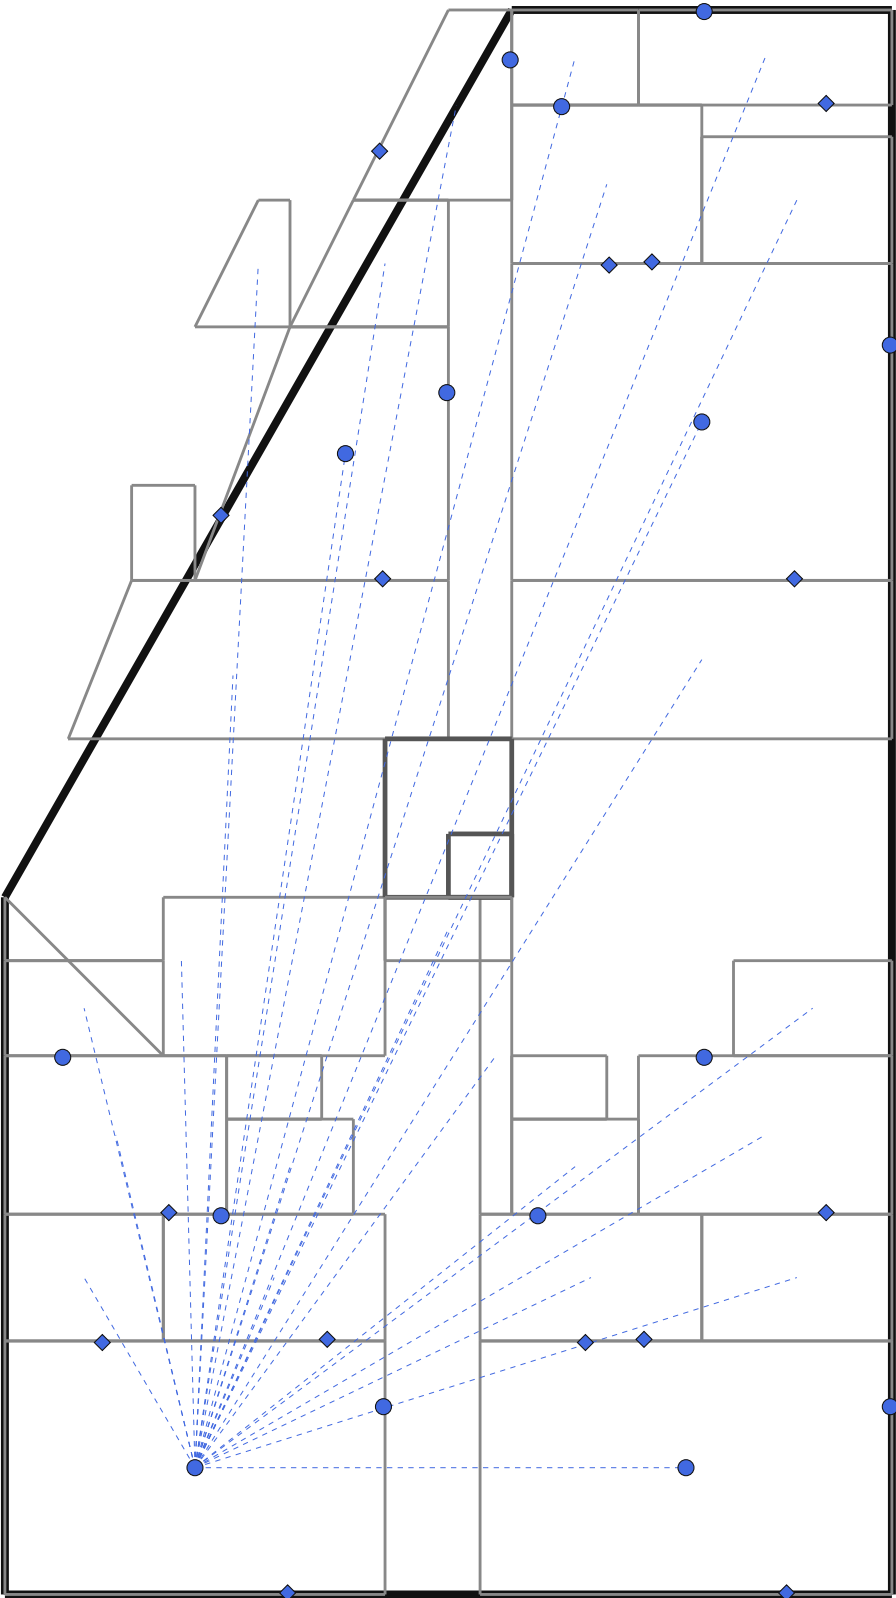

NOMENCLATURE — 520 LCU — Courants Faibles

- Prise RJ45: 15
- Prise TV: 11
- Point d'accès WiFi: 4


TIJAN AI Bureau d'Études Automatisé	Résidence Papa Oumar Sakho Dakar, Sénégal	Éch: 1/100 Pl. 112/137
	520 LCU — Courants Faibles — R+3	
Date: 06/05/2026	Réf: 1711	BIM vLCU-112 Phase: APD

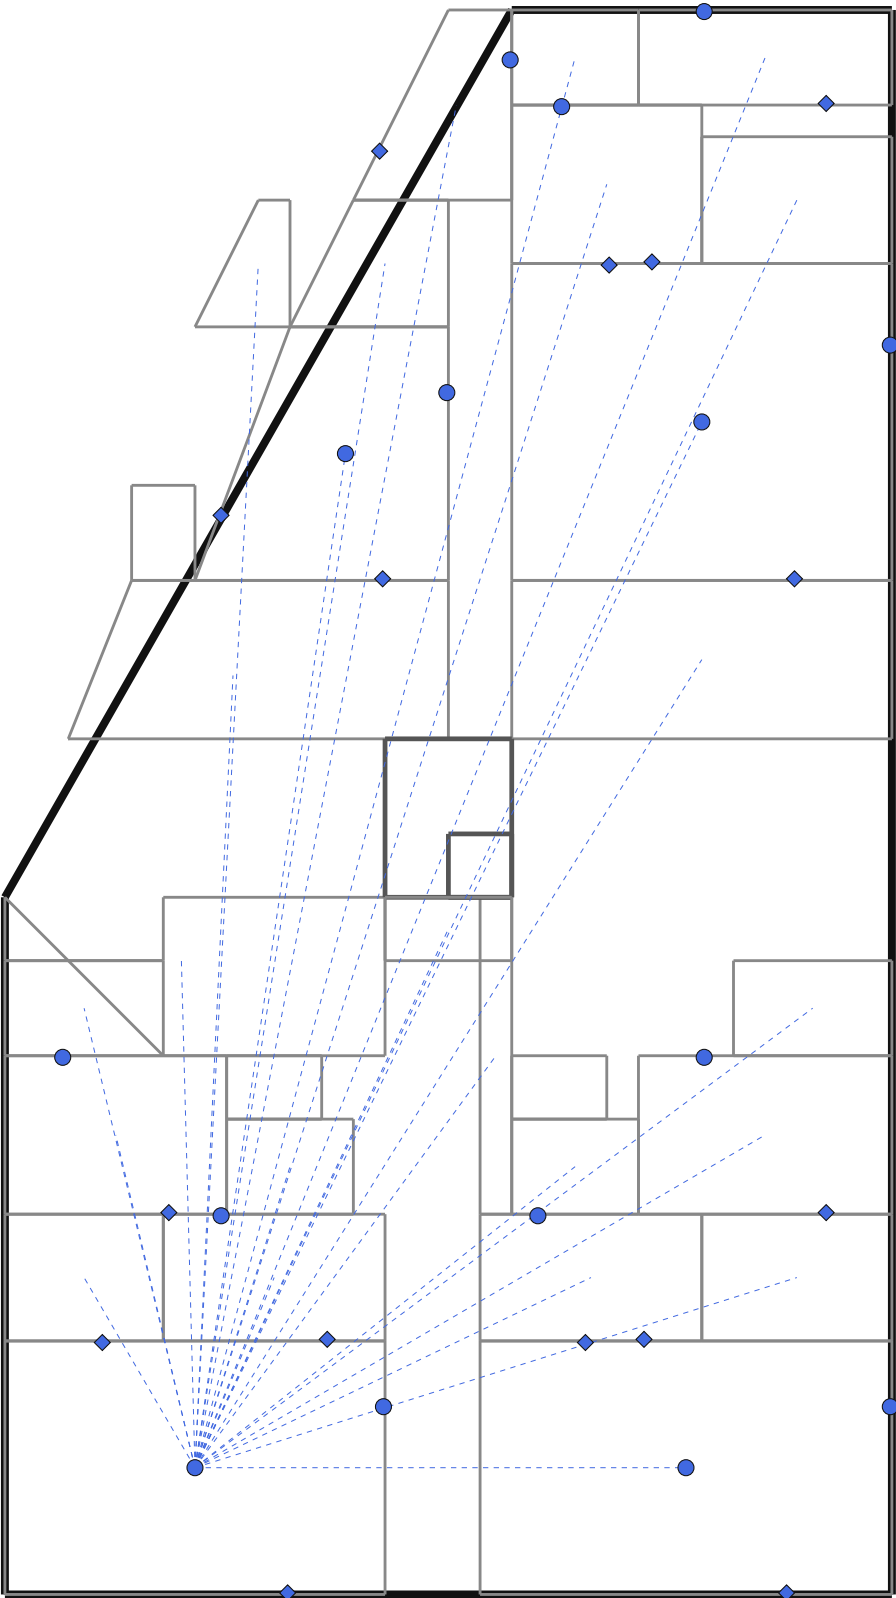

NOMENCLATURE — 520 LCU — Courants Faibles

- Prise RJ45: 15
- Prise TV: 11
- Point d'accès WiFi: 4


TIJAN AI Bureau d'Études Automatisé	Résidence Papa Oumar Sakho Dakar, Sénégal	Éch: 1/100 Pl. 113/137
	520 LCU — Courants Faibles — R+4	
Date: 06/05/2026	Réf: 1711	BIM vLCU-113 Phase: APD

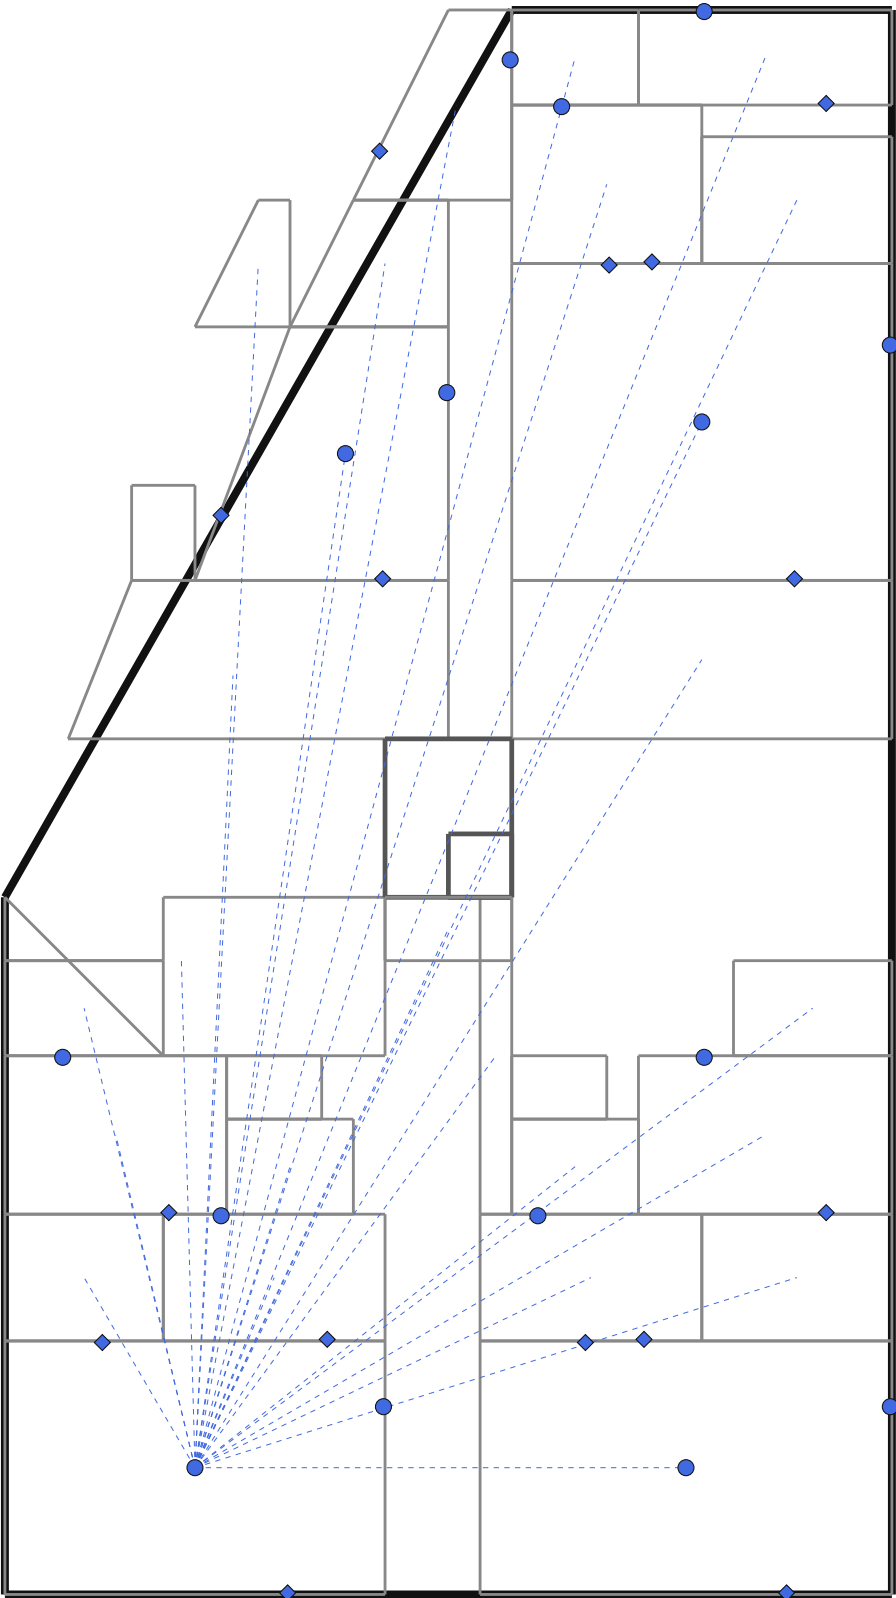

NOMENCLATURE — 520 LCU — Courants Faibles

- Prise RJ45: 15
- Prise TV: 11
- Point d'accès WiFi: 4


TIJAN AI Bureau d'Études Automatisé	Résidence Papa Oumar Sakho Dakar, Sénégal	Éch: 1/100 Pl. 114/137
	520 LCU — Courants Faibles — R+5	
Date: 06/05/2026	Réf: 1711	BIM vLCU-114 Phase: APD

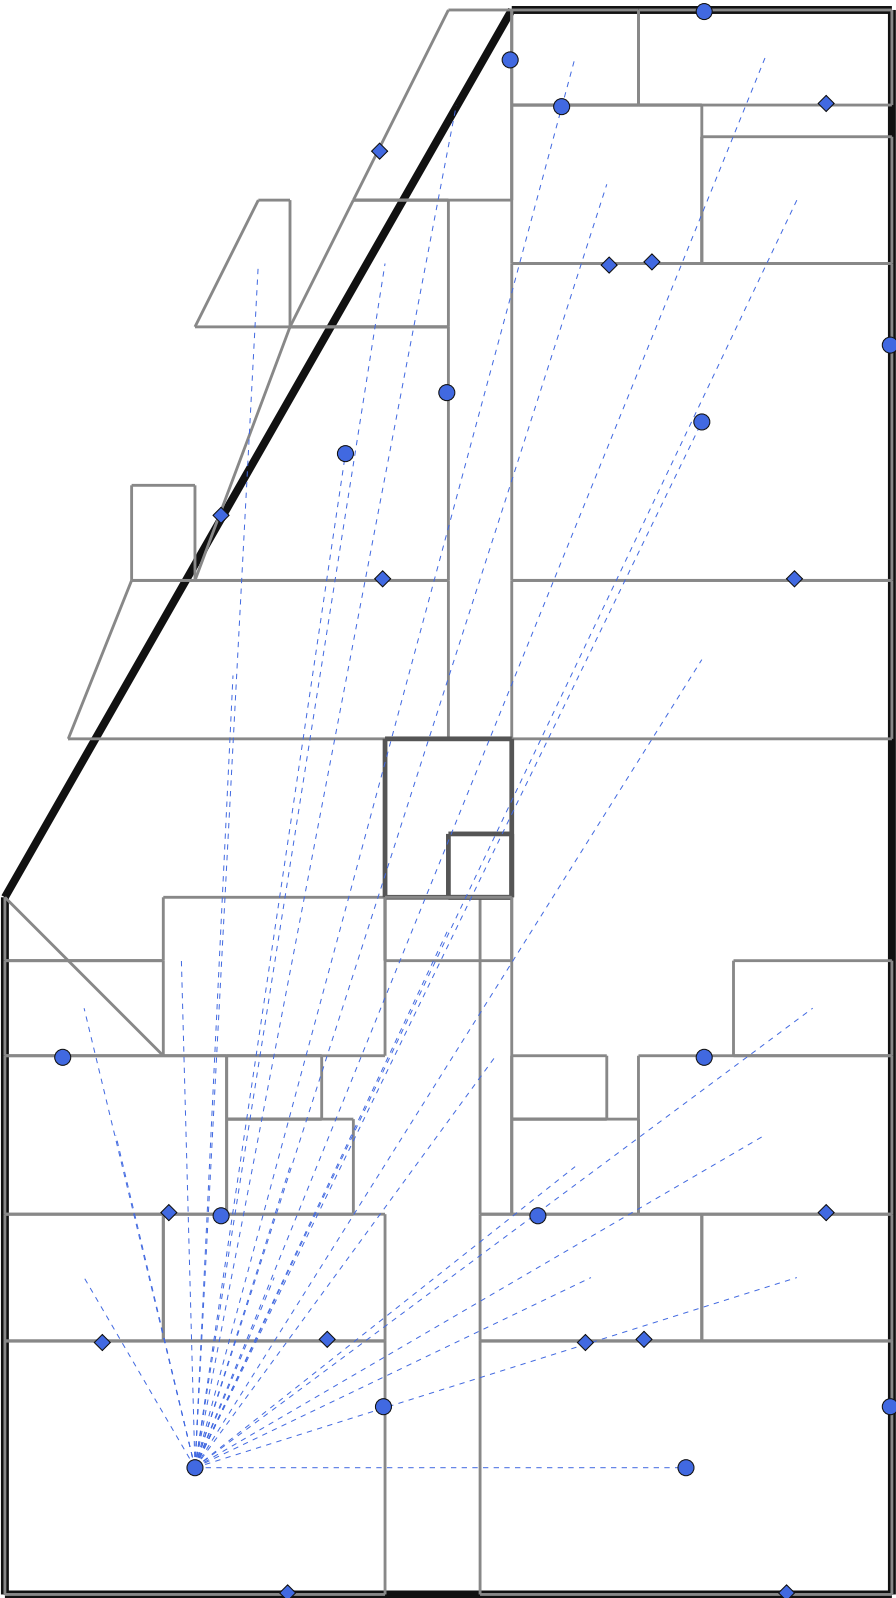

NOMENCLATURE — 520 LCU — Courants Faibles

- Prise RJ45: 15
- Prise TV: 11
- Point d'accès WiFi: 4


TIJAN AI Bureau d'Études Automatisé	Résidence Papa Oumar Sakho Dakar, Sénégal	Éch: 1/100 Pl. 115/137
	520 LCU — Courants Faibles — R+6	
Date: 06/05/2026	Réf: 1711	BIM vLCU-115 Phase: APD

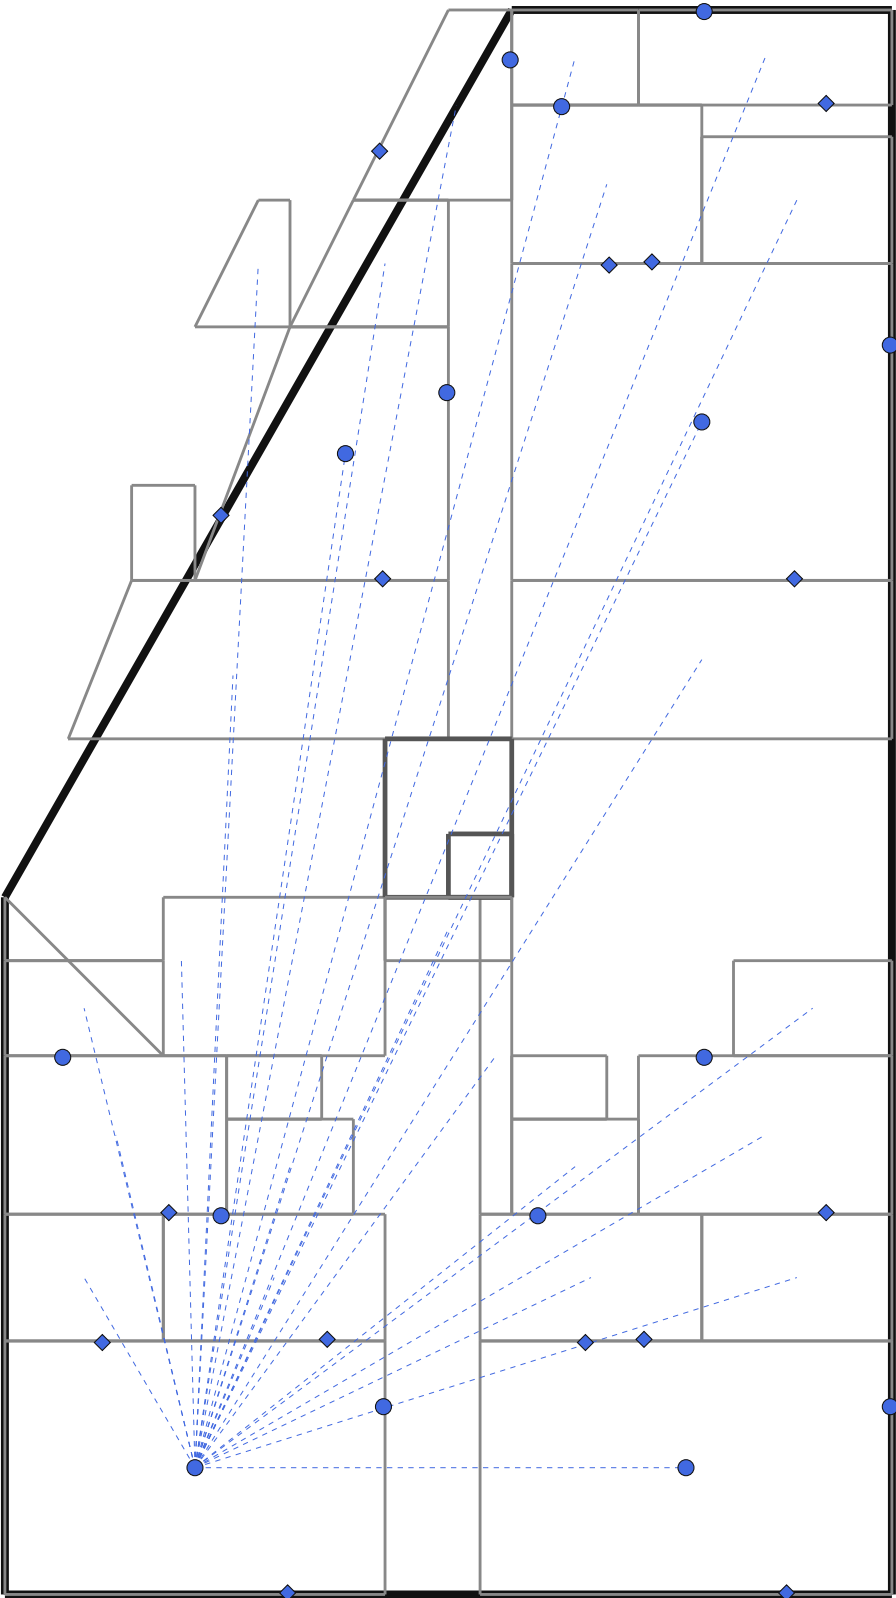

NOMENCLATURE — 520 LCU — Courants Faibles

- Prise RJ45: 15
- Prise TV: 11
- Point d'accès WiFi: 4


TIJAN AI Bureau d'Études Automatisé	Résidence Papa Oumar Sakho Dakar, Sénégal	Éch: 1/100 Pl. 116/137
	520 LCU — Courants Faibles — R+7	
Date: 06/05/2026	Réf: 1711	BIM v.LCU-116 Phase: APD

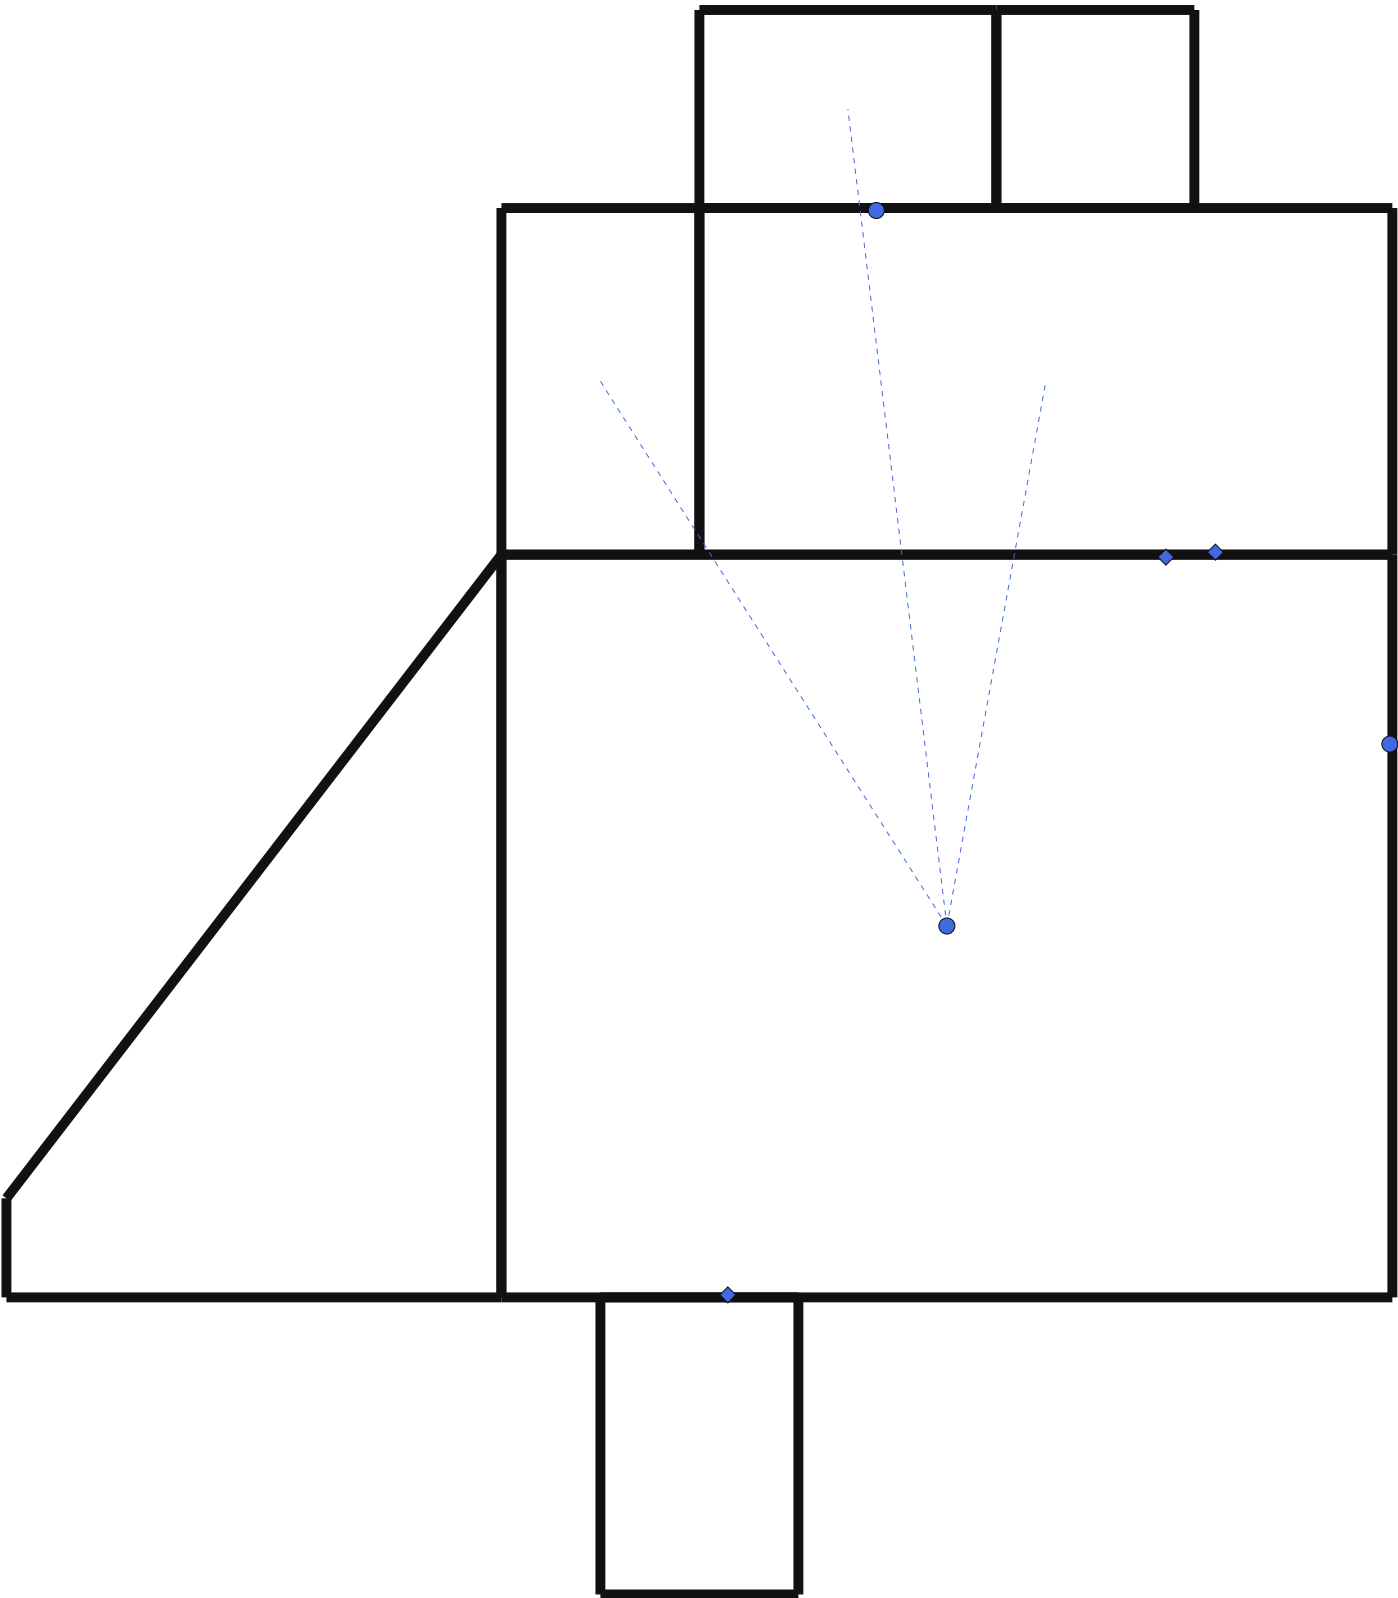

NOMENCLATURE — 520 LCU — Courants Faibles

- Prise RJ45: 3
- Prise TV: 2
- Point d'accès WiFi: 1

TIJAN AI Bureau d'Études Automatisé	Résidence Papa Oumar Sakho Dakar, Sénégal	Éch: 1/100 Pl. 117/137
	520 LCU — Courants Faibles — R+8	
Date: 06/05/2026	Réf: 1711	BIM v.LCU-117 Phase: APD

 

TIJAN AI

Bureau d'Études Automatisé

Résidence Papa Oumar Sakho

Dakar, Sénégal

Éch: 1/100

Pl. 118/137


113 RC — Faux Plafond — Sous-Sol

Date: 06/05/2026


Réf: 1711

BIM vRC-118


Phase: APD

 

TIJAN AI Bureau d'Études Automatisé	Résidence Papa Oumar Sakho Dakar, Sénégal	Éch: 1/100 Pl. 119/137
	113 RC — Faux Plafond — RDC	
Date: 06/05/2026	Réf: 1711	BIM VRC-119 Phase: APD

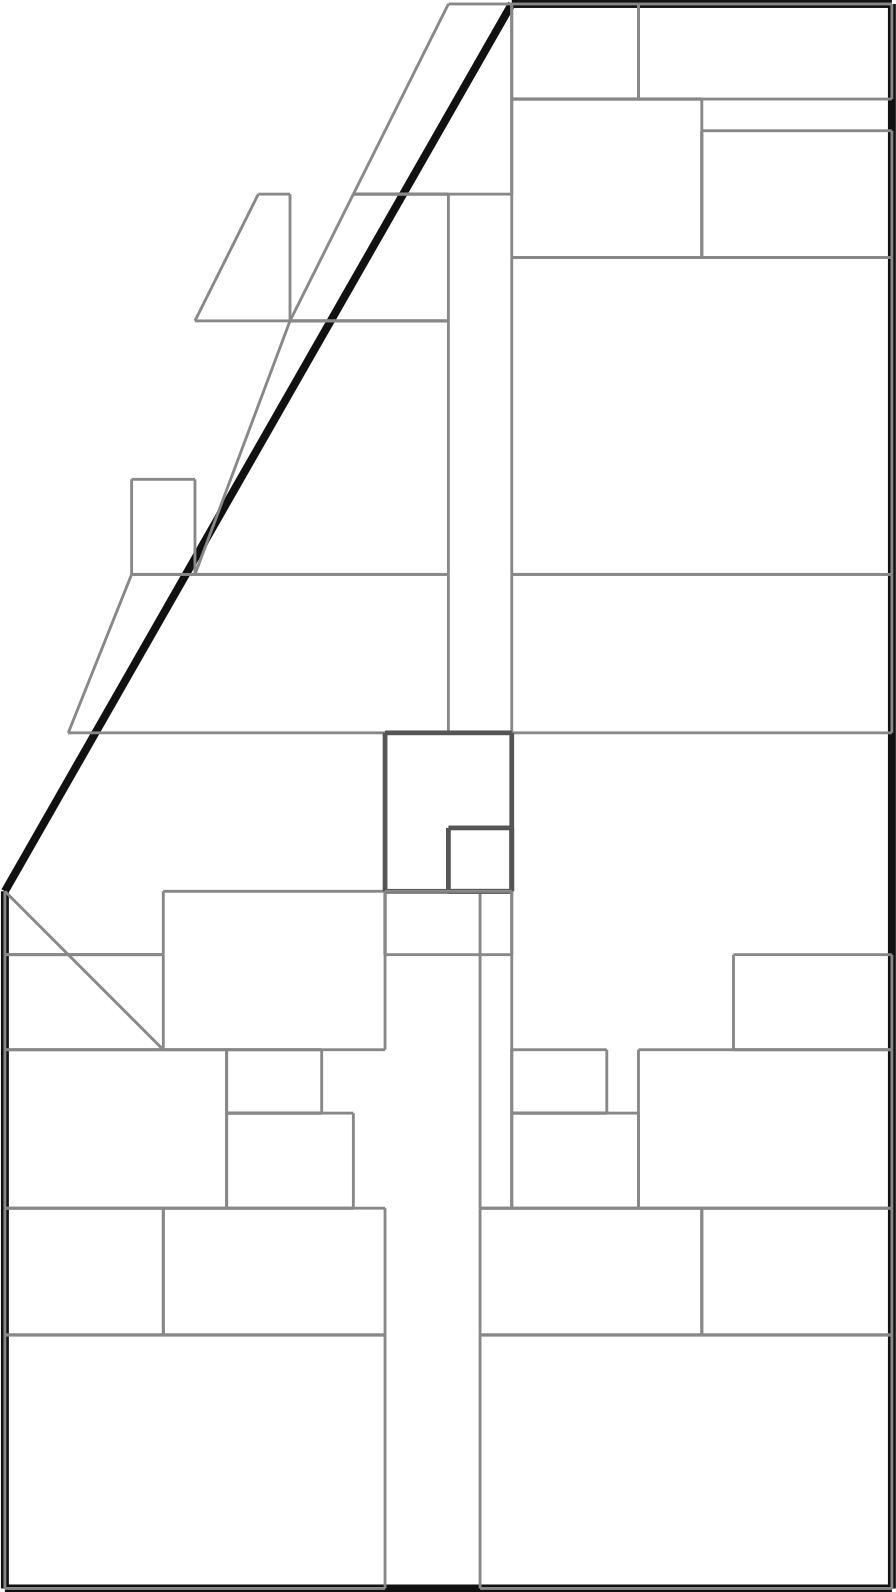

TIJAN AI Bureau d'Études Automatisé	Résidence Papa Oumar Sakho Dakar, Sénégal	Éch: 1/100 Pl. 120/137
	113 RC — Faux Plafond — R+1	
Date: 06/05/2026	Réf: 1711	BIM vRC-120 Phase: APD

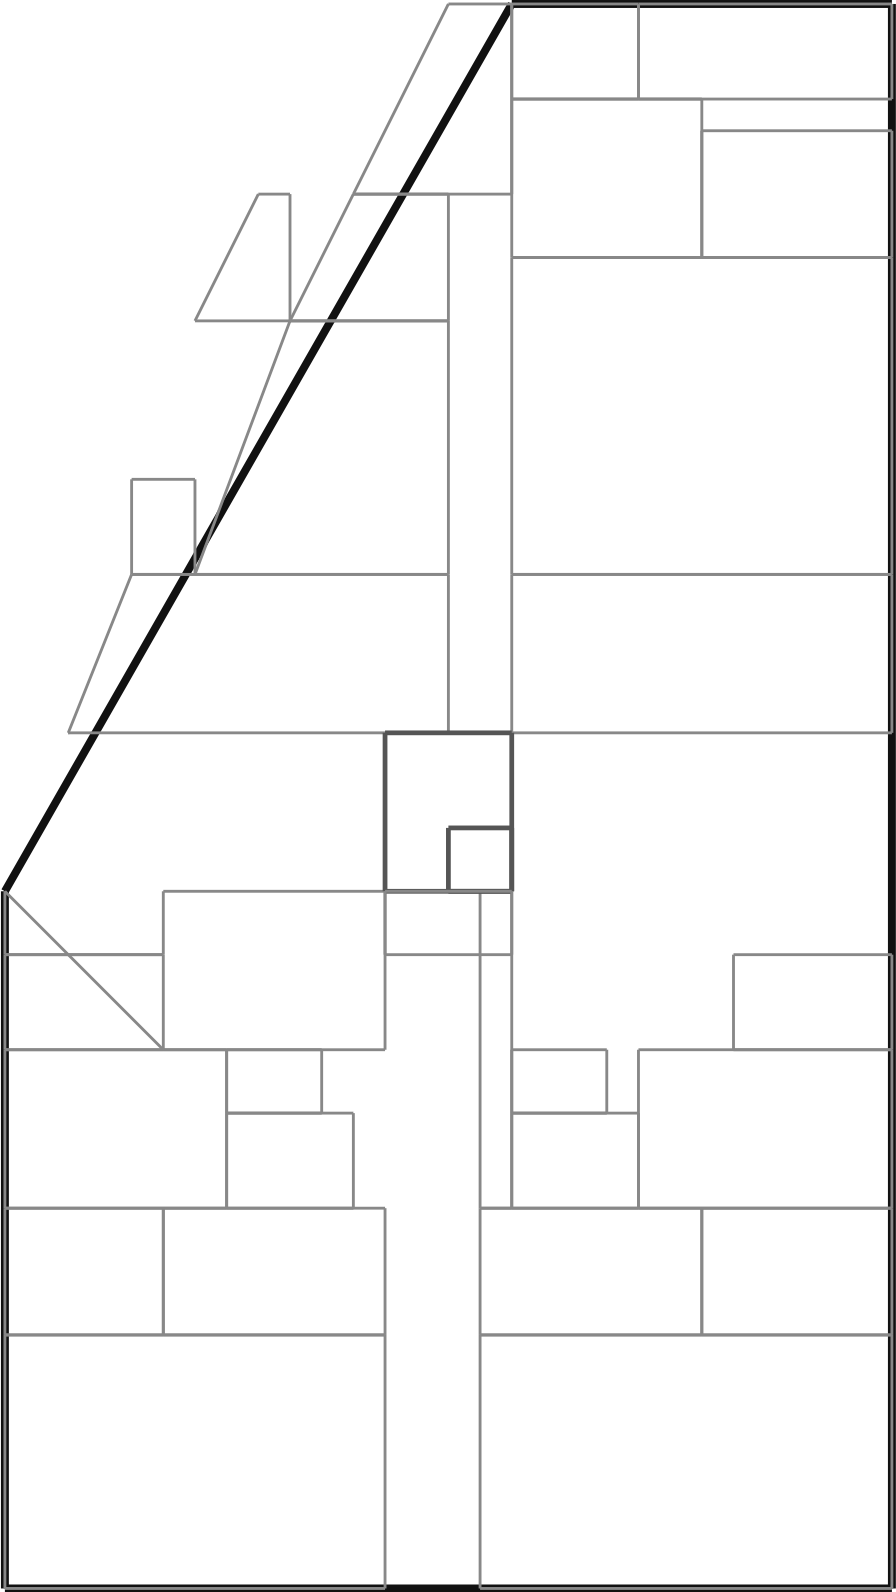

TIJAN AI

Bureau d'Études Automatisé

Résidence Papa Oumar Sakho

Dakar, Sénégal

Éch: 1/100

Pl. 121/137


113 RC — Faux Plafond — R+2

Date: 06/05/2026

Réf: 1711

BIM VRC-121

Phase: APD

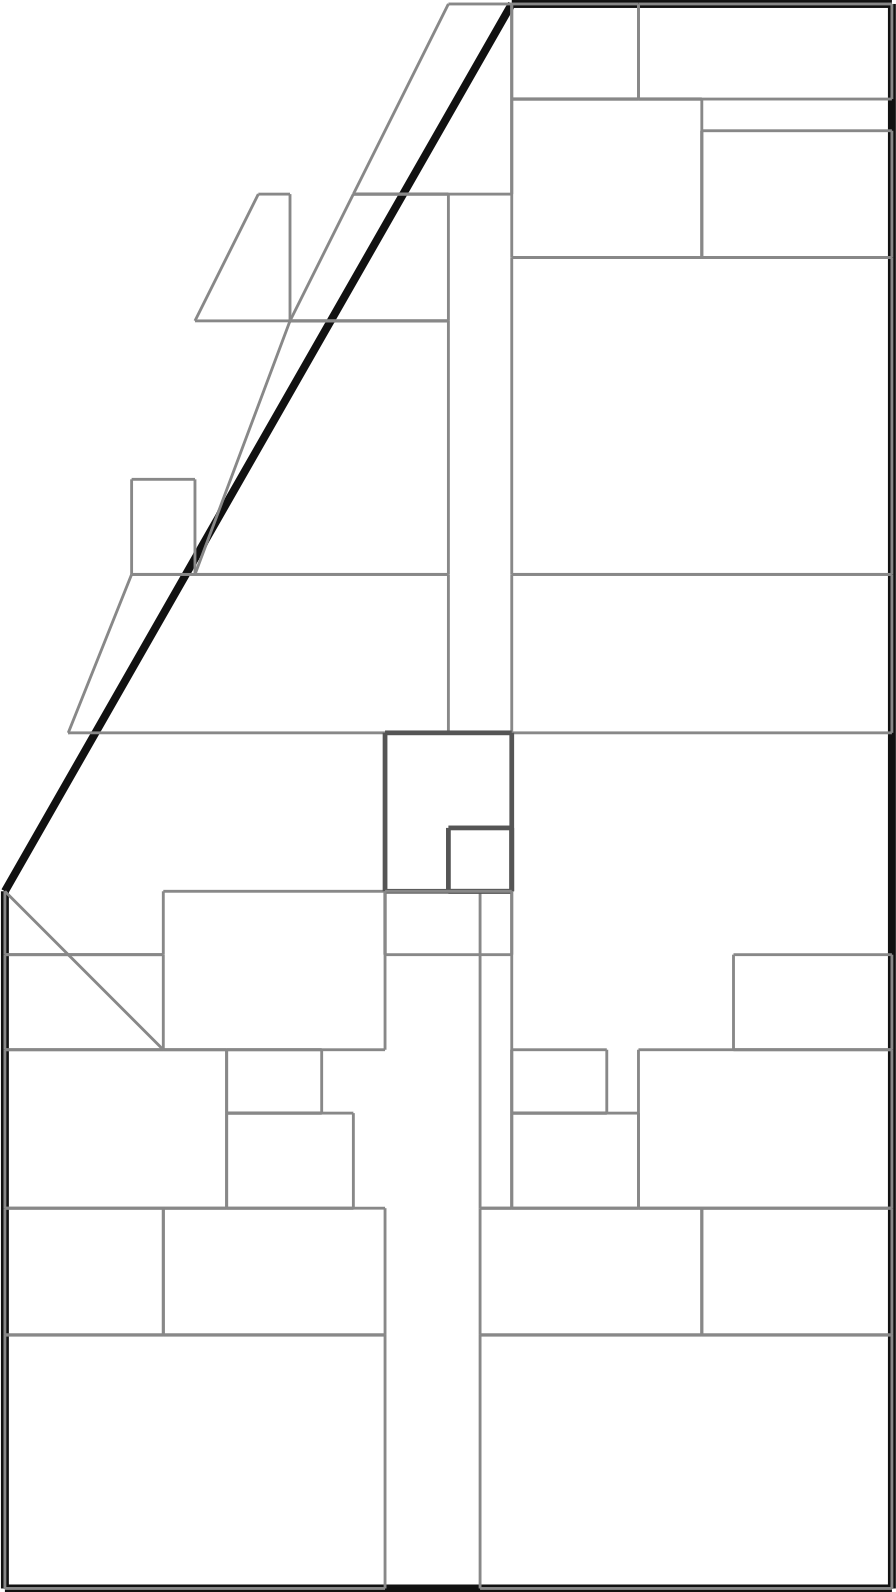

TIJAN AI

Bureau d'Études Automatisé

Résidence Papa Oumar Sakho

Dakar, Sénégal

Éch: 1/100

Pl. 122/137


113 RC — Faux Plafond — R+3

Date: 06/05/2026


Réf: 1711

BIM VRC-122


Phase: APD

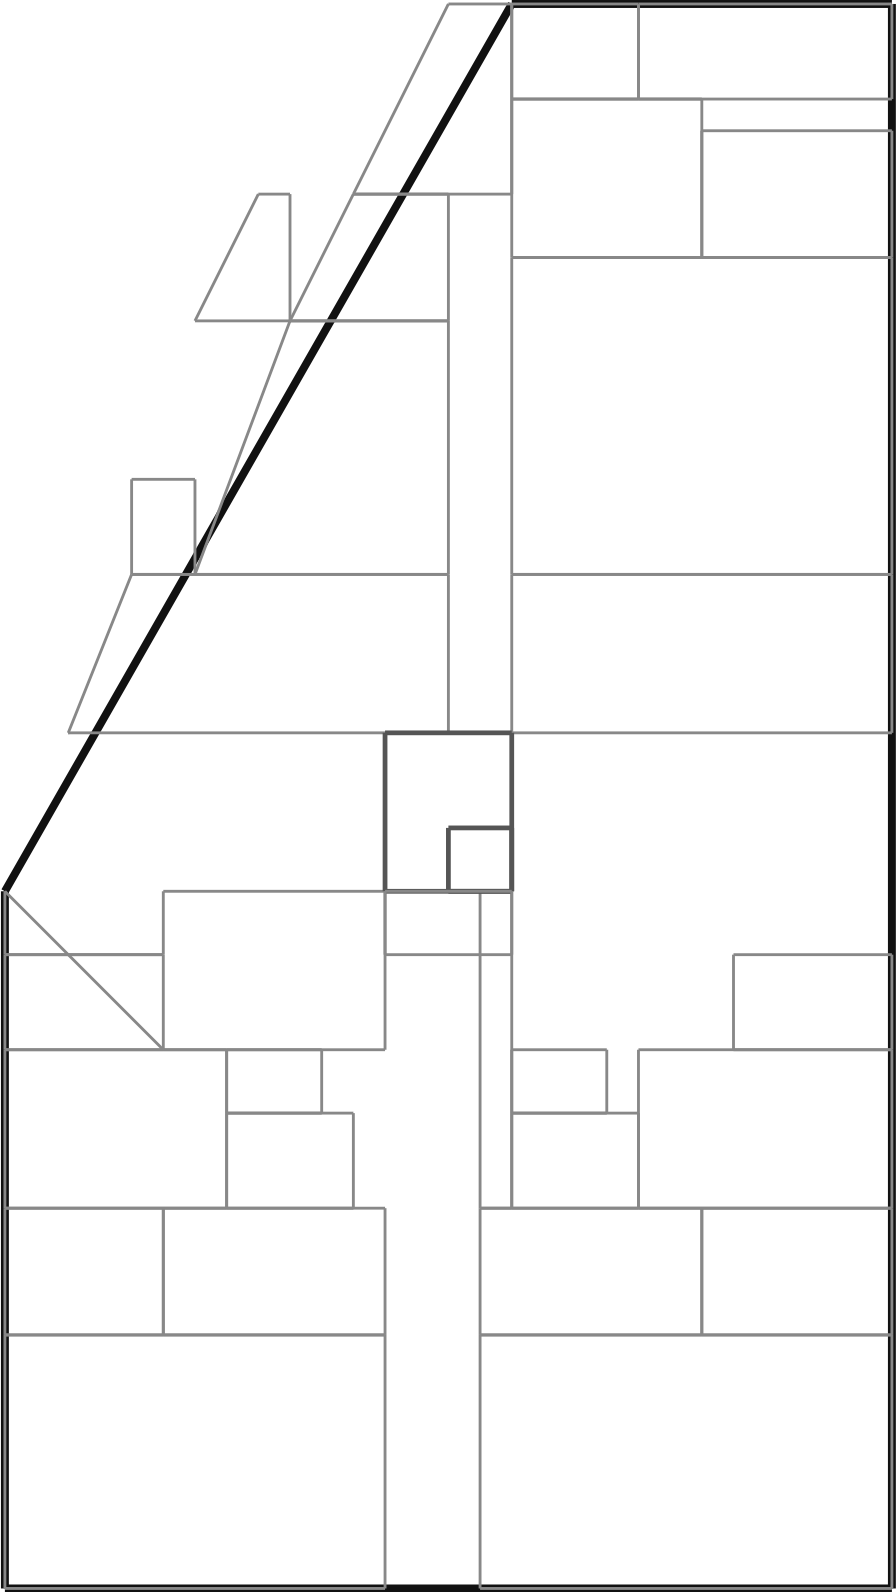


TIJAN AI Bureau d'Études Automatisé	Résidence Papa Oumar Sakho Dakar, Sénégal	Éch: 1/100 Pl. 123/137
	113 RC — Faux Plafond — R+4	
Date: 06/05/2026	Réf: 1711	BIM vRC-123 Phase: APD

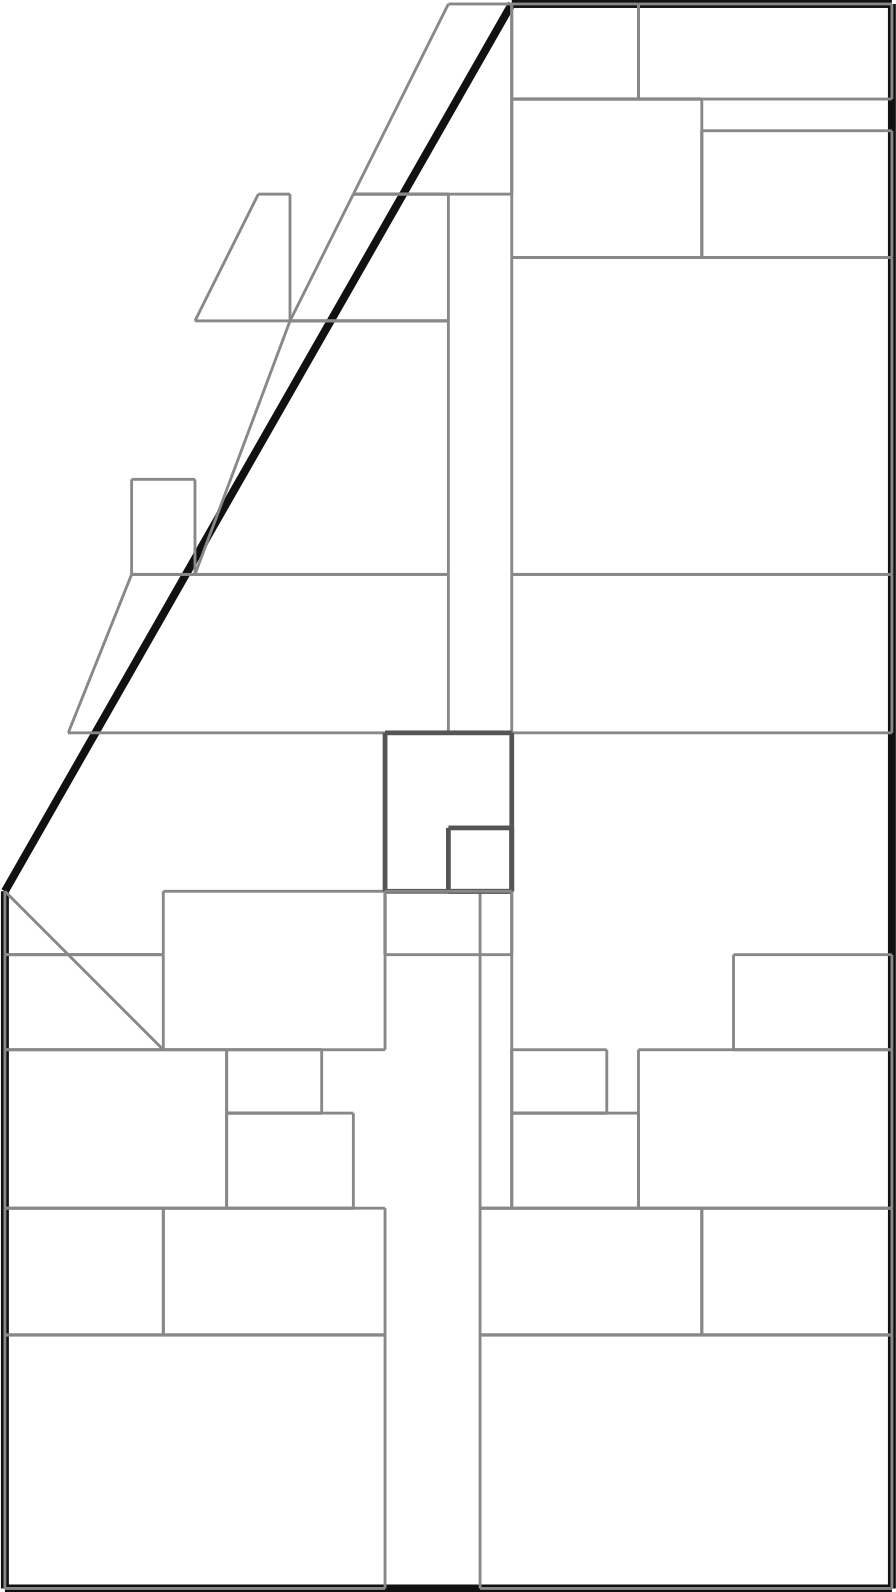

TIJAN AI Bureau d'Études Automatisé	Résidence Papa Oumar Sakho Dakar, Sénégal	Éch: 1/100 Pl. 124/137
	113 RC — Faux Plafond — R+5	
Date: 06/05/2026	Réf: 1711	BIM vRC-124 Phase: APD

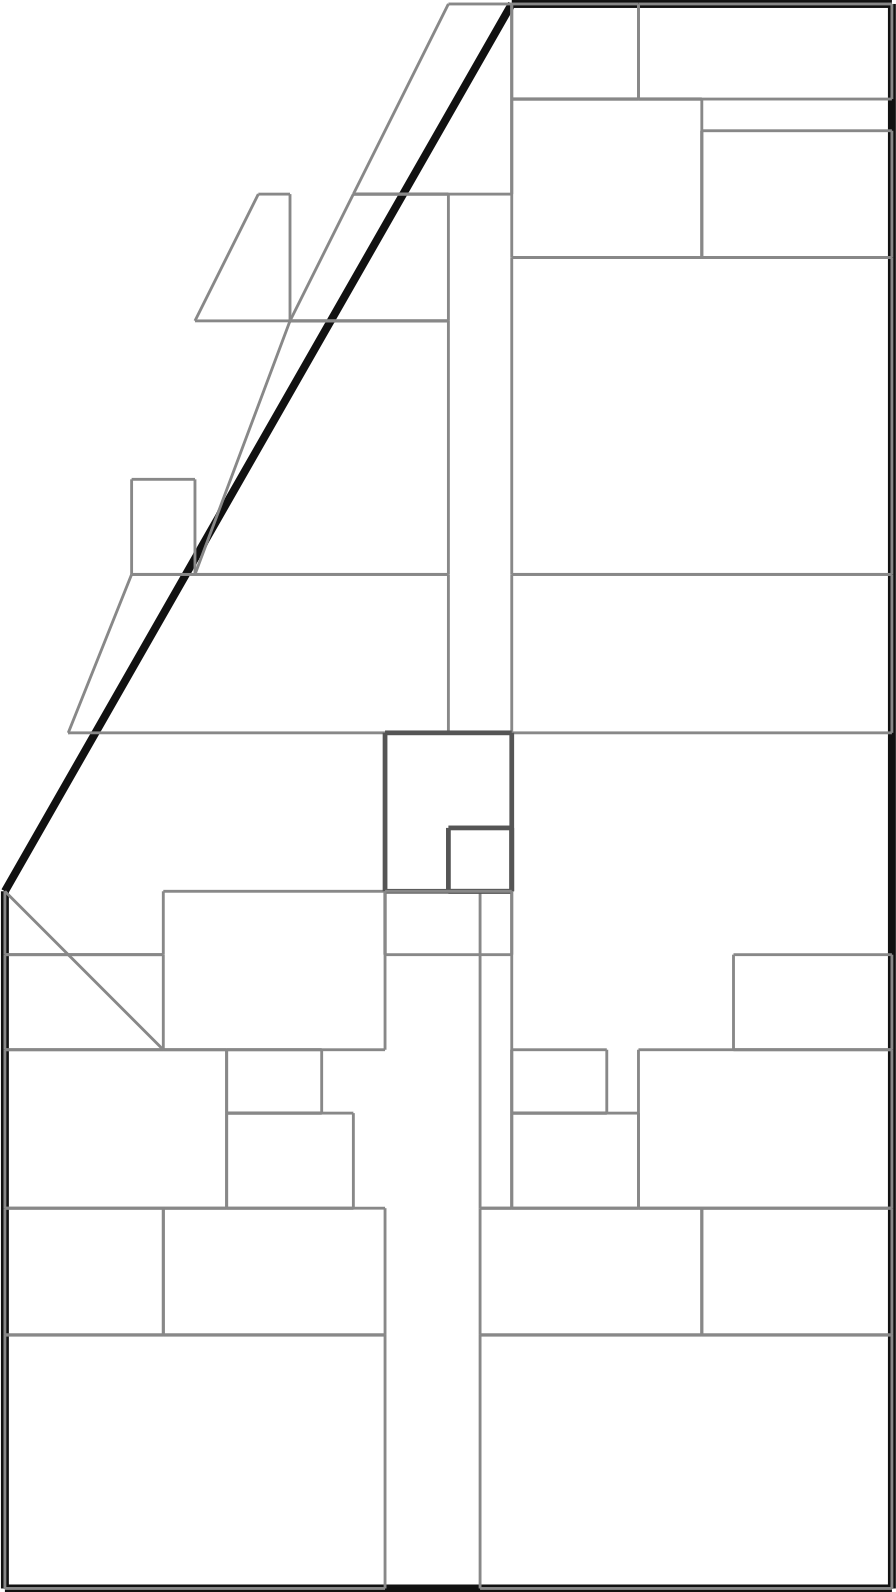

TIJAN AI Bureau d'Études Automatisé	Résidence Papa Oumar Sakho Dakar, Sénégal	Éch: 1/100 Pl. 125/137
	113 RC — Faux Plafond — R+6	
Date: 06/05/2026	Réf: 1711	BIM vRC-125 Phase: APD

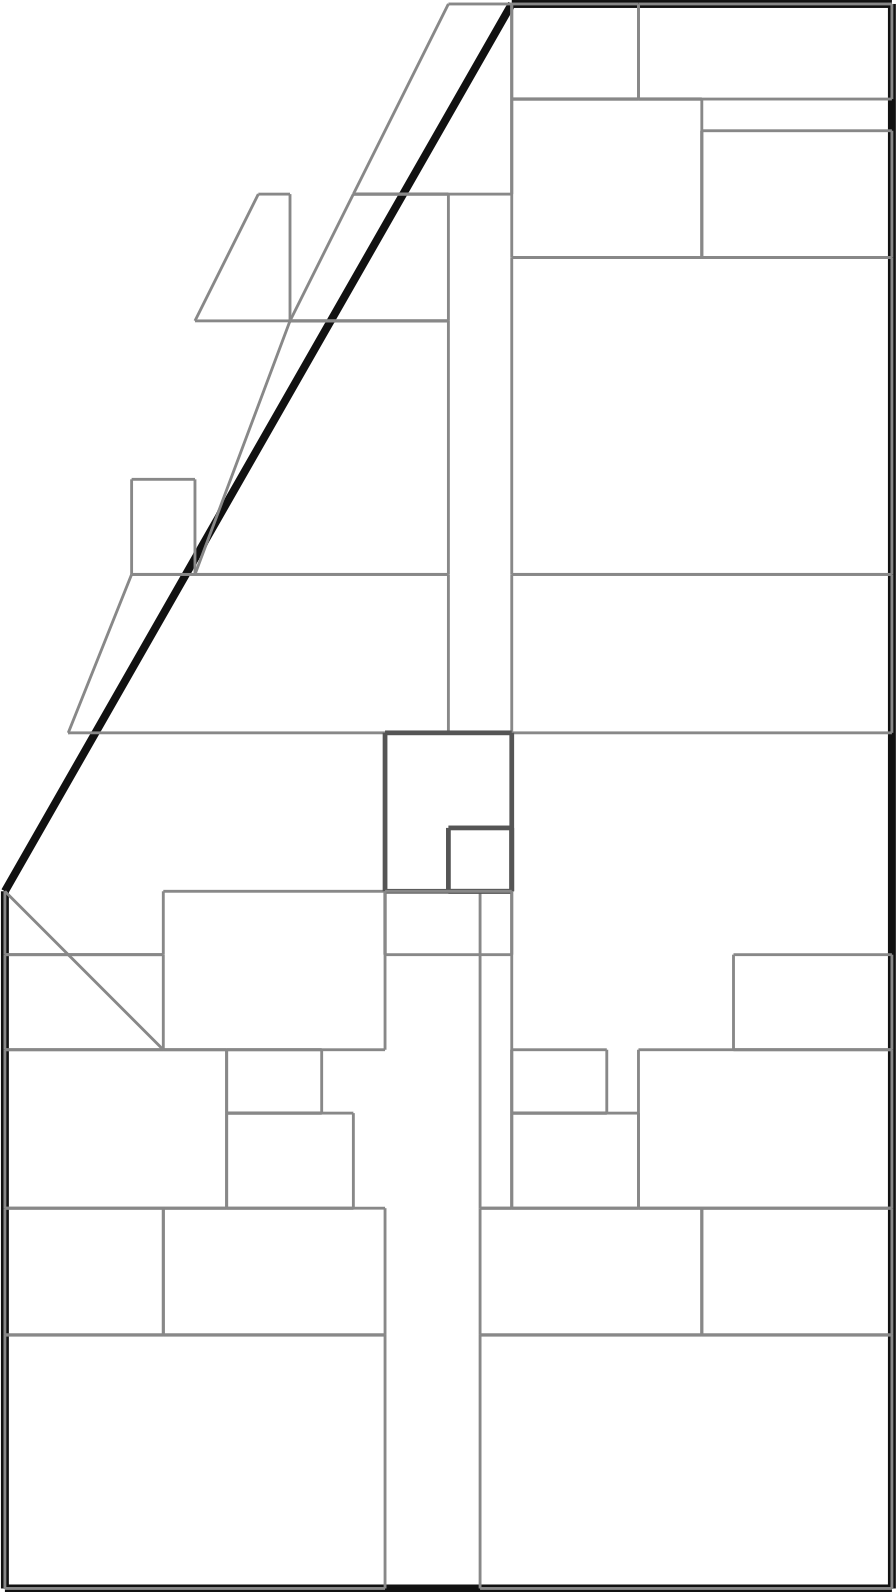

TIJAN AI

Bureau d'Études Automatisé

Résidence Papa Oumar Sakho

Dakar, Sénégal

Éch: 1/100

Pl. 126/137


113 RC — Faux Plafond — R+7

Date: 06/05/2026

Réf: 1711

BIM vRC-126

Phase: APD

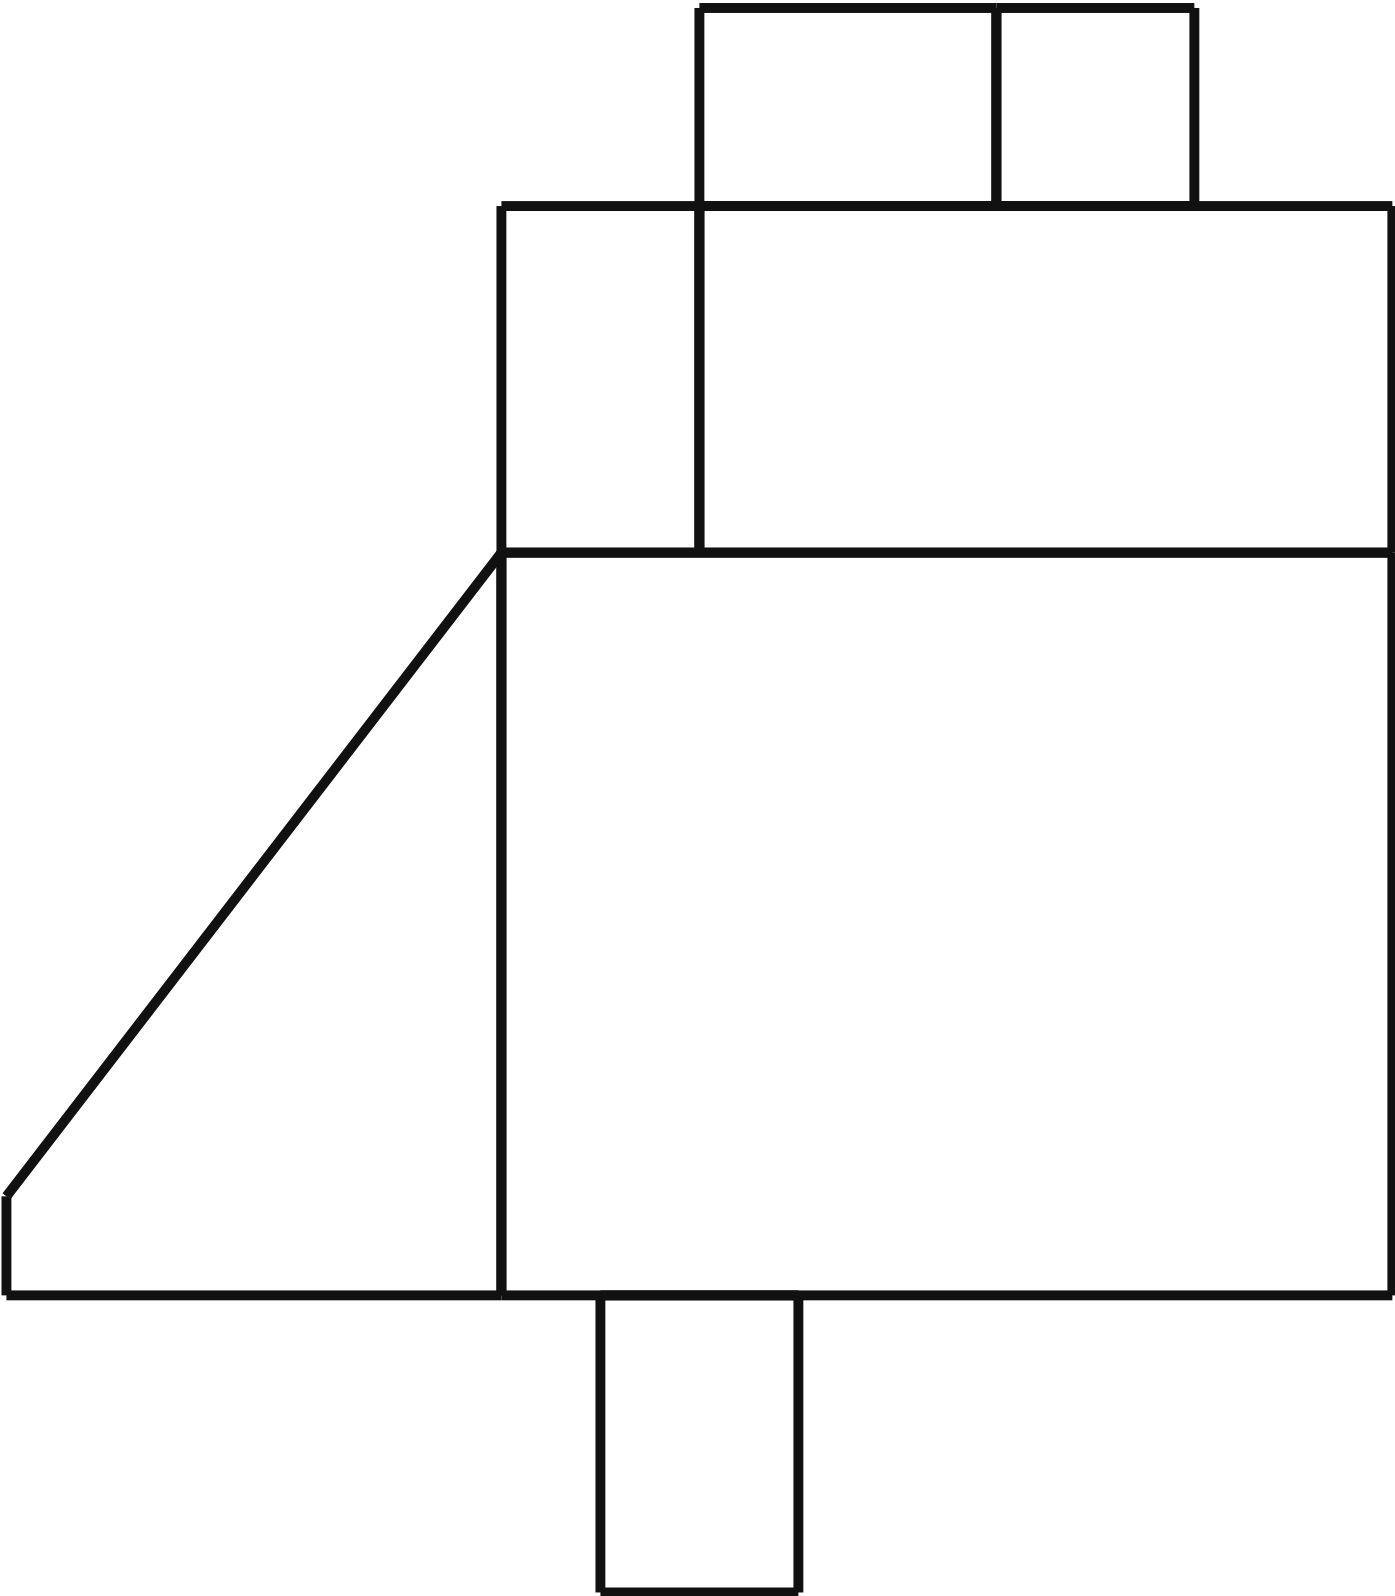

TIJAN AI

Bureau d'Études Automatisé

Résidence Papa Oumar Sakho

Dakar, Sénégal

Éch: 1/100

Pl. 127/137

113 RC — Faux Plafond — R+8

Date: 06/05/2026

Réf: 1711


BIM vRC-127

Phase: APD

001 SYN — Synthèse — Sous-Sol

LÉGENDE RÉSEAUX

- EF — Eau Froide
- EC — Eau Chaude
- EU — Eaux Usées
- CLIM — Réfrigérant
- VMC — Extraction
- HCU — Courants Forts
- LCU — Courants Faibles
- SPK — Sprinkler

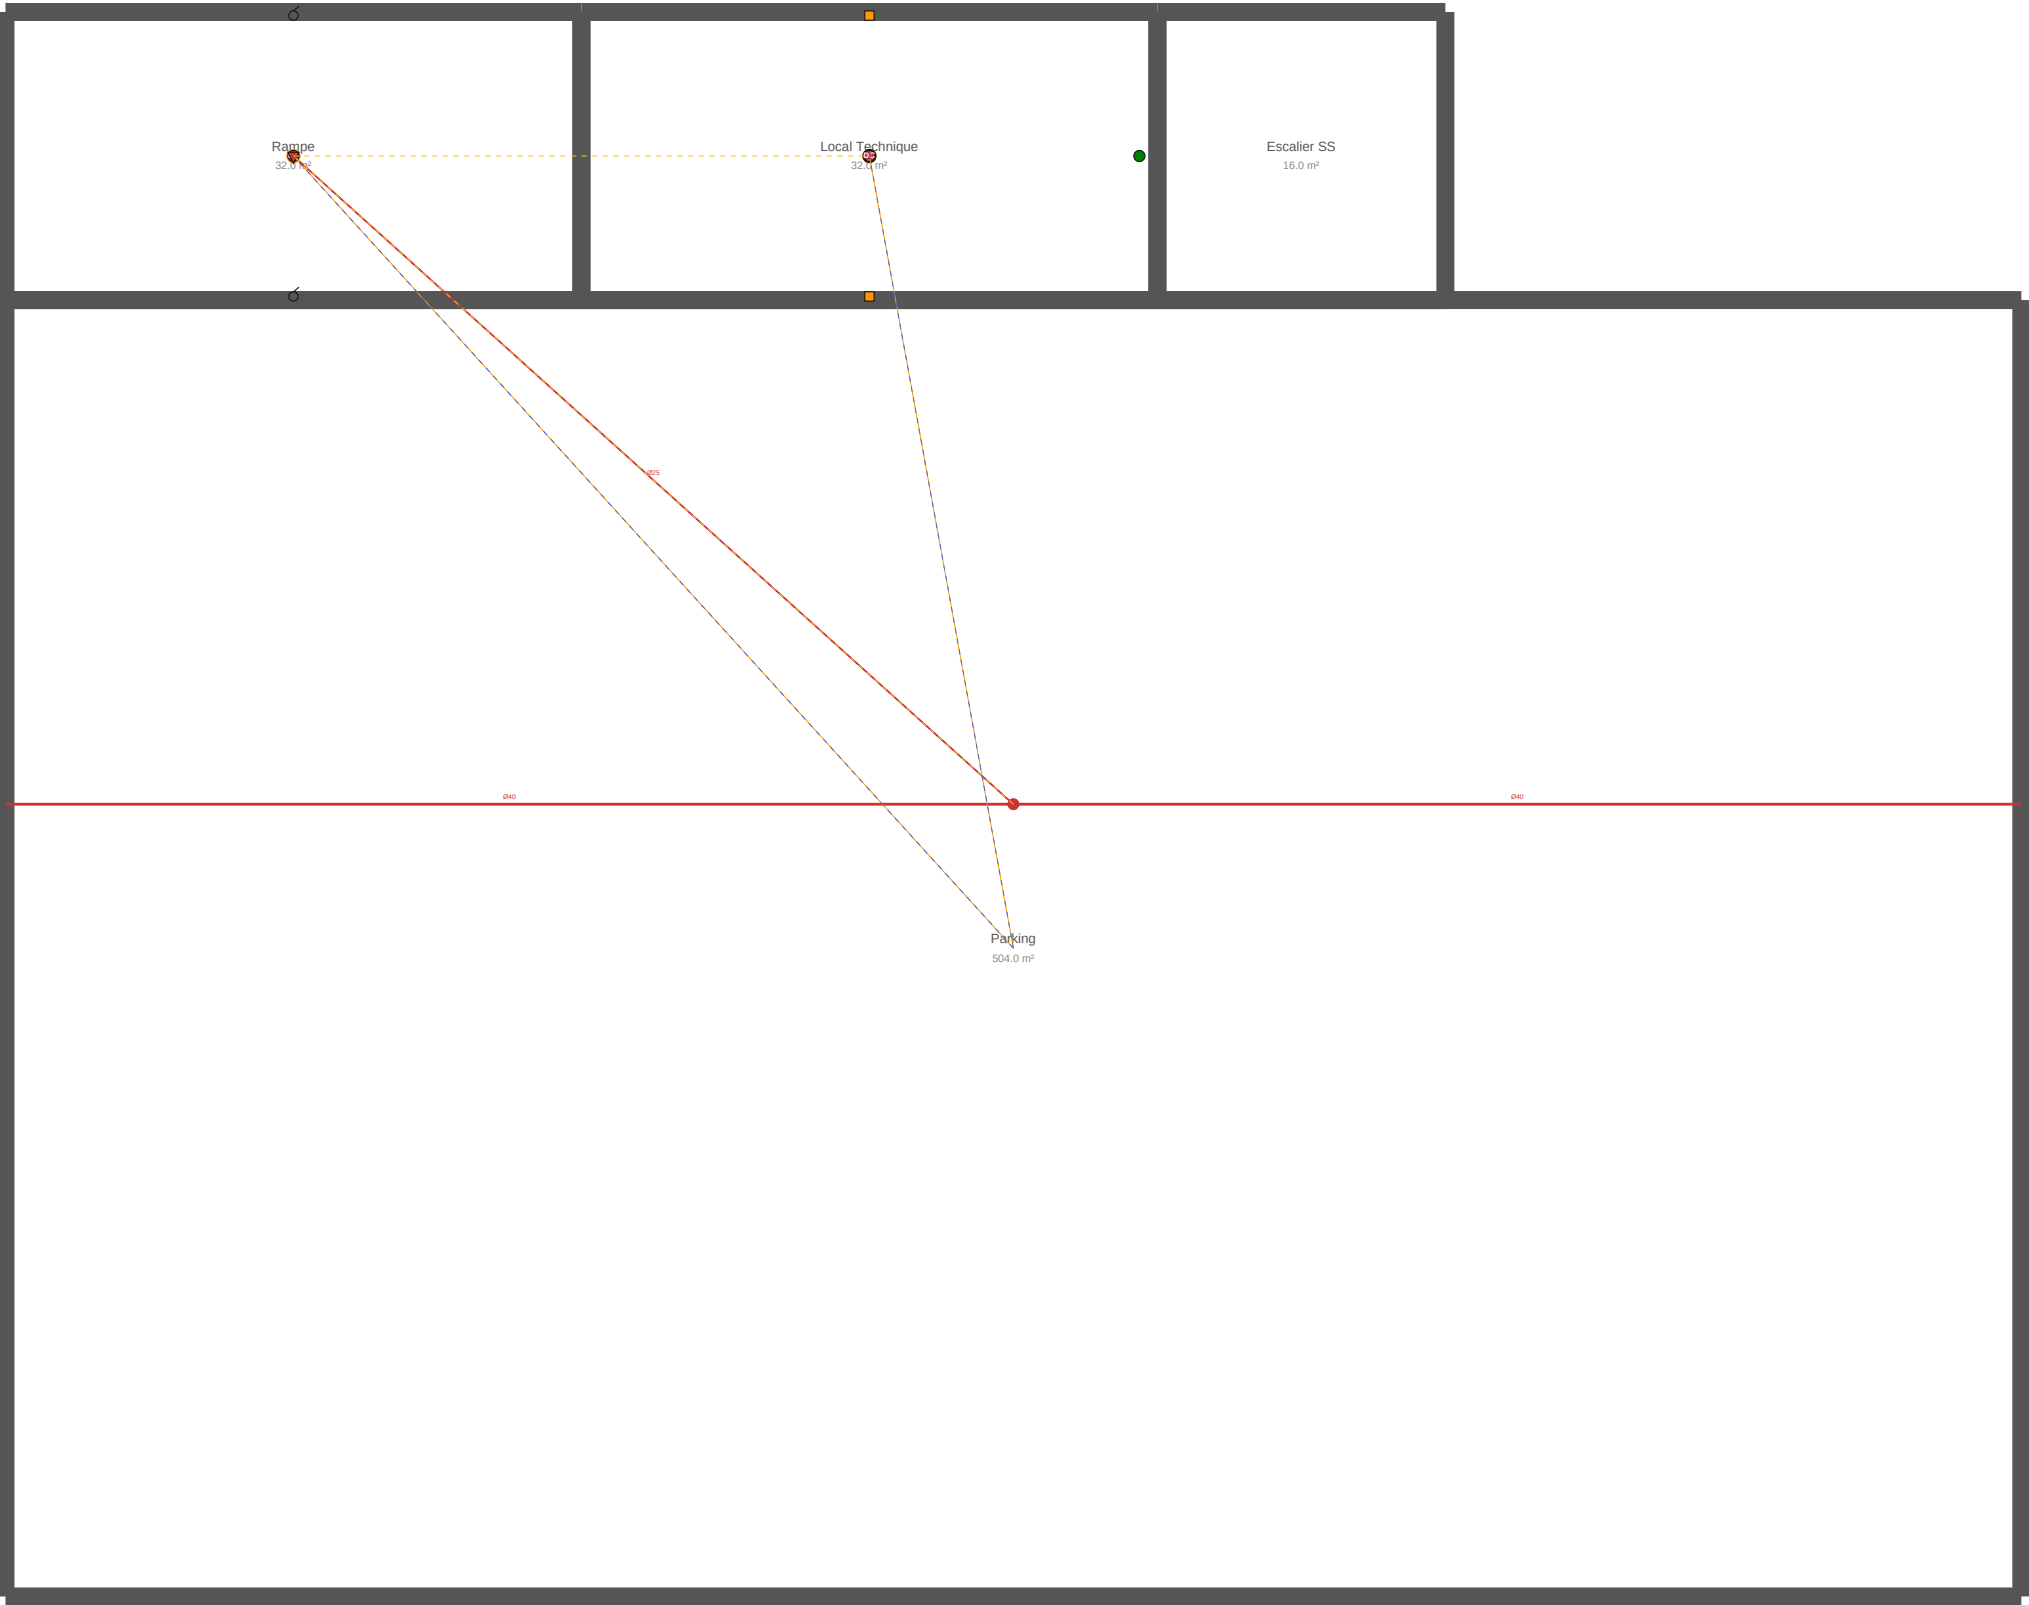


TIJAN AI Bureau d'Études Automatisé	Résidence Papa Oumar Sakho Dakar, Sénégal	Éch: 1/100 Pl. 128/137
	001 SYN — Synthèse — Sous-Sol	
Date: 06/05/2026	Réf: 1711	BIM vSYN-128 Phase: APD

001 SYN — Synthèse — RDC

LÉGENDE RÉSEAUX

- EF — Eau Froide
- EC — Eau Chaude
- EU — Eaux Usées
- CLIM — Réfrigérant
- VMC — Extraction
- HCU — Courants Forts
- LCU — Courants Faibles
- SPK — Sprinkler

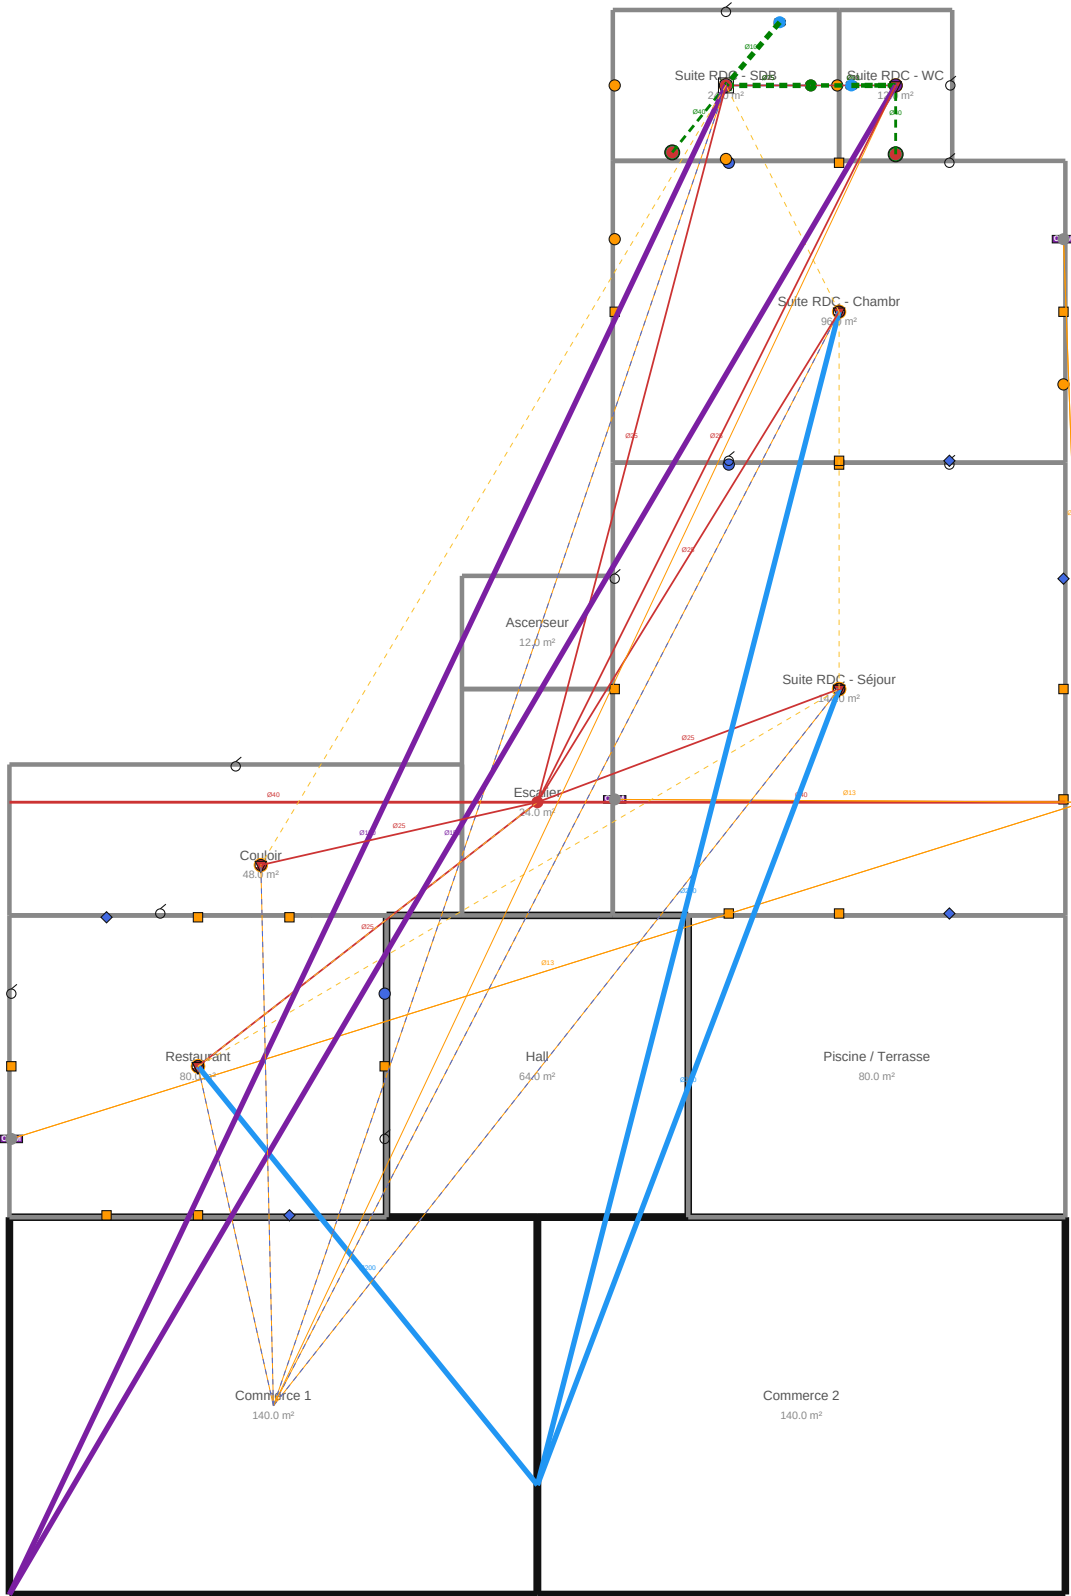


TIJAN AI Bureau d'Études Automatisé	Résidence Papa Oumar Sakho Dakar, Sénégal	Éch: 1/100 Pl. 129/137
	001 SYN — Synthèse — RDC	
Date: 06/05/2026	Réf: 1711	BIM vSYN-129 Phase: APD

001 SYN — Synthèse — R+1

LÉGENDE RÉSEAUX

- EF — Eau Froide
- EC — Eau Chaude
- EU — Eaux Usées
- CLIM — Réfrigérant
- VMC — Extraction
- HCU — Courants Forts
- LCU — Courants Faibles
- SPK — Sprinkler

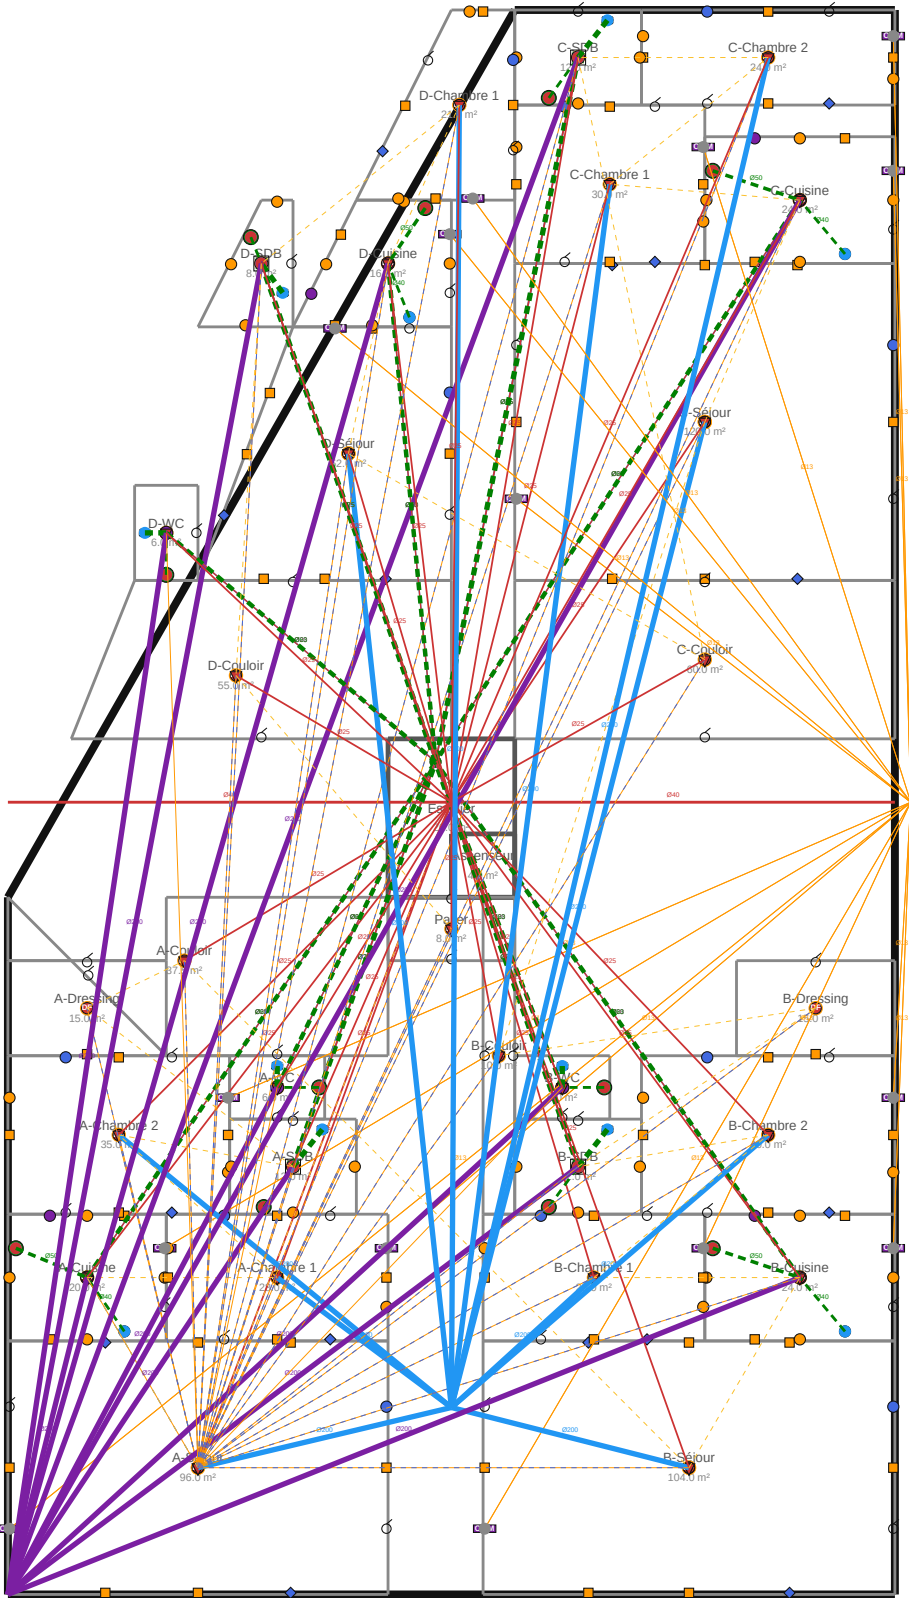


TIJAN AI Bureau d'Études Automatisé	Résidence Papa Oumar Sakho Dakar, Sénégal	Éch: 1/100 Pl. 130/137
	001 SYN — Synthèse — R+1	
Date: 06/05/2026	Réf: 1711	BIM vSYN-130 Phase: APD

001 SYN — Synthèse — R+2

LÉGENDE RÉSEAUX

-  EF — Eau Froide
-  EC — Eau Chaude
-  EU — Eaux Usées
-  CLIM — Réfrigérant
-  VMC — Extraction
-  HCU — Courants Forts
-  LCU — Courants Faibles
-  SPK — Sprinkler

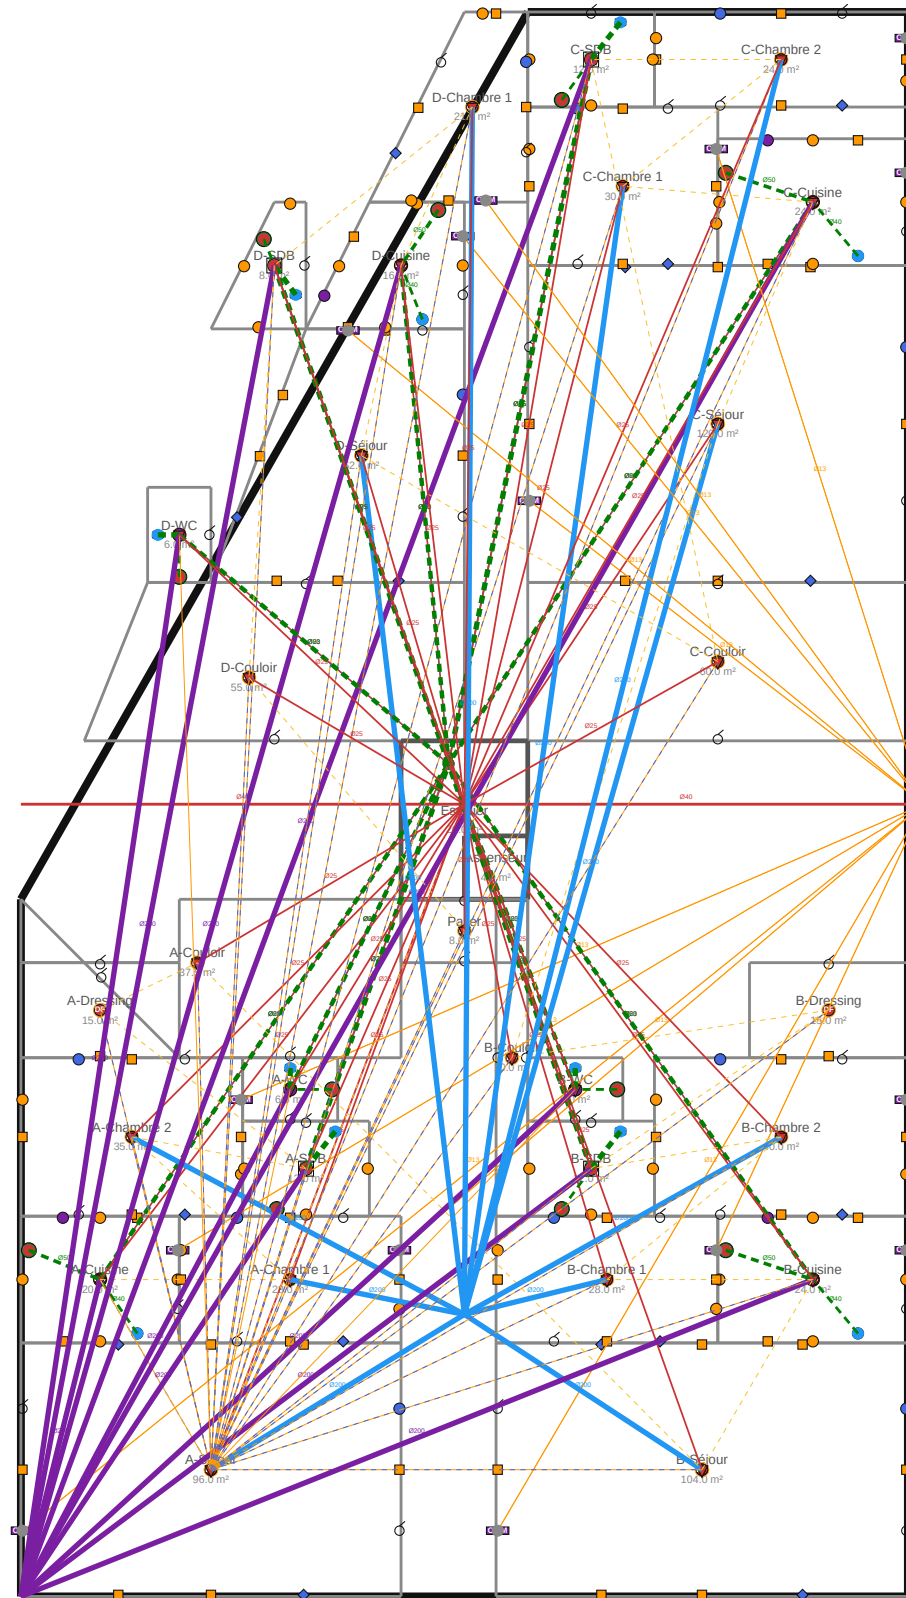


TIJAN AI Bureau d'Études Automatisé	Résidence Papa Oumar Sakho Dakar, Sénégal	Éch: 1/100 Pl. 131/137
	001 SYN — Synthèse — R+2	
Date: 06/05/2026	Réf: 1711	BIM vSYN-131 Phase: APD

001 SYN — Synthèse — R+3

LÉGENDE RÉSEAUX

- EF — Eau Froide
- EC — Eau Chaude
- EU — Eaux Usées
- CLIM — Réfrigérant
- VMC — Extraction
- HCU — Courants Forts
- LCU — Courants Faibles
- SPK — Sprinkler

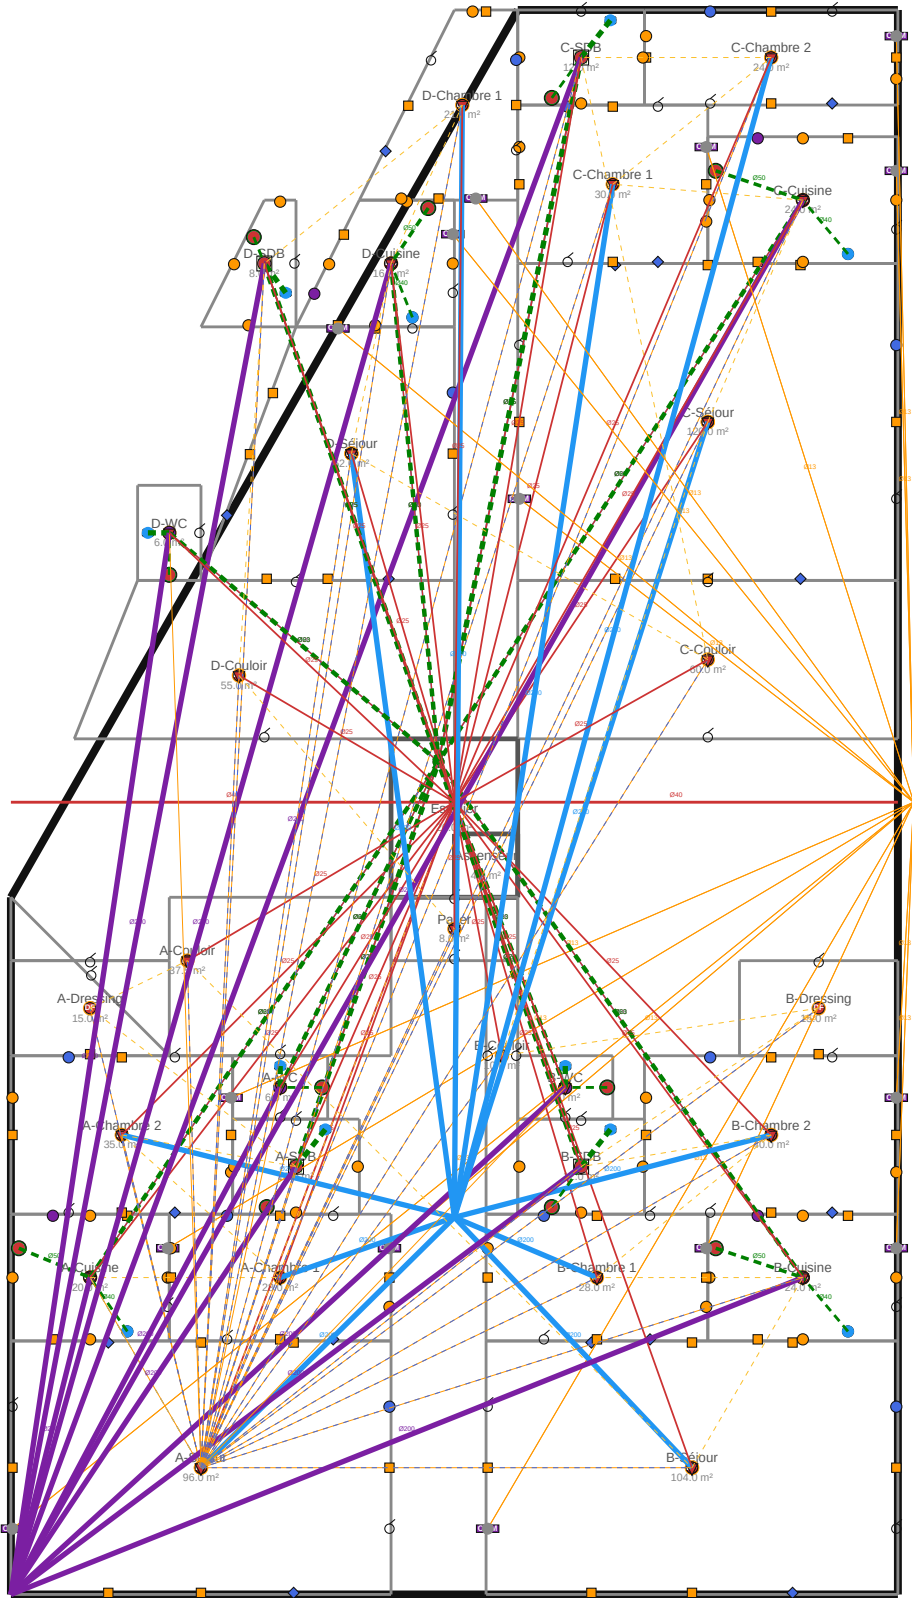


TIJAN AI Bureau d'Études Automatisé	Résidence Papa Oumar Sakho Dakar, Sénégal	Éch: 1/100 Pl. 132/137
	001 SYN — Synthèse — R+3	
Date: 06/05/2026	Réf: 1711	BIM vSYN-132 Phase: APD

001 SYN — Synthèse — R+4

LÉGENDE RÉSEAUX

- EF — Eau Froide
- EC — Eau Chaude
- EU — Eaux Usées
- CLIM — Réfrigérant
- VMC — Extraction
- HCU — Courants Forts
- LCU — Courants Faibles
- SPK — Sprinkler

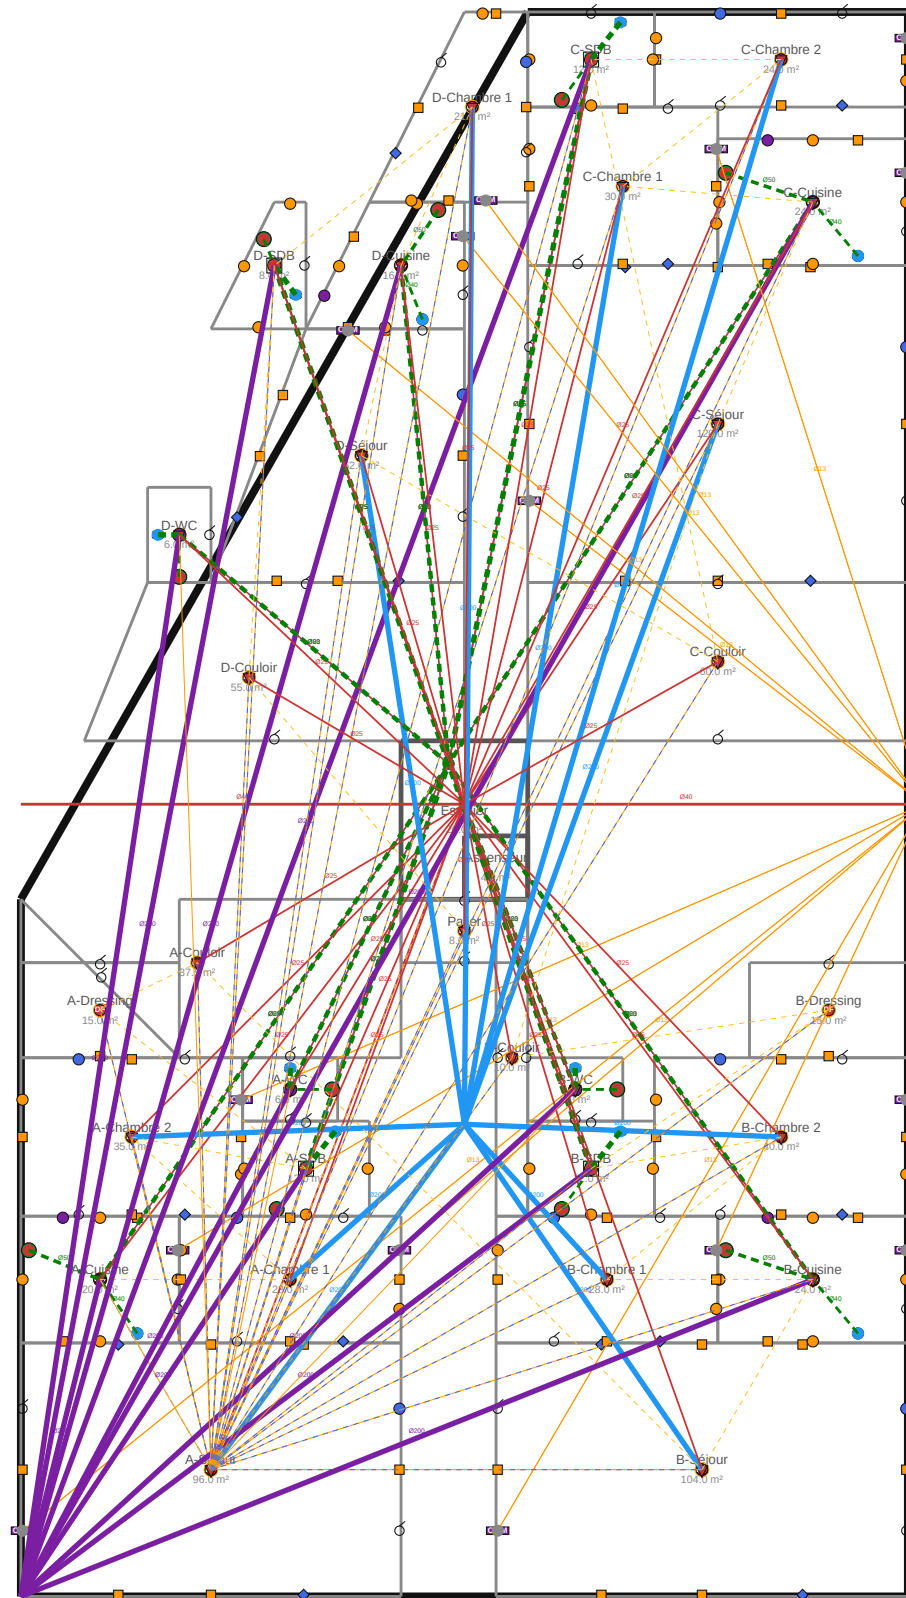


TIJAN AI Bureau d'Études Automatisé	Résidence Papa Oumar Sakho Dakar, Sénégal	Éch: 1/100 Pl. 133/137
	001 SYN — Synthèse — R+4	
Date: 06/05/2026	Réf: 1711	BIM vSYN-133 Phase: APD

001 SYN — Synthèse — R+5

LÉGENDE RÉSEAUX

- EF — Eau Froide
- EC — Eau Chaude
- EU — Eaux Usées
- CLIM — Réfrigérant
- VMC — Extraction
- HCU — Courants Forts
- LCU — Courants Faibles
- SPK — Sprinkler

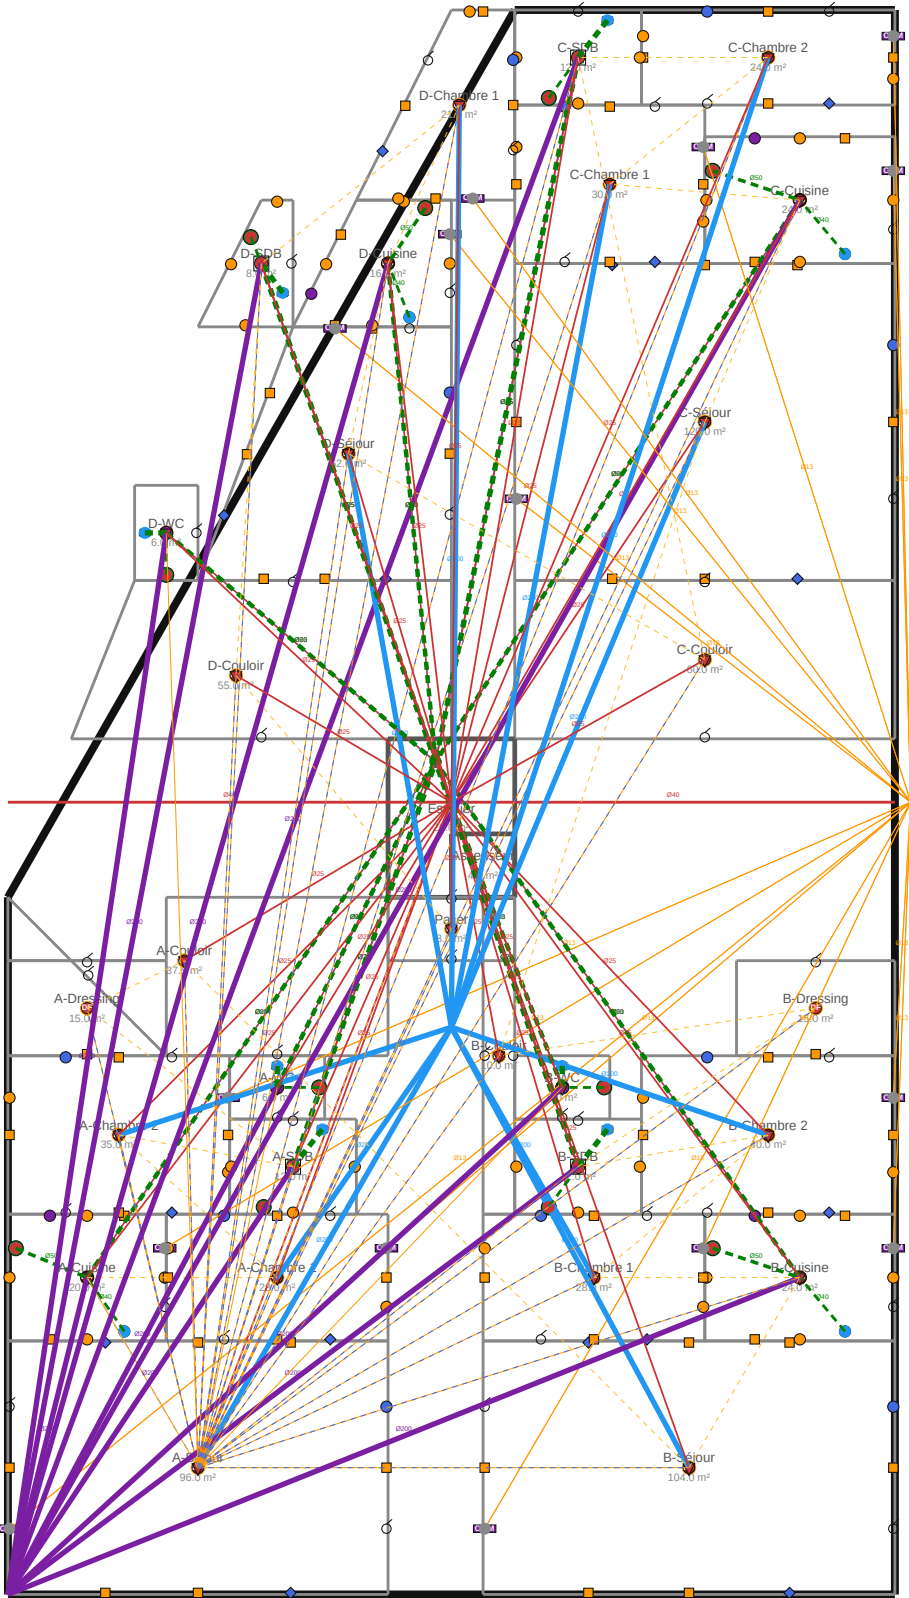


TIJAN AI Bureau d'Études Automatisé	Résidence Papa Oumar Sakho Dakar, Sénégal	Éch: 1/100 Pl. 134/137
	001 SYN — Synthèse — R+5	
Date: 06/05/2026	Réf: 1711	BIM vSYN-134 Phase: APD

001 SYN — Synthèse — R+6

LÉGENDE RÉSEAUX

- EF — Eau Froide
- EC — Eau Chaude
- EU — Eaux Usées
- CLIM — Réfrigérant
- VMC — Extraction
- HCU — Courants Forts
- LCU — Courants Faibles
- SPK — Sprinkler

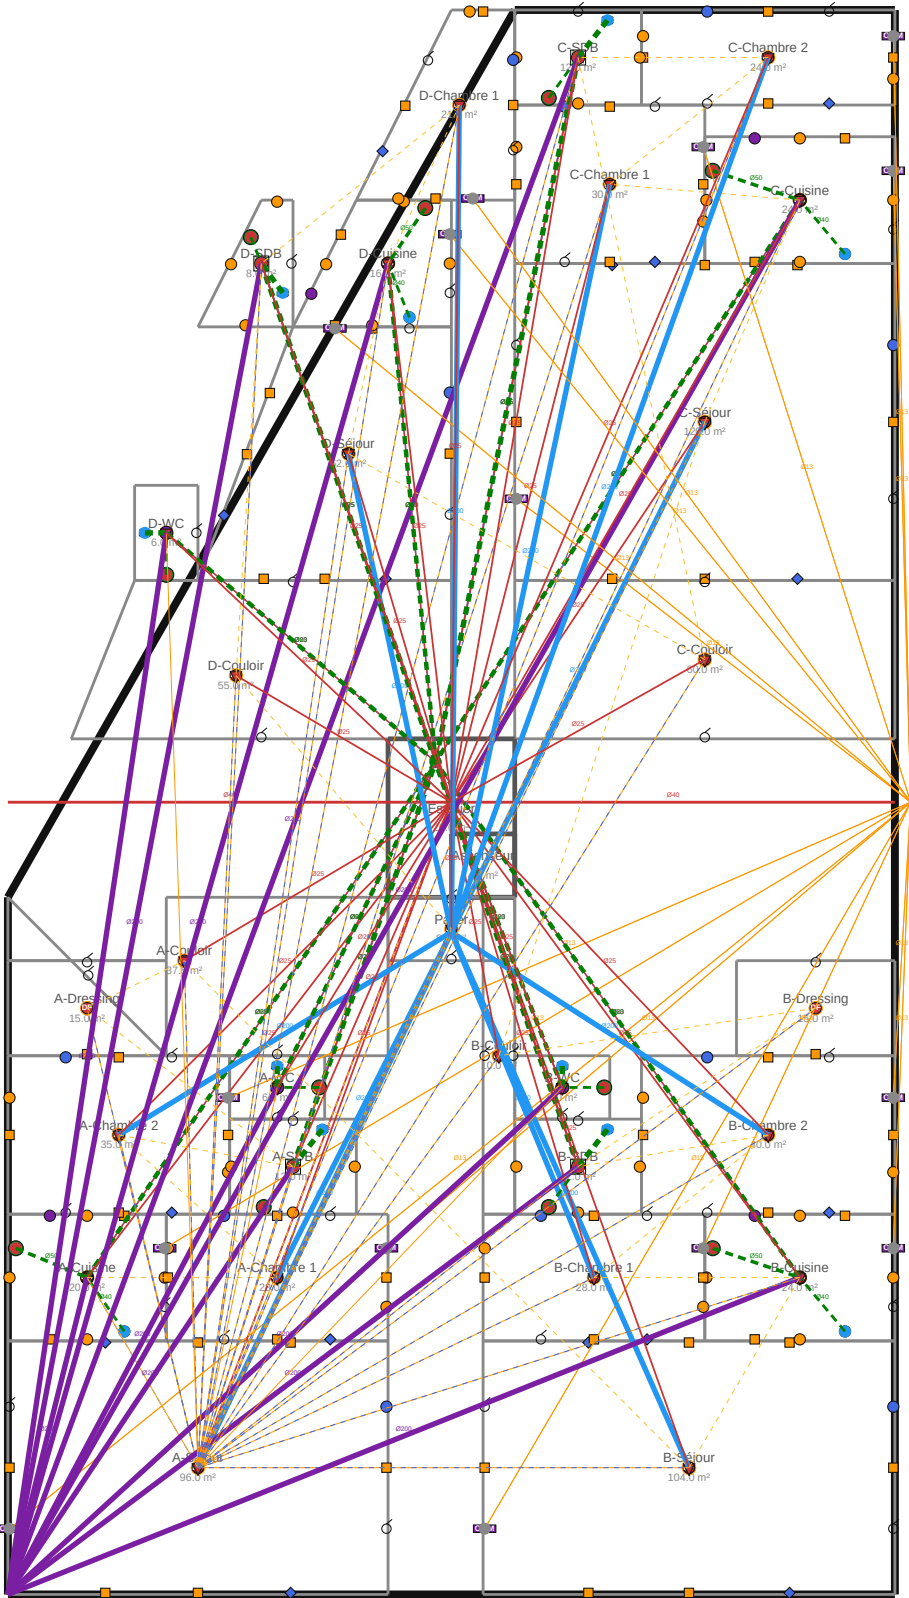


TIJAN AI Bureau d'Études Automatisé	Résidence Papa Oumar Sakho Dakar, Sénégal	Éch: 1/100 Pl. 135/137
	001 SYN — Synthèse — R+6	
Date: 06/05/2026	Réf: 1711	BIM vSYN-135 Phase: APD

001 SYN — Synthèse — R+7

LÉGENDE RÉSEAUX

- EF — Eau Froide
- EC — Eau Chaude
- EU — Eaux Usées
- CLIM — Réfrigérant
- VMC — Extraction
- HCU — Courants Forts
- LCU — Courants Faibles
- SPK — Sprinkler

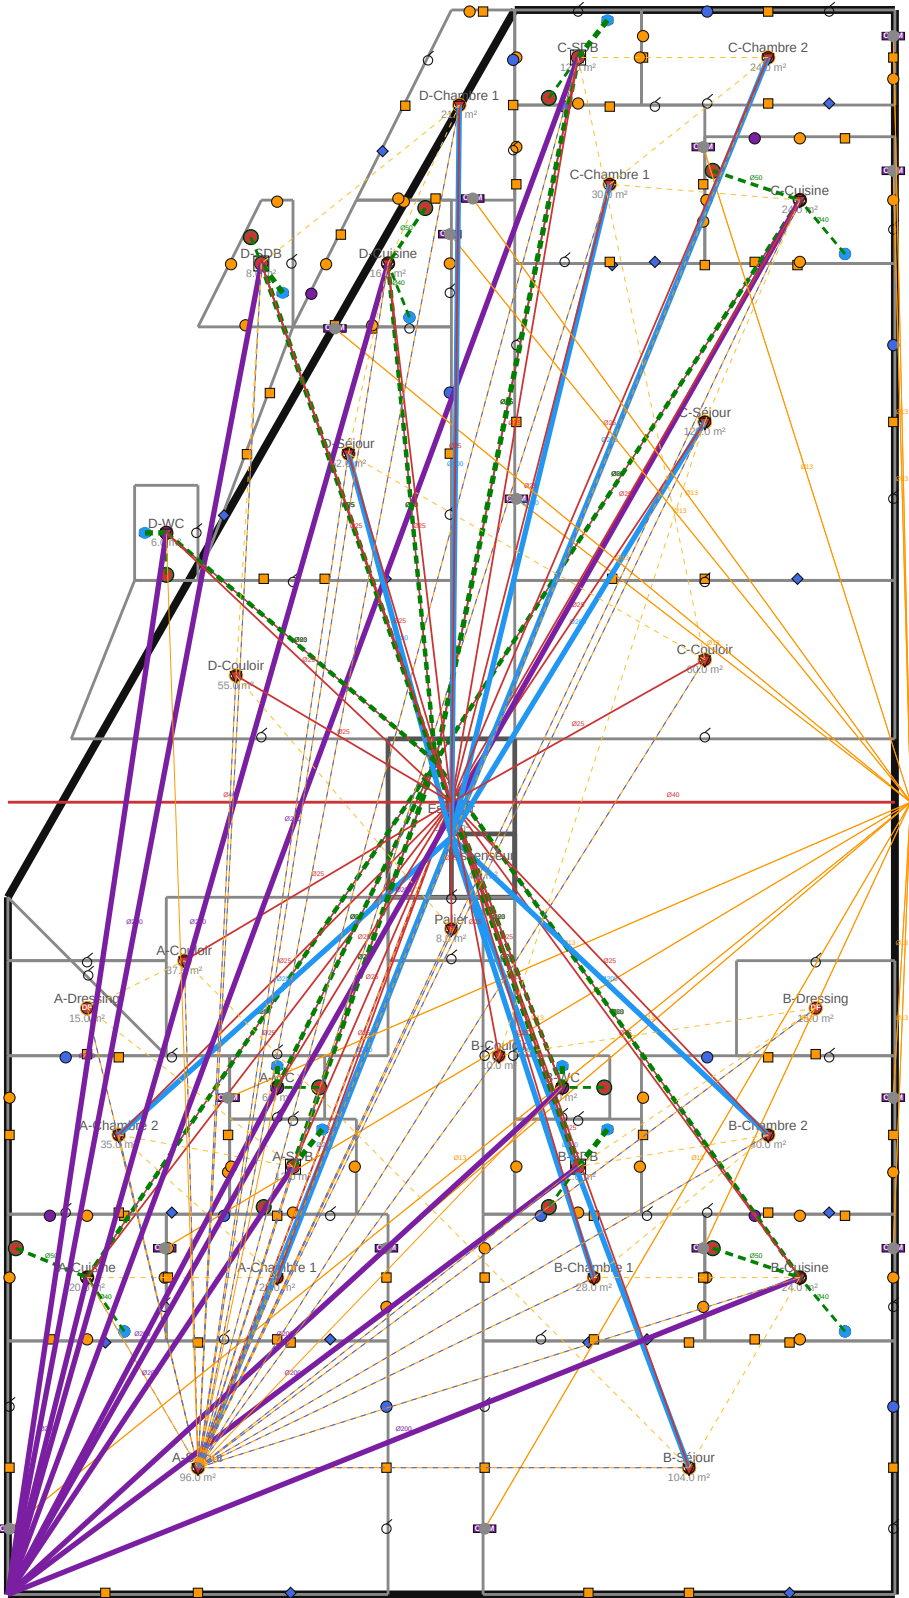


TIJAN AI Bureau d'Études Automatisé	Résidence Papa Oumar Sakho Dakar, Sénégal	Éch: 1/100 Pl. 136/137
	001 SYN — Synthèse — R+7	
Date: 06/05/2026	Réf: 1711	BIM vSYN-136 Phase: APD

001 SYN — Synthèse — R+8

LÉGENDE RÉSEAUX

- EF — Eau Froide
- EC — Eau Chaude
- EU — Eaux Usées
- CLIM — Réfrigérant
- VMC — Extraction
- HCU — Courants Forts
- LCU — Courants Faibles
- SPK — Sprinkler

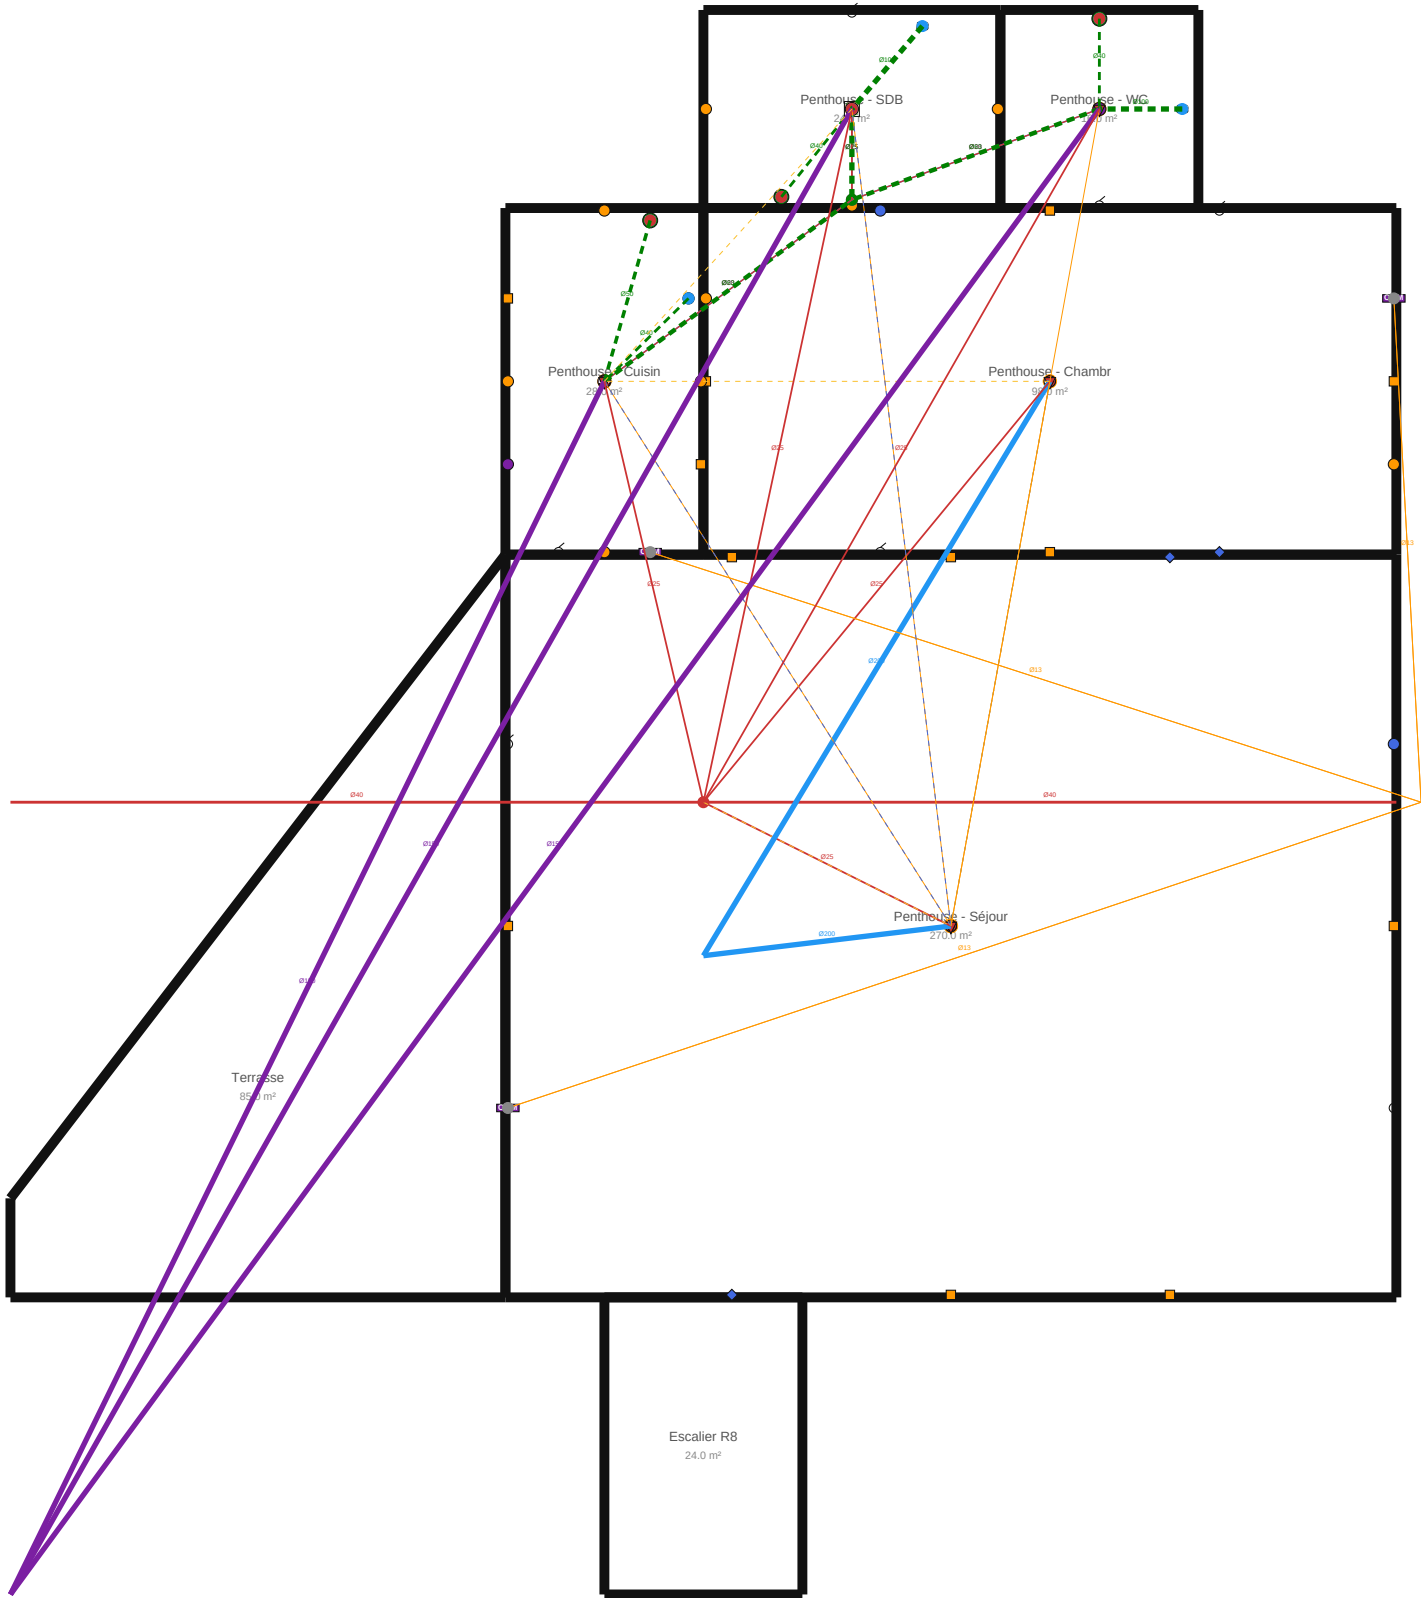

TIJAN AI Bureau d'Études Automatisé	Résidence Papa Oumar Sakho Dakar, Sénégal	Éch: 1/100 Pl. 137/137
	001 SYN — Synthèse — R+8	
Date: 06/05/2026	Réf: 1711	BIM vSYN-137 Phase: APD