



PLAN DE COFFRAGE — SOUS-SOL

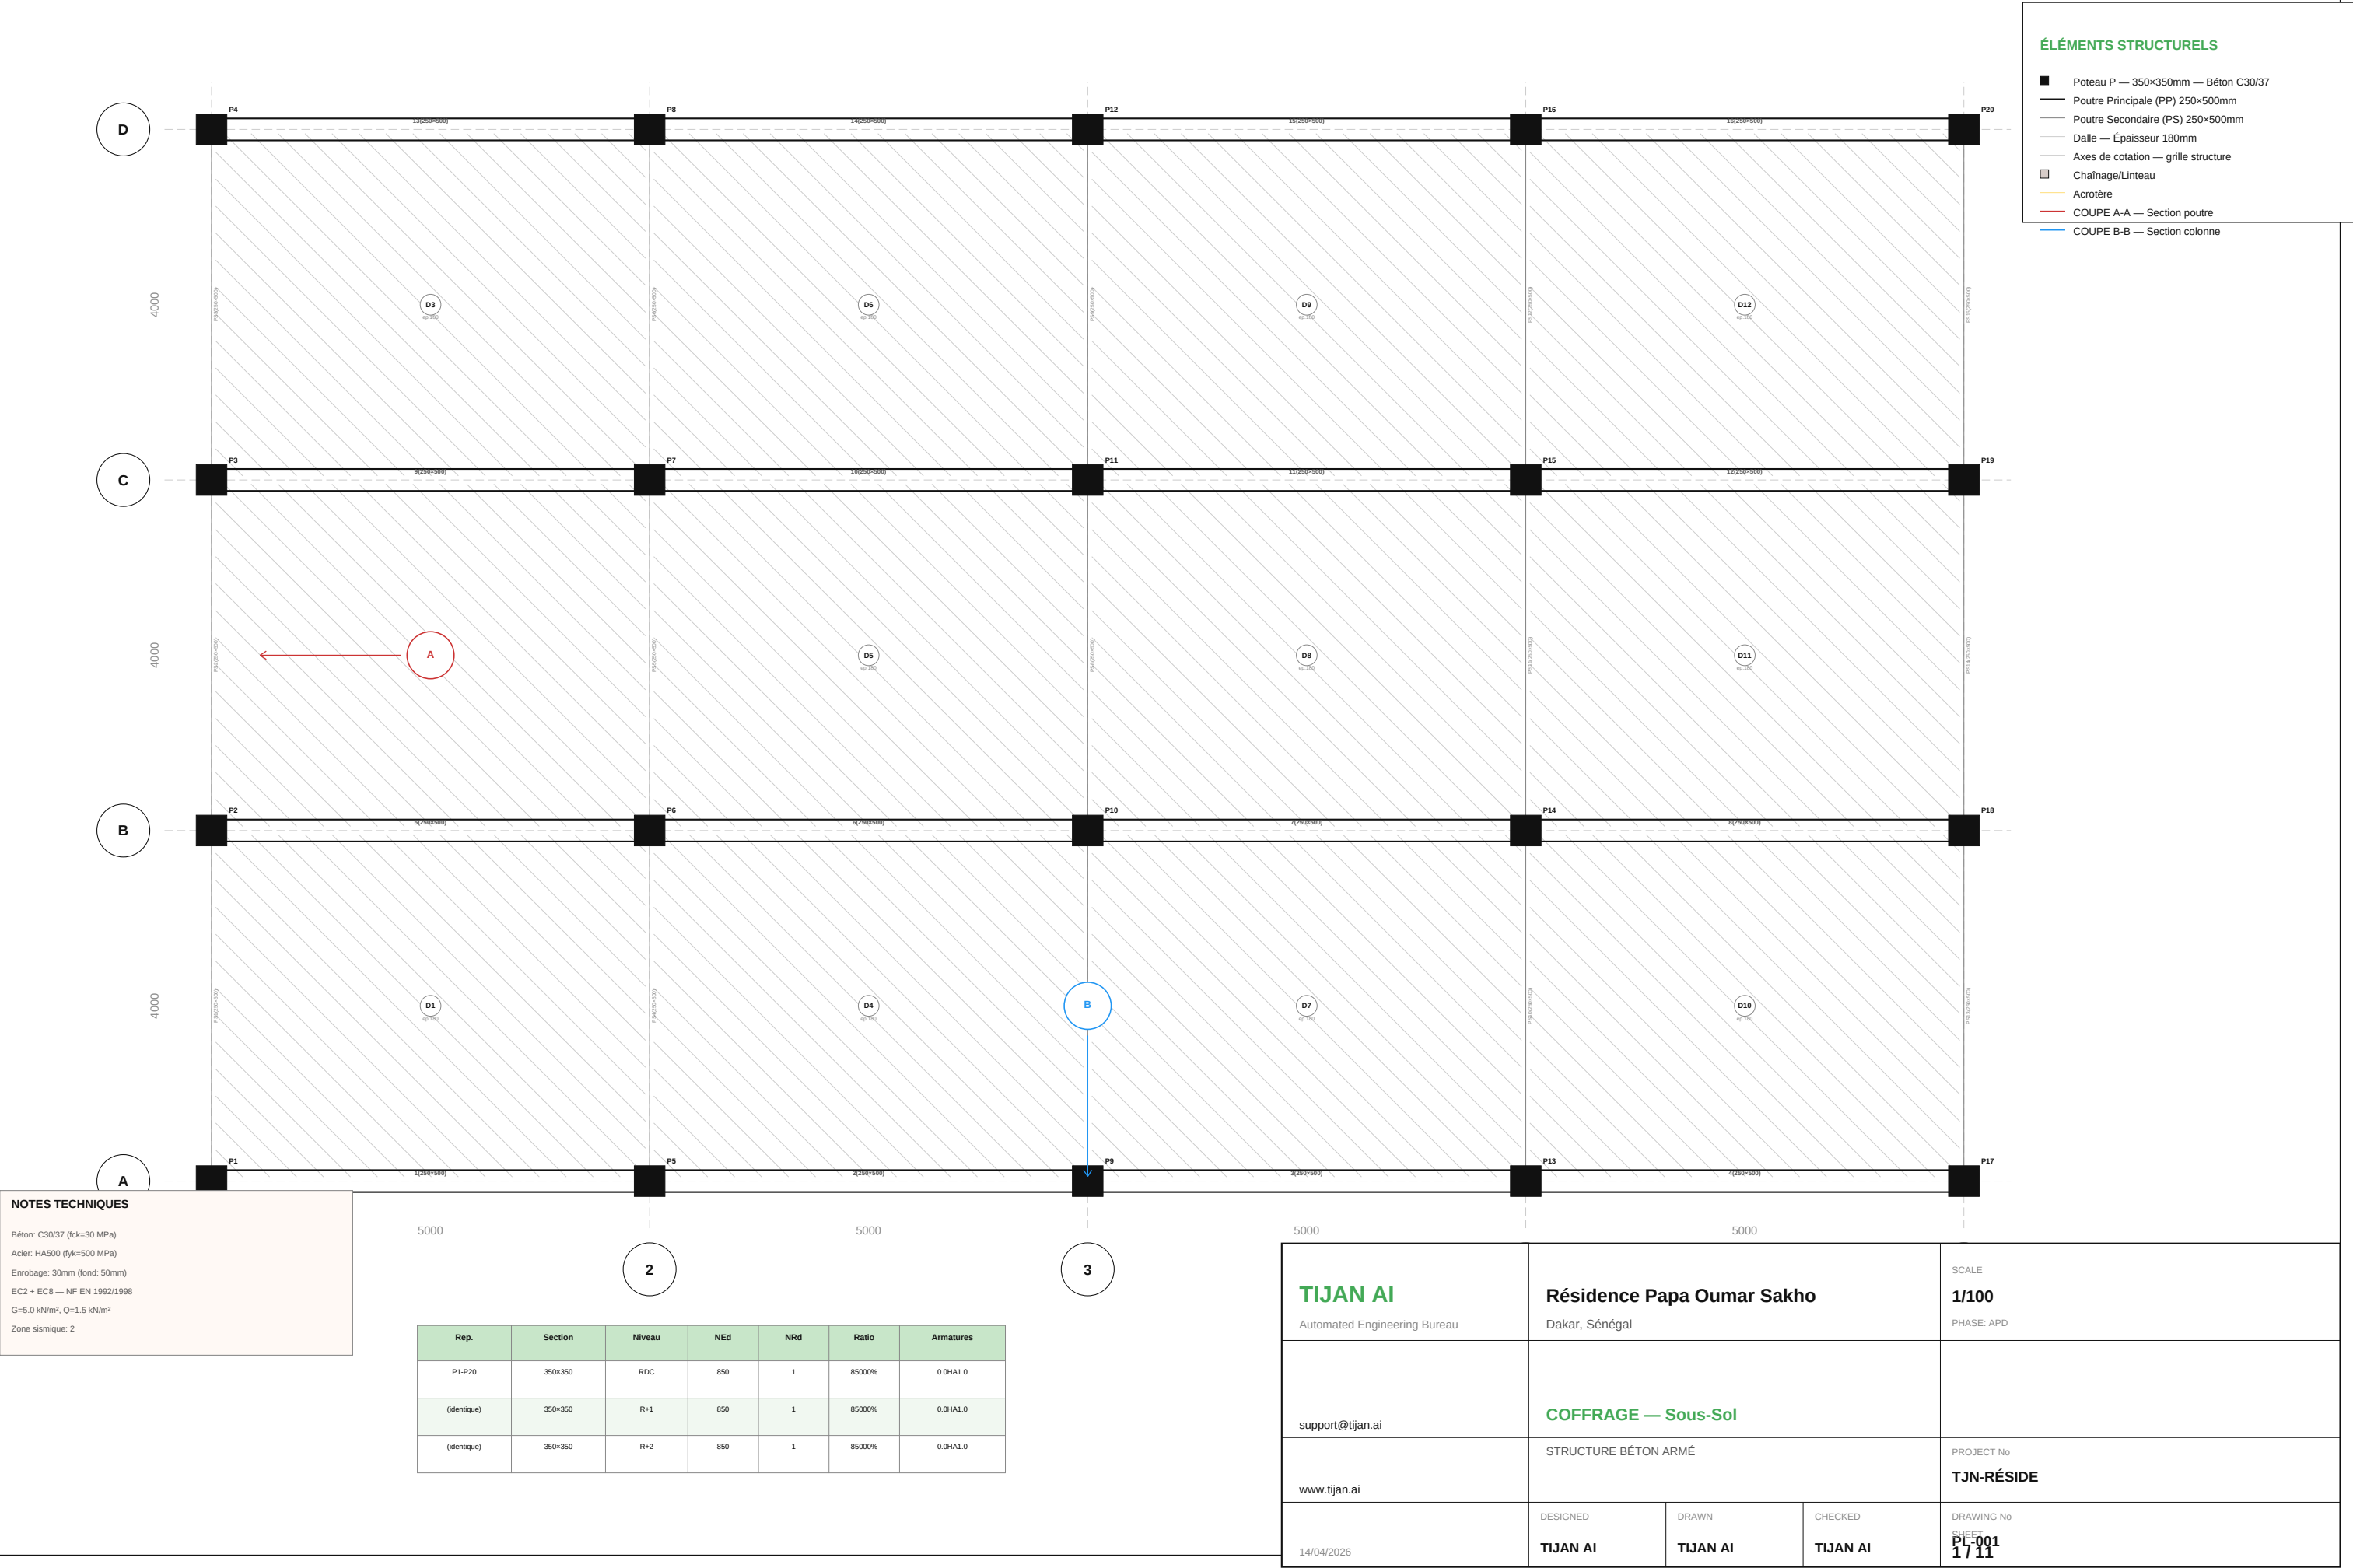

PLAN DE COFFRAGE — RDC

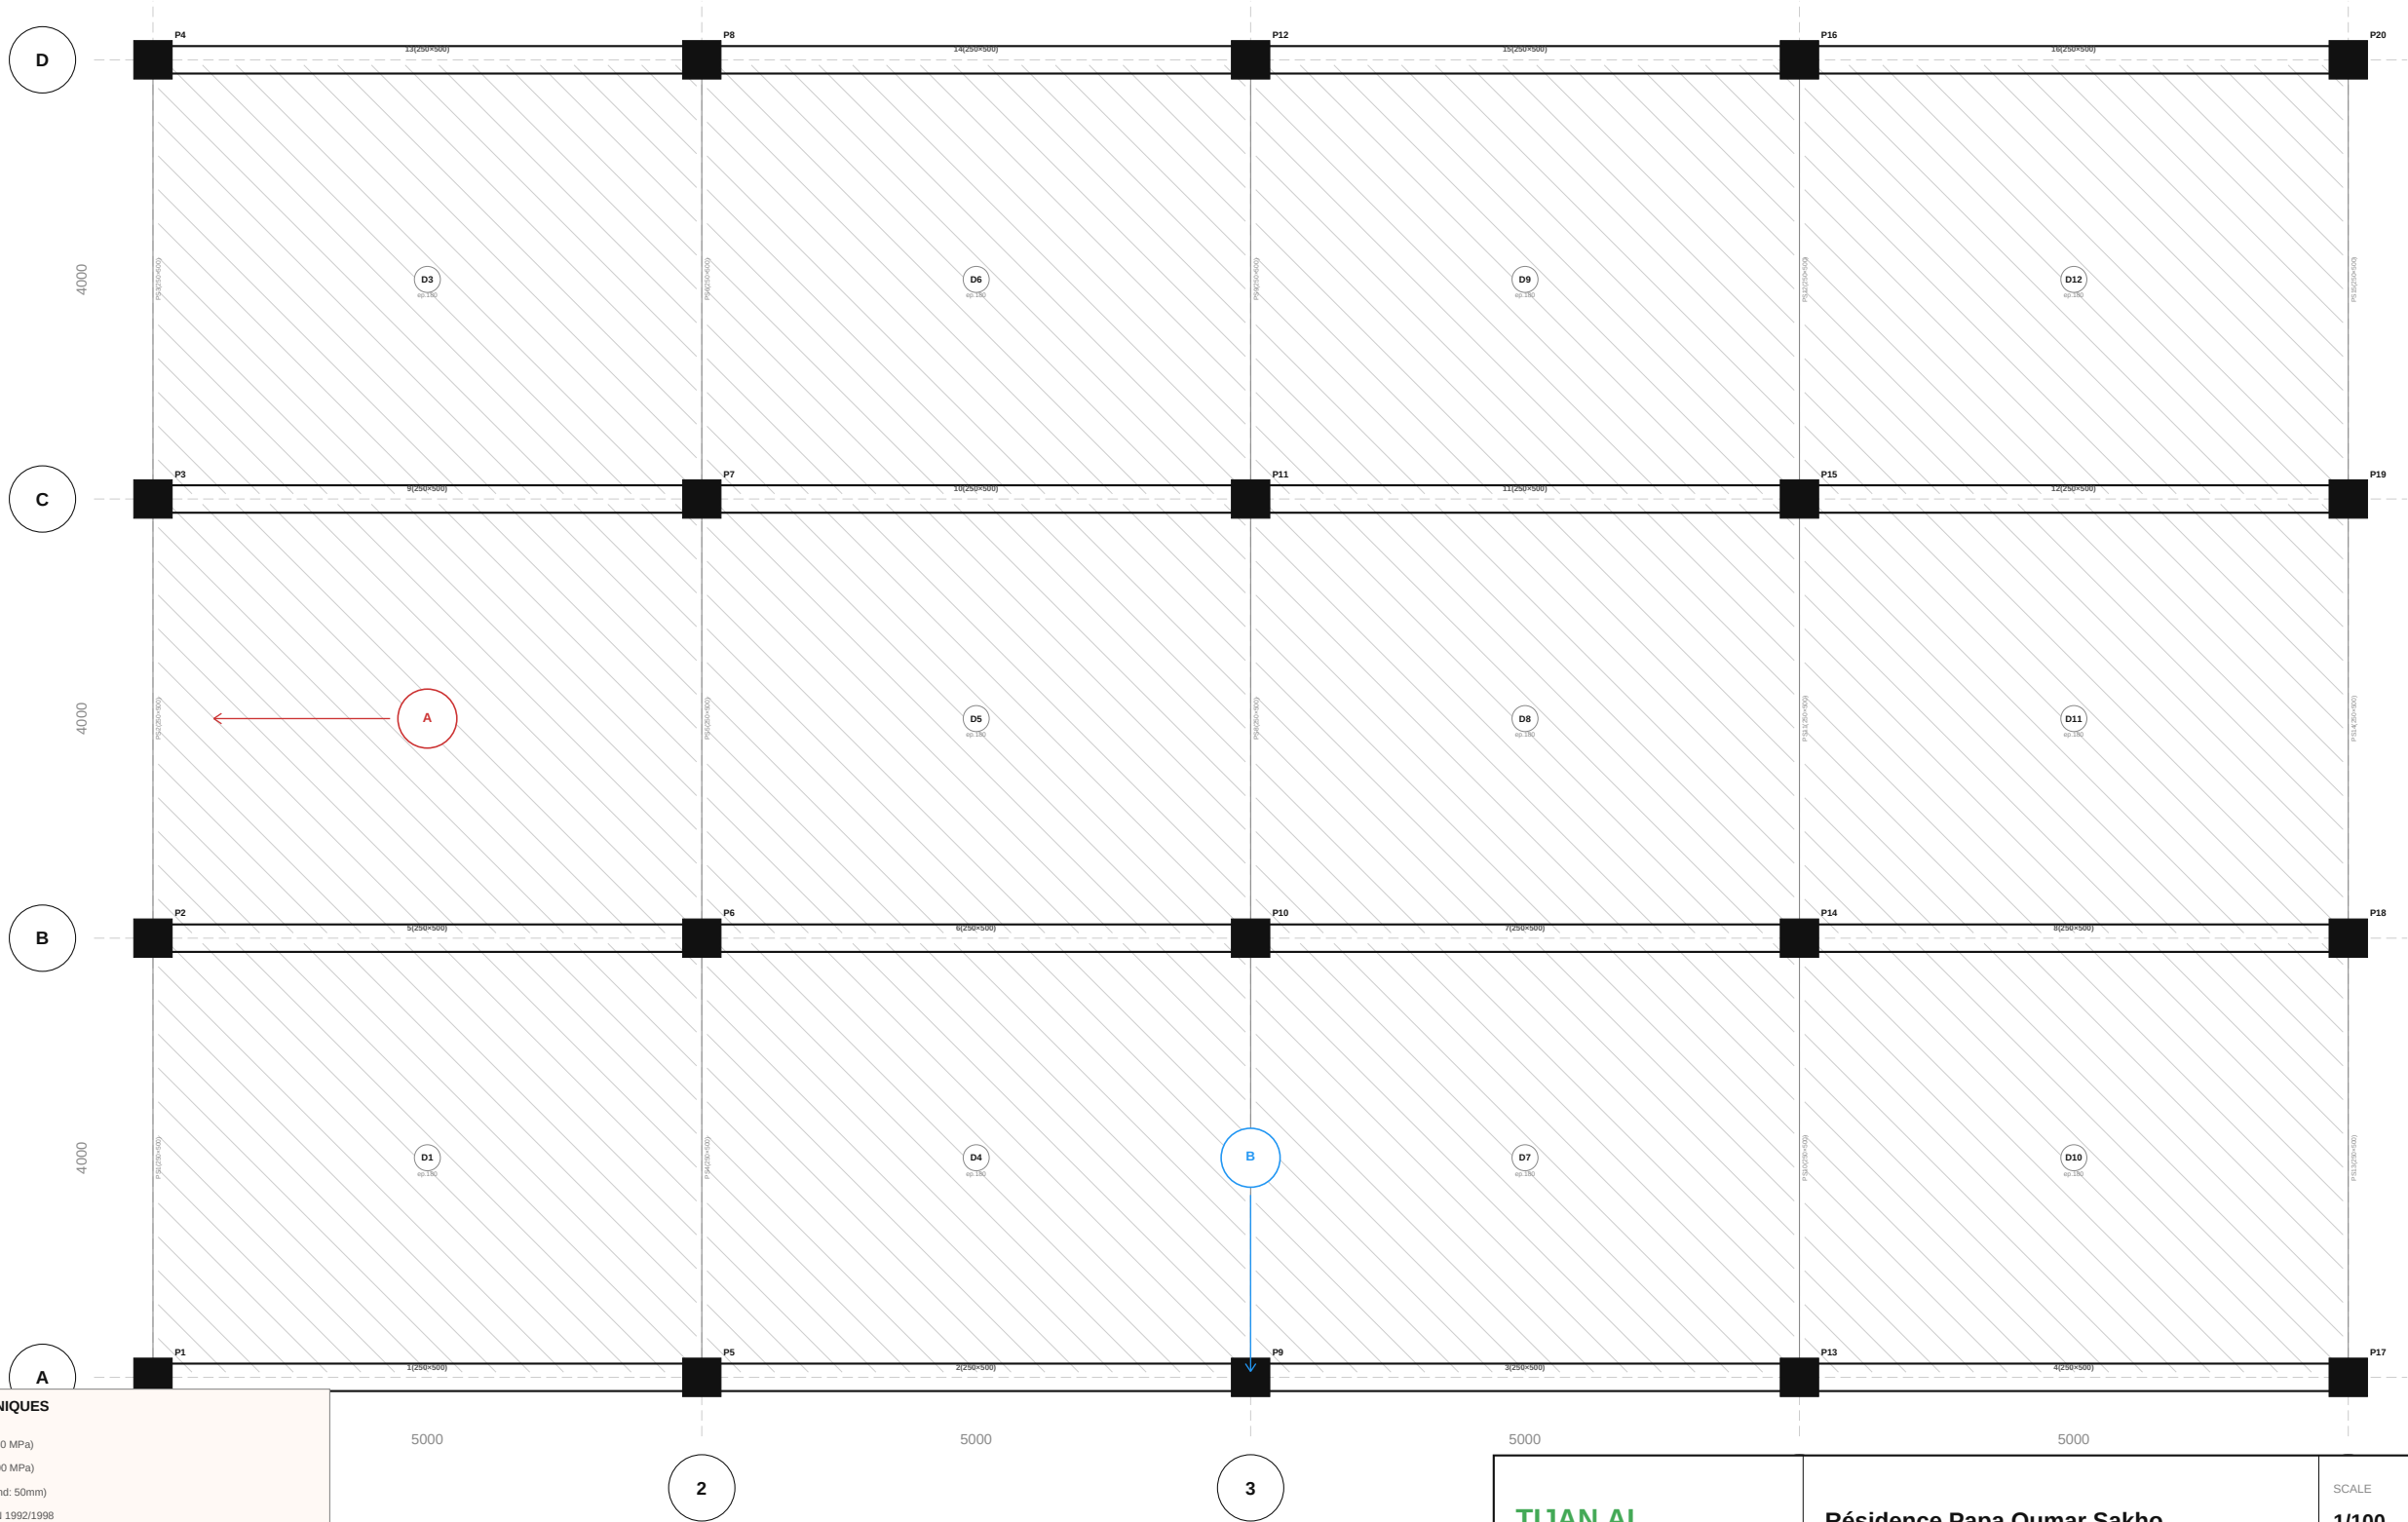

- ## ÉLÉMENTS STRUCTURELS
- Poteau P — 350×350mm — Béton C30/37
 - Poutre Principale (PP) 250×600mm
 - Poutre Secondaire (PS) 250×500mm
 - Dalle — Épaisseur 180mm
 - Axes de cotation — grille structure
 - Chainage/Linteau
 - Acrotère
 - COUPE A-A — Section poutre
 - COUPE B-B — Section colonne

NOTES TECHNIQUES

Béton: C30/37 ($f_{ck}=30$ MPa)

Acier: HA500 ($f_{yk}=500$ MPa)

Enrobage: 30mm (fond: 50mm)

EC2 + EC8 — NF EN 1992/1998


$G=5.0$ kN/m², $Q=1.5$ kN/m²

Zone sismique: 2


Rep.	Section	Niveau	Ned	Nrd	Ratio	Armatures
P1-P20	350x350	RDC	850	1	85000%	0.0x11.0
(identique)	350x350	R+1	850	1	85000%	0.0x11.0
(identique)	350x350	R+2	850	1	85000%	0.0x11.0

TIJAN AI Automated Engineering Bureau		Résidence Papa Oumar Sakho Dakar, Sénégal		SCALE 1/100 PHASE: APD
support@tjan.ai		COFFRAGE — RDC		
www.tjan.ai		STRUCTURE BÉTON ARMÉ		PROJECT No TJN-RÉSIDE
14/04/2026	DESIGNED TIJAN AI	DRAWN TIJAN AI	CHECKED TIJAN AI	DRAWING No PL-002 SHEET 27/11

PLAN DE COFFRAGE — ÉTAGE COURANT

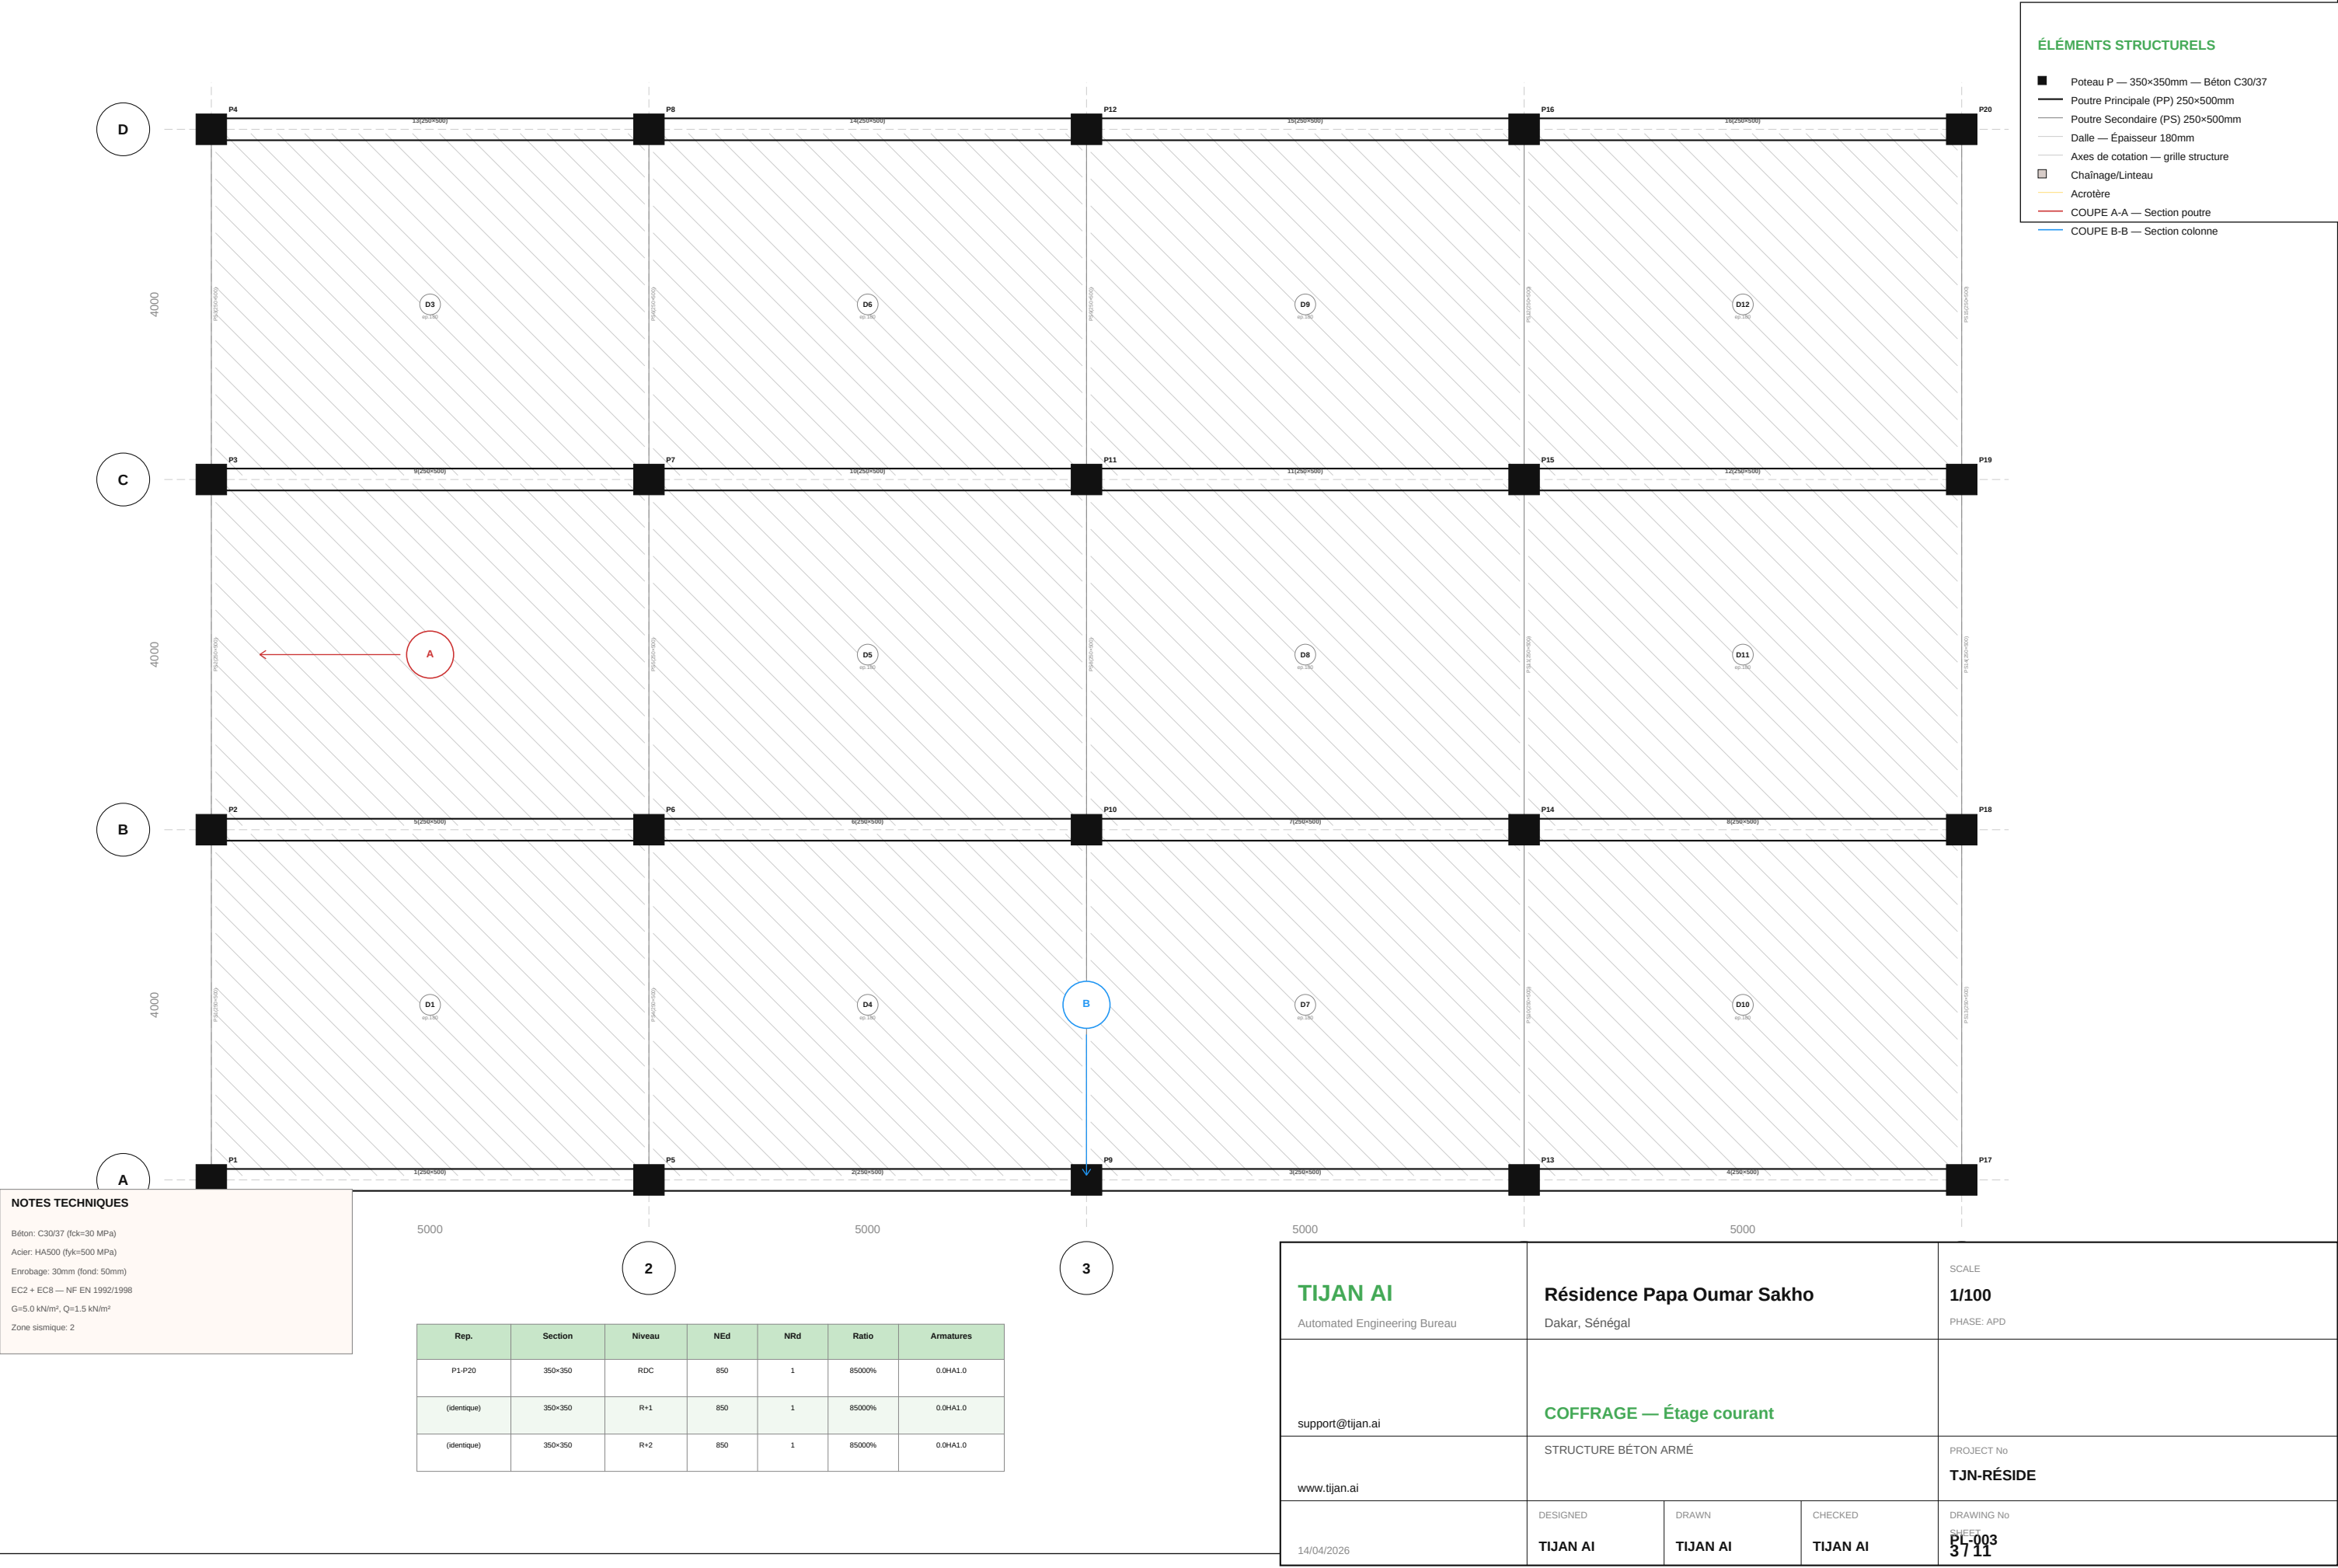

PLAN DE COFFRAGE — TERRASSE

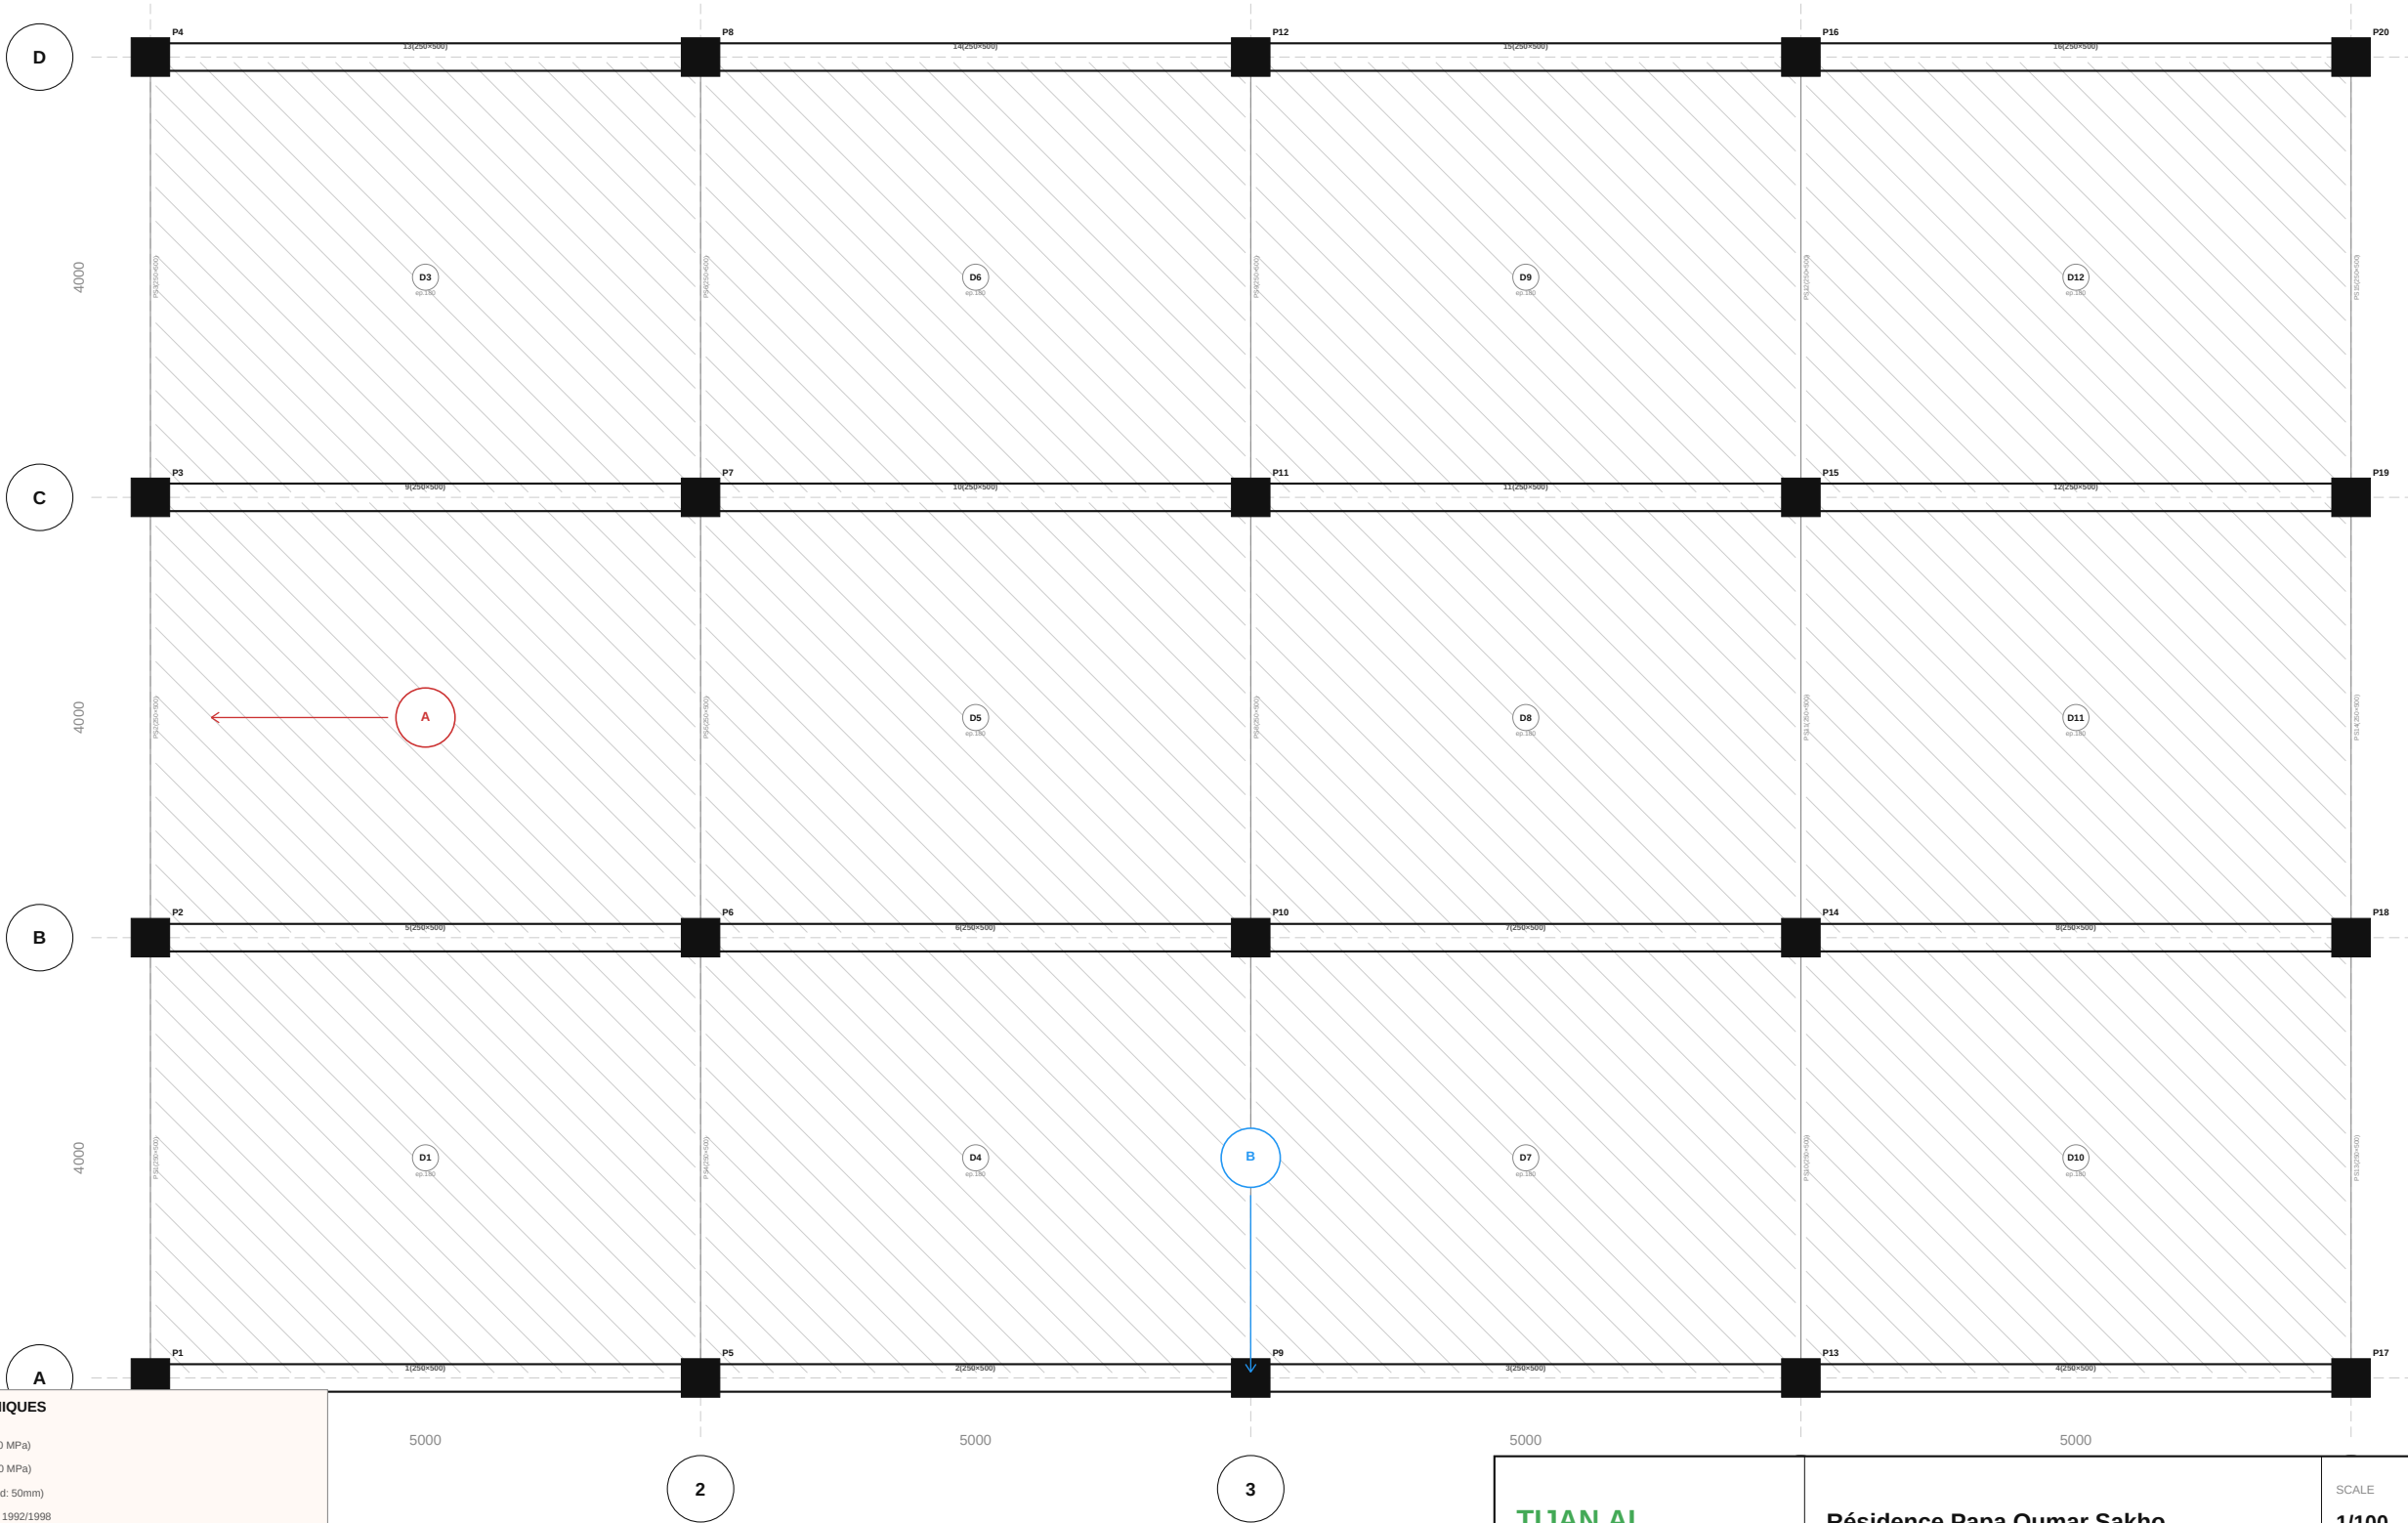

ÉLÉMENTS STRUCTURELS

■

Poteau P — 350×350mm — Béton C30/37

—

Poutre Principale (PP) 250×500mm

—

Poutre Secondaire (PS) 250×500mm

—

Dalle — Épaisseur 180mm

—

Axes de cotation — grille structure

▤

Chainage/Linteau

—

Acrotère

—

COUPE A-A — Section poutre

—

COUPE B-B — Section colonne

NOTES TECHNIQUES

Béton: C30/37 (fck=30 MPa)

Acier: HA500 (fyk=500 MPa)

Enrobage: 30mm (fond: 50mm)

EC2 + EC8 — NF EN 1992/1998

G=5.0 kN/m², Q=1.5 kN/m²

Zone sismique: 2

Rep.	Section	Niveau	NEd	NRd	Ratio	Armatures
P1-P20	350×350	RDC	850	1	85000%	0.0HA1.0
(identique)	350×350	R+1	850	1	85000%	0.0HA1.0
(identique)	350×350	R+2	850	1	85000%	0.0HA1.0

TIJAN AI

Automated Engineering Bureau

support@tijan.ai

www.tijan.ai

14/04/2026

Résidence Papa Oumar Sakho

Dakar, Sénégal

COFFRAGE — Terrasse

STRUCTURE BÉTON ARMÉ

DESIGNED

TIJAN AI

DRAWN

TIJAN AI

CHECKED

TIJAN AI

SCALE

1/100

PHASE: APD


PROJECT No

TJN-RÉSIDE

DRAWING No

SHEET
PL-004
47/11

FERRAILLAGE INFÉRIEUR DALLE — PH NIVEAU COURANT

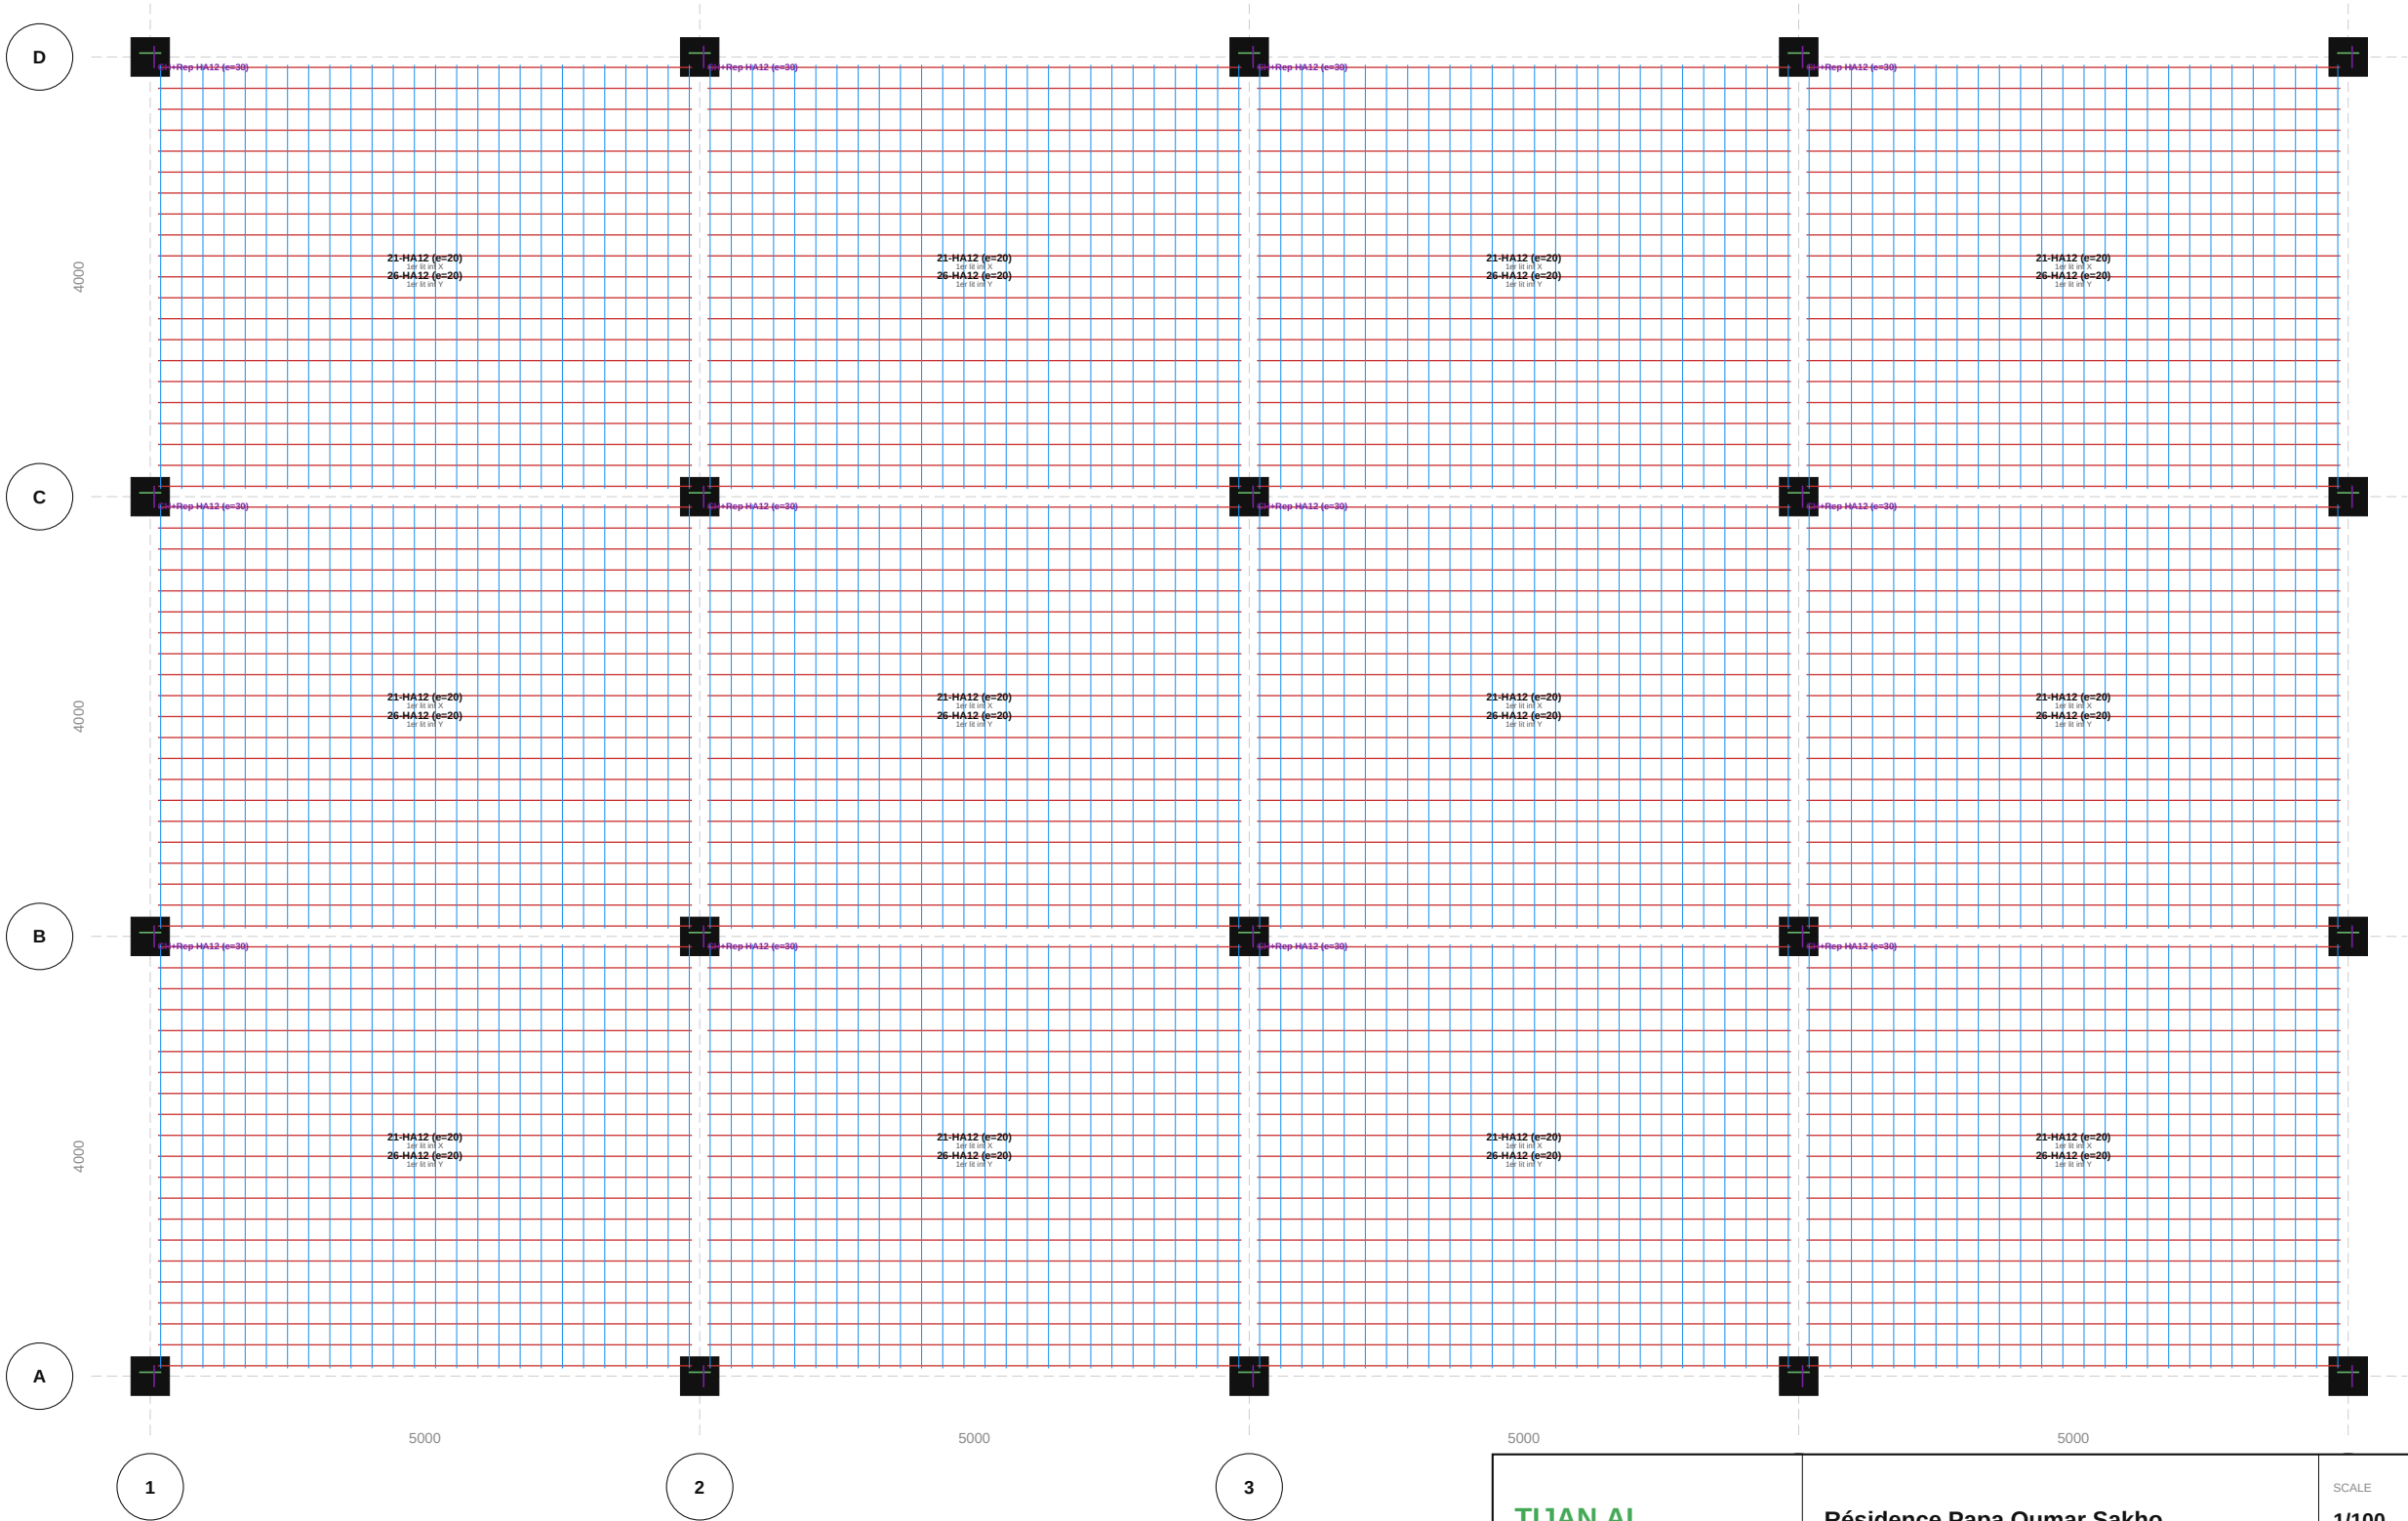

FERRAILLAGE INFÉRIEUR

1er lit inf. X — HA12 esp.20 (As=3.50 cm²/ml)

1er lit inf. Y — HA12 esp.20 (As=3.00 cm²/ml)


2e lit inf. — Renforts locaux en zone de moment max.

Poteau 350×350mm

Repères armatures (cf. nomenclature bas de planche)

TIJAN AI Automated Engineering Bureau support@tijan.ai www.tijan.ai 14/04/2026	Résidence Papa Oumar Sakho Dakar, Sénégal			SCALE 1/100 PHASE: APD
	FERRAILLAGE INF. DALLE			
LOT 01 — STRUCTURE / FERRAILLAGE B.A.			PROJECT No TJN-RÉSIDE	
DESIGNED TIJAN AI		DRAWN TIJAN AI	CHECKED TIJAN AI	DRAWING No TJN-STR-FER-INF-005 5 / 11

FERRAILLAGE SUPÉRIEUR DALLE — PH NIVEAU COURANT

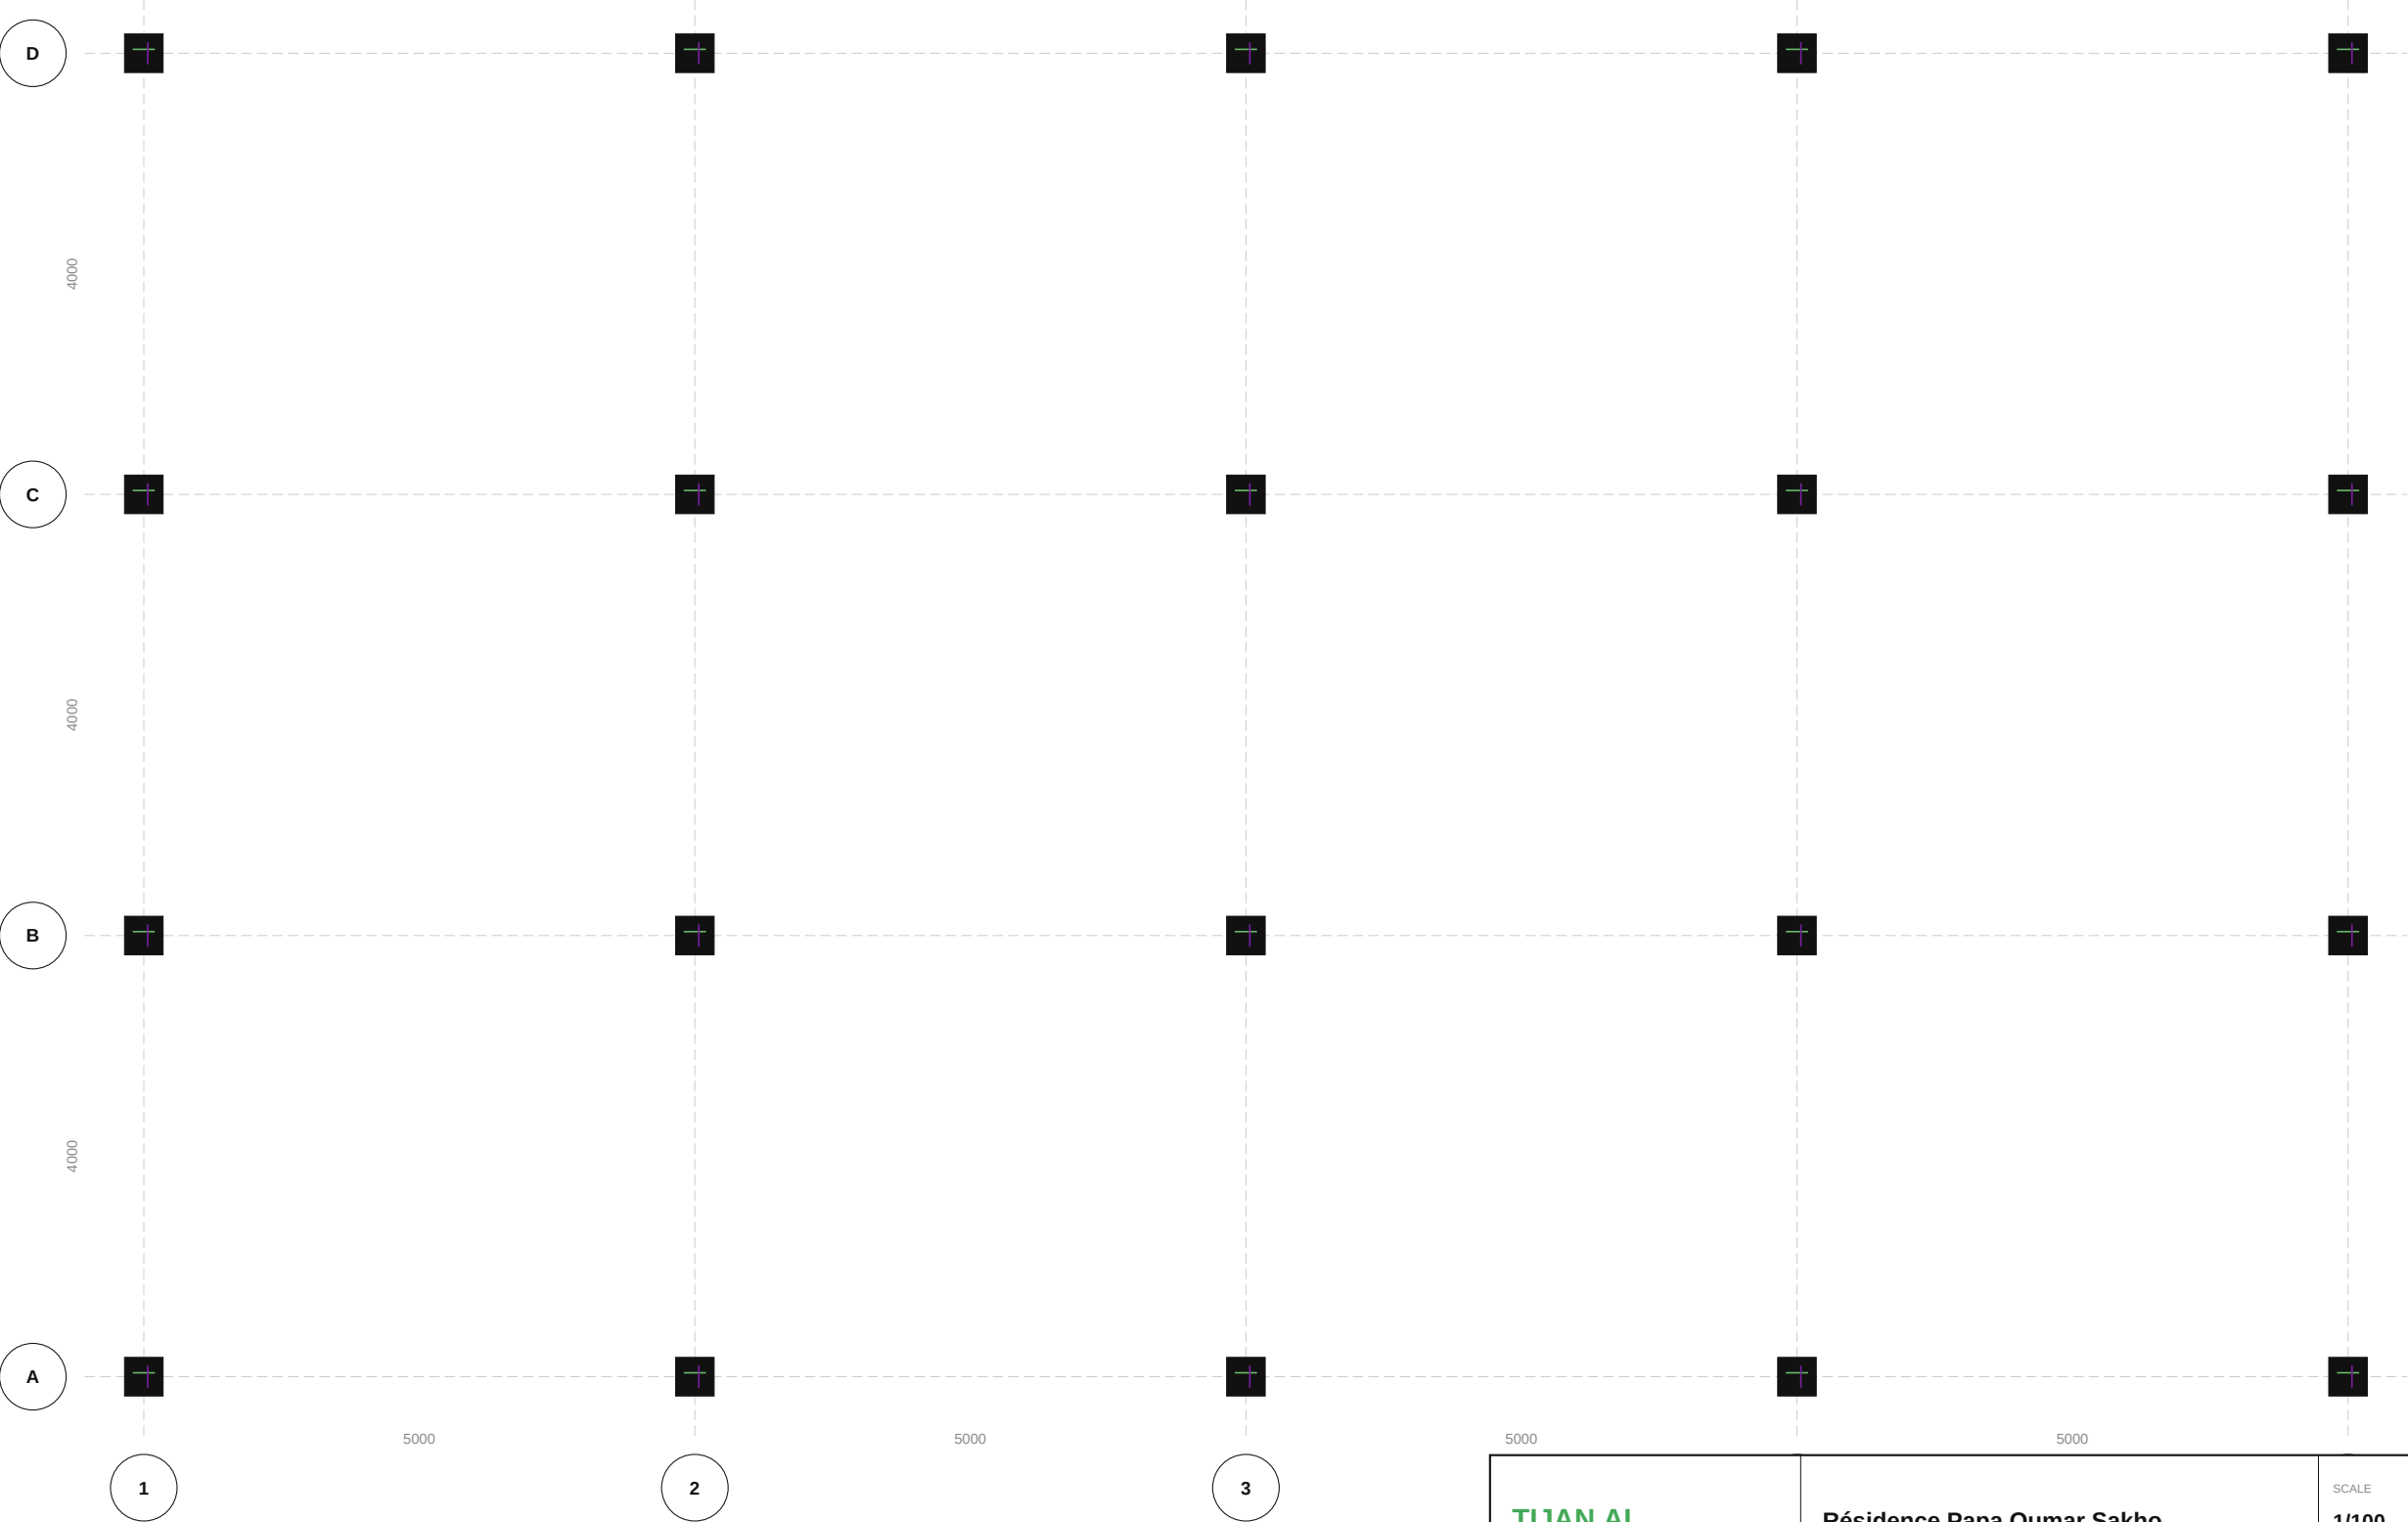

TIJAN AI

Automated Engineering Bureau

Résidence Papa Oumar Sakho

Dakar, Sénégal

SCALE

1/100

PHASE: APD

support@tijan.ai

FERRAILLAGE SUP. DALLE

www.tijan.ai

LOT 01 — STRUCTURE / FERRAILLAGE B.A.

PROJECT No

TJN-RÉSIDE

14/04/2026

DESIGNED

TIJAN AI

DRAWN

TIJAN AI


CHECKED

TIJAN AI

DRAWING No


TJN-STR-FER-SUP-006
6 / 11

COUPE TYPE DALLE — DÉTAIL FERRAILLAGE A-A

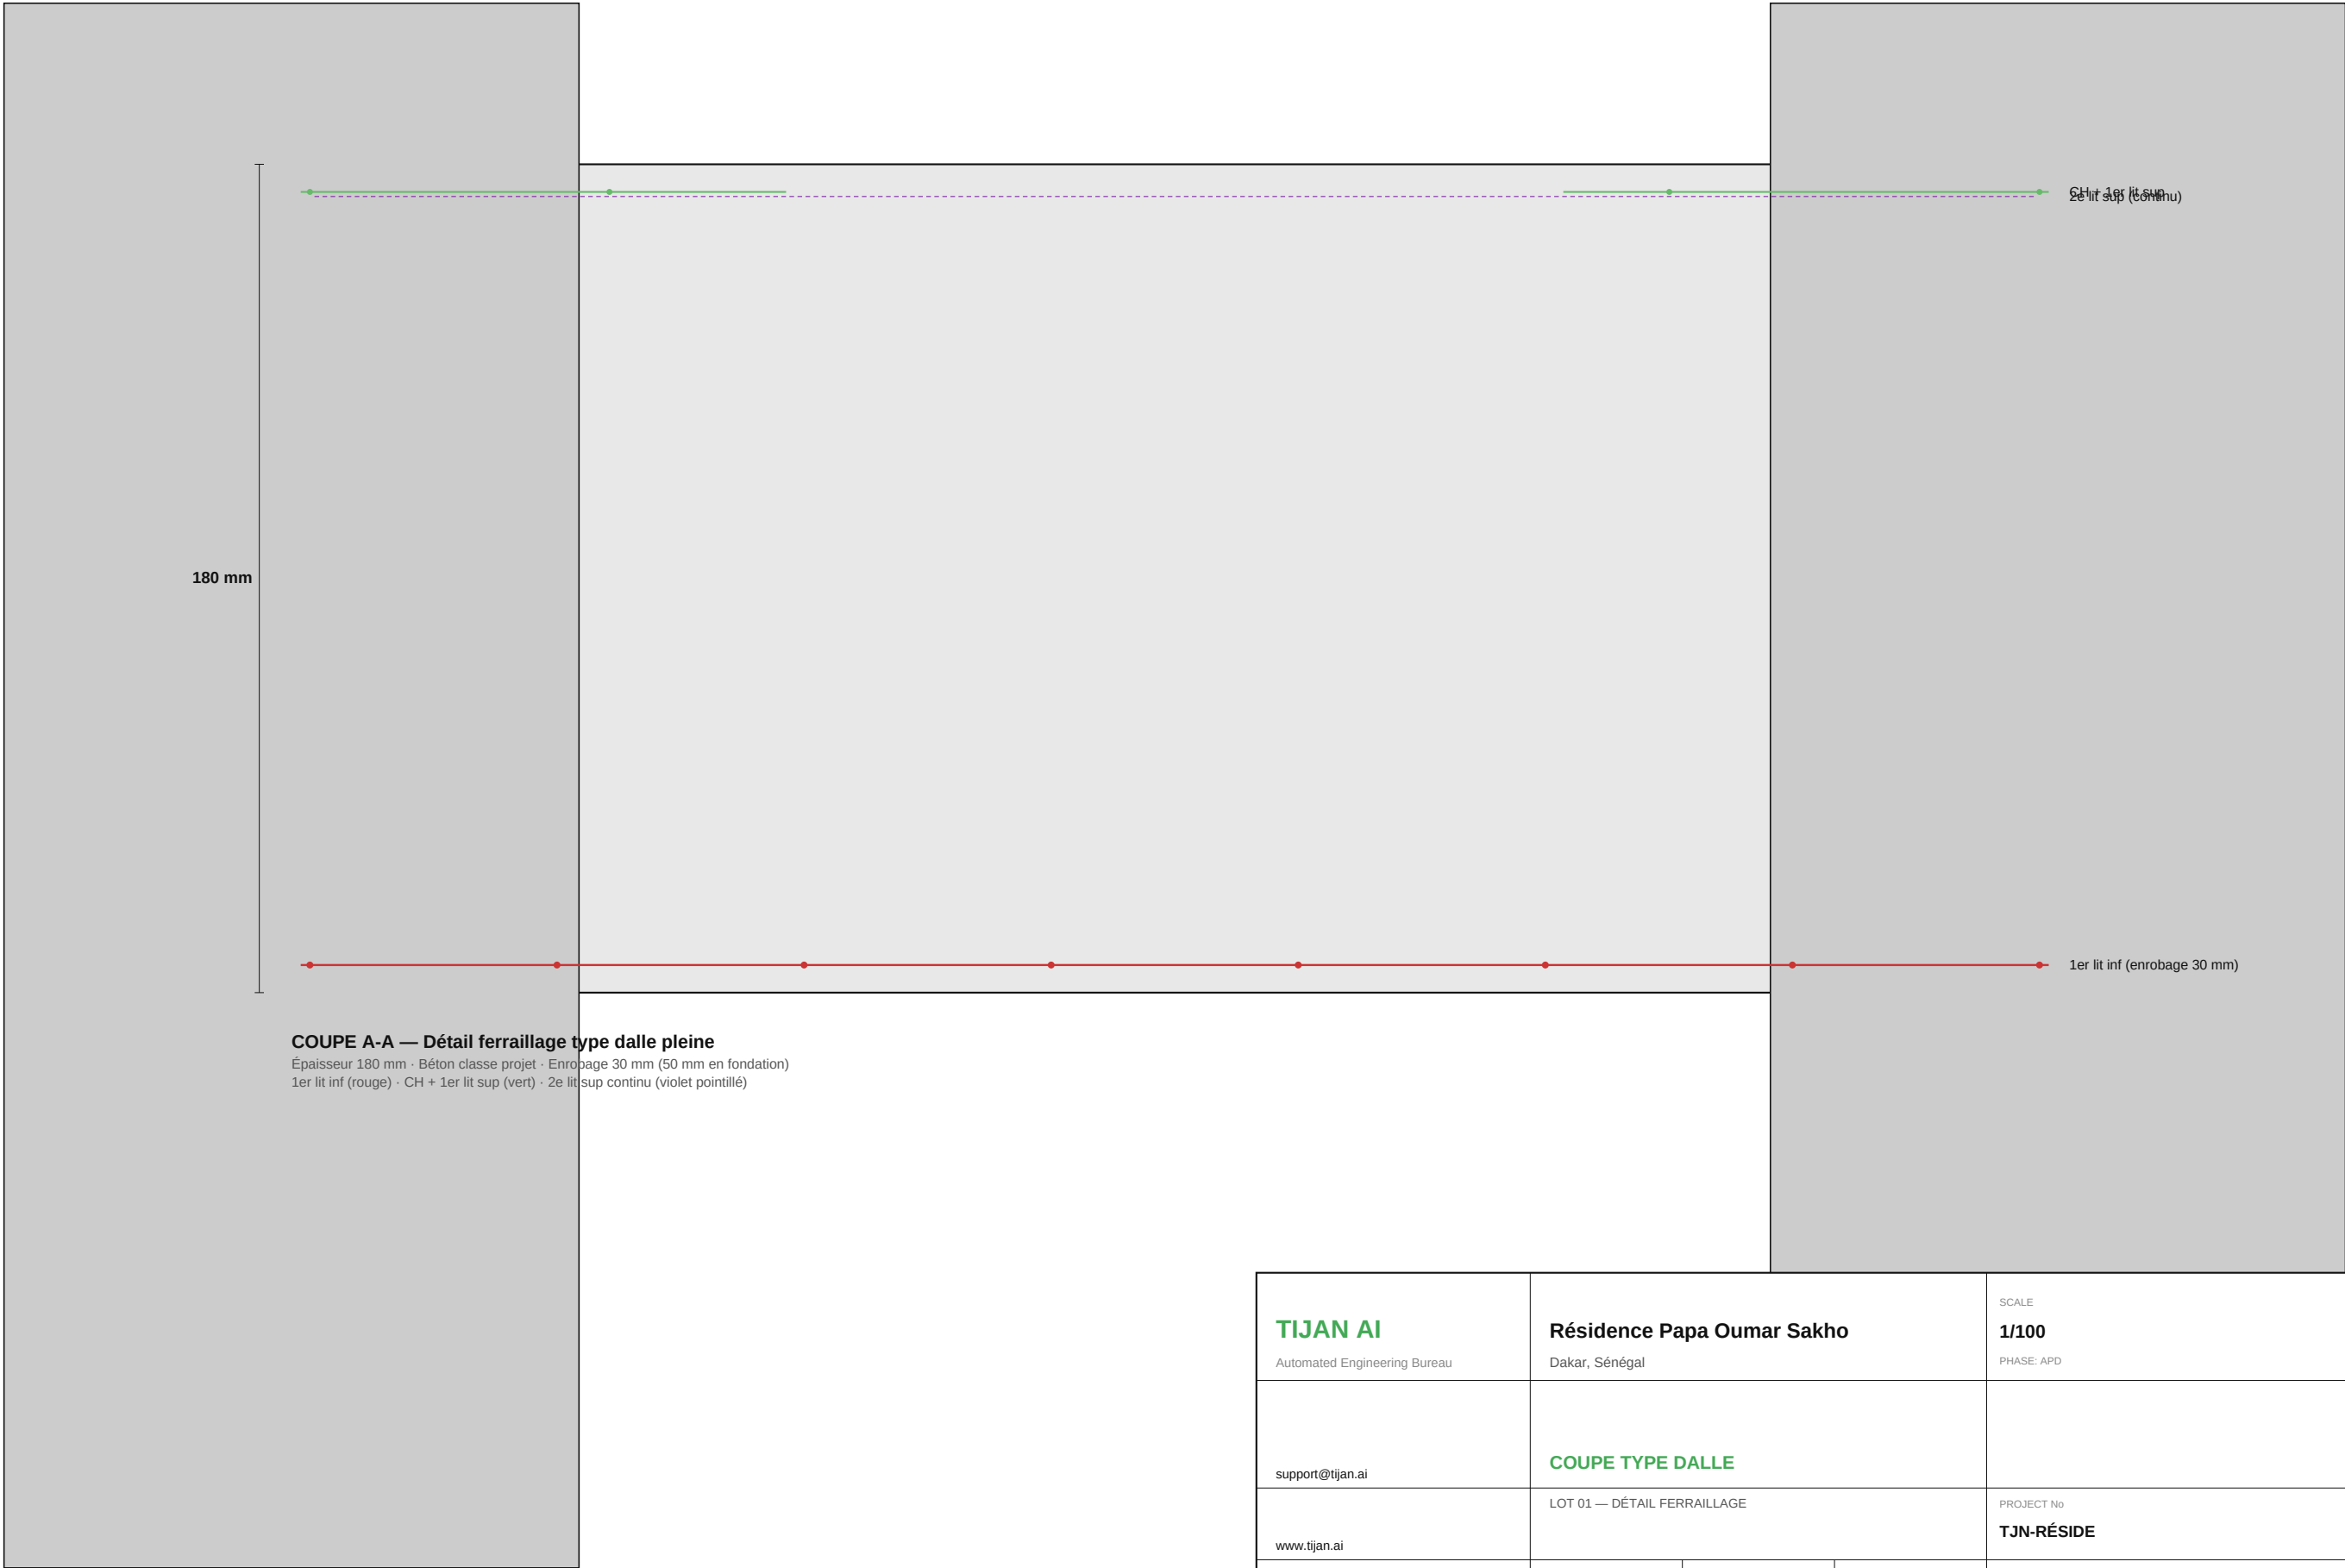

TIJAN AI Automated Engineering Bureau	Résidence Papa Oumar Sakho Dakar, Sénégal			SCALE 1/100 PHASE: APD
support@tijan.ai	COUPE TYPE DALLE			
www.tijan.ai	LOT 01 — DÉTAIL FERRAILLAGE			PROJECT No TJN-RÉSIDE
14/04/2026	DESIGNED TIJAN AI	DRAWN TIJAN AI	CHECKED TIJAN AI	DRAWING No TJN-STR-COUP-007 SHEET 7 / 11


PLAN DE FONDATIONS

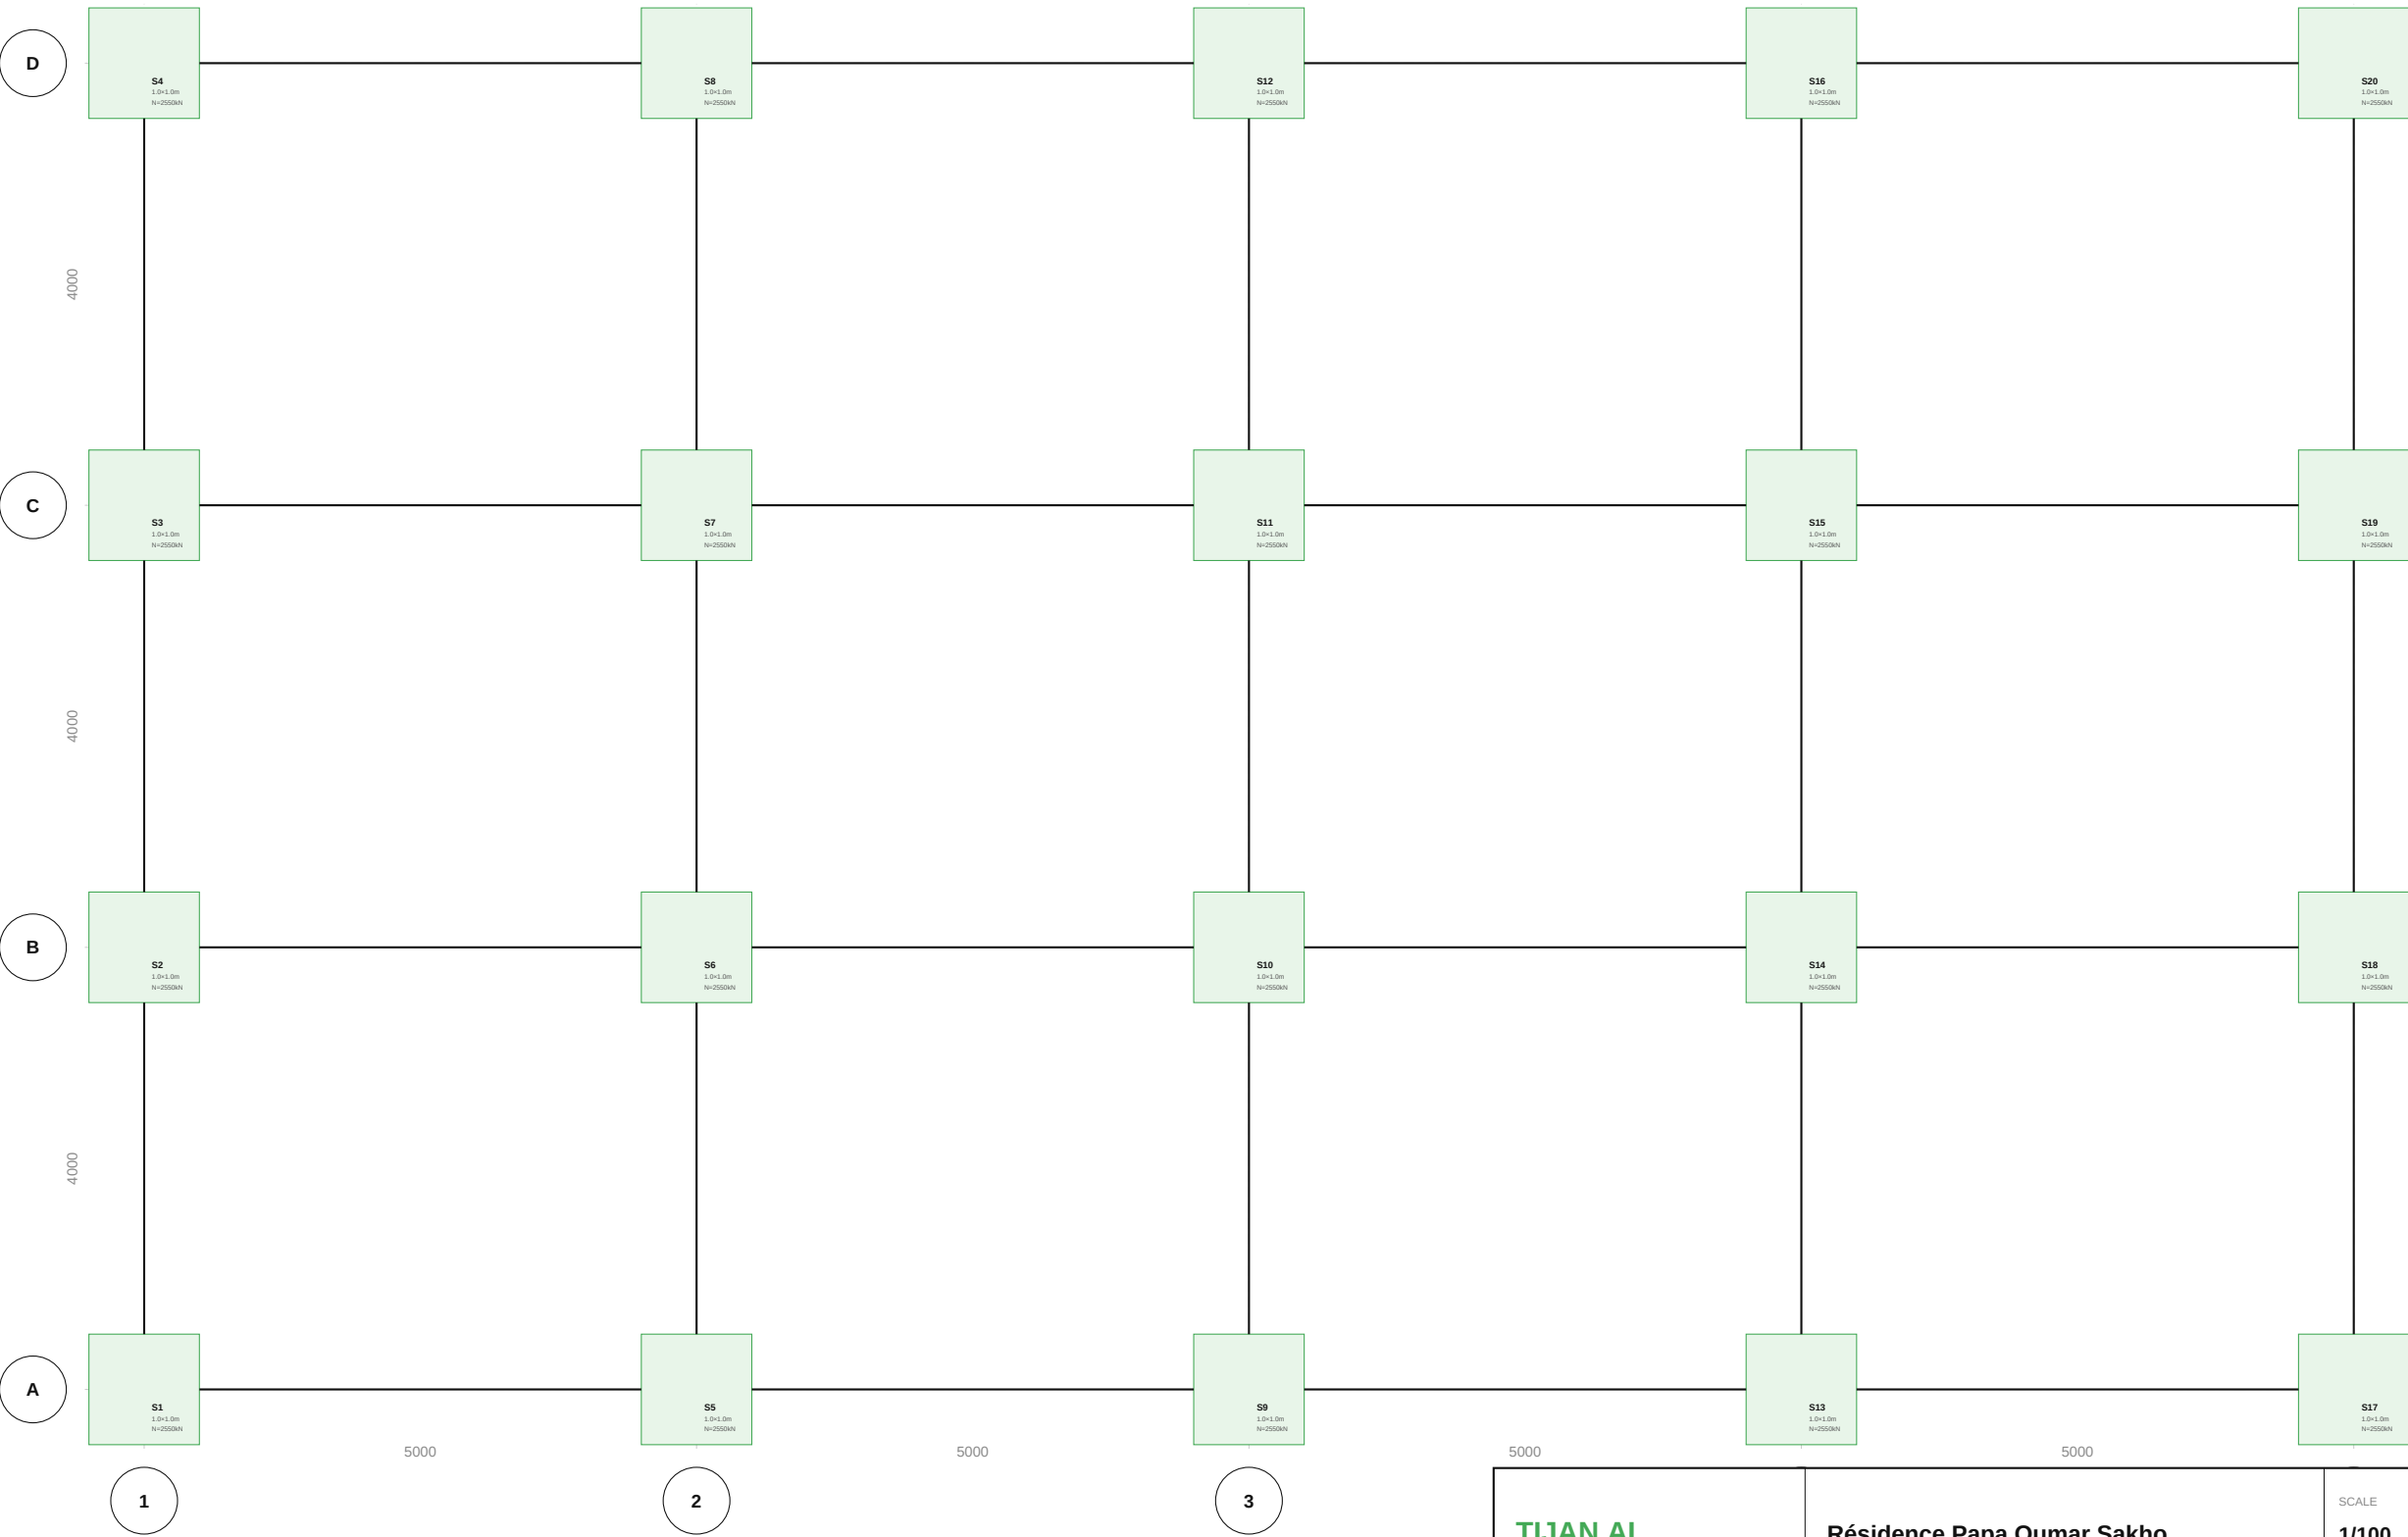

Semelle Isolee — prof.1.5m — σ_{sol} =0.25MPa — C30/37

TIJAN AI Automated Engineering Bureau support@tijan.ai www.tijan.ai 14/04/2026	Résidence Papa Oumar Sakho			SCALE 1/100 PHASE: APD
	FONDATIONS			
	FONDATIONS STRUCTURE			PROJECT No TJN-RÉSIDE
	DESIGNED TIJAN AI	DRAWN TIJAN AI	CHECKED TIJAN AI	DRAWING No SHEET PL-008 8711

COUPE GÉNÉRALE

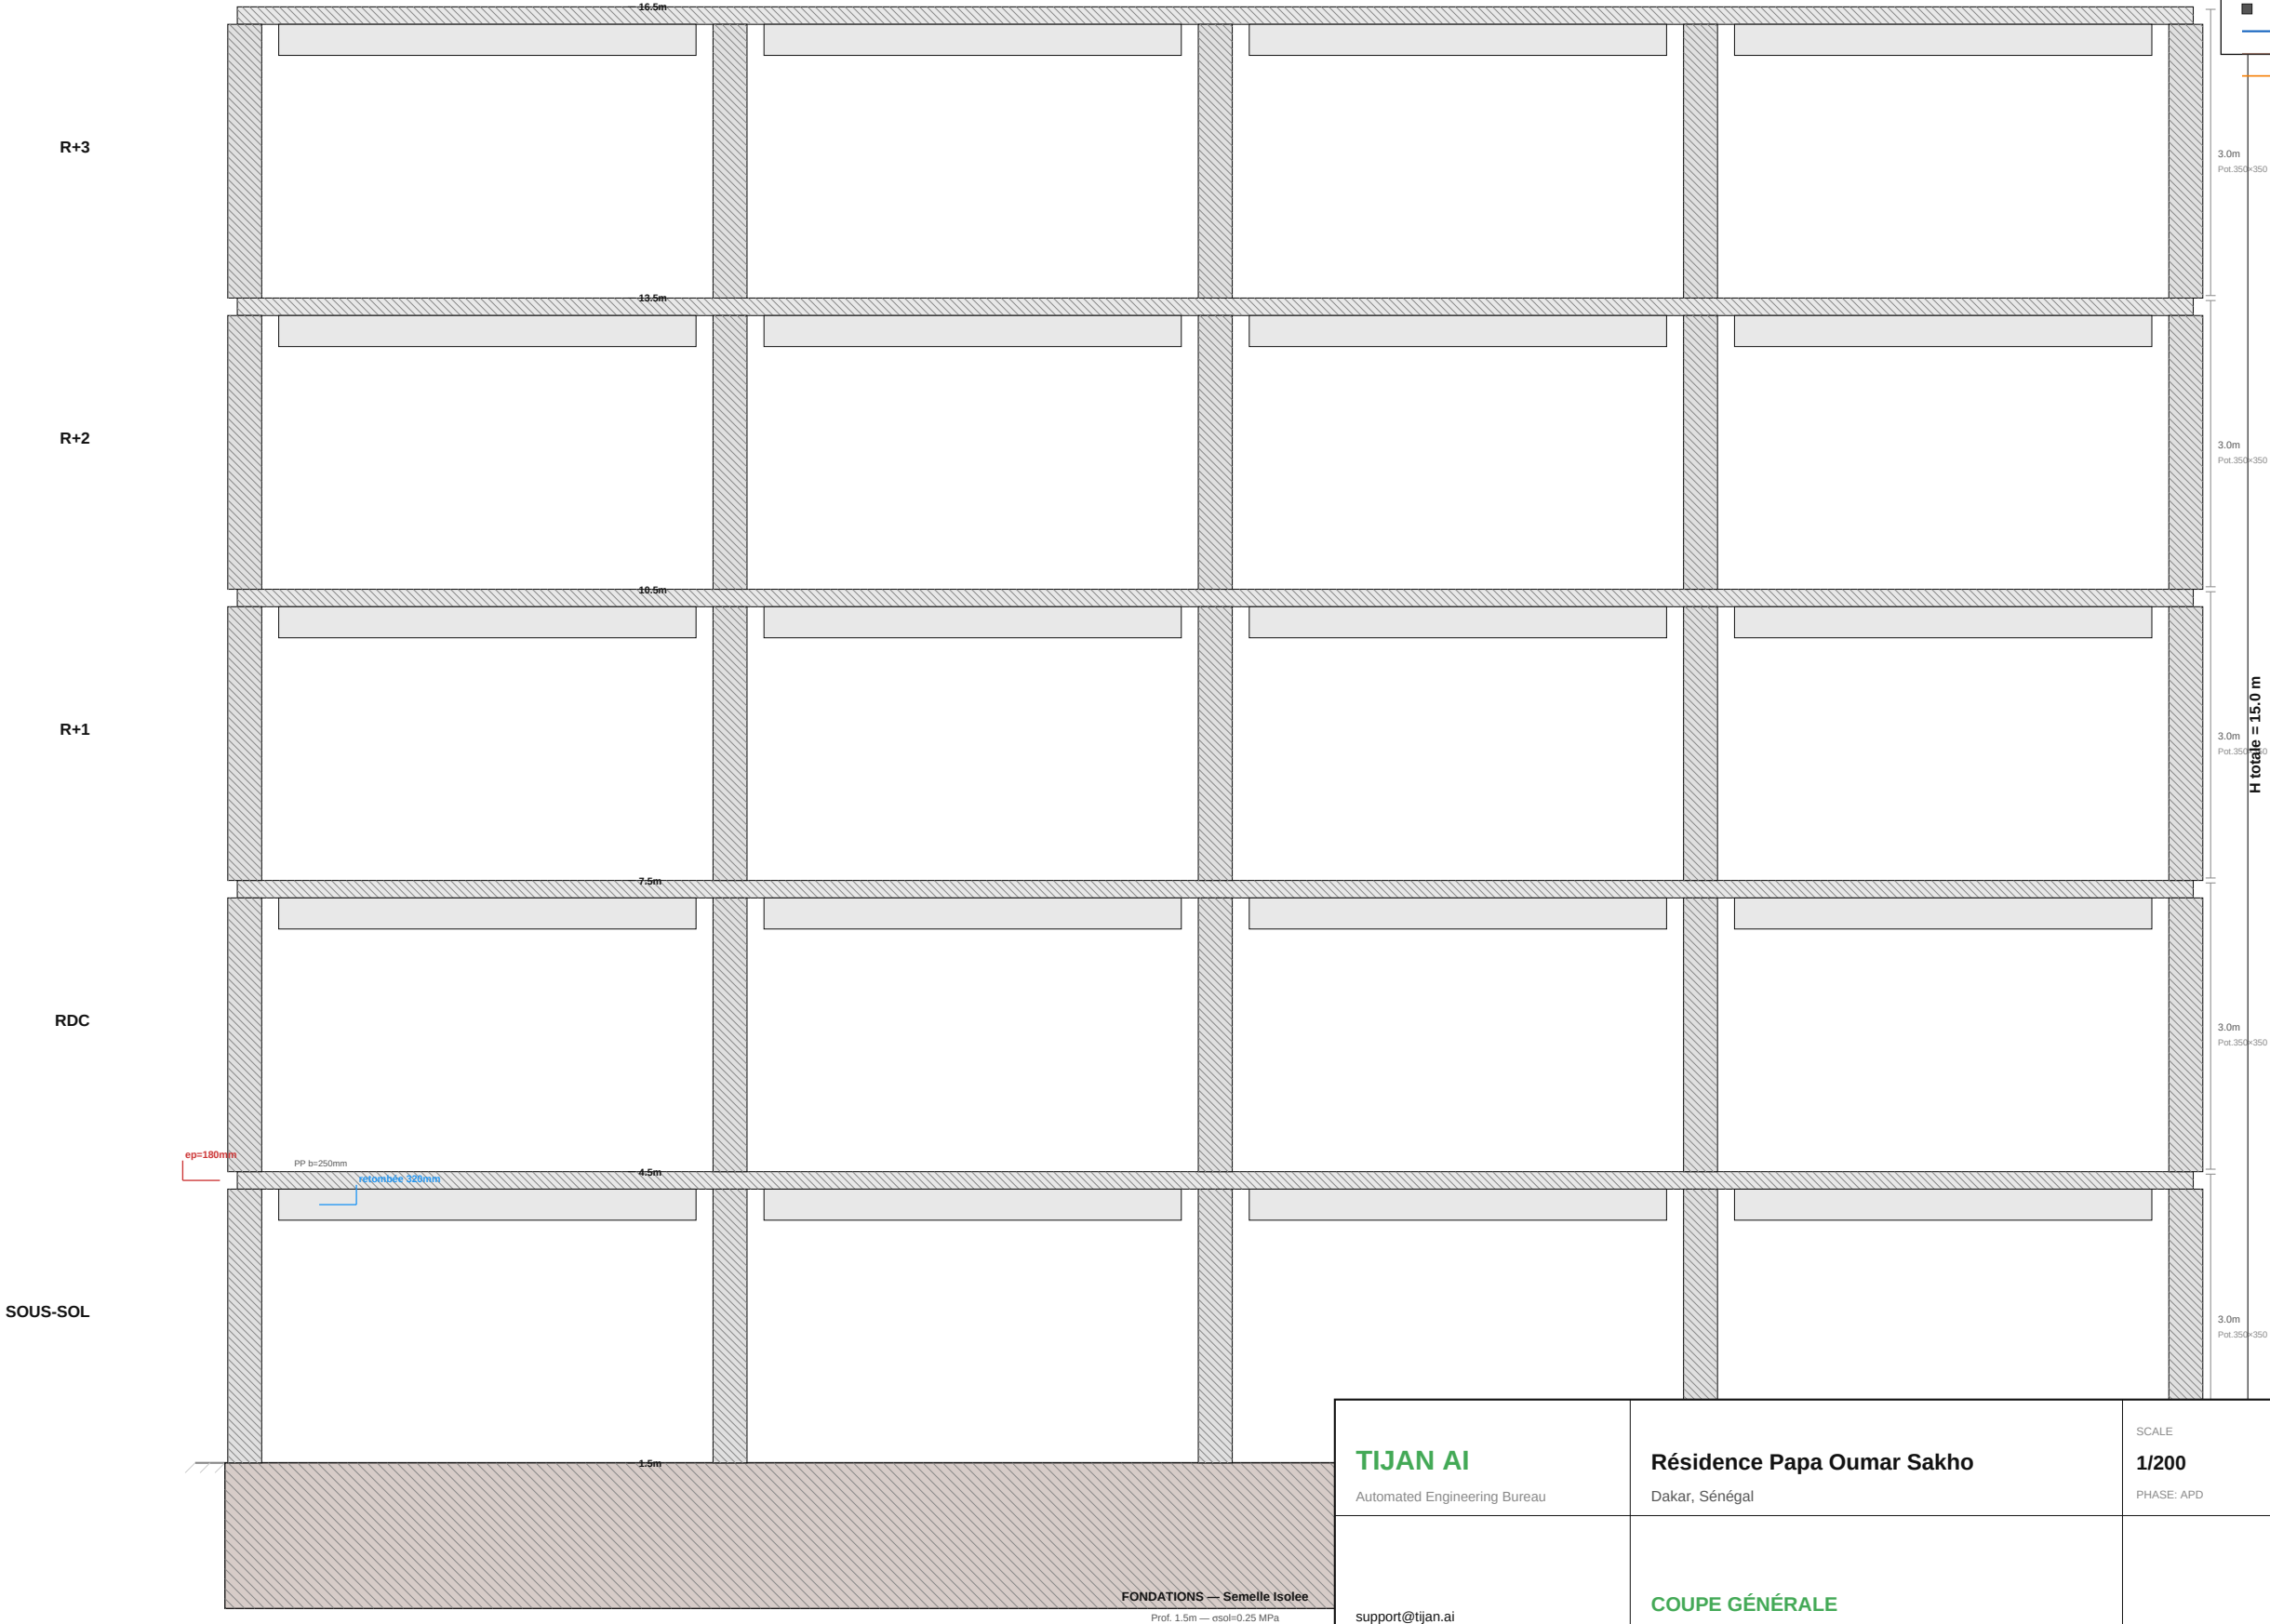

COUPE GÉNÉRALE

Poteau 350×350mm — Béton C30/37

Poutre principale 250×500mm

Dalle ep.180mm


Fondation prof.1.5m

TIJAN AI Automated Engineering Bureau support@tijan.ai www.tijan.ai 14/04/2026	Résidence Papa Oumar Sakho Dakar, Sénégal			SCALE 1/200 PHASE: APD
	COUPE GÉNÉRALE STRUCTURE BÉTON ARMÉ			PROJECT No TJN-RÉSIDE
	DESIGNED TIJAN AI	DRAWN TIJAN AI	CHECKED TIJAN AI	DRAWING No SHEET PL-009 97/11


FERRAILLAGE POUTRE PRINCIPALE

PP1 — Section 250×500 mm — Portée 5.0 m

Pos.	Armature	l (m)
①	88HA 12 l=5.20	5.20
②	127HA 10 l=5.40	5.40
③	2HA 8 l=5.10	5.10
④	5000HA 1.0 cadres	1.70

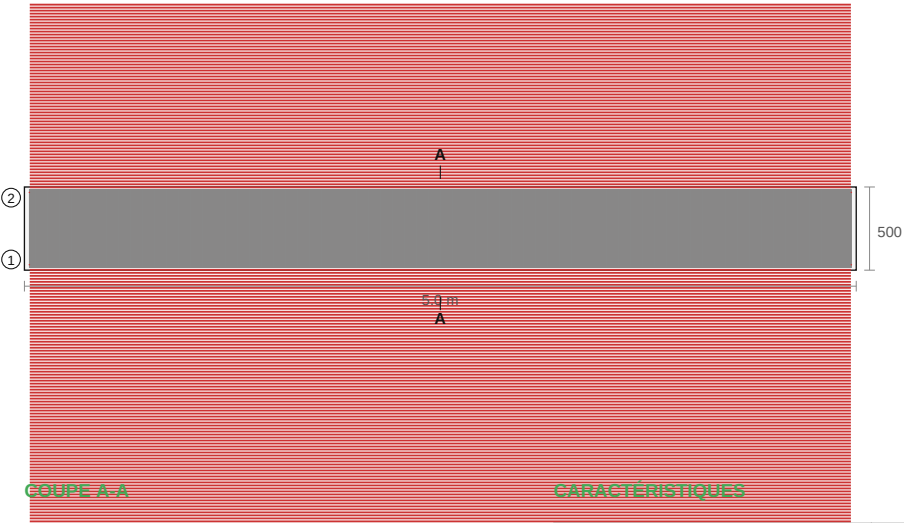

Section	250 × 500 mm
As inf (travée)	1.00 cm² — 88 barres
As sup (appuis)	1.00 cm² — 127 barres
Étriers	HA1.0 / 1.0 mm
Portée	5.0 m
Béton	C30/37
Acier	HA 500
Enrobage	30 mm

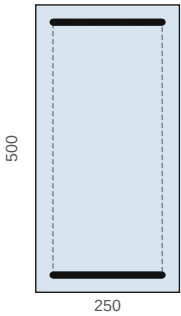

Section 250×500
215 barres

Béton C30/37 — Acier HA 500 — Enrobage 3 cm — Fissuration peu préjudiciable

TIJAN AI Engineering Intelligence Date: 14/04/2026	Résidence Papa Oumar Sakho	Éch: 1/100 Dakar
	FERRAILLAGE POUTRE PRINCIPALE	Pl. 2/4

FERRAILLAGE POTEAUX

Coupes transversales et sections par niveau

COUPE POTEAU RDC

