



001 Architecture — RDC

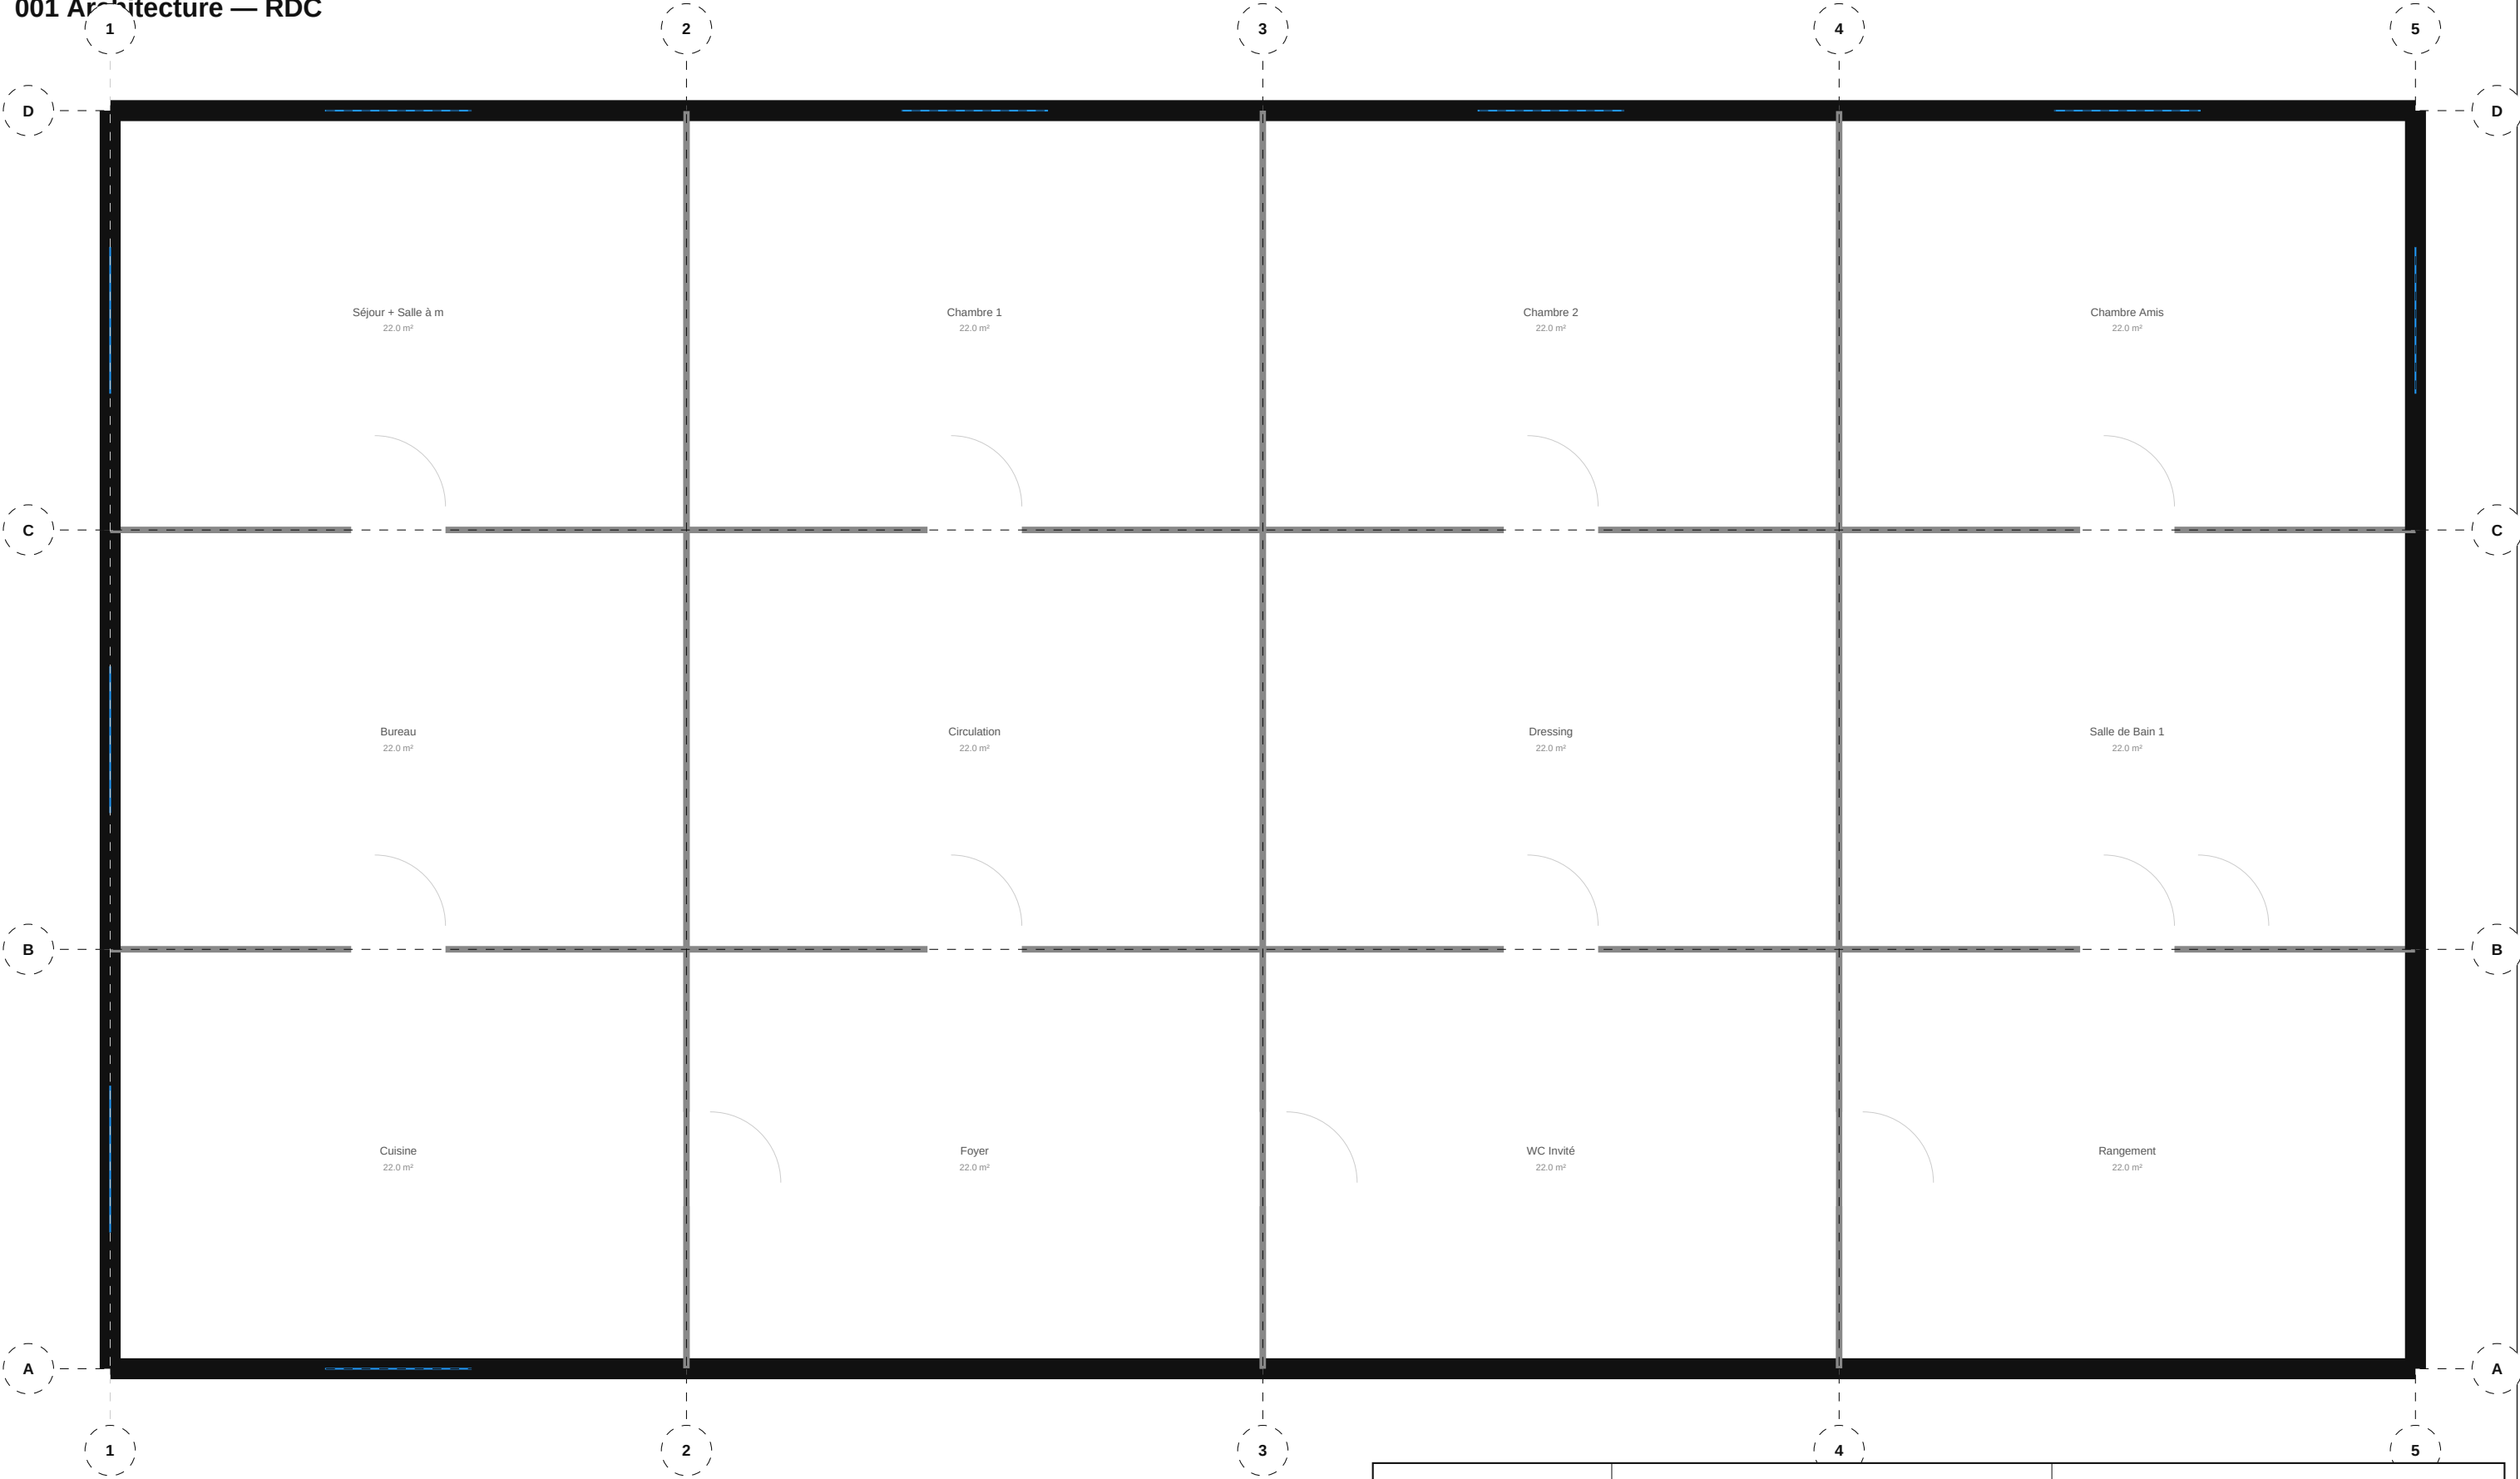


|                                               |                                                     |                            |
|-----------------------------------------------|-----------------------------------------------------|----------------------------|
| <b>TIJAN AI</b><br>Bureau d'Études Automatisé | <b>Résidence Papa Oumar Sakho</b><br>Dakar, Senegal | Éch: 1/100<br>Pl. 1/32     |
|                                               | <b>Architecture — RDC</b>                           |                            |
| Date: 06/05/2026                              | Réf: ARC                                            | BIM vARC-001<br>Phase: APD |

001 Architecture — Étage 1

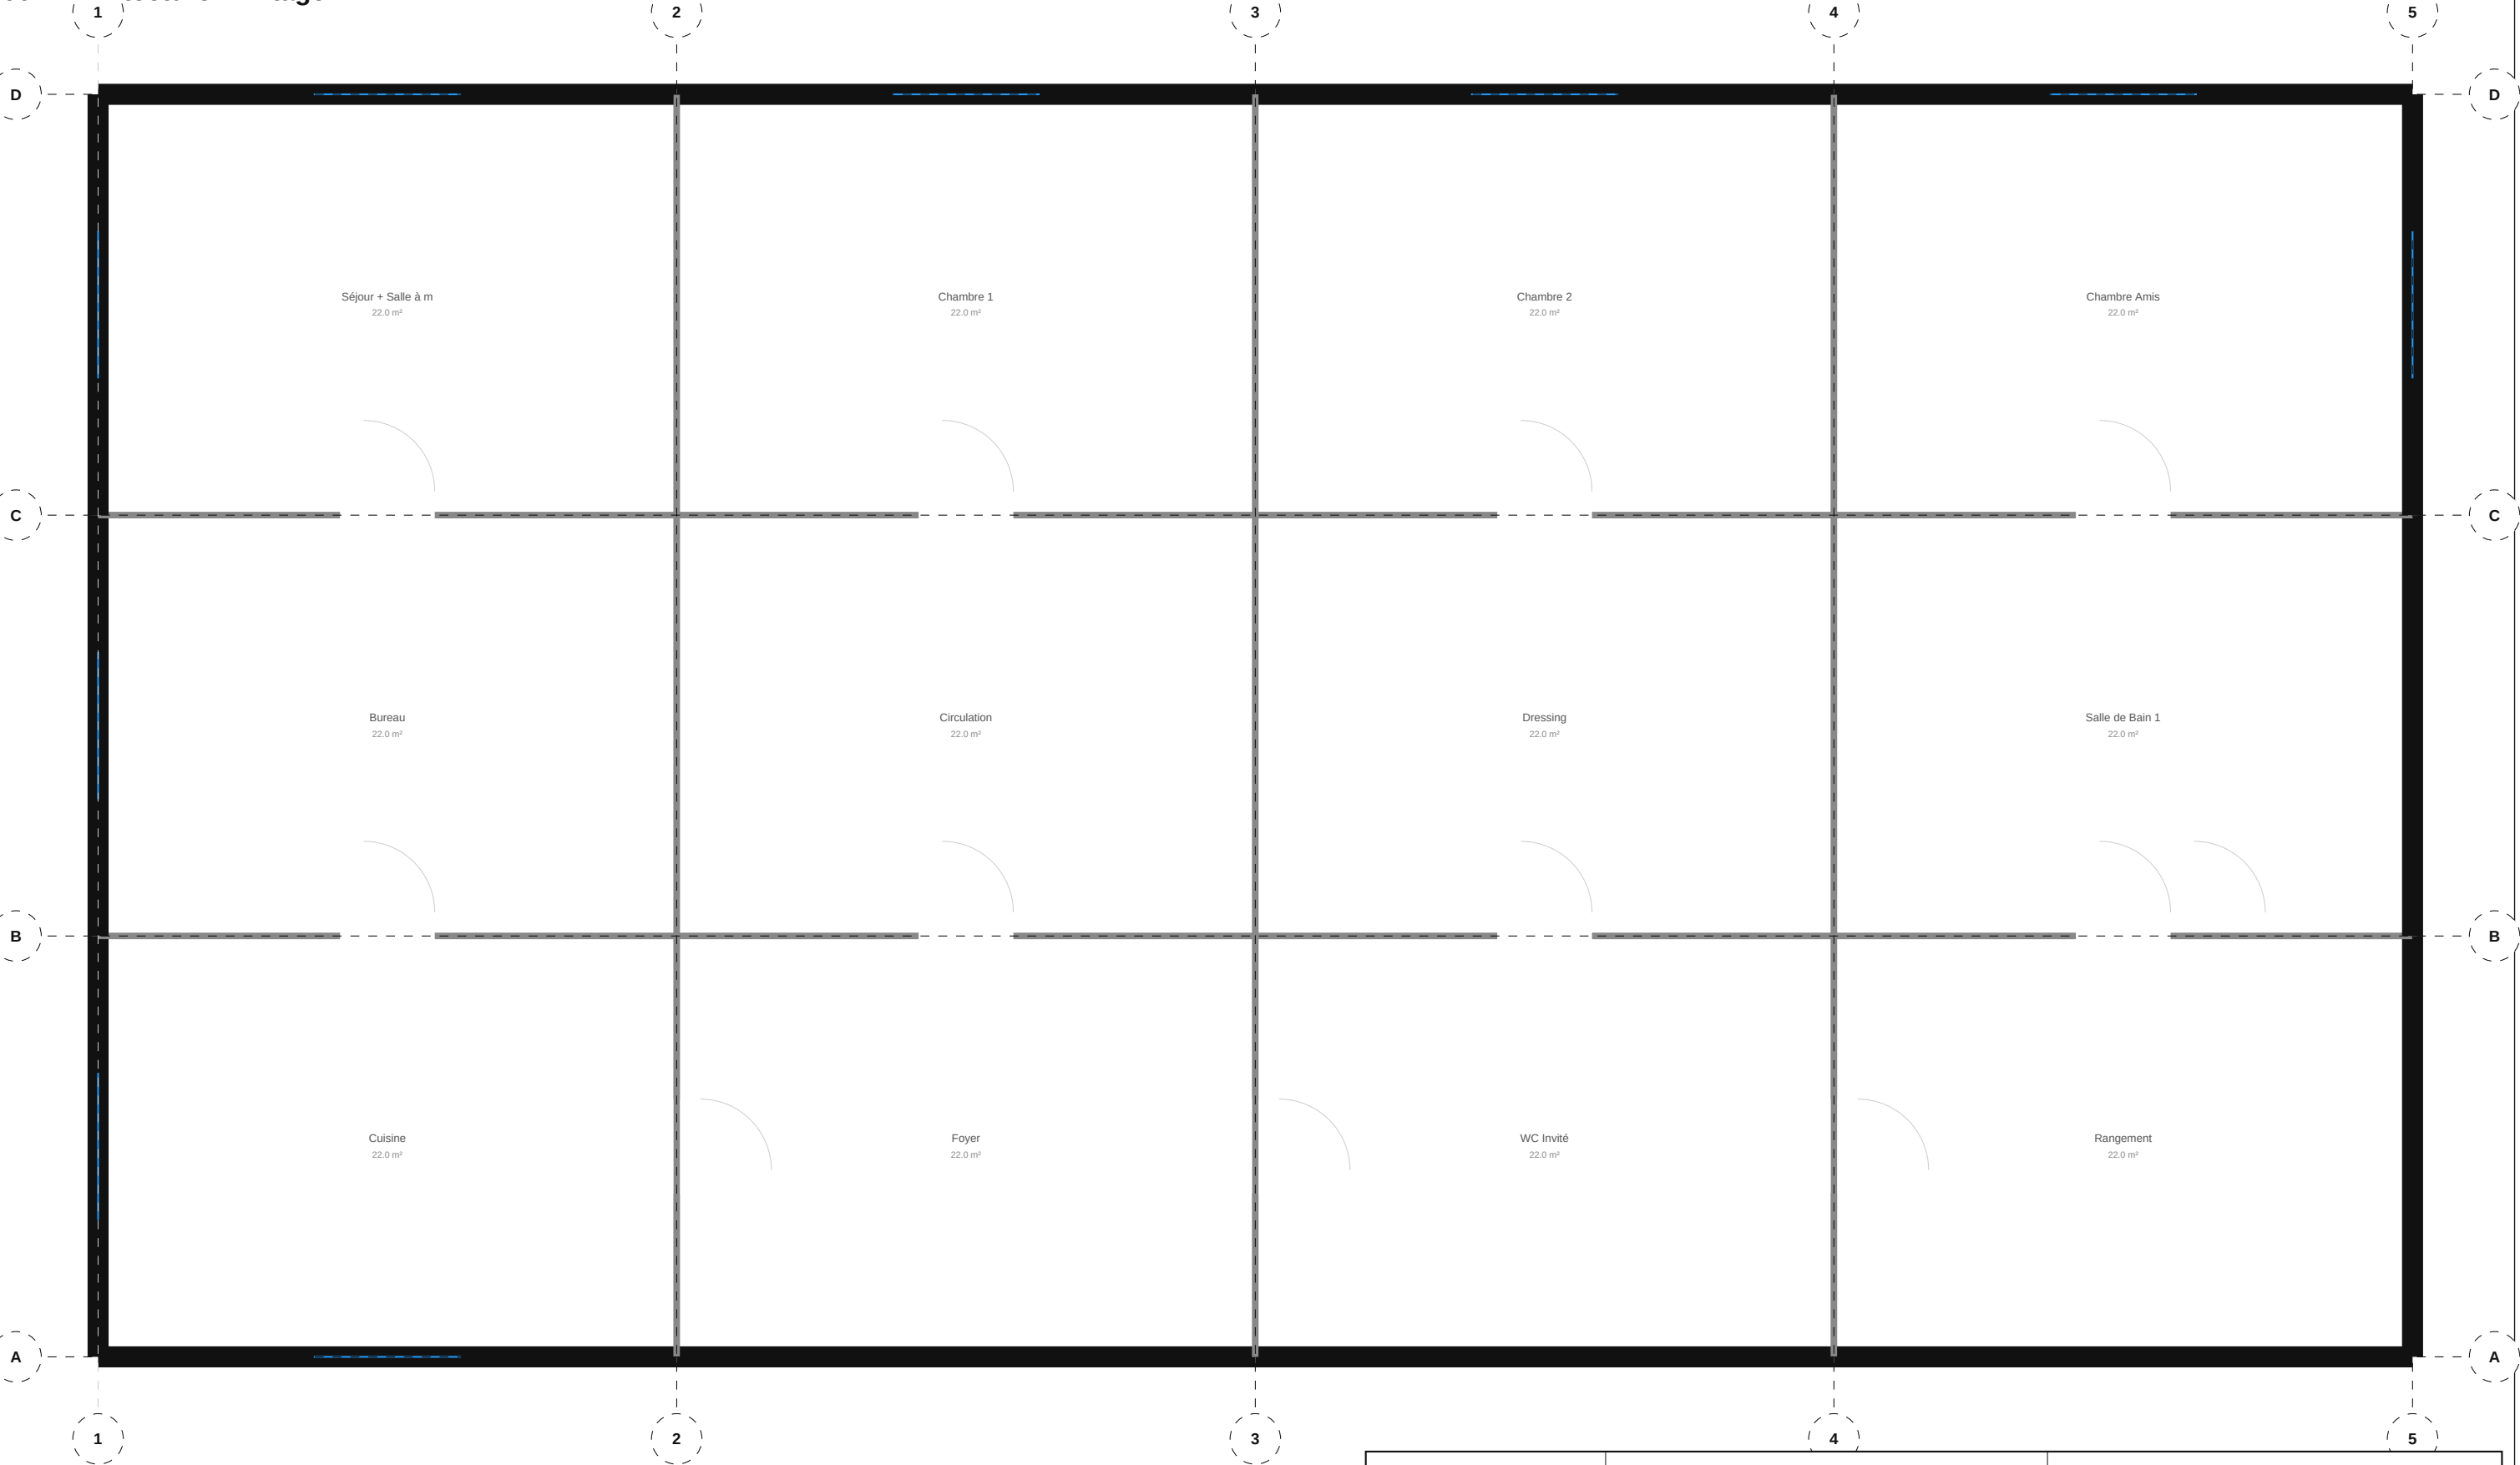


|                                                           |                                                                 |                                               |
|-----------------------------------------------------------|-----------------------------------------------------------------|-----------------------------------------------|
| <div>TIJAN AI</div> <div>Bureau d'Études Automatisé</div> | <div>Résidence Papa Oumar Sakho</div> <div>Dakar, Senegal</div> | <div>Éch: 1/100</div> <div>Pl. 2/32</div>     |
|                                                           | Architecture — Étage 1                                          |                                               |
| <div>Date: 06/05/2026</div>                               | <div>Réf: ARC</div>                                             | <div>BIM vARC-002</div> <div>Phase: APD</div> |

001 Architecture — Étage 2

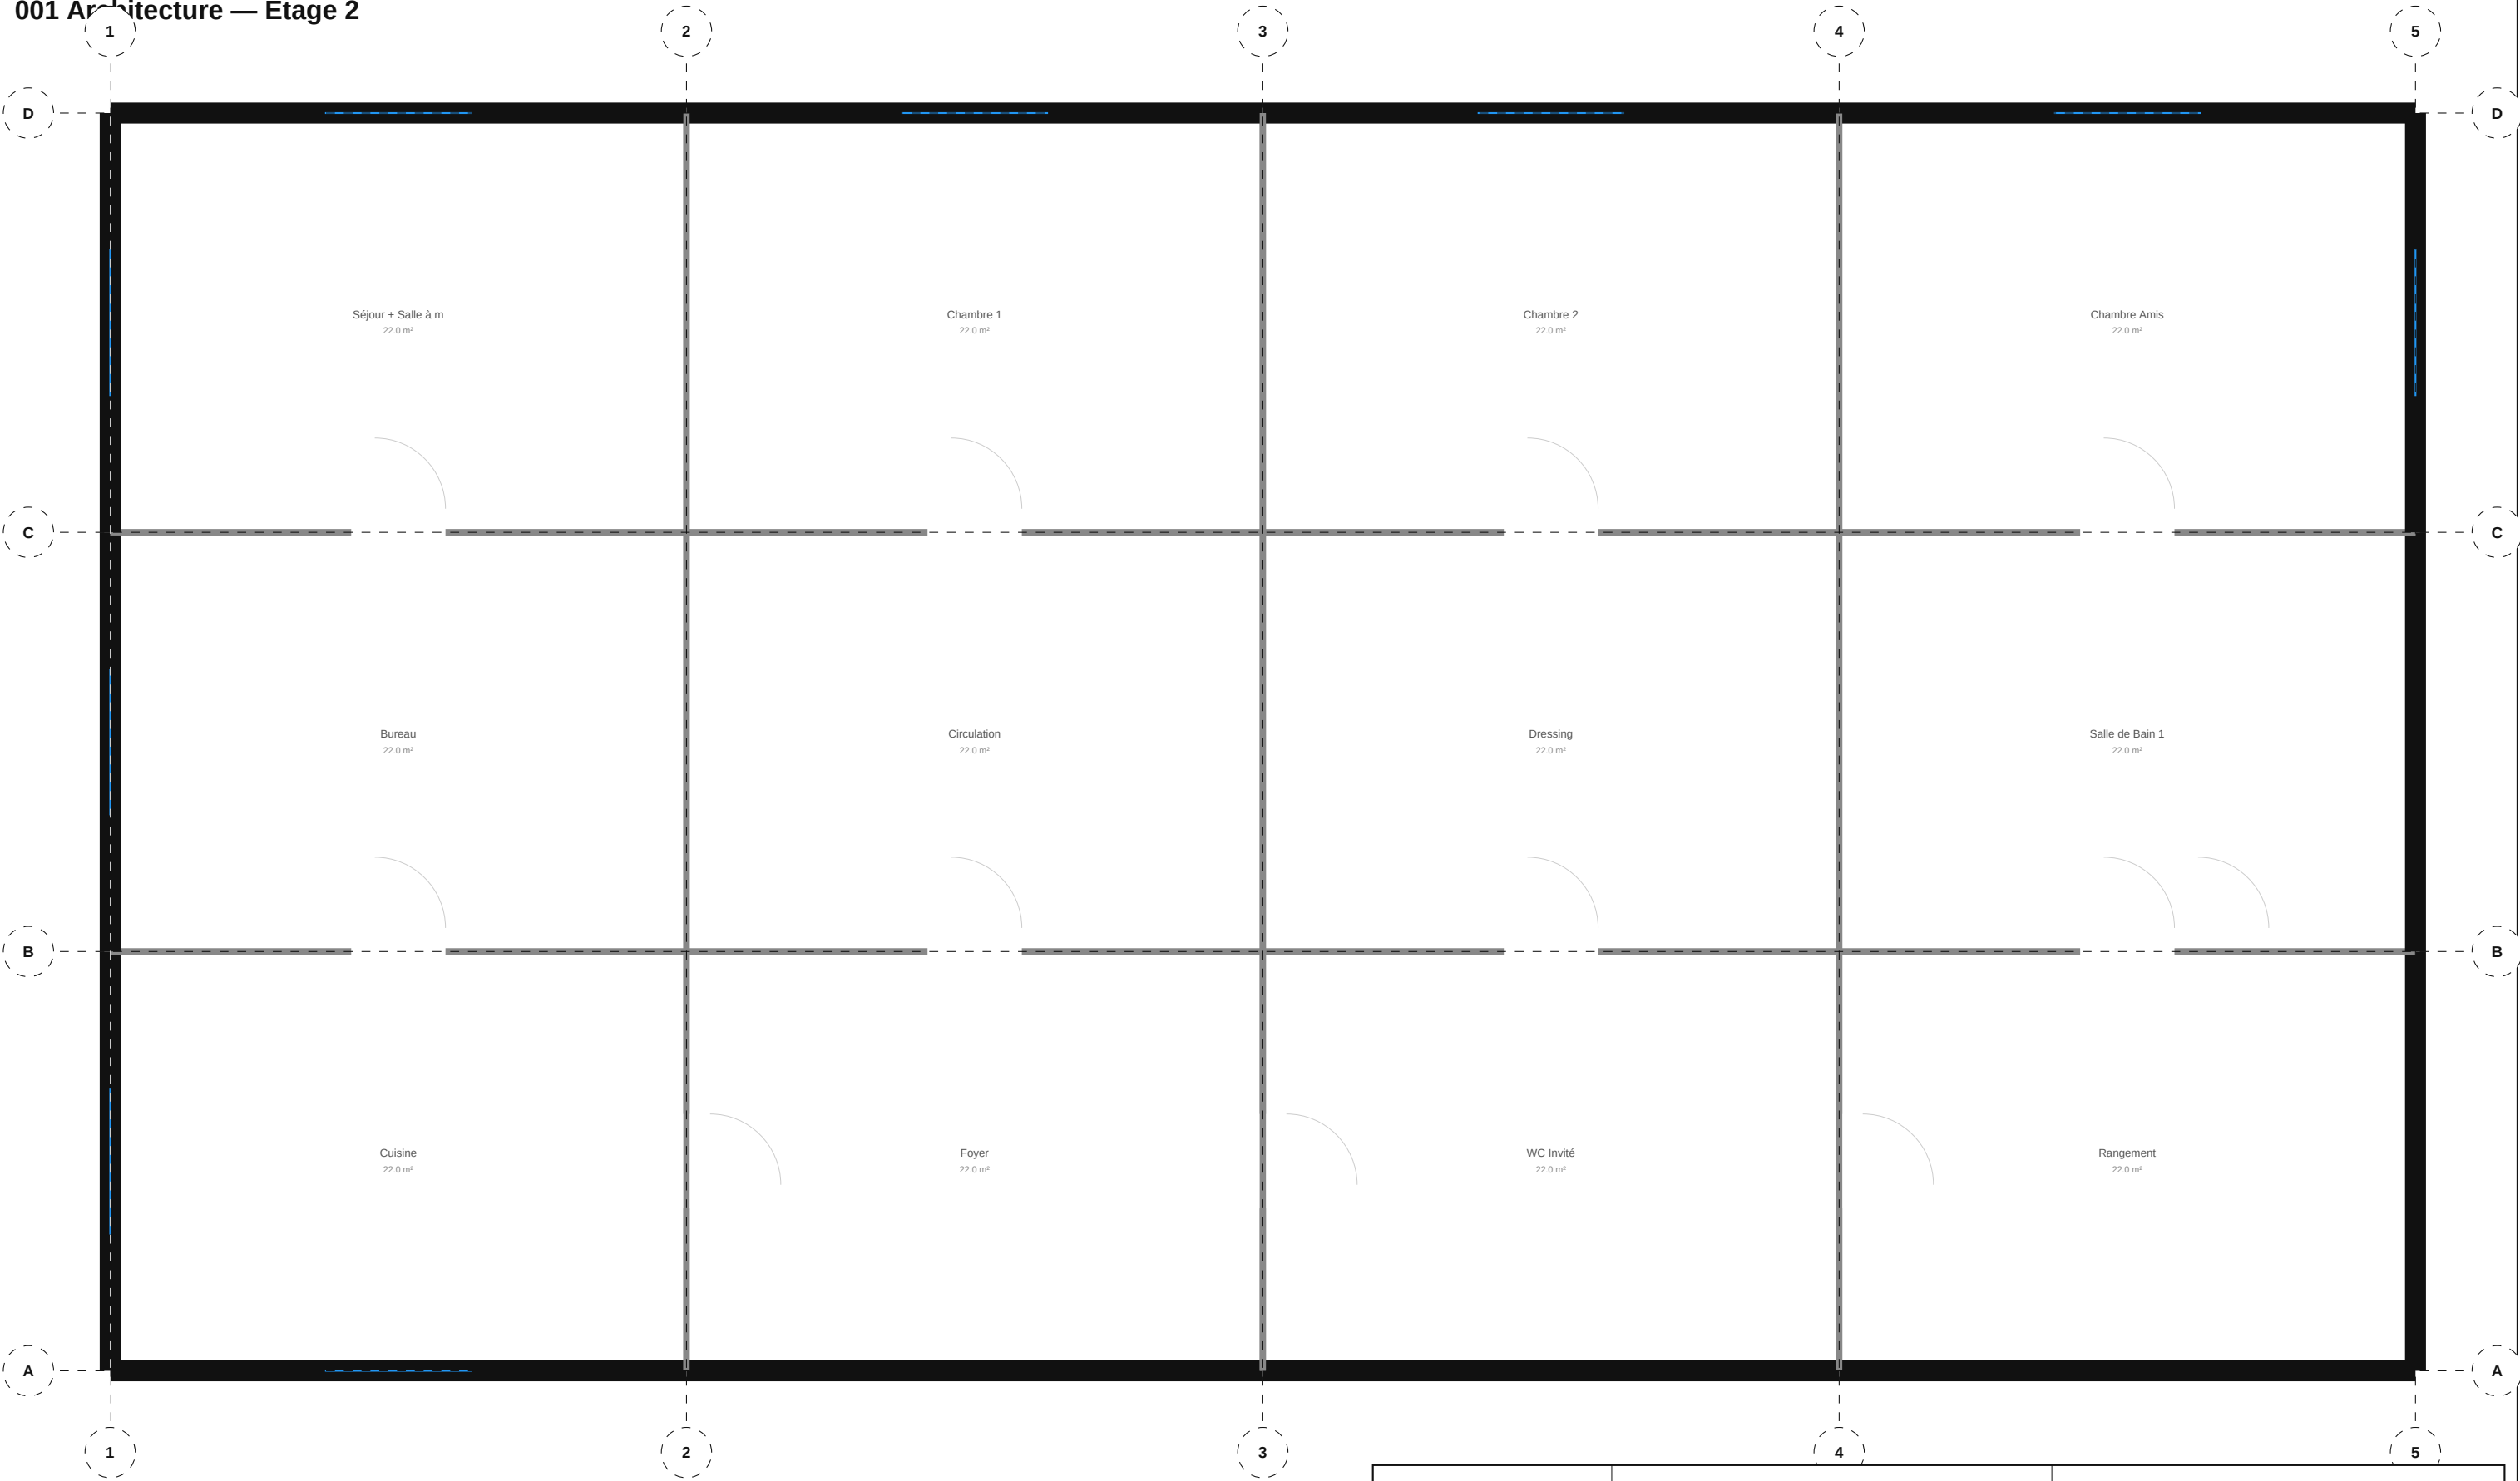


|                                                           |                                                                 |                                               |
|-----------------------------------------------------------|-----------------------------------------------------------------|-----------------------------------------------|
| <div>TIJAN AI</div> <div>Bureau d'Études Automatisé</div> | <div>Résidence Papa Oumar Sakho</div> <div>Dakar, Senegal</div> | <div>Éch: 1/100</div> <div>Pl. 3/32</div>     |
|                                                           | <div>Architecture — Étage 2</div>                               |                                               |
| <div>Date: 06/05/2026</div>                               | <div>Réf: ARC</div>                                             | <div>BIM vARC-003</div> <div>Phase: APD</div> |

001 Architecture — Étage 3

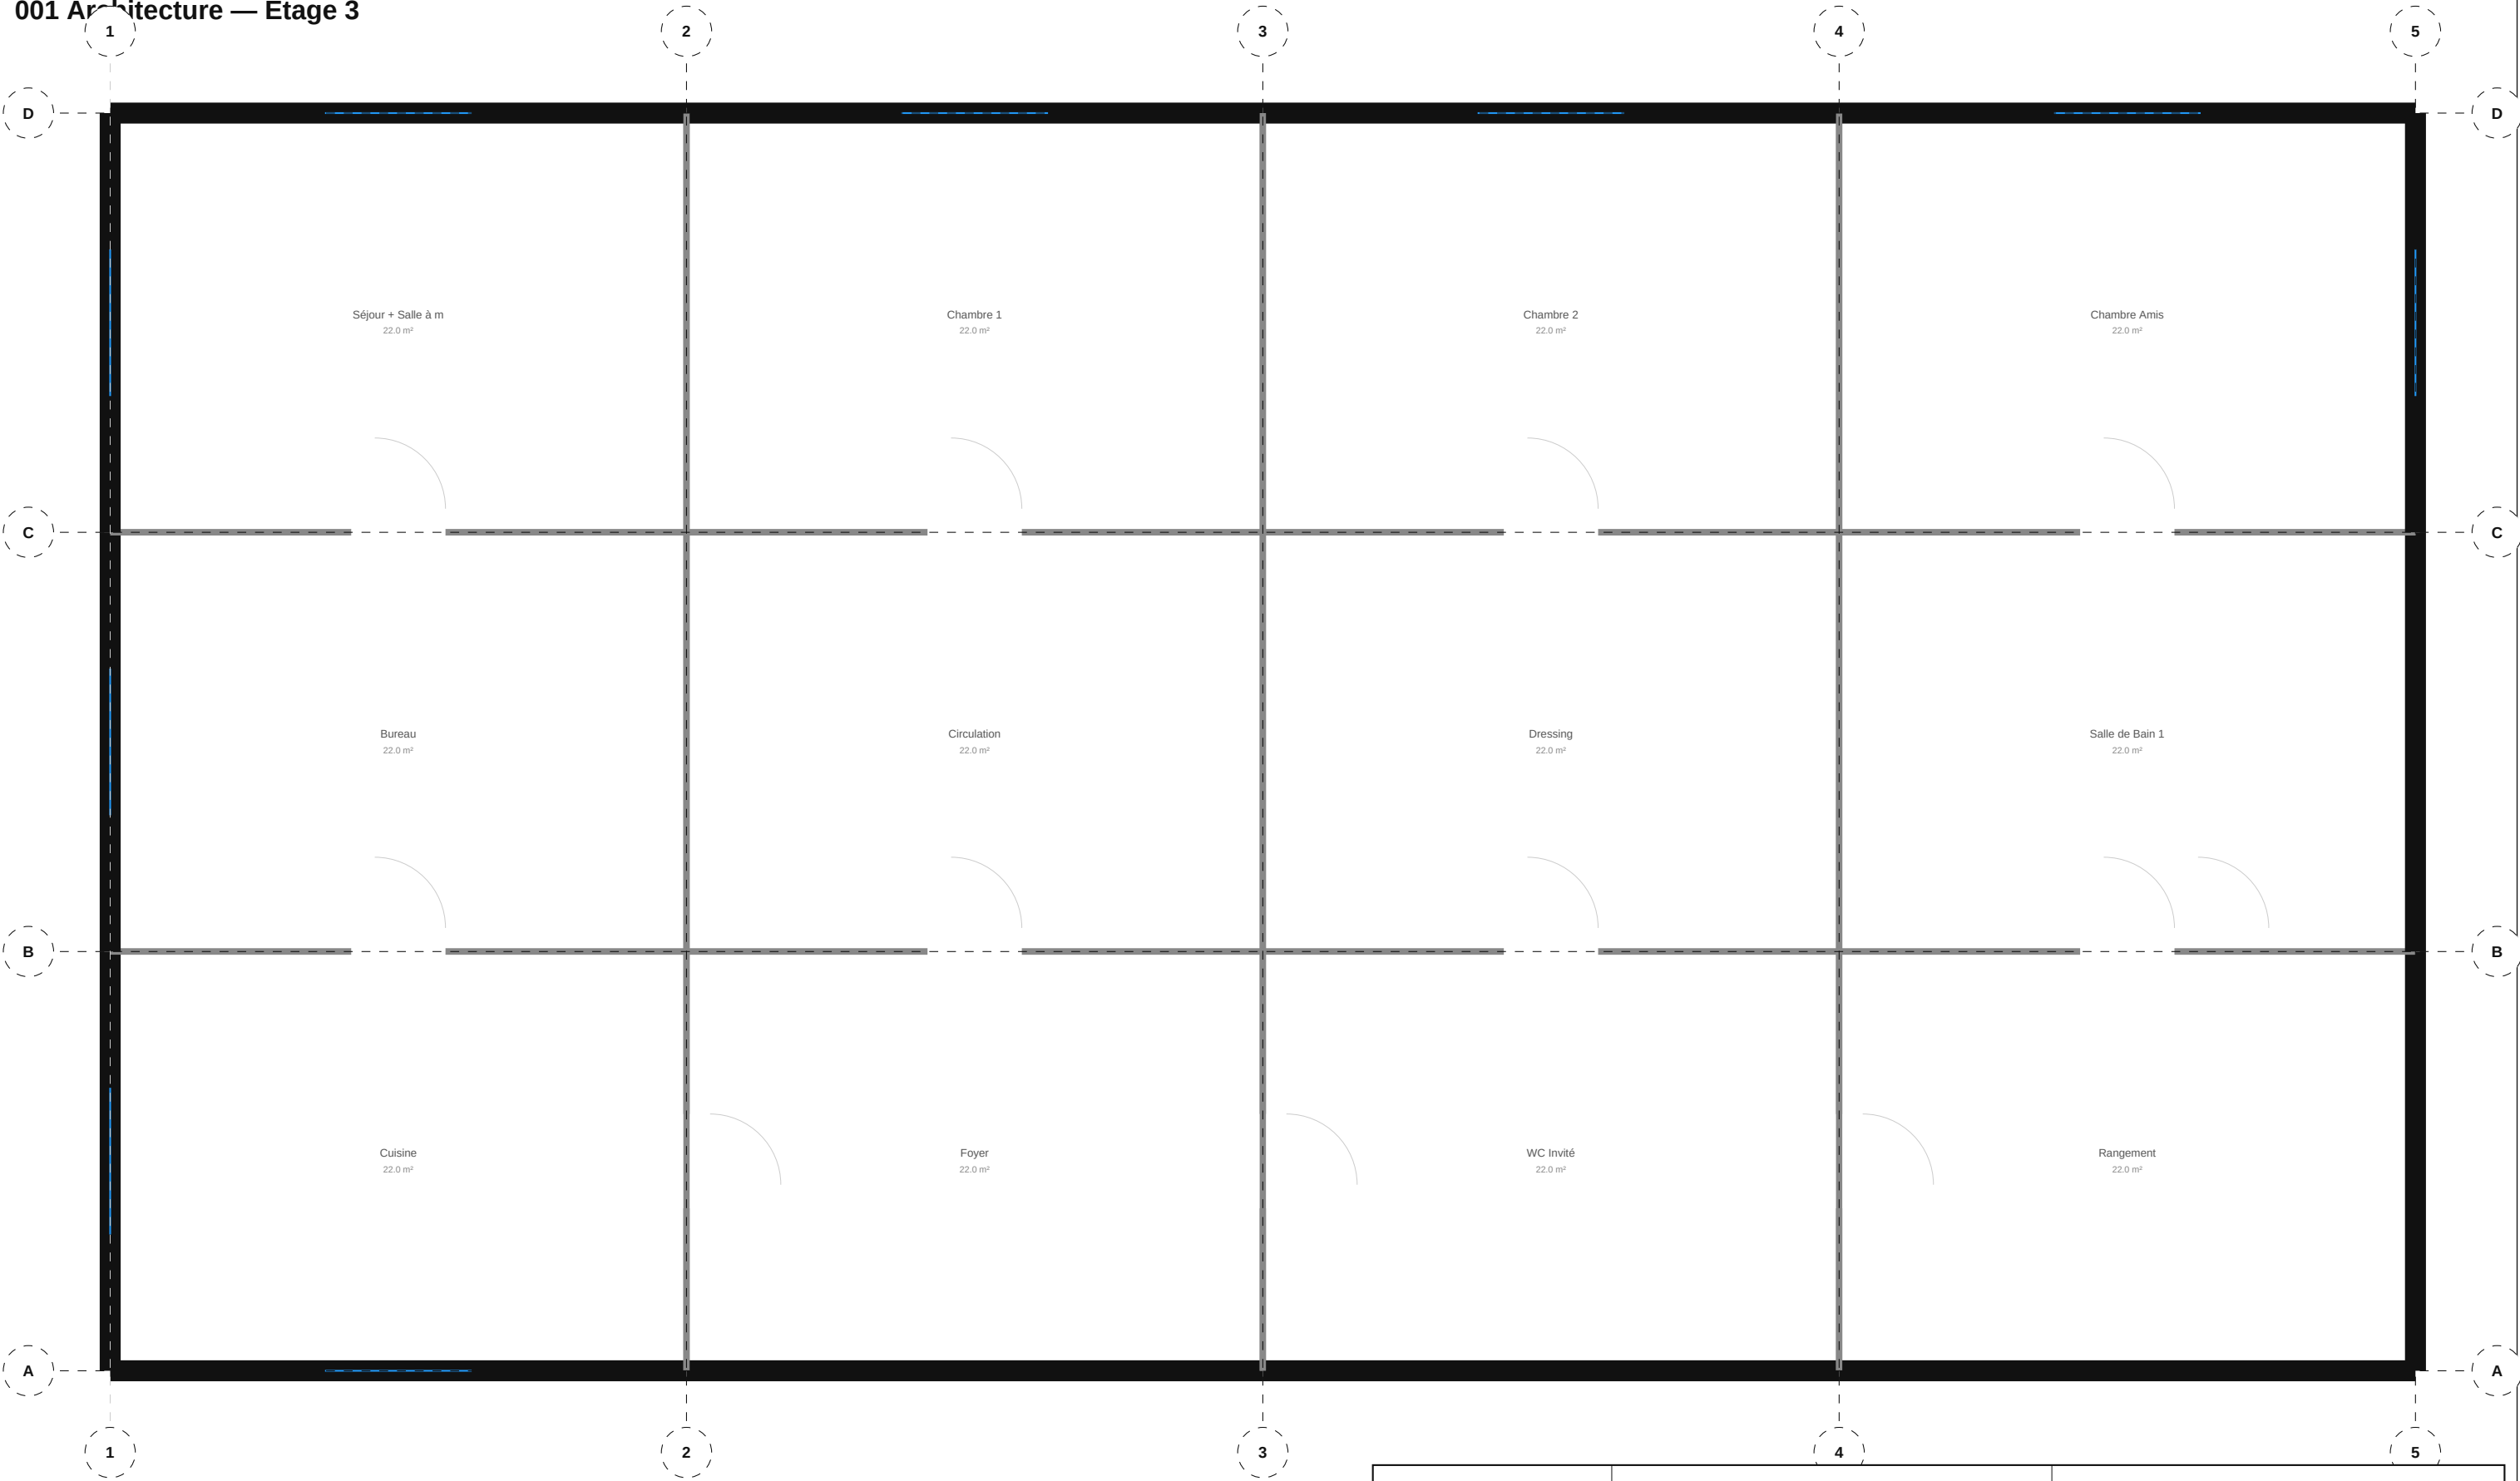

|                                                           |                                                                 |                                               |
|-----------------------------------------------------------|-----------------------------------------------------------------|-----------------------------------------------|
| <div>TIJAN AI</div> <div>Bureau d'Études Automatisé</div> | <div>Résidence Papa Oumar Sakho</div> <div>Dakar, Senegal</div> | <div>Éch: 1/100</div> <div>Pl. 4/32</div>     |
|                                                           | Architecture — Étage 3                                          |                                               |
| Date: 06/05/2026                                          | Réf: ARC                                                        | <div>BIM vARC-004</div> <div>Phase: APD</div> |

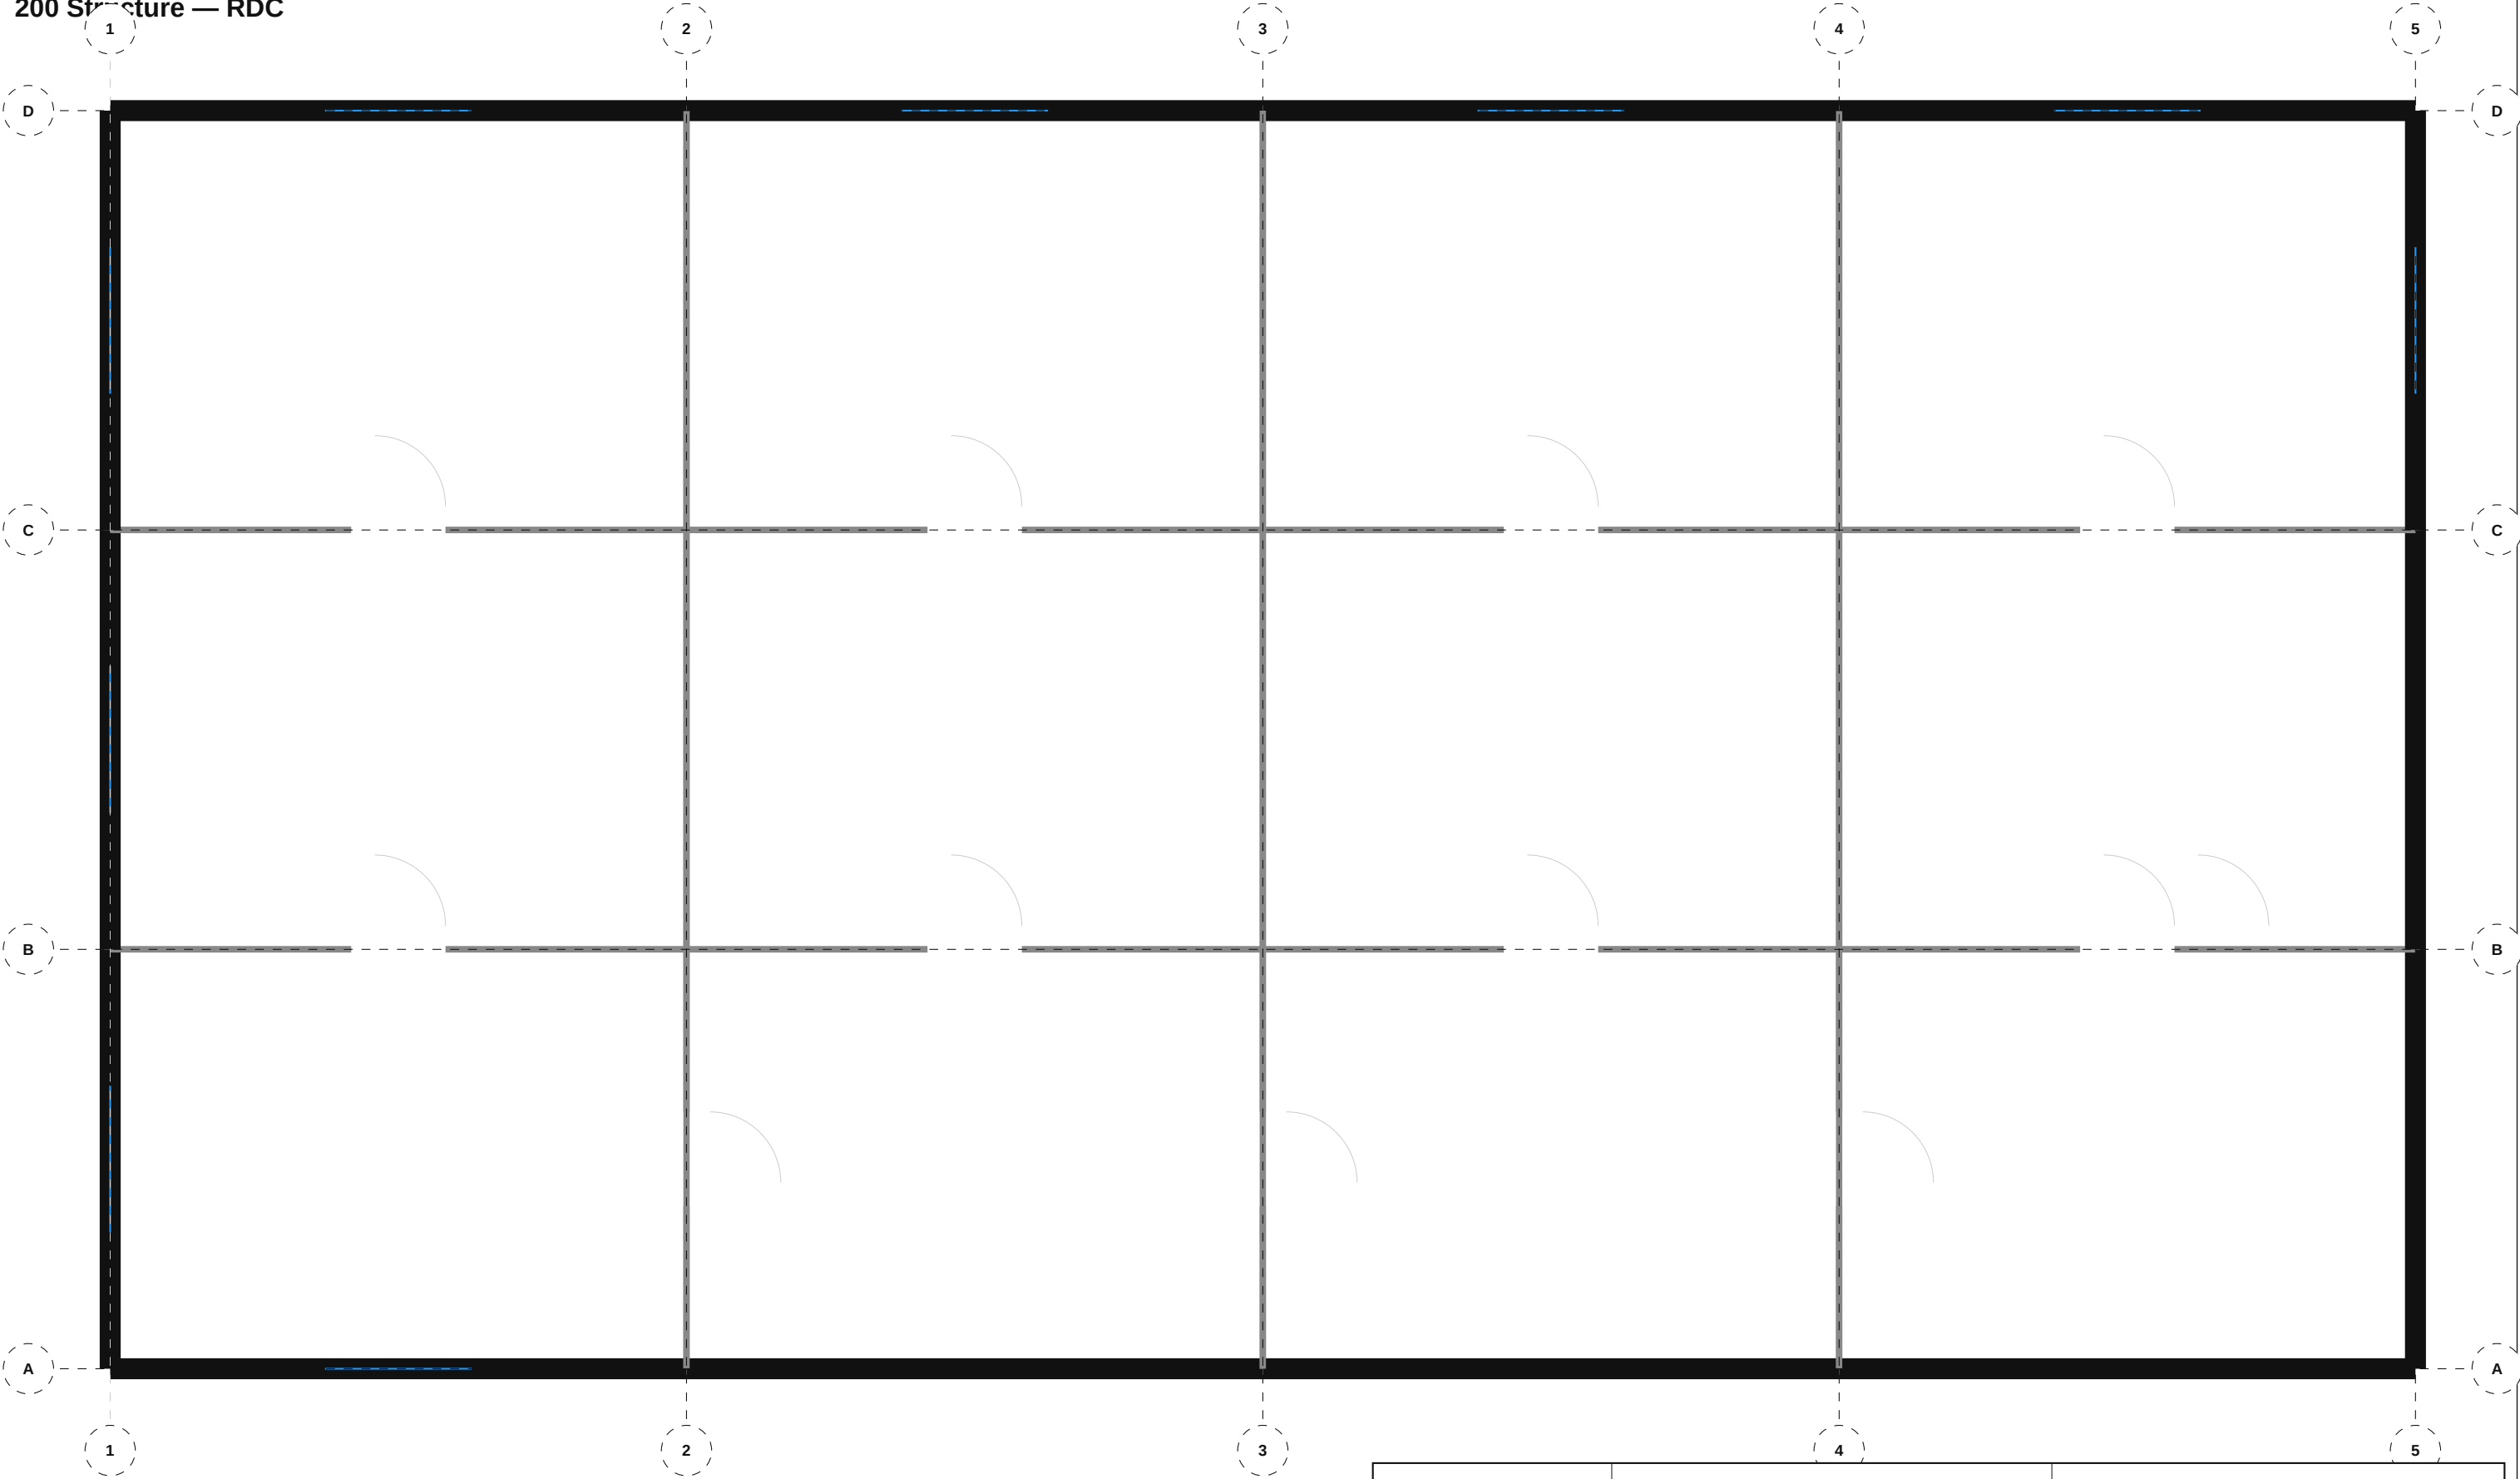

**TIJAN AI**

Bureau d'Études Automatisé

**Résidence Papa Oumar Sakho**

Dakar, Senegal

Éch: 1/100

Pl. 5/32


Structure — RDC

Date: 06/05/2026

Réf: STR

BIM vSTR-005

Phase: APD

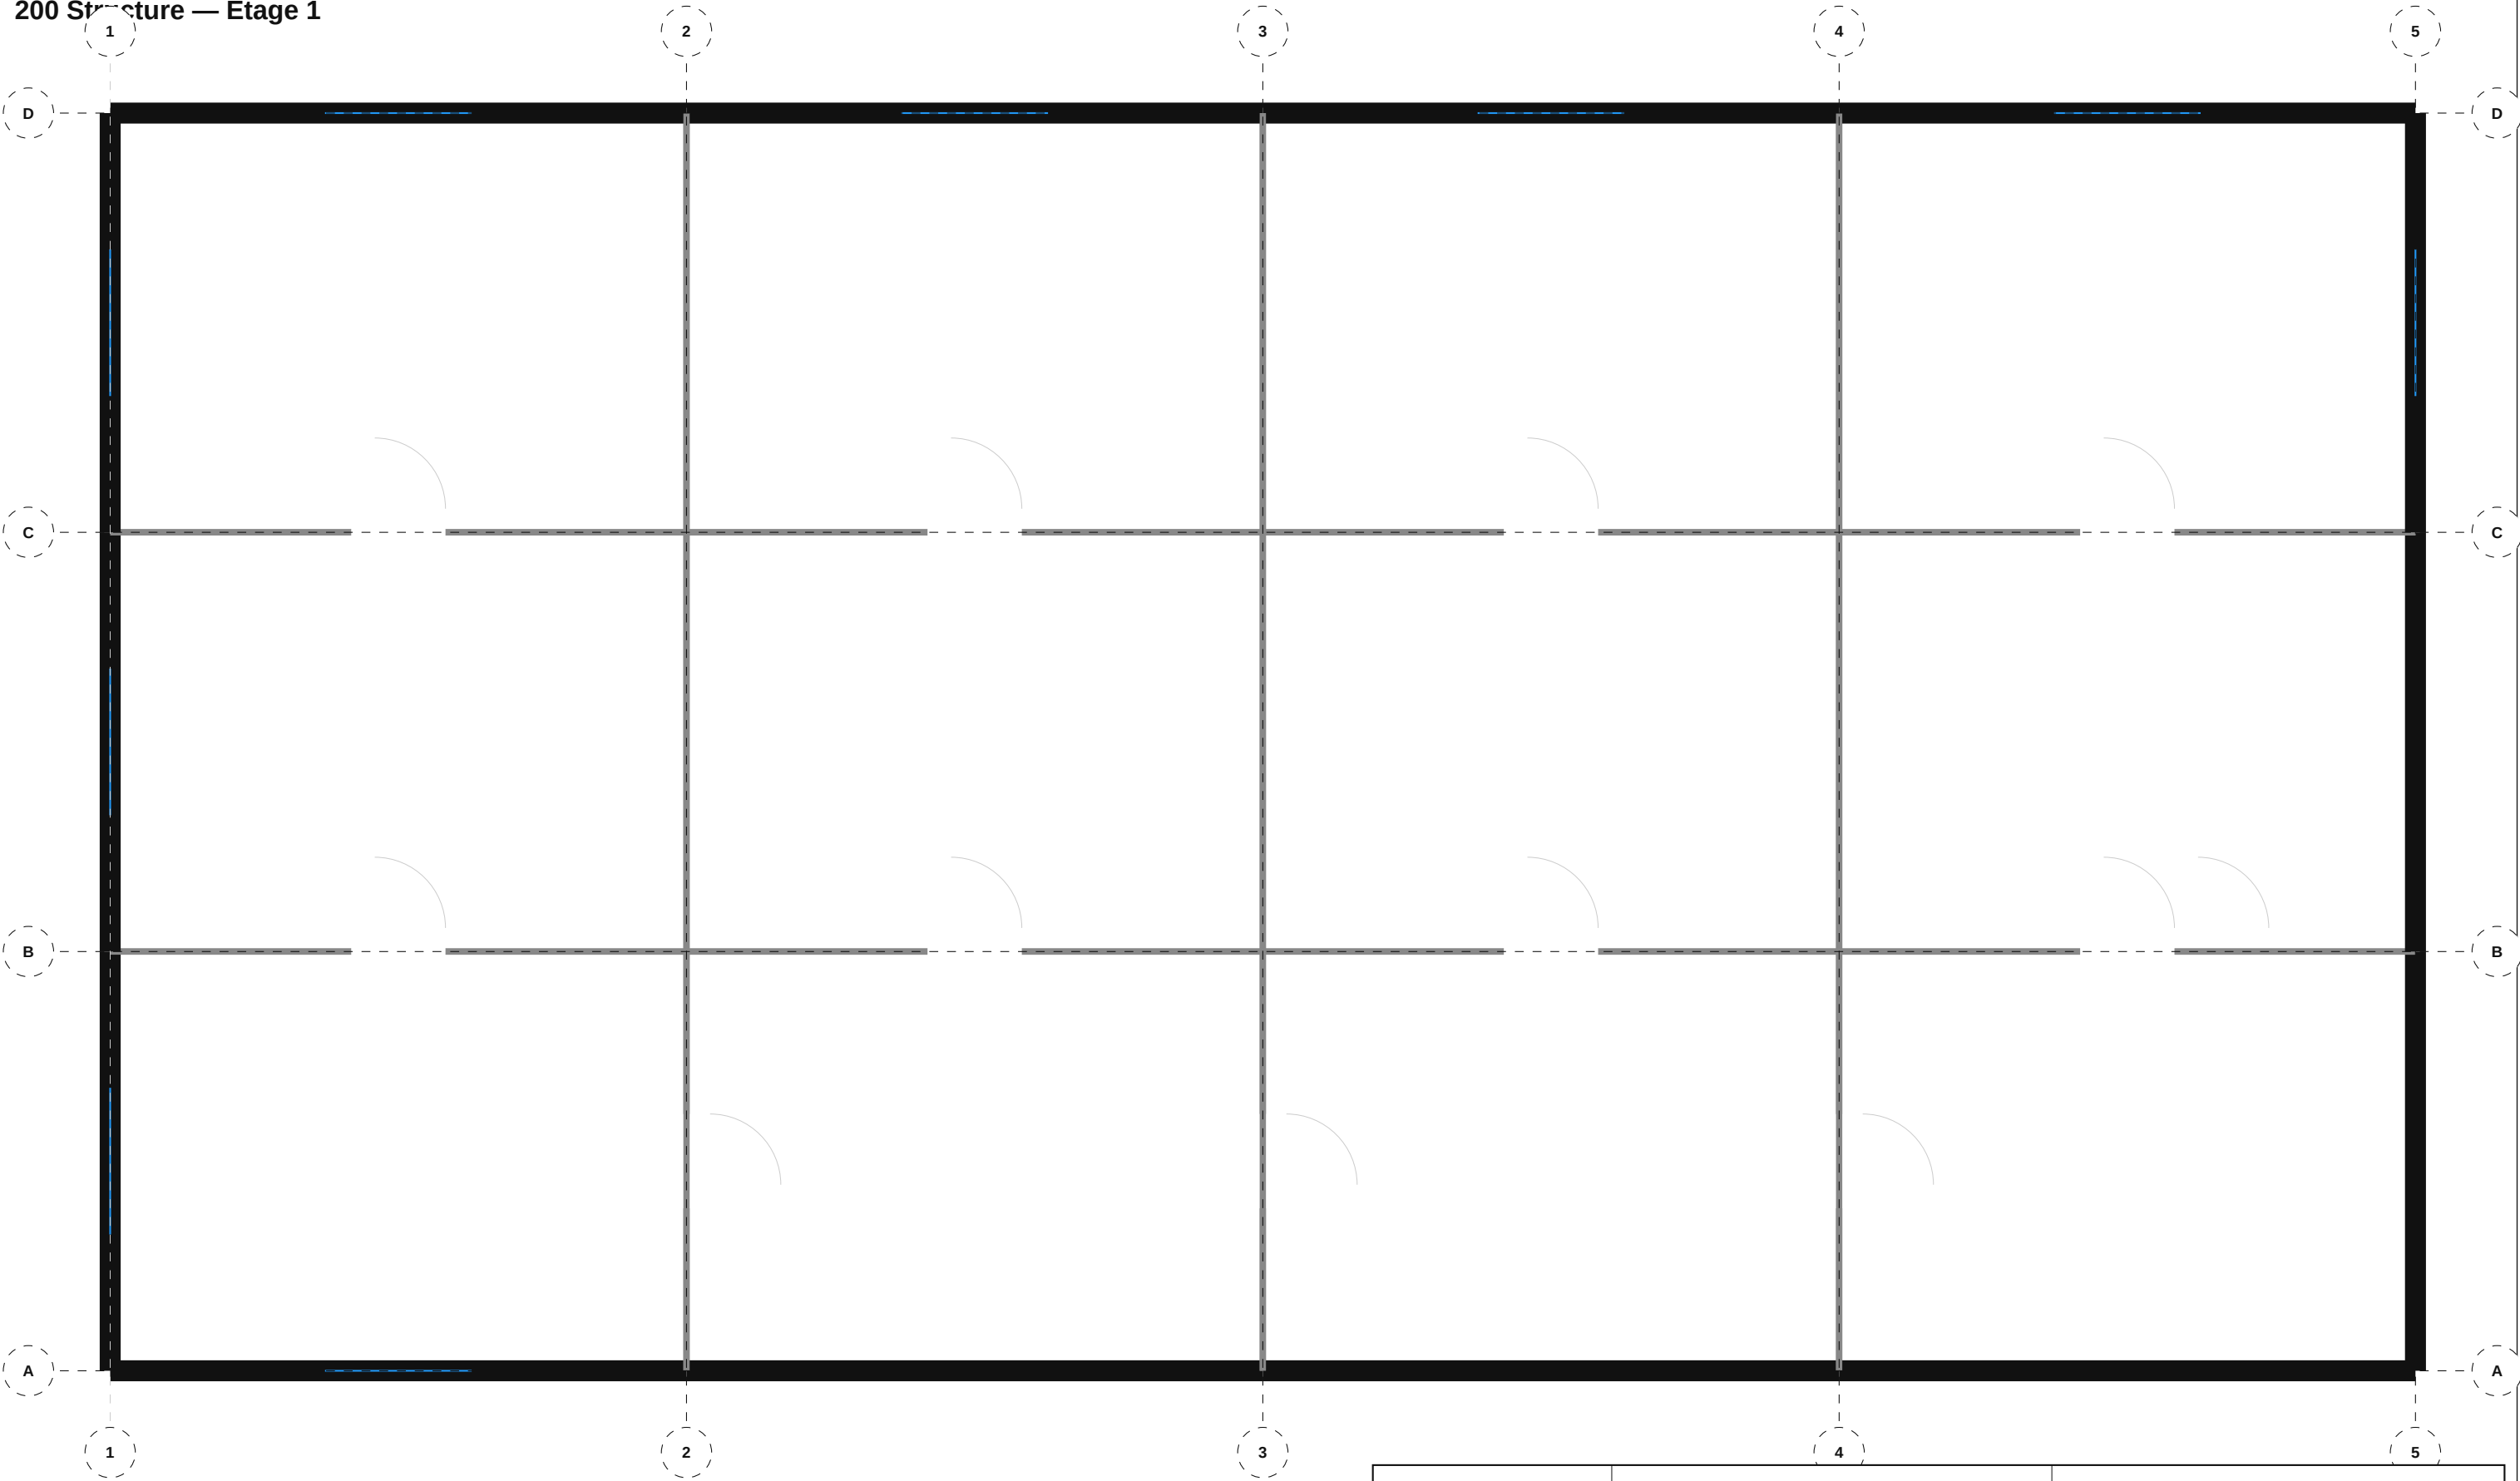

TIJAN AI

Bureau d'Études Automatisé

Résidence Papa Oumar Sakho

Dakar, Senegal

Éch: 1/100

Pl. 6/32

Structure — Étage 1


Date: 06/05/2026

Réf: STR

BIM vSTR-006


Phase: APD



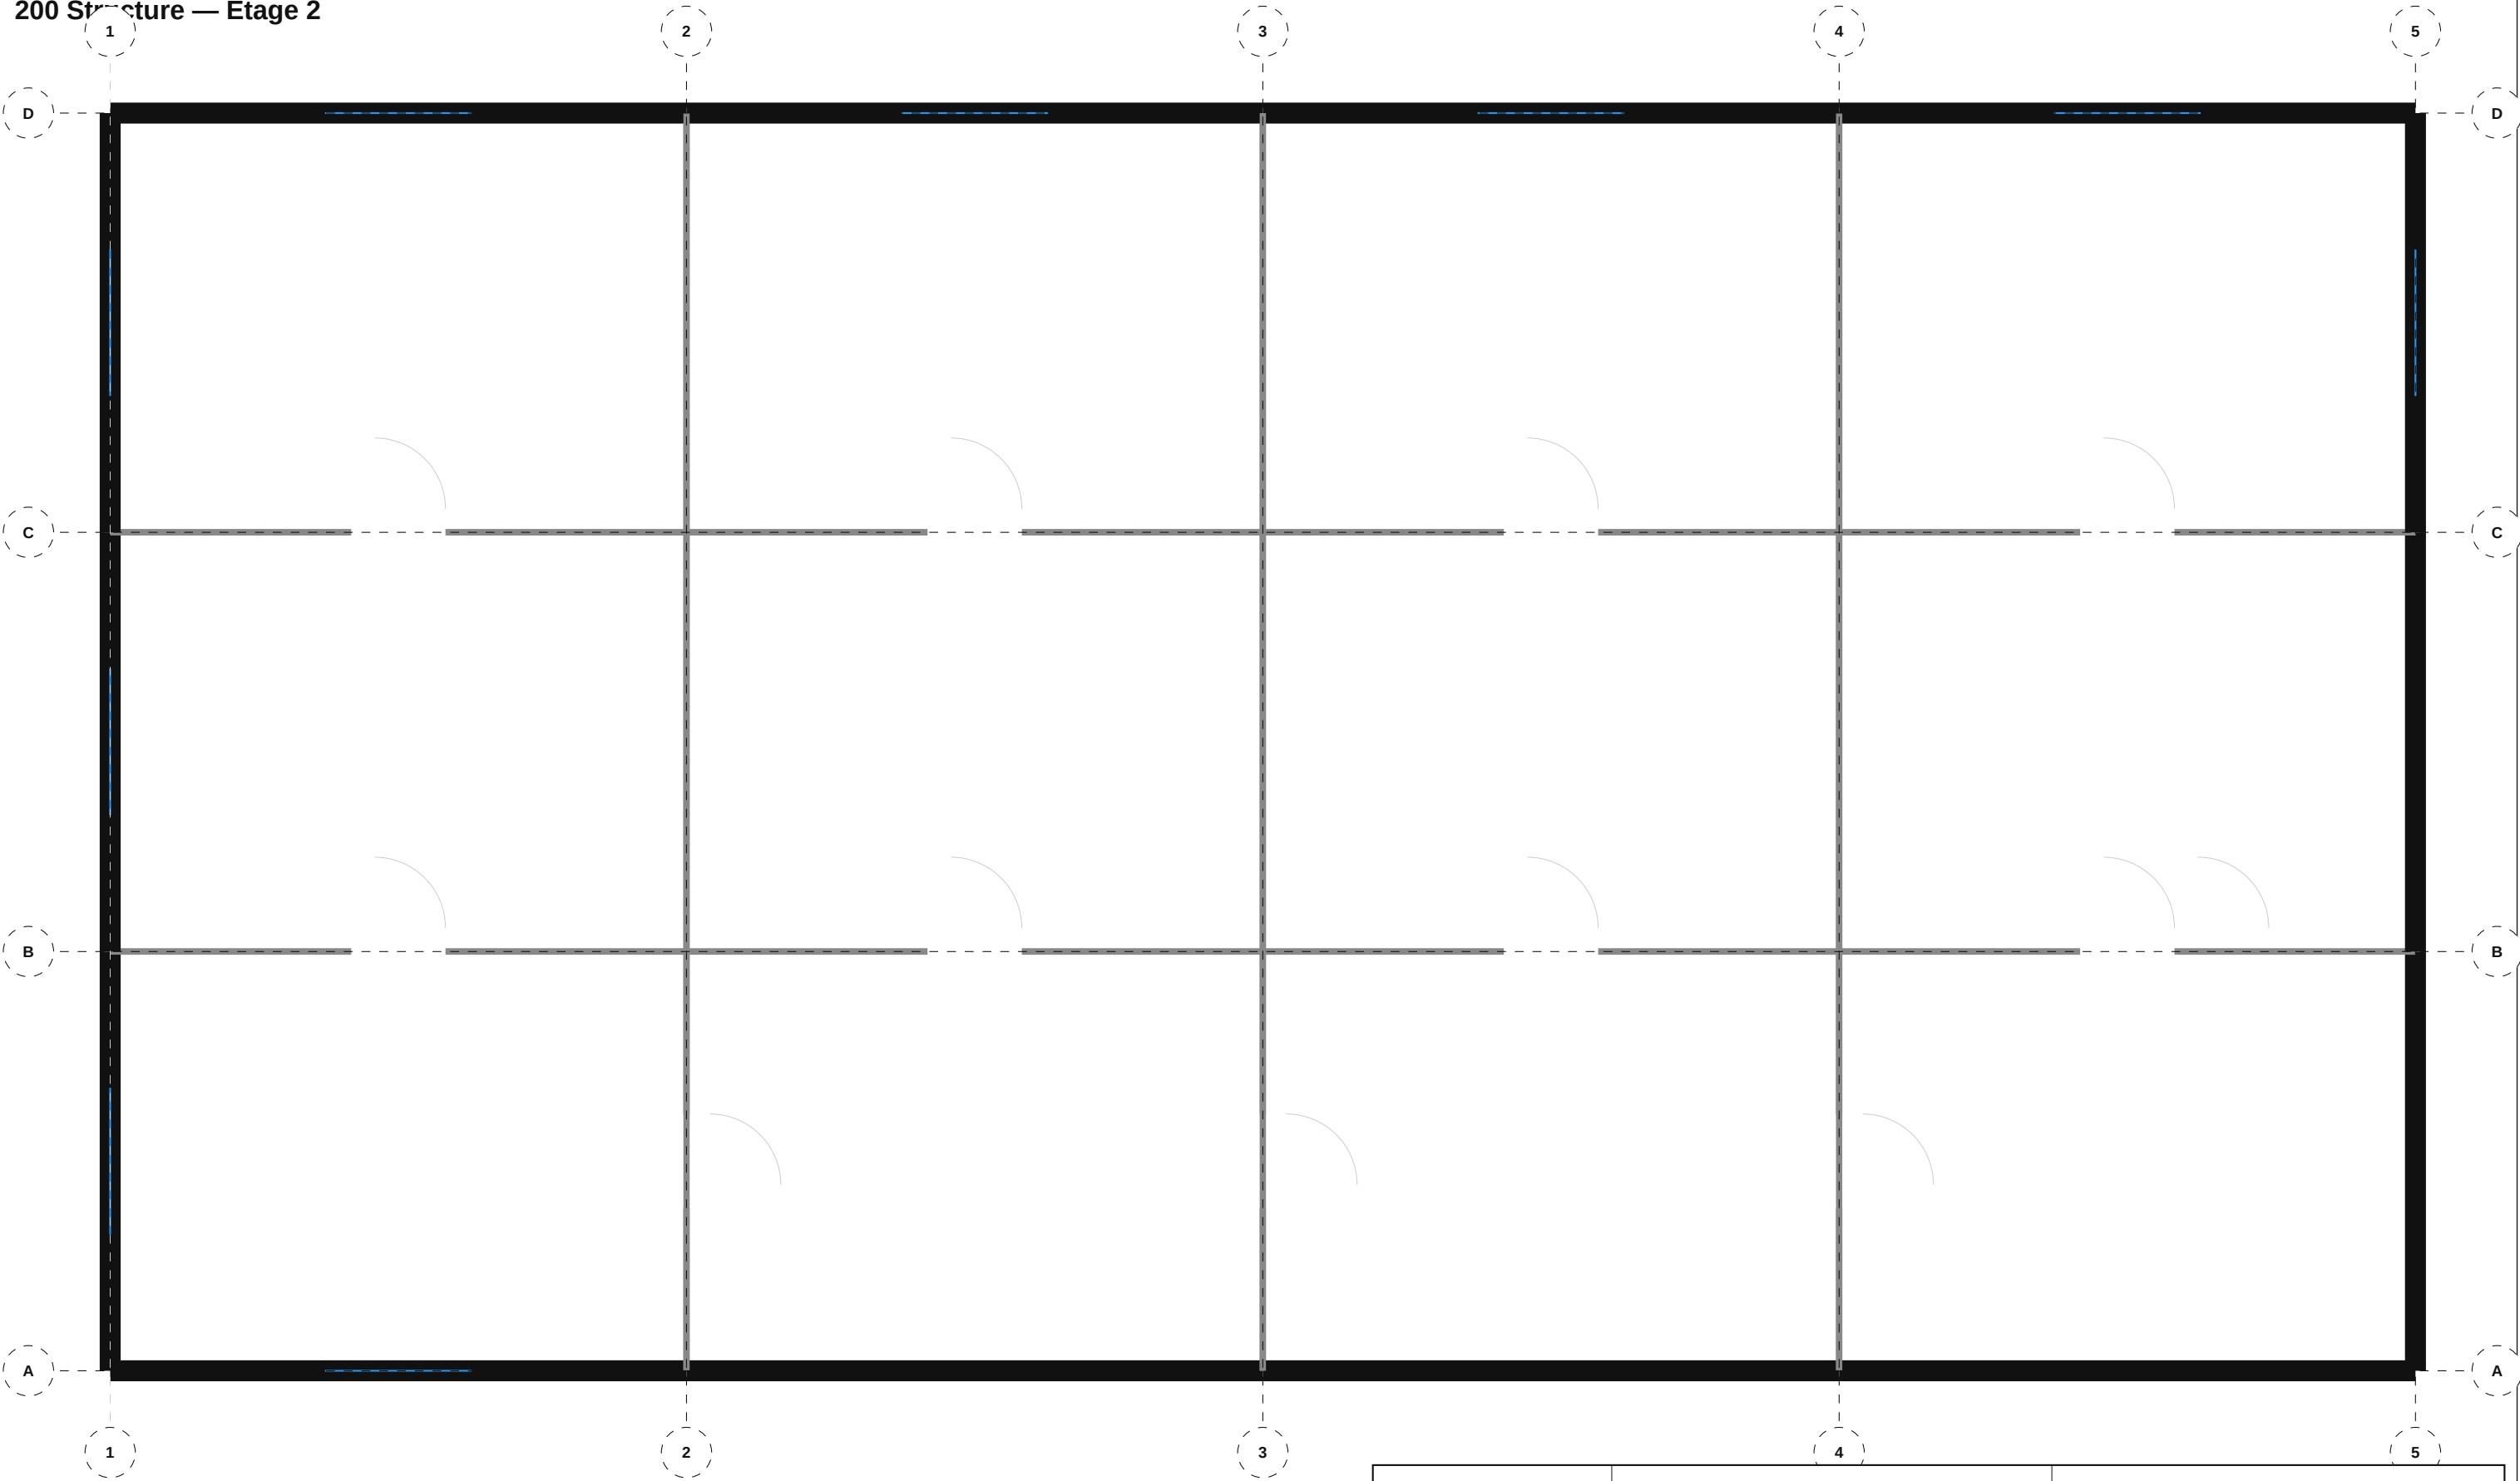


|                                                           |                                                                 |                                               |
|-----------------------------------------------------------|-----------------------------------------------------------------|-----------------------------------------------|
| <div>TIJAN AI</div> <div>Bureau d'Études Automatisé</div> | <div>Résidence Papa Oumar Sakho</div> <div>Dakar, Senegal</div> | <div>Éch: 1/100</div> <div>Pl. 7/32</div>     |
|                                                           | Structure — Étage 2                                             |                                               |
| Date: 06/05/2026                                          | Réf: STR                                                        | <div>BIM vSTR-007</div> <div>Phase: APD</div> |

## 200 Structure — Étage 3

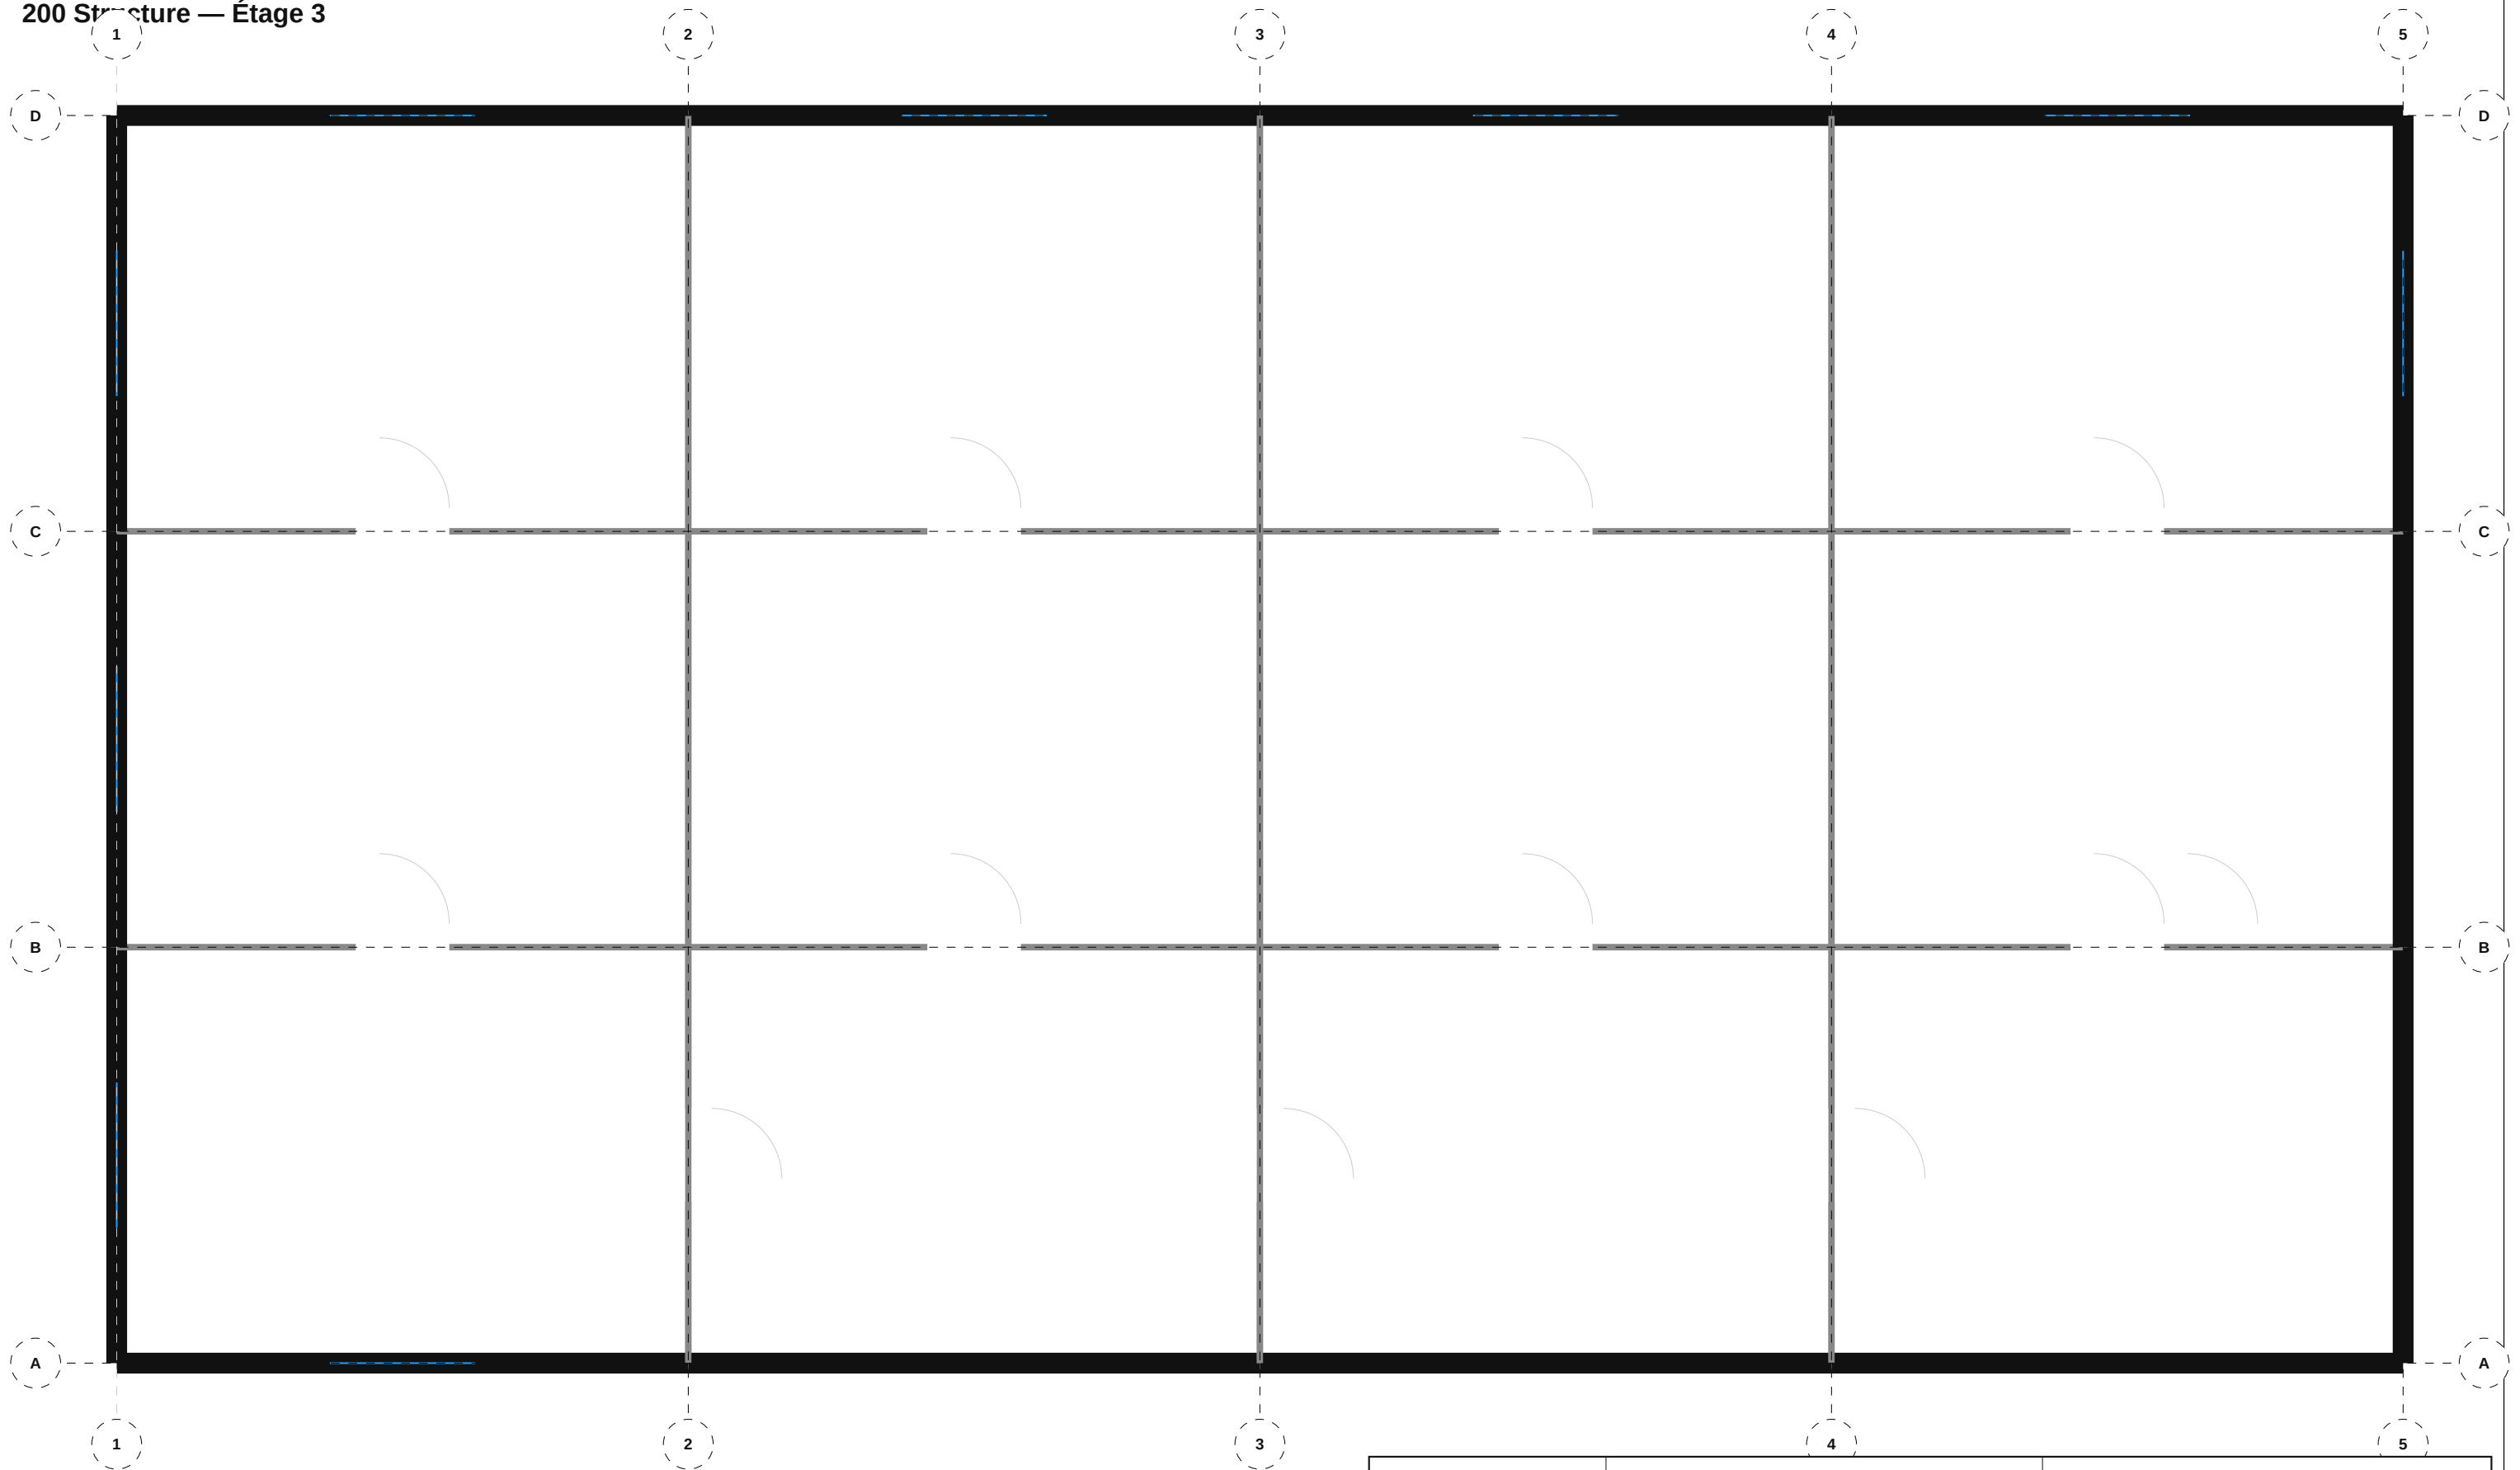


|                                                                                |                                                                           |                                                         |
|--------------------------------------------------------------------------------|---------------------------------------------------------------------------|---------------------------------------------------------|
| <div><div><div>TIJAN AI</div><div>Bureau d'Études Automatisé</div></div></div> | <div><div>Résidence Papa Oumar Sakho</div><div>Dakar, Senegal</div></div> | <div><div>Éch: 1/100</div><div>Pl. 8/32</div></div>     |
|                                                                                | <div>Structure — Étage 3</div>                                            |                                                         |
| <div>Date: 06/05/2026</div>                                                    | <div>Réf: STR</div>                                                       | <div><div>BIM vSTR-008</div><div>Phase: APD</div></div> |



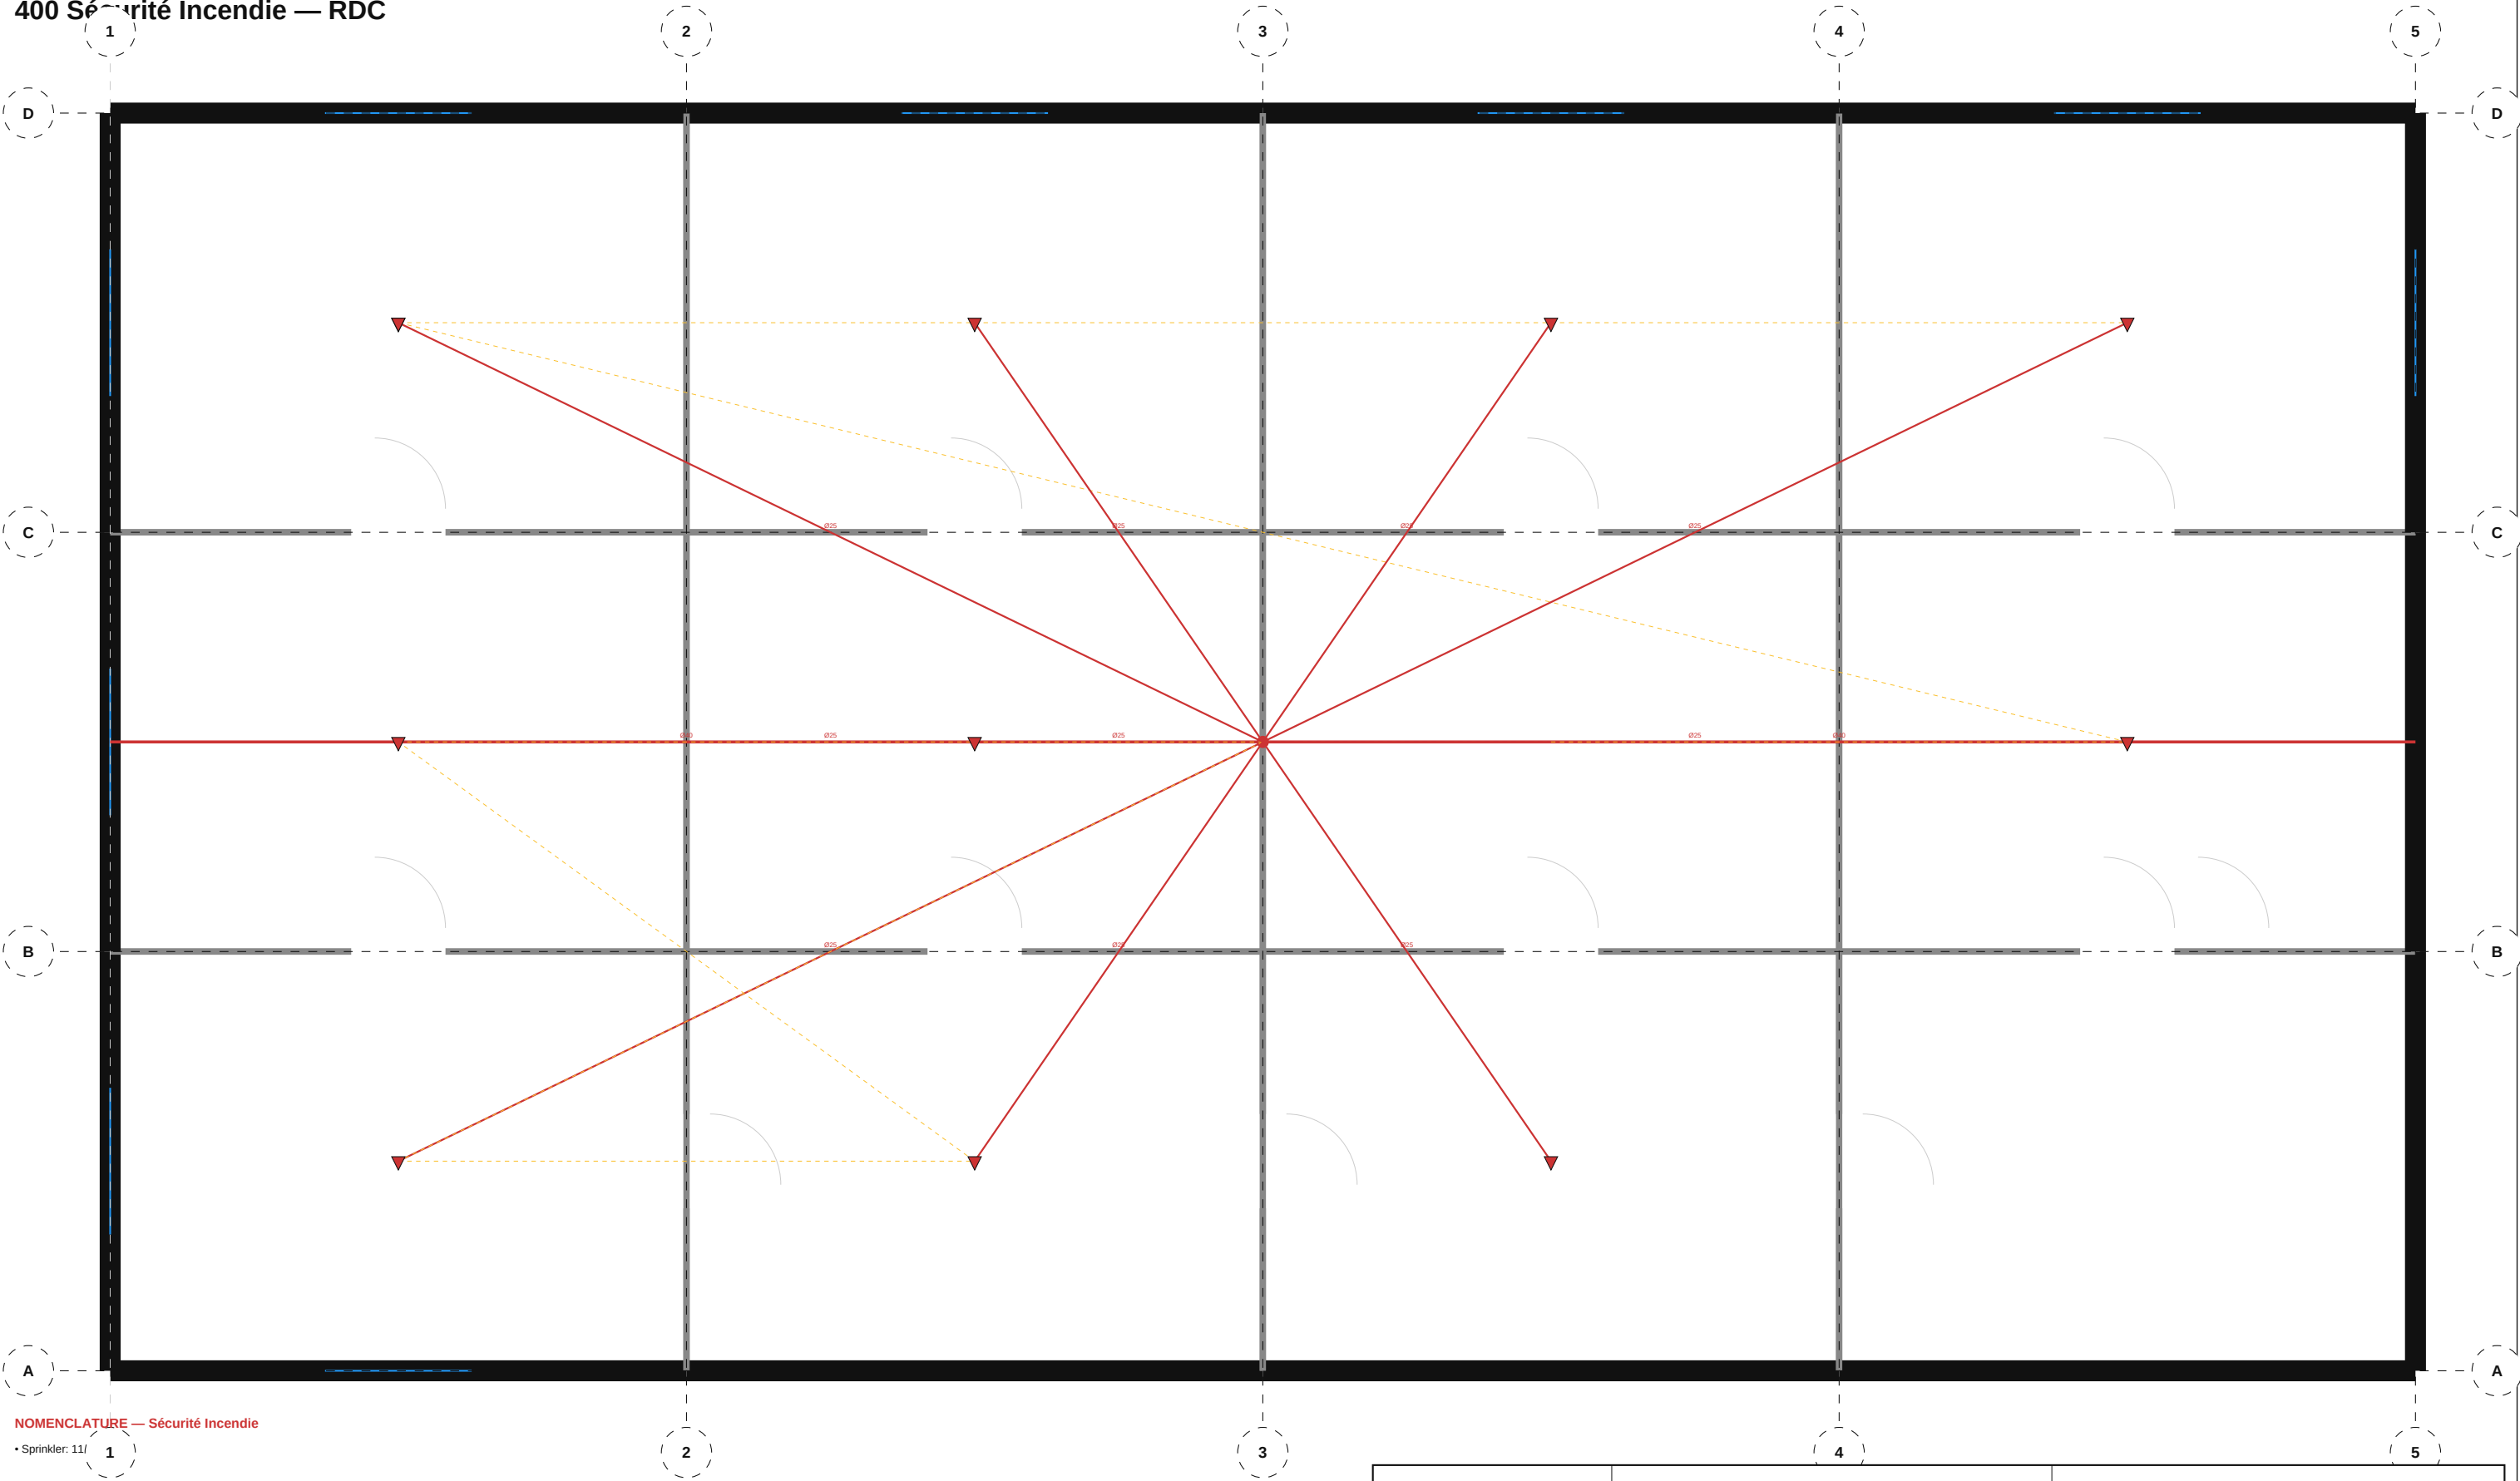


|                                               |                                                     |                            |
|-----------------------------------------------|-----------------------------------------------------|----------------------------|
| <b>TIJAN AI</b><br>Bureau d'Études Automatisé | <b>Résidence Papa Oumar Sakho</b><br>Dakar, Senegal | Éch: 1/100<br>Pl. 9/32     |
|                                               | <b>Sécurité Incendie — RDC</b>                      |                            |
| Date: 06/05/2026                              | Réf: FIF                                            | BIM VFIF-009<br>Phase: APD |

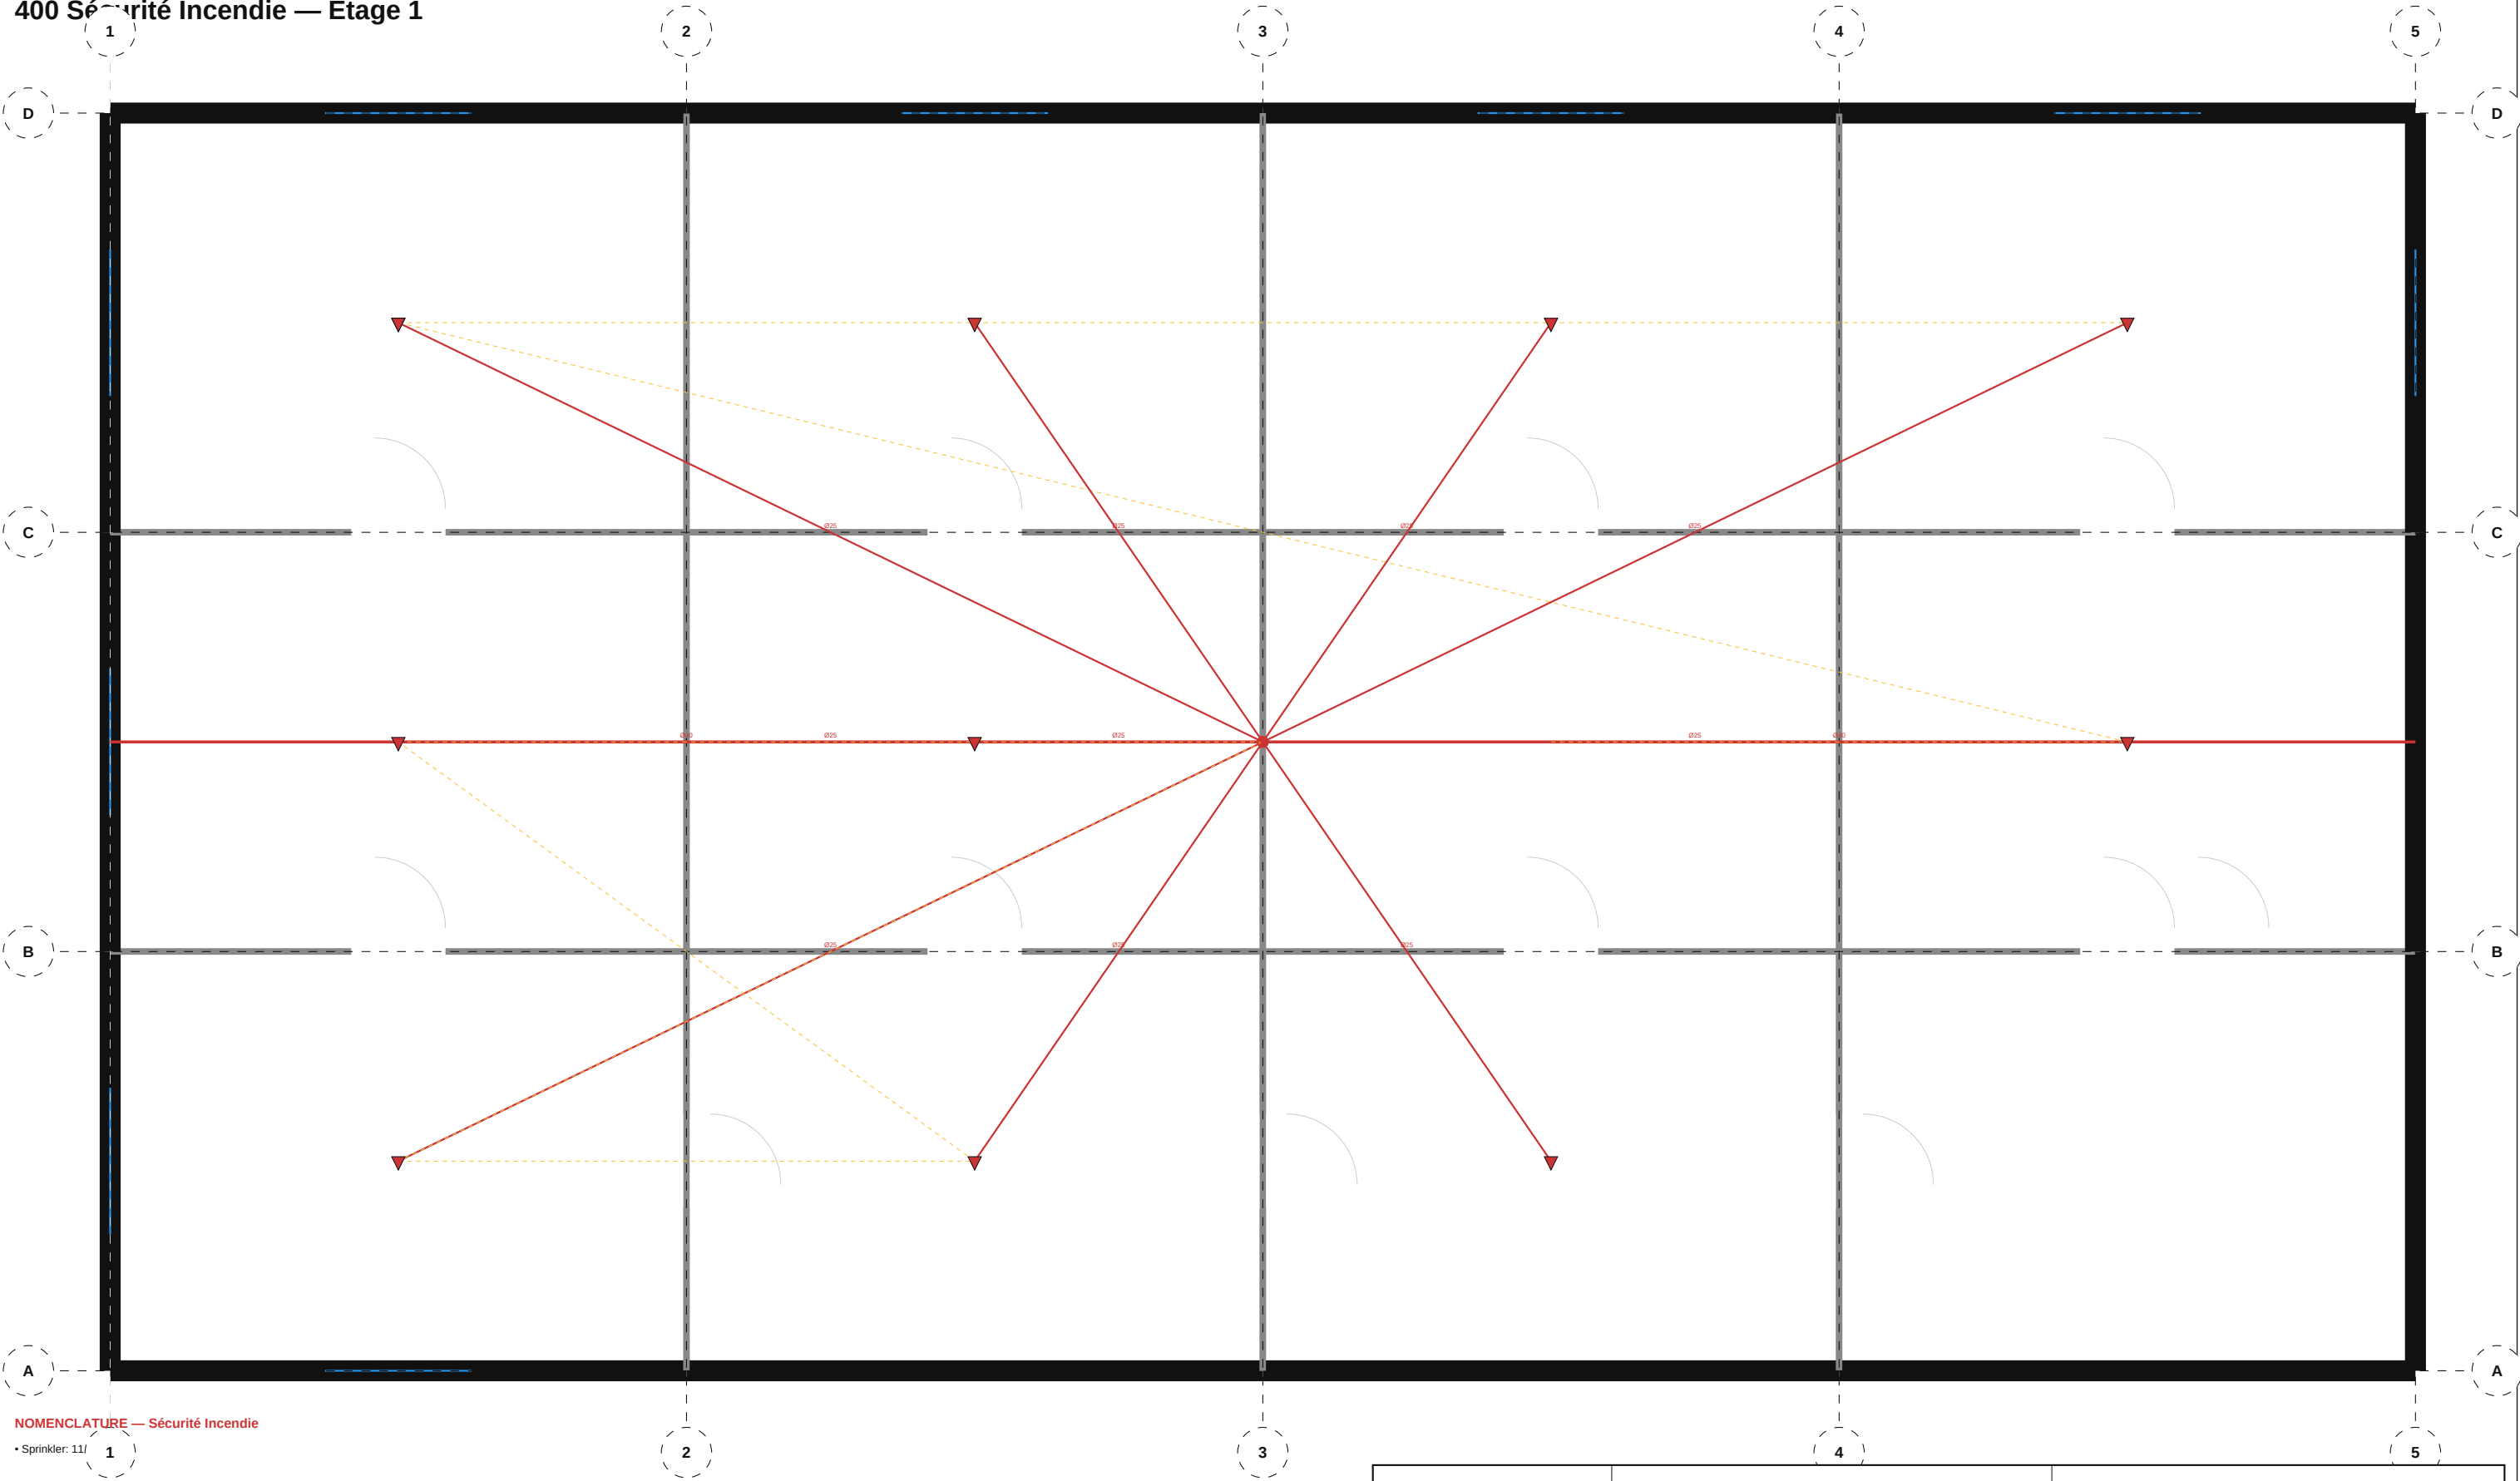

NOMENCLATURE — Sécurité Incendie

• Sprinkler: 11/


|                                                           |                                                                 |                                               |
|-----------------------------------------------------------|-----------------------------------------------------------------|-----------------------------------------------|
| <div>TIJAN AI</div> <div>Bureau d'Études Automatisé</div> | <div>Résidence Papa Oumar Sakho</div> <div>Dakar, Senegal</div> | <div>Éch: 1/100</div> <div>Pl. 10/32</div>    |
|                                                           | <div>Sécurité Incendie — Étage 1</div>                          |                                               |
| <div>Date: 06/05/2026</div>                               | <div>Réf: FIF</div>                                             | <div>BIM VFIF-010</div> <div>Phase: APD</div> |

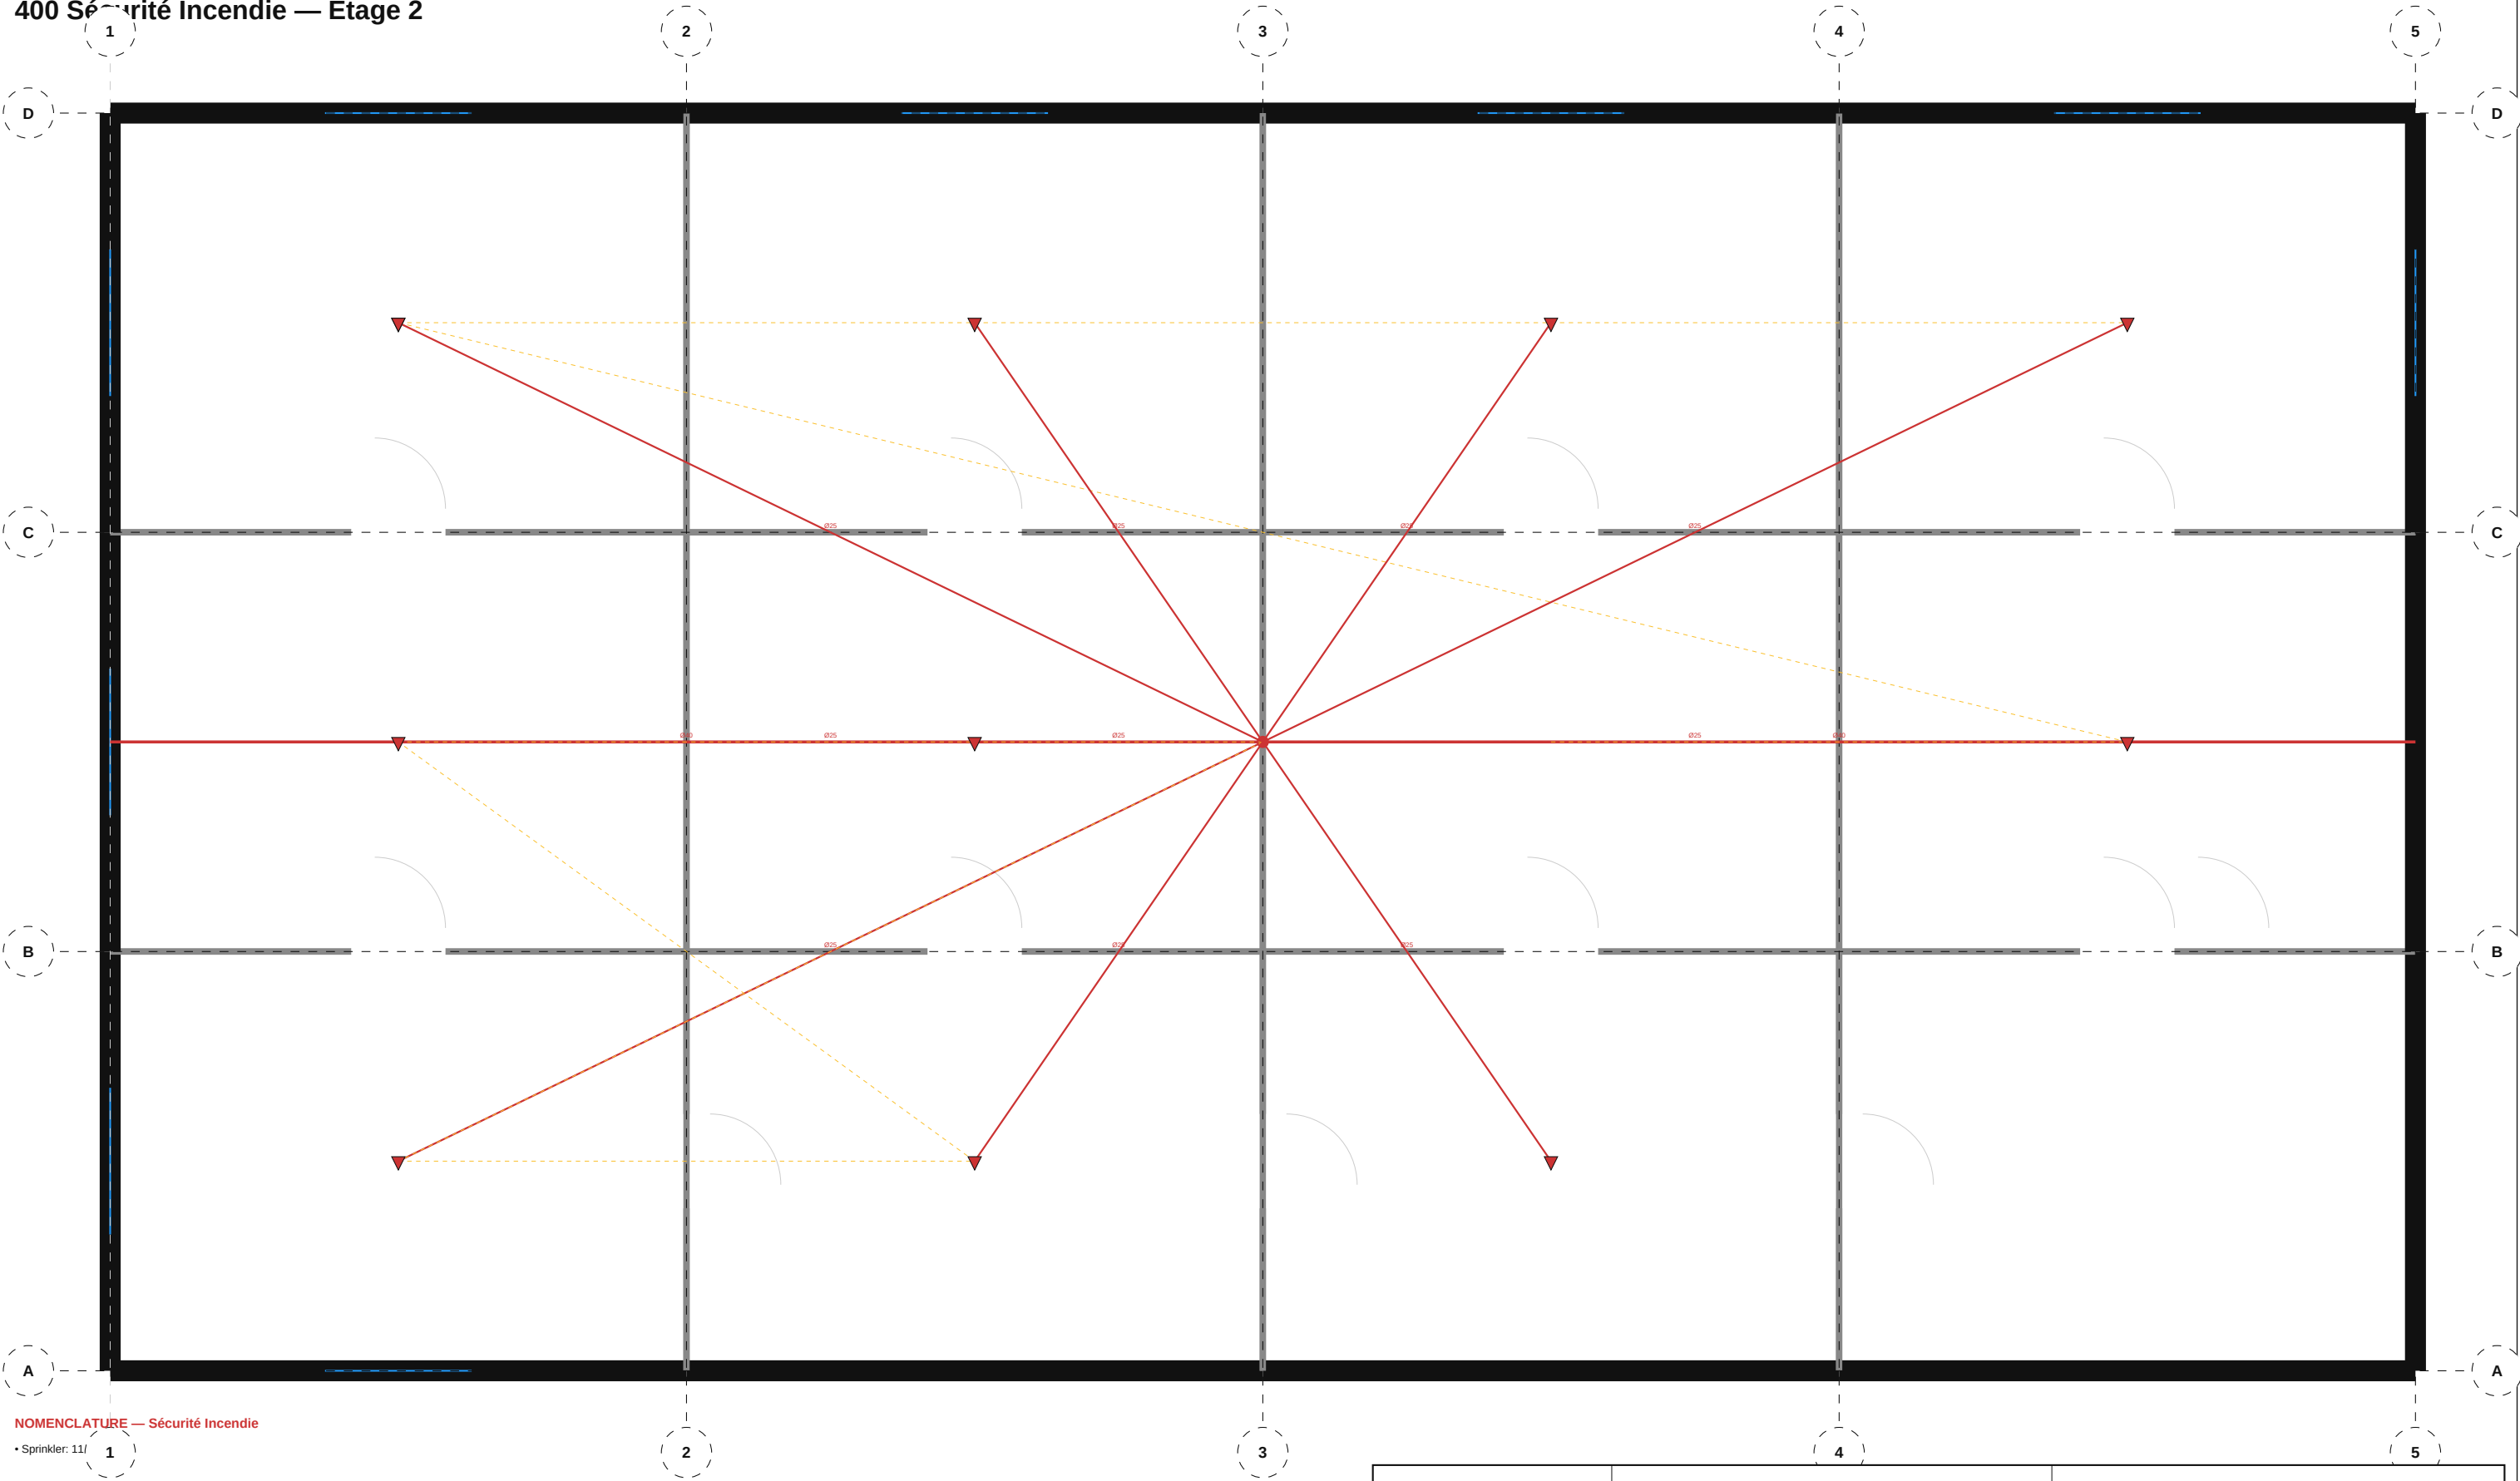

NOMENCLATURE — Sécurité Incendie

• Sprinkler: 11/

|                                                                     |                                                                 |                                               |
|---------------------------------------------------------------------|-----------------------------------------------------------------|-----------------------------------------------|
| <div><div>TIJAN AI</div><div>Bureau d'Études Automatisé</div></div> | <div>Résidence Papa Oumar Sakho</div> <div>Dakar, Senegal</div> | <div>Éch: 1/100</div> <div>Pl. 11/32</div>    |
|                                                                     | <div>Sécurité Incendie — Étage 2</div>                          |                                               |
| <div>Date: 06/05/2026</div>                                         | <div>Réf: FIF</div>                                             | <div>BIM VFIF-011</div> <div>Phase: APD</div> |

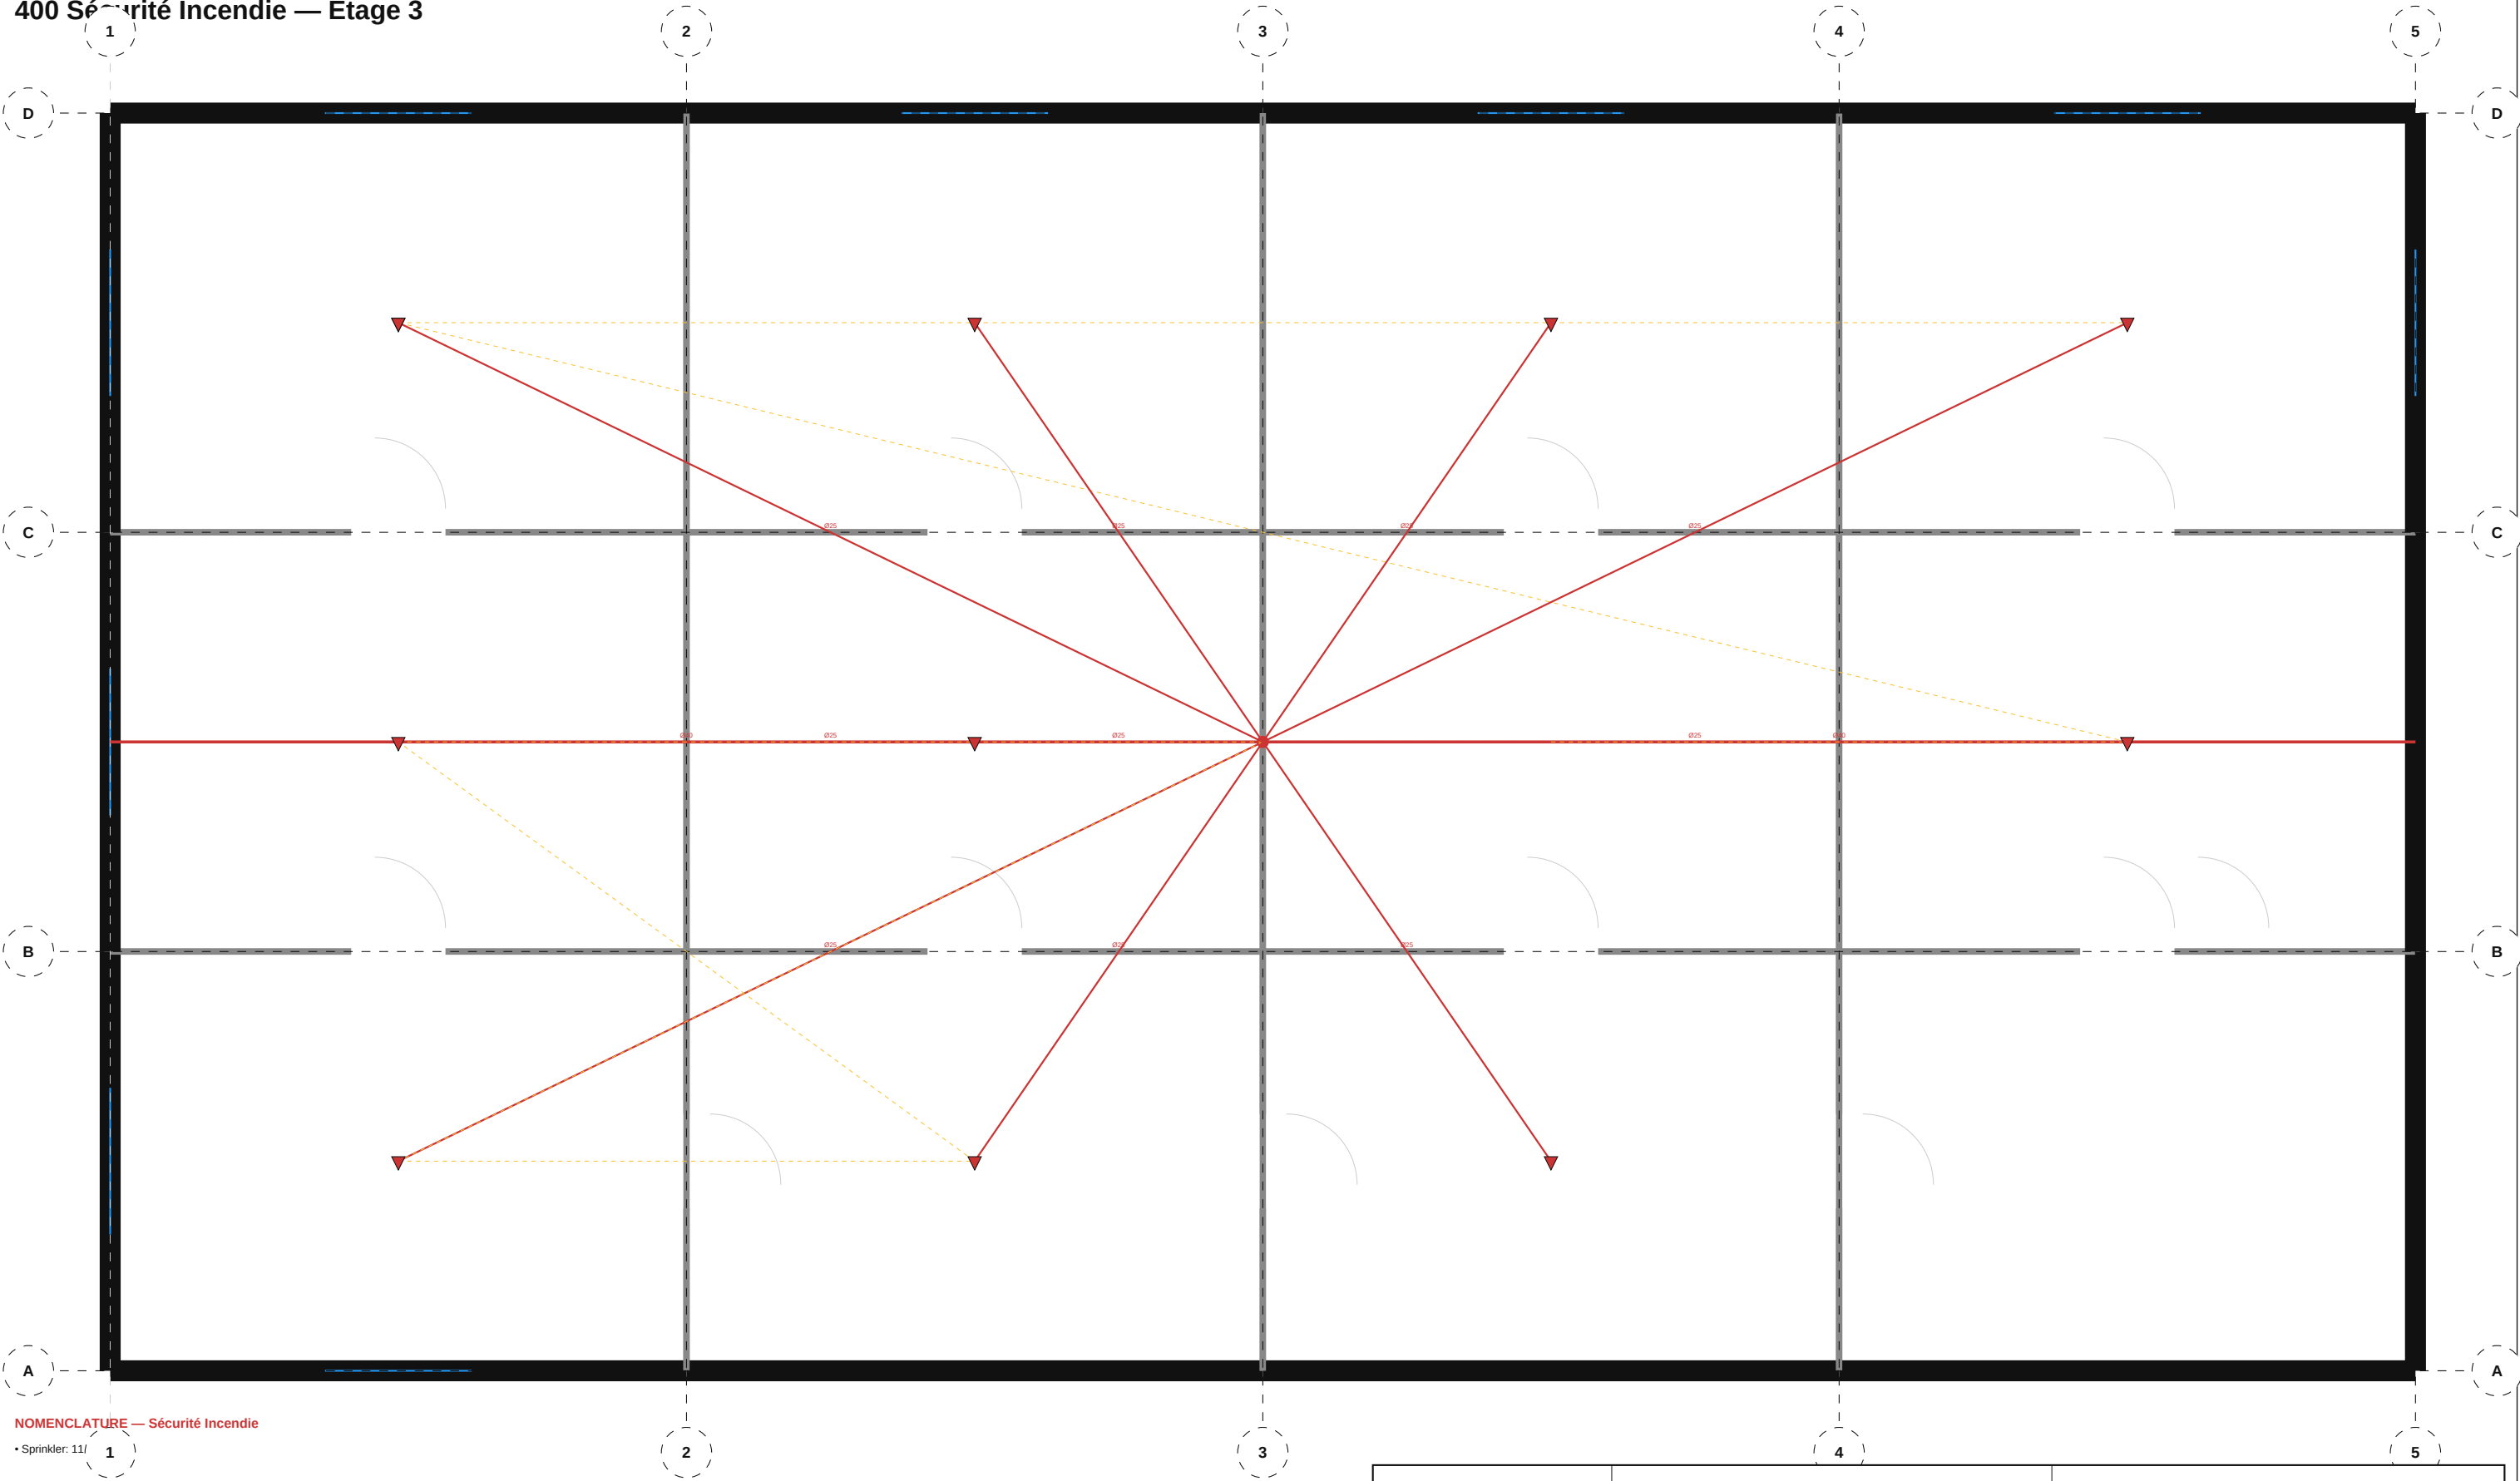

NOMENCLATURE — Sécurité Incendie


• Sprinkler: 11/

|                                                           |                                                                 |                                               |
|-----------------------------------------------------------|-----------------------------------------------------------------|-----------------------------------------------|
| <div>TIJAN AI</div> <div>Bureau d'Études Automatisé</div> | <div>Résidence Papa Oumar Sakho</div> <div>Dakar, Senegal</div> | <div>Éch: 1/100</div> <div>Pl. 12/32</div>    |
|                                                           | <div>Sécurité Incendie — Étage 3</div>                          |                                               |
| <div>Date: 06/05/2026</div>                               | <div>Réf: FIF</div>                                             | <div>BIM VFIF-012</div> <div>Phase: APD</div> |

NOMENCLATURE — Plomberie

- Douche: 1
- Lavabo: 1
- Lave-mains: 1
- Lave-vaisselle: 1
- WC suspendu: 2
- Évier cuisine: 1

|                                                           |                                                                 |                                               |
|-----------------------------------------------------------|-----------------------------------------------------------------|-----------------------------------------------|
| <div>TIJAN AI</div> <div>Bureau d'Études Automatisé</div> | <div>Résidence Papa Oumar Sakho</div> <div>Dakar, Senegal</div> | <div>Éch: 1/100</div> <div>Pl. 13/32</div>    |
|                                                           | <div>Plomberie — RDC</div>                                      |                                               |
| <div>Date: 06/05/2026</div>                               | <div>Réf: PLU</div>                                             | <div>BIM vPLU-013</div> <div>Phase: APD</div> |

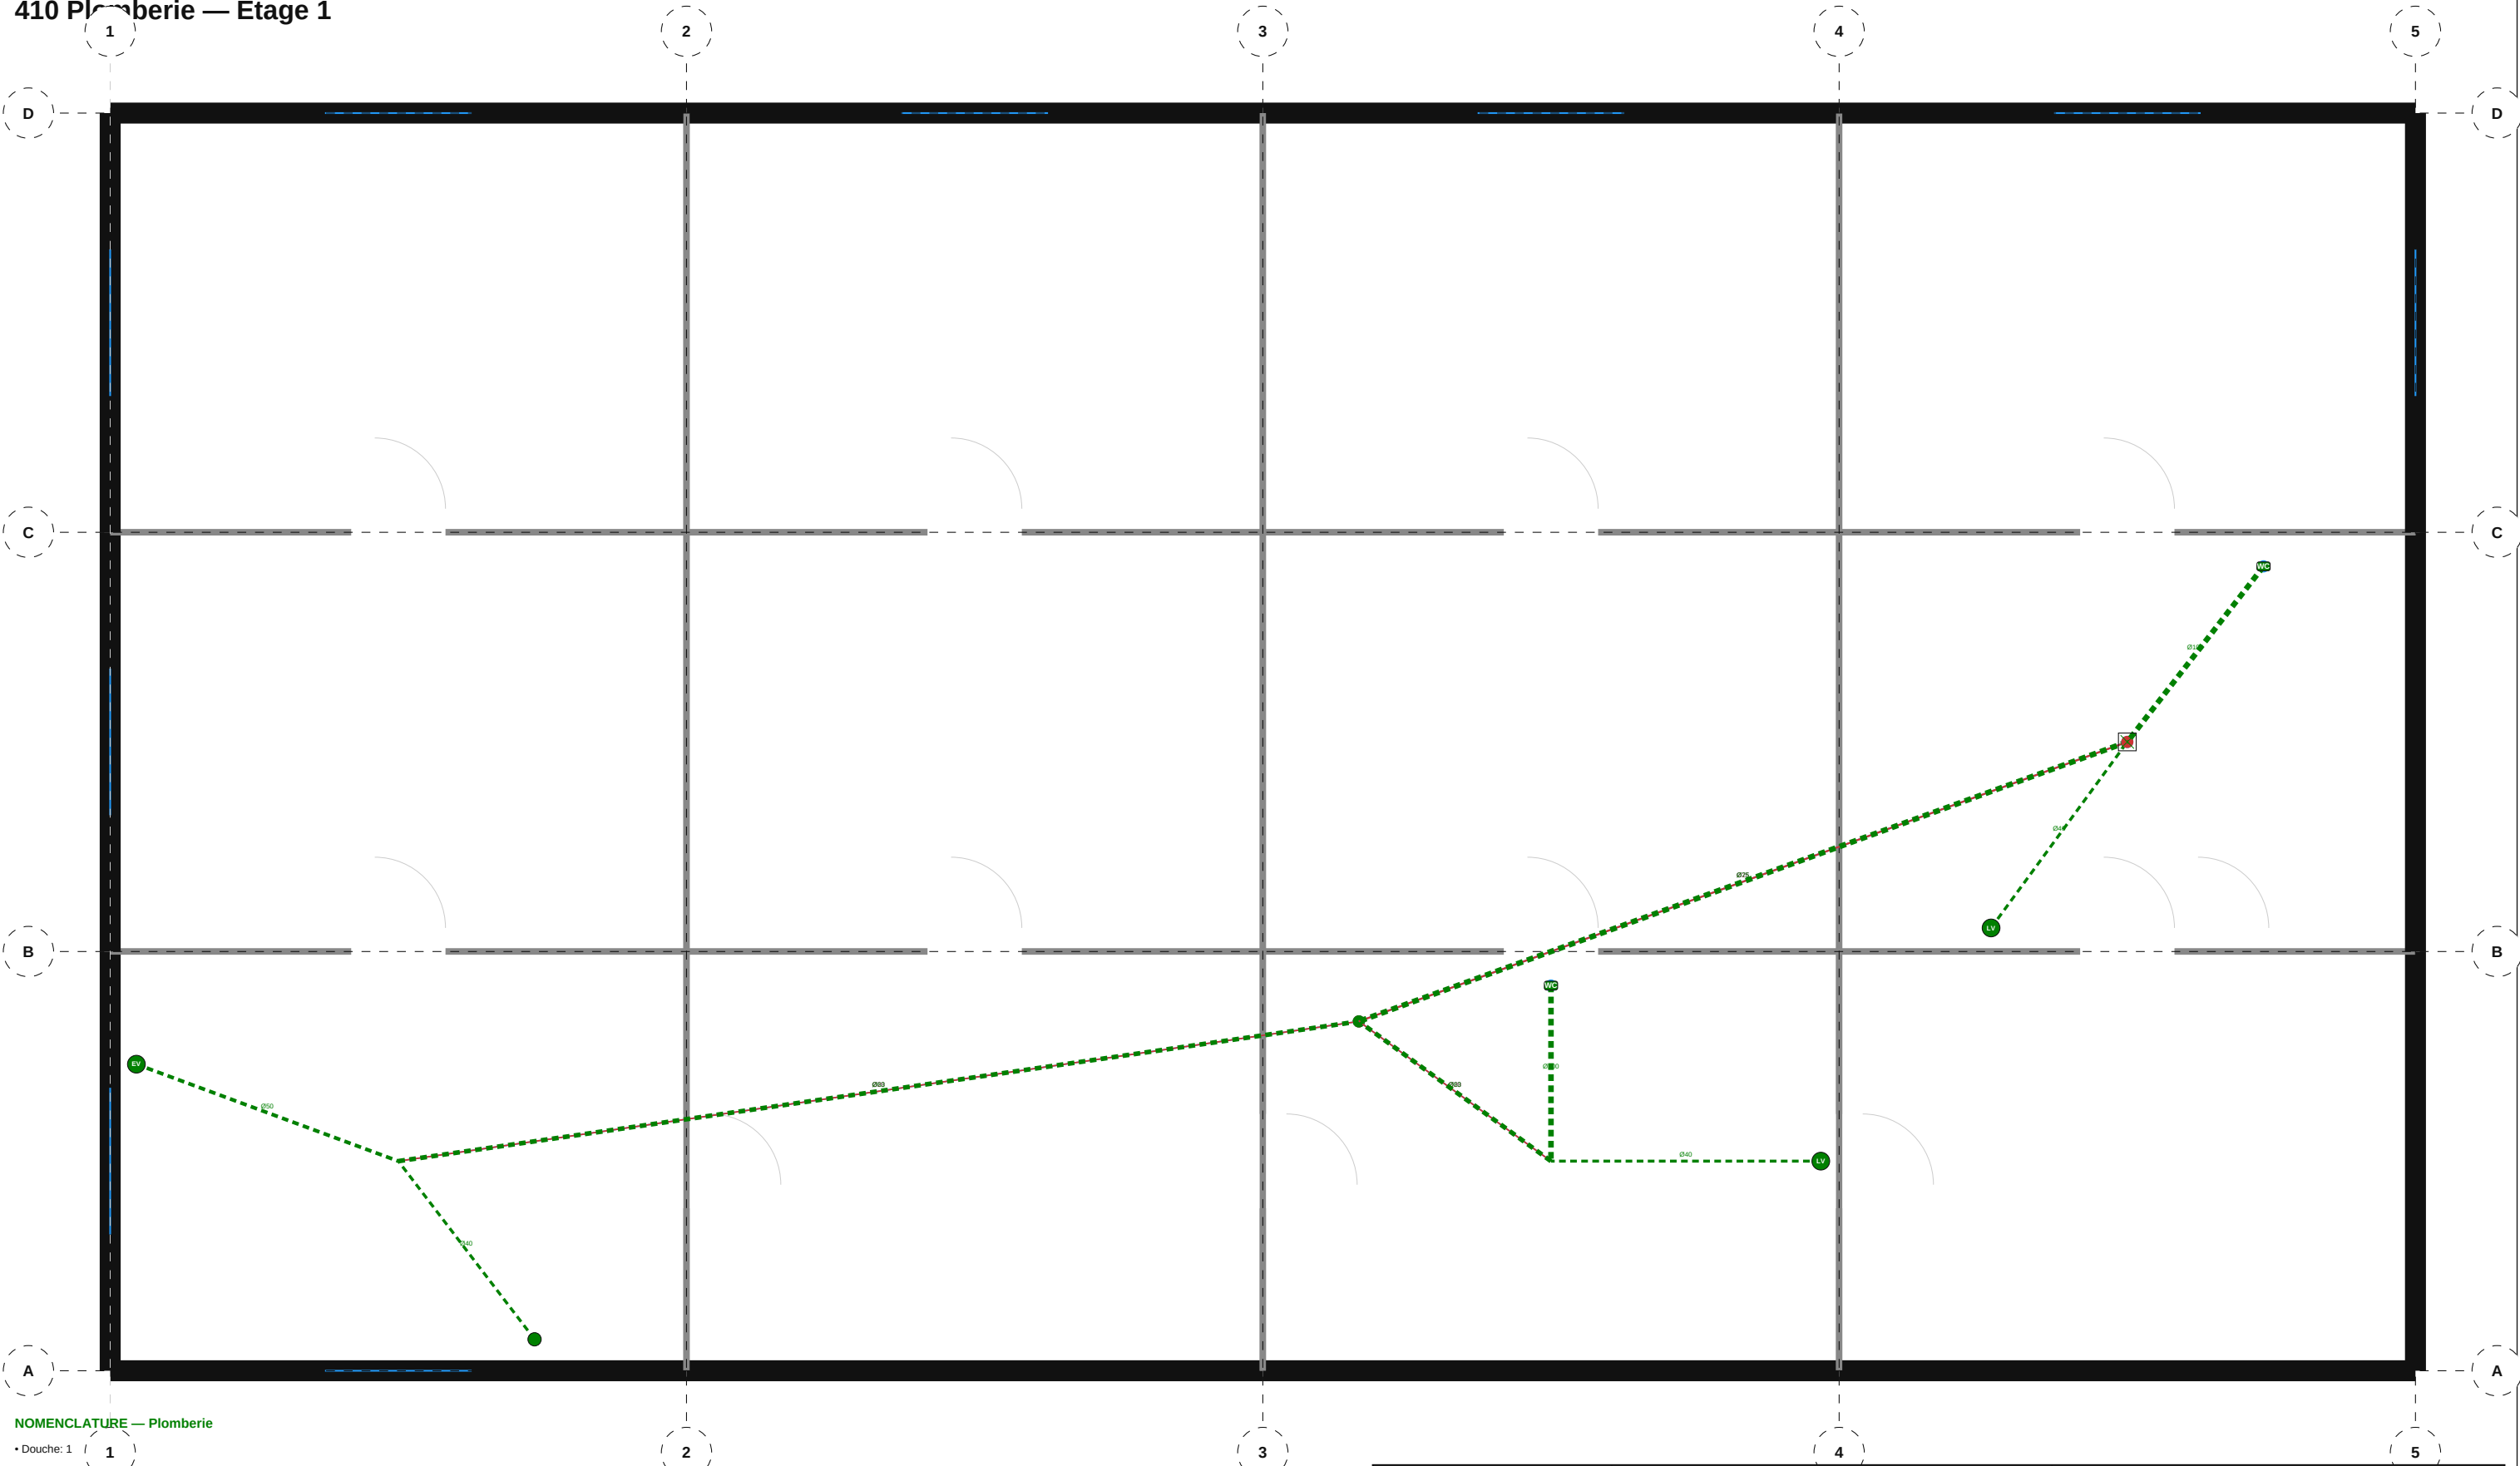

NOMENCLATURE — Plomberie

- Douche: 1
- Lavabo: 1
- Lave-mains: 1
- Lave-vaisselle: 1
- WC suspendu: 2
- Évier cuisine: 1

TIJAN AI

Bureau d'Études Automatisé

Résidence Papa Oumar Sakho

Dakar, Senegal

Éch: 1/100

Pl. 14/32

Plomberie — Étage 1


Date: 06/05/2026

Réf: PLU

BIM vPLU-014

Phase: APD



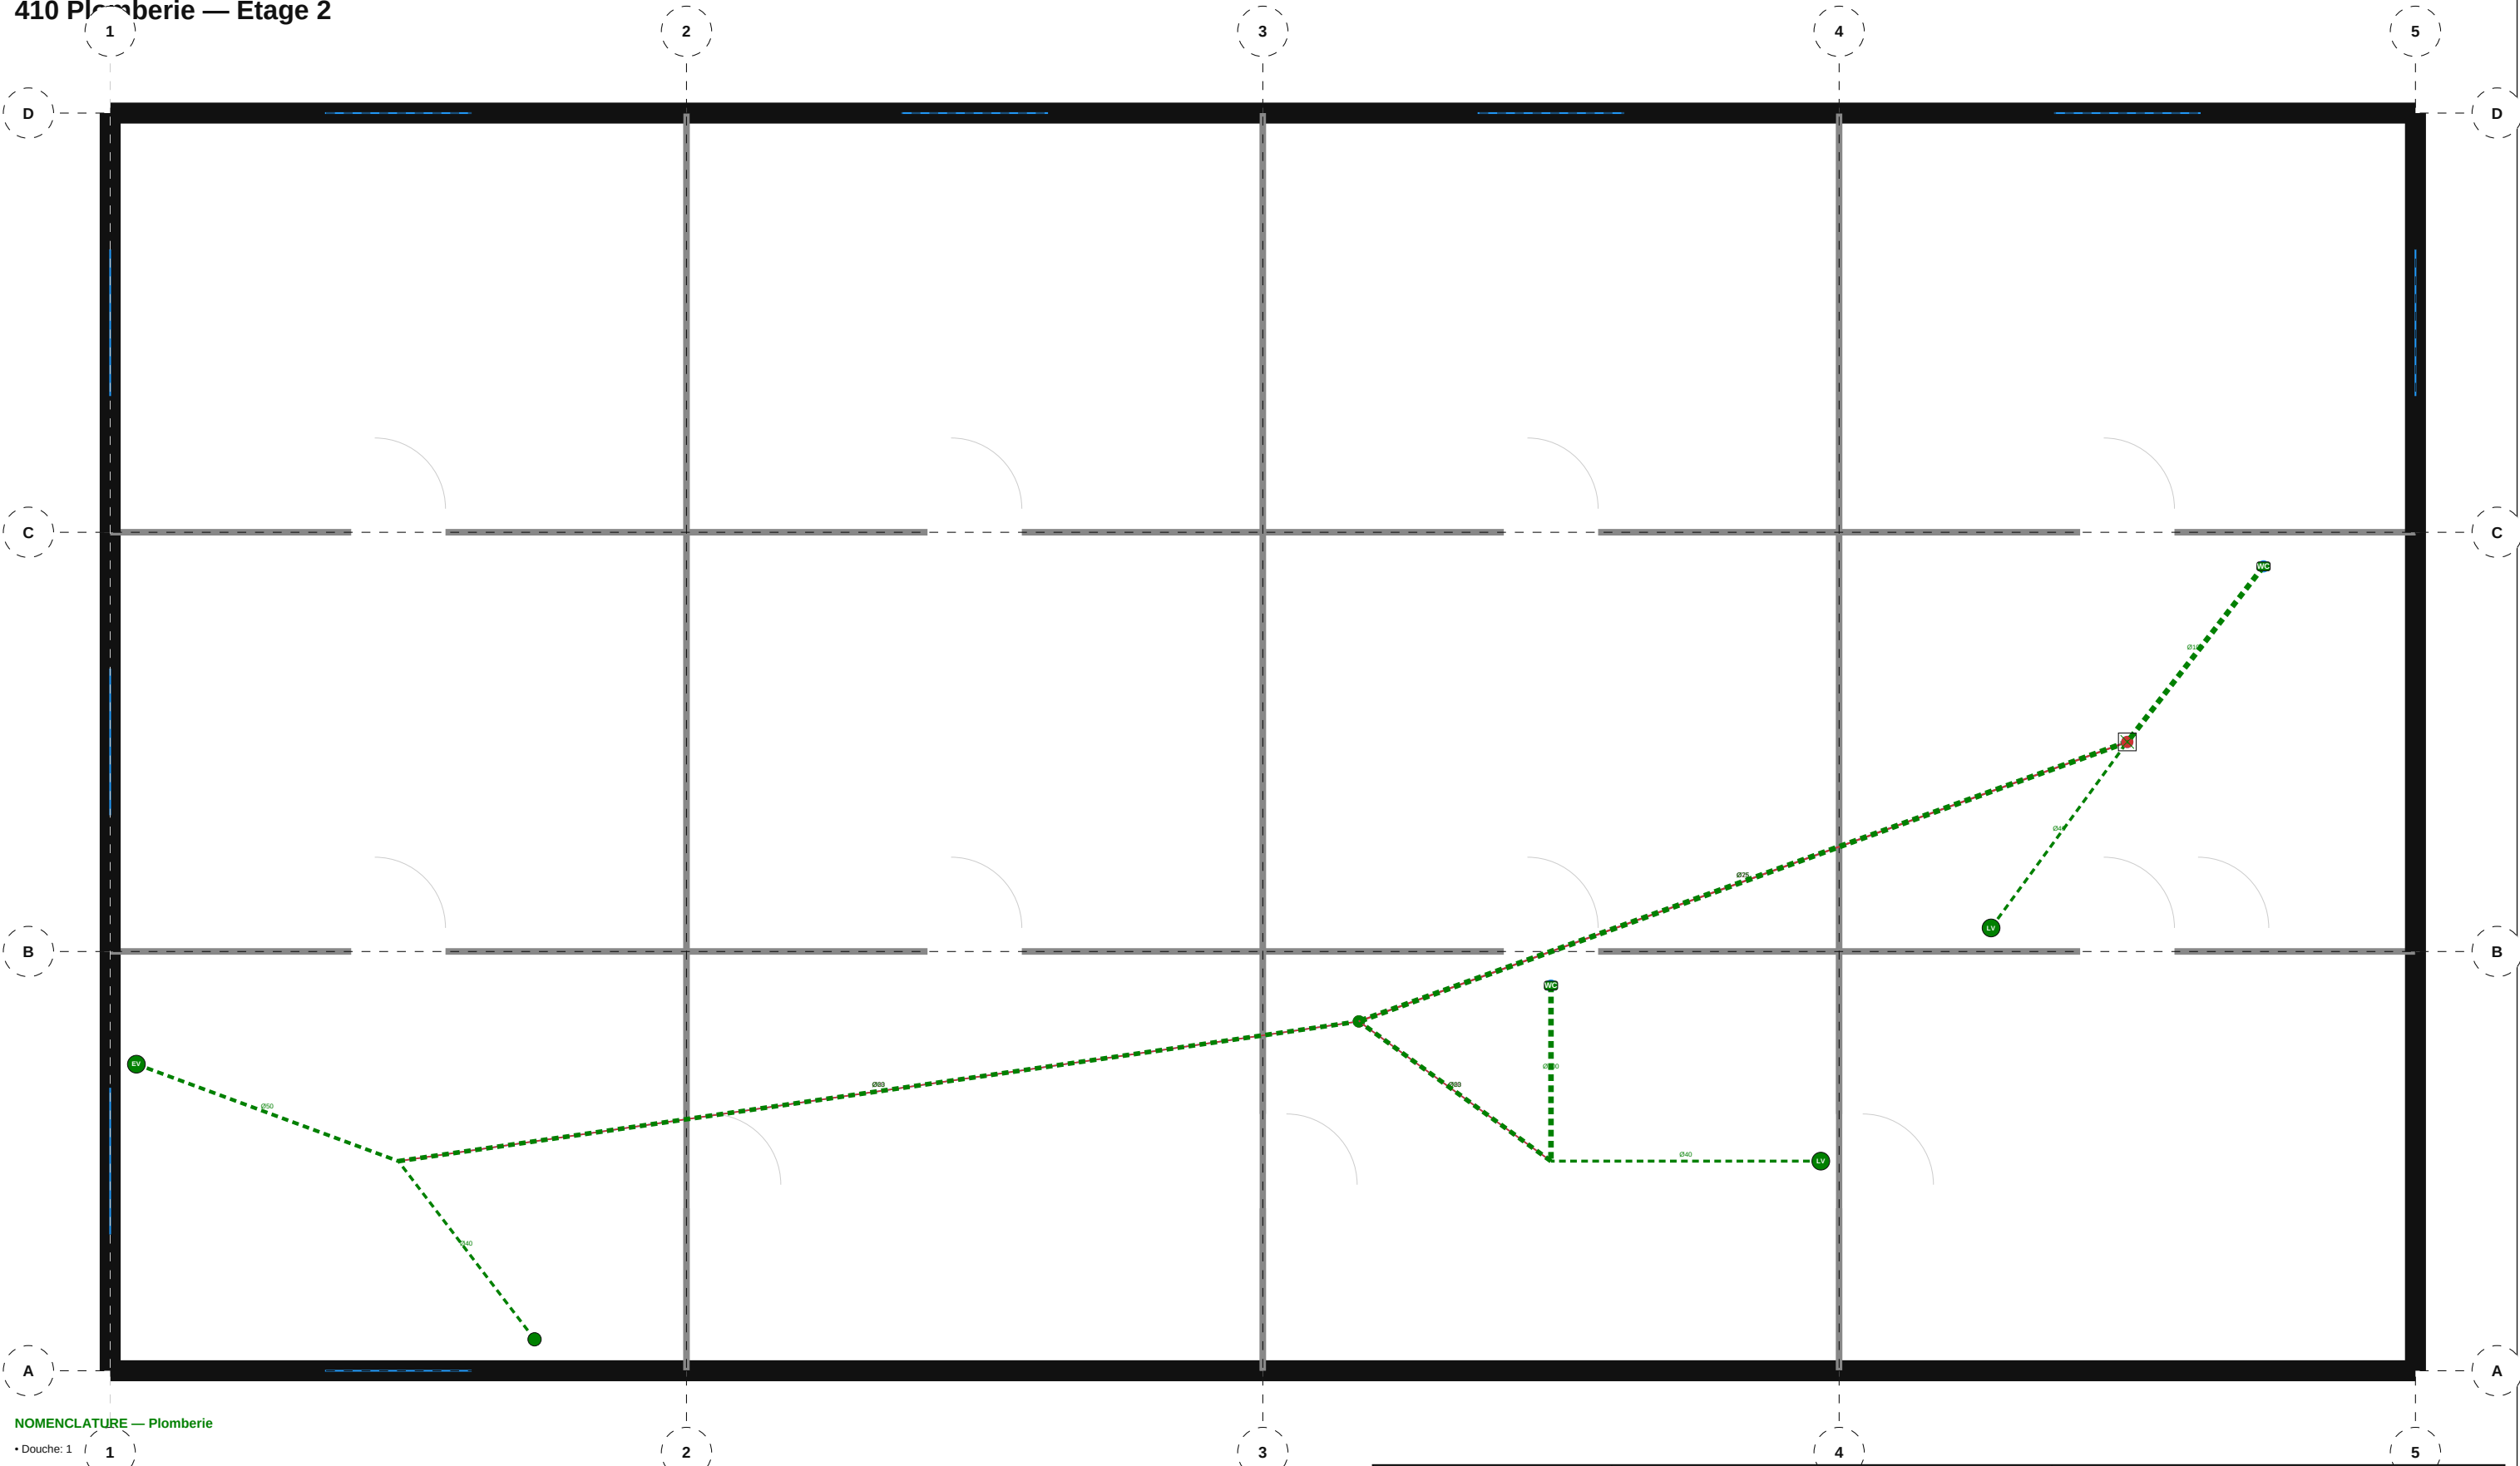


NOMENCLATURE — Plomberie

- Douche: 1
- Lavabo: 1
- Lave-mains: 1
- Lave-vaisselle: 1
- WC suspendu: 2
- Évier cuisine: 1

|                                                           |                                                                 |                                               |
|-----------------------------------------------------------|-----------------------------------------------------------------|-----------------------------------------------|
| <div>TIJAN AI</div> <div>Bureau d'Études Automatisé</div> | <div>Résidence Papa Oumar Sakho</div> <div>Dakar, Senegal</div> | <div>Éch: 1/100</div> <div>Pl. 15/32</div>    |
|                                                           | <div>Plomberie — Étage 2</div>                                  |                                               |
| <div>Date: 06/05/2026</div>                               | <div>Réf: PLU</div>                                             | <div>BIM vPLU-015</div> <div>Phase: APD</div> |

### 410 Plomberie — Étage 3

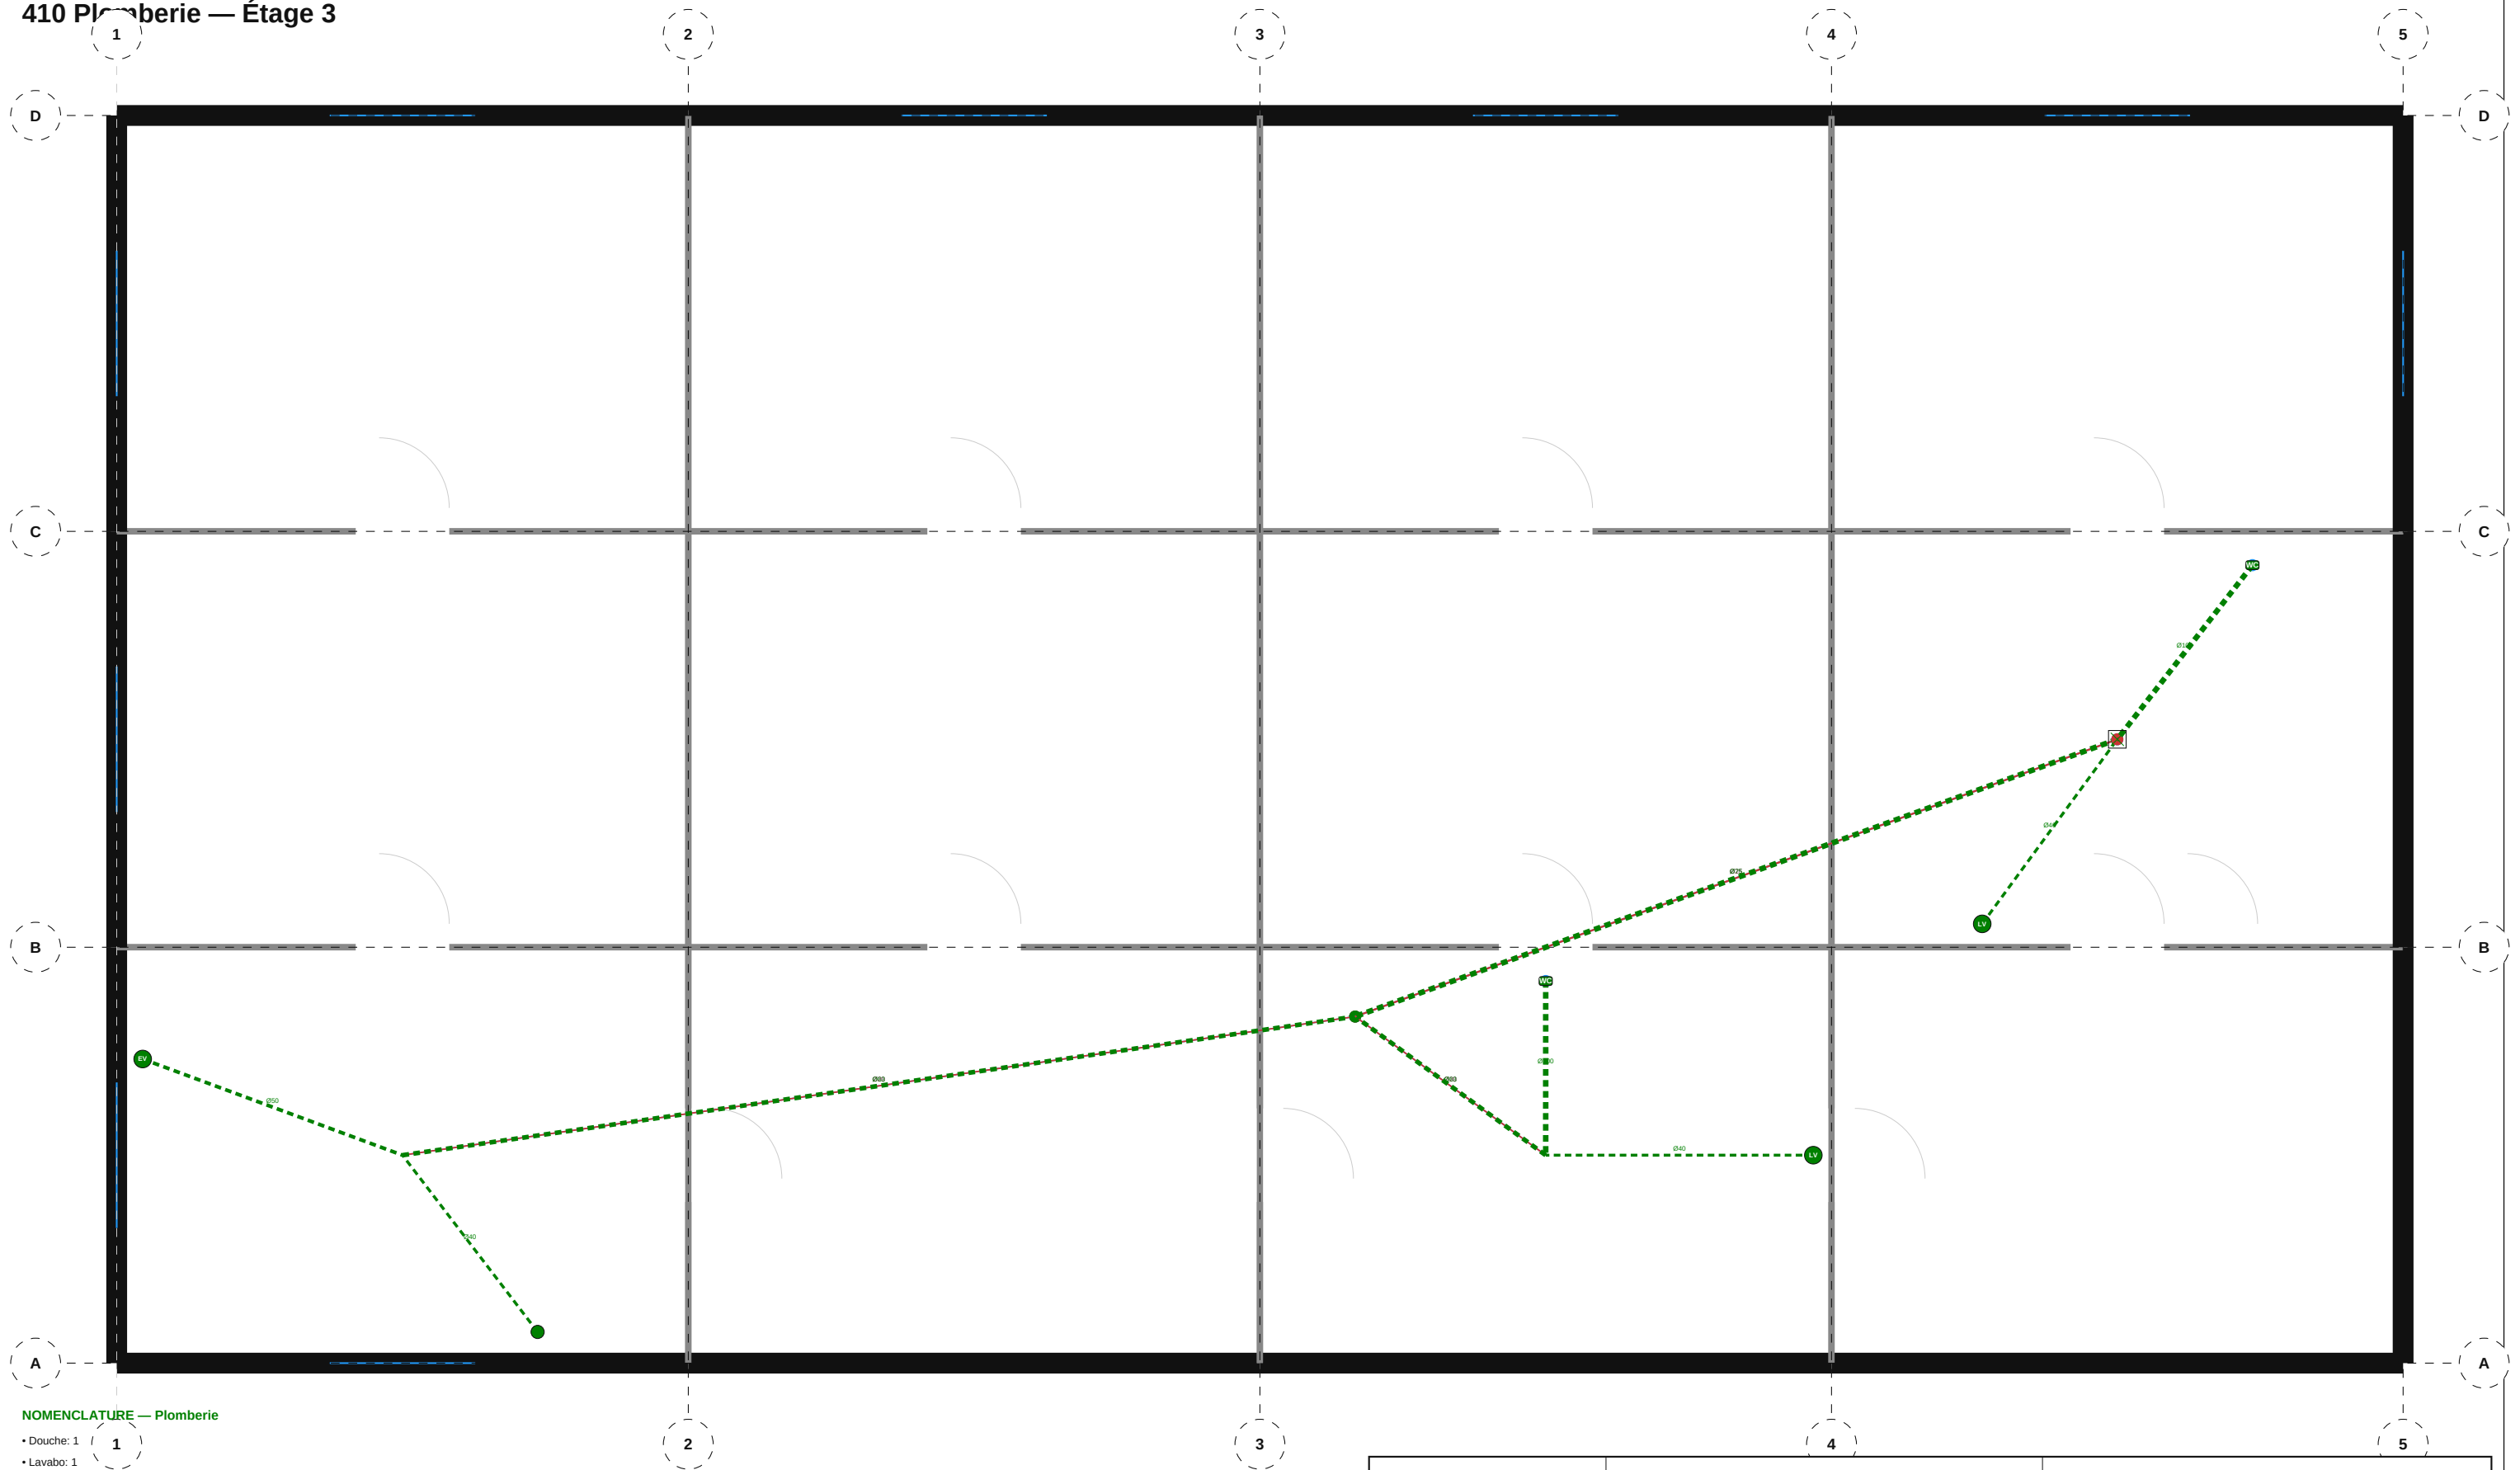


## NOMENCLATURE — Plomberie

- Douche: 1
- Lavabo: 1
- Lave-mains: 1
- Lave-vaisselle: 1
- WC suspendu: 2
- Évier cuisine: 1

|                                                                                |                                                                           |                                                         |
|--------------------------------------------------------------------------------|---------------------------------------------------------------------------|---------------------------------------------------------|
| <div><div><div>TIJAN AI</div><div>Bureau d'Études Automatisé</div></div></div> | <div><div>Résidence Papa Oumar Sakho</div><div>Dakar, Senegal</div></div> | <div><div>Éch: 1/100</div><div>Pl. 16/32</div></div>    |
|                                                                                | <div>Plomberie — Étage 3</div>                                            |                                                         |
| <div>Date: 06/05/2026</div>                                                    | <div>Réf: PLU</div>                                                       | <div><div>BIM vPLU-016</div><div>Phase: APD</div></div> |



413 CVC / Ventilation — RDC

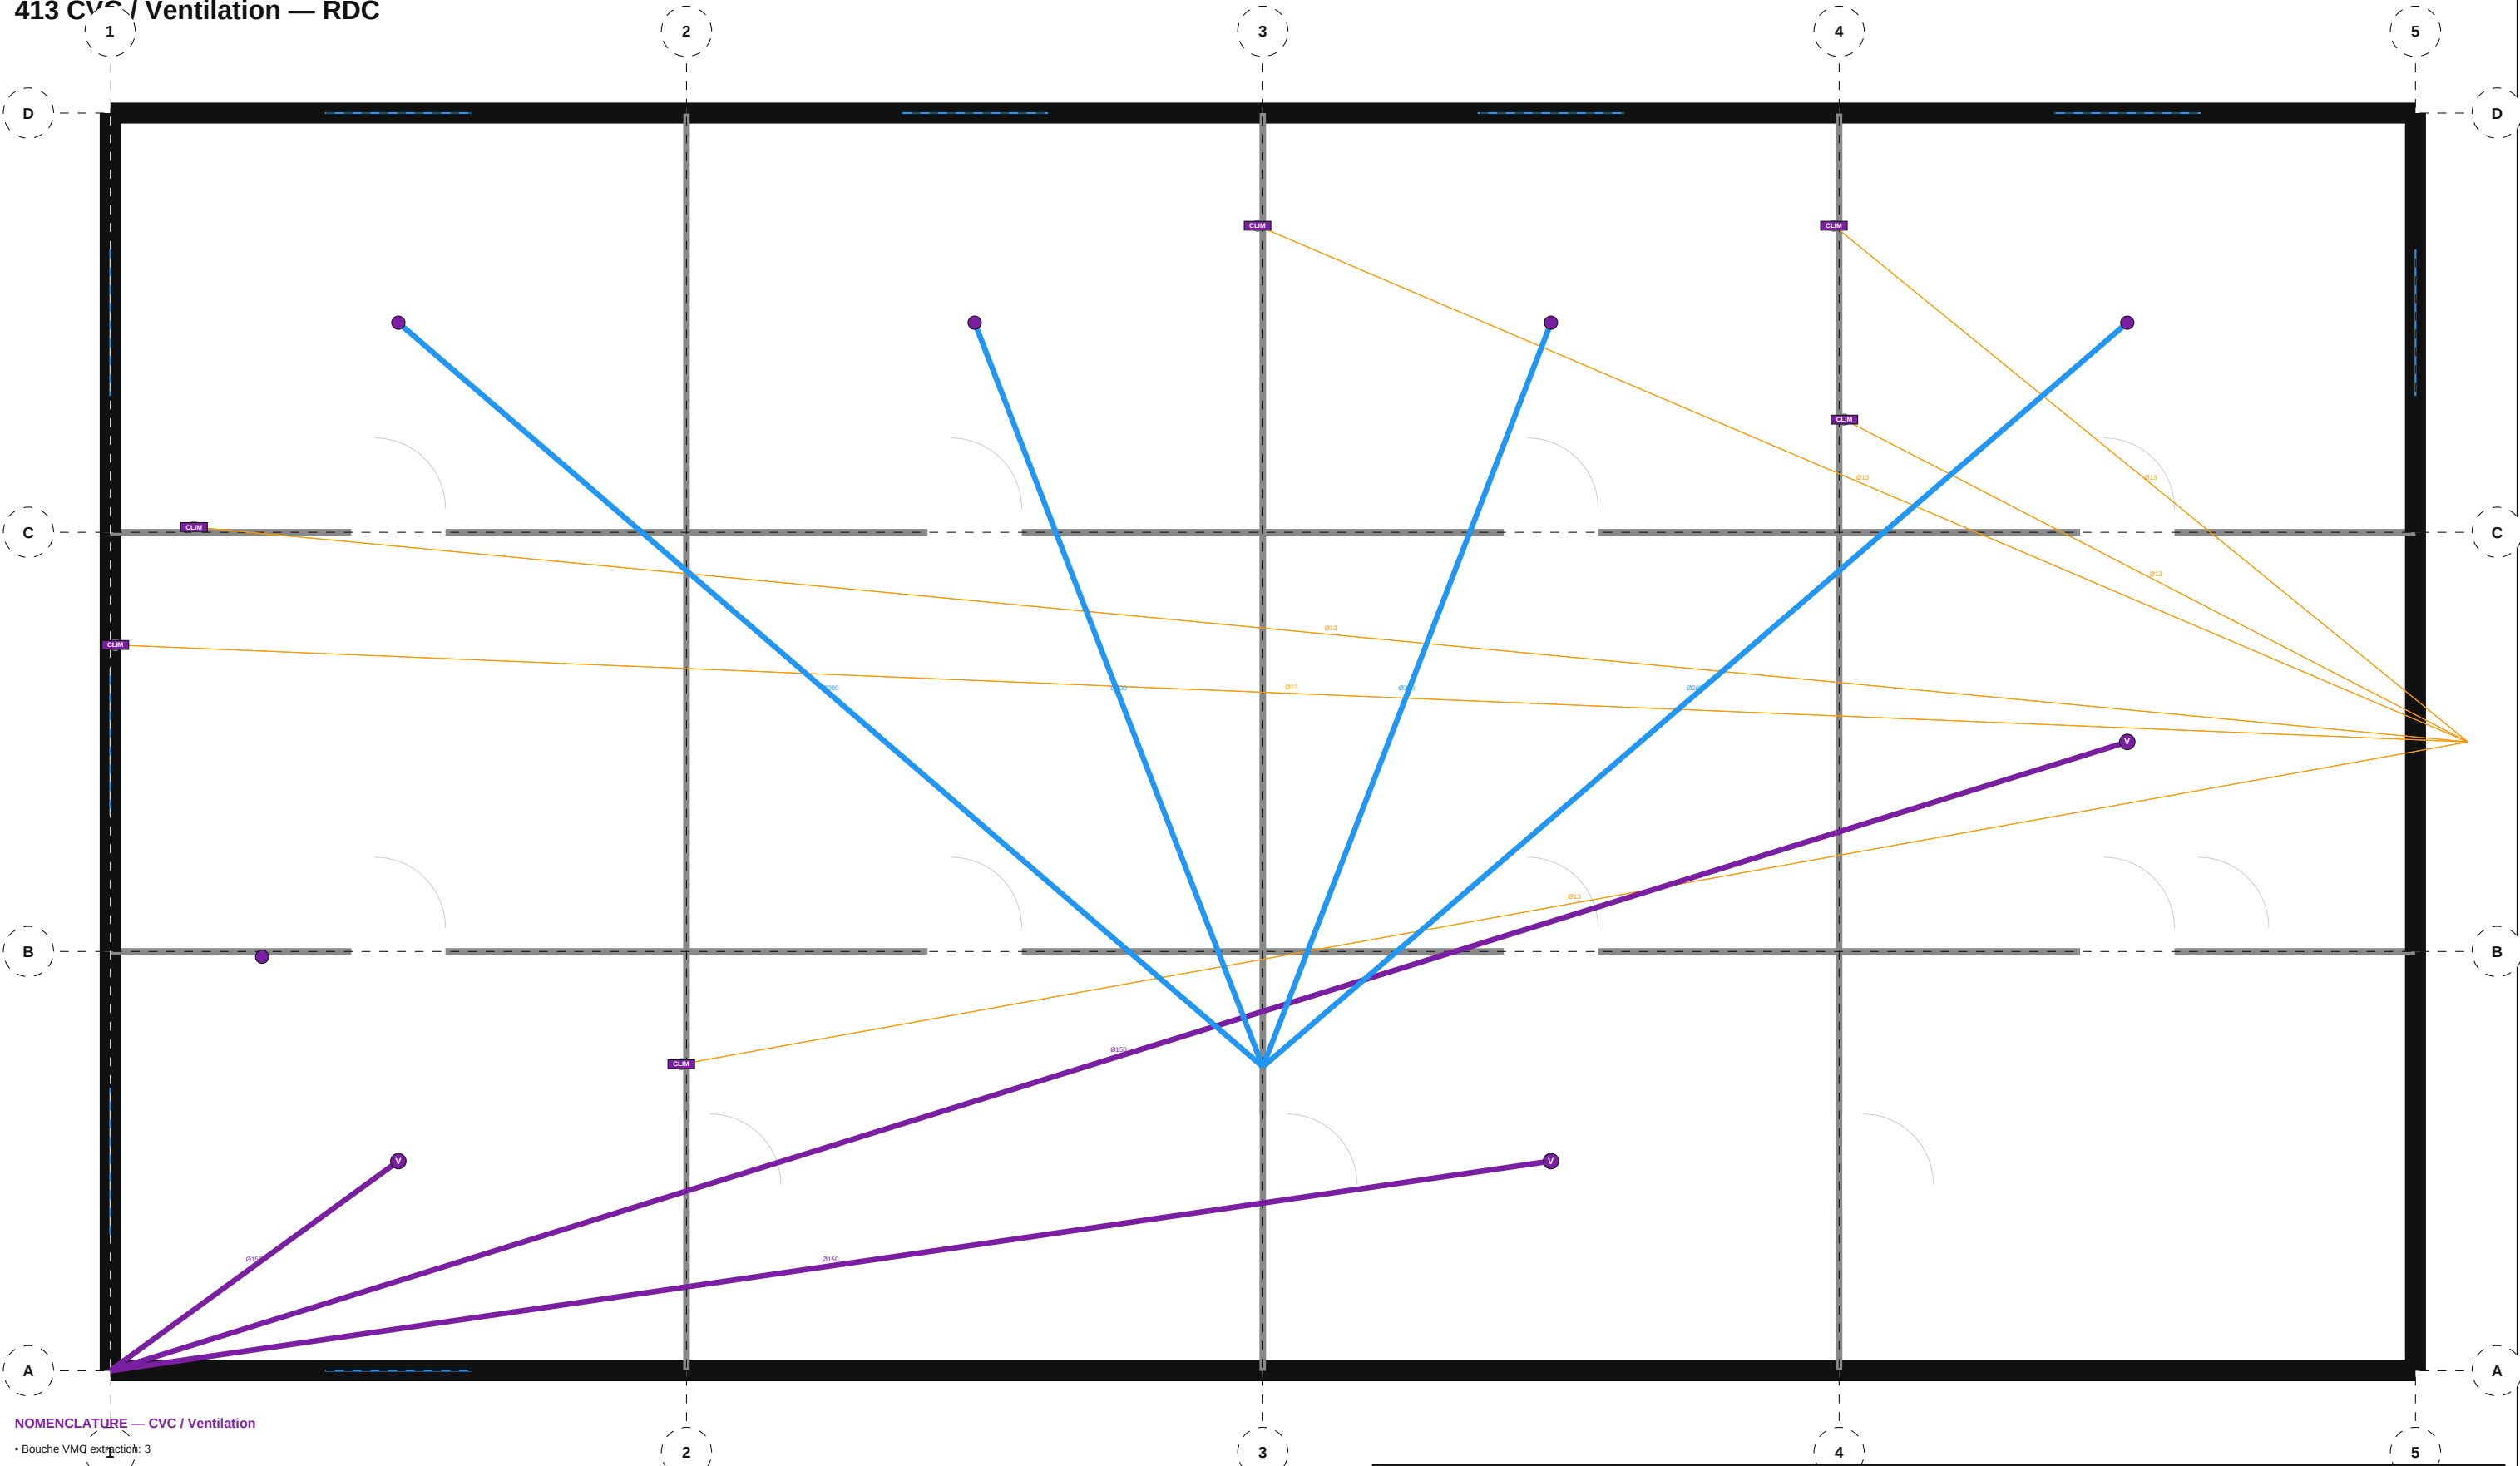


NOMENCLATURE — CVC / Ventilation

- Bouche VMQ extraction: 3
- Grille soufflage: 4
- Hotte aspirante: 1
- Split climatiseur: 6

|                                               |                                                     |                            |
|-----------------------------------------------|-----------------------------------------------------|----------------------------|
| <b>TIJAN AI</b><br>Bureau d'Études Automatisé | <b>Résidence Papa Oumar Sakho</b><br>Dakar, Senegal | Éch: 1/100<br>Pl. 17/32    |
|                                               | <b>CVC / Ventilation — RDC</b>                      |                            |
| Date: 06/05/2026                              | Réf: HVC                                            | BIM vHVC-017<br>Phase: APD |

413 CVC / Ventilation — Étage 1

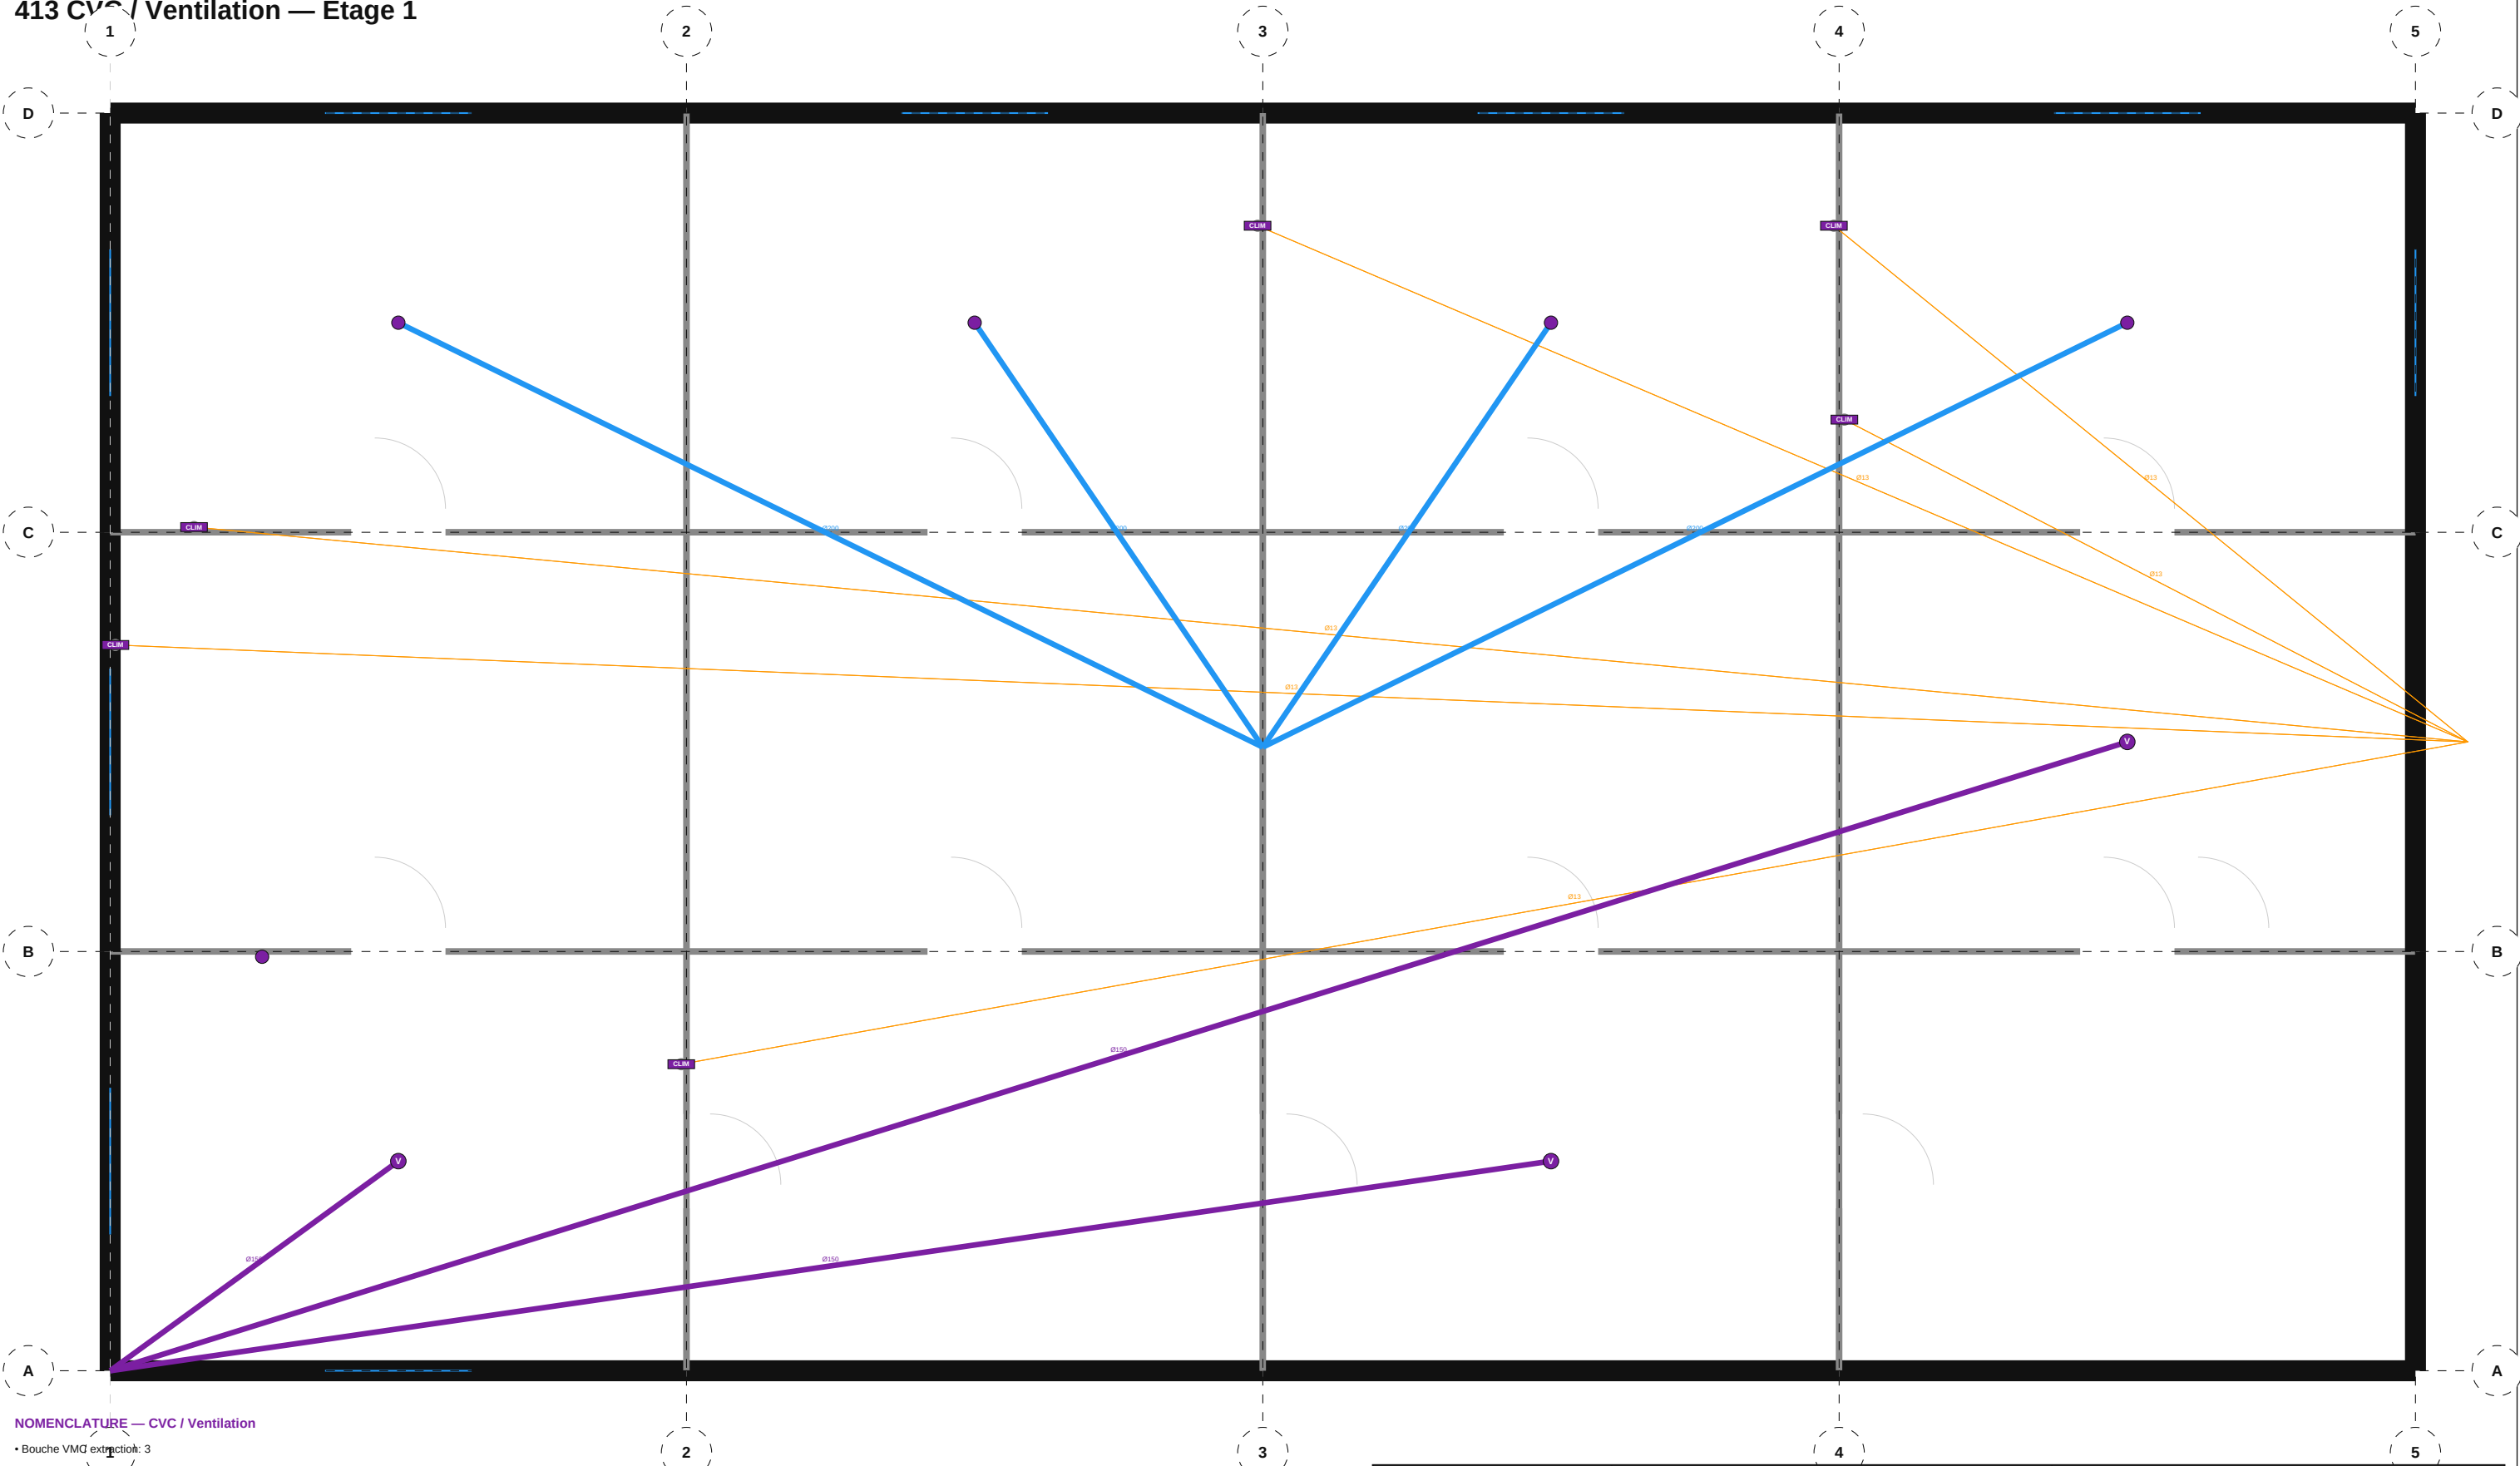


NOMENCLATURE — CVC / Ventilation

- Bouche VMQ extraction: 3
- Grille soufflage: 4
- Hotte aspirante: 1
- Split climatiseur: 6

|                                                           |                                                                 |                                               |
|-----------------------------------------------------------|-----------------------------------------------------------------|-----------------------------------------------|
| <div>TIJAN AI</div> <div>Bureau d'Études Automatisé</div> | <div>Résidence Papa Oumar Sakho</div> <div>Dakar, Senegal</div> | <div>Éch: 1/100</div> <div>Pl. 18/32</div>    |
|                                                           | <div>CVC / Ventilation — Étage 1</div>                          |                                               |
| <div>Date: 06/05/2026</div>                               | <div>Réf: HVC</div>                                             | <div>BIM vHVC-018</div> <div>Phase: APD</div> |

413 CVC / Ventilation — Étage 2

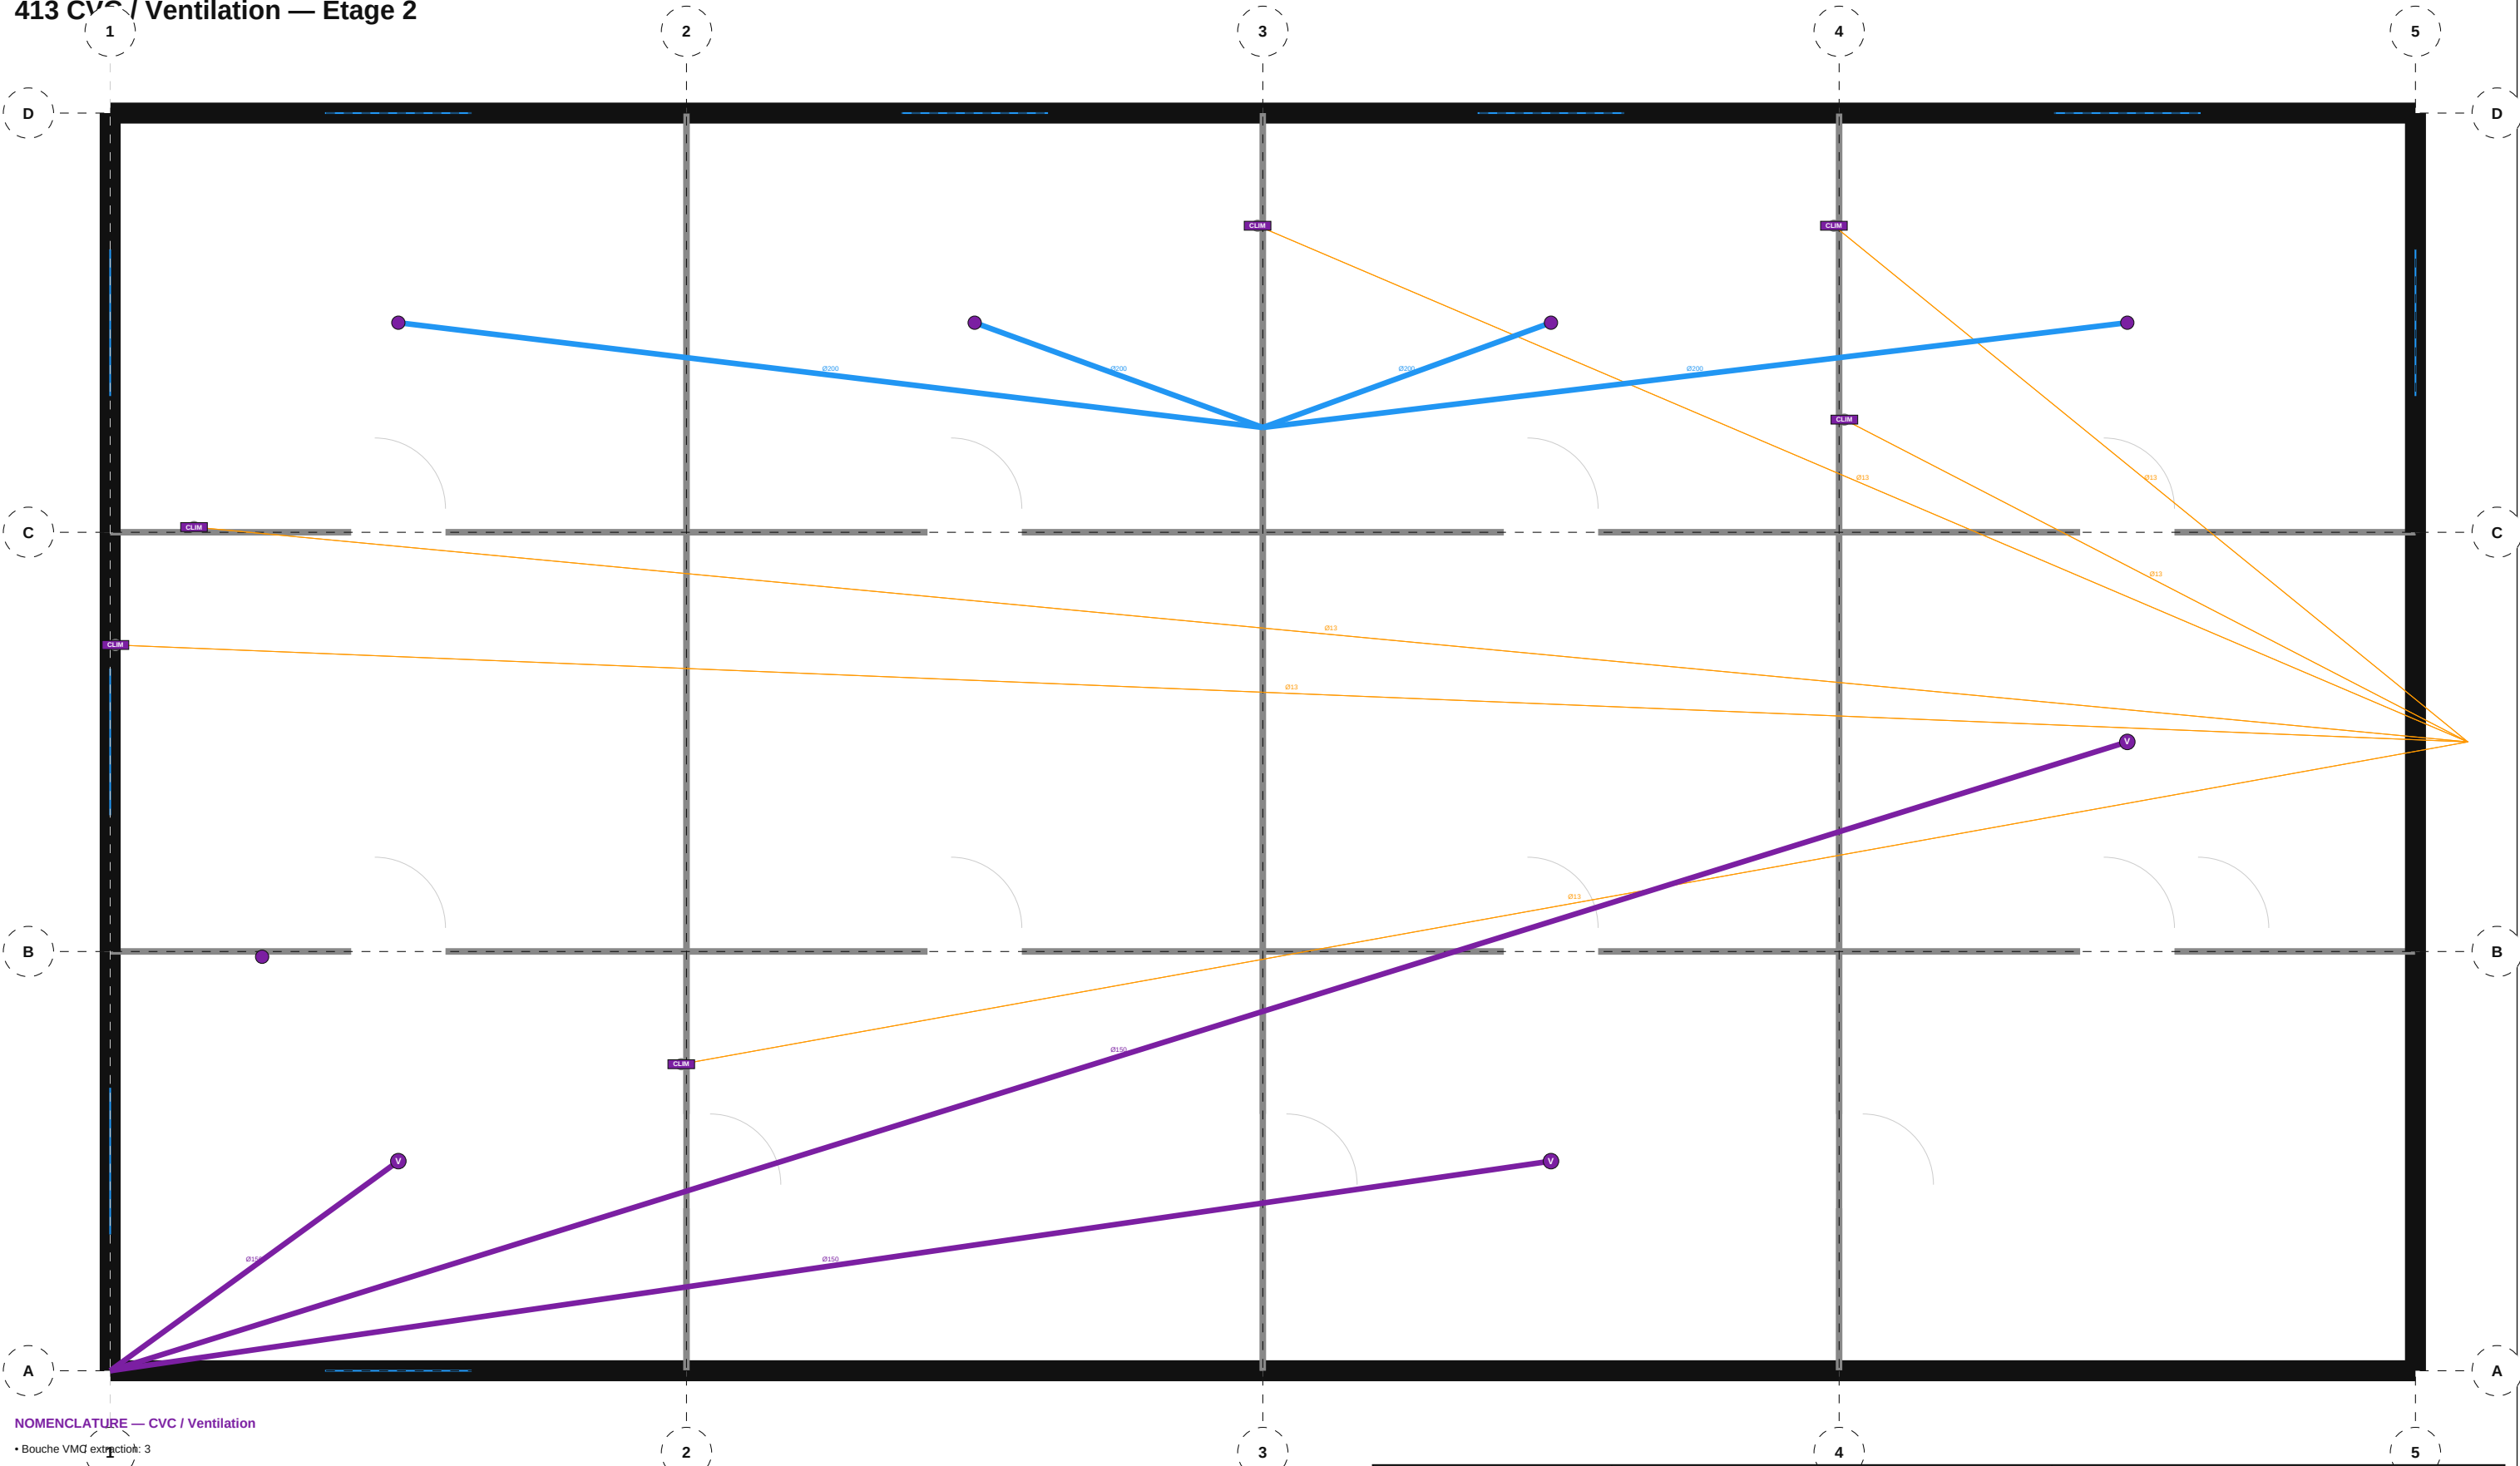


NOMENCLATURE — CVC / Ventilation

- Bouche VMQ extraction: 3
- Grille soufflage: 4
- Hotte aspirante: 1
- Split climatiseur: 6

|                                        |                                              |                            |
|----------------------------------------|----------------------------------------------|----------------------------|
| TIJAN AI<br>Bureau d'Études Automatisé | Résidence Papa Oumar Sakho<br>Dakar, Senegal | Éch: 1/100<br>Pl. 19/32    |
|                                        | CVC / Ventilation — Étage 2                  |                            |
| Date: 06/05/2026                       | Réf: HVC                                     | BIM vHVC-019<br>Phase: APD |

413 CVC / Ventilation — Étage 3

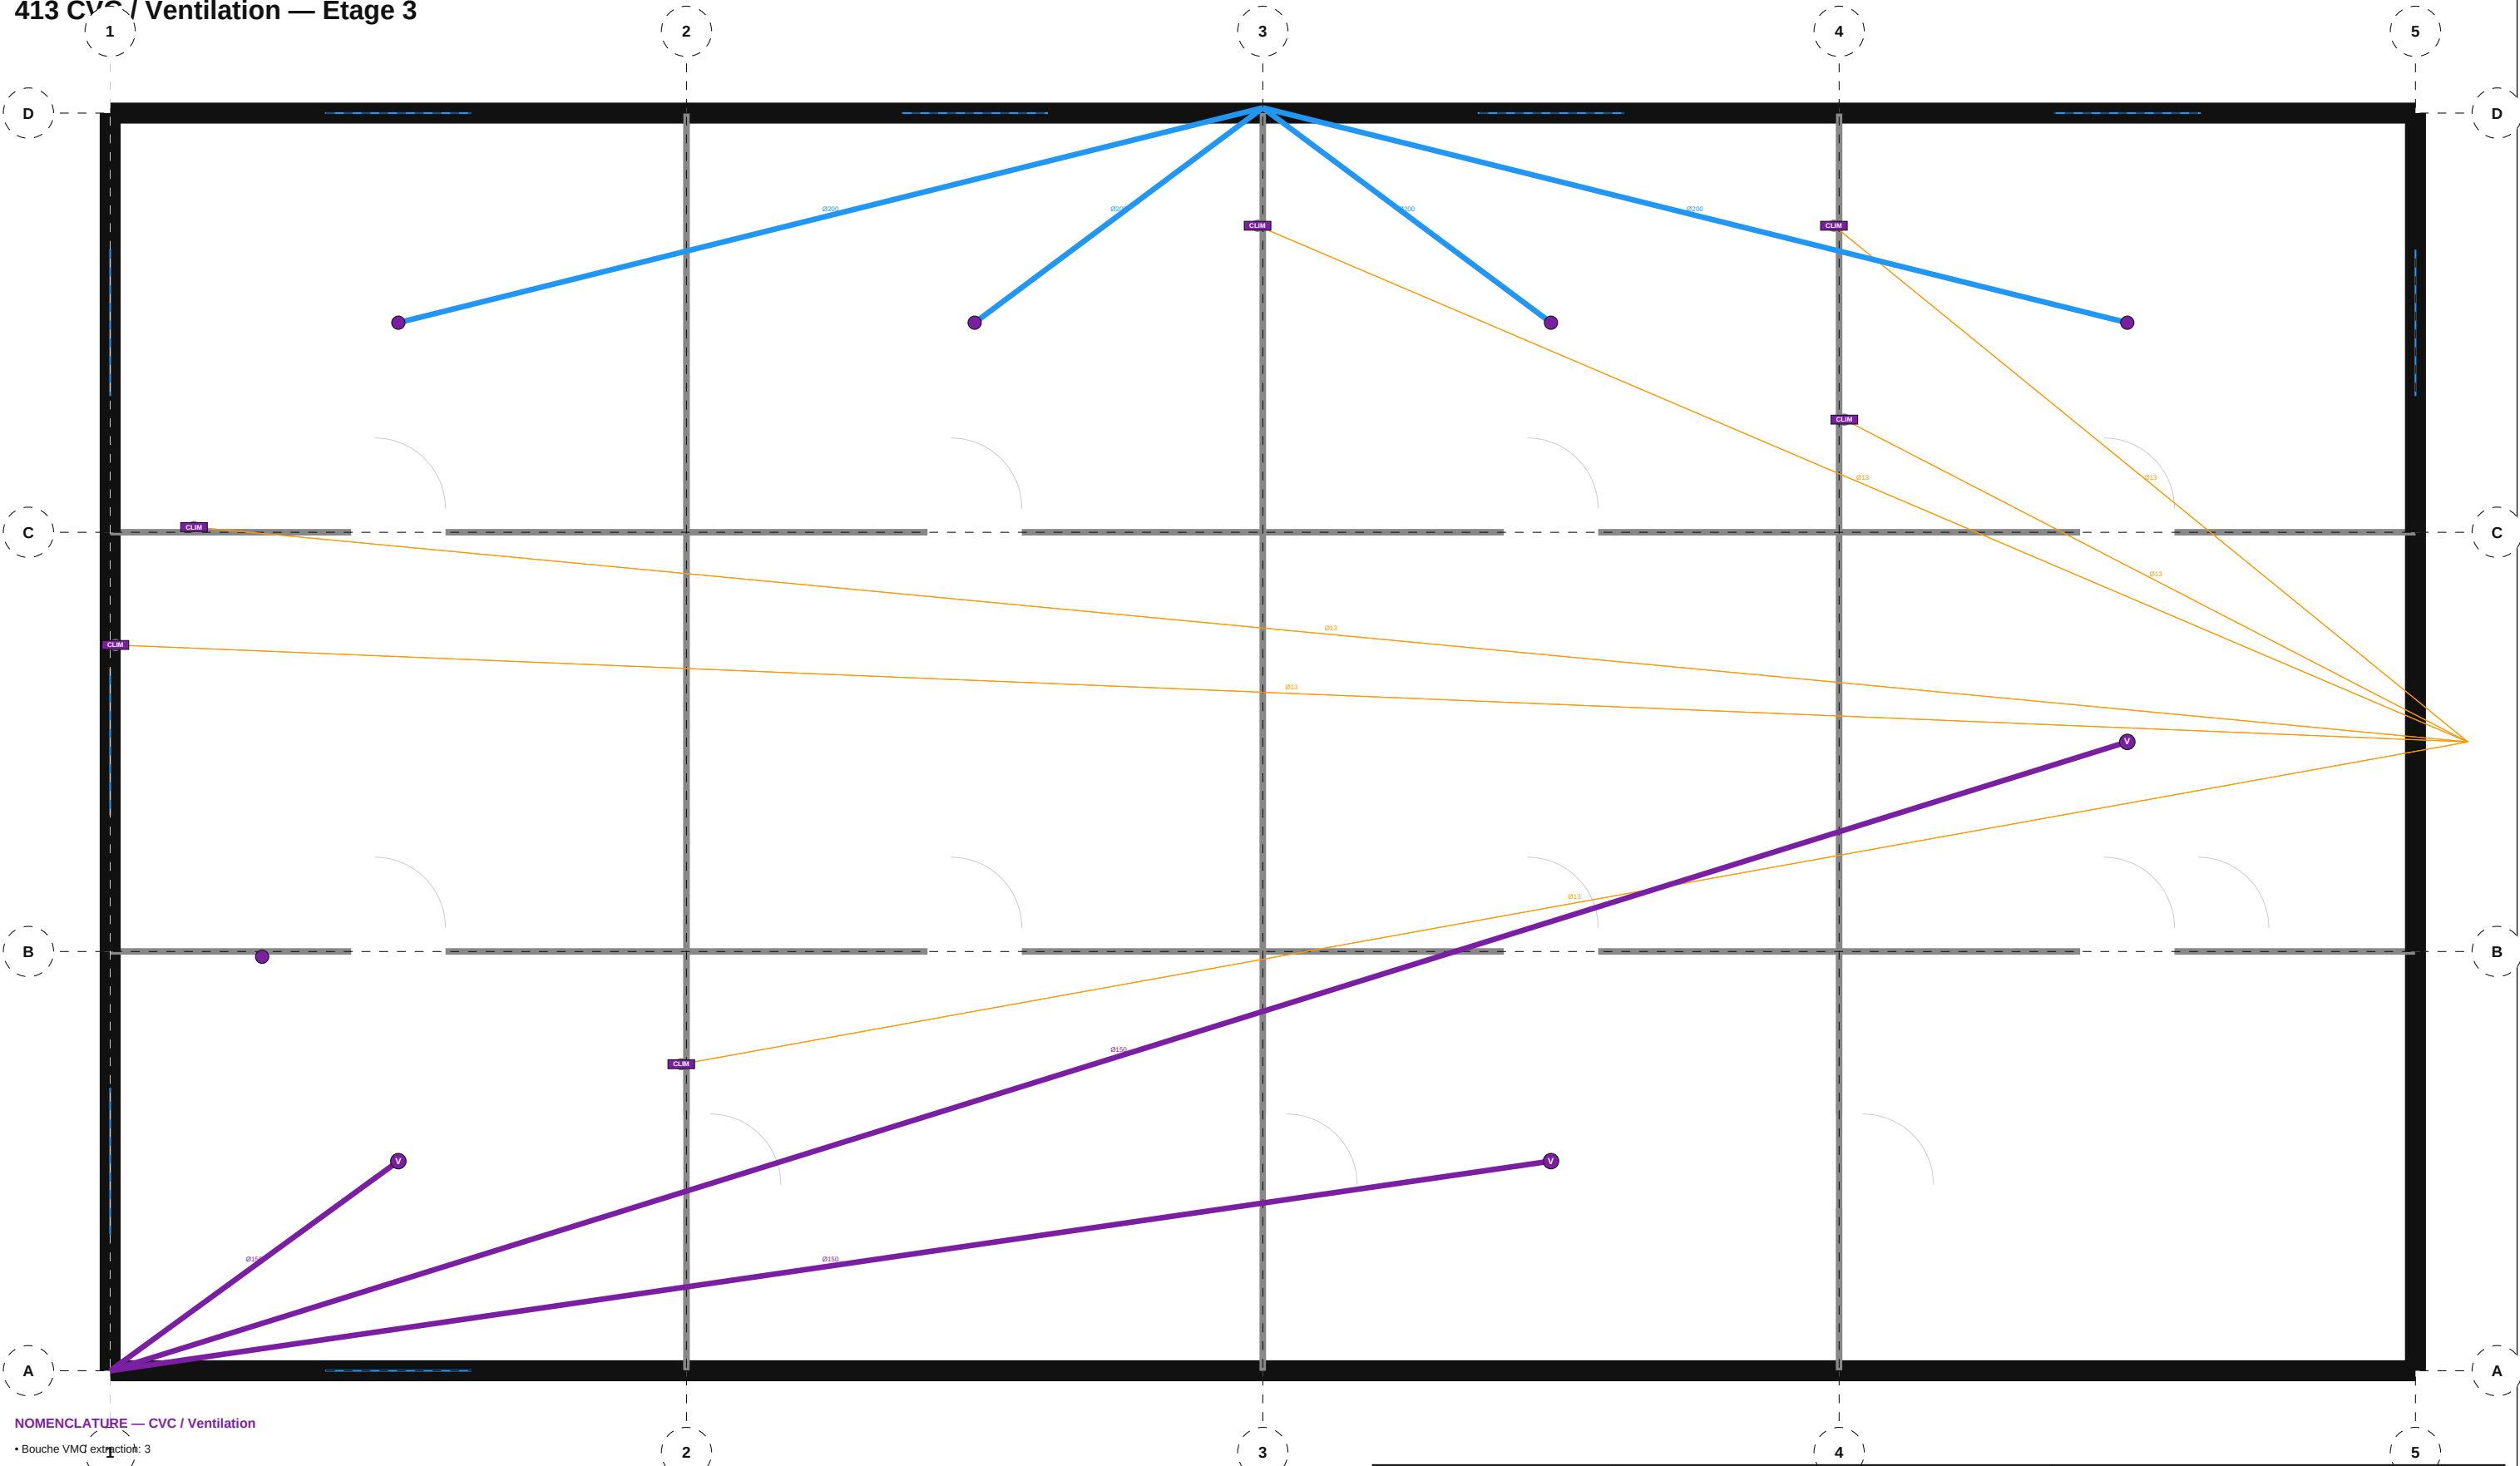


NOMENCLATURE — CVC / Ventilation

- Bouche VMQ extraction: 3
- Grille soufflage: 4
- Hotte aspirante: 1
- Split climatiseur: 6

|                                                           |                                                                 |                                               |
|-----------------------------------------------------------|-----------------------------------------------------------------|-----------------------------------------------|
| <div>TIJAN AI</div> <div>Bureau d'Études Automatisé</div> | <div>Résidence Papa Oumar Sakho</div> <div>Dakar, Senegal</div> | <div>Éch: 1/100</div> <div>Pl. 20/32</div>    |
|                                                           | <div>CVC / Ventilation — Étage 3</div>                          |                                               |
| <div>Date: 06/05/2026</div>                               | <div>Réf: HVC</div>                                             | <div>BIM vHVC-020</div> <div>Phase: APD</div> |

510 Courants Forts — RDC

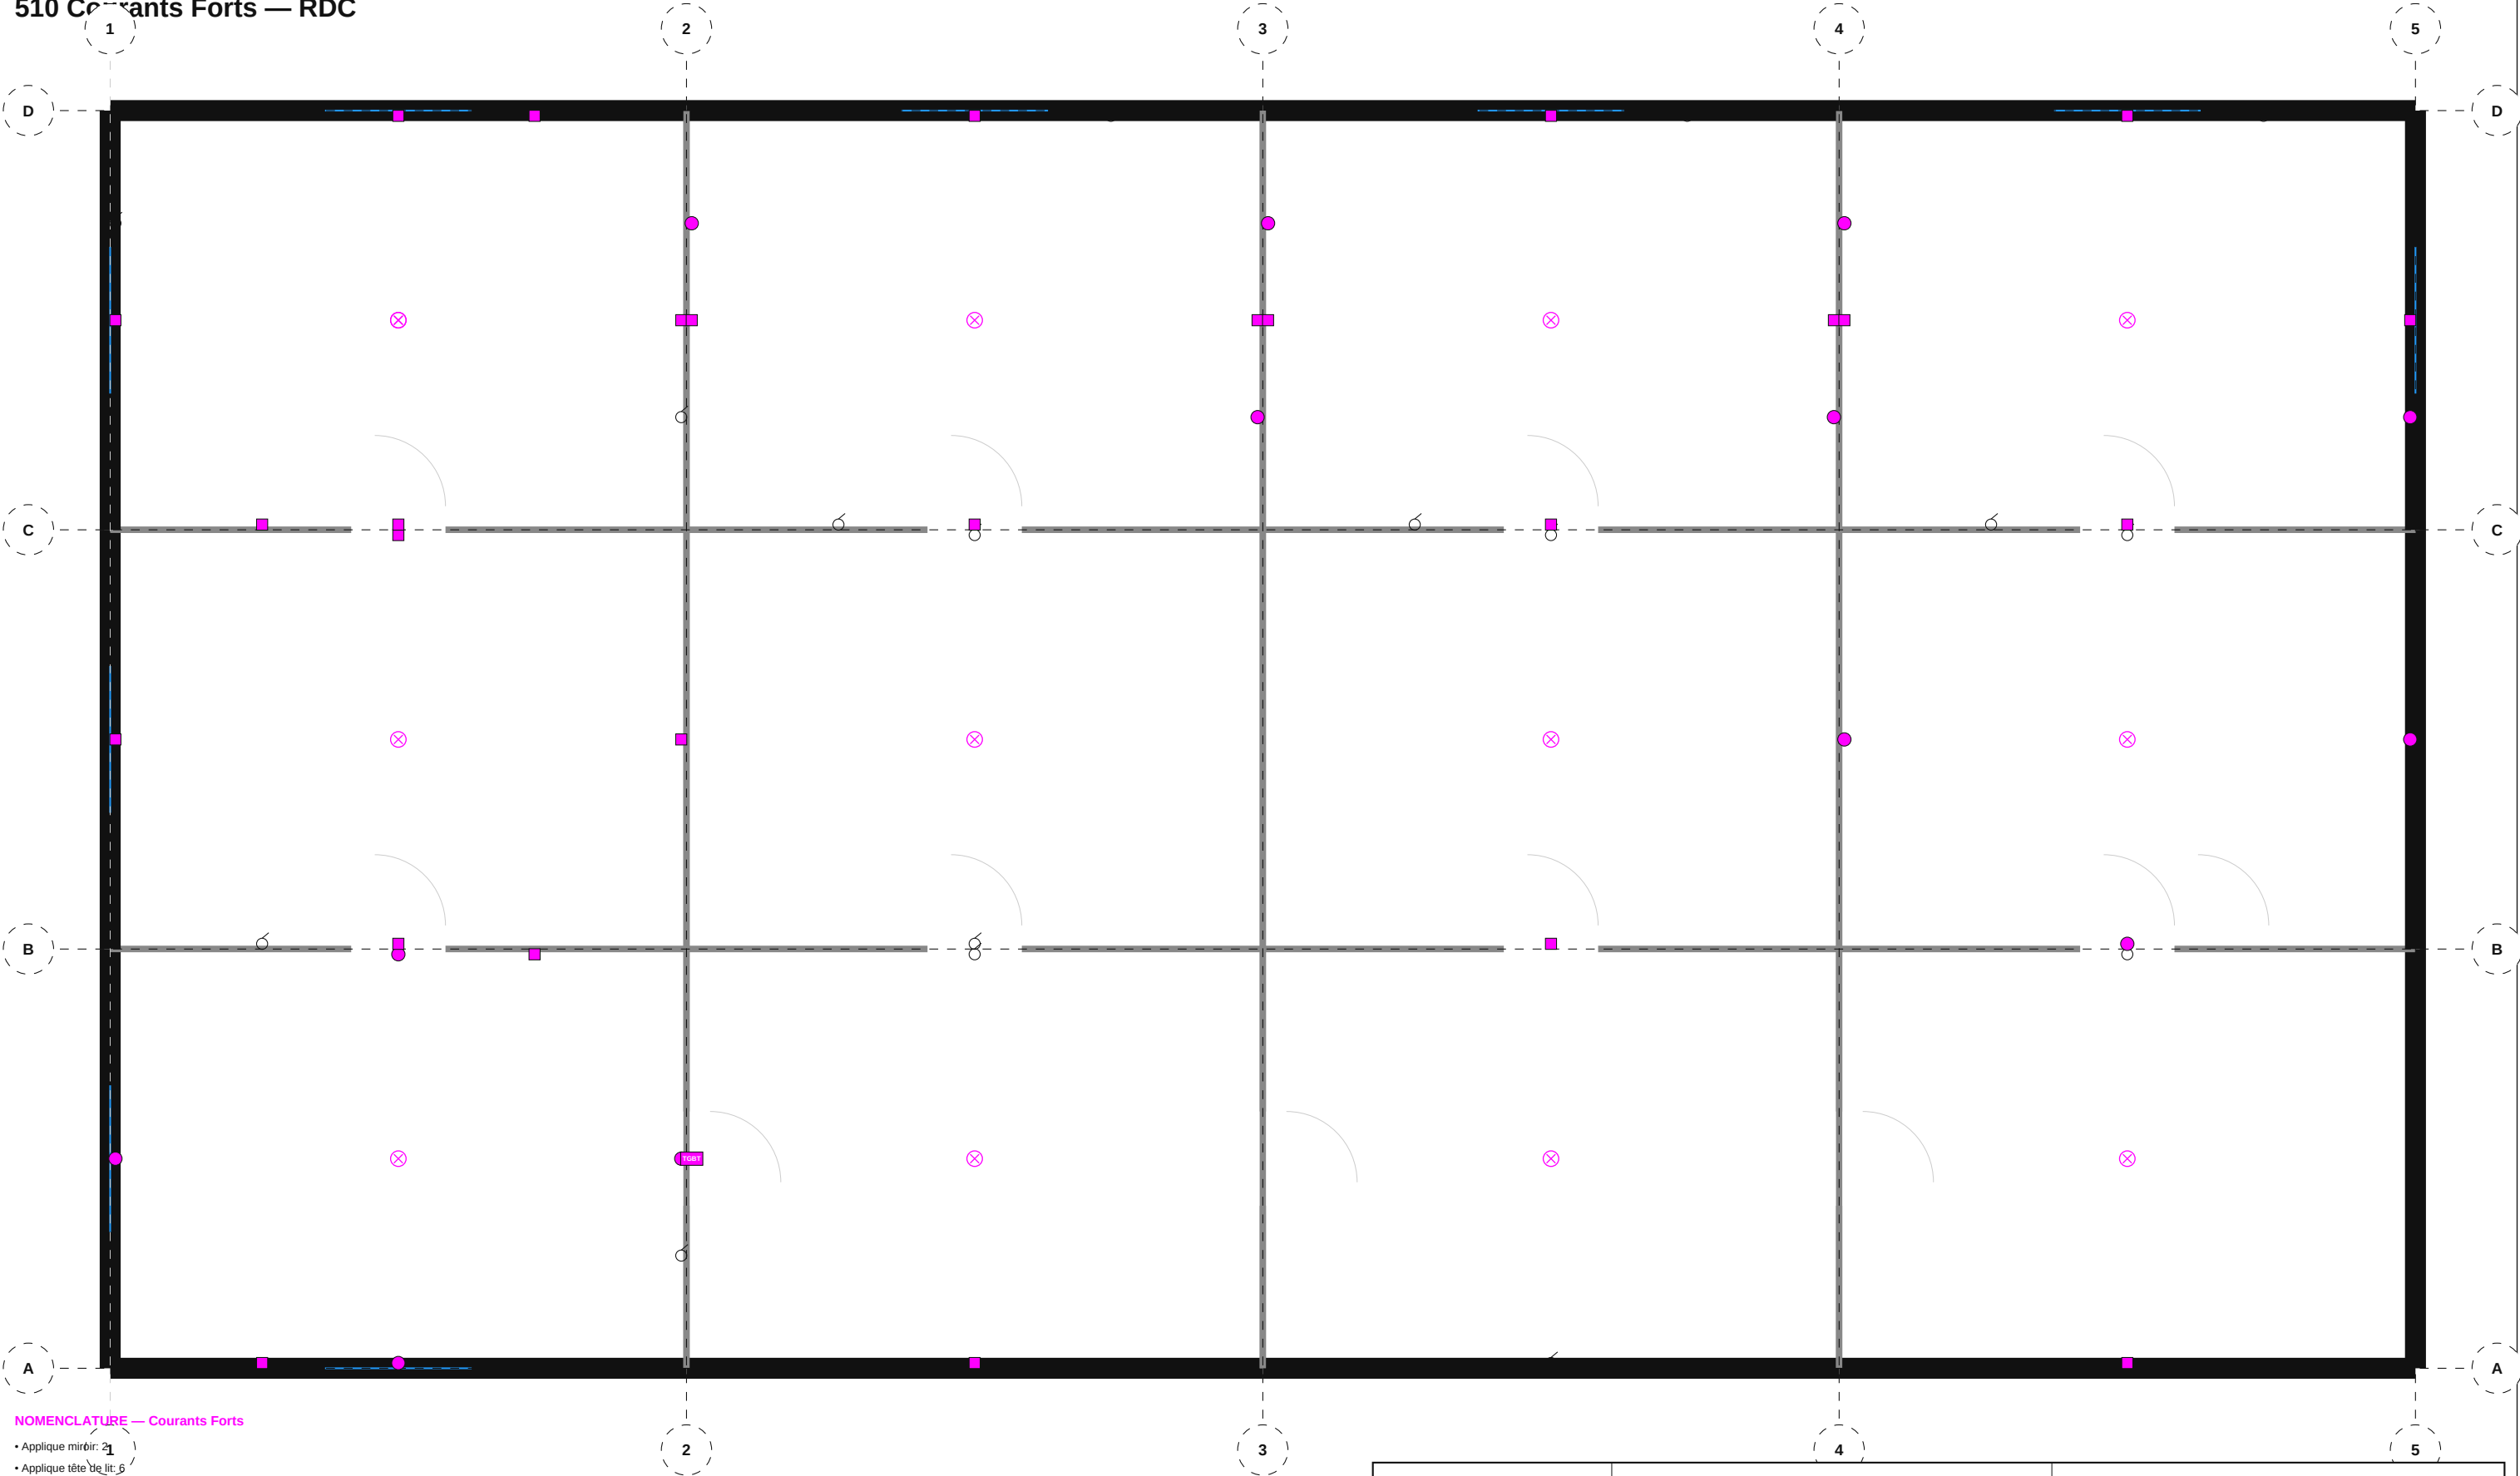

NOMENCLATURE — Courants Forts

- Applique miroir: 21
- Applique tête de lit: 6
- Interrupteur: 7
- Interrupteur va-et-vient: 10
- Plafonnier: 12
- Plafonnier IP44: 1
- Prise 2P+T: 1
- Prise 2P+T 16A: 26
- Prise plan de travail: 4
- Prise étanche 2P+T: 1
- Tableau électrique: 1

TIJAN AI

Bureau d'Études Automatisé

Résidence Papa Oumar Sakho

Dakar, Senegal

Éch: 1/100

Pl. 21/32

Courants Forts — RDC


Date: 06/05/2026

Réf: HCU

BIM vHCU-021

Phase: APD

510 Courants Forts — Étage 1

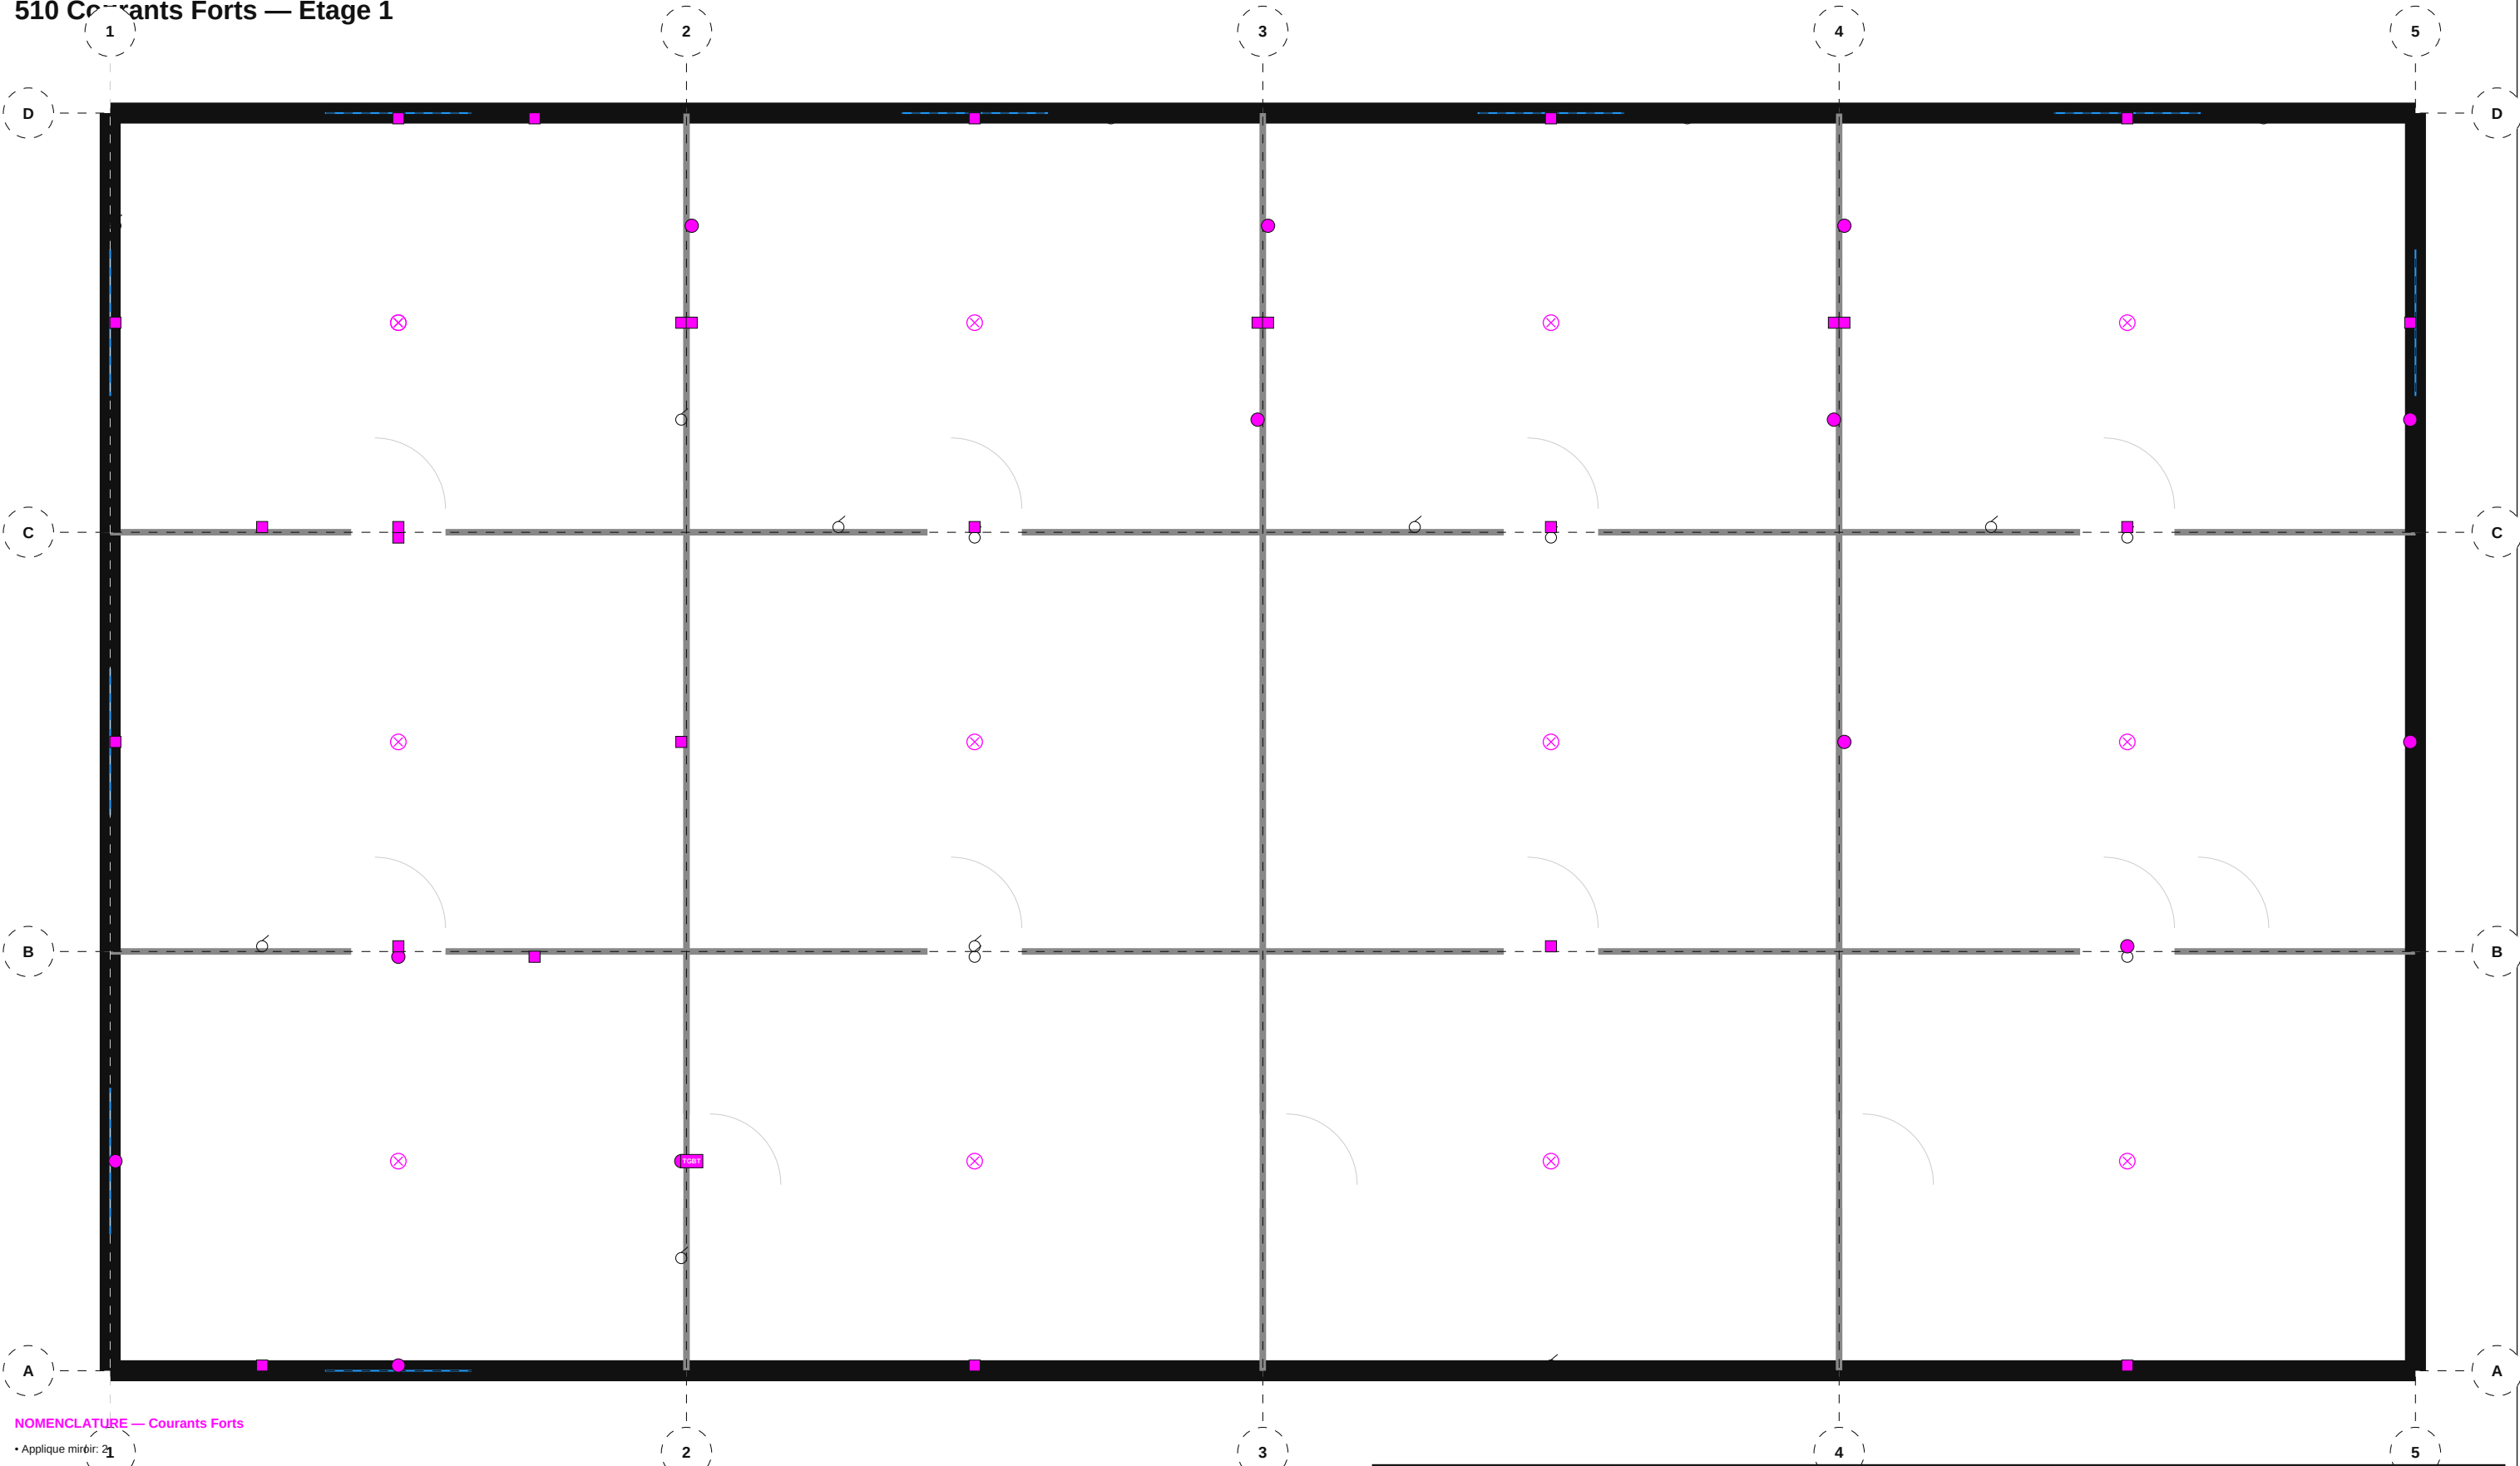

NOMENCLATURE — Courants Forts

- Applique miroir: 21
- Applique tête de lit: 6
- Interrupteur: 7
- Interrupteur va-et-vient: 10
- Plafonnier: 12
- Plafonnier IP44: 1
- Prise 2P+T: 1
- Prise 2P+T 16A: 26
- Prise plan de travail: 4
- Prise étanche 2P+T: 1
- Tableau électrique: 1

TIJAN AI

Bureau d'Études Automatisé

Résidence Papa Oumar Sakho

Dakar, Senegal

Éch: 1/100

Pl. 22/32

Courants Forts — Étage 1

Date: 06/05/2026


Réf: HCU

BIM vHCU-022

Phase: APD



510 Courants Forts — Étage 2

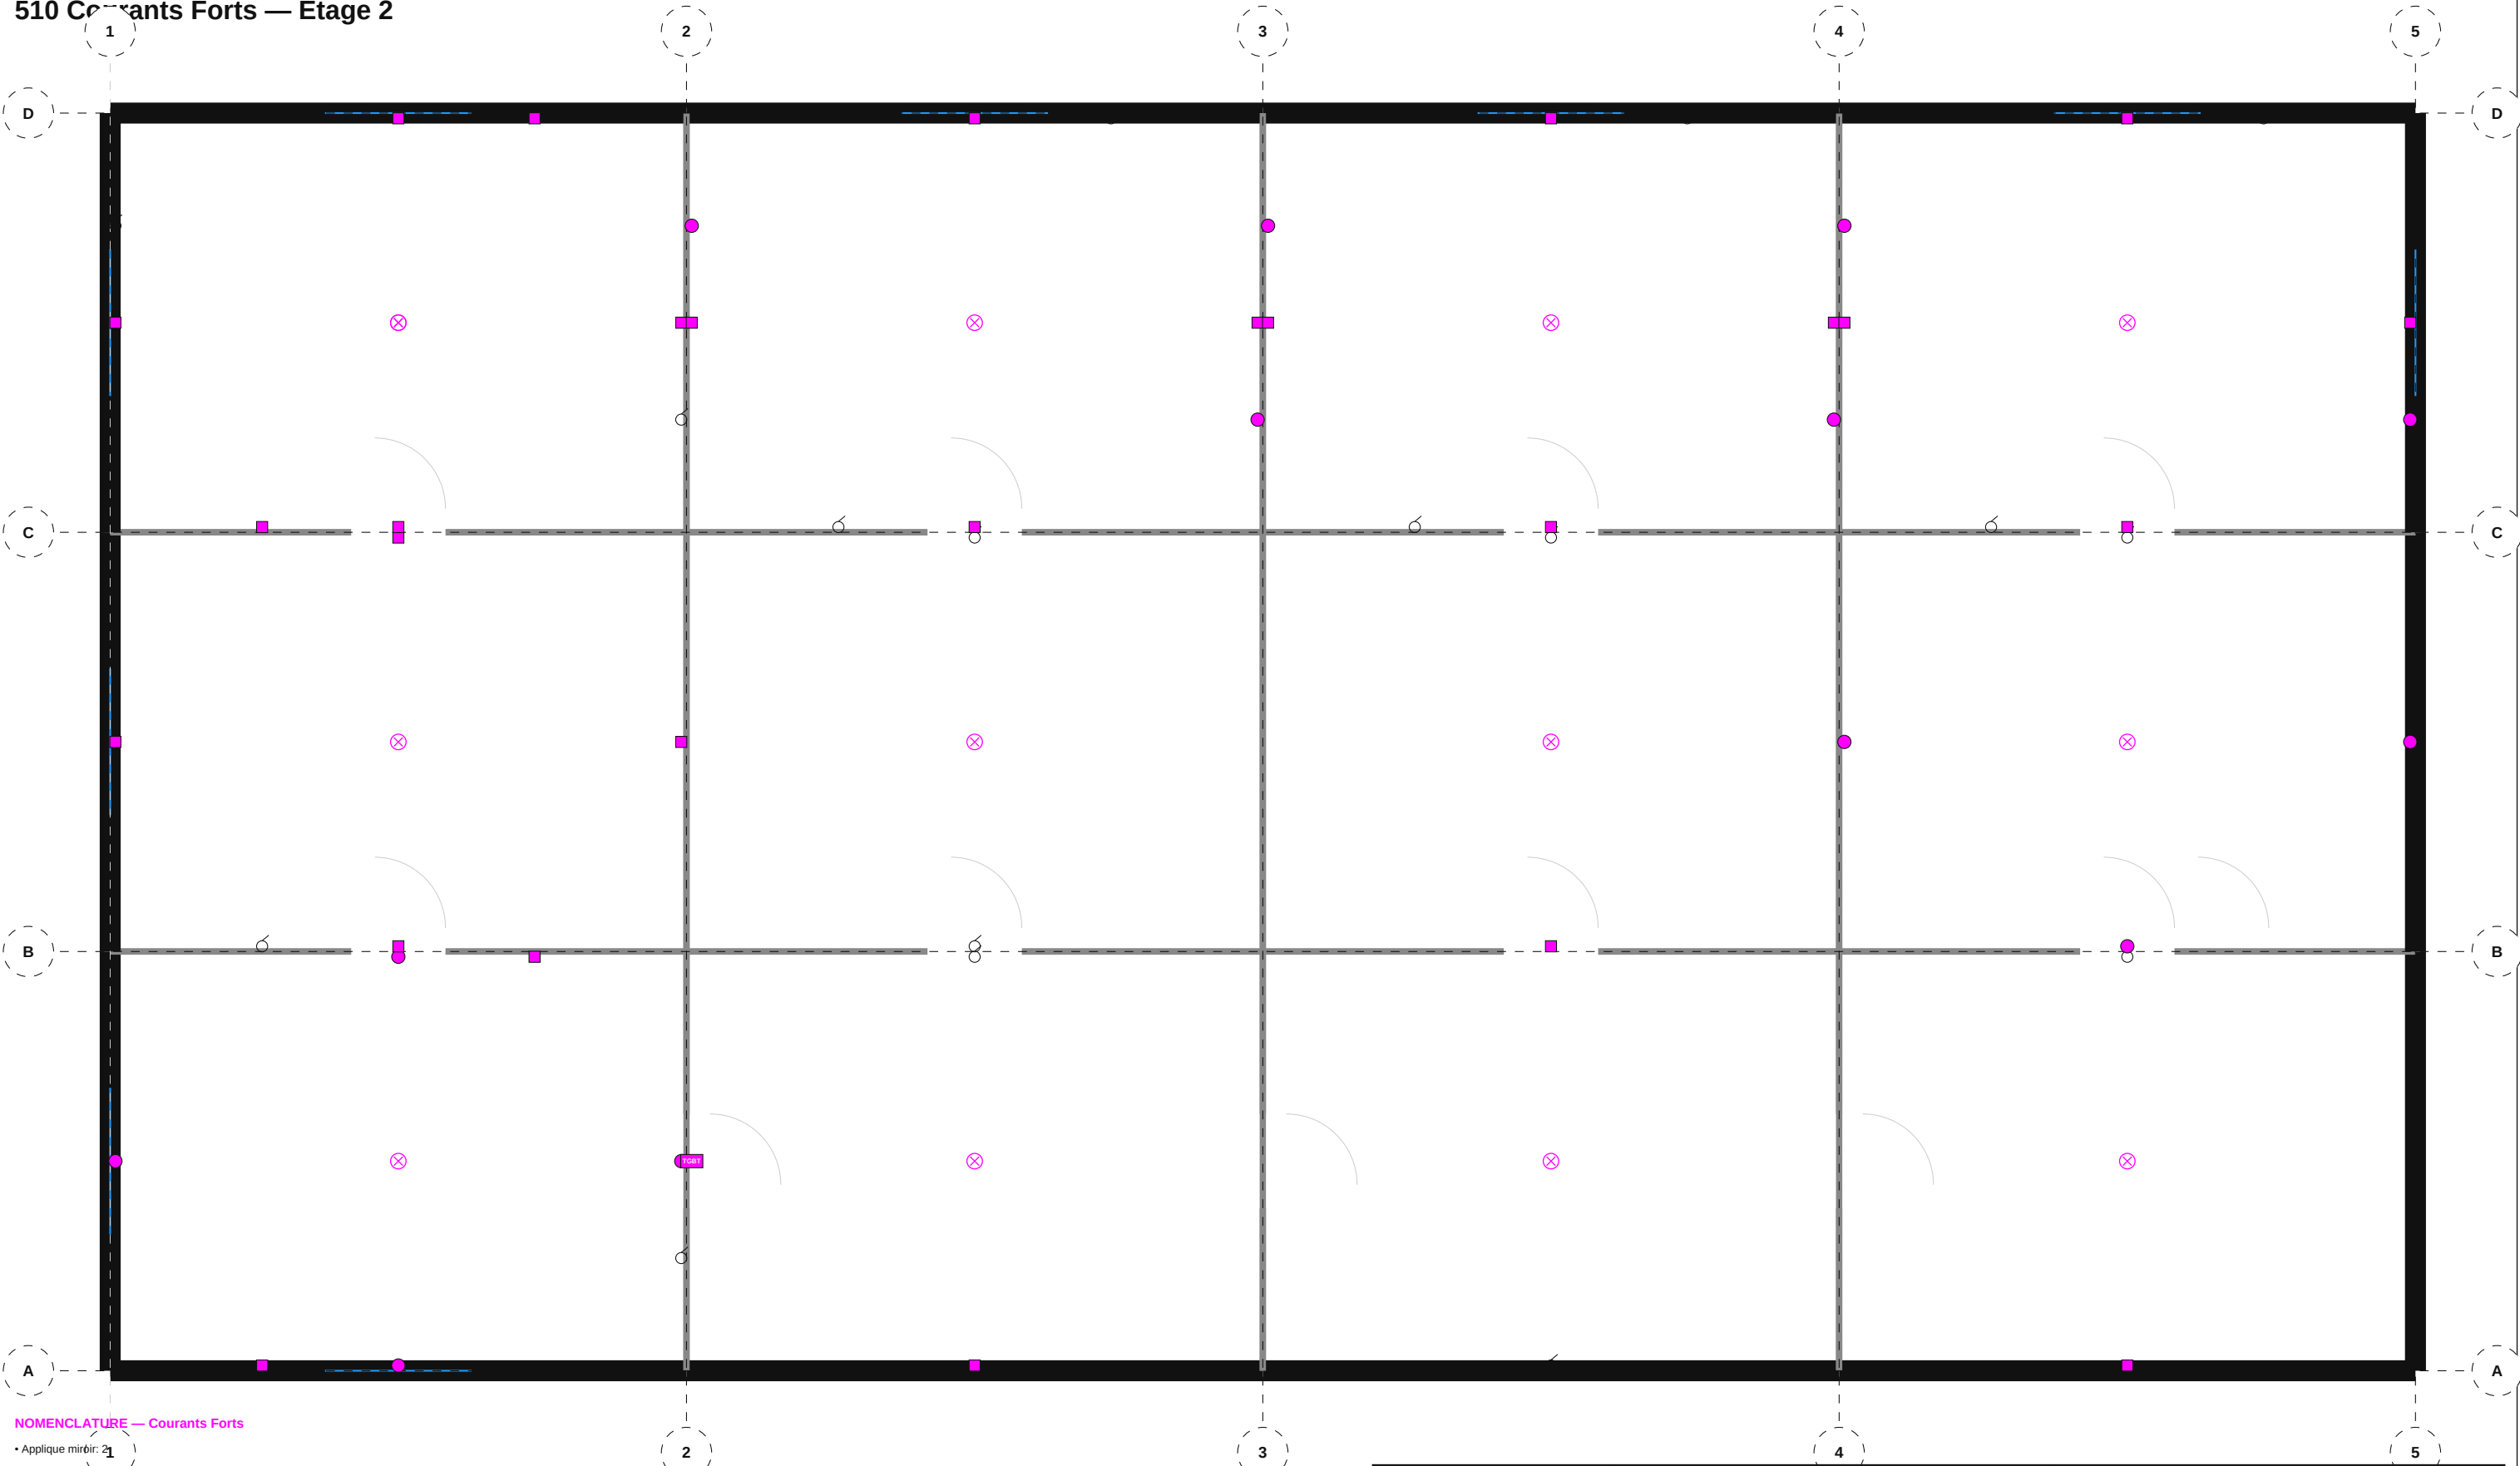

NOMENCLATURE — Courants Forts

- Applique miroir: 21
- Applique tête de lit: 6
- Interrupteur: 7
- Interrupteur va-et-vient: 10
- Plafonnier: 12
- Plafonnier IP44: 1
- Prise 2P+T: 1
- Prise 2P+T 16A: 26
- Prise plan de travail: 4
- Prise étanche 2P+T: 1
- Tableau électrique: 1

TIJAN AI

Bureau d'Études Automatisé

Résidence Papa Oumar Sakho

Dakar, Senegal

Éch: 1/100

Pl. 23/32

Courants Forts — Étage 2


Date: 06/05/2026

Réf: HCU

BIM vHCU-023

Phase: APD

510 Courants Forts — Étage 3

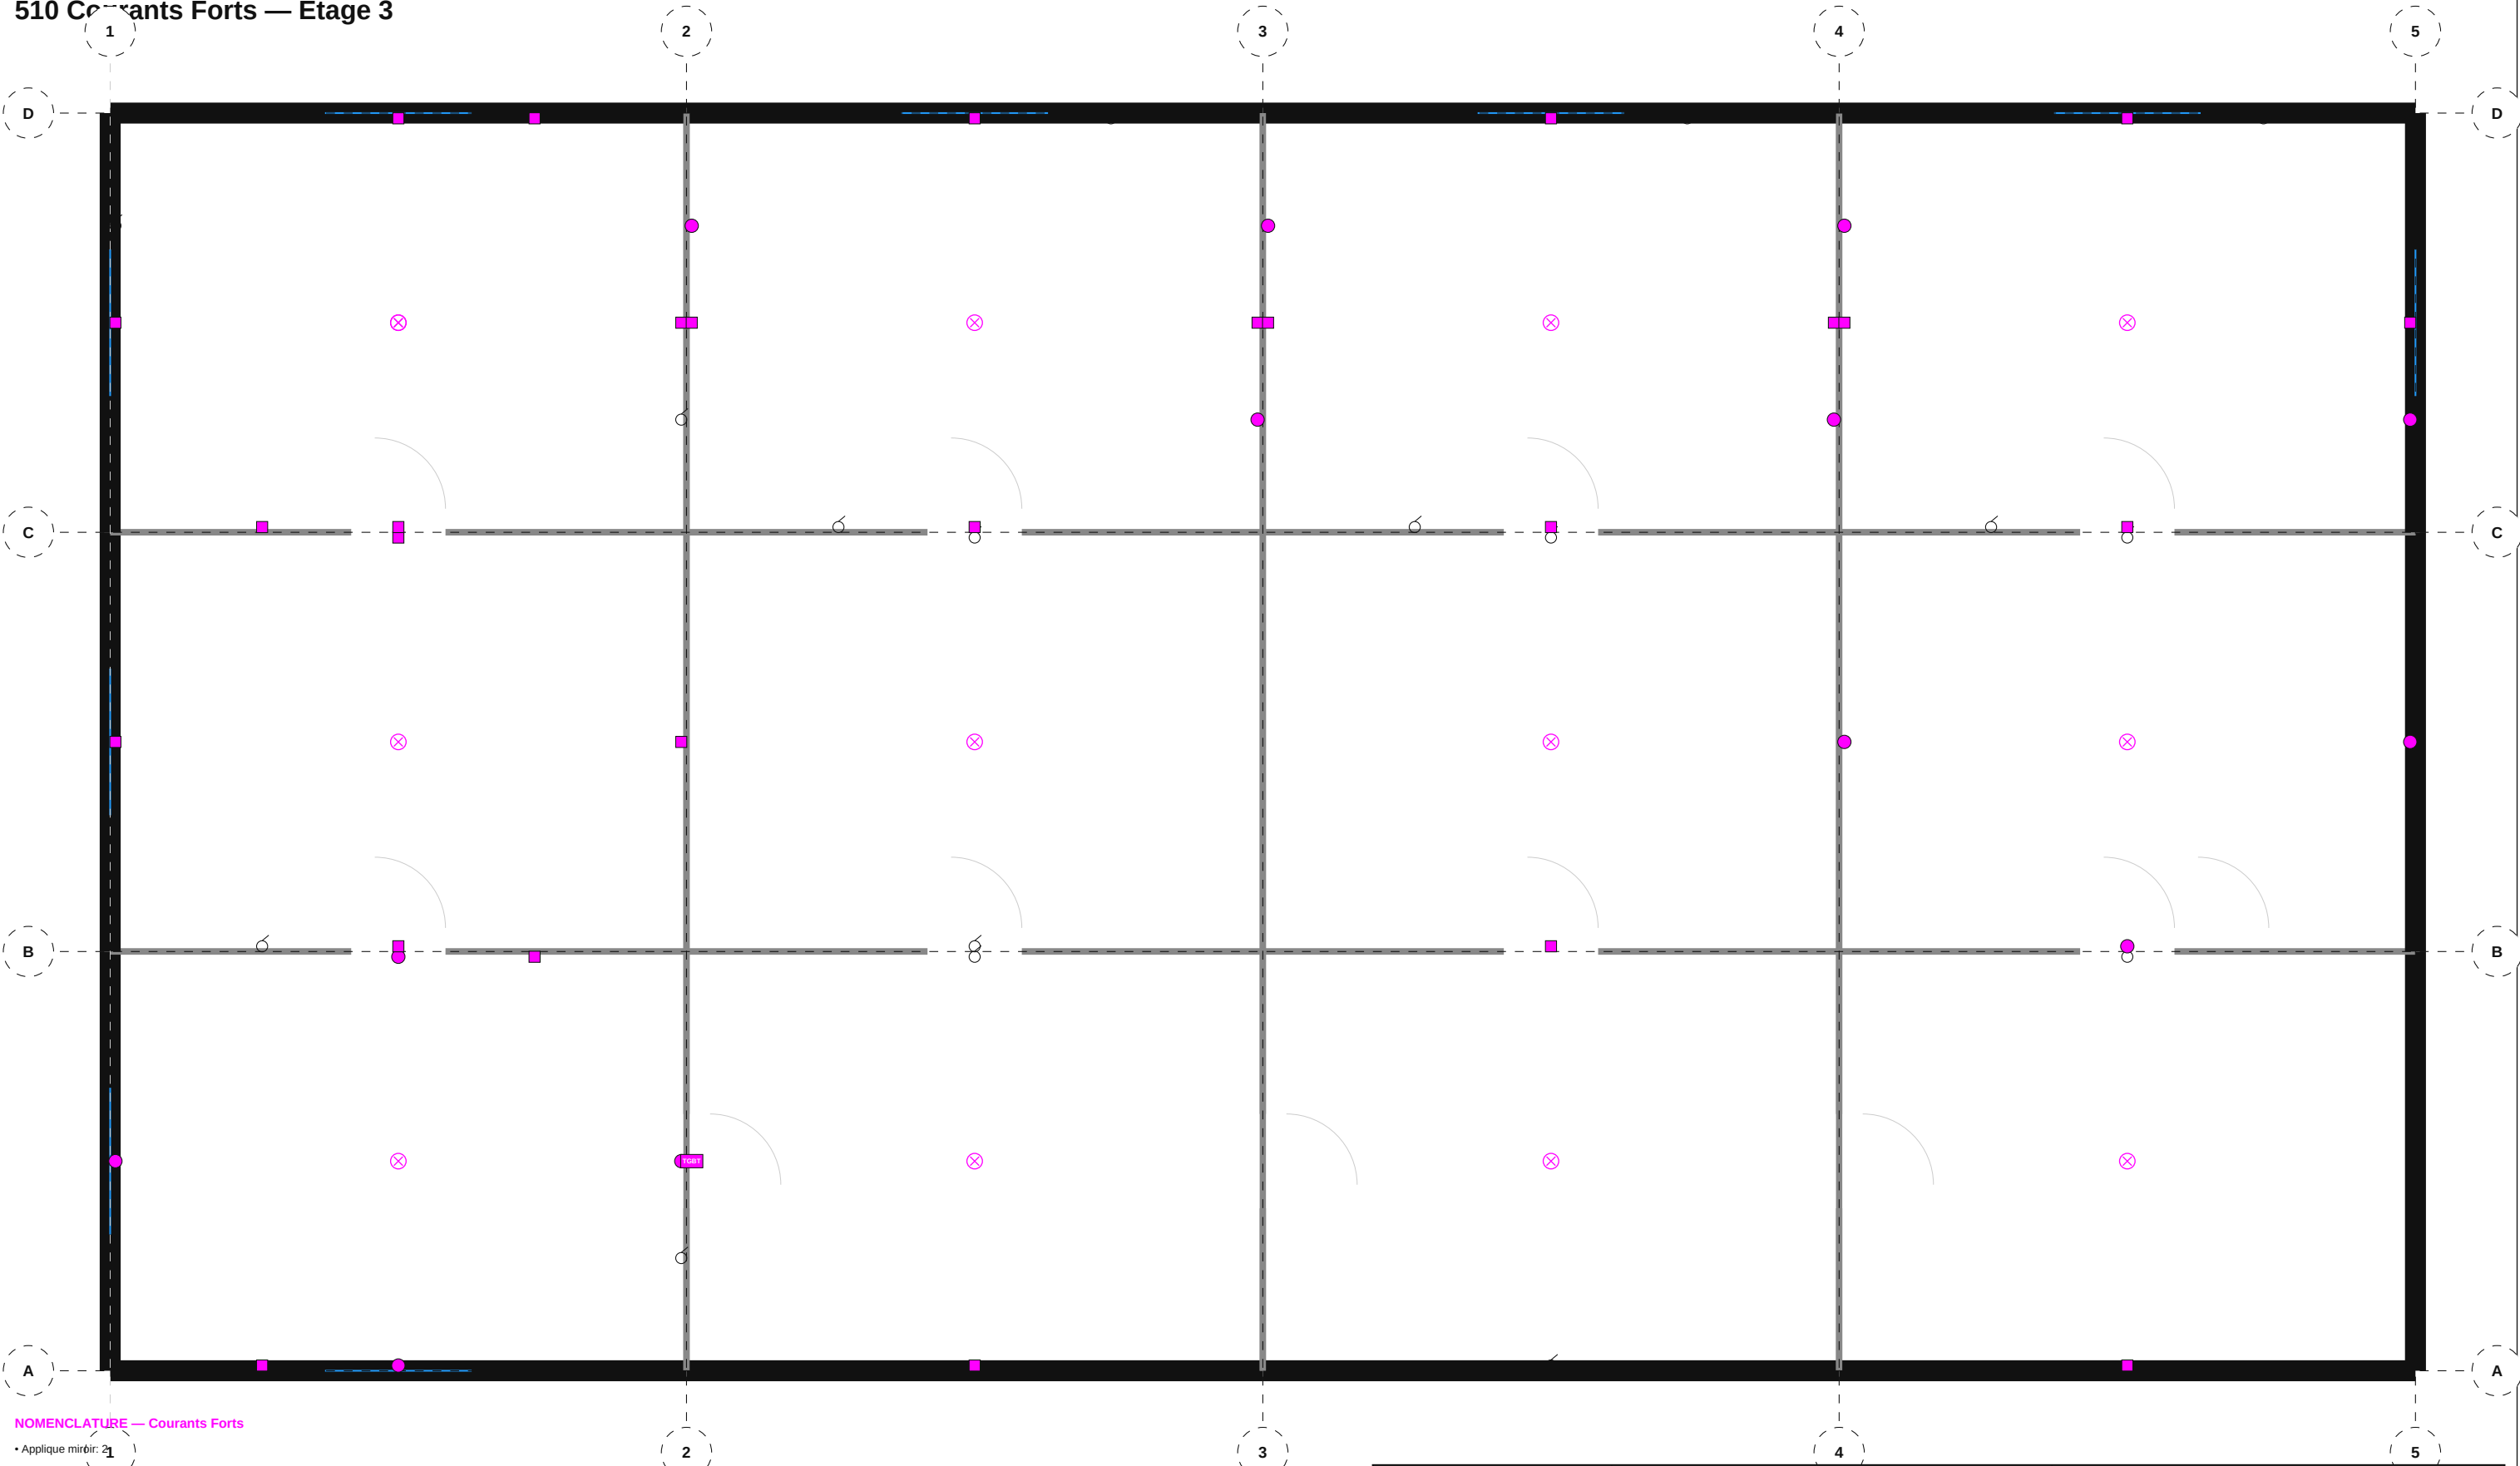


NOMENCLATURE — Courants Forts

- Applique miroir: 21
- Applique tête de lit: 6
- Interrupteur: 7
- Interrupteur va-et-vient: 10
- Plafonnier: 12
- Plafonnier IP44: 1
- Prise 2P+T: 1
- Prise 2P+T 16A: 26
- Prise plan de travail: 4
- Prise étanche 2P+T: 1
- Tableau électrique: 1

|                                                           |                                                                 |                                               |
|-----------------------------------------------------------|-----------------------------------------------------------------|-----------------------------------------------|
| <div>TIJAN AI</div> <div>Bureau d'Études Automatisé</div> | <div>Résidence Papa Oumar Sakho</div> <div>Dakar, Senegal</div> | <div>Éch: 1/100</div> <div>Pl. 24/32</div>    |
|                                                           | <div>Courants Forts — Étage 3</div>                             |                                               |
| <div>Date: 06/05/2026</div>                               | <div>Réf: HCU</div>                                             | <div>BIM vHCU-024</div> <div>Phase: APD</div> |



520 Courants Faibles — RDC

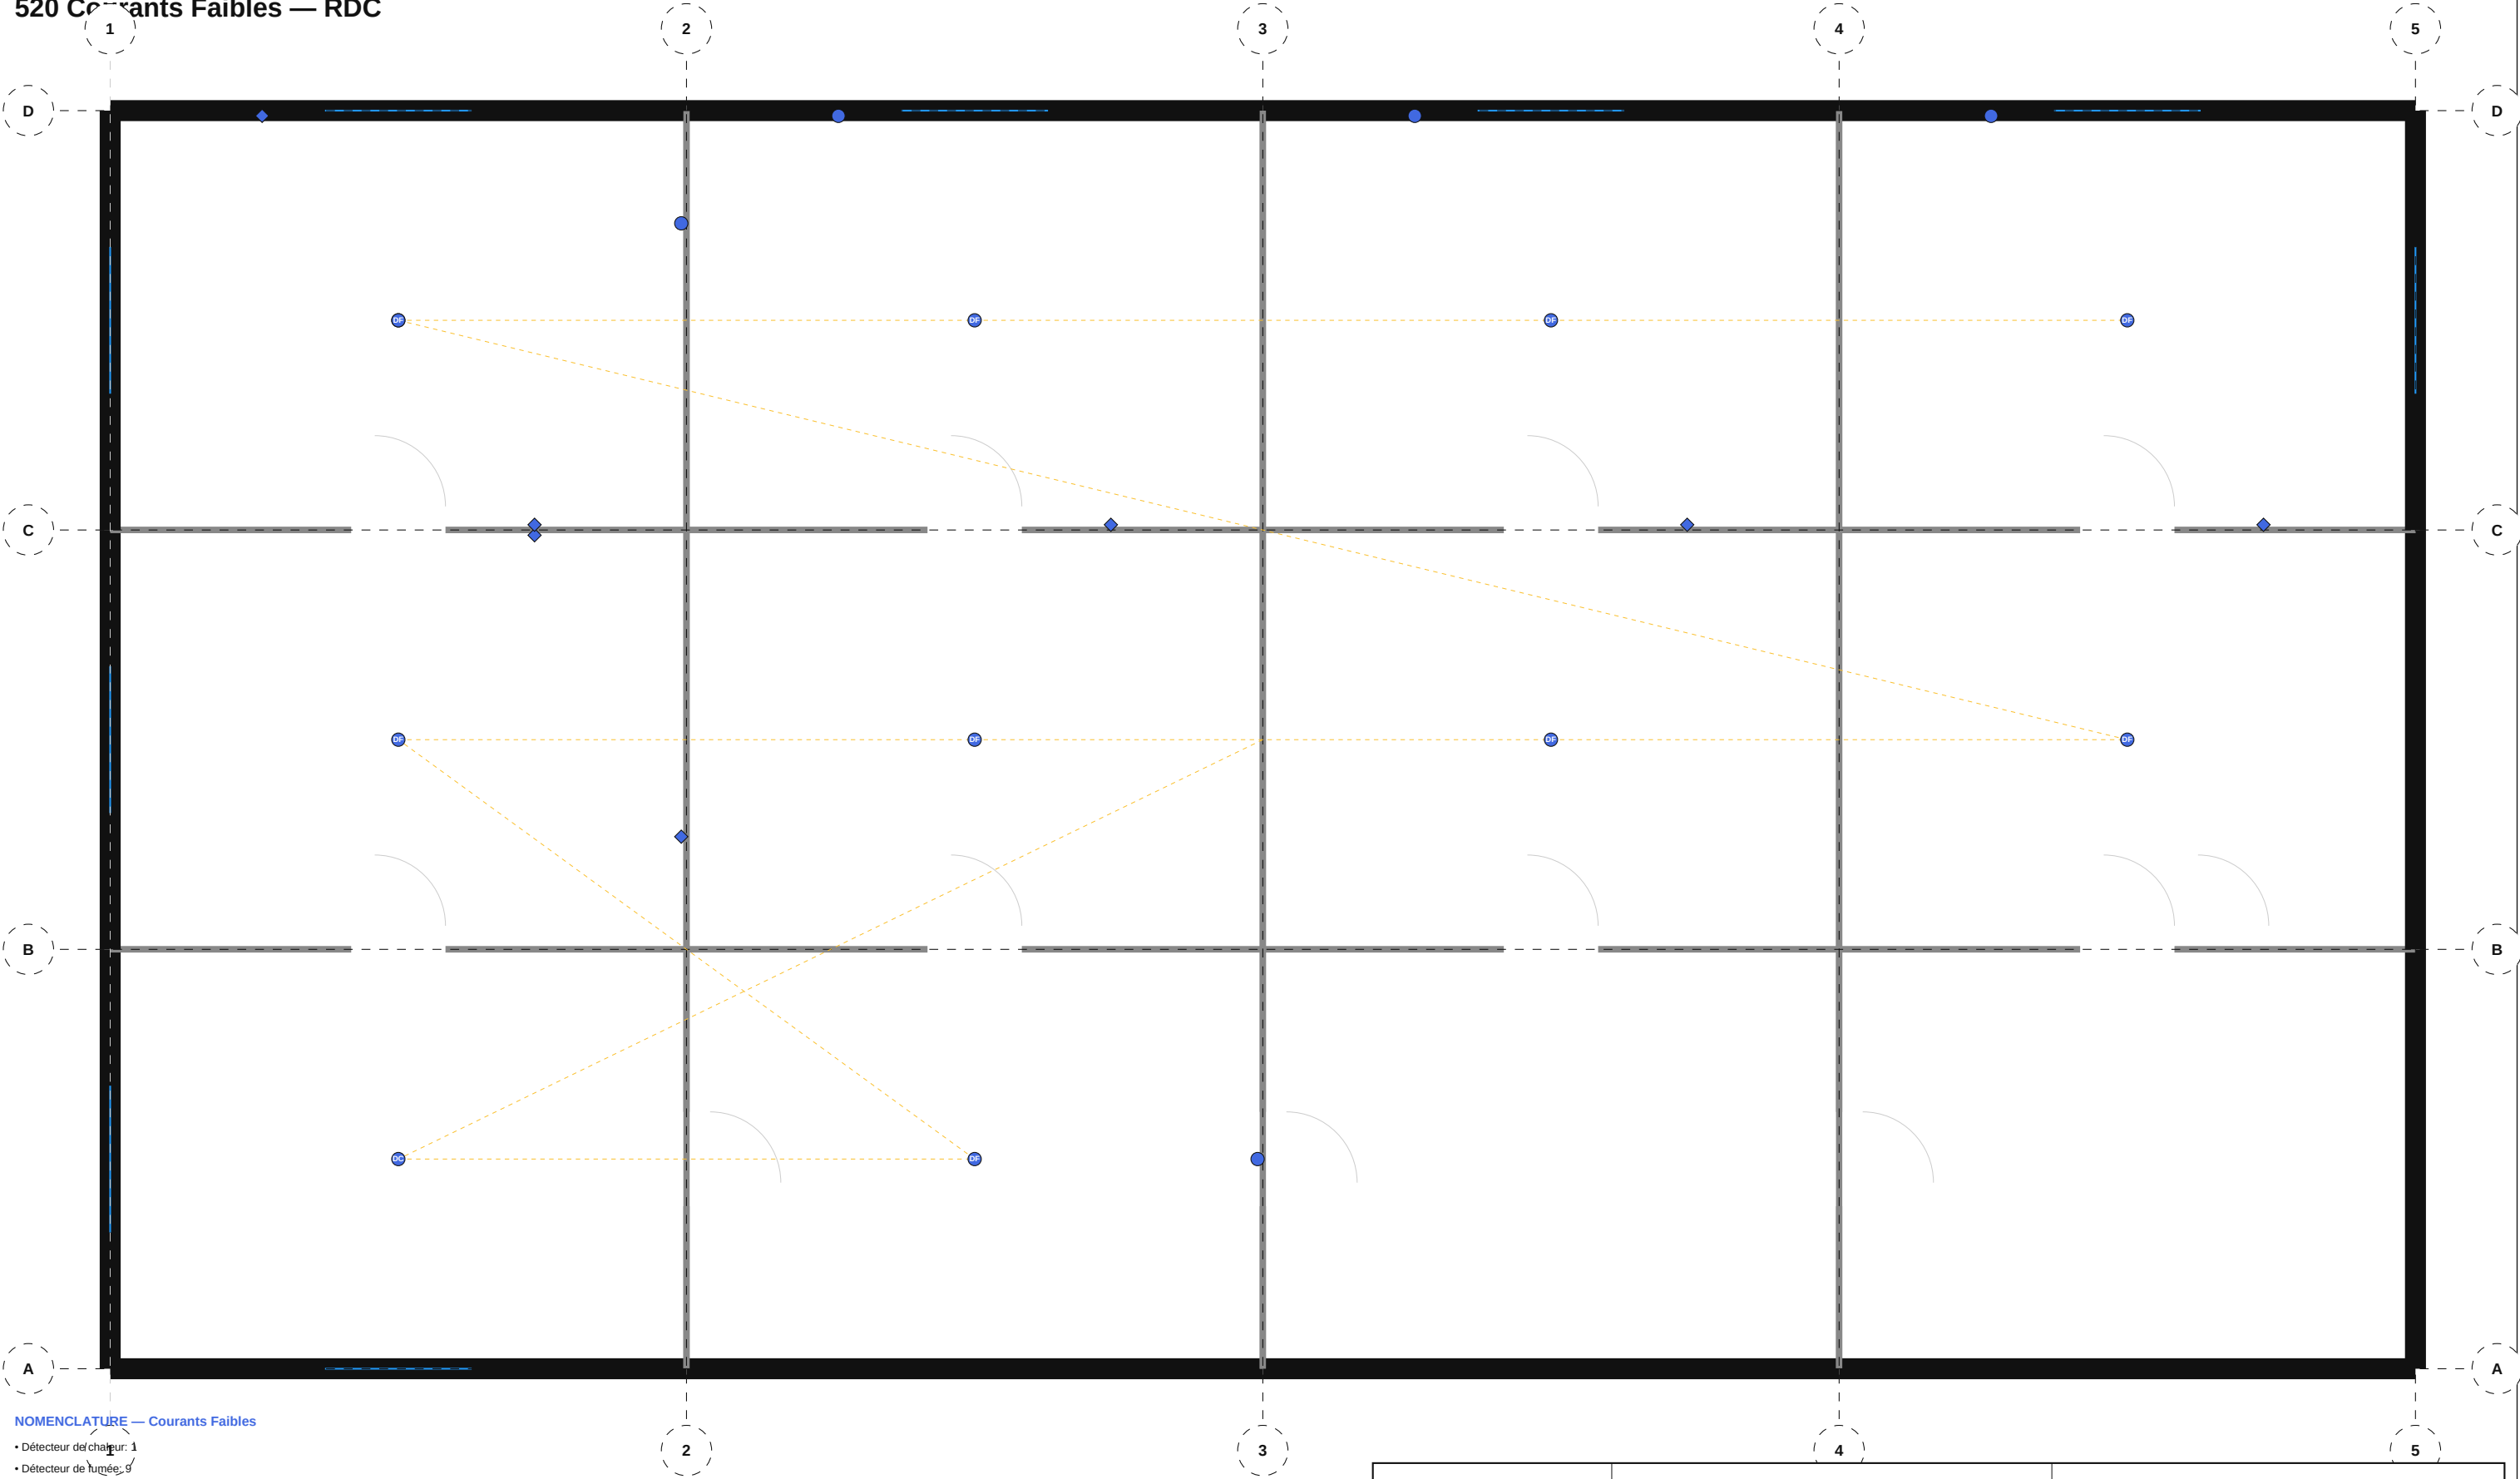


NOMENCLATURE — Courants Faibles

- Détecteur de chaleur: 1
- Détecteur de fumée: 9
- Interphone: 1
- Point d'accès WiFi: 1
- Prise RJ45: 7
- Prise TV: 4

|                                                                     |                                                                 |                                                |
|---------------------------------------------------------------------|-----------------------------------------------------------------|------------------------------------------------|
| <div><div>TIJAN AI</div><div>Bureau d'Études Automatisé</div></div> | <div>Résidence Papa Oumar Sakho</div> <div>Dakar, Senegal</div> | <div>Éch: 1/100</div> <div>Pl. 25/32</div>     |
|                                                                     | <div>Courants Faibles — RDC</div>                               |                                                |
| <div>Date: 06/05/2026</div>                                         | <div>Réf: LCU</div>                                             | <div>BIM V.LCU-025</div> <div>Phase: APD</div> |

520 Courants Faibles — Étage 1

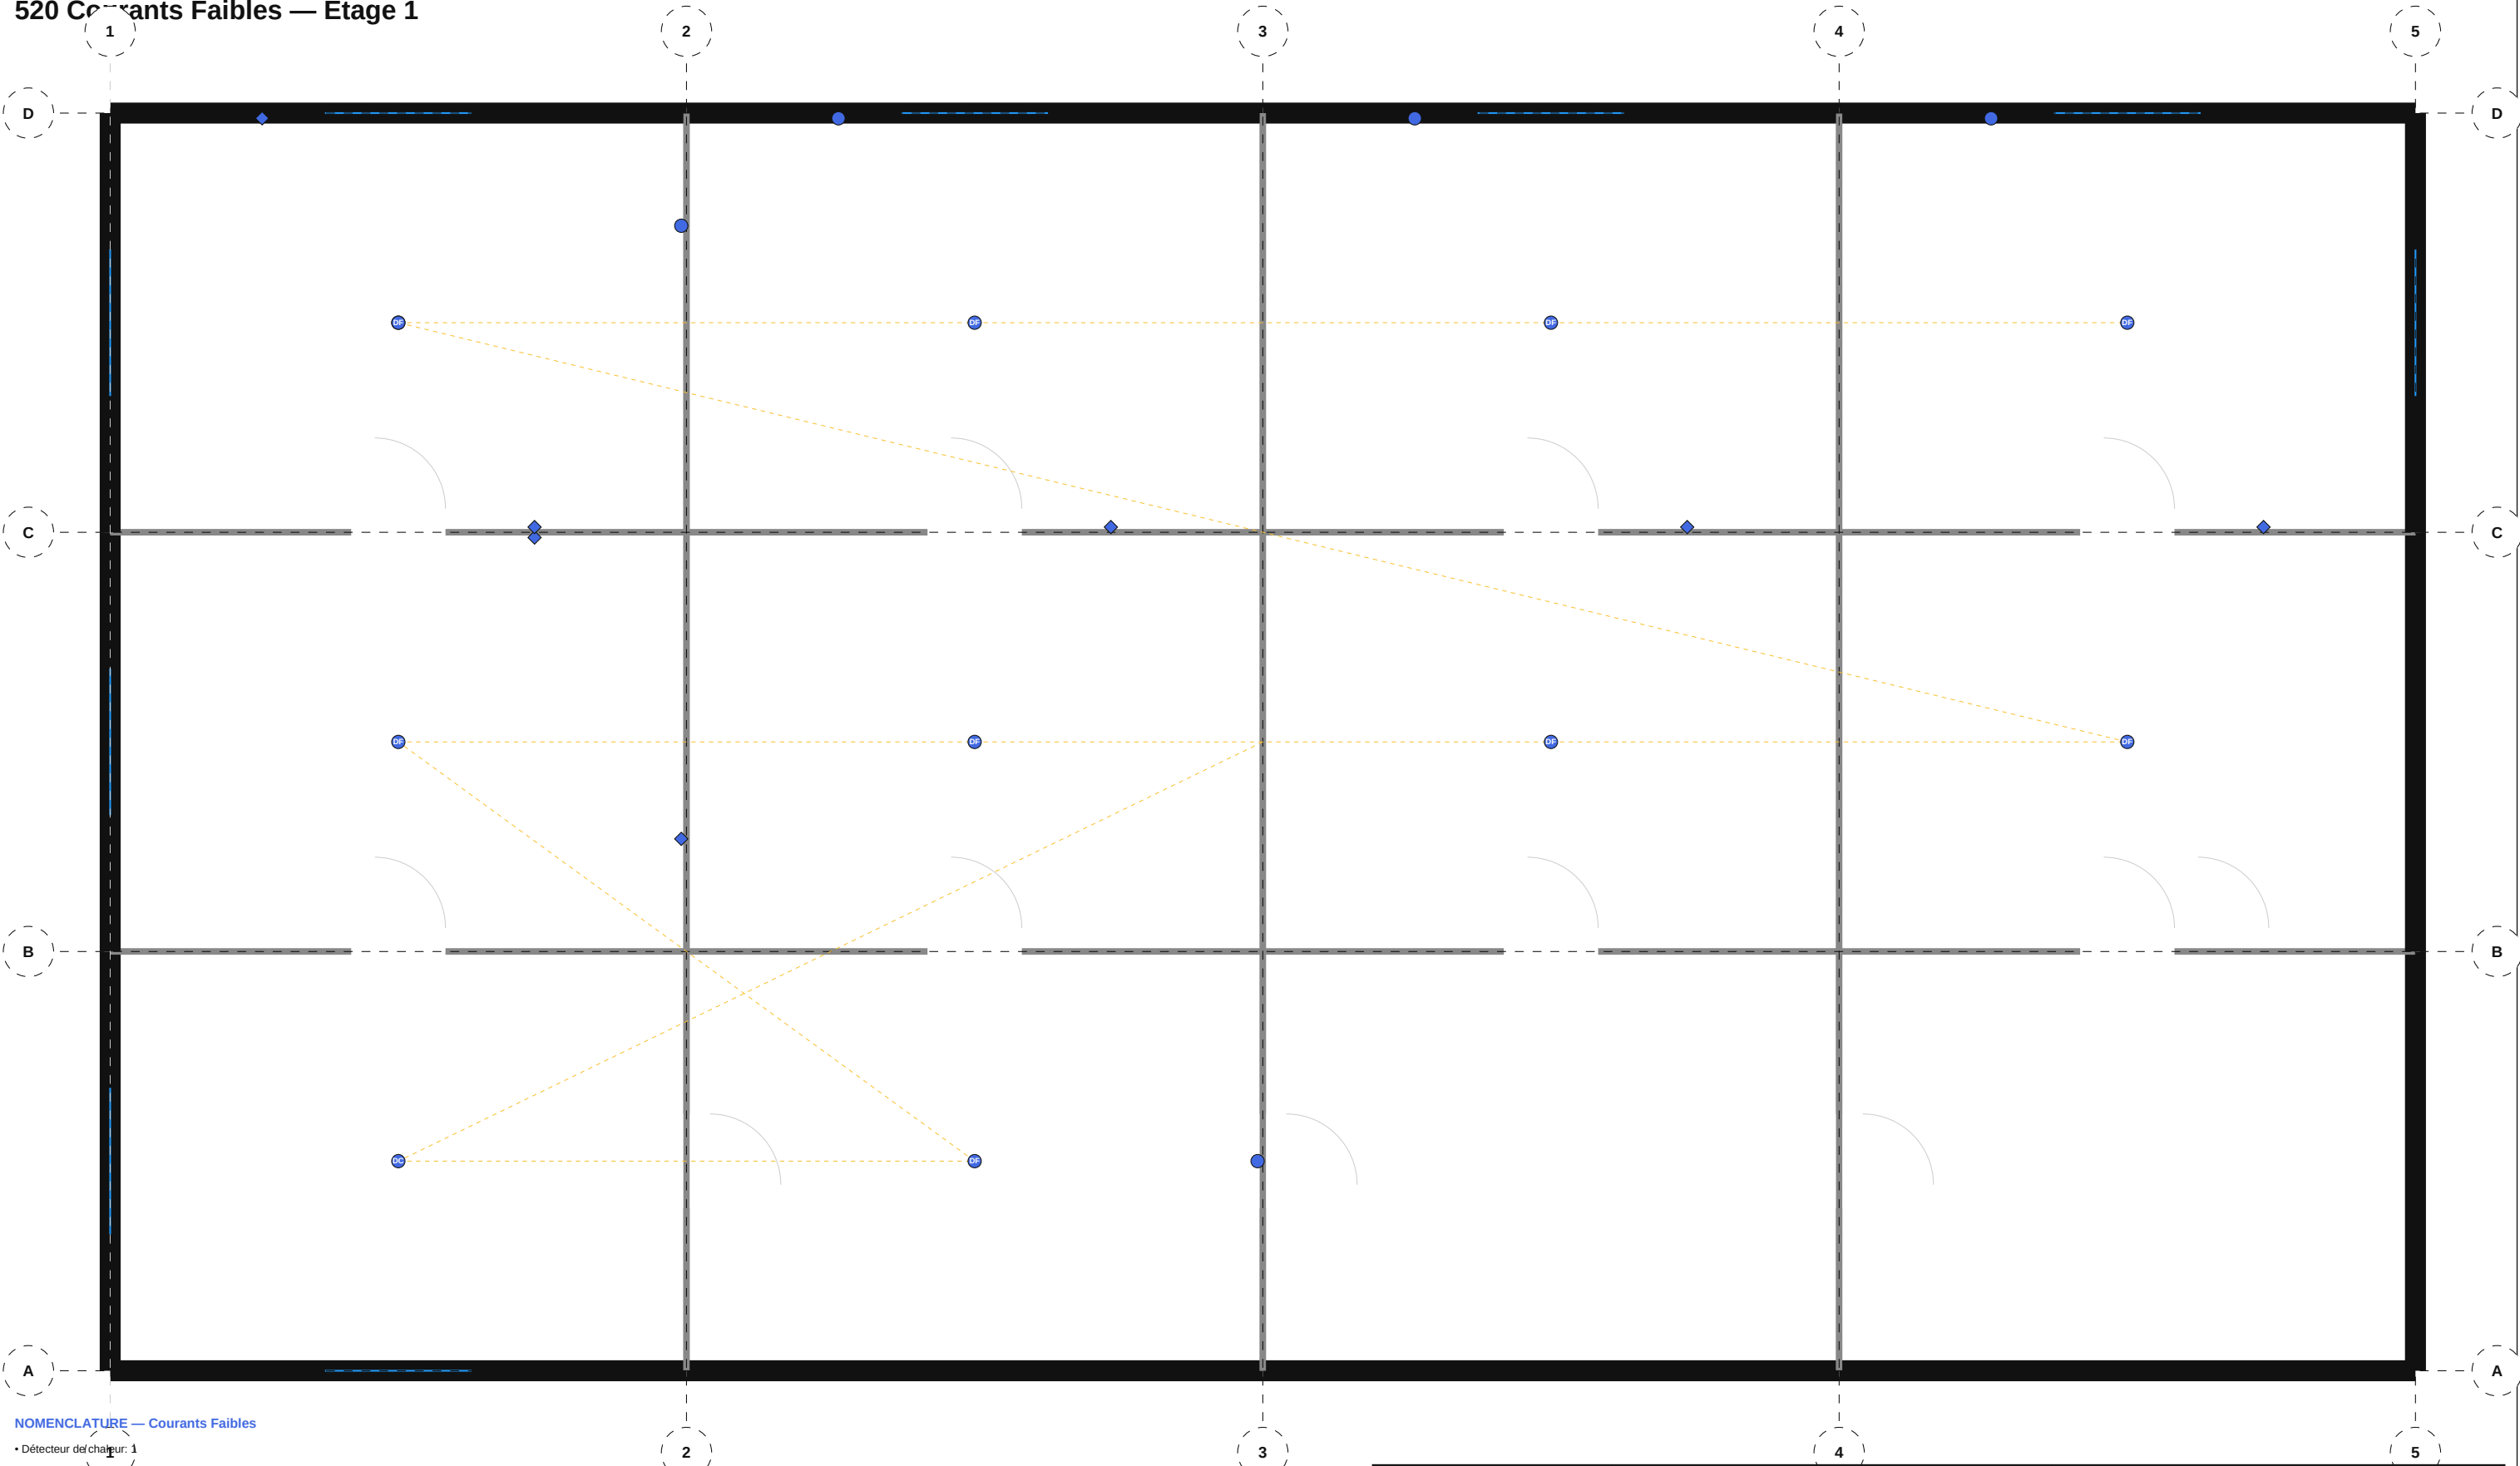


NOMENCLATURE — Courants Faibles

- Détecteur de chaleur: 1
- Détecteur de fumée: 9
- Interphone: 1
- Point d'accès WiFi: 1
- Prise RJ45: 7
- Prise TV: 4

|                                                           |                                                                 |                                               |
|-----------------------------------------------------------|-----------------------------------------------------------------|-----------------------------------------------|
| <div>TIJAN AI</div> <div>Bureau d'Études Automatisé</div> | <div>Résidence Papa Oumar Sakho</div> <div>Dakar, Senegal</div> | <div>Éch: 1/100</div> <div>Pl. 26/32</div>    |
|                                                           | <div>Courants Faibles — Étage 1</div>                           |                                               |
| <div>Date: 06/05/2026</div>                               | <div>Réf: LCU</div>                                             | <div>BIM vLCU-026</div> <div>Phase: APD</div> |

## 520 Courants Faibles — Étage 2

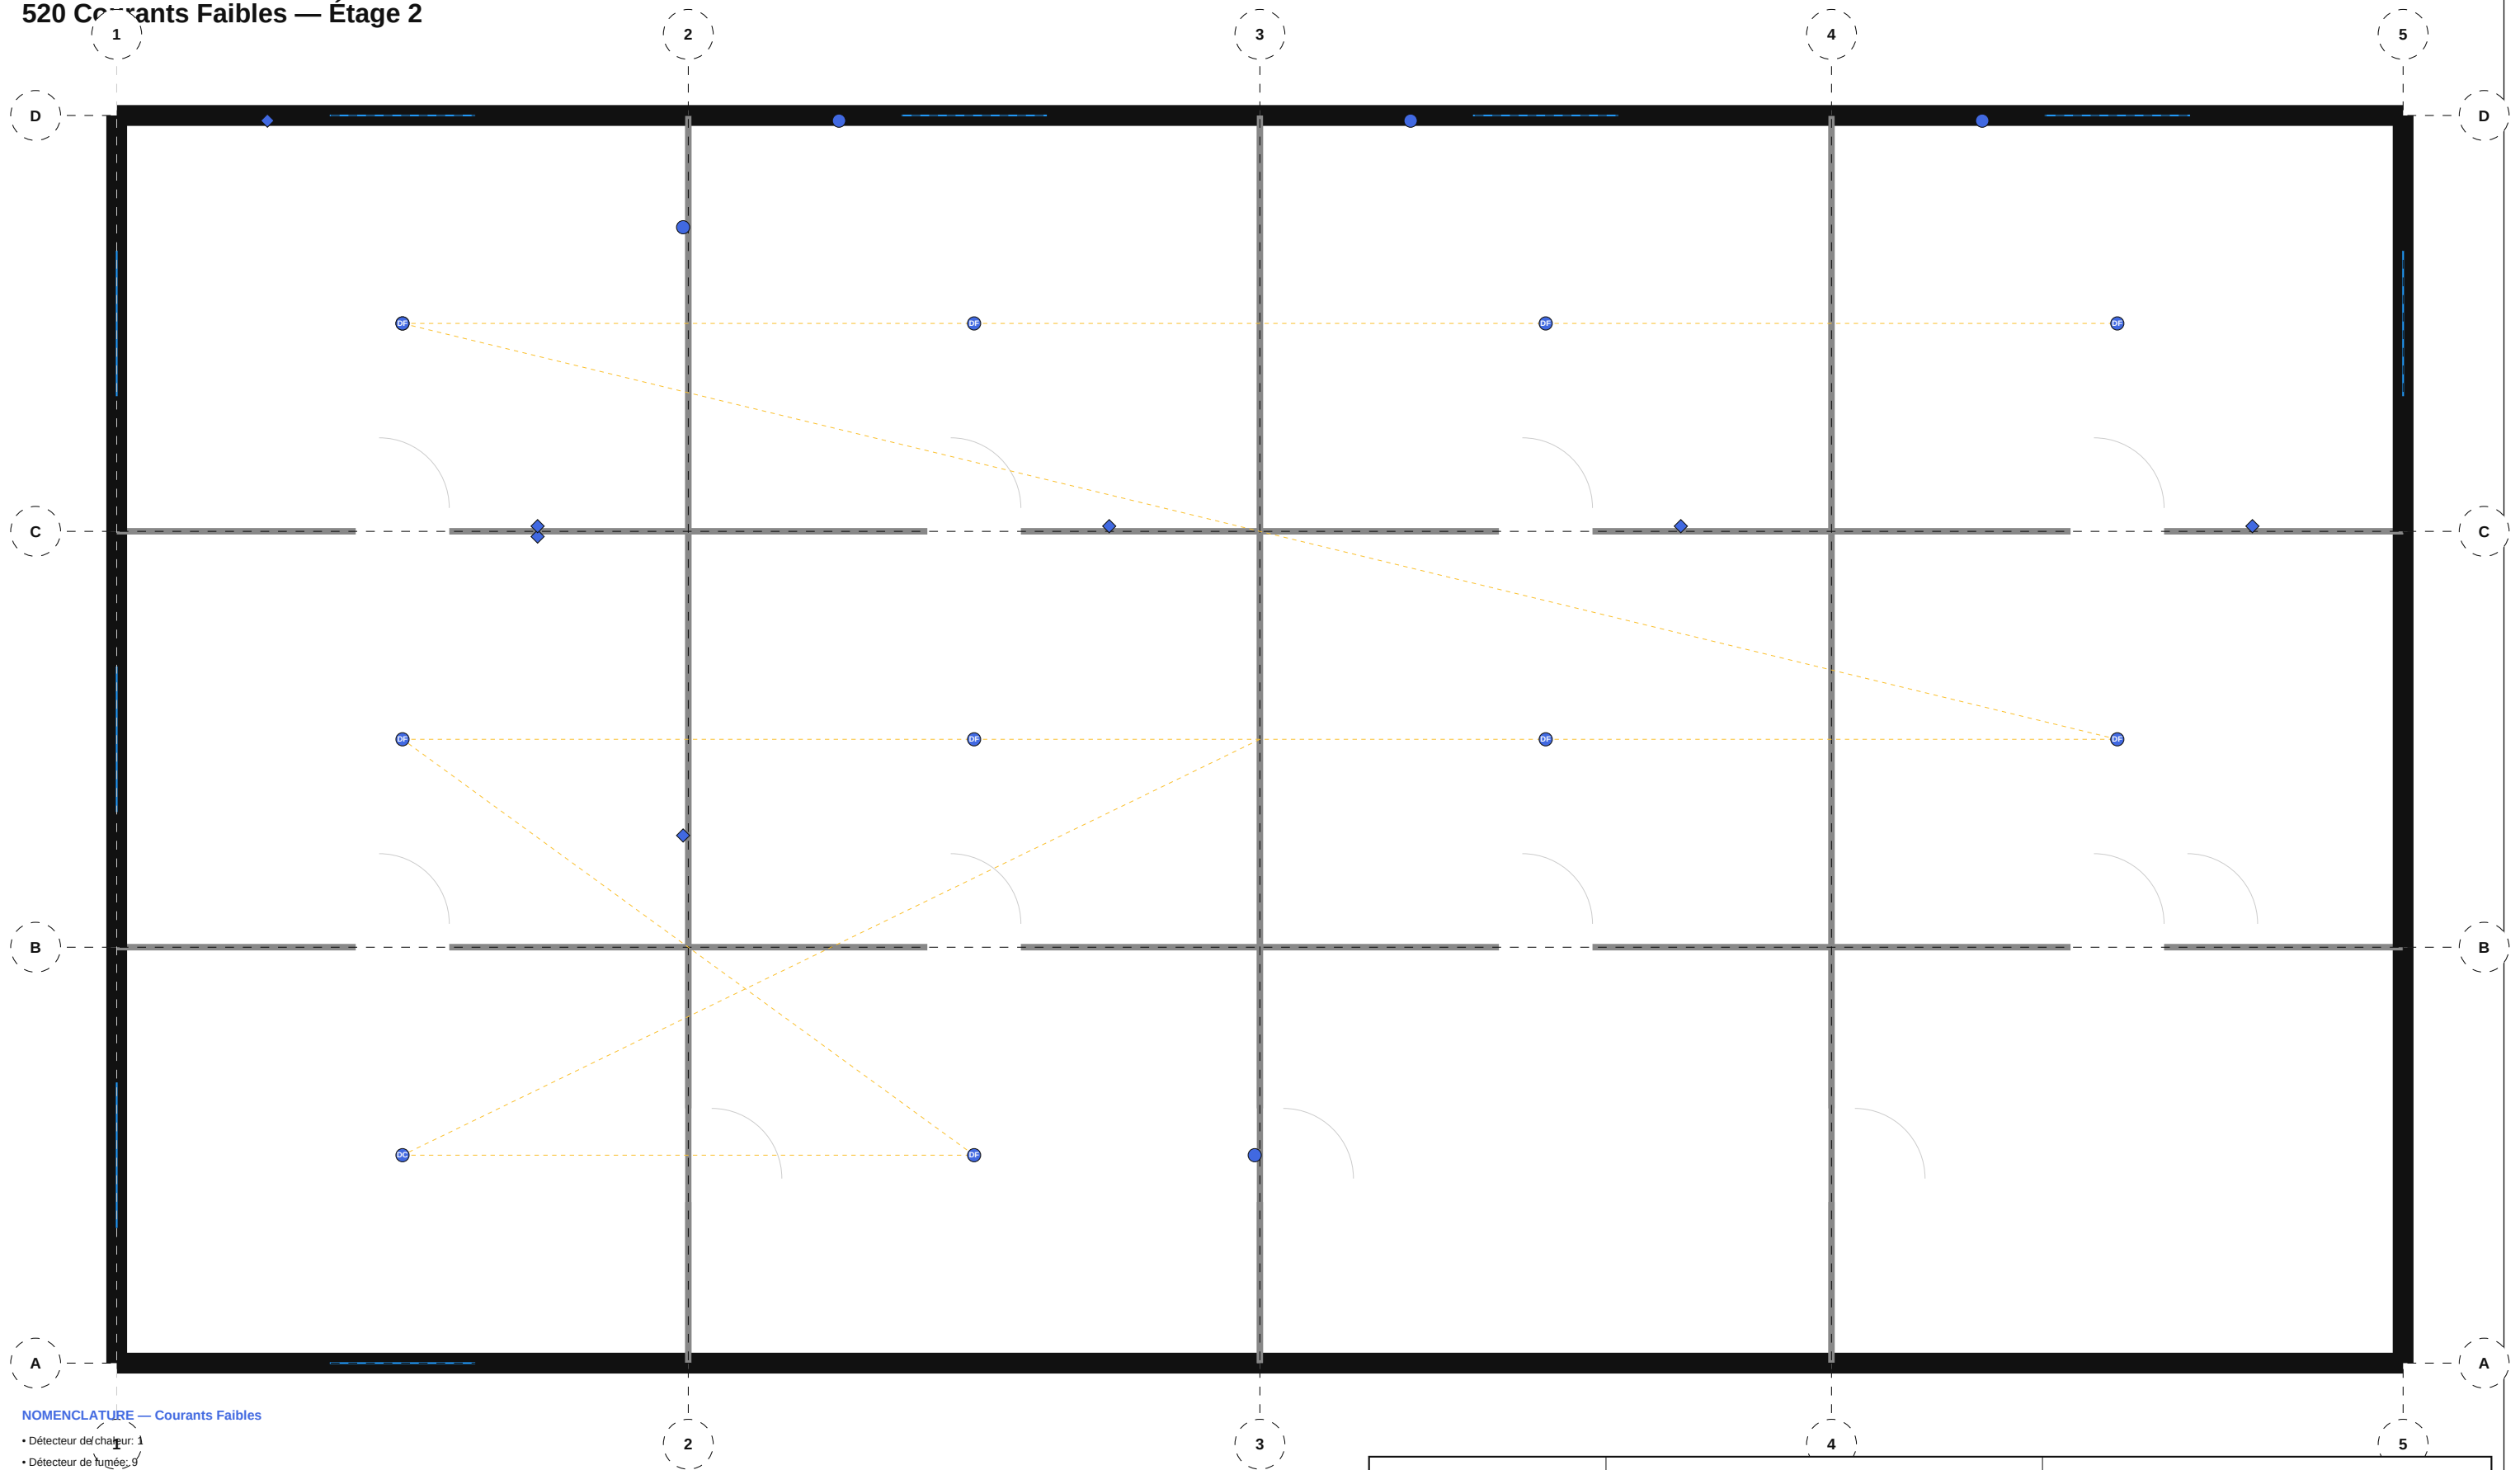


## NOMENCLATURE — Courants Faibles

- Détecteur de chaleur: 1
- Détecteur de fumée: 9
- Interphone: 1
- Point d'accès WiFi: 1
- Prise RJ45: 7
- Prise TV: 4

|                                                                                |                                                                                      |                                                                 |
|--------------------------------------------------------------------------------|--------------------------------------------------------------------------------------|-----------------------------------------------------------------|
| <div><div><div>TIJAN AI</div><div>Bureau d'Études Automatisé</div></div></div> | <div><div><div>Résidence Papa Oumar Sakho</div><div>Dakar, Senegal</div></div></div> | <div><div><div>Éch: 1/100</div><div>Pl. 27/32</div></div></div> |
|                                                                                | <div><div>Courants Faibles — Étage 2</div></div>                                     |                                                                 |
| <div><div>Date: 06/05/2026</div></div>                                         | <div><div>Réf: LCU</div></div>                                                       | <div><div>BIM vLCU-027</div><div>Phase: APD</div></div>         |

520 Courants Faibles — Étage 3

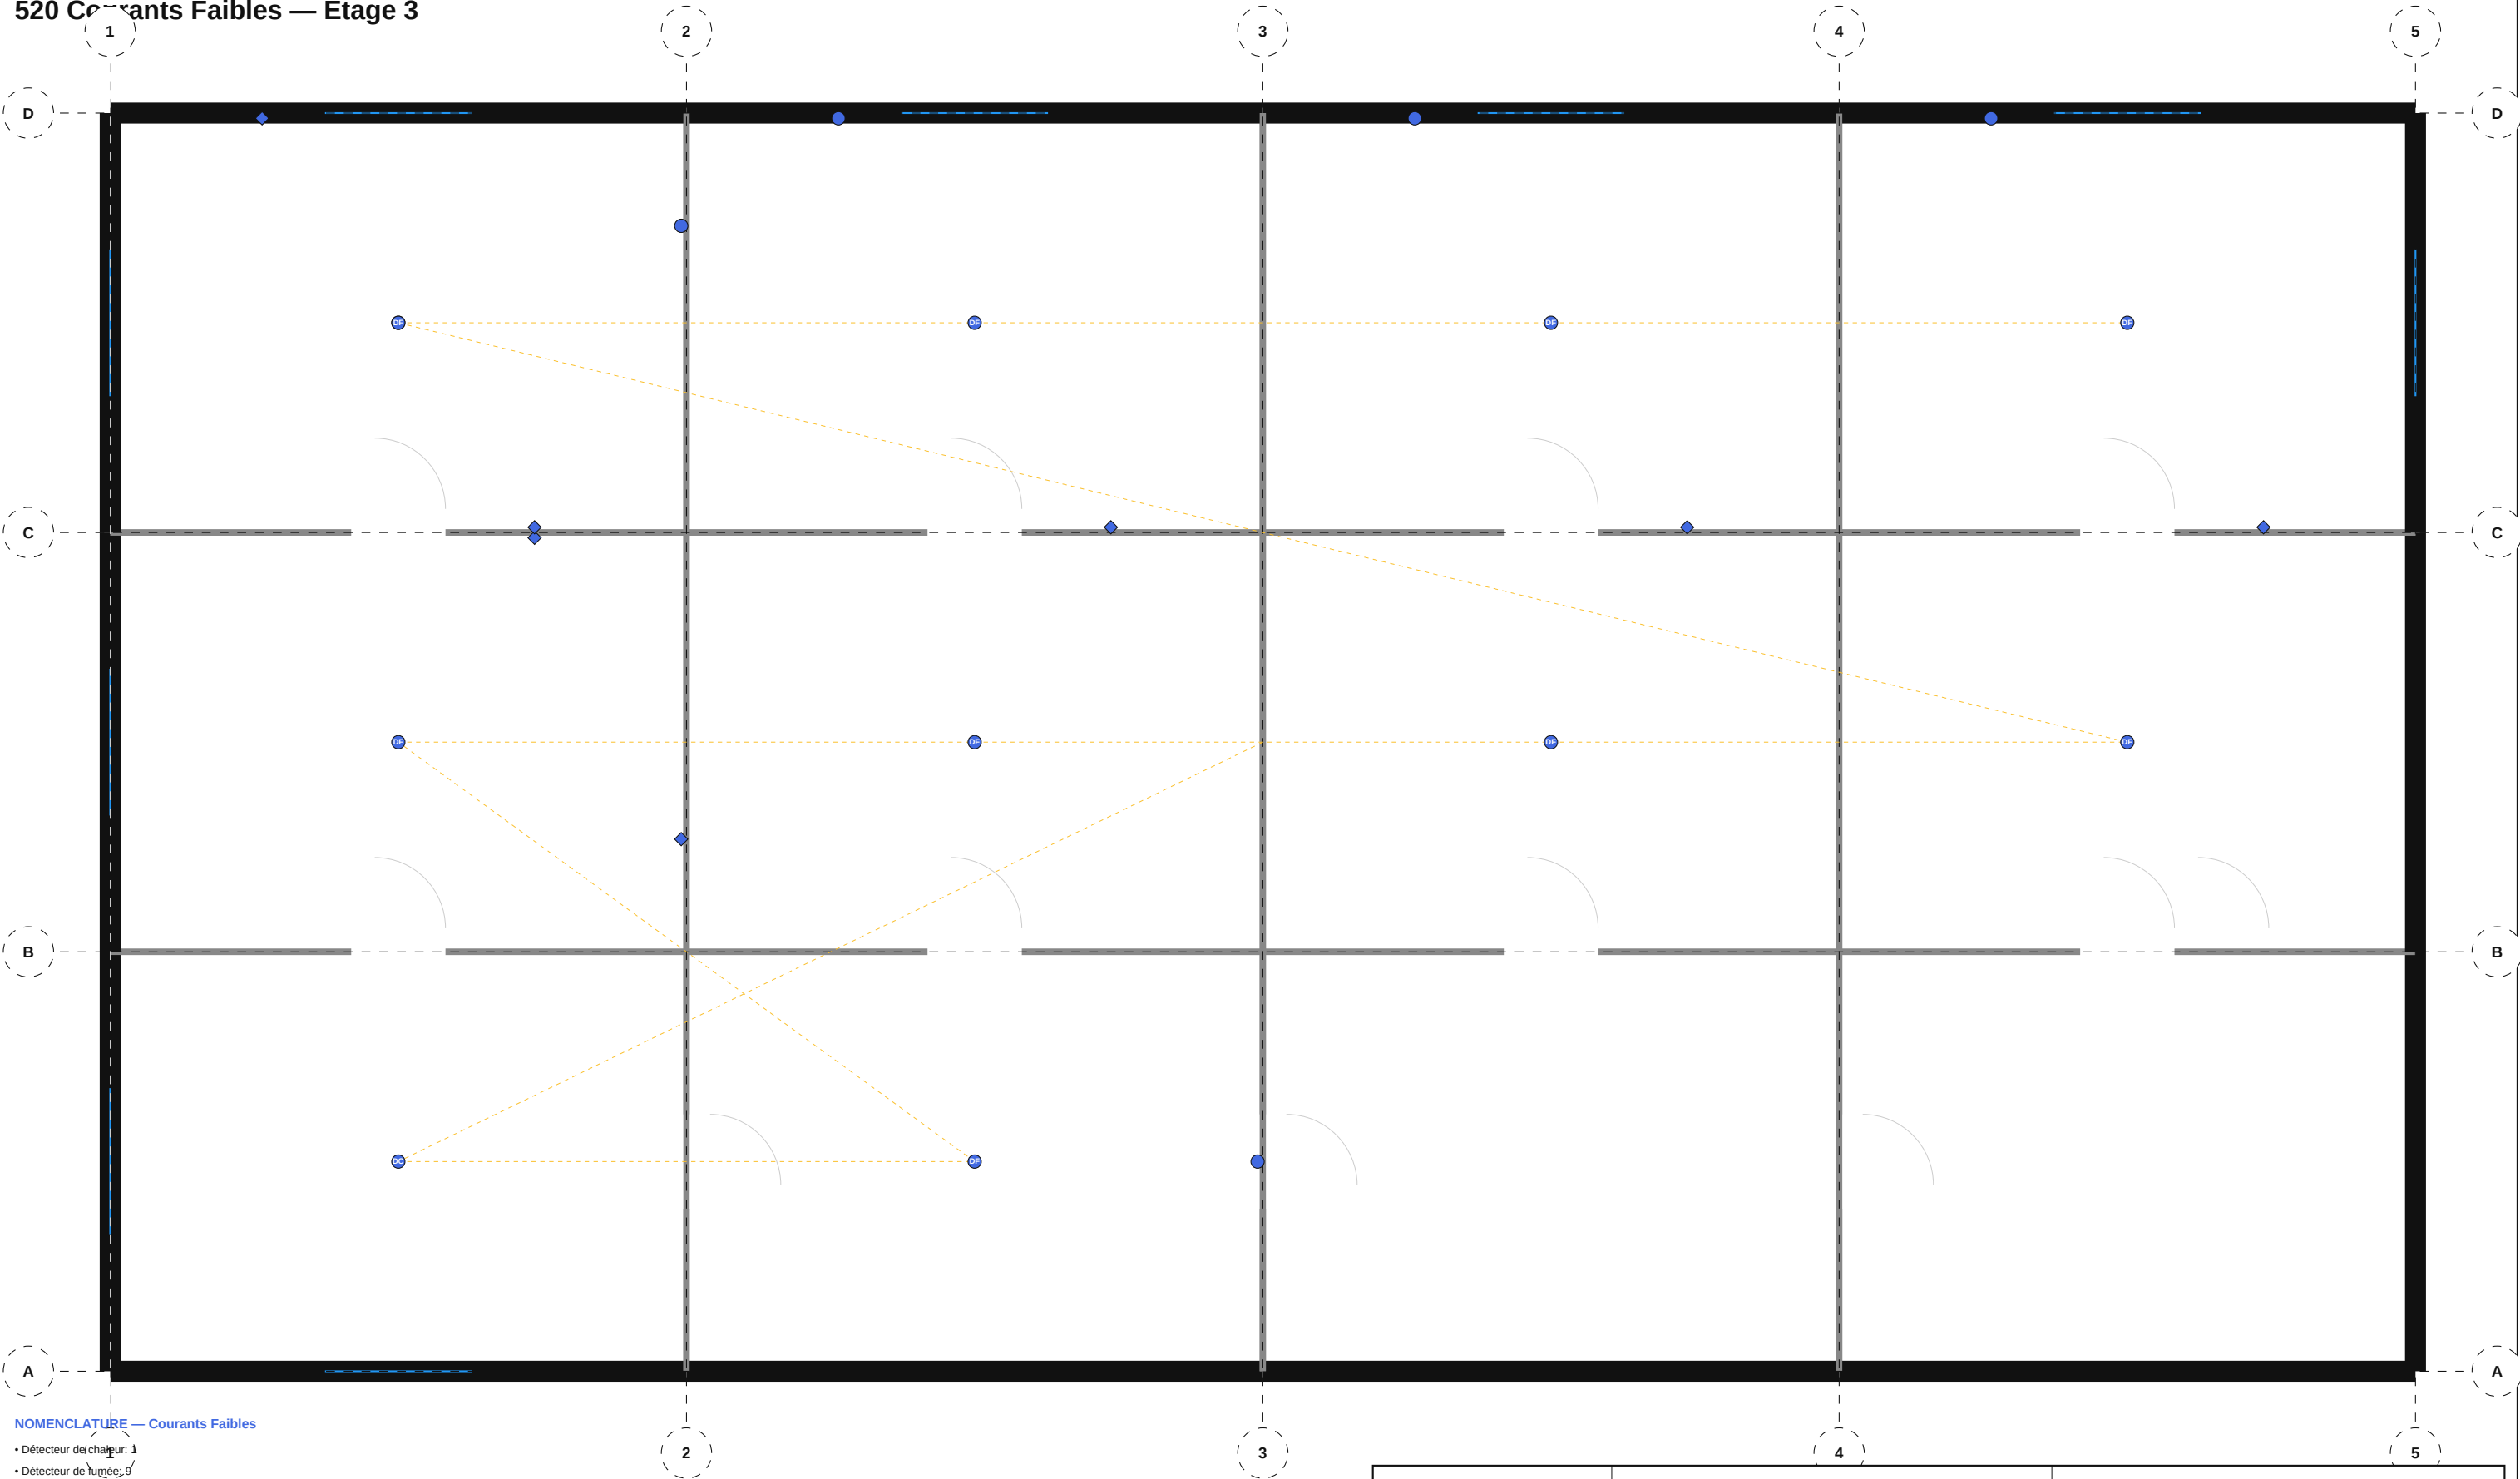

NOMENCLATURE — Courants Faibles

- Détecteur de chaleur: 1
- Détecteur de fumée: 9
- Interphone: 1
- Point d'accès WiFi: 1
- Prise RJ45: 7
- Prise TV: 4

TIJAN AI

Bureau d'Études Automatisé

Résidence Papa Oumar Sakho

Dakar, Senegal

Éch: 1/100

Pl. 28/32

Courants Faibles — Étage 3

Date: 06/05/2026

Réf: LCU


BIM vLCU-028

Phase: APD

001 Synthèse / Coordination — RDC

LÉGENDE RÉSEAUX

- EF — Eau Froide
- EC — Eau Chaude
- EU — Eaux Usées
- CLIM — Réfrigération
- VMC — Extraction
- HCU — Courants Froids
- LCU — Courants Chauds
- SPK — Sprinklers

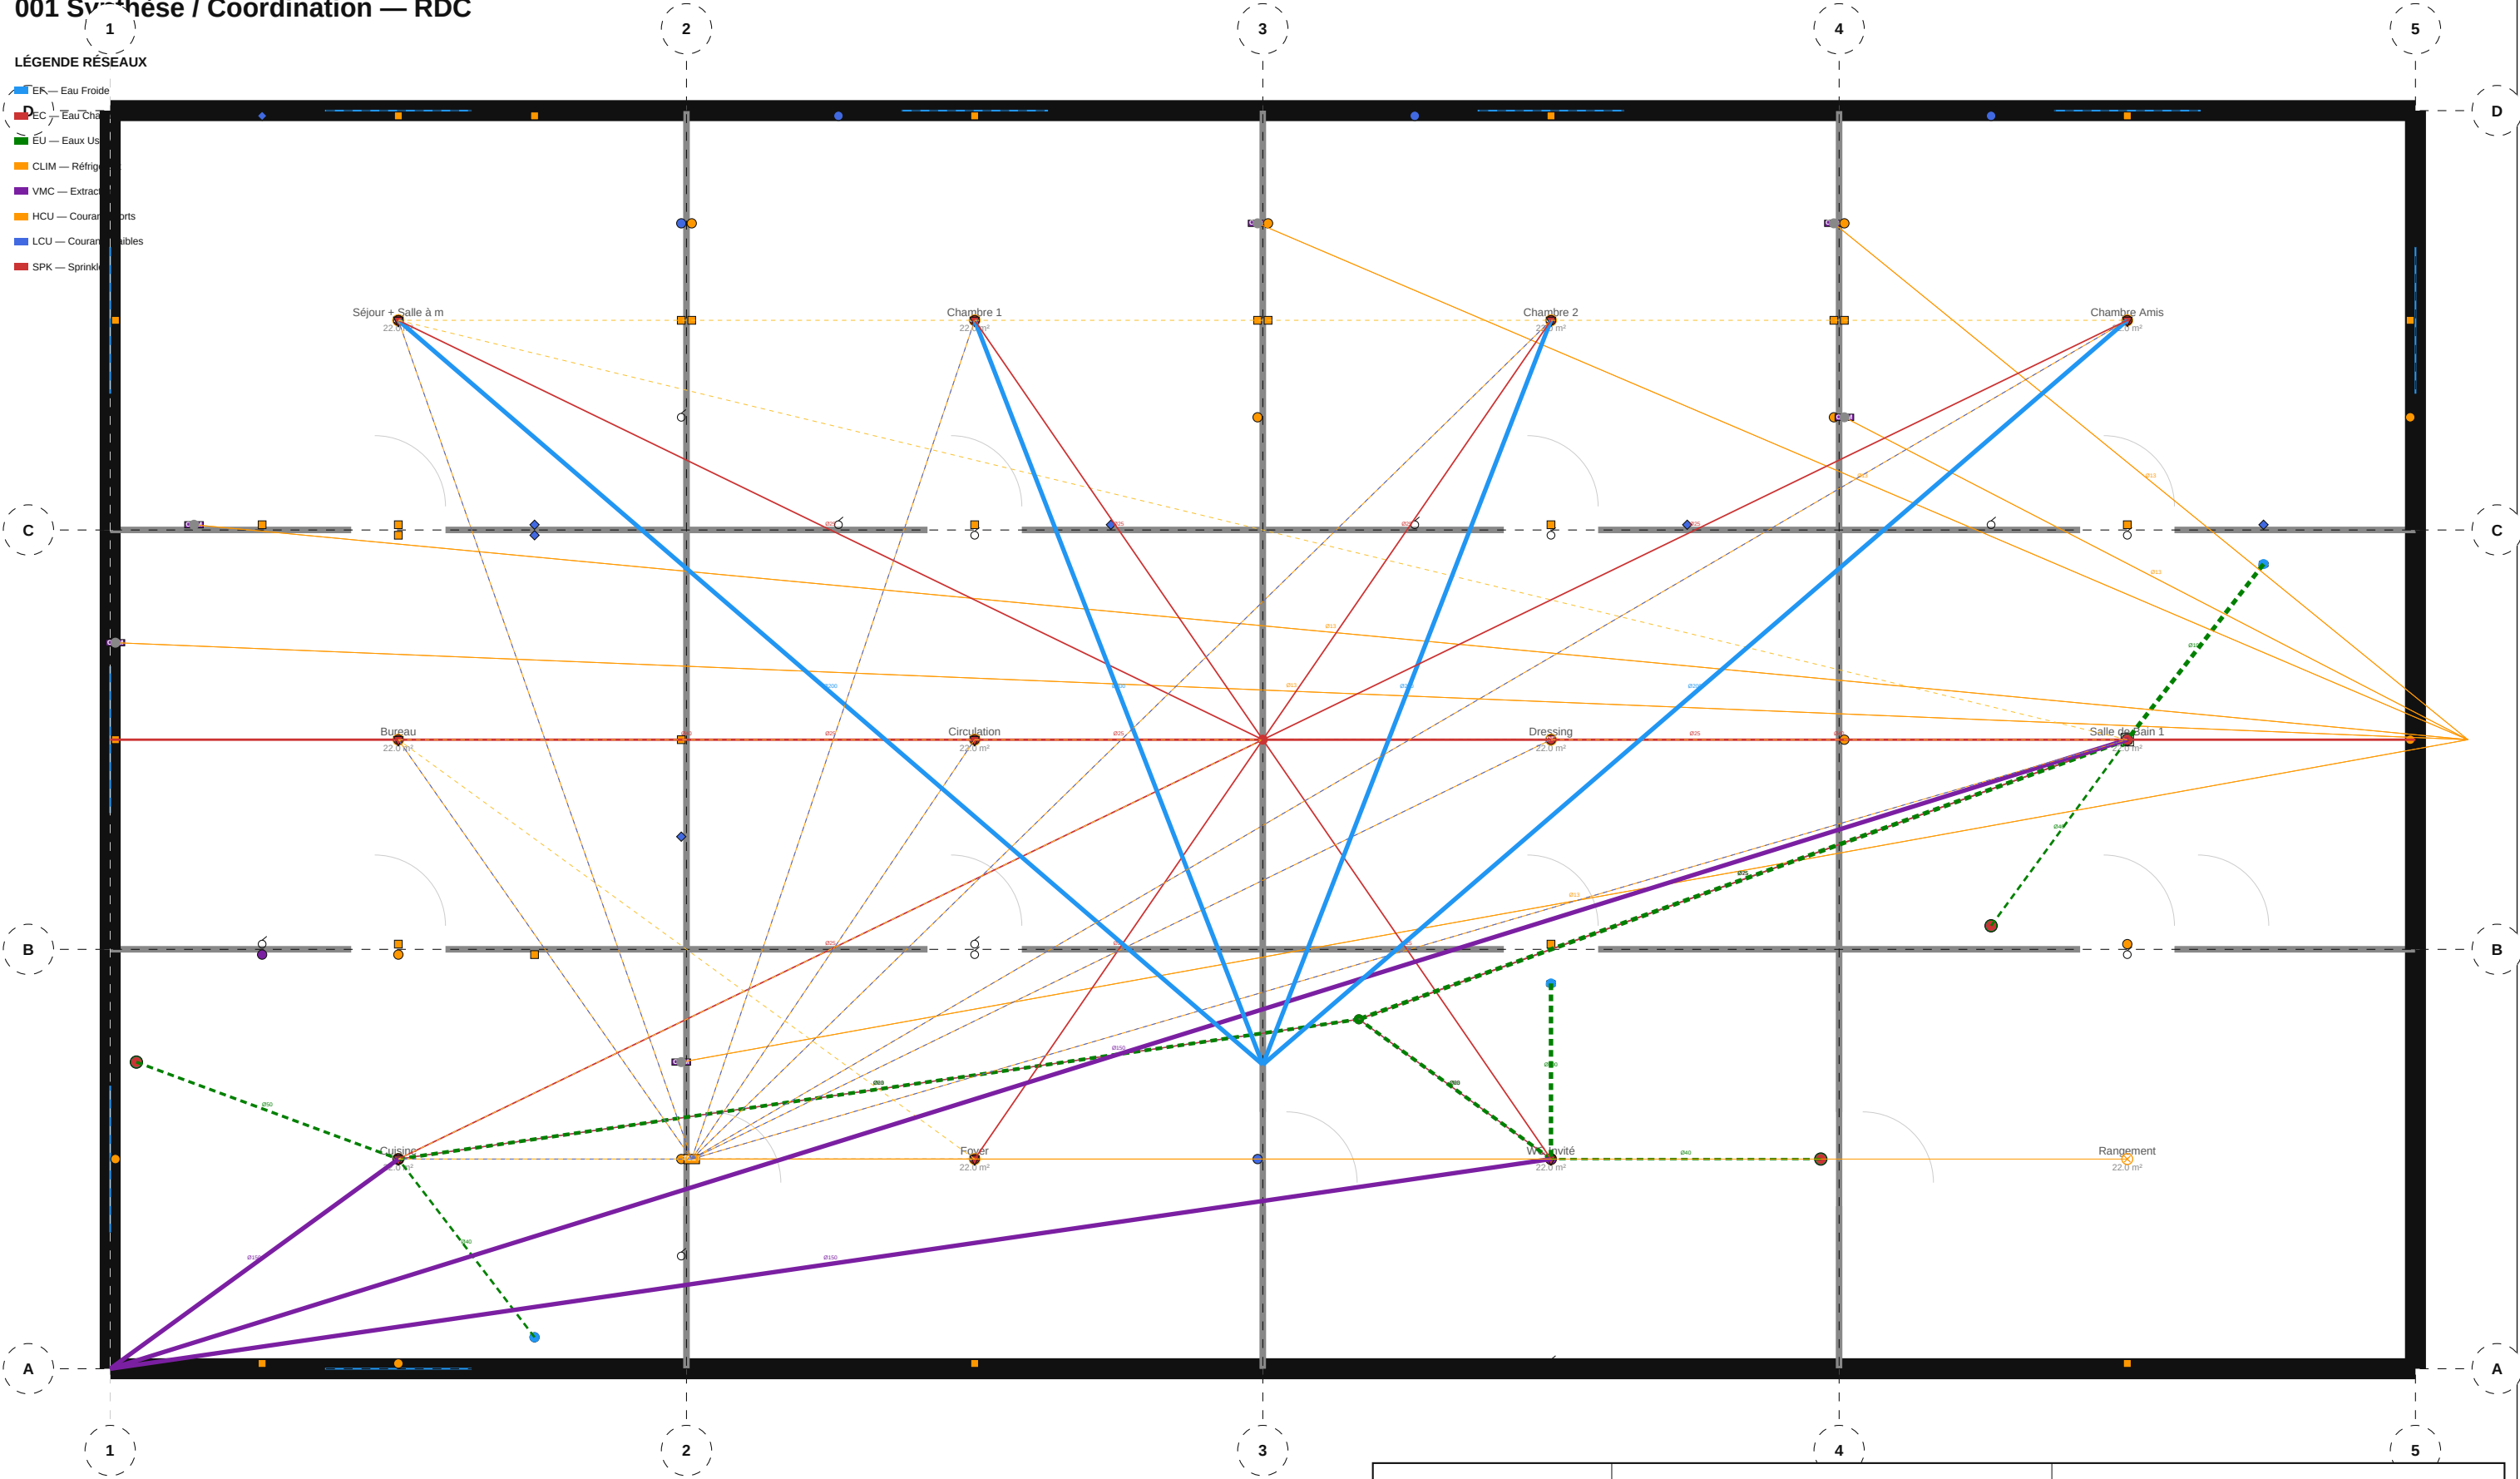


|                                               |                                                     |                            |
|-----------------------------------------------|-----------------------------------------------------|----------------------------|
| <b>TIJAN AI</b><br>Bureau d'Études Automatisé | <b>Résidence Papa Oumar Sakho</b><br>Dakar, Senegal | Éch: 1/100<br>Pl. 29/32    |
|                                               | <b>Synthèse / Coordination — RDC</b>                |                            |
| Date: 06/05/2026                              | Réf: SYN                                            | BIM vSYN-029<br>Phase: APD |

001 Synthèse / Coordination — Étage 1

LÉGENDE RÉSEAUX

- EF — Eau Froide
- EC — Eau Chaude
- EU — Eaux Usées
- CLIM — Réfrigération
- VMC — Extraction
- HCU — Courant Hauts
- LCU — Courant Bas
- SPK — Sprinkler

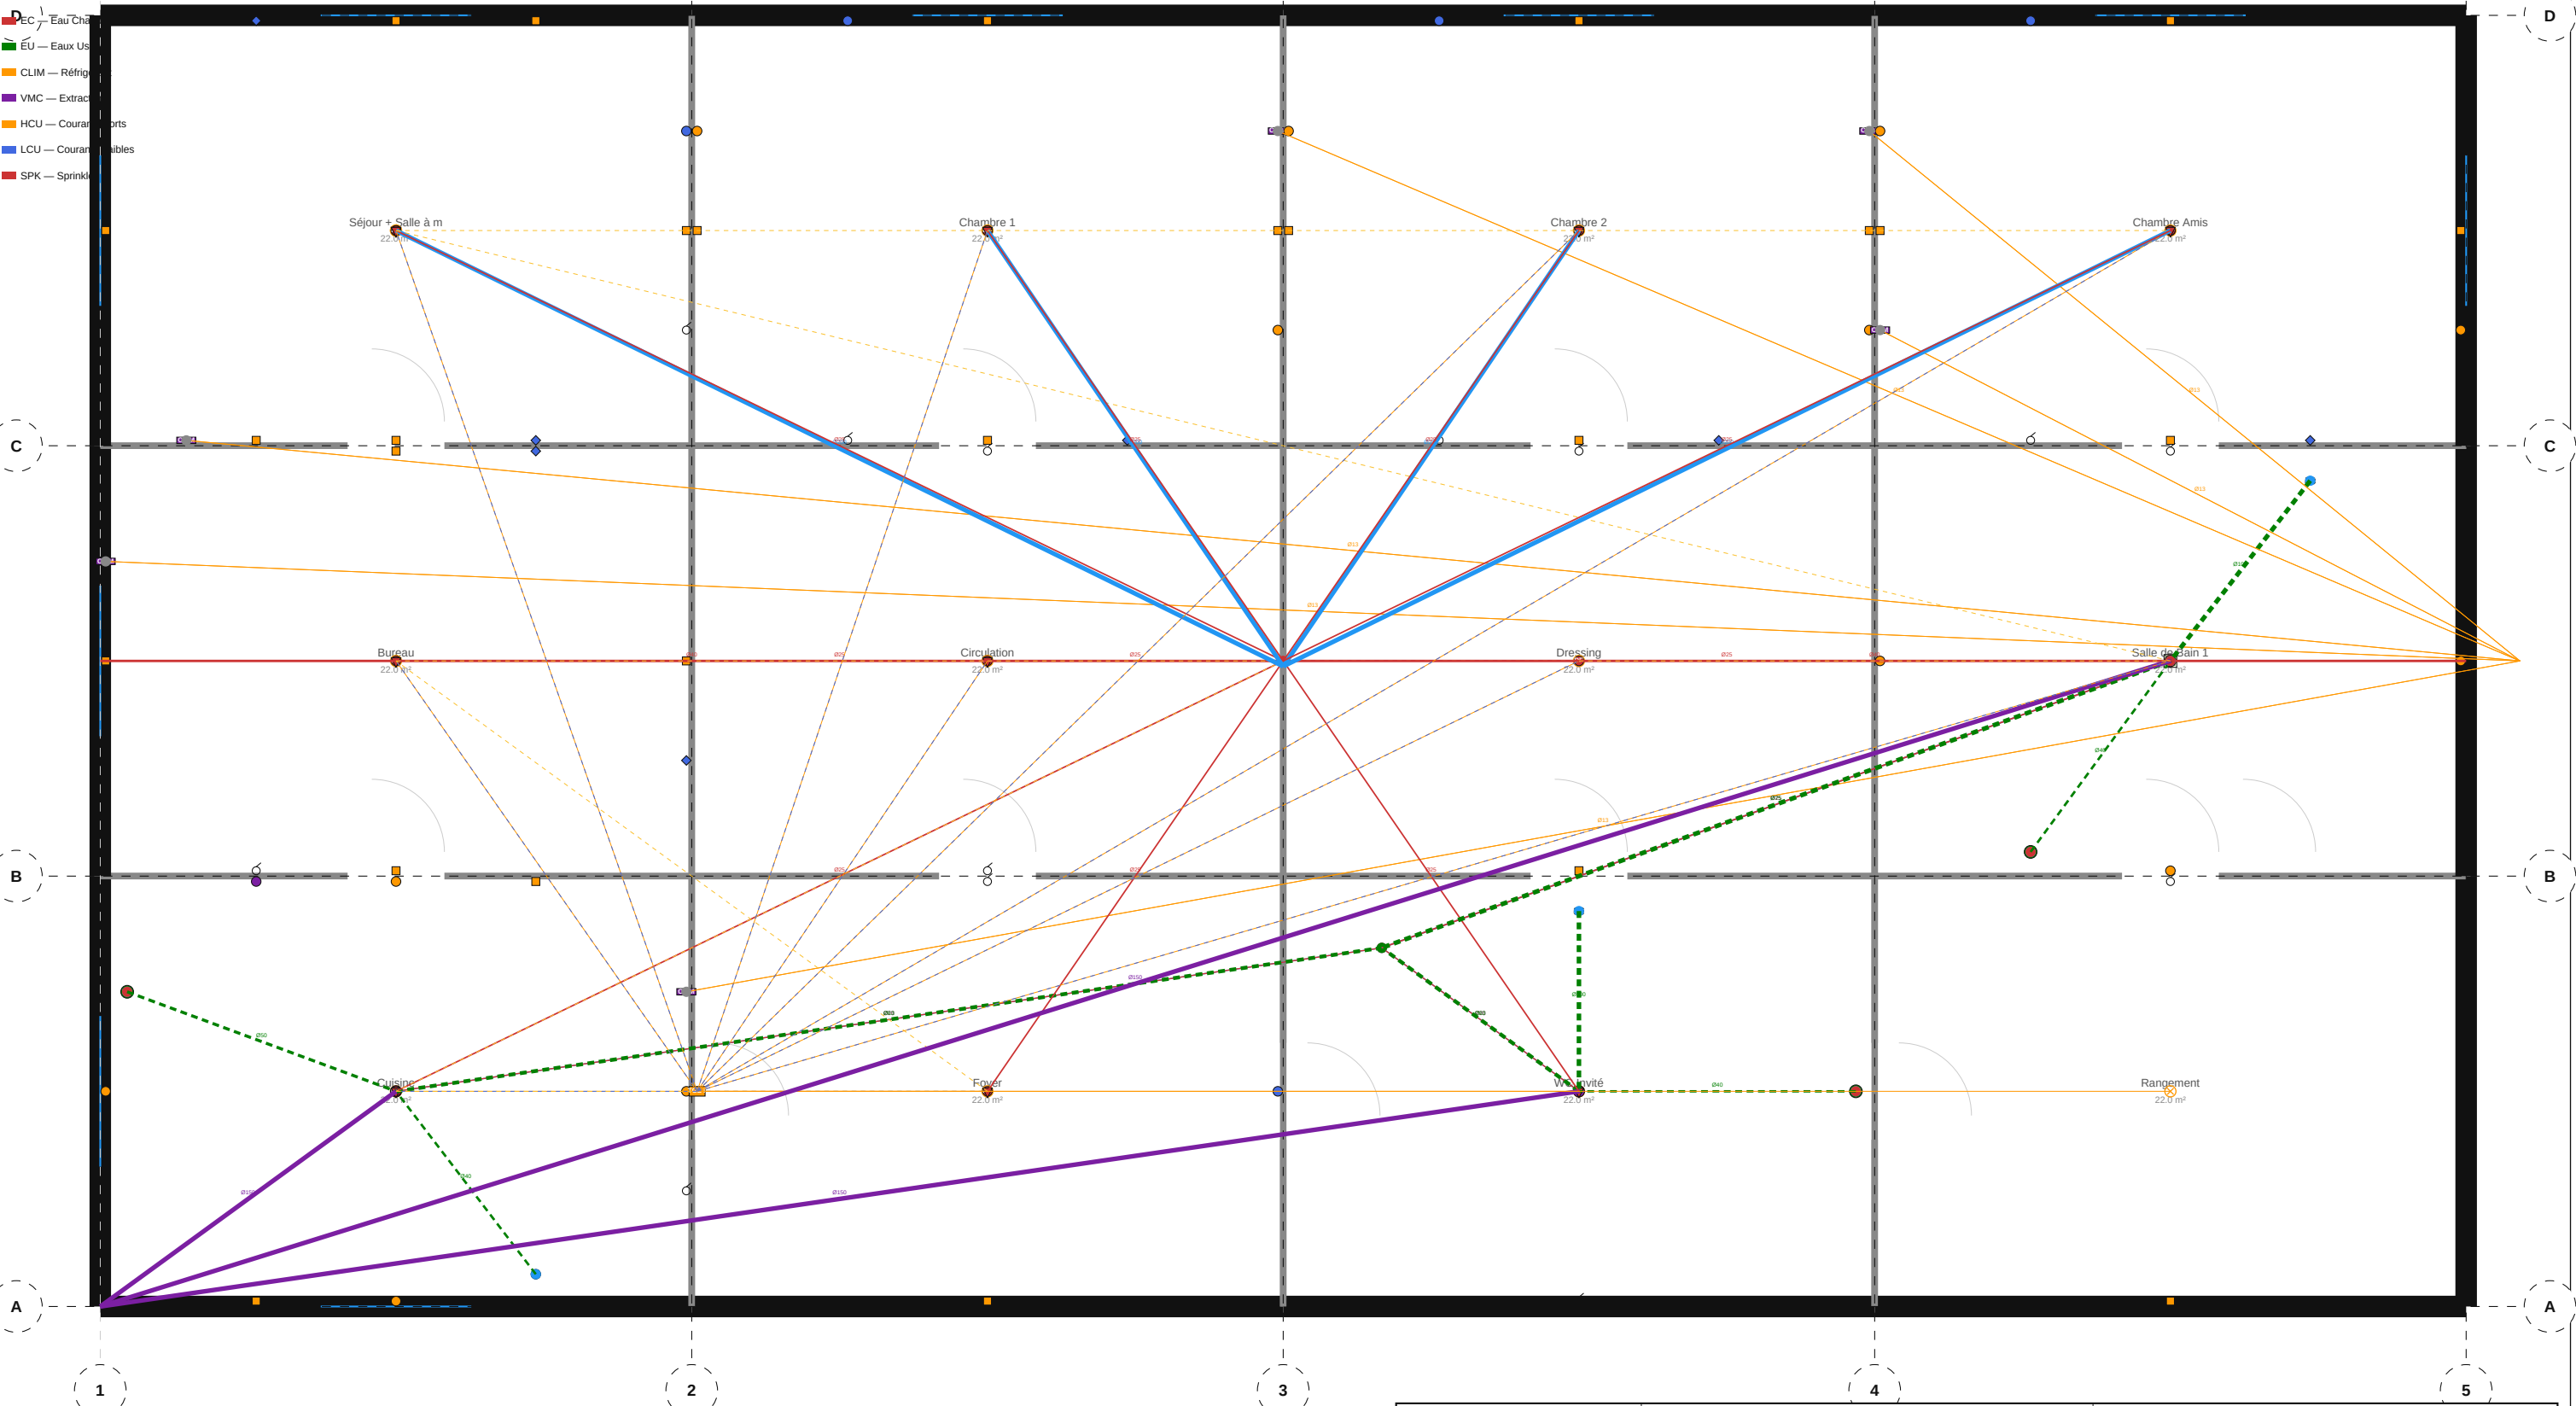


|                                               |                                                     |                            |
|-----------------------------------------------|-----------------------------------------------------|----------------------------|
| <b>TIJAN AI</b><br>Bureau d'Études Automatisé | <b>Résidence Papa Oumar Sakho</b><br>Dakar, Senegal | Éch: 1/100<br>Pl. 30/32    |
|                                               | <b>Synthèse / Coordination — Étage 1</b>            |                            |
| Date: 06/05/2026                              | Réf: SYN                                            | BIM vSYN-030<br>Phase: APD |



001 Synthèse / Coordination — Étage 2

LÉGENDE RÉSEAUX

- EF — Eau Froide
- EC — Eau Chaude
- EU — Eaux Usées
- CLIM — Réfrigération
- VMC — Extraction
- HCU — Courant Hauts
- LCU — Courant Bas
- SPK — Sprinkler

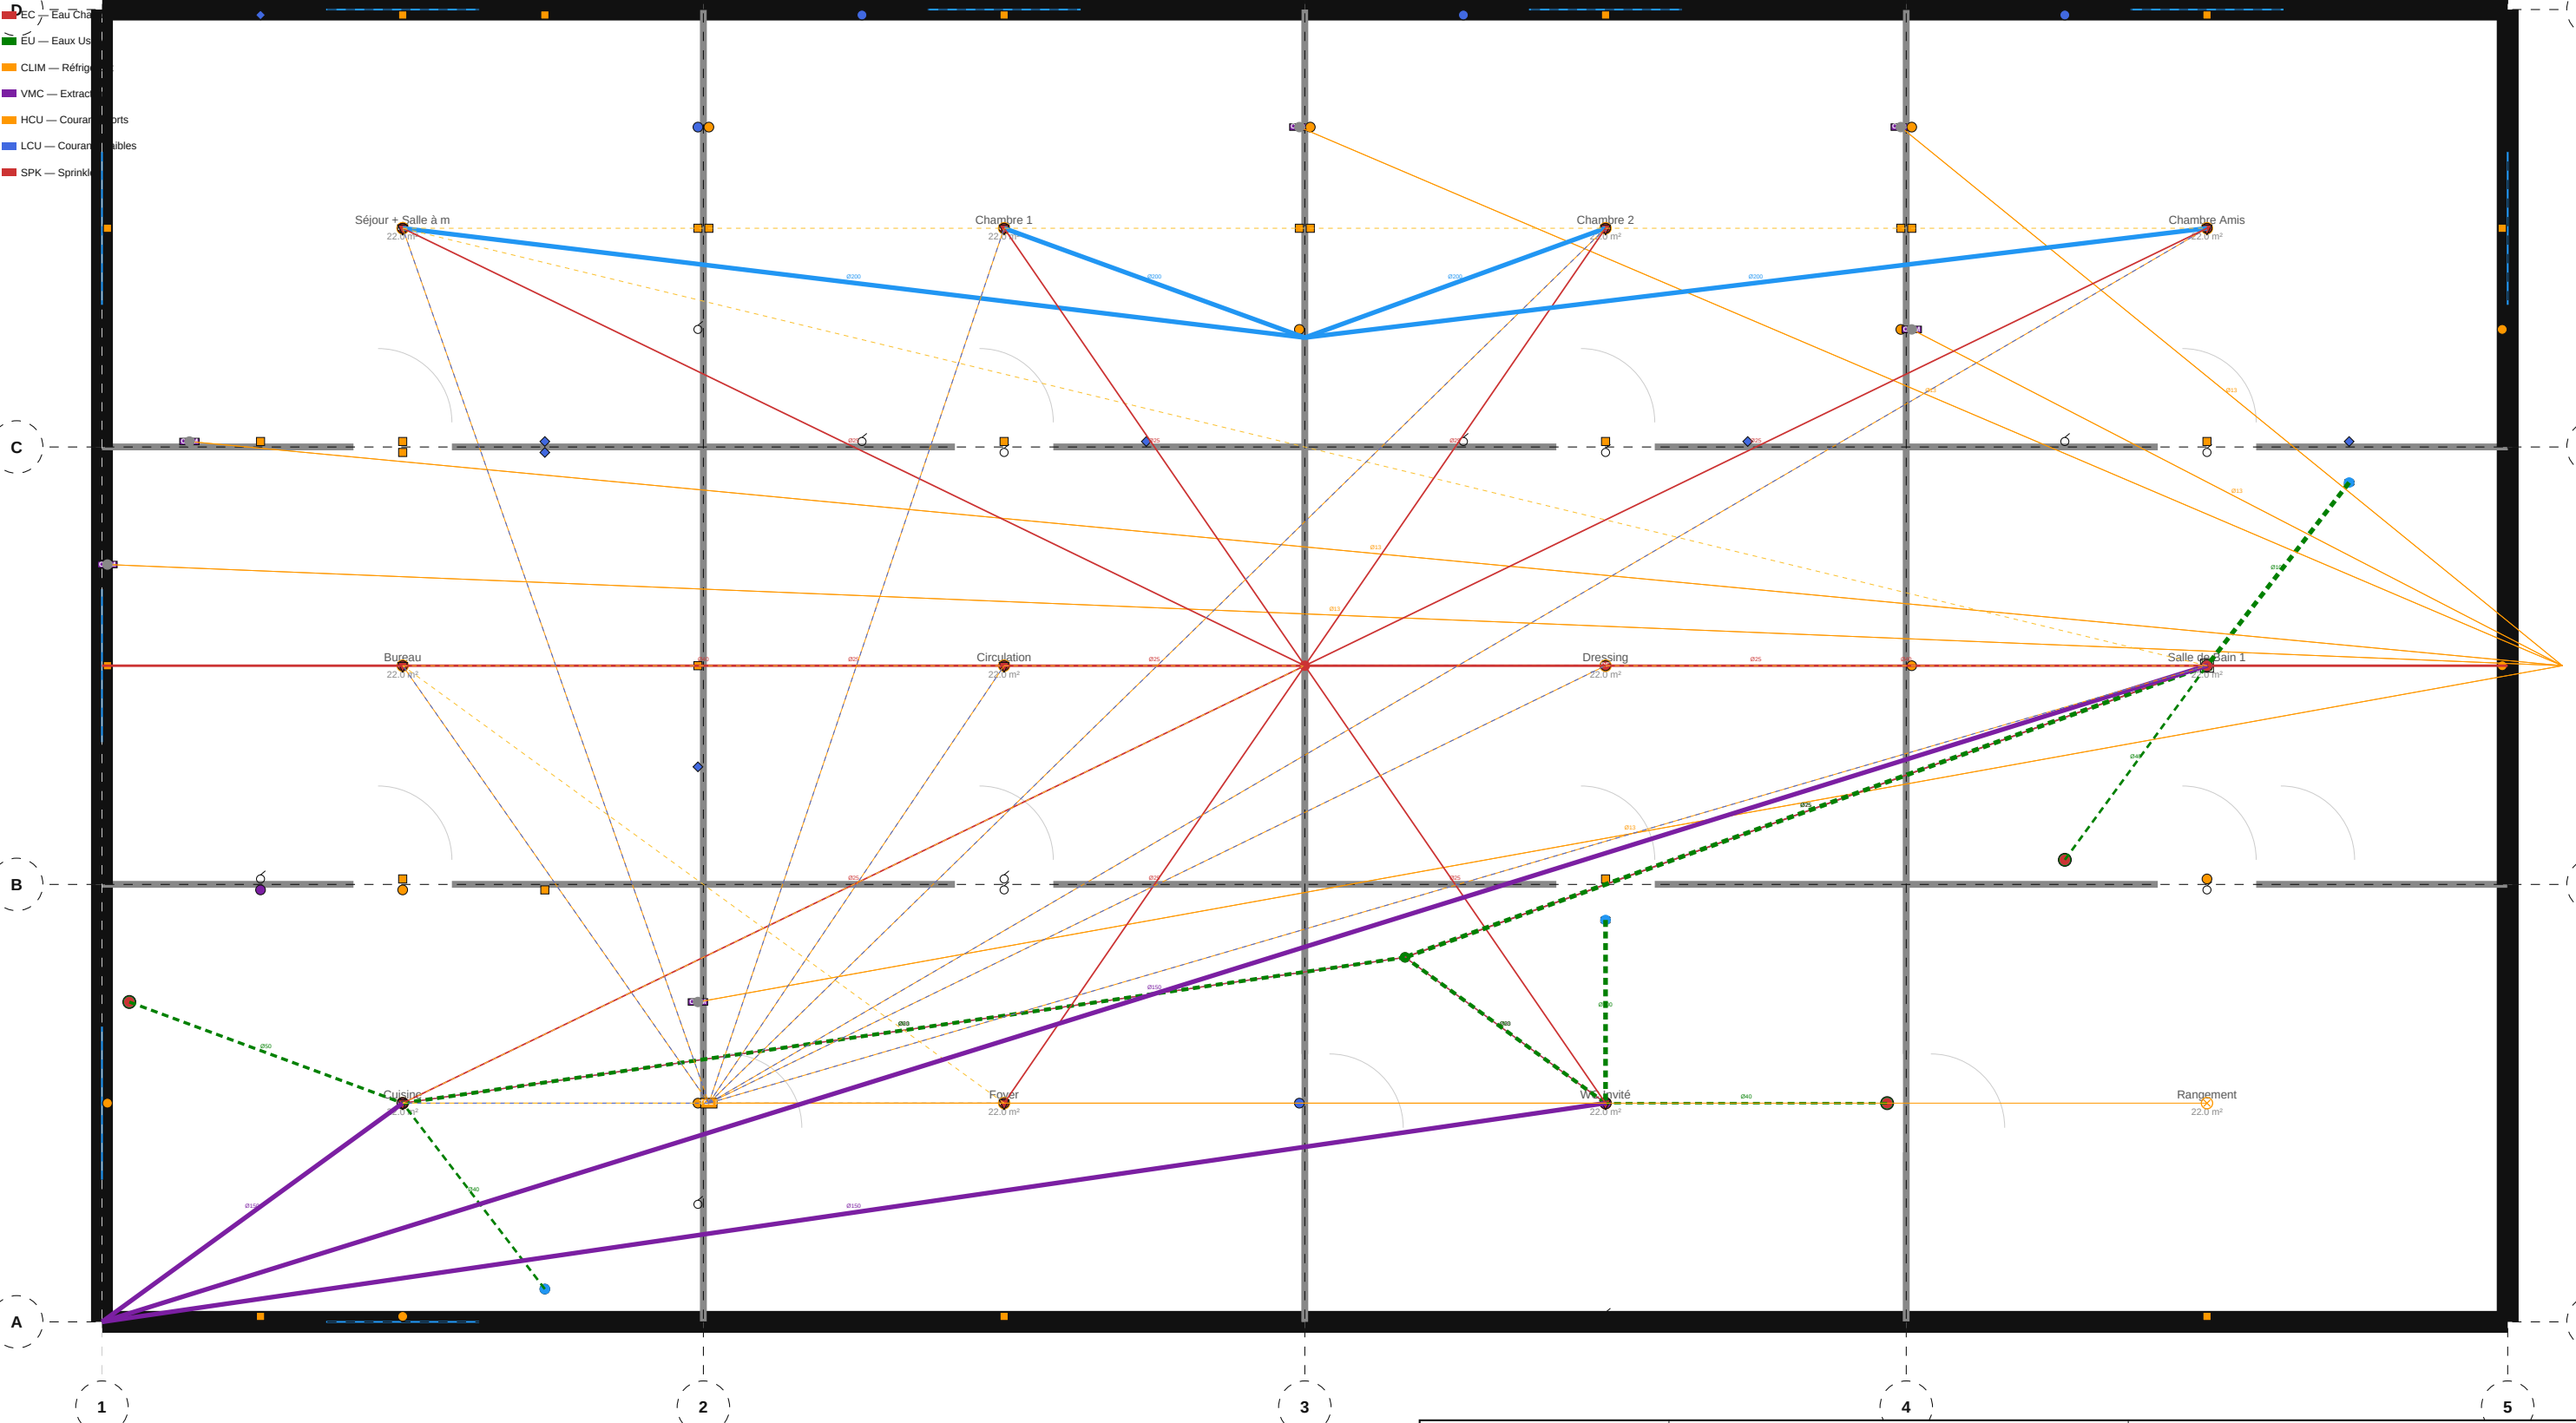


|                                                           |                                                                 |                                               |
|-----------------------------------------------------------|-----------------------------------------------------------------|-----------------------------------------------|
| <div>TIJAN AI</div> <div>Bureau d'Études Automatisé</div> | <div>Résidence Papa Oumar Sakho</div> <div>Dakar, Senegal</div> | <div>Éch: 1/100</div> <div>Pl. 31/32</div>    |
|                                                           | <div>Synthèse / Coordination — Étage 2</div>                    |                                               |
| <div>Date: 06/05/2026</div>                               | <div>Réf: SYN</div>                                             | <div>BIM vSYN-031</div> <div>Phase: APD</div> |

001 Synthèse / Coordination — Étage 3

LÉGENDE RÉSEAUX

- EF — Eau Froide
- EC — Eau Chaude
- EU — Eaux Usées
- CLIM — Réfrigération
- VMC — Extraction
- HCU — Courant Hauts
- LCU — Courant Bas
- SPK — Sprinkler

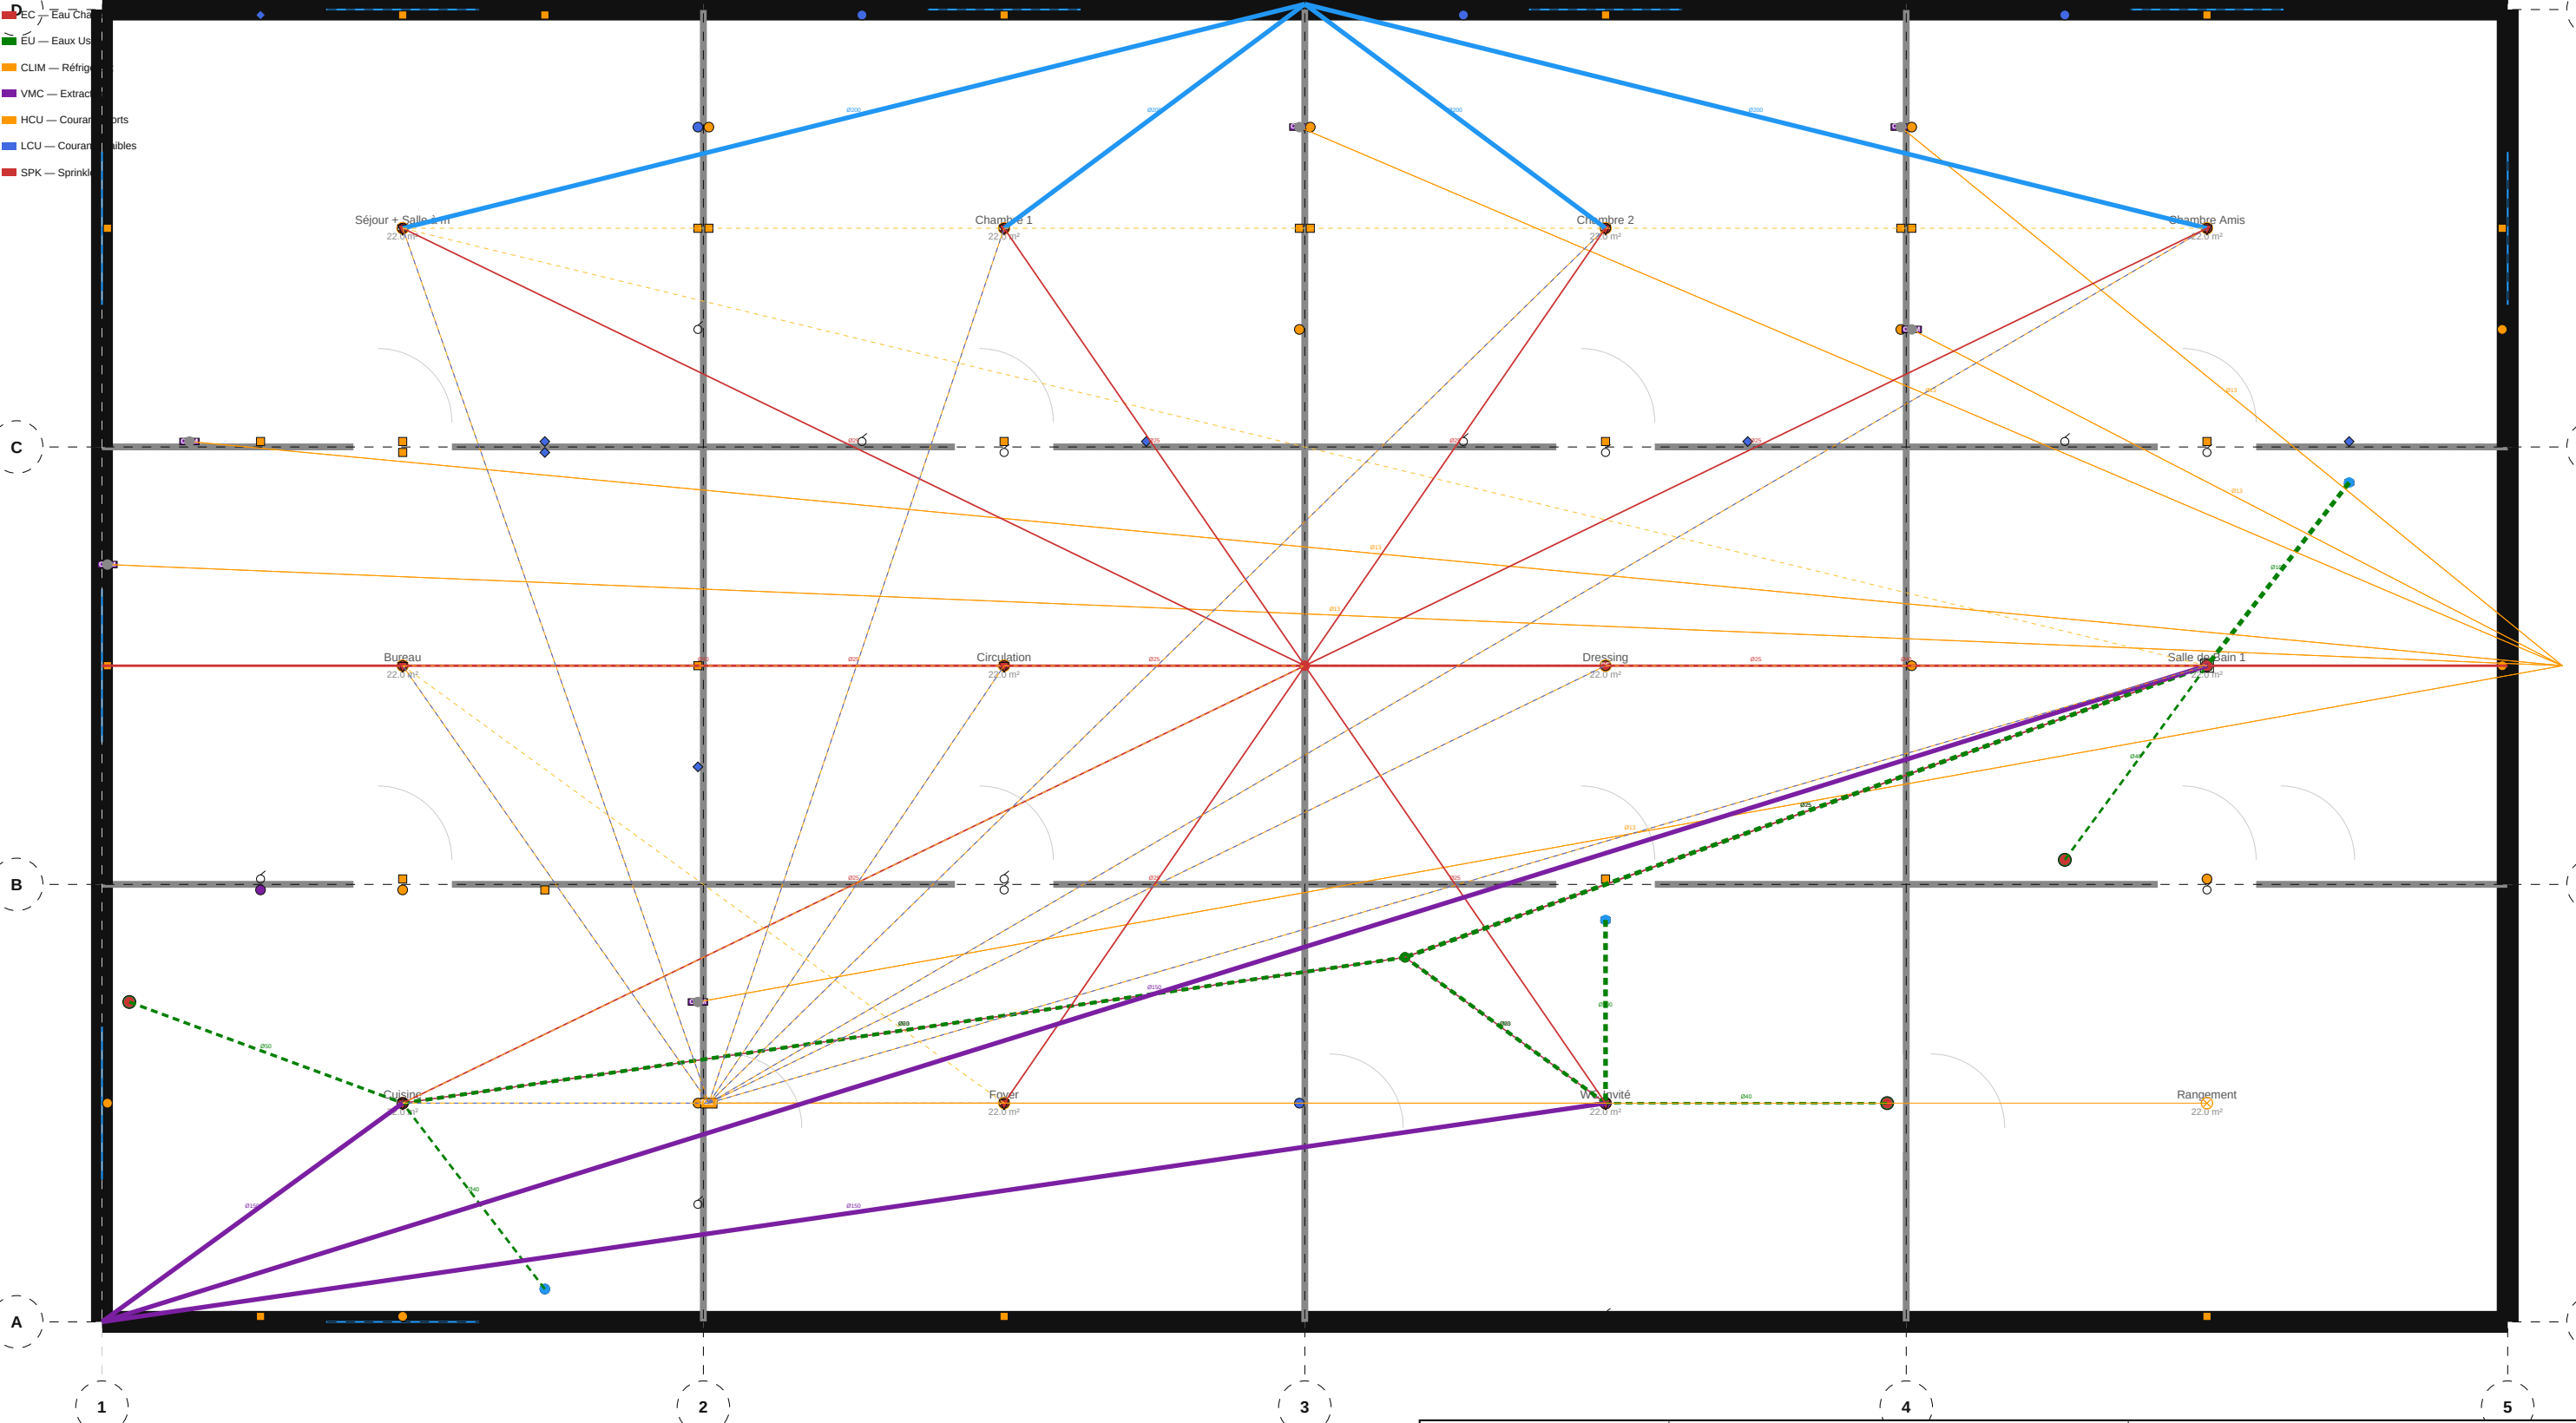

|                                               |                                                     |                            |
|-----------------------------------------------|-----------------------------------------------------|----------------------------|
| <b>TIJAN AI</b><br>Bureau d'Études Automatisé | <b>Résidence Papa Oumar Sakho</b><br>Dakar, Senegal | Éch: 1/100<br>Pl. 32/32    |
|                                               | <b>Synthèse / Coordination — Étage 3</b>            |                            |
| Date: 06/05/2026                              | Réf: SYN                                            | BIM vSYN-032<br>Phase: APD |