


PLAN DE COFFRAGE — RDC

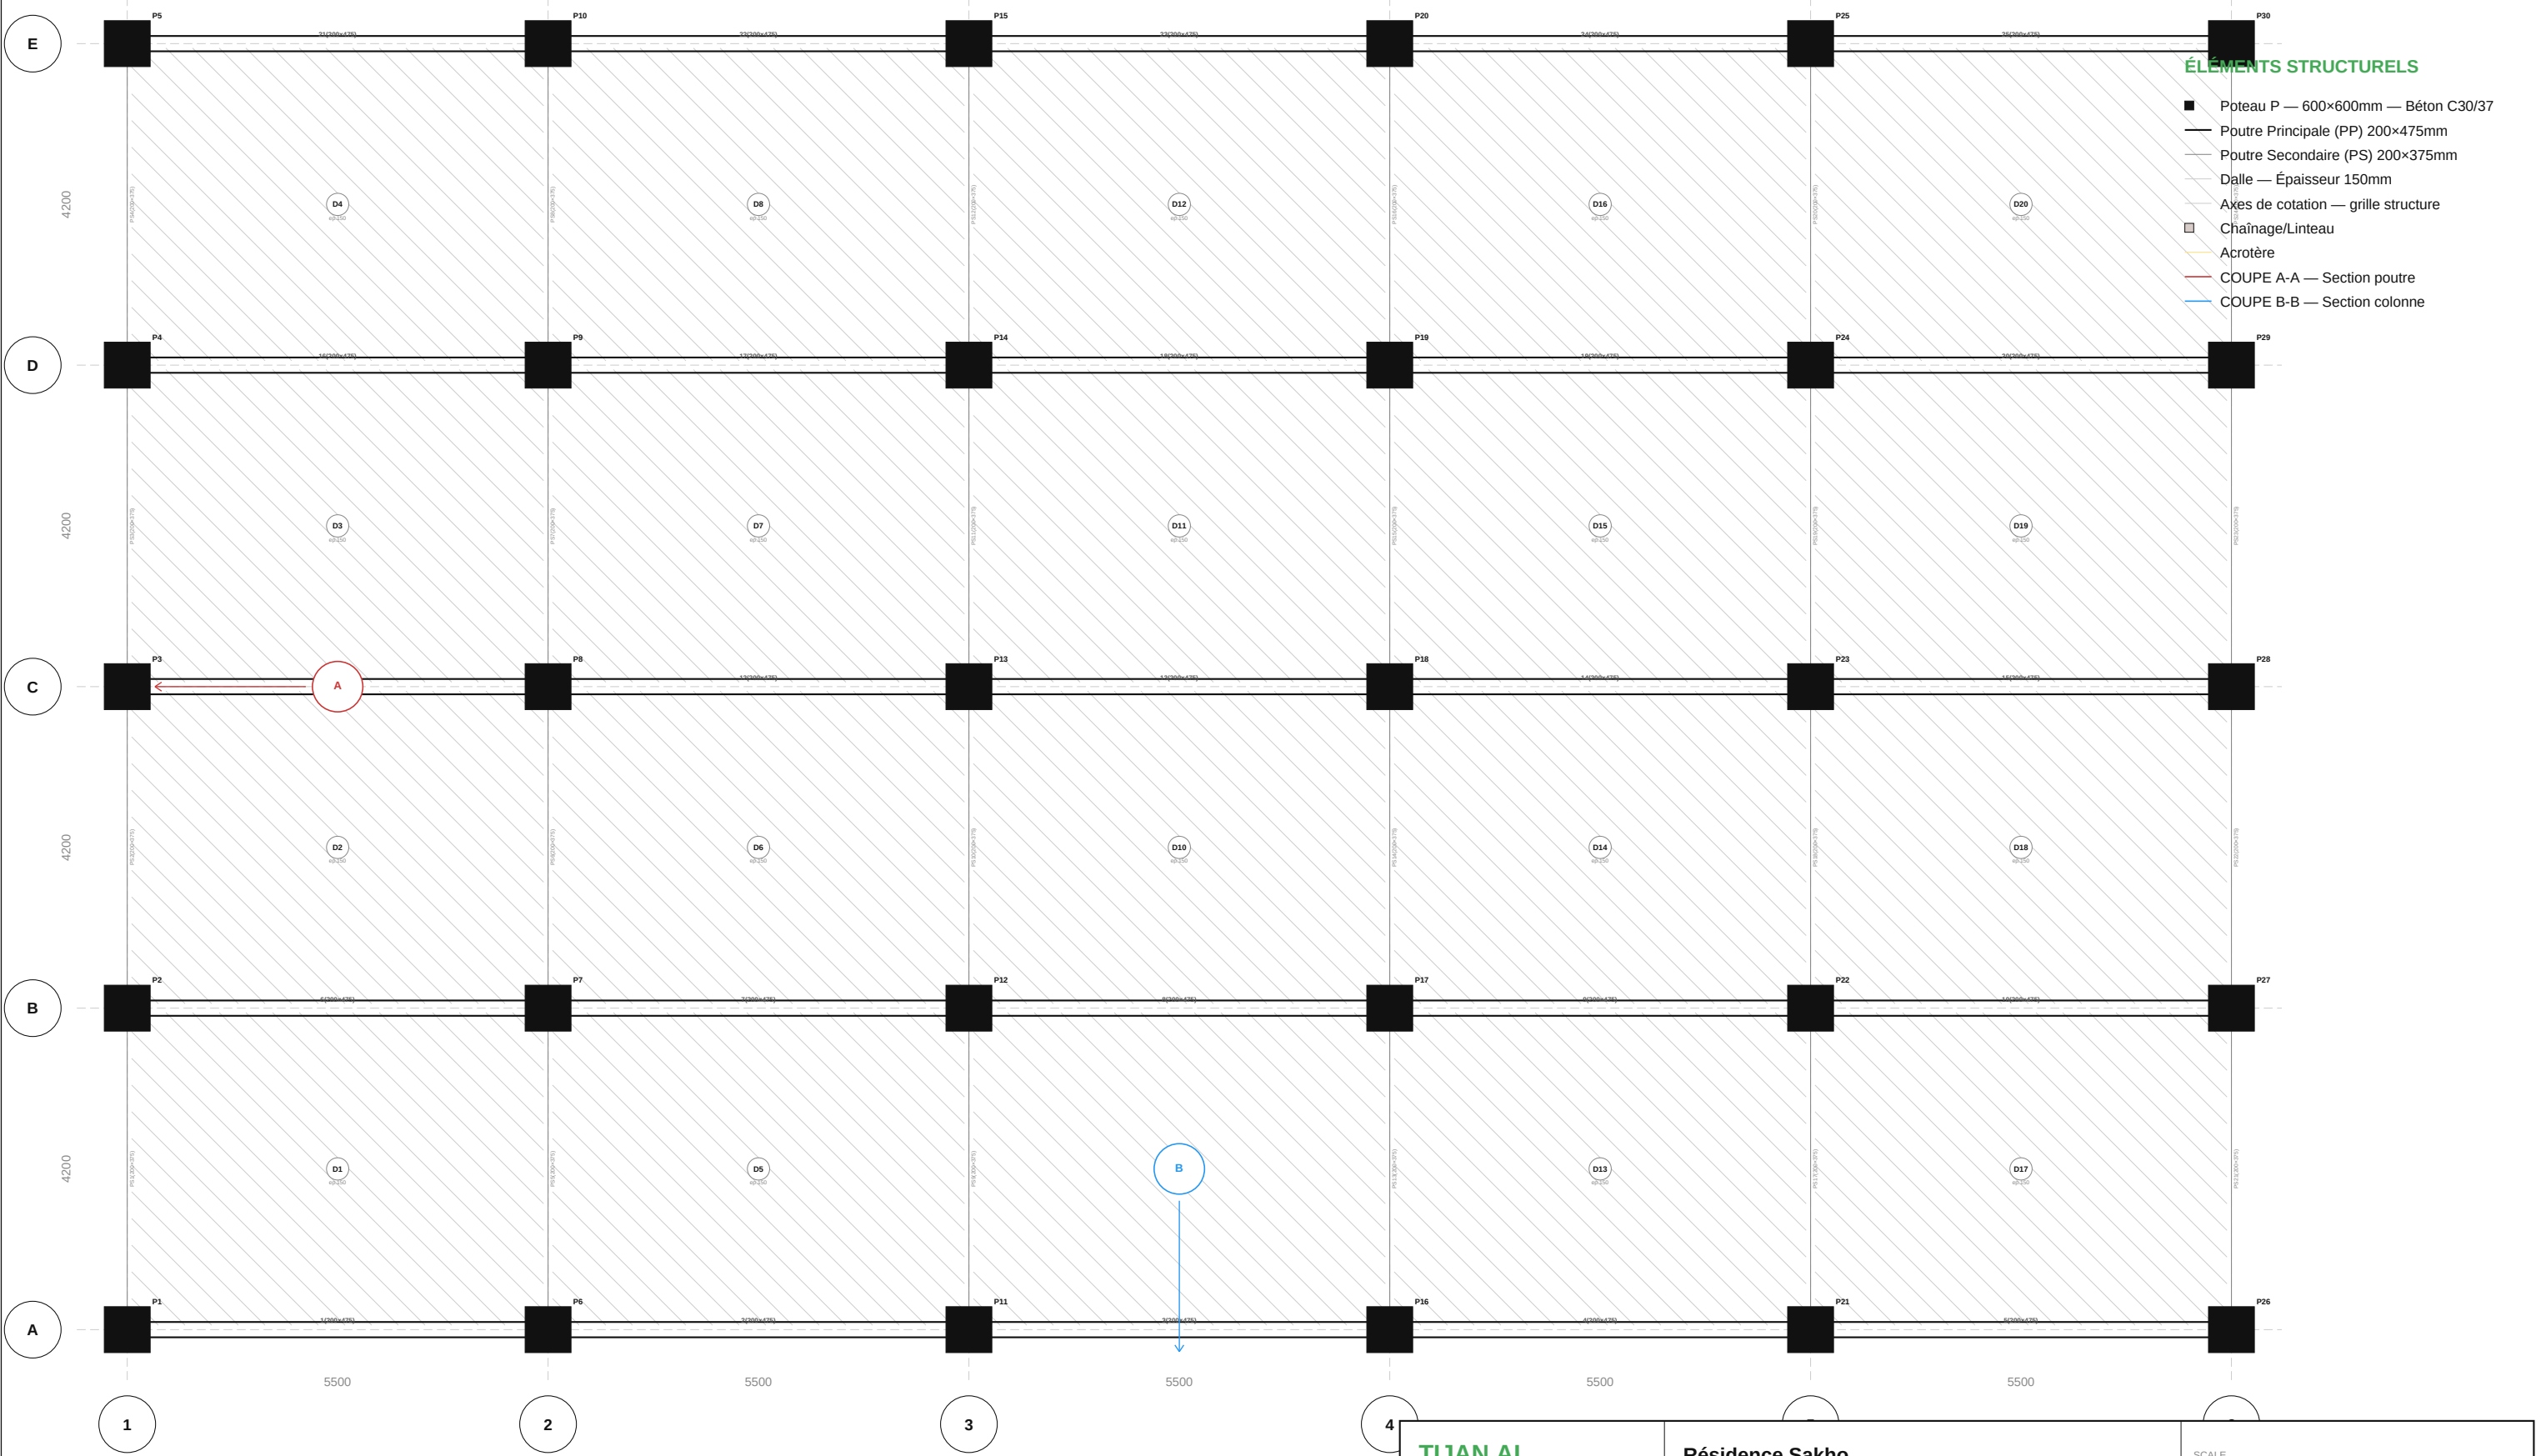

NOTES TECHNIQUES

Béton: C30/37 (fck=30 MPa)
Acier: HA500 (fyk=500 MPa)
Enrobage: 30mm (fond: 50mm)
EC2 + EC8 — NF EN 1992/1998
G=6.5 kN/m², Q=2.5 kN/m²
Zone sismique: 1

Rep.	Section	Niveau	NEd	NRd	Ratio	Armatures
P1-P30	600×600	RDC	2604	7397	35%	4HA12
—	600×600	N1	2315	7397	31%	4HA12

TIJAN AI

Automated Engineering Bureau

Résidence Sakho

Dakar, Senegal

SCALE

1/100

support@tijan.ai

COFFRAGE — RDC

STRUCTURE BÉTON ARMÉ

PHASE: APP

TJN-RÉSIDE

www.tijan.ai

DESIGNED

TIJAN AI

DRAWN

TIJAN AI

CHECKED

TIJAN AI


DRAWING No

PL-001

SHEET

1 / 17

PLAN DE COFFRAGE — R+1

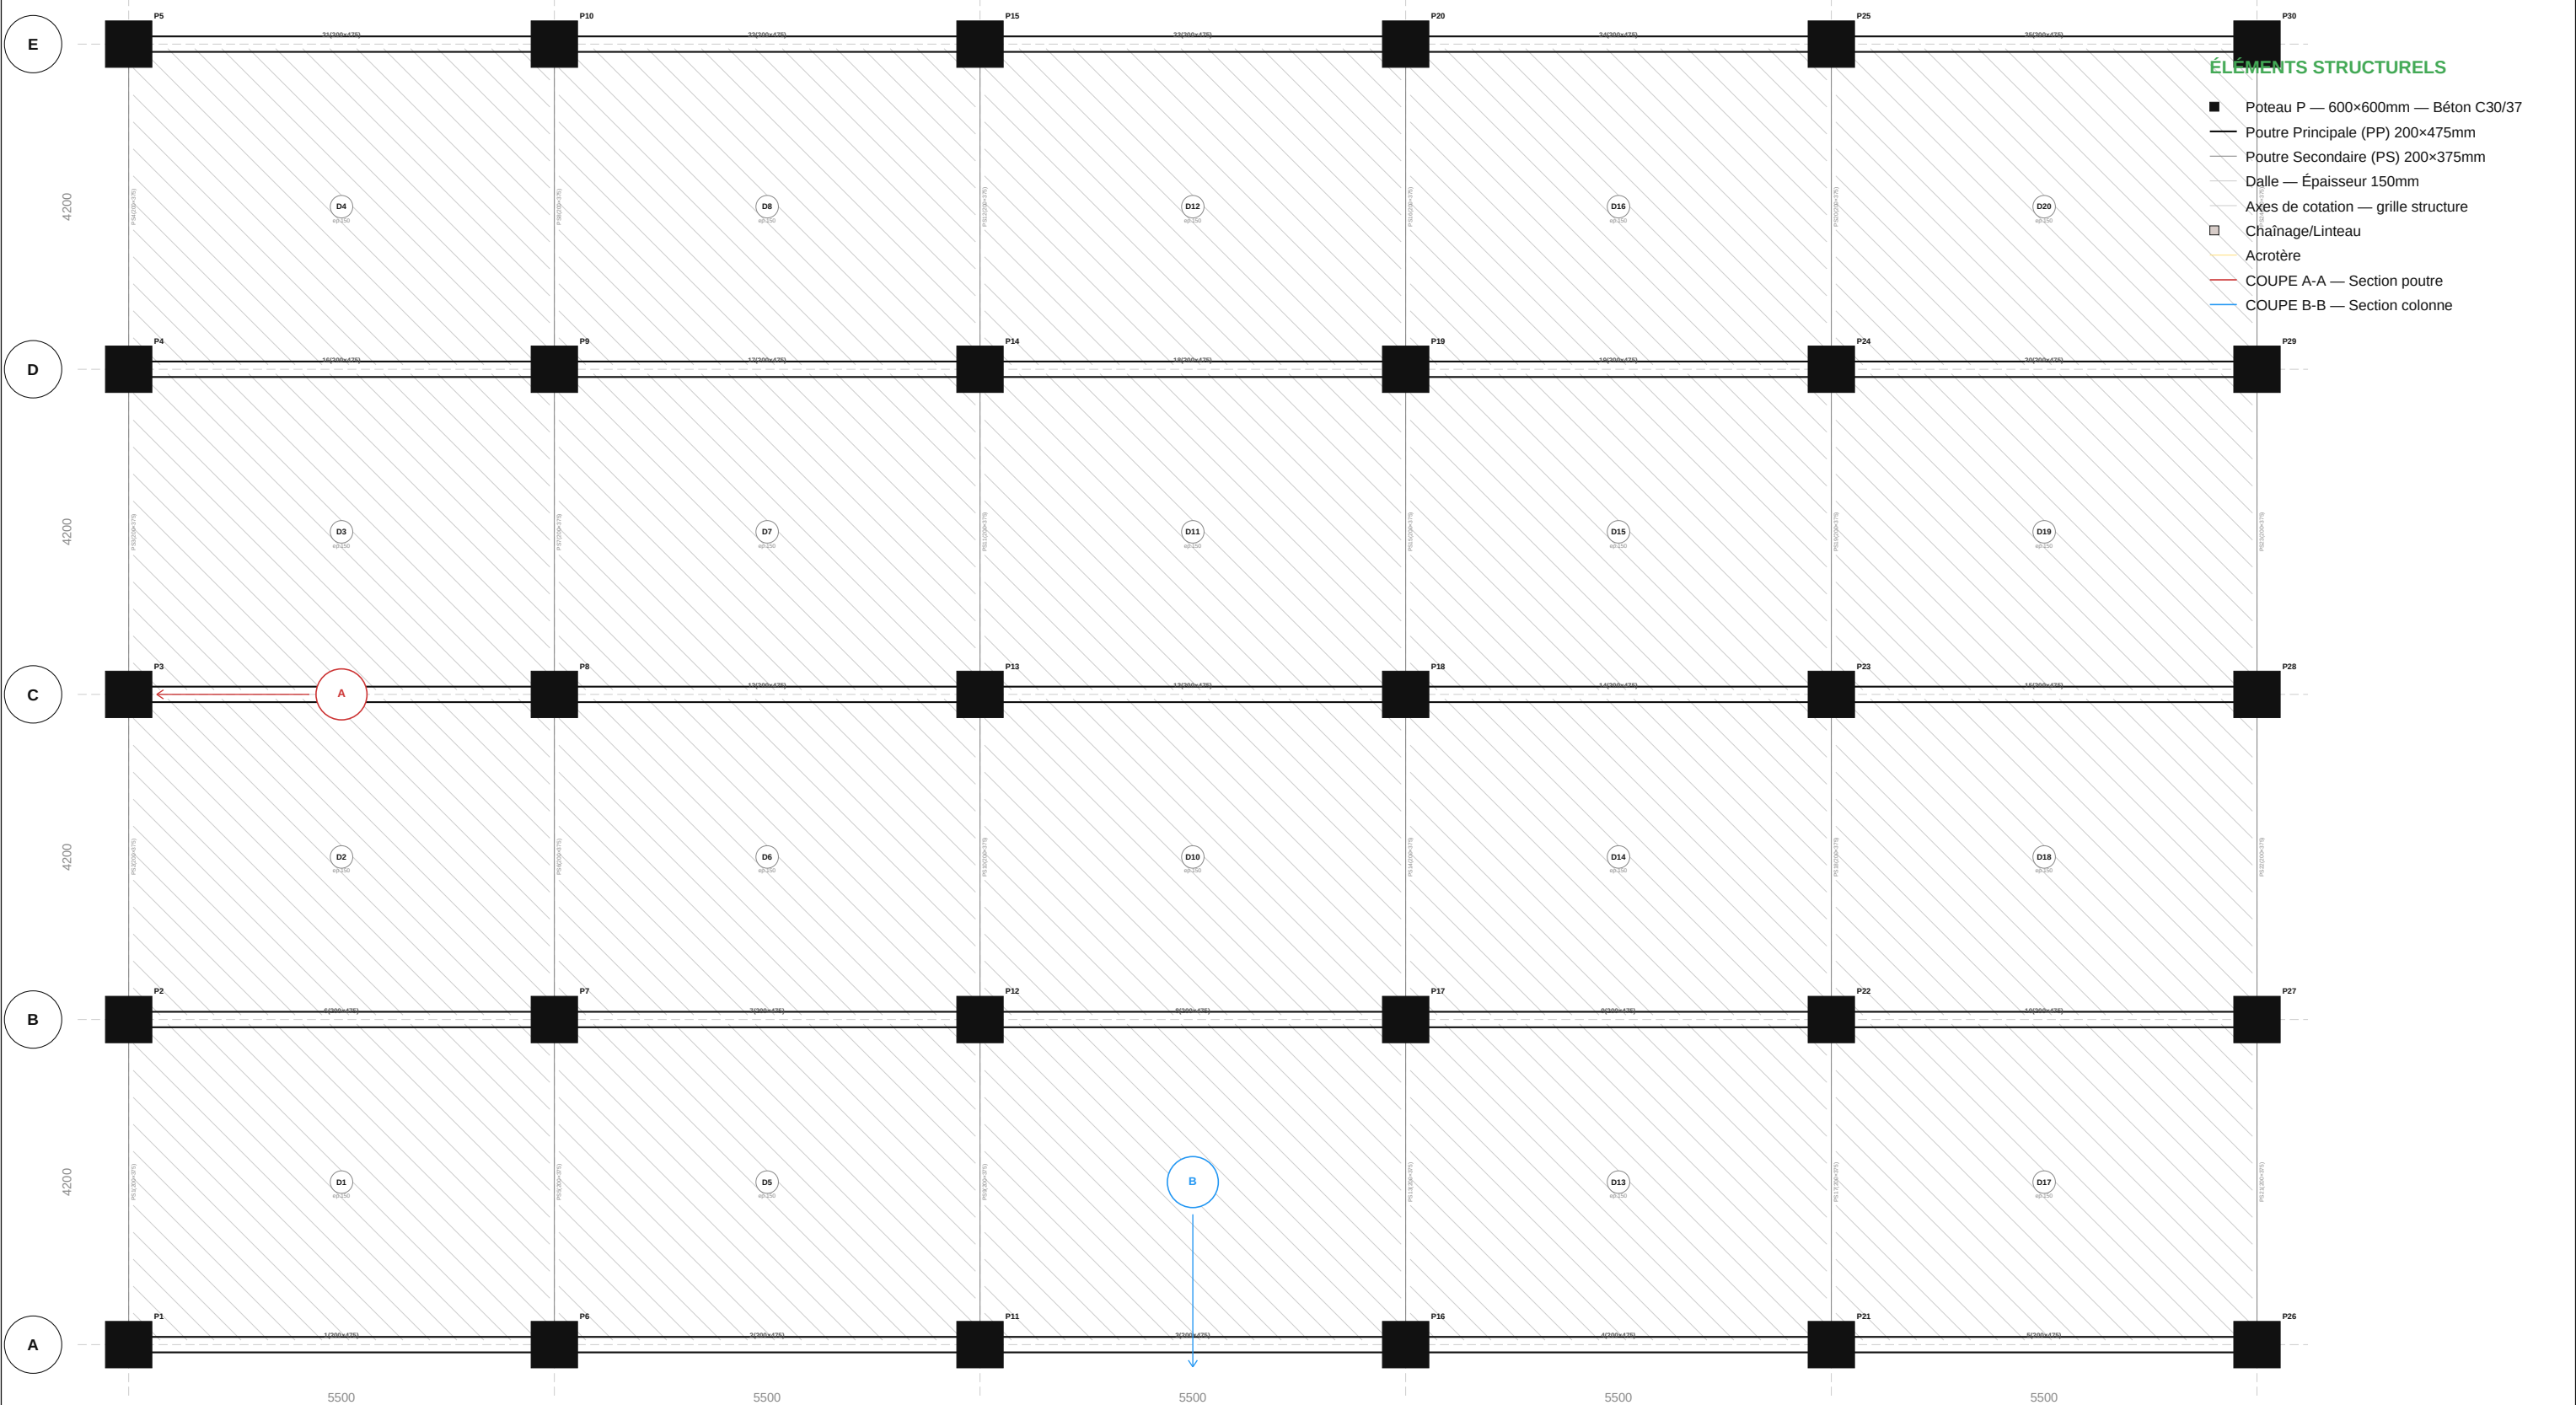


NOTES TECHNIQUES

Béton: C30/37 (fck=30 MPa)
Acier: HA500 (fyk=500 MPa)
Enrobage: 30mm (fond: 50mm)
EC2 + EC8 — NF EN 1992/1998
G=6.5 kN/m², Q=2.5 kN/m²
Zone sismique: 1

Rep.	Section	Niveau	NEd	NRd	Ratio	Armatures
P1-P30	600×600	N1	2315	7397	31%	4HA12
—	600×600	RDC	2604	7397	35%	4HA12
—	600×600	N2	2025	7397	27%	4HA12

TIJAN AI Automated Engineering Bureau support@tijan.ai www.tijan.ai 06/05/2026	Résidence Sakho Dakar, Senegal			SCALE 1/100	
	COFFRAGE — R+1 STRUCTURE BÉTON ARMÉ			PHASE: APP TJN-RÉSIDE	
DESIGNED TIJAN AI		DRAWN TIJAN AI	CHECKED TIJAN AI	DRAWING No PL-002	SHEET 2 / 17

PLAN DE COFFRAGE — R+2

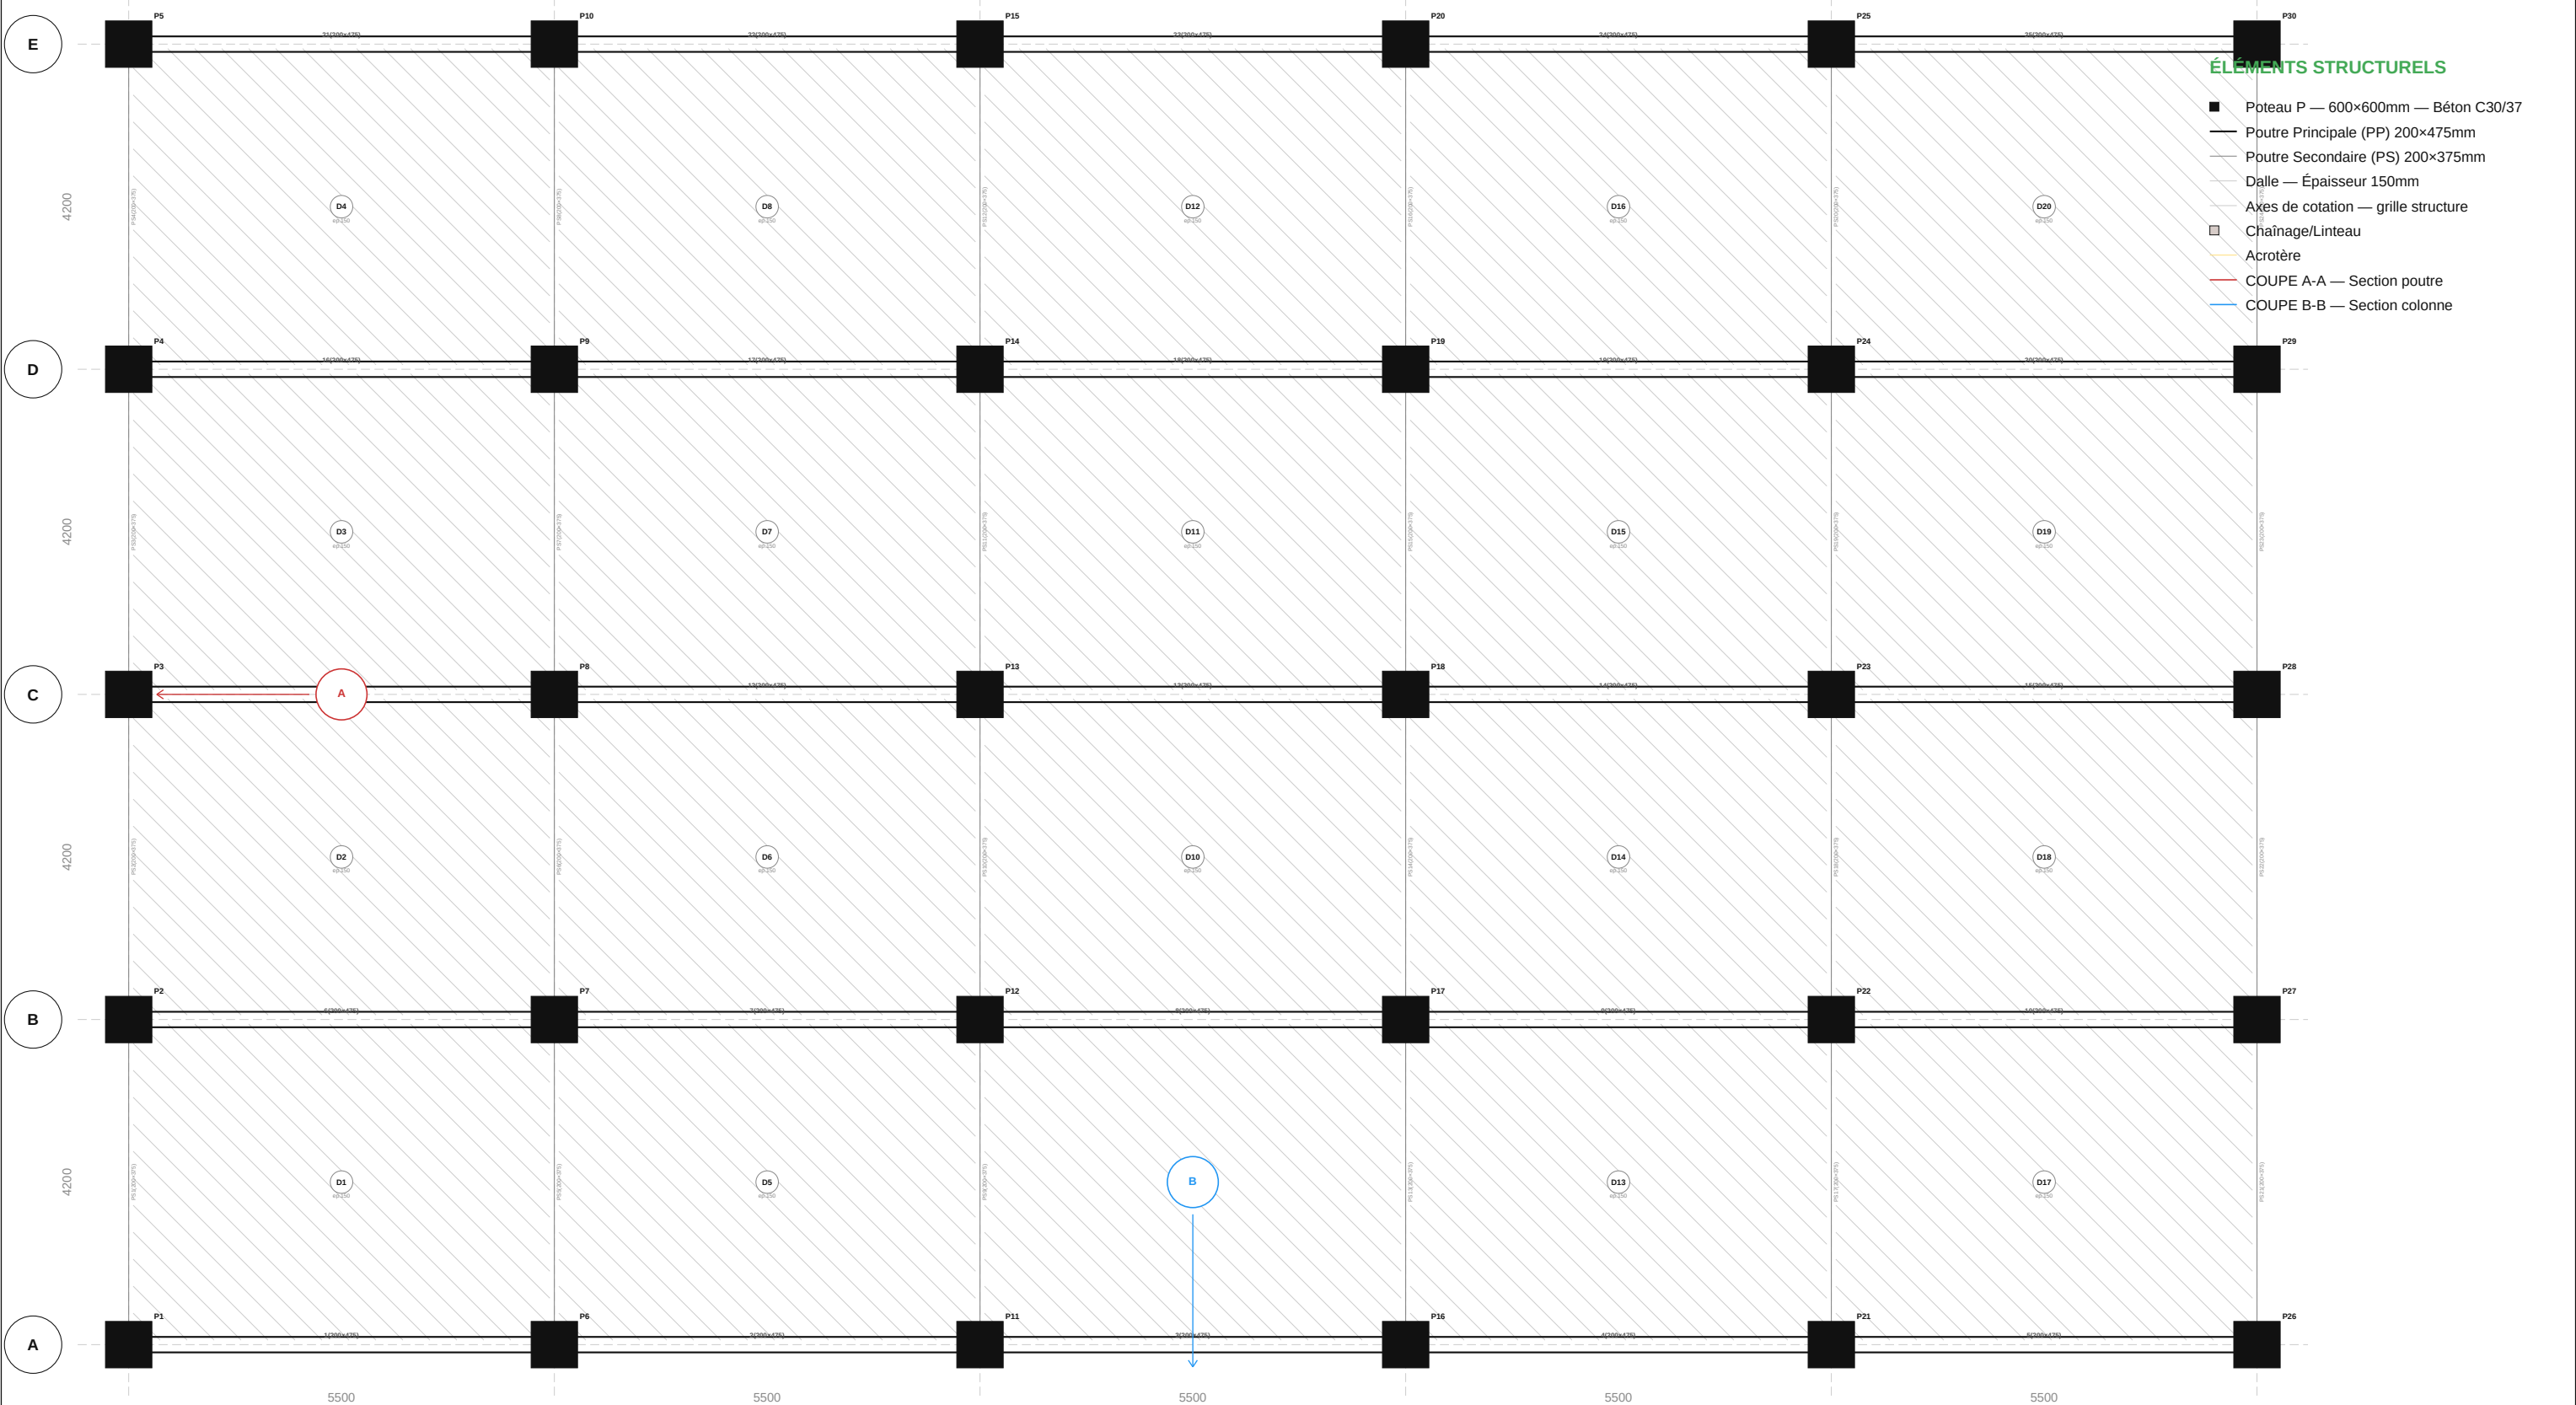


NOTES TECHNIQUES

Béton: C30/37 (fck=30 MPa)
Acier: HA500 (fyk=500 MPa)
Enrobage: 30mm (fond: 50mm)
EC2 + EC8 — NF EN 1992/1998
G=6.5 kN/m², Q=2.5 kN/m²
Zone sismique: 1

Rep.	Section	Niveau	NEd	NRd	Ratio	Armatures
P1-P30	600×600	N2	2025	7397	27%	4HA12
—	600×600	N1	2315	7397	31%	4HA12
—	600×600	N3	1736	7397	23%	4HA12

TIJAN AI Automated Engineering Bureau support@tijan.ai www.tijan.ai 06/05/2026	Résidence Sakho Dakar, Senegal			SCALE 1/100	
	COFFRAGE — R+2 STRUCTURE BÉTON ARMÉ			PHASE: APP TJN-RÉSIDE	
DESIGNED TIJAN AI		DRAWN TIJAN AI	CHECKED TIJAN AI	DRAWING No PL-003	SHEET 3 / 17

PLAN DE COFFRAGE — R+3

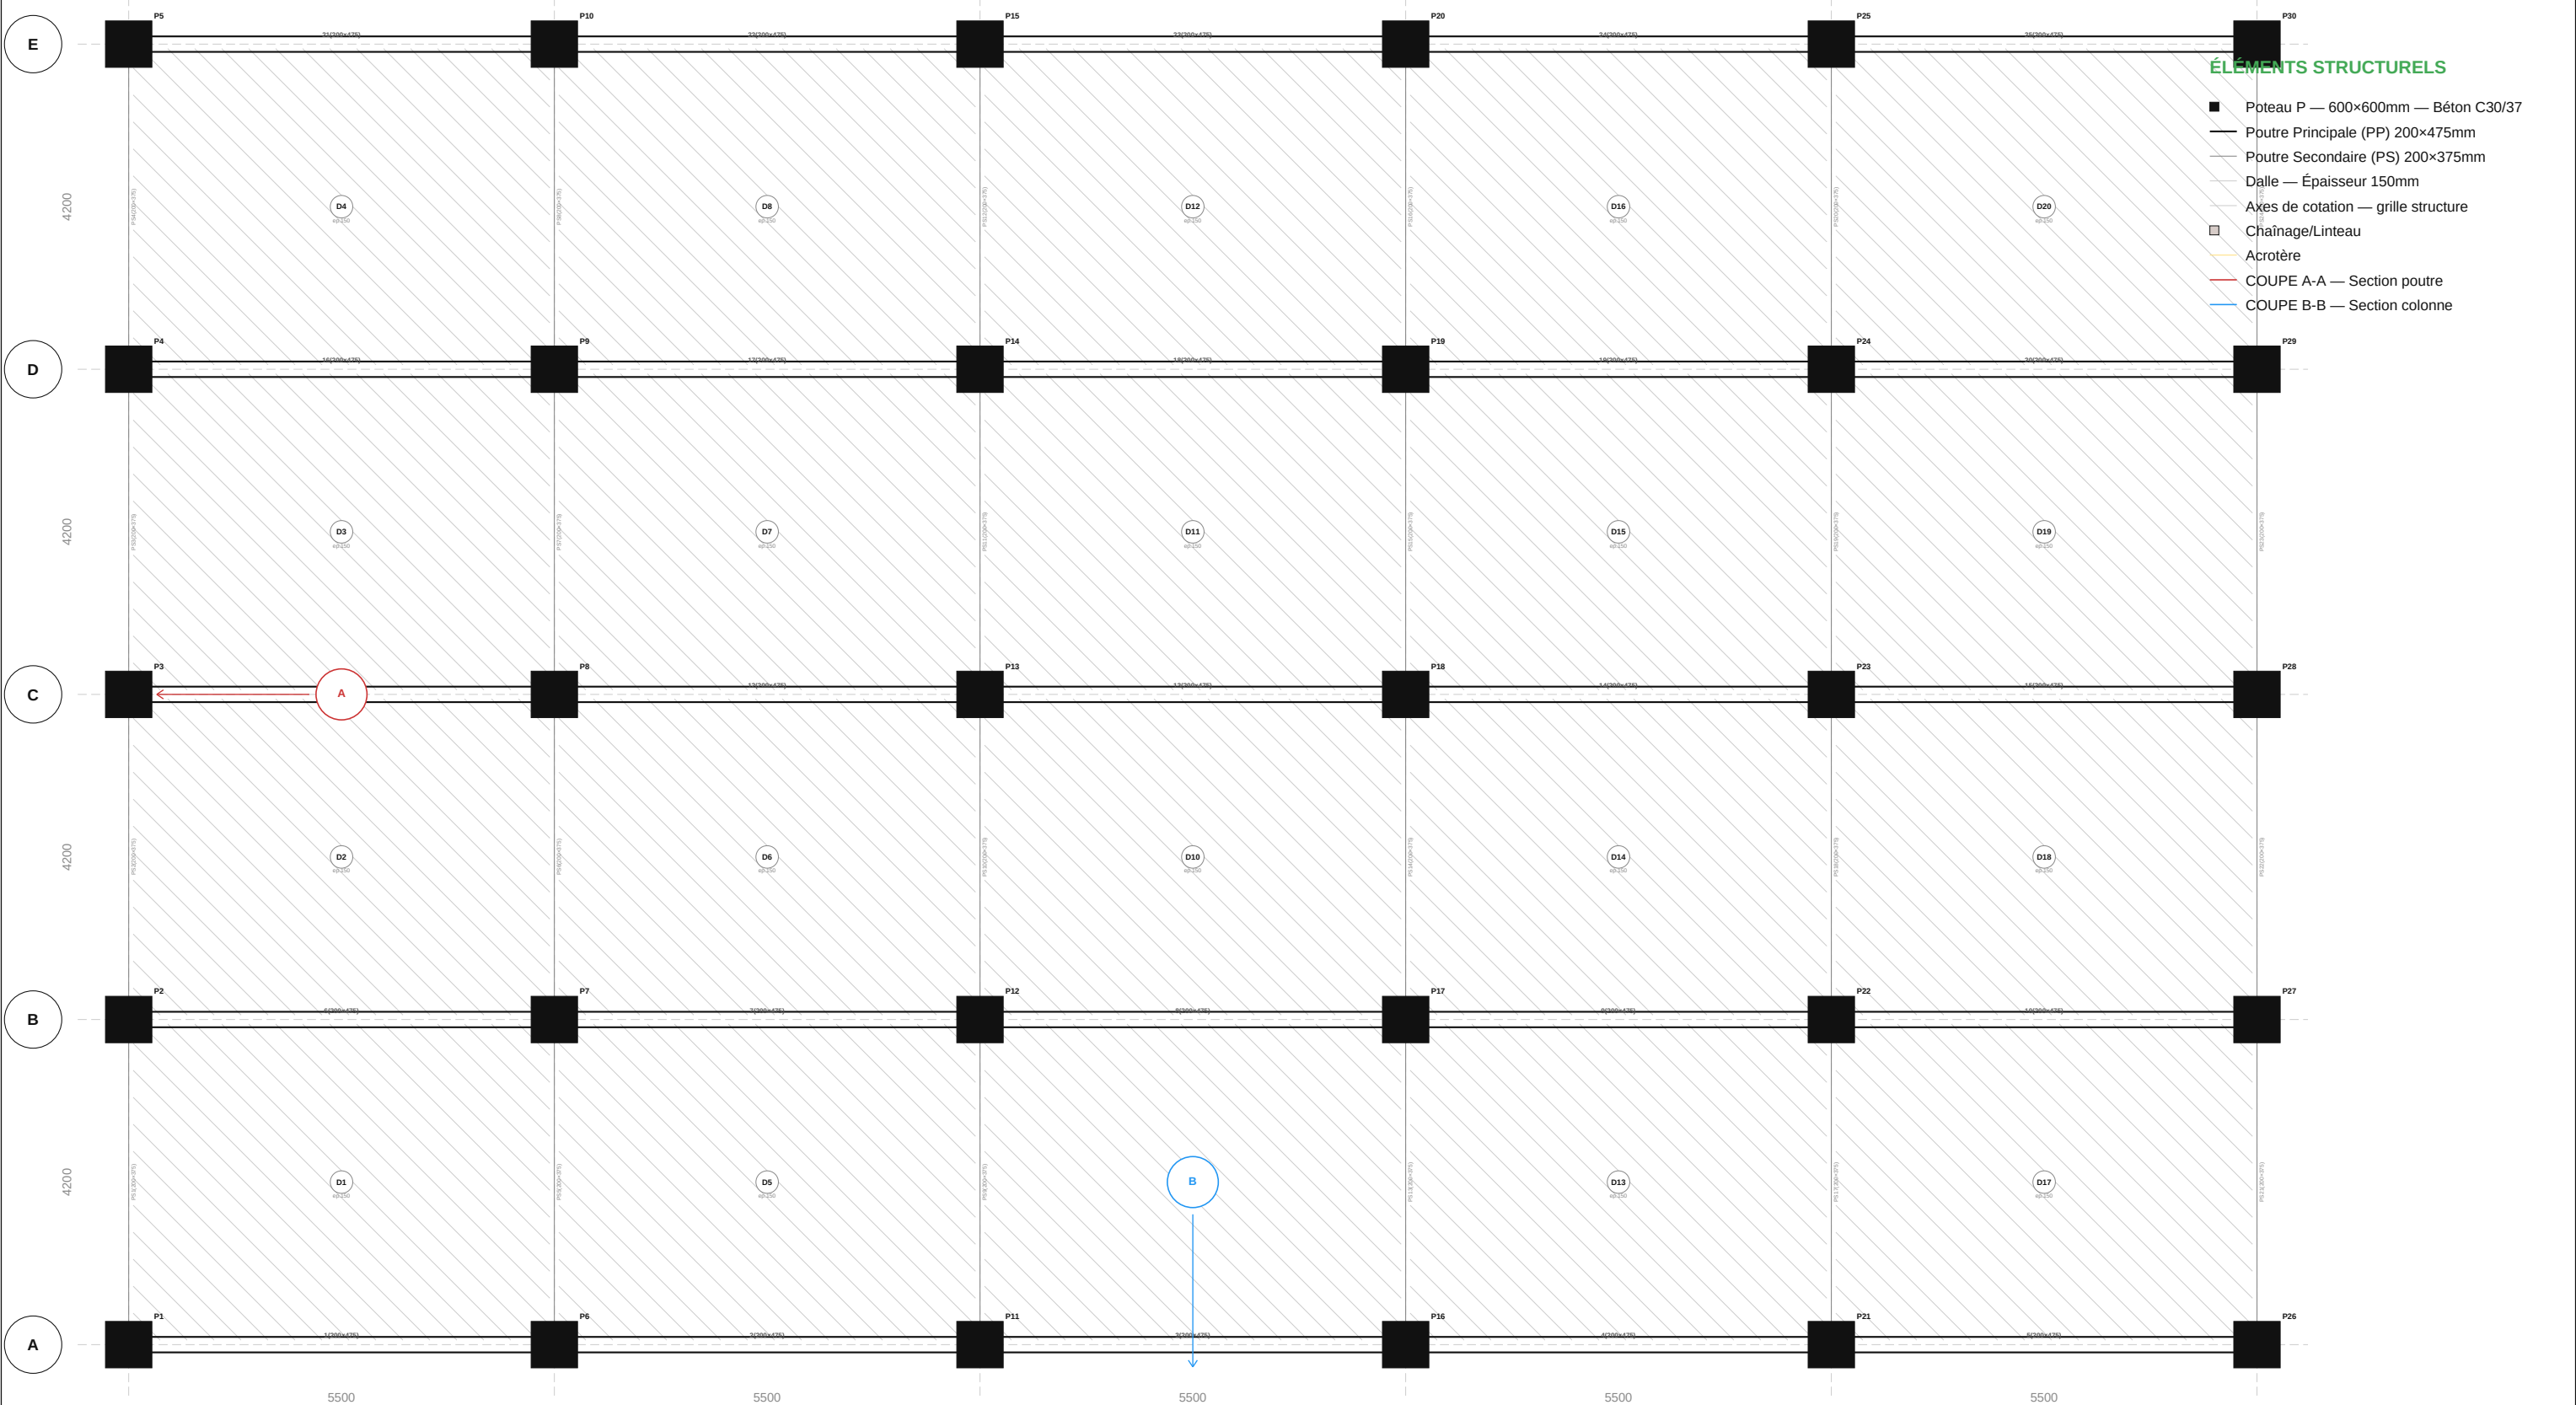


NOTES TECHNIQUES

Béton: C30/37 (fck=30 MPa)
Acier: HA500 (fyk=500 MPa)
Enrobage: 30mm (fond: 50mm)
EC2 + EC8 — NF EN 1992/1998
G=6.5 kN/m², Q=2.5 kN/m²
Zone sismique: 1

Rep.	Section	Niveau	NEd	NRd	Ratio	Armatures
P1-P30	600×600	N3	1736	7397	23%	4HA12
—	600×600	N2	2025	7397	27%	4HA12
—	600×600	N4	1447	7397	20%	4HA12

TIJAN AI Automated Engineering Bureau support@tijan.ai www.tijan.ai 06/05/2026	Résidence Sakho Dakar, Senegal			SCALE 1/100	
	COFFRAGE — R+3 STRUCTURE BÉTON ARMÉ			PHASE: APP TJN-RÉSIDE	
DESIGNED TIJAN AI		DRAWN TIJAN AI	CHECKED TIJAN AI	DRAWING No PL-004	SHEET 4 / 17

PLAN DE COFFRAGE — R+4

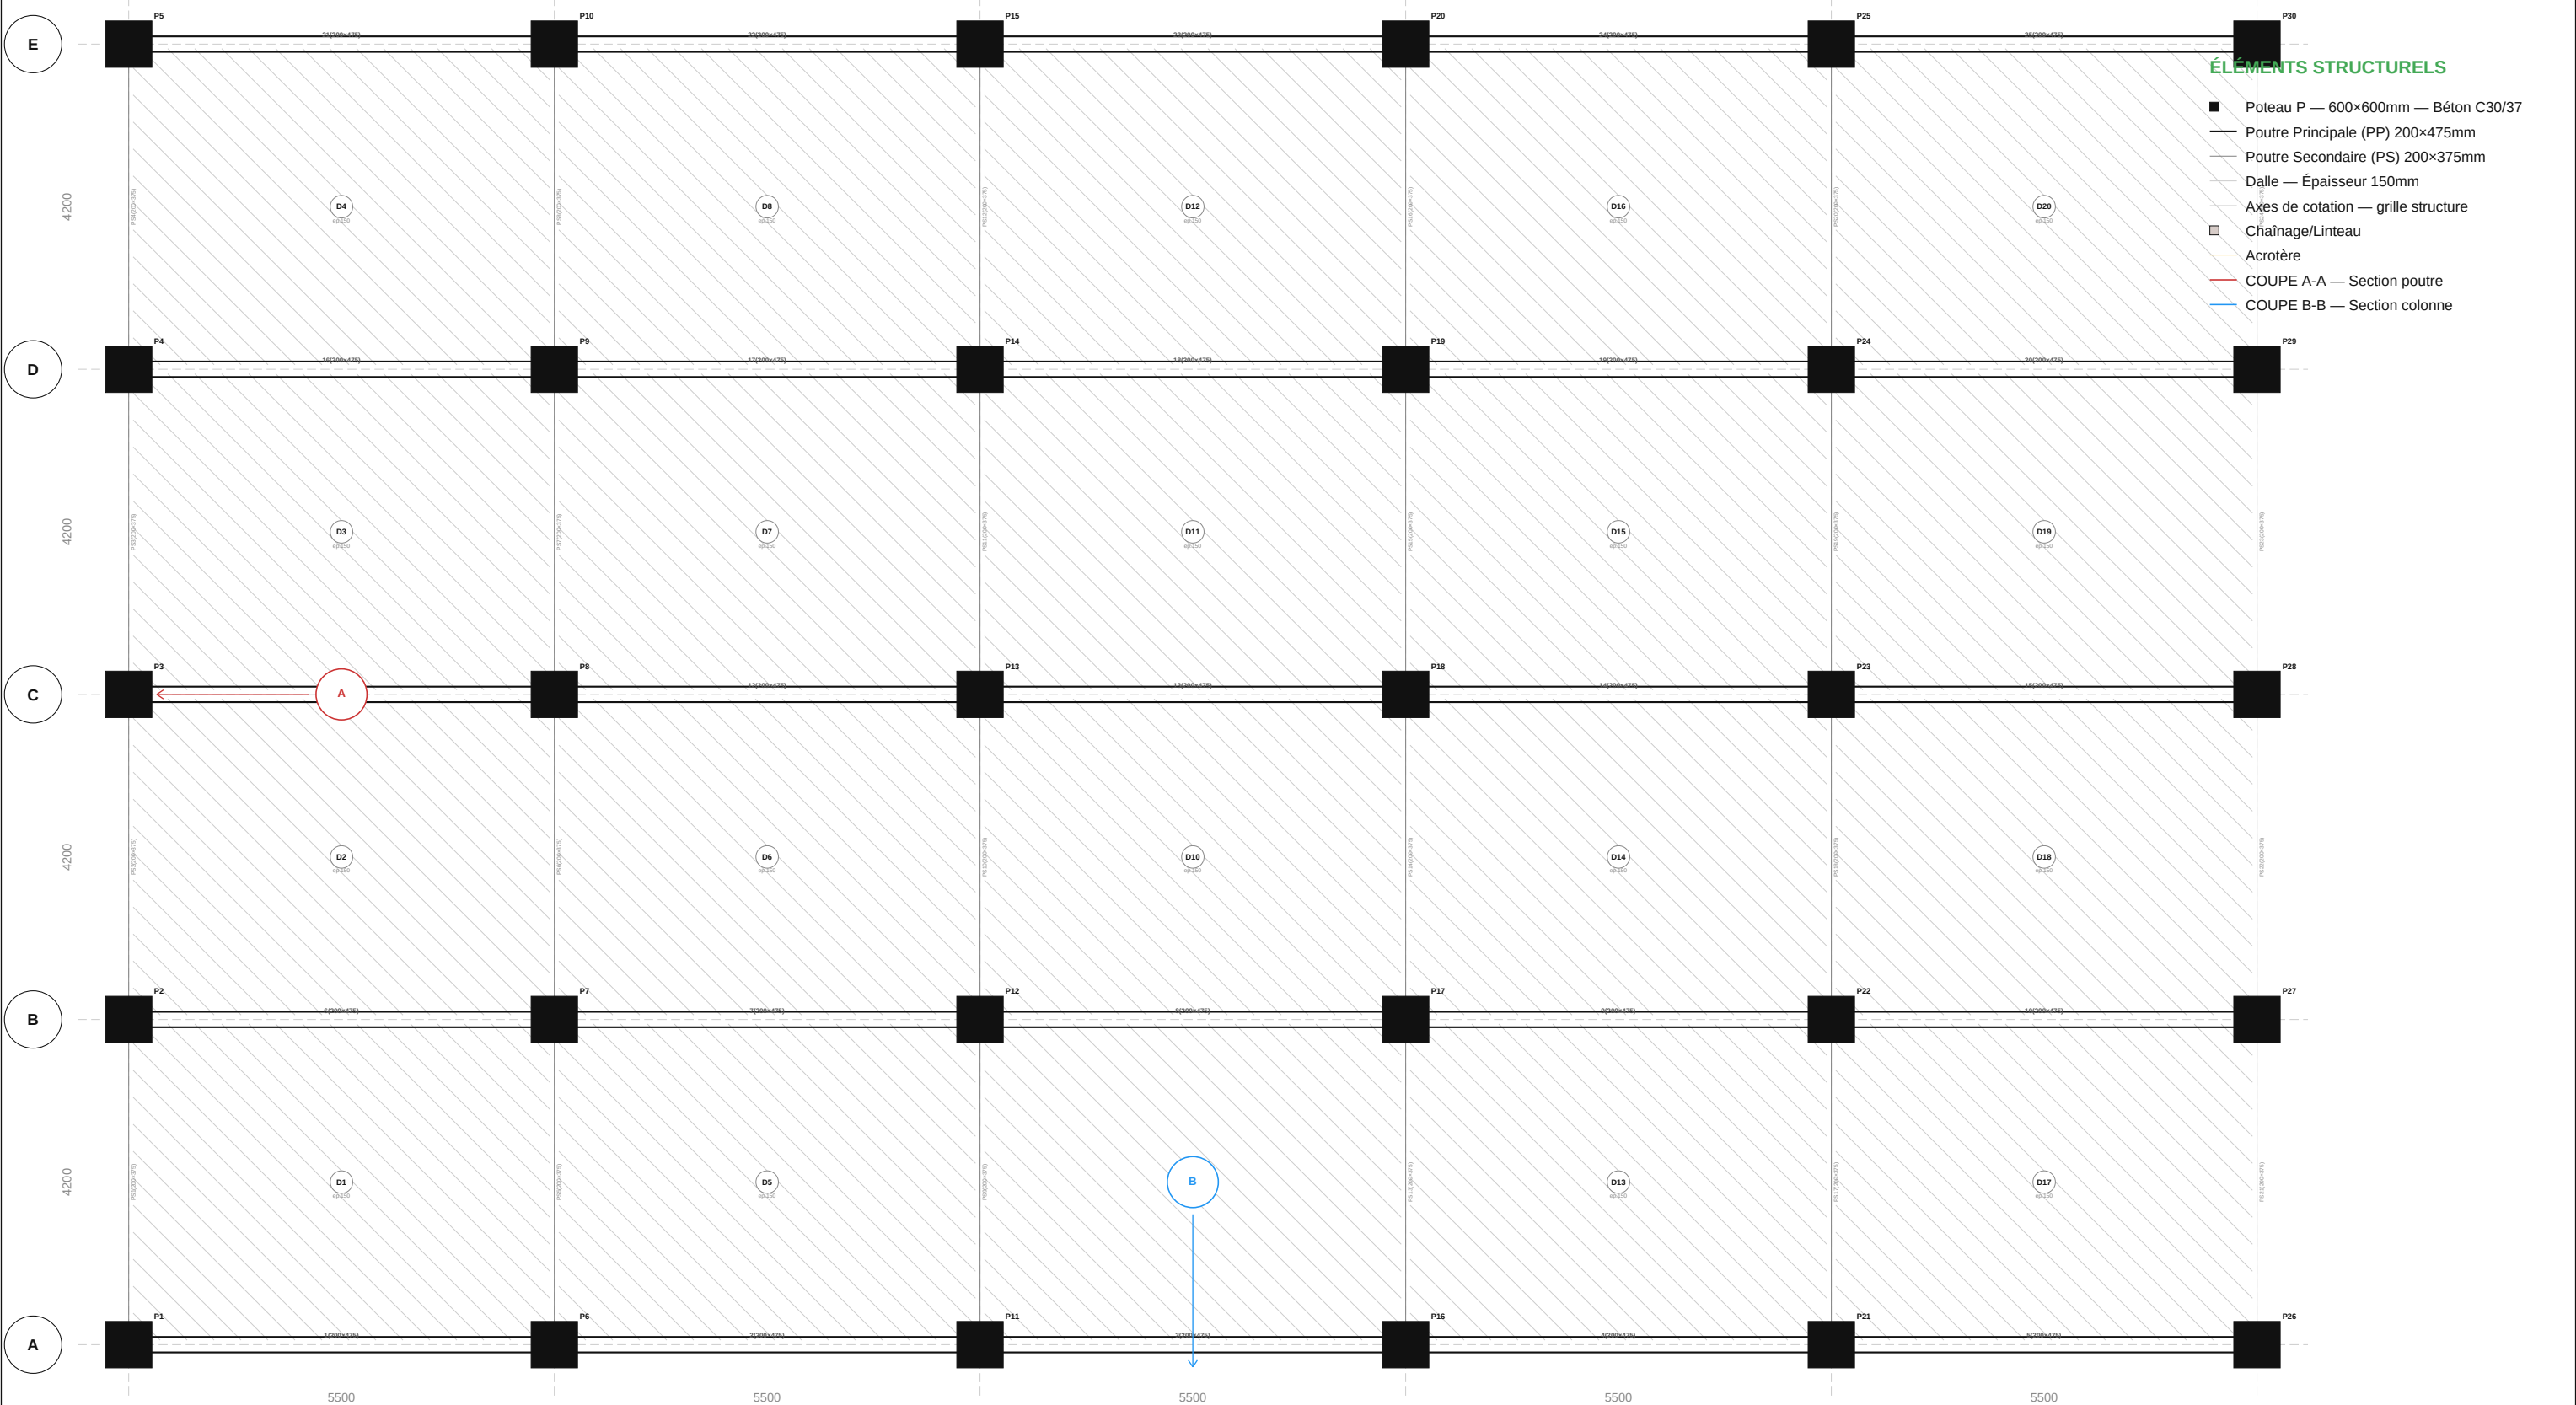


NOTES TECHNIQUES

Béton: C30/37 (fck=30 MPa)
Acier: HA500 (fyk=500 MPa)
Enrobage: 30mm (fond: 50mm)
EC2 + EC8 — NF EN 1992/1998
G=6.5 kN/m², Q=2.5 kN/m²
Zone sismique: 1

Rep.	Section	Niveau	NEd	NRd	Ratio	Armatures
P1-P30	600×600	N4	1447	7397	20%	4HA12
—	600×600	N3	1736	7397	23%	4HA12
—	600×600	N5	1157	7397	16%	4HA12

TIJAN AI Automated Engineering Bureau support@tijan.ai www.tijan.ai 06/05/2026	Résidence Sakho Dakar, Senegal			SCALE 1/100	
	COFFRAGE — R+4 STRUCTURE BÉTON ARMÉ			PHASE: AFD TJN-RÉSIDE	
DESIGNED TIJAN AI		DRAWN TIJAN AI	CHECKED TIJAN AI	DRAWING No PL-005	SHEET 5 / 17

PLAN DE COFFRAGE — R+5

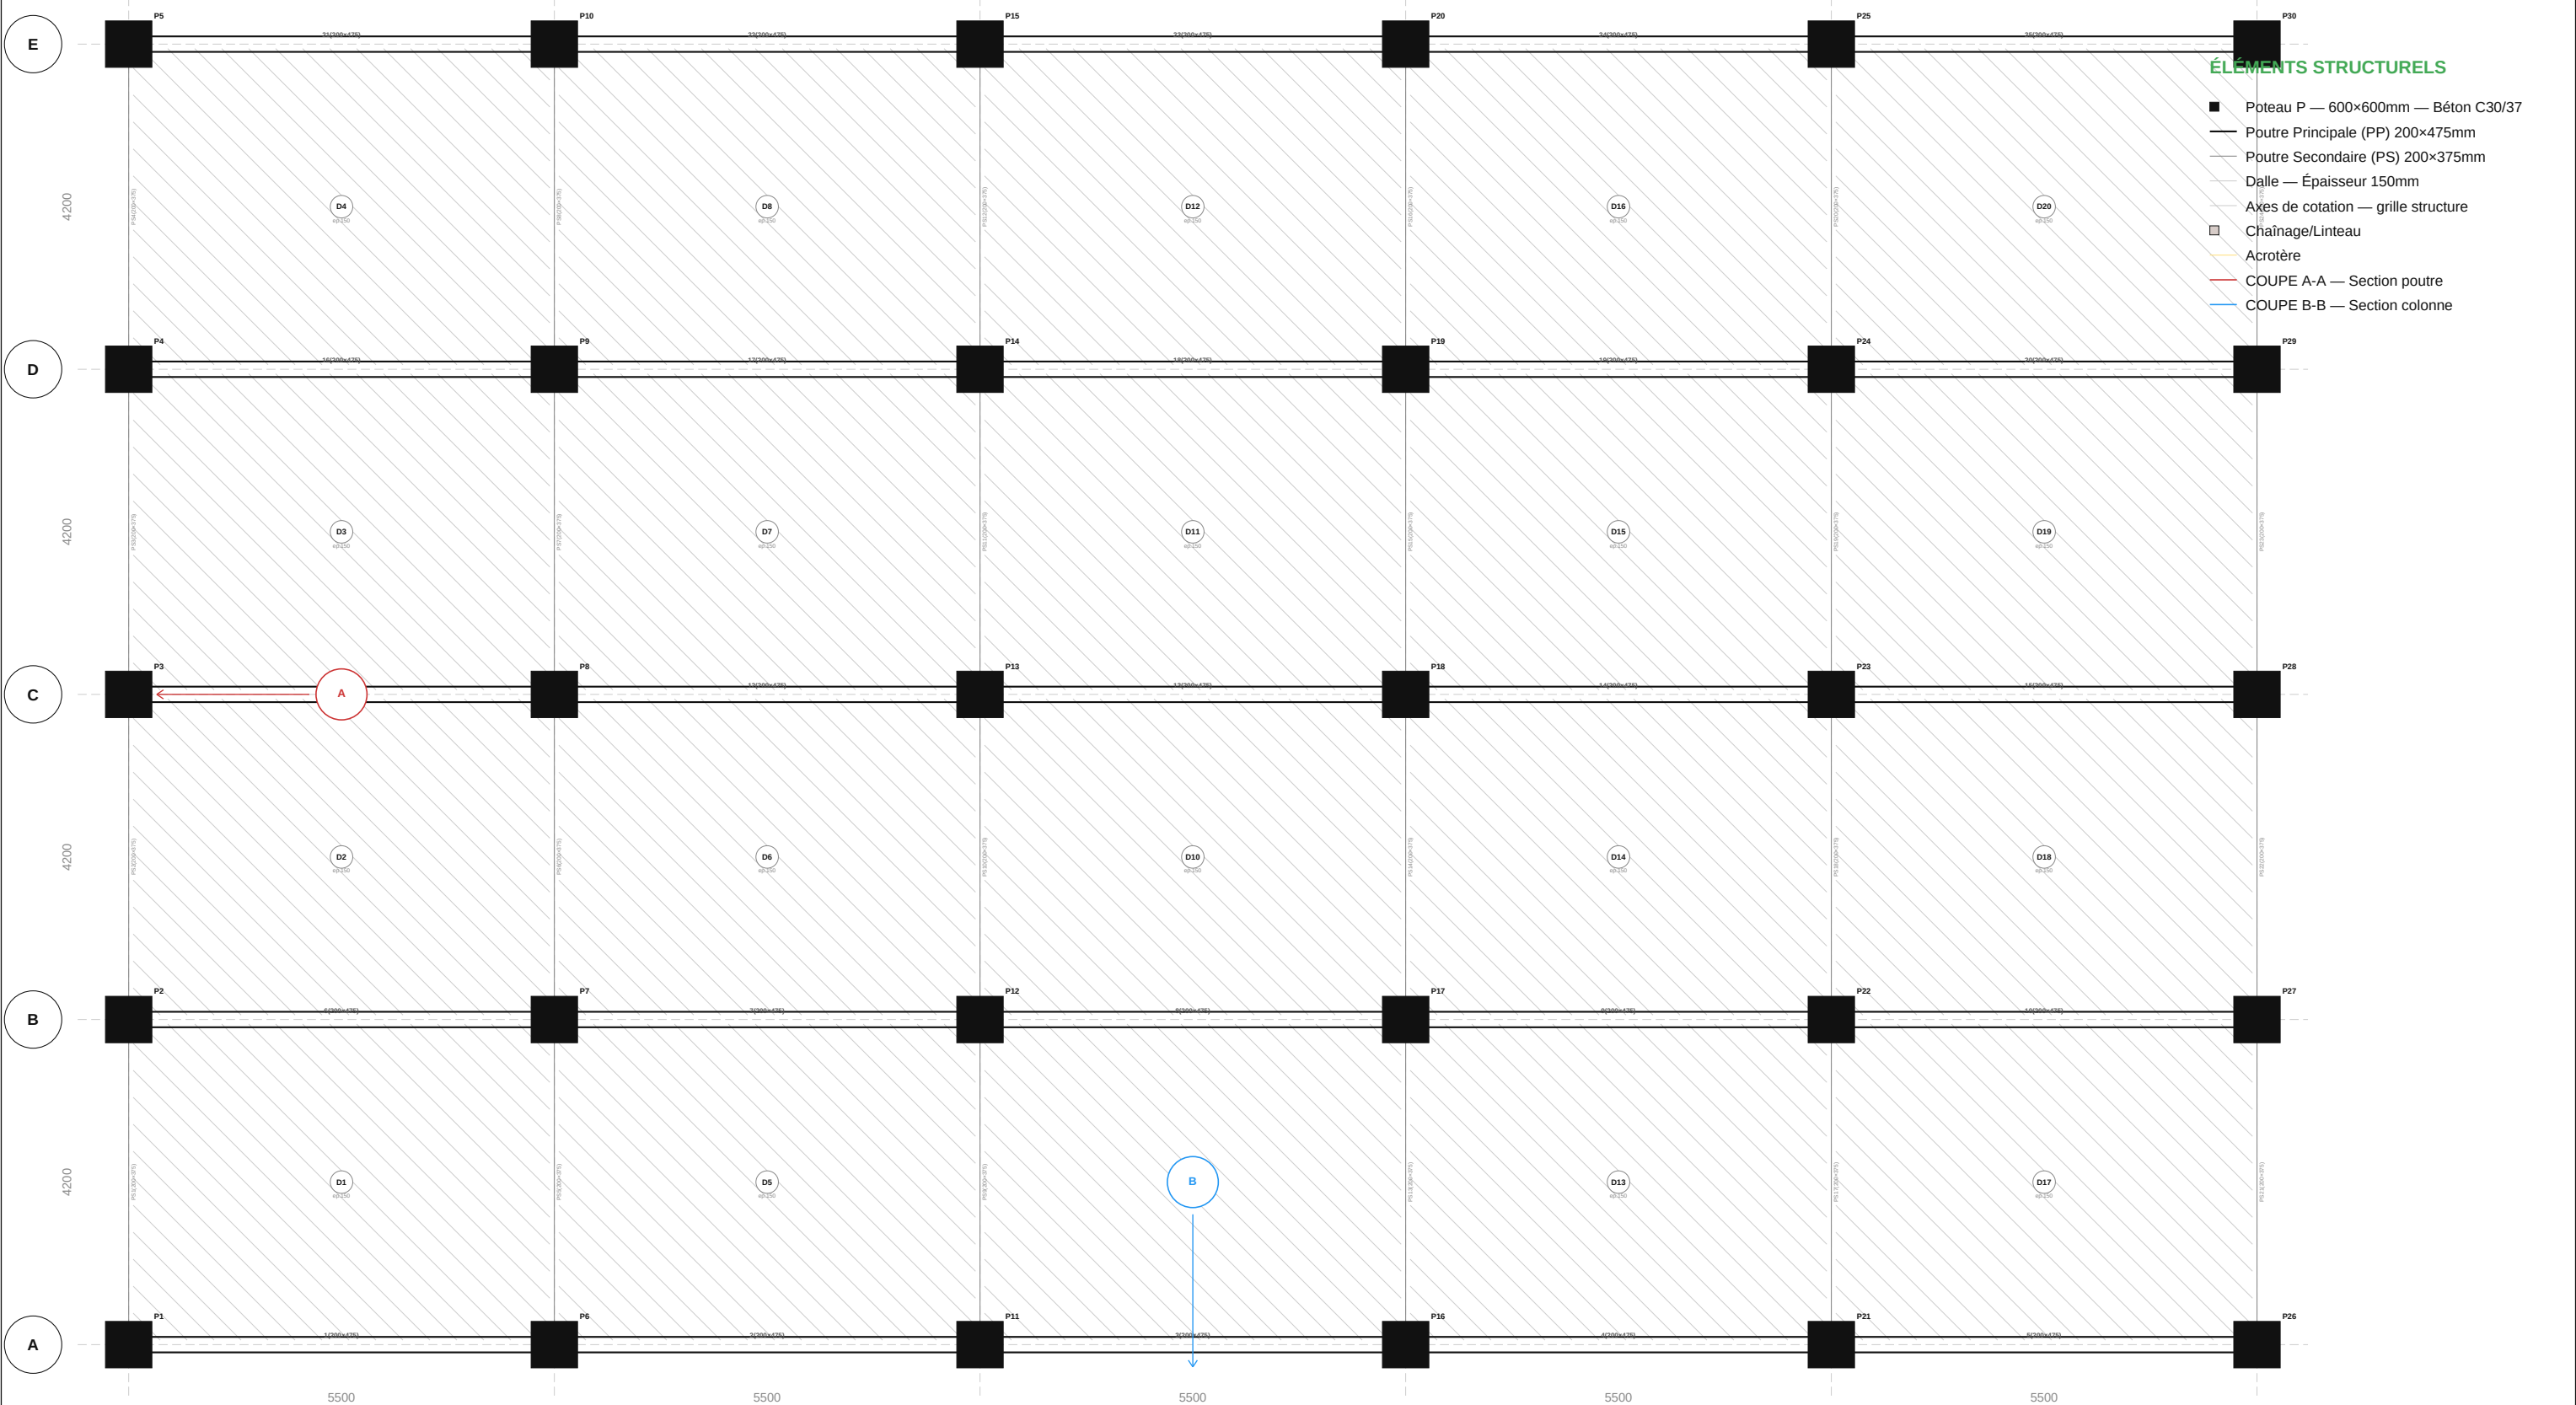

ÉLÉMENTS STRUCTURELS

- Poteau P — 600×600mm — Béton C30/37
- Poutre Principale (PP) 200×475mm
- Poutre Secondaire (PS) 200×375mm
- Dalle — Épaisseur 150mm
- Axes de cotation — grille structure
- Chânage/Linteau
- Acrotère
- COUPE A-A — Section poutre
- COUPE B-B — Section colonne

NOTES TECHNIQUES

Béton: C30/37 (fck=30 MPa)
Acier: HA500 (fyk=500 MPa)
Enrobage: 30mm (fond: 50mm)
EC2 + EC8 — NF EN 1992/1998
G=6.5 kN/m², Q=2.5 kN/m²
Zone sismique: 1

Rep.	Section	Niveau	NEd	NRd	Ratio	Armatures
P1-P30	600×600	N5	1157	7397	16%	4HA12
—	600×600	N4	1447	7397	20%	4HA12
—	600×600	N6	868	7397	12%	4HA12

TIJAN AI

Automated Engineering Bureau

support@tijan.ai

www.tijan.ai

06/05/2026

Résidence Sakho

Dakar, Senegal

COFFRAGE — R+5

STRUCTURE BÉTON ARMÉ

DESIGNED

TIJAN AI

DRAWN

TIJAN AI

CHECKED

TIJAN AI

SCALE

1/100

PHASE: AFD

TJN-RÉSIDE


DRAWING No

PL-006

SHEET

6 / 17

PLAN DE COFFRAGE — R+6

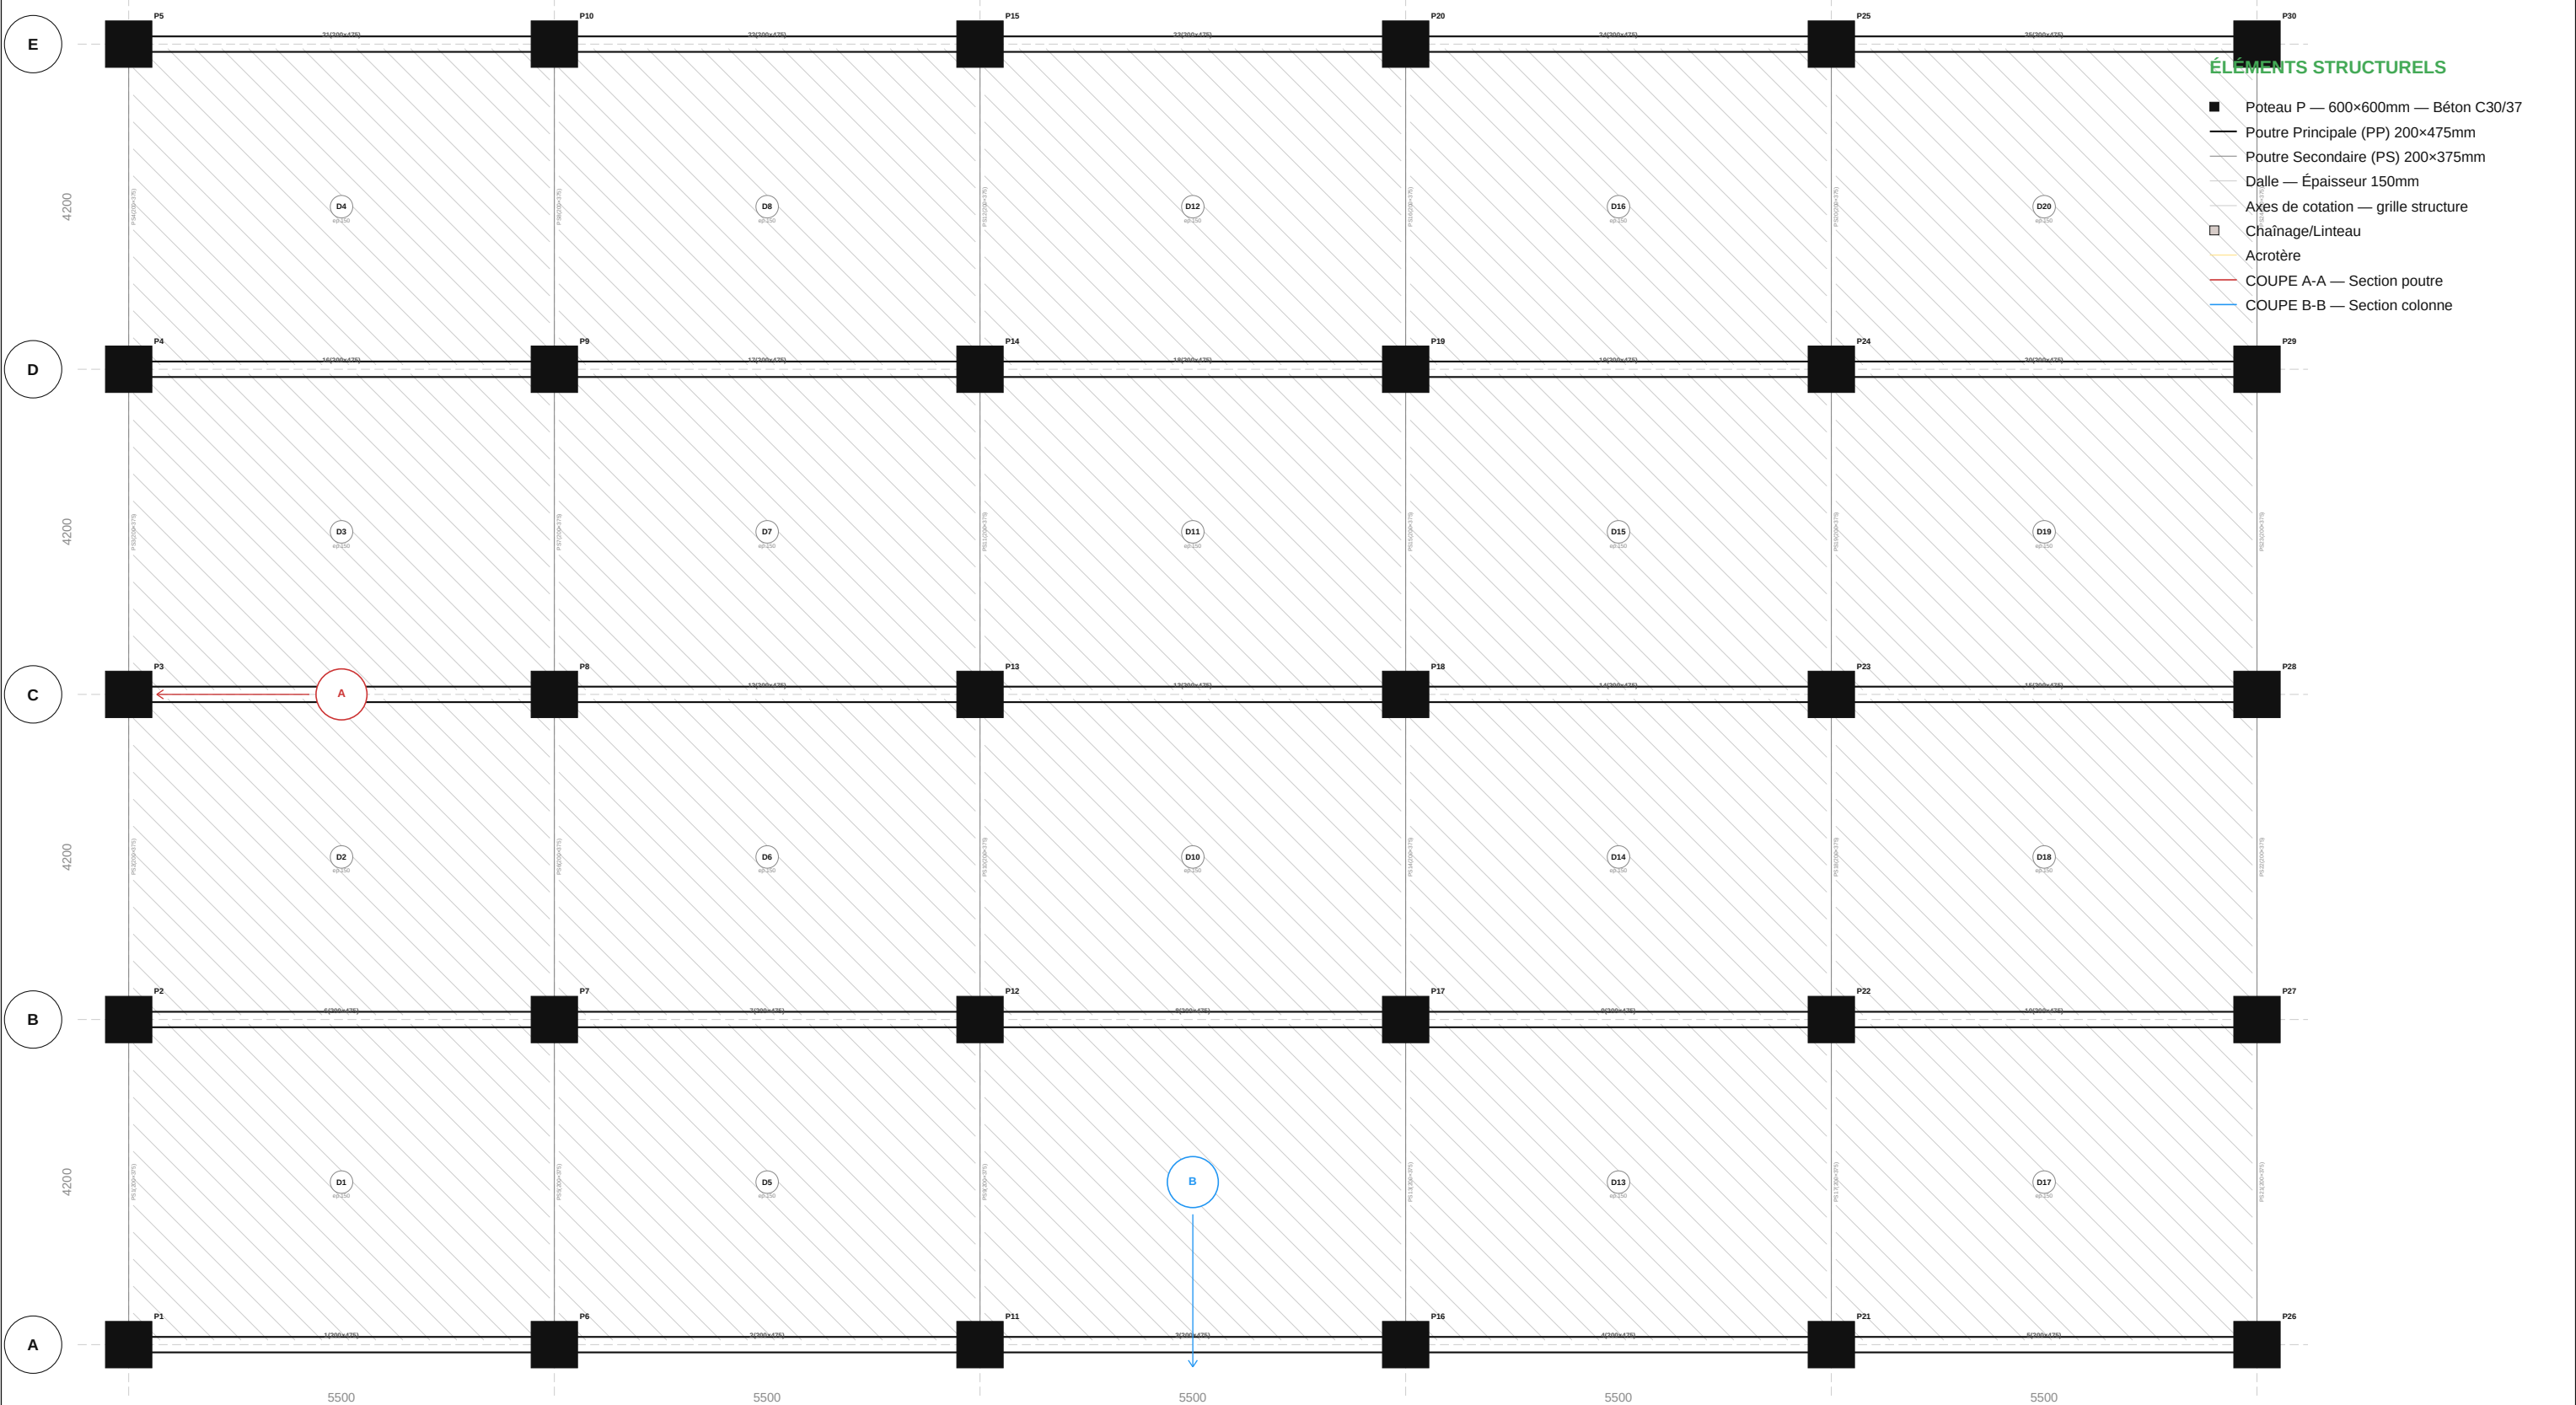


NOTES TECHNIQUES

Béton: C30/37 (fck=30 MPa)
Acier: HA500 (fyk=500 MPa)
Enrobage: 30mm (fond: 50mm)
EC2 + EC8 — NF EN 1992/1998
G=6.5 kN/m², Q=2.5 kN/m²
Zone sismique: 1

Rep.	Section	Niveau	NEd	NRd	Ratio	Armatures
P1-P30	600×600	N6	868	7397	12%	4HA12
—	600×600	N5	1157	7397	16%	4HA12
—	600×600	N7	579	7397	8%	4HA12

TIJAN AI Automated Engineering Bureau support@tijan.ai www.tijan.ai 06/05/2026	Résidence Sakho Dakar, Senegal			SCALE 1/100	
	COFFRAGE — R+6 STRUCTURE BÉTON ARMÉ			PHASE: APP TJN-RÉSIDE	
	DESIGNED TIJAN AI	DRAWN TIJAN AI	CHECKED TIJAN AI	DRAWING No PL-007	SHEET 7 / 17

PLAN DE COFFRAGE — R+7

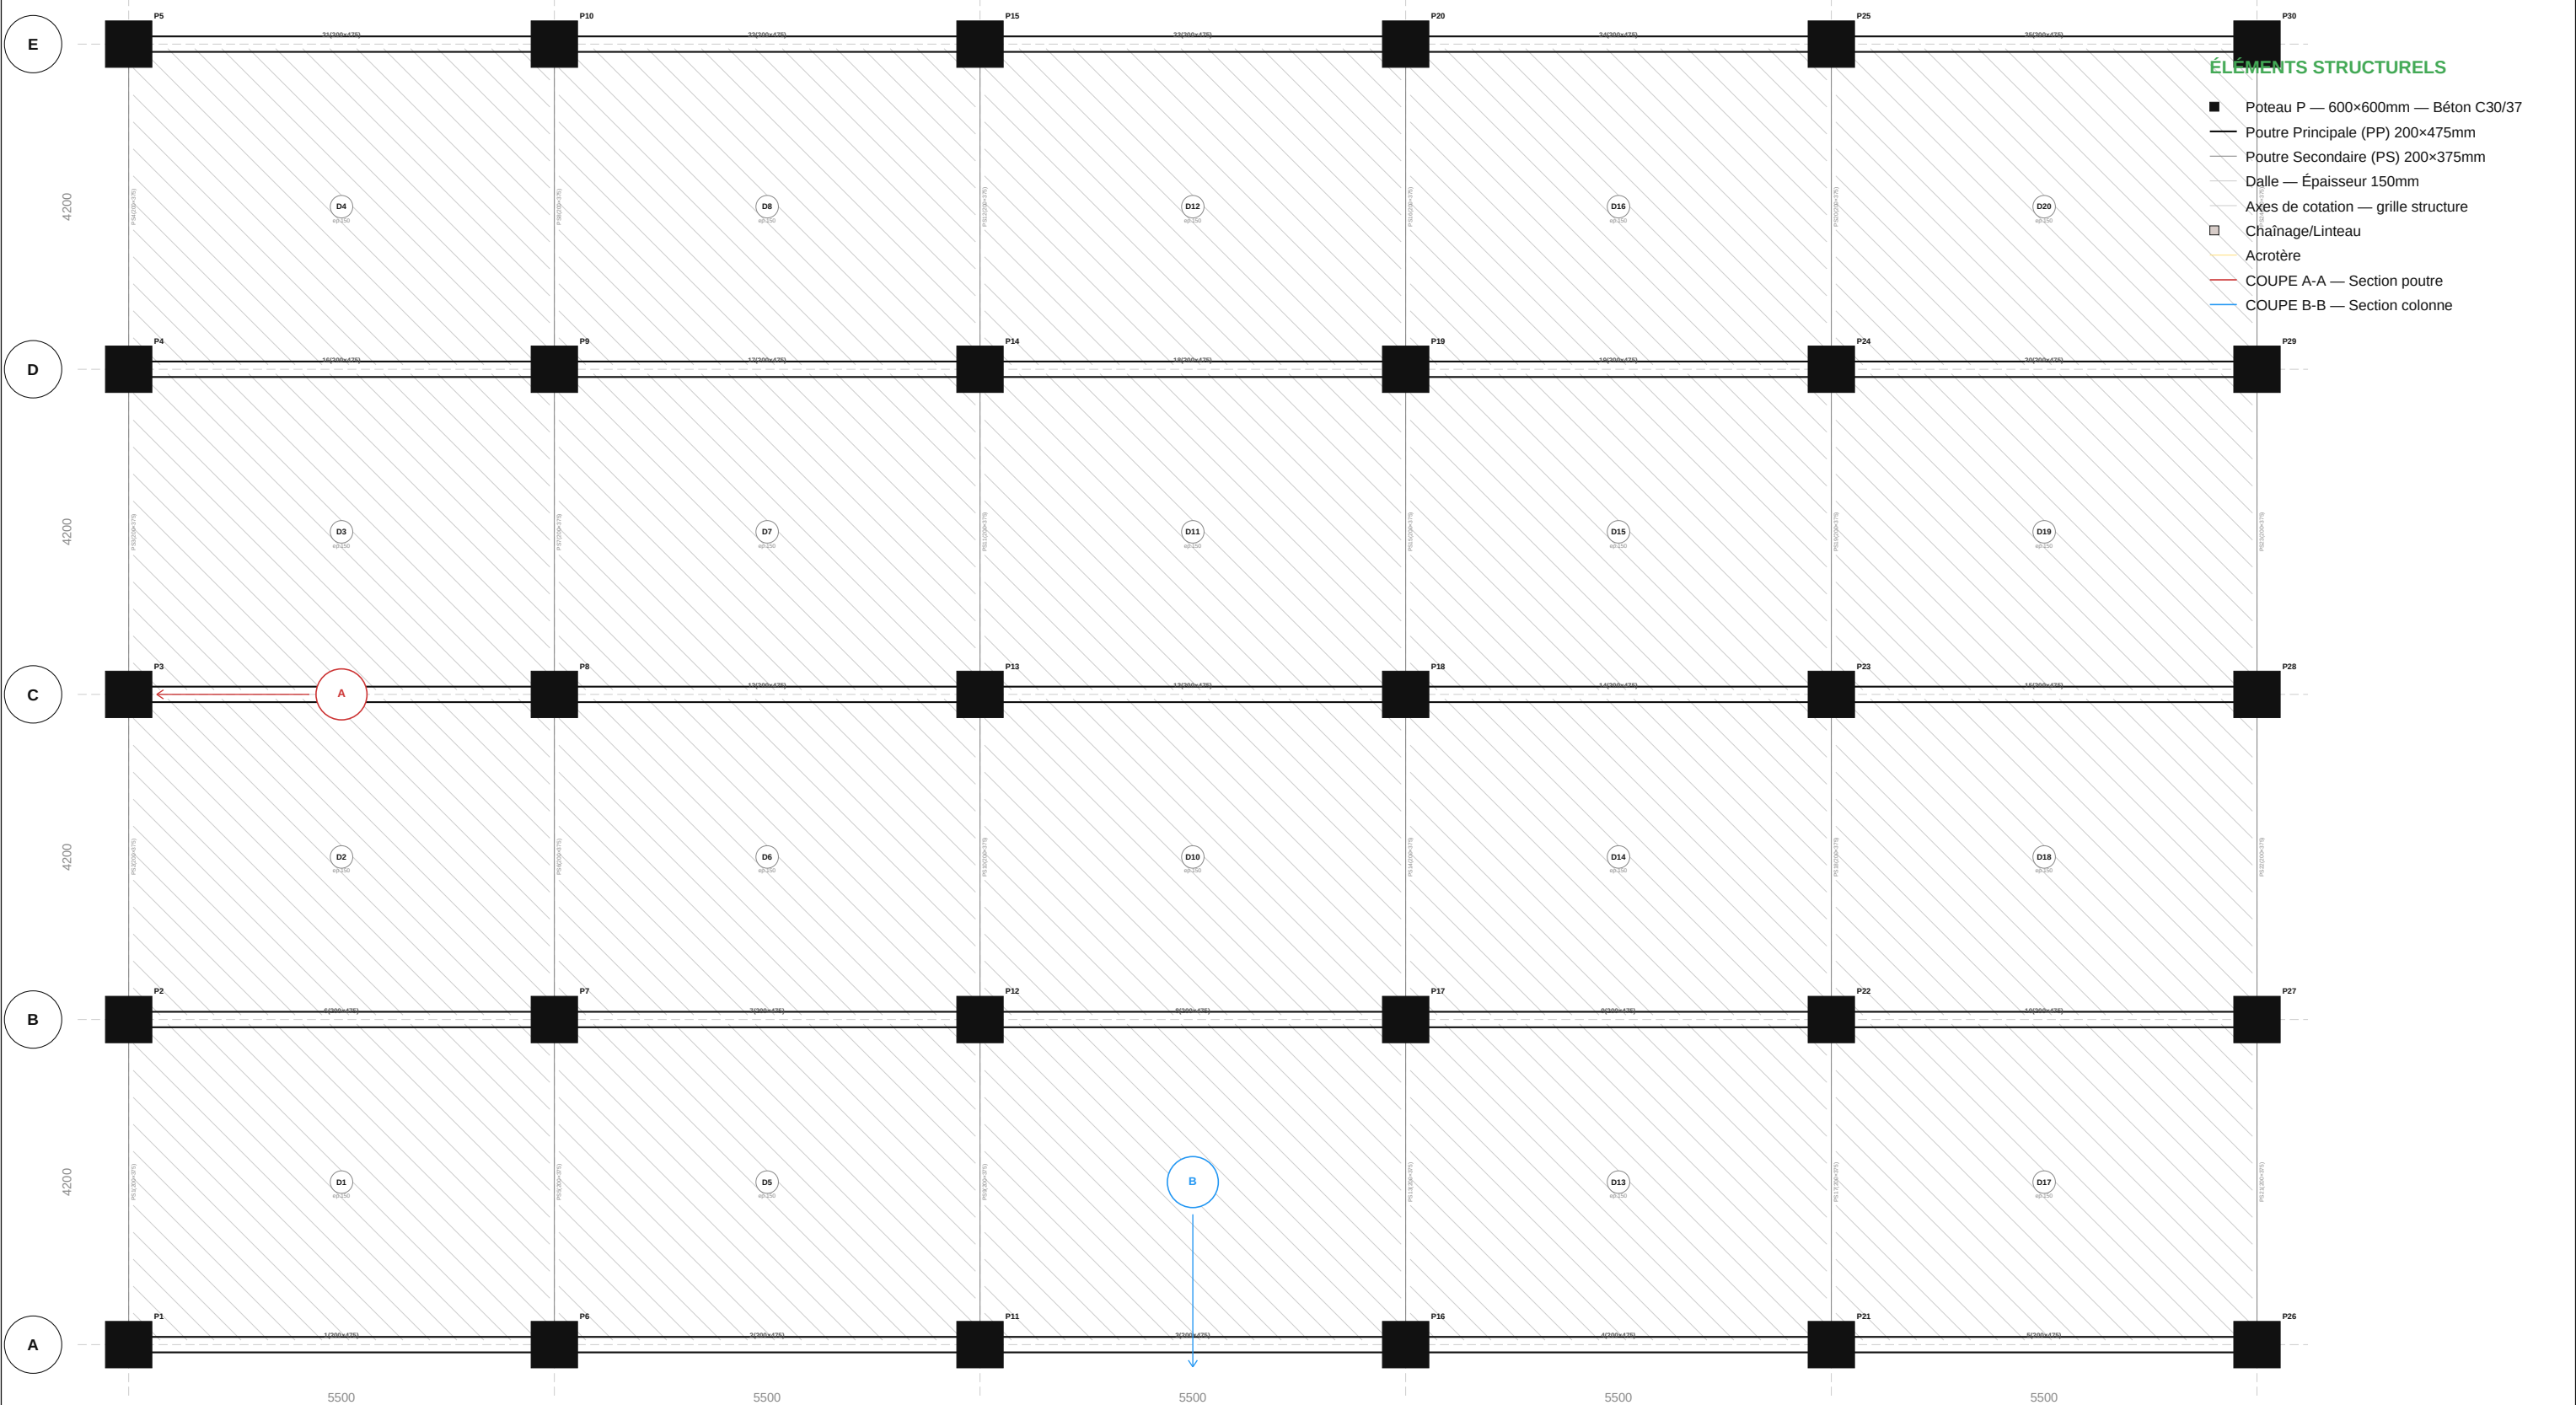

ÉLÉMENTS STRUCTURELS

- Poteau P — 600×600mm — Béton C30/37
- Poutre Principale (PP) 200×475mm
- Poutre Secondaire (PS) 200×375mm
- Dalle — Épaisseur 150mm
- Axes de cotation — grille structure
- Chânage/Linteau
- Acrotère
- COUPE A-A — Section poutre
- COUPE B-B — Section colonne

NOTES TECHNIQUES

Béton: C30/37 (fck=30 MPa)
Acier: HA500 (fyk=500 MPa)
Enrobage: 30mm (fond: 50mm)
EC2 + EC8 — NF EN 1992/1998
G=6.5 kN/m², Q=2.5 kN/m²
Zone sismique: 1

Rep.	Section	Niveau	NEd	NRd	Ratio	Armatures
P1-P30	600×600	N7	579	7397	8%	4HA12
—	600×600	N6	868	7397	12%	4HA12
—	600×600	Toiture	289	7397	4%	4HA12

TIJAN AI

Automated Engineering Bureau

support@tjan.ai

www.tjan.ai

06/05/2026

Résidence Sakho

Dakar, Senegal

COFFRAGE — R+7

STRUCTURE BÉTON ARMÉ

DESIGNED

TIJAN AI

DRAWN

TIJAN AI

CHECKED

TIJAN AI

SCALE

1/100

PHASE: AFD

TJN-RÉSIDE


DRAWING No

PL-008

SHEET

8 / 17

PLAN DE COFFRAGE — R+8

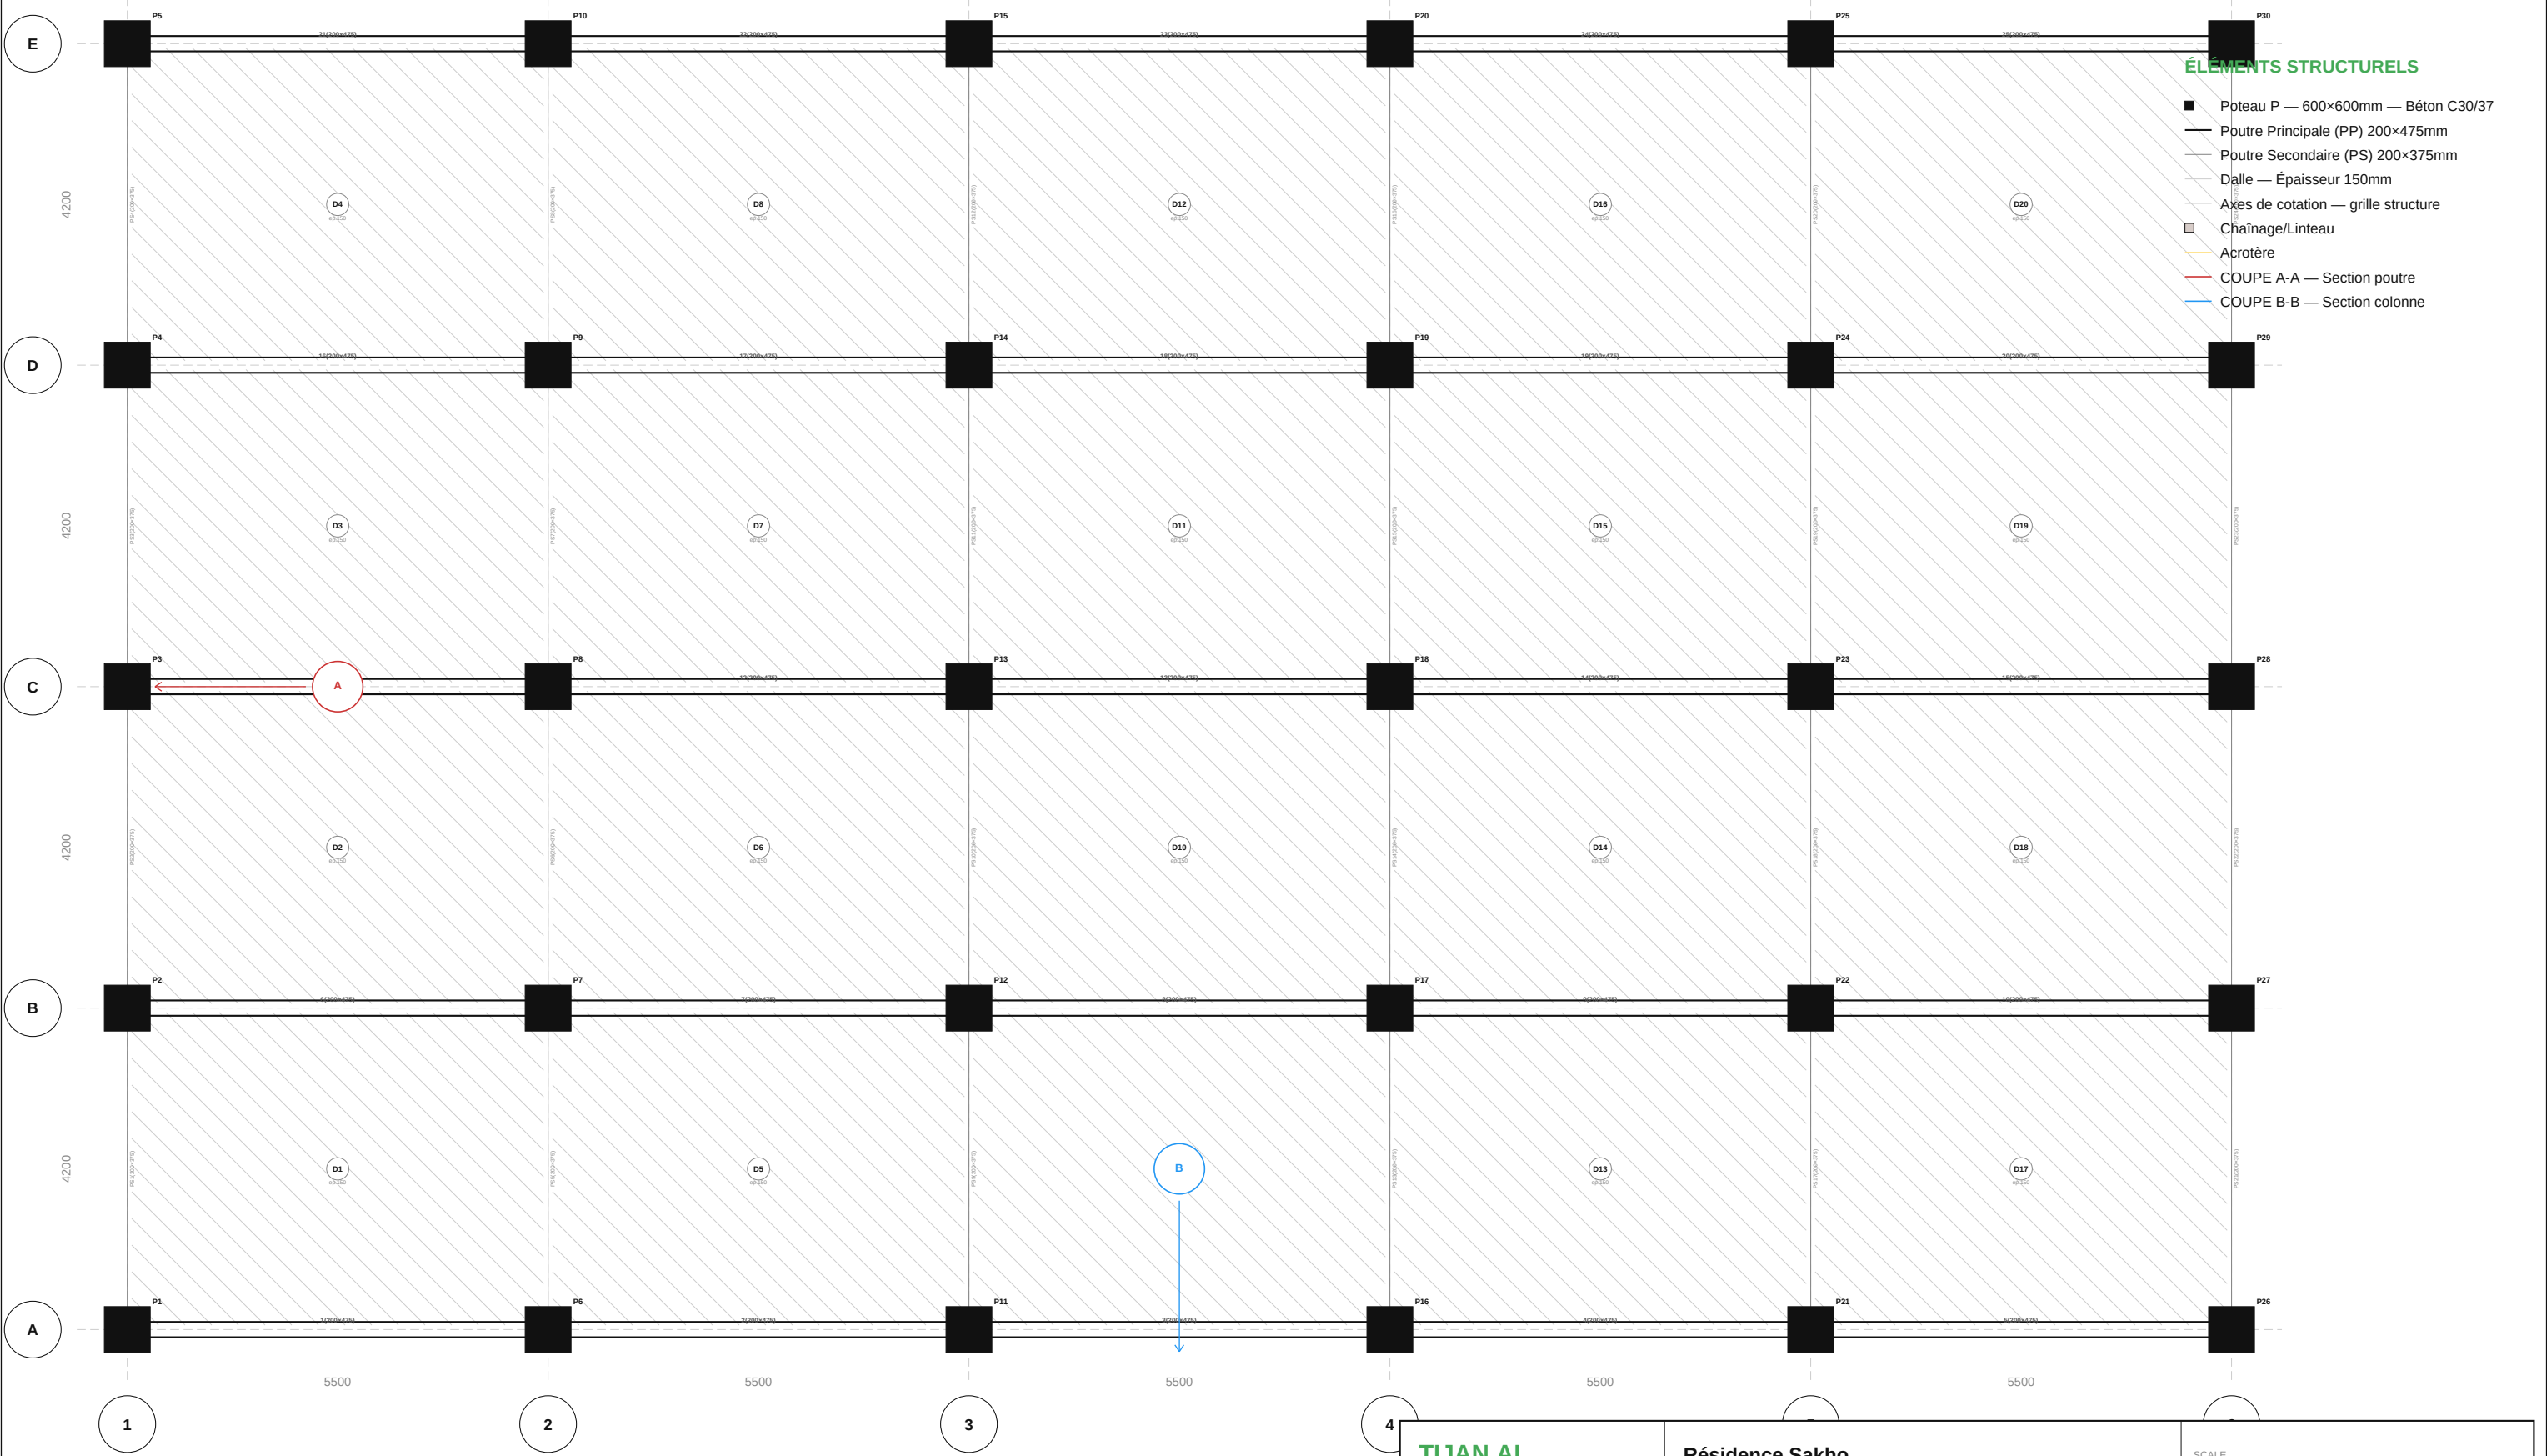


NOTES TECHNIQUES

Béton: C30/37 (fck=30 MPa)
Acier: HA500 (fyk=500 MPa)
Enrobage: 30mm (fond: 50mm)
EC2 + EC8 — NF EN 1992/1998
G=6.5 kN/m², Q=2.5 kN/m²
Zone sismique: 1

Rep.	Section	Niveau	NEd	NRd	Ratio	Armatures
P1-P30	600×600	Toiture	289	7397	4%	4HA12
—	600×600	N7	579	7397	8%	4HA12

TIJAN AI Automated Engineering Bureau support@tijan.ai www.tijan.ai 06/05/2026	Résidence Sakho Dakar, Senegal			SCALE 1/100	
	COFFRAGE — R+8 STRUCTURE BÉTON ARMÉ			PHASE: APP TJN-RÉSIDE	
	DESIGNED TIJAN AI	DRAWN TIJAN AI	CHECKED TIJAN AI	DRAWING No PL-009	SHEET 9 / 17

PLAN DE COFFRAGE — TERRASSE

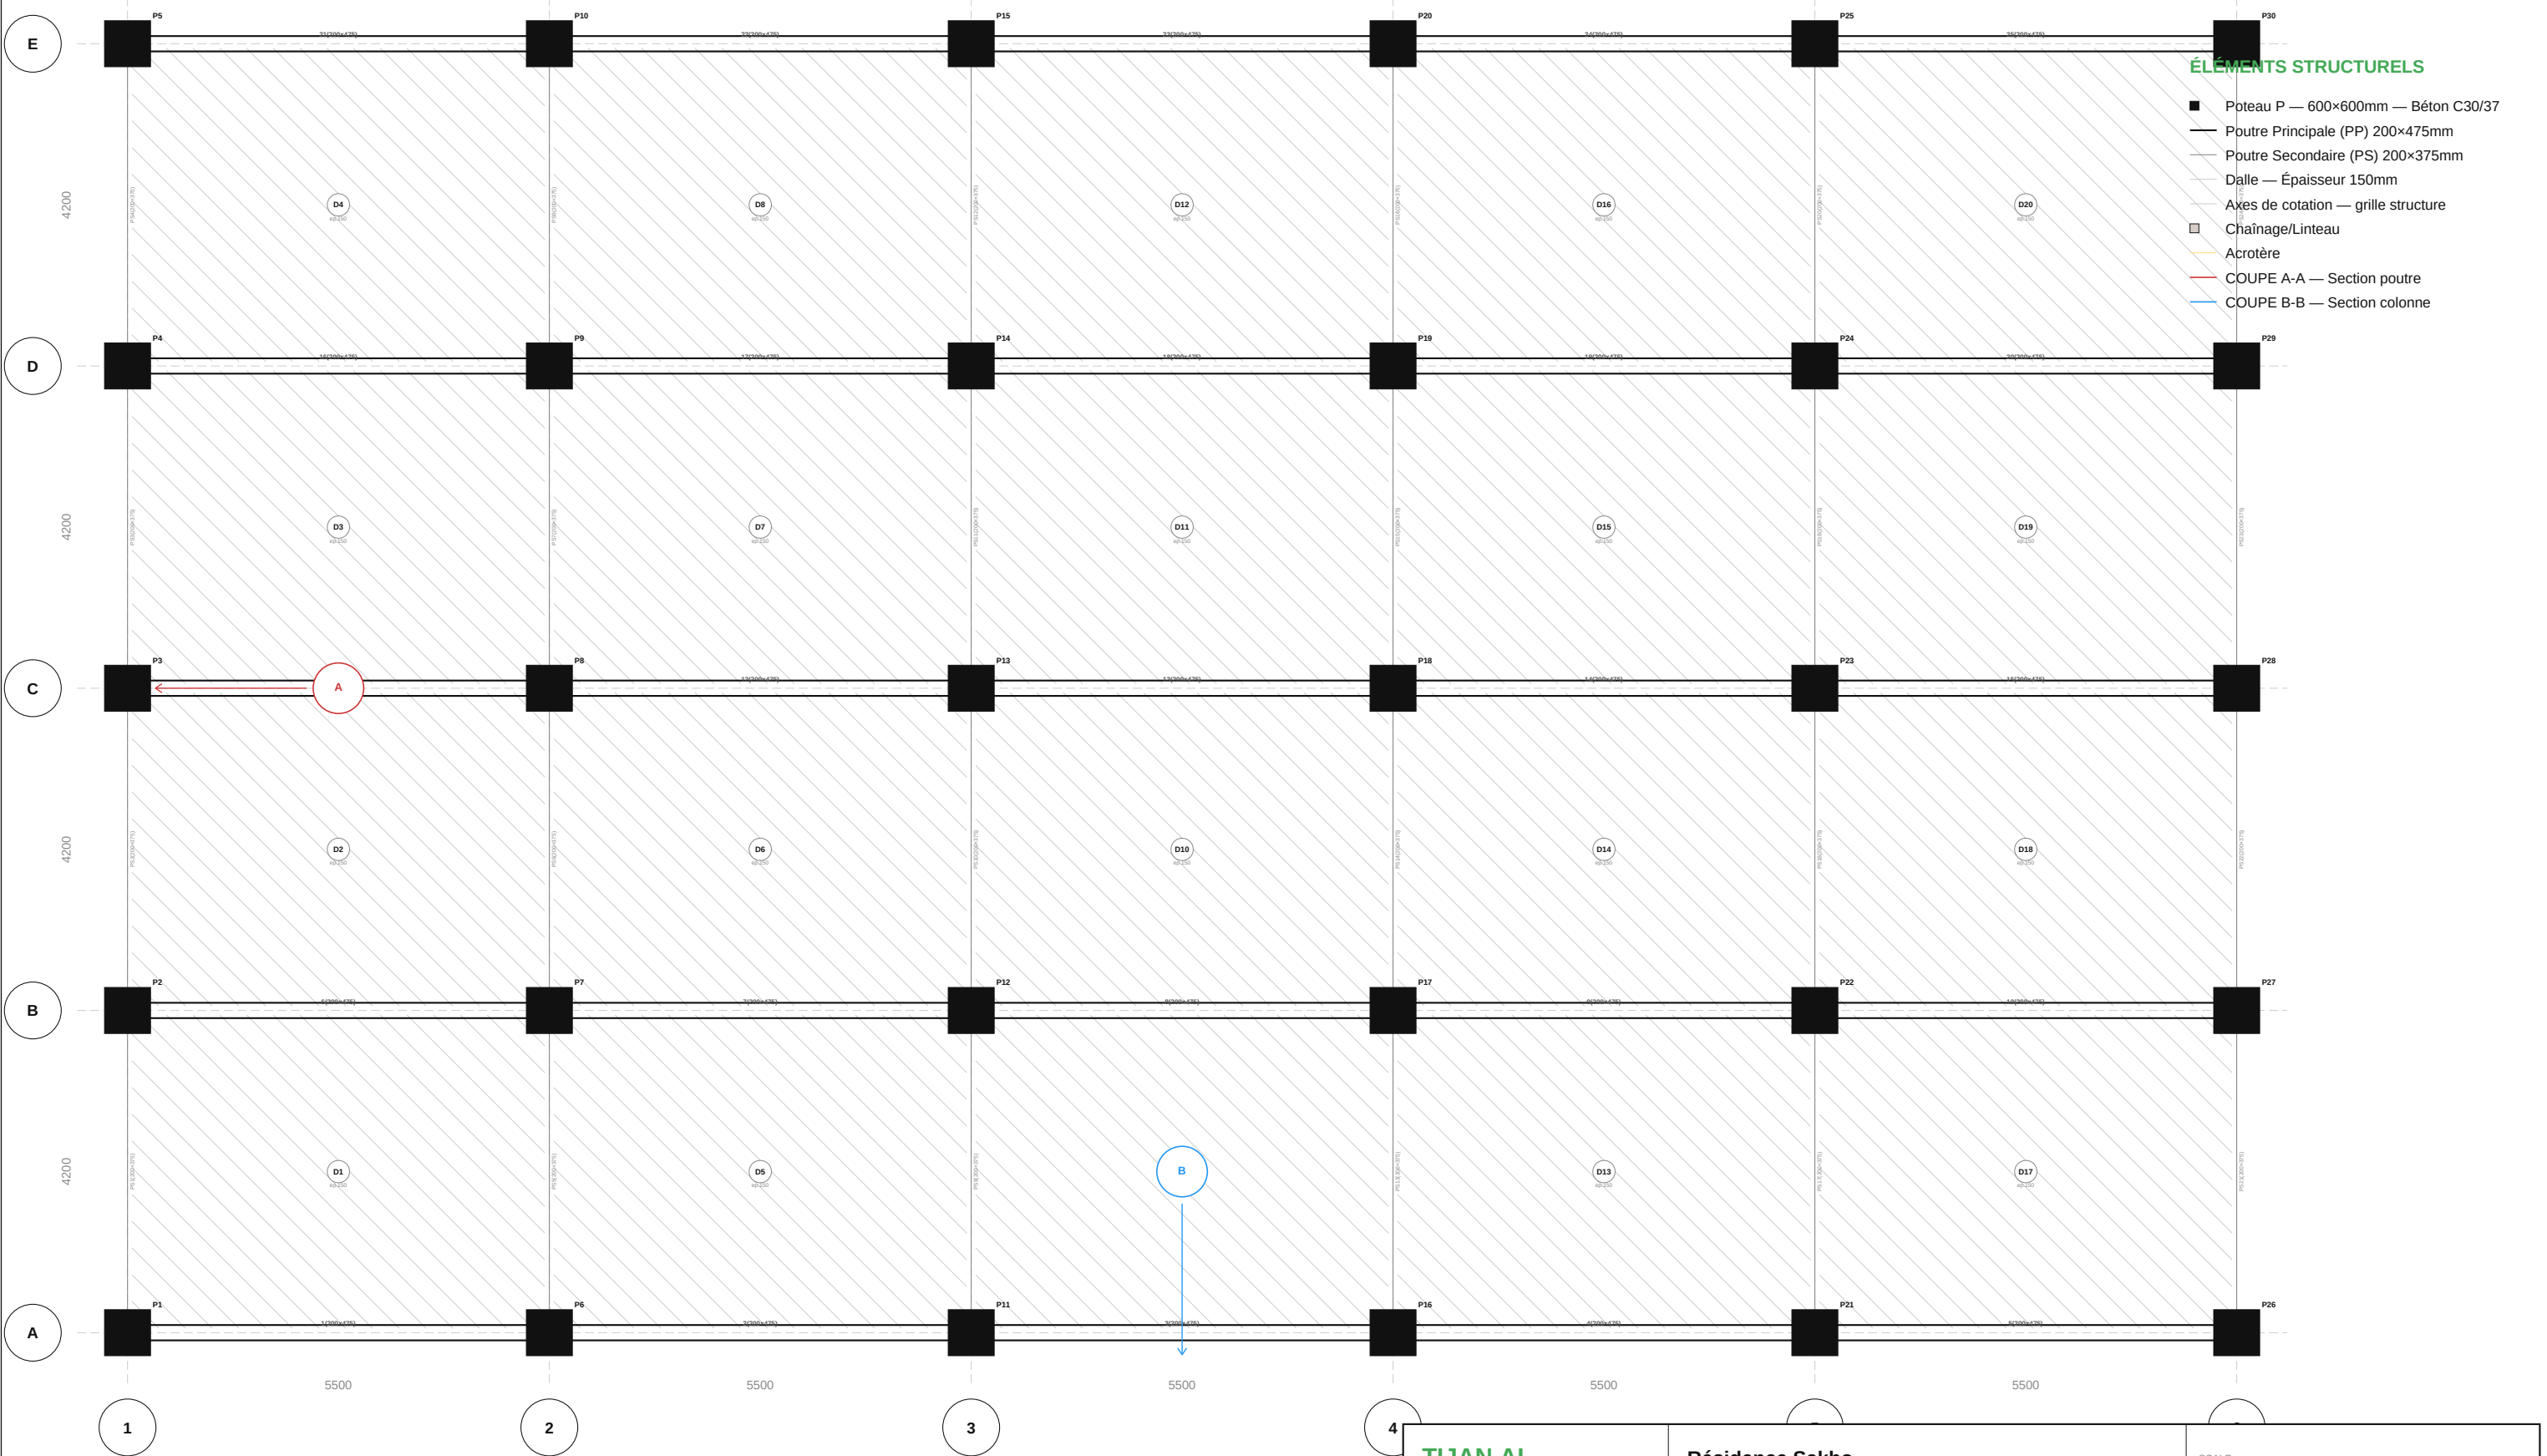

NOTES TECHNIQUES

Béton: C30/37 (fck=30 MPa)

Acier: HA500 (fyk=500 MPa)

Enrobage: 30mm (fond: 50mm)

EC2 + EC8 — NF EN 1992/1998

G=6.5 kN/m², Q=2.5 kN/m²

Zone sismique: 1

Rep.	Section	Niveau	NEd	NRd	Ratio	Armatures
P1-P30	600×600	Toiture	289	7397	4%	4HA12
—	600×600	N7	579	7397	8%	4HA12

TIJAN AI

Automated Engineering Bureau

support@tijan.ai

www.tijan.ai

06/05/2026

Résidence Sakho

Dakar, Senegal

COFFRAGE — Terrasse

STRUCTURE BÉTON ARMÉ

DESIGNED

TIJAN AI

DRAWN

TIJAN AI

CHECKED

TIJAN AI

SCALE

1/100

PHASE: PRO

TJN-RÉSIDE

DRAWING No

PL-010


SHEET

10 / 17

[illegible]


1	2	3	4	<table> <tr> <td> TIJAN AI Automated Engineering Bureau </td><td colspan="3"> Résidence Sakho Dakar, Senegal </td><td> SCALE 1/100 </td></tr> <tr> <td>support@tijan.ai</td><td colspan="3"> FERRAILLAGE INF. DALLE LOT 01 — STRUCTURE / FERRAILLAGE B.A. </td><td> PROJET TJN-RÉSIDE </td></tr> <tr> <td> www.tijan.ai 06/05/2026 </td><td> DESIGNED TIJAN AI </td><td> DRAWN TIJAN AI </td><td> CHECKED TIJAN AI </td><td> DRAWING No TJN-STR-FER-INF-01111 / 17 </td></tr> </table>	TIJAN AI Automated Engineering Bureau	Résidence Sakho Dakar, Senegal			SCALE 1/100	support@tijan.ai	FERRAILLAGE INF. DALLE LOT 01 — STRUCTURE / FERRAILLAGE B.A.			PROJET TJN-RÉSIDE	www.tijan.ai 06/05/2026	DESIGNED TIJAN AI	DRAWN TIJAN AI	CHECKED TIJAN AI	DRAWING No TJN-STR-FER-INF-01111 / 17
TIJAN AI Automated Engineering Bureau	Résidence Sakho Dakar, Senegal			SCALE 1/100															
support@tijan.ai	FERRAILLAGE INF. DALLE LOT 01 — STRUCTURE / FERRAILLAGE B.A.			PROJET TJN-RÉSIDE															
www.tijan.ai 06/05/2026	DESIGNED TIJAN AI	DRAWN TIJAN AI	CHECKED TIJAN AI	DRAWING No TJN-STR-FER-INF-01111 / 17															

FERRAILLAGE SUPÉRIEUR DALLE — PH NIVEAU COURANT

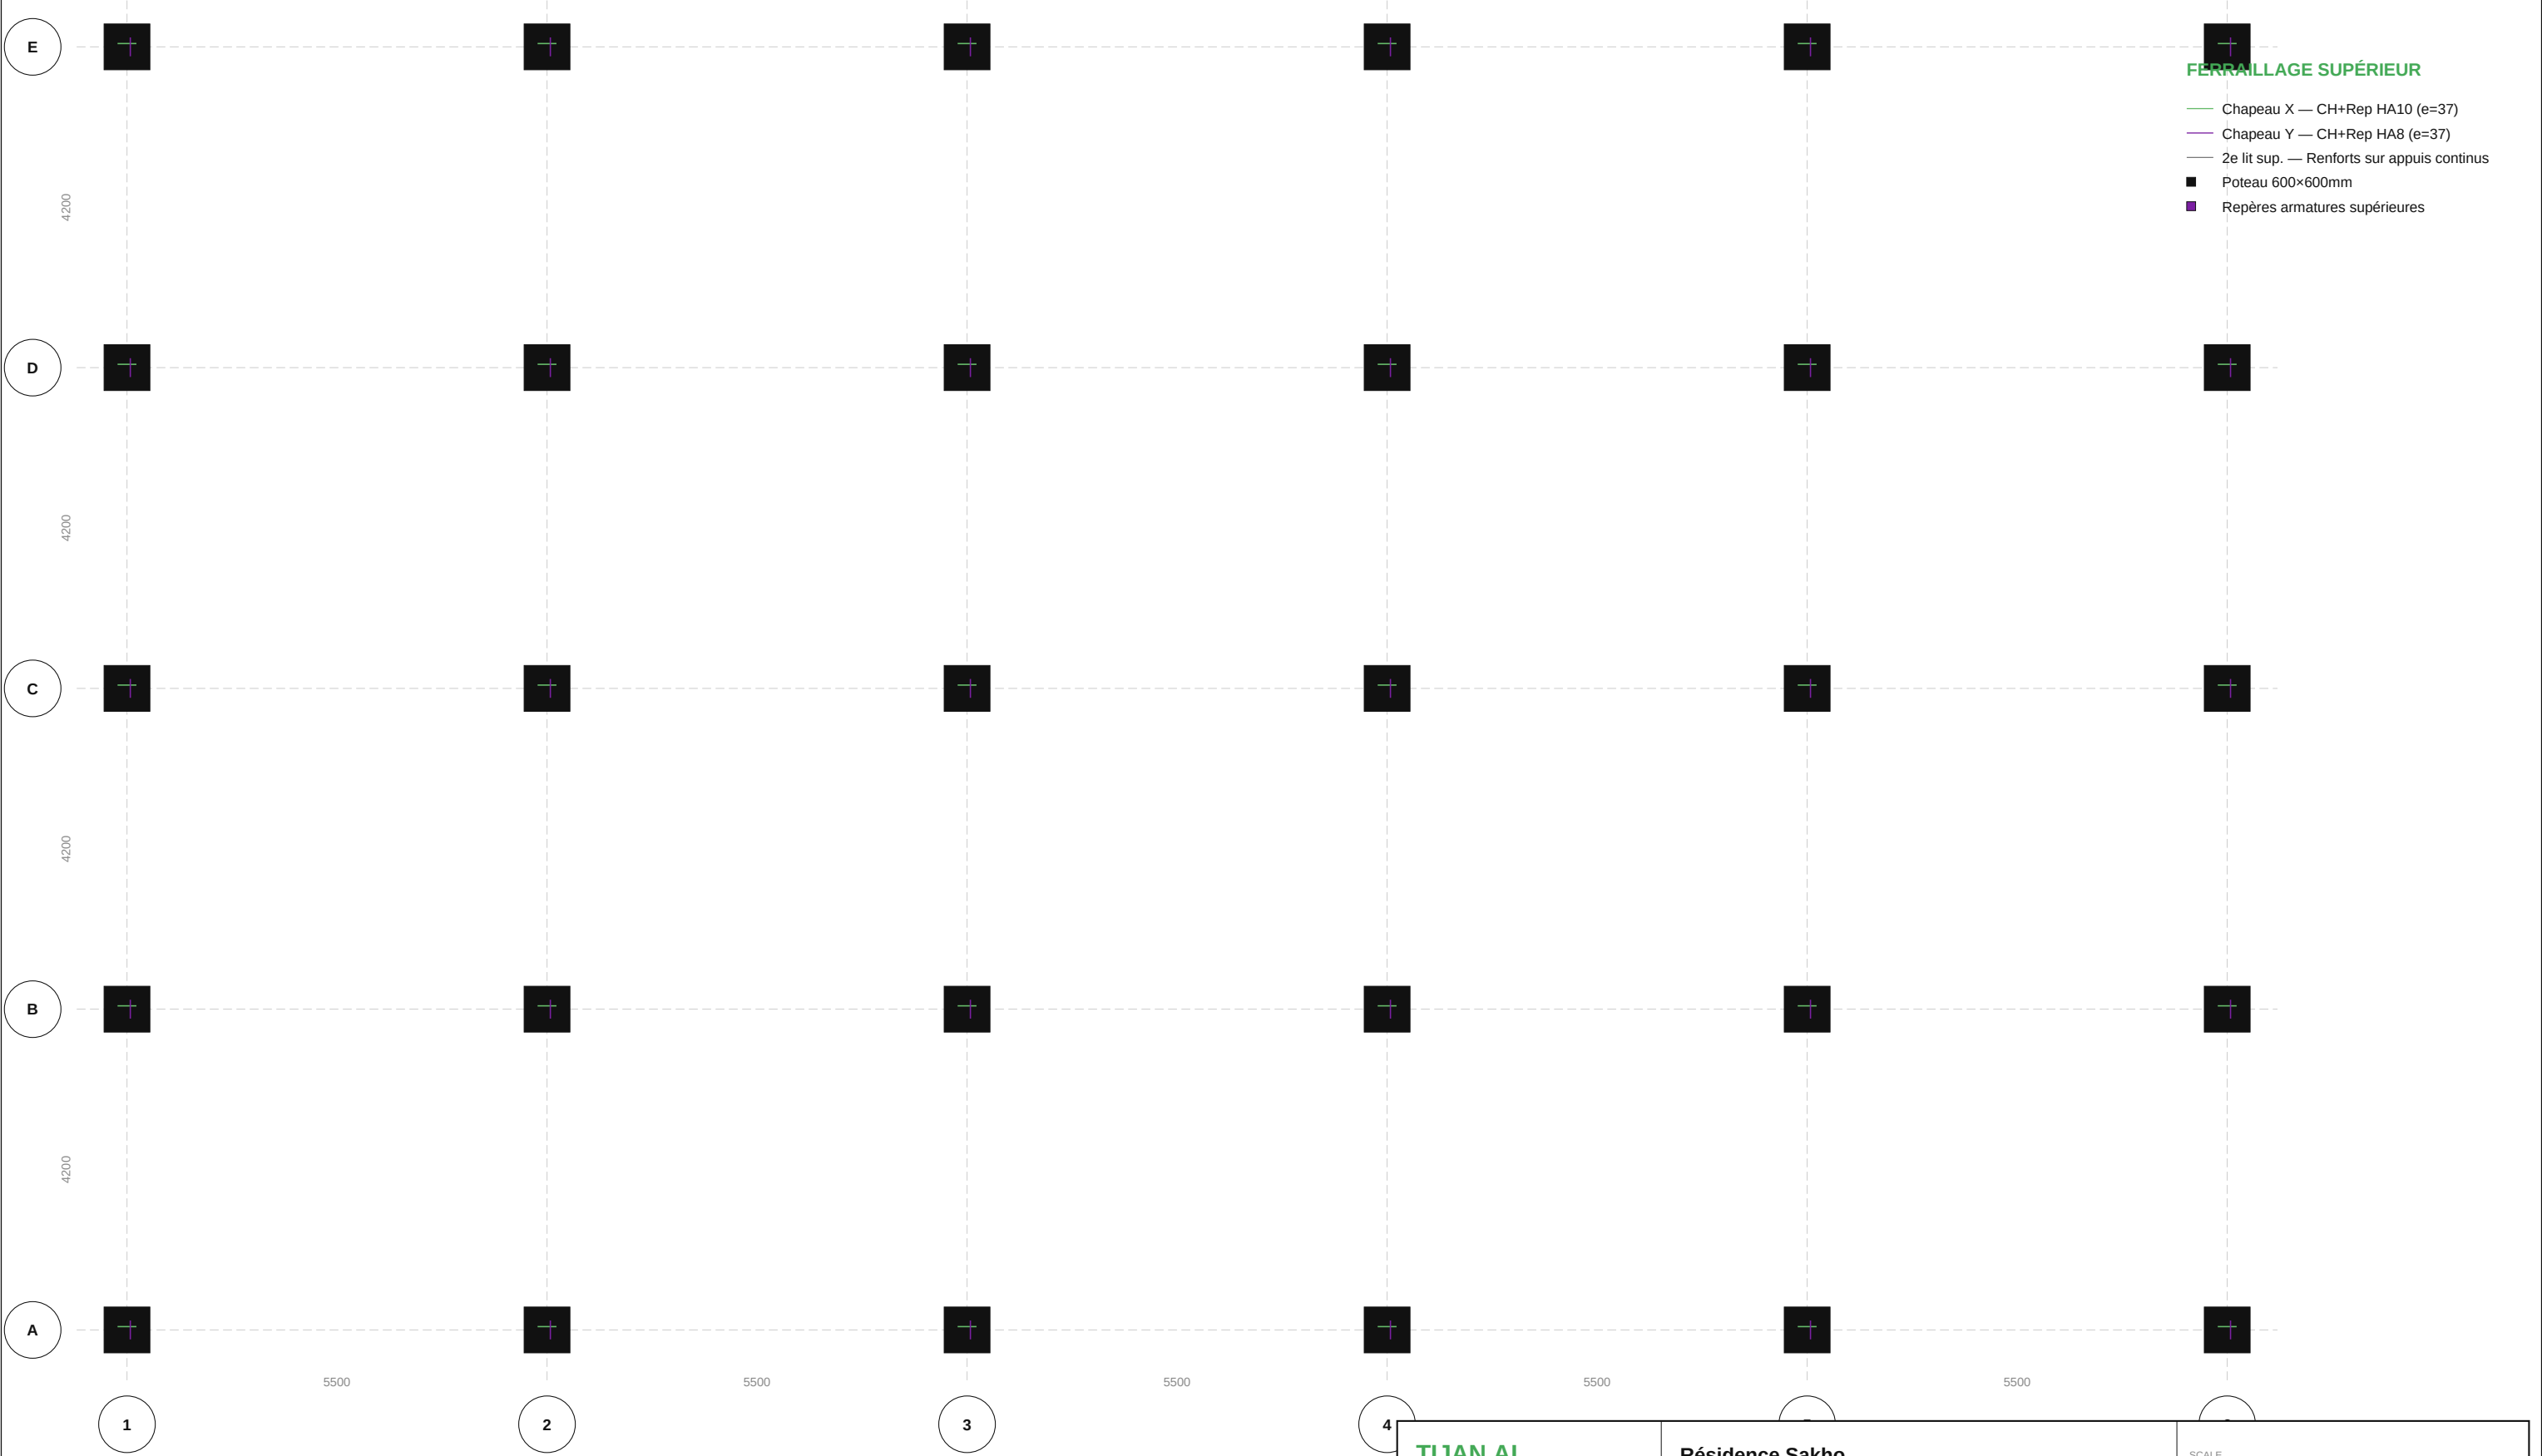


TIJAN AI Automated Engineering Bureau	Résidence Sakho Dakar, Senegal			SCALE 1/100
support@tijan.ai	FERRAILLAGE SUP. DALLE LOT 01 — STRUCTURE / FERRAILLAGE B.A.			PHASE TJN-RÉSIDE
www.tijan.ai 06/05/2026	DESIGNED TIJAN AI	DRAWN TIJAN AI	CHECKED TIJAN AI	DRAWING No TJN-STR-FER-SUP-01 SHEET 12 / 17

COUPE TYPE DALLE — DÉTAIL FERRAILLAGE A-A

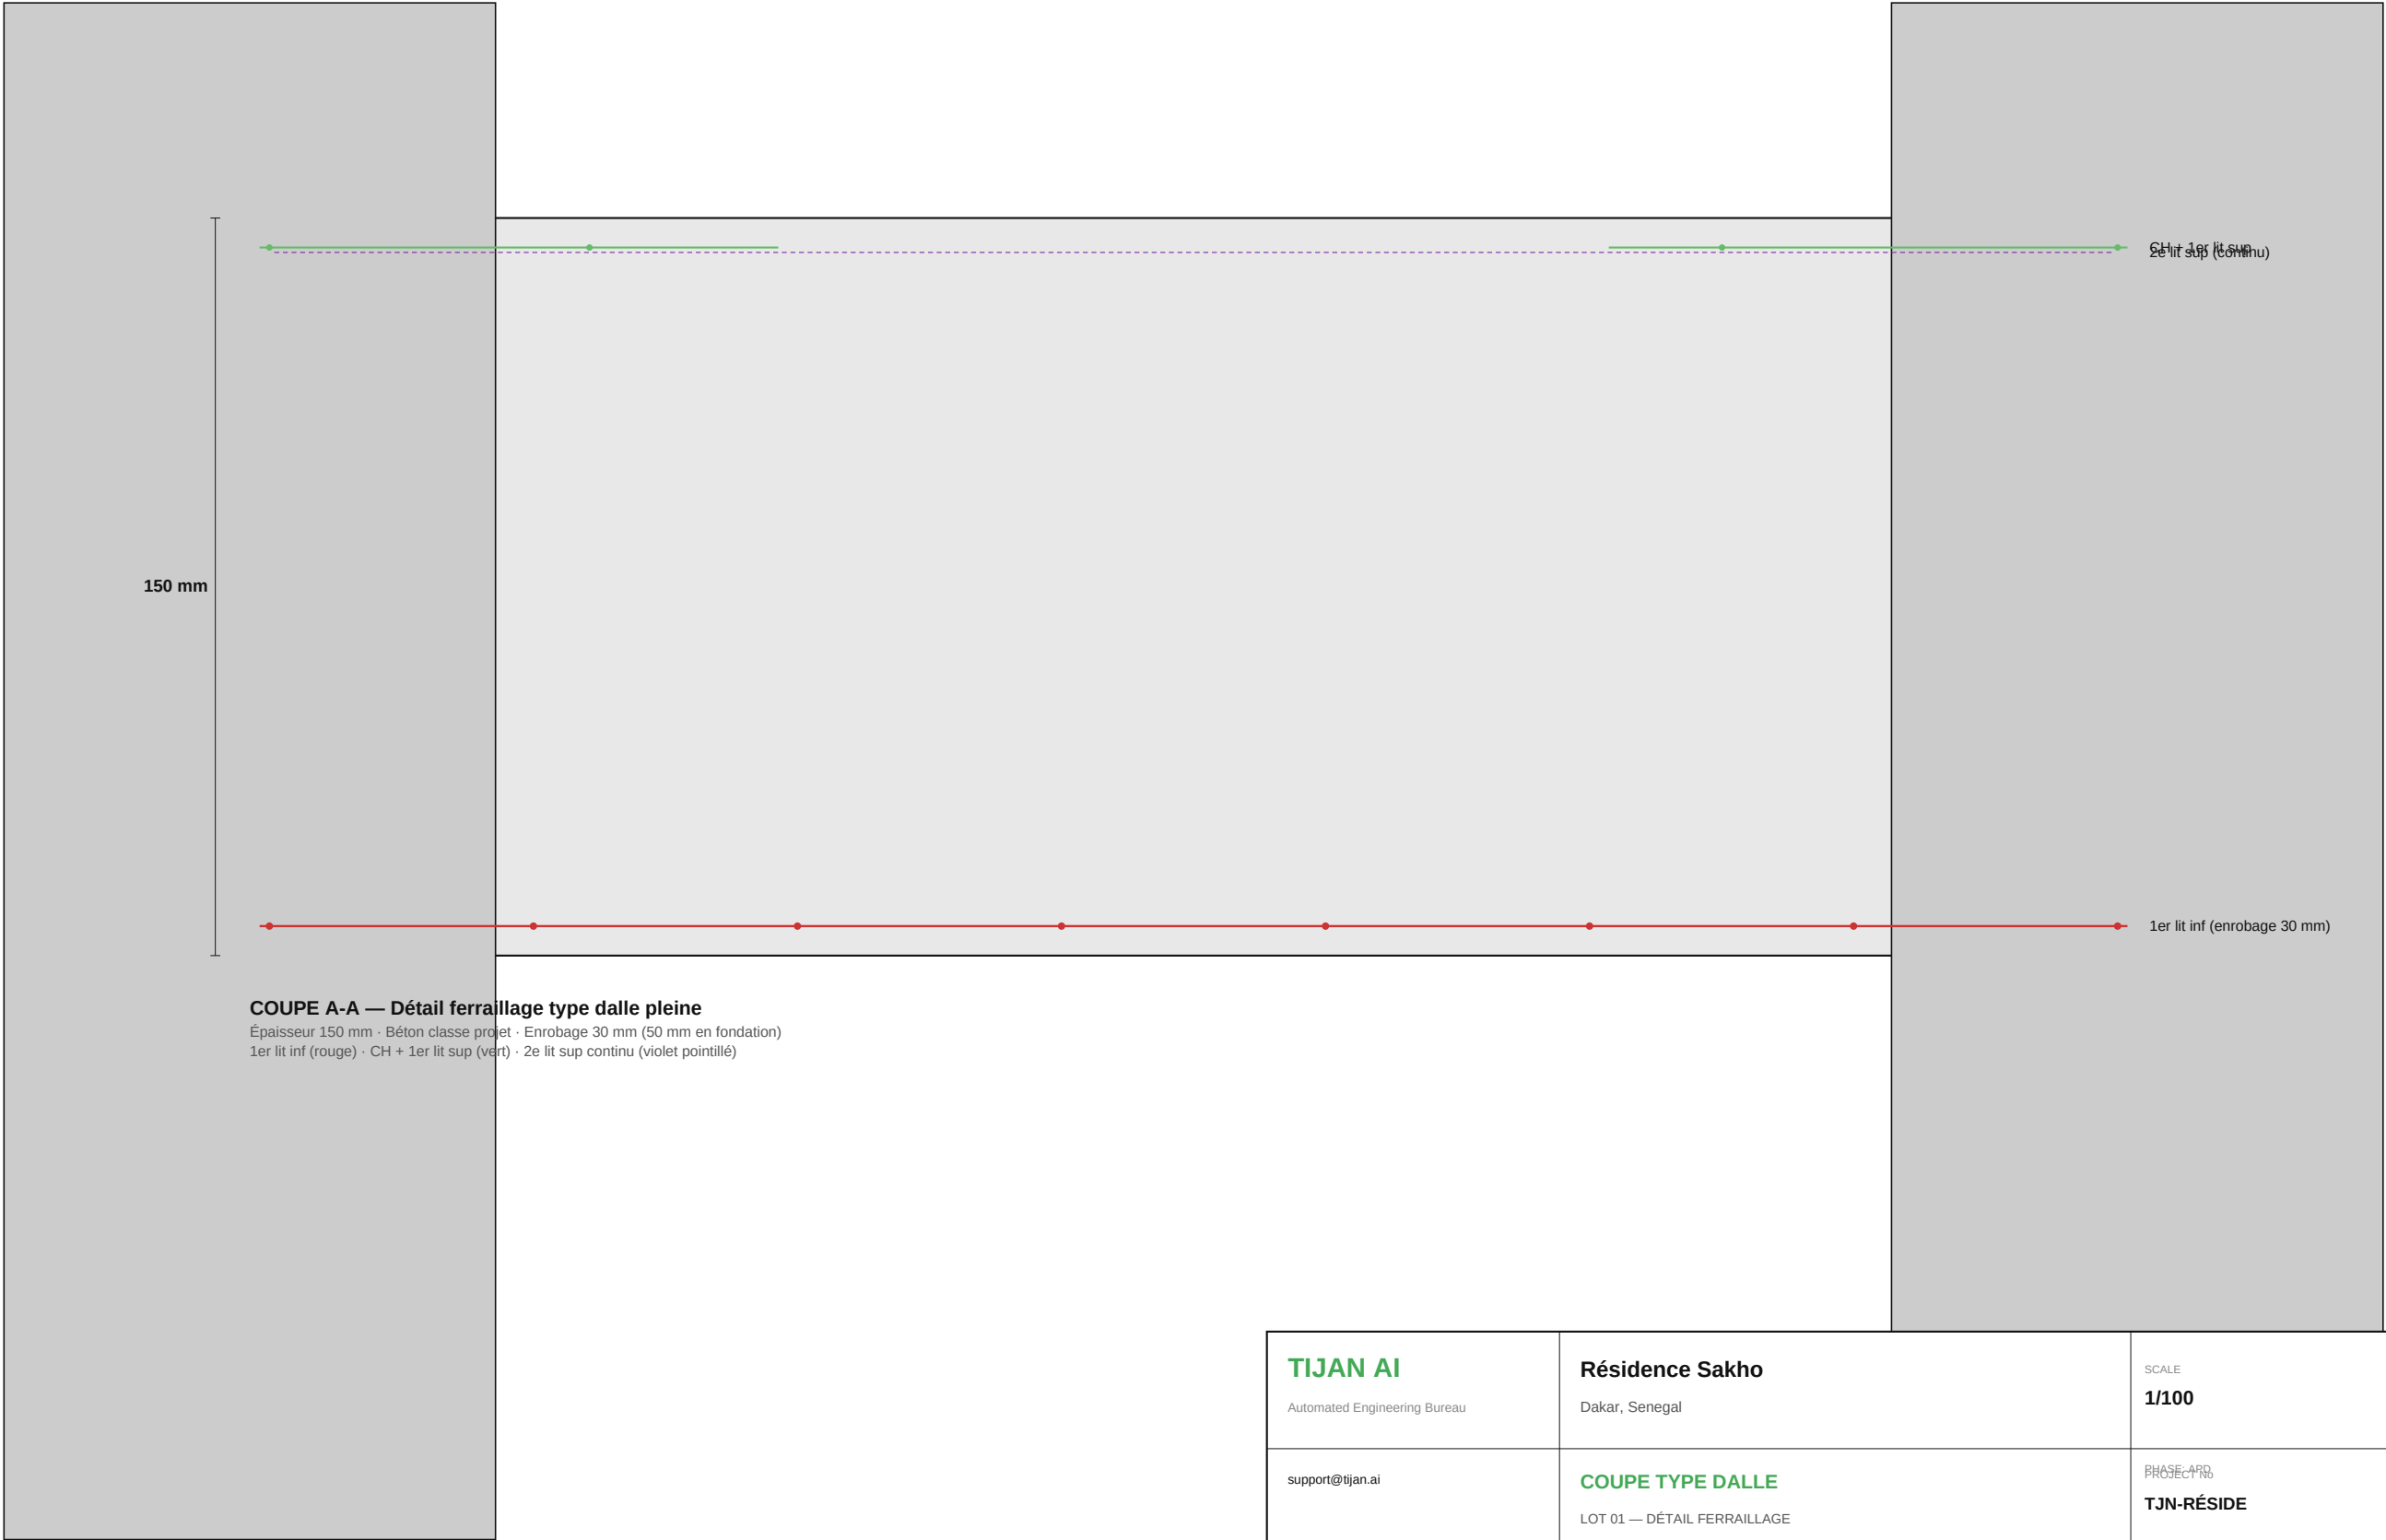


TIJAN AI Automated Engineering Bureau	Résidence Sakho Dakar, Senegal			SCALE 1/100
support@tijan.ai	COUPE TYPE DALLE LOT 01 — DÉTAIL FERRAILLAGE			PHASE TJN-RÉSIDE
www.tijan.ai 06/05/2026	DESIGNED TIJAN AI	DRAWN TIJAN AI	CHECKED TIJAN AI	DRAWING No TJN-STR-COUP-013 SHEET 13 / 17

PLAN DE FONDATIONS

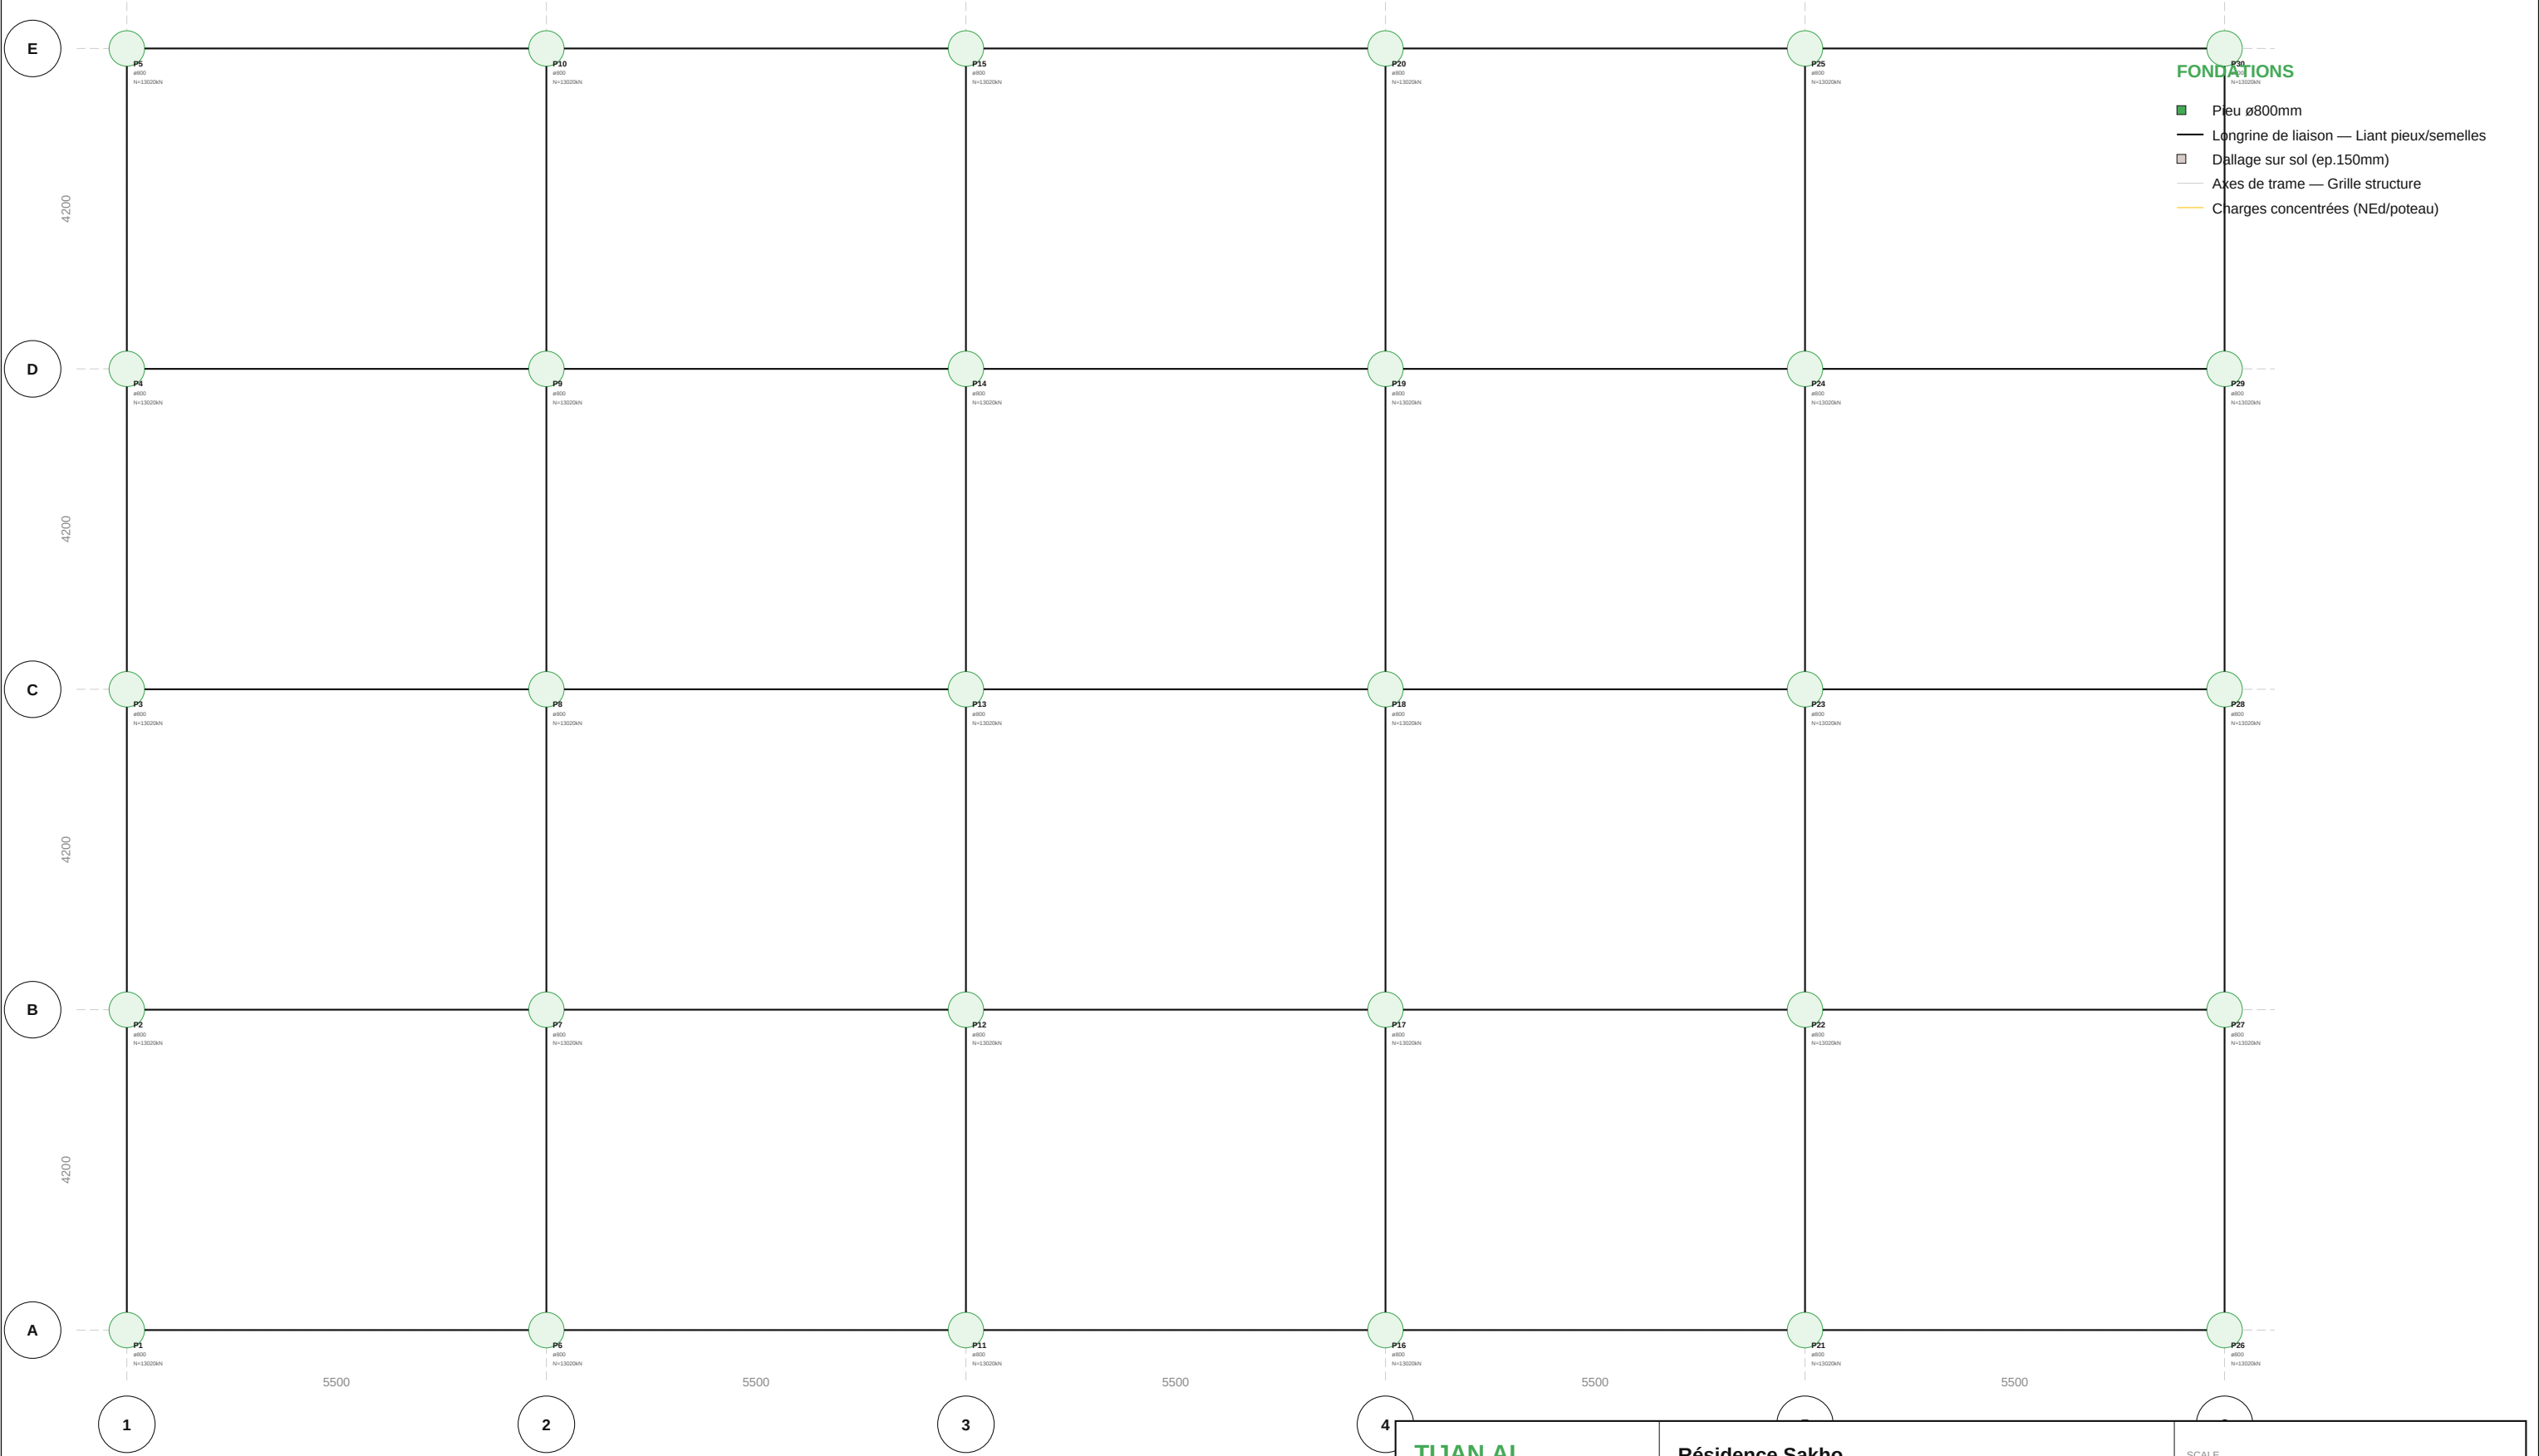

TIJAN AI Automated Engineering Bureau support@tijan.ai www.tijan.ai 06/05/2026	Résidence Sakho Dakar, Senegal			SCALE 1/100	
	FONDATIONS FONDATIONS STRUCTURE			PHASE: PRO TJN-RÉSIDE	
	DESIGNED TIJAN AI	DRAWN TIJAN AI	CHECKED TIJAN AI	DRAWING No PL-014	SHEET 14 / 17

COUPE GÉNÉRALE

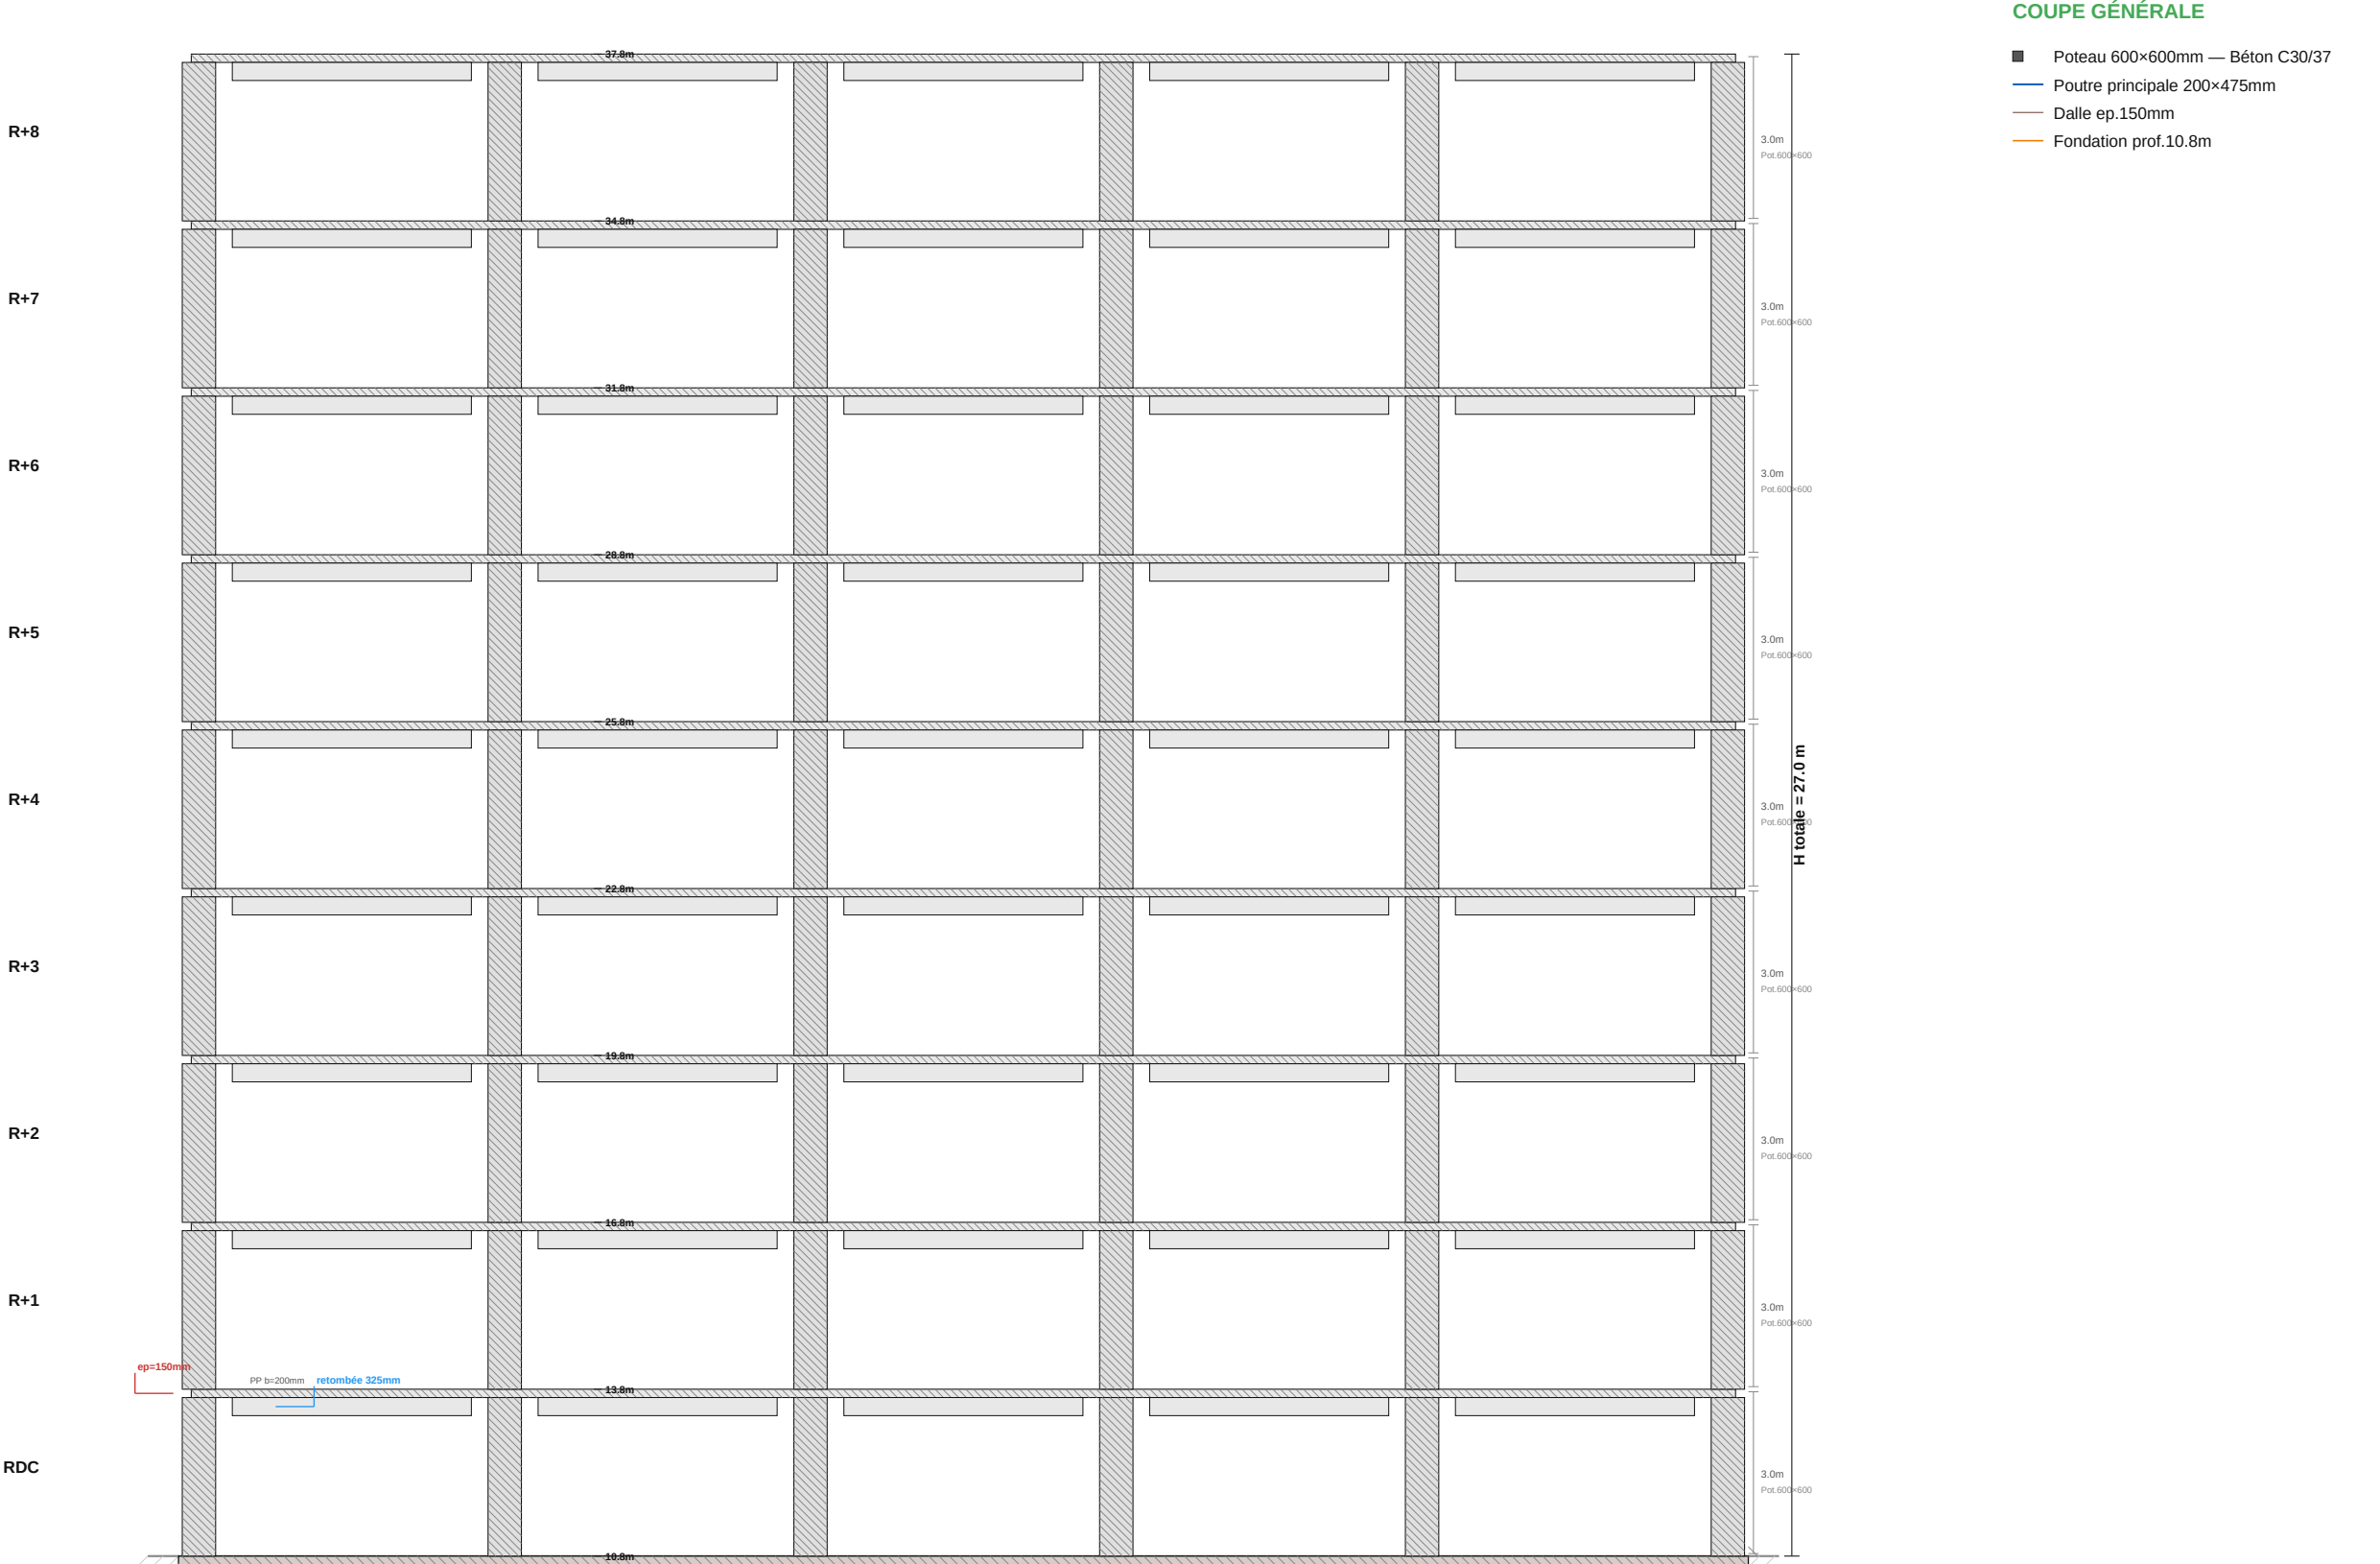


Béton C30/37 — Acier HA500
Dalle ep.150mm — PP 200×475mm

TIJAN AI Automated Engineering Bureau support@tijan.ai www.tijan.ai 06/05/2026	Résidence Sakho Dakar, Senegal			SCALE 1/200	
	COUPE GÉNÉRALE STRUCTURE BÉTON ARMÉ			PHASE: A/RD TJN-RÉSIDE	
	DESIGNED TIJAN AI	DRAWN TIJAN AI	CHECKED TIJAN AI	DRAWING No PL-015	SHEET 15 / 17


FERRAILLAGE POUTRE PRINCIPALE

PP1 — Section 200×475 mm — Portée 5.5 m

Pos.	Armature	l (m)
①	689HA 12 l=5.70	5.70
②	598HA 10 l=5.90	5.90
③	2HA 8 l=5.60	5.60
④	22HA 8 cadres	1.55

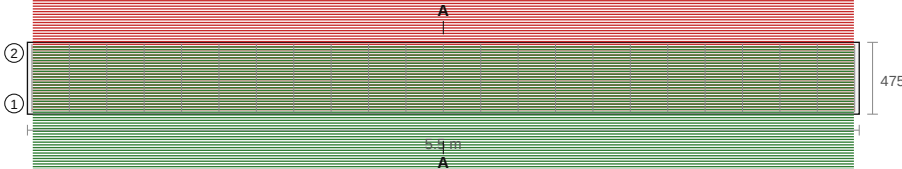

COUPE A-A

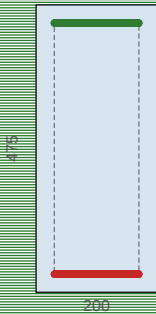

Section 200×475
1287 barres

CARACTÉRISTIQUES

Section	200 × 475 mm
As inf (travée)	7.80 cm ² — 689 barres
As sup (appuis)	4.70 cm ² — 598 barres
Étriers	HA8 / 250 mm
Portée	5.5 m
Béton	C30/37
Acier	HA 500
Enrobage	30 mm

Béton C30/37 — Acier HA 500 — Enrobage 30 mm — Ferraillage par orthogonalité

TIJAN AI

Engineering Intelligence

Date: 06/05/2026

Résidence Sakho

FERRAILLAGE POUTRE PRINCIPALE

Éch: 1/100


Dakar

Pl. 2/4

FERRAILLAGE POTEAUX

Coupes transversales et sections par niveau

COUPE POTEAU RDC

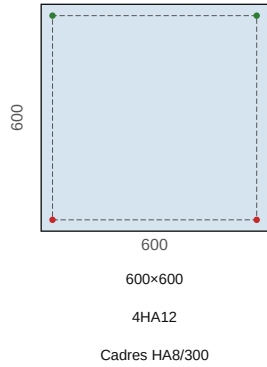

ÉLÉVATION SCHÉMATIQUE

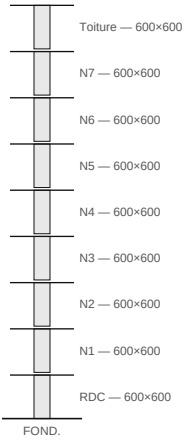


TABLEAU DES SECTIONS PAR NIVEAU

Niveau	NEd (kN)	Section	Armatures	Cadres	ρ (%)
RDC	2604	600×600	4HA12	HA8/300	0.13
N1	2315	600×600	4HA12	HA8/300	0.13
N2	2025	600×600	4HA12	HA8/300	0.13
N3	1736	600×600	4HA12	HA8/300	0.13
N4	1447	600×600	4HA12	HA8/300	0.13
N5	1157	600×600	4HA12	HA8/300	0.13
N6	868	600×600	4HA12	HA8/300	0.13
N7	579	600×600	4HA12	HA8/300	0.13
Toiture	289	600×600	4HA12	HA8/300	0.13

TIJAN AI

Engineering Intelligence

Date: 06/05/2026

Résidence Sakho

FERRAILLAGE POTEAUX

Éch: 1/100

Dakar

Pl. 3/4