

TIJAN AI

Bureau d'Études Automatisé

DOSSIER BIM UNIFIÉ

Plans d'exécution — Tous corps d'état

Projet: Résidence Papa Oumar Sakho

Ville: Dakar

Réf.: 1711

Niveaux: 10

Béton: C30/37

Acier: HA500

133

pages

10

niveaux

Contenu du dossier

2556

équipements

2659

segments

59613

conflits

SOMMAIRE

001 ARC — Architecture

Sous-Sol	R+2	41
RDC	R+3	42
R+1	R+4	43
R+2	R+5	44
R+3	R+6	45
R+4	R+7	46
R+5		
R+6		
R+7		
R+8 Terrasse		

200 STR — Coffrage

Sous-Sol	R+4	51
RDC	R+5	52
R+1	R+6	53
R+2	R+7	54
R+3		
R+4		
R+5		
R+6		
R+7		
R+8 Terrasse		

410 PLU — Eau Froide (EF)

R+1	R+5	61
R+2	R+6	62
R+3	R+7	63
R+4	R+8 Terrasse	64

410 PLU — Eau Chaude (EC)

Sous-Sol	R+4	69
RDC	R+5	70
R+1	R+6	71
R+2	R+7	72
R+3		
R+4		
R+5		
R+6		
R+7		
R+8 Terrasse		

410 PLU — Eaux Usées (EU)

R+1		
-----	--	--

413 HVC — Climatisation (CLIM)

RDC	47
R+1	48
R+2	49
R+3	50
R+4	51
R+5	52
R+6	53
R+7	54

413 HVC — Ventilation (VMC)

Sous-Sol	17
RDC	18
R+1	19
R+2	20
R+3	21
R+4	22
R+5	61
R+6	62
R+7	63
R+8 Terrasse	64

400 FIF — Extinction (SPK)


RDC	27
R+1	28
R+2	29
R+3	68
R+4	69
R+5	70
R+6	71
R+7	72

400 FIF — Détection (DET)

Sous-Sol	73
RDC	74
R+1	75
R+2	76
R+3	39
R+4	
R+5	

Rapport de Co

TIJAN AI Bureau d'Études Automatisé	Résidence Papa Oumar Sakho Dakar, Senegal	Éch: 1/100 Pl. 2/133
	Sommaire	
Date: 06/05/2026	Réf: 1711	BIM vARC-002 Phase: APD

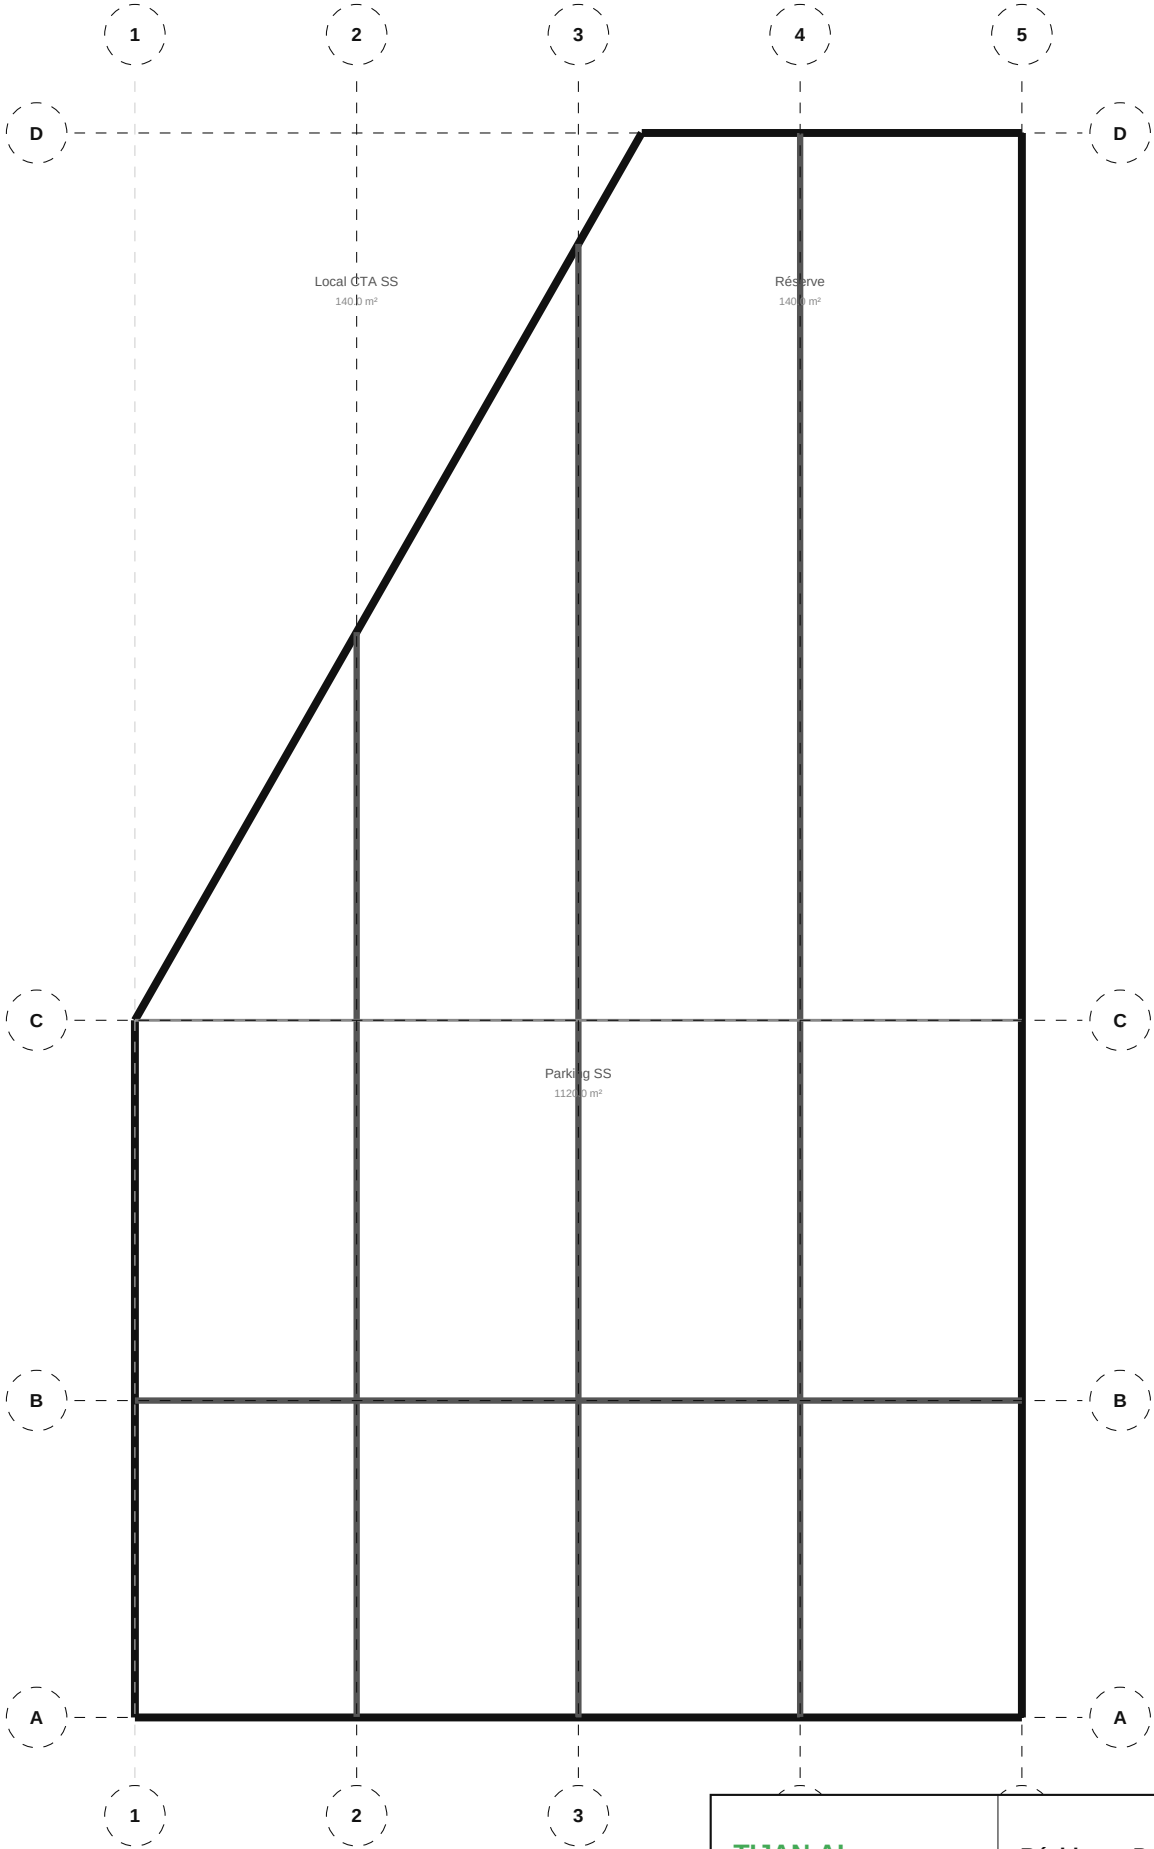

TIJAN AI Bureau d'Études Automatisé	Résidence Papa Oumar Sakho Dakar, Senegal	Éch: 1/100 Pl. 3/133
	001 ARC — Architecture — Sous-Sol	
Date: 06/05/2026	Réf: 1711	BIM vARC-003 Phase: APD

1

2

3

4

5

Local Technique
35.0 m²

Loge Gardien
35.0 m²

Cour RDC
70.0 m²

B

B

Escalier RDC
8.0 m²

Commerce 1
100.0 m²

Commerce 2
100.0 m²

Hall d'entrée
64.0 m²

A

A

1

2

3

4

5

TIJAN AI

Bureau d'Études Automatisé

Résidence Papa Oumar Sakho

Dakar, Senegal

Éch: 1/100

Pl. 4/133

001 ARC — Architecture — RDC

Date: 06/05/2026

Réf: 1711

BIM vARC-004

Phase: APD

TIJAN AI

Bureau d'Études Automatisé

Résidence Papa Oumar Sakho

Dakar, Senegal

Éch: 1/100

Pl. 5/133


001 ARC — Architecture — R+1

Date: 06/05/2026

Réf: 1711

BIM vARC-005

Phase: APD

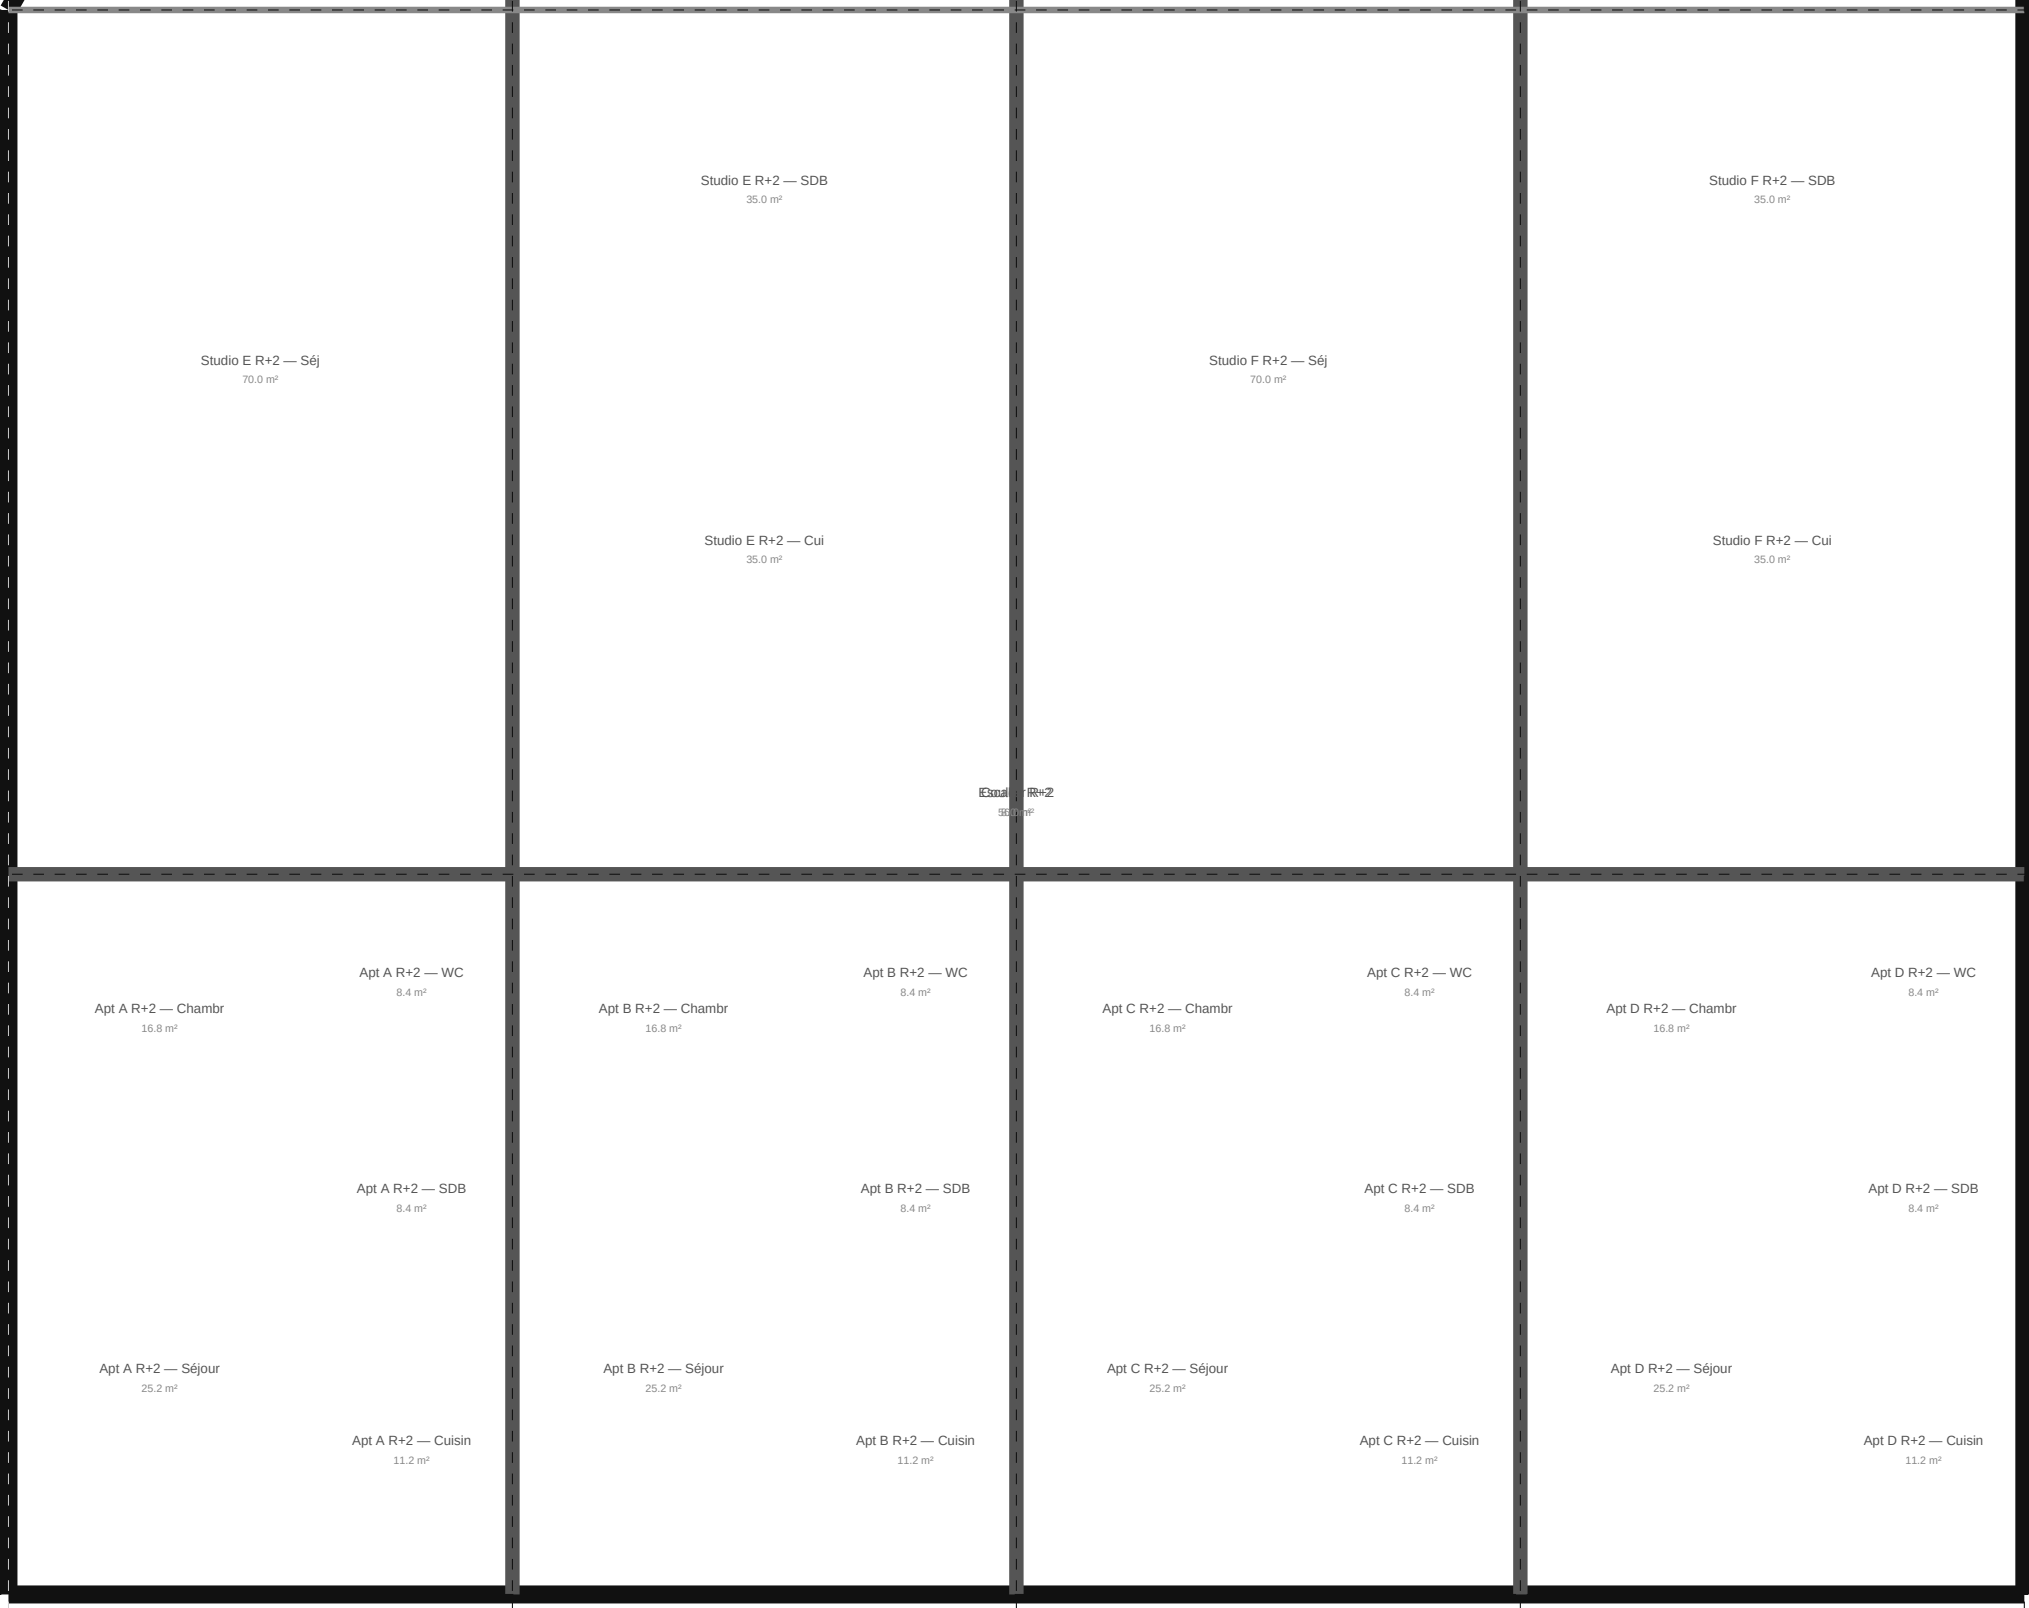

Studio E R+3 — Séj
70.0 m²

Studio E R+3 — SDB
35.0 m²

Studio E R+3 — Cui
35.0 m²

Studio F R+3 — Séj
70.0 m²

Studio F R+3 — SDB
35.0 m²

Studio F R+3 — Cui
35.0 m²

Apt A R+3 — Chambr
16.8 m²

Apt A R+3 — WC
8.4 m²

Apt A R+3 — SDB
8.4 m²

Apt A R+3 — Séjour
25.2 m²

Apt A R+3 — Cuisin
11.2 m²

Apt B R+3 — Chambr
16.8 m²

Apt B R+3 — WC
8.4 m²

Apt B R+3 — SDB
8.4 m²

Apt B R+3 — Séjour
25.2 m²

Apt B R+3 — Cuisin
11.2 m²

Apt C R+3 — Chambr
16.8 m²

Apt C R+3 — WC
8.4 m²

Apt C R+3 — SDB
8.4 m²

Apt C R+3 — Séjour
25.2 m²

Apt C R+3 — Cuisin
11.2 m²

Apt D R+3 — Chambr
16.8 m²

Apt D R+3 — WC
8.4 m²


Apt D R+3 — SDB
8.4 m²

Apt D R+3 — Séjour
25.2 m²

Apt D R+3 — Cuisin
11.2 m²





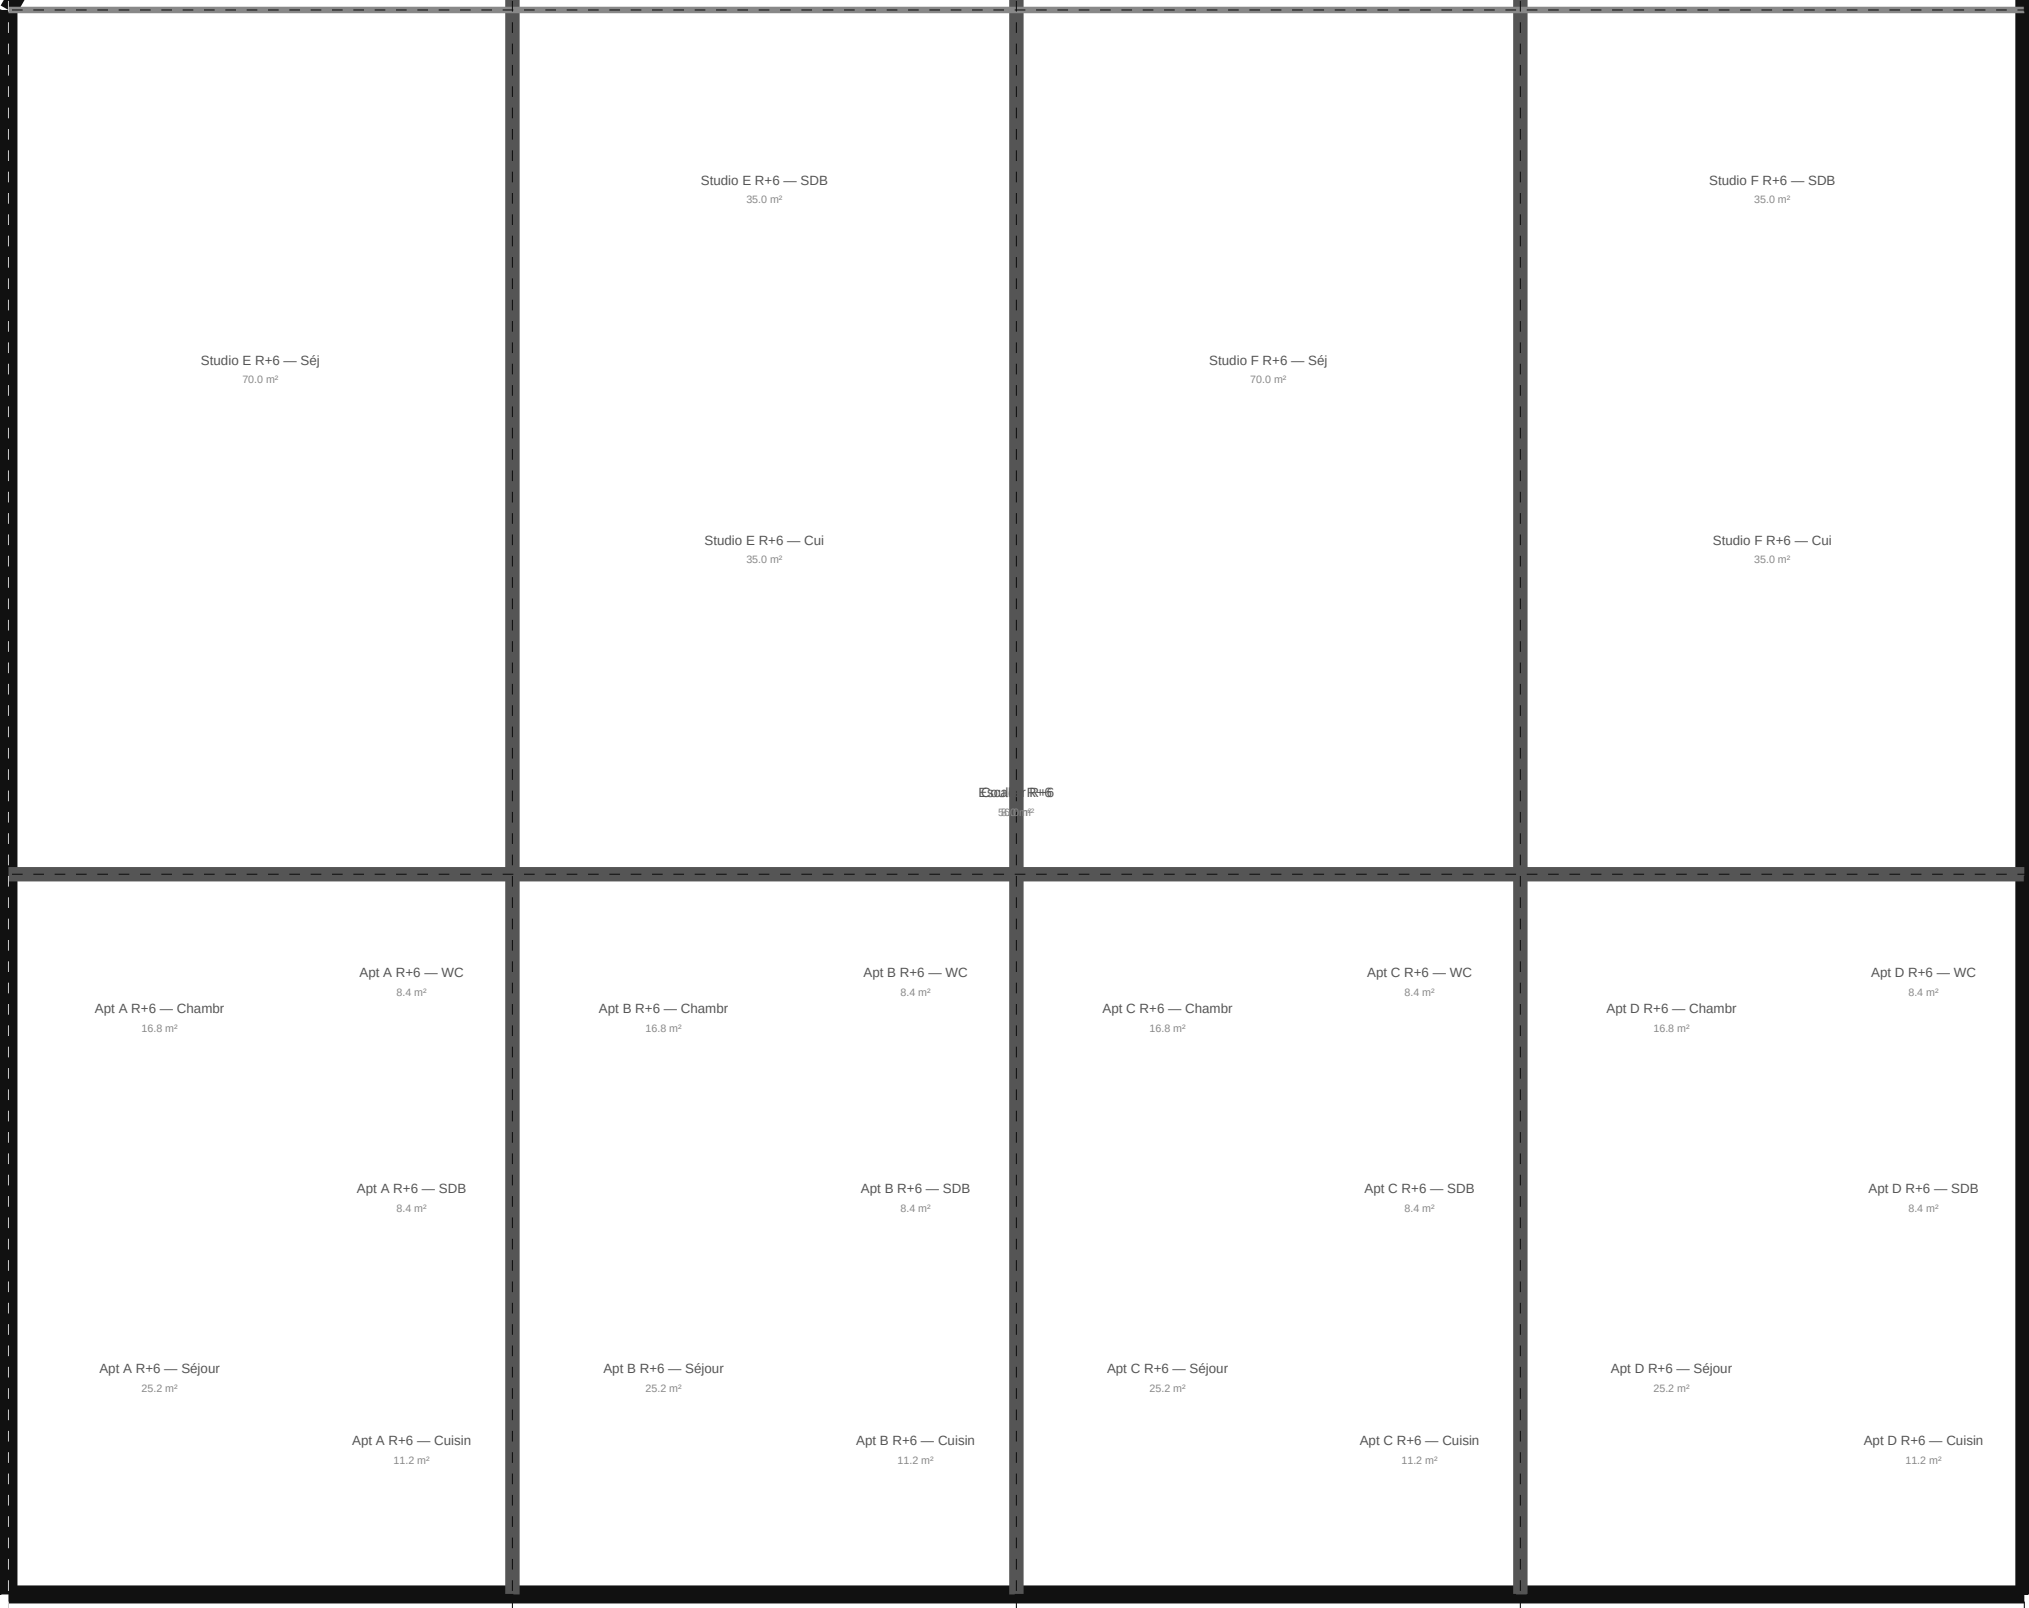

Studio E R+7 — SDB
35.0 m²

Studio E R+7 — Séj
70.0 m²

Studio E R+7 — Cui
35.0 m²

Studio F R+7 — SDB
35.0 m²

Studio F R+7 — Séj
70.0 m²

Studio F R+7 — Cui
35.0 m²

Escalier R+7
35.0 m²

Apt A R+7 — Chambr
16.8 m²

Apt A R+7 — WC
8.4 m²

Apt A R+7 — SDB
8.4 m²

Apt A R+7 — Séjour
25.2 m²

Apt A R+7 — Cuisin
11.2 m²

Apt B R+7 — Chambr
16.8 m²

Apt B R+7 — WC
8.4 m²

Apt B R+7 — SDB
8.4 m²

Apt B R+7 — Séjour
25.2 m²

Apt B R+7 — Cuisin
11.2 m²

Apt C R+7 — Chambr
16.8 m²

Apt C R+7 — WC
8.4 m²

Apt C R+7 — SDB
8.4 m²

Apt C R+7 — Séjour
25.2 m²

Apt C R+7 — Cuisin
11.2 m²


Apt D R+7 — Chambr
16.8 m²

Apt D R+7 — WC
8.4 m²


Apt D R+7 — SDB
8.4 m²

Apt D R+7 — Séjour
25.2 m²


Apt D R+7 — Cuisin
11.2 m²

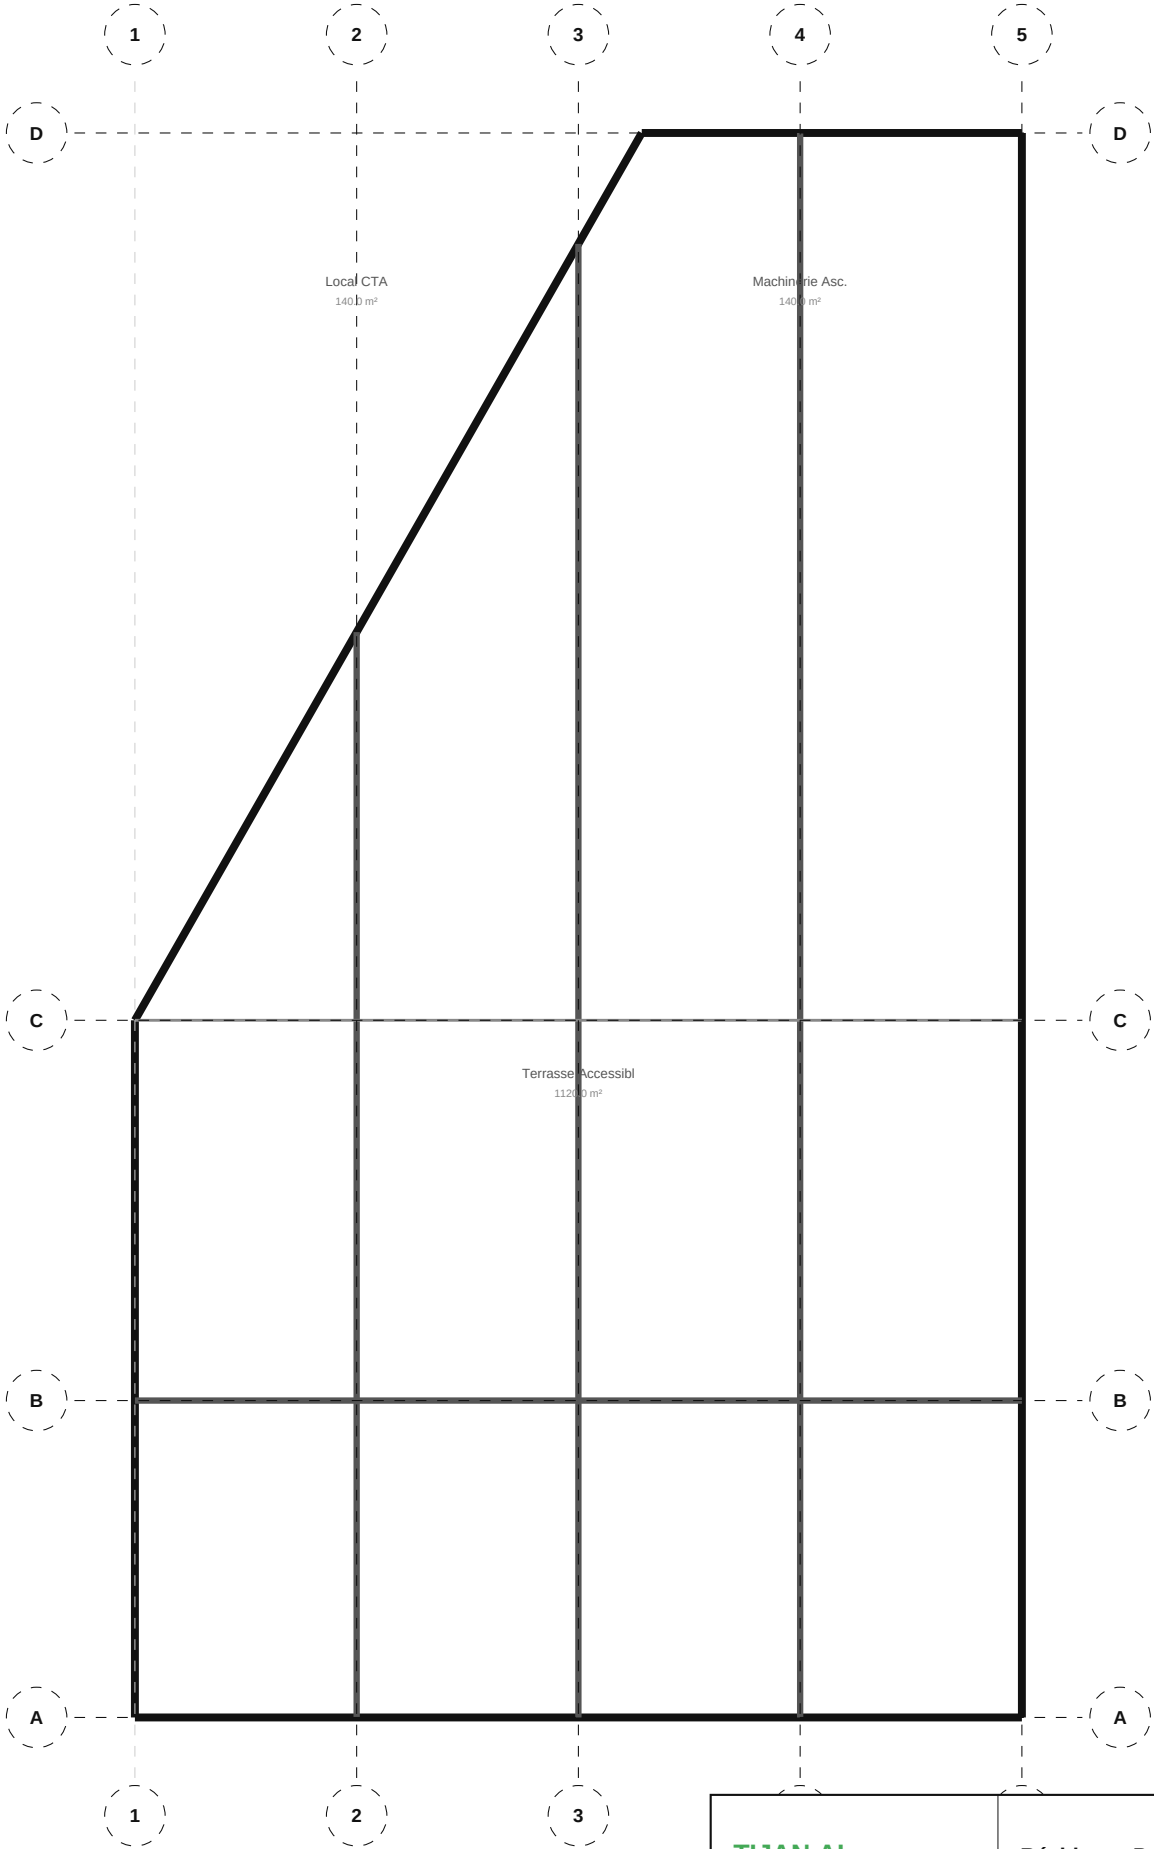


TIJAN AI Bureau d'Études Automatisé	Résidence Papa Oumar Sakho Dakar, Senegal	Éch: 1/100 Pl. 12/133
	001 ARC — Architecture — R+8 Terrasse	
Date: 06/05/2026	Réf: 1711	BIM vARC-012 Phase: APD

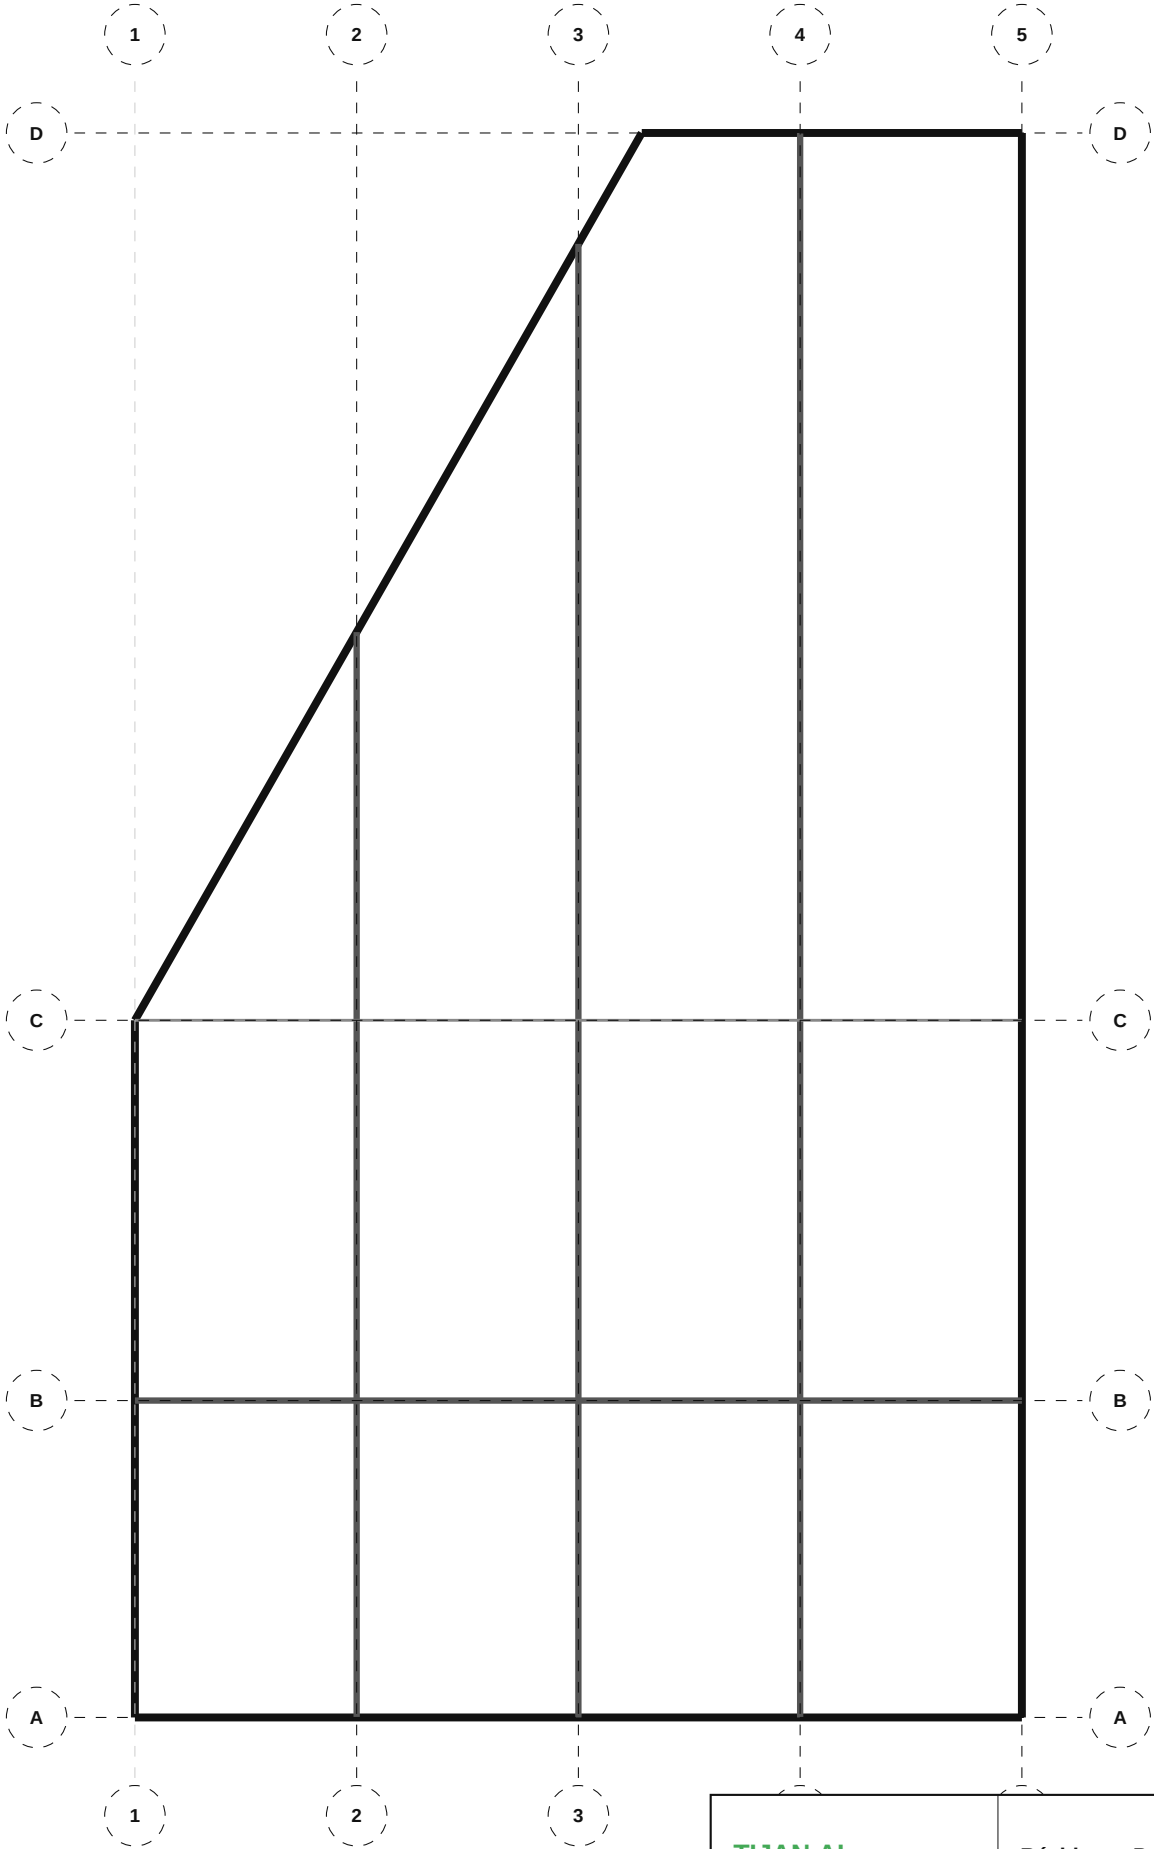

TIJAN AI Bureau d'Études Automatisé	Résidence Papa Oumar Sakho Dakar, Senegal	Éch: 1/100 Pl. 13/133
	200 STR — Coffrage — Sous-Sol	
Date: 06/05/2026	Réf: 1711	BIM vSTR-013 Phase: APD

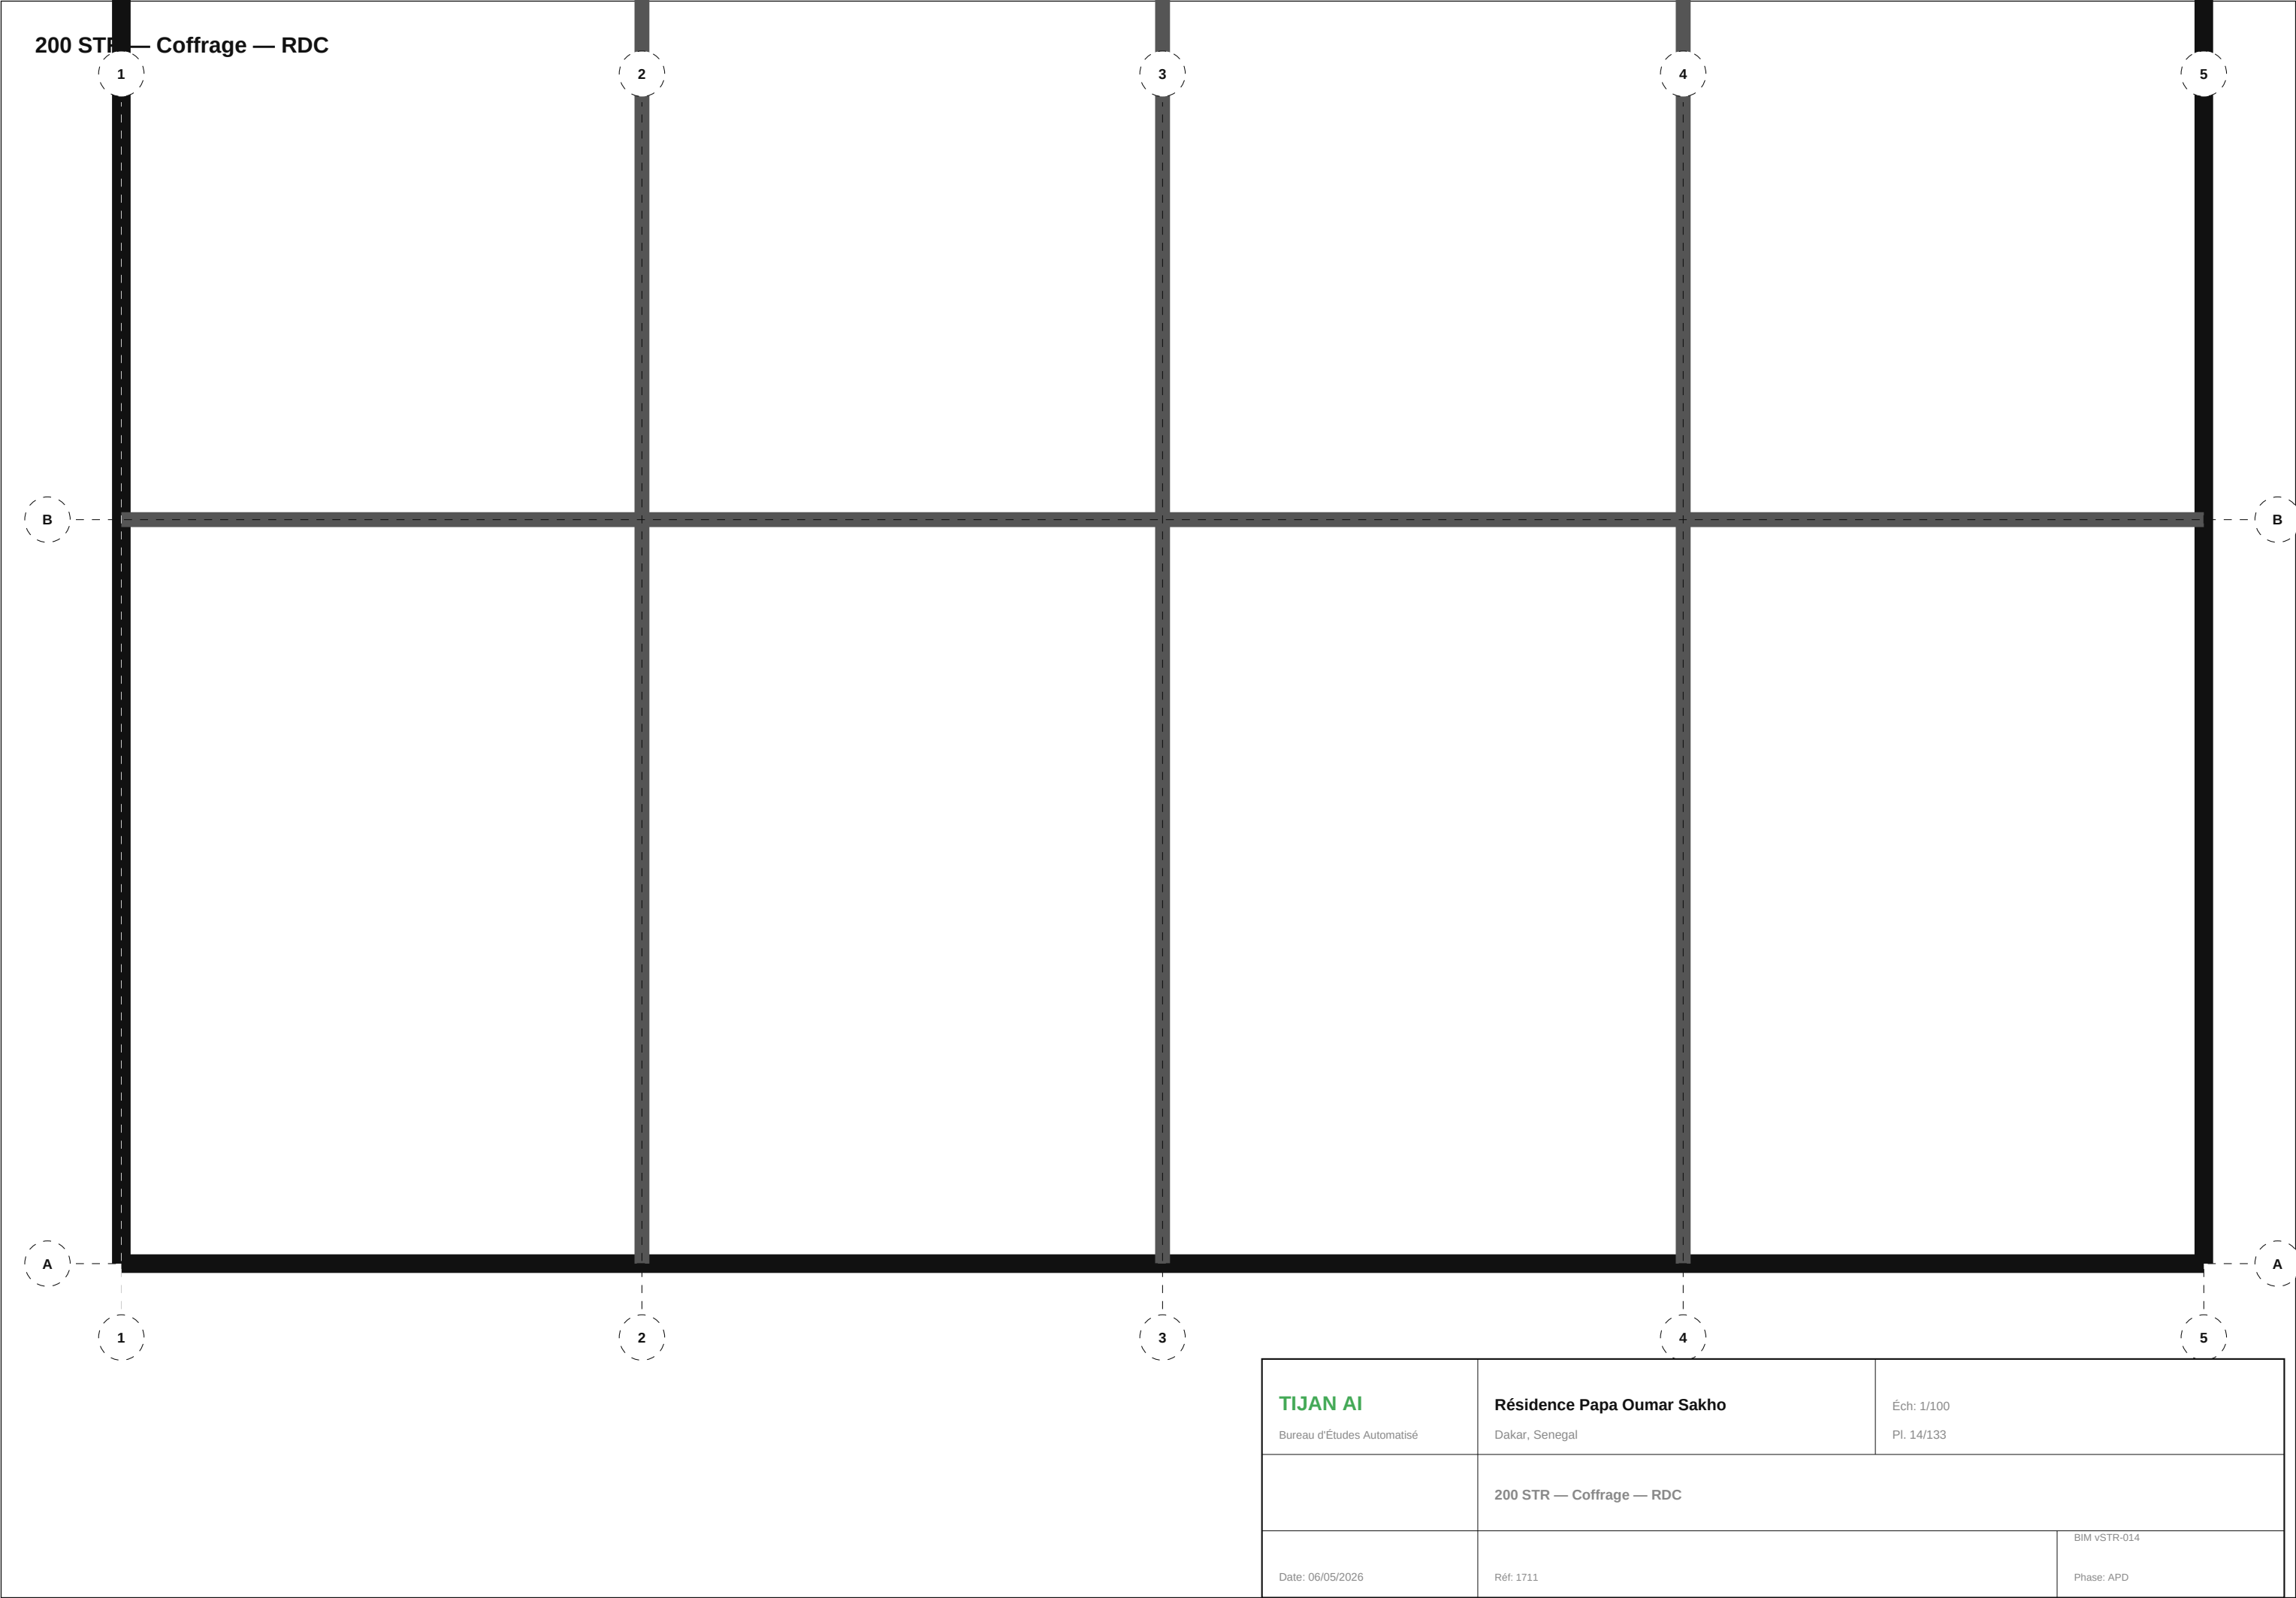

200 STR — Coffrage — R+1

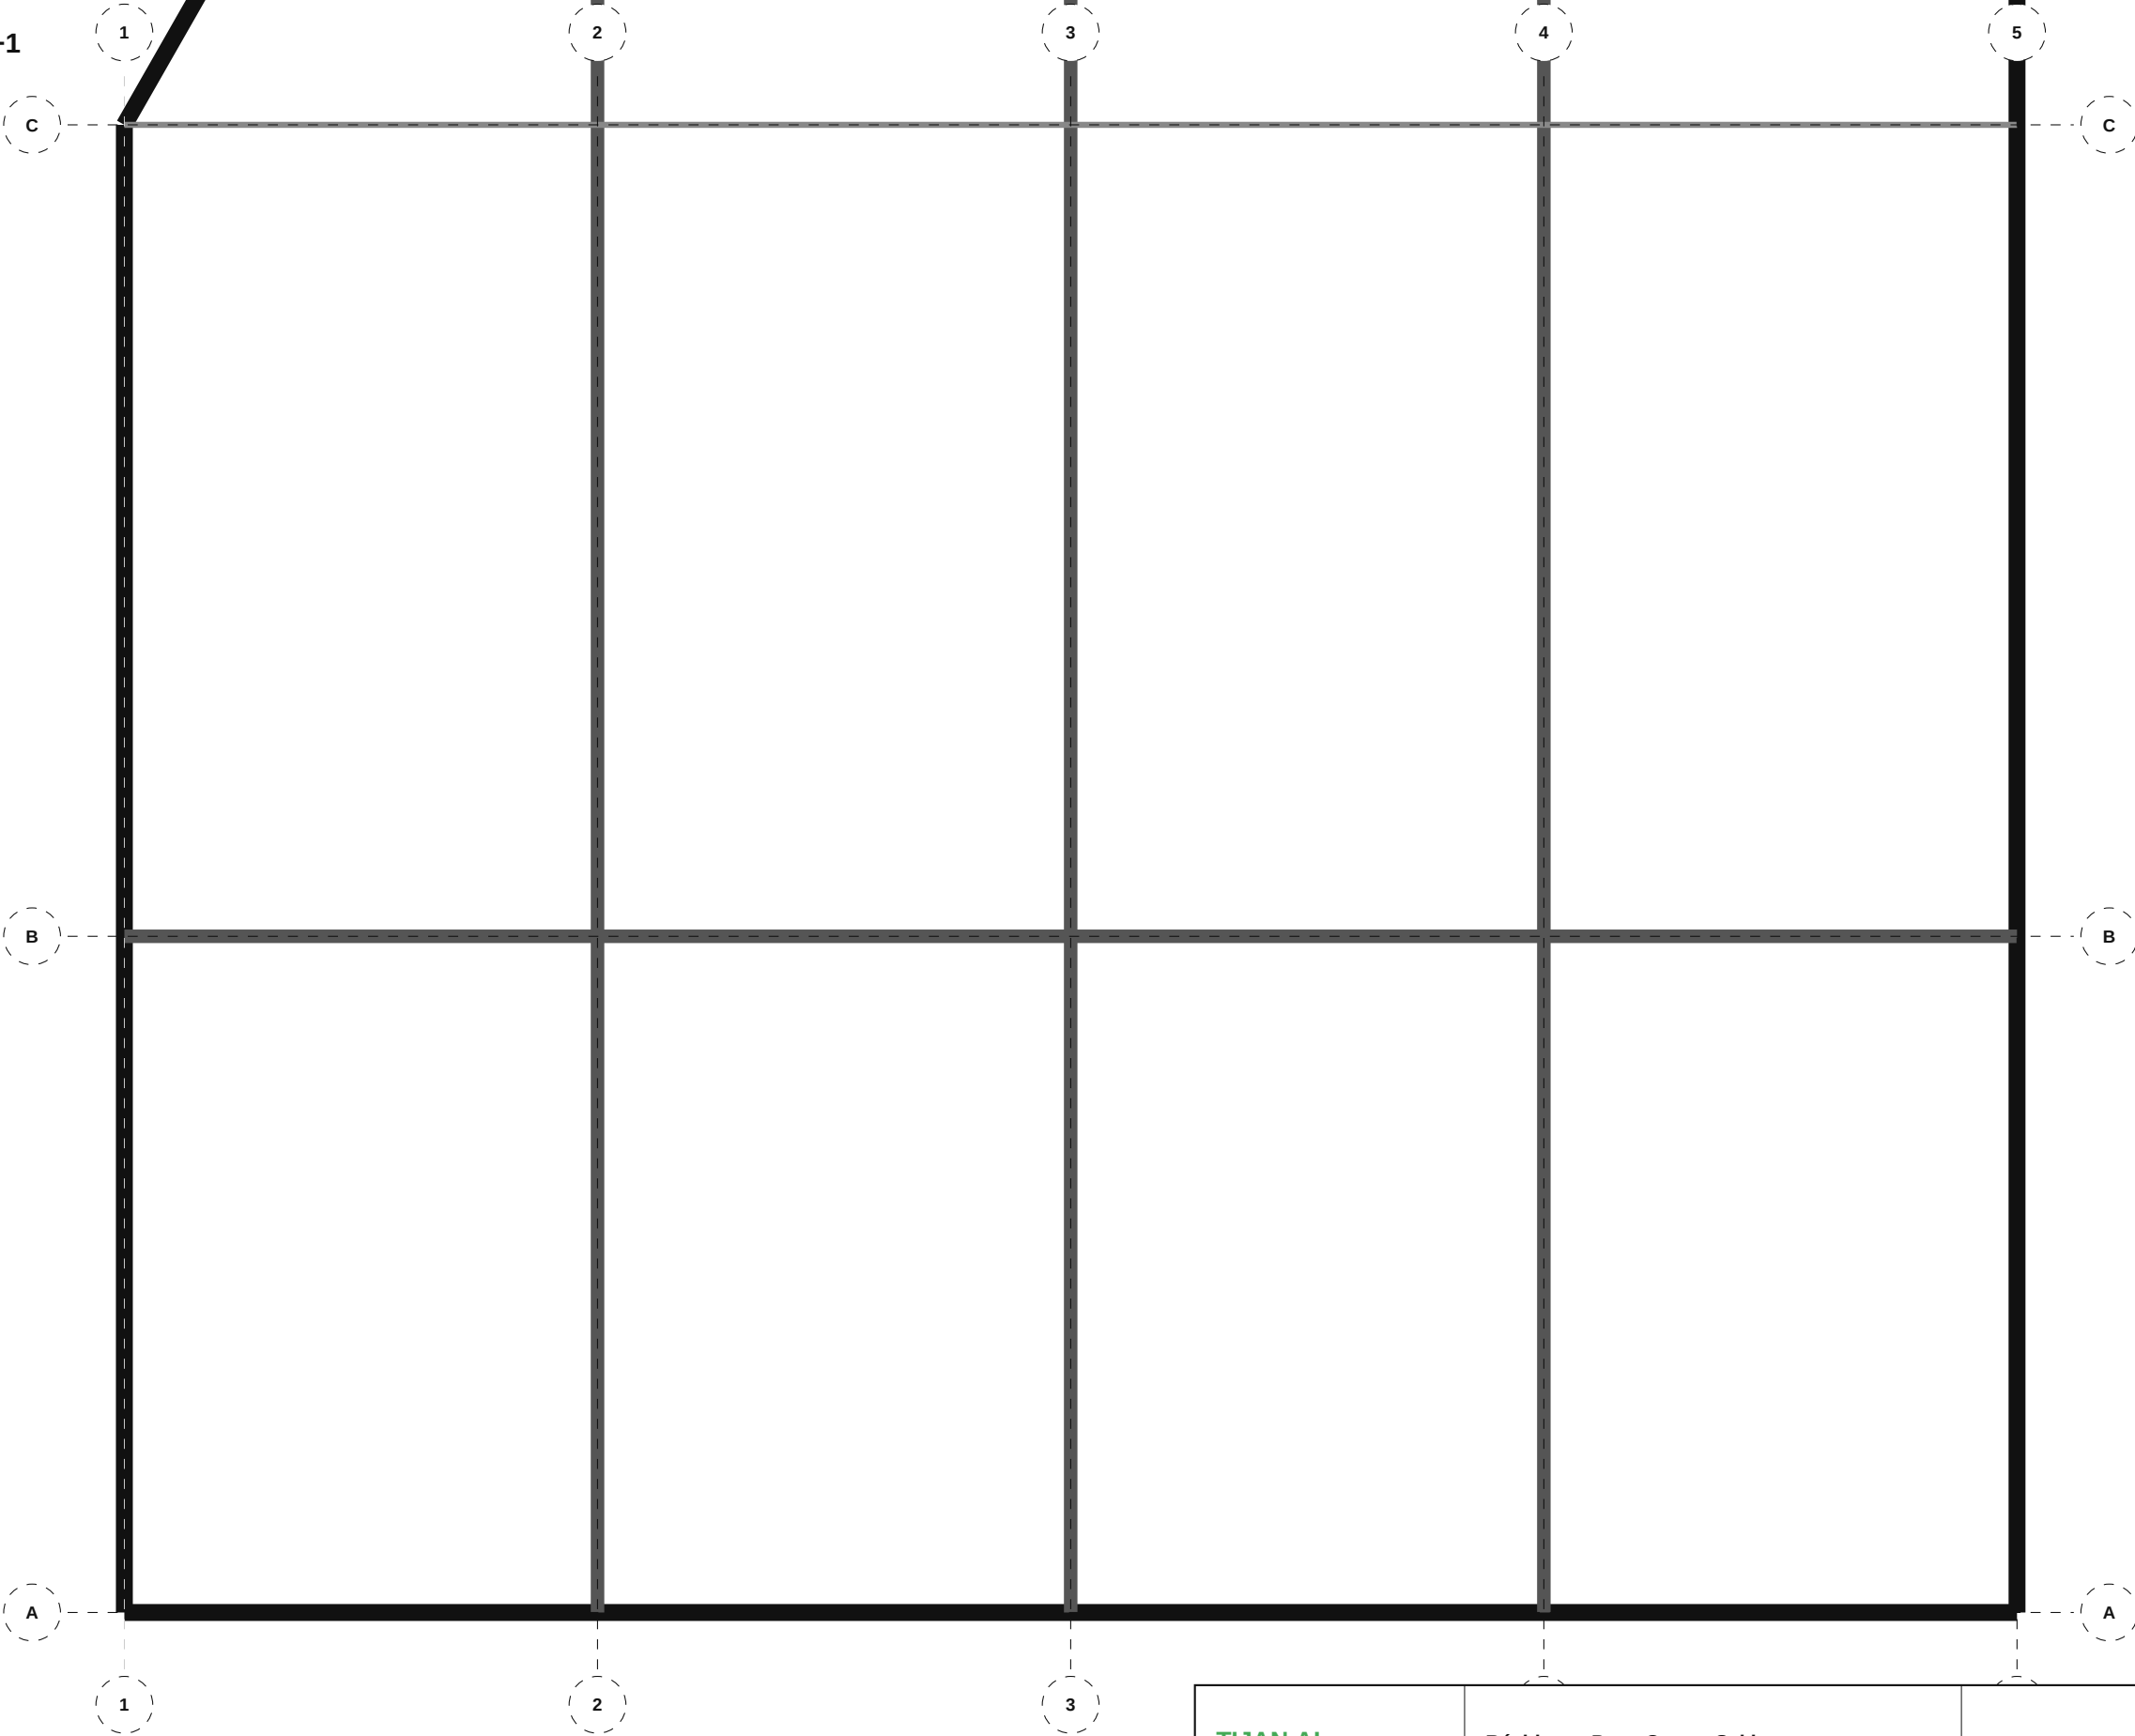

TIJAN AI

Bureau d'Études Automatisé

Résidence Papa Oumar Sakho

Dakar, Senegal

Éch: 1/100

Pl. 15/133


200 STR — Coffrage — R+1

Date: 06/05/2026

Réf: 1711


BIM vSTR-015

Phase: APD

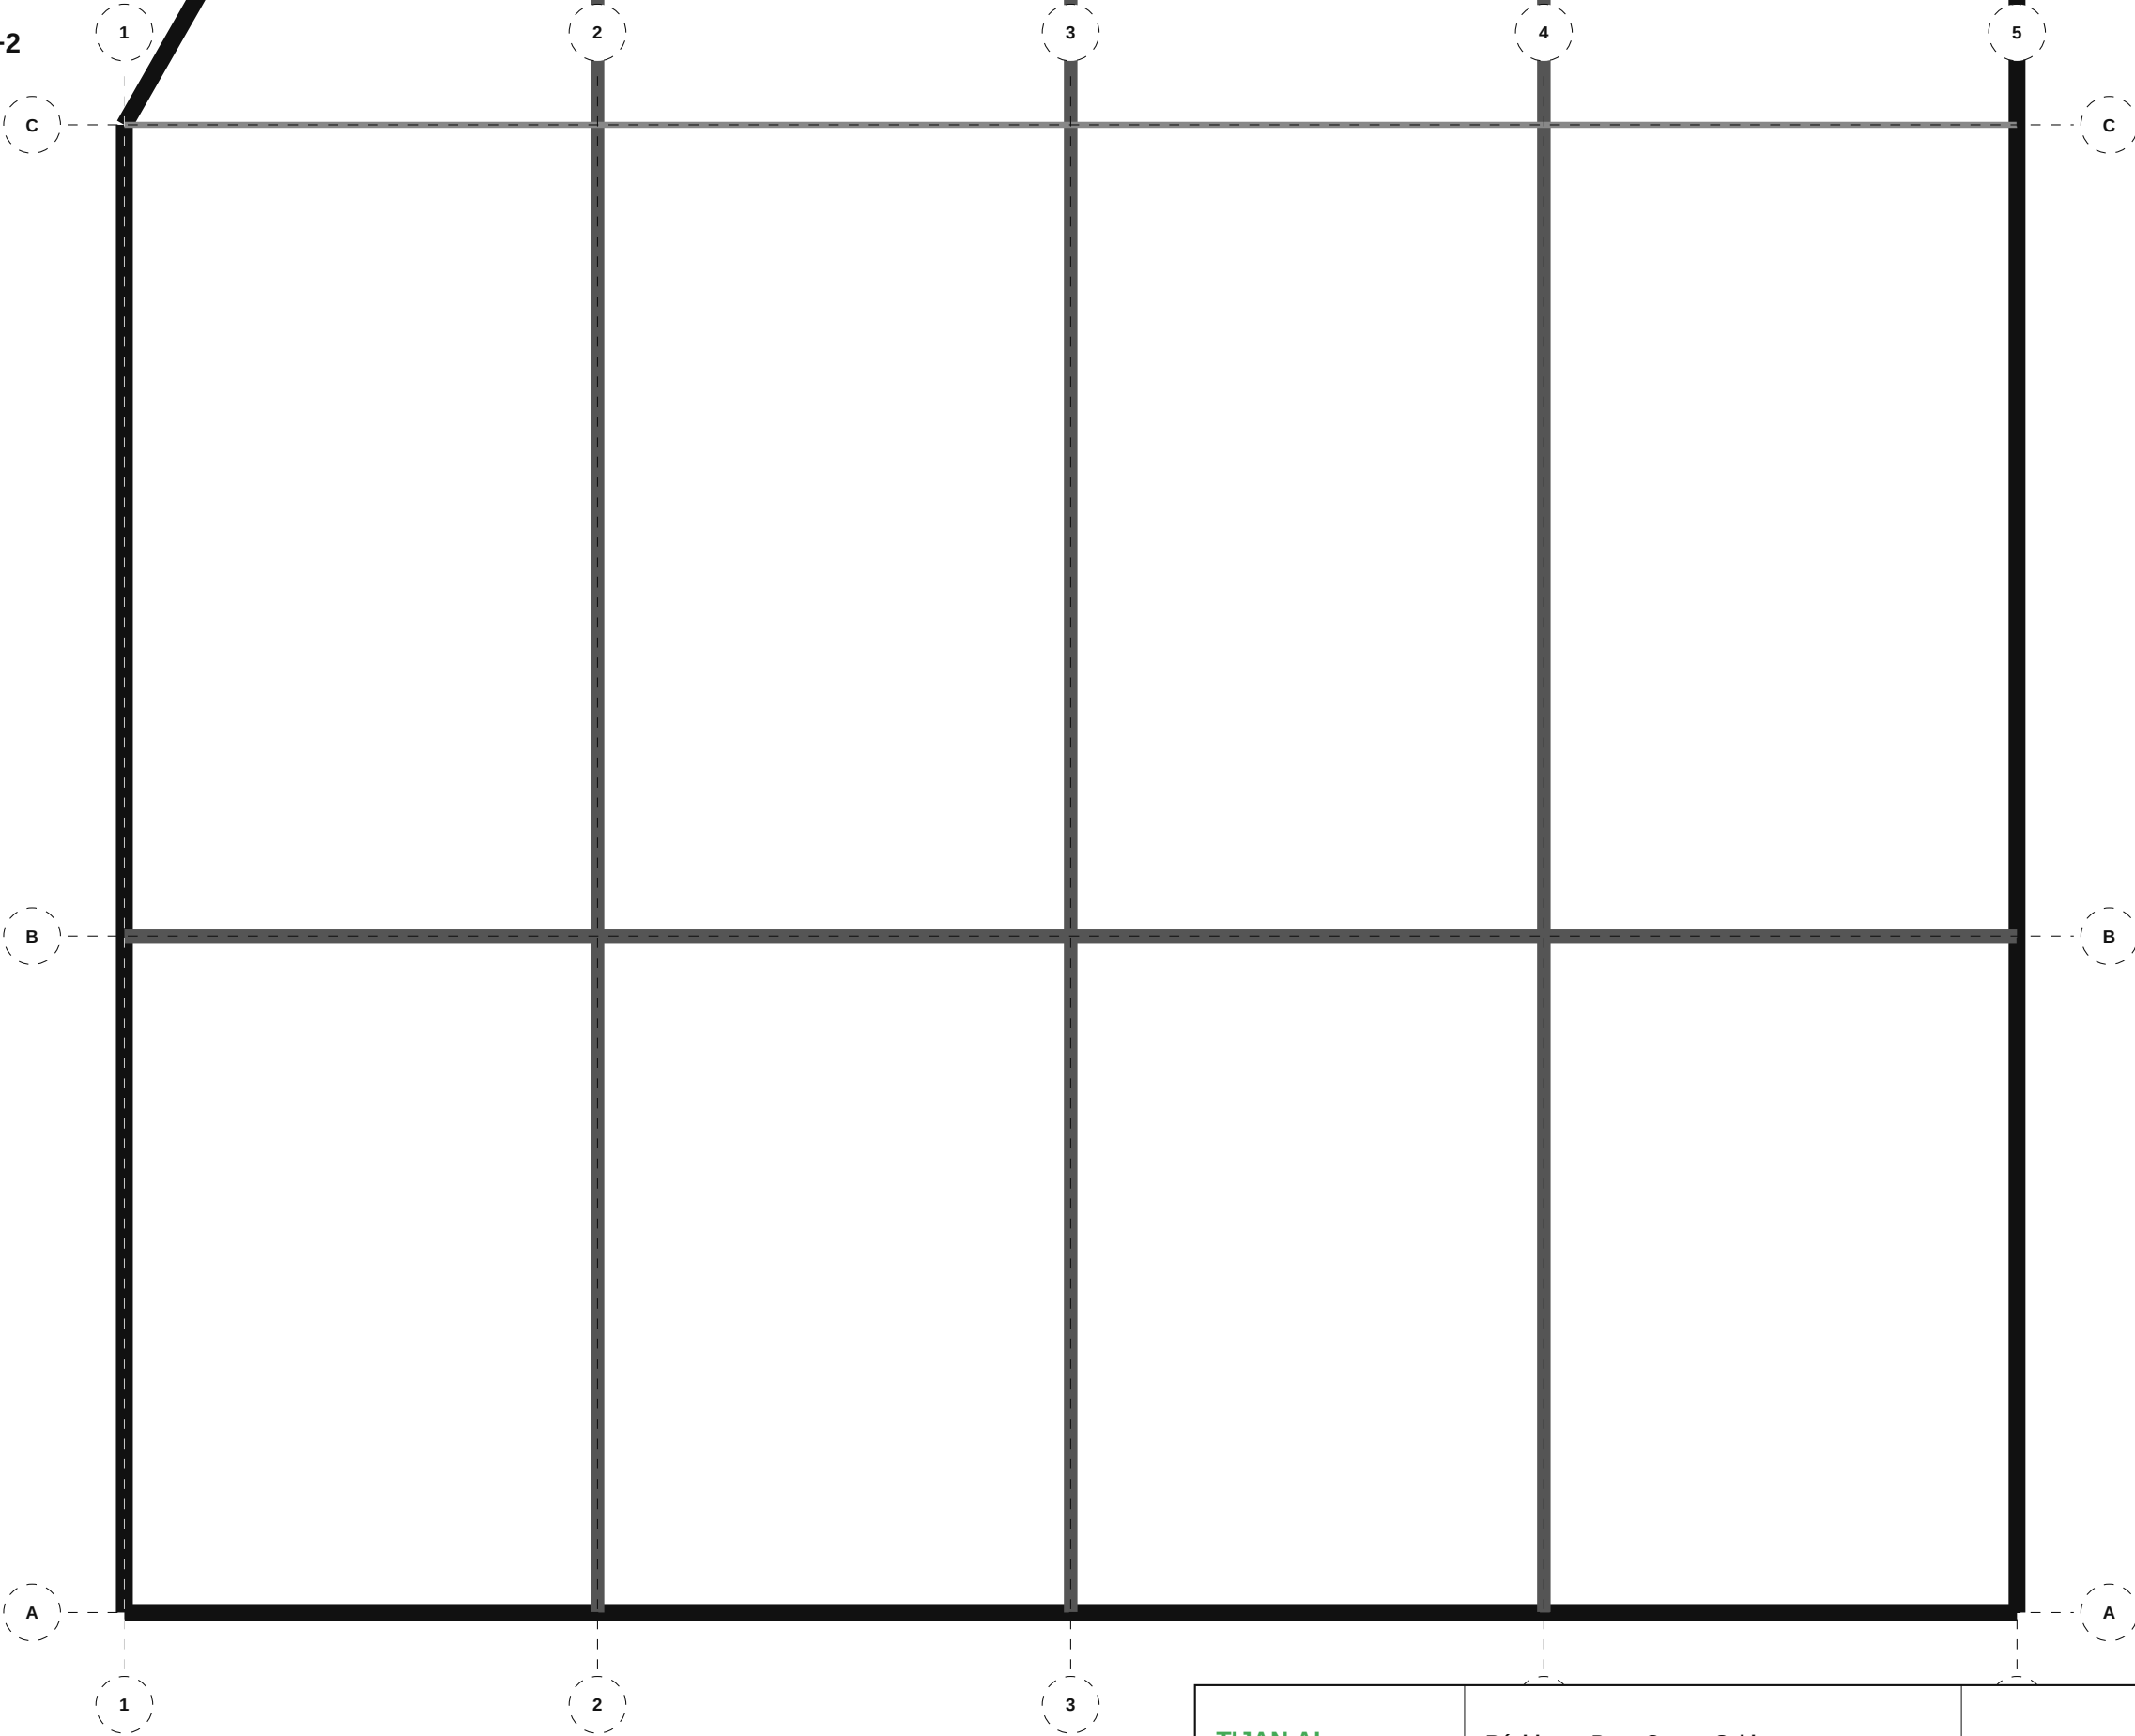


TIJAN AI Bureau d'Études Automatisé	Résidence Papa Oumar Sakho Dakar, Senegal	Éch: 1/100 Pl. 16/133
	200 STR — Coffrage — R+2	
Date: 06/05/2026	Réf: 1711	BIM vSTR-016 Phase: APD

200 STR — Coffrage — R+3

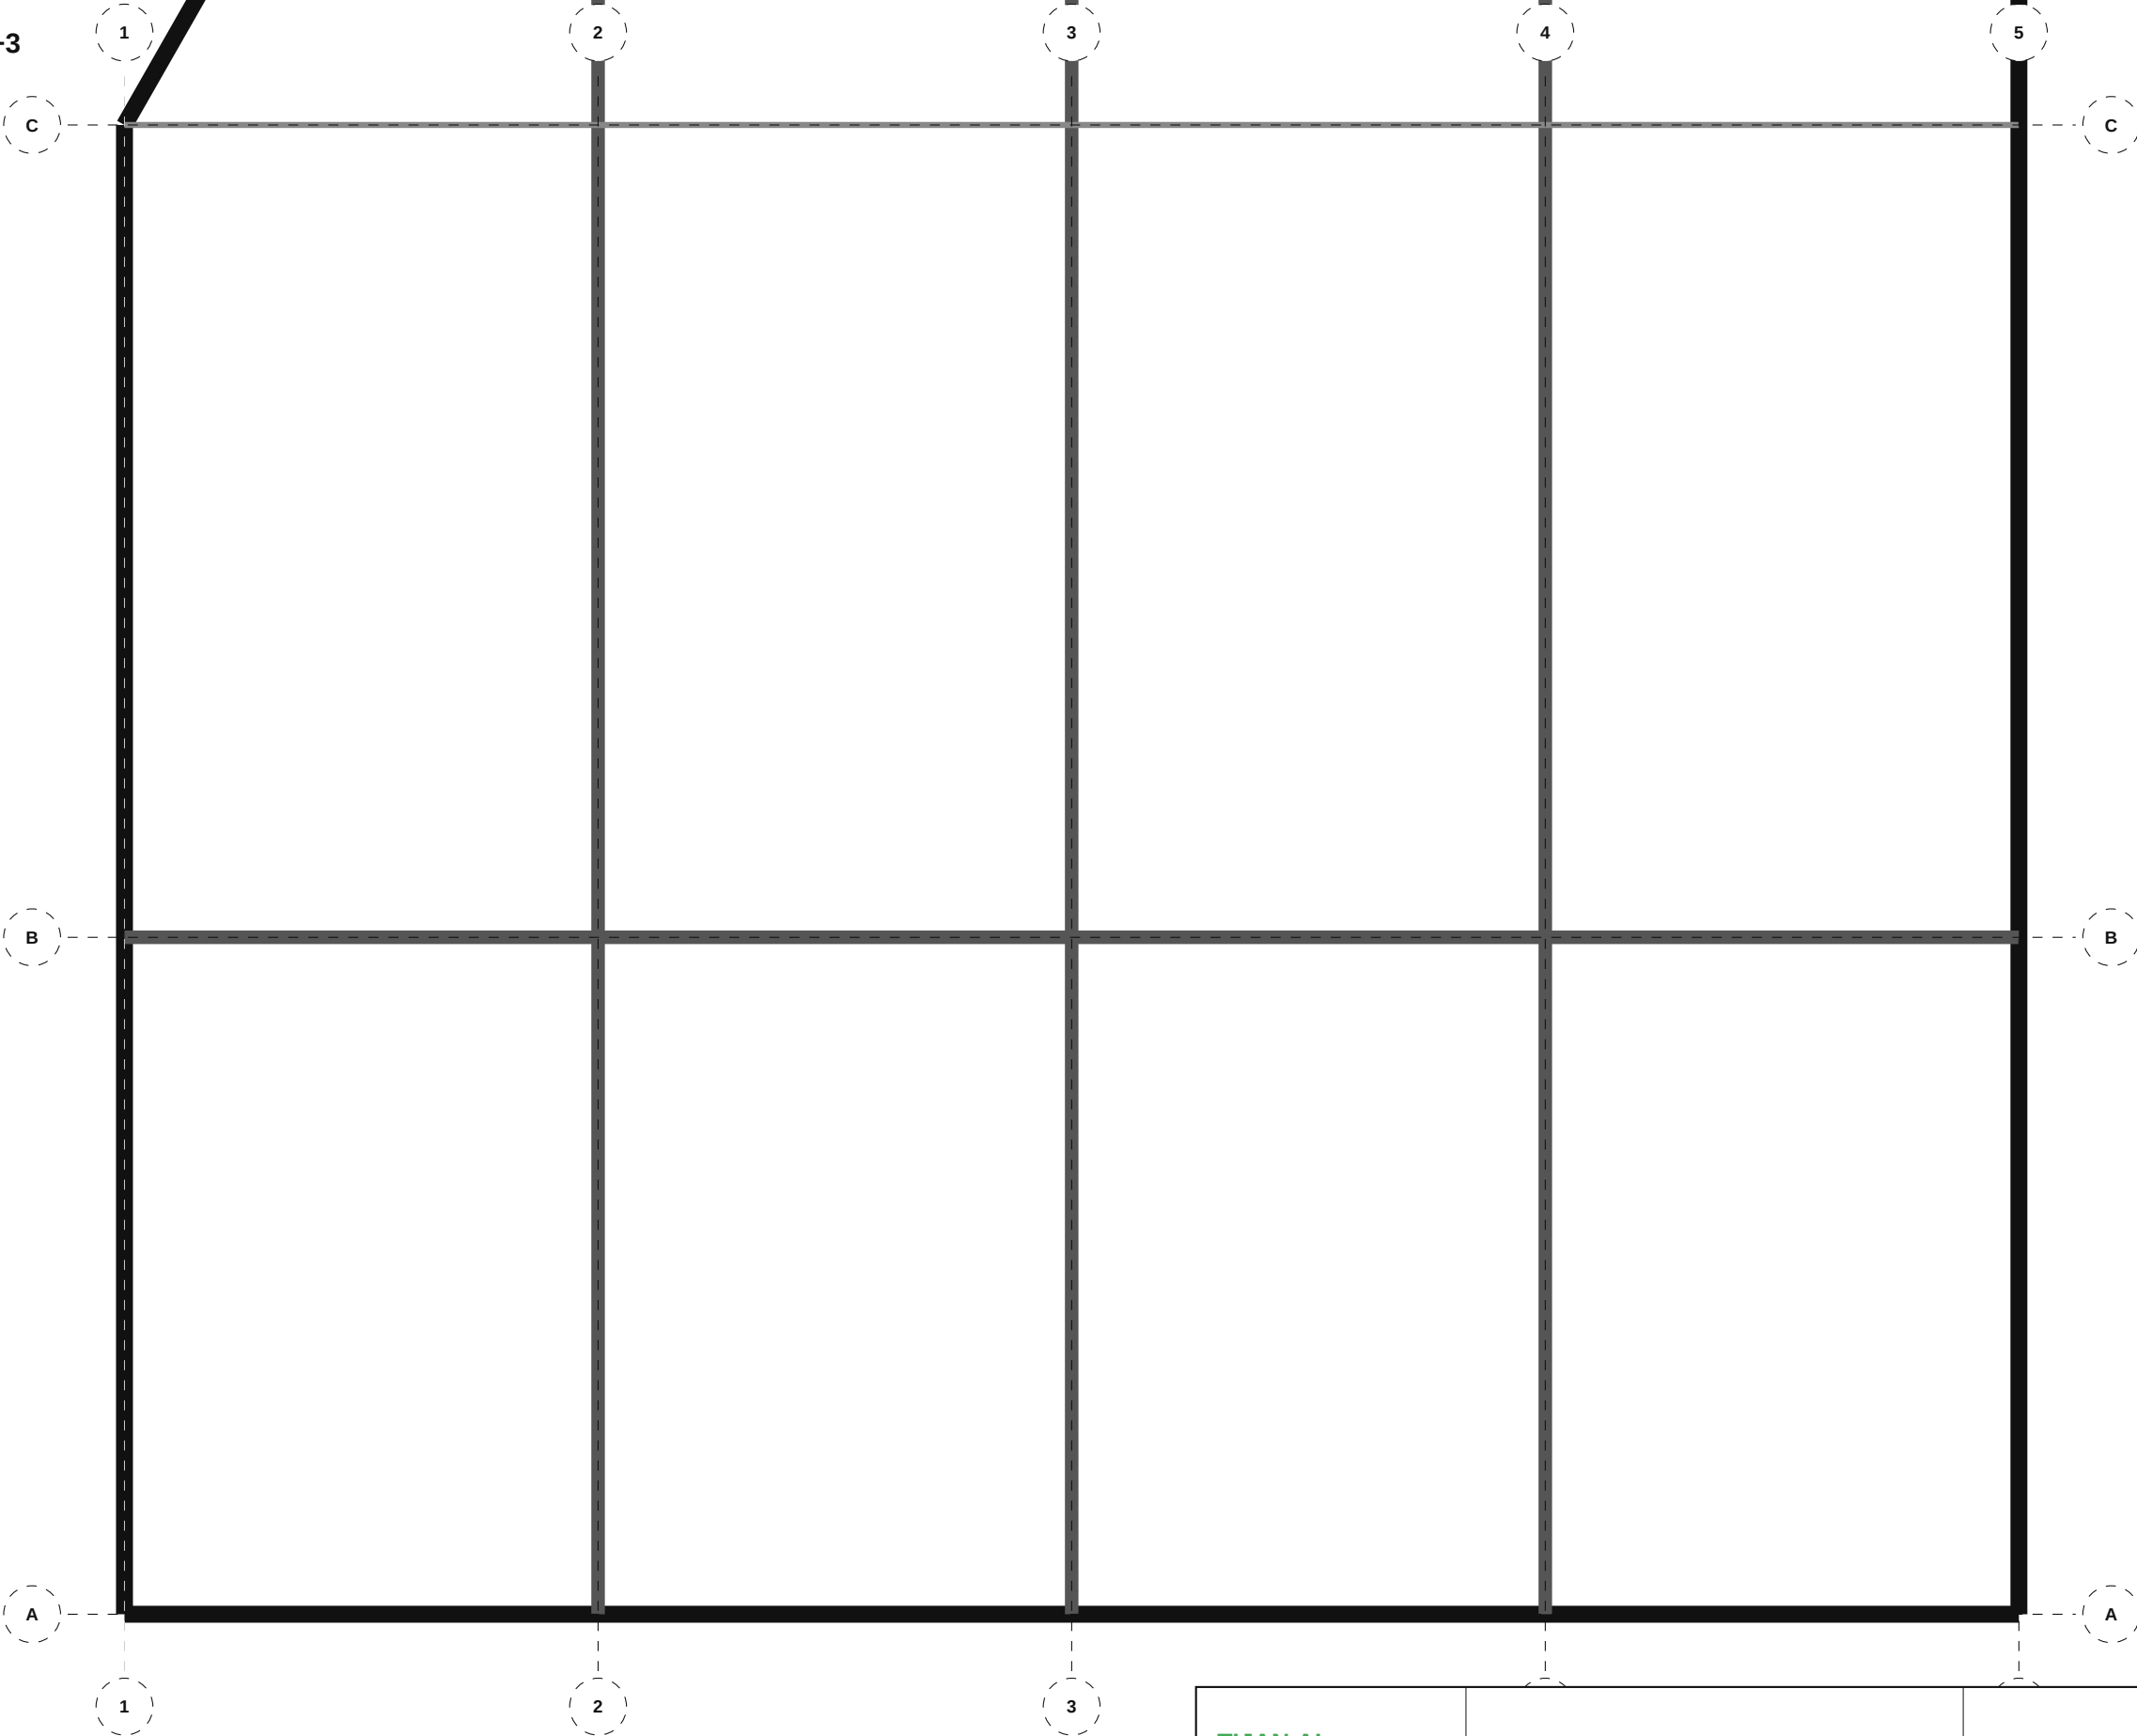


TIJAN AI Bureau d'Études Automatisé	Résidence Papa Oumar Sakho Dakar, Senegal	Éch: 1/100 Pl. 17/133
	200 STR — Coffrage — R+3	
Date: 06/05/2026	Réf: 1711	BIM vSTR-017 Phase: APD

200 STR — Coffrage — R+4

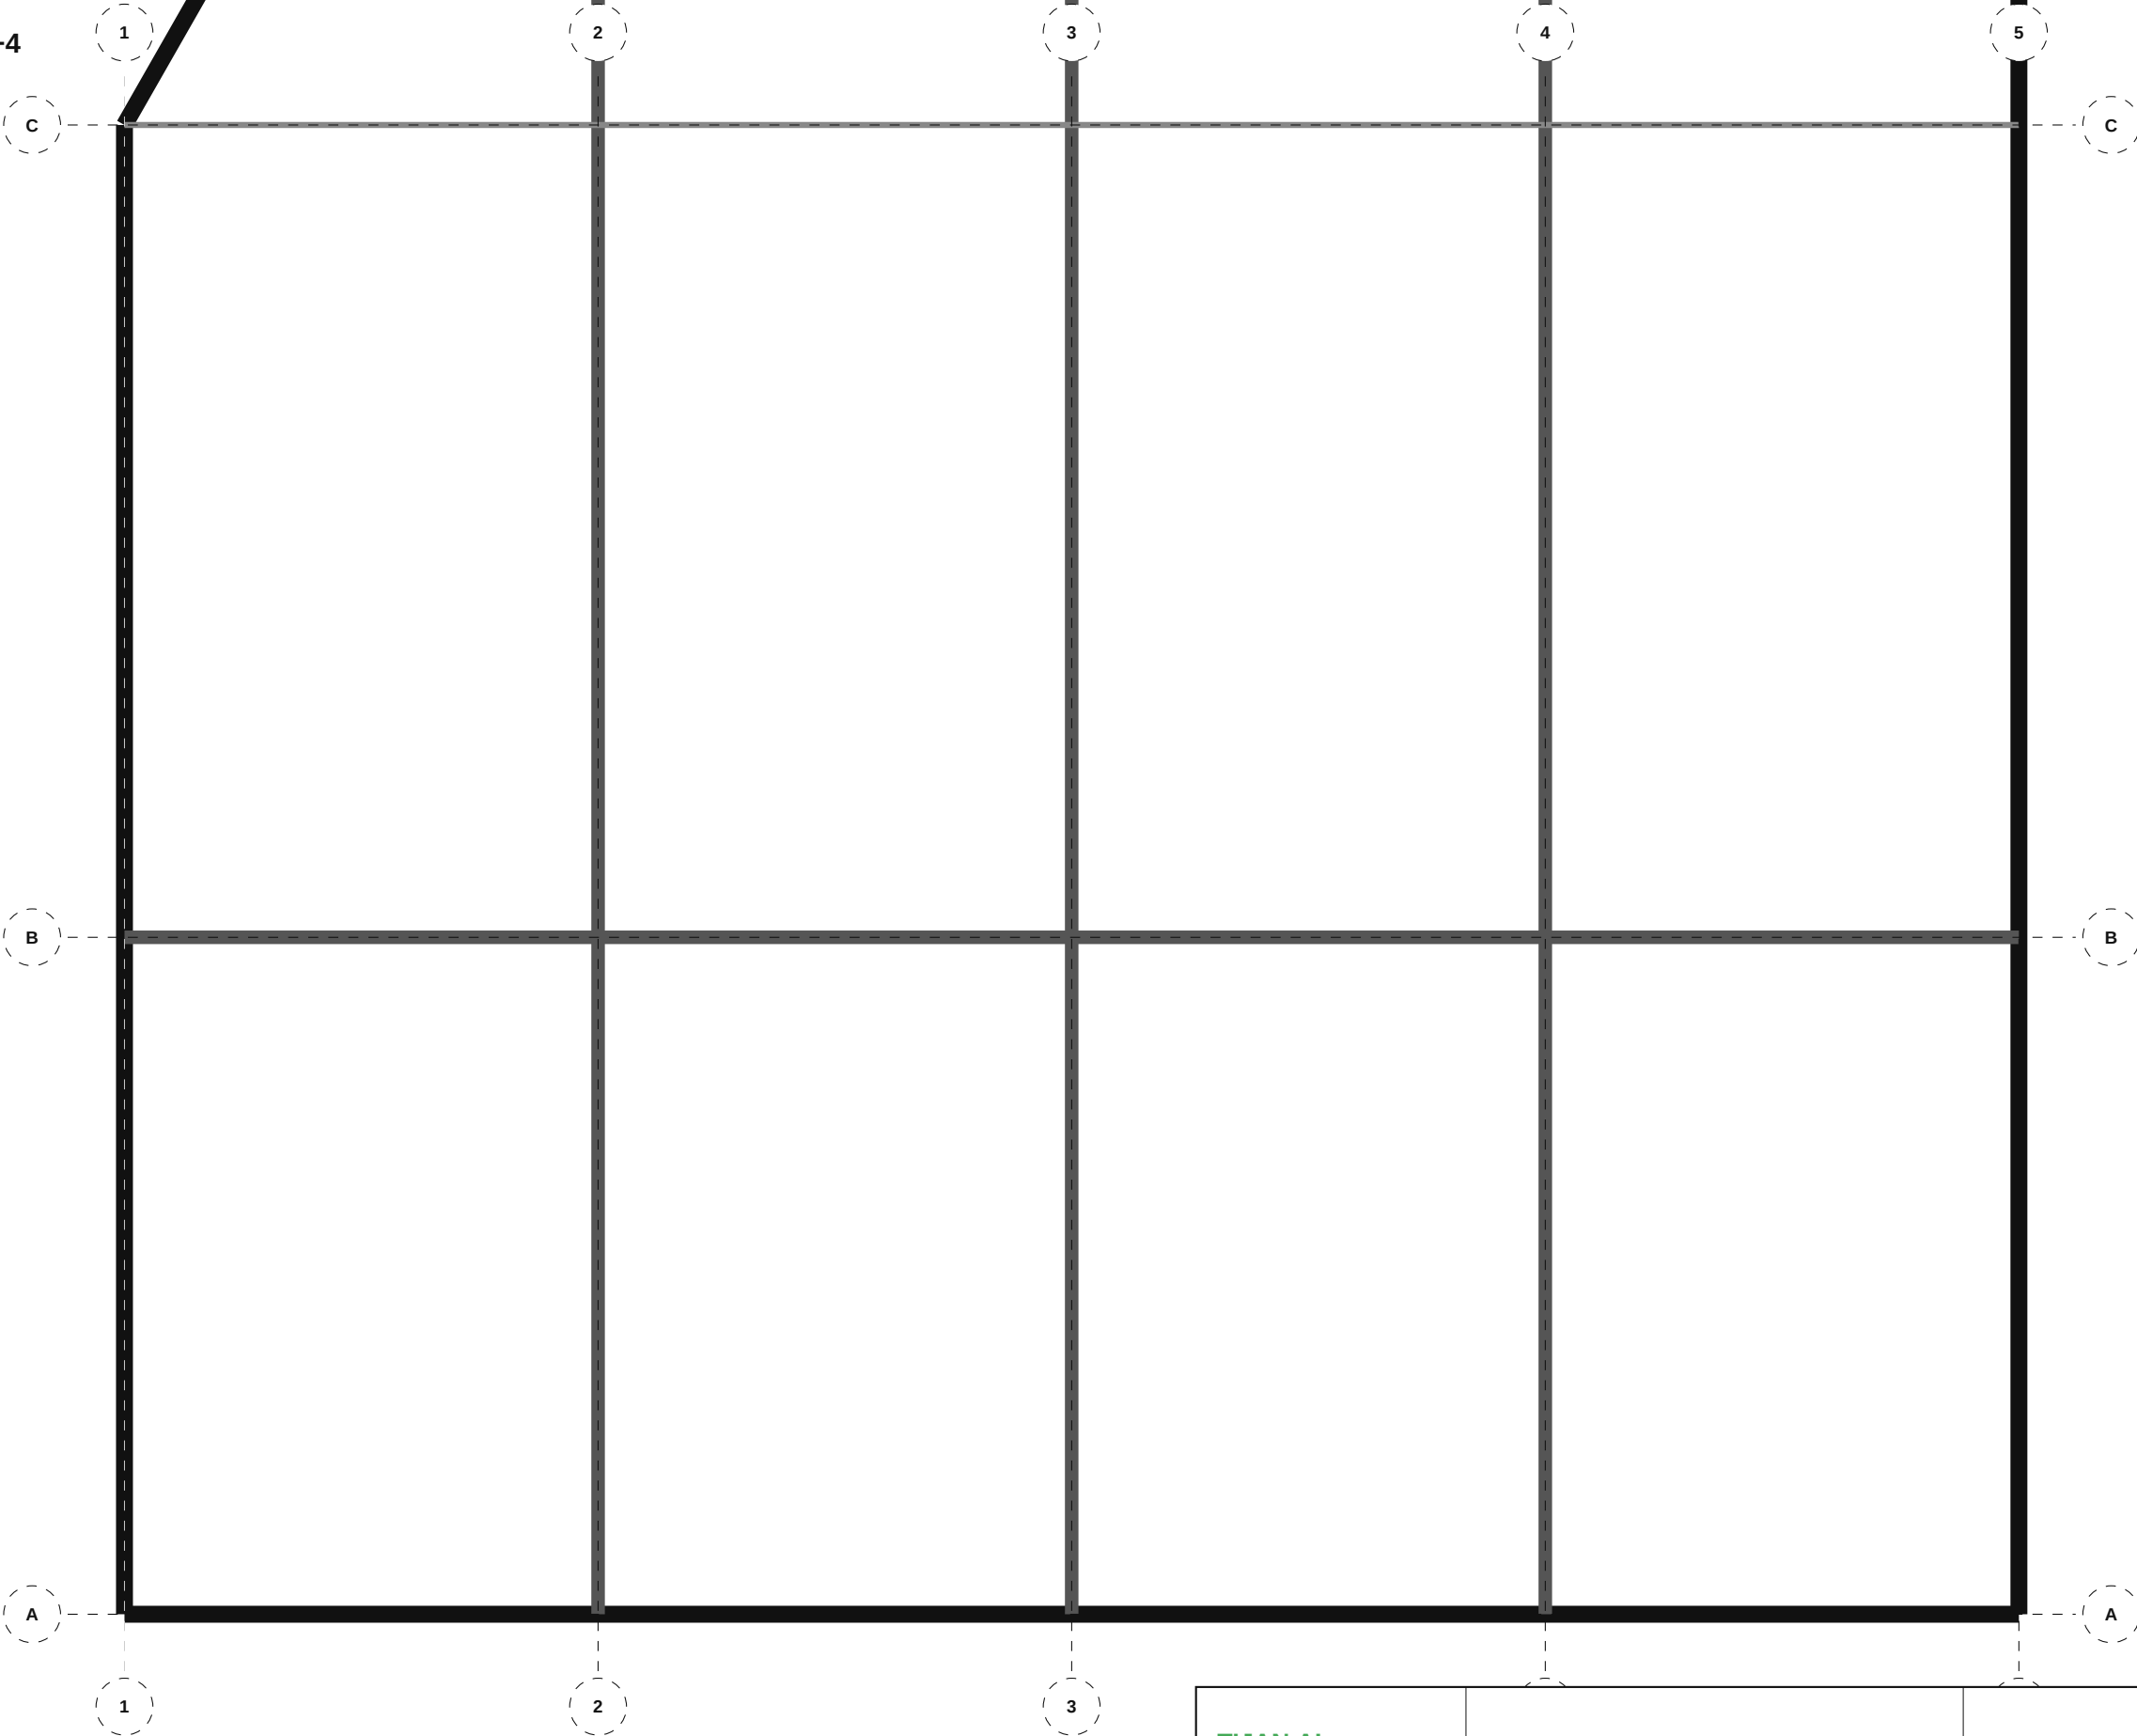


TIJAN AI Bureau d'Études Automatisé	Résidence Papa Oumar Sakho Dakar, Senegal	Éch: 1/100 Pl. 18/133
	200 STR — Coffrage — R+4	
Date: 06/05/2026	Réf: 1711	BIM vSTR-018 Phase: APD

200 STR — Coffrage — R+5

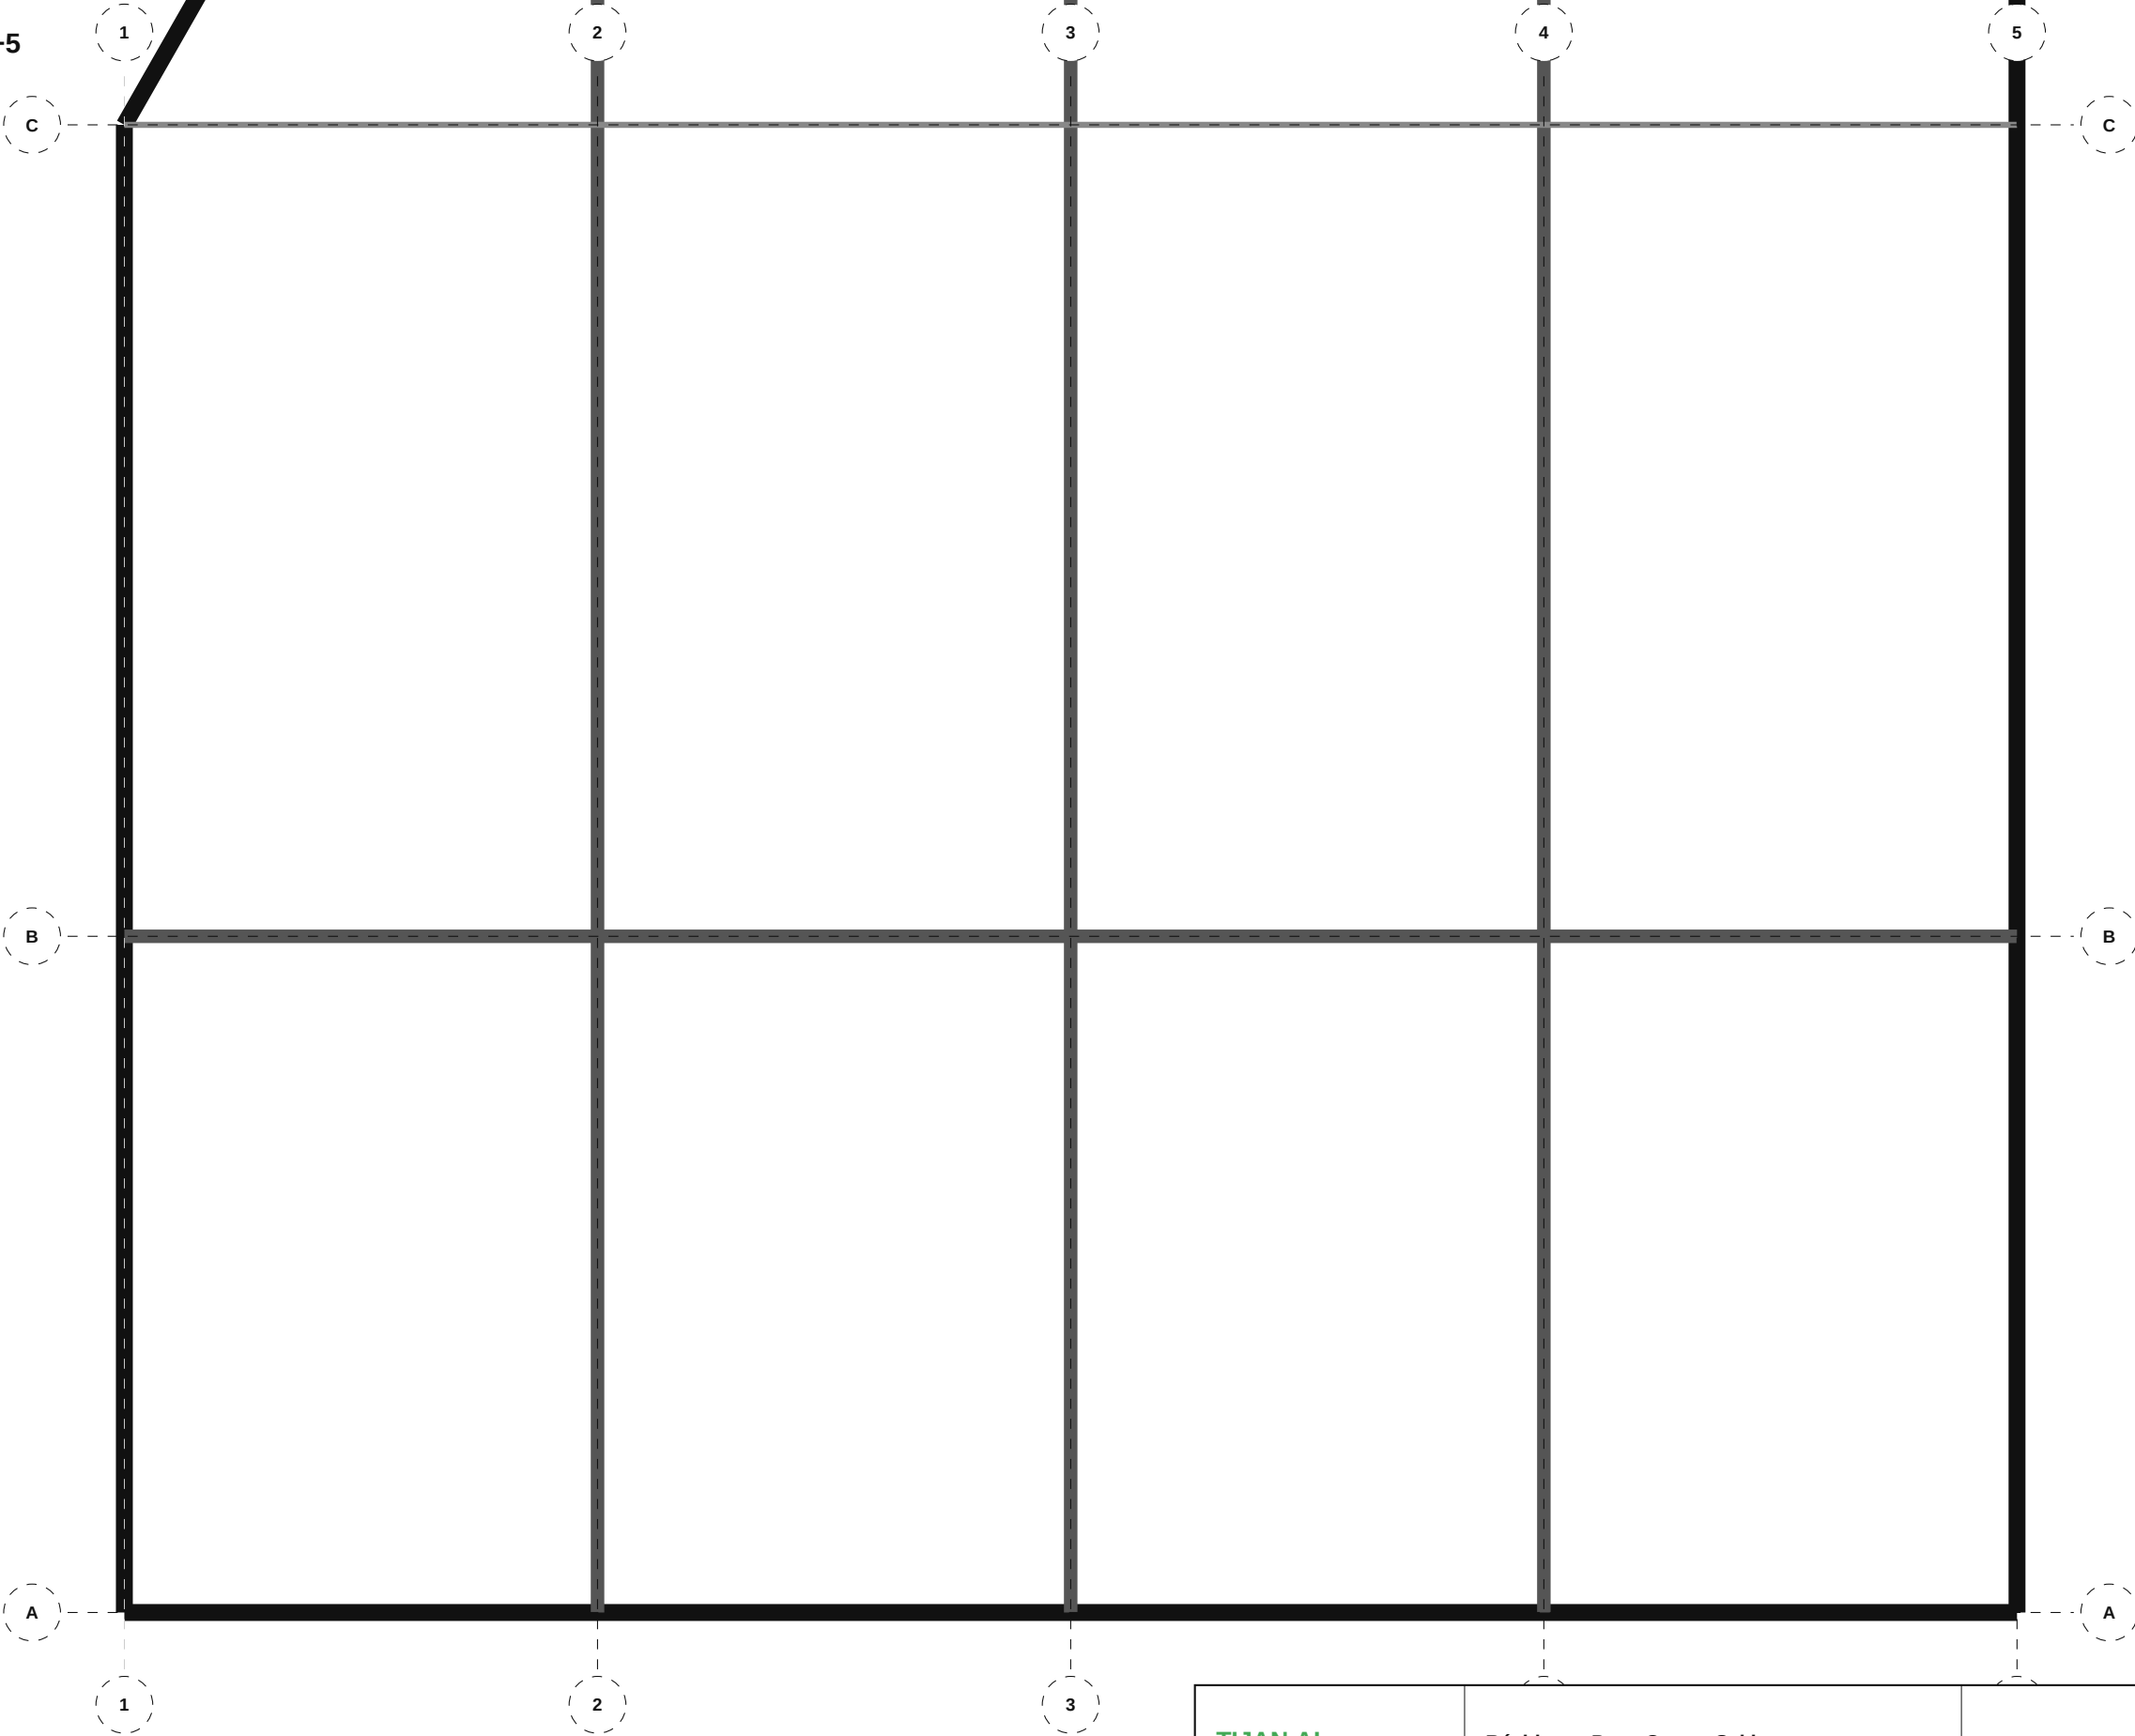


TIJAN AI Bureau d'Études Automatisé	Résidence Papa Oumar Sakho Dakar, Senegal	Éch: 1/100 Pl. 19/133
	200 STR — Coffrage — R+5	
Date: 06/05/2026	Réf: 1711	BIM vSTR-019 Phase: APD

200 STR — Coffrage — R+6

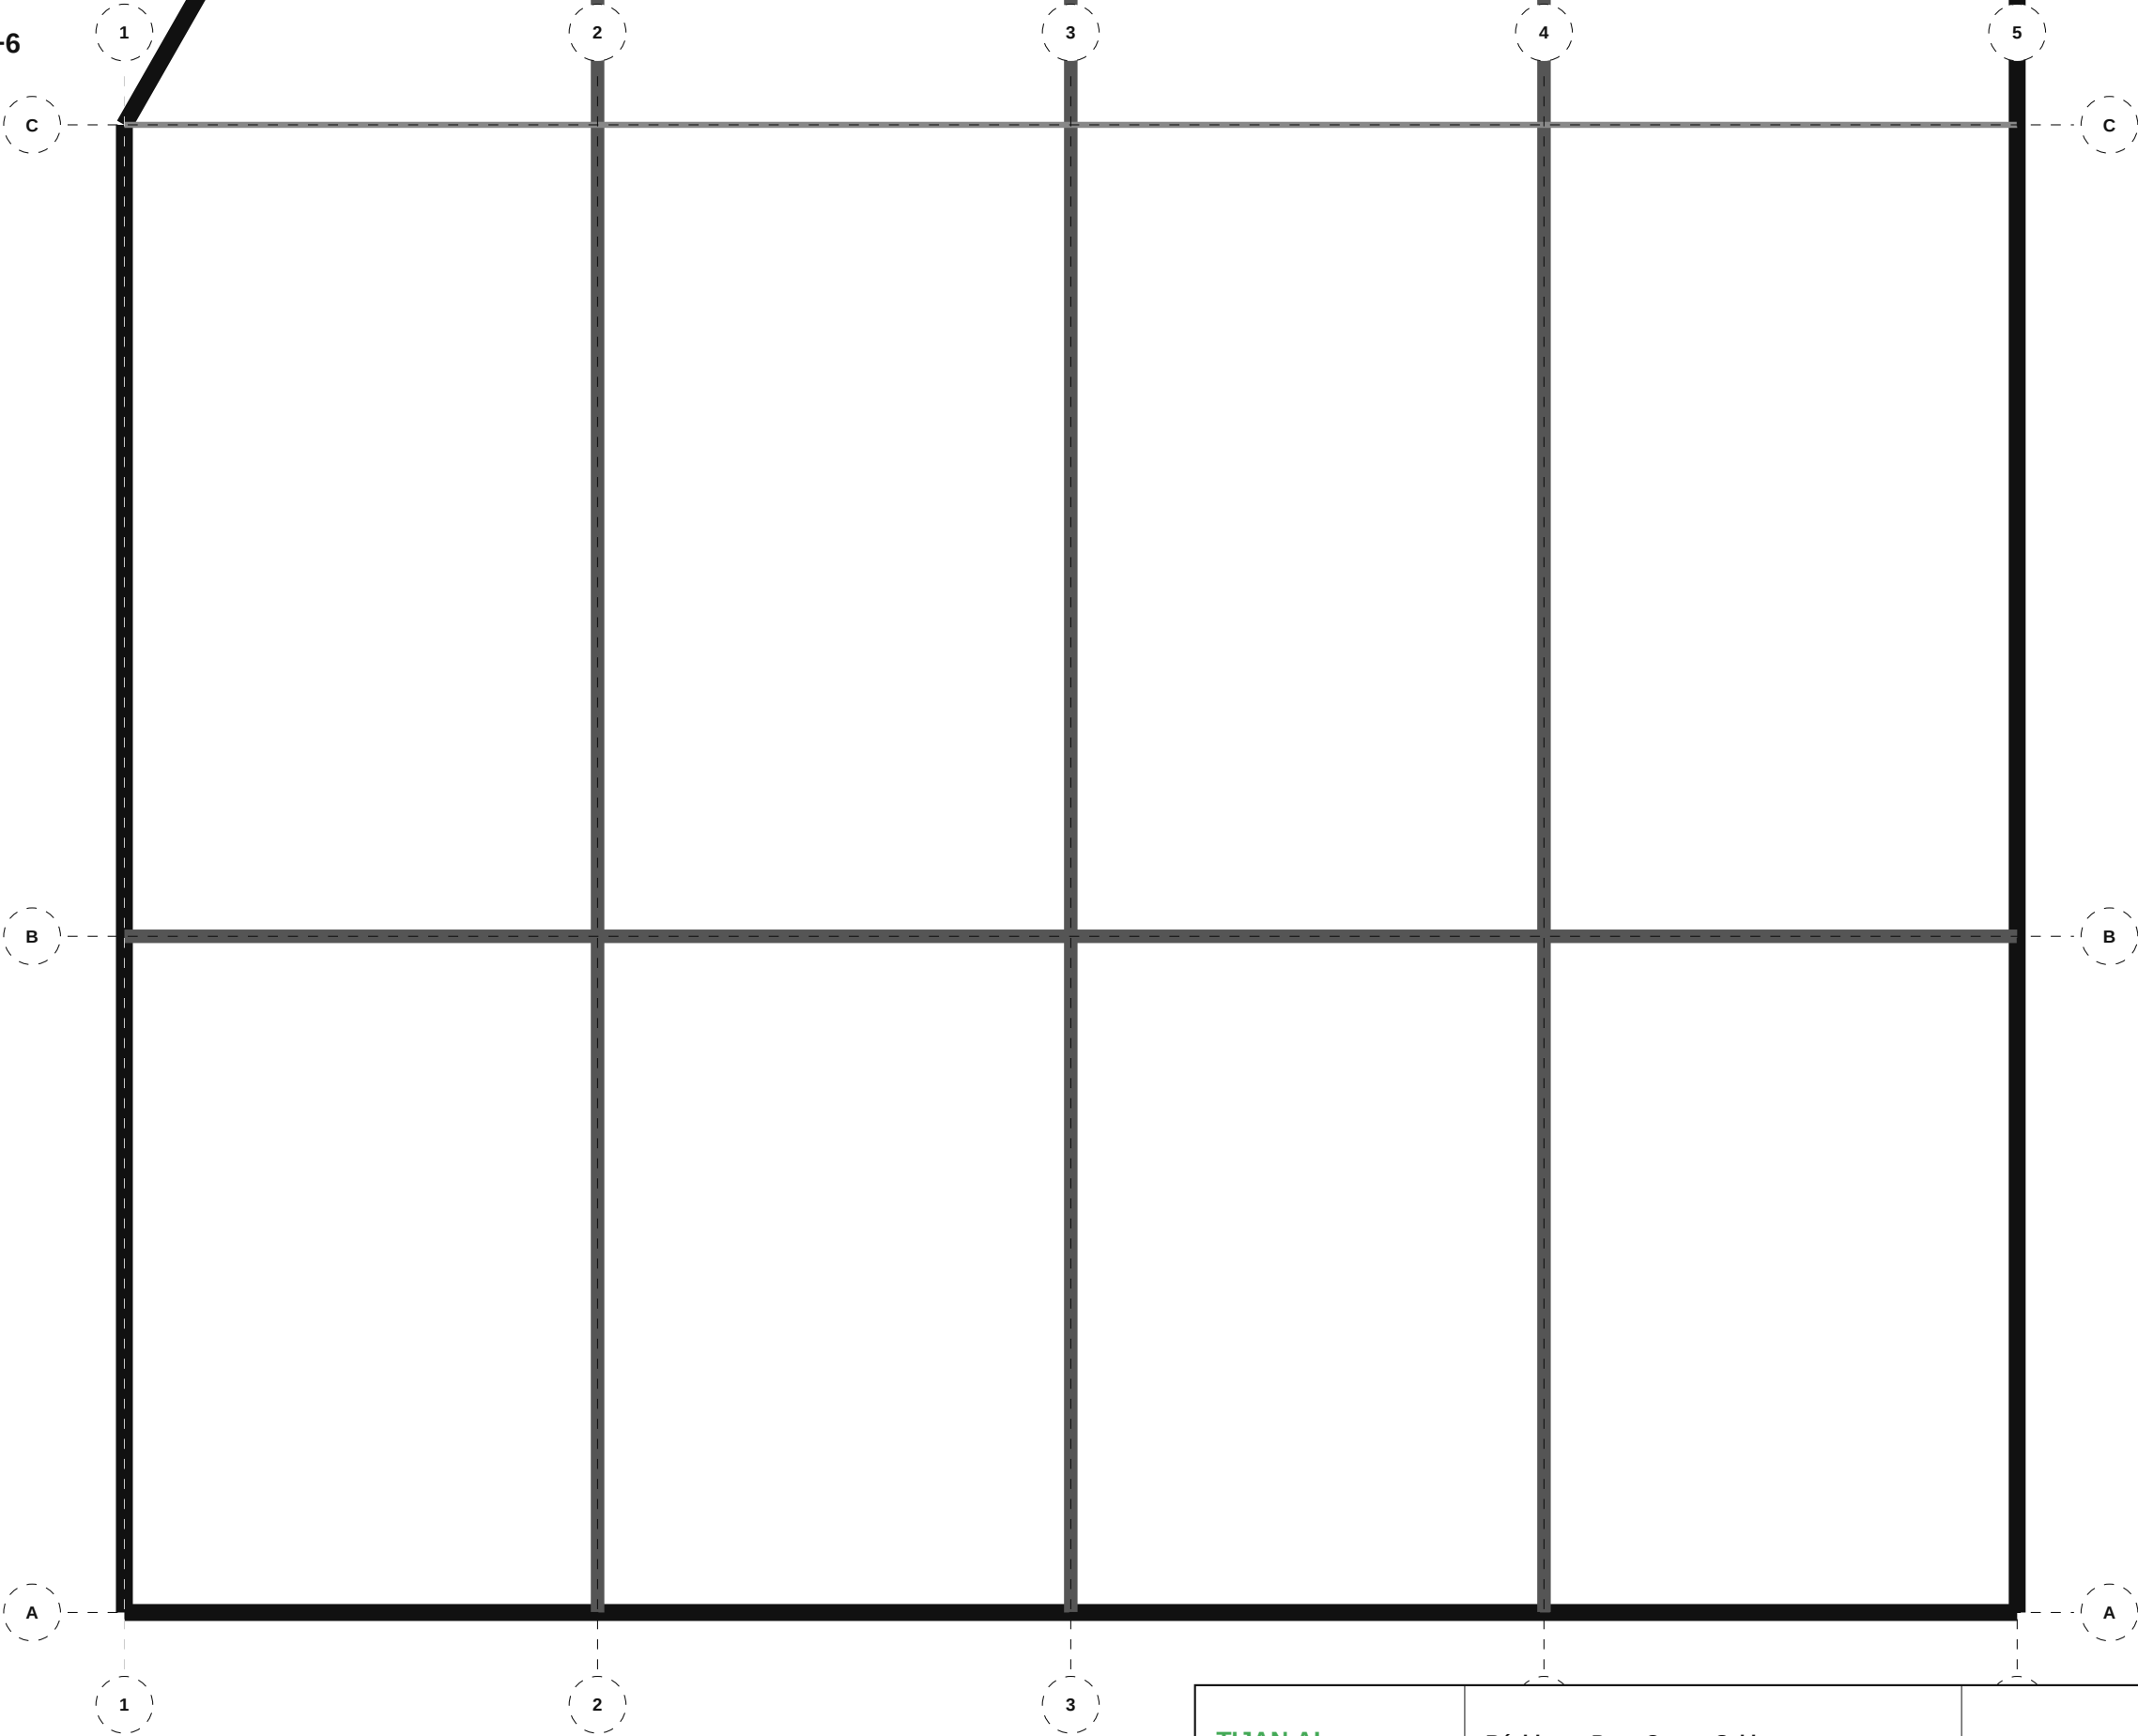


TIJAN AI Bureau d'Études Automatisé	Résidence Papa Oumar Sakho Dakar, Senegal	Éch: 1/100 Pl. 20/133
	200 STR — Coffrage — R+6	
Date: 06/05/2026	Réf: 1711	BIM vSTR-020 Phase: APD

200 STR — Coffrage — R+7

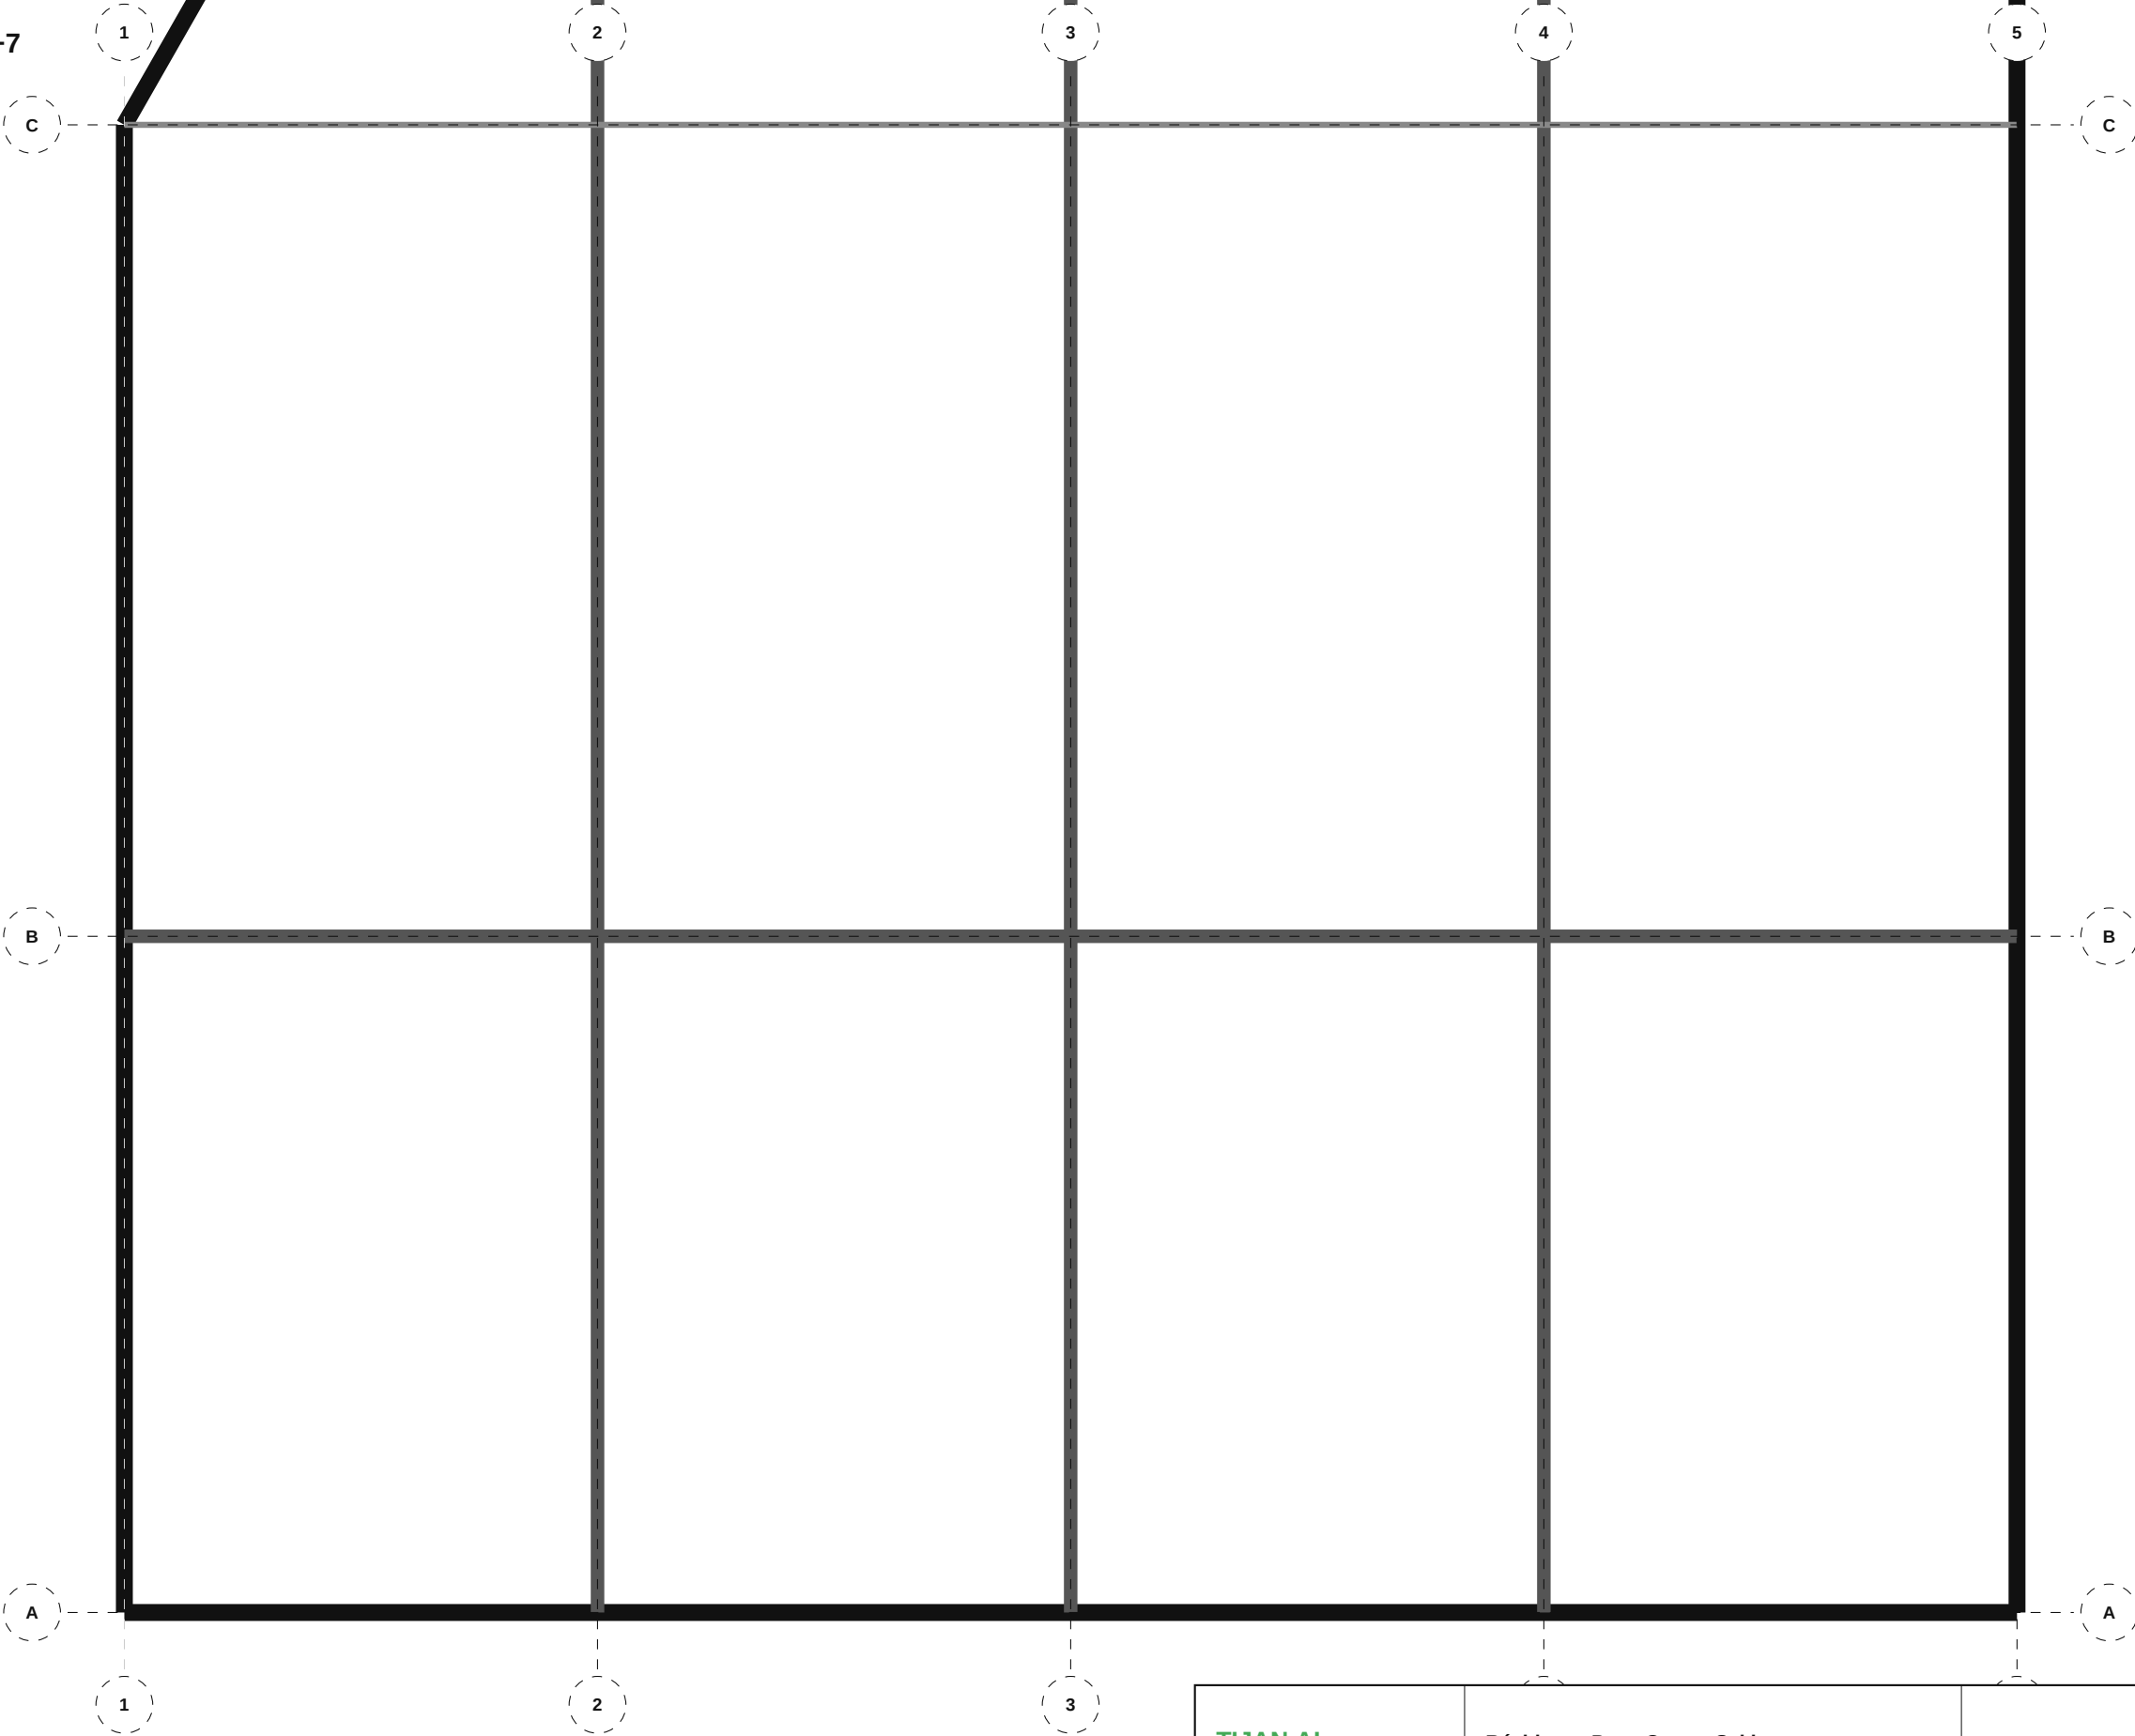

TIJAN AI Bureau d'Études Automatisé	Résidence Papa Oumar Sakho Dakar, Senegal	Éch: 1/100 Pl. 21/133
	200 STR — Coffrage — R+7	
Date: 06/05/2026	Réf: 1711	BIM vSTR-021 Phase: APD

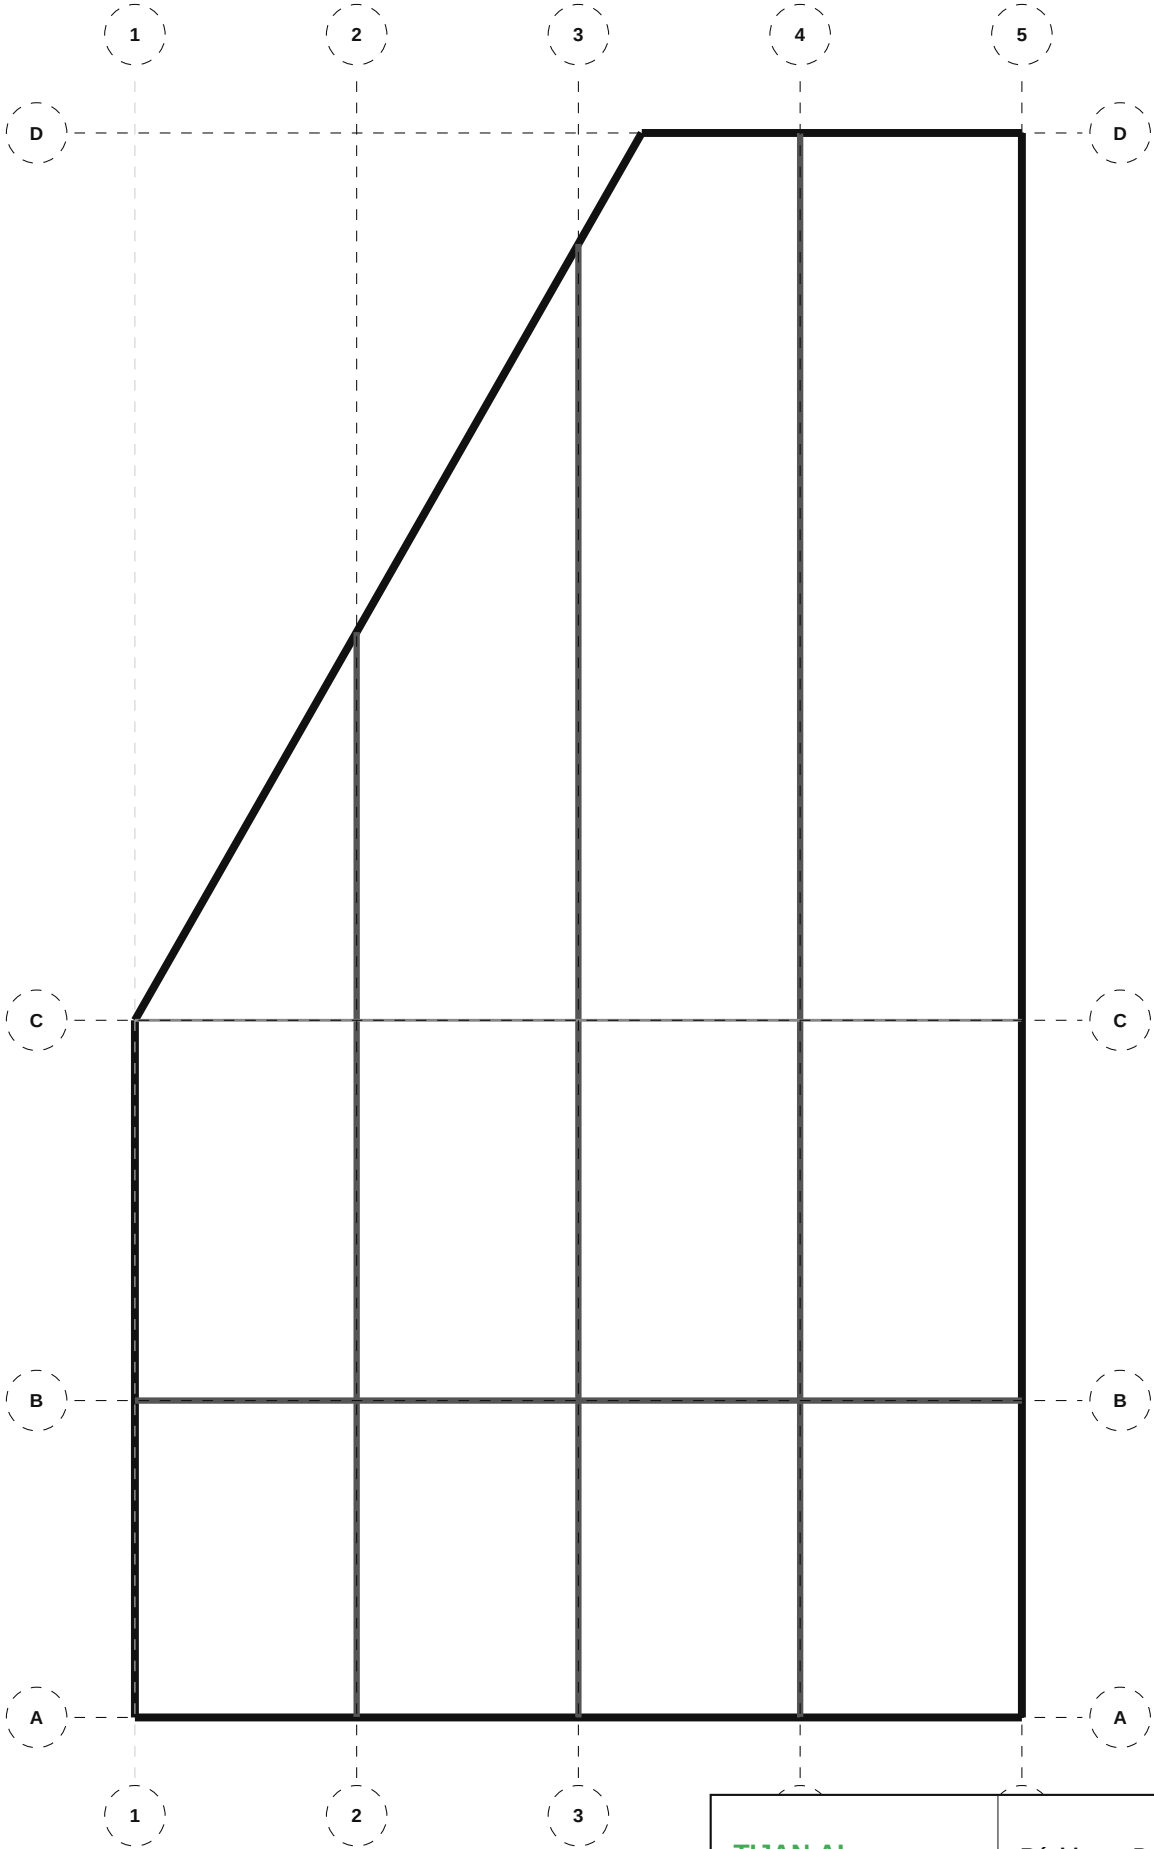

TIJAN AI Bureau d'Études Automatisé	Résidence Papa Oumar Sakho Dakar, Senegal	Éch: 1/100 Pl. 22/133
	200 STR — Coffrage — R+8 Terrasse	
Date: 06/05/2026	Réf: 1711	BIM vSTR-022 Phase: APD

1

C

2

3

4

5

C

B

B

A

A

1

2

3

Bureau d'Études Automatisé

Dakar, Senegal

Pl. 23/133


- WC suspendu: 10
- Évier cuisine: 6
- Lave-vaisselle: 6
- Lavabo: 6
- Douche: 6
- Lave-mains: 4

BIM vPLU-023

Date: 06/05/2026

Réf: 1711

Phase: APD

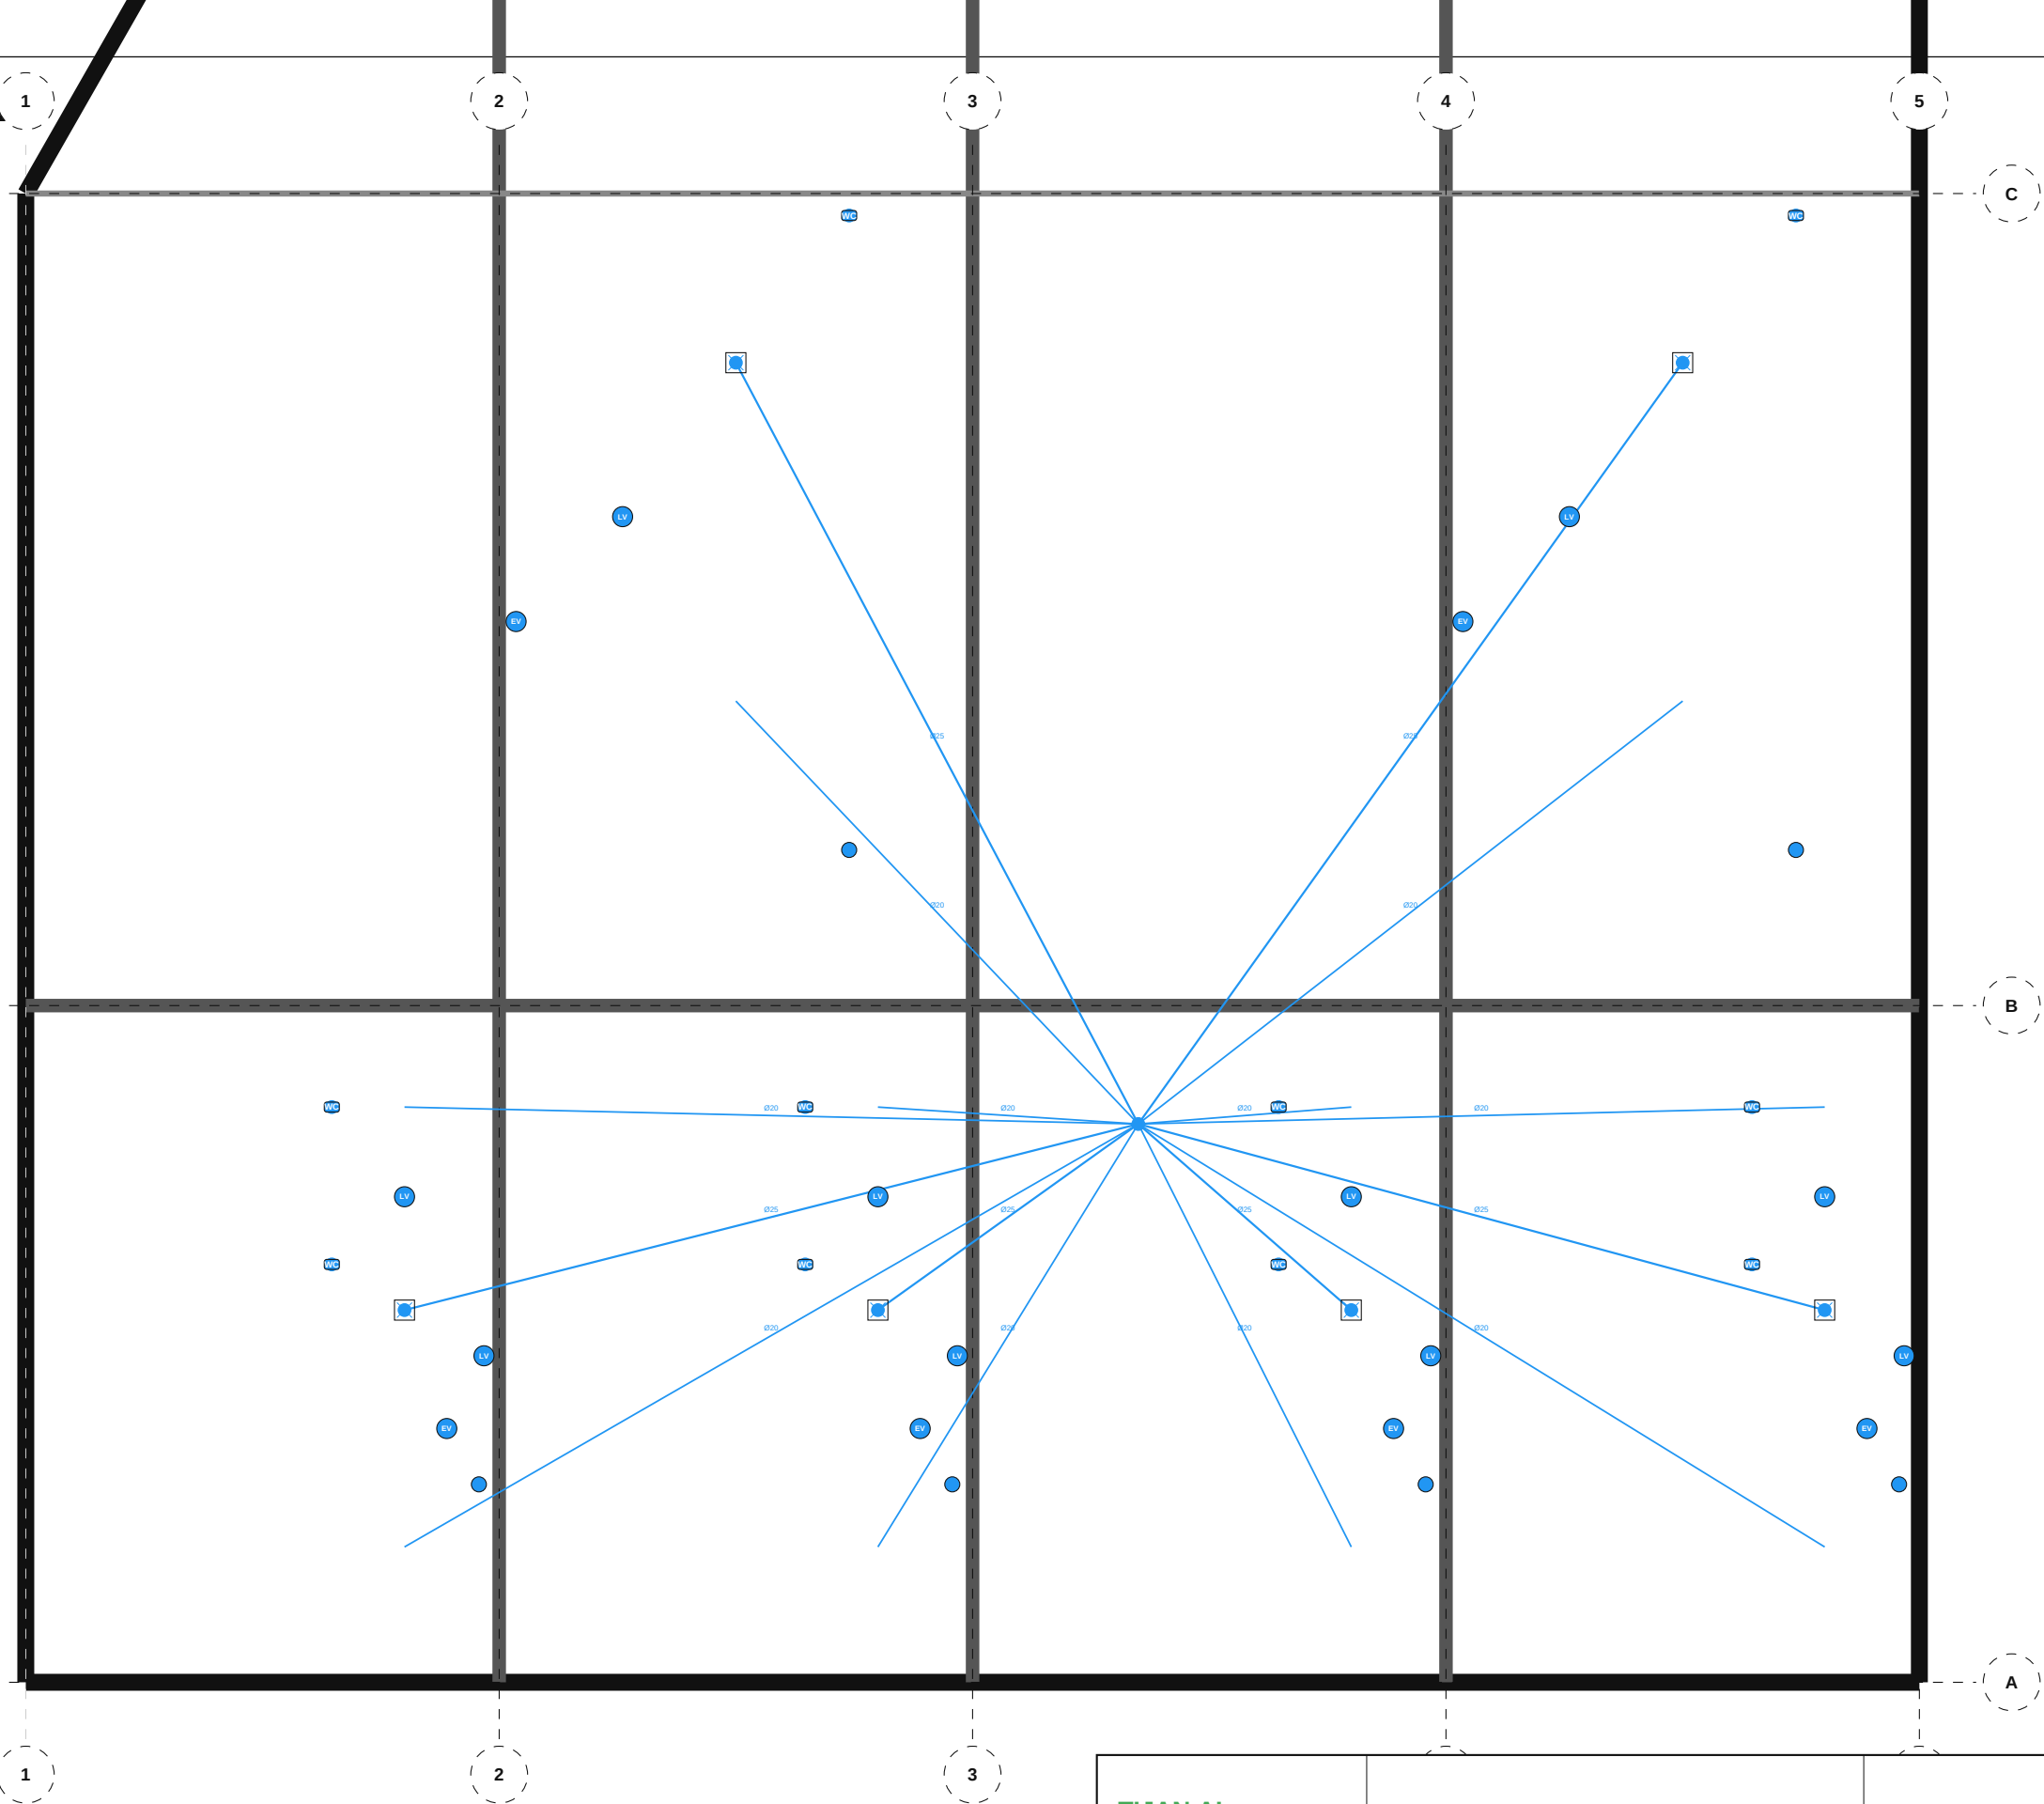

NOMENCLATURE — 410 PLU — Eau Froide (EF)

- WC suspendu: 10
- Évier cuisine: 6
- Lave-vaisselle: 6
- Lavabo: 6
- Douche: 6
- Lave-mains: 4

TIJAN AI

Bureau d'Études Automatisé

Résidence Papa Oumar Sakho

Dakar, Senegal

Éch: 1/100

Pl. 24/133


410 PLU — Eau Froide (EF) — R+2

Date: 06/05/2026

Réf: 1711

BIM vPLU-024

Phase: APD

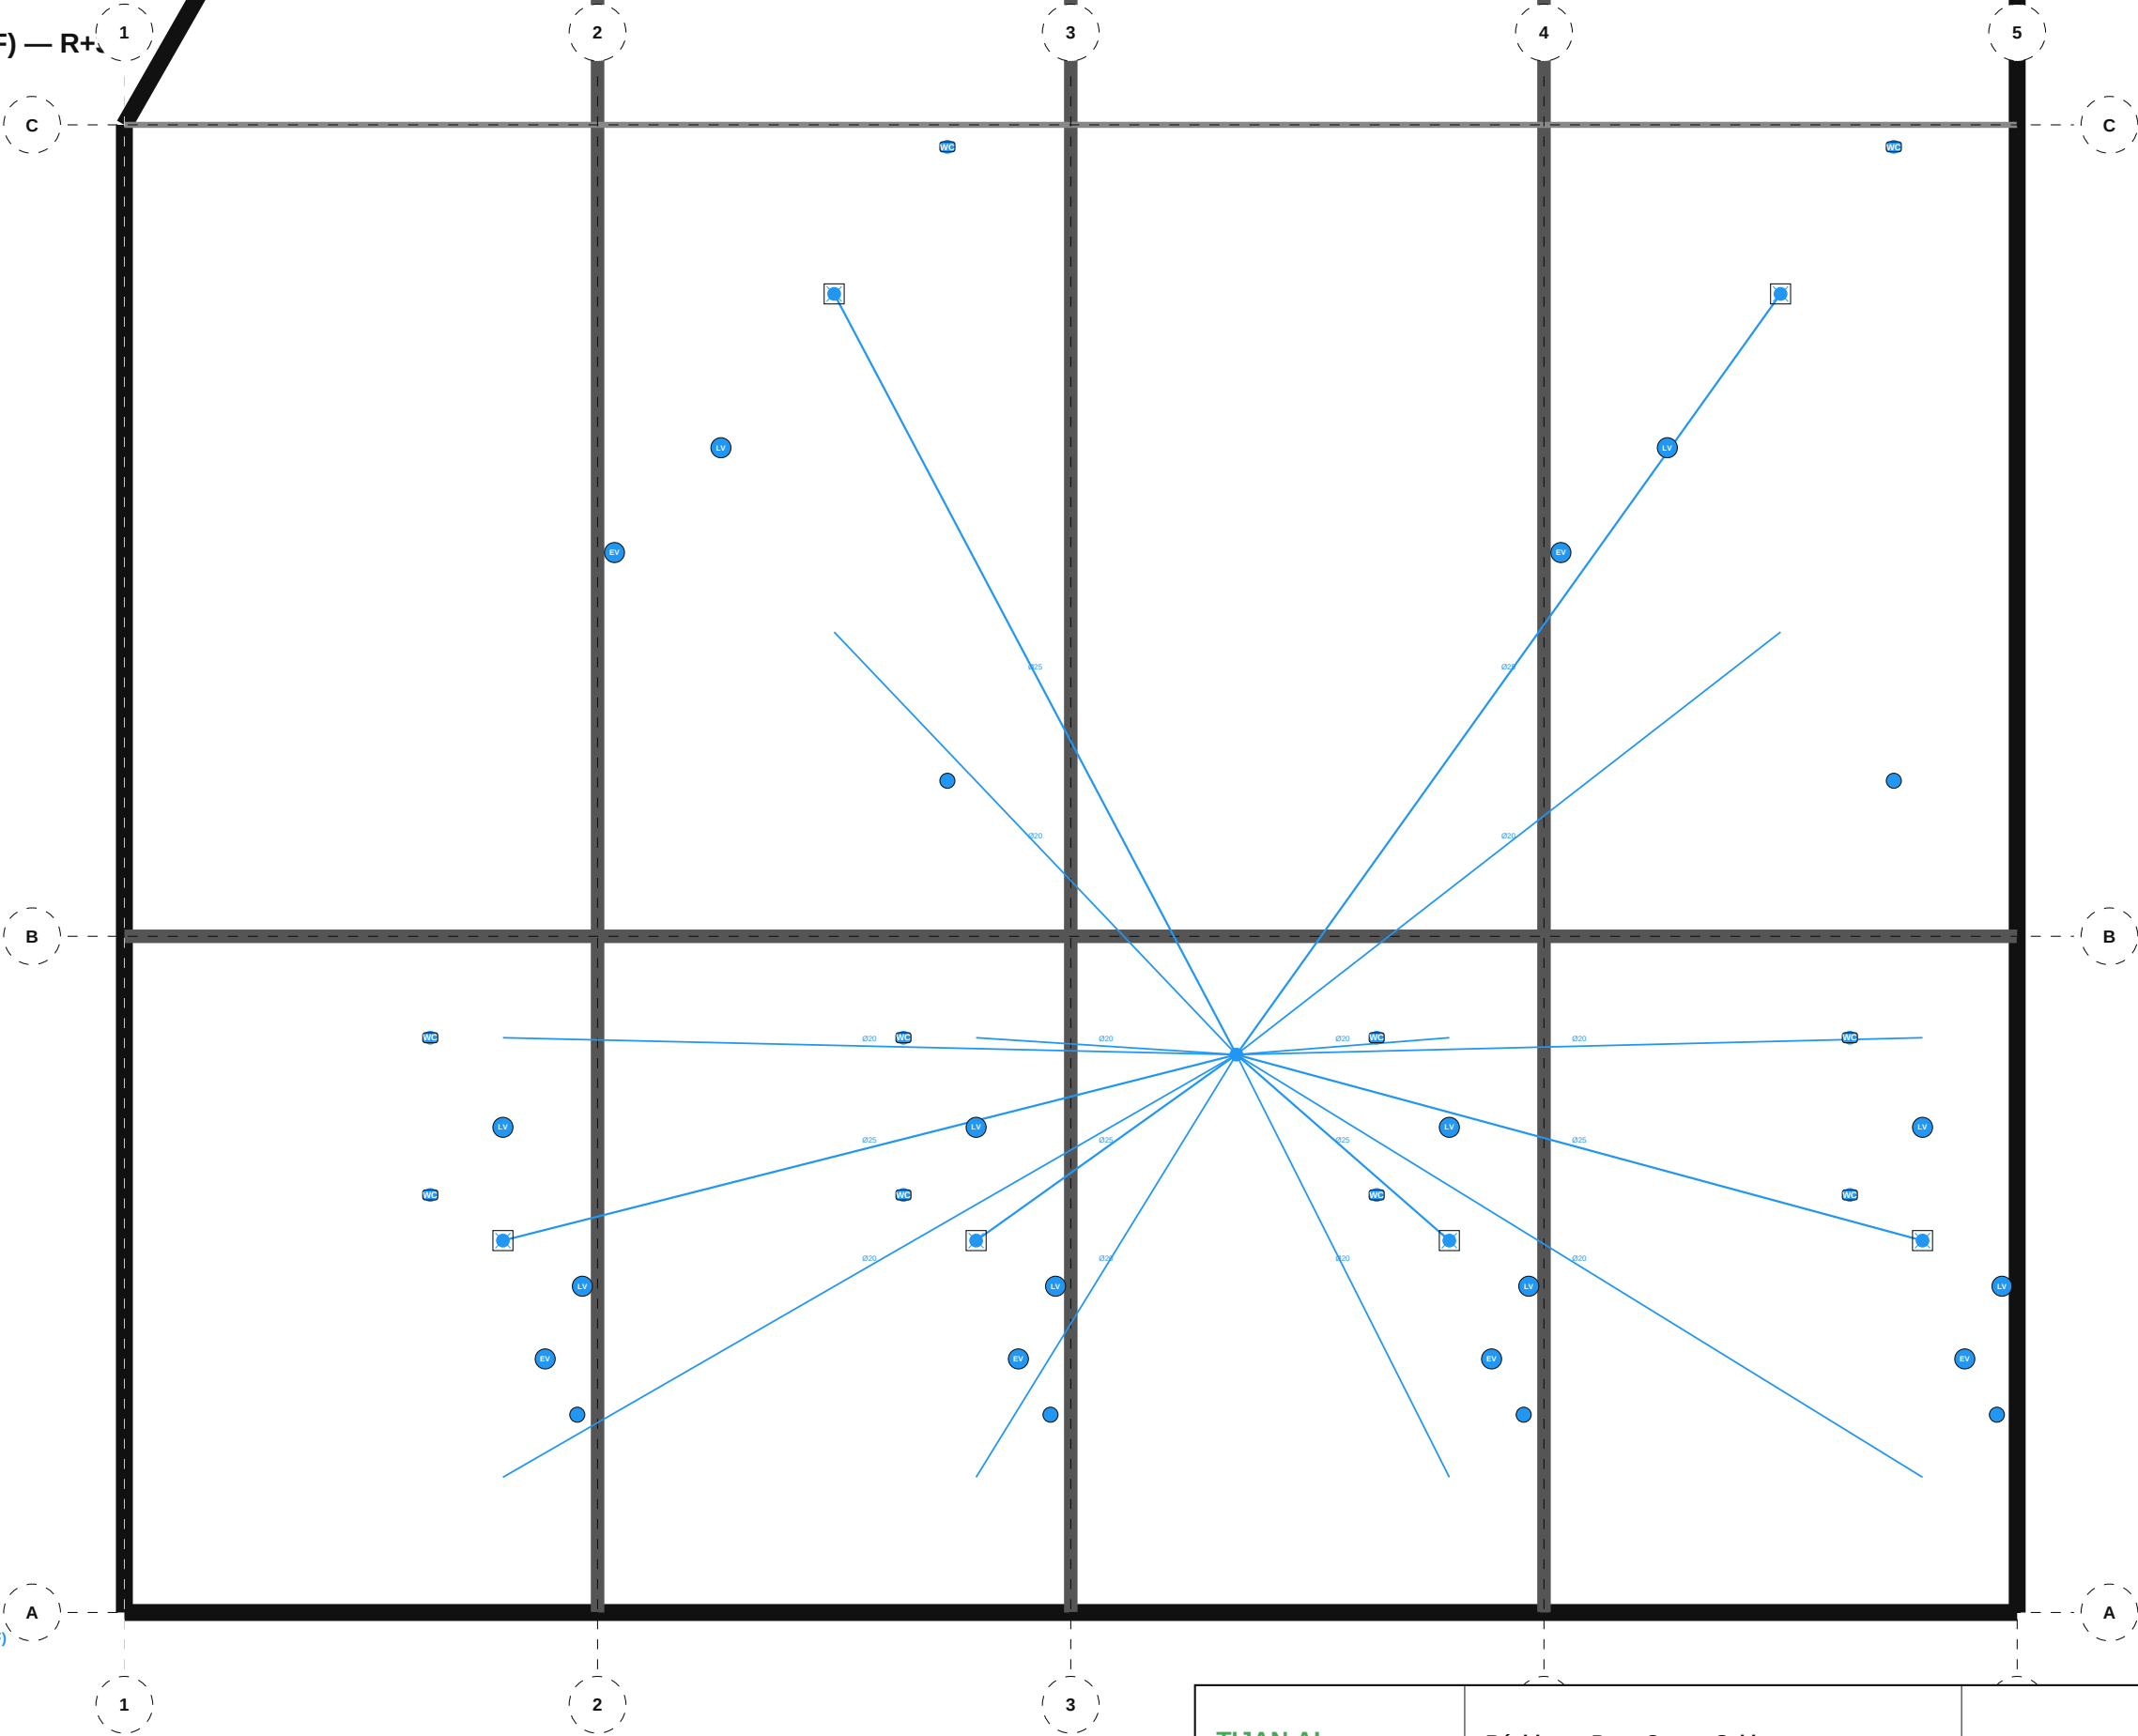

NOMENCLATURE — 410 PLU — Eau Froide (EF)

- WC suspendu: 10
- Évier cuisine: 6
- Lave-vaisselle: 6
- Lavabo: 6
- Douche: 6
- Lave-mains: 4

TIJAN AI

Bureau d'Études Automatisé

Résidence Papa Oumar Sakho

Dakar, Senegal

Éch: 1/100

Pl. 25/133


410 PLU — Eau Froide (EF) — R+3

Date: 06/05/2026

Réf: 1711

BIM vPLU-025

Phase: APD

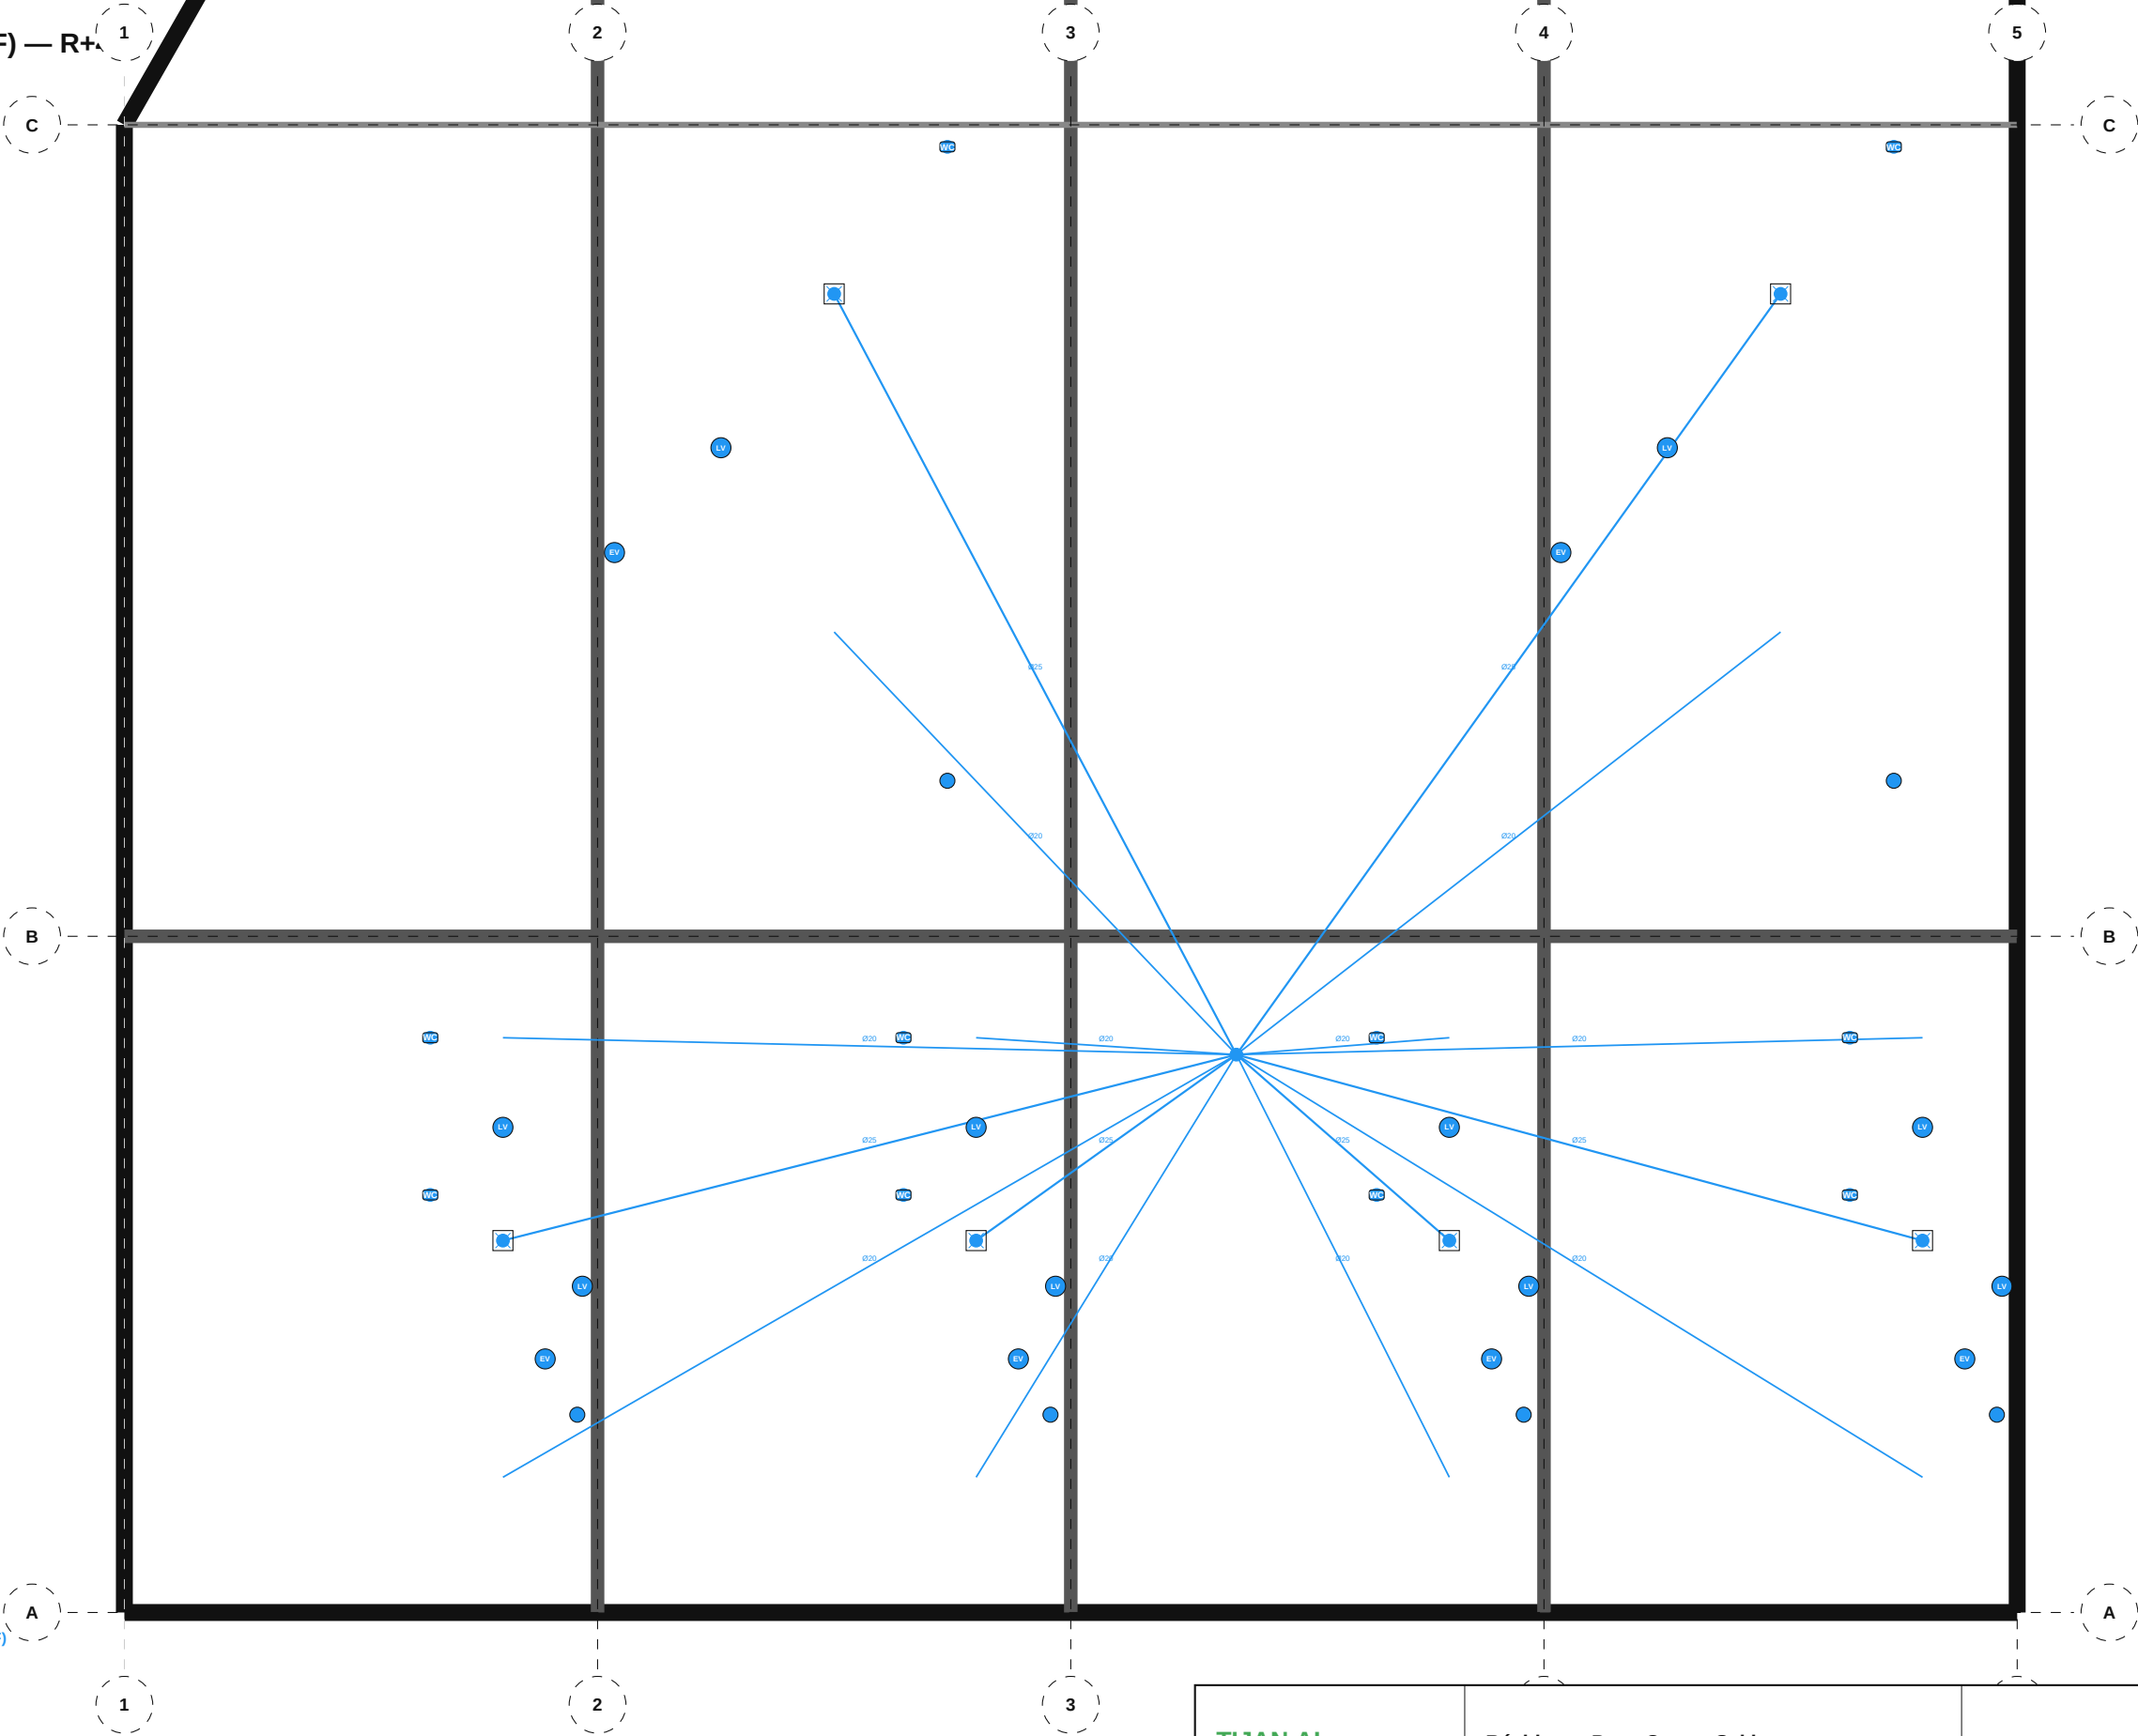

NOMENCLATURE — 410 PLU — Eau Froide (EF)

- WC suspendu: 10
- Évier cuisine: 6
- Lave-vaisselle: 6
- Lavabo: 6
- Douche: 6
- Lave-mains: 4

TIJAN AI

Bureau d'Études Automatisé

Résidence Papa Oumar Sakho

Dakar, Senegal

Éch: 1/100

Pl. 26/133


410 PLU — Eau Froide (EF) — R+4

Date: 06/05/2026

Réf: 1711

BIM vPLU-026

Phase: APD

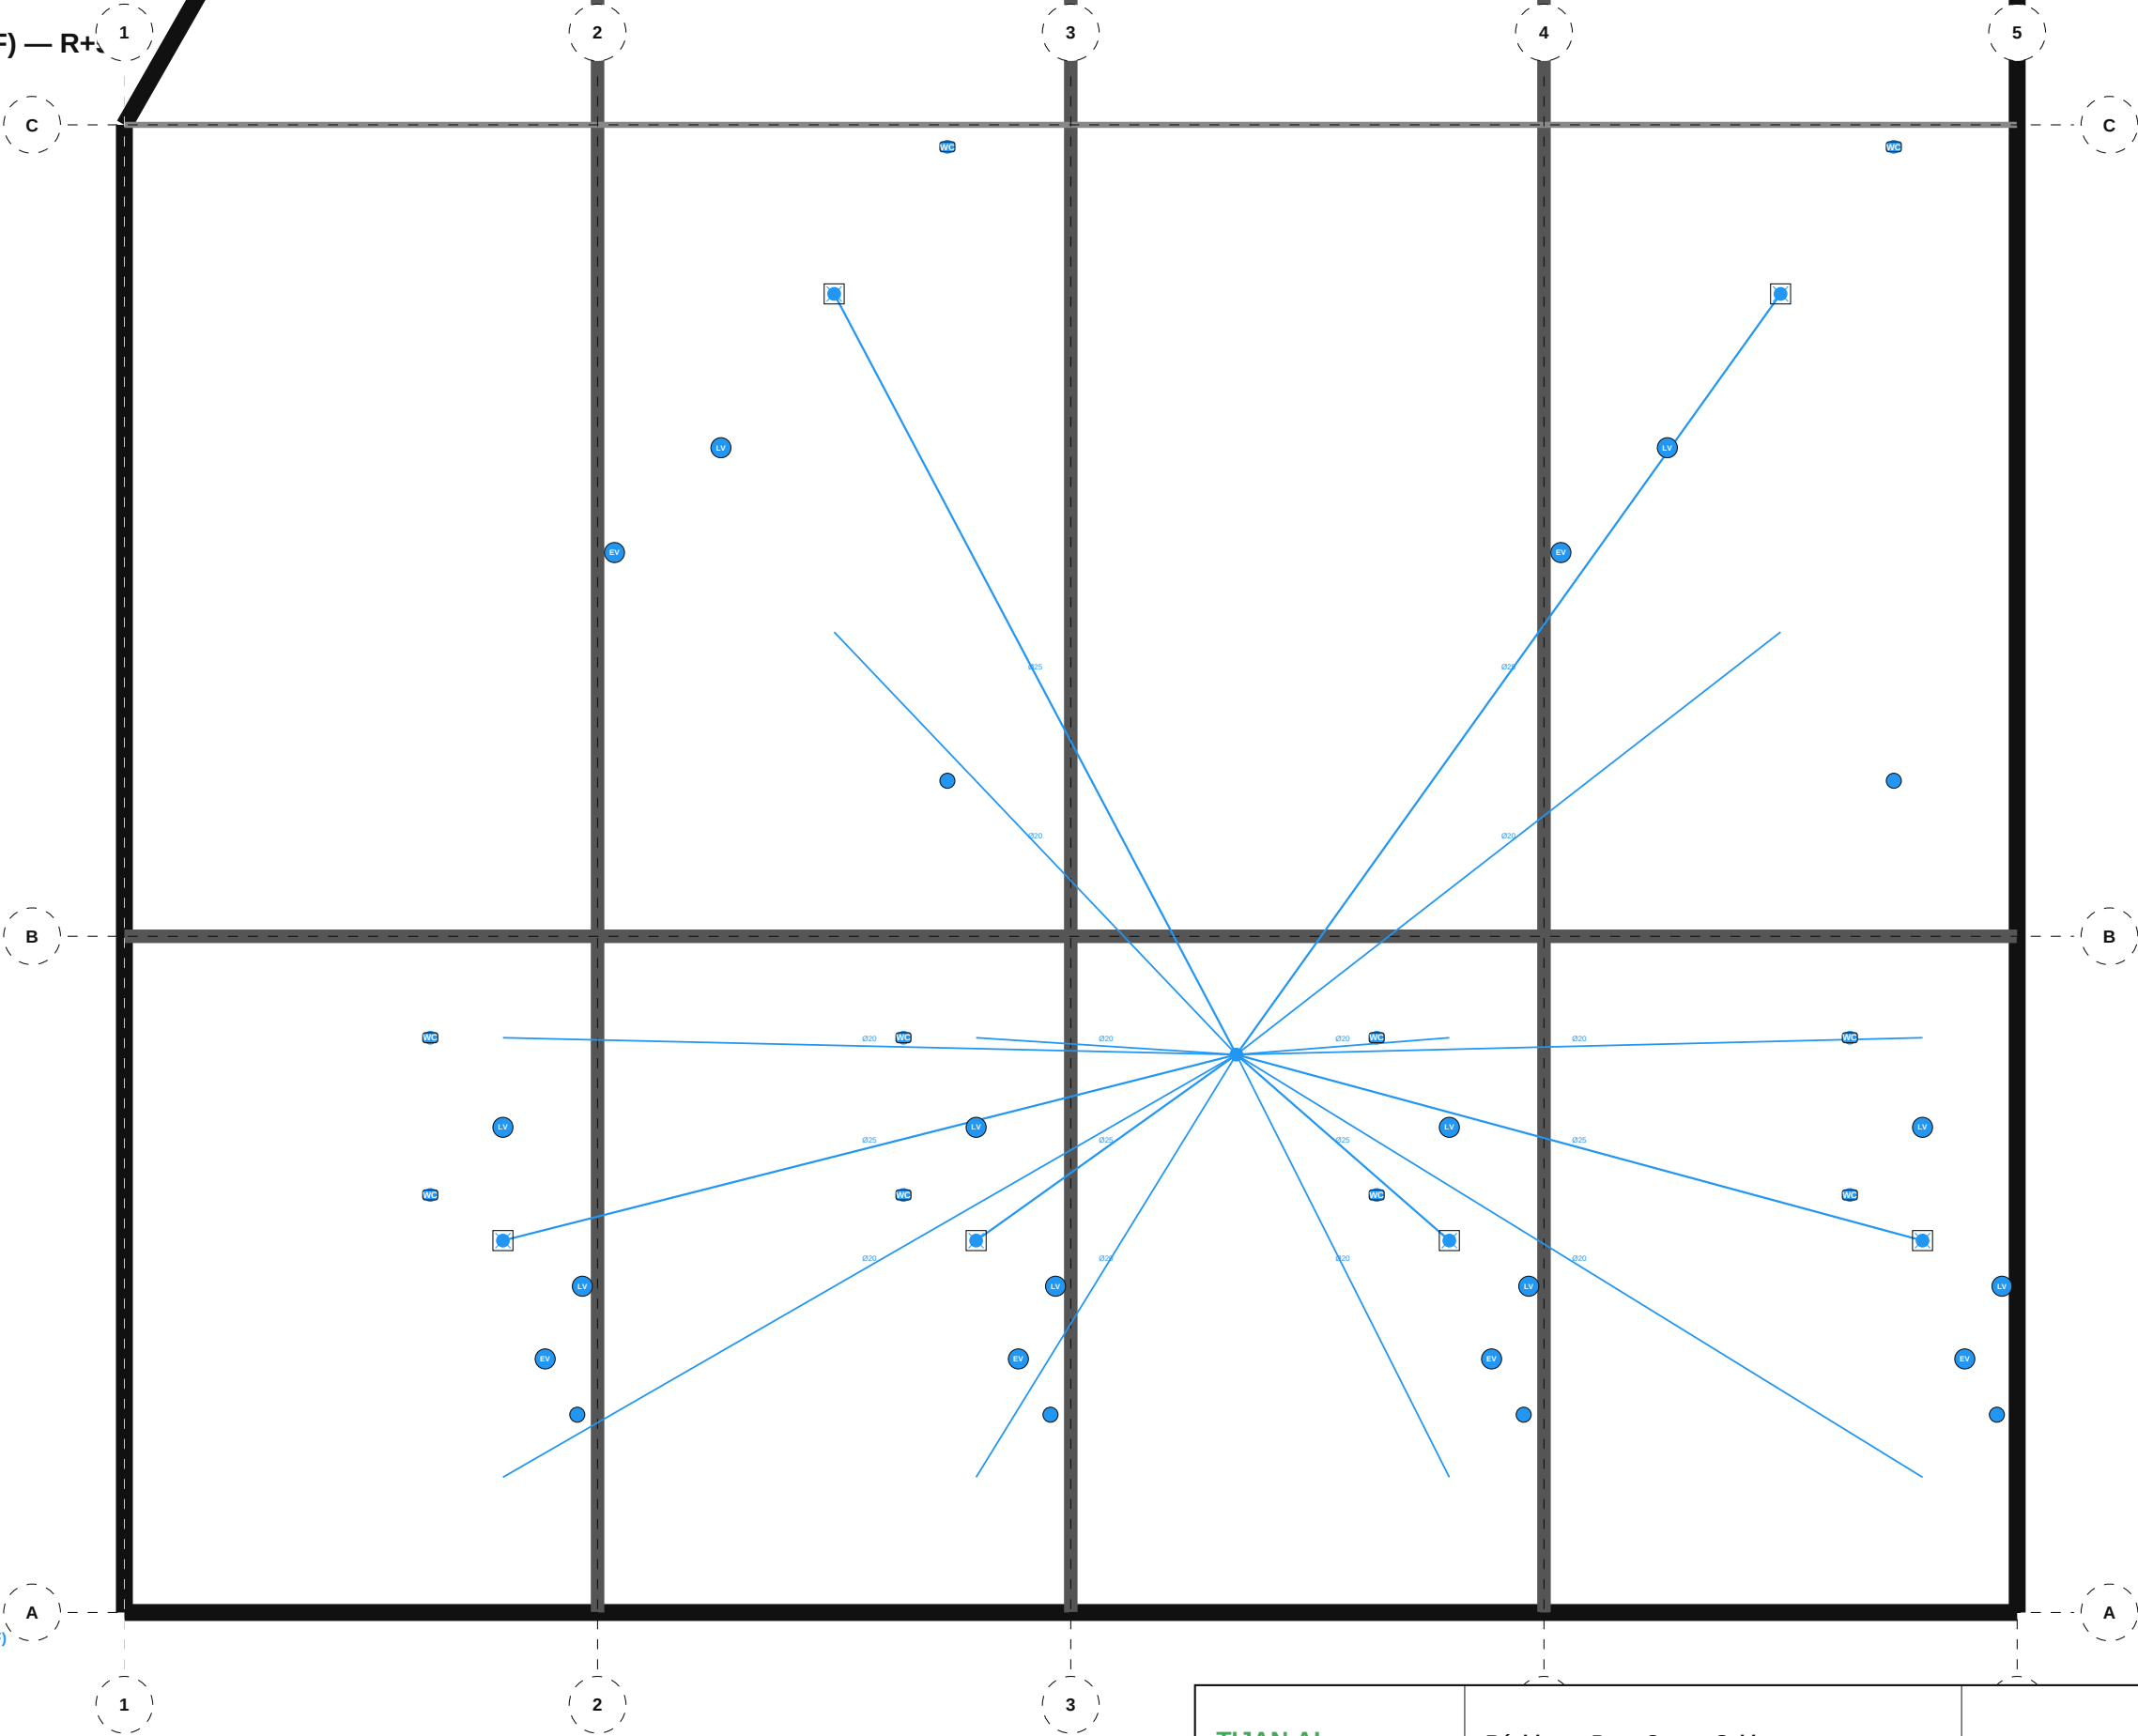

NOMENCLATURE — 410 PLU — Eau Froide (EF)

- WC suspendu: 10
- Évier cuisine: 6
- Lave-vaisselle: 6
- Lavabo: 6
- Douche: 6
- Lave-mains: 4

TIJAN AI

Bureau d'Études Automatisé

Résidence Papa Oumar Sakho

Dakar, Senegal

Éch: 1/100

Pl. 27/133


410 PLU — Eau Froide (EF) — R+5

Date: 06/05/2026

Réf: 1711

BIM vPLU-027

Phase: APD

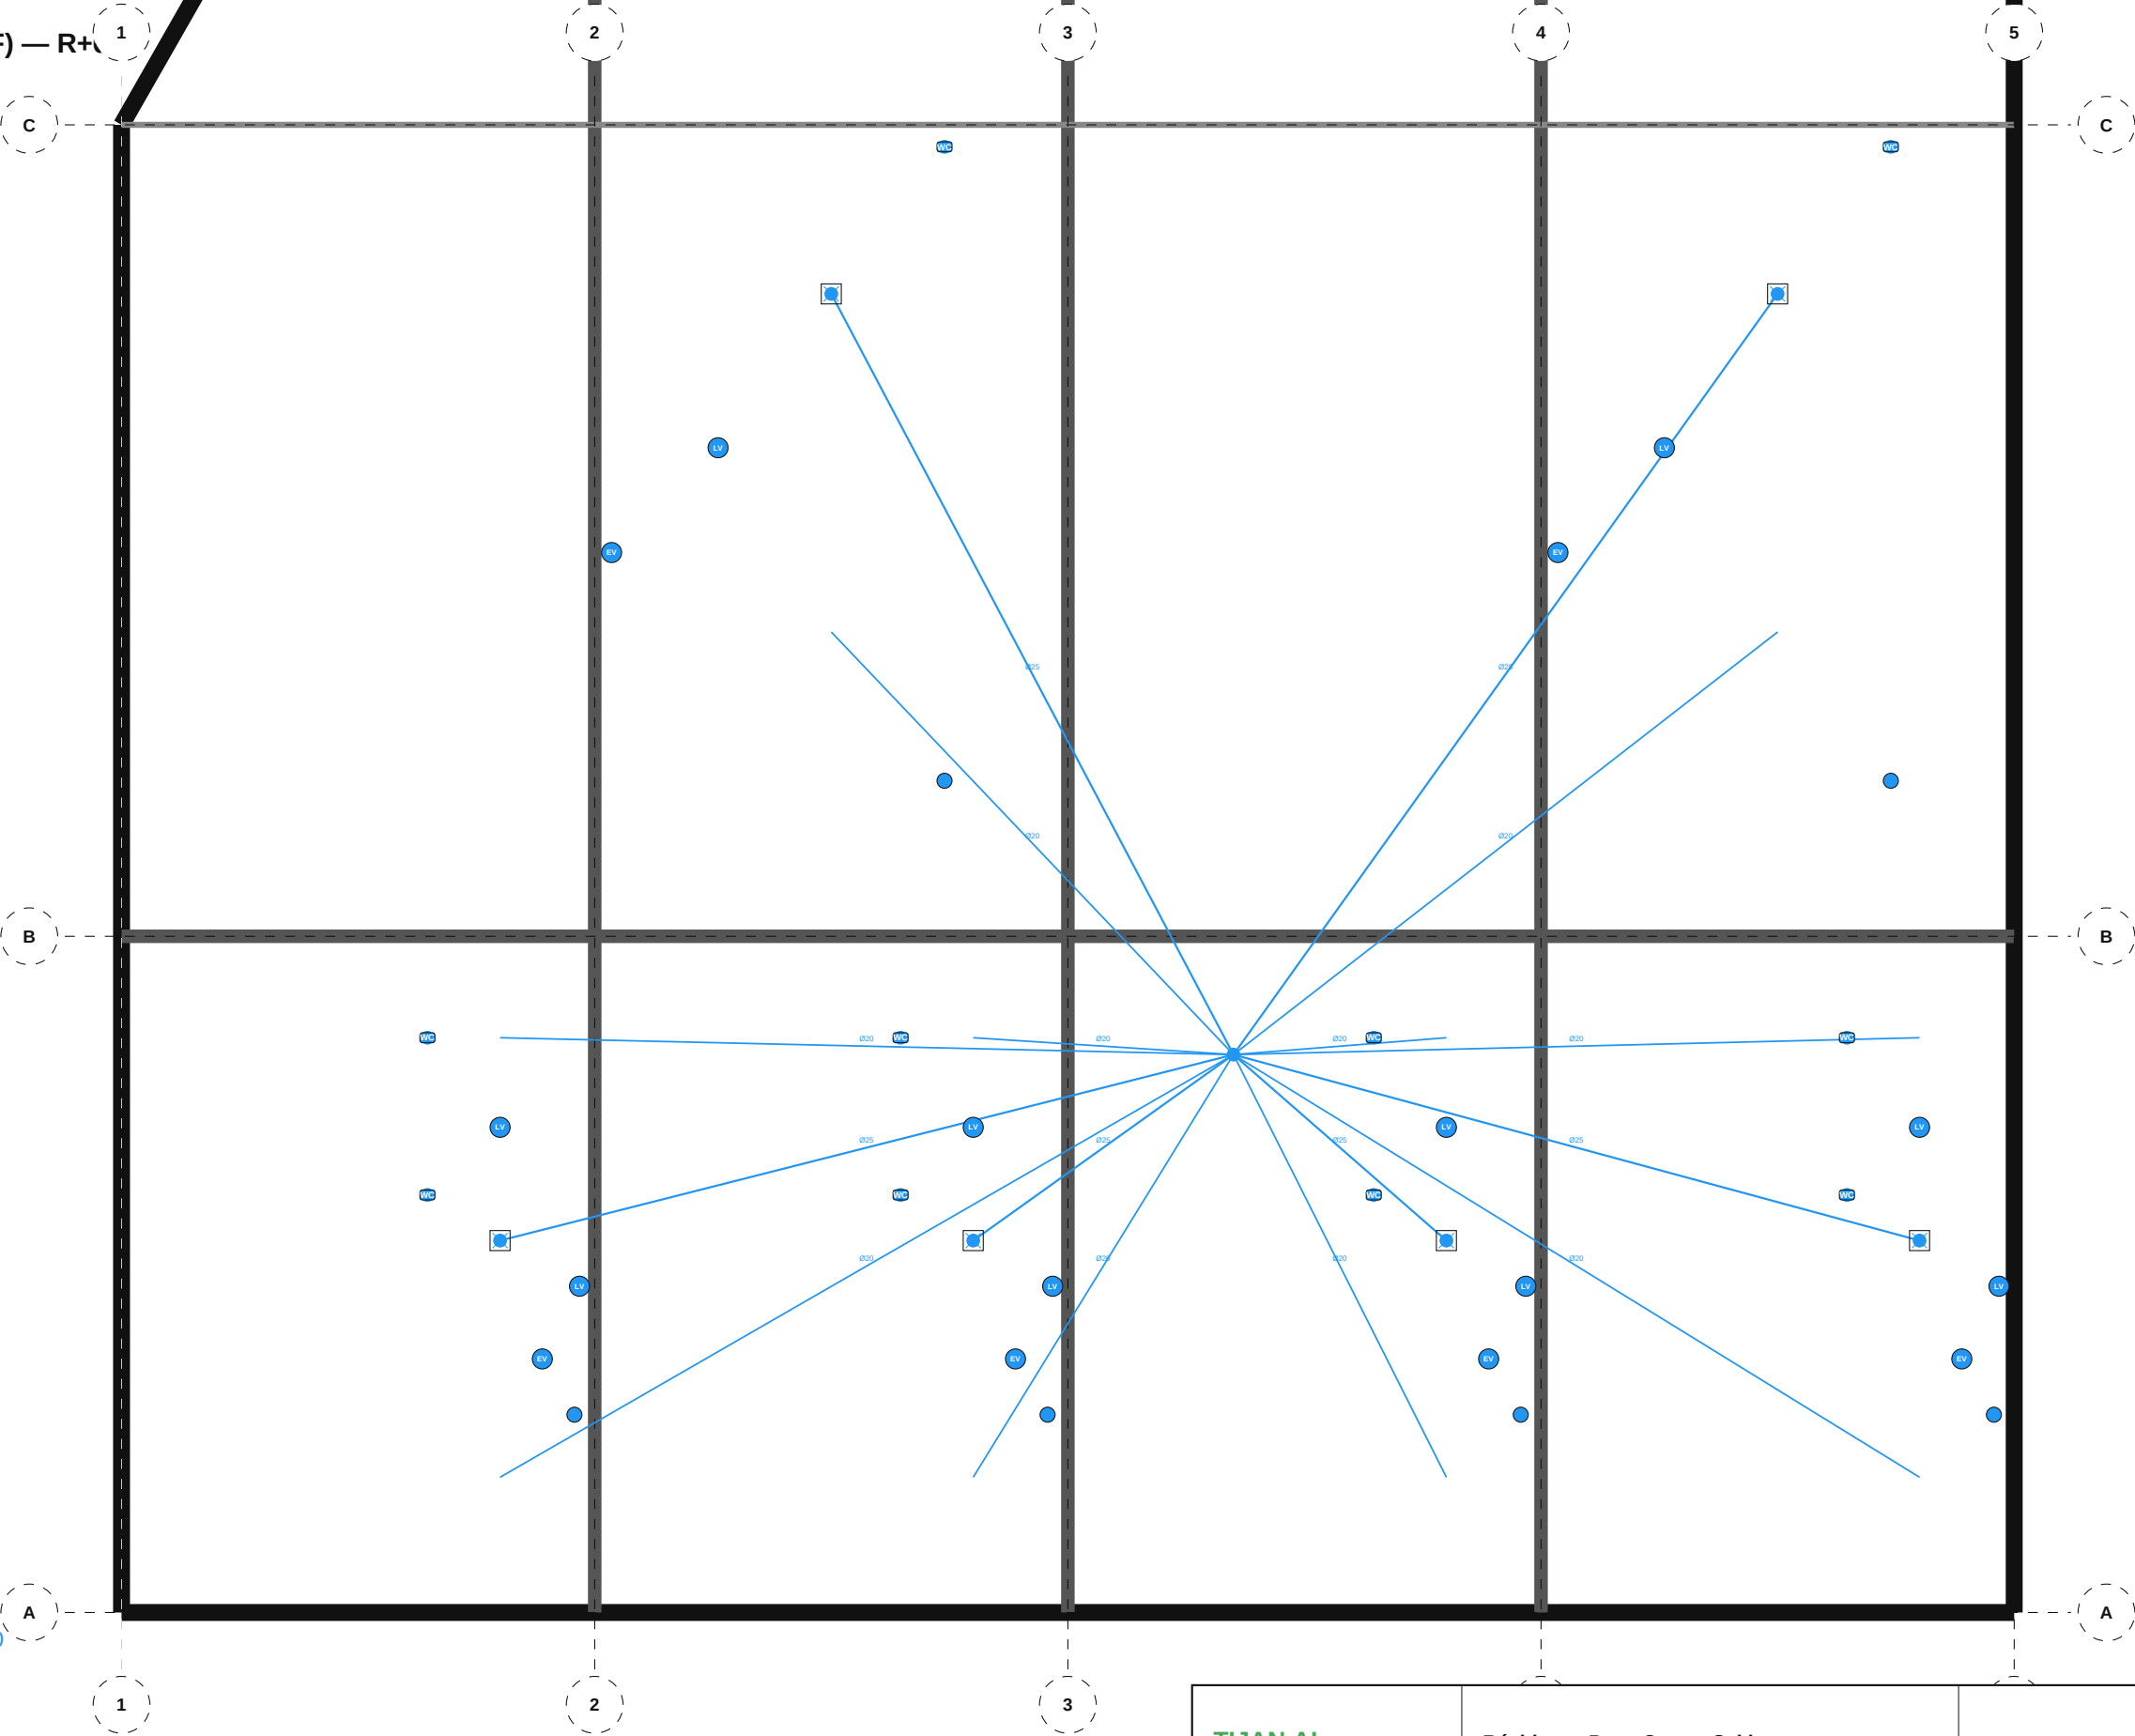

NOMENCLATURE — 410 PLU — Eau Froide (EF)

- WC suspendu: 10
- Évier cuisine: 6
- Lave-vaisselle: 6
- Lavabo: 6
- Douche: 6
- Lave-mains: 4

TIJAN AI

Bureau d'Études Automatisé

Résidence Papa Oumar Sakho

Dakar, Senegal

Éch: 1/100

Pl. 28/133


410 PLU — Eau Froide (EF) — R+6

Date: 06/05/2026

Réf: 1711

BIM vPLU-028

Phase: APD

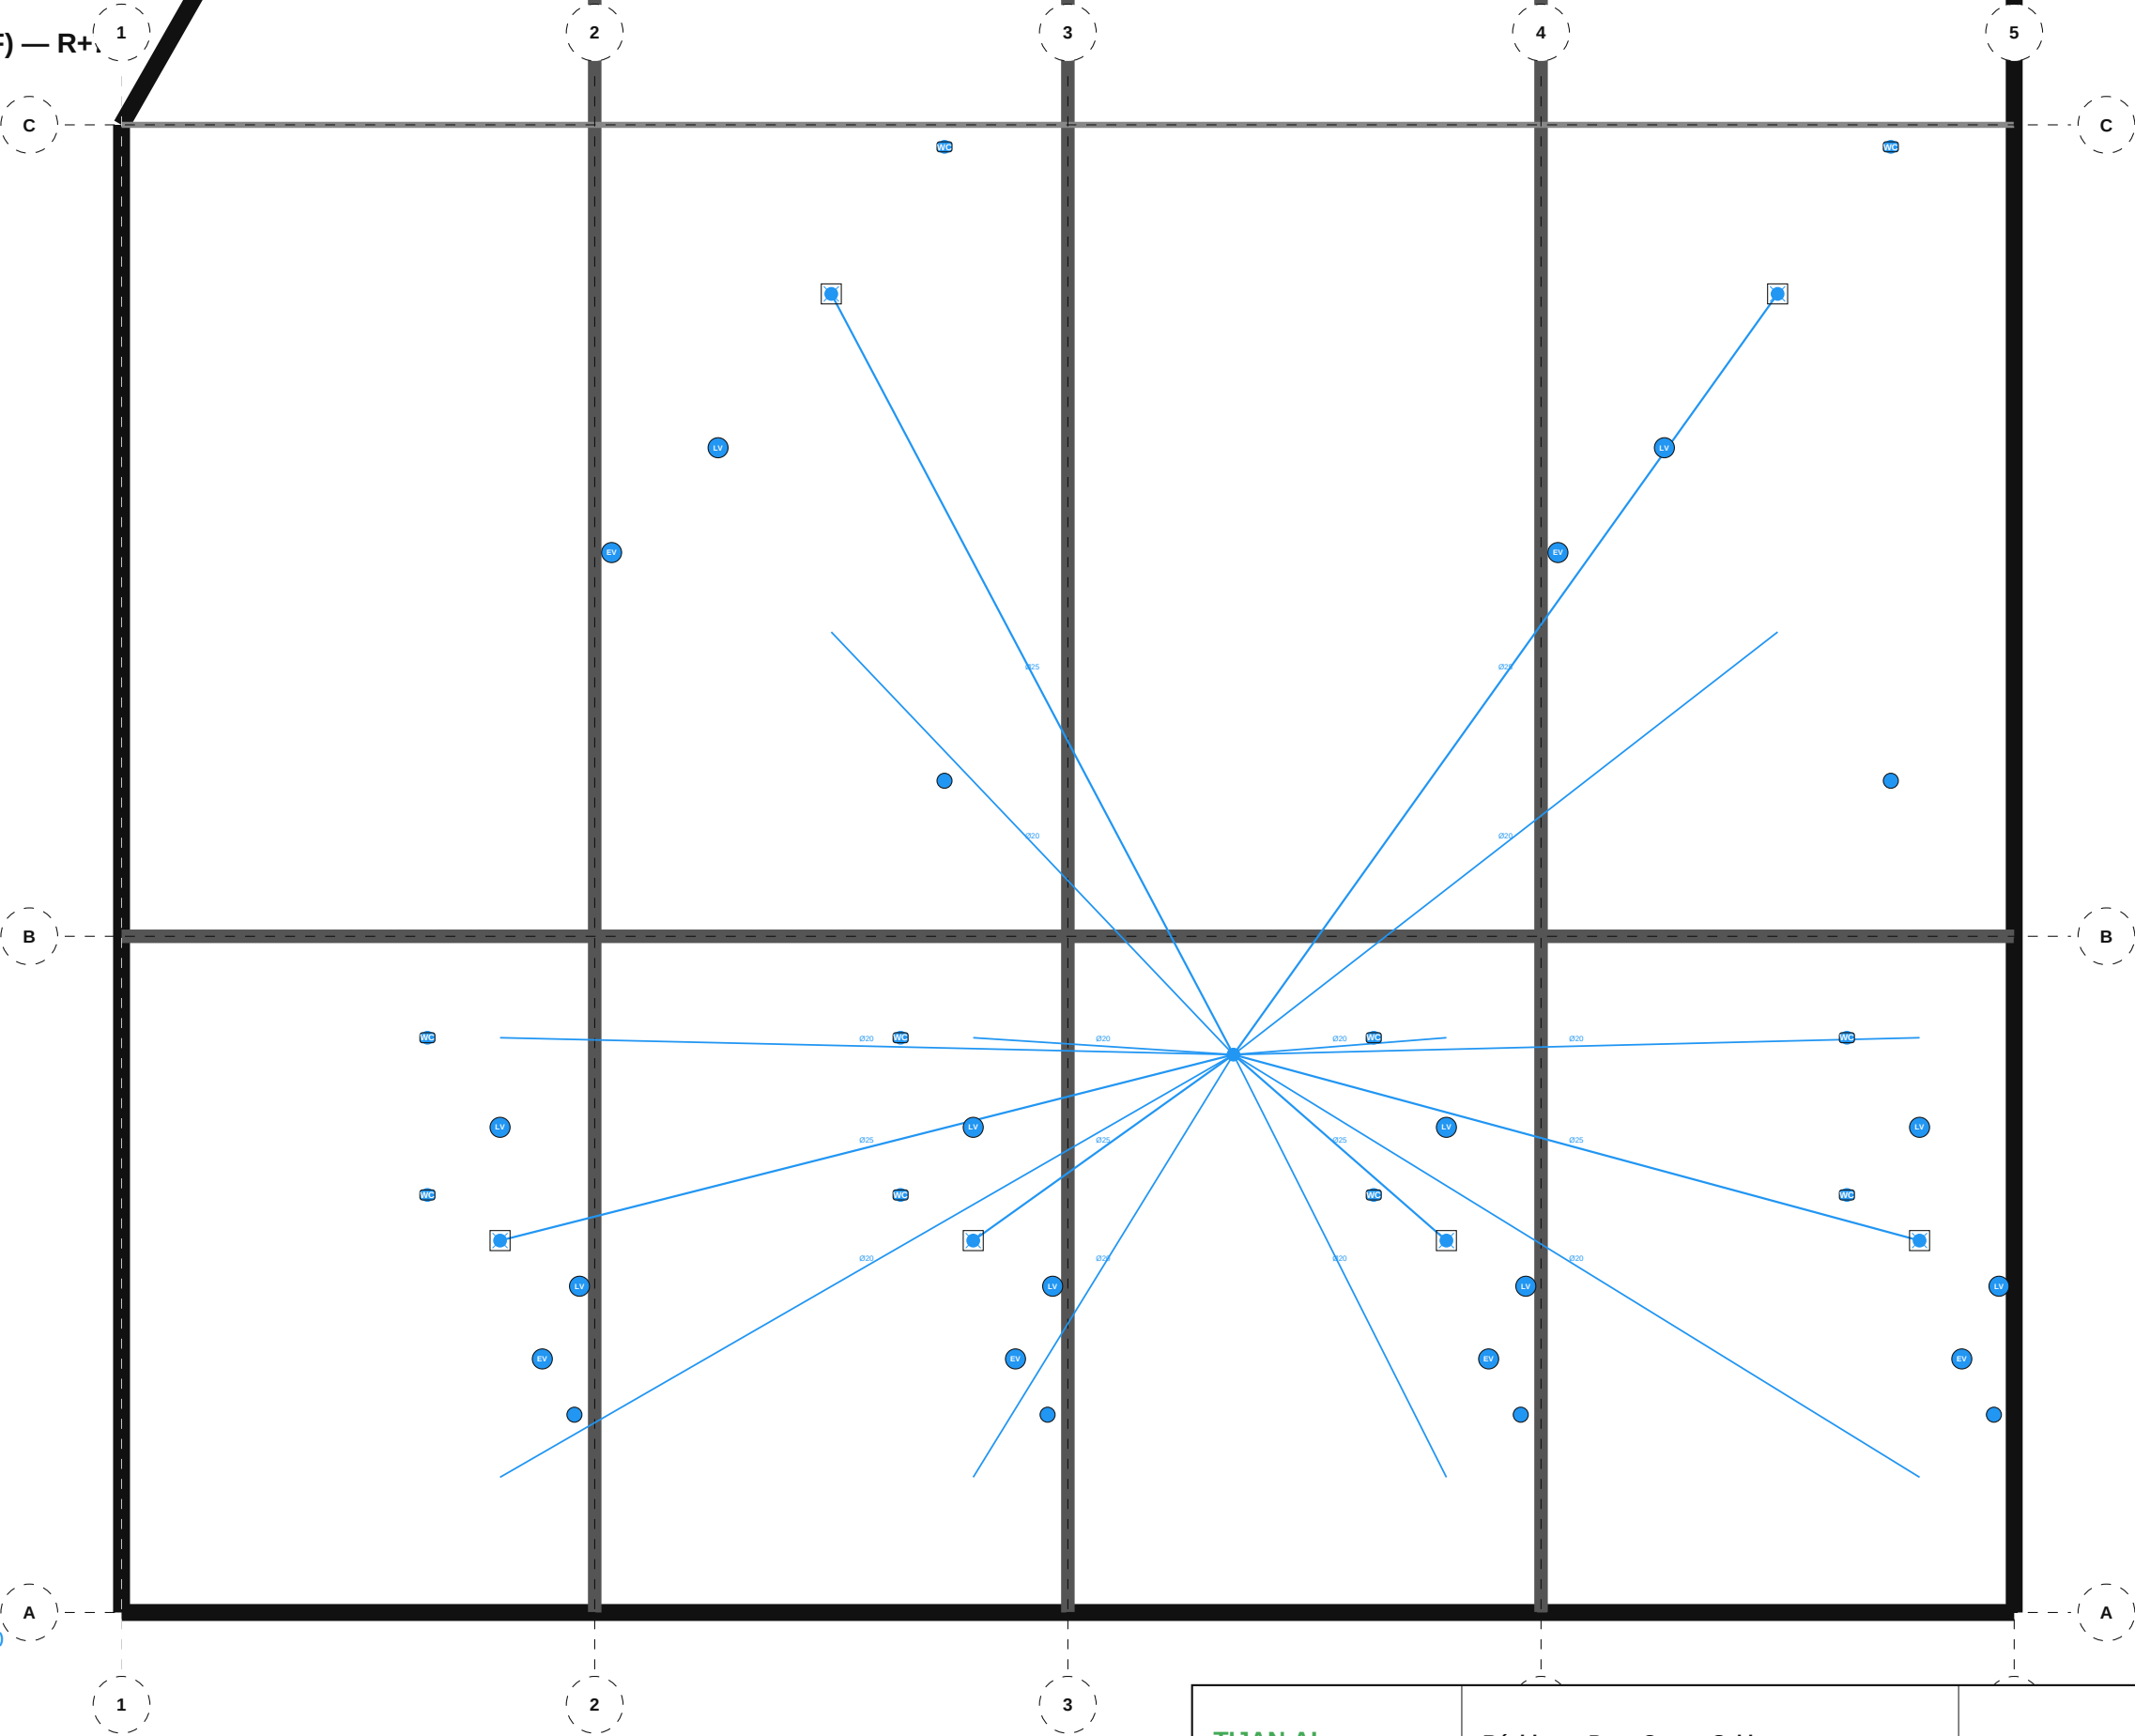

NOMENCLATURE — 410 PLU — Eau Froide (EF)

- WC suspendu: 10
- Évier cuisine: 6
- Lave-vaisselle: 6
- Lavabo: 6
- Douche: 6
- Lave-mains: 4

TIJAN AI

Bureau d'Études Automatisé

Résidence Papa Oumar Sakho

Dakar, Senegal

Éch: 1/100

Pl. 29/133


410 PLU — Eau Froide (EF) — R+7

Date: 06/05/2026

Réf: 1711

BIM vPLU-029

Phase: APD

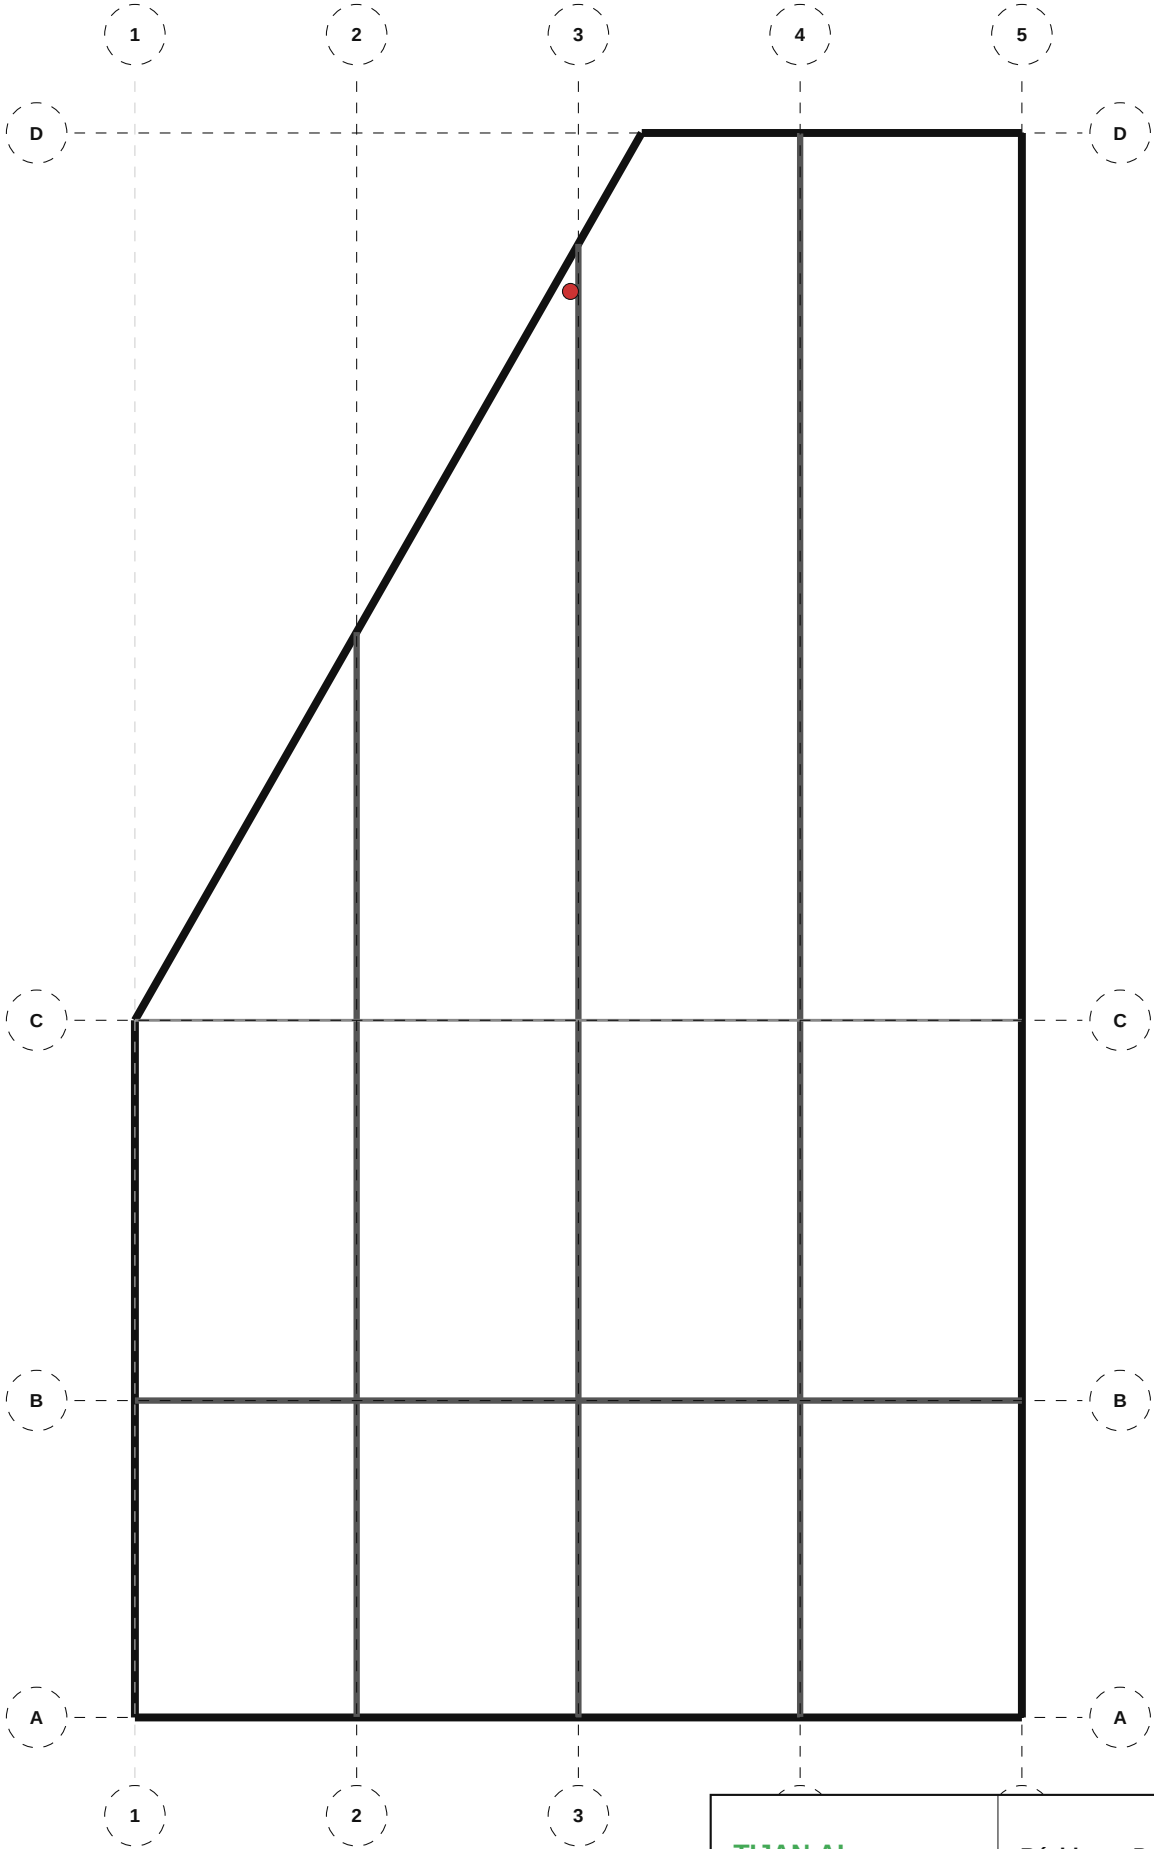

NOMENCLATURE — 410 PLU — Eau Chaude (EC)

• Chauffe-eau: 1

TIJAN AI Bureau d'Études Automatisé	Résidence Papa Oumar Sakho Dakar, Senegal	Éch: 1/100 Pl. 30/133
	410 PLU — Eau Chaude (EC) — Sous-Sol	
Date: 06/05/2026	Réf: 1711	BIM vPLU-030 Phase: APD

410 PLU — Eau Chaude (EC) — RDC

1

2

3

4

5

B

B

A

A

NOMENCLATURE — 410 PLU — Eau Chaude (EC)

• Chauffe-eau: 1

1

2

3

4

5

TIJAN AI

Bureau d'Études Automatisé

Résidence Papa Oumar Sakho

Dakar, Senegal

Éch: 1/100

Pl. 31/133


410 PLU — Eau Chaude (EC) — RDC

Date: 06/05/2026

Réf: 1711

BIM vPLU-031

Phase: APD

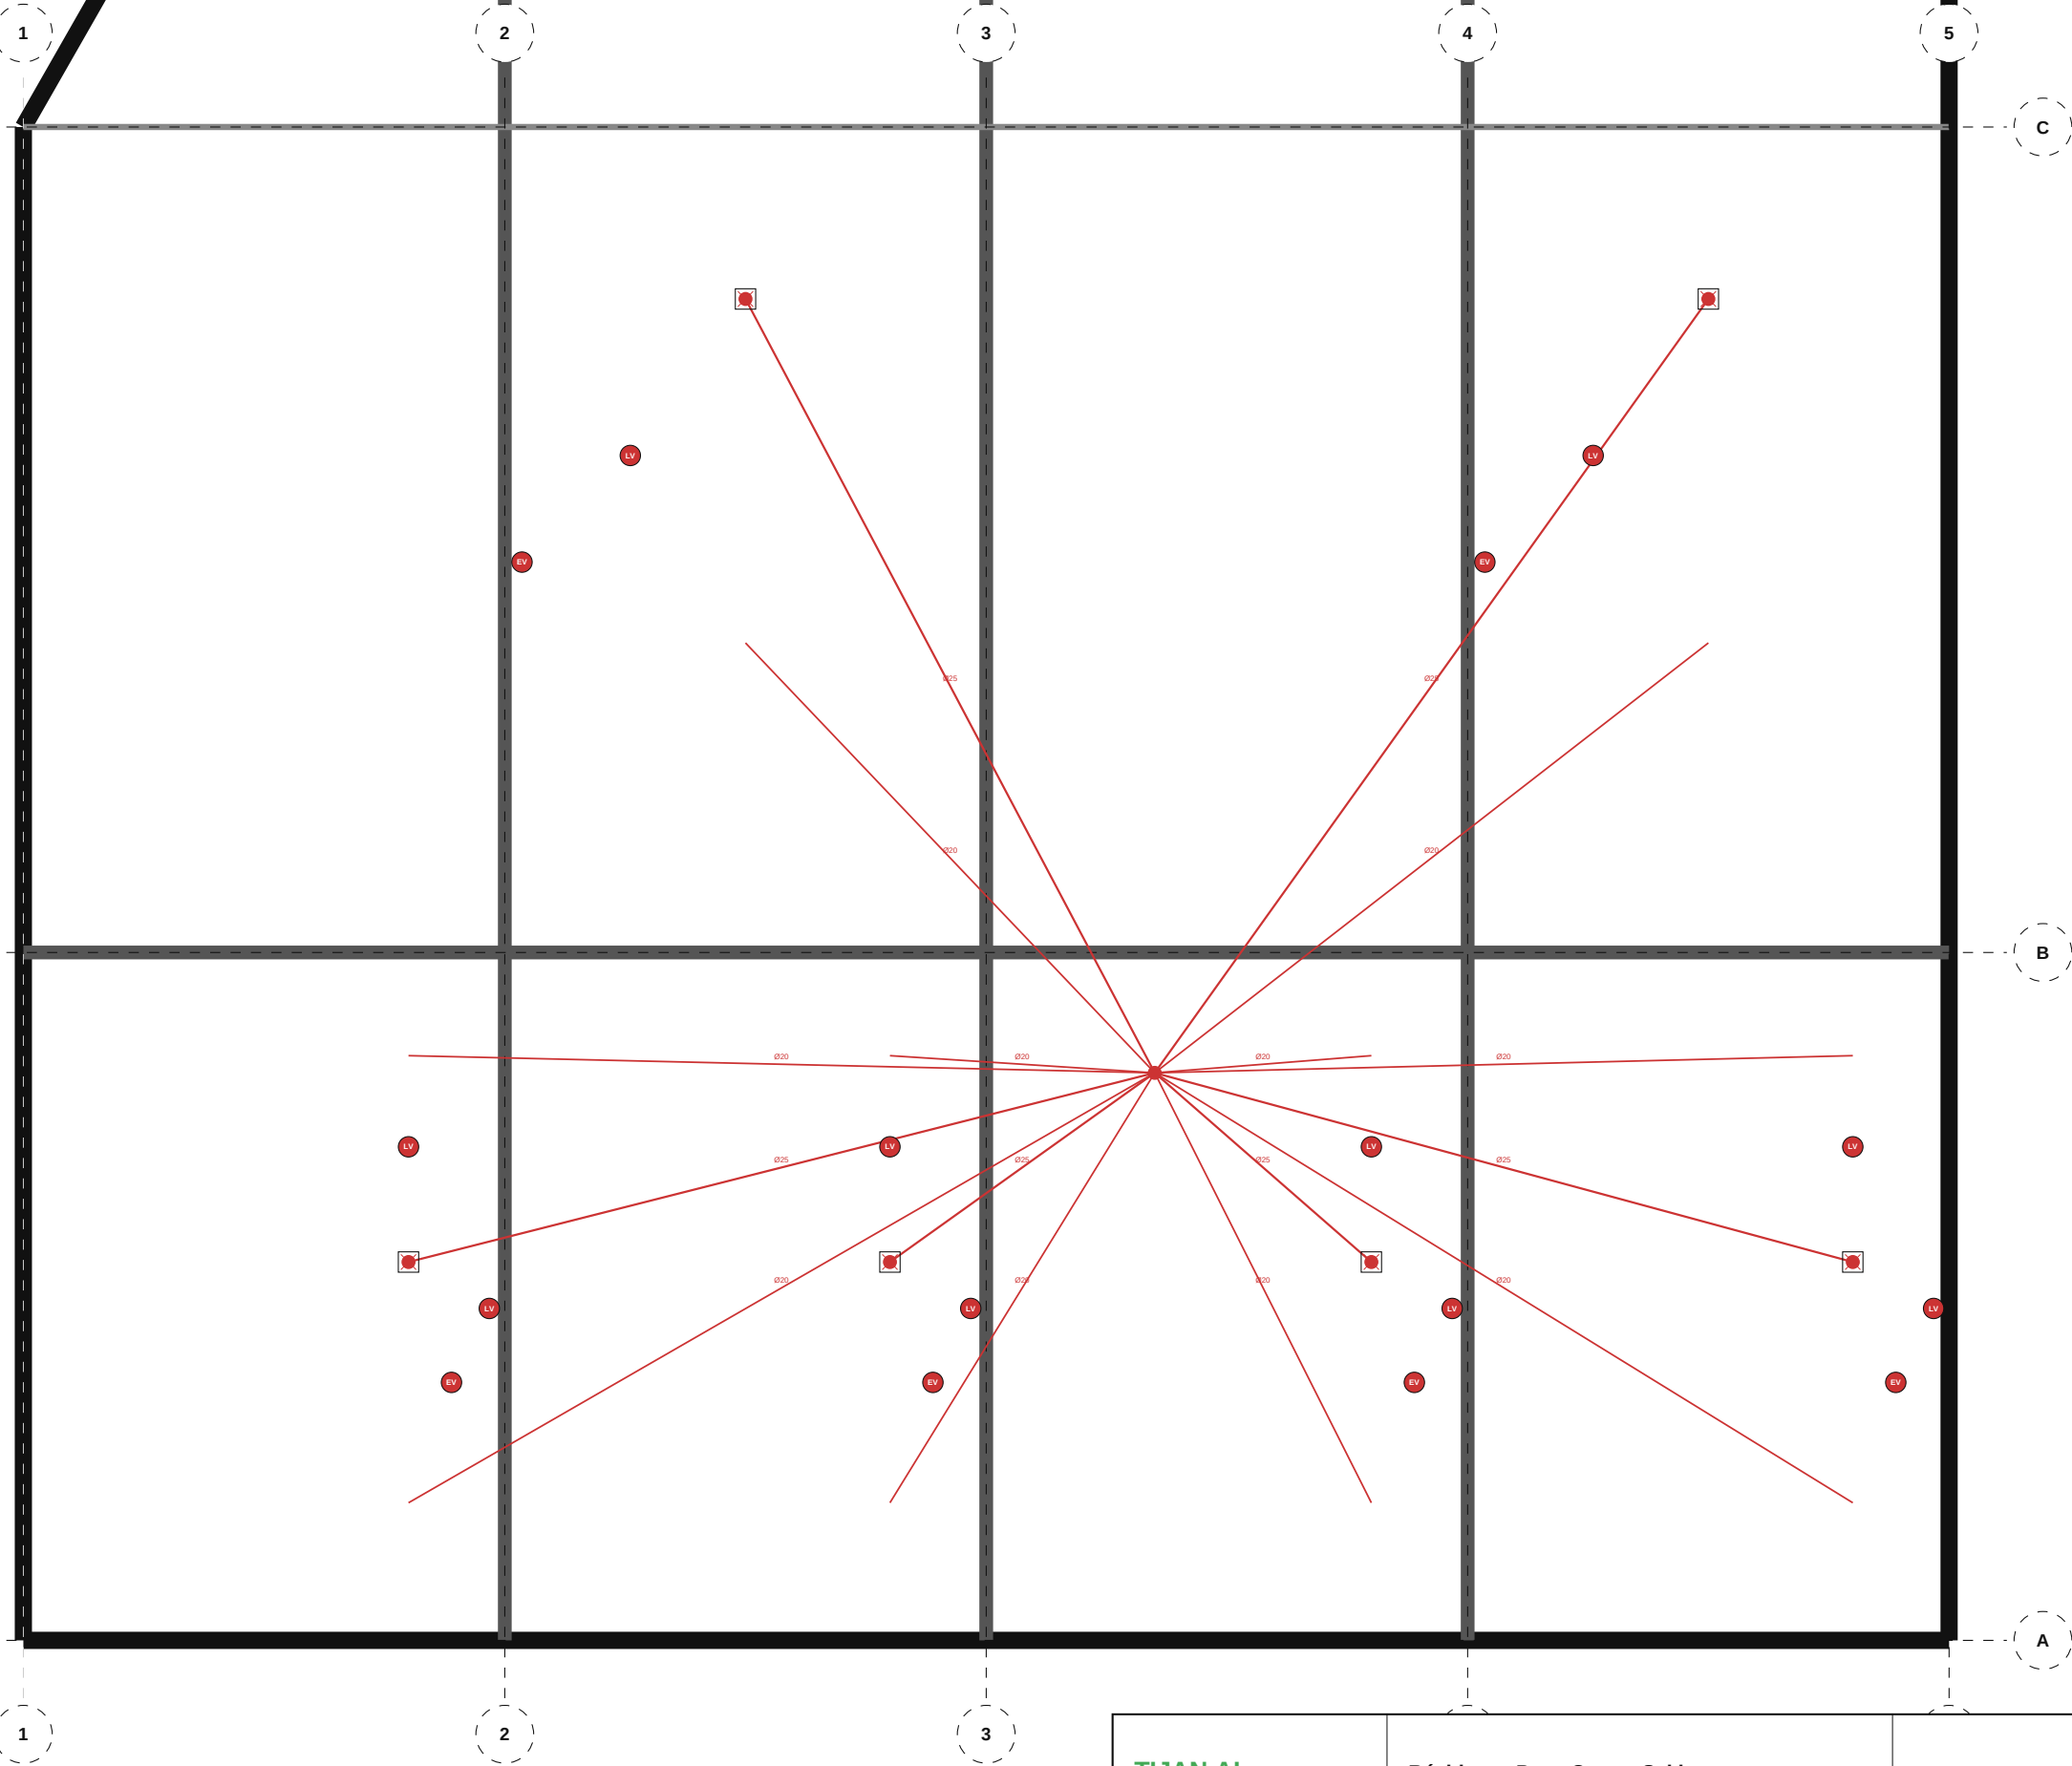

NOMENCLATURE — 410 PLU — Eau Chaude (EC)

- Évier cuisine: 6
- Lavabo: 6
- Douche: 6
- Lave-mains: 4

TIJAN AI

Bureau d'Études Automatisé

Résidence Papa Oumar Sakho

Dakar, Senegal

Éch: 1/100

Pl. 32/133


410 PLU — Eau Chaude (EC) — R+1

Date: 06/05/2026

Réf: 1711

BIM vPLU-032


Phase: APD

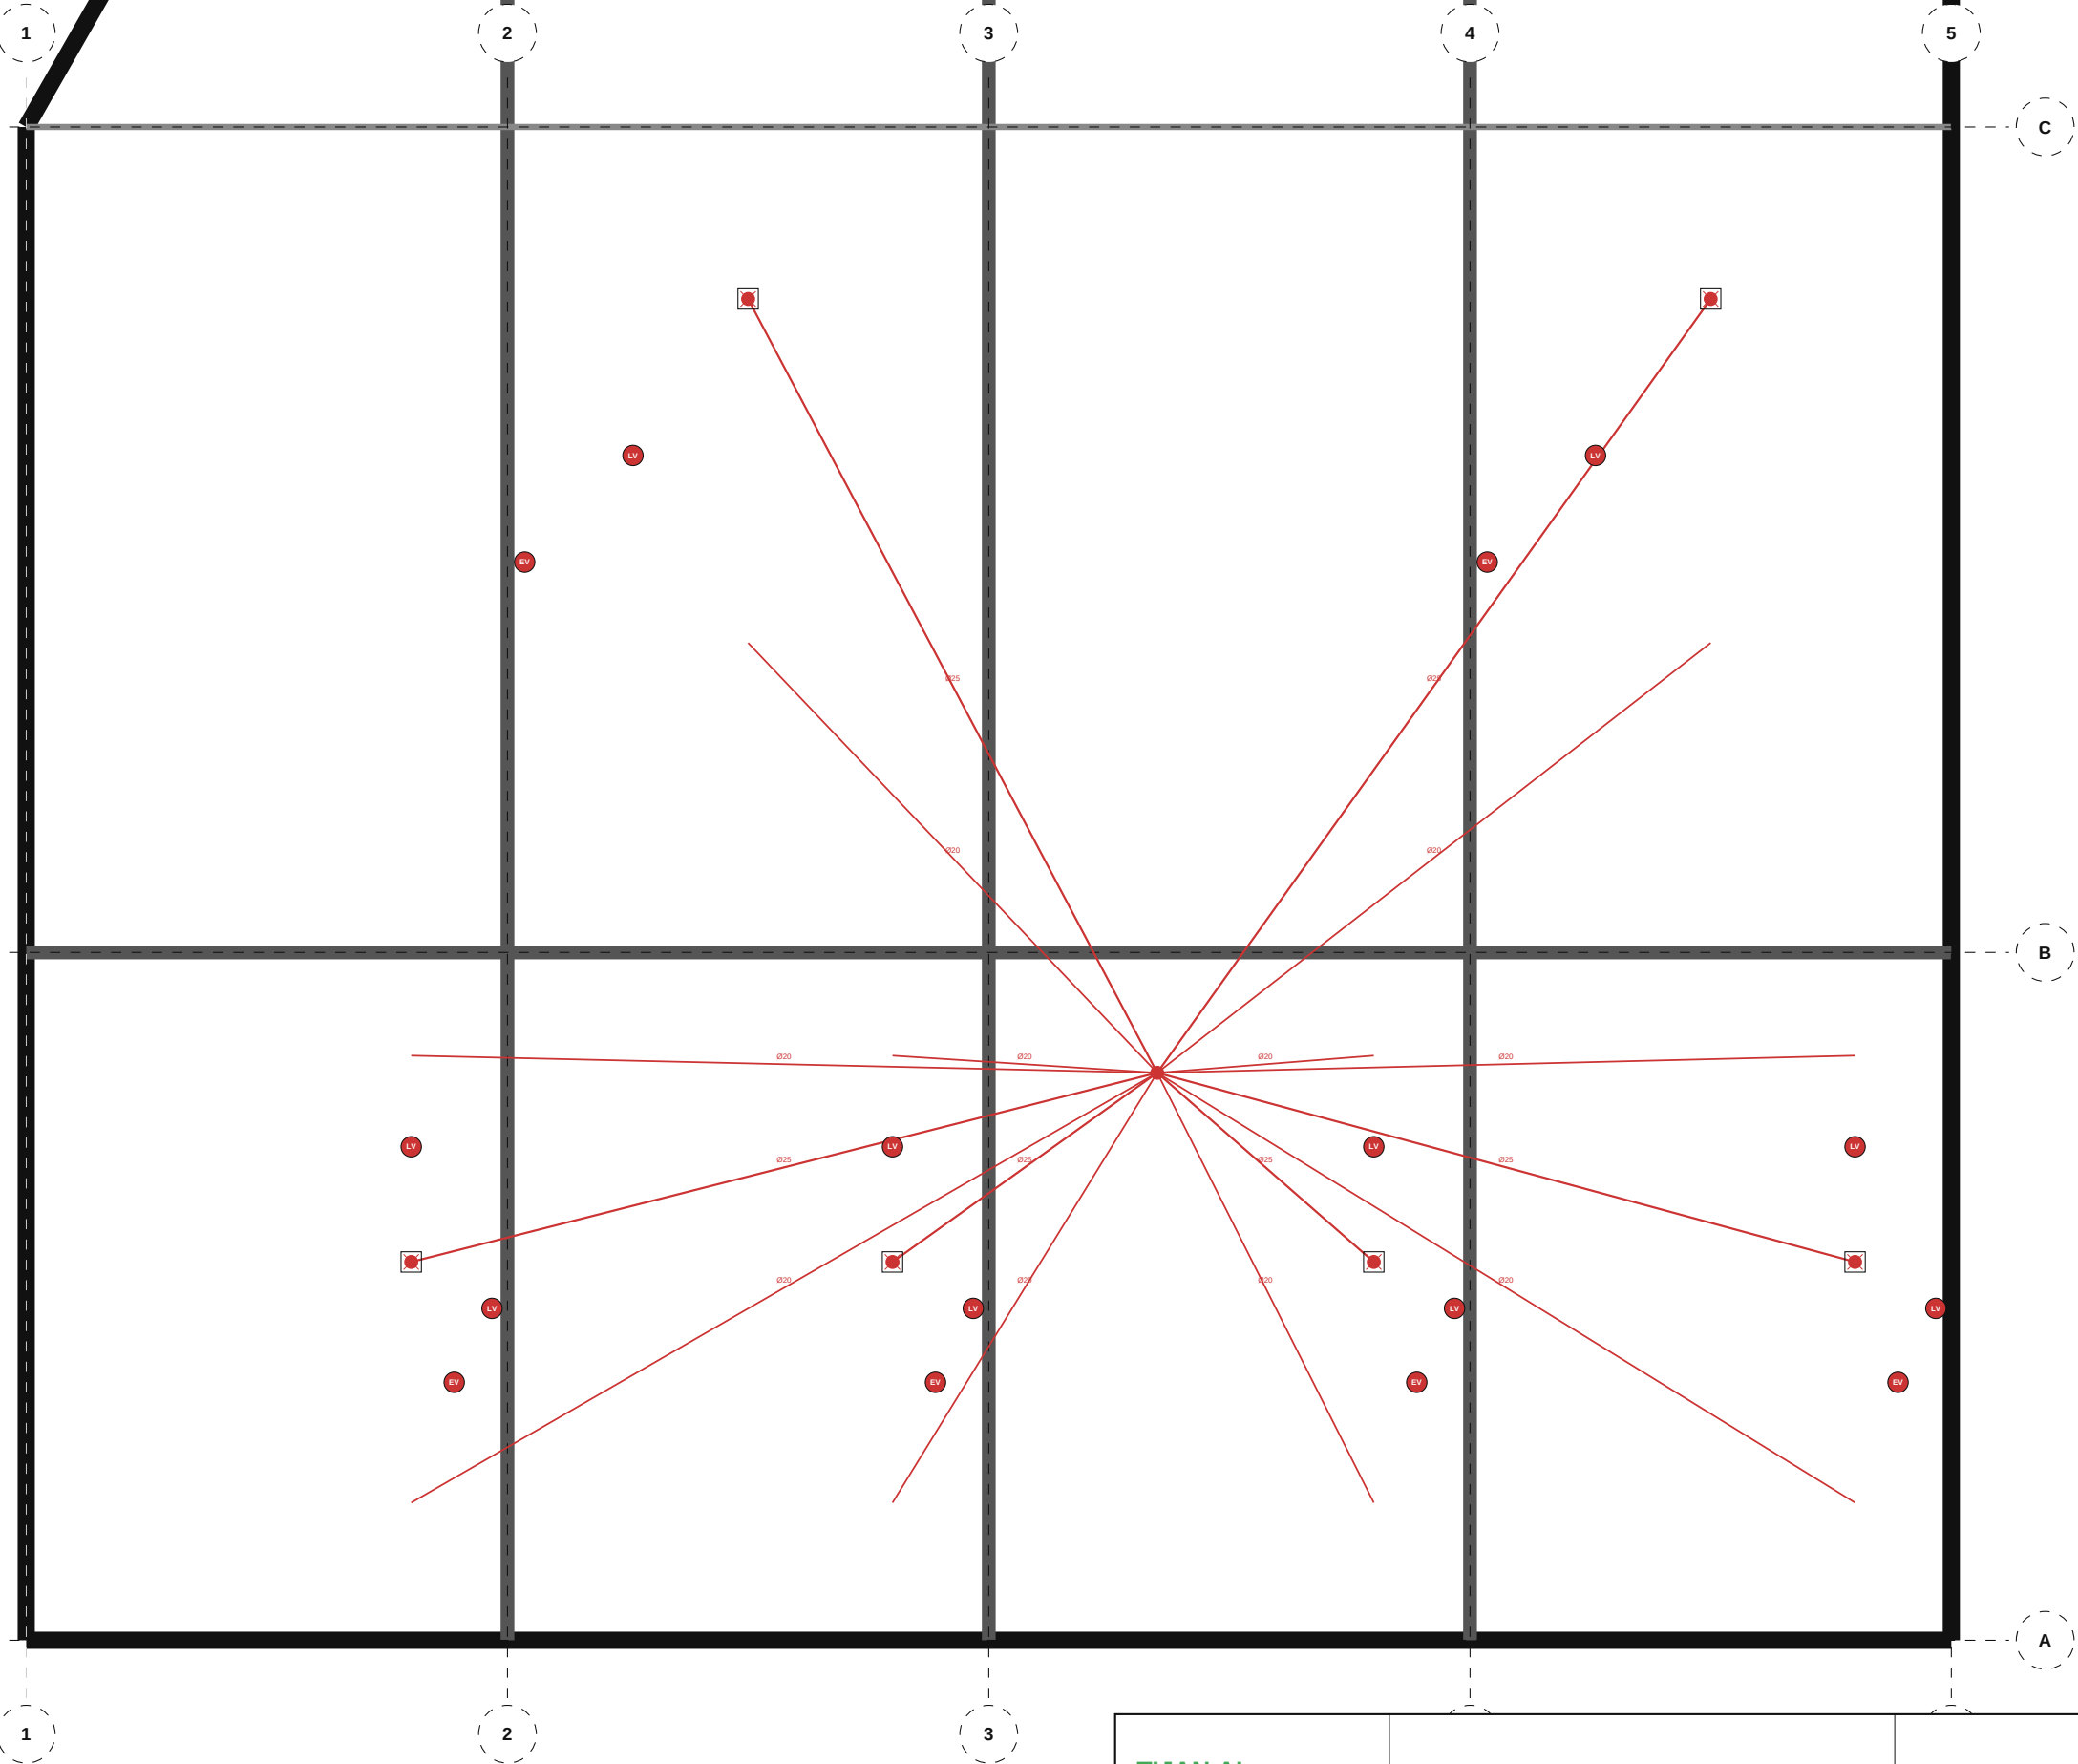

NOMENCLATURE — 410 PLU — Eau Chaude (EC)

- Évier cuisine: 6
- Lavabo: 6
- Douche: 6
- Lave-mains: 4

TIJAN AI Bureau d'Études Automatisé	Résidence Papa Oumar Sakho Dakar, Senegal	Éch: 1/100 Pl. 33/133
	410 PLU — Eau Chaude (EC) — R+2	
Date: 06/05/2026	Réf: 1711	BIM vPLU-033 Phase: APD

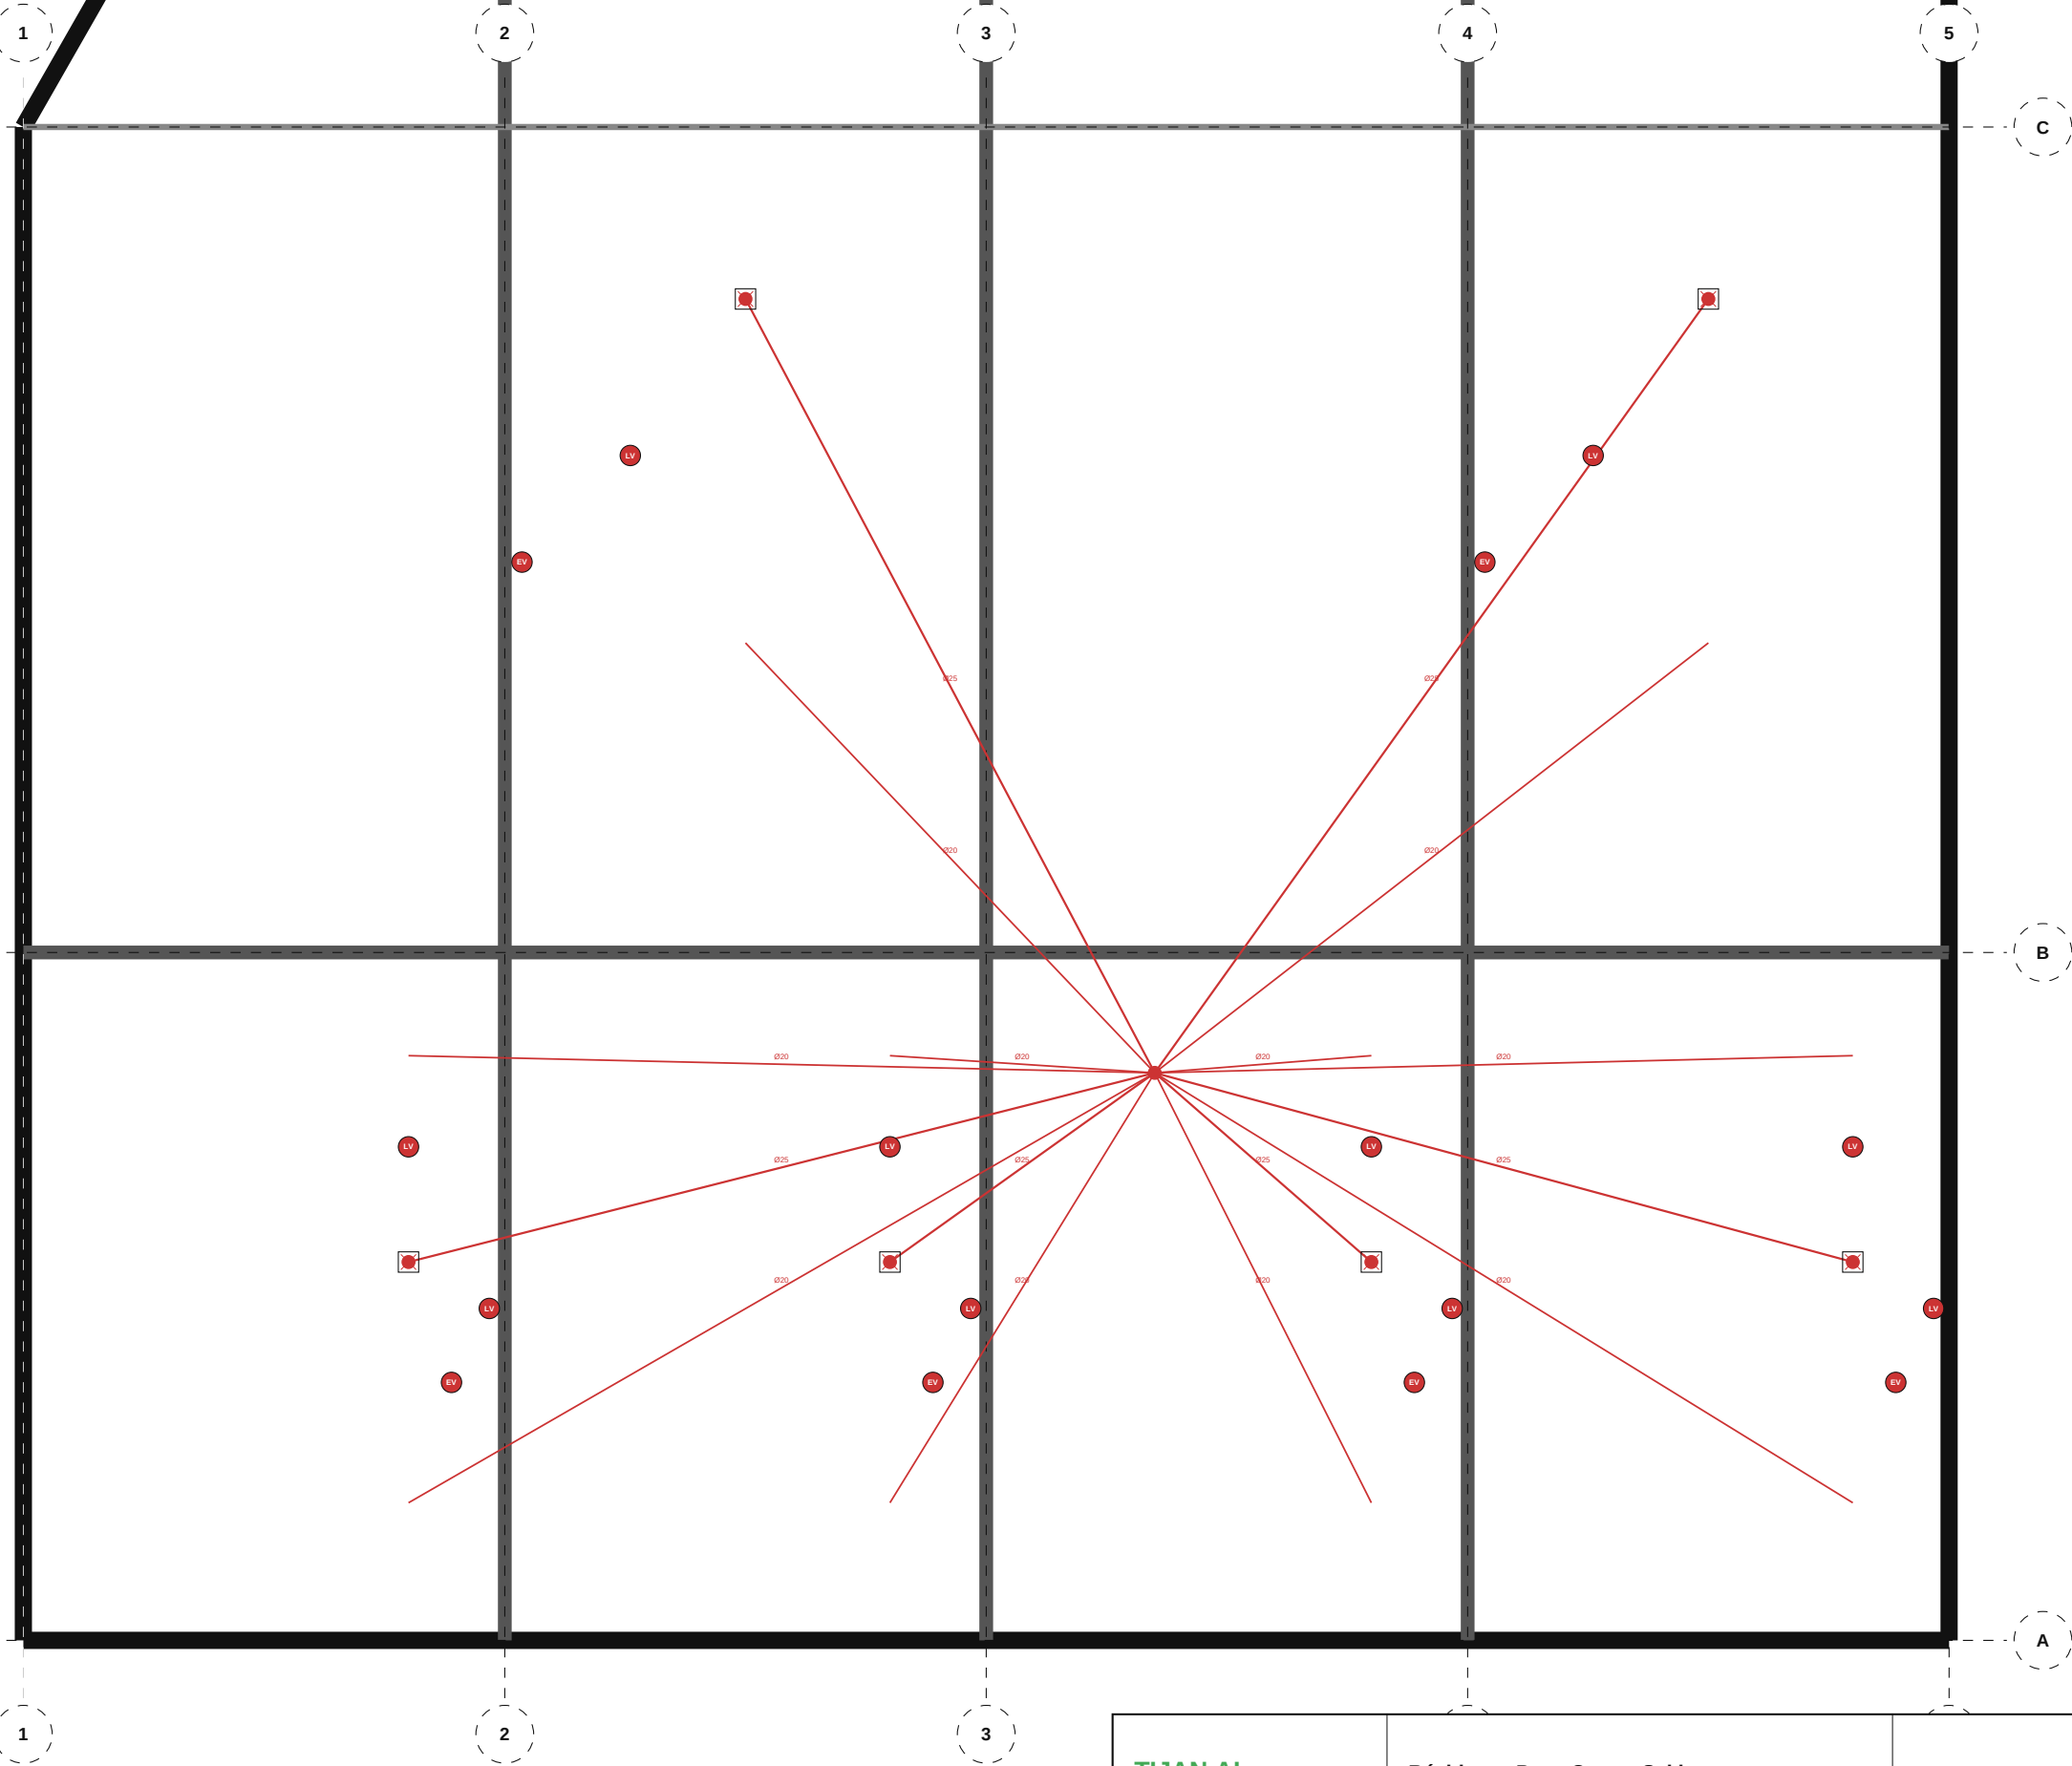

NOMENCLATURE — 410 PLU — Eau Chaude (EC)

- Évier cuisine: 6
- Lavabo: 6
- Douche: 6
- Lave-mains: 4

TIJAN AI

Bureau d'Études Automatisé

Résidence Papa Oumar Sakho

Dakar, Senegal

Éch: 1/100

Pl. 34/133


410 PLU — Eau Chaude (EC) — R+3

Date: 06/05/2026

Réf: 1711

BIM vPLU-034

Phase: APD

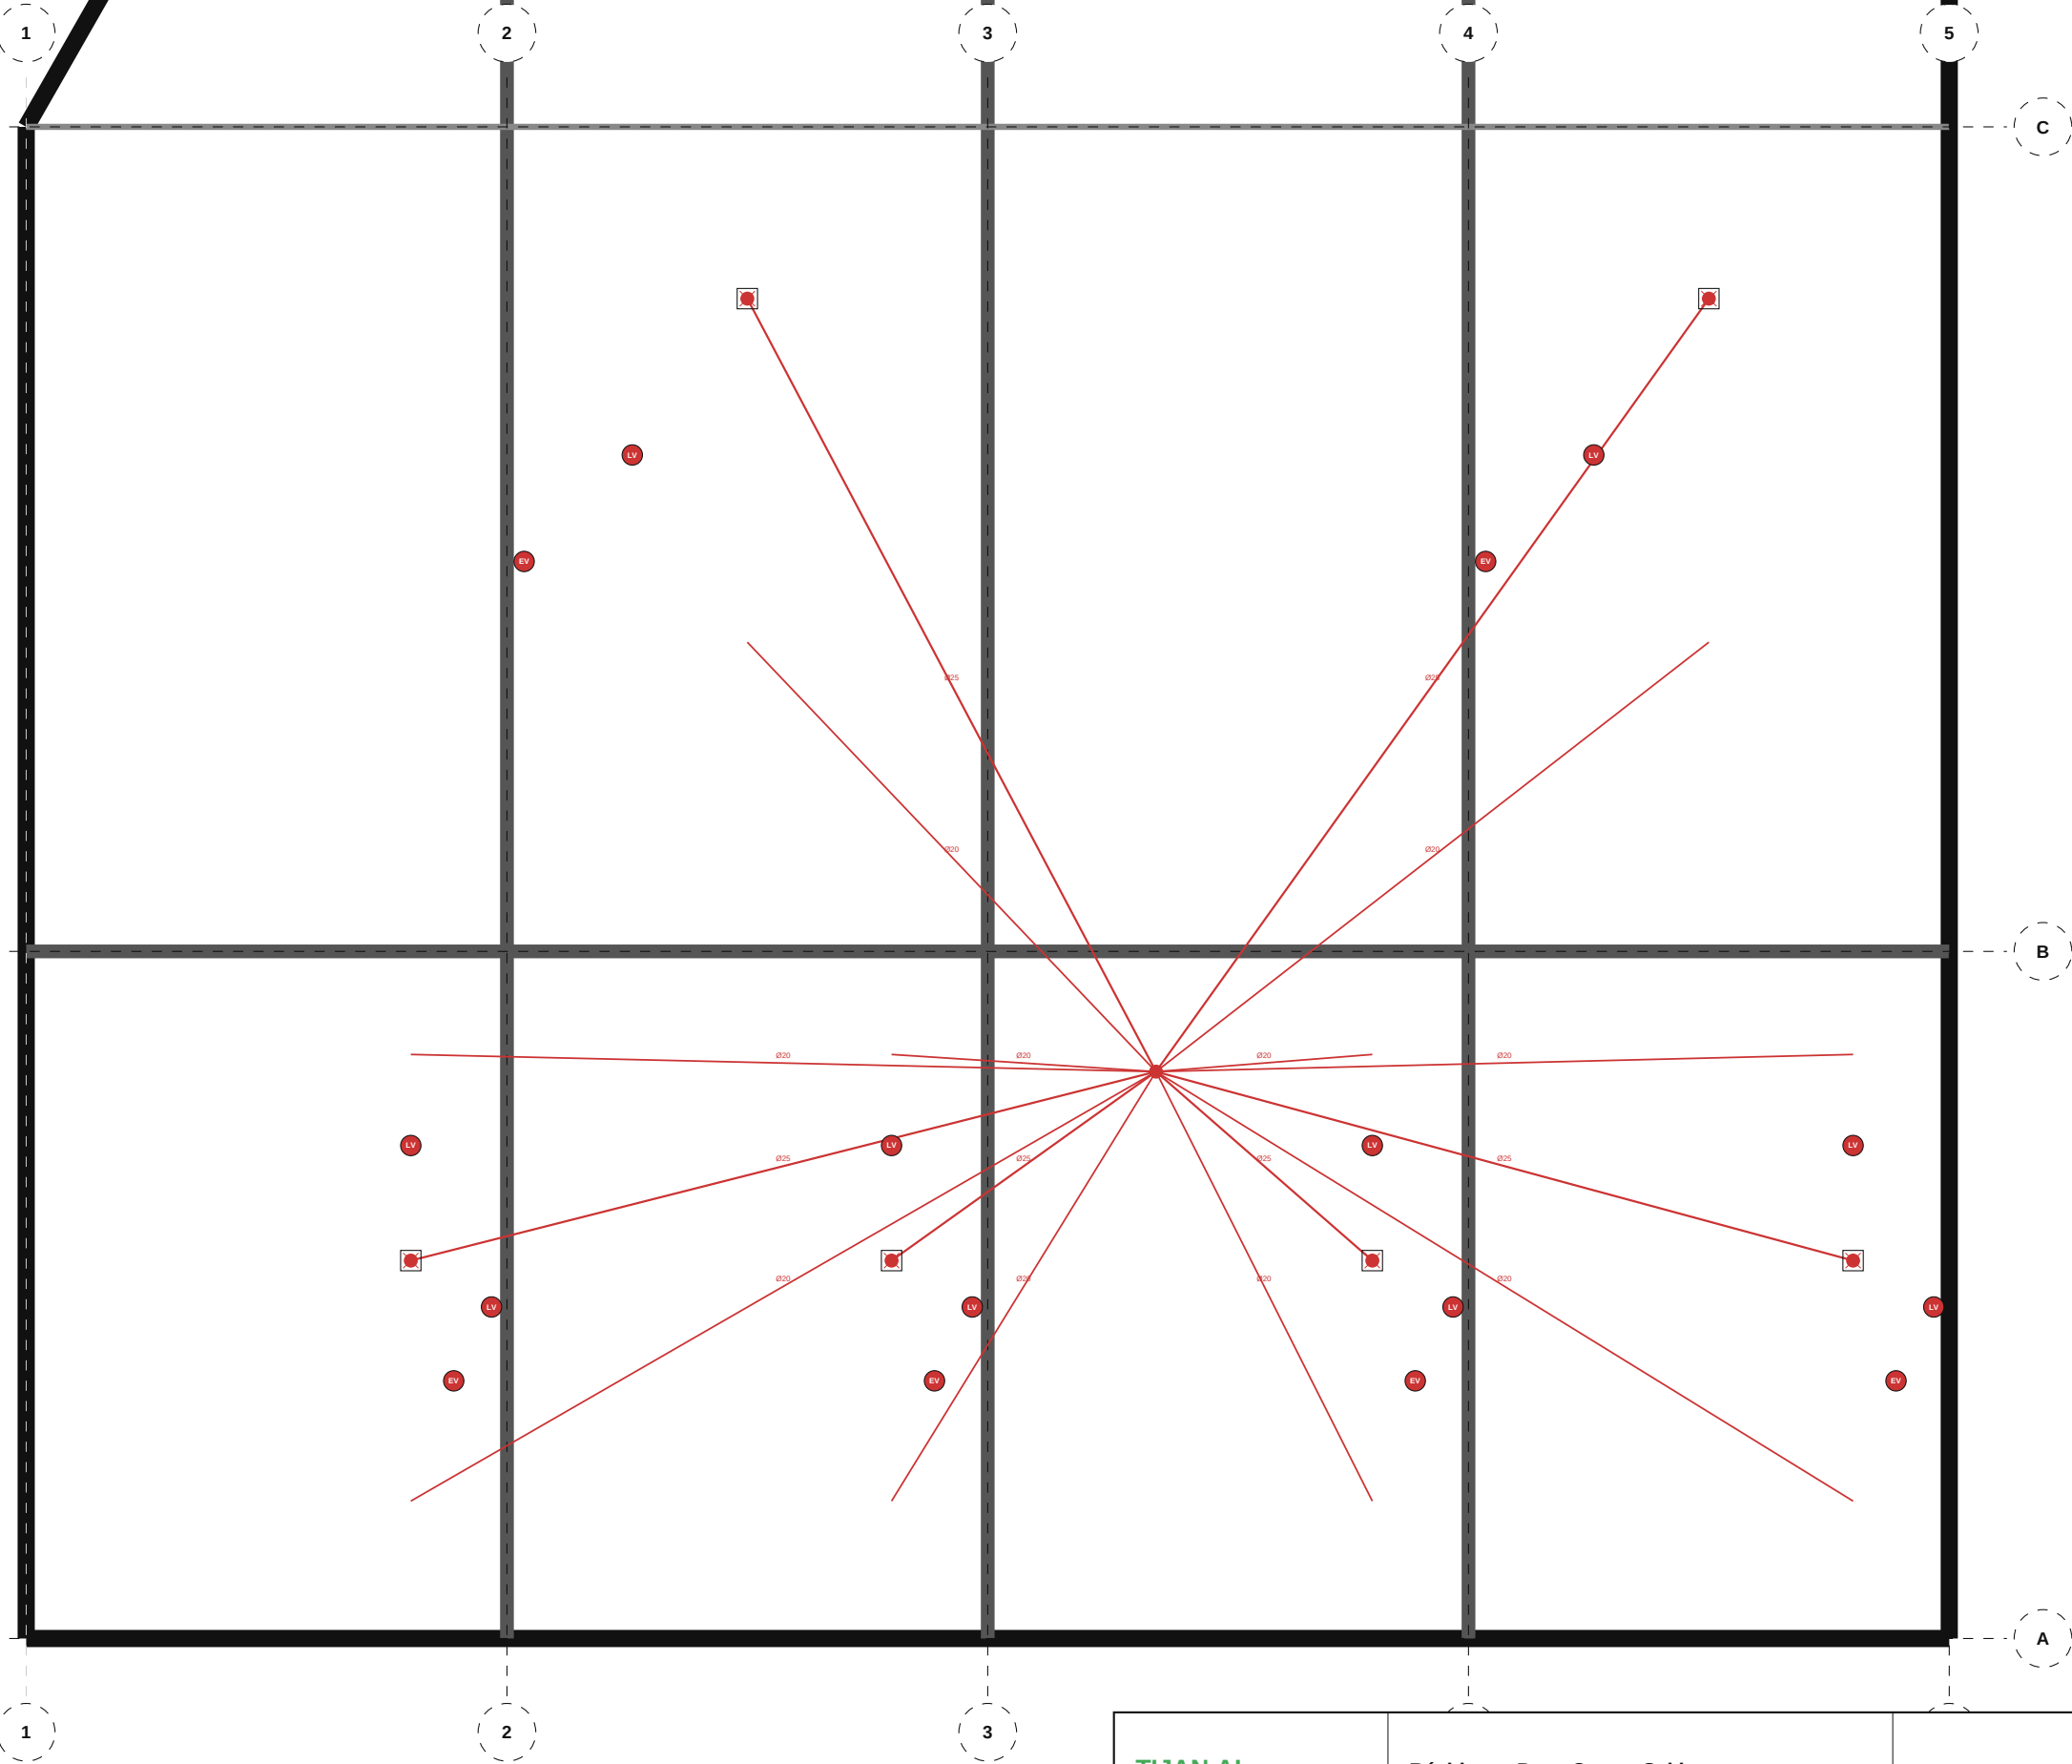

NOMENCLATURE — 410 PLU — Eau Chaude (EC)

- Évier cuisine: 6
- Lavabo: 6
- Douche: 6
- Lave-mains: 4

TIJAN AI

Bureau d'Études Automatisé

Résidence Papa Oumar Sakho

Dakar, Senegal

Éch: 1/100

Pl. 35/133


410 PLU — Eau Chaude (EC) — R+4

Date: 06/05/2026

Réf: 1711

BIM vPLU-035

Phase: APD

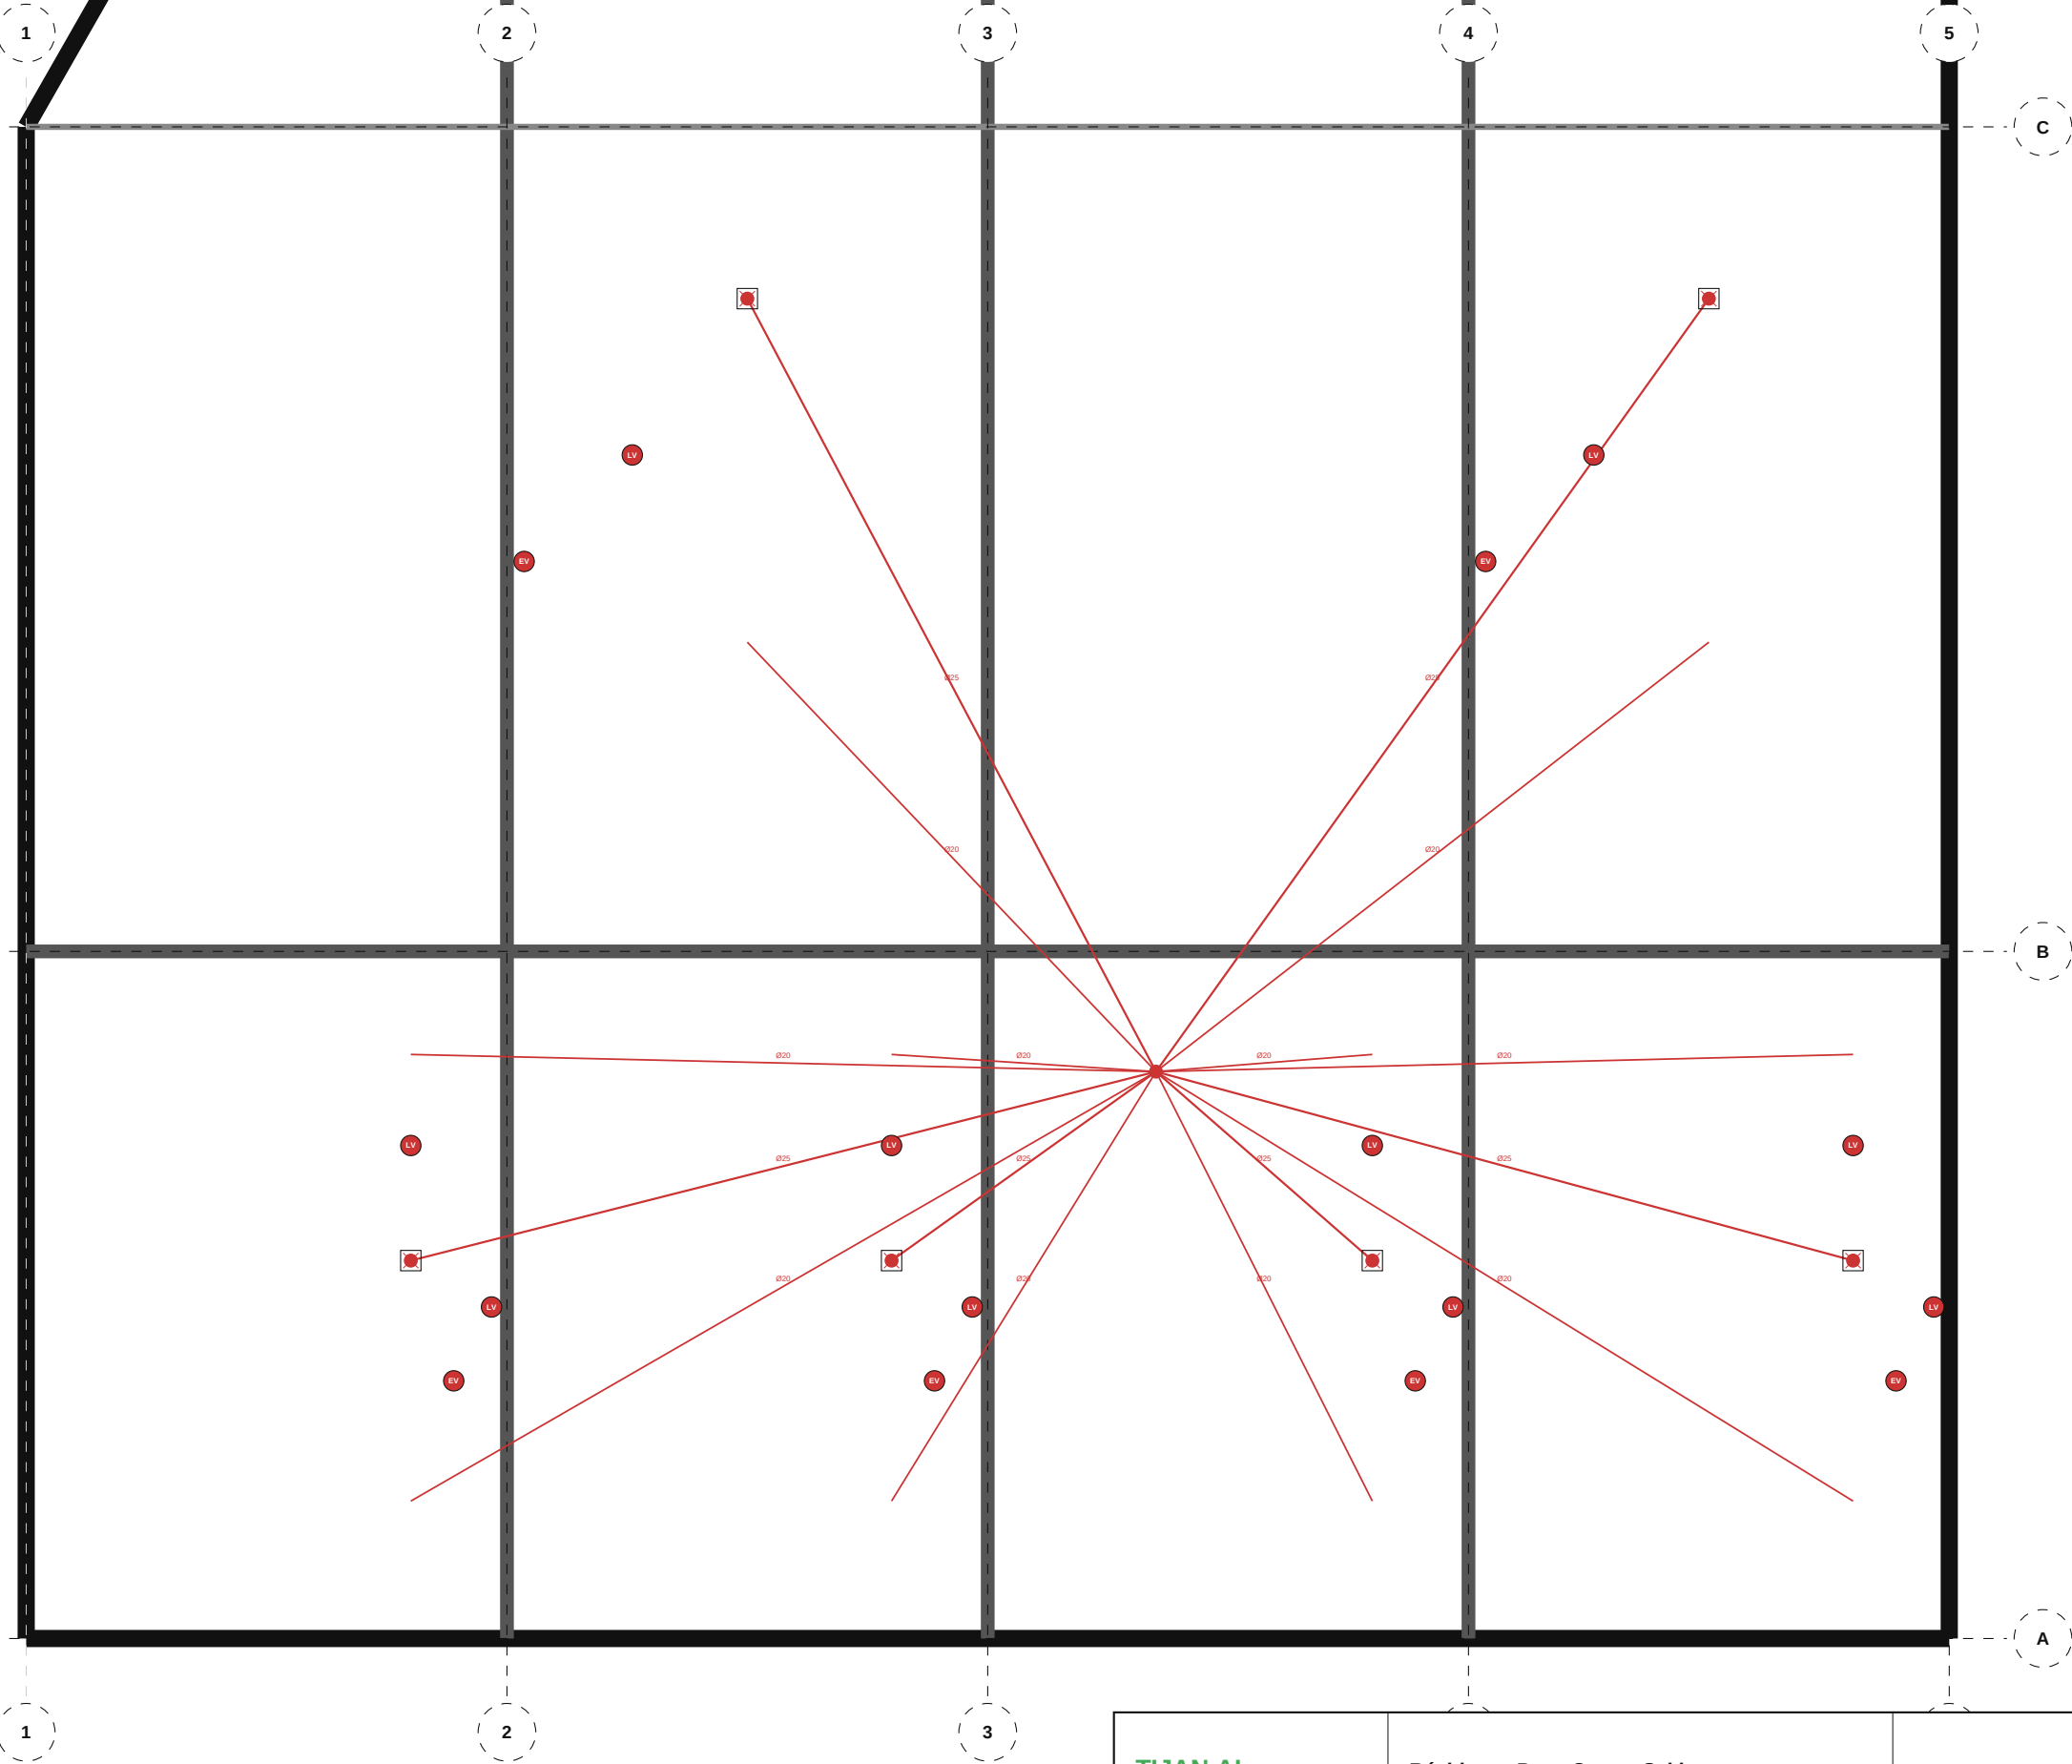

NOMENCLATURE — 410 PLU — Eau Chaude (EC)

- Évier cuisine: 6
- Lavabo: 6
- Douche: 6
- Lave-mains: 4

TIJAN AI

Bureau d'Études Automatisé

Résidence Papa Oumar Sakho

Dakar, Senegal

Éch: 1/100

Pl. 36/133


410 PLU — Eau Chaude (EC) — R+5

Date: 06/05/2026

Réf: 1711

BIM vPLU-036

Phase: APD

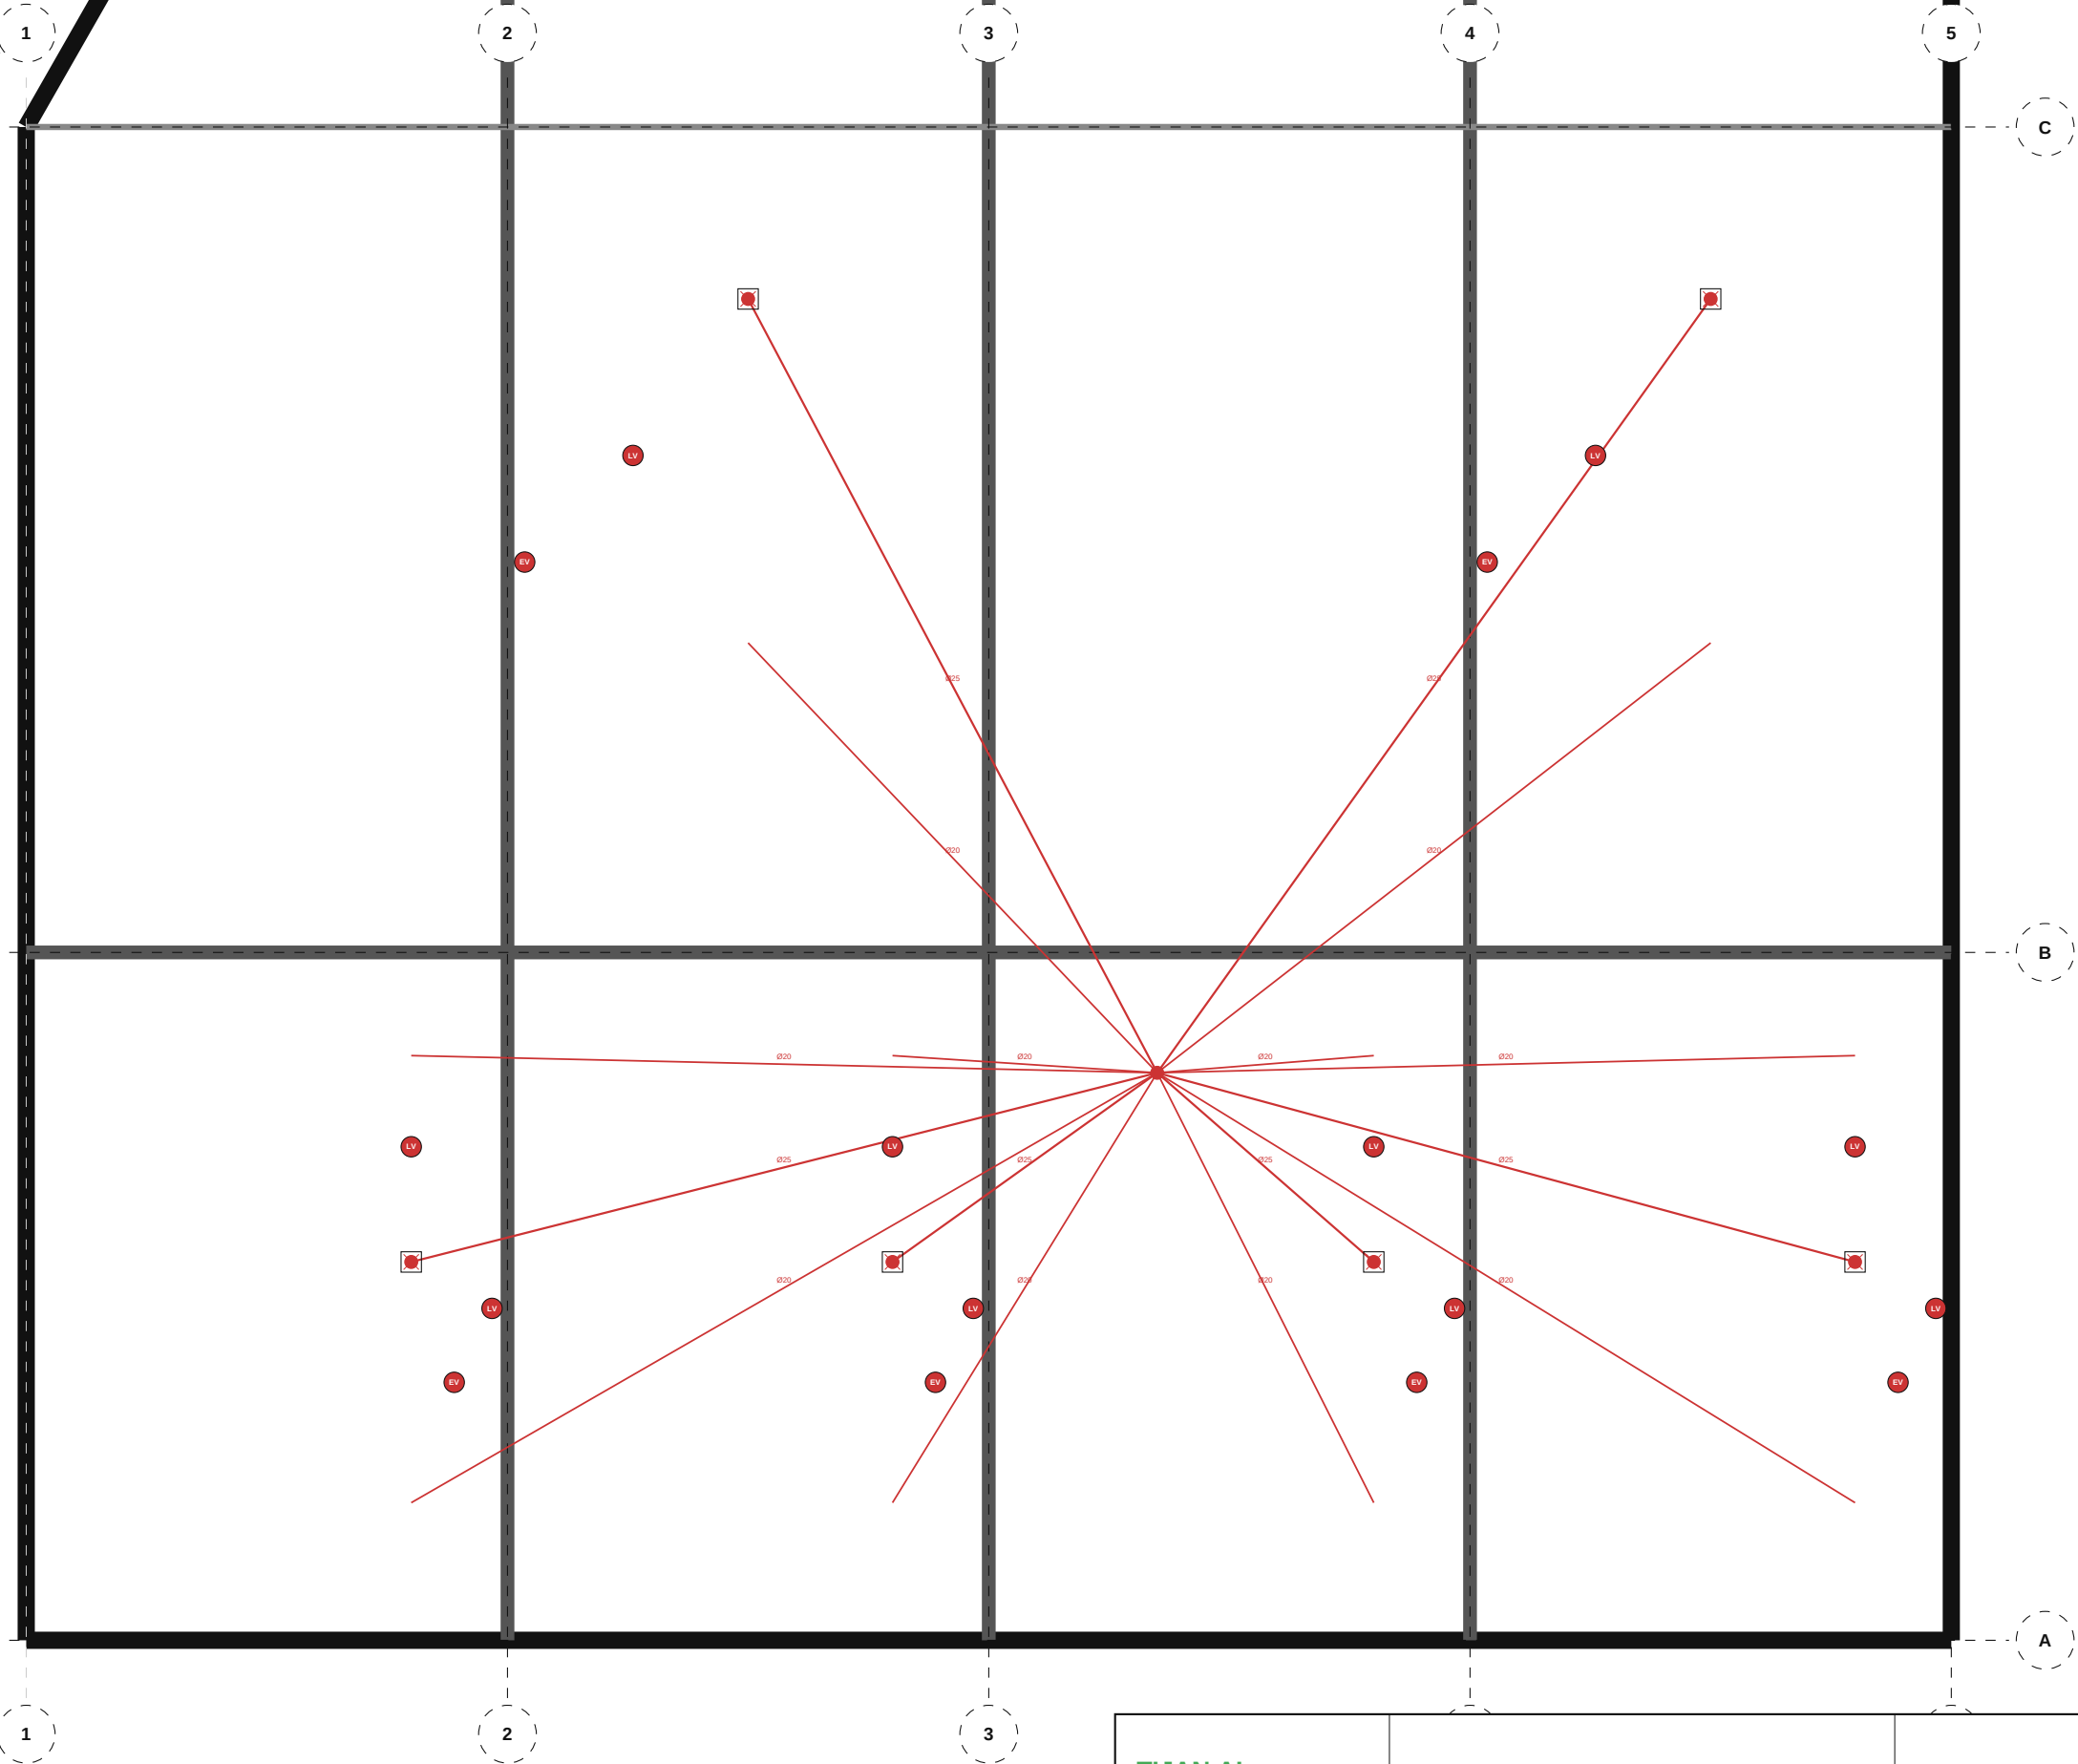

NOMENCLATURE — 410 PLU — Eau Chaude (EC)

- Évier cuisine: 6
- Lavabo: 6
- Douche: 6
- Lave-mains: 4

TIJAN AI

Bureau d'Études Automatisé

Résidence Papa Oumar Sakho

Dakar, Senegal

Éch: 1/100

Pl. 37/133


410 PLU — Eau Chaude (EC) — R+6

Date: 06/05/2026

Réf: 1711

BIM vPLU-037

Phase: APD

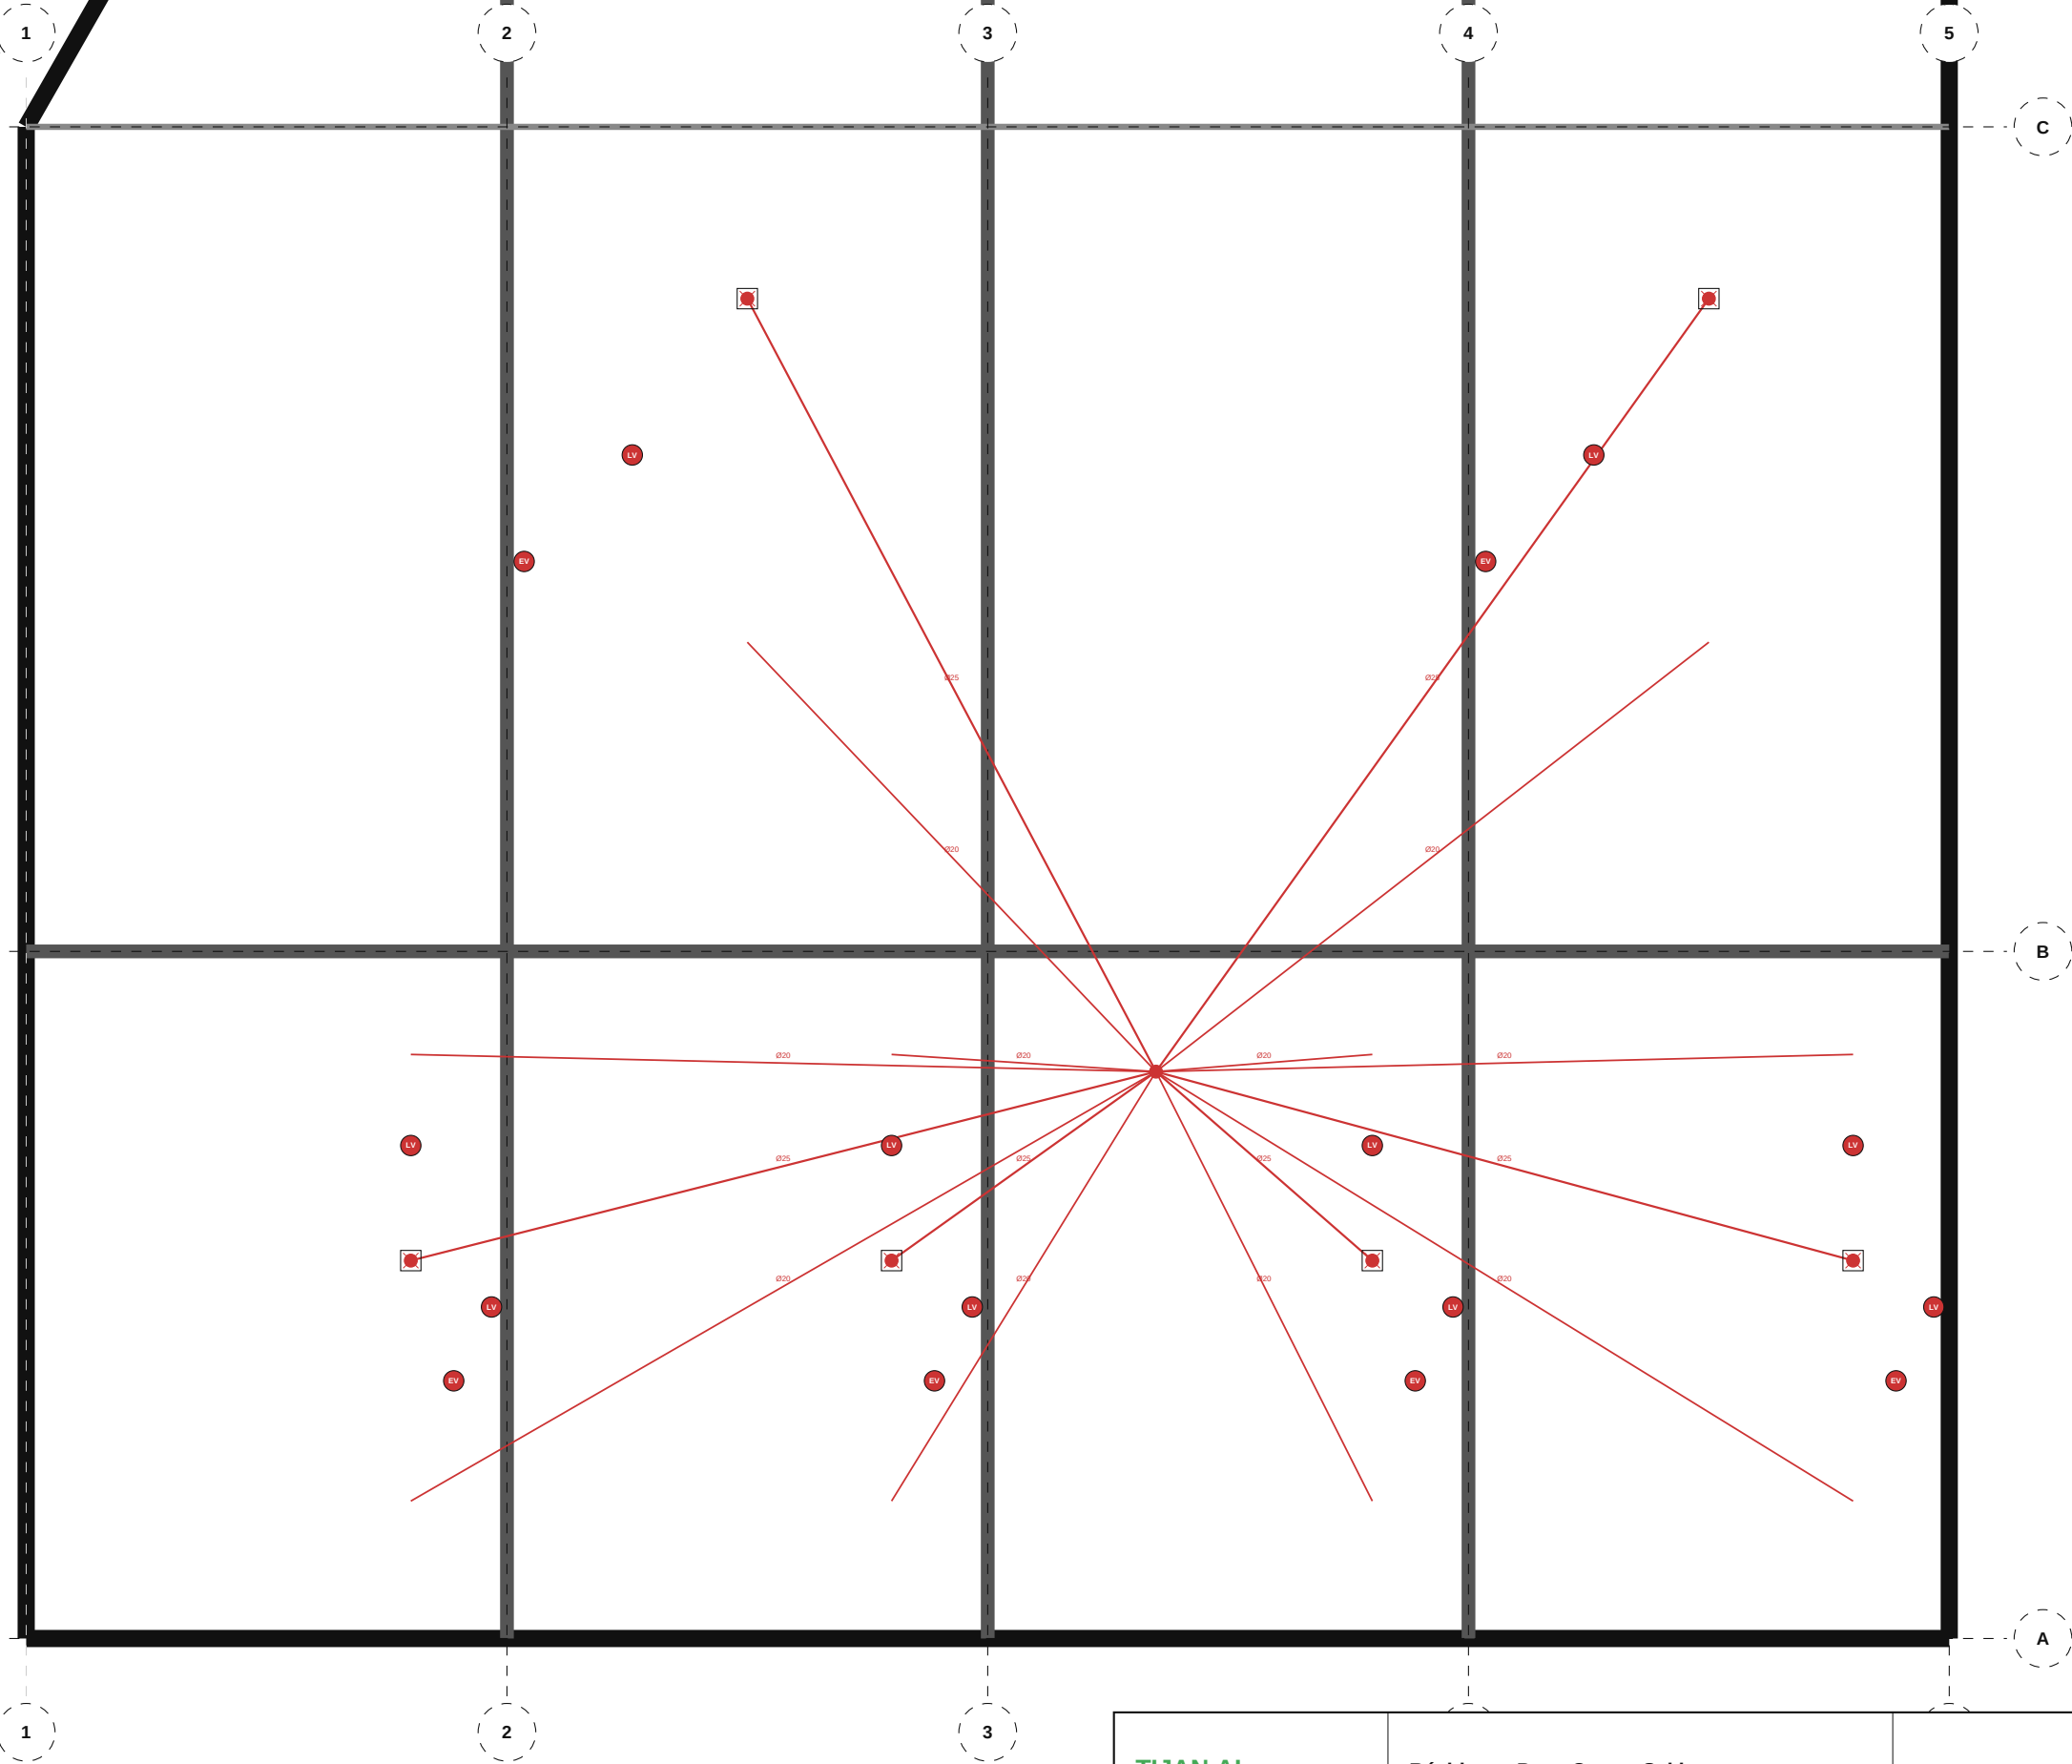

NOMENCLATURE — 410 PLU — Eau Chaude (EC)

- Évier cuisine: 6
- Lavabo: 6
- Douche: 6
- Lave-mains: 4

TIJAN AI

Bureau d'Études Automatisé

Résidence Papa Oumar Sakho

Dakar, Senegal

Éch: 1/100

Pl. 38/133


410 PLU — Eau Chaude (EC) — R+7

Date: 06/05/2026

Réf: 1711

BIM vPLU-038


Phase: APD

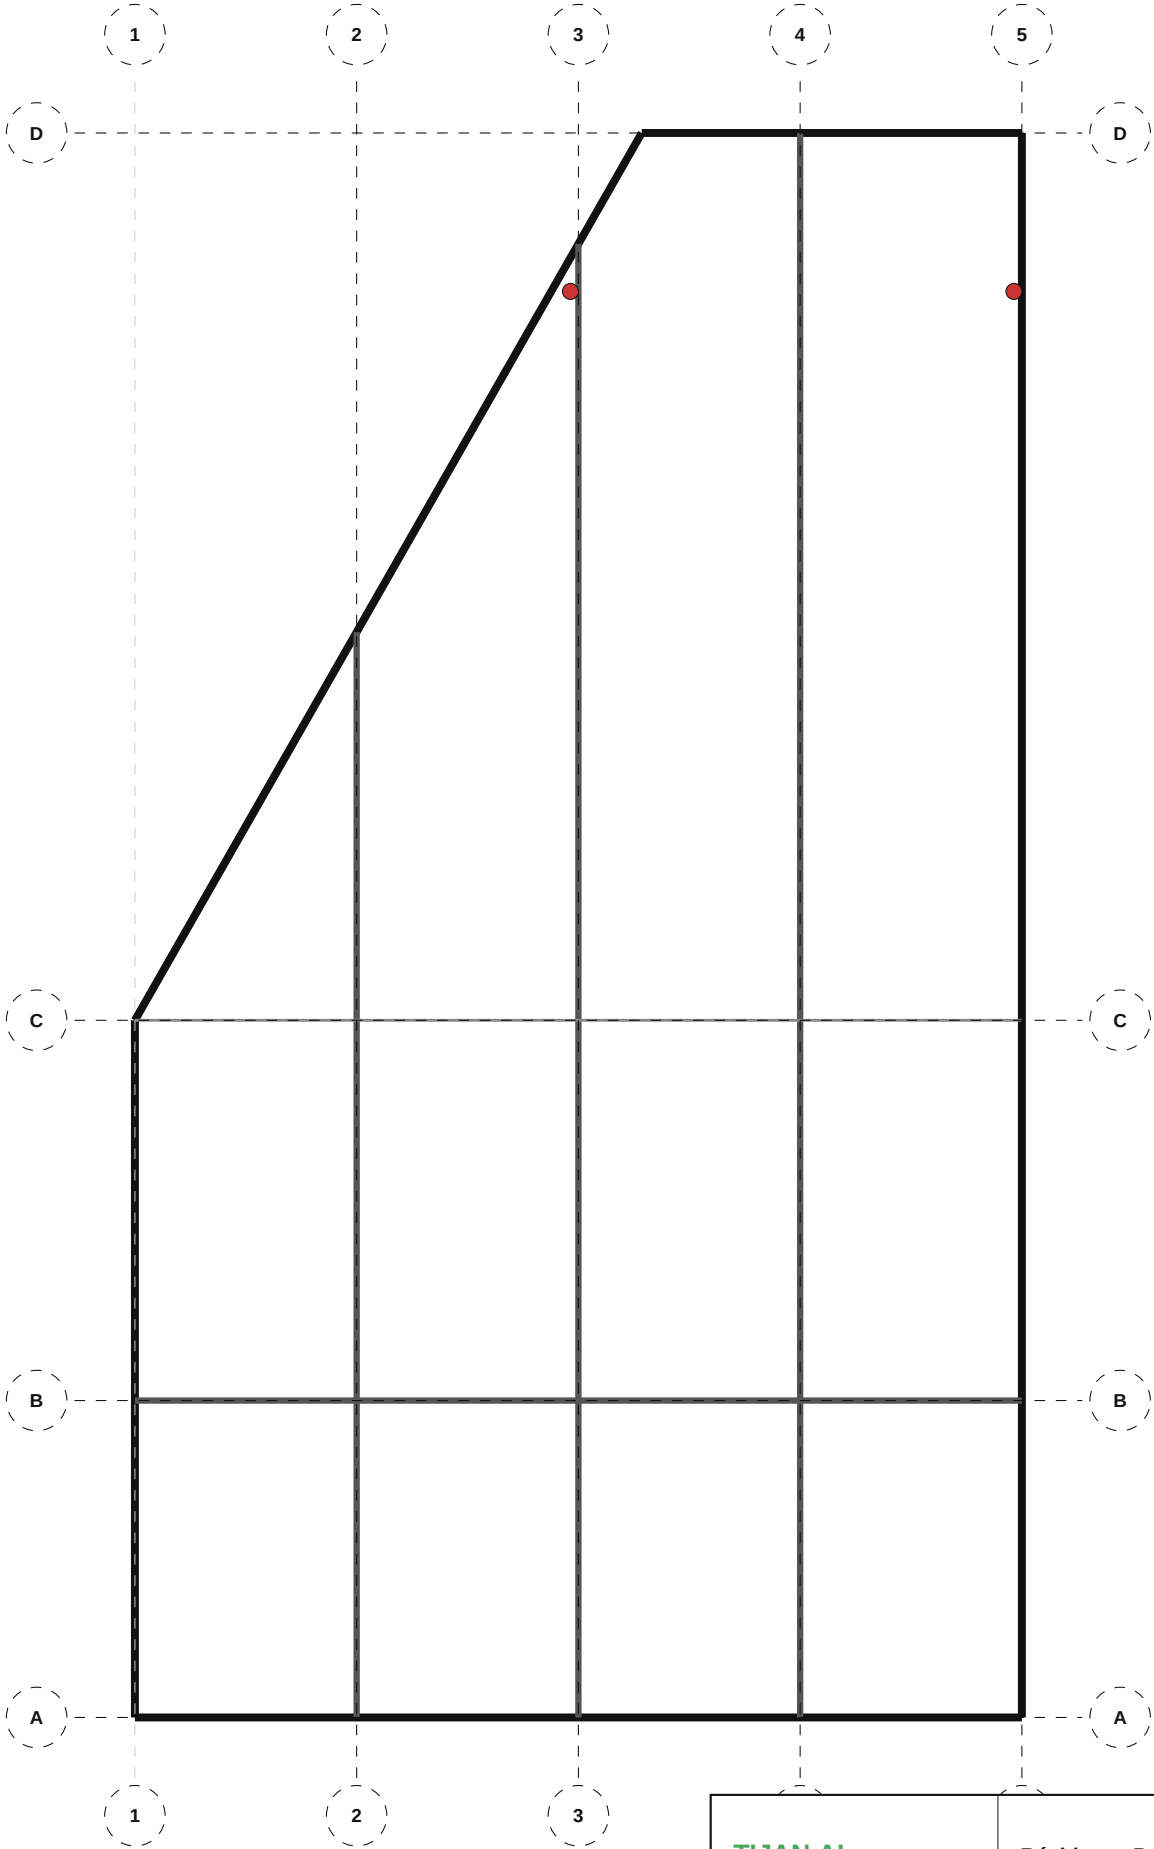

NOMENCLATURE — 410 PLU — Eau Chaude (EC)

• Chauffe-eau: 2

TIJAN AI Bureau d'Études Automatisé	Résidence Papa Oumar Sakho Dakar, Senegal	Éch: 1/100 Pl. 39/133
	410 PLU — Eau Chaude (EC) — R+8 Terrasse	
Date: 06/05/2026	Réf: 1711	BIM vPLU-039 Phase: APD

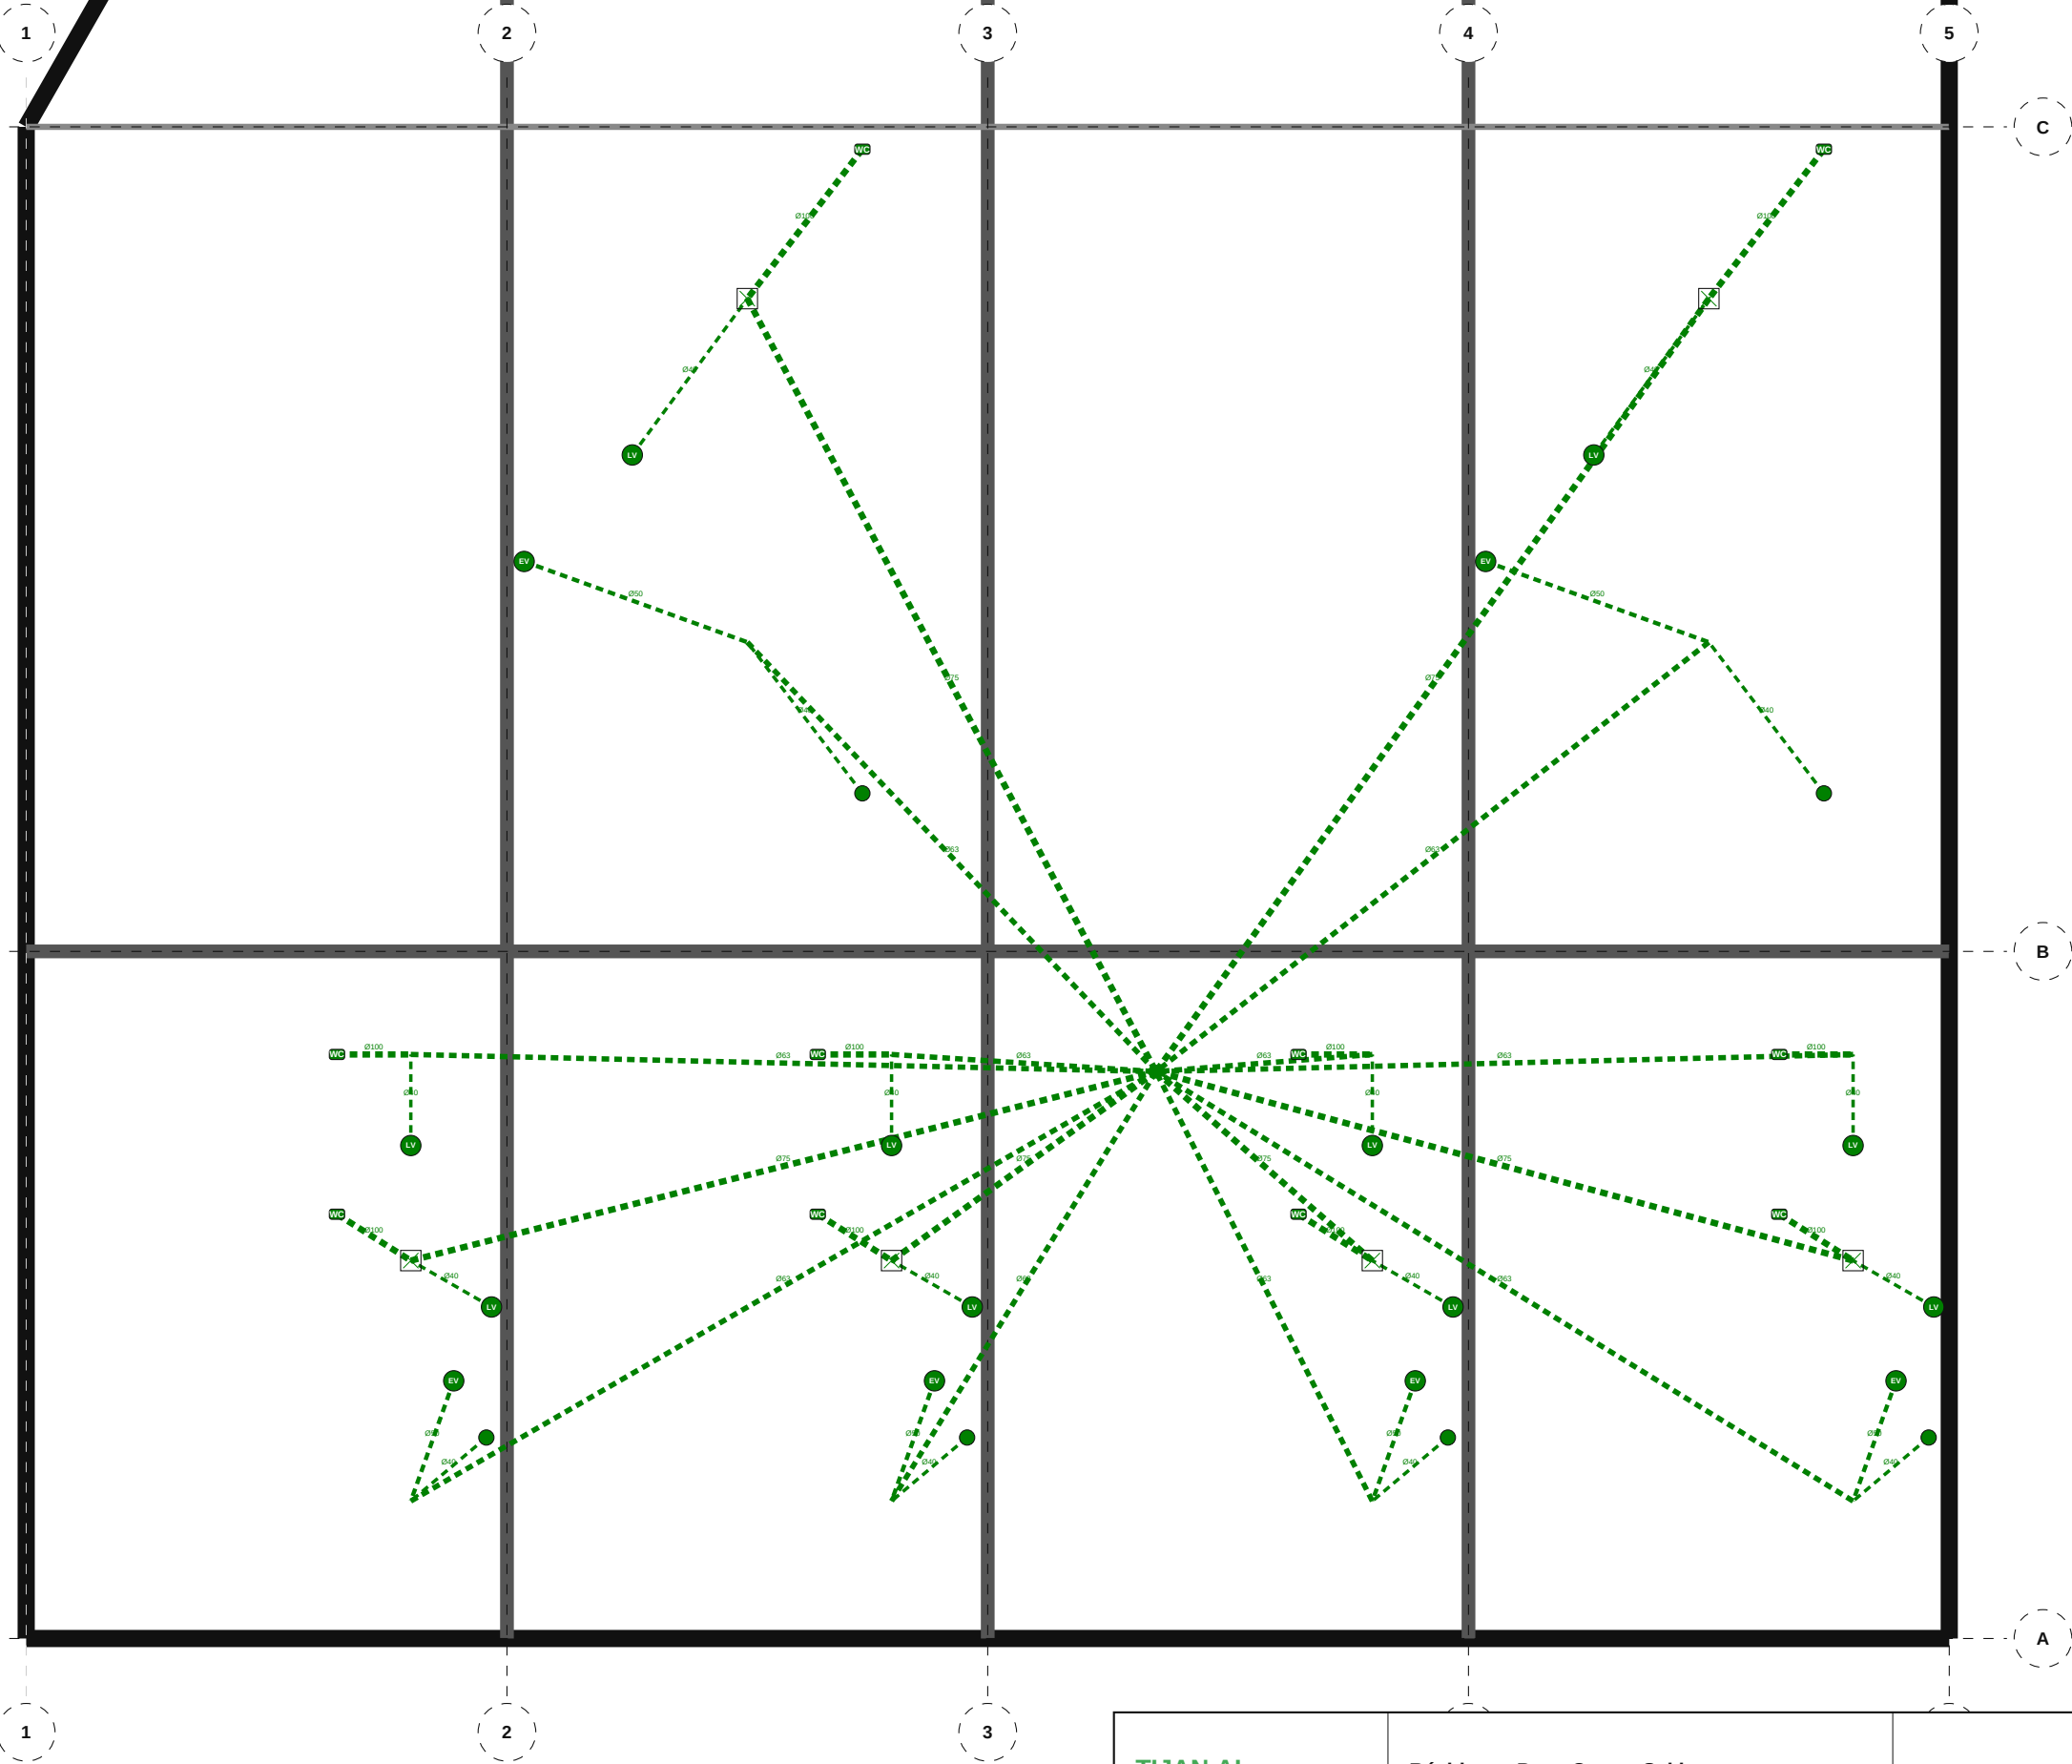

NOMENCLATURE — 410 PLU — Eaux Usées (EU)

- WC suspendu: 10
- Évier cuisine: 6
- Lave-vaisselle: 6
- Lavabo: 6
- Douche: 6
- Lave-mains: 4

TIJAN AI

Bureau d'Études Automatisé

Résidence Papa Oumar Sakho

Dakar, Senegal

Éch: 1/100

Pl. 40/133


410 PLU — Eaux Usées (EU) — R+1

Date: 06/05/2026

Réf: 1711

BIM vPLU-040

Phase: APD

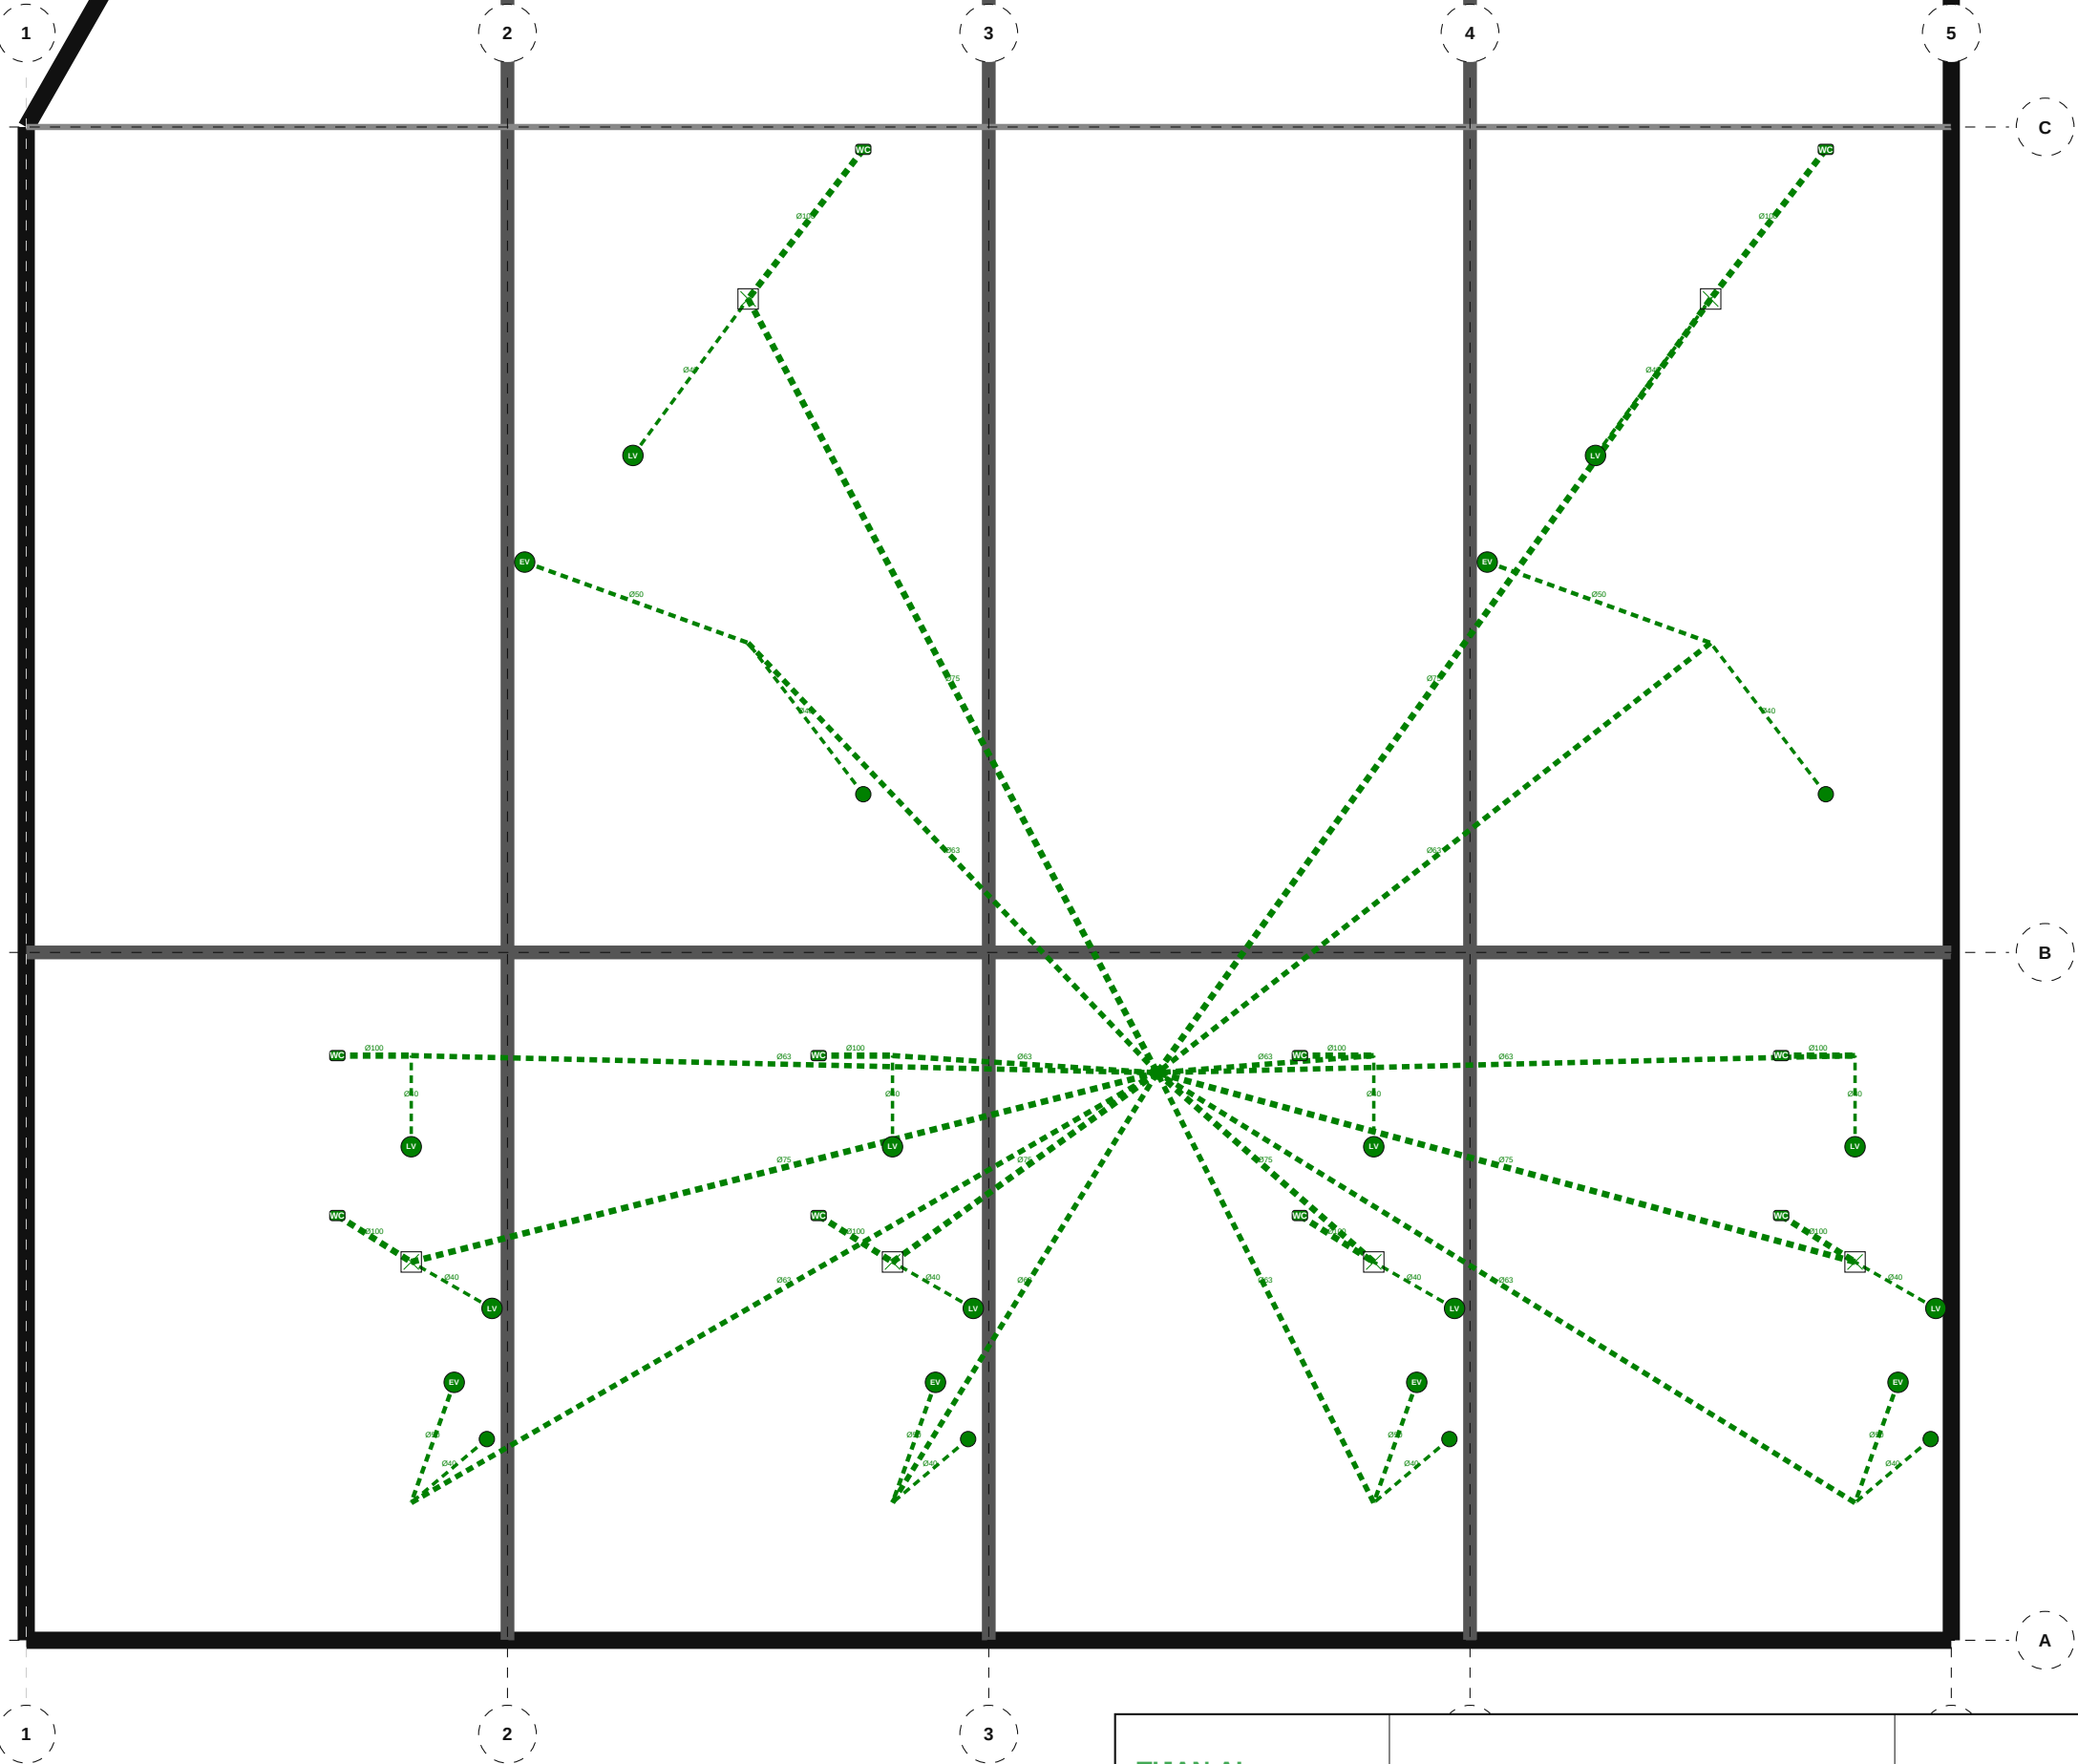

NOMENCLATURE — 410 PLU — Eaux Usées (EU)

- WC suspendu: 10
- Évier cuisine: 6
- Lave-vaisselle: 6
- Lavabo: 6
- Douche: 6
- Lave-mains: 4

TIJAN AI

Bureau d'Études Automatisé

Résidence Papa Oumar Sakho

Dakar, Senegal

Éch: 1/100

Pl. 41/133


410 PLU — Eaux Usées (EU) — R+2

Date: 06/05/2026

Réf: 1711

BIM vPLU-041

Phase: APD

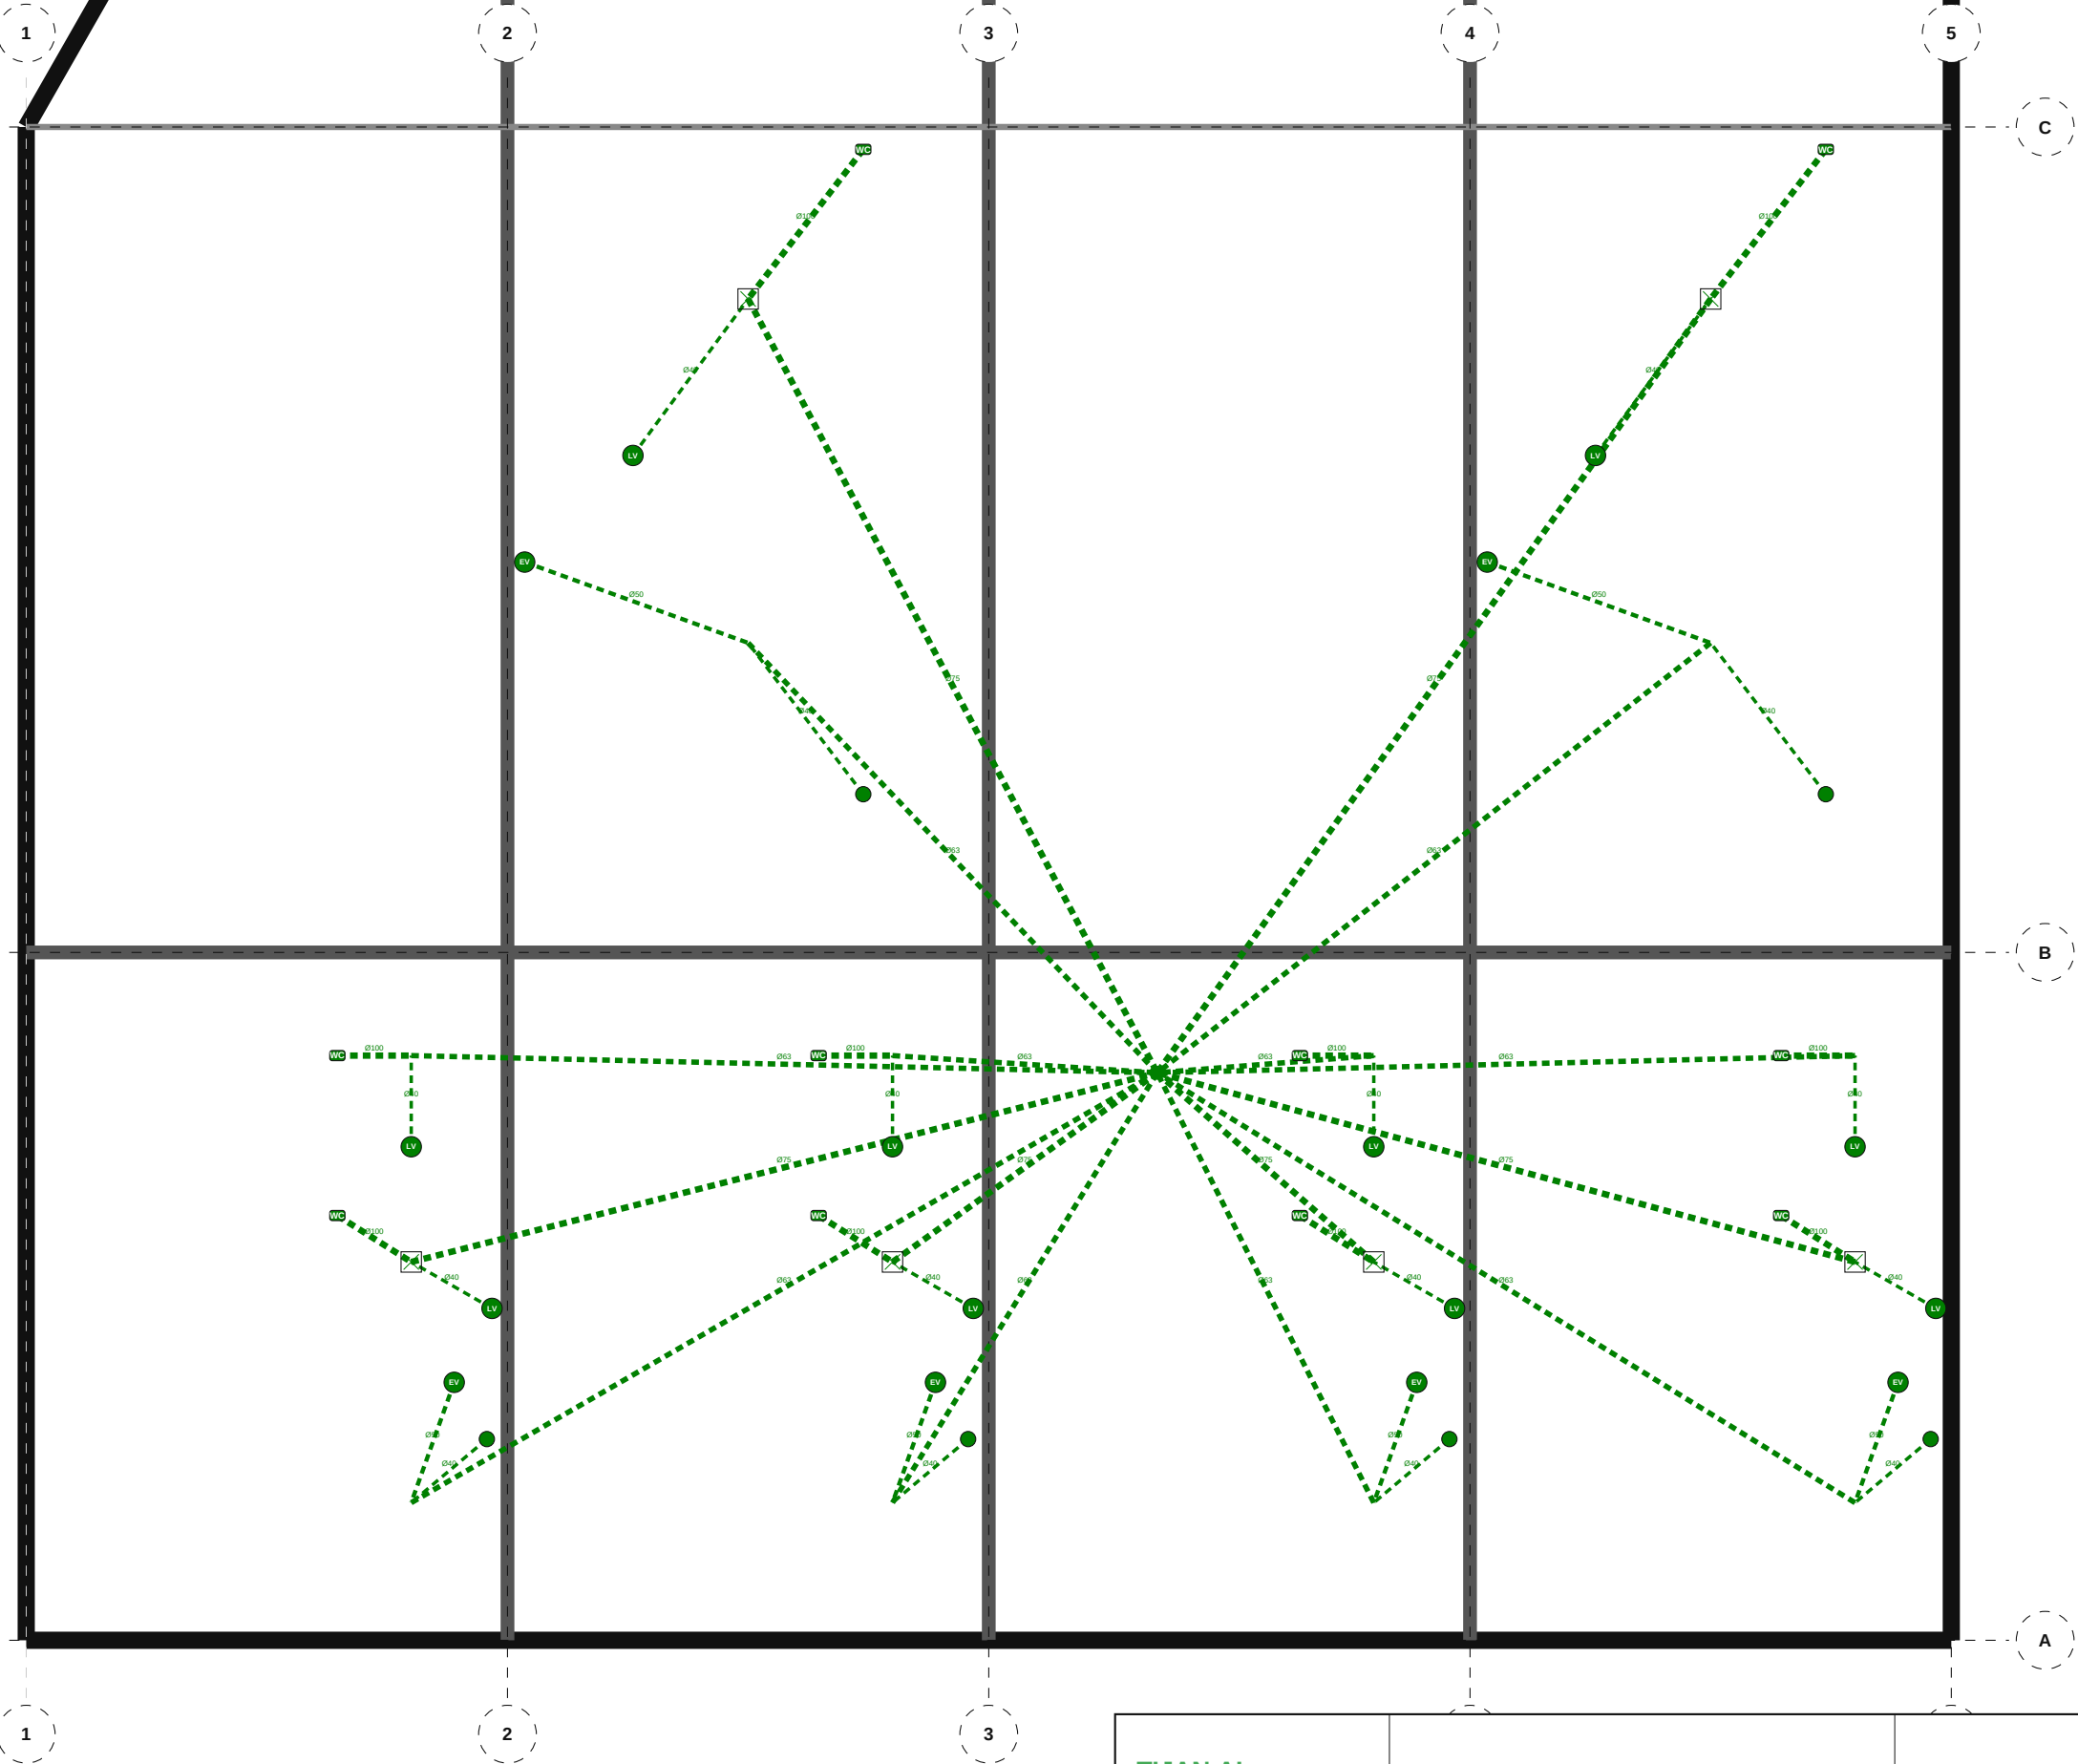

NOMENCLATURE — 410 PLU — Eaux Usées (EU)

- WC suspendu: 10
- Évier cuisine: 6
- Lave-vaisselle: 6
- Lavabo: 6
- Douche: 6
- Lave-mains: 4

TIJAN AI

Bureau d'Études Automatisé

Résidence Papa Oumar Sakho

Dakar, Senegal

Éch: 1/100

Pl. 42/133


410 PLU — Eaux Usées (EU) — R+3

Date: 06/05/2026

Réf: 1711

BIM vPLU-042


Phase: APD

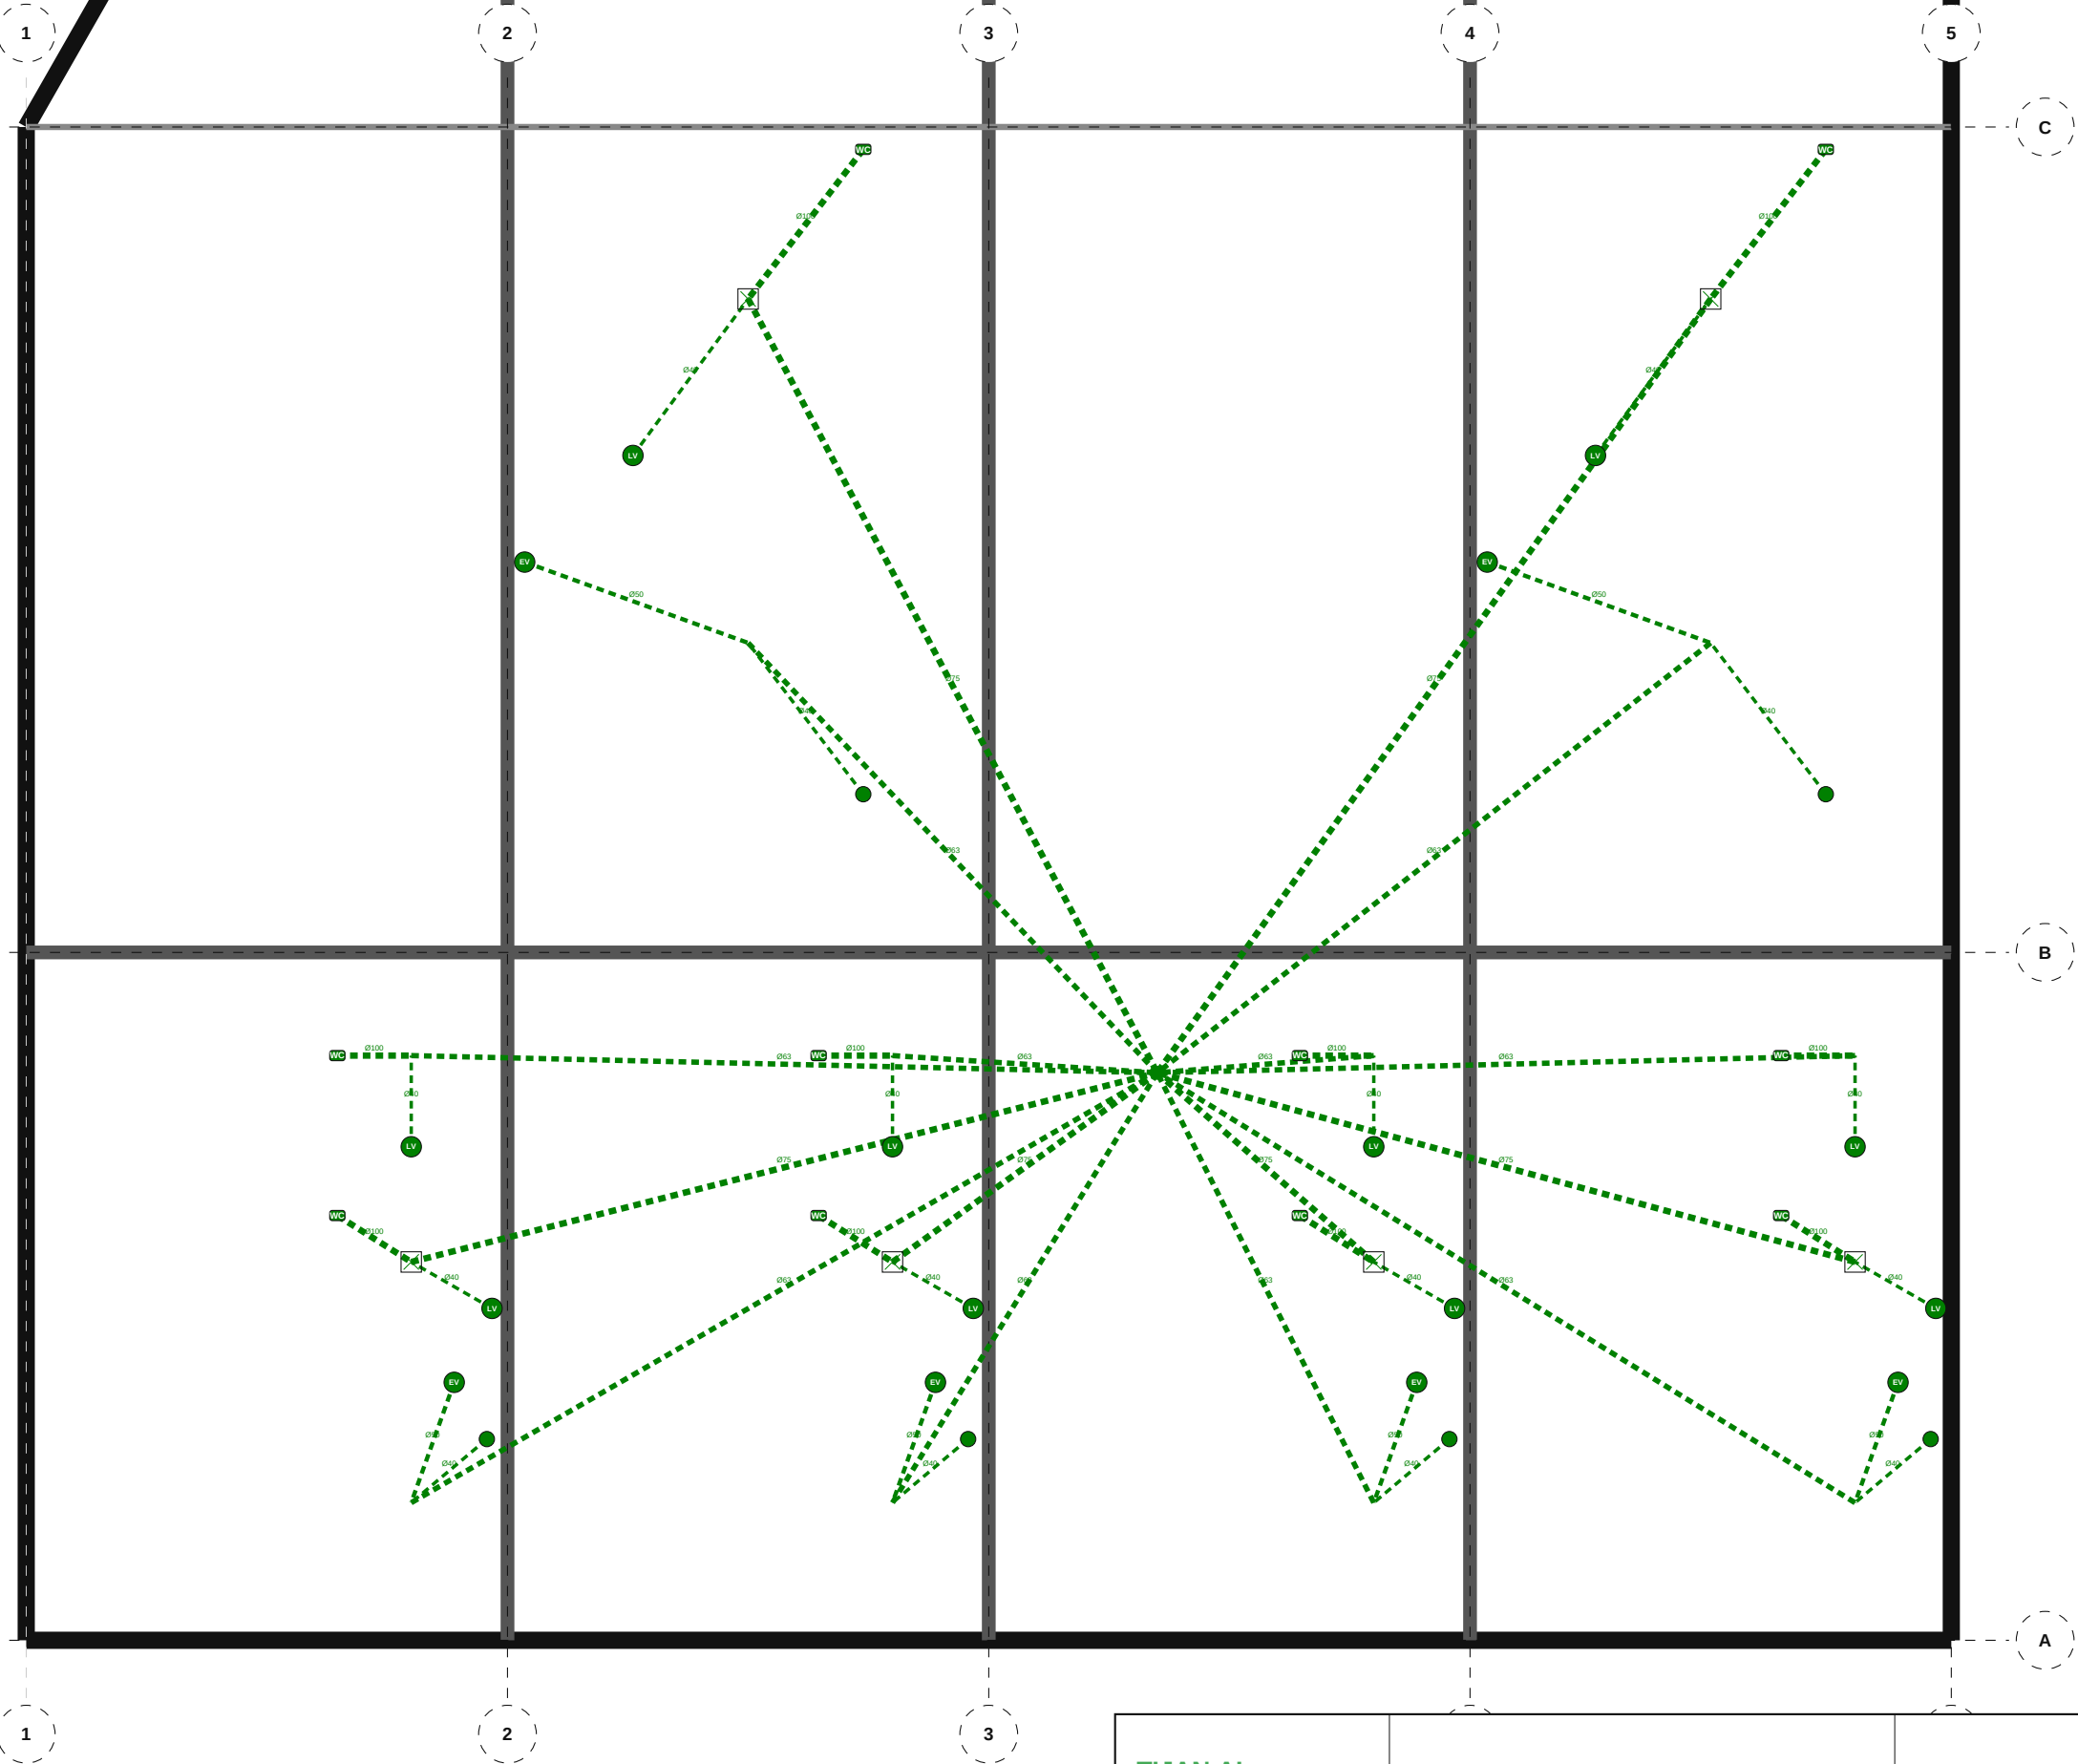

NOMENCLATURE — 410 PLU — Eaux Usées (EU)

- WC suspendu: 10
- Évier cuisine: 6
- Lave-vaisselle: 6
- Lavabo: 6
- Douche: 6
- Lave-mains: 4

TIJAN AI Bureau d'Études Automatisé	Résidence Papa Oumar Sakho Dakar, Senegal	Éch: 1/100 Pl. 43/133
	410 PLU — Eaux Usées (EU) — R+4	
Date: 06/05/2026	Réf: 1711	BIM vPLU-043 Phase: APD

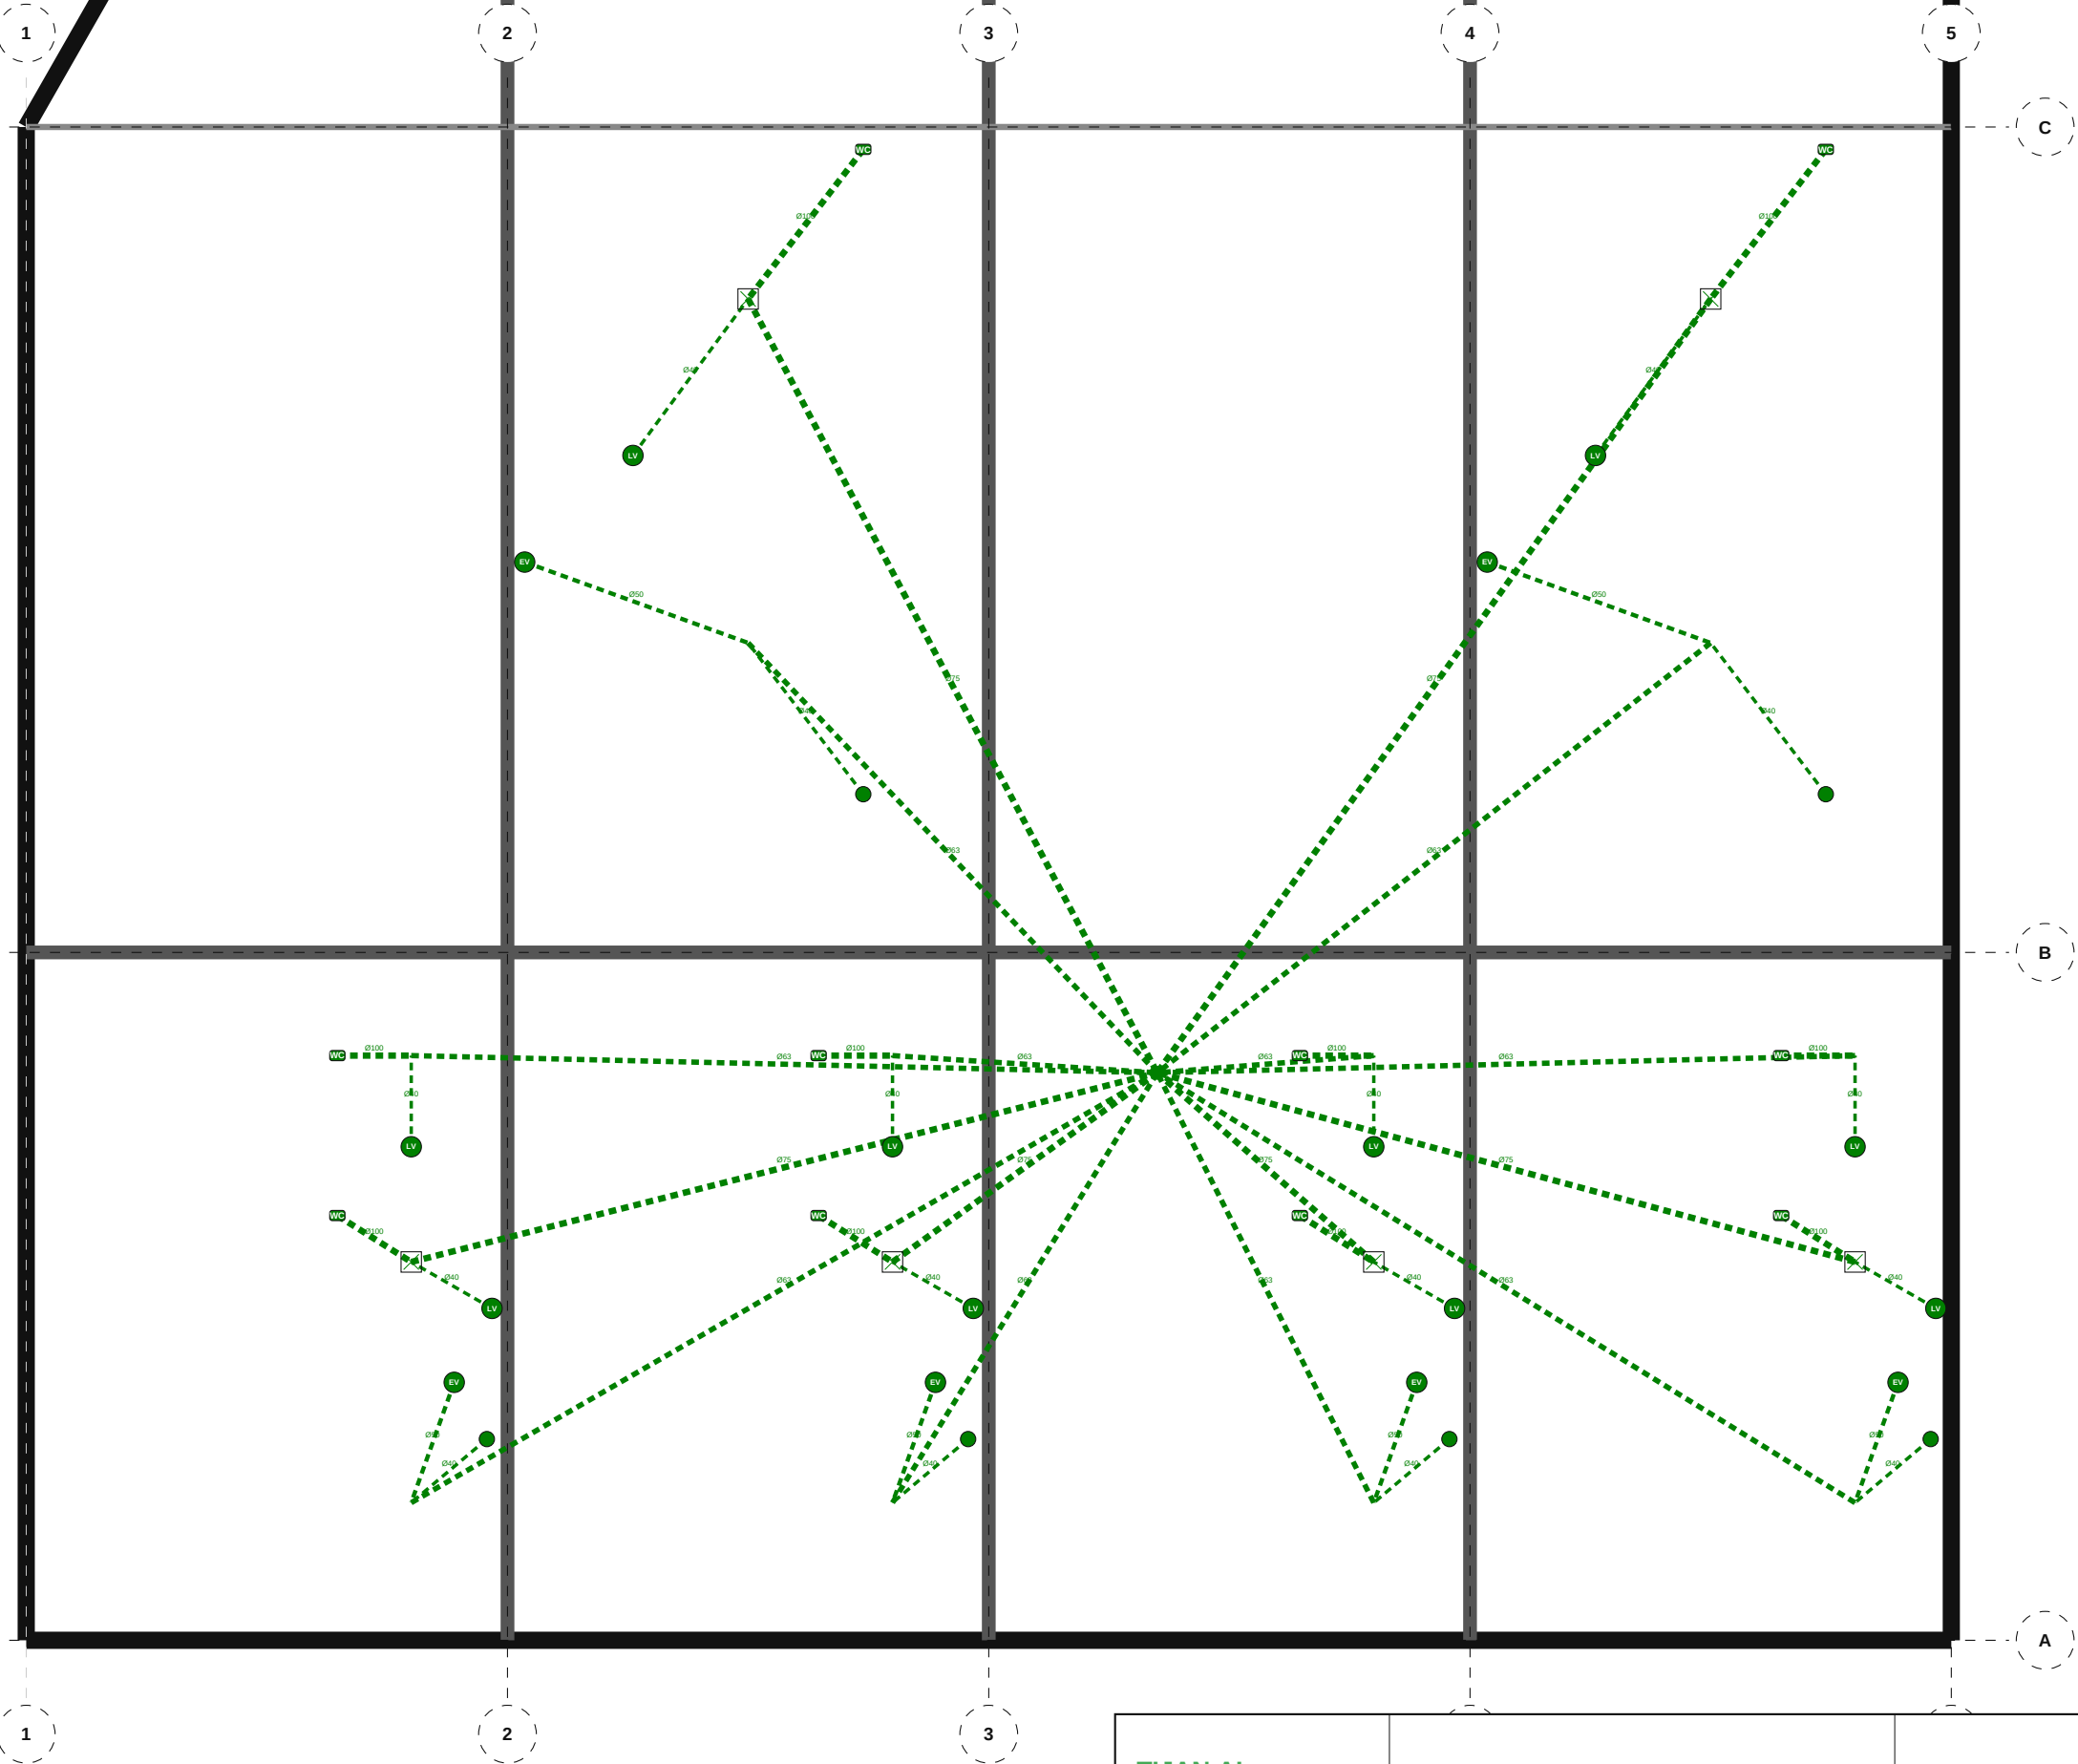

NOMENCLATURE — 410 PLU — Eaux Usées (EU)

- WC suspendu: 10
- Évier cuisine: 6
- Lave-vaisselle: 6
- Lavabo: 6
- Douche: 6
- Lave-mains: 4

TIJAN AI

Bureau d'Études Automatisé

Résidence Papa Oumar Sakho

Dakar, Senegal

Éch: 1/100

Pl. 44/133


410 PLU — Eaux Usées (EU) — R+5

Date: 06/05/2026

Réf: 1711

BIM vPLU-044

Phase: APD

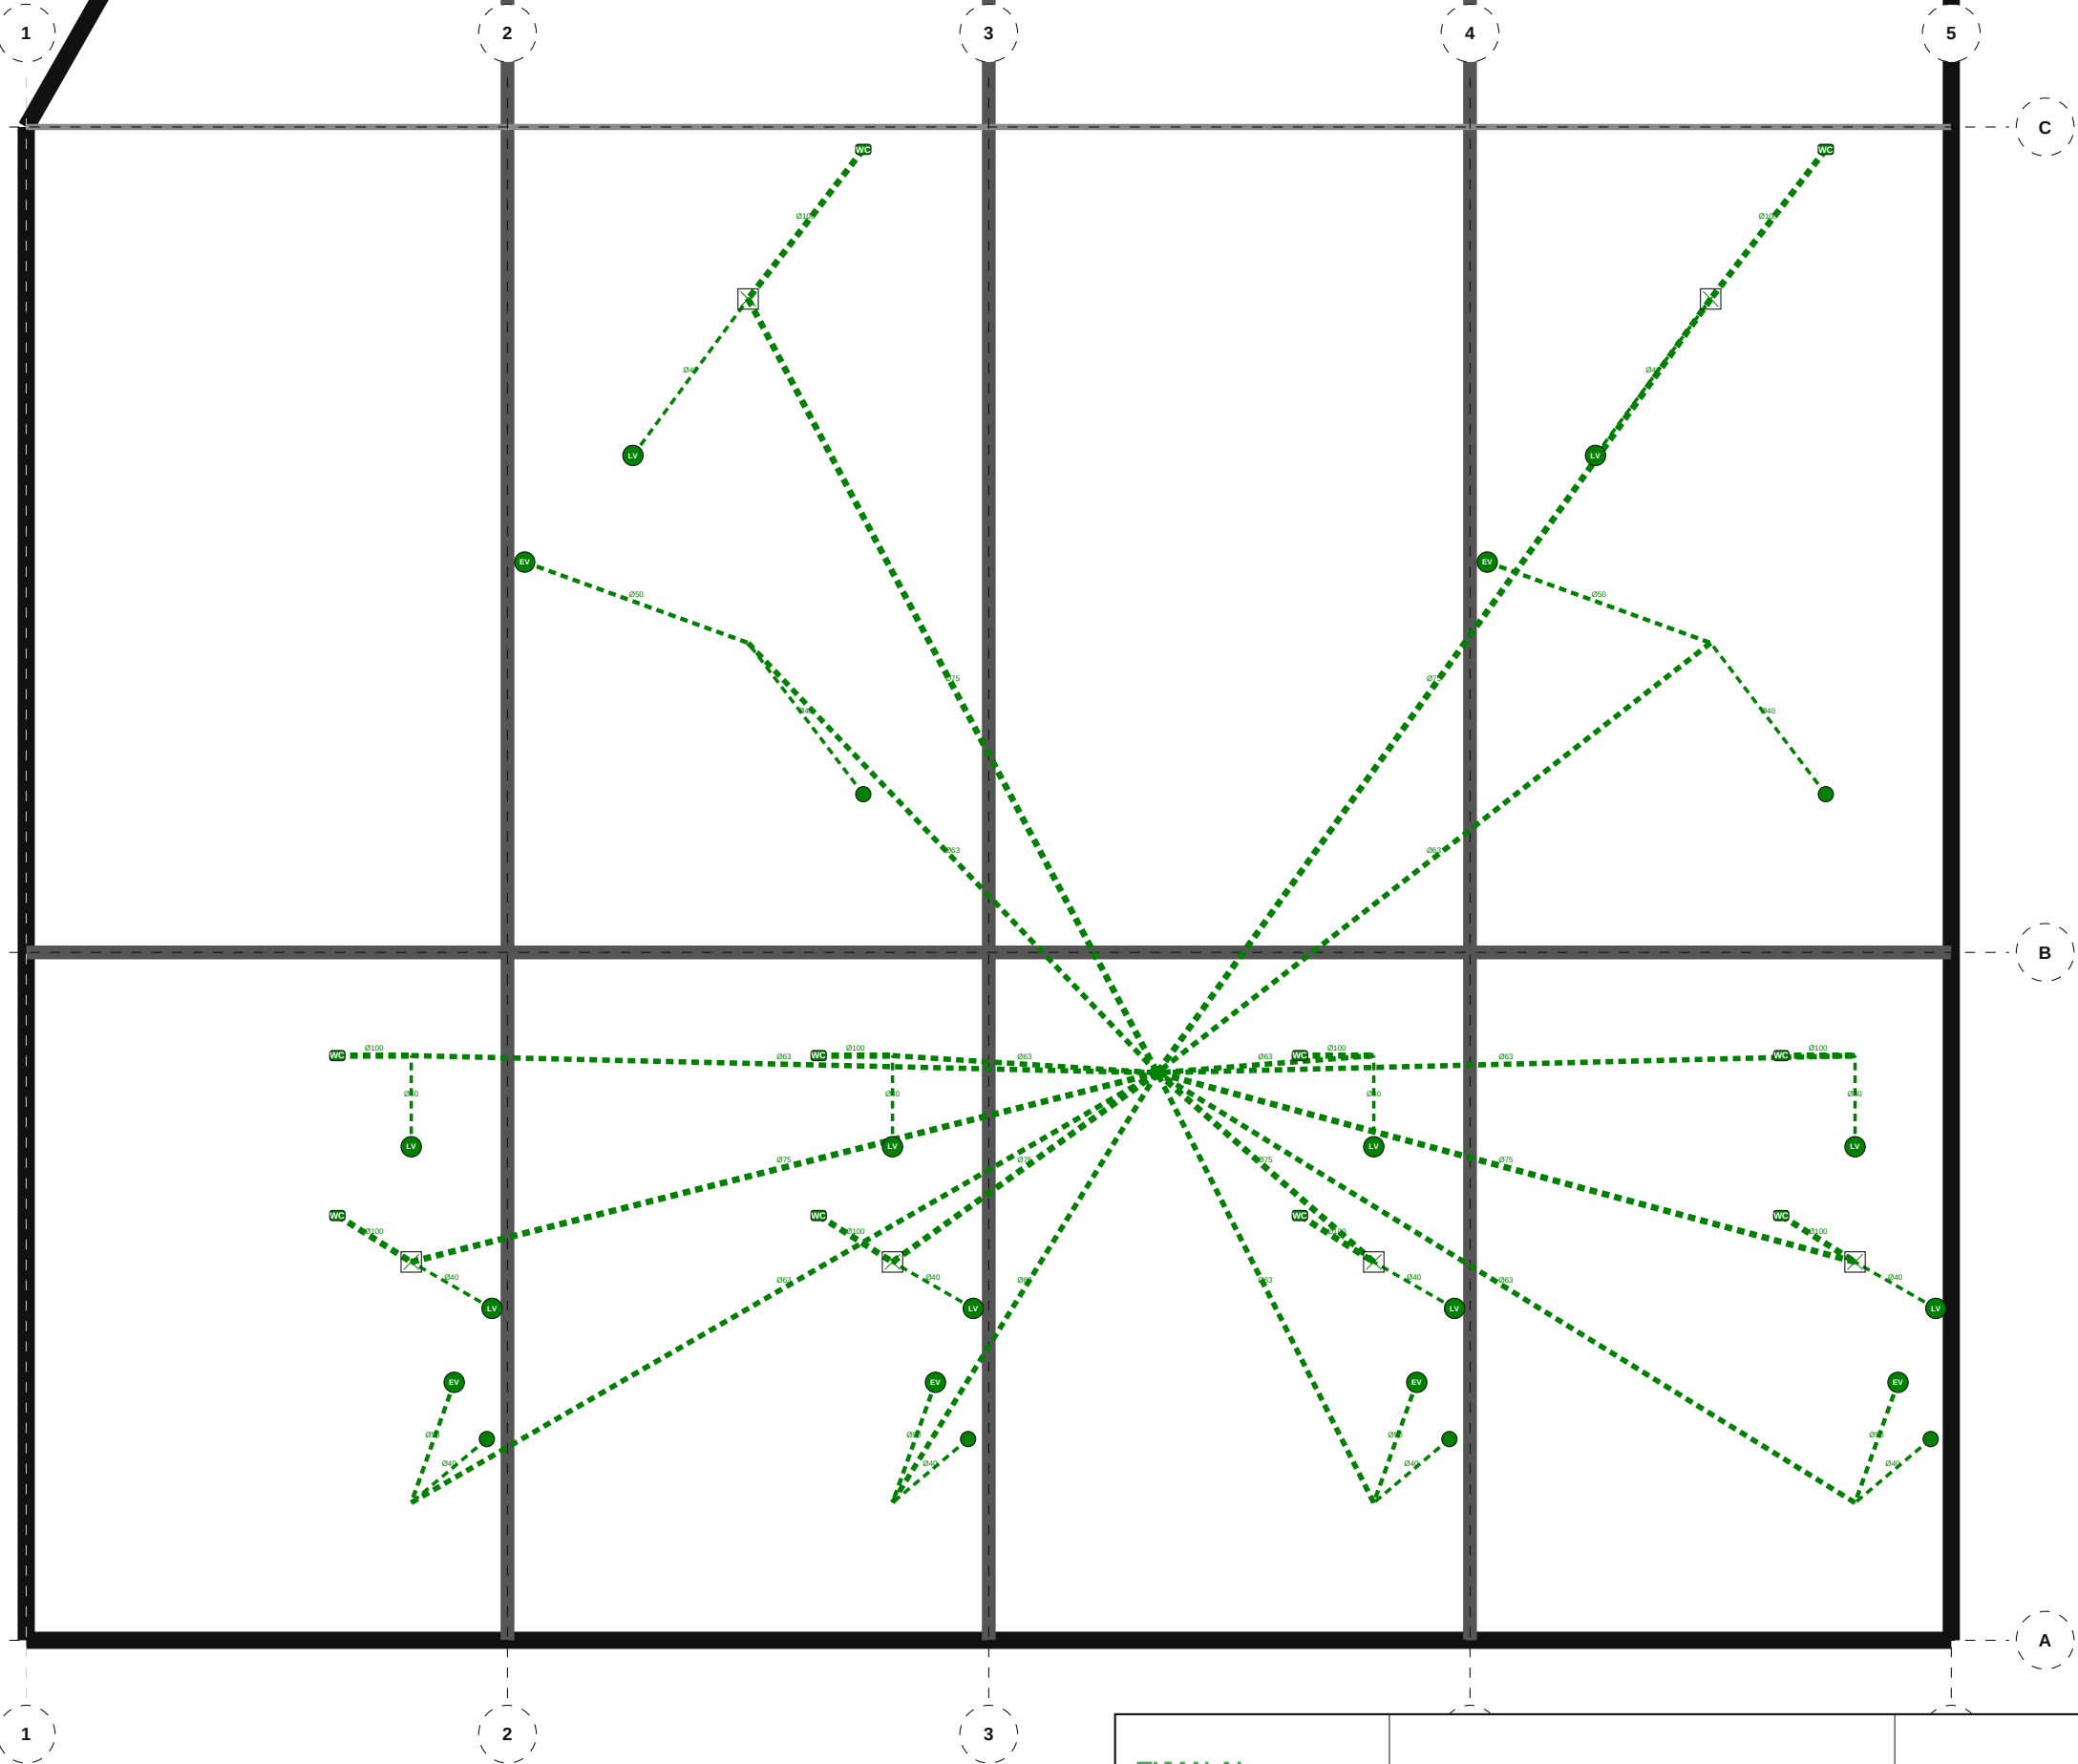

NOMENCLATURE — 410 PLU — Eaux Usées (EU)

- WC suspendu: 10
- Évier cuisine: 6
- Lave-vaisselle: 6
- Lavabo: 6
- Douche: 6
- Lave-mains: 4

TIJAN AI

Bureau d'Études Automatisé

Résidence Papa Oumar Sakho

Dakar, Senegal

Éch: 1/100

Pl. 45/133


410 PLU — Eaux Usées (EU) — R+6

Date: 06/05/2026

Réf: 1711

BIM vPLU-045

Phase: APD

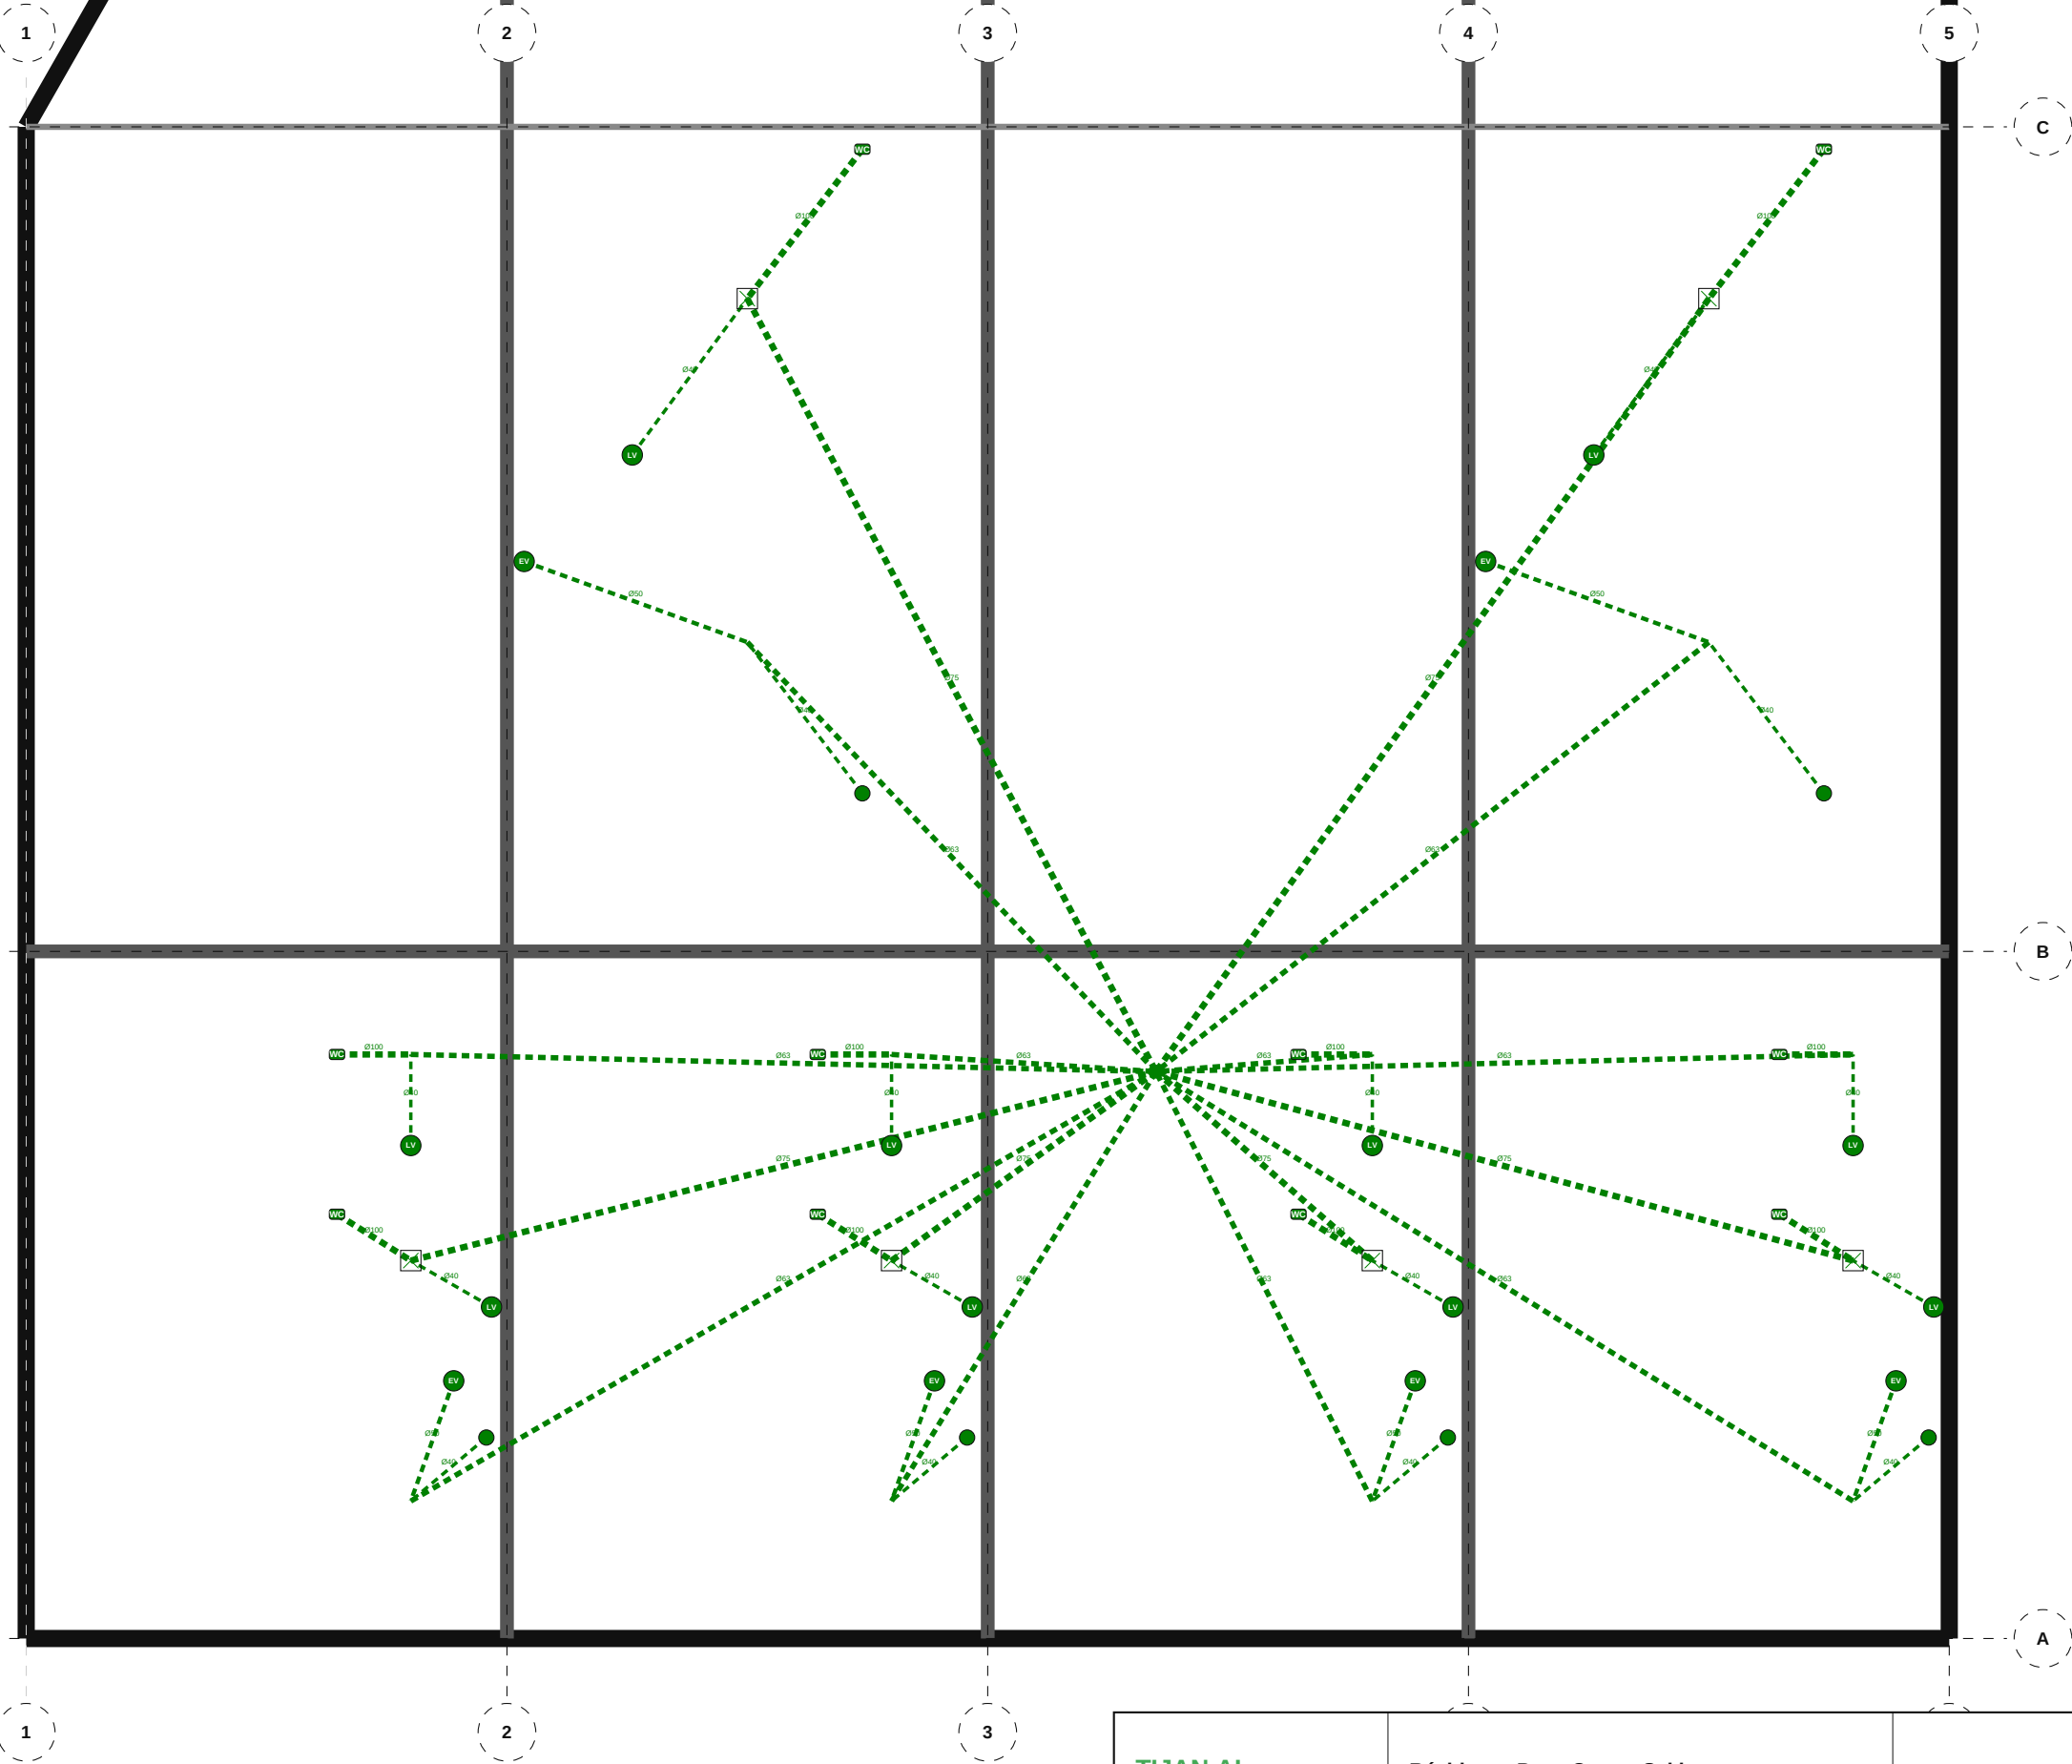

NOMENCLATURE — 410 PLU — Eaux Usées (EU)

- WC suspendu: 10
- Évier cuisine: 6
- Lave-vaisselle: 6
- Lavabo: 6
- Douche: 6
- Lave-mains: 4

TIJAN AI

Bureau d'Études Automatisé

Résidence Papa Oumar Sakho

Dakar, Senegal

Éch: 1/100

Pl. 46/133

410 PLU — Eaux Usées (EU) — R+7

Date: 06/05/2026

Réf: 1711

BIM vPLU-046

Phase: APD

413 HVC — Climatisation (CLIM) — RDC

1

2

3

4

5

B

B

A

A

NOMENCLATURE — 413 HVC — Climatisation (CLIM)

1

• Split climatiseur:

2

3

4

5

TIJAN AI

Bureau d'Études Automatisé

Résidence Papa Oumar Sakho

Dakar, Senegal

Éch: 1/100

Pl. 47/133


413 HVC — Climatisation (CLIM) — RDC

Date: 06/05/2026

Réf: 1711

BIM vHVC-047


Phase: APD

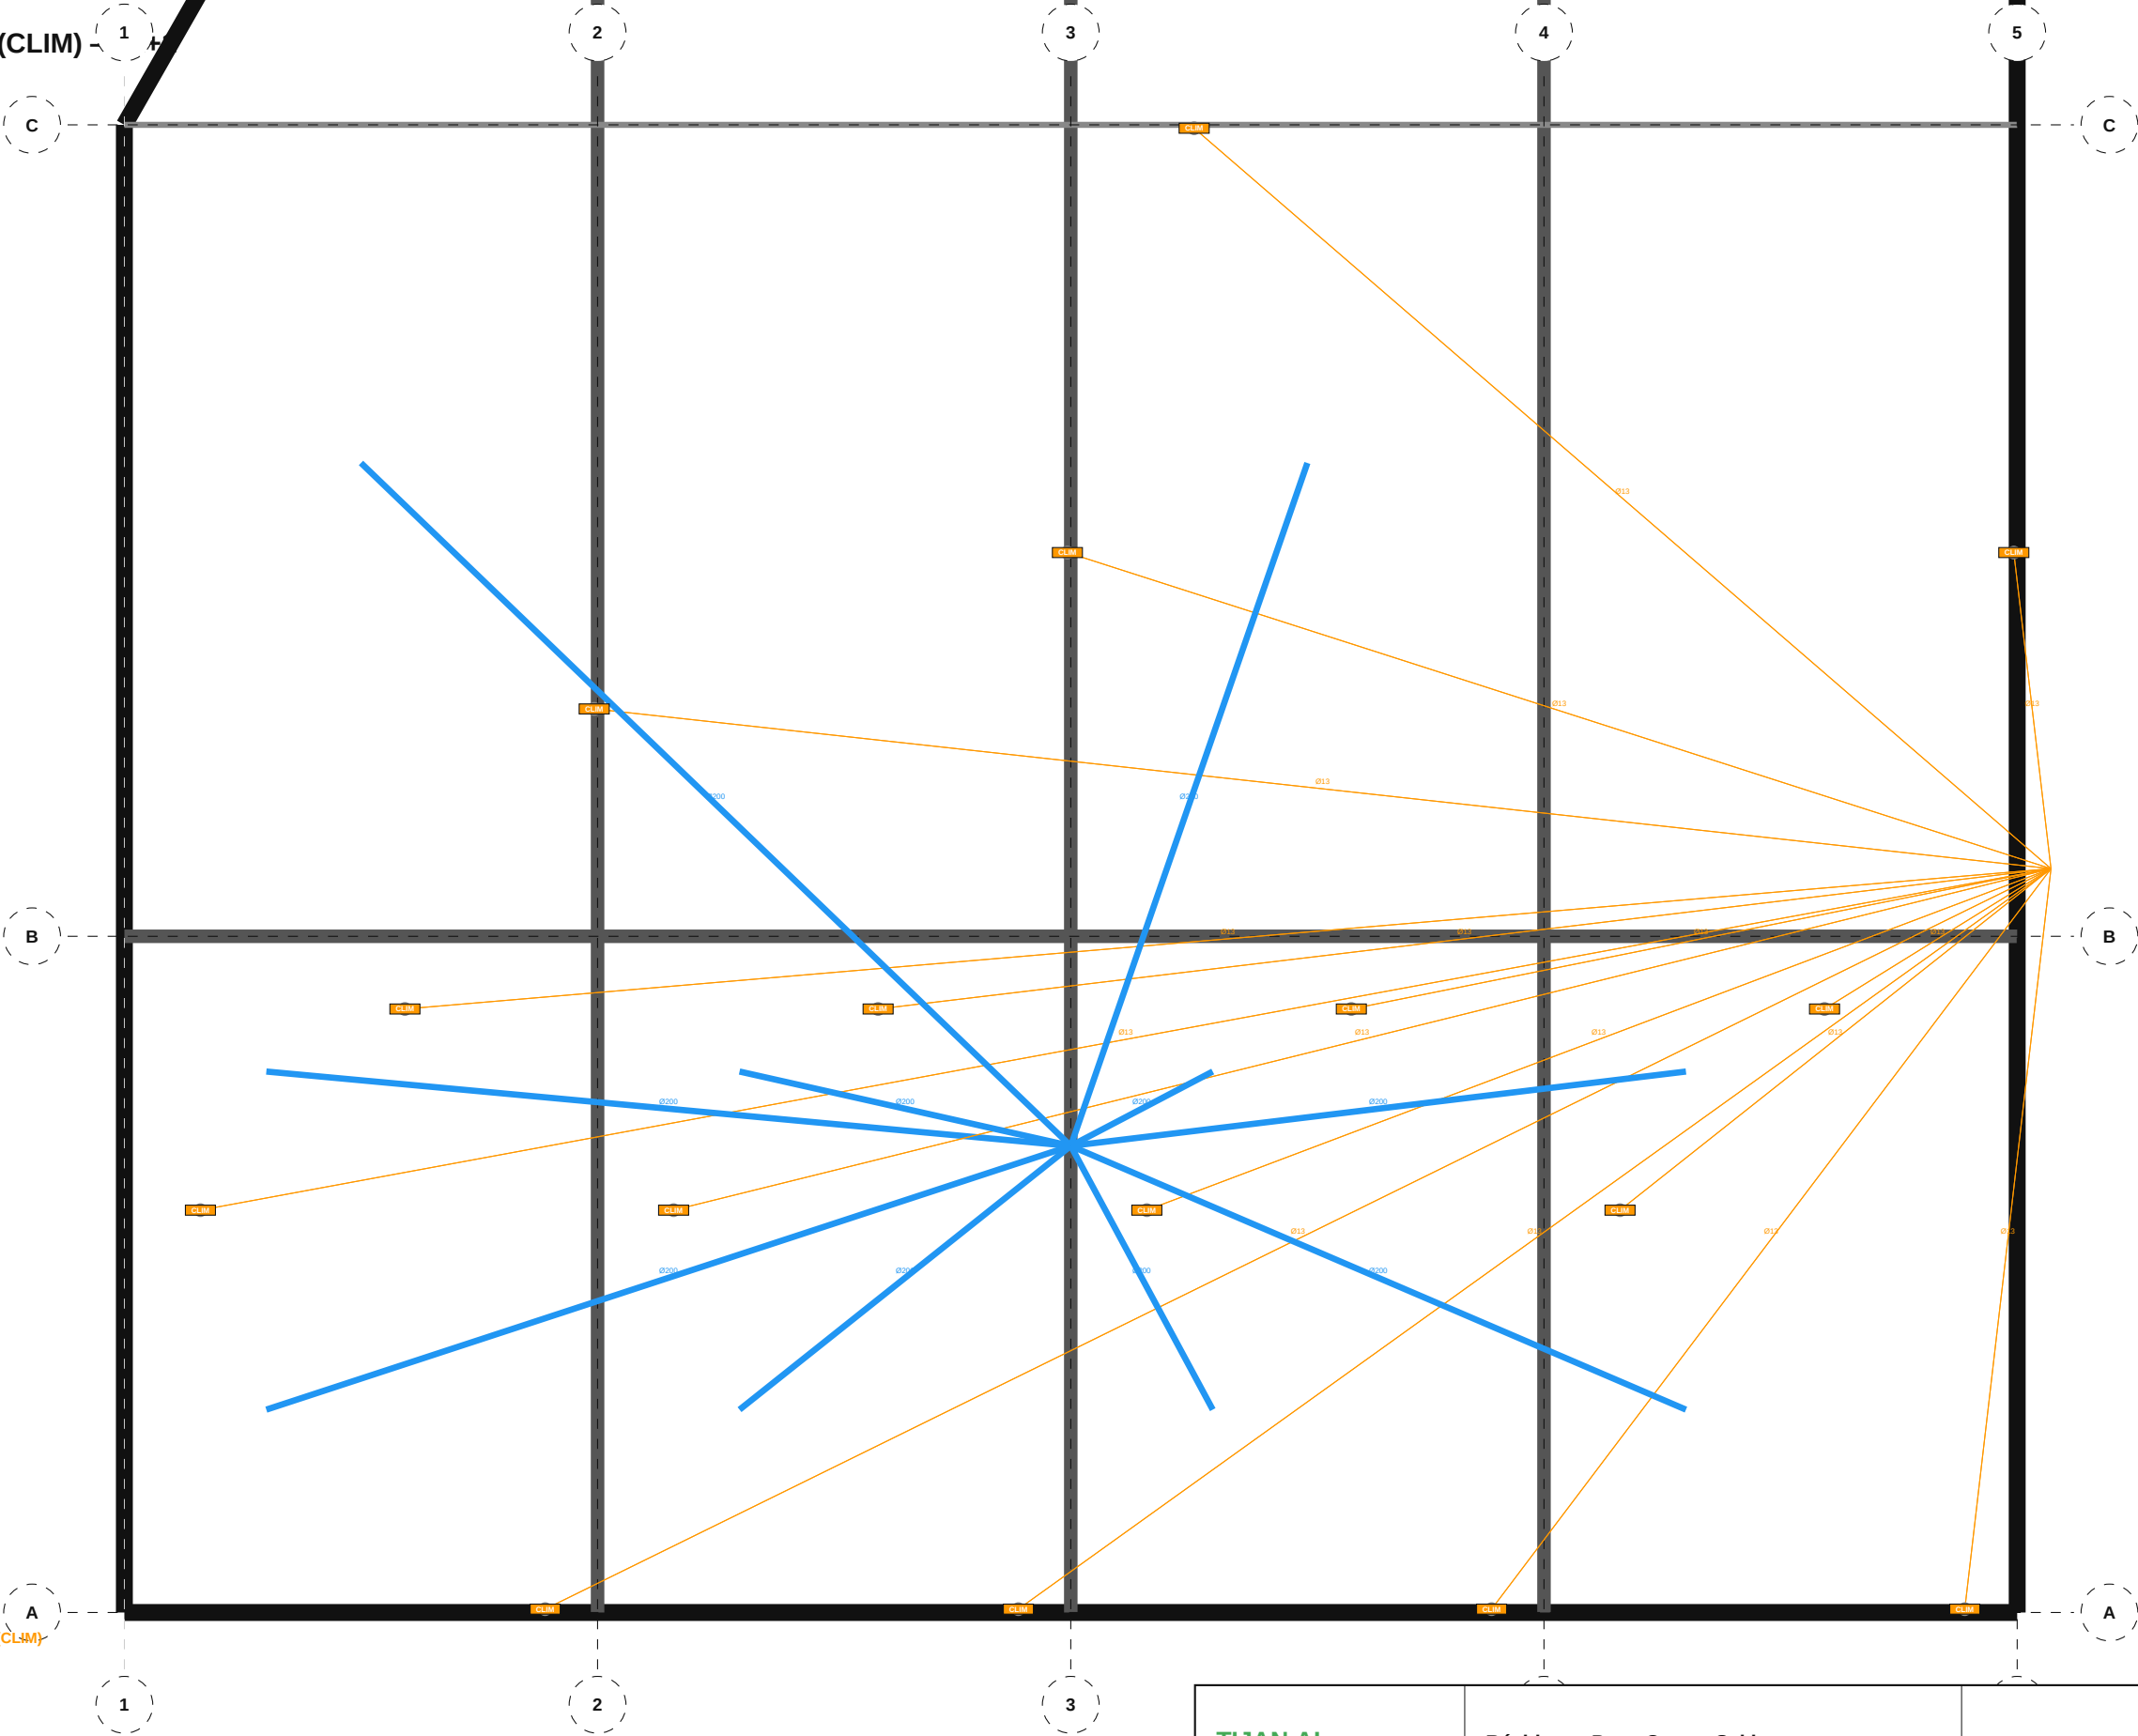

NOMENCLATURE — 413 HVC — Climatisation (CLIM)
• Split climatiseur: 16

TIJAN AI Bureau d'Études Automatisé	Résidence Papa Oumar Sakho Dakar, Senegal	Éch: 1/100 Pl. 48/133
	413 HVC — Climatisation (CLIM) — R+1	
Date: 06/05/2026	Réf: 1711	BIM vHVC-048 Phase: APD

413 HVC — Climatisation (CLIM)

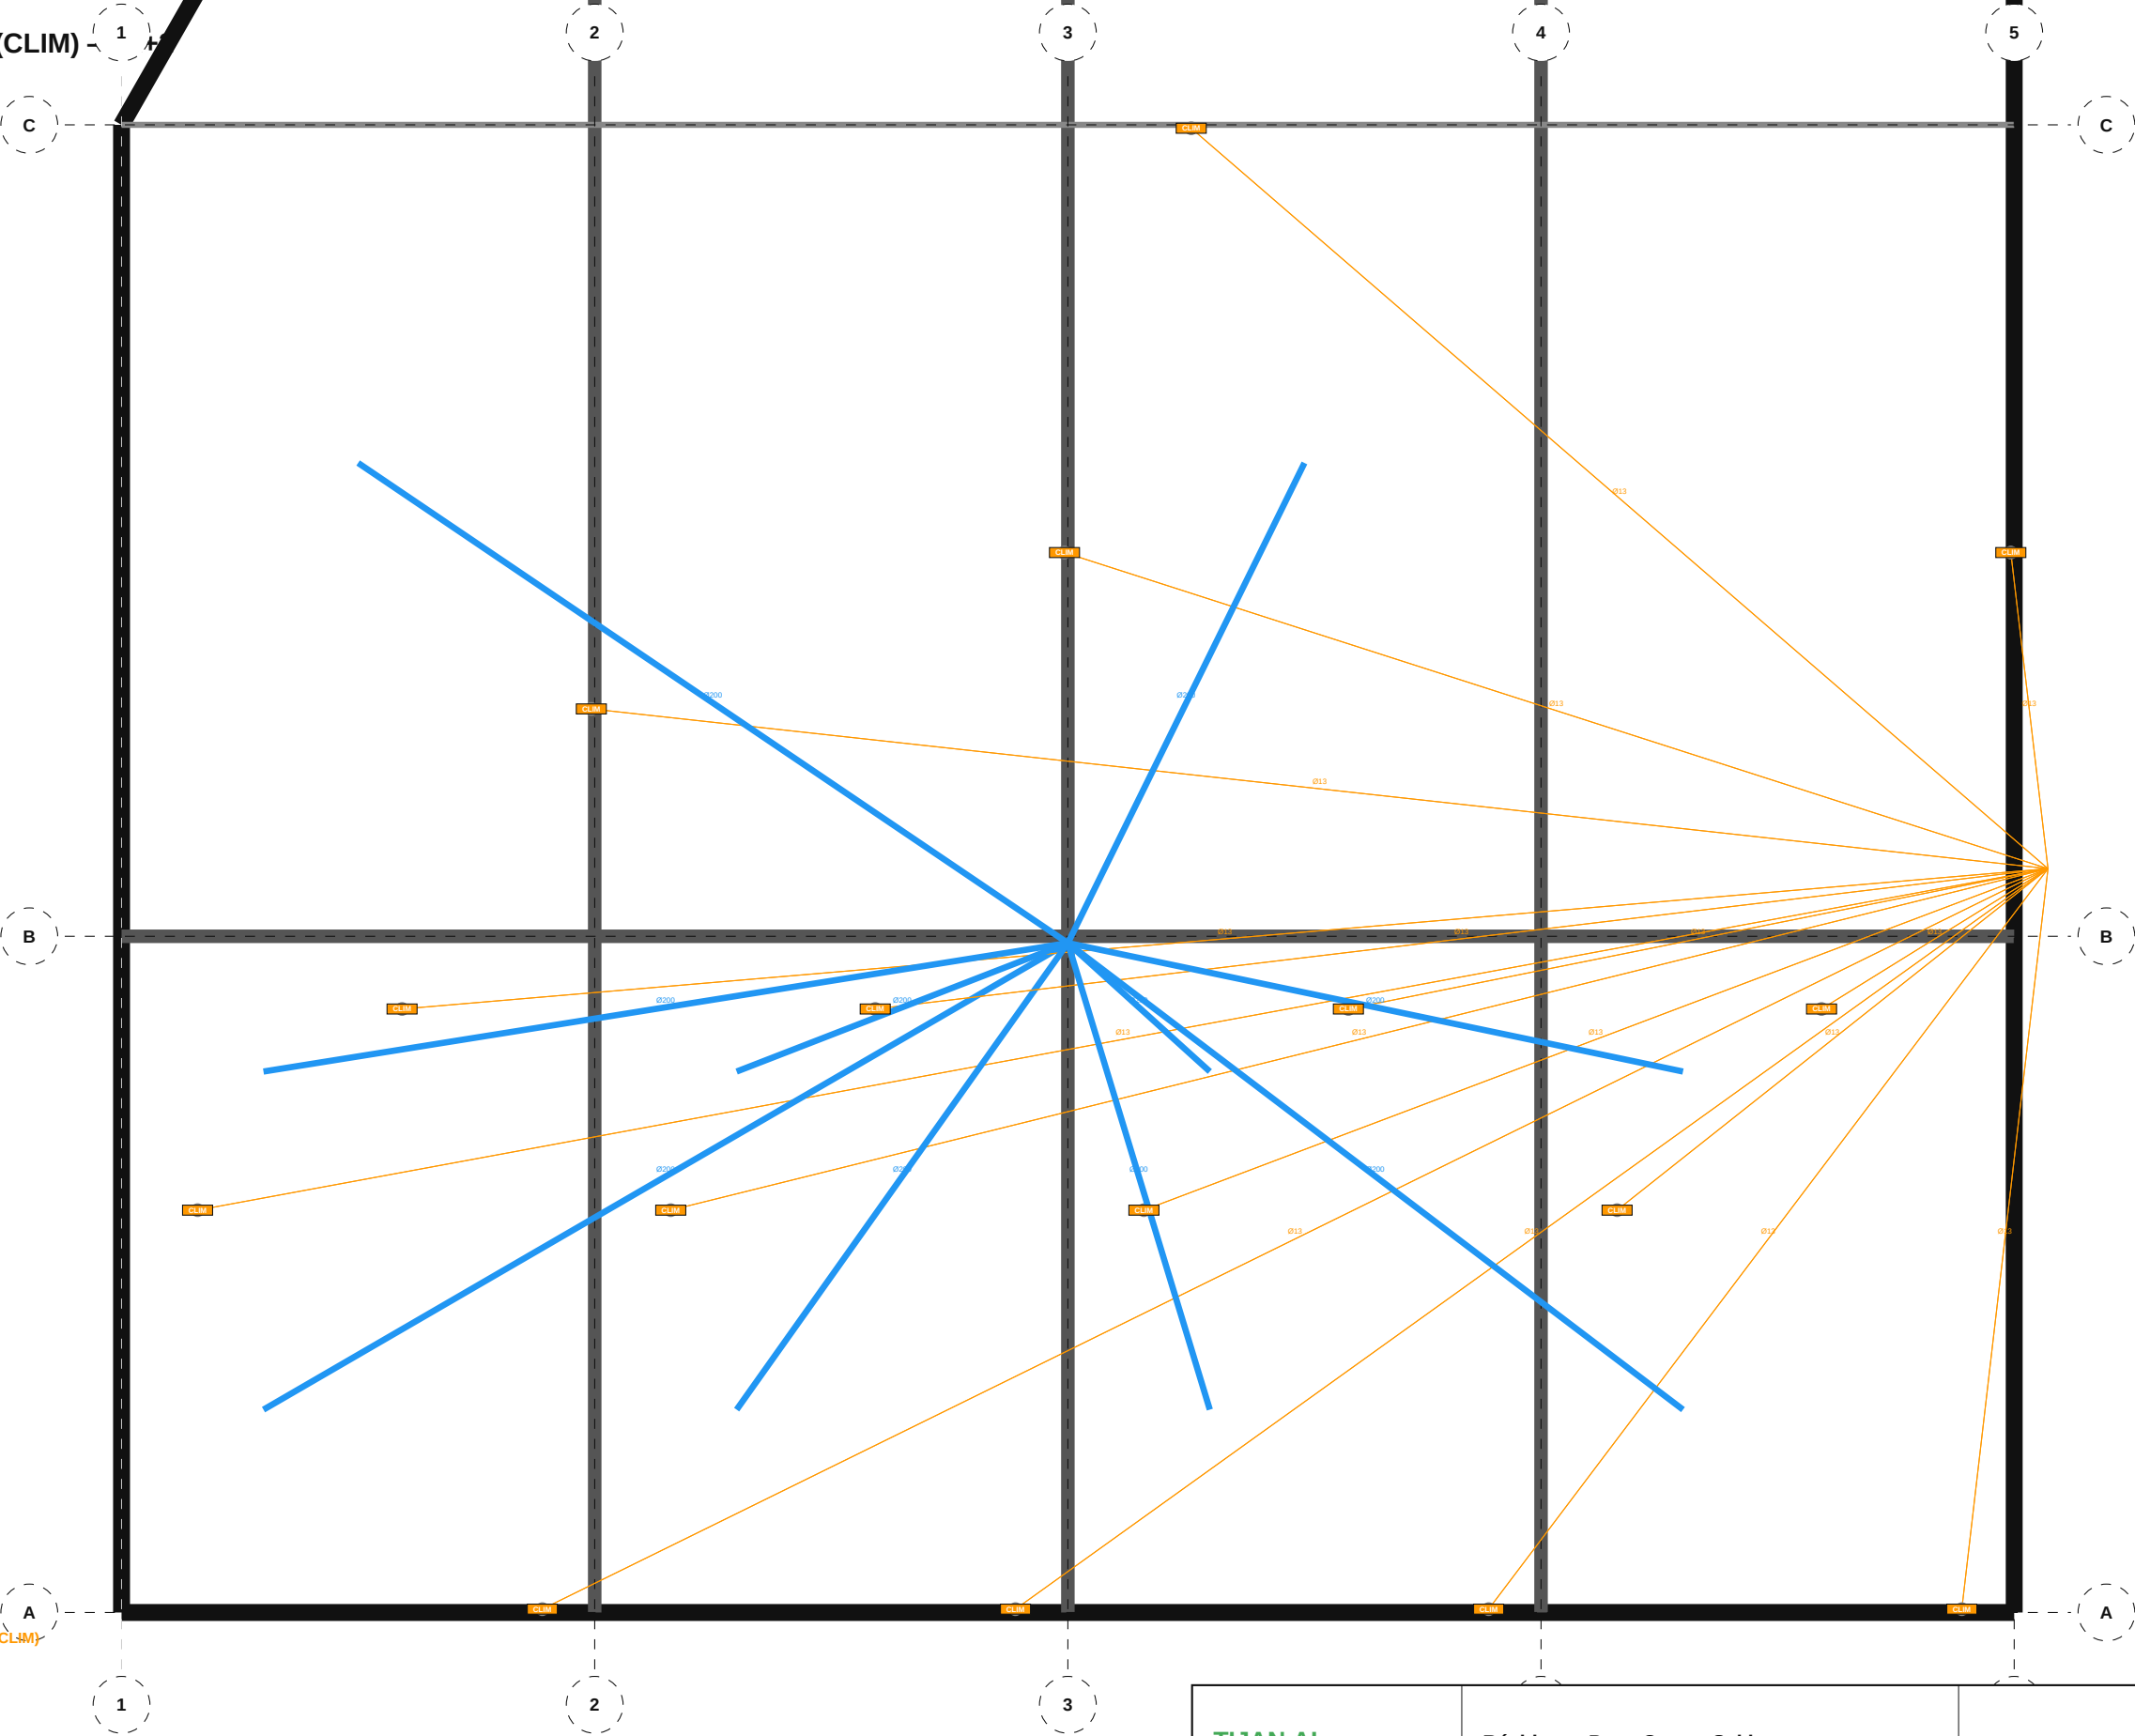


NOMENCLATURE — 413 HVC — Climatisation (CLIM)

• Split climatiseur: 16

TIJAN AI Bureau d'Études Automatisé	Résidence Papa Oumar Sakho Dakar, Senegal	Éch: 1/100 Pl. 49/133
	413 HVC — Climatisation (CLIM) — R+2	
Date: 06/05/2026	Réf: 1711	BIM vHVC-049 Phase: APD

413 HVC — Climatisation (CLIM)

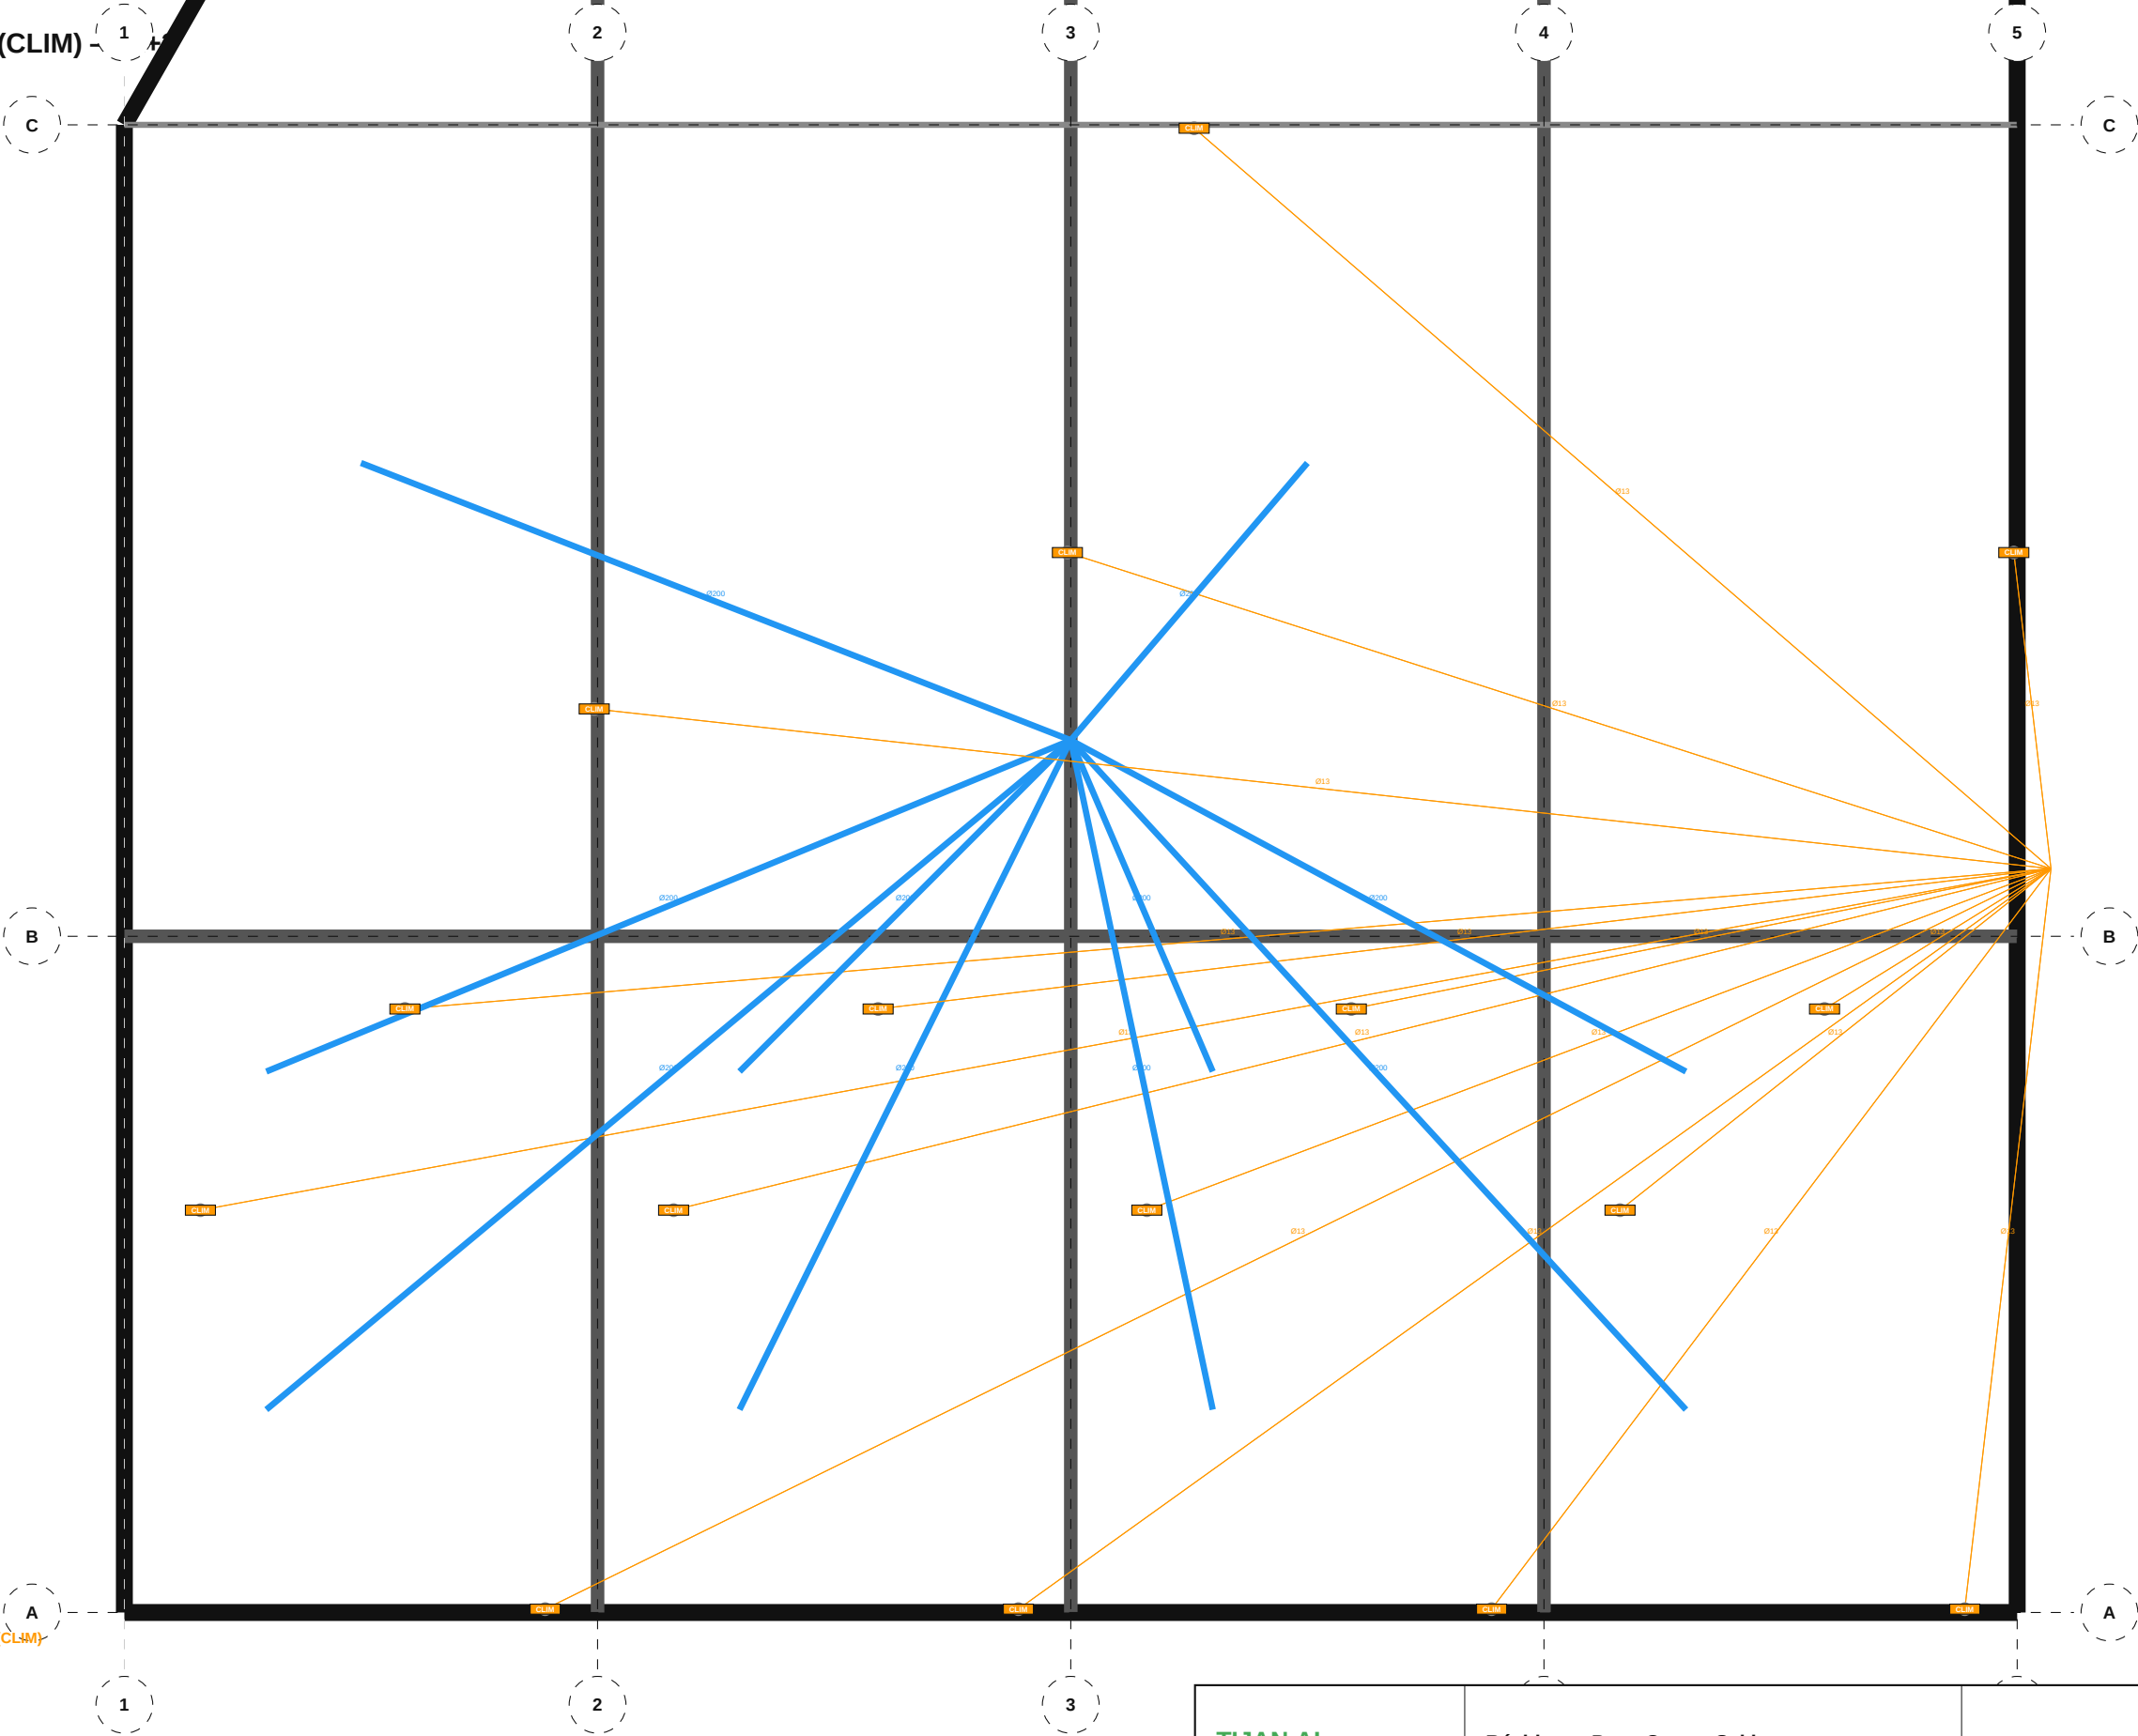

NOMENCLATURE — 413 HVC — Climatisation (CLIM)

• Split climatiseur: 16

TIJAN AI Bureau d'Études Automatisé	Résidence Papa Oumar Sakho Dakar, Senegal	Éch: 1/100 Pl. 50/133
	413 HVC — Climatisation (CLIM) — R+3	
Date: 06/05/2026	Réf: 1711	BIM vHVC-050 Phase: APD

14

C

2

3

4

5

C

B

B

A

A

1

2

3

Bureau d'Études Automatisé

Dakar, Senegal


Pl. 51/133

413 HVC — Climatisation (CLIM) — R+4

Réf: 1711

Phase: APD

413 HVC — Climatisation (CLIM)

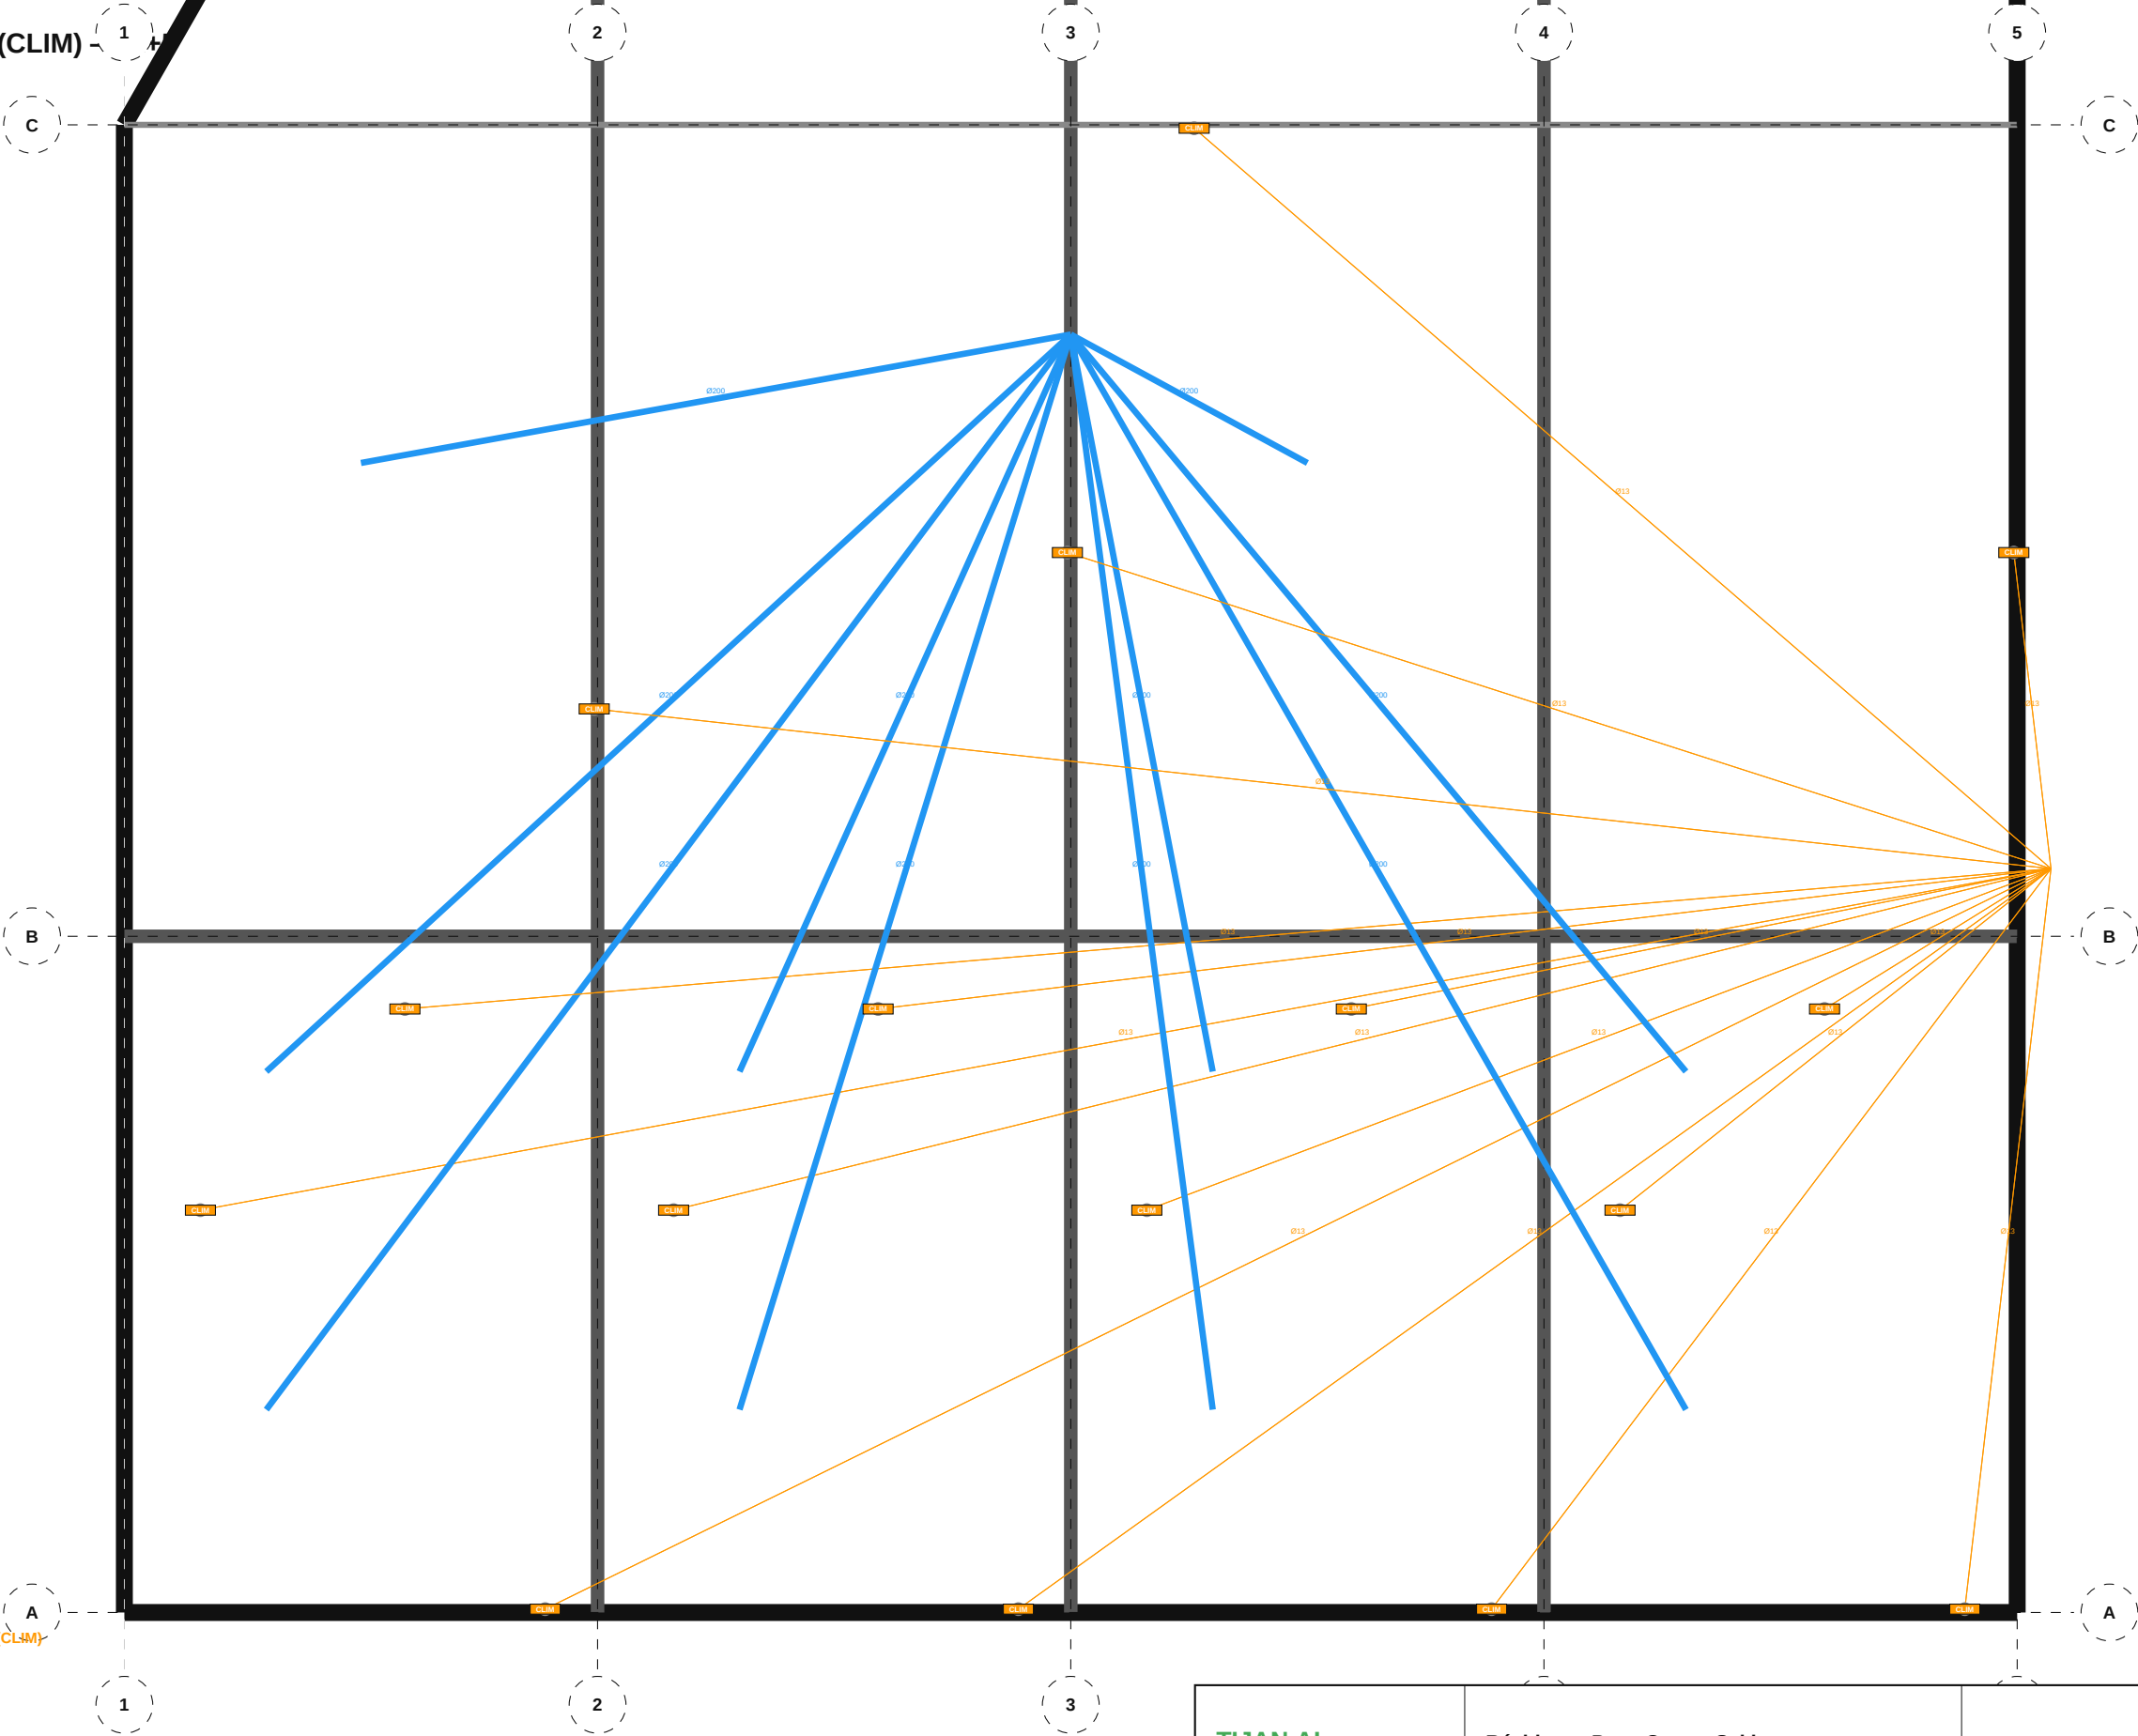


NOMENCLATURE — 413 HVC — Climatisation (CLIM)

• Split climatiseur: 16

TIJAN AI Bureau d'Études Automatisé	Résidence Papa Oumar Sakho Dakar, Senegal	Éch: 1/100 Pl. 52/133
	413 HVC — Climatisation (CLIM) — R+5	
Date: 06/05/2026	Réf: 1711	BIM vHVC-052 Phase: APD

413 HVC — Climatisation (CLIM)

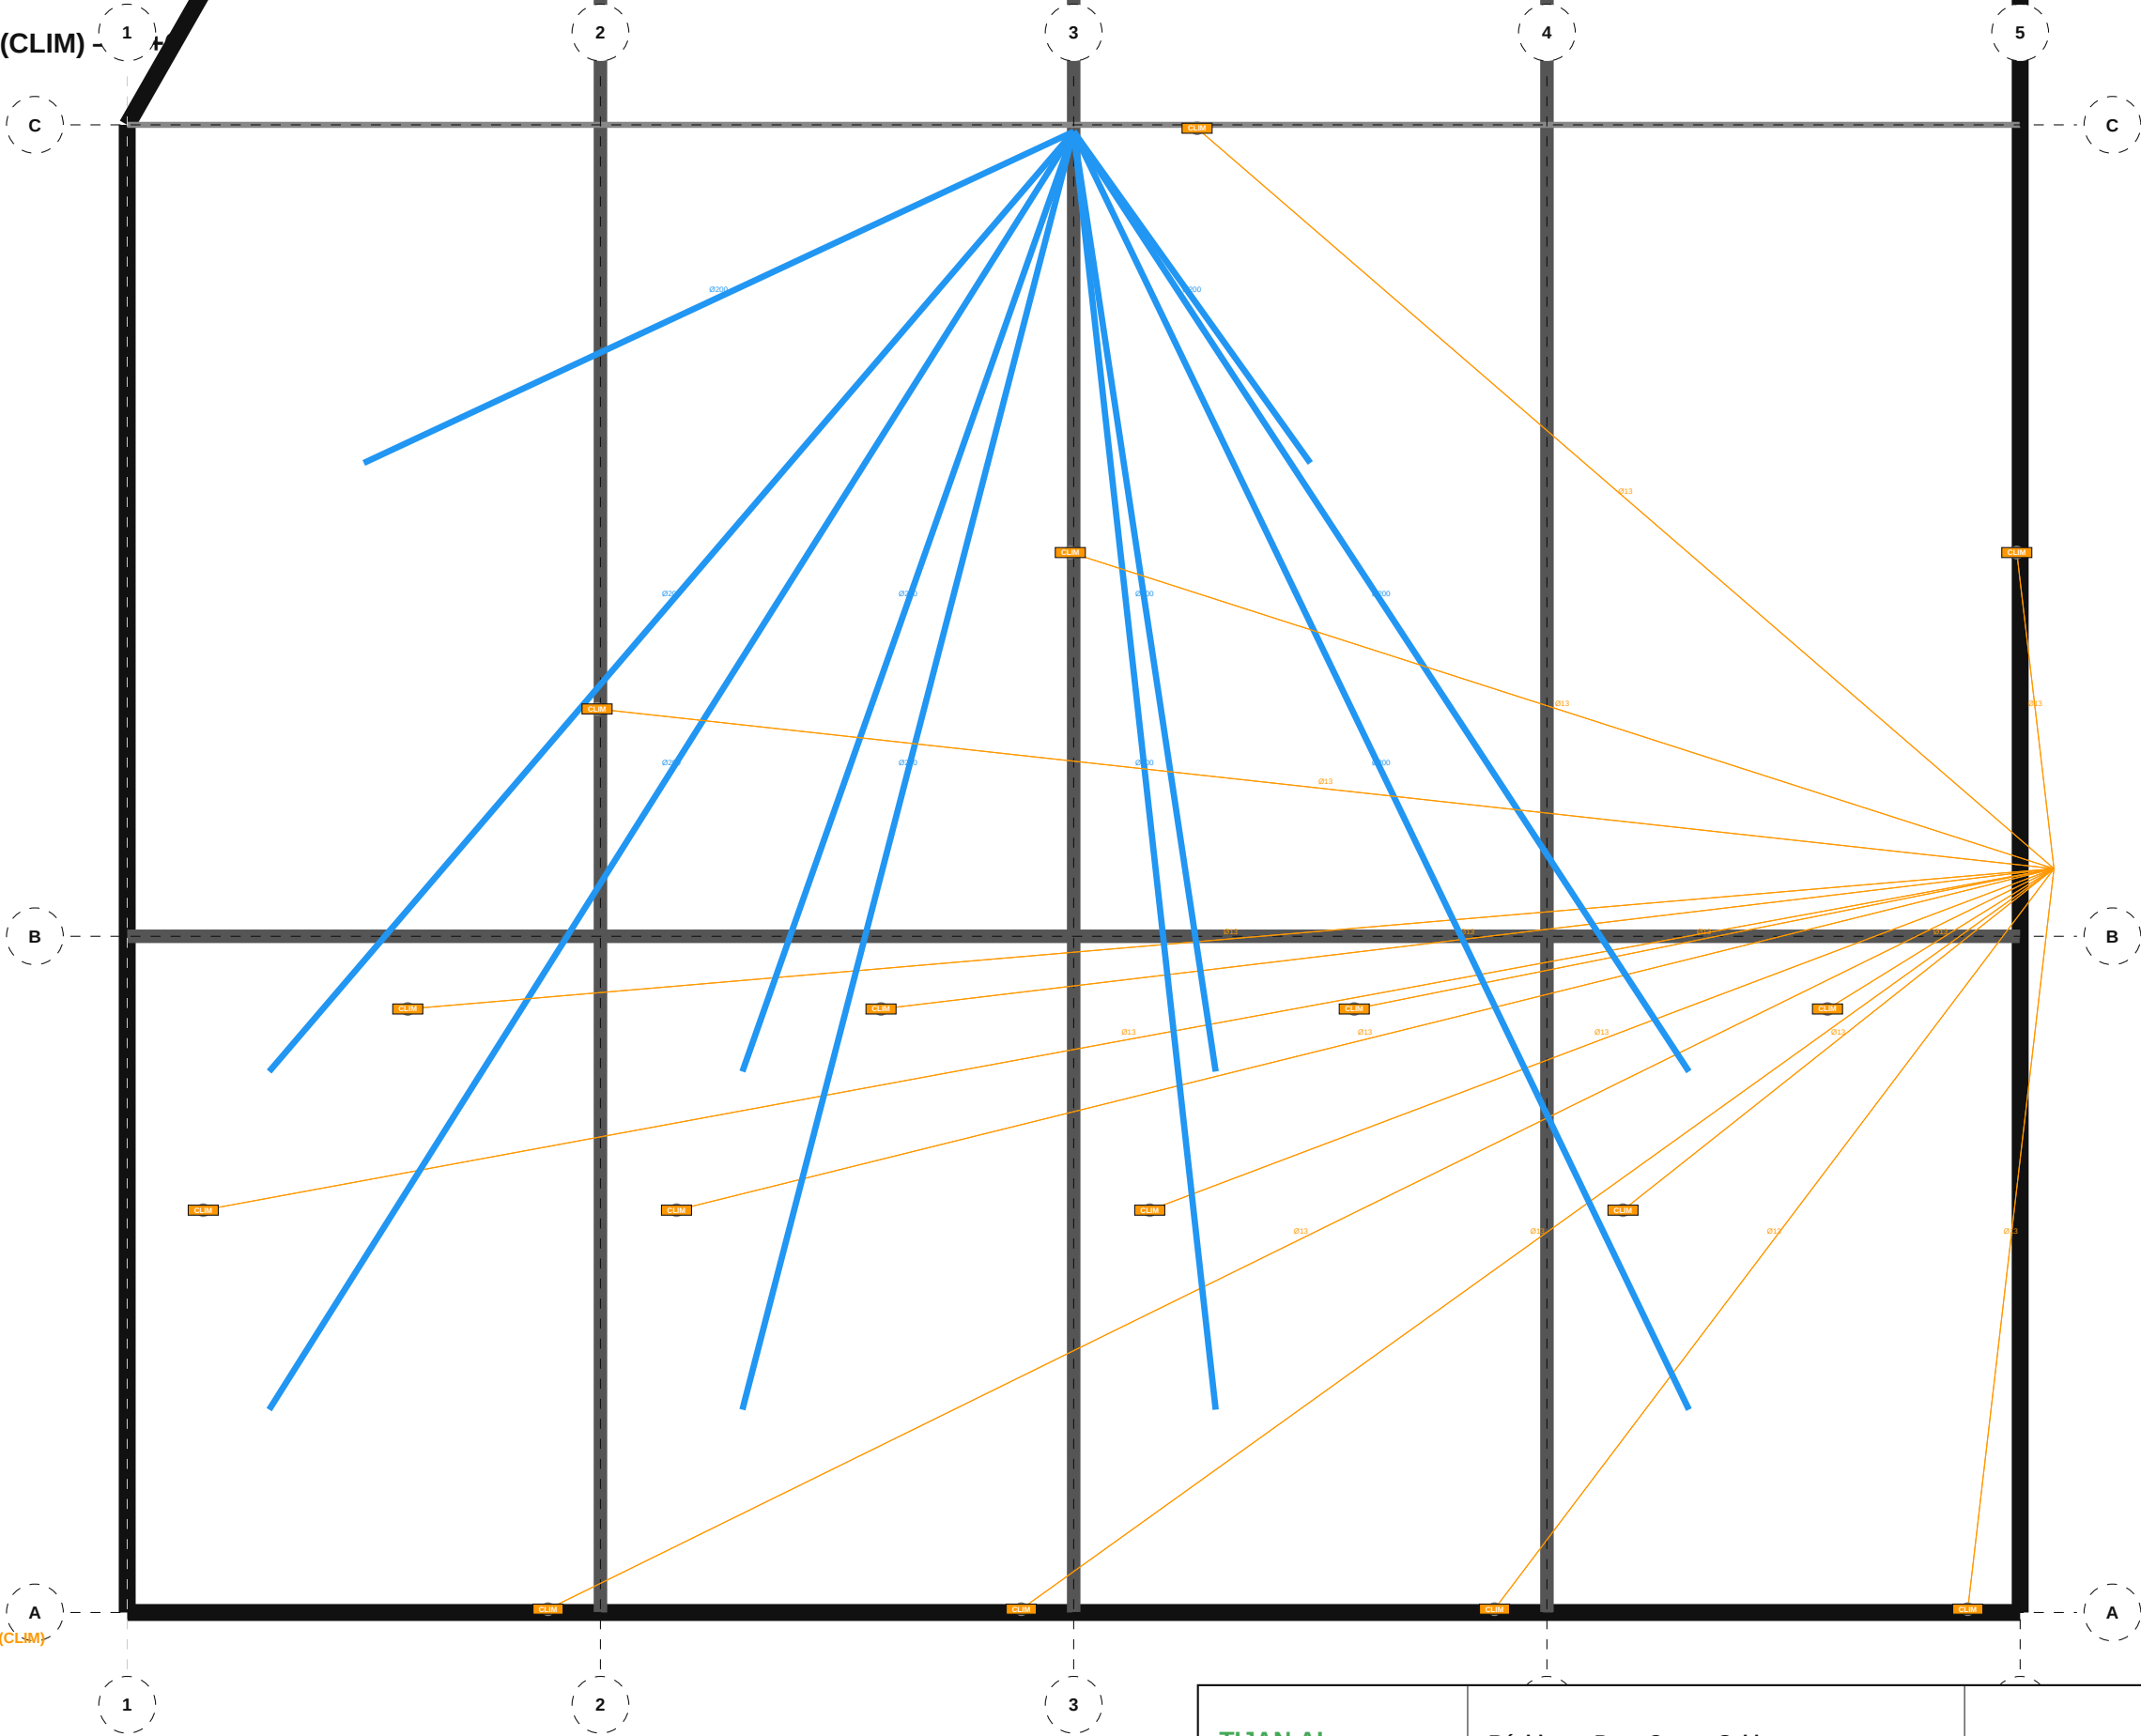


NOMENCLATURE — 413 HVC — Climatisation (CLIM)

• Split climatiseur: 16

TIJAN AI Bureau d'Études Automatisé	Résidence Papa Oumar Sakho Dakar, Senegal	Éch: 1/100 Pl. 53/133
	413 HVC — Climatisation (CLIM) — R+6	
Date: 06/05/2026	Réf: 1711	BIM vHVC-053 Phase: APD

413 HVC — Climatisation (CLIM)

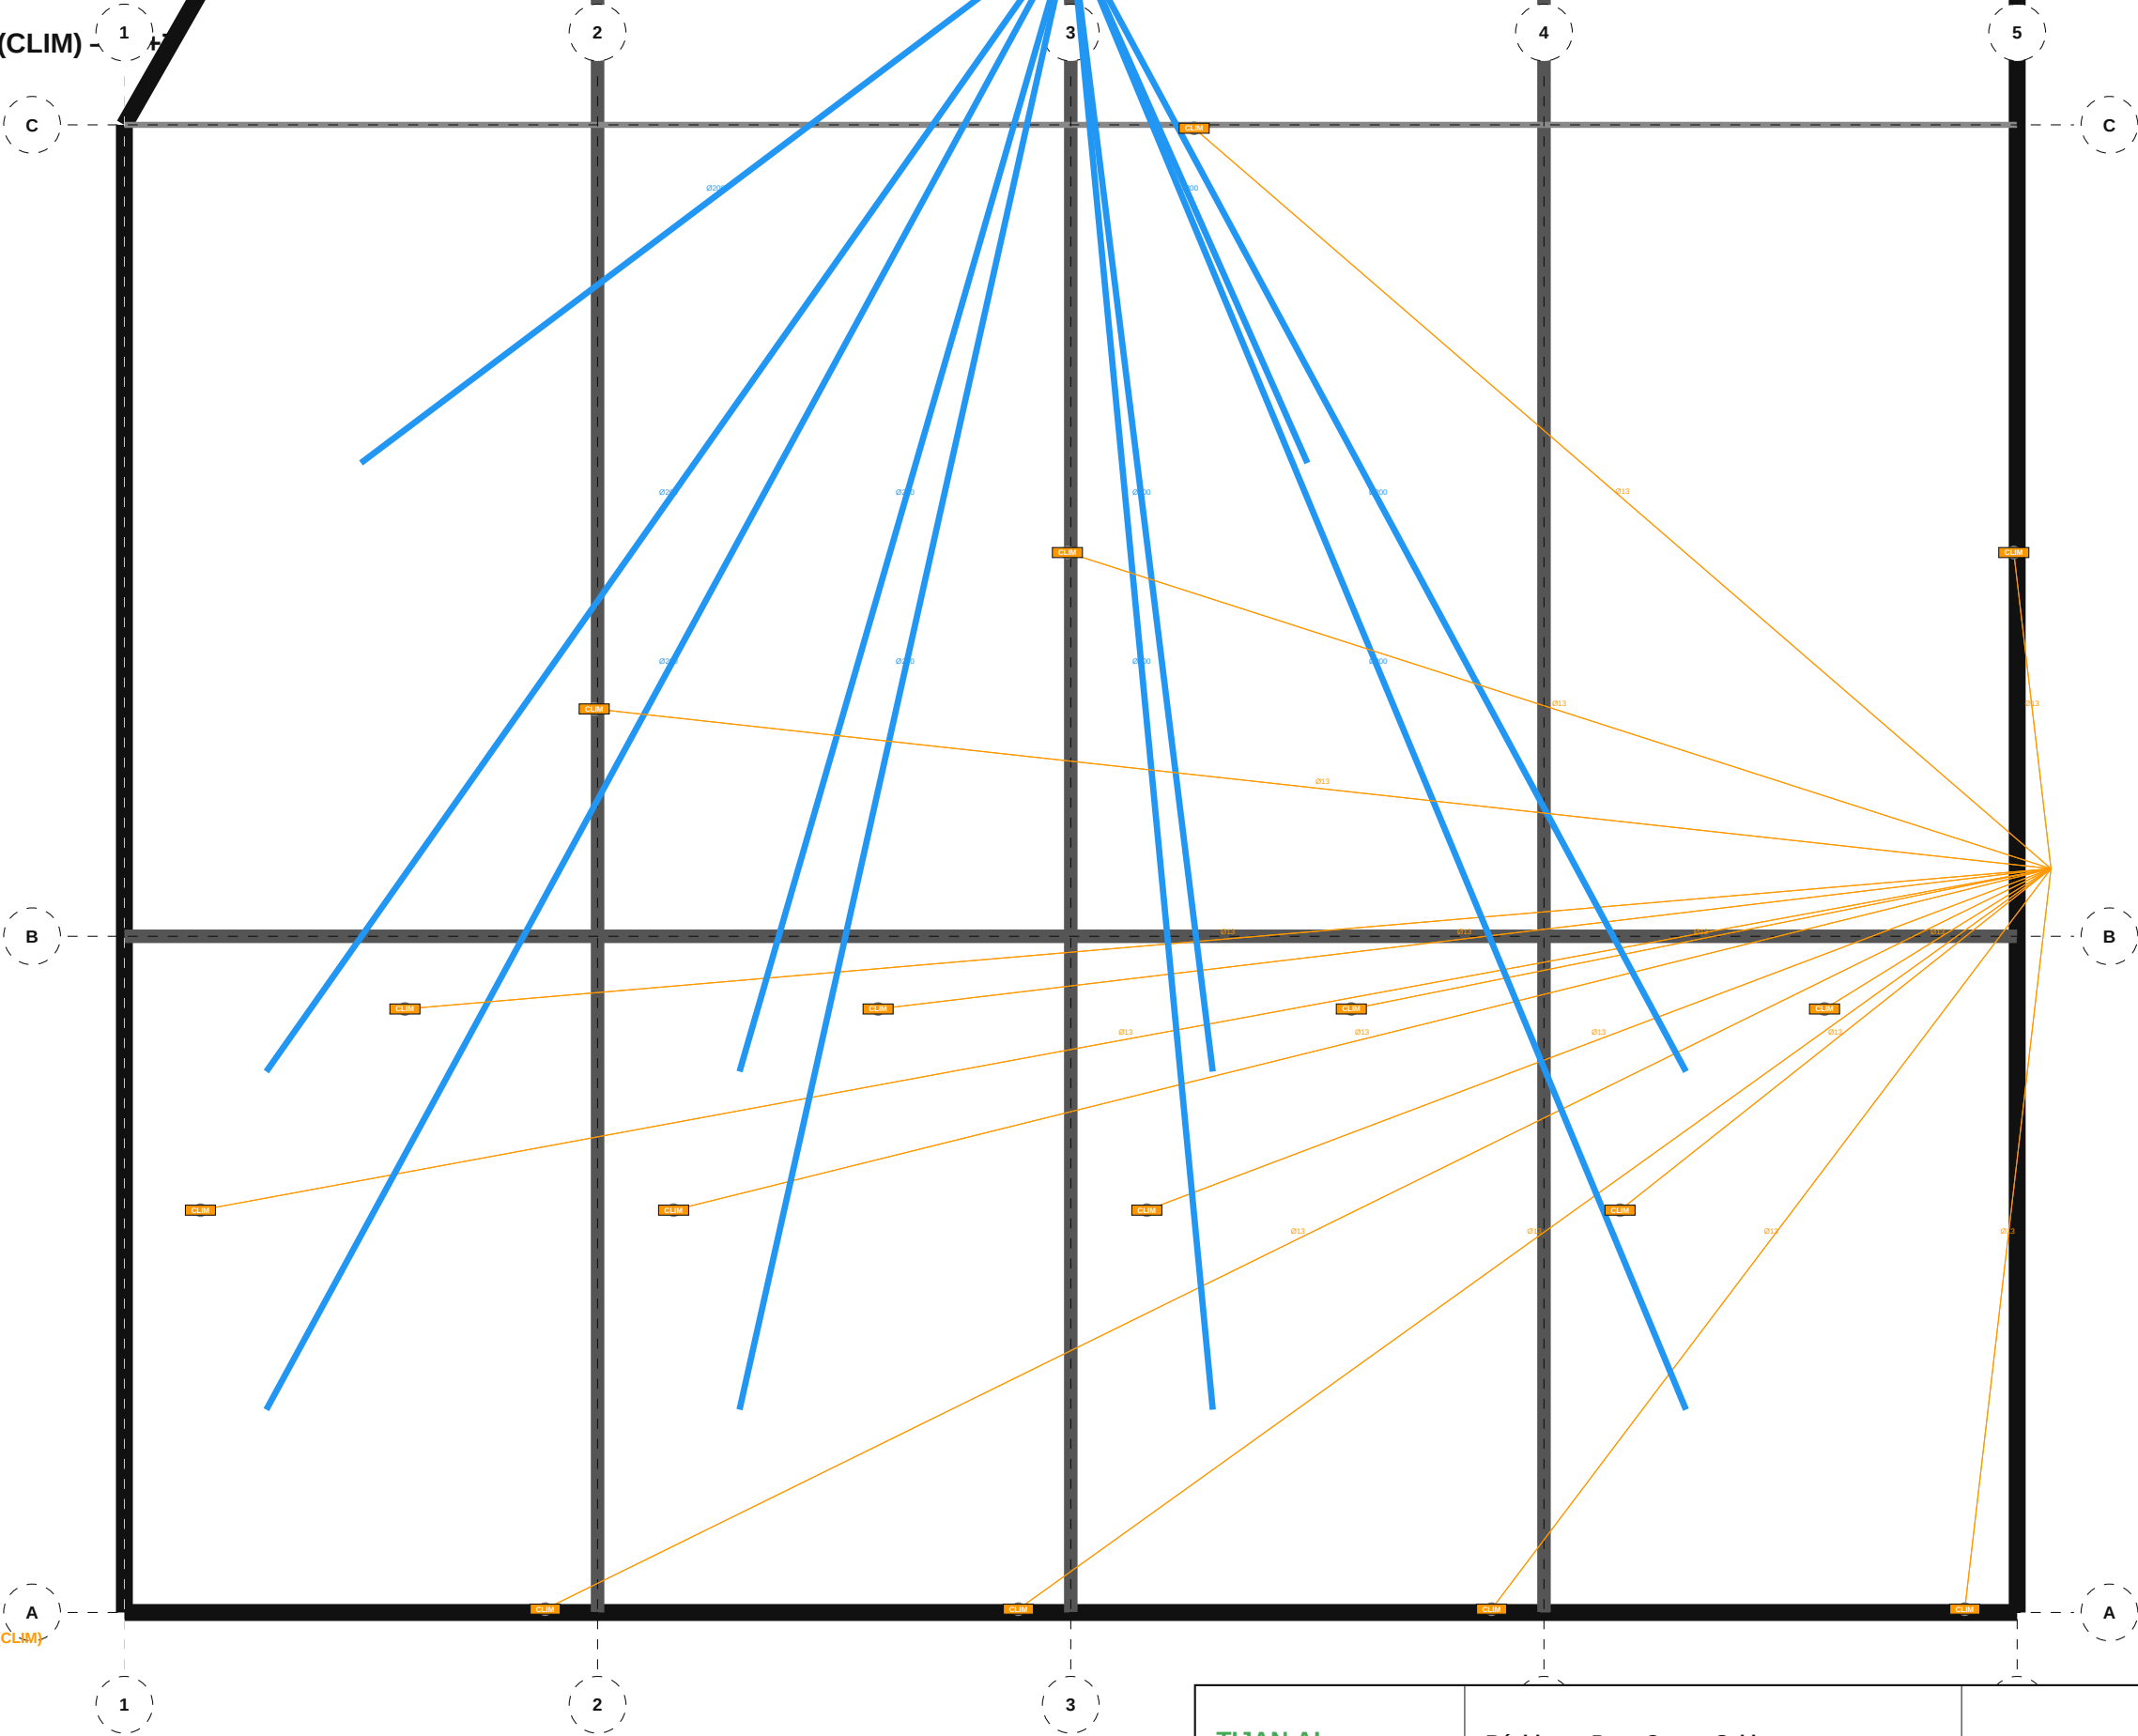

NOMENCLATURE — 413 HVC — Climatisation (CLIM)

• Split climatiseur: 16

TIJAN AI

Bureau d'Études Automatisé

Résidence Papa Oumar Sakho

Dakar, Senegal

Éch: 1/100

Pl. 54/133


413 HVC — Climatisation (CLIM) — R+7

Date: 06/05/2026

Réf: 1711

BIM vHVC-054

Phase: APD

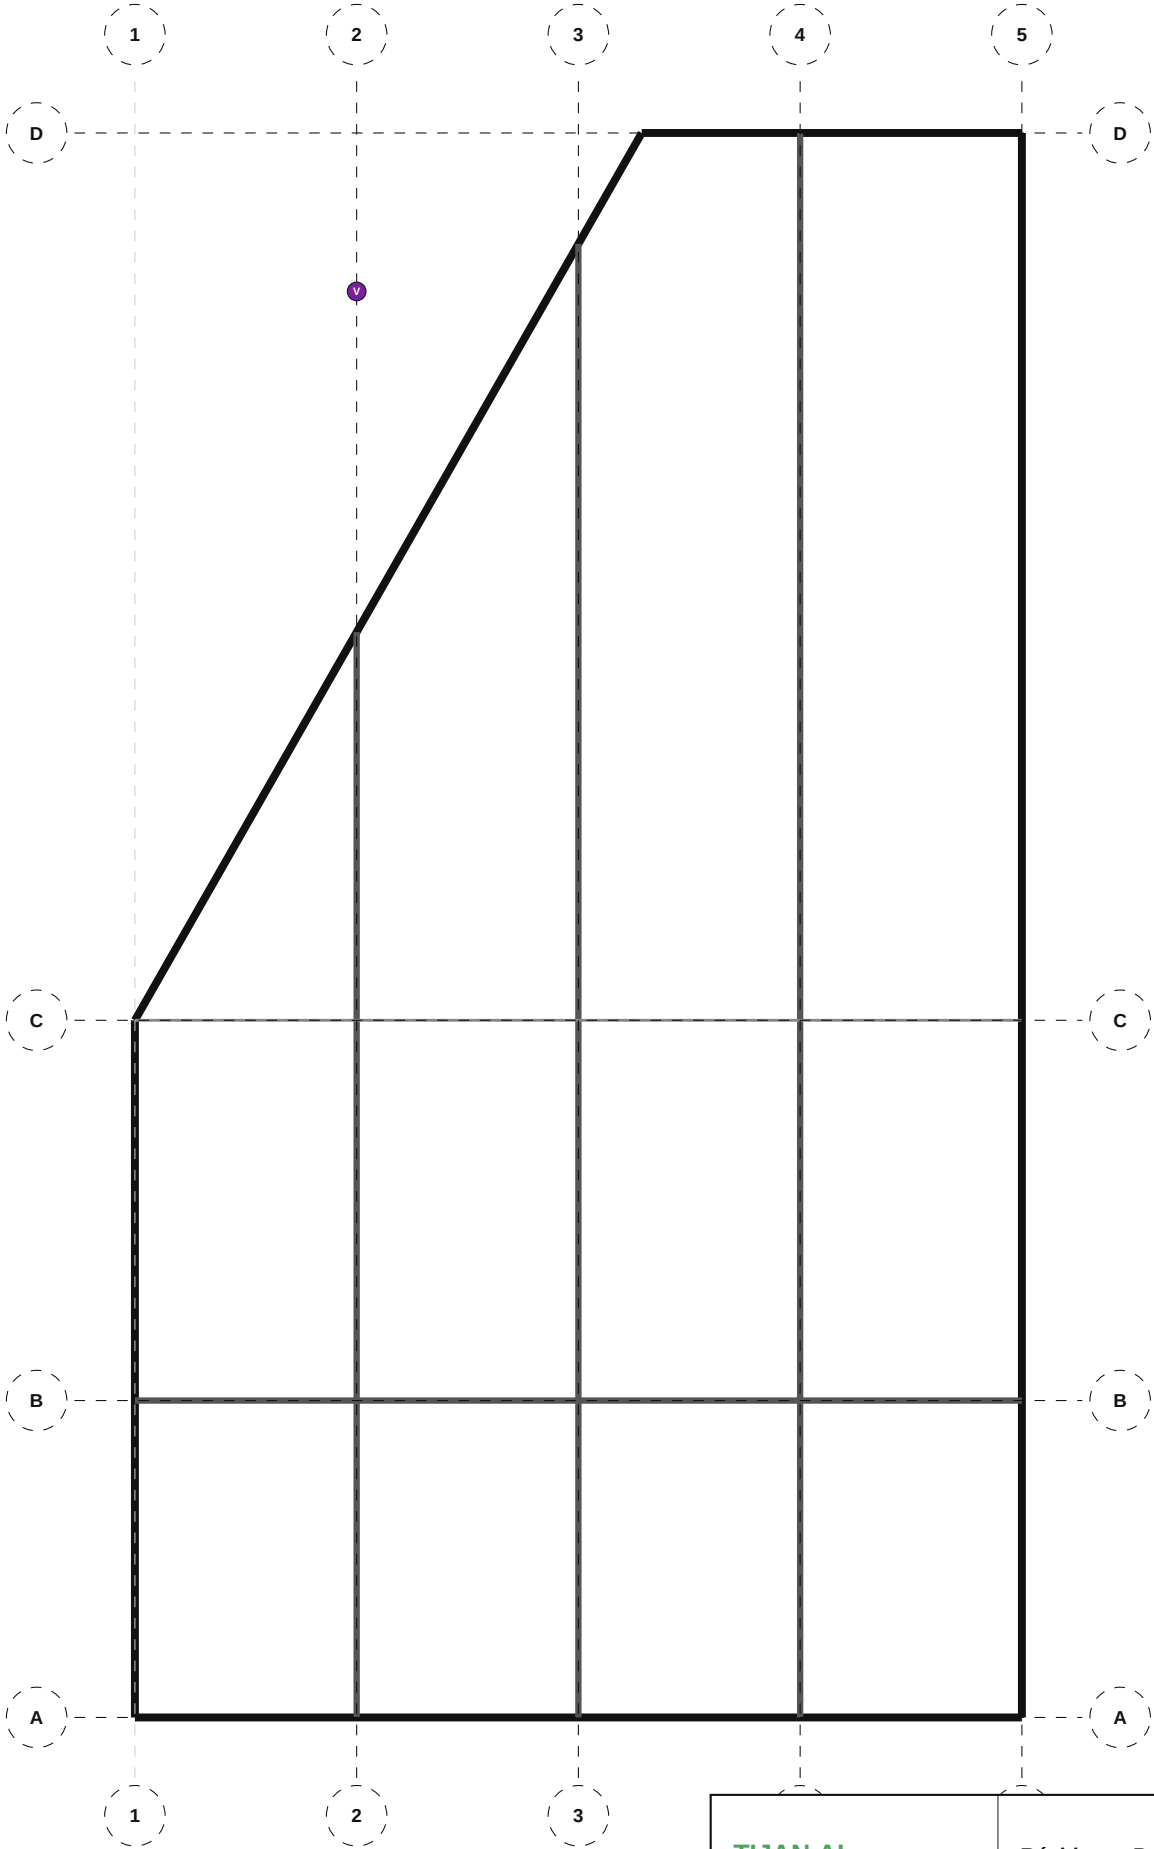

NOMENCLATURE — 413 HVC — Ventilation (VMC)

• Bouche VMC: 1

TIJAN AI Bureau d'Études Automatisé	Résidence Papa Oumar Sakho Dakar, Senegal	Éch: 1/100 Pl. 55/133
	413 HVC — Ventilation (VMC) — Sous-Sol	
Date: 06/05/2026	Réf: 1711	BIM vHVC-055 Phase: APD

413 HVC — Ventilation (VMC) — RDC

1

2

3

4

5

B

B

A

A

NOMENCLATURE — 413 HVC — Ventilation (VMC)

1

• Bouche VMC: 1

2

3

4

5

TIJAN AI

Bureau d'Études Automatisé

Résidence Papa Oumar Sakho

Dakar, Senegal

Éch: 1/100

Pl. 56/133

413 HVC — Ventilation (VMC) — RDC


Date: 06/05/2026

Réf: 1711

BIM vHVC-056

Phase: APD

413 HVC — Ventilation (VMC) — R+1

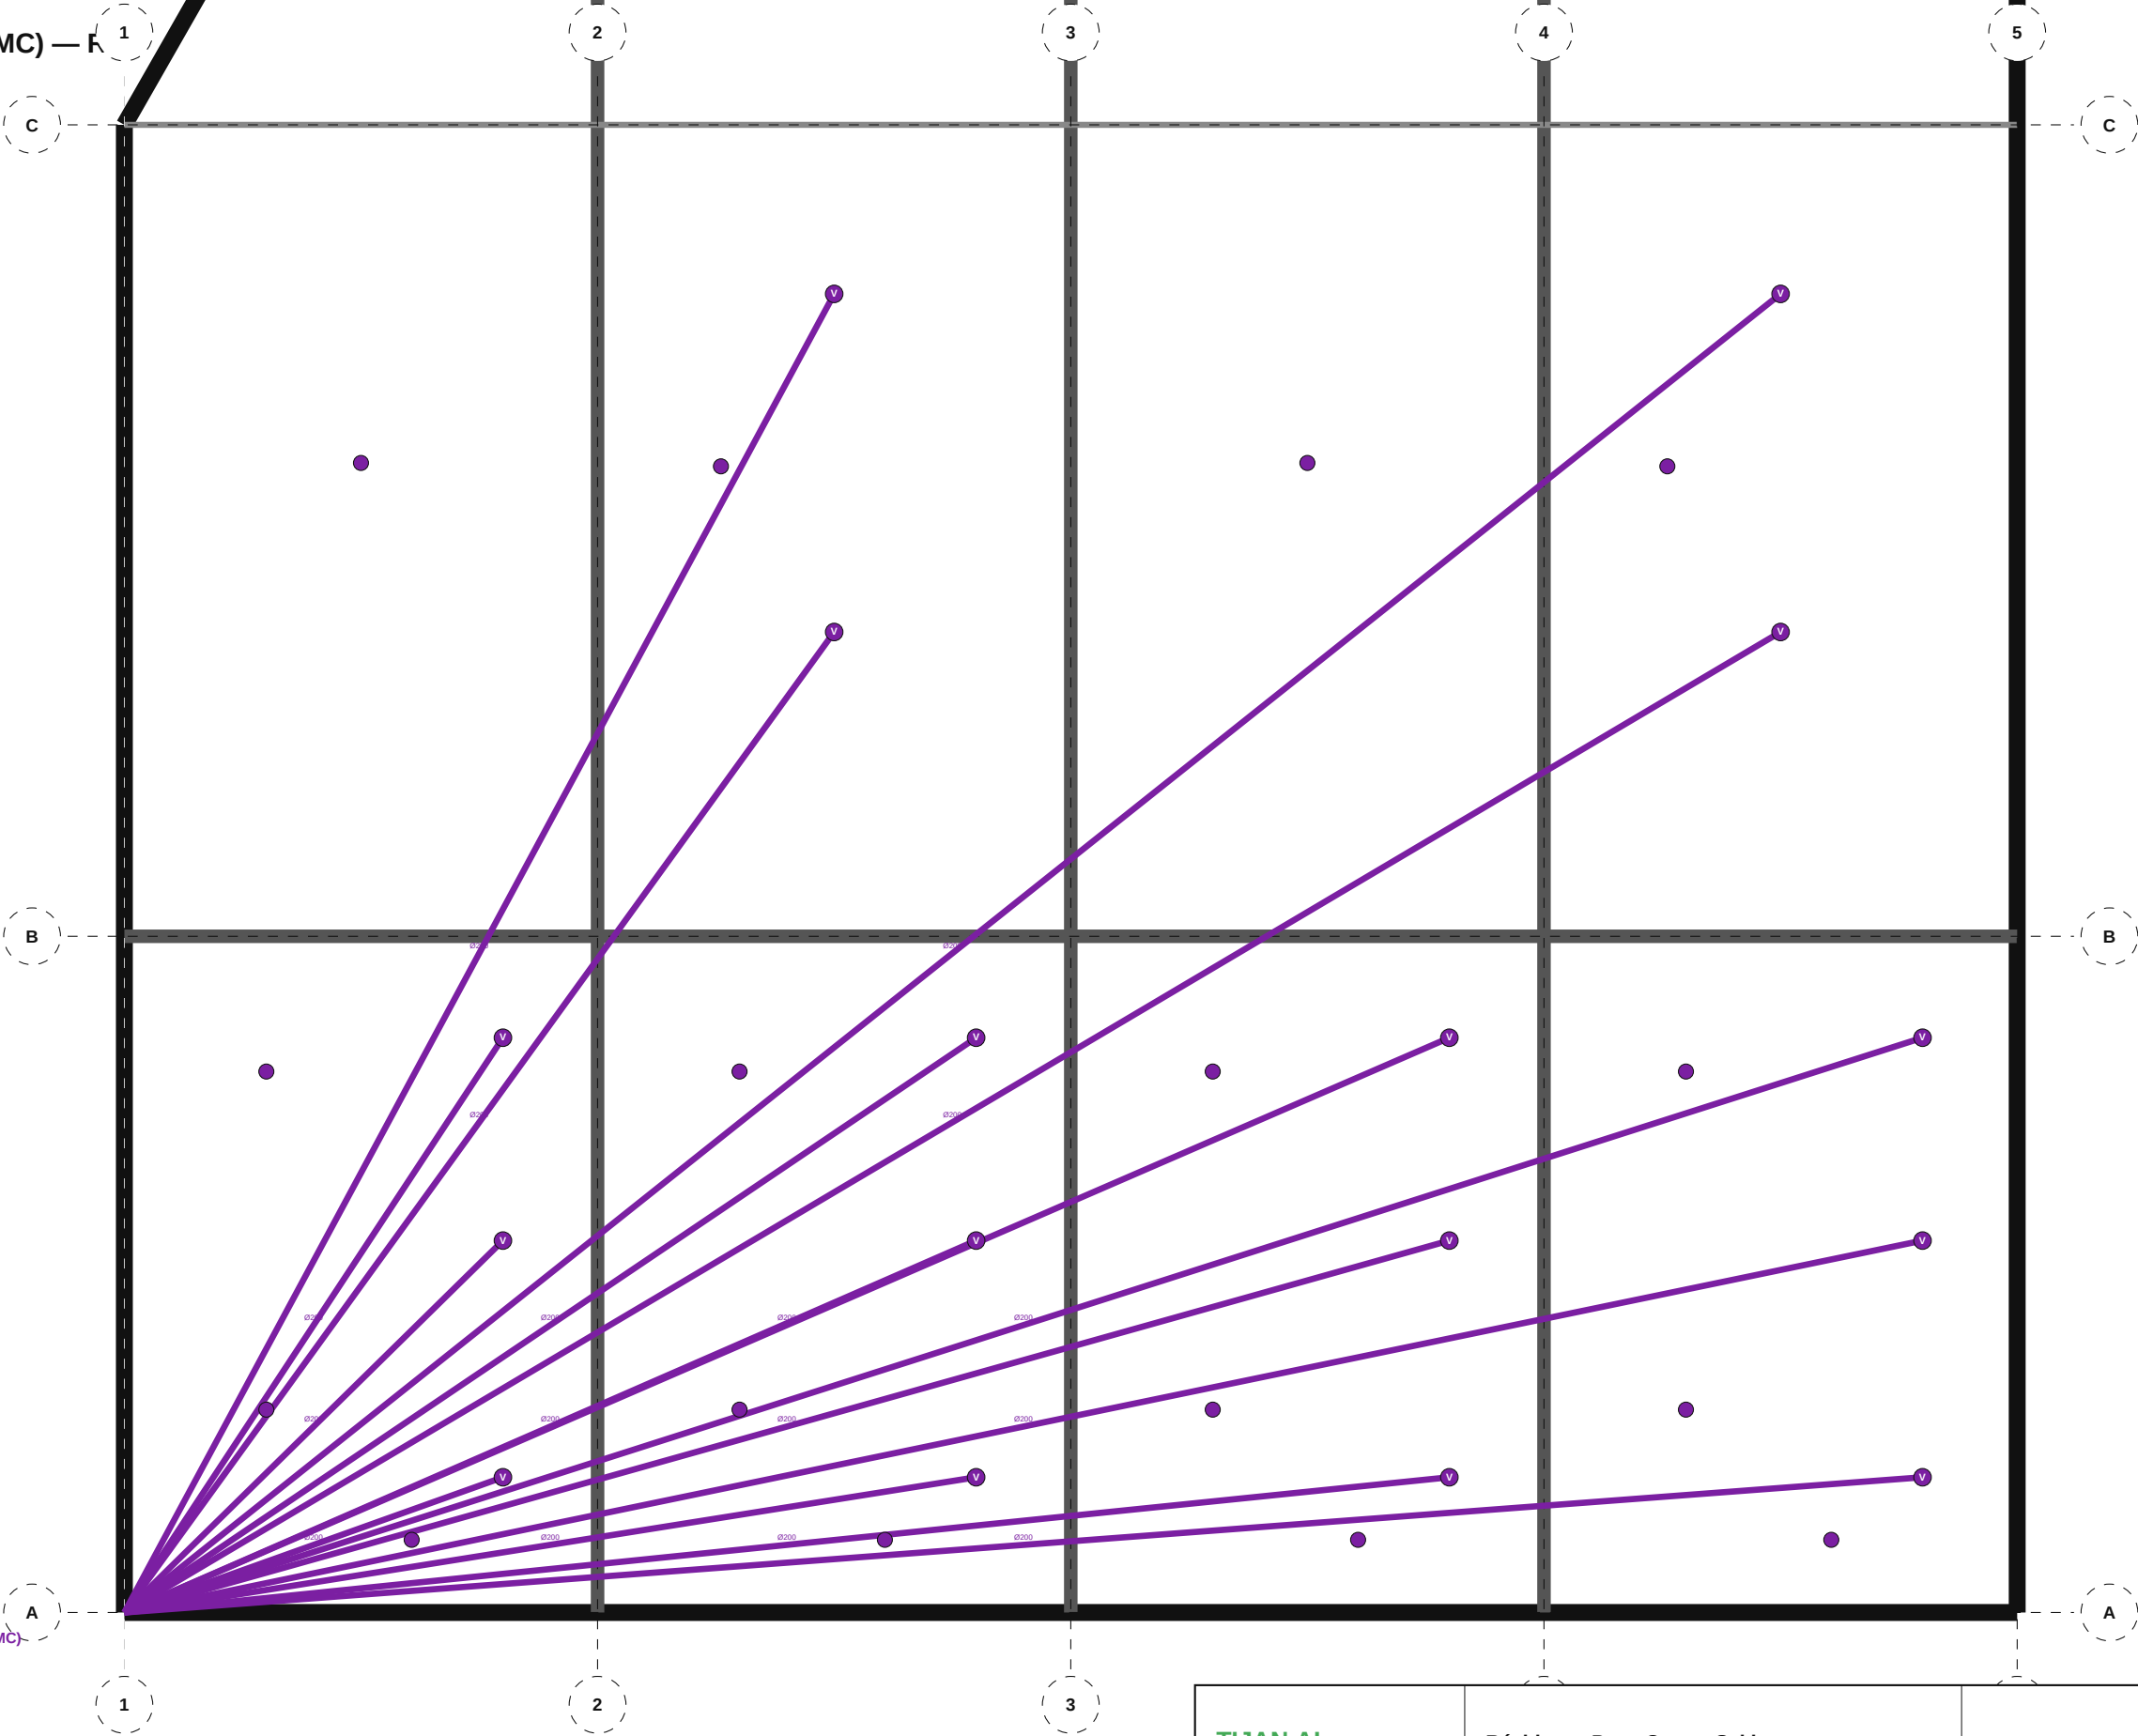

NOMENCLATURE — 413 HVC — Ventilation (VMC)

- Bouche VMC extraction: 16
- Grille soufflage: 10
- Hotte aspirante: 6

TIJAN AI

Bureau d'Études Automatisé

Résidence Papa Oumar Sakho

Dakar, Senegal

Éch: 1/100

Pl. 57/133

413 HVC — Ventilation (VMC) — R+1


Date: 06/05/2026

Réf: 1711

BIM vHVC-057

Phase: APD

413 HVC — Ventilation (VMC) — R+2

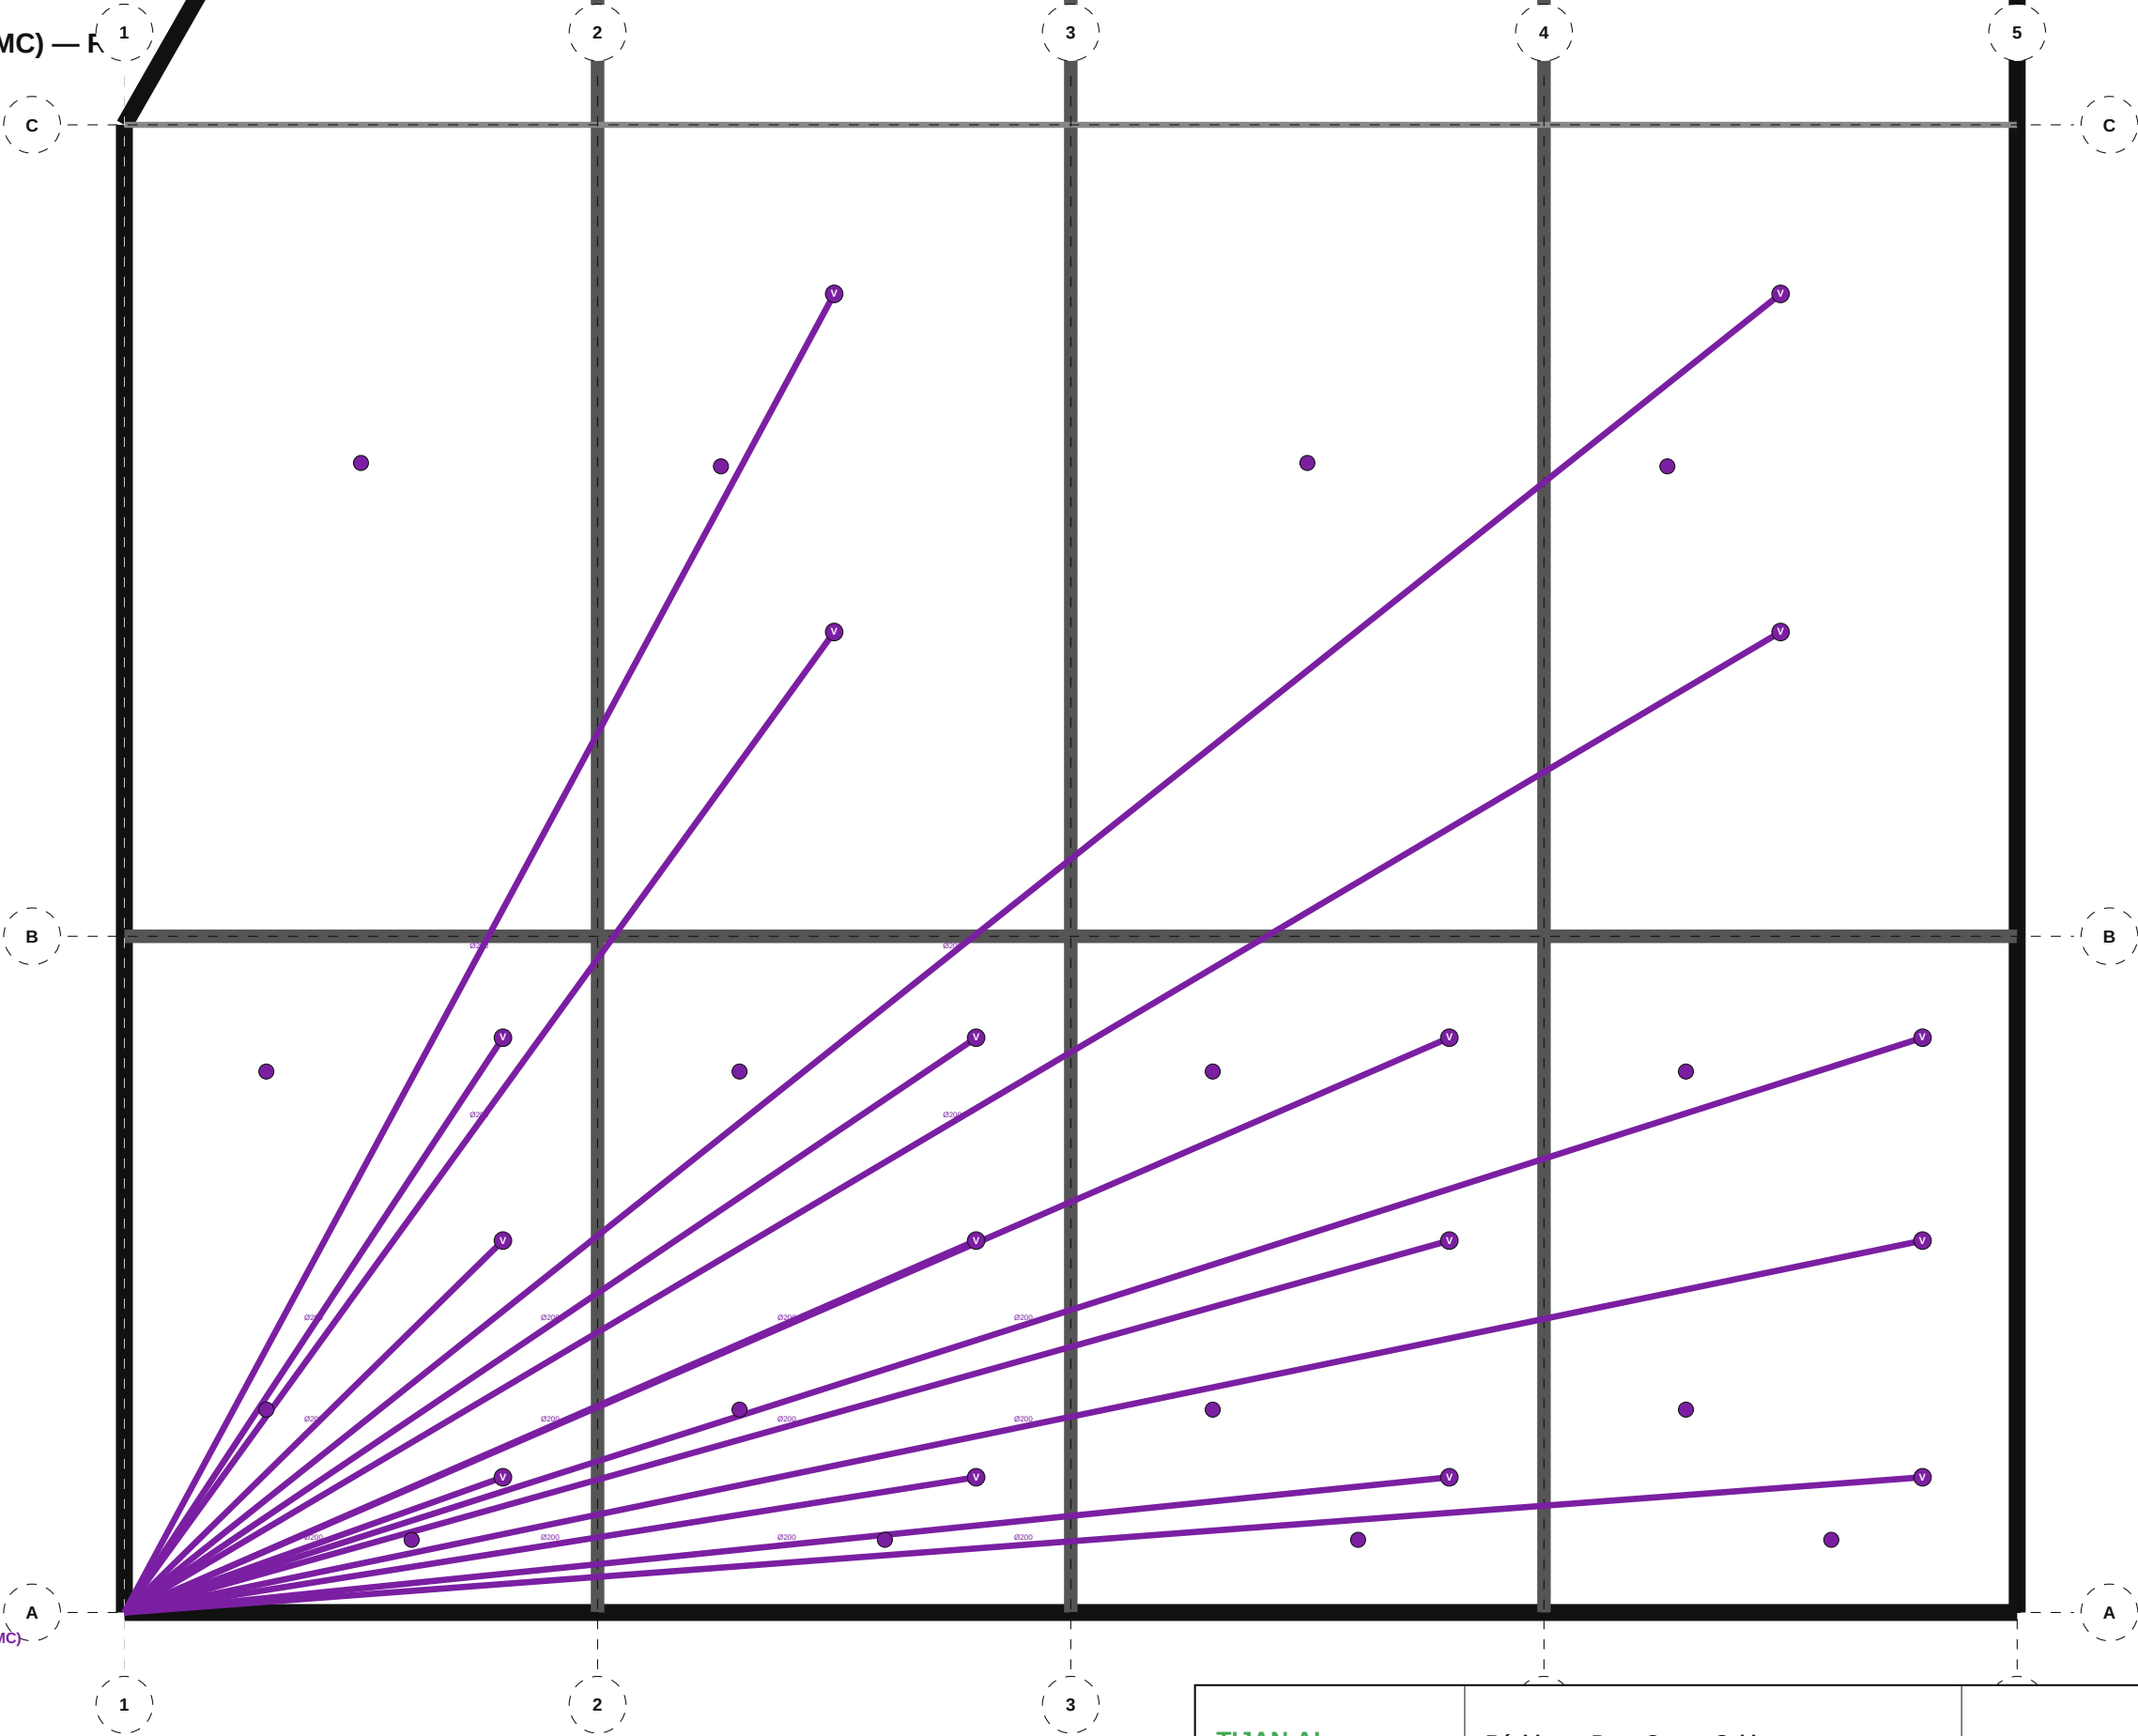


NOMENCLATURE — 413 HVC — Ventilation (VMC)

- Bouche VMC extraction: 16
- Grille soufflage: 10
- Hotte aspirante: 6

TIJAN AI Bureau d'Études Automatisé	Résidence Papa Oumar Sakho Dakar, Senegal	Éch: 1/100 Pl. 58/133
	413 HVC — Ventilation (VMC) — R+2	
Date: 06/05/2026	Réf: 1711	BIM vHVC-058 Phase: APD

413 HVC — Ventilation (VMC) — R+3

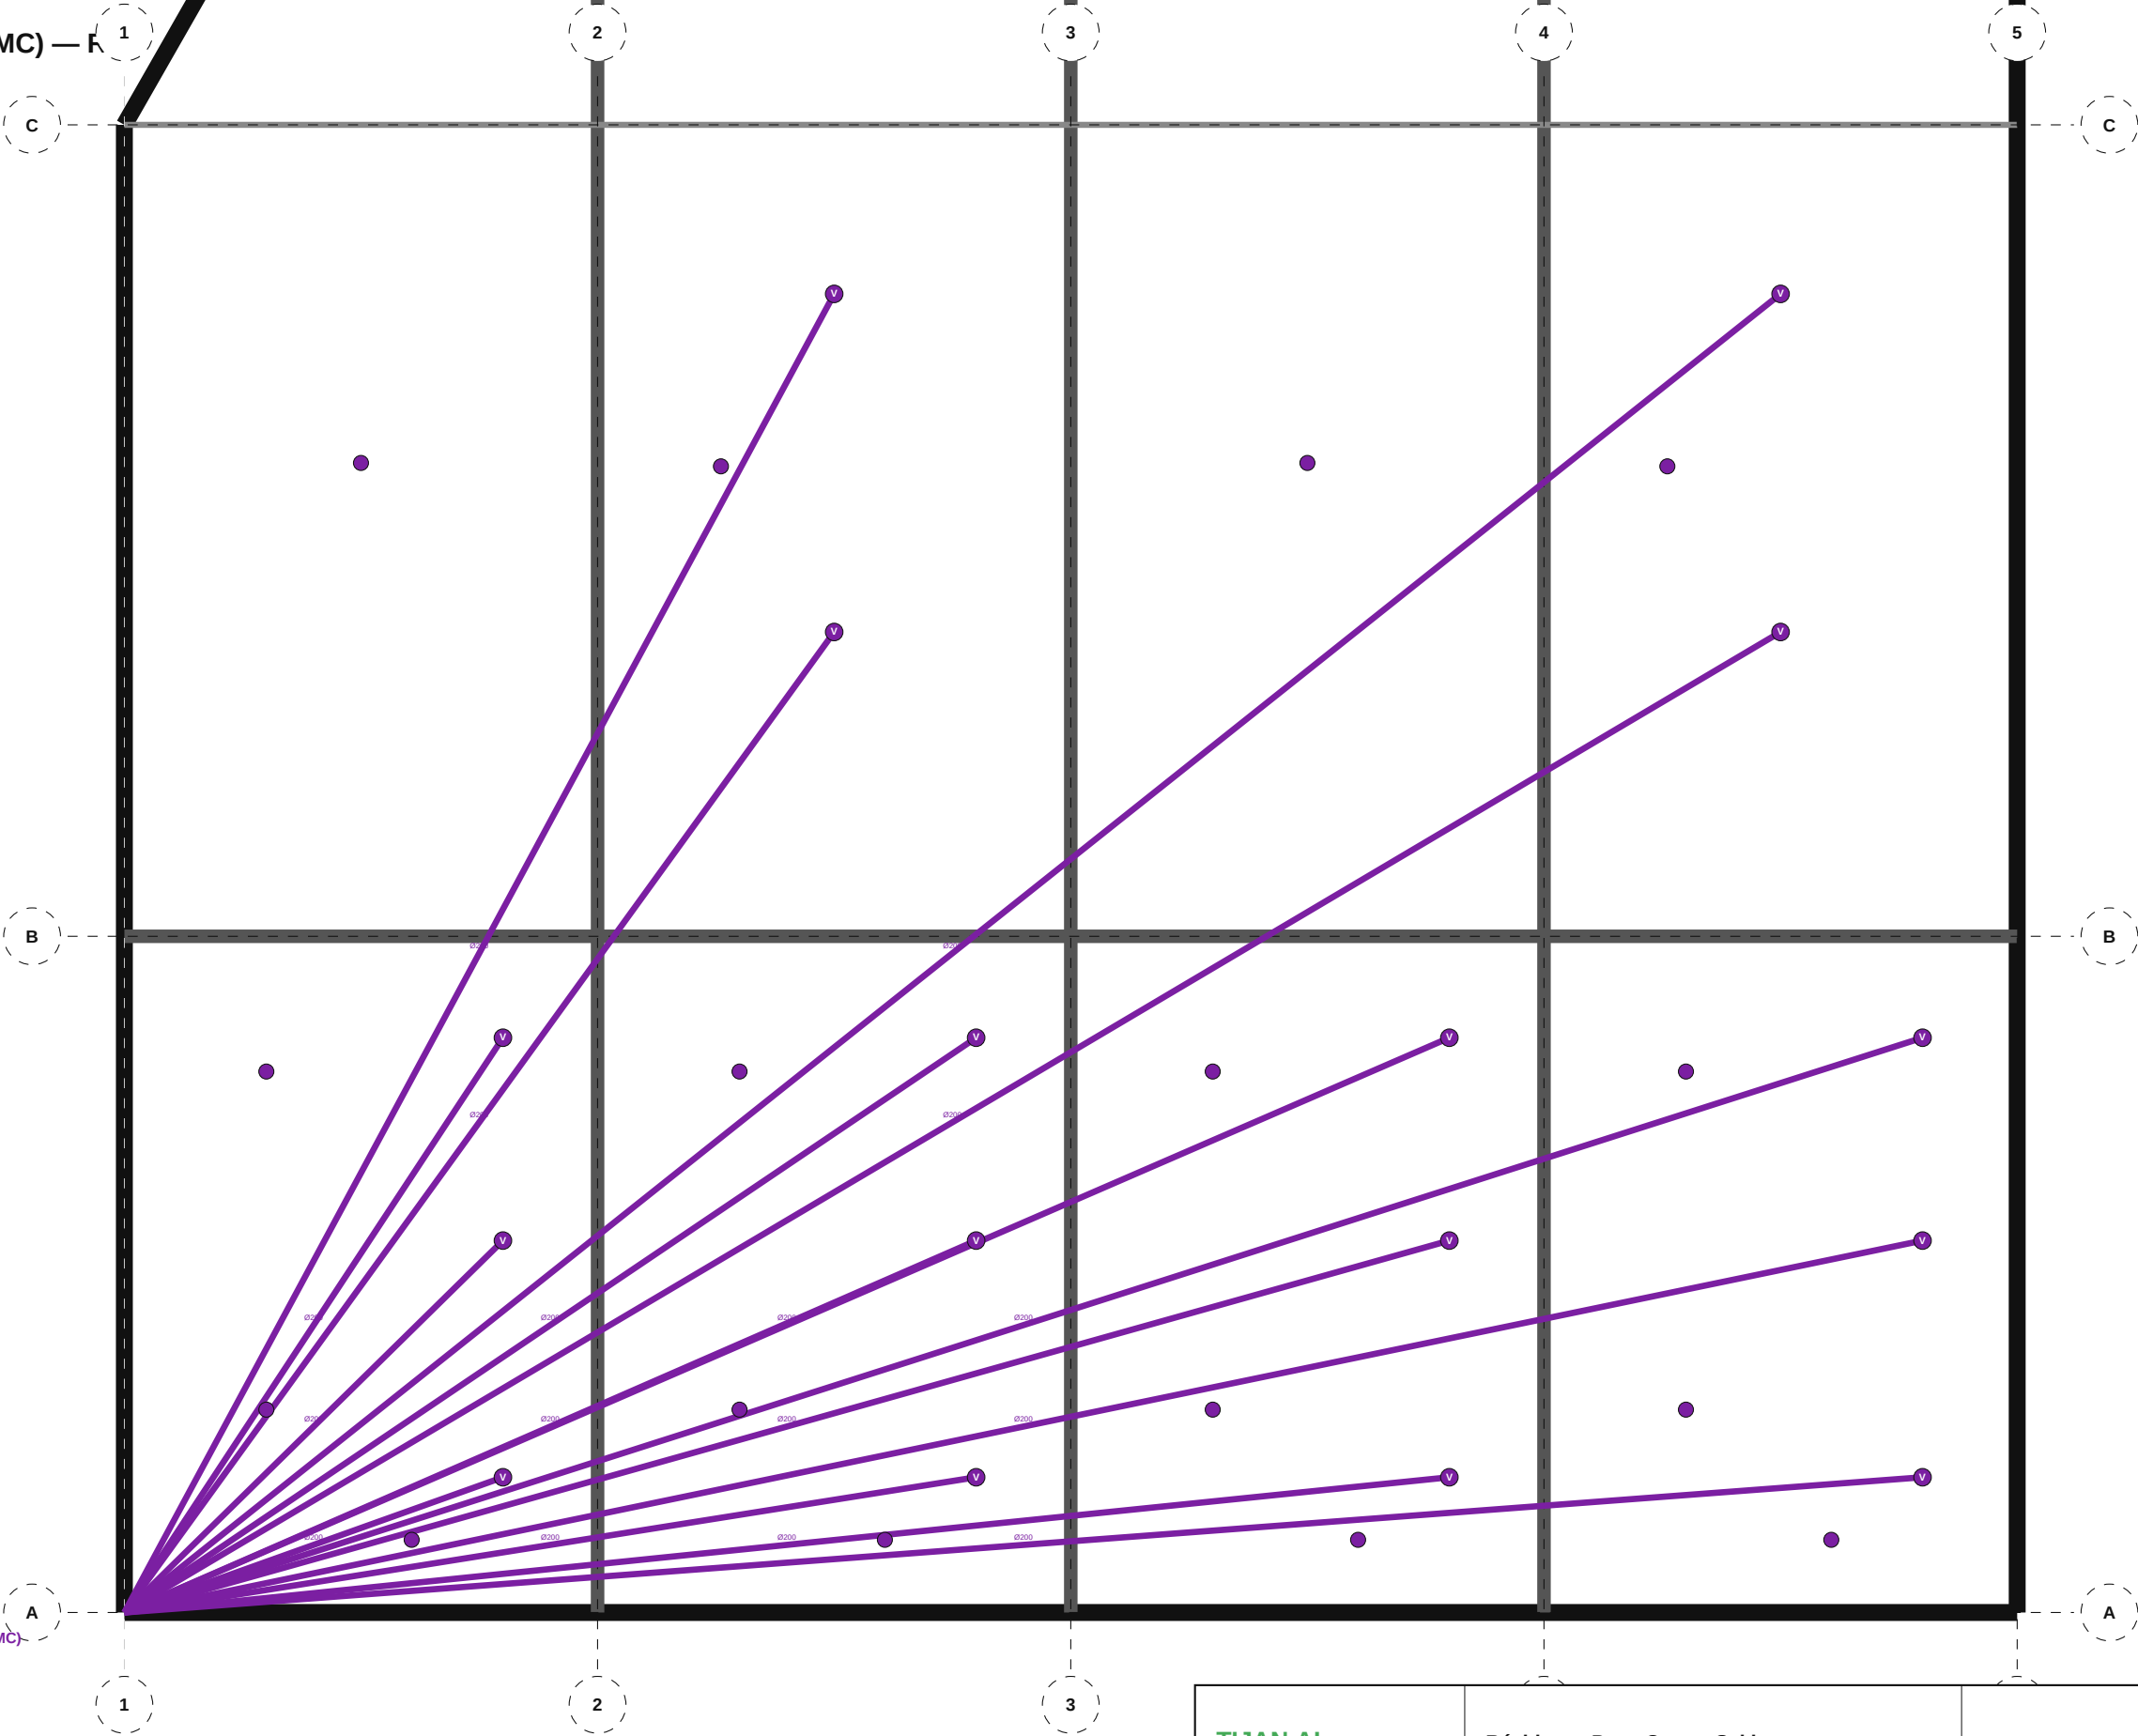

NOMENCLATURE — 413 HVC — Ventilation (VMC)

- Bouche VMC extraction: 16
- Grille soufflage: 10
- Hotte aspirante: 6

TIJAN AI

Bureau d'Études Automatisé

Résidence Papa Oumar Sakho

Dakar, Senegal

Éch: 1/100

Pl. 59/133

413 HVC — Ventilation (VMC) — R+3


Date: 06/05/2026

Réf: 1711

BIM vHVC-059

Phase: APD

413 HVC — Ventilation (VMC) — R+4

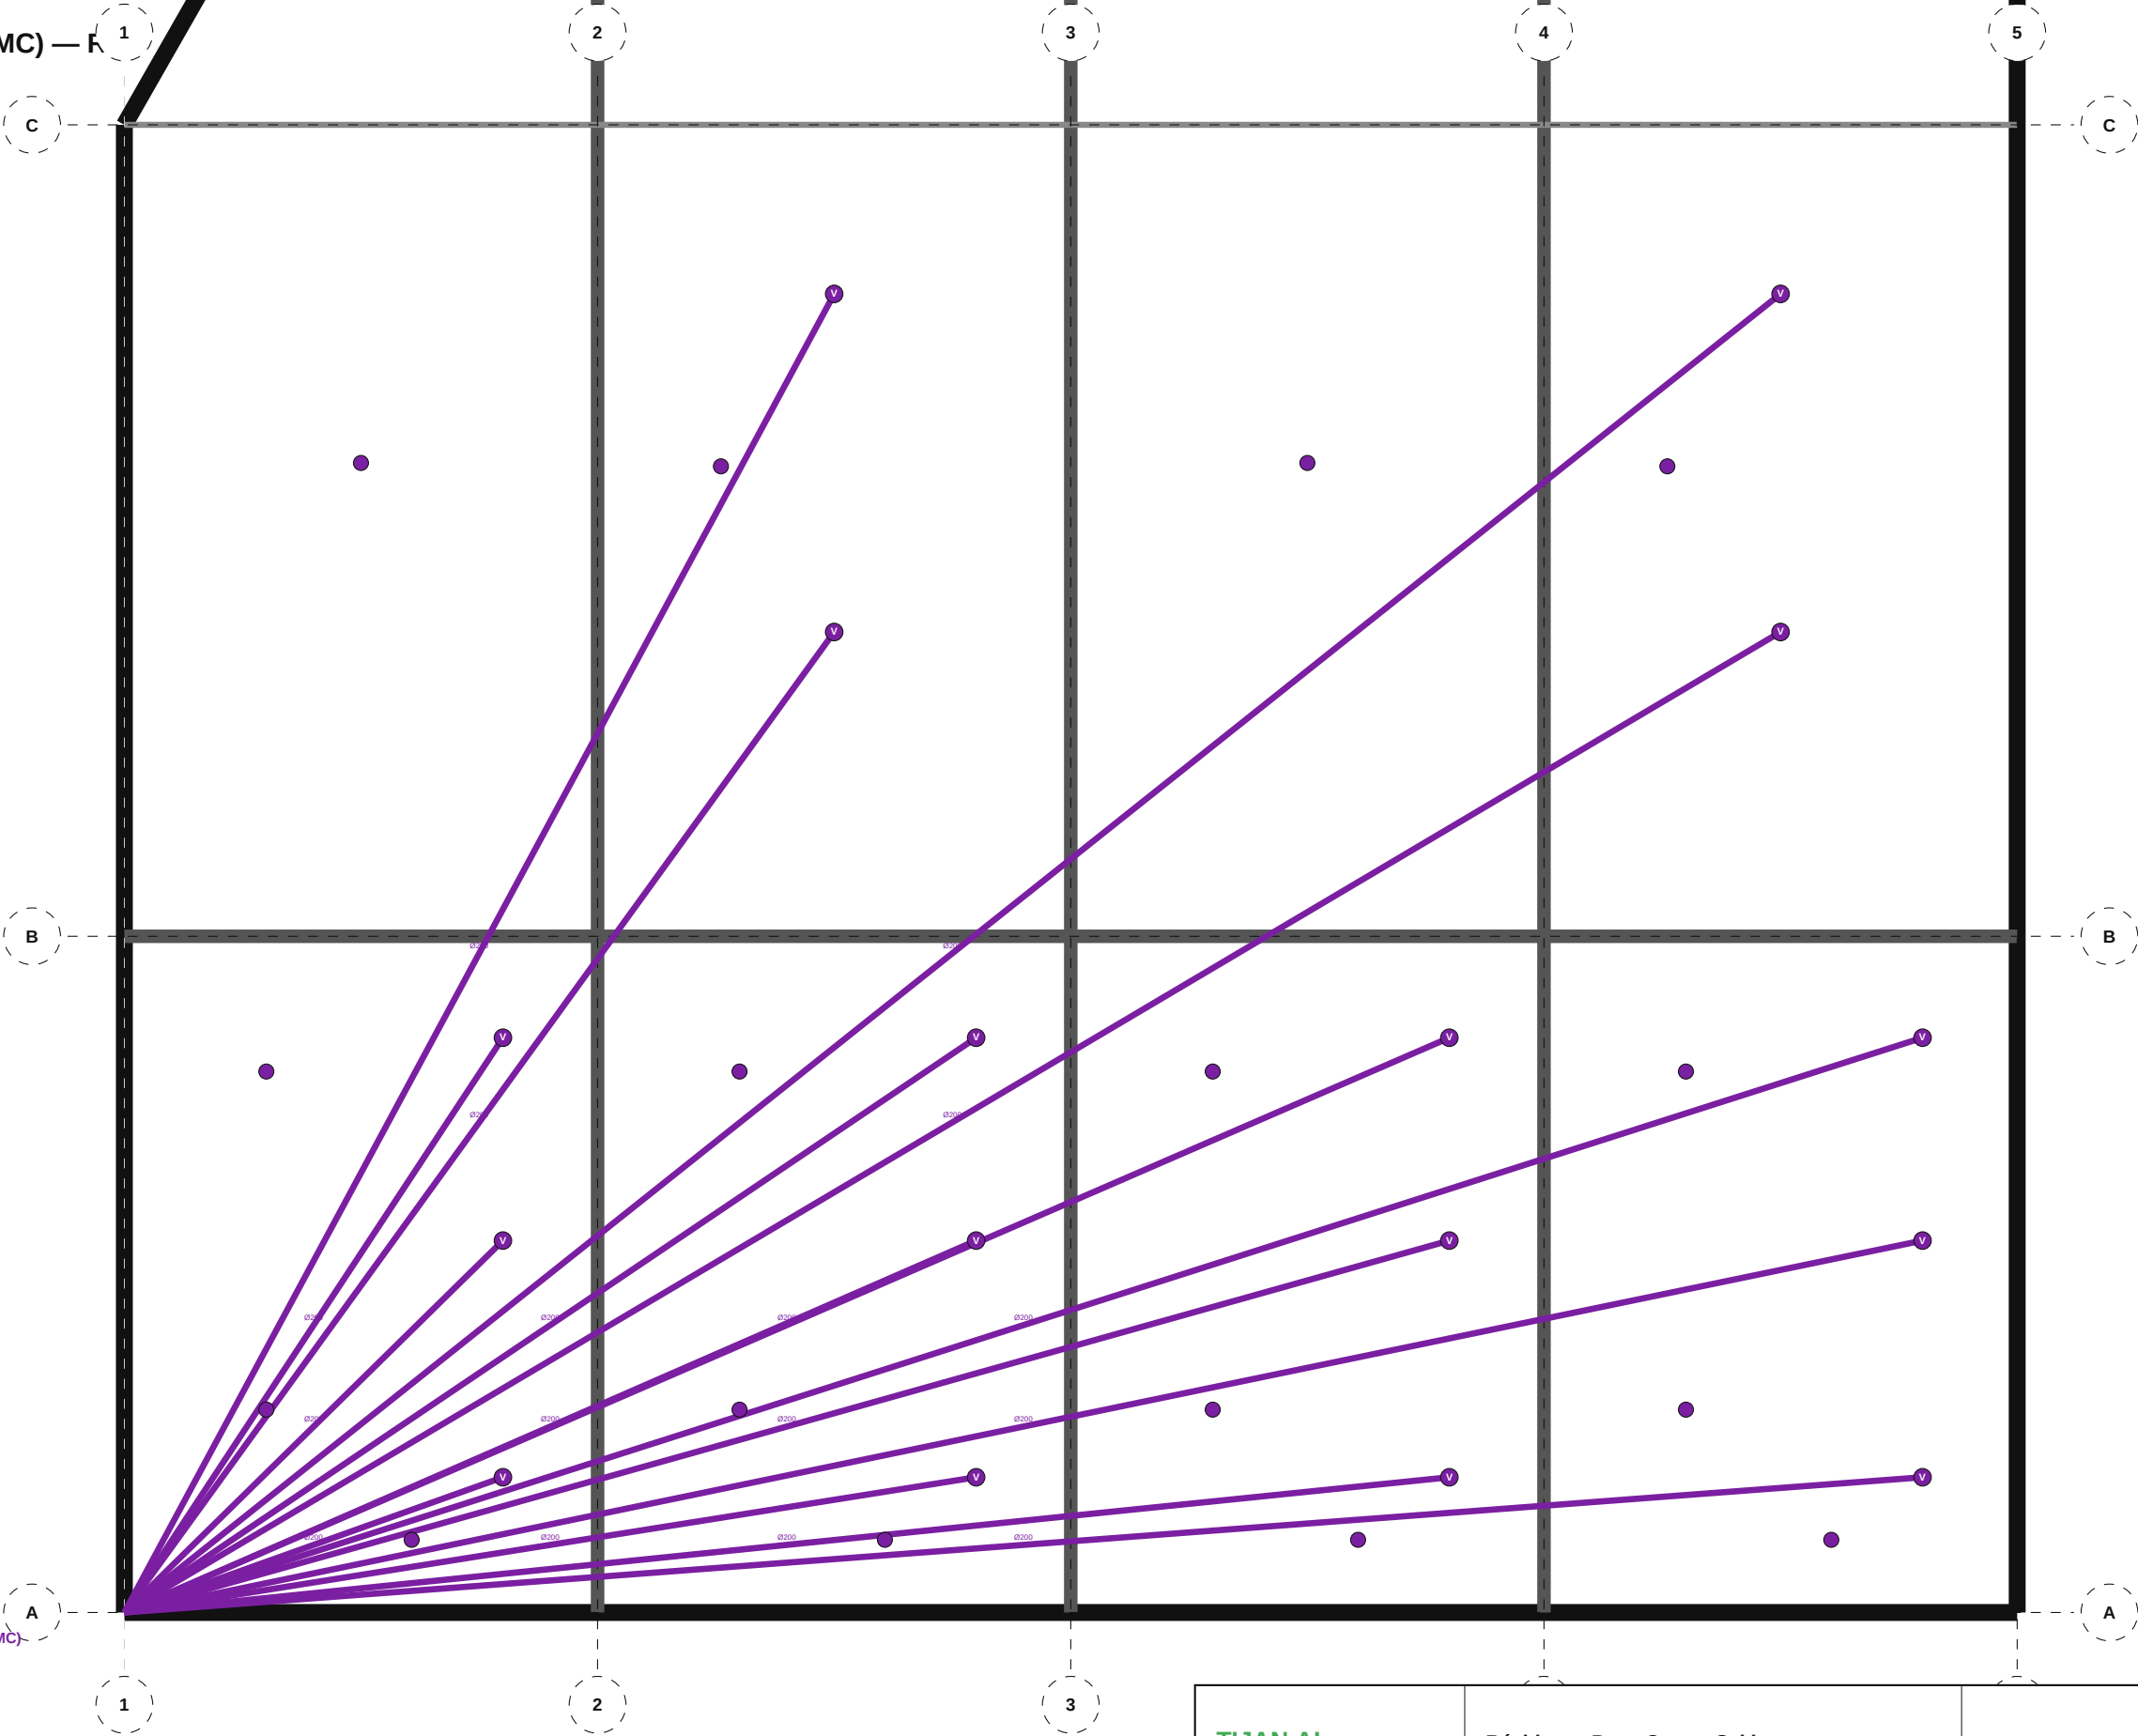

NOMENCLATURE — 413 HVC — Ventilation (VMC)

- Bouche VMC extraction: 16
- Grille soufflage: 10
- Hotte aspirante: 6

TIJAN AI

Bureau d'Études Automatisé

Résidence Papa Oumar Sakho

Dakar, Senegal

Éch: 1/100

Pl. 60/133

413 HVC — Ventilation (VMC) — R+4


Date: 06/05/2026

Réf: 1711

BIM vHVC-060

Phase: APD

413 HVC — Ventilation (VMC) — R+5

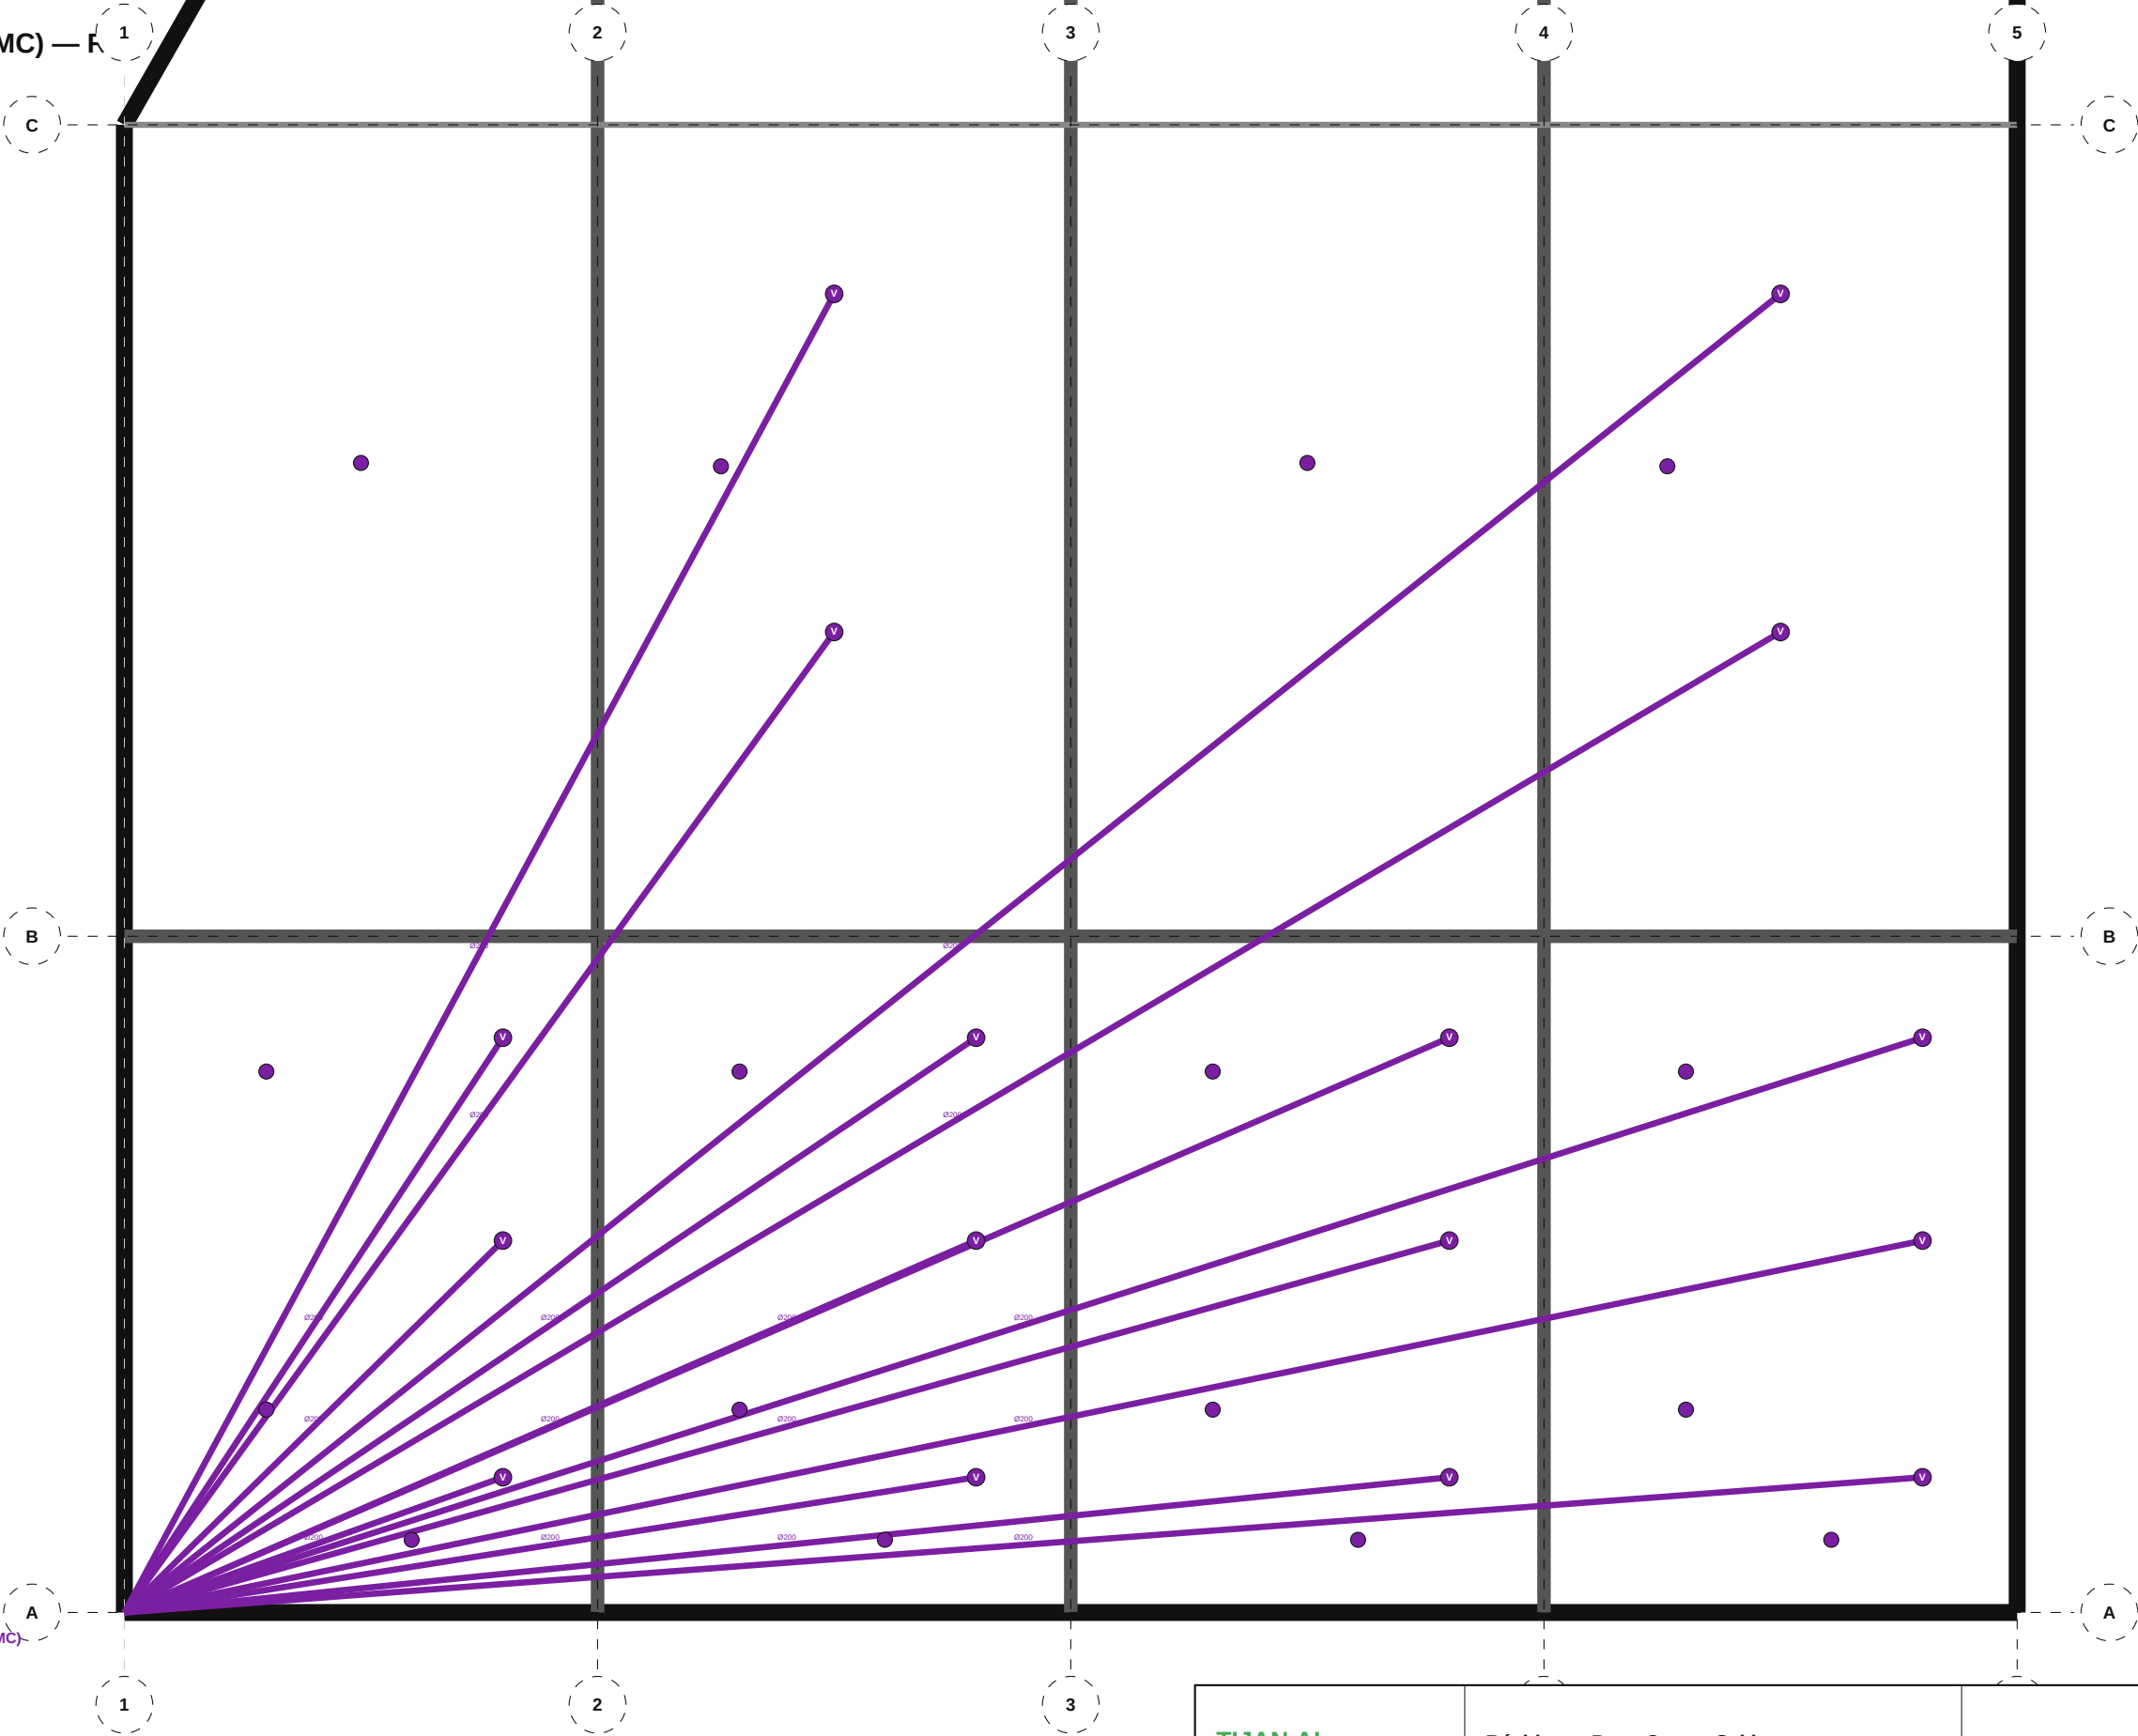


NOMENCLATURE — 413 HVC — Ventilation (VMC)

- Bouche VMC extraction: 16
- Grille soufflage: 10
- Hotte aspirante: 6

TIJAN AI Bureau d'Études Automatisé	Résidence Papa Oumar Sakho Dakar, Senegal	Éch: 1/100 Pl. 61/133
	413 HVC — Ventilation (VMC) — R+5	
Date: 06/05/2026	Réf: 1711	BIM vHVC-061 Phase: APD

413 HVC — Ventilation (VMC) — R+6

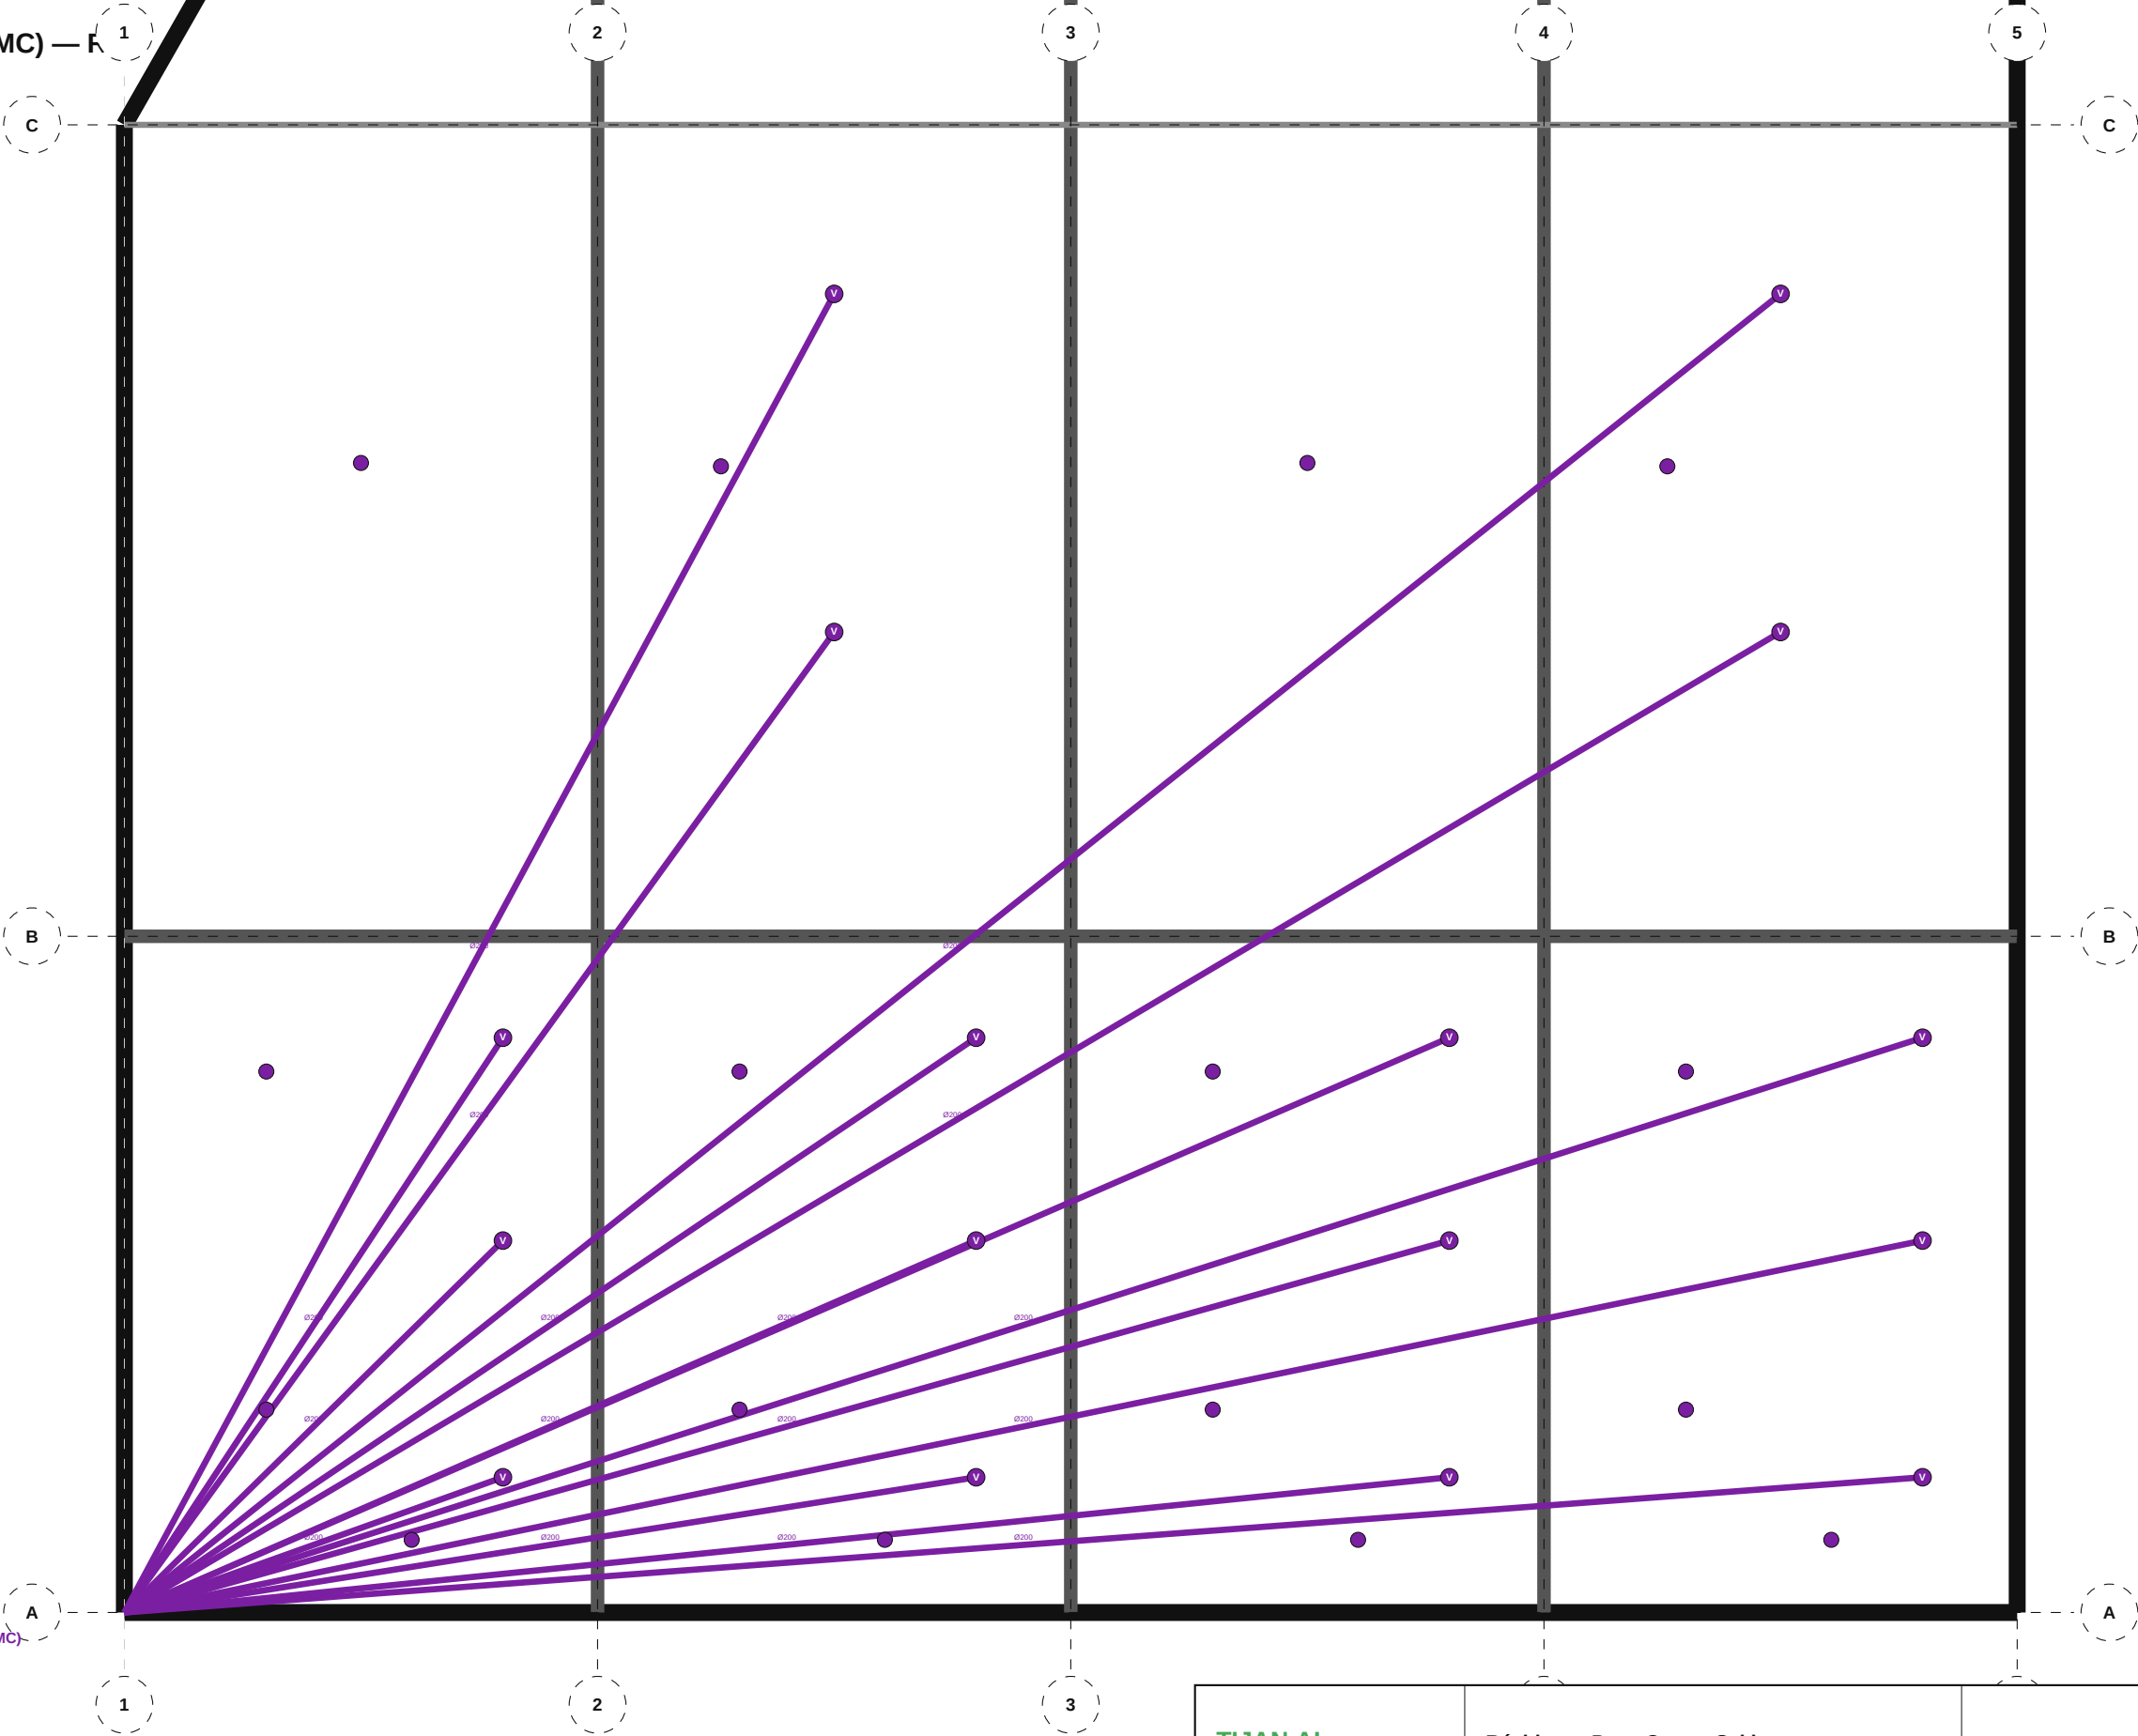

NOMENCLATURE — 413 HVC — Ventilation (VMC)

- Bouche VMC extraction: 16
- Grille soufflage: 10
- Hotte aspirante: 6

TIJAN AI

Bureau d'Études Automatisé

Résidence Papa Oumar Sakho

Dakar, Senegal

Éch: 1/100

Pl. 62/133

413 HVC — Ventilation (VMC) — R+6


Date: 06/05/2026

Réf: 1711

BIM vHVC-062

Phase: APD

413 HVC — Ventilation (VMC) — R+7

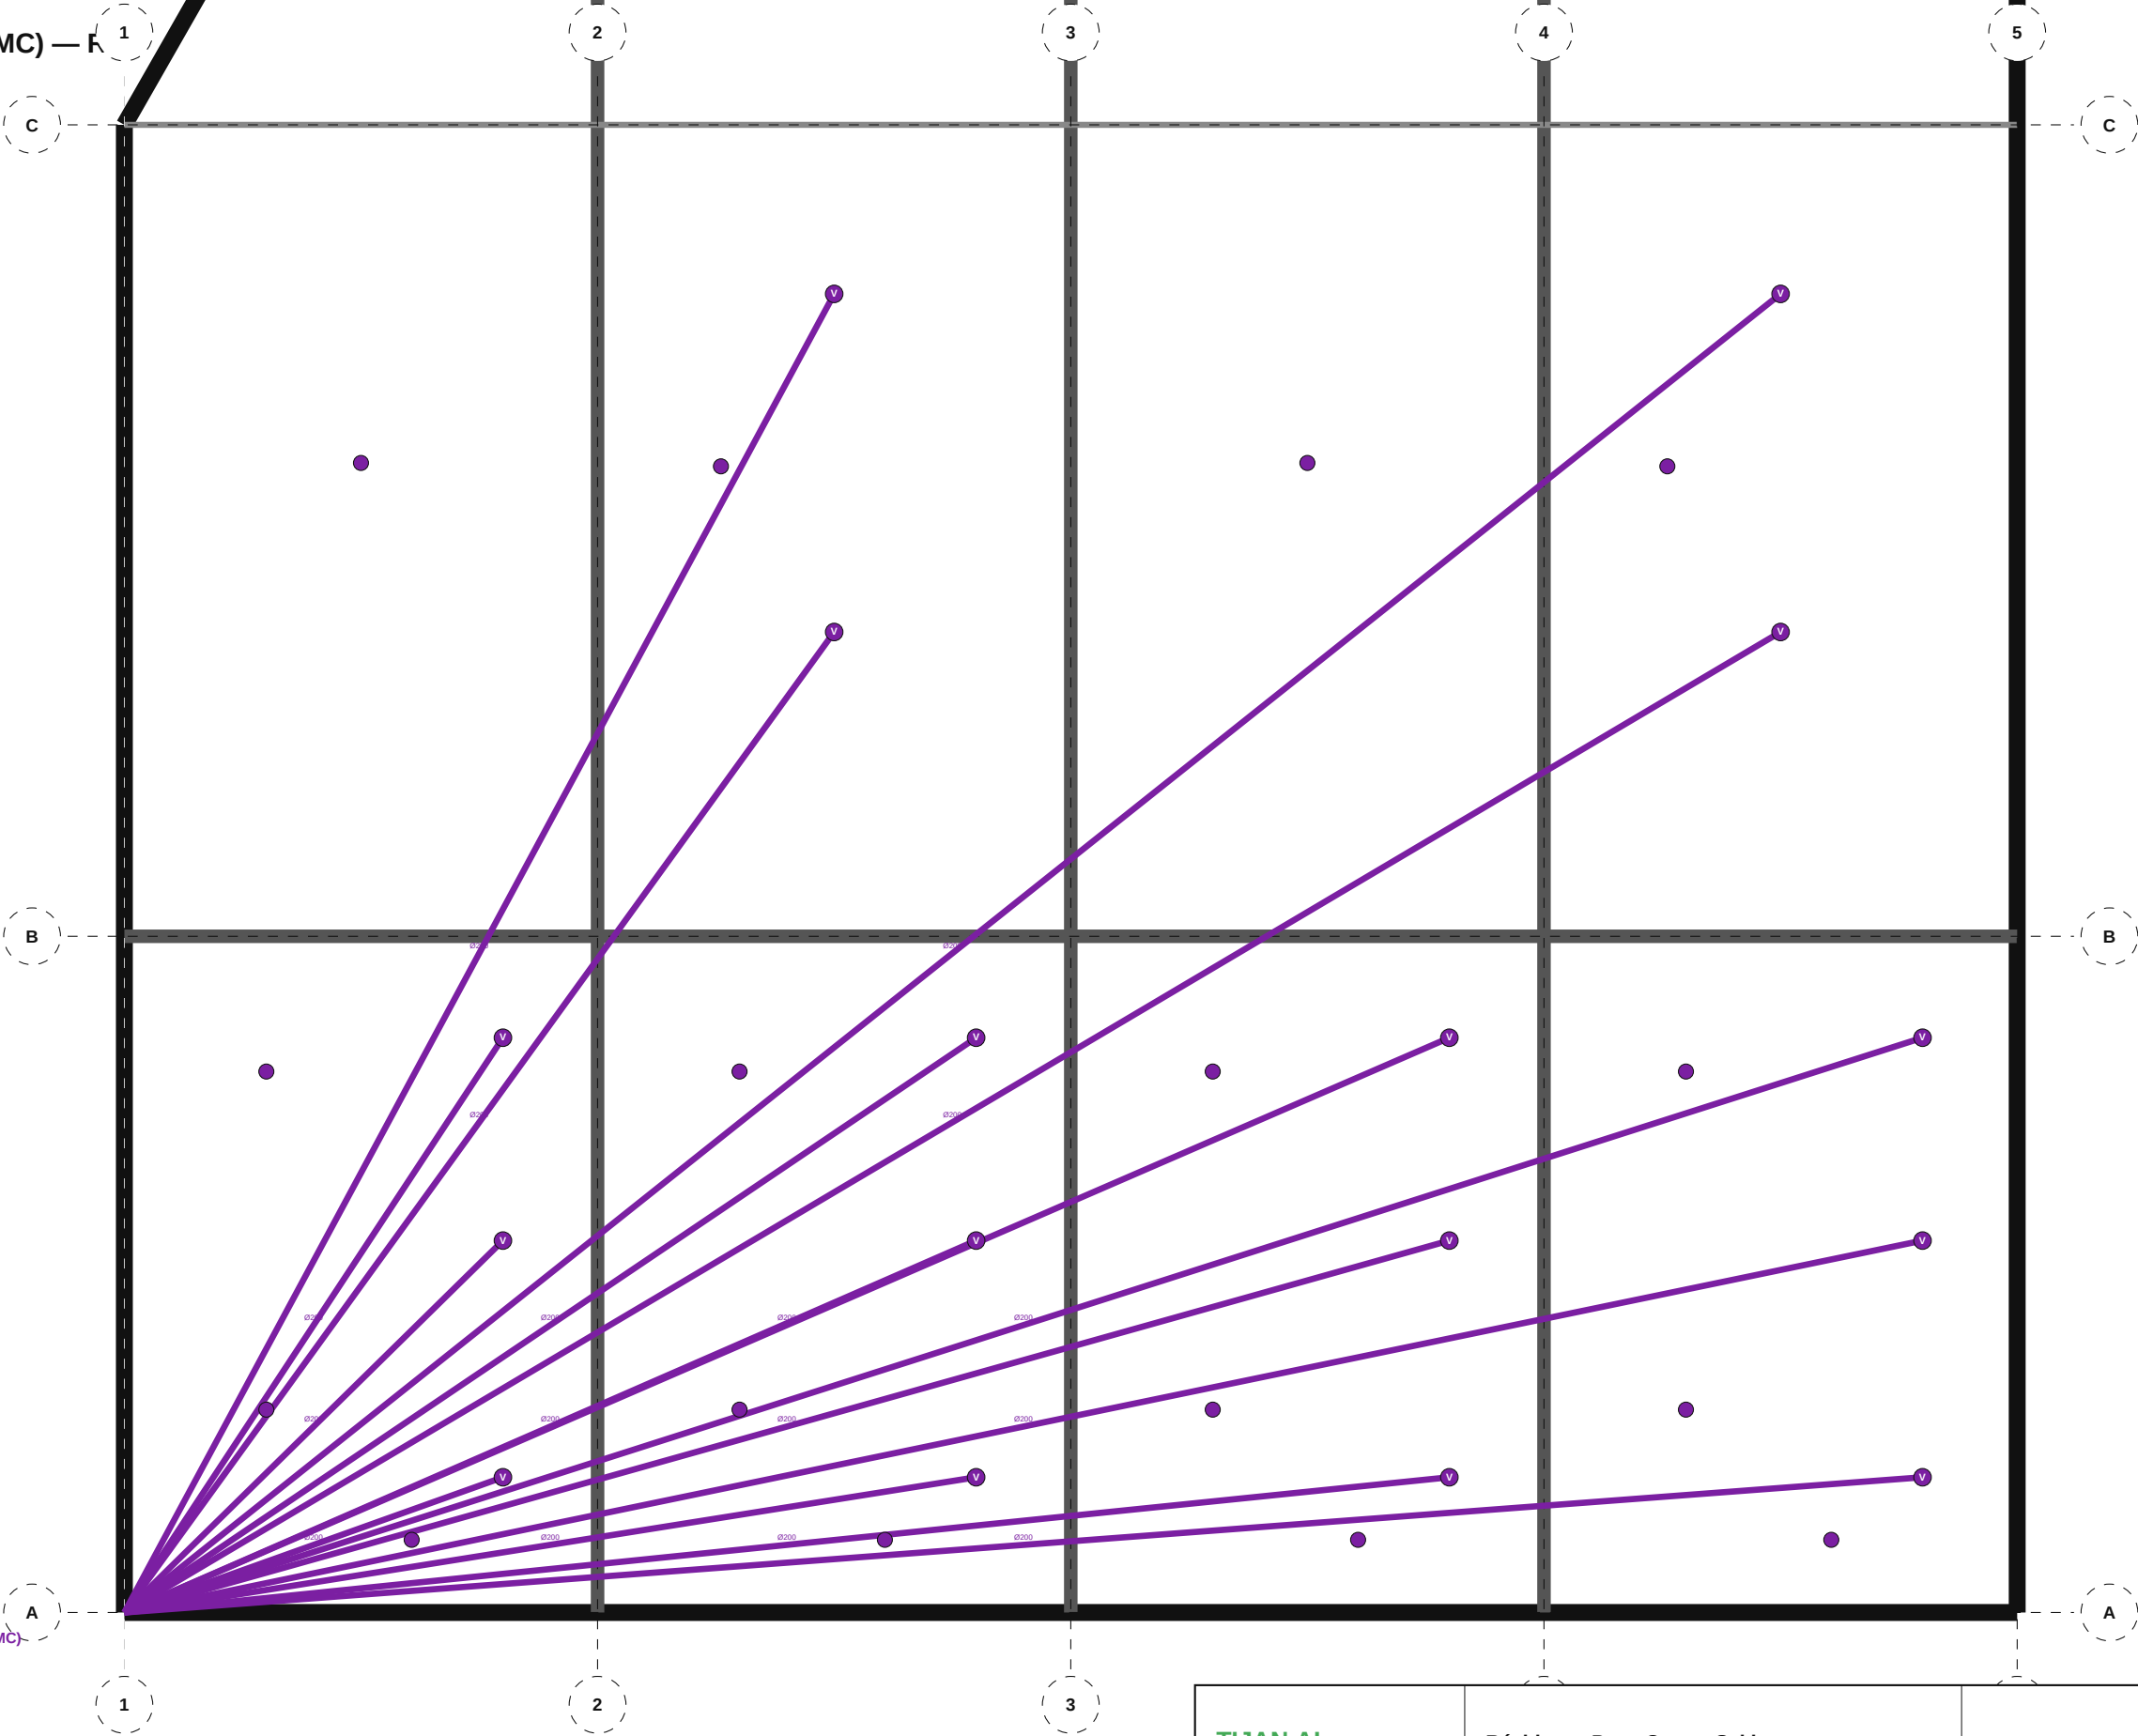


NOMENCLATURE — 413 HVC — Ventilation (VMC)

- Bouche VMC extraction: 16
- Grille soufflage: 10
- Hotte aspirante: 6

TIJAN AI Bureau d'Études Automatisé	Résidence Papa Oumar Sakho Dakar, Senegal	Éch: 1/100 Pl. 63/133
	413 HVC — Ventilation (VMC) — R+7	
Date: 06/05/2026	Réf: 1711	BIM vHVC-063 Phase: APD

413 HVC — Ventilation (VMC) — R+8 Terrasse

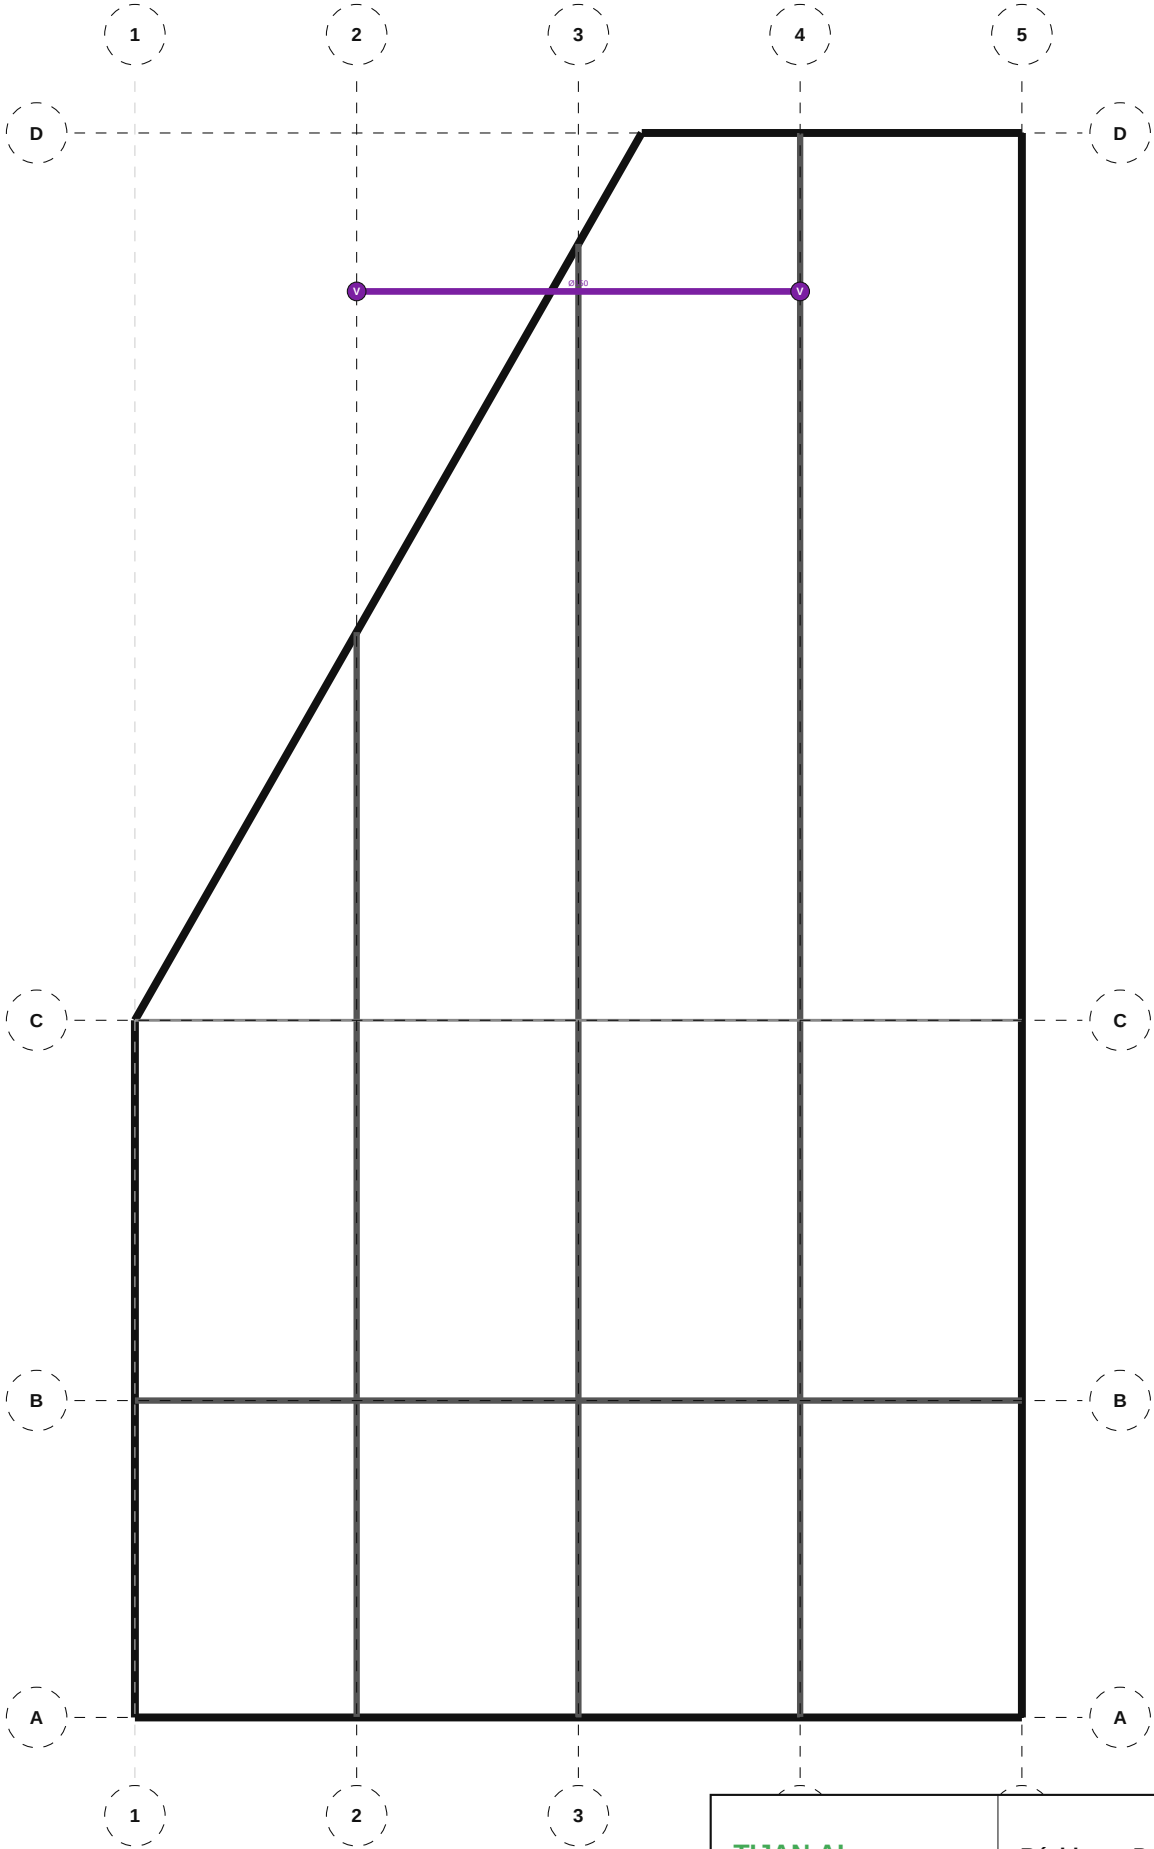

NOMENCLATURE — 413 HVC — Ventilation (VMC)

• Bouche VMC: 2

TIJAN AI Bureau d'Études Automatisé	Résidence Papa Oumar Sakho Dakar, Senegal	Éch: 1/100 Pl. 64/133
	413 HVC — Ventilation (VMC) — R+8 Terrasse	
Date: 06/05/2026	Réf: 1711	BIM vHVC-064 Phase: APD

400 FIF — Extinction (SPK) — RDC

12345

B

B

A


A

NOMENCLATURE — 400 FIF — Extinction (SPK)

• Sprinkler: 2

12345


TIJAN AI Bureau d'Études Automatisé	Résidence Papa Oumar Sakho Dakar, Senegal	Éch: 1/100 Pl. 65/133
	400 FIF — Extinction (SPK) — RDC	
Date: 06/05/2026	Réf: 1711	BIM vFIF-065 Phase: APD

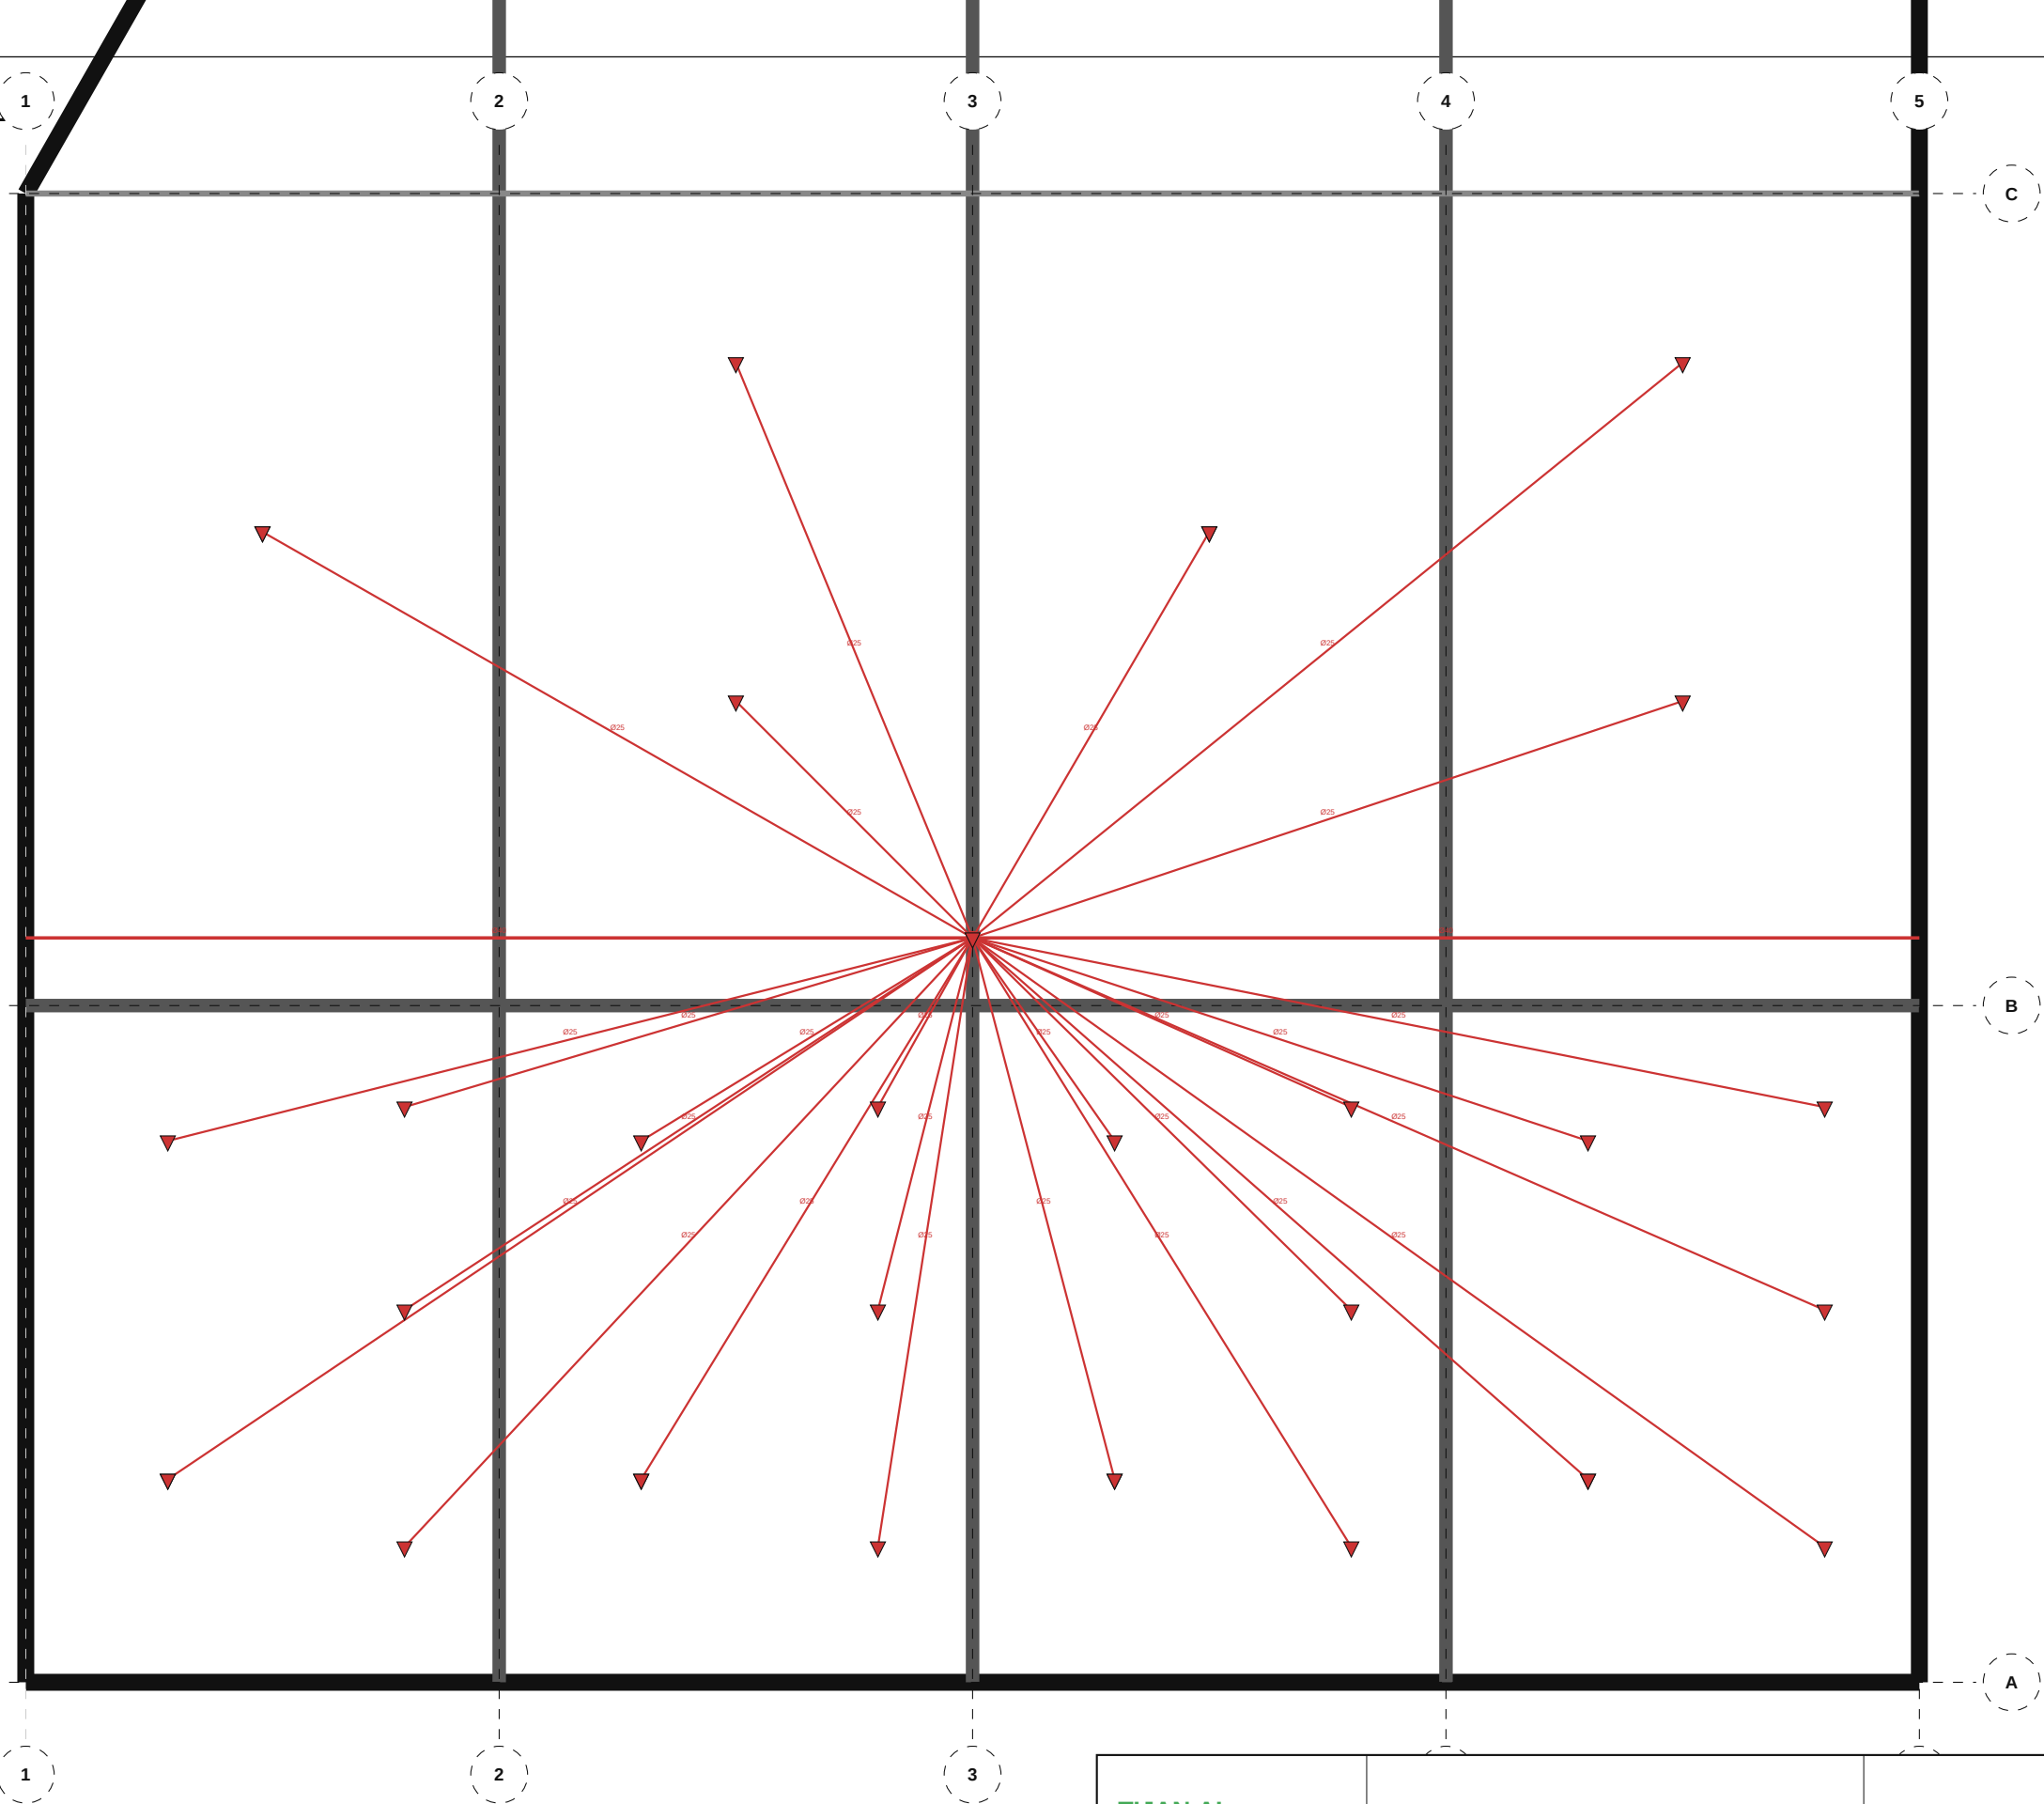

NOMENCLATURE — 400 FIF — Extinction (SPK)

• Sprinkler: 33

TIJAN AI Bureau d'Études Automatisé	Résidence Papa Oumar Sakho Dakar, Senegal	Éch: 1/100 Pl. 66/133
	400 FIF — Extinction (SPK) — R+1	
Date: 06/05/2026	Réf: 1711	BIM vFIF-066 Phase: APD

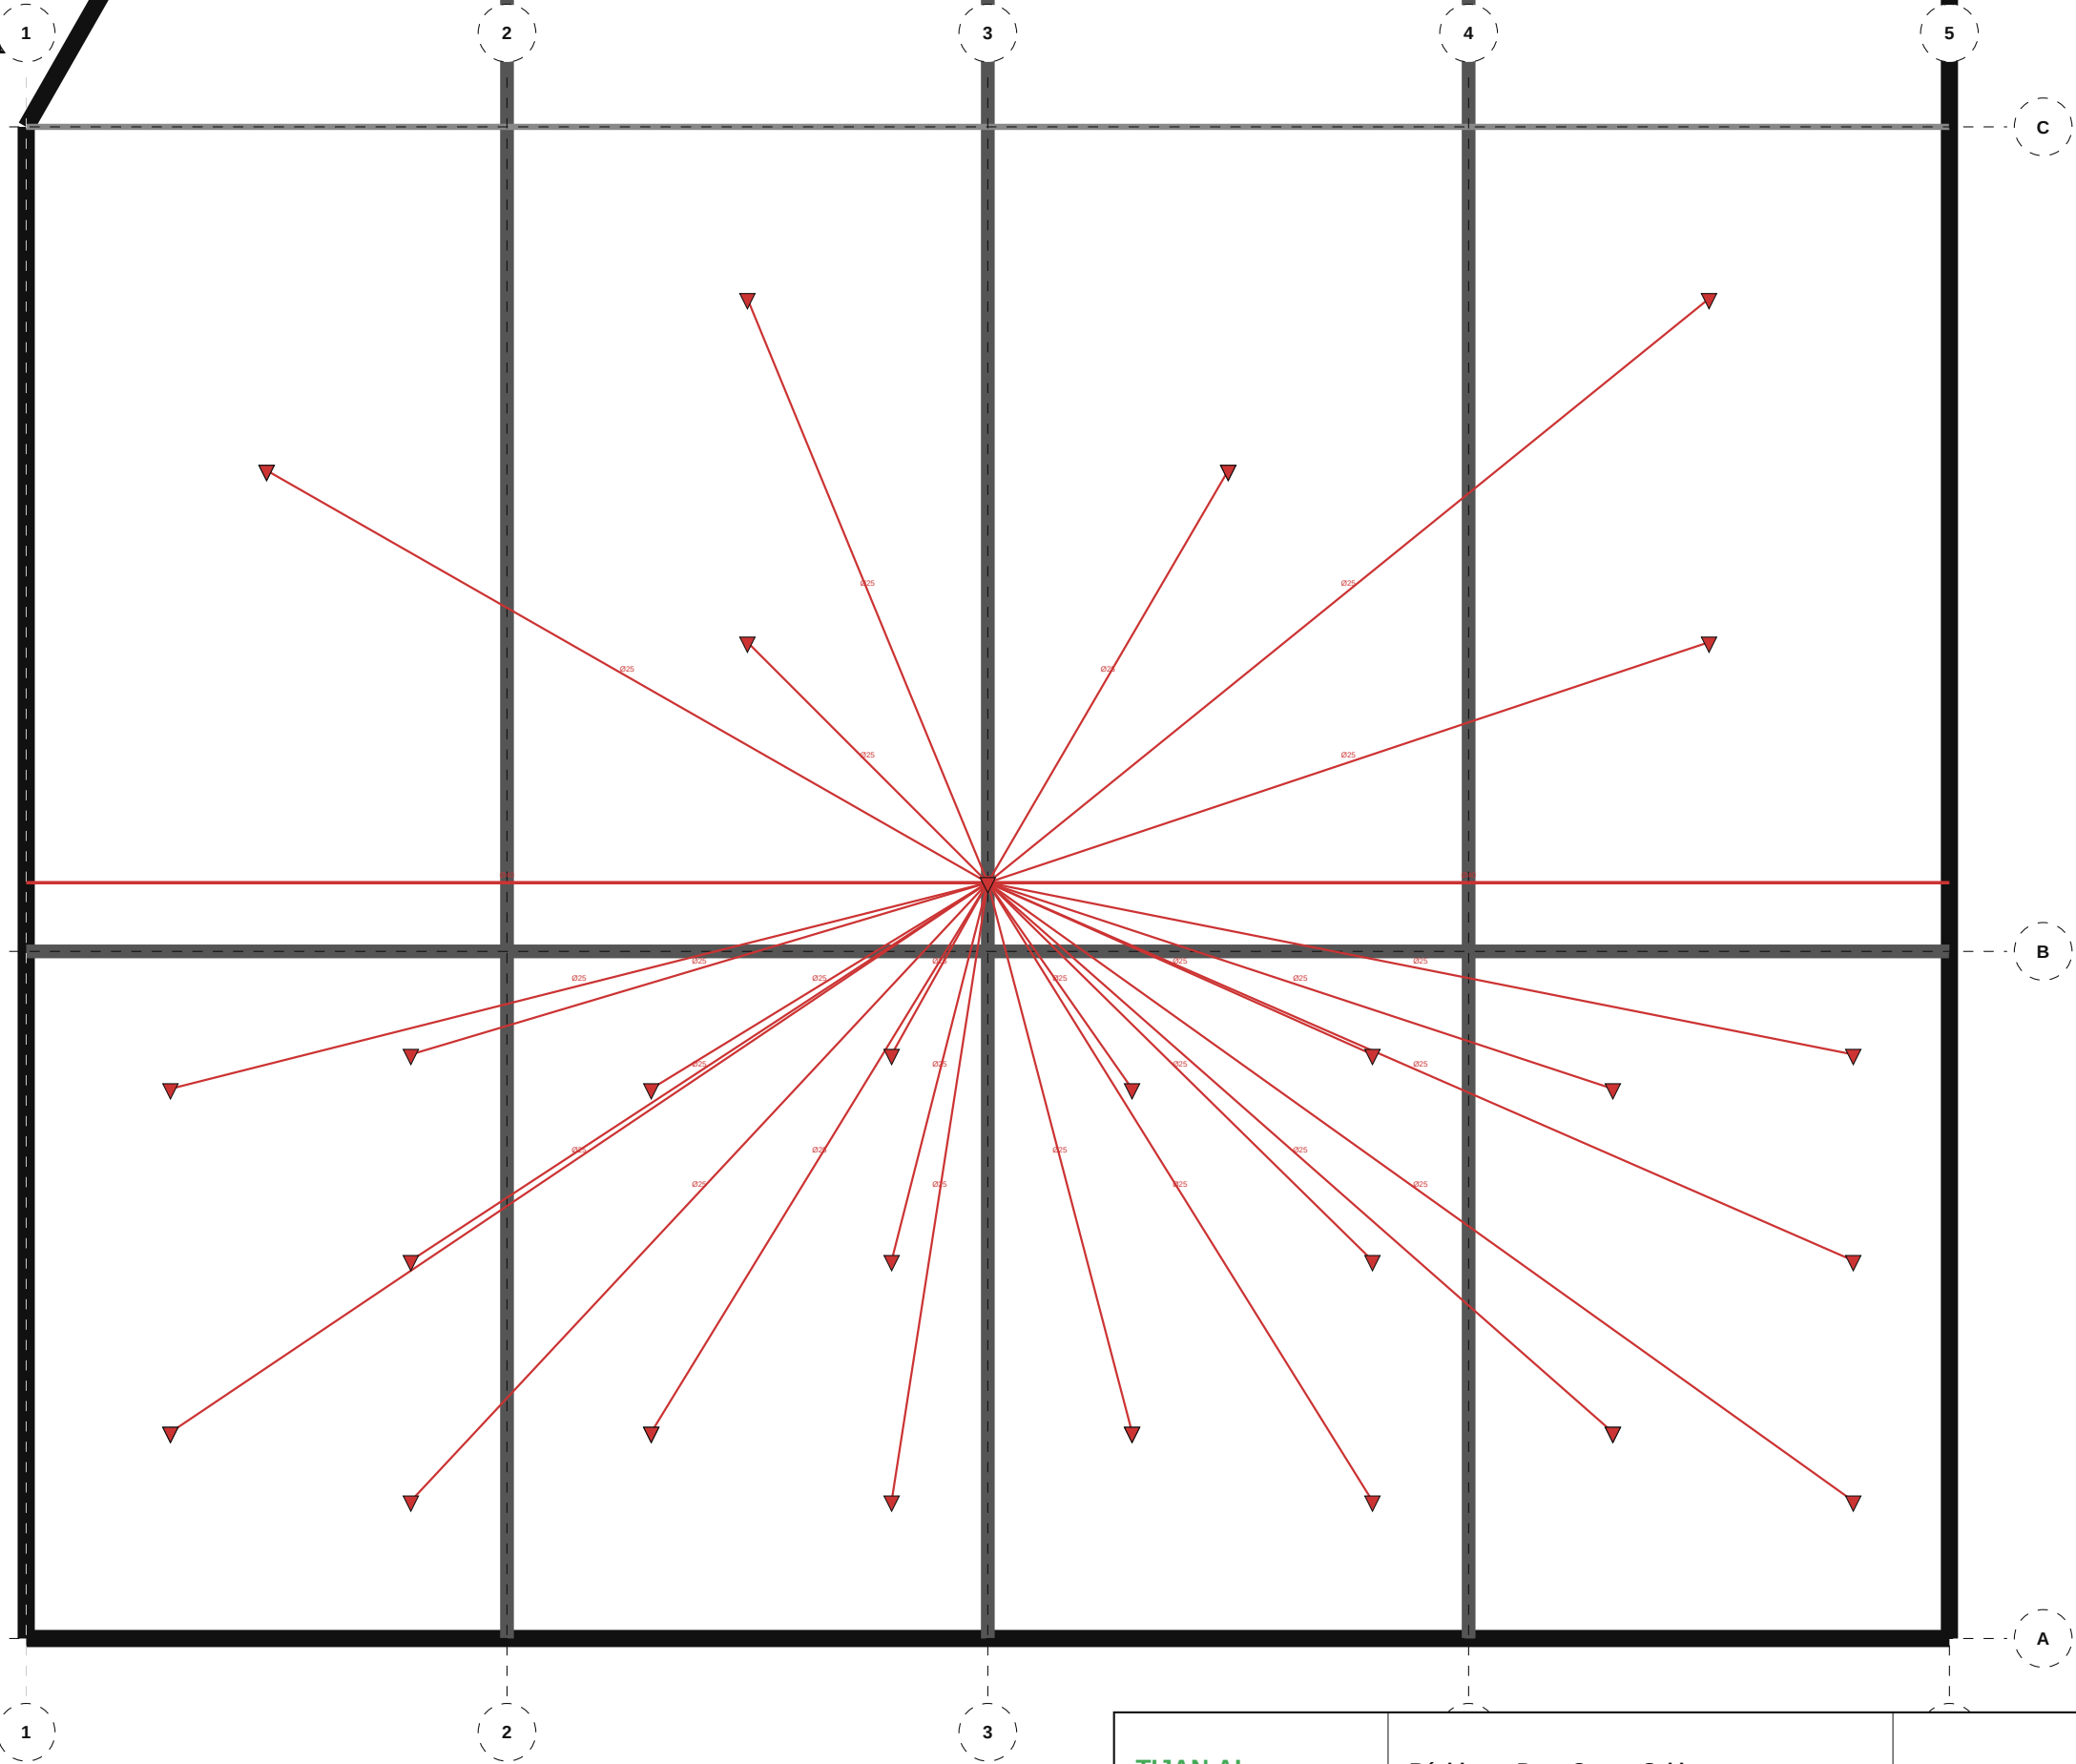

NOMENCLATURE — 400 FIF — Extinction (SPK)

• Sprinkler: 33

TIJAN AI

Bureau d'Études Automatisé

Résidence Papa Oumar Sakho

Dakar, Senegal

Éch: 1/100

Pl. 67/133


400 FIF — Extinction (SPK) — R+2

Date: 06/05/2026

Réf: 1711

BIM VFIF-067


Phase: APD

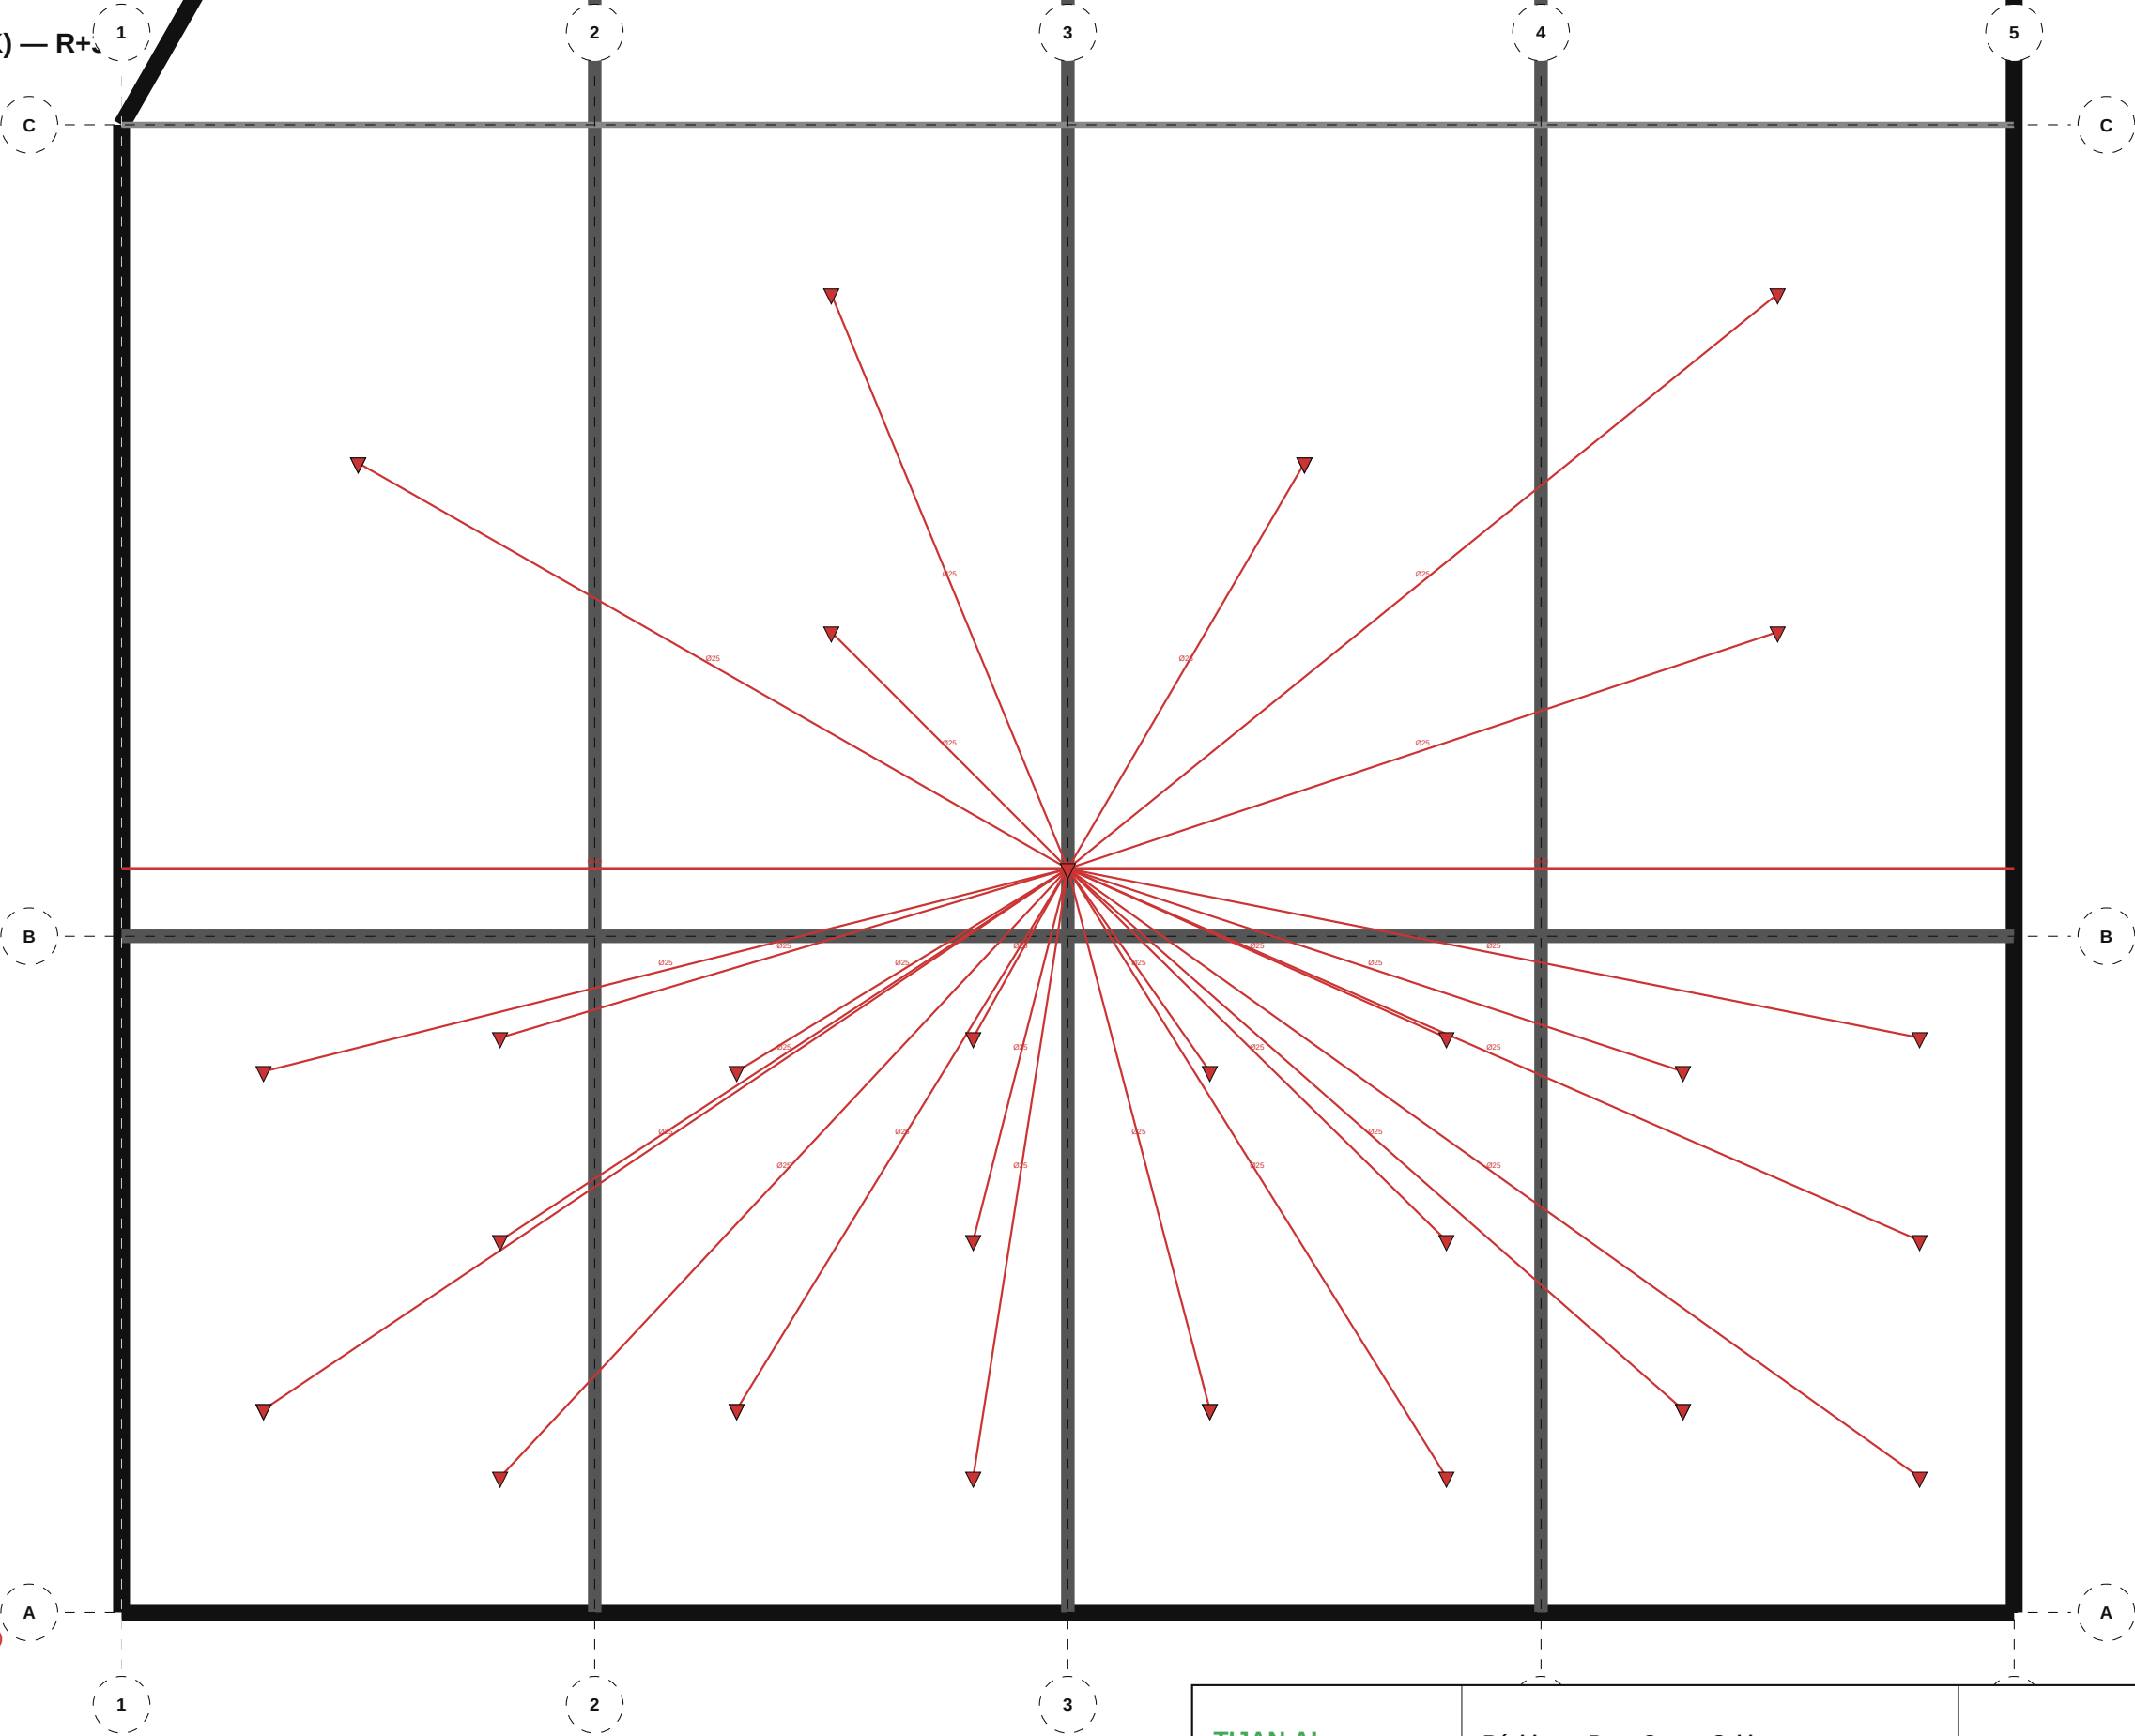

NOMENCLATURE — 400 FIF — Extinction (SPK)

• Sprinkler: 33

TIJAN AI Bureau d'Études Automatisé	Résidence Papa Oumar Sakho Dakar, Senegal	Éch: 1/100 Pl. 68/133
	400 FIF — Extinction (SPK) — R+3	
Date: 06/05/2026	Réf: 1711	BIM VFIF-068 Phase: APD

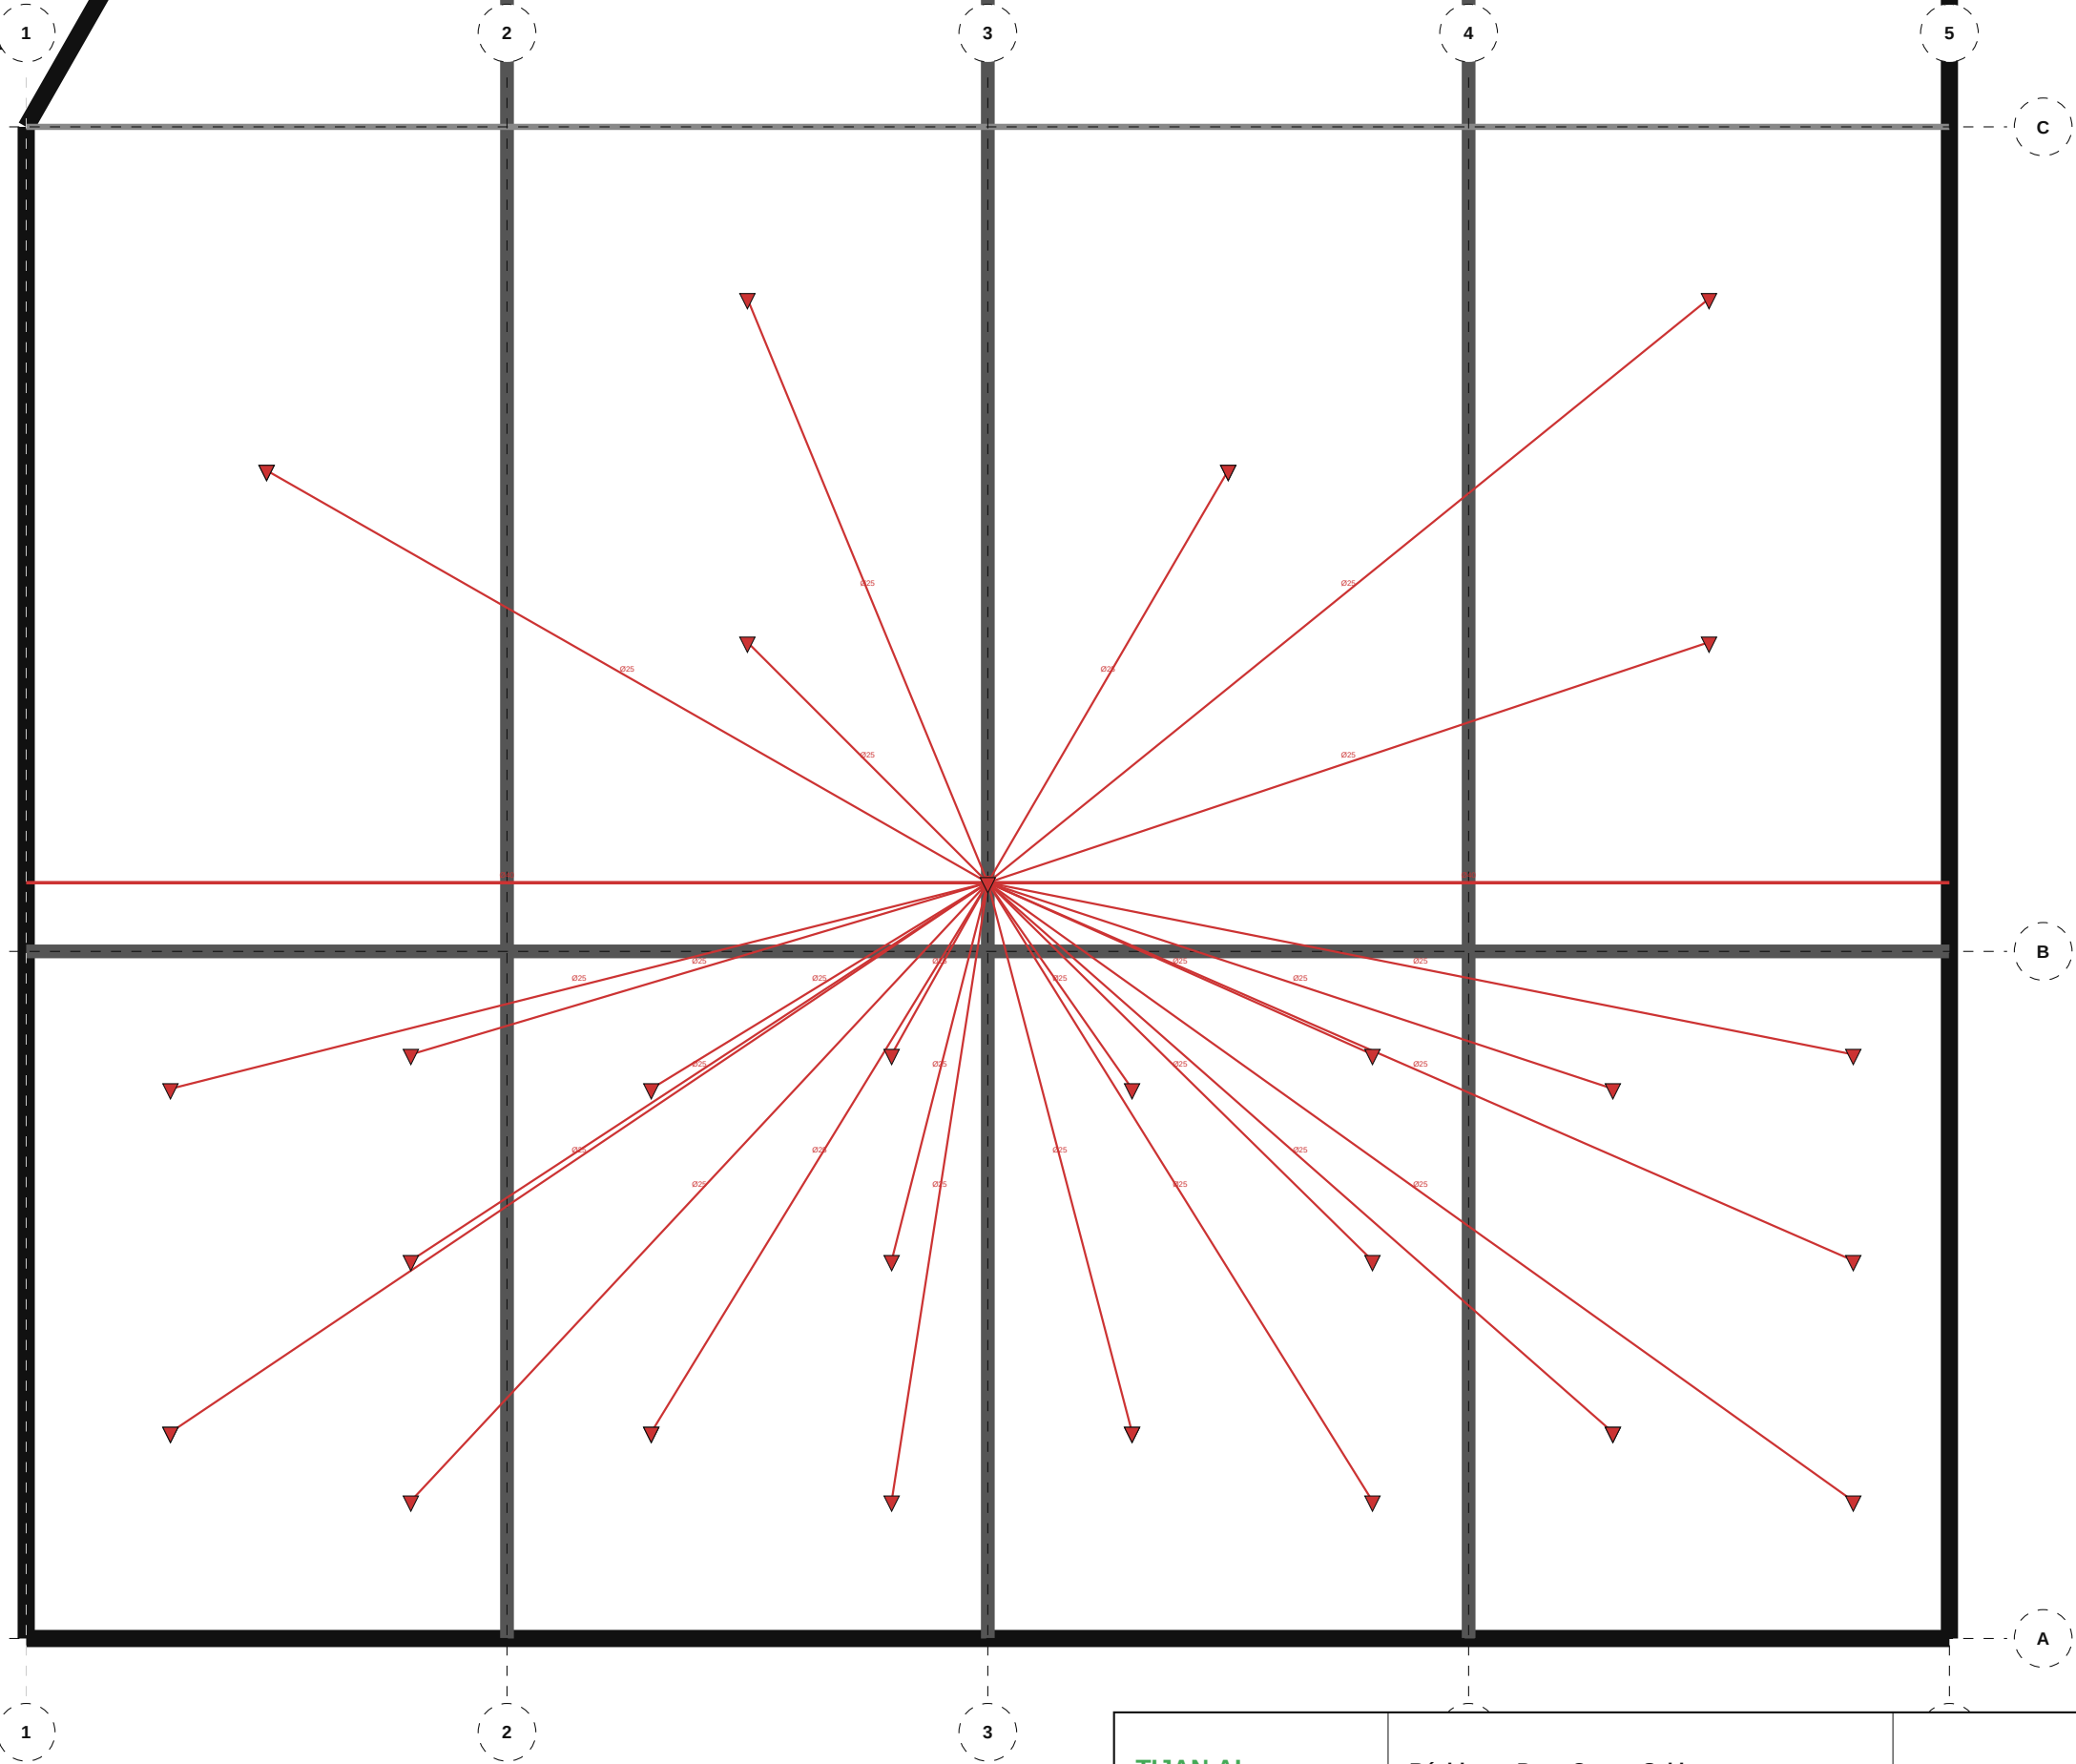


NOMENCLATURE — 400 FIF — Extinction (SPK)

• Sprinkler: 33

TIJAN AI Bureau d'Études Automatisé	Résidence Papa Oumar Sakho Dakar, Senegal	Éch: 1/100 Pl. 69/133
	400 FIF — Extinction (SPK) — R+4	
Date: 06/05/2026	Réf: 1711	BIM VFIF-069 Phase: APD

400 FIF — Extinction (SPK) — R+5

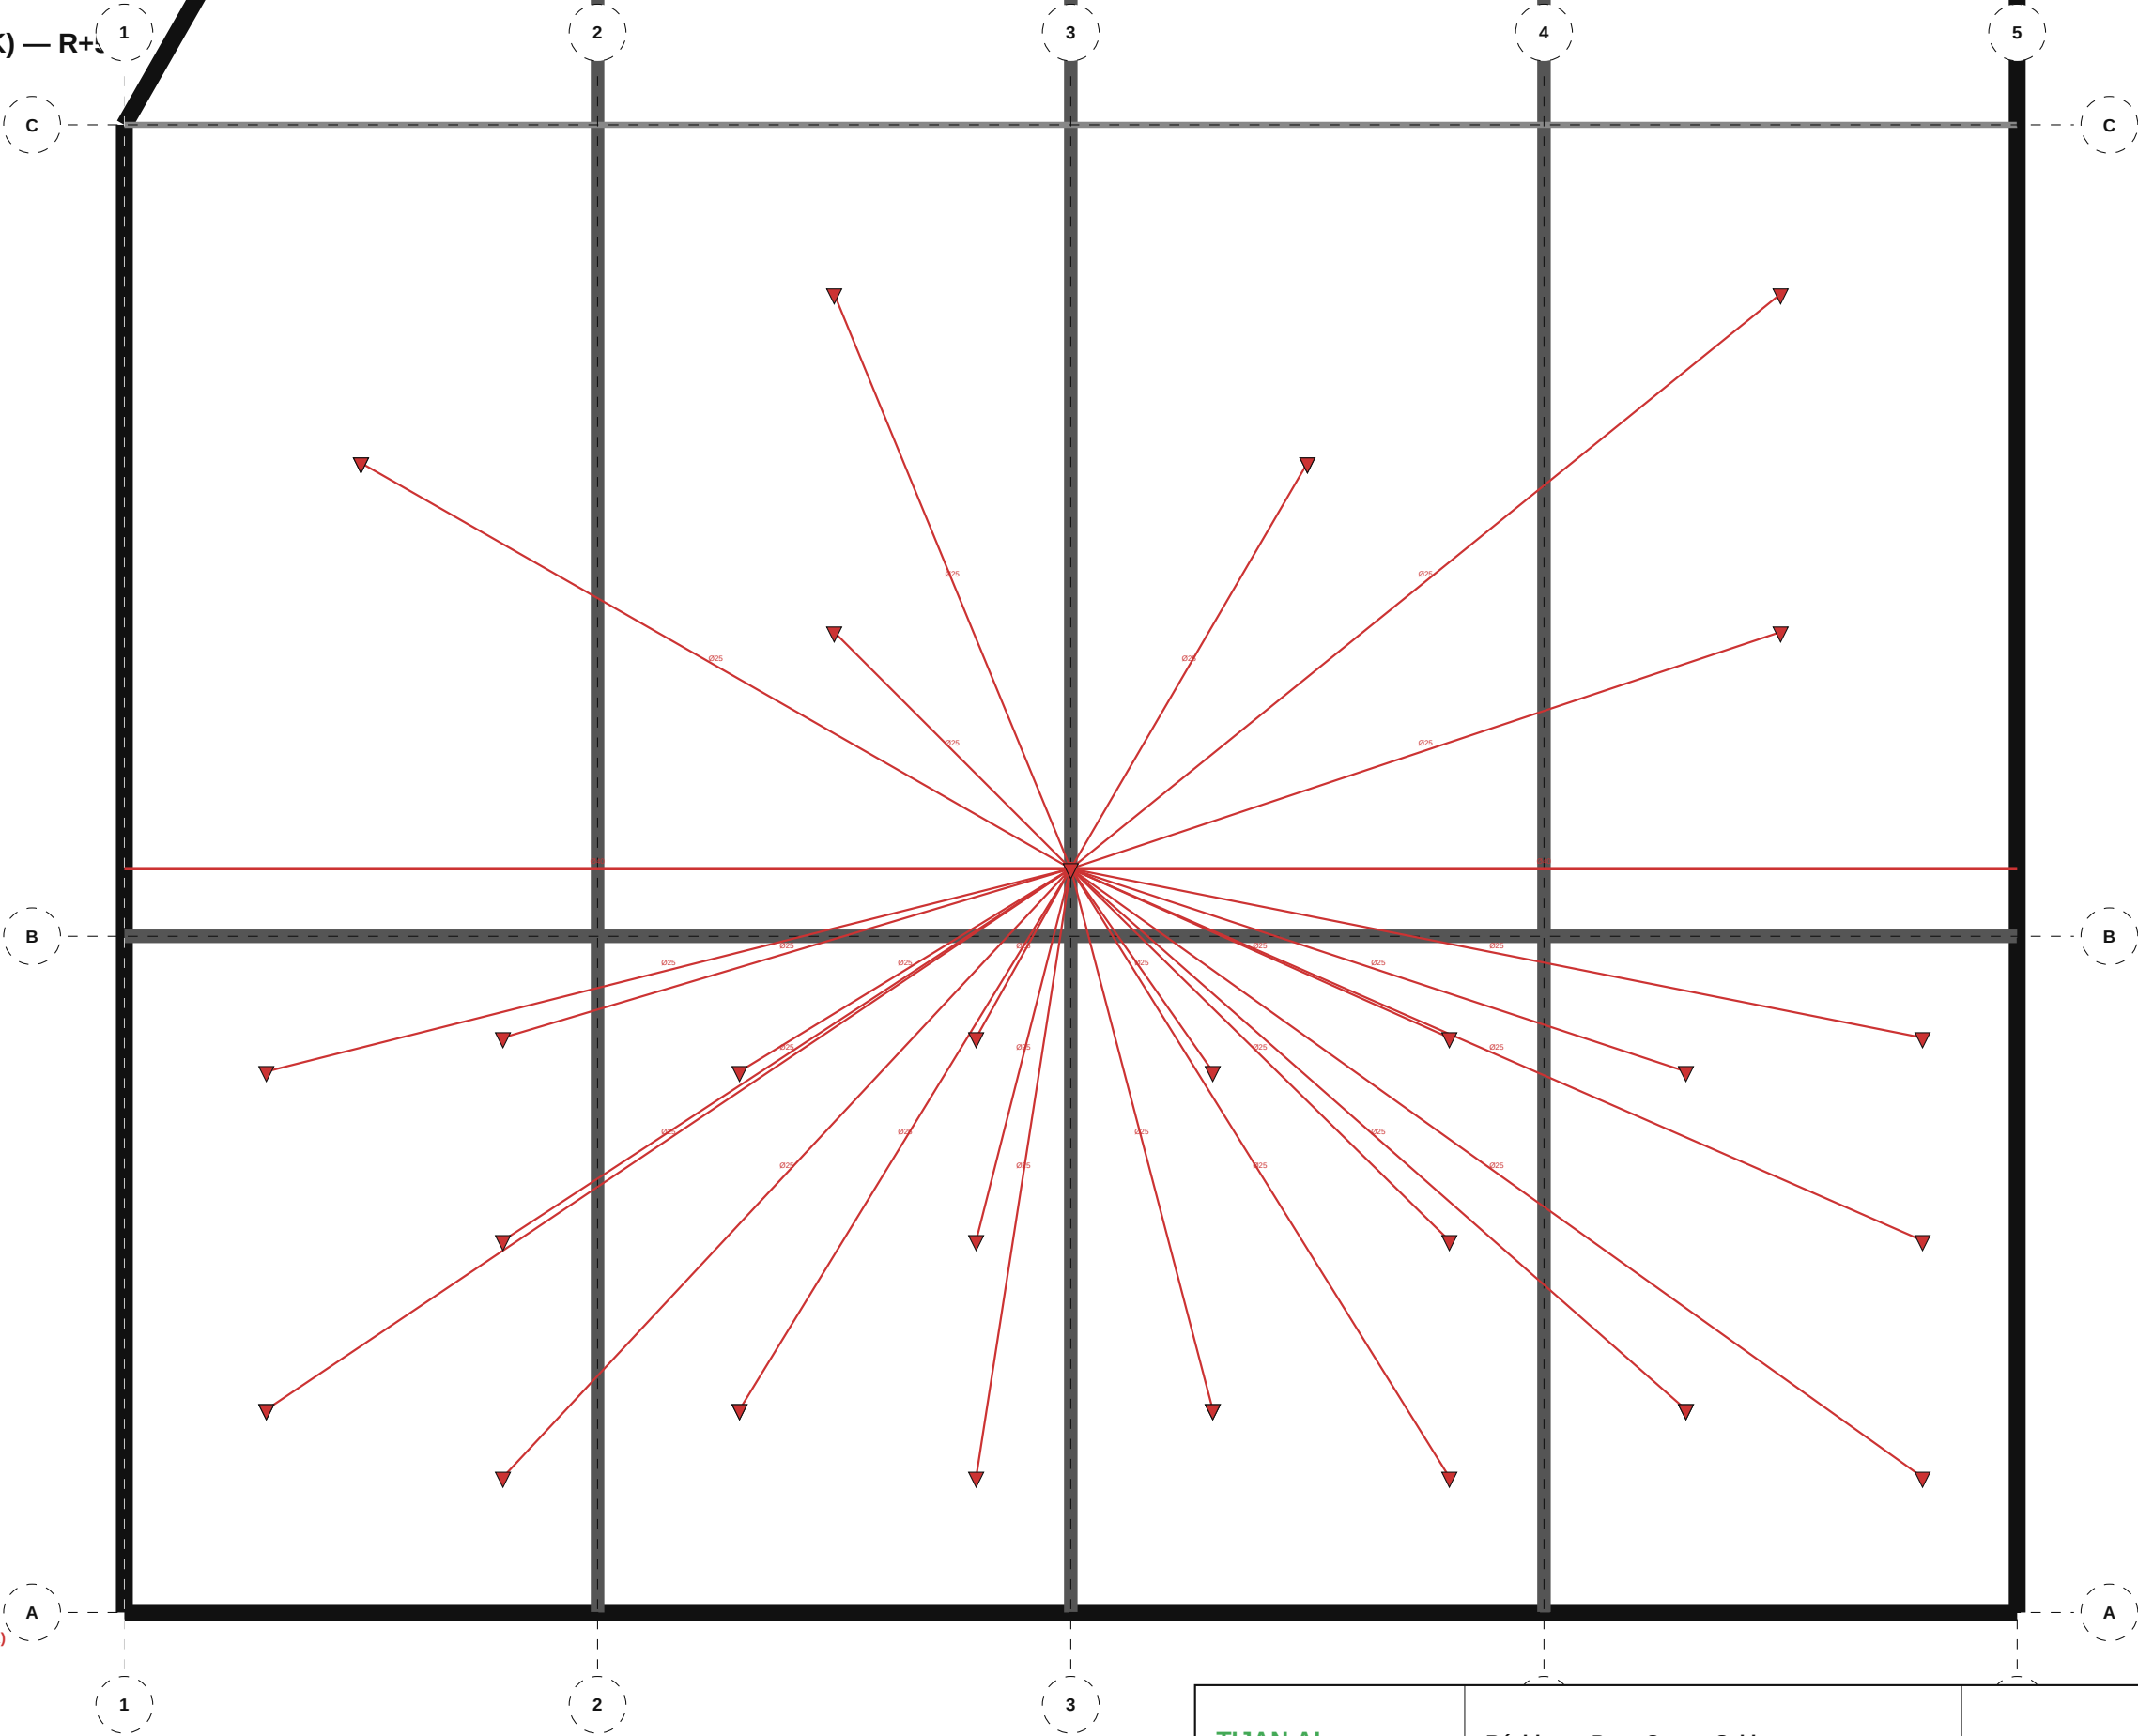

NOMENCLATURE — 400 FIF — Extinction (SPK)

• Sprinkler: 33

TIJAN AI

Bureau d'Études Automatisé

Résidence Papa Oumar Sakho

Dakar, Senegal

Éch: 1/100

Pl. 70/133


400 FIF — Extinction (SPK) — R+5

Date: 06/05/2026

Réf: 1711

BIM vFIF-070

Phase: APD

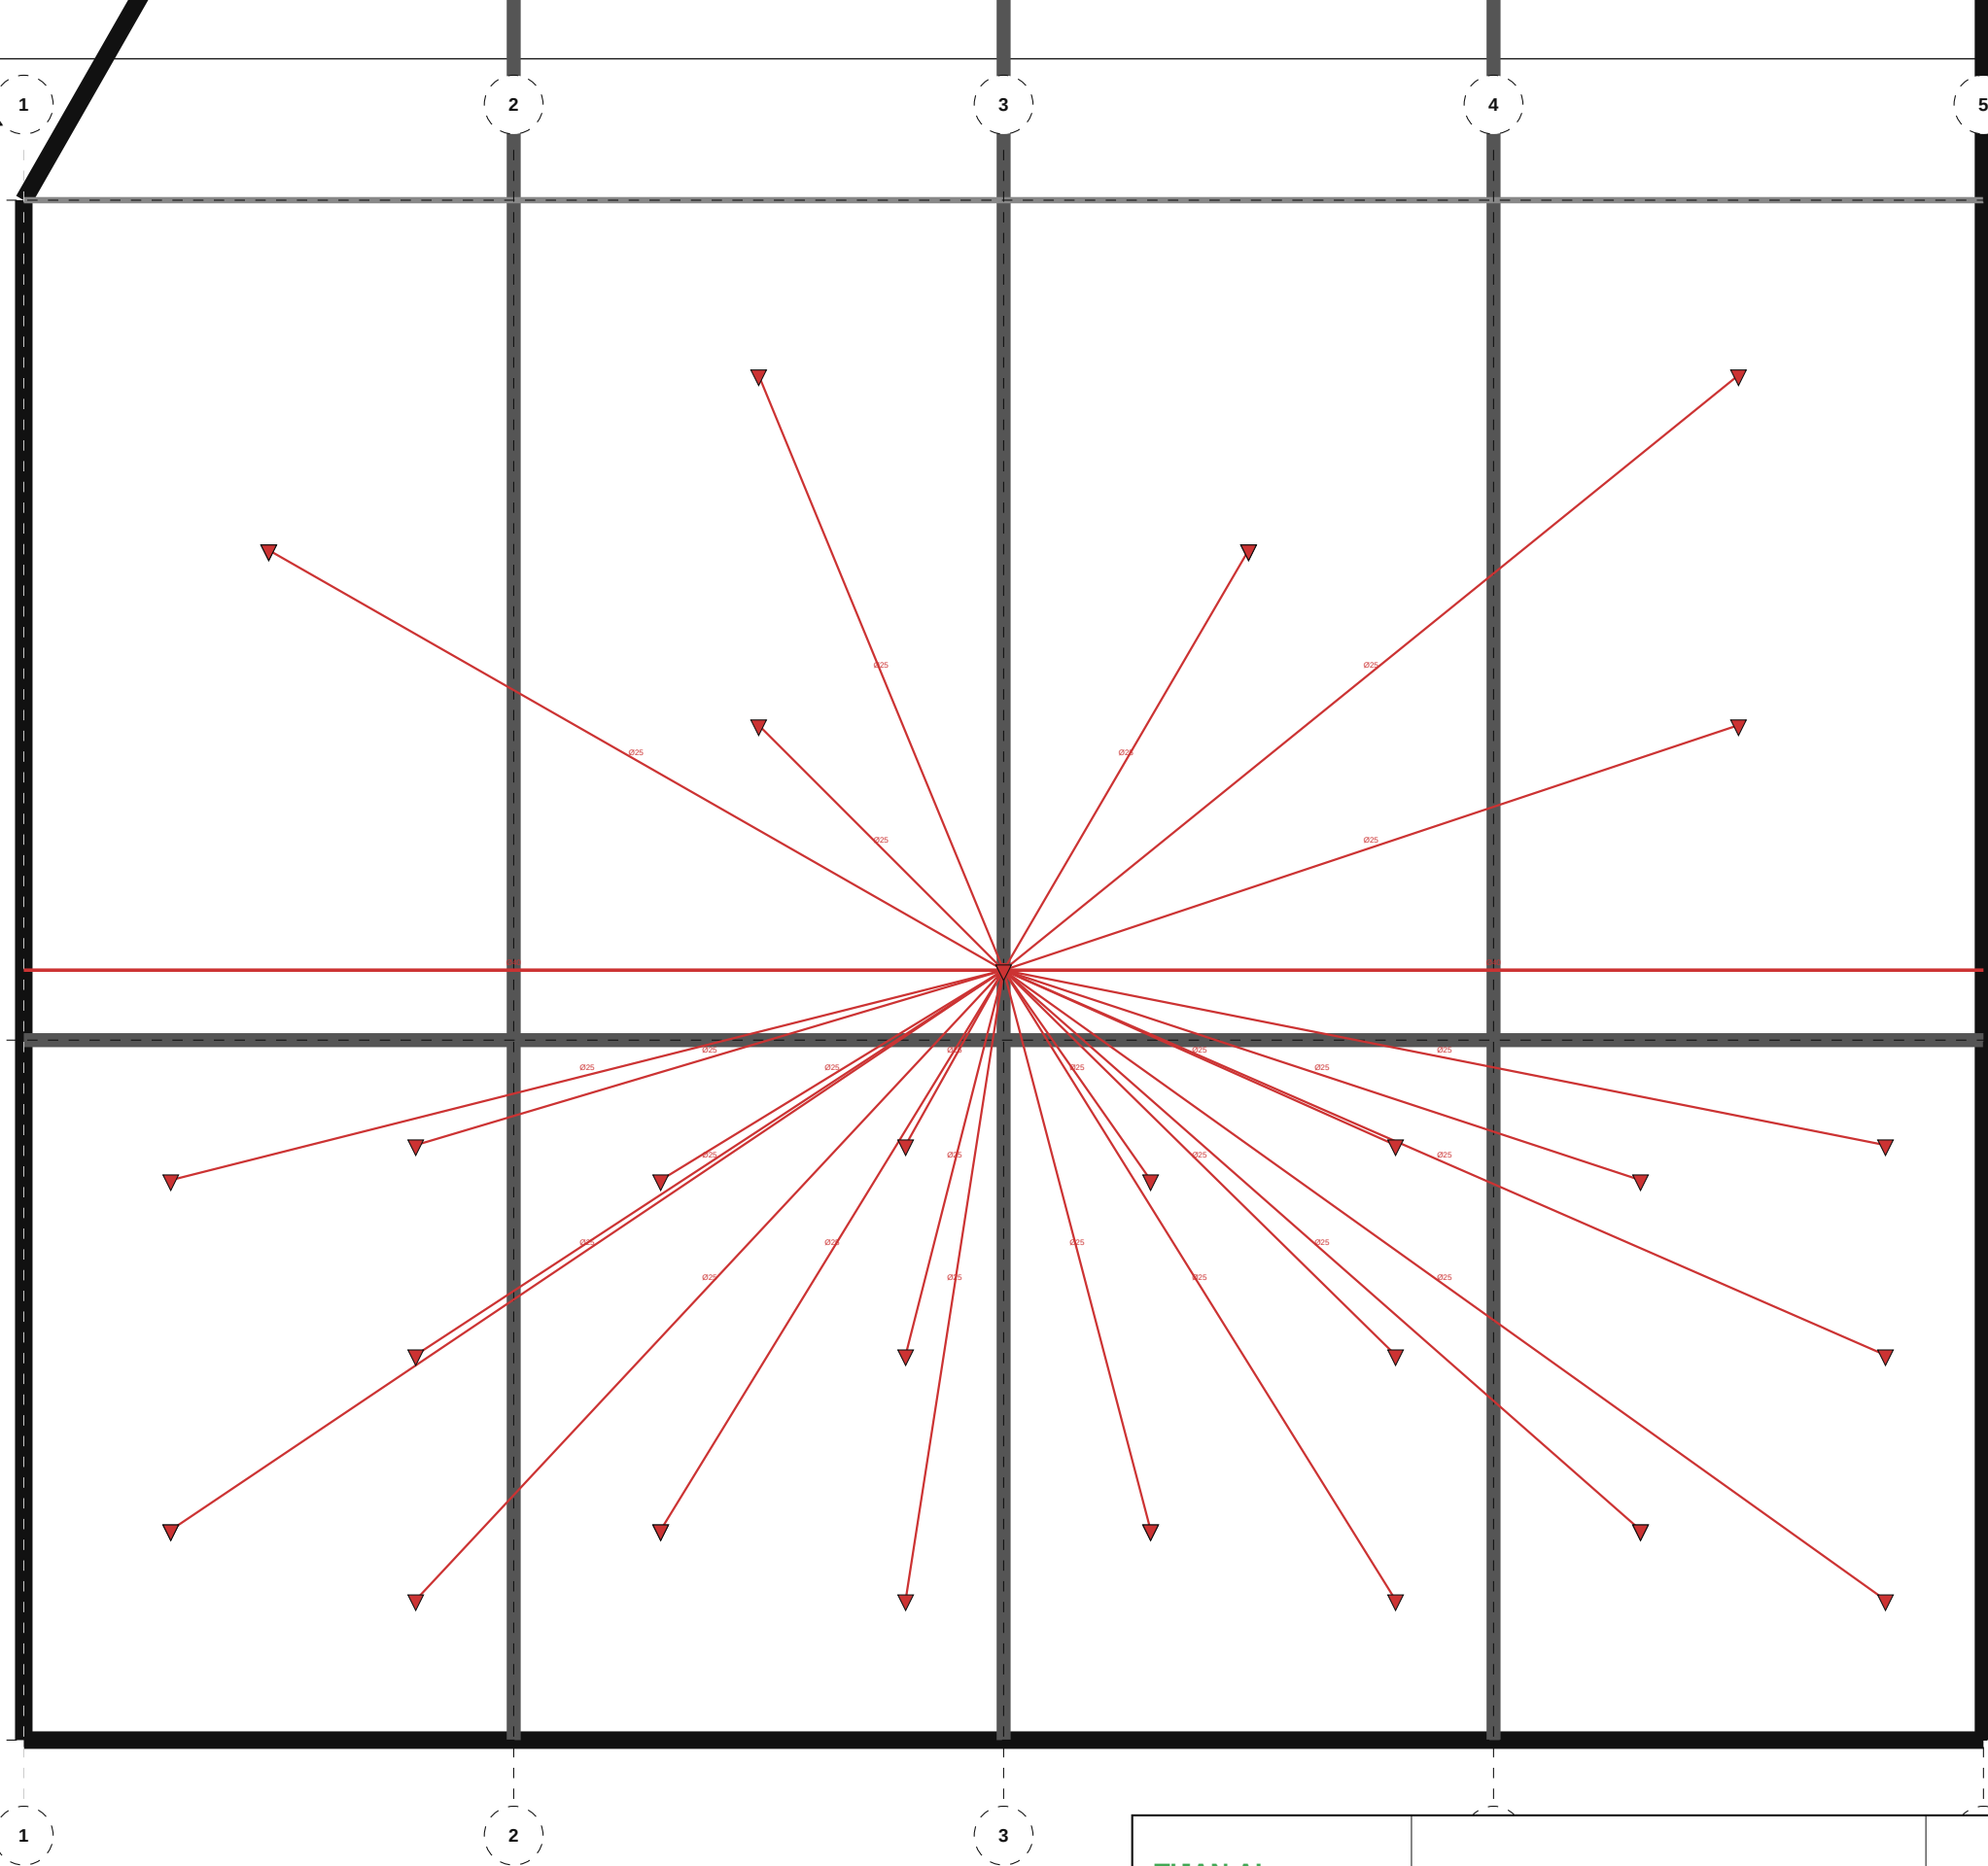

NOMENCLATURE — 400 FIF — Extinction (SPK)


• Sprinkler: 33

TIJAN AI Bureau d'Études Automatisé	Résidence Papa Oumar Sakho Dakar, Senegal	Éch: 1/100 Pl. 71/133
	400 FIF — Extinction (SPK) — R+6	
Date: 06/05/2026	Réf: 1711	BIM vFIF-071 Phase: APD

The diagram shows a square grid with a central point. Red arrows radiate from this point in many directions. The grid is labeled with numbers 1, 2, 3, 4, 5 along the top and bottom edges, and letters A, B, C along the right edge. A small table is visible at the bottom right corner.

- Sprinkler: 33

TIJAN AI Bureau d'Études Automatisé	Résidence Papa Oumar Sakho Dakar, Senegal	Éch: 1/100 Pl. 72/133
	400 FIF — Extinction (SPK) — R+7	
Date: 06/05/2026	Réf: 1711	BIM vFIF-072 Phase: APD

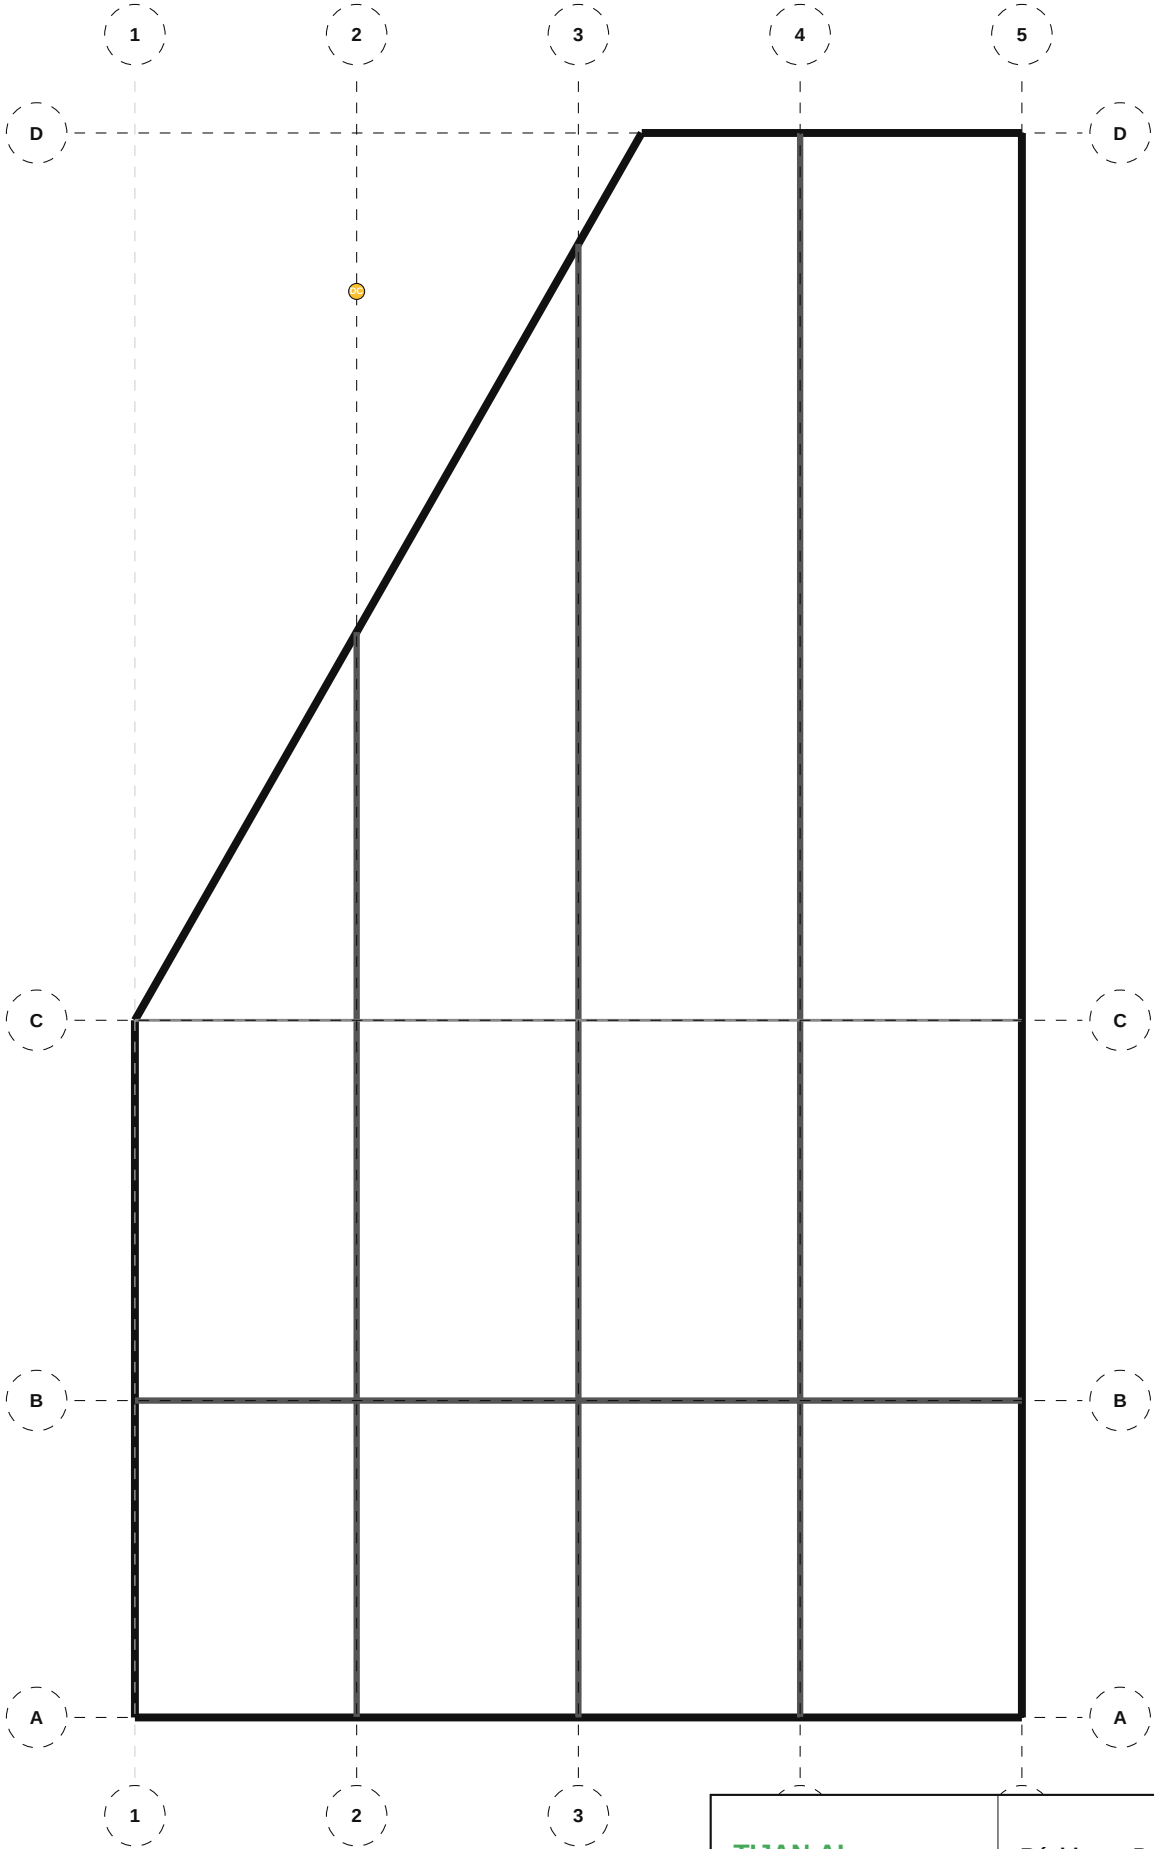

NOMENCLATURE — 400 FIF — Détection (DET)

• Détecteur de chaleur: 1

TIJAN AI Bureau d'Études Automatisé	Résidence Papa Oumar Sakho Dakar, Senegal	Éch: 1/100 Pl. 73/133
	400 FIF — Détection (DET) — Sous-Sol	
Date: 06/05/2026	Réf: 1711	BIM vFIF-073 Phase: APD


1

2

3

4

5

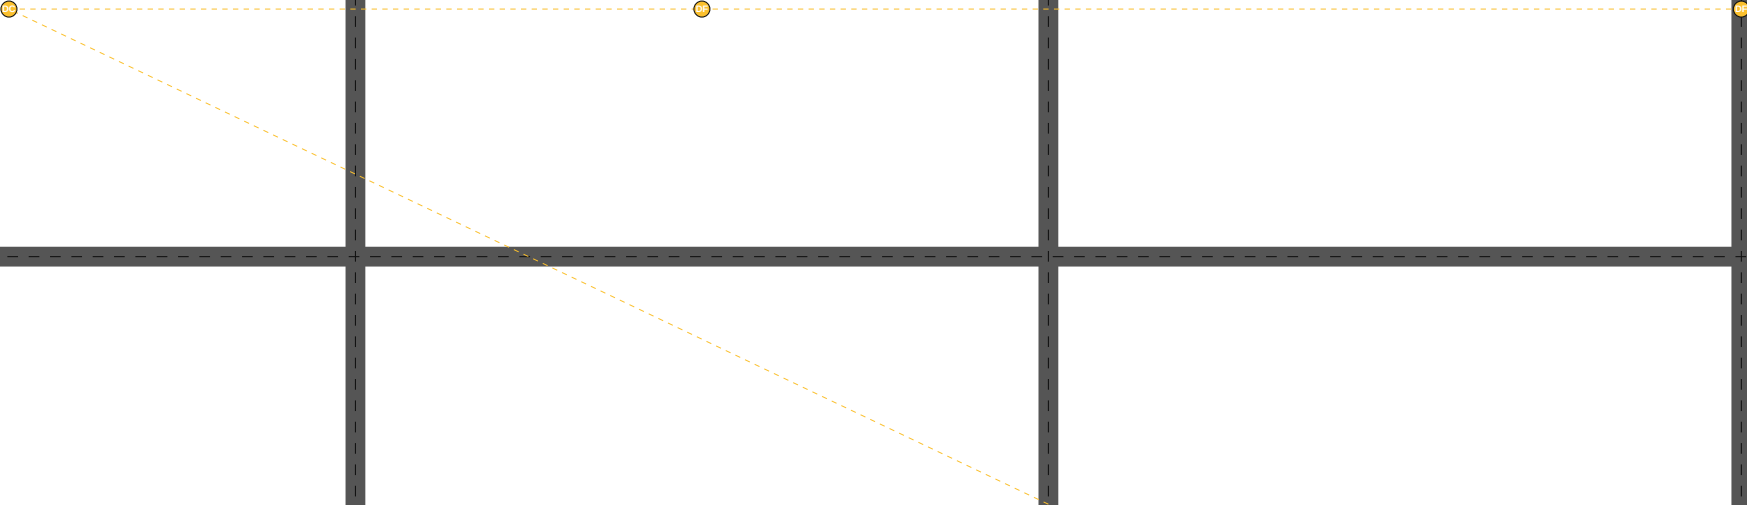

B

B

A

A

NOMENCLATURE — 400 FIF — Détection (DET)

- 1
- Détecteur de fumée: 2
 - Détecteur de chaleur: 1


2

3

4

5


TIJAN AI Bureau d'Études Automatisé	Résidence Papa Oumar Sakho Dakar, Senegal	Éch: 1/100 Pl. 74/133
	400 FIF — Détection (DET) — RDC	
Date: 06/05/2026	Réf: 1711	BIM vFIF-074 Phase: APD

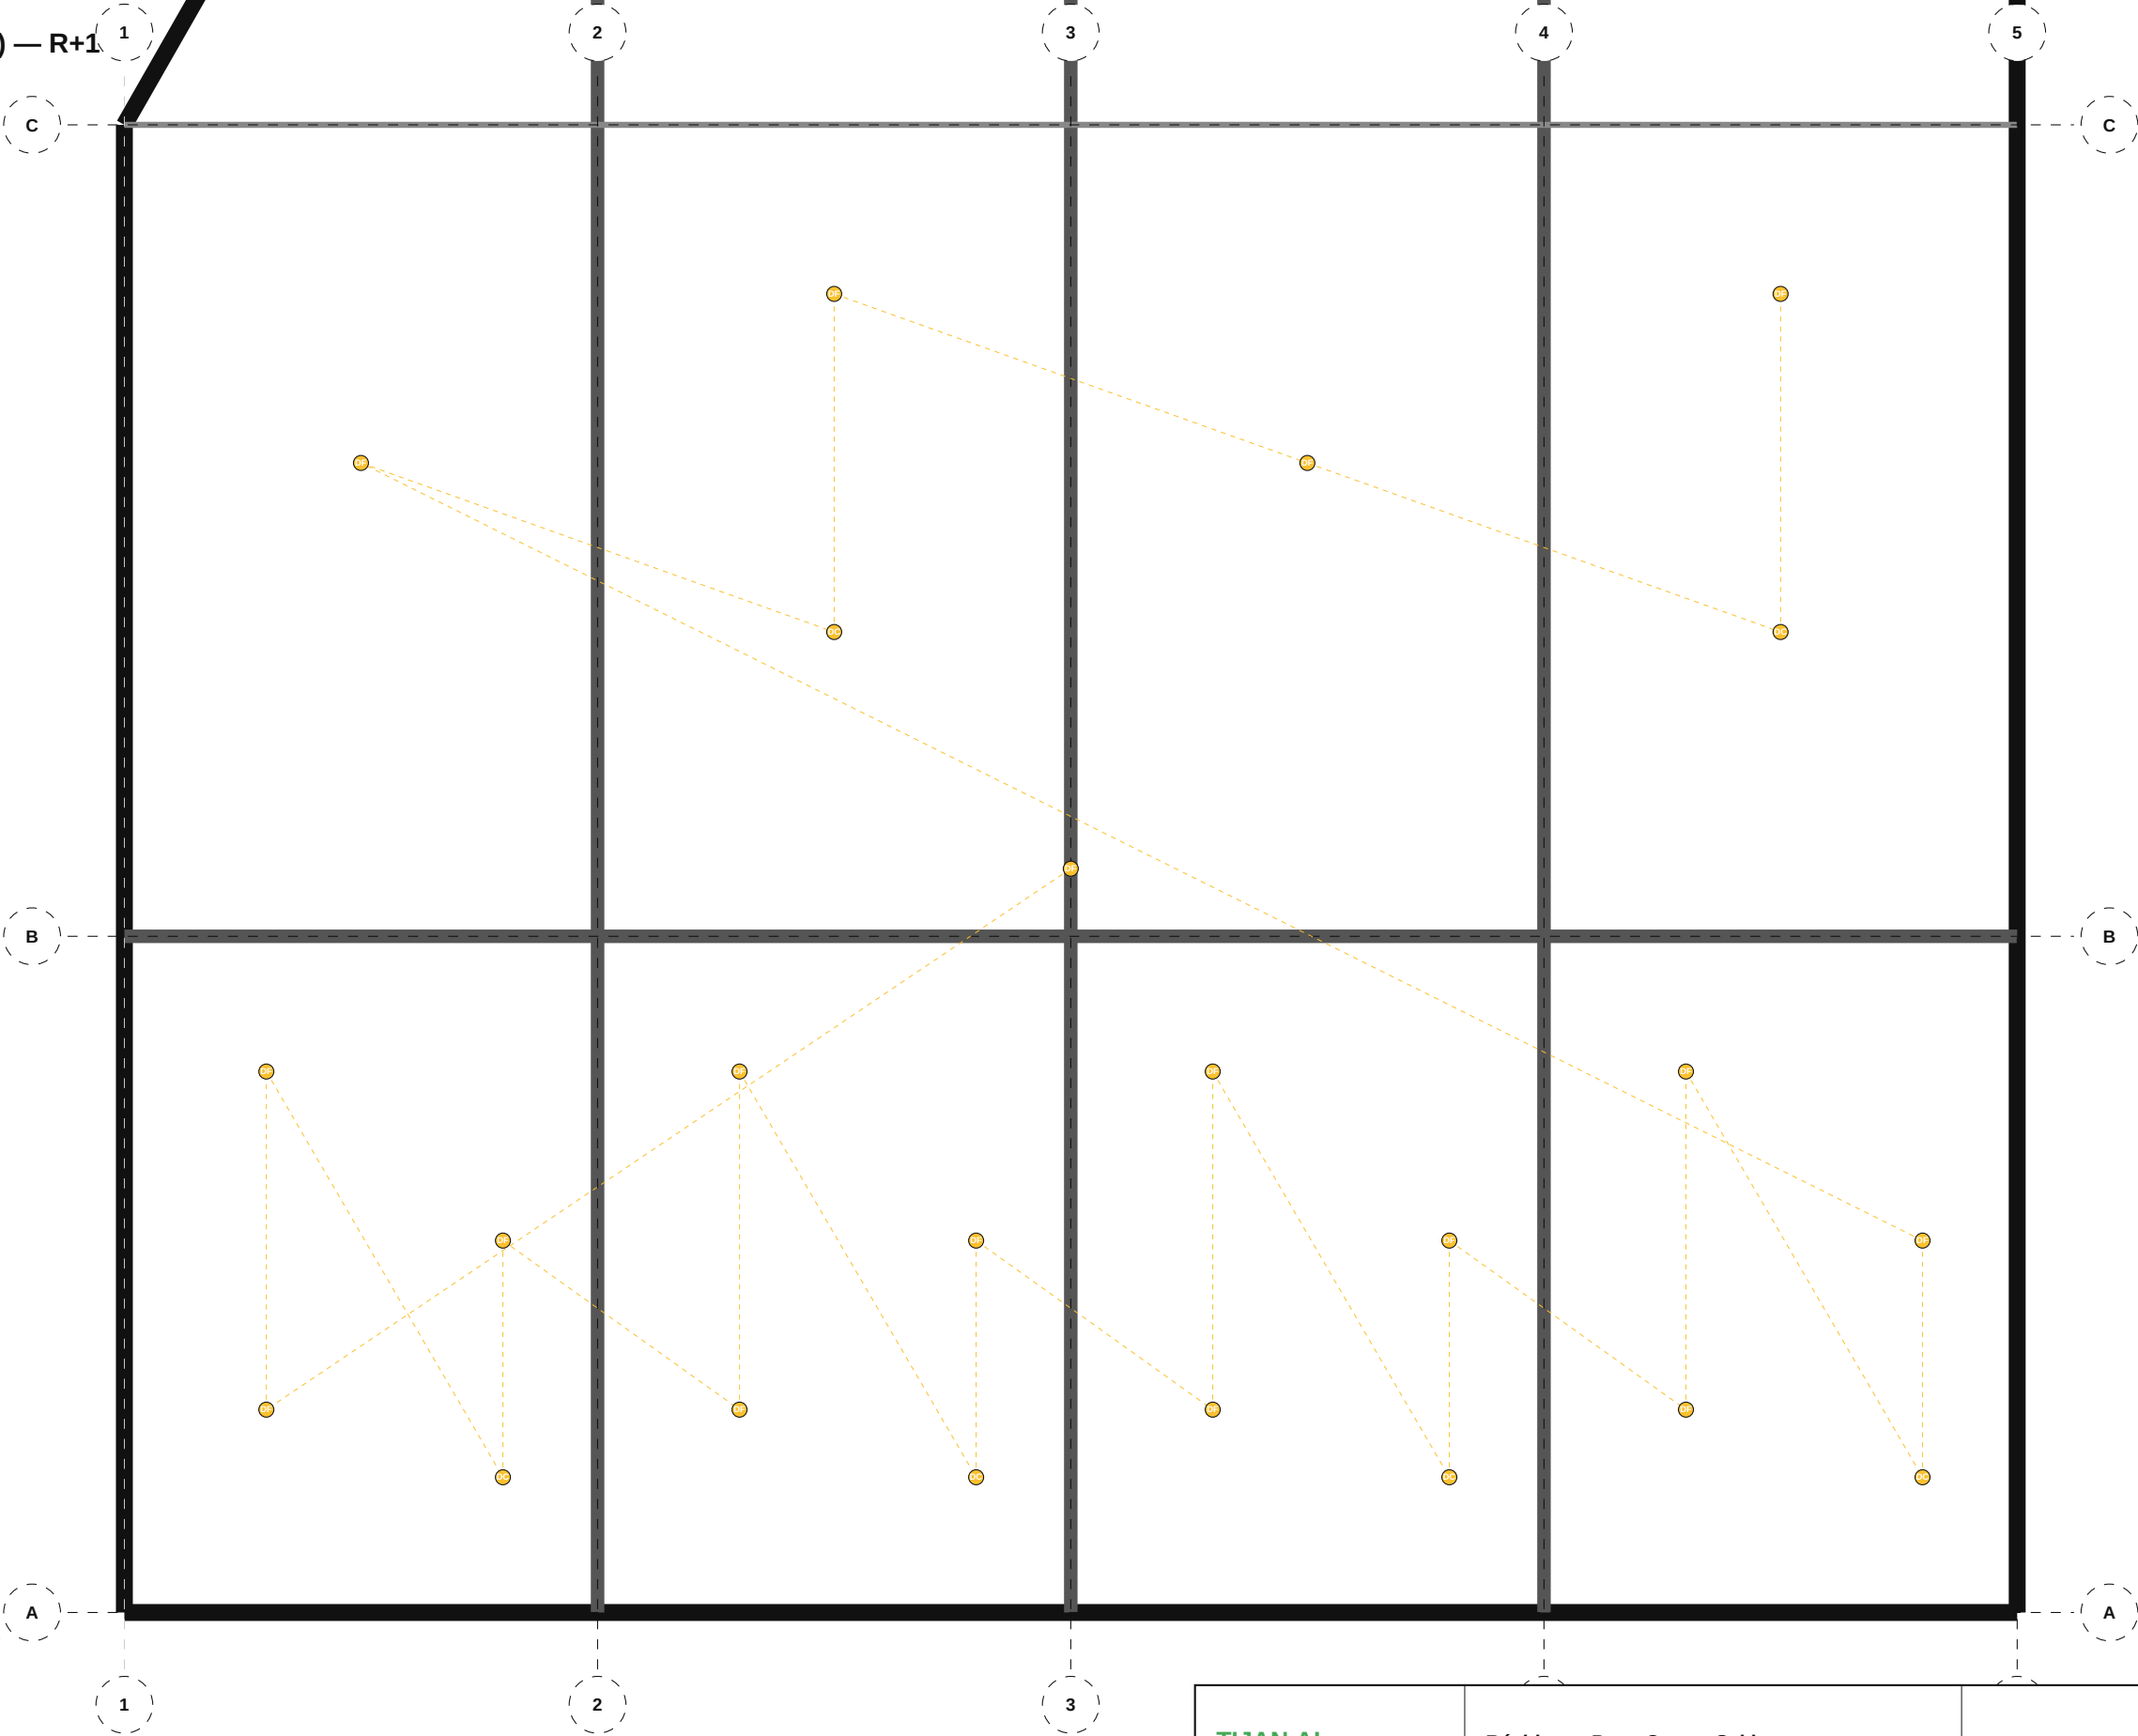

NOMENCLATURE — 400 FIF — Détection (DET)

- Détecteur de fumée: 17
- Détecteur de chaleur: 6


TIJAN AI Bureau d'Études Automatisé	Résidence Papa Oumar Sakho Dakar, Senegal	Éch: 1/100 Pl. 75/133
	400 FIF — Détection (DET) — R+1	
Date: 06/05/2026	Réf: 1711	BIM vFIF-075 Phase: APD

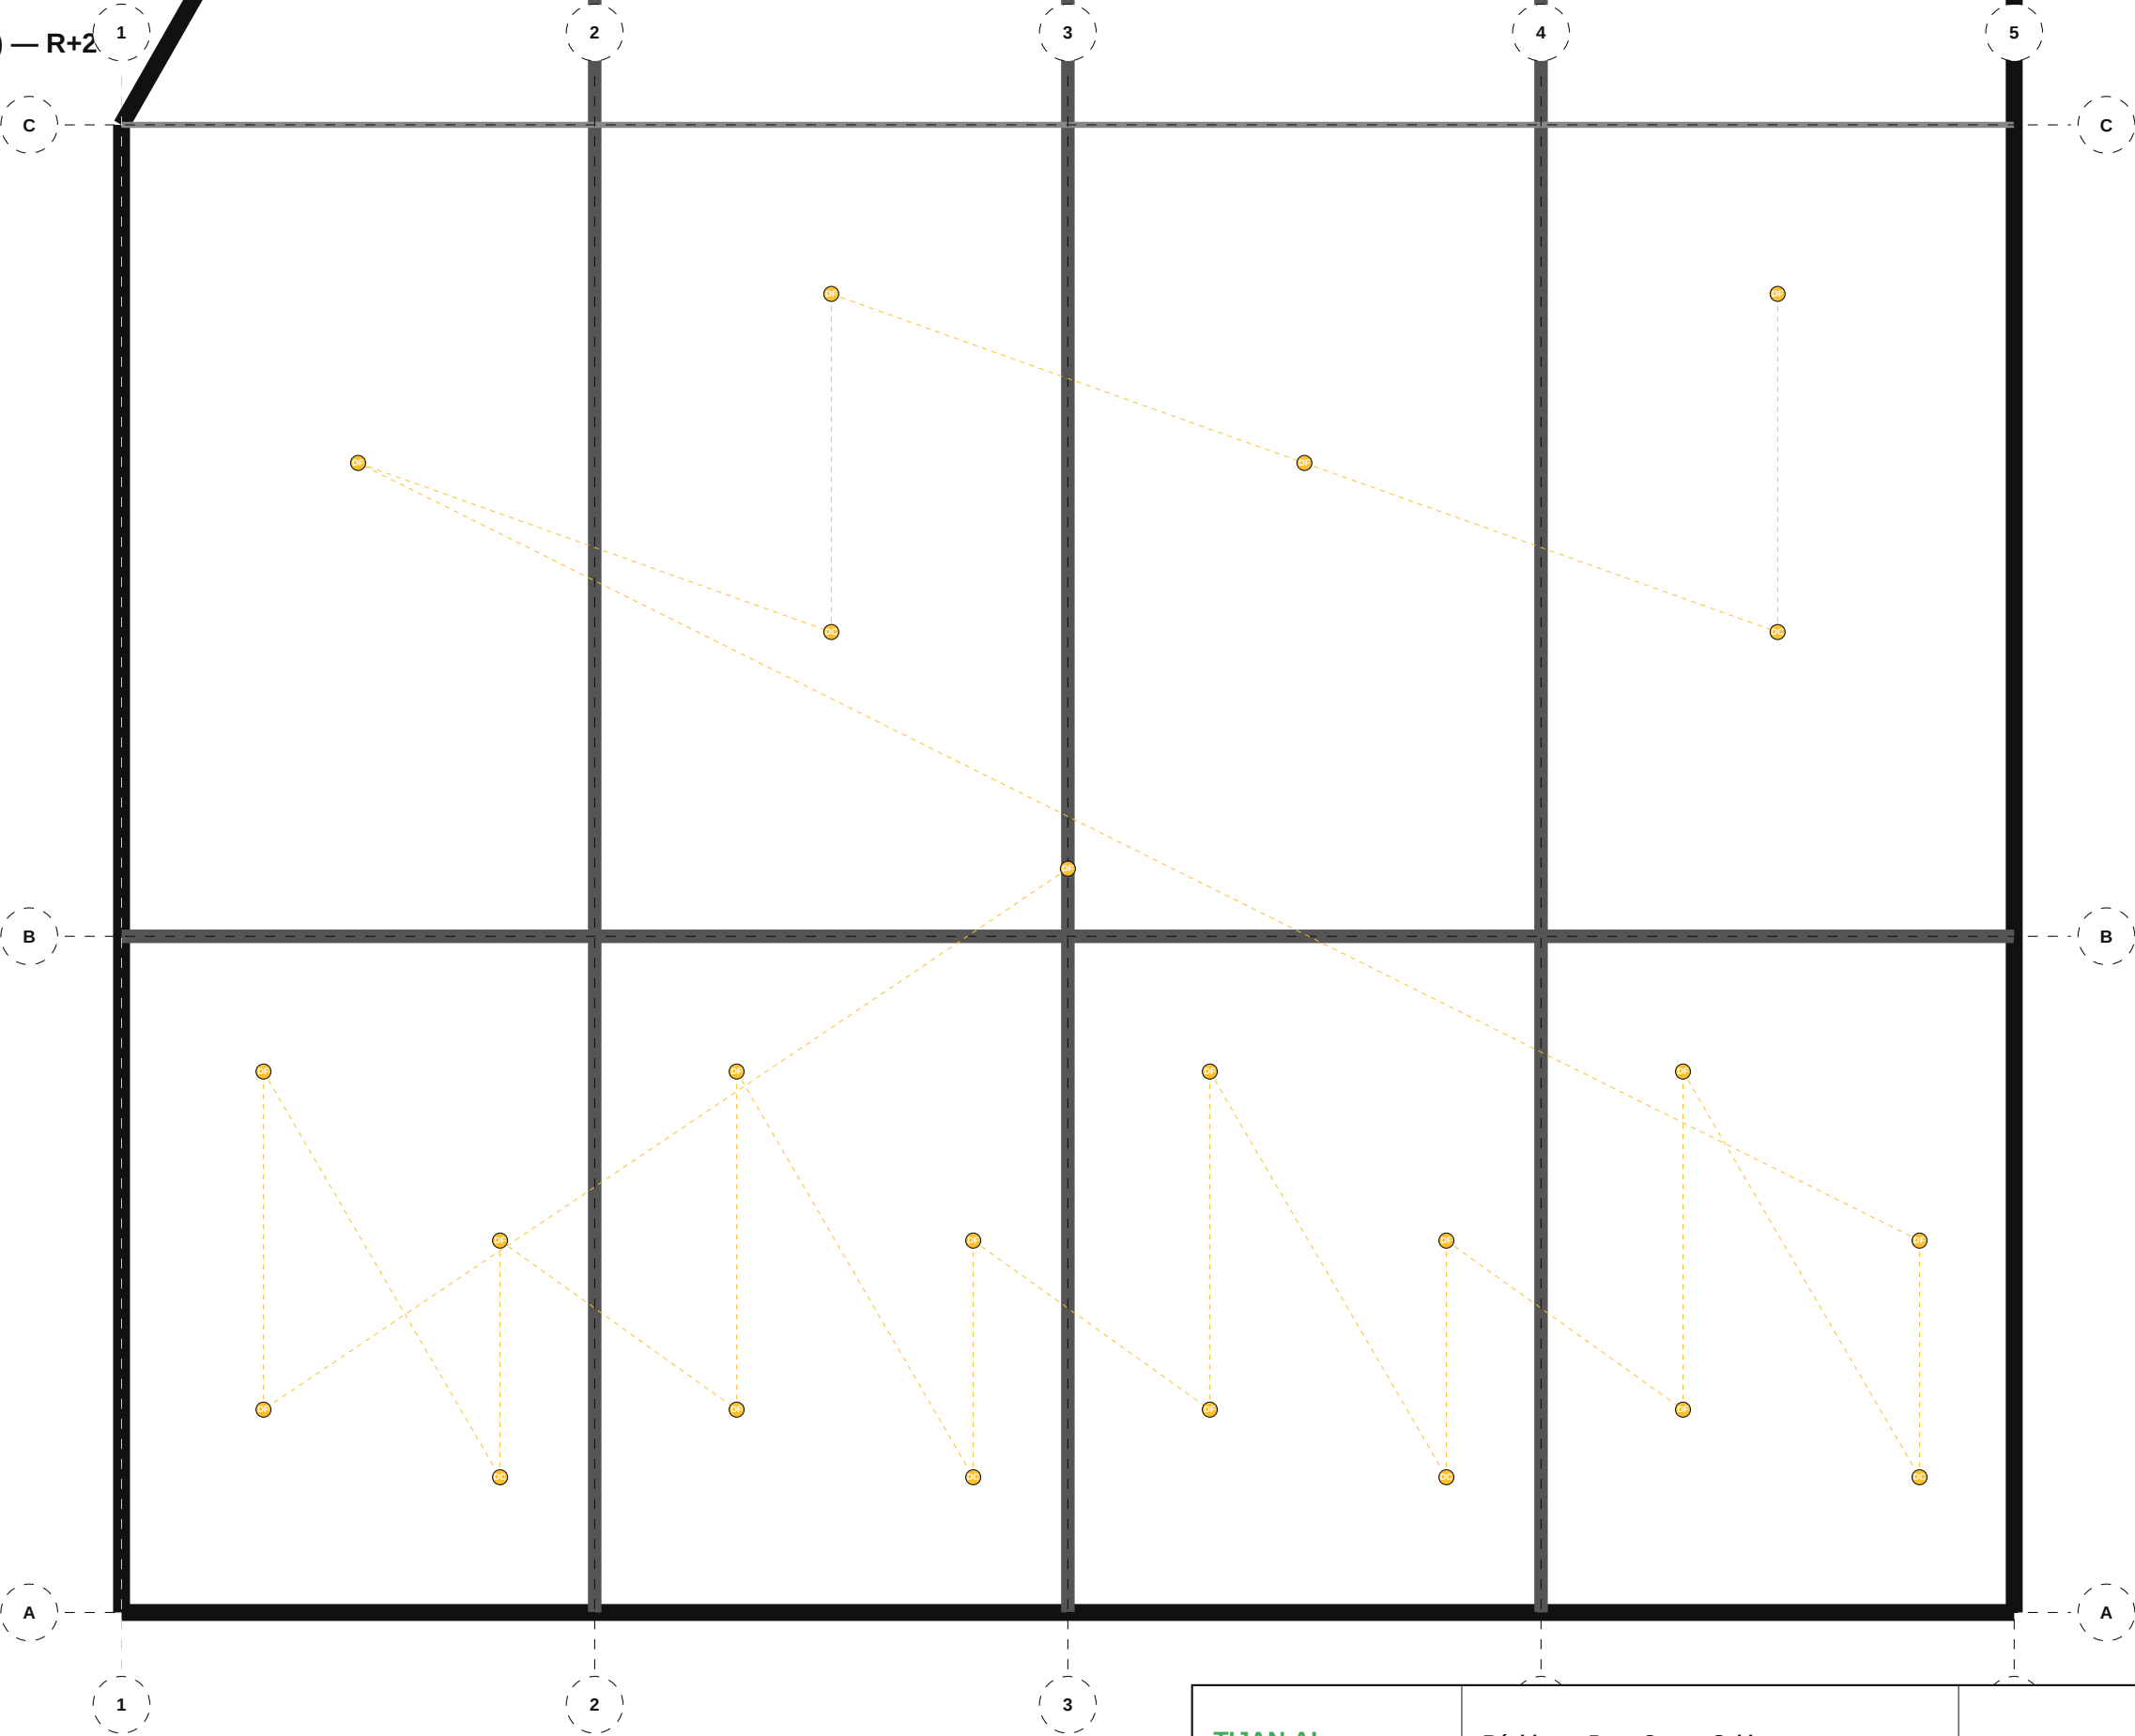

NOMENCLATURE — 400 FIF — Détection (DET)

- Détecteur de fumée: 17
- Détecteur de chaleur: 6


TIJAN AI Bureau d'Études Automatisé	Résidence Papa Oumar Sakho Dakar, Senegal	Éch: 1/100 Pl. 76/133
	400 FIF — Détection (DET) — R+2	
Date: 06/05/2026	Réf: 1711	BIM vFIF-076 Phase: APD

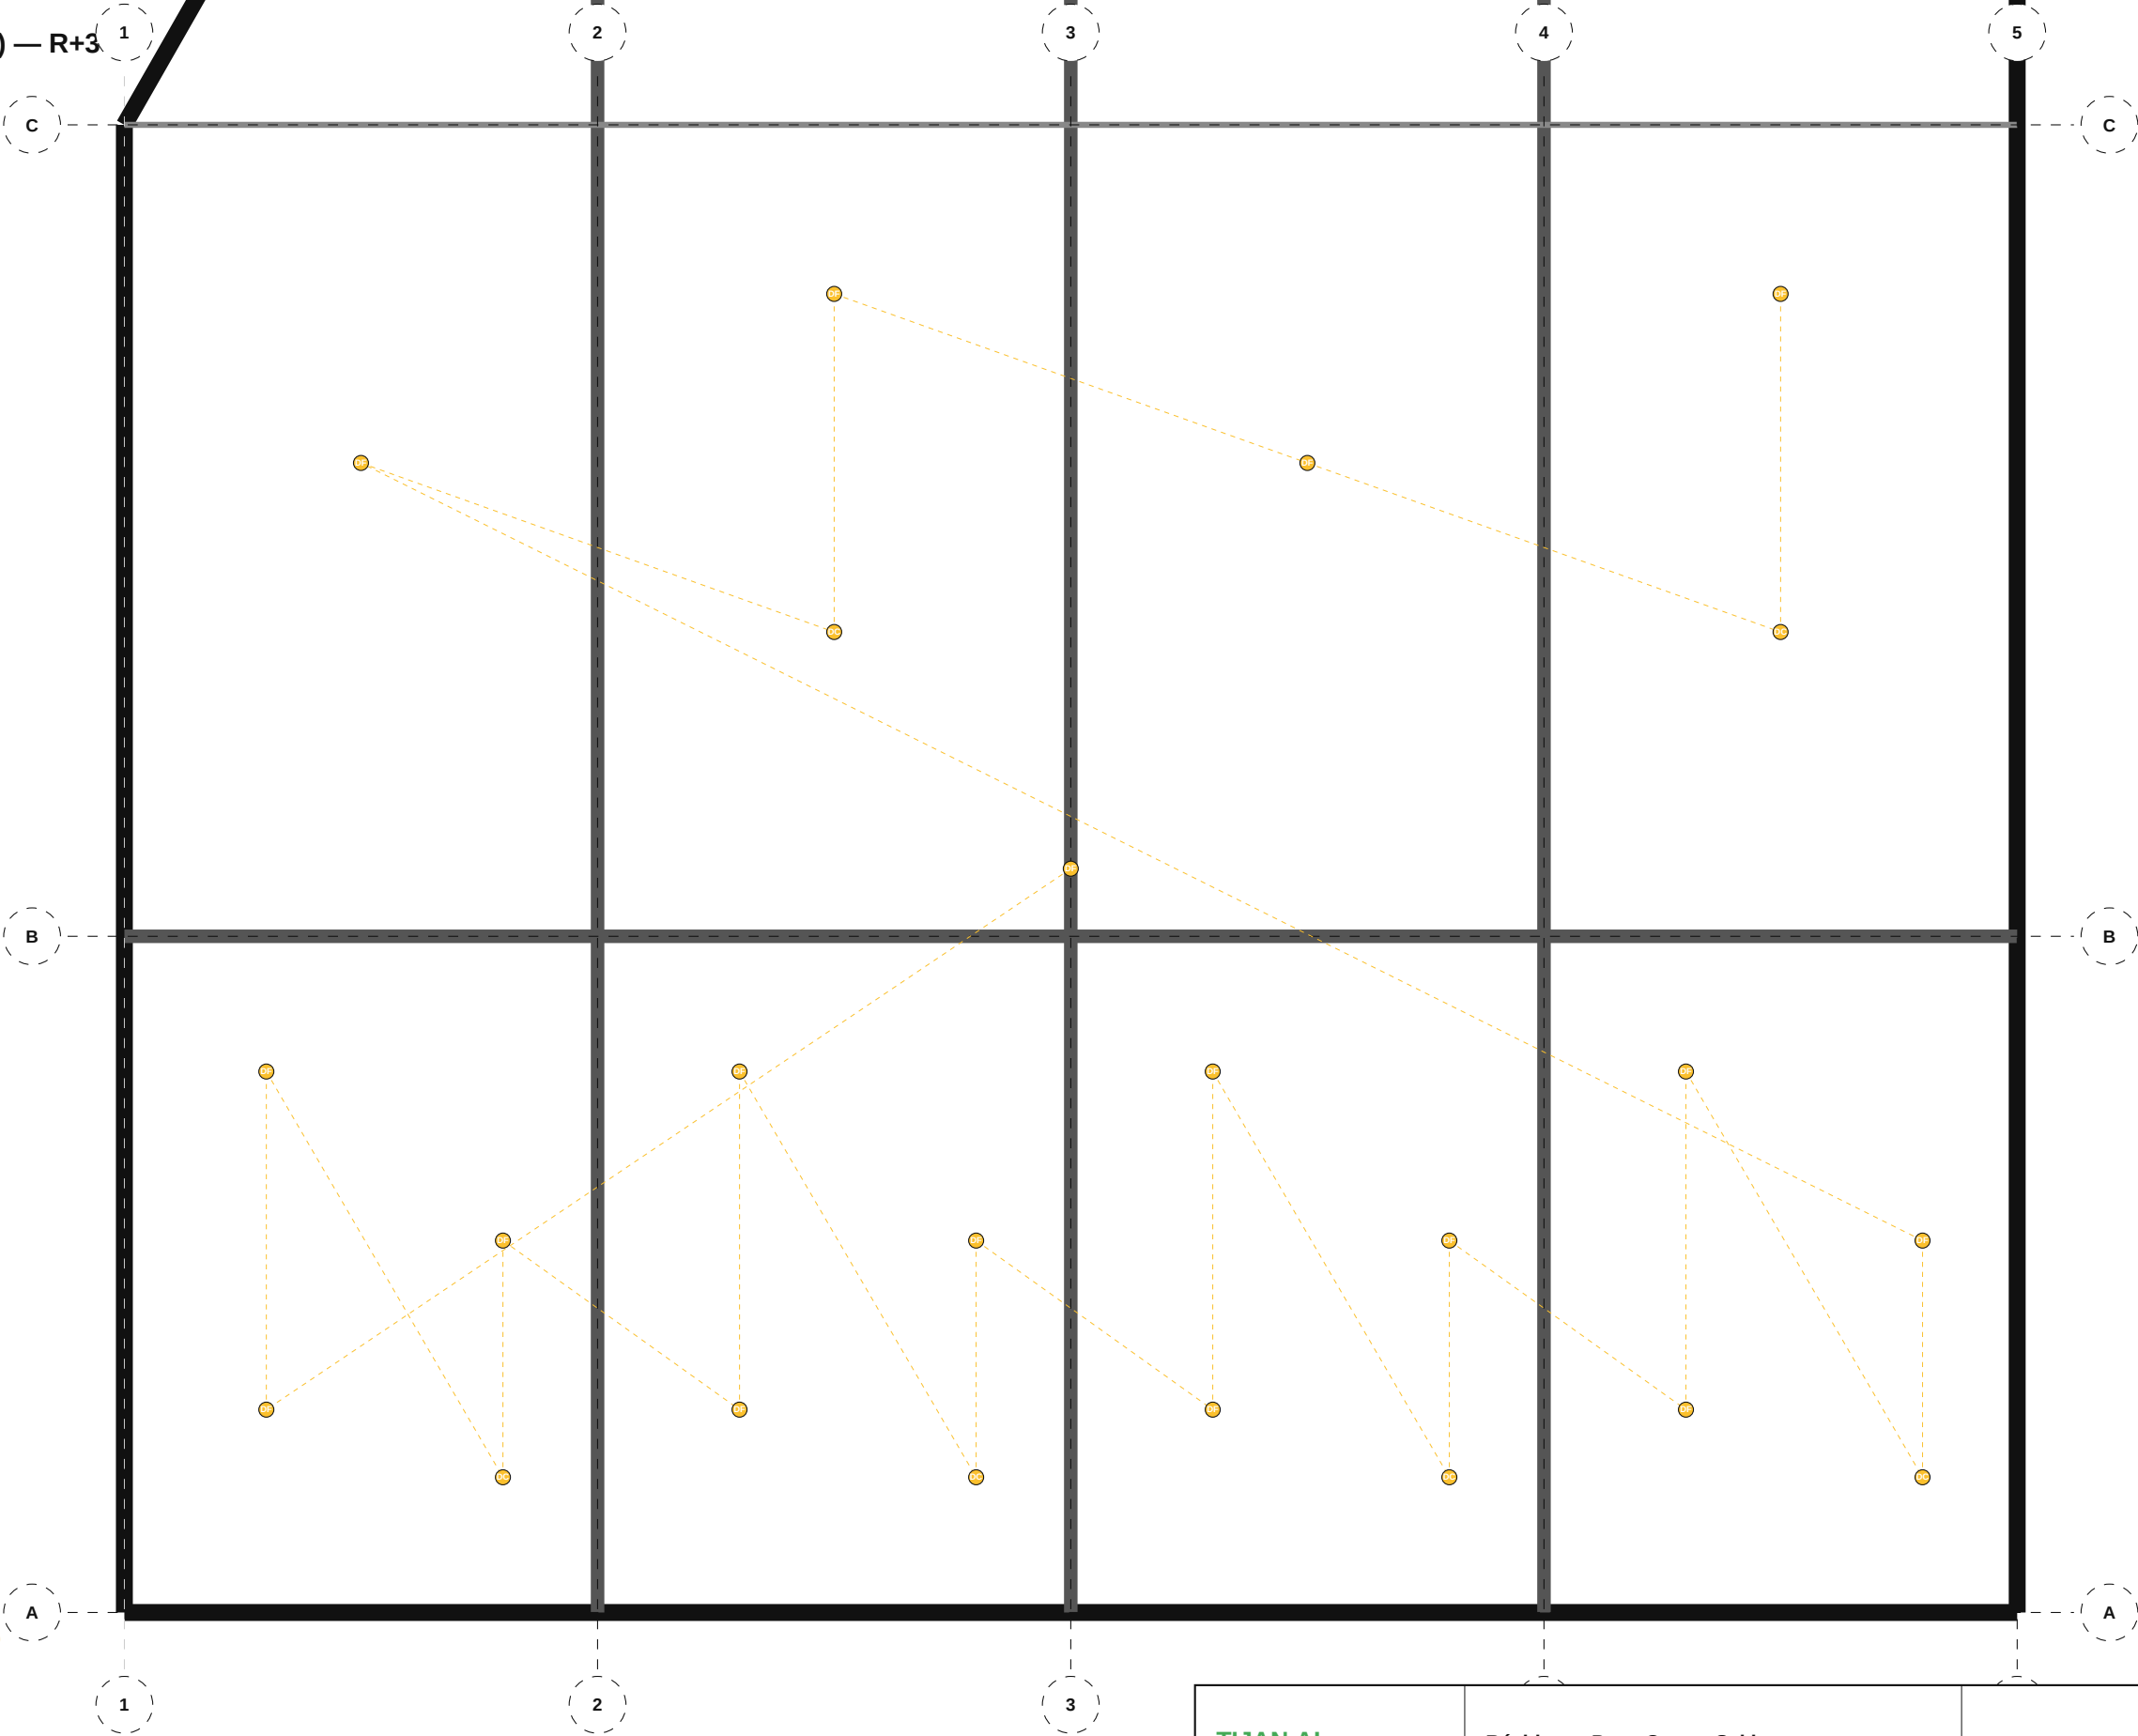

NOMENCLATURE — 400 FIF — Détection (DET)

- Détecteur de fumée: 17
- Détecteur de chaleur: 6


TIJAN AI Bureau d'Études Automatisé	Résidence Papa Oumar Sakho Dakar, Senegal	Éch: 1/100 Pl. 77/133
	400 FIF — Détection (DET) — R+3	
Date: 06/05/2026	Réf: 1711	BIM vFIF-077 Phase: APD

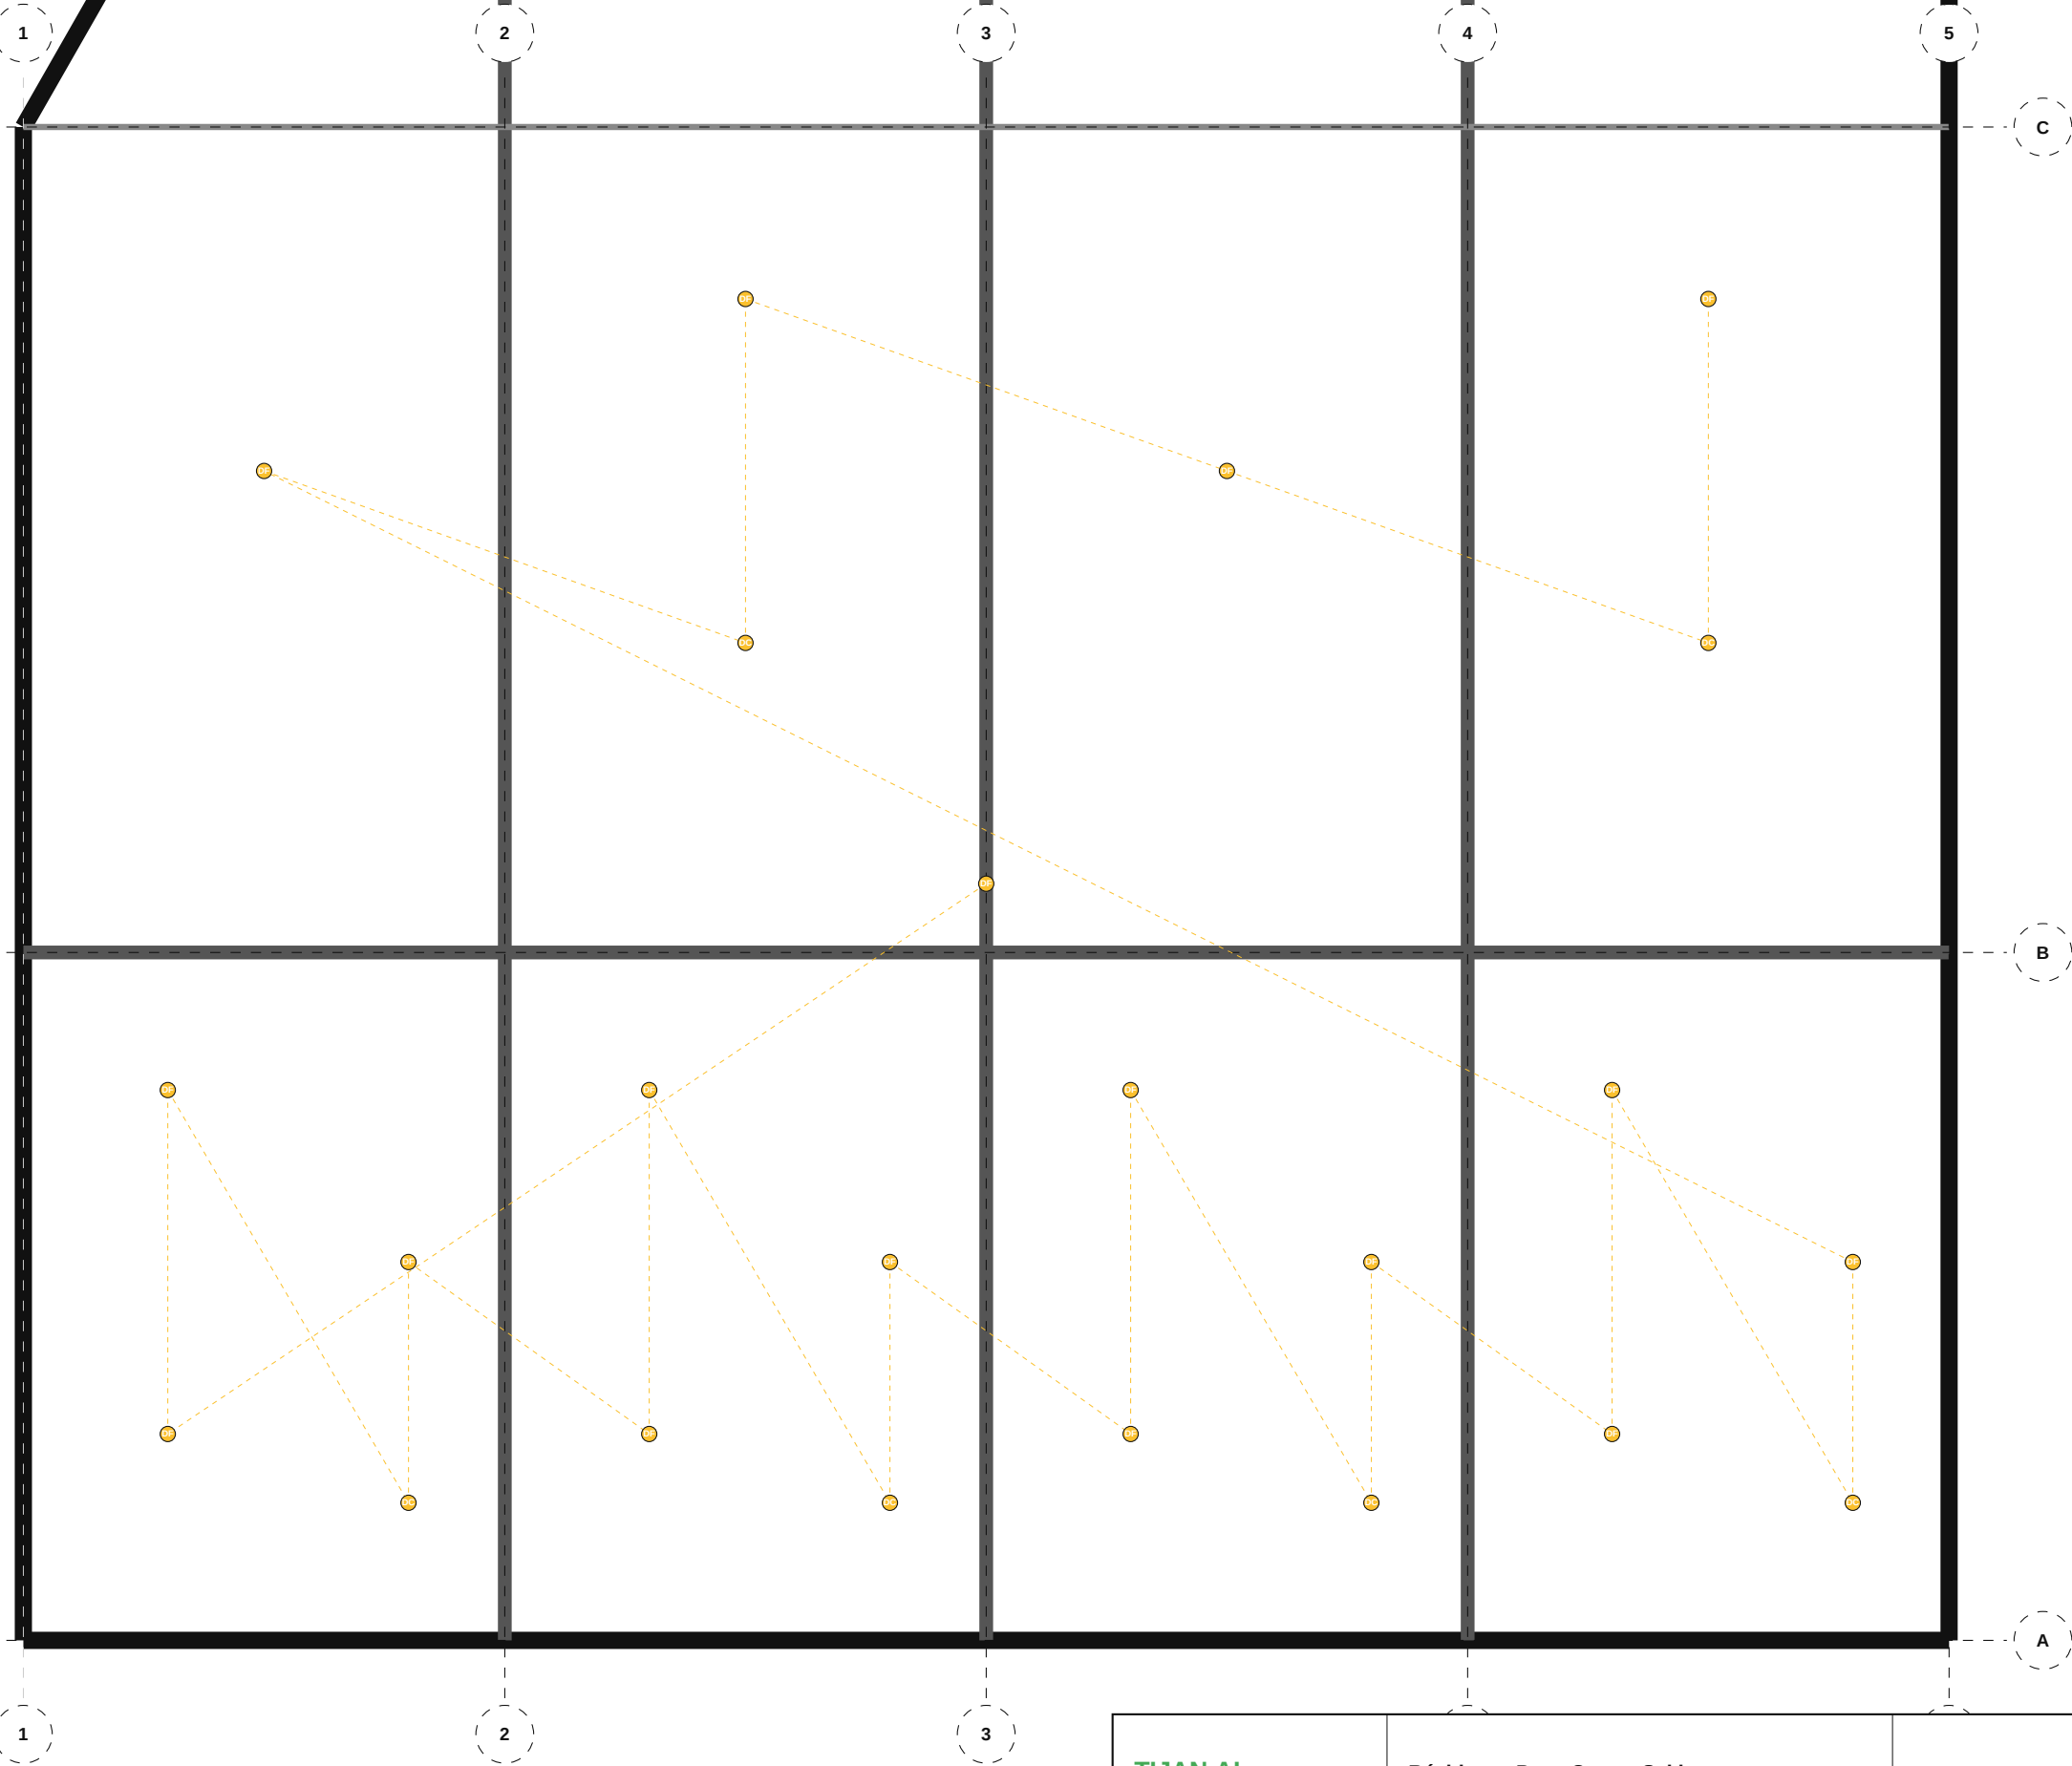

NOMENCLATURE — 400 FIF — Détection (DET)

- Détecteur de fumée: 17
- Détecteur de chaleur: 6


TIJAN AI Bureau d'Études Automatisé	Résidence Papa Oumar Sakho Dakar, Senegal	Éch: 1/100 Pl. 78/133
	400 FIF — Détection (DET) — R+4	
Date: 06/05/2026	Réf: 1711	BIM vFIF-078 Phase: APD

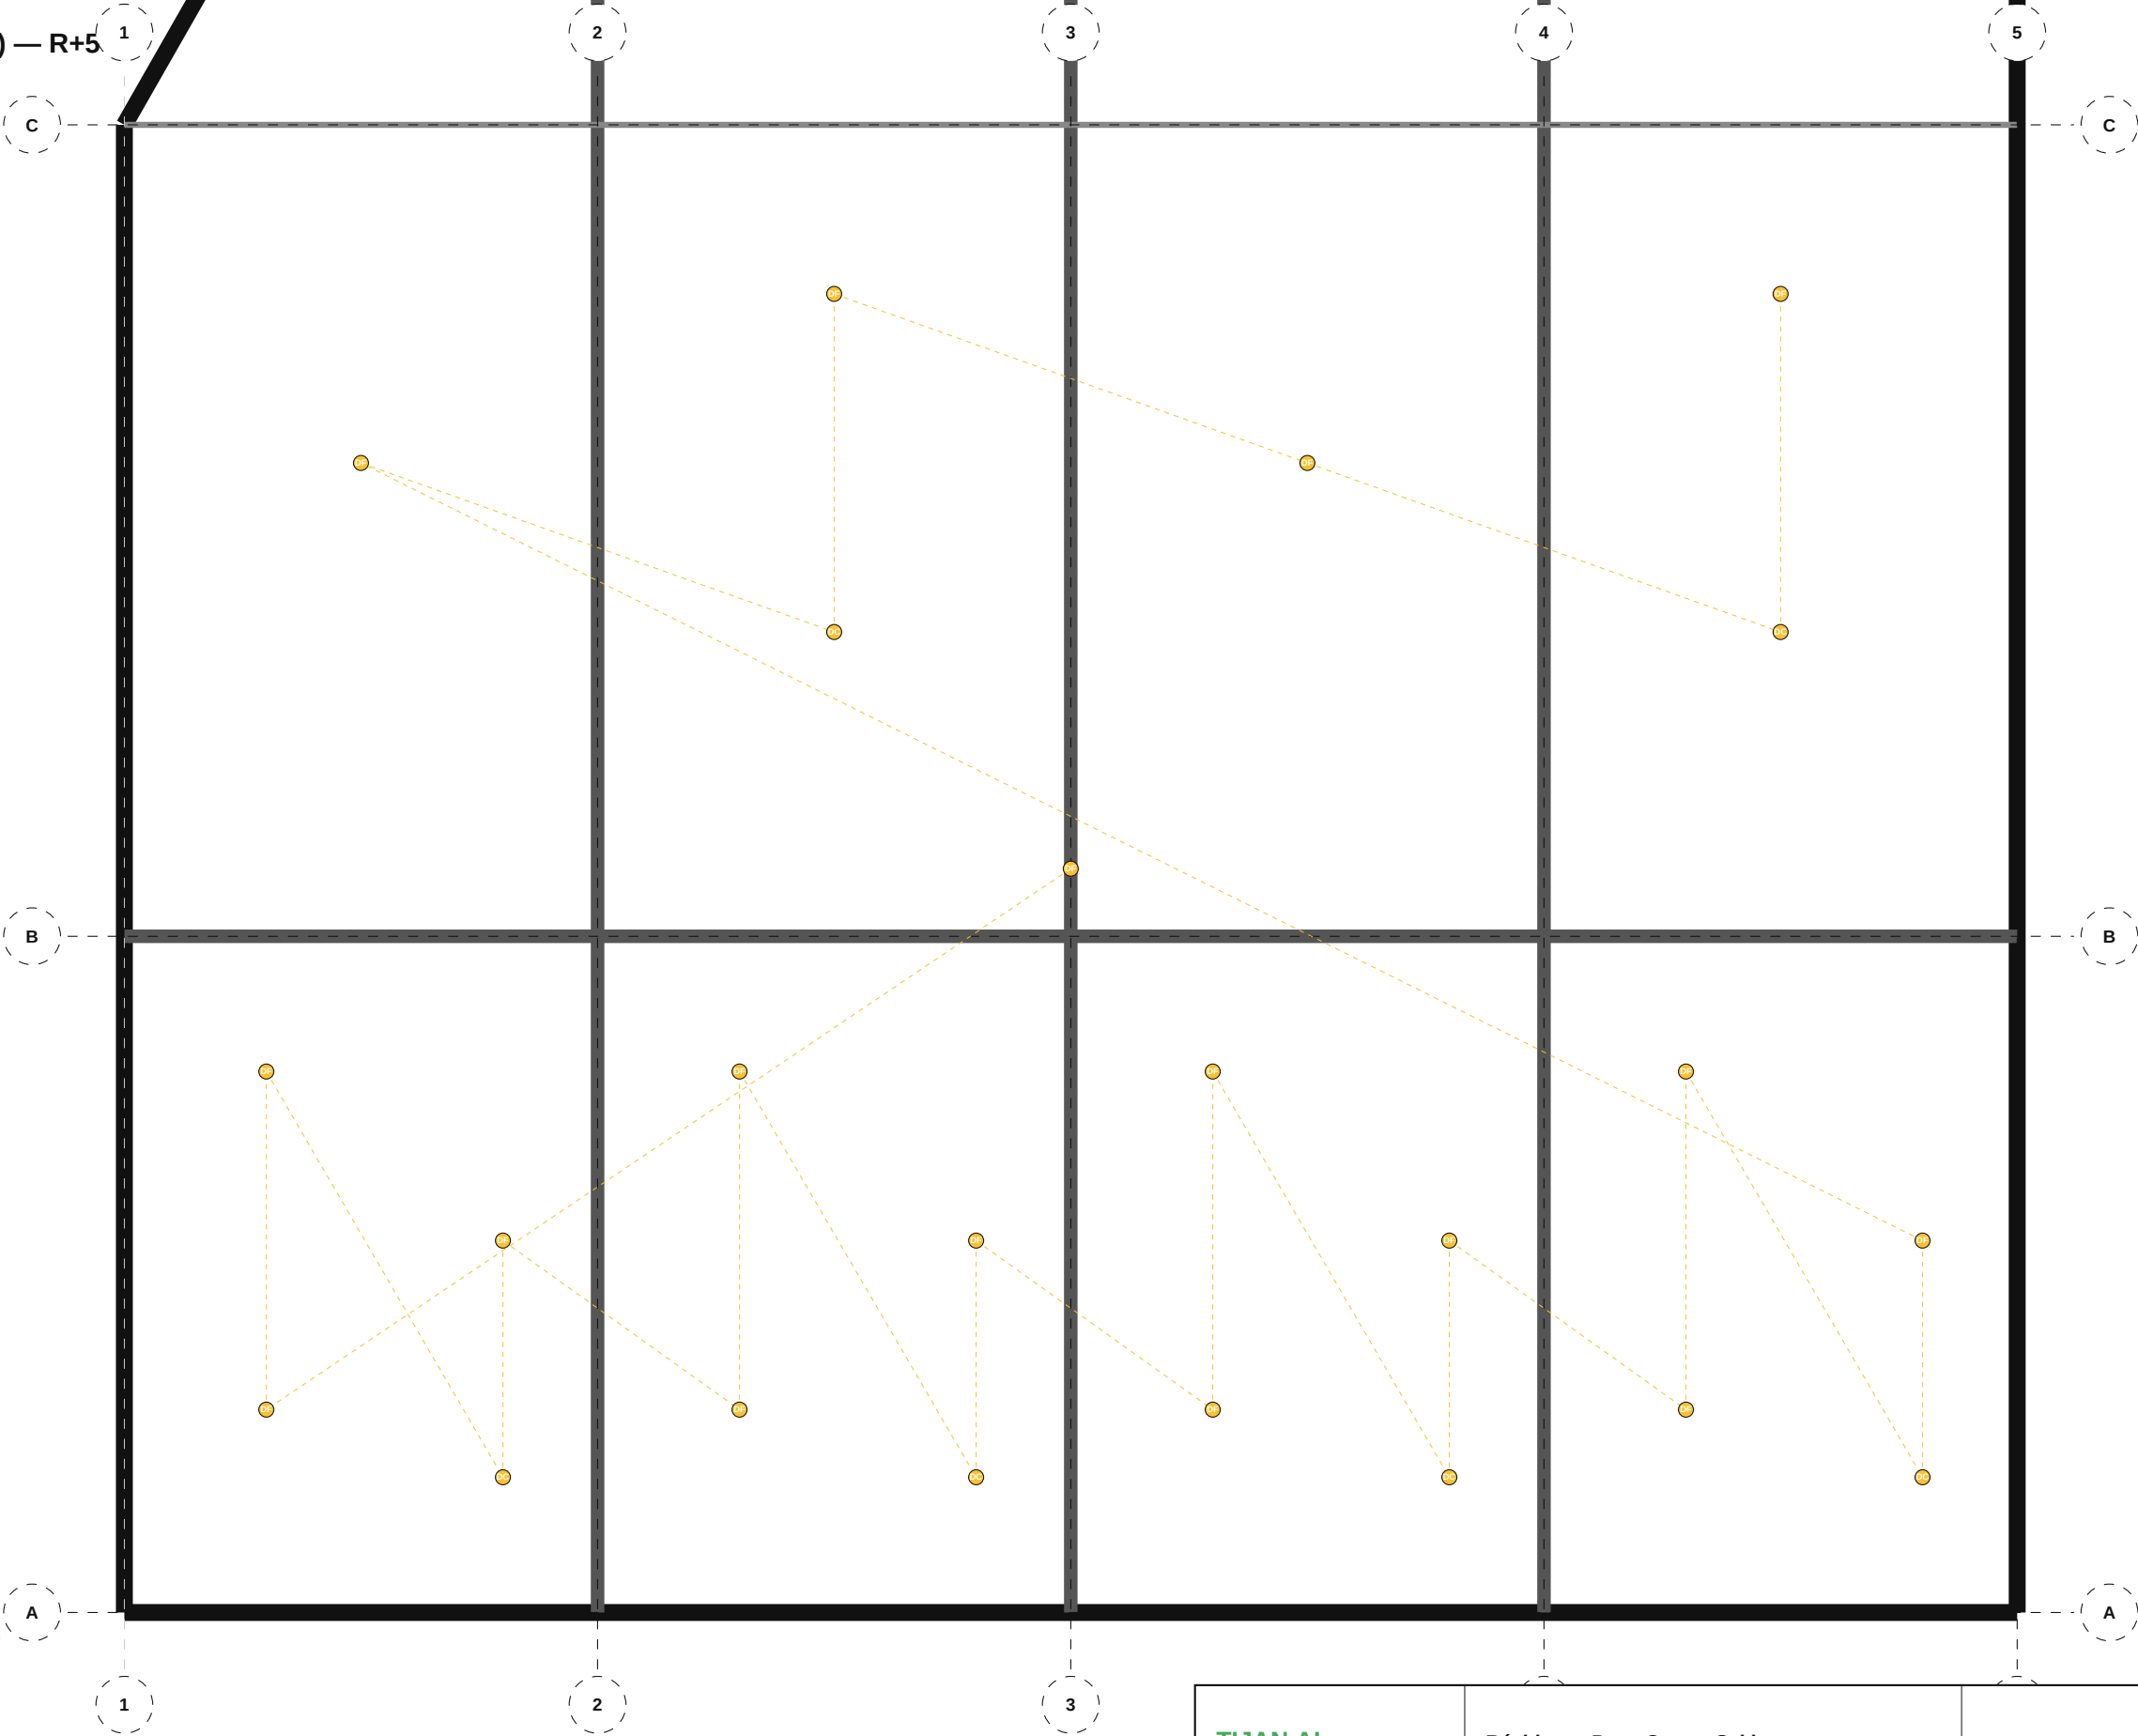

NOMENCLATURE — 400 FIF — Détection (DET)

- Détecteur de fumée: 17
- Détecteur de chaleur: 6


TIJAN AI Bureau d'Études Automatisé	Résidence Papa Oumar Sakho Dakar, Senegal	Éch: 1/100 Pl. 79/133
	400 FIF — Détection (DET) — R+5	
Date: 06/05/2026	Réf: 1711	BIM vFIF-079 Phase: APD

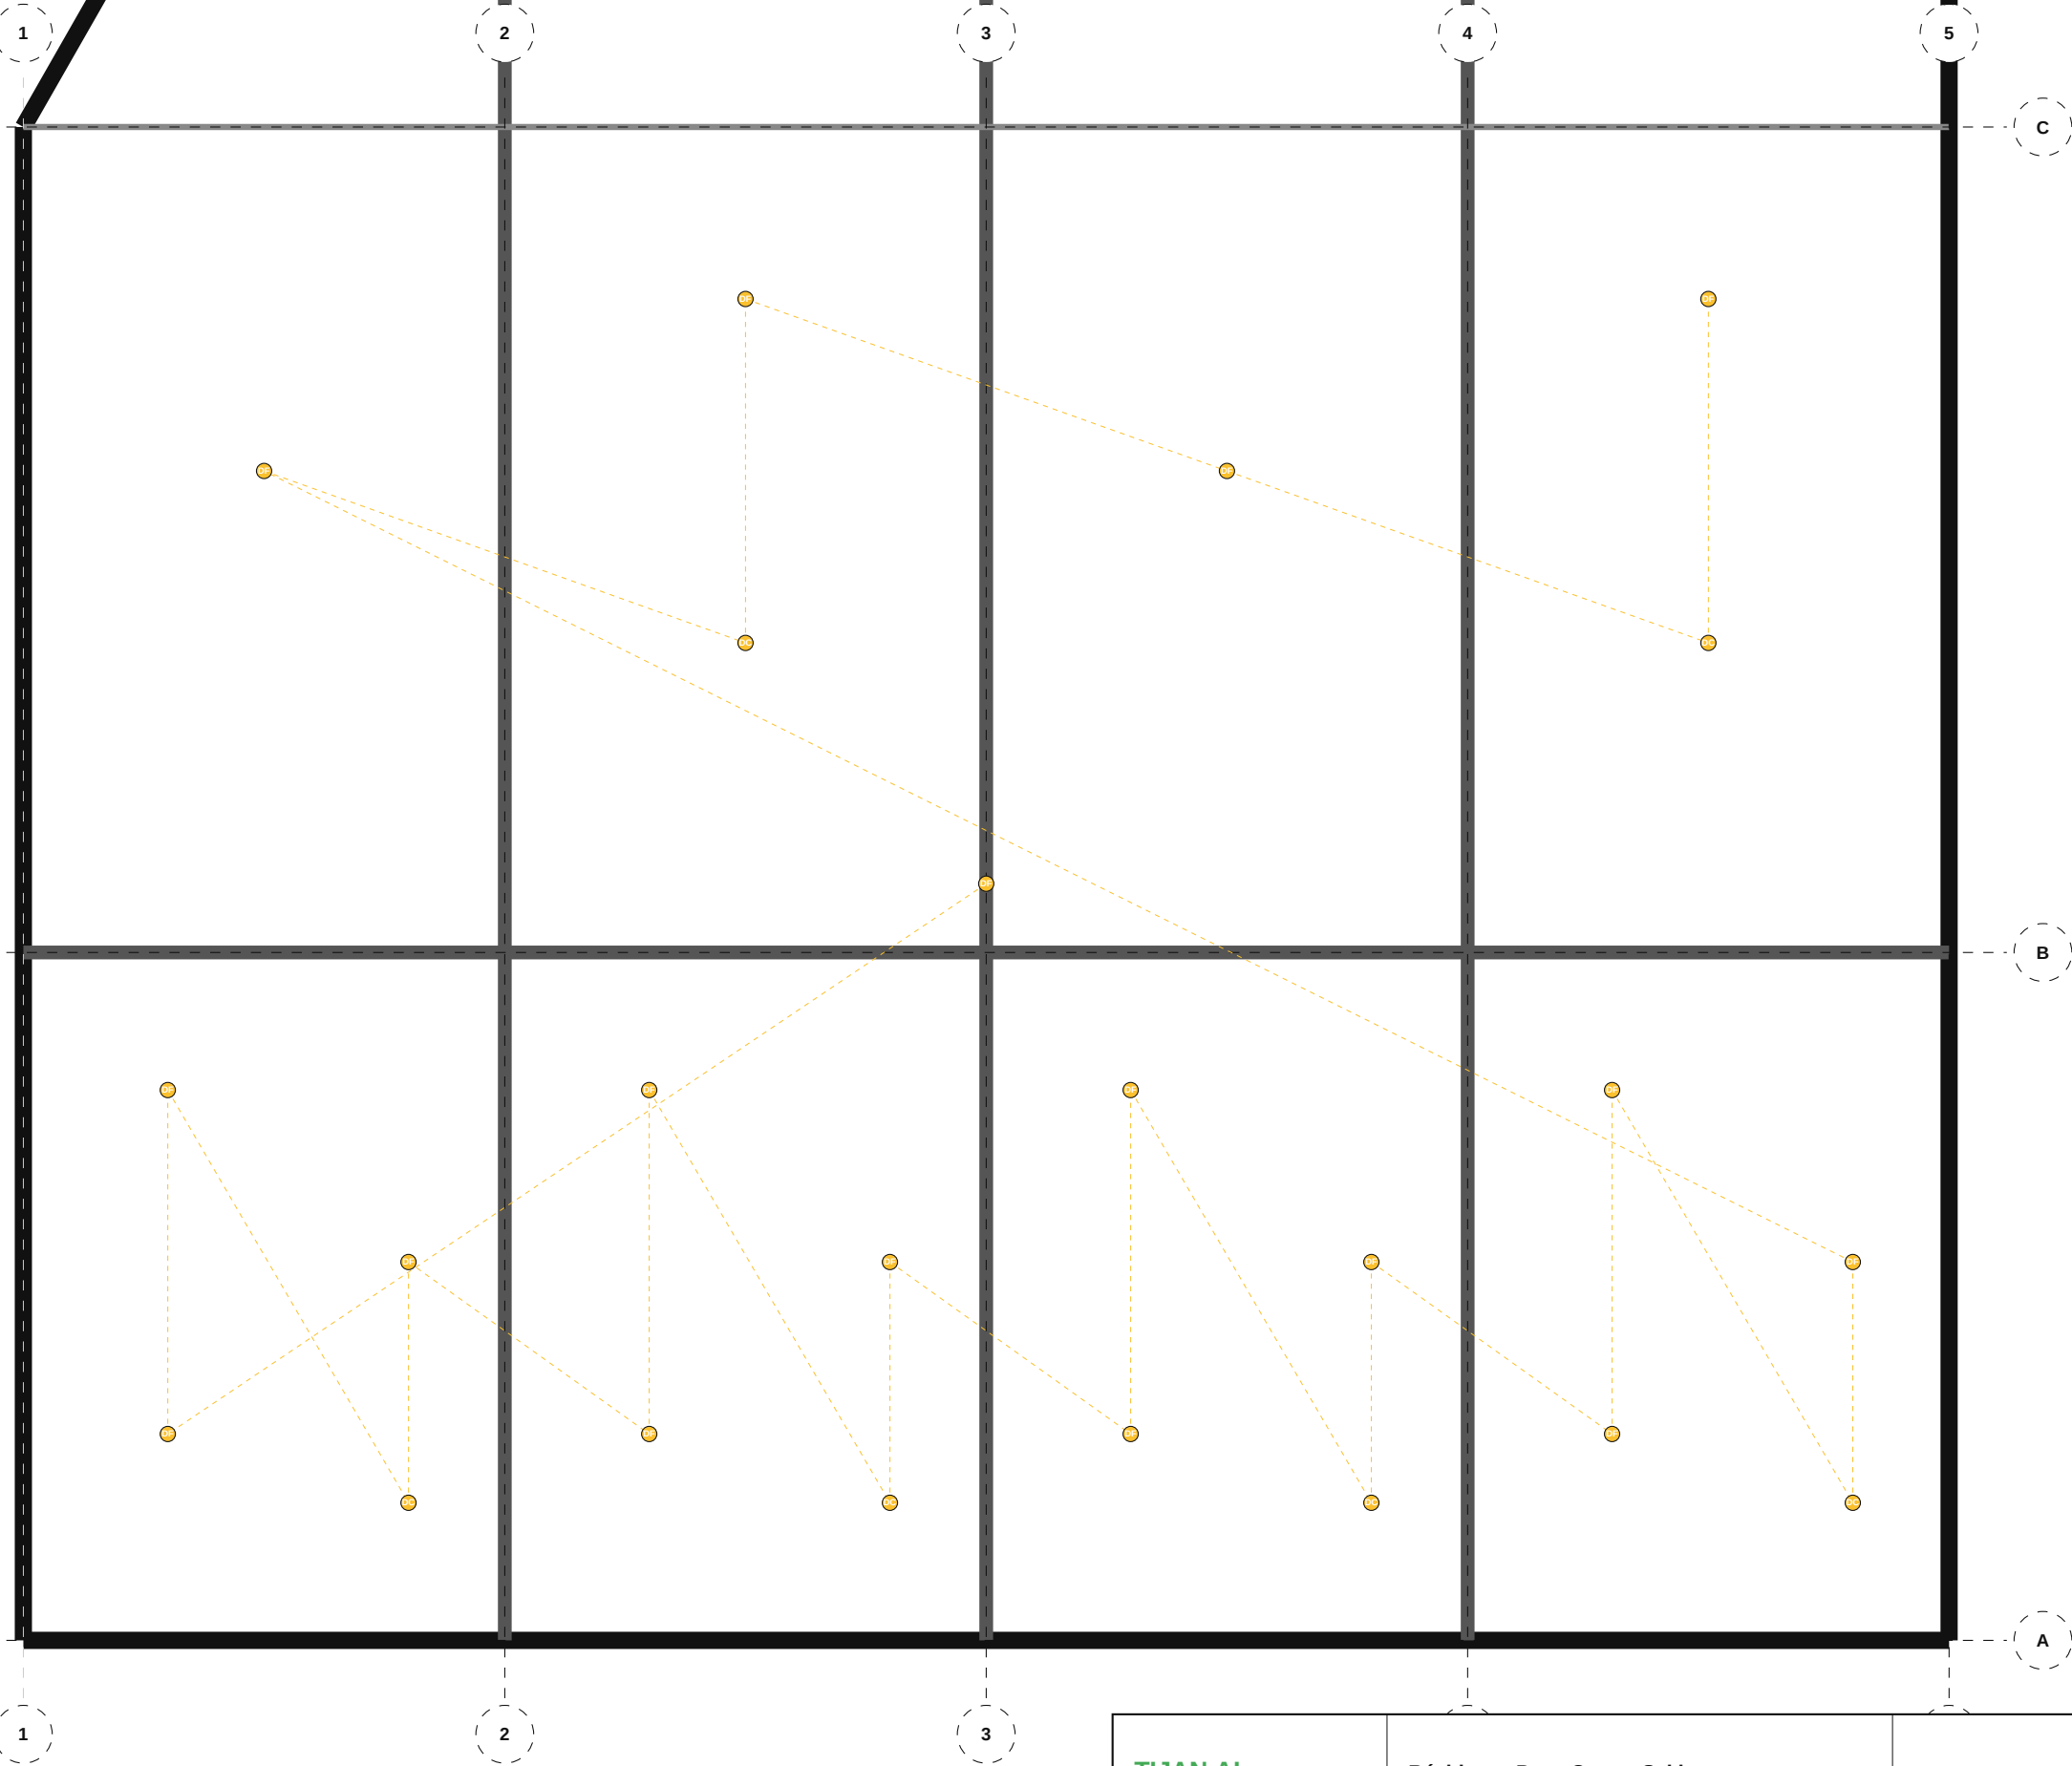

NOMENCLATURE — 400 FIF — Détection (DET)

- Détecteur de fumée: 17
- Détecteur de chaleur: 6


TIJAN AI Bureau d'Études Automatisé	Résidence Papa Oumar Sakho Dakar, Senegal	Éch: 1/100 Pl. 80/133
	400 FIF — Détection (DET) — R+6	
Date: 06/05/2026	Réf: 1711	BIM VFIF-080 Phase: APD

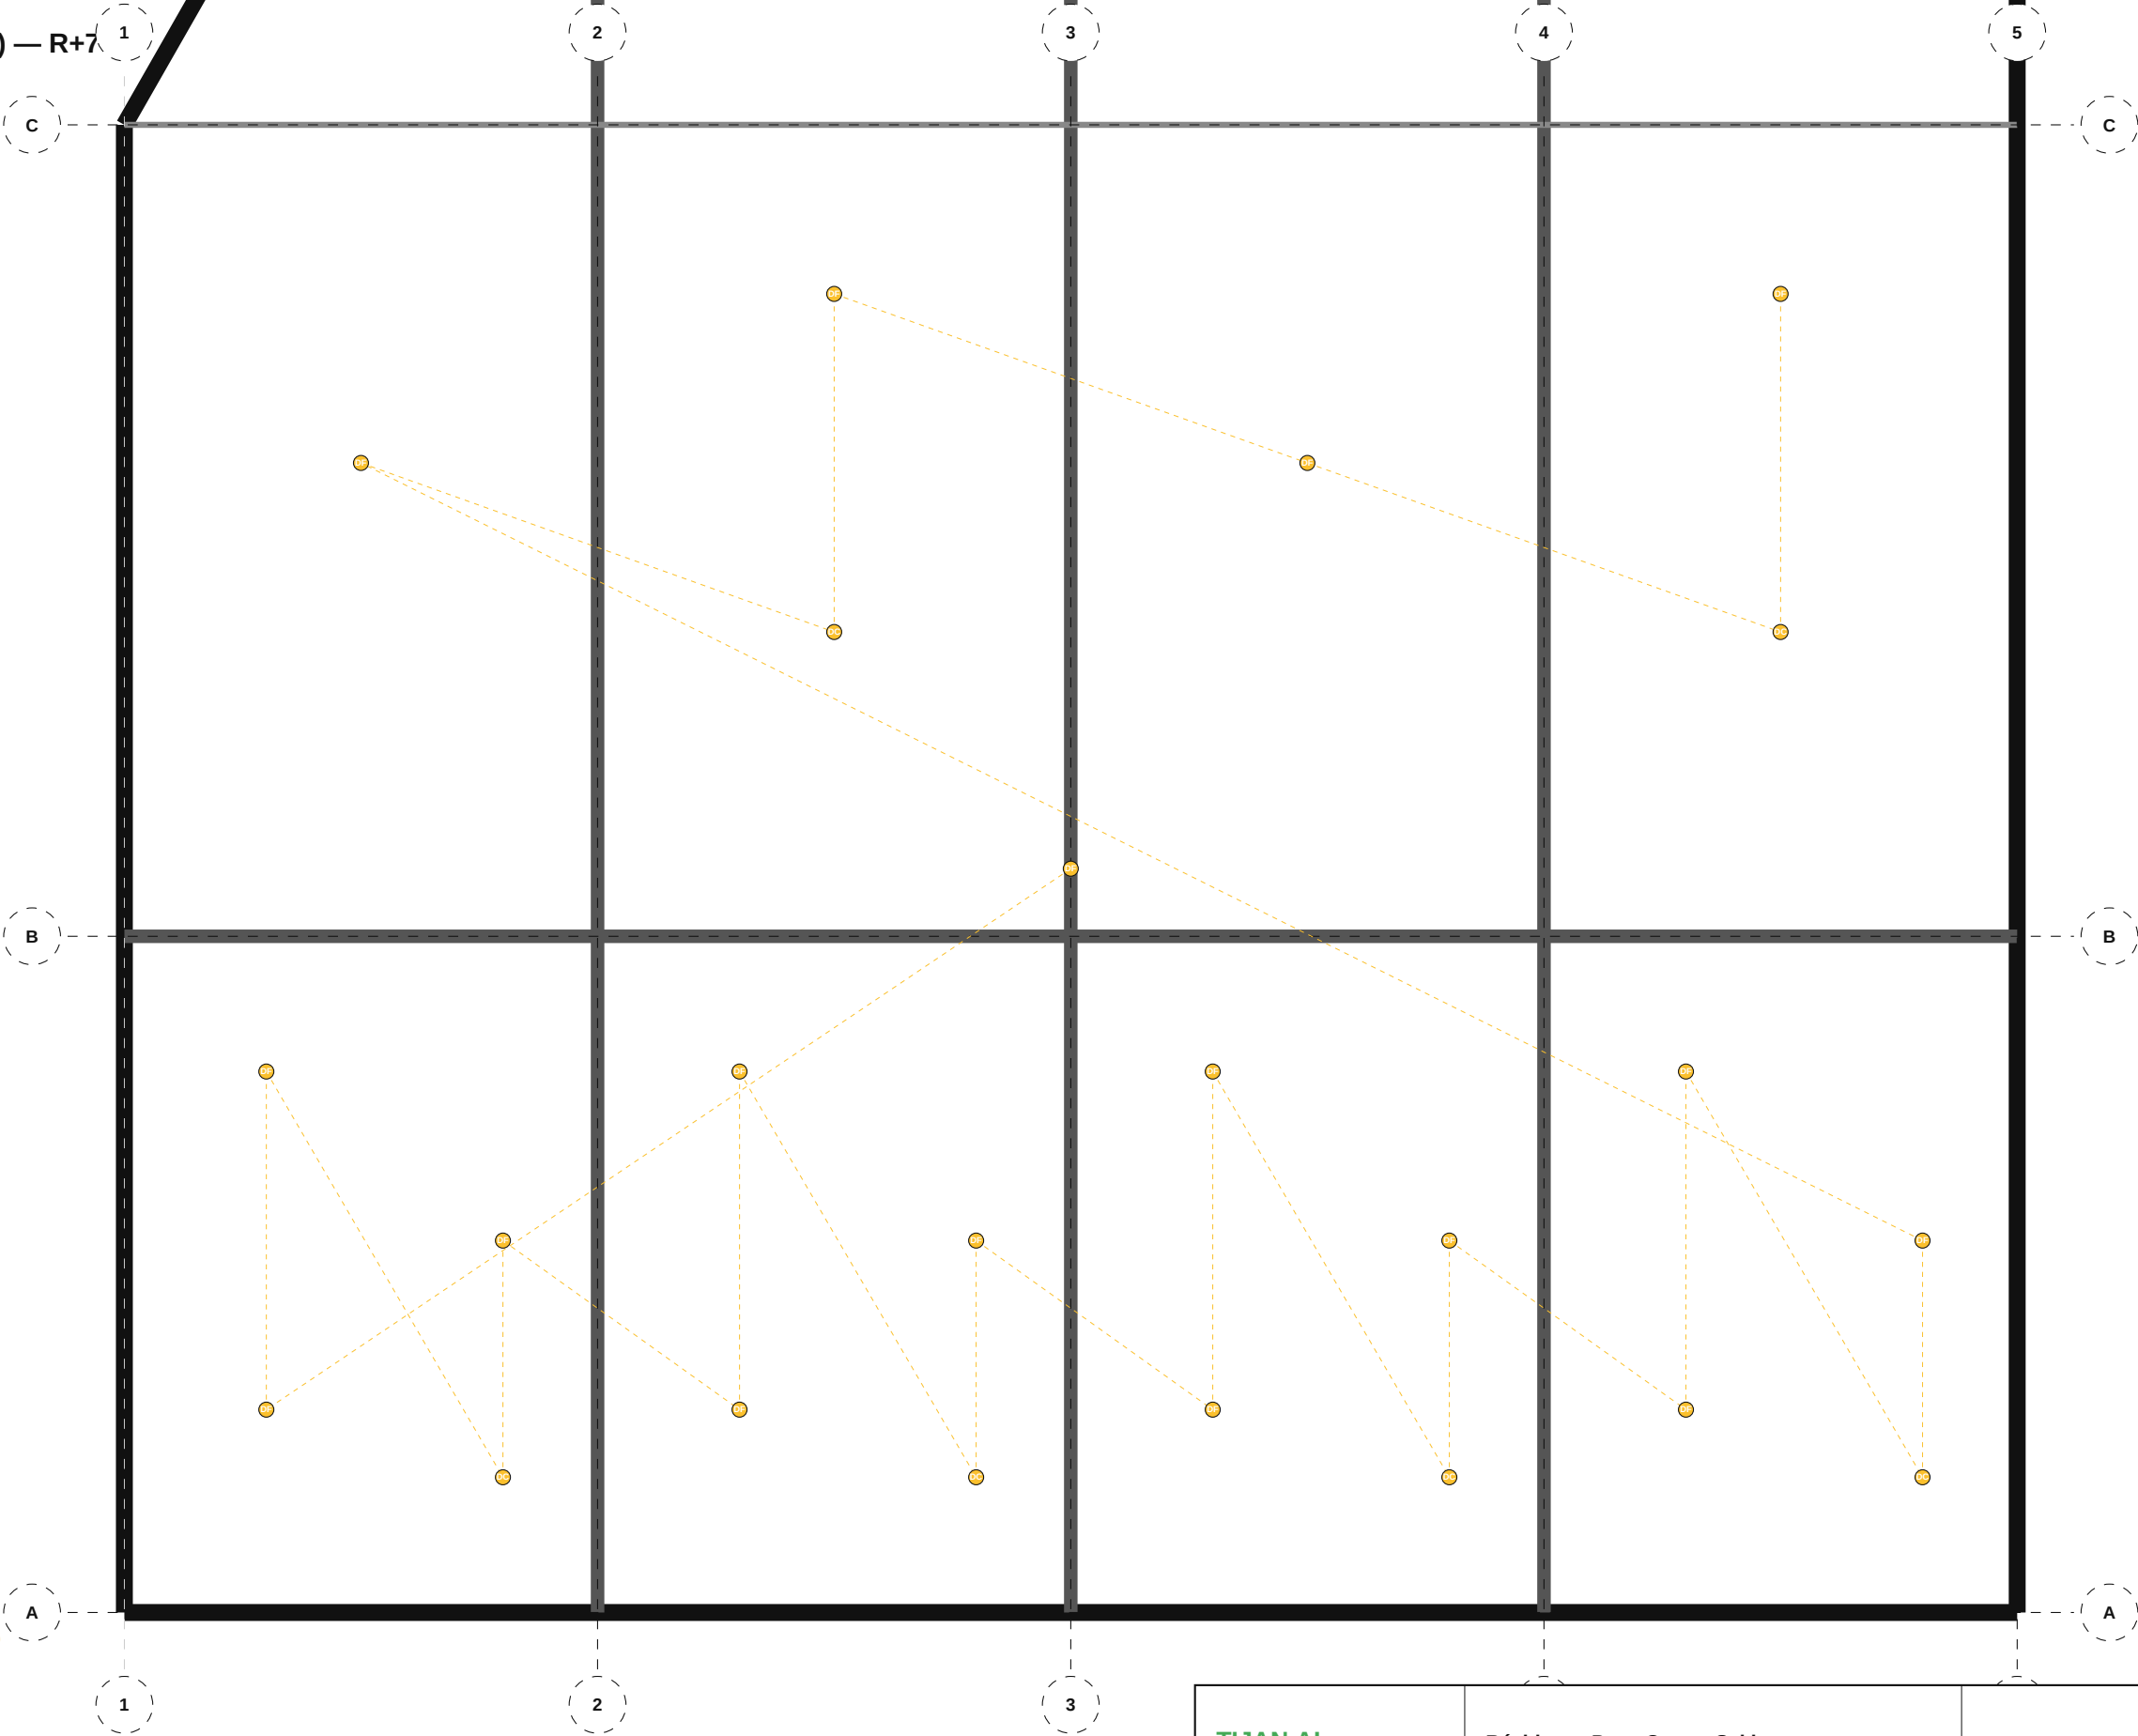

NOMENCLATURE — 400 FIF — Détection (DET)

- Détecteur de fumée: 17
- Détecteur de chaleur: 6

TIJAN AI Bureau d'Études Automatisé	Résidence Papa Oumar Sakho Dakar, Senegal	Éch: 1/100 Pl. 81/133
	400 FIF — Détection (DET) — R+7	
Date: 06/05/2026	Réf: 1711	BIM VFIF-081 Phase: APD

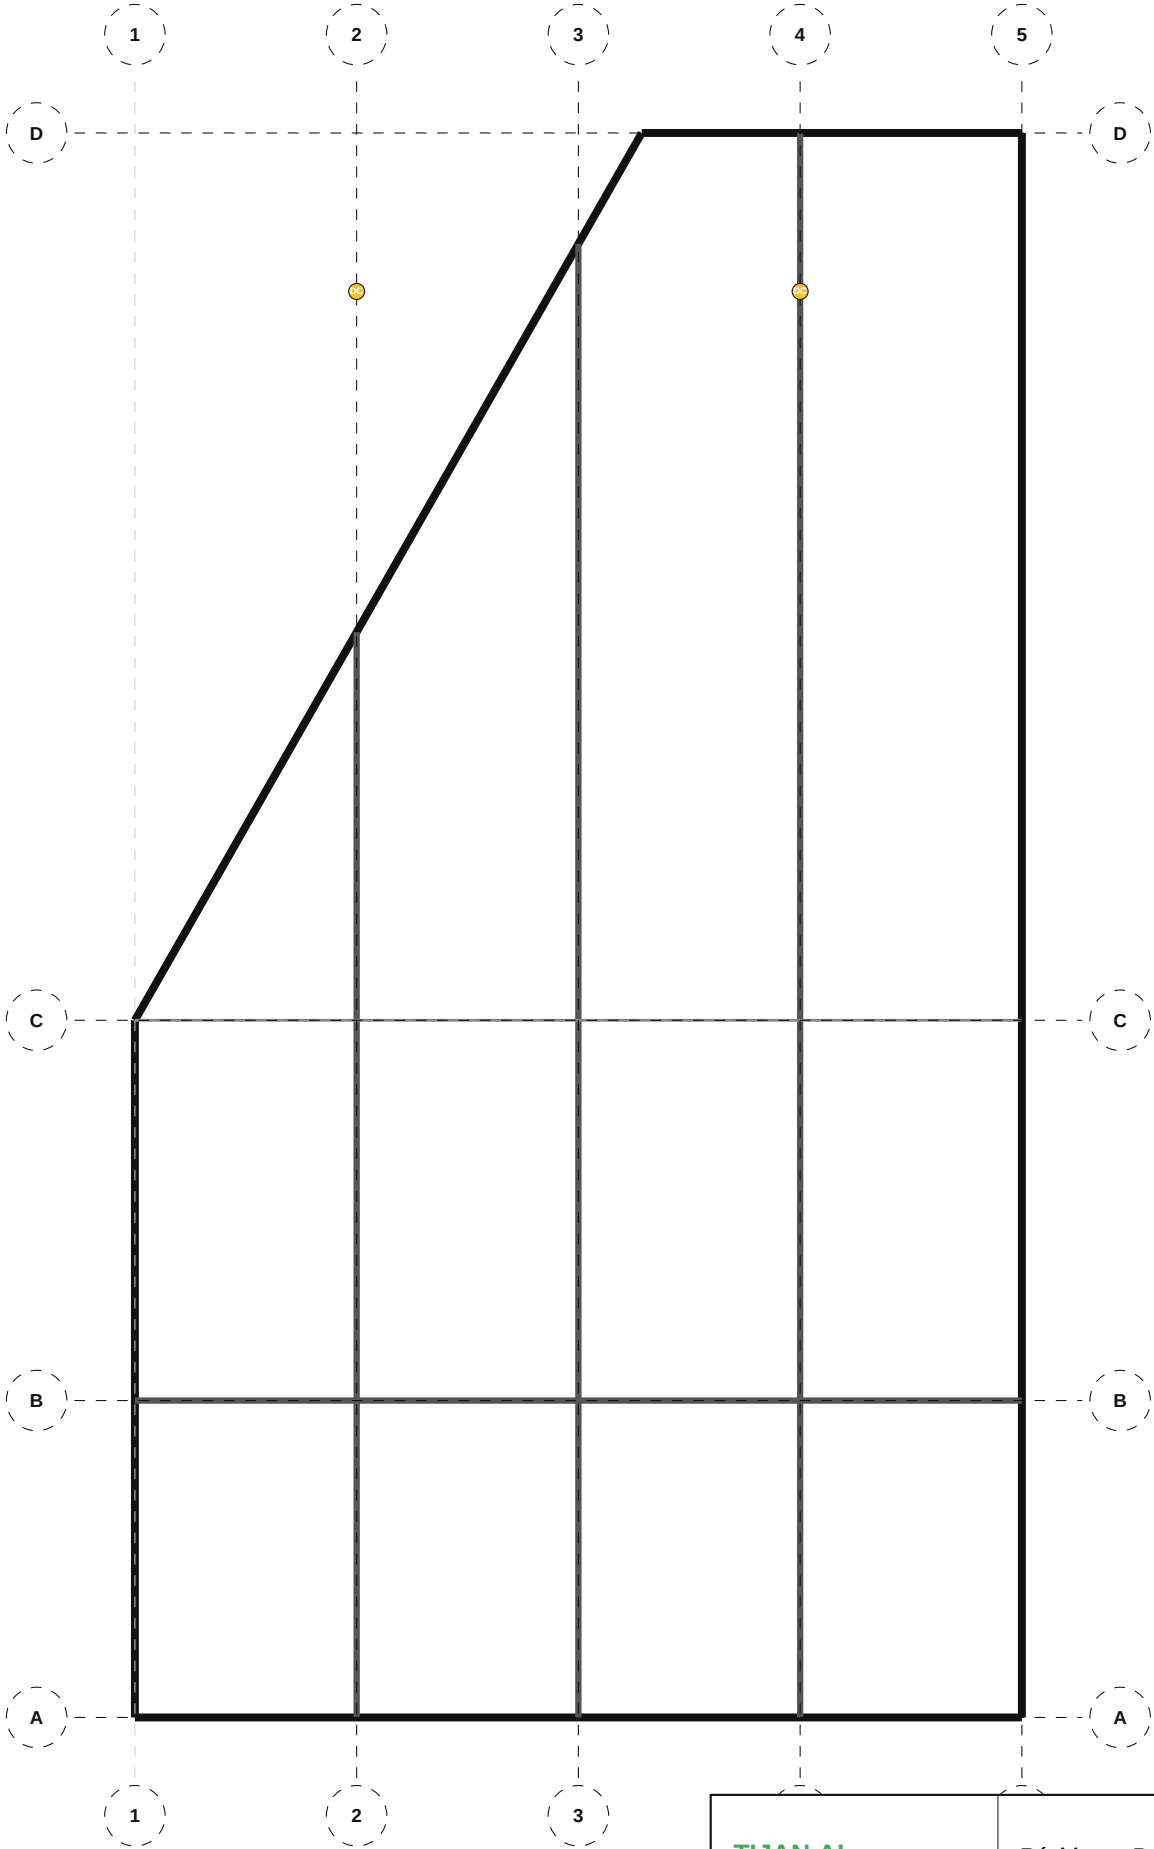


NOMENCLATURE — 400 FIF — Détection (DET)

• Détecteur de chaleur: 2

TIJAN AI Bureau d'Études Automatisé	Résidence Papa Oumar Sakho Dakar, Senegal	Éch: 1/100 Pl. 82/133
	400 FIF — Détection (DET) — R+8 Terrasse	
Date: 06/05/2026	Réf: 1711	BIM VFIF-082 Phase: APD

510 HCU — Éclairage (ECL) — Sous-Sol

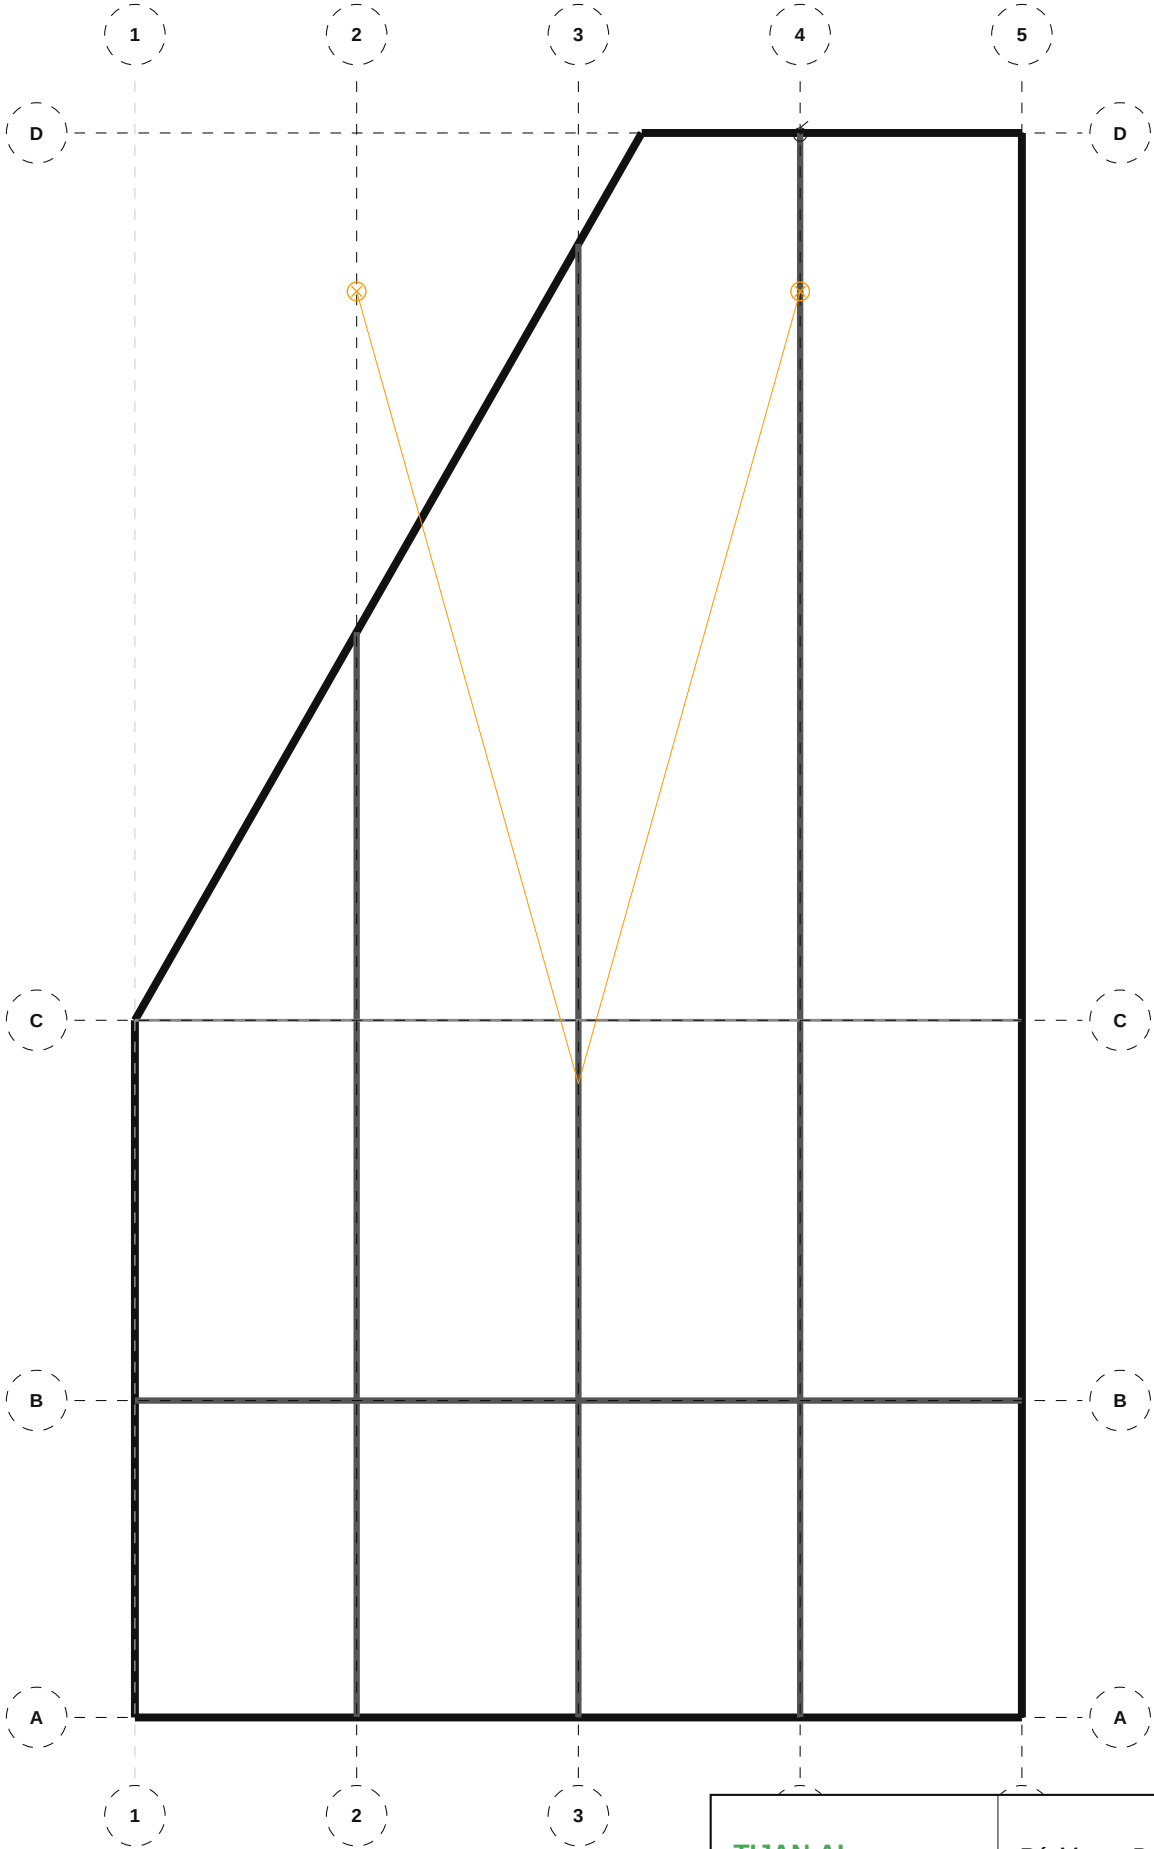

NOMENCLATURE — 510 HCU — Éclairage (ECL)

- Plafonnier: 2
- Interrupteur: 1

TIJAN AI Bureau d'Études Automatisé	Résidence Papa Oumar Sakho Dakar, Senegal	Éch: 1/100 Pl. 83/133
	510 HCU — Éclairage (ECL) — Sous-Sol	
Date: 06/05/2026	Réf: 1711	BIM vHCU-083 Phase: APD

510 HCU — Éclairage (ECL) — RDC

12345

B

B

A

A

NOMENCLATURE — 510 HCU — Éclairage (ECL)

- Plafonnier: 3
- Interrupteur va-et-vient: 2
- Interrupteur: 1

1

2

3

4

5

TIJAN AI

Bureau d'Études Automatisé

Résidence Papa Oumar Sakho

Dakar, Senegal

Éch: 1/100

Pl. 84/133


510 HCU — Éclairage (ECL) — RDC

Date: 06/05/2026

Réf: 1711

BIM vHCU-084

Phase: APD

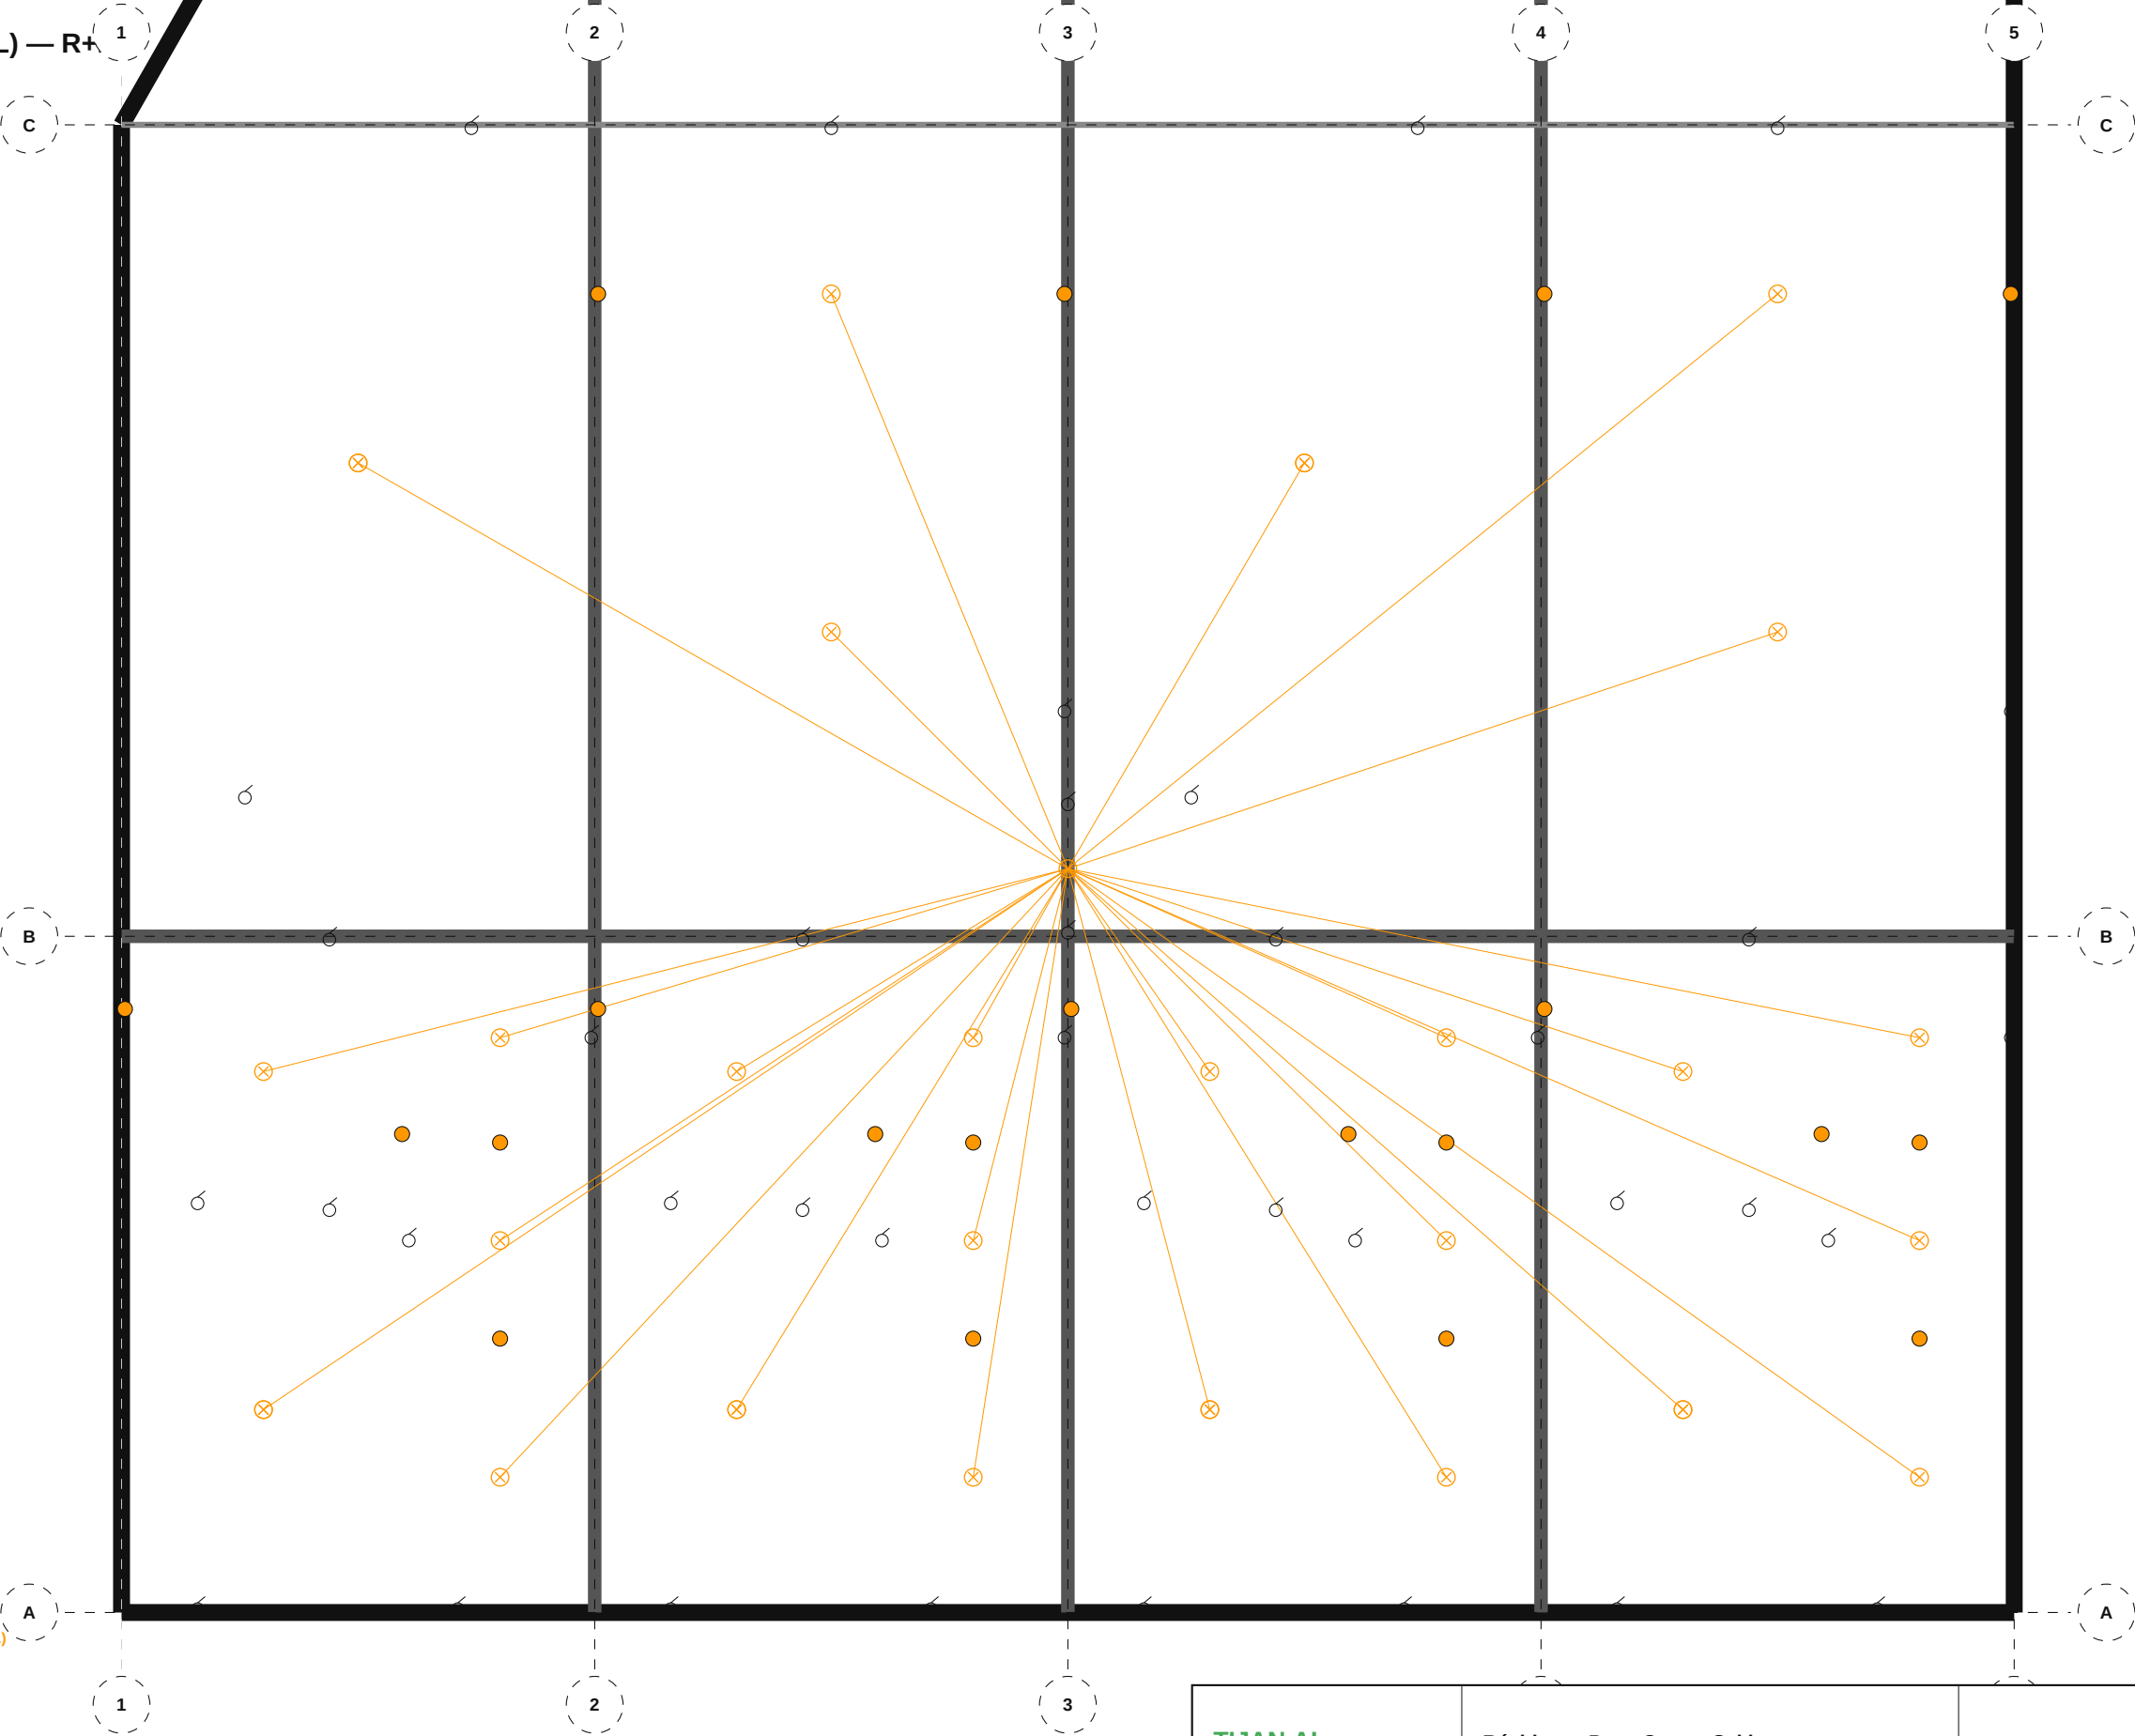

NOMENCLATURE — 510 HCU — Éclairage (ECL)

- Plafonnier: 27
- Interrupteur va-et-vient: 22
- Interrupteur: 16
- Applique miroir: 12
- Applique tête de lit: 8
- Plafonnier IP44: 6

TIJAN AI

Bureau d'Études Automatisé

Résidence Papa Oumar Sakho

Dakar, Senegal

Éch: 1/100

Pl. 85/133


510 HCU — Éclairage (ECL) — R+1

Date: 06/05/2026

Réf: 1711

BIM vHCU-085

Phase: APD

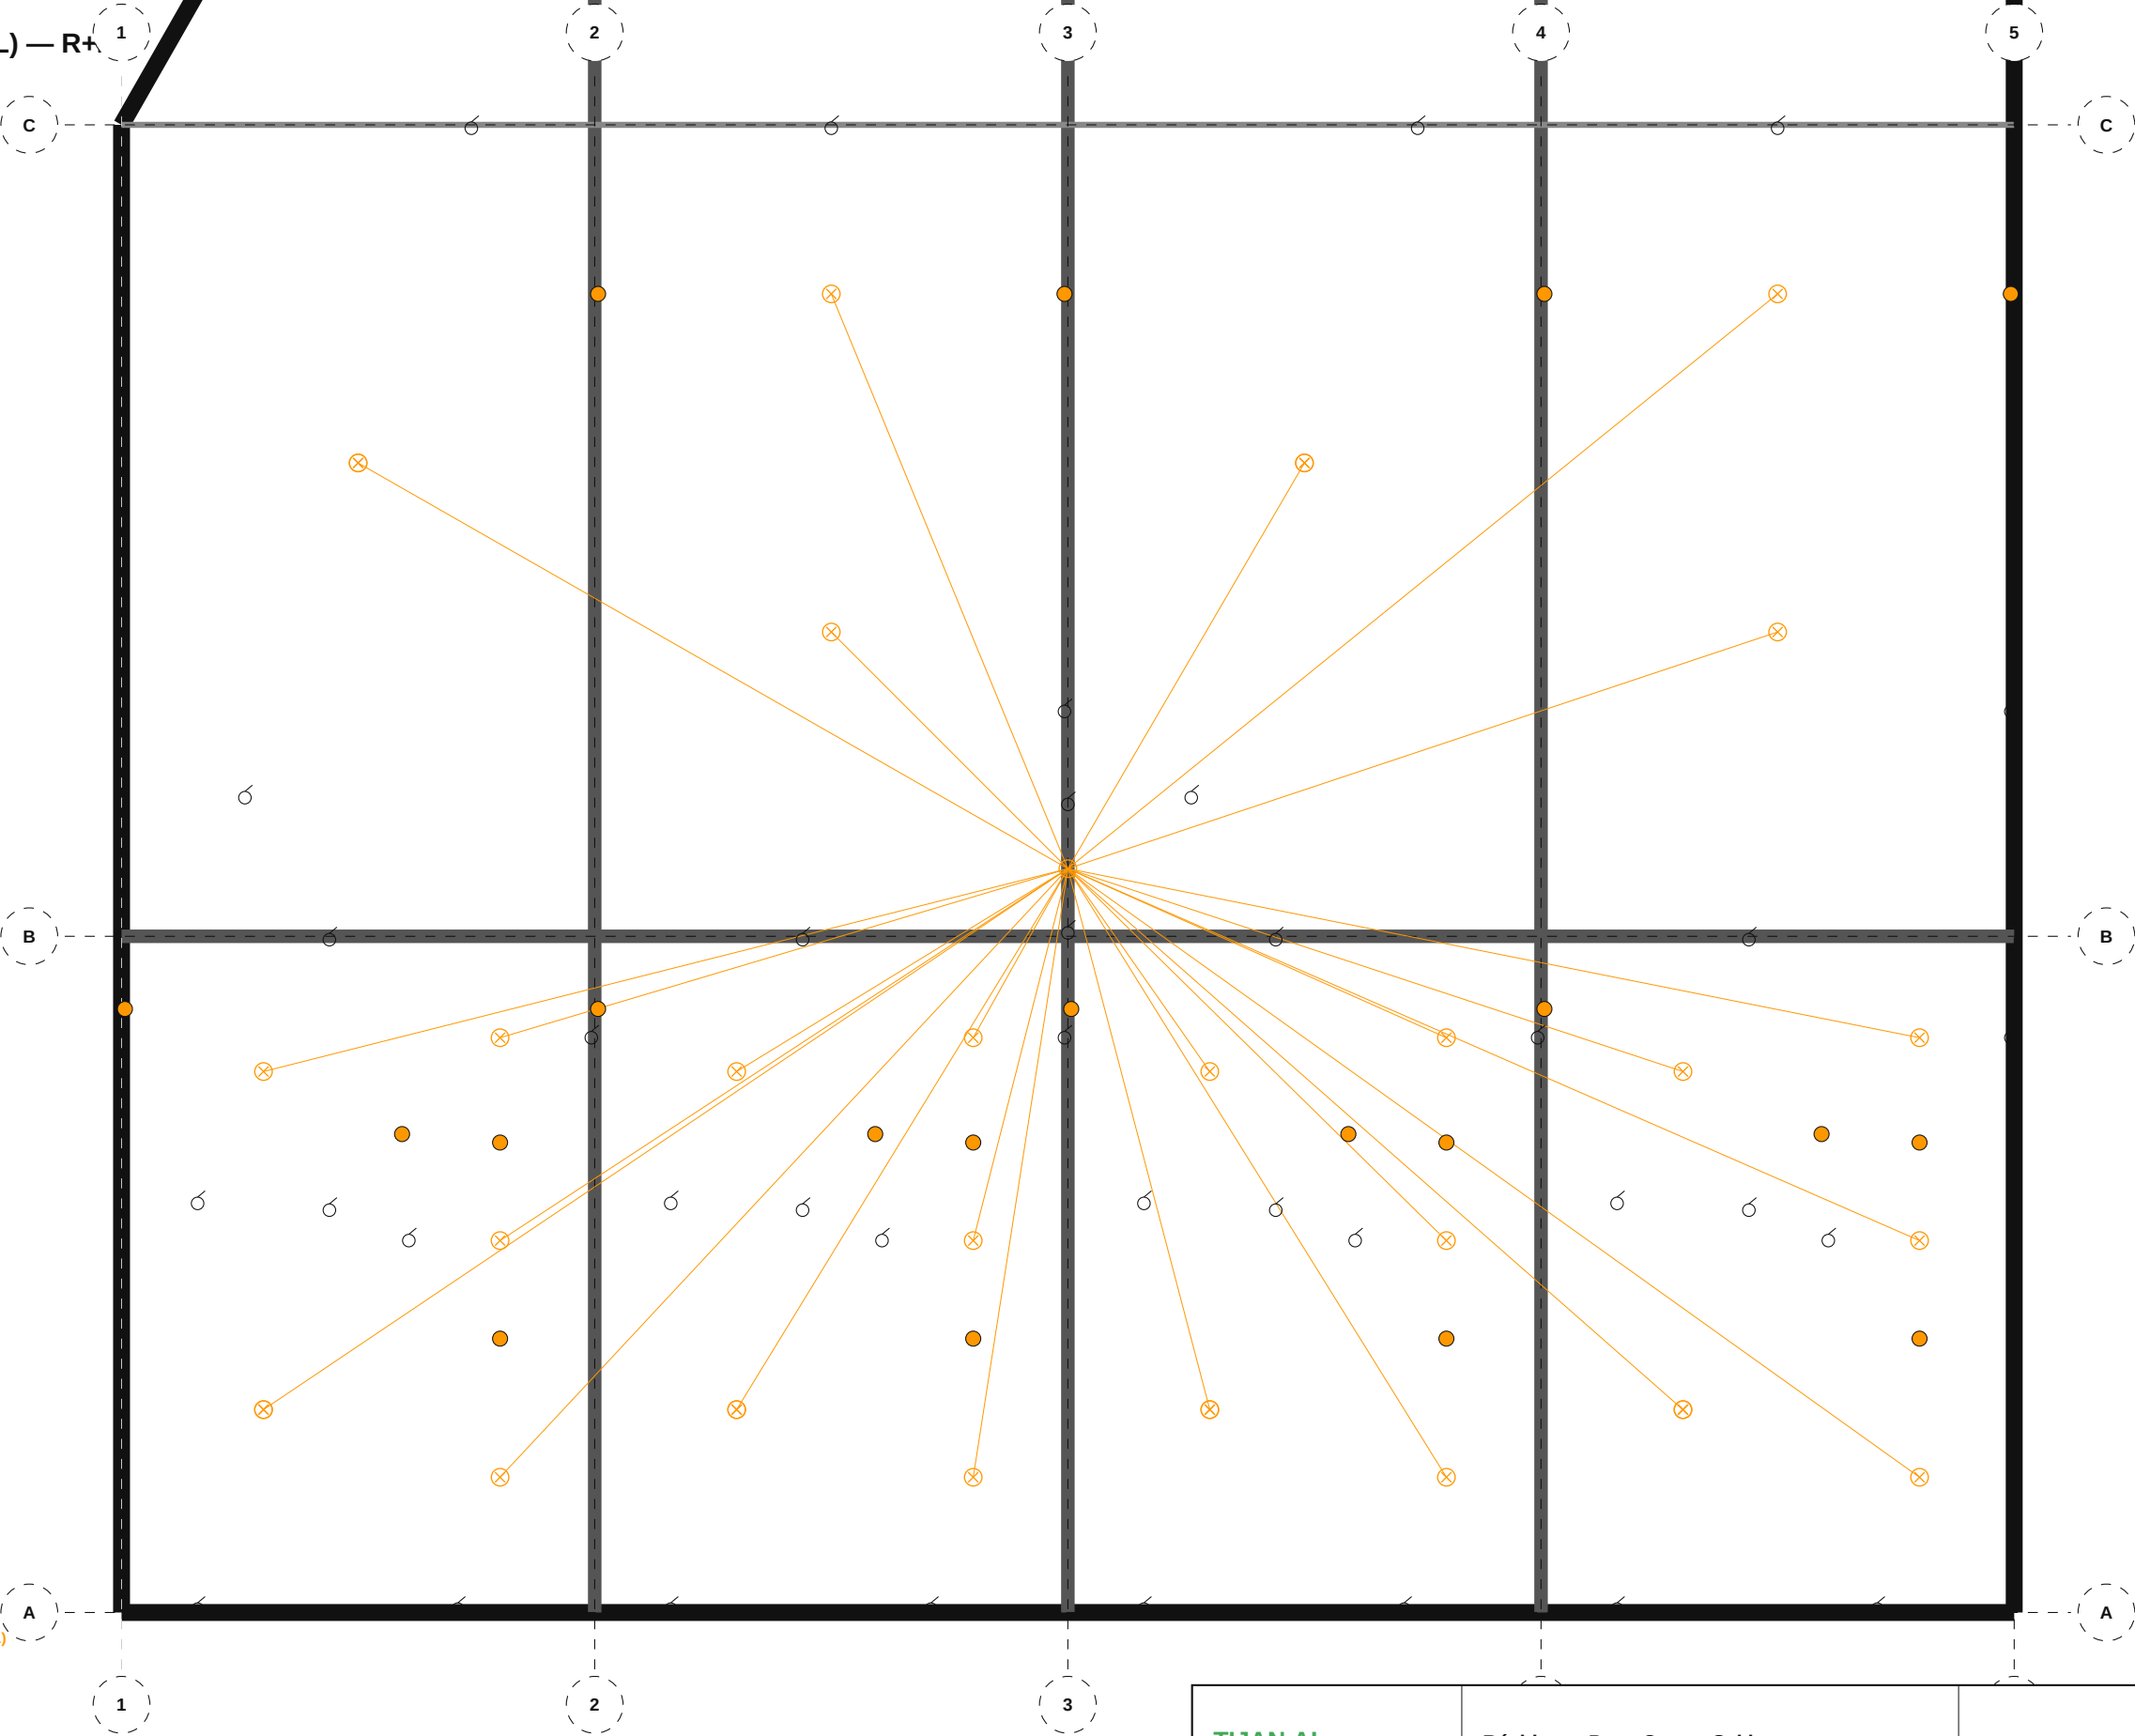

NOMENCLATURE — 510 HCU — Éclairage (ECL)

- Plafonnier: 27
- Interrupteur va-et-vient: 22
- Interrupteur: 16
- Applique miroir: 12
- Applique tête de lit: 8
- Plafonnier IP44: 6

TIJAN AI

Bureau d'Études Automatisé

Résidence Papa Oumar Sakho

Dakar, Senegal

Éch: 1/100

Pl. 86/133


510 HCU — Éclairage (ECL) — R+2

Date: 06/05/2026

Réf: 1711

BIM vHCU-086

Phase: APD

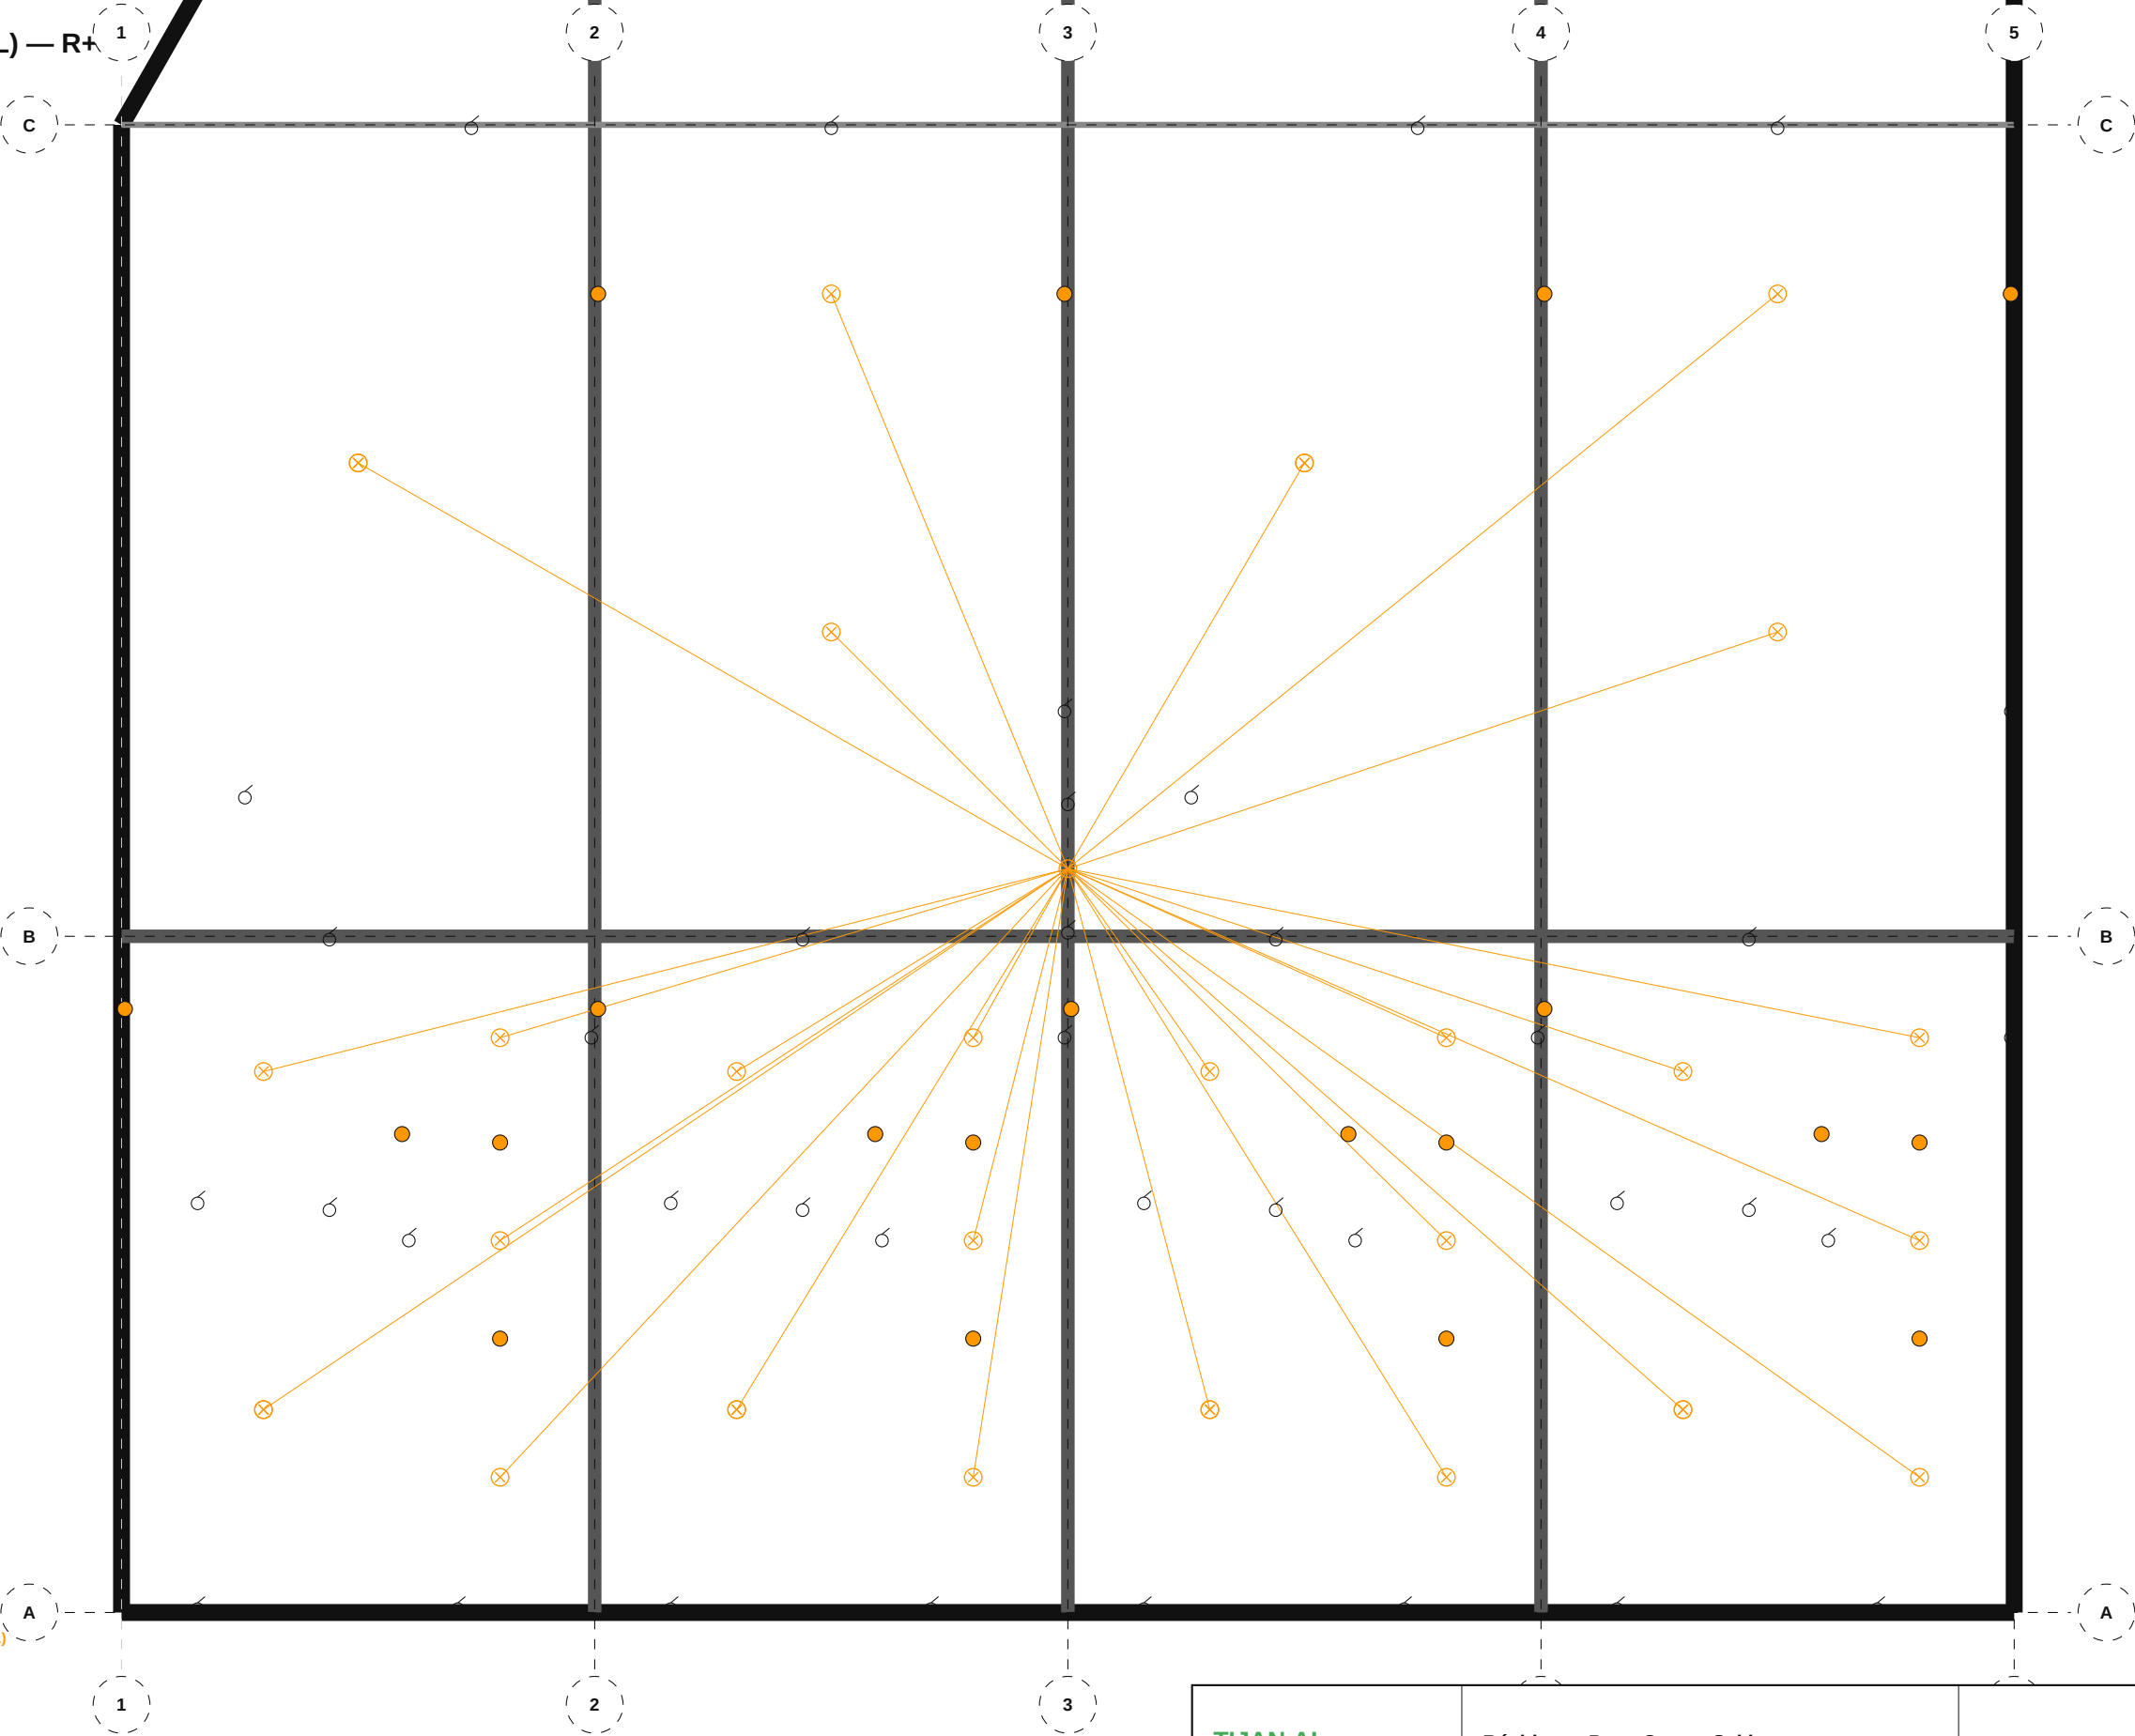

NOMENCLATURE — 510 HCU — Éclairage (ECL)

- Plafonnier: 27
- Interrupteur va-et-vient: 22
- Interrupteur: 16
- Applique miroir: 12
- Applique tête de lit: 8
- Plafonnier IP44: 6

TIJAN AI

Bureau d'Études Automatisé

Résidence Papa Oumar Sakho

Dakar, Senegal

Éch: 1/100

Pl. 87/133

510 HCU — Éclairage (ECL) — R+3


Date: 06/05/2026

Réf: 1711

BIM vHCU-087

Phase: APD


TIJAN AI Bureau d'Études Automatisé	Résidence Papa Oumar Sakho Dakar, Senegal	Éch: 1/100 Pl. 88/133
	510 HCU — Éclairage (ECL) — R+4	
Date: 06/05/2026	Réf: 1711	BIM vHCU-088 Phase: APD

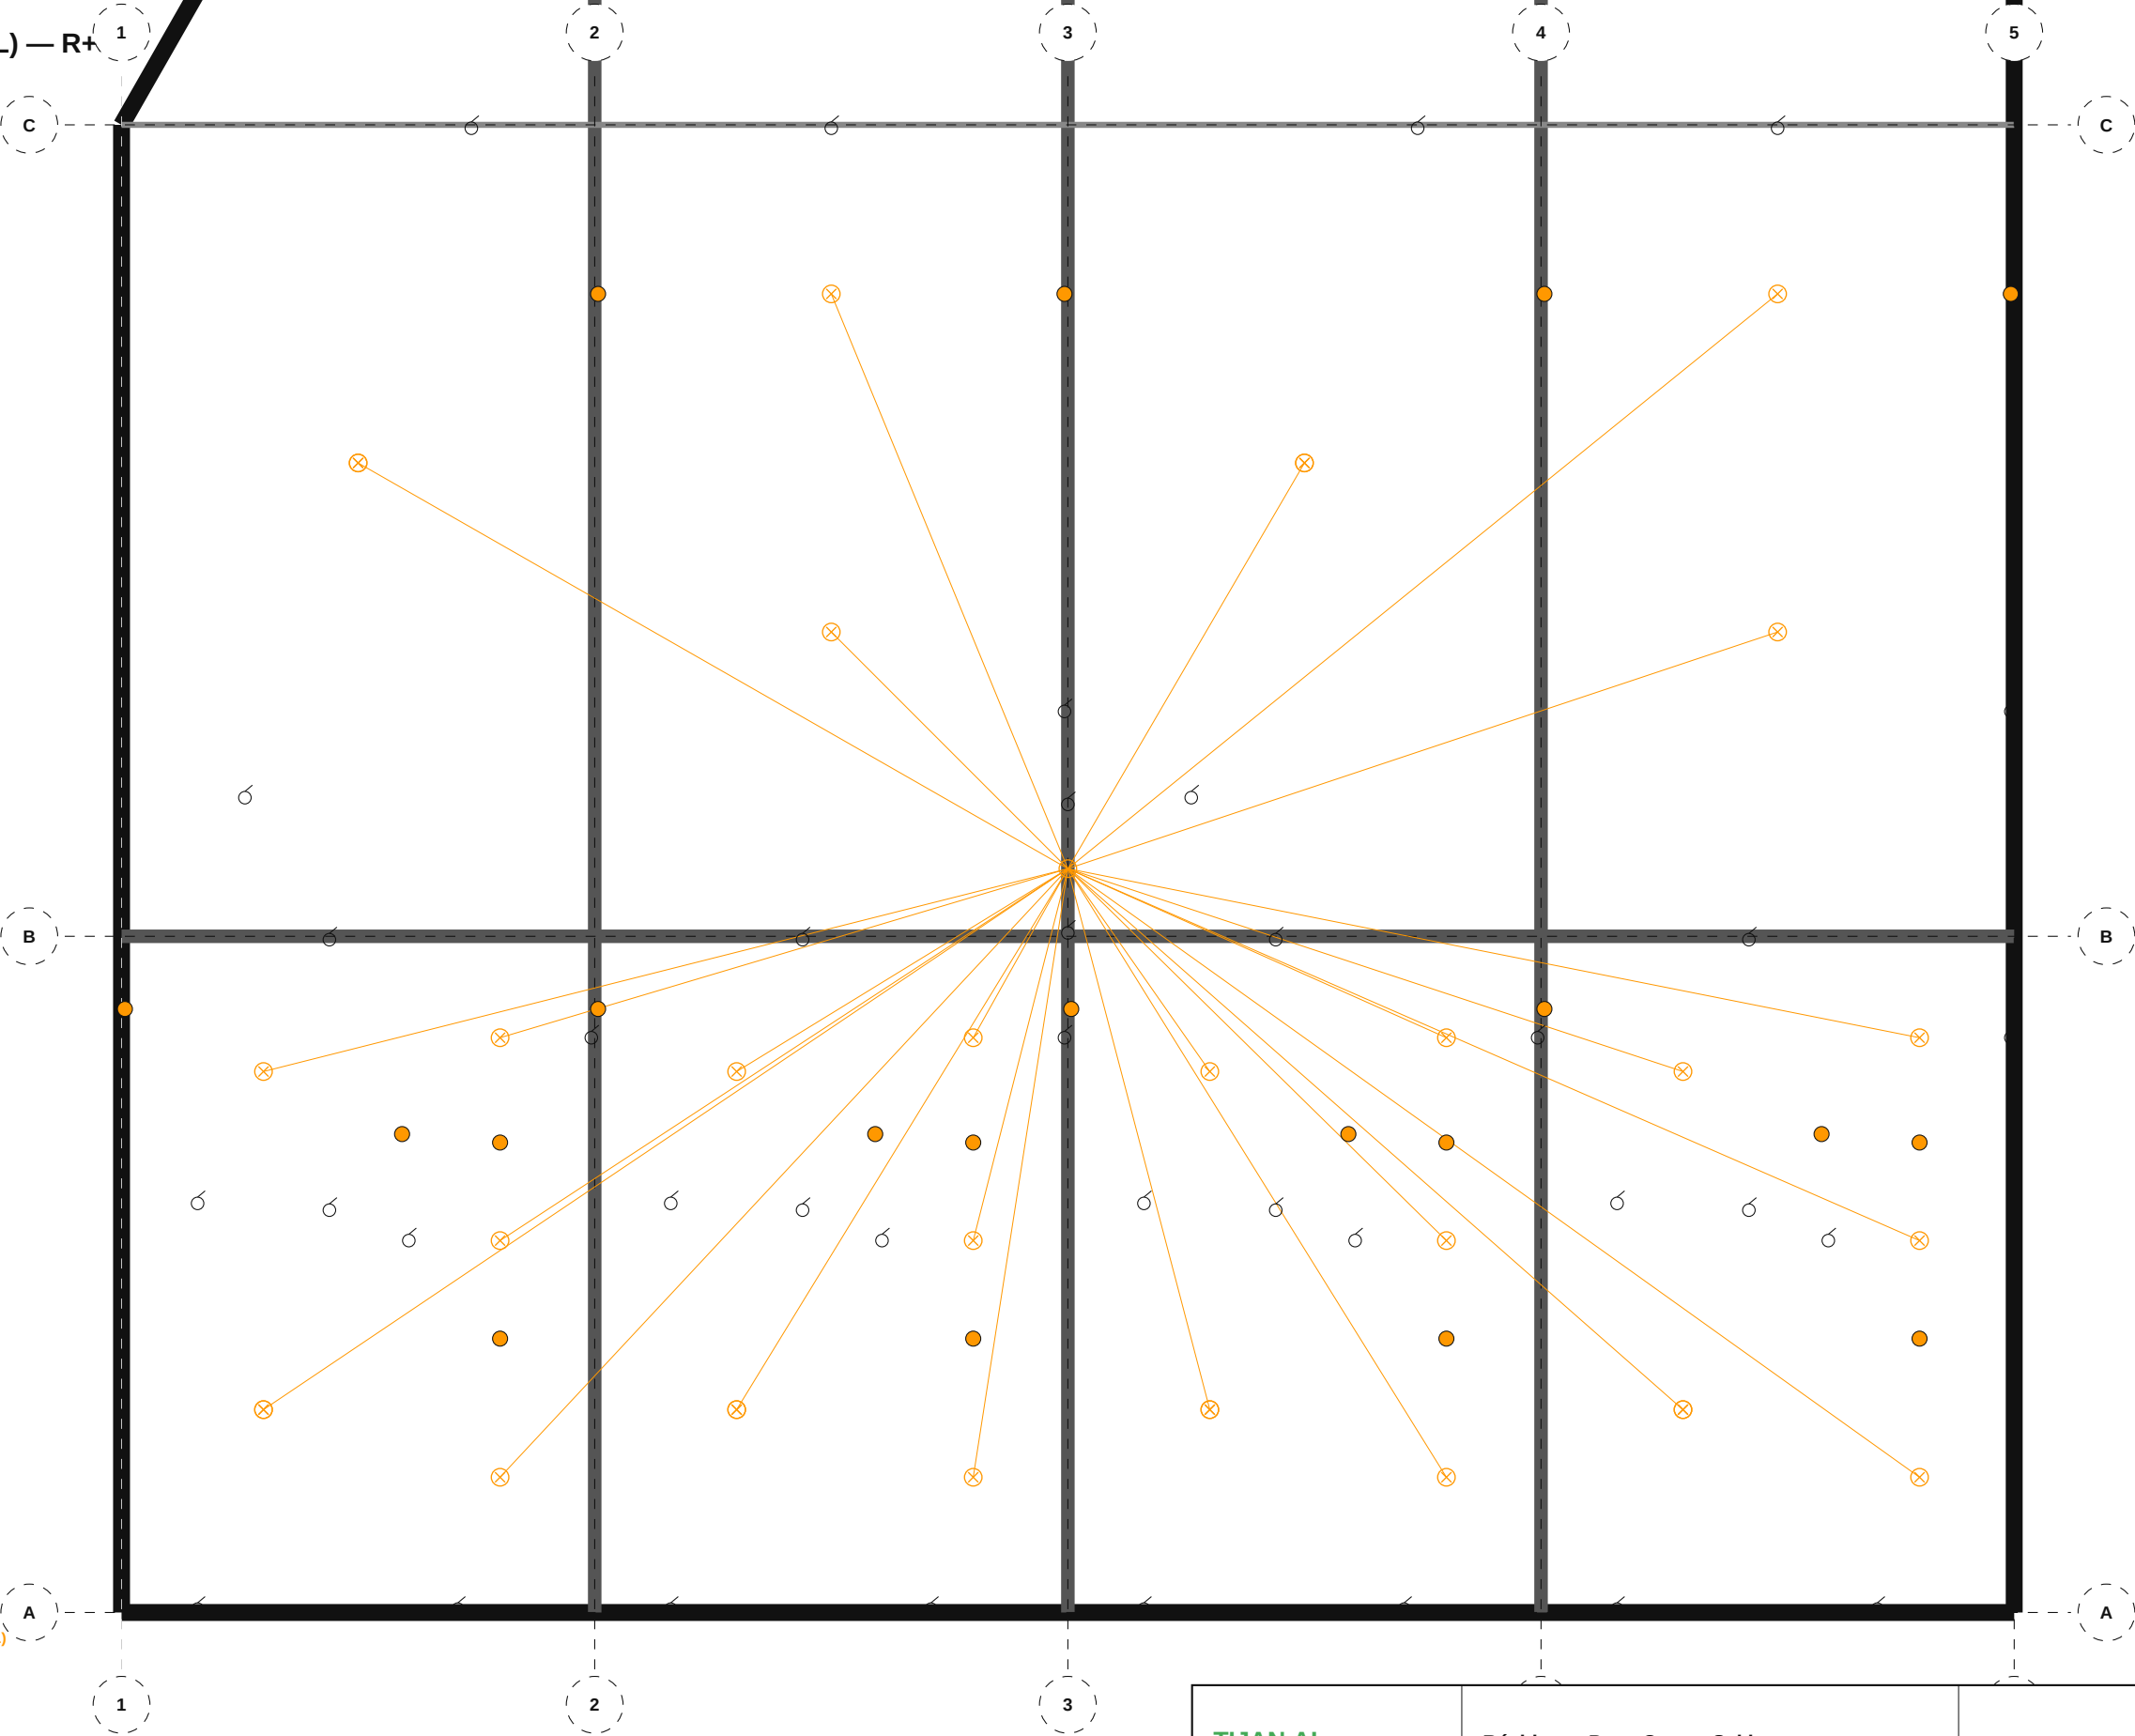

NOMENCLATURE — 510 HCU — Éclairage (ECL)

- Plafonnier: 27
- Interrupteur va-et-vient: 22
- Interrupteur: 16
- Applique miroir: 12
- Applique tête de lit: 8
- Plafonnier IP44: 6

TIJAN AI Bureau d'Études Automatisé	Résidence Papa Oumar Sakho Dakar, Senegal	Éch: 1/100 Pl. 89/133
	510 HCU — Éclairage (ECL) — R+5	
Date: 06/05/2026	Réf: 1711	BIM vHCU-089 Phase: APD

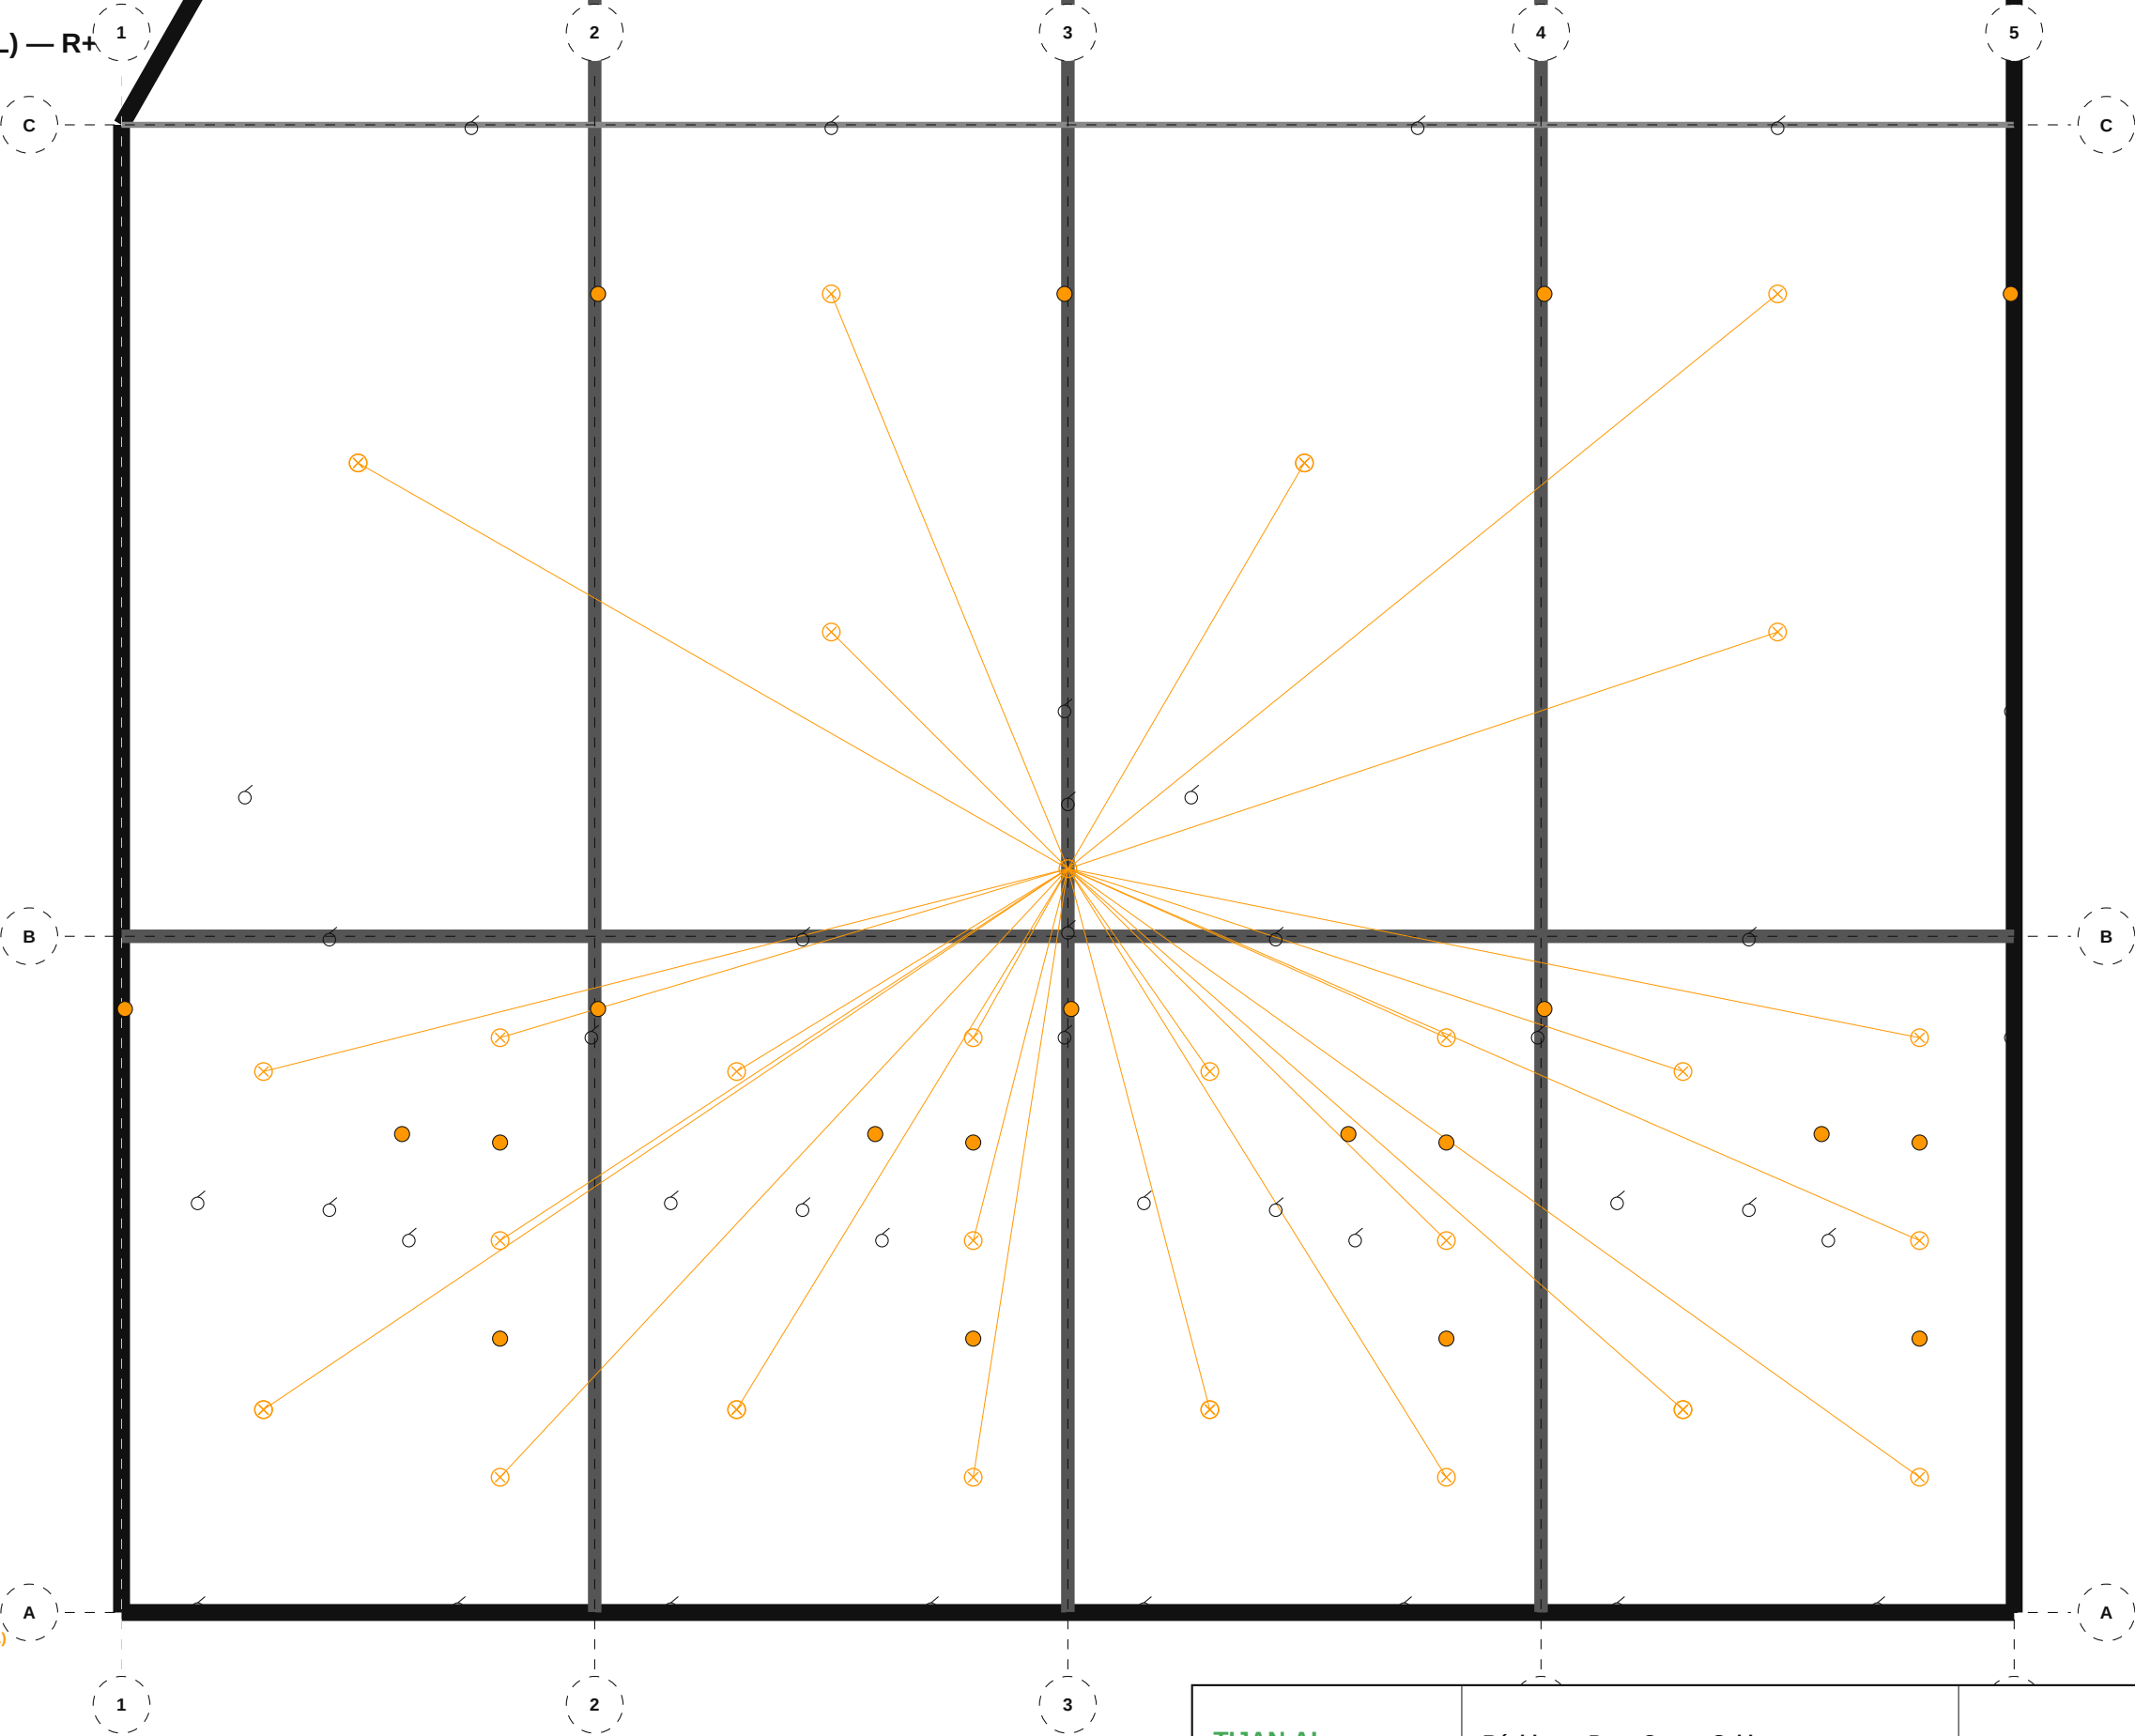

NOMENCLATURE — 510 HCU — Éclairage (ECL)

- Plafonnier: 27
- Interrupteur va-et-vient: 22
- Interrupteur: 16
- Applique miroir: 12
- Applique tête de lit: 8
- Plafonnier IP44: 6

TIJAN AI

Bureau d'Études Automatisé

Résidence Papa Oumar Sakho

Dakar, Senegal

Éch: 1/100

Pl. 90/133


510 HCU — Éclairage (ECL) — R+6

Date: 06/05/2026

Réf: 1711

BIM vHCU-090

Phase: APD

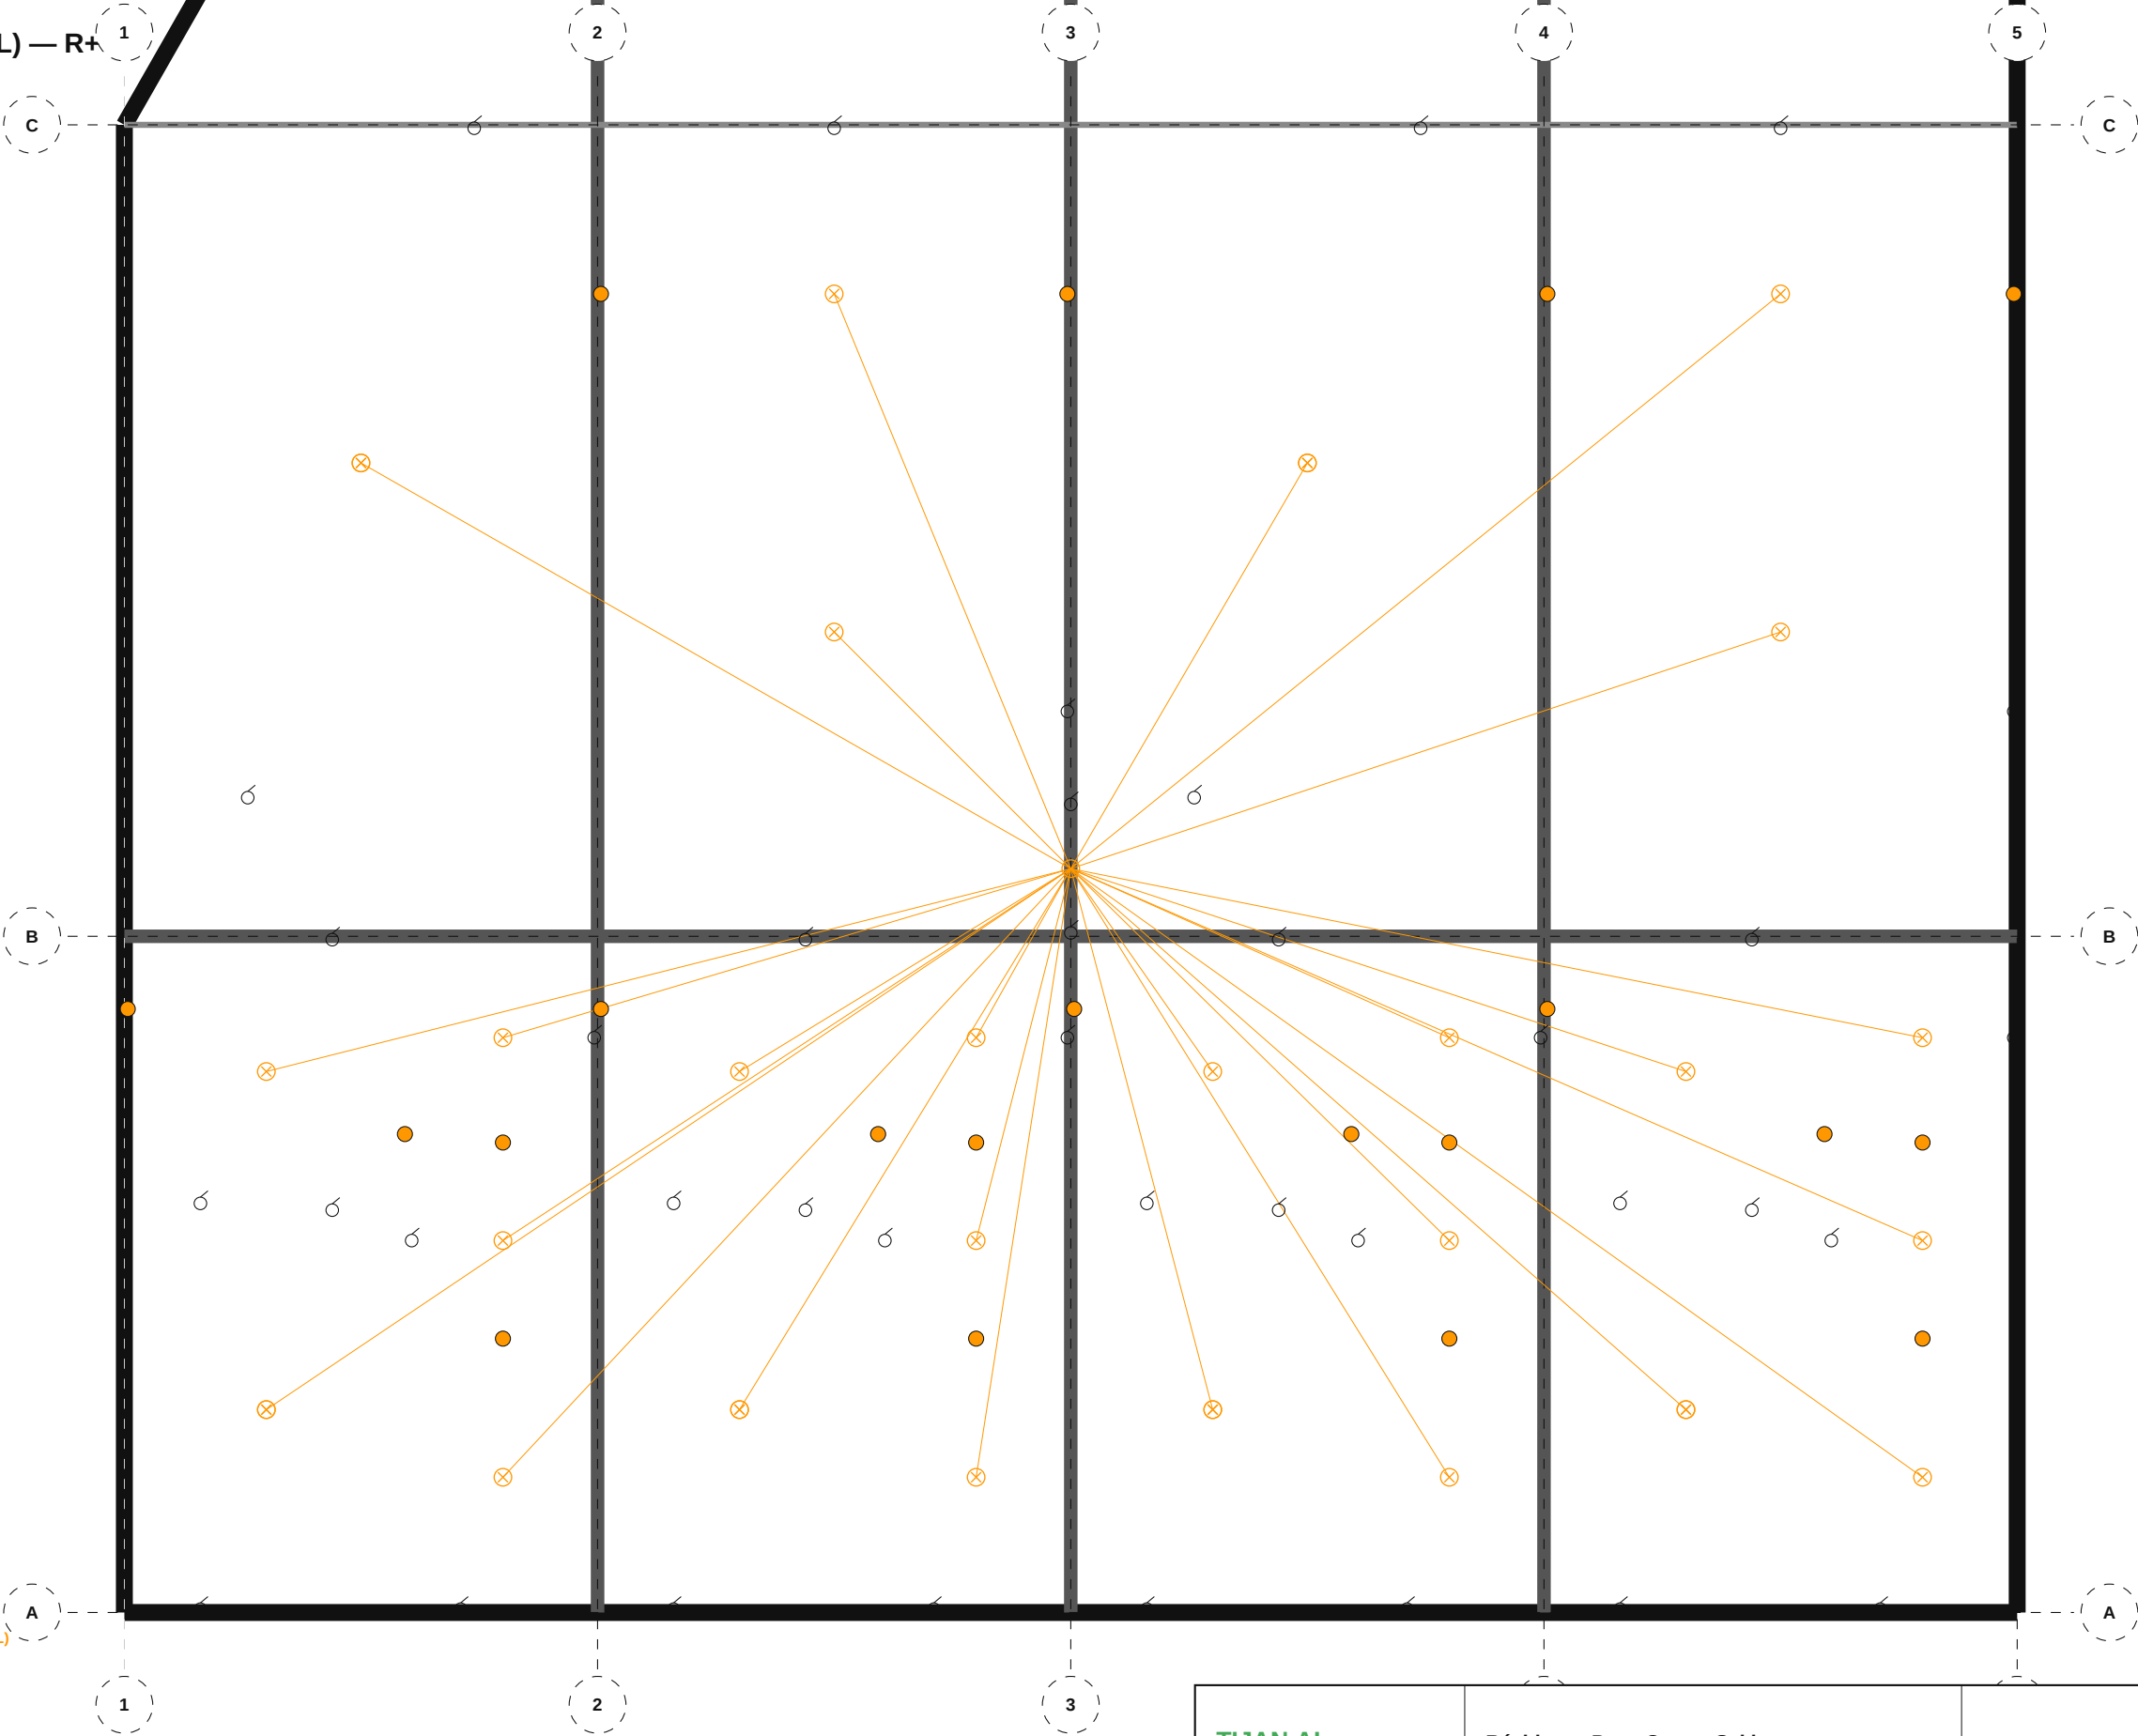

NOMENCLATURE — 510 HCU — Éclairage (ECL)

- Plafonnier: 27
- Interrupteur va-et-vient: 22
- Interrupteur: 16
- Applique miroir: 12
- Applique tête de lit: 8
- Plafonnier IP44: 6

TIJAN AI

Bureau d'Études Automatisé

Résidence Papa Oumar Sakho

Dakar, Senegal

Éch: 1/100

Pl. 91/133

510 HCU — Éclairage (ECL) — R+7


Date: 06/05/2026

Réf: 1711

BIM vHCU-091

Phase: APD


510 HCU — Éclairage (ECL) — R+8 Terrasse

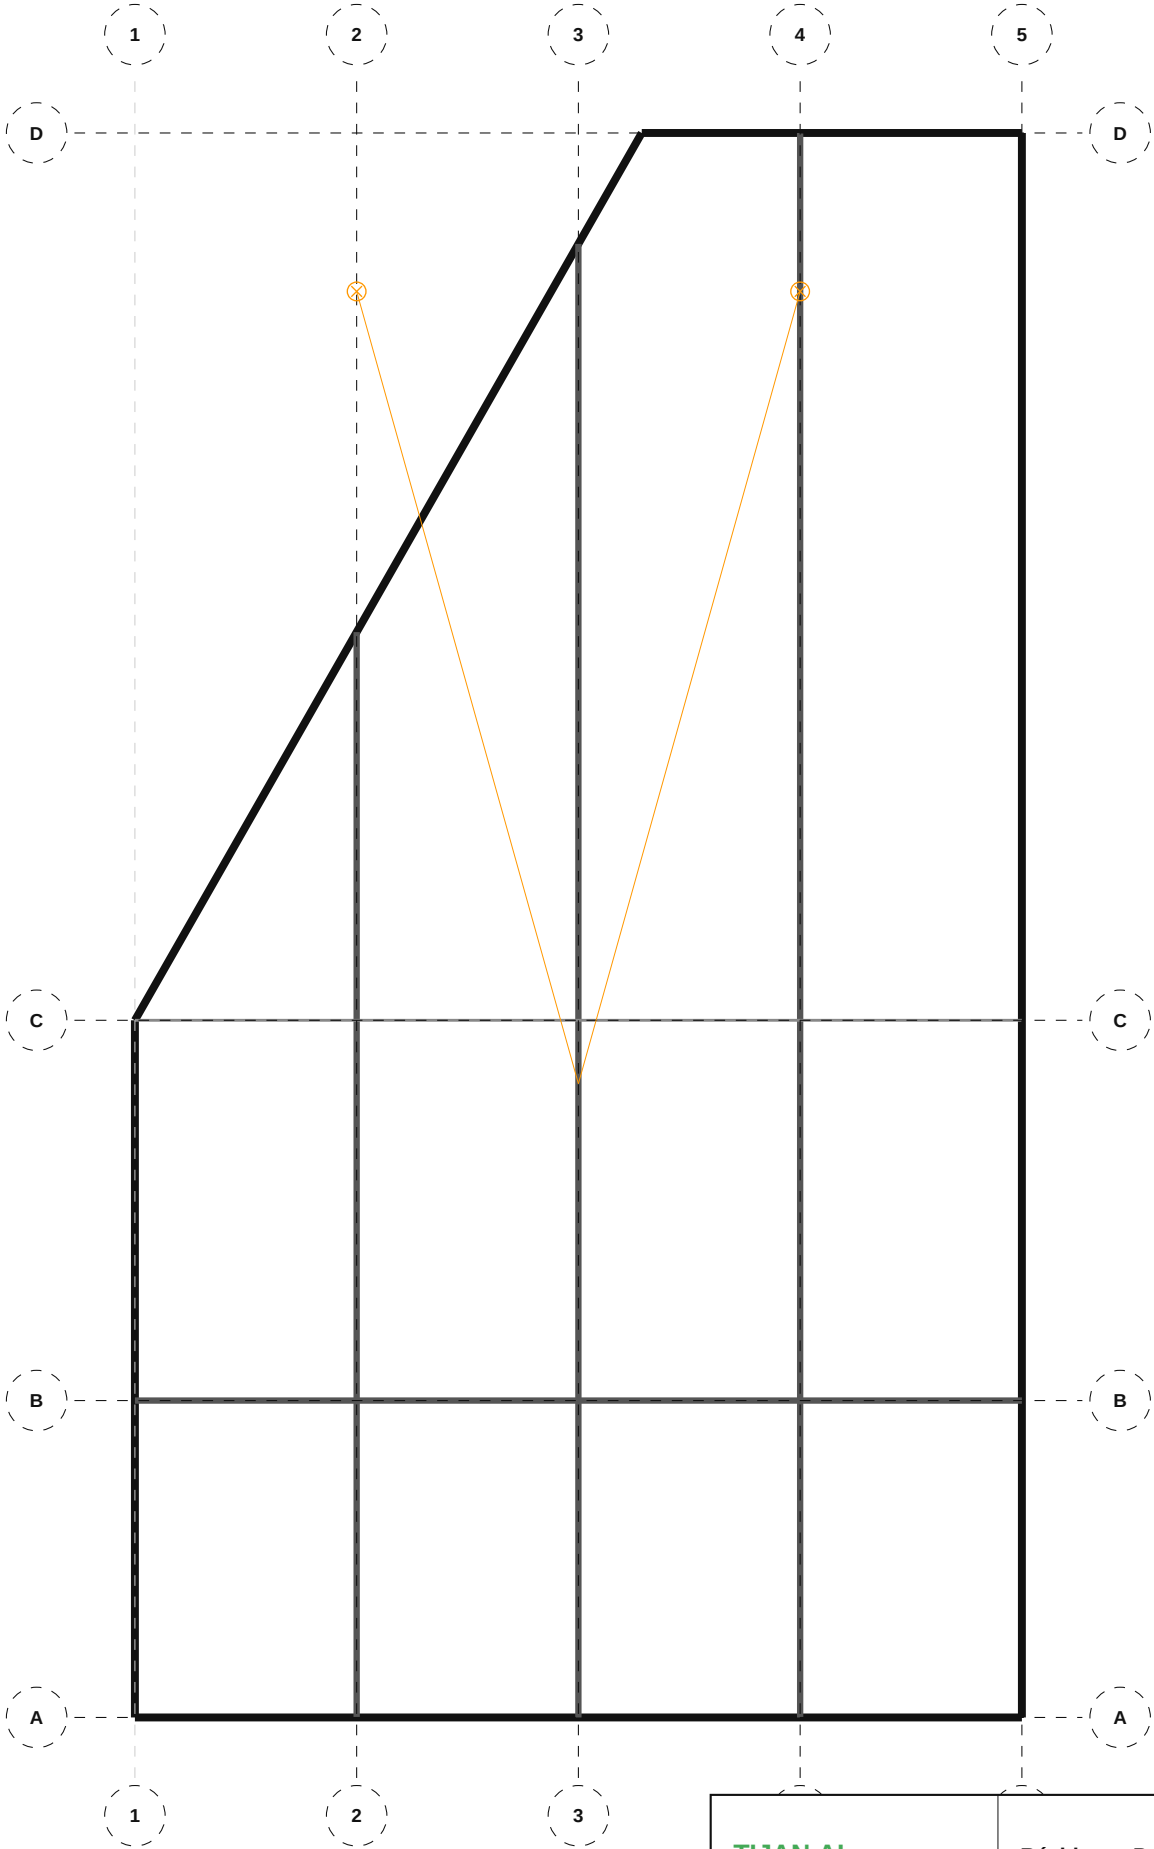

NOMENCLATURE — 510 HCU — Éclairage (ECL)

• Plafonnier: 2

TIJAN AI Bureau d'Études Automatisé	Résidence Papa Oumar Sakho Dakar, Senegal	Éch: 1/100 Pl. 92/133
	510 HCU — Éclairage (ECL) — R+8 Terrasse	
Date: 06/05/2026	Réf: 1711	BIM vHCU-092 Phase: APD

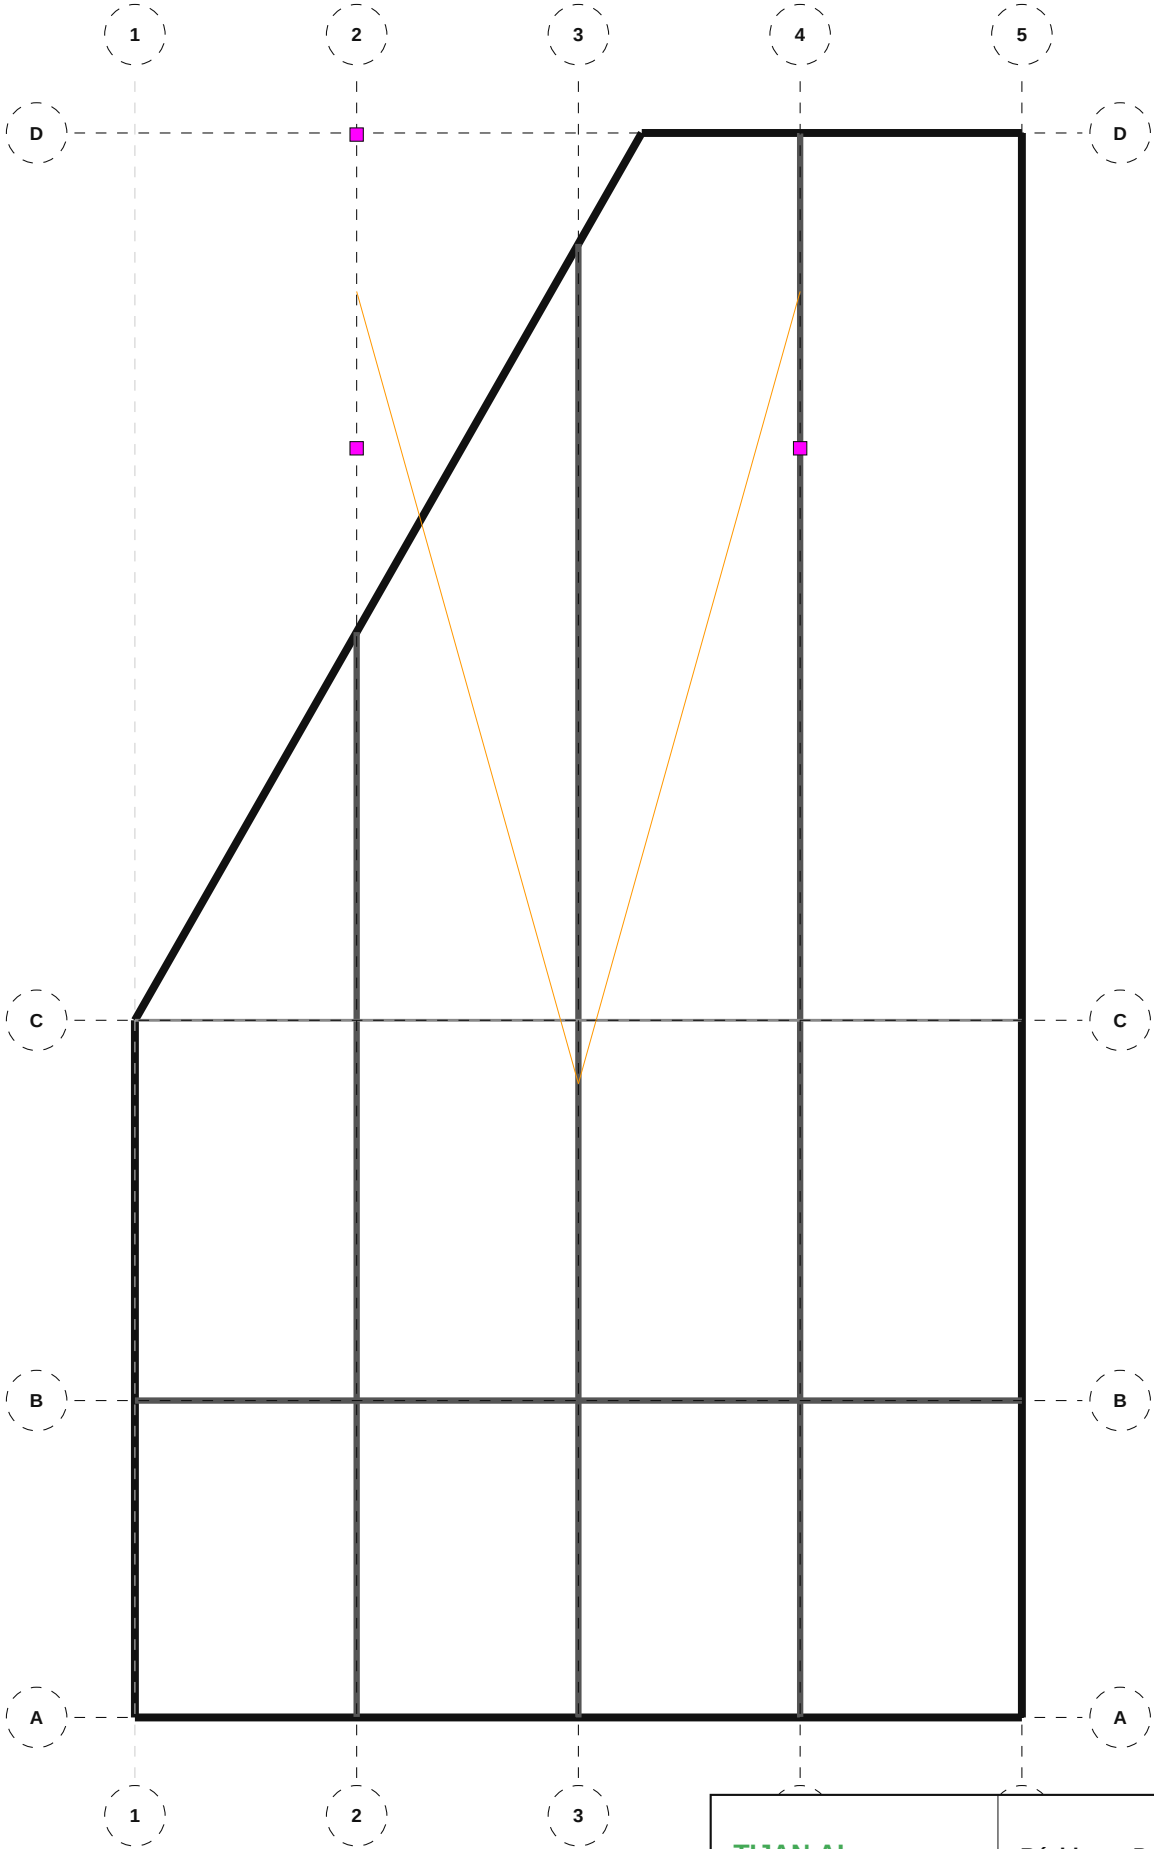

NOMENCLATURE — 510 HCU — Prises de Courant (PC)

- Prise 2P+T 16A: 2
- Prise 2P+T: 1

TIJAN AI Bureau d'Études Automatisé	Résidence Papa Oumar Sakho Dakar, Senegal	Éch: 1/100 Pl. 93/133
	510 HCU — Prises de Courant (PC) — Sous-Sol	
Date: 06/05/2026	Réf: 1711	BIM vHCU-093 Phase: APD

510 HCU — Prises de Courant (PC) — RDC

1

2

3

4

5

B

B

A

A

NOMENCLATURE — 510 HCU — Prises de Courant (PC)

1

• Prise 2P+T 16A

2

3

4

5

TIJAN AI

Bureau d'Études Automatisé

Résidence Papa Oumar Sakho

Dakar, Senegal

Éch: 1/100

Pl. 94/133

510 HCU — Prises de Courant (PC) — RDC


Date: 06/05/2026

Réf: 1711

BIM vHCU-094

Phase: APD

510 HCU — Prises de Courant (PC) — R+1

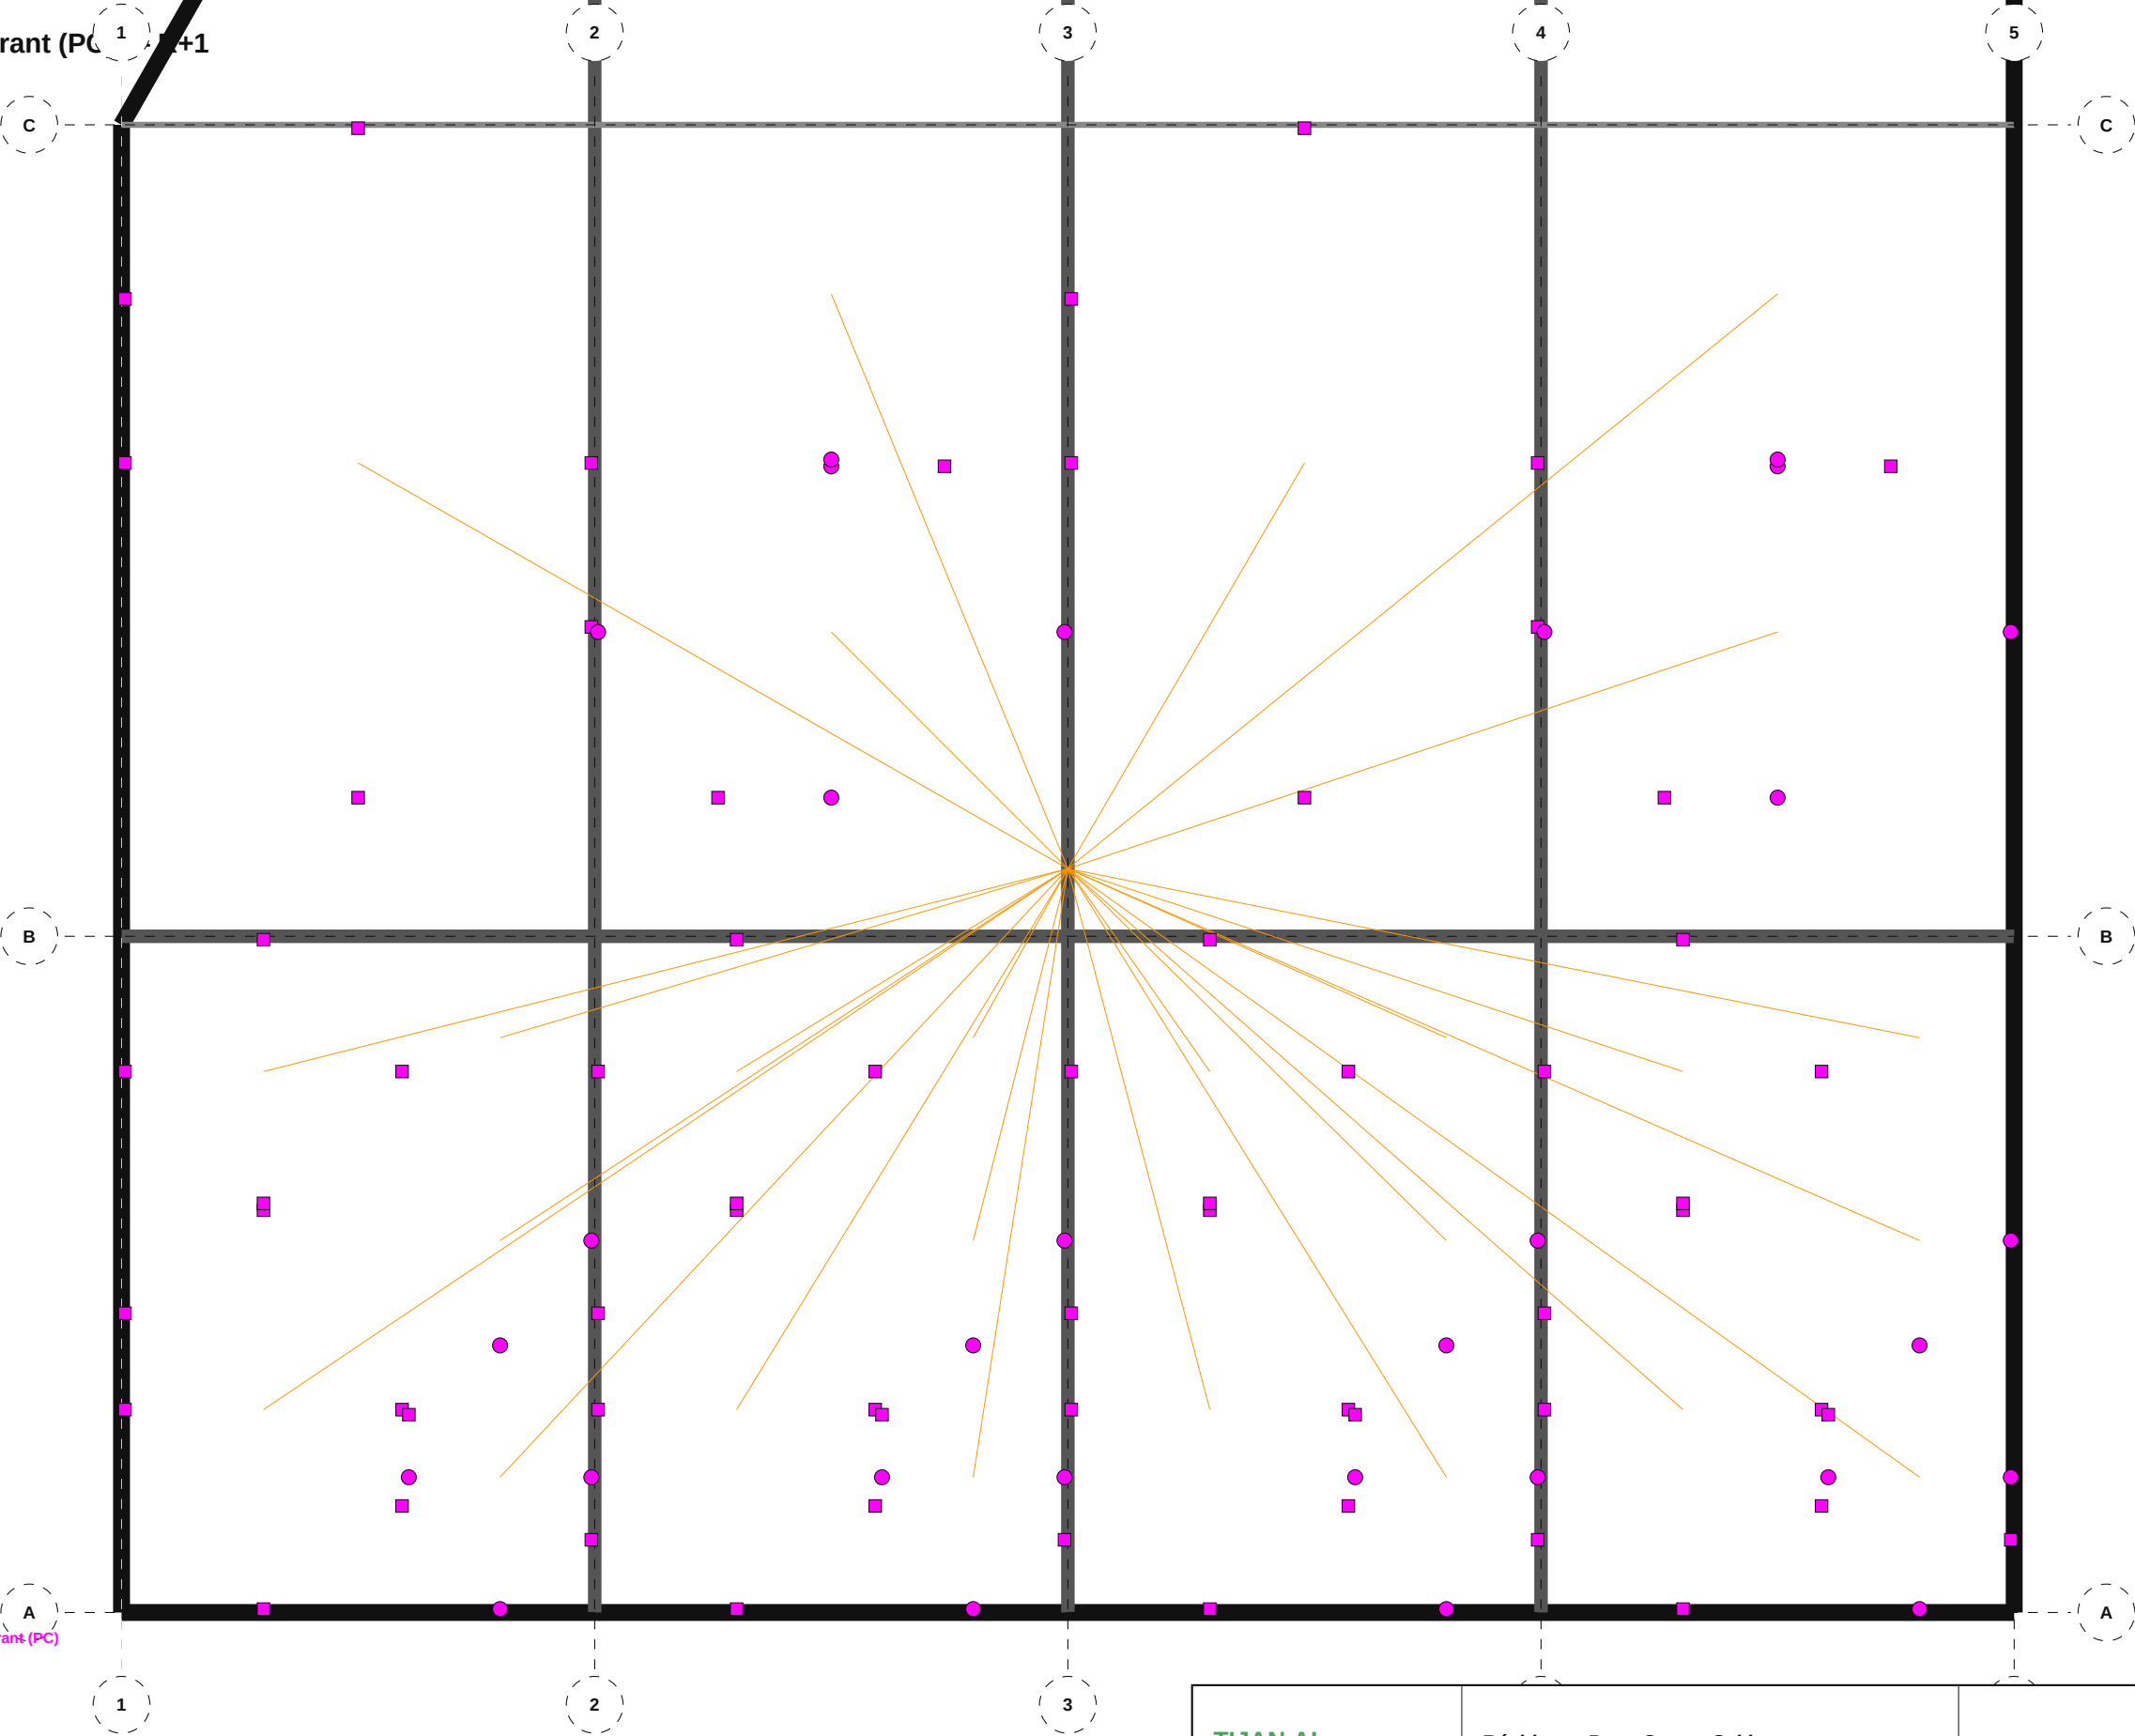


NOMENCLATURE — 510 HCU — Prises de Courant (PC)

- Prise 2P+T 16A: 64
- Prise plan de travail: 24
- Prise étanche 2P+T: 6

TIJAN AI Bureau d'Études Automatisé	Résidence Papa Oumar Sakho Dakar, Senegal	Éch: 1/100 Pl. 95/133
	510 HCU — Prises de Courant (PC) — R+1	
Date: 06/05/2026	Réf: 1711	BIM vHCU-095 Phase: APD

510 HCU — Prises de Courant (PC) — R+2

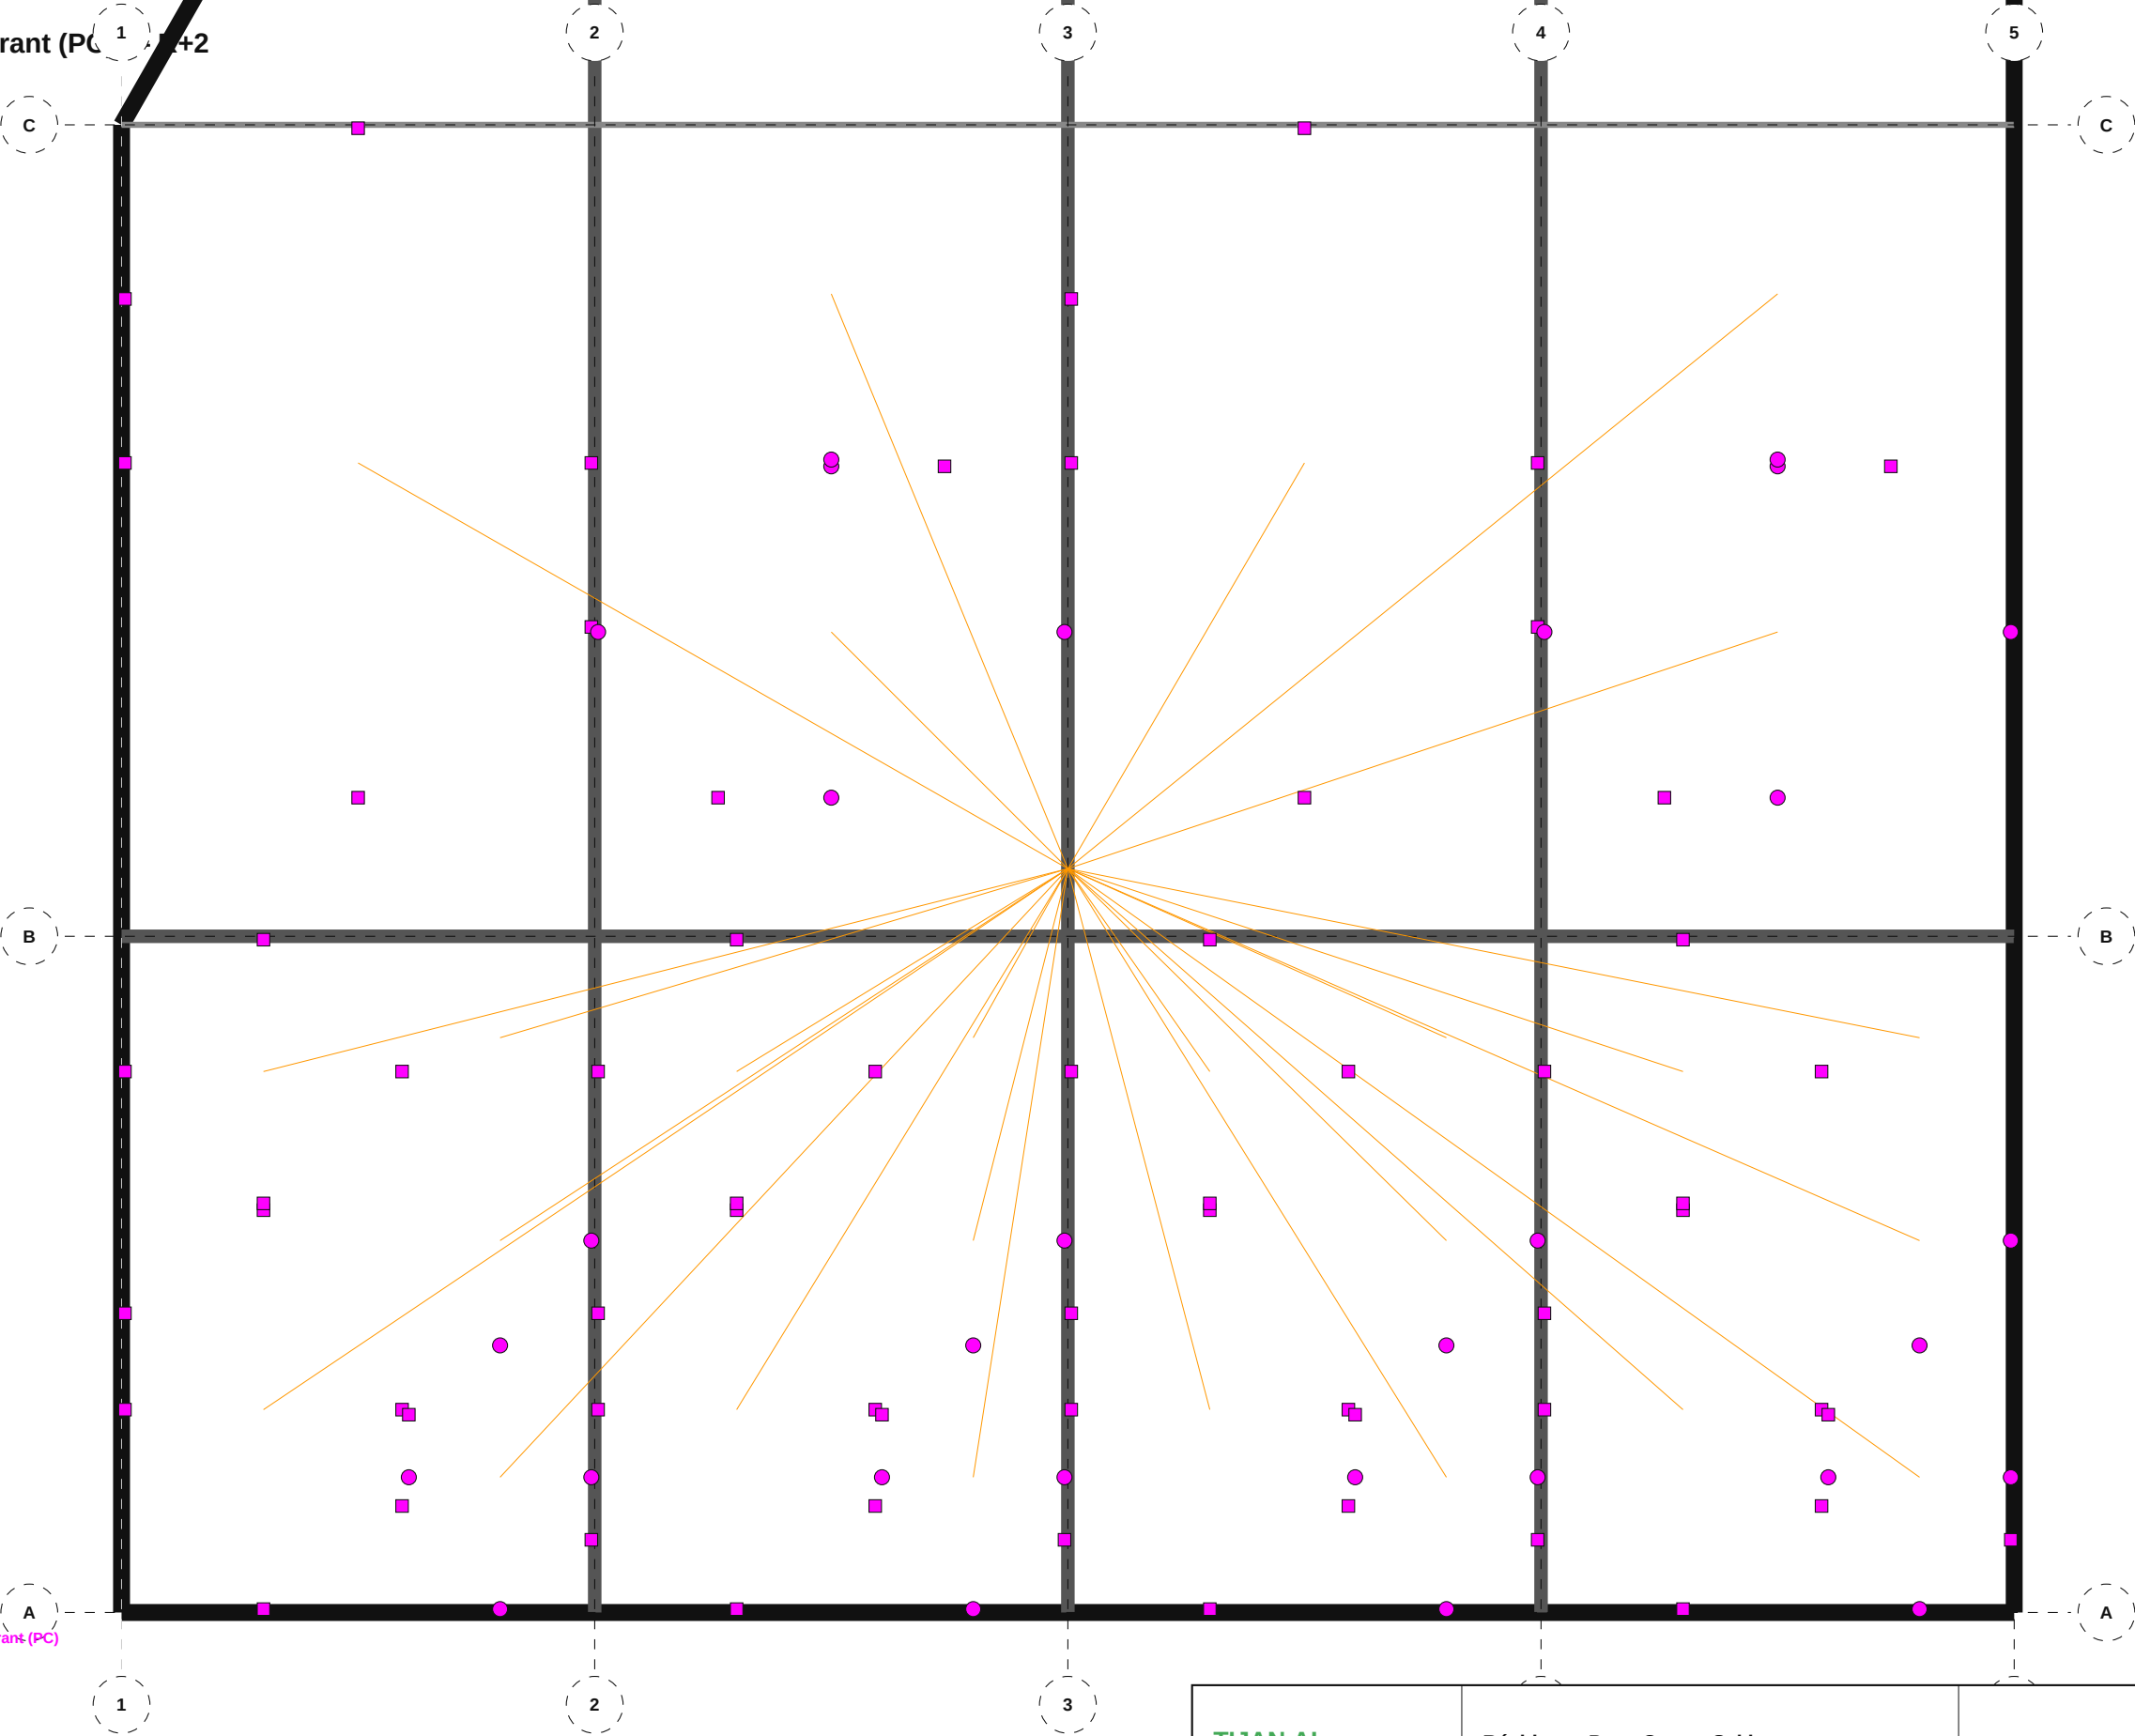


NOMENCLATURE — 510 HCU — Prises de Courant (PC)

- Prise 2P+T 16A: 64
- Prise plan de travail: 24
- Prise étanche 2P+T: 6

TIJAN AI Bureau d'Études Automatisé	Résidence Papa Oumar Sakho Dakar, Senegal	Éch: 1/100 Pl. 96/133
	510 HCU — Prises de Courant (PC) — R+2	
Date: 06/05/2026	Réf: 1711	BIM vHCU-096 Phase: APD

510 HCU — Prises de Courant (PC) — R+3

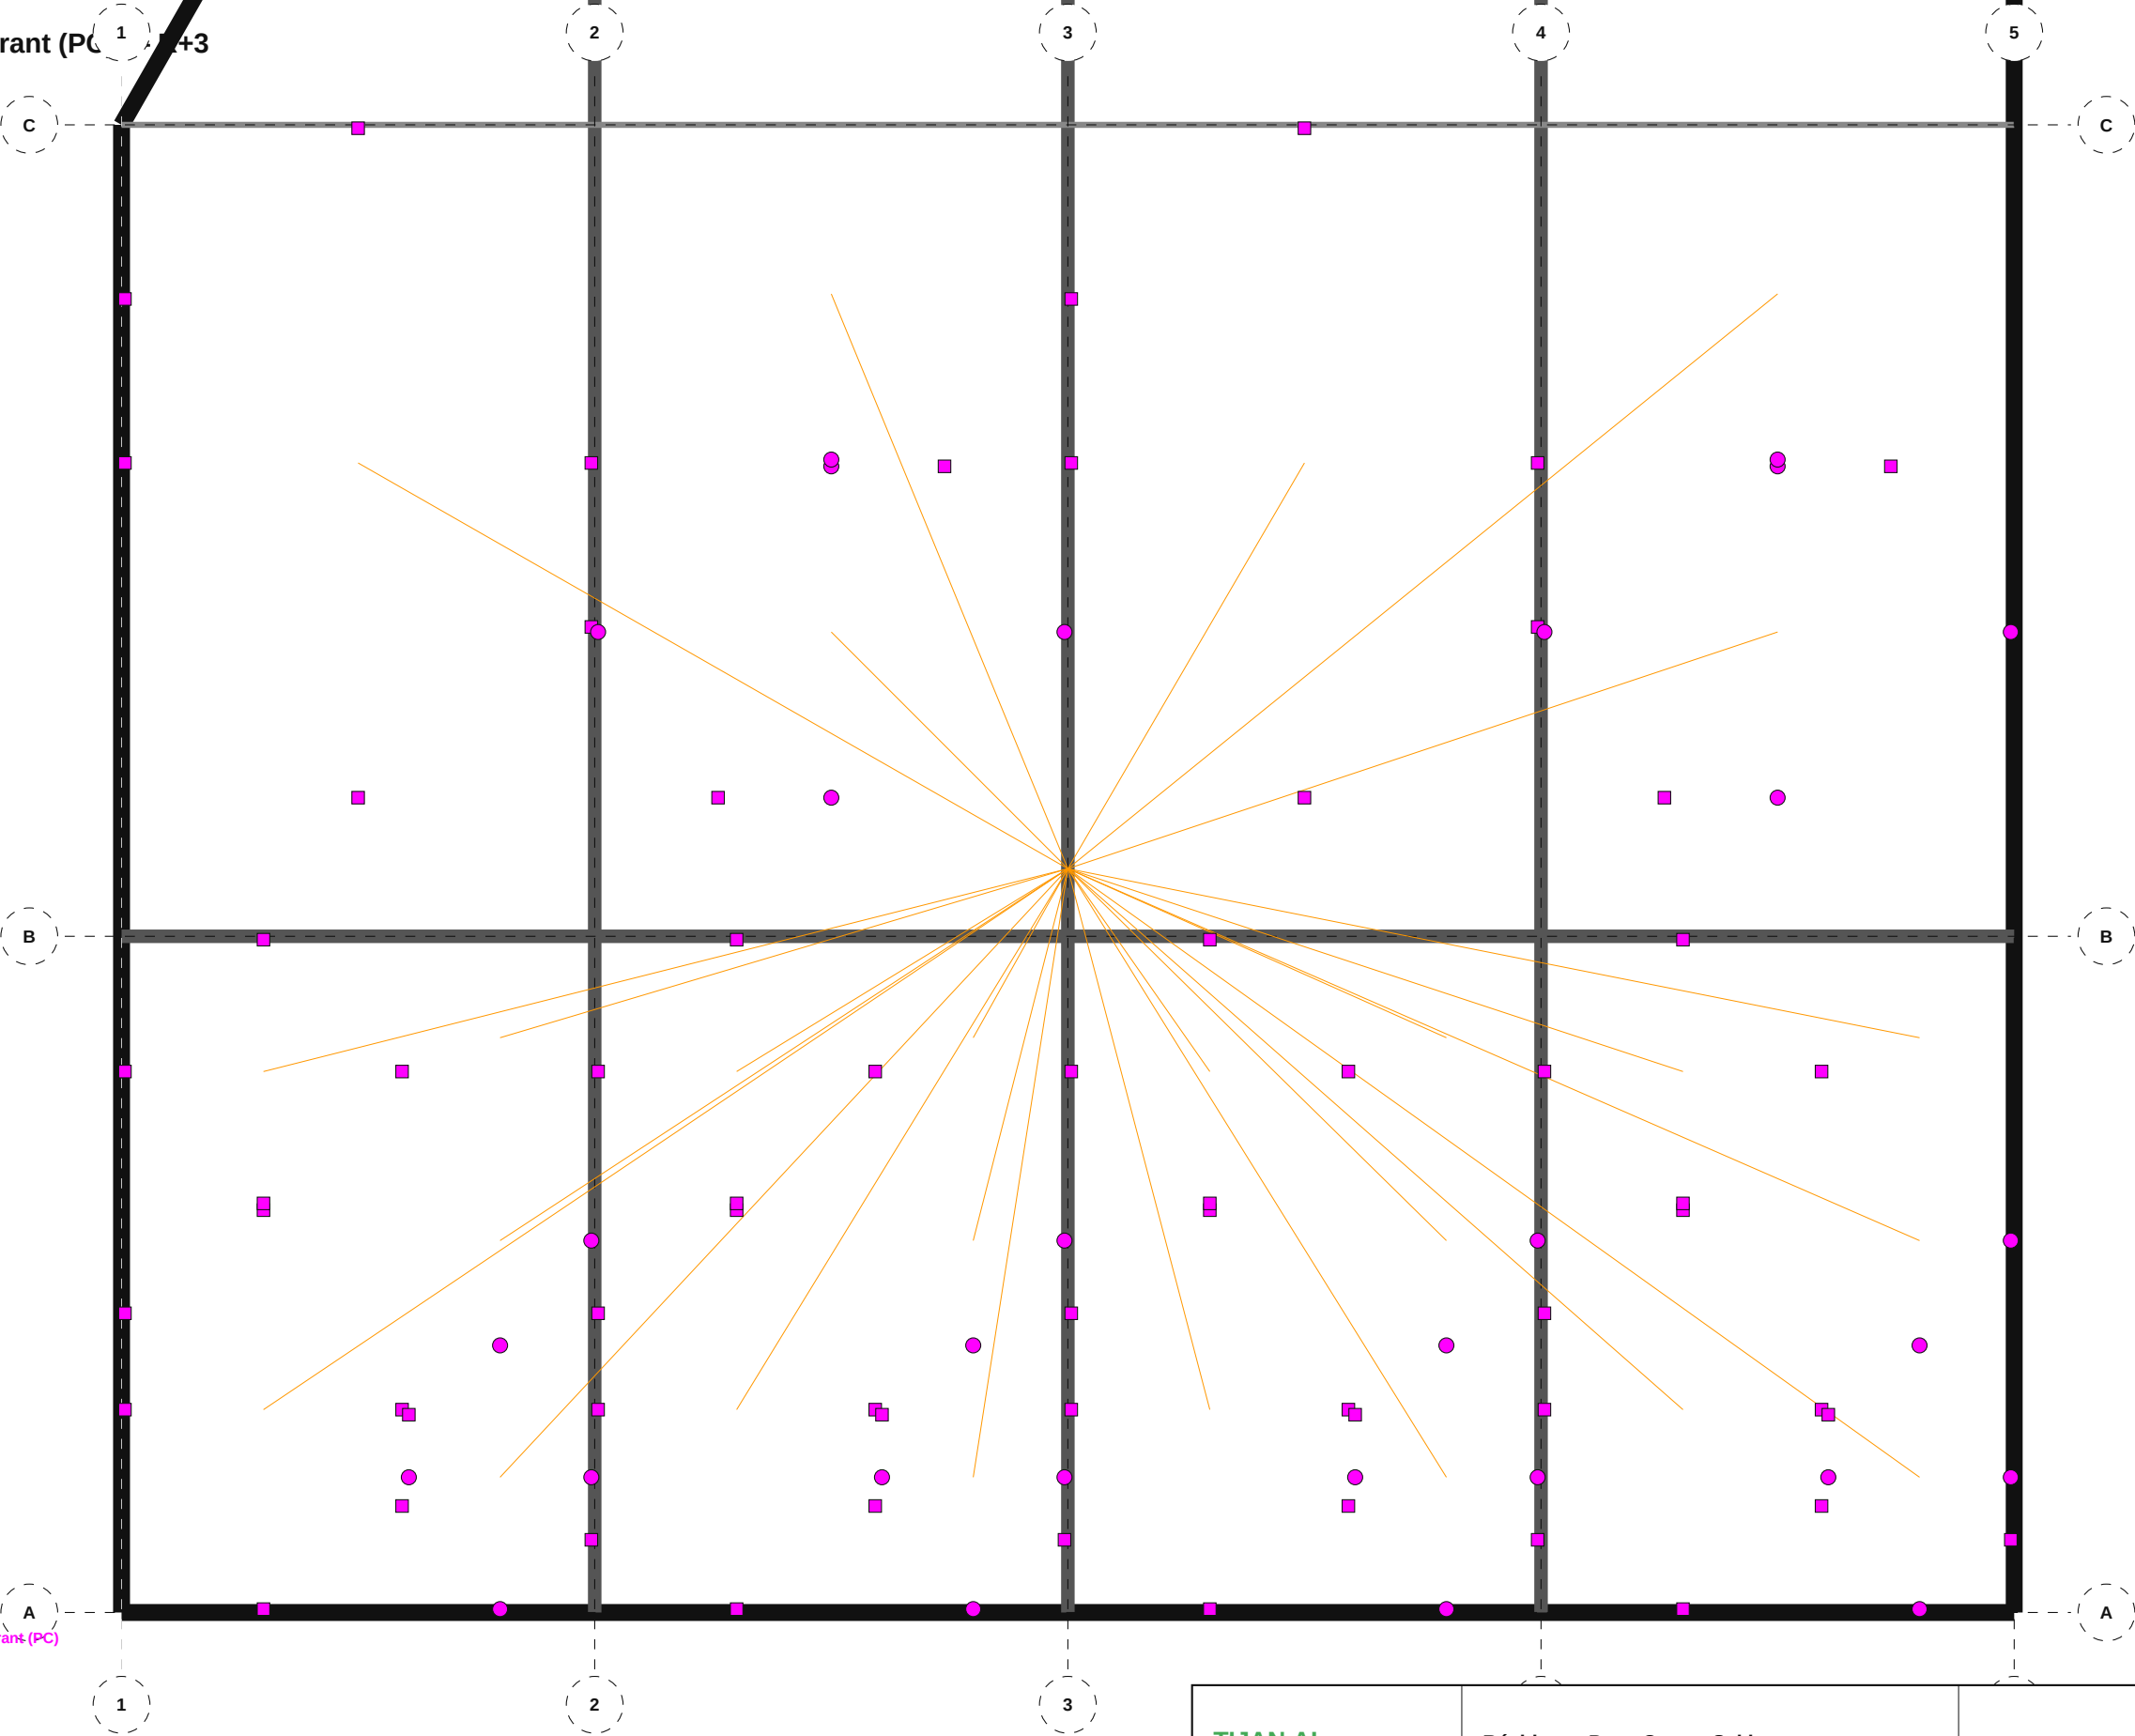

NOMENCLATURE — 510 HCU — Prises de Courant (PC)

- Prise 2P+T 16A: 64
- Prise plan de travail: 24
- Prise étanche 2P+T: 6

TIJAN AI

Bureau d'Études Automatisé

Résidence Papa Oumar Sakho

Dakar, Senegal

Éch: 1/100

Pl. 97/133

510 HCU — Prises de Courant (PC) — R+3


Date: 06/05/2026

Réf: 1711

BIM vHCU-097

Phase: APD

510 HCU — Prises de Courant (PC) — R+4

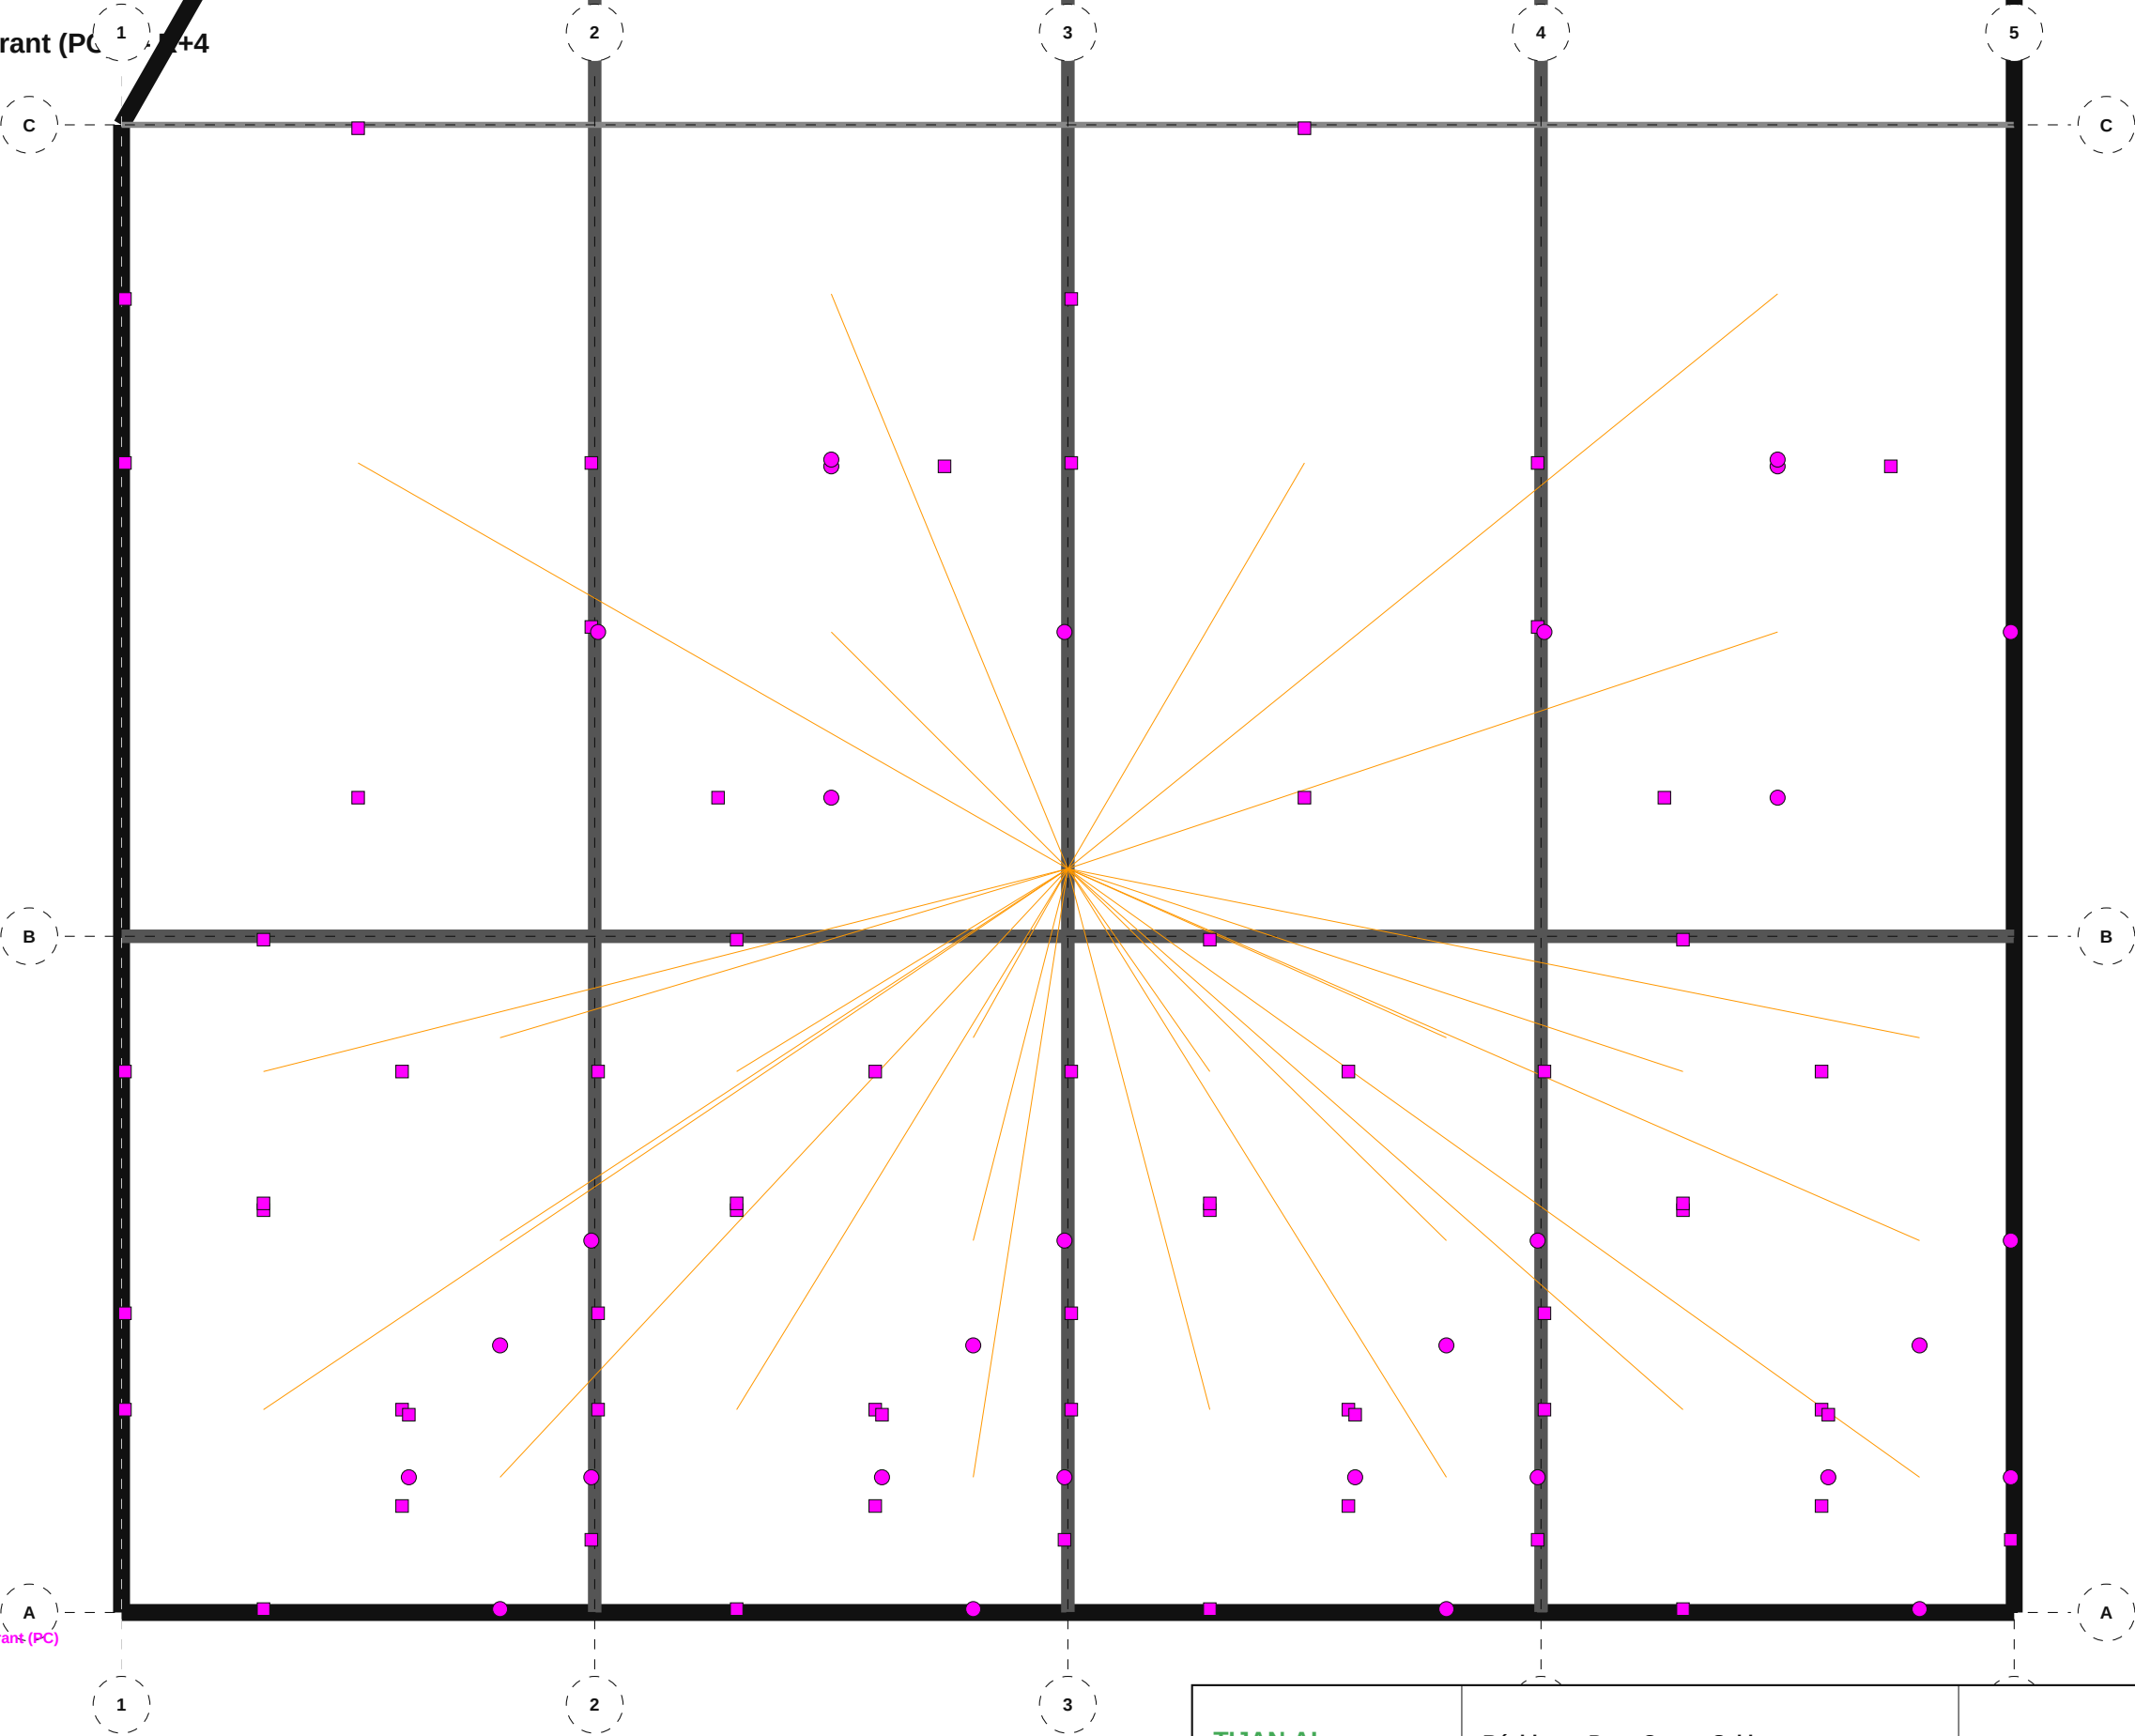

NOMENCLATURE — 510 HCU — Prises de Courant (PC)

- Prise 2P+T 16A: 64
- Prise plan de travail: 24
- Prise étanche 2P+T: 6

TIJAN AI

Bureau d'Études Automatisé

Résidence Papa Oumar Sakho

Dakar, Senegal

Éch: 1/100

Pl. 98/133


510 HCU — Prises de Courant (PC) — R+4

Date: 06/05/2026

Réf: 1711

BIM vHCU-098

Phase: APD

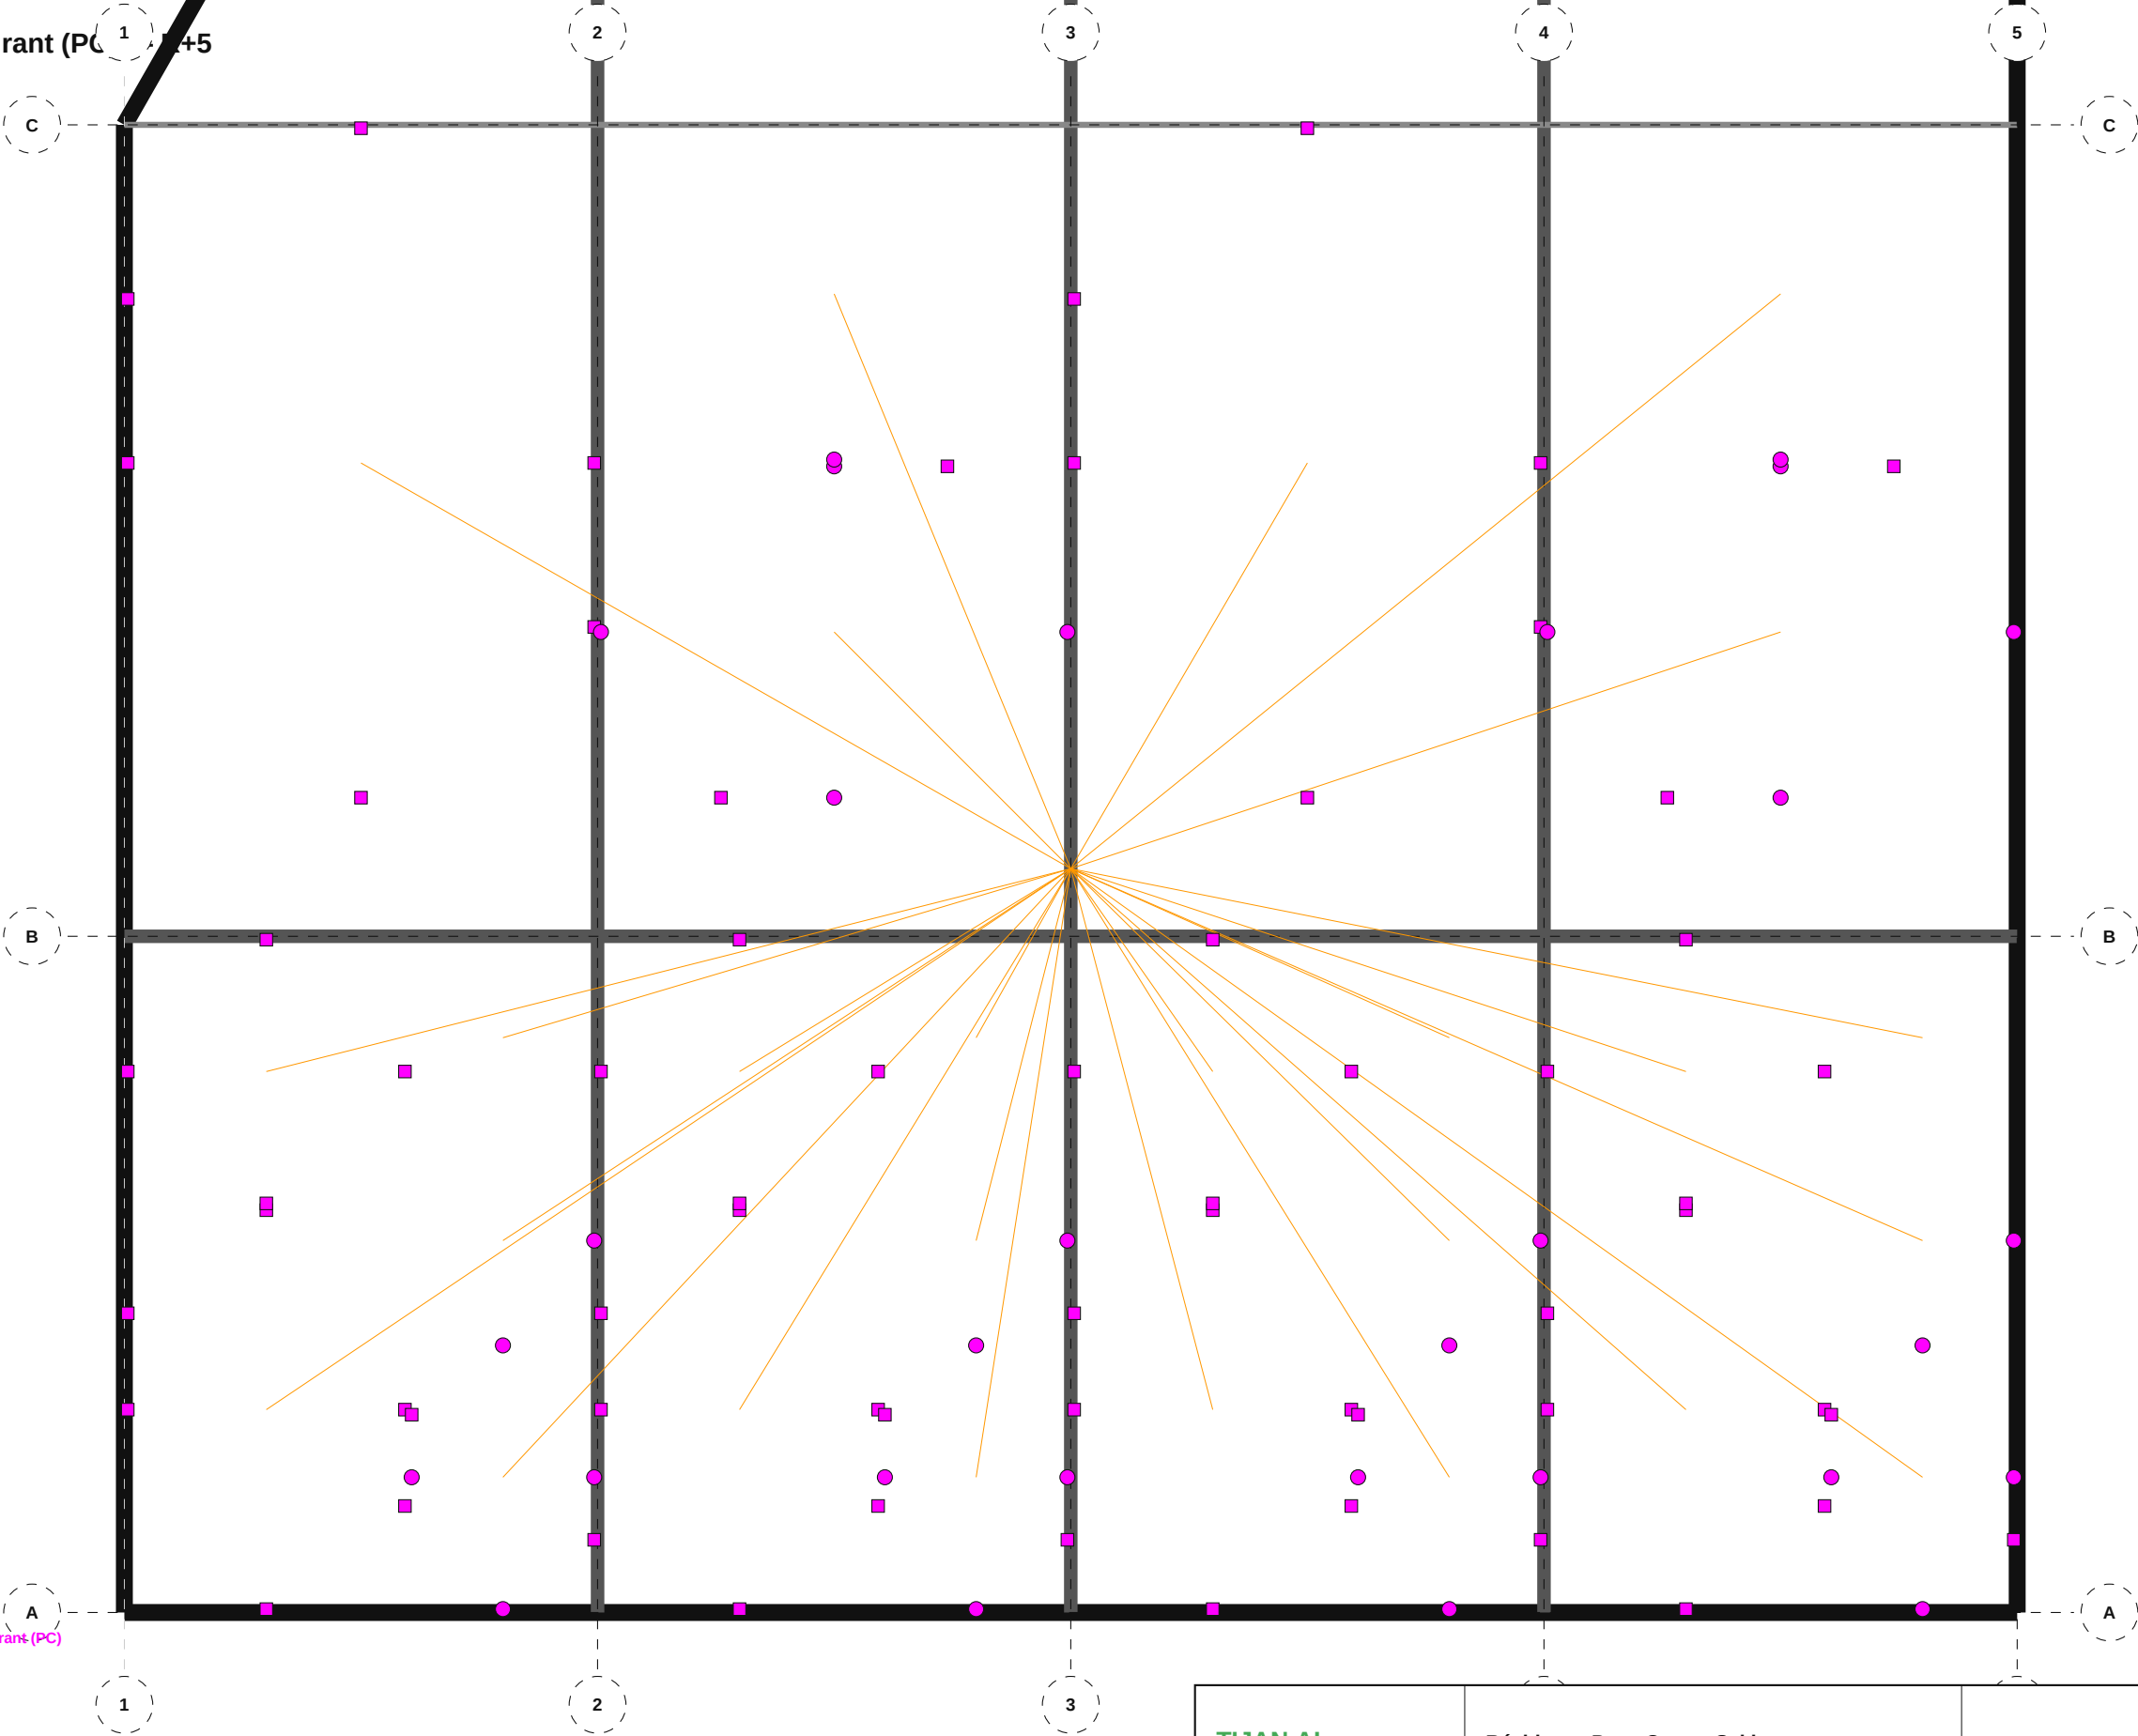


NOMENCLATURE — 510 HCU — Prises de Courant (PC)

- Prise 2P+T 16A: 64
- Prise plan de travail: 24
- Prise étanche 2P+T: 6

TIJAN AI Bureau d'Études Automatisé	Résidence Papa Oumar Sakho Dakar, Senegal	Éch: 1/100 Pl. 99/133
	510 HCU — Prises de Courant (PC) — R+5	
Date: 06/05/2026	Réf: 1711	BIM vHCU-099 Phase: APD

510 HCU — Prises de Courant (PC) — R+6

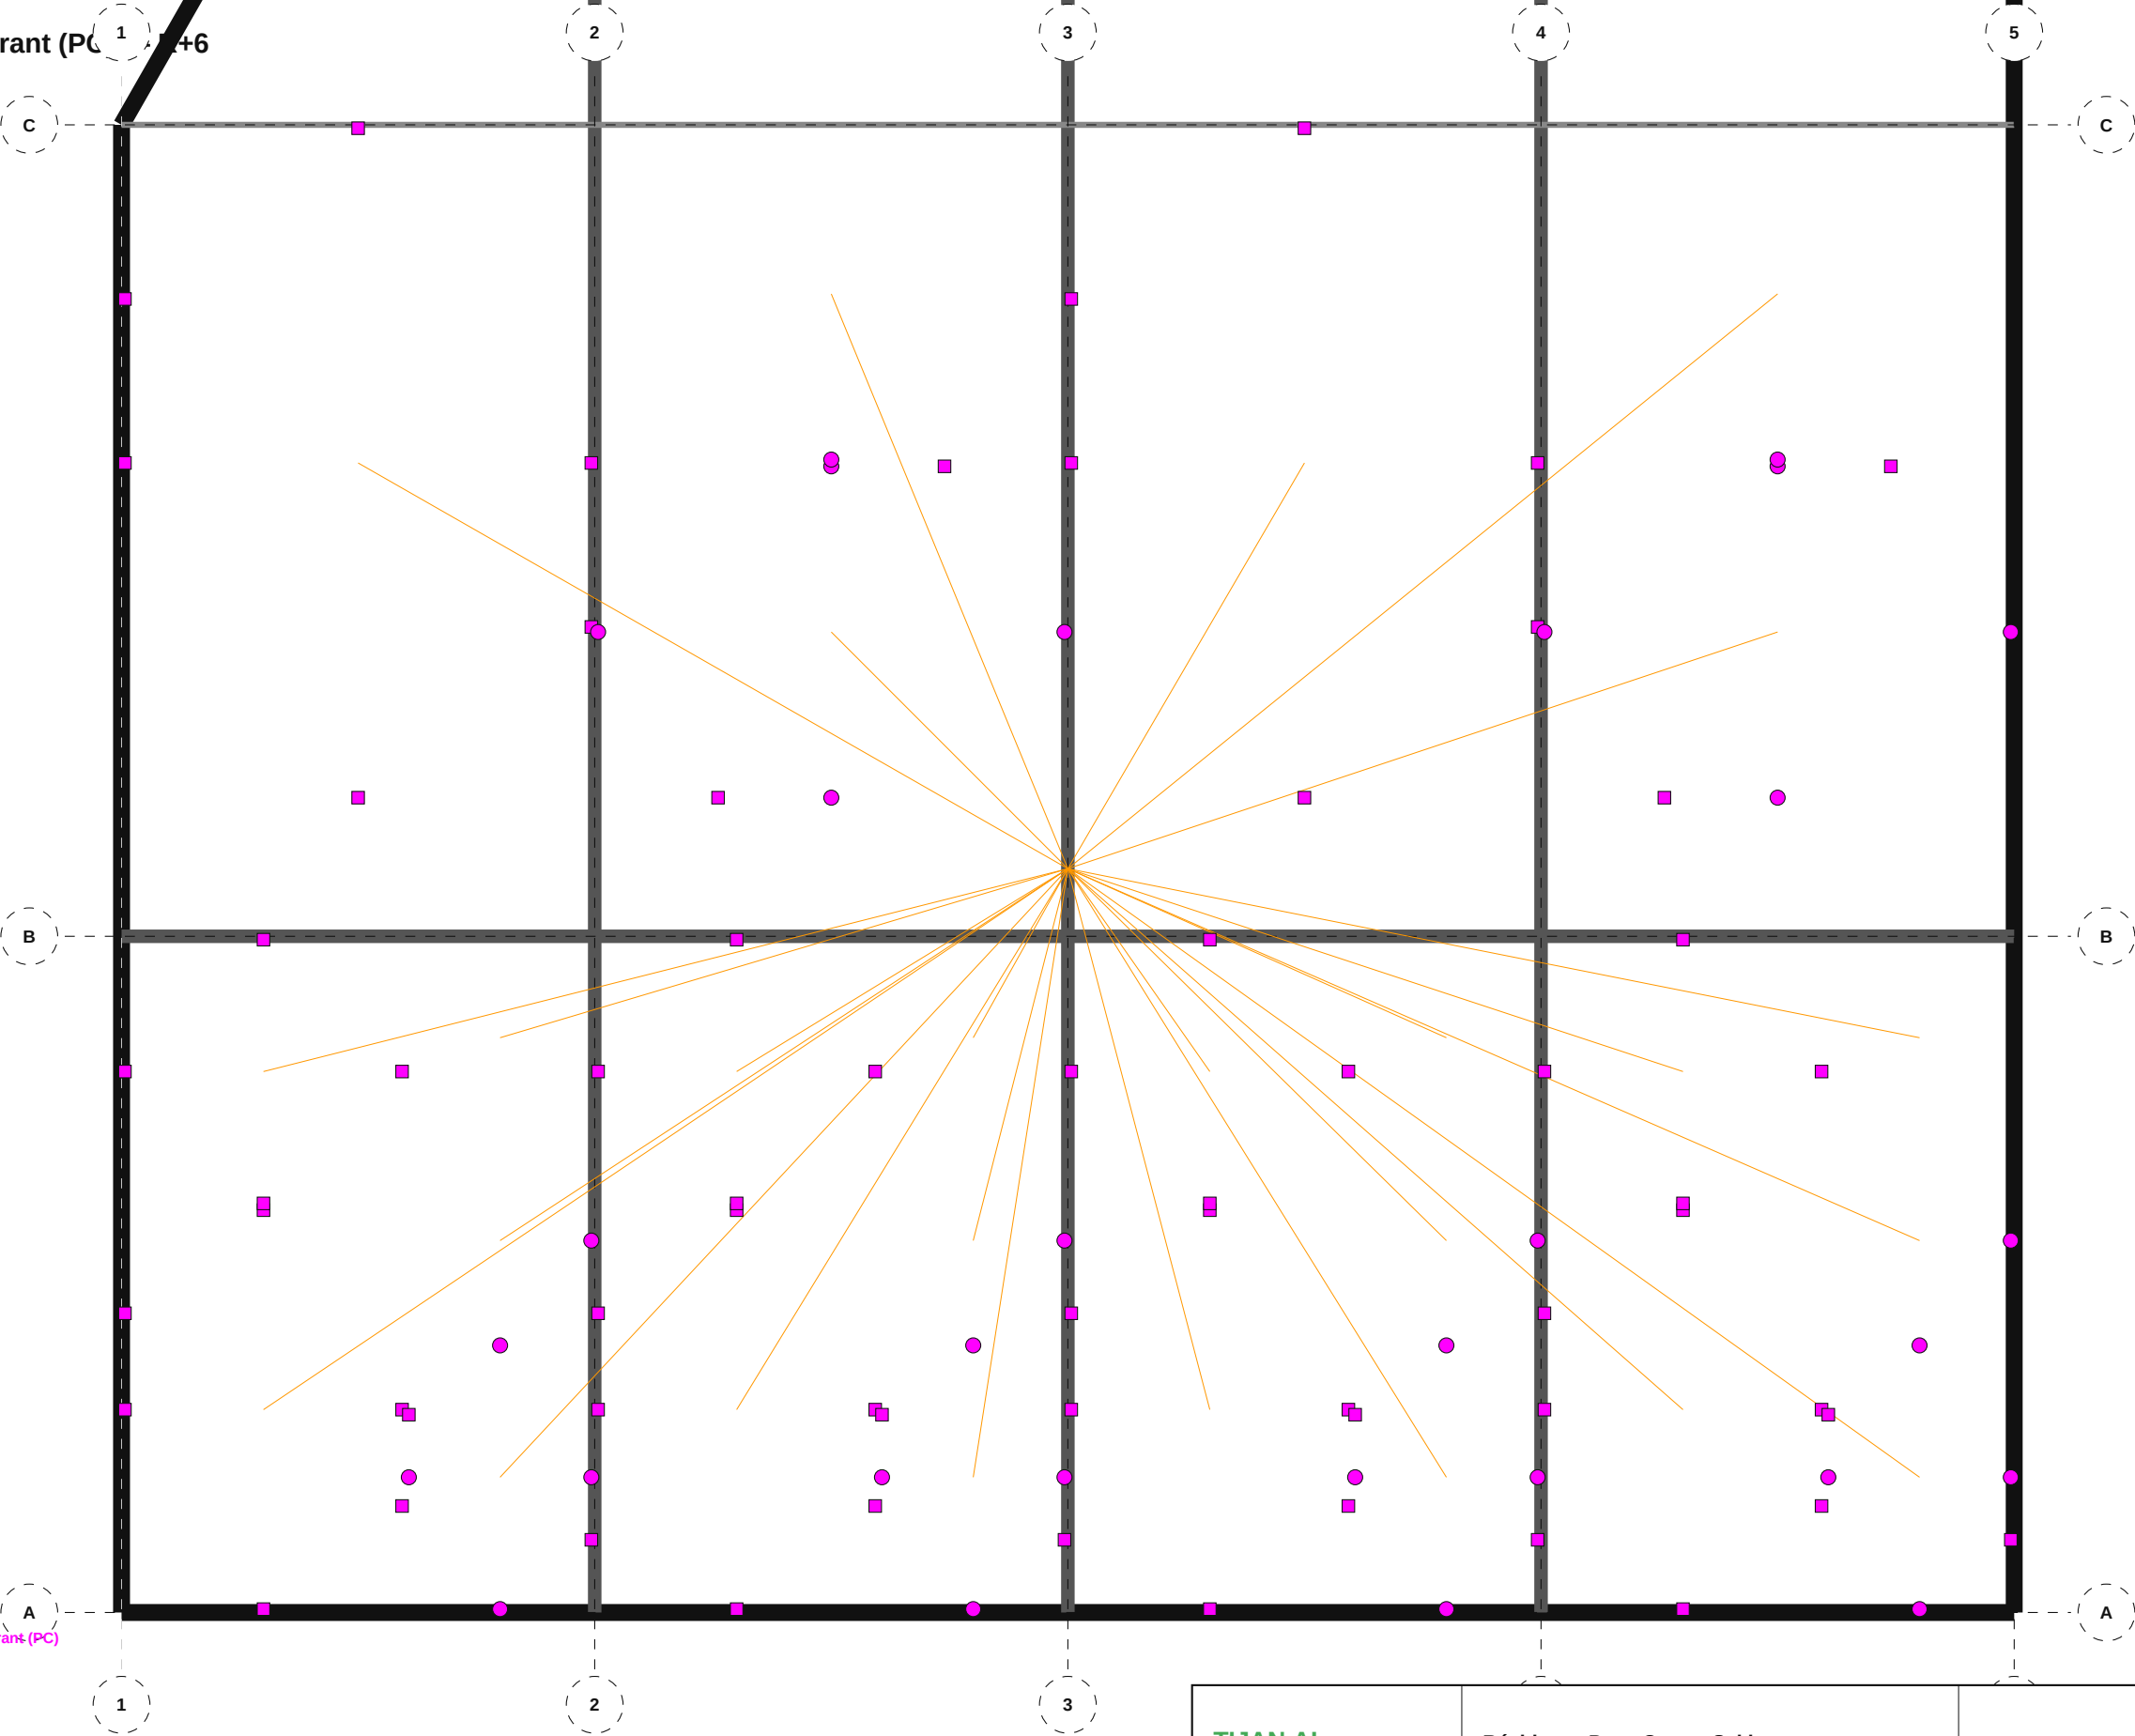


NOMENCLATURE — 510 HCU — Prises de Courant (PC)

- Prise 2P+T 16A: 64
- Prise plan de travail: 24
- Prise étanche 2P+T: 6

TIJAN AI Bureau d'Études Automatisé	Résidence Papa Oumar Sakho Dakar, Senegal	Éch: 1/100 Pl. 100/133
	510 HCU — Prises de Courant (PC) — R+6	
Date: 06/05/2026	Réf: 1711	BIM vHCU-100 Phase: APD

510 HCU — Prises de Courant (PC) — R+7

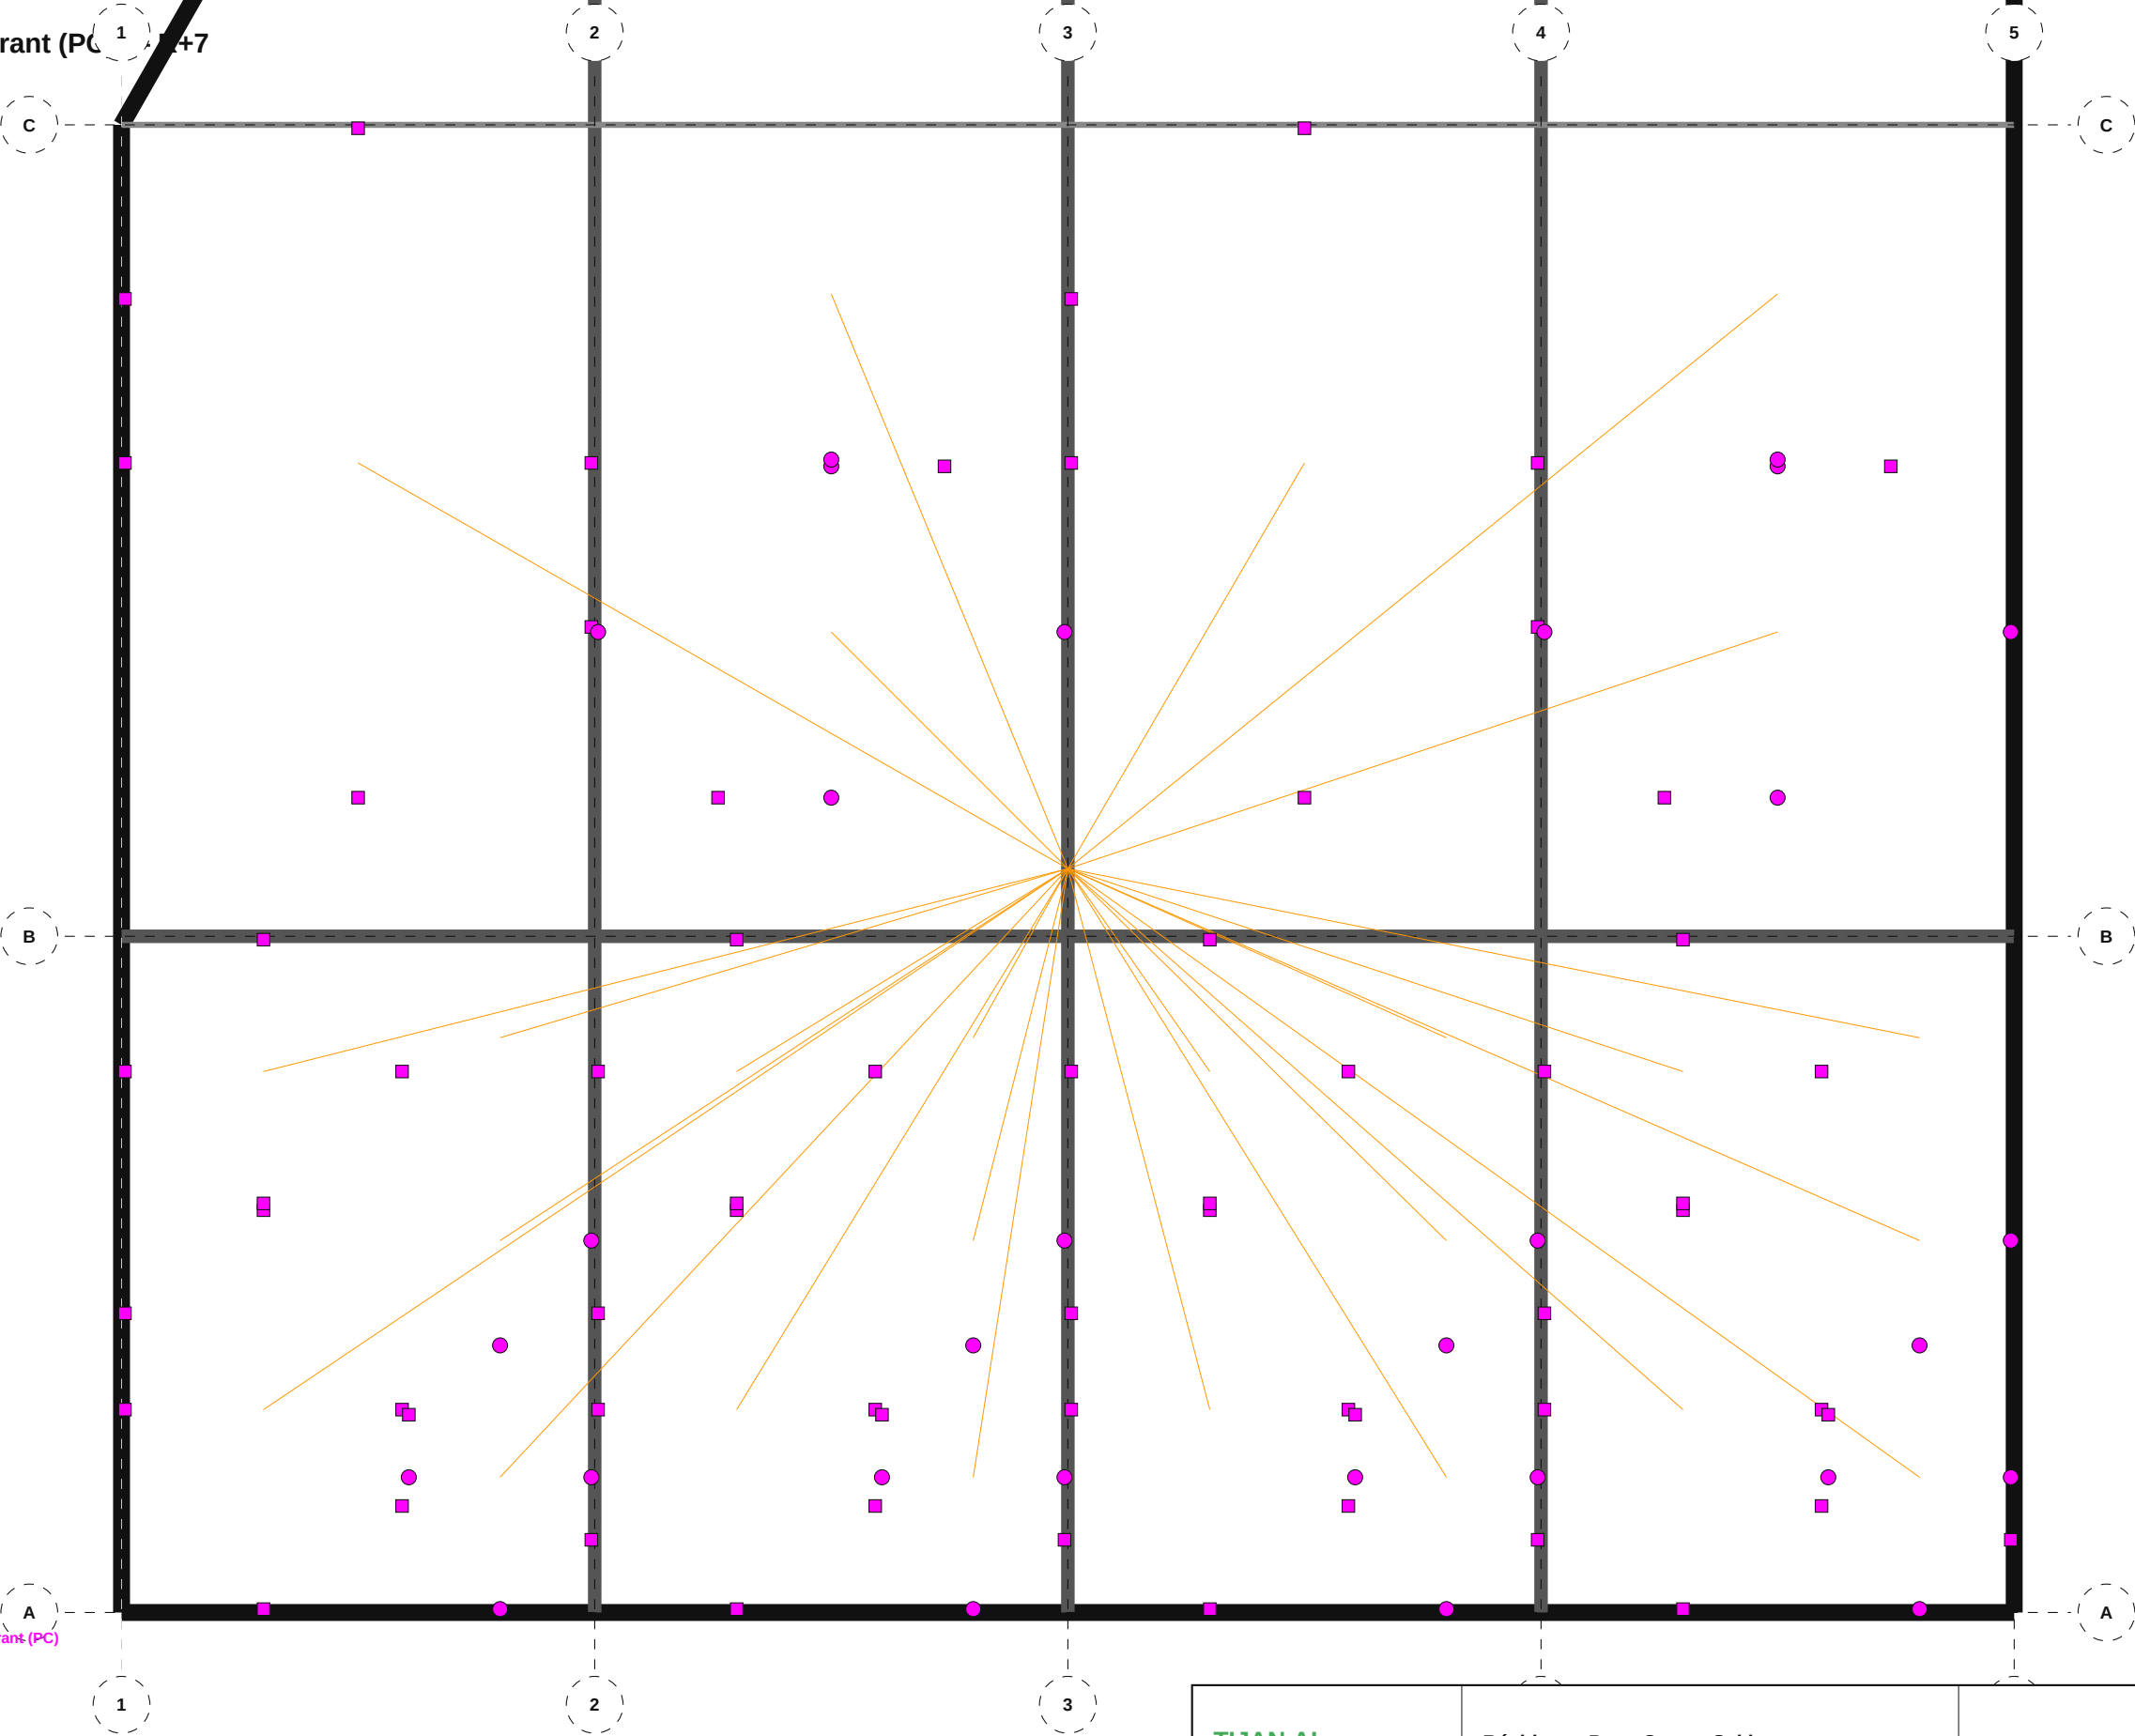


NOMENCLATURE — 510 HCU — Prises de Courant (PC)

- Prise 2P+T 16A: 64
- Prise plan de travail: 24
- Prise étanche 2P+T: 6

TIJAN AI Bureau d'Études Automatisé	Résidence Papa Oumar Sakho Dakar, Senegal	Éch: 1/100 Pl. 101/133
	510 HCU — Prises de Courant (PC) — R+7	
Date: 06/05/2026	Réf: 1711	BIM vHCU-101 Phase: APD


510 HCU — Prises de Courant (PC) — R+8 Terrasse

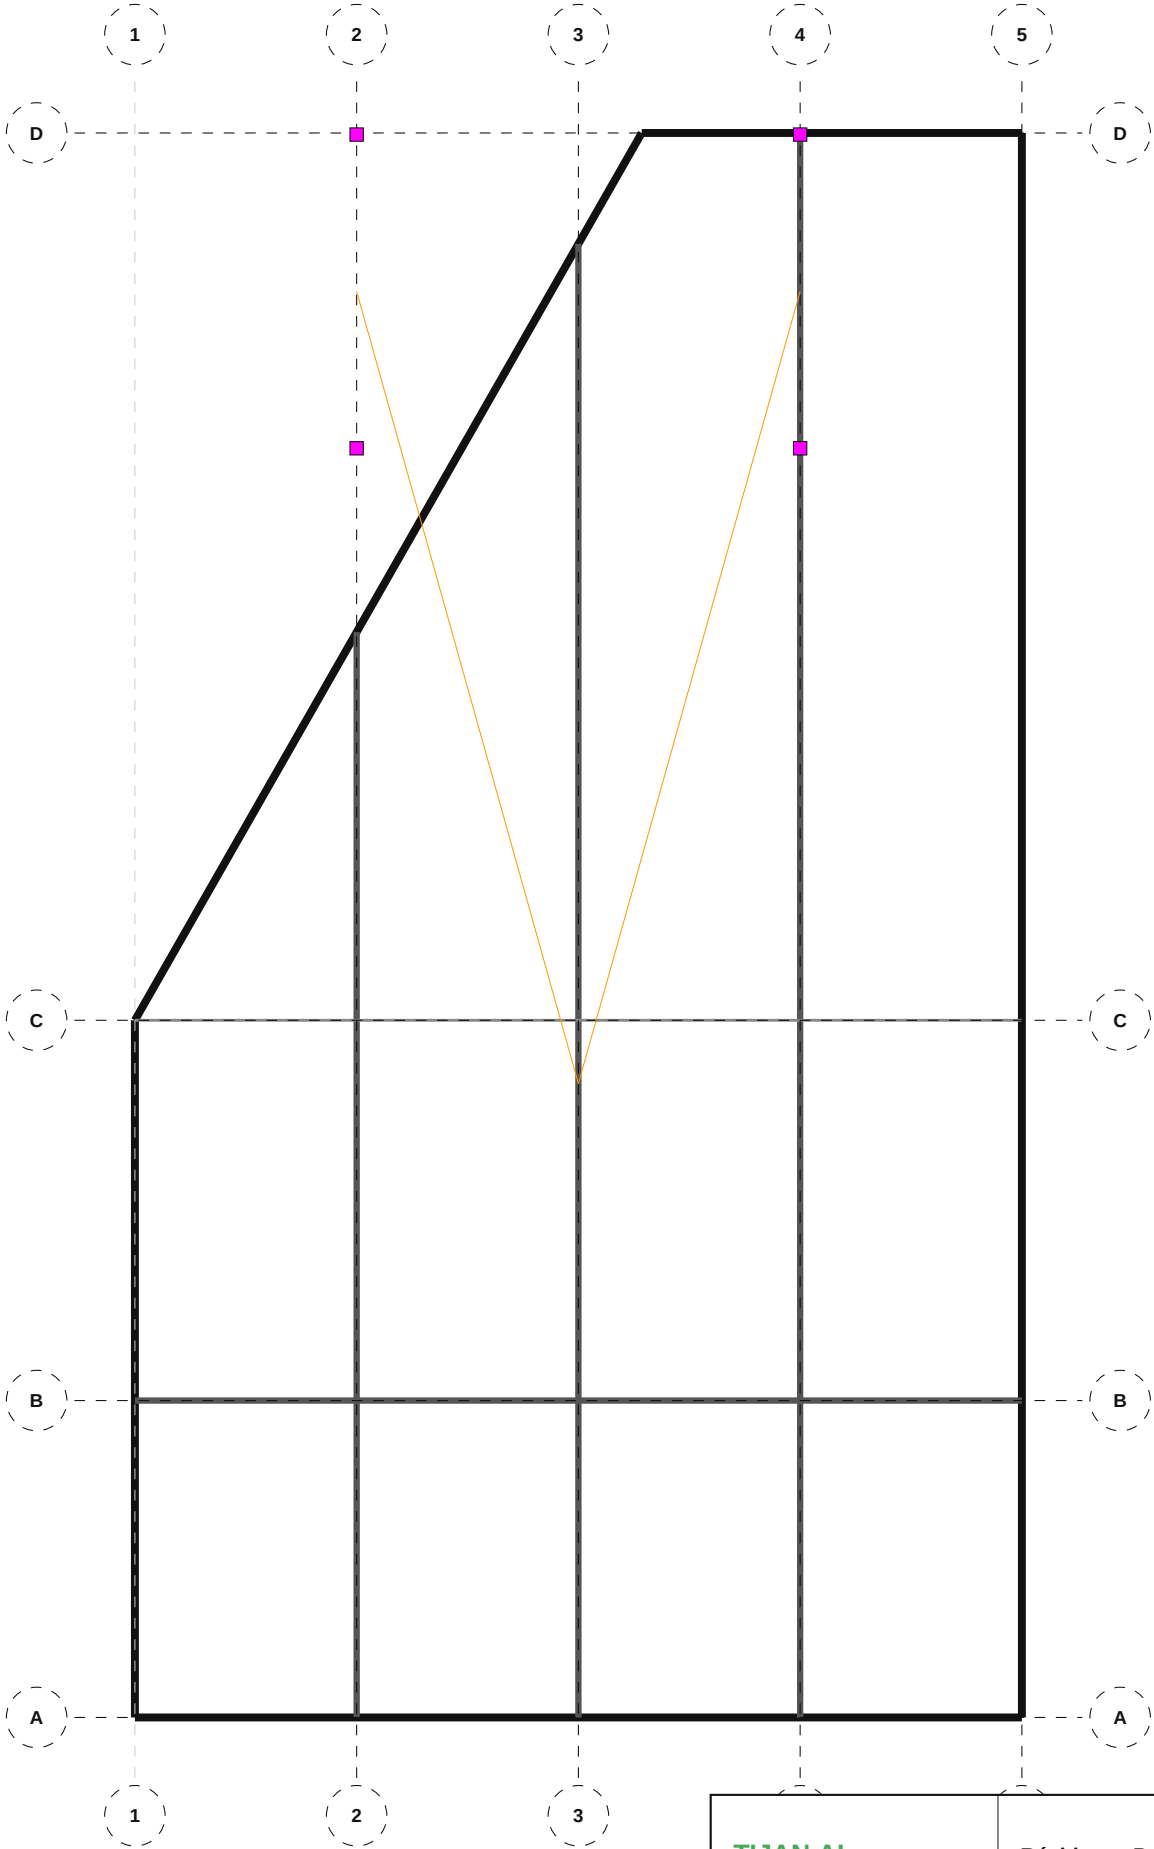

NOMENCLATURE — 510 HCU — Prises de Courant (PC)

• Prise 2P+T 16A: 4

TIJAN AI Bureau d'Études Automatisé	Résidence Papa Oumar Sakho Dakar, Senegal	Éch: 1/100 Pl. 102/133
	510 HCU — Prises de Courant (PC) — R+8 Terrasse	
Date: 06/05/2026	Réf: 1711	BIM vHCU-102 Phase: APD

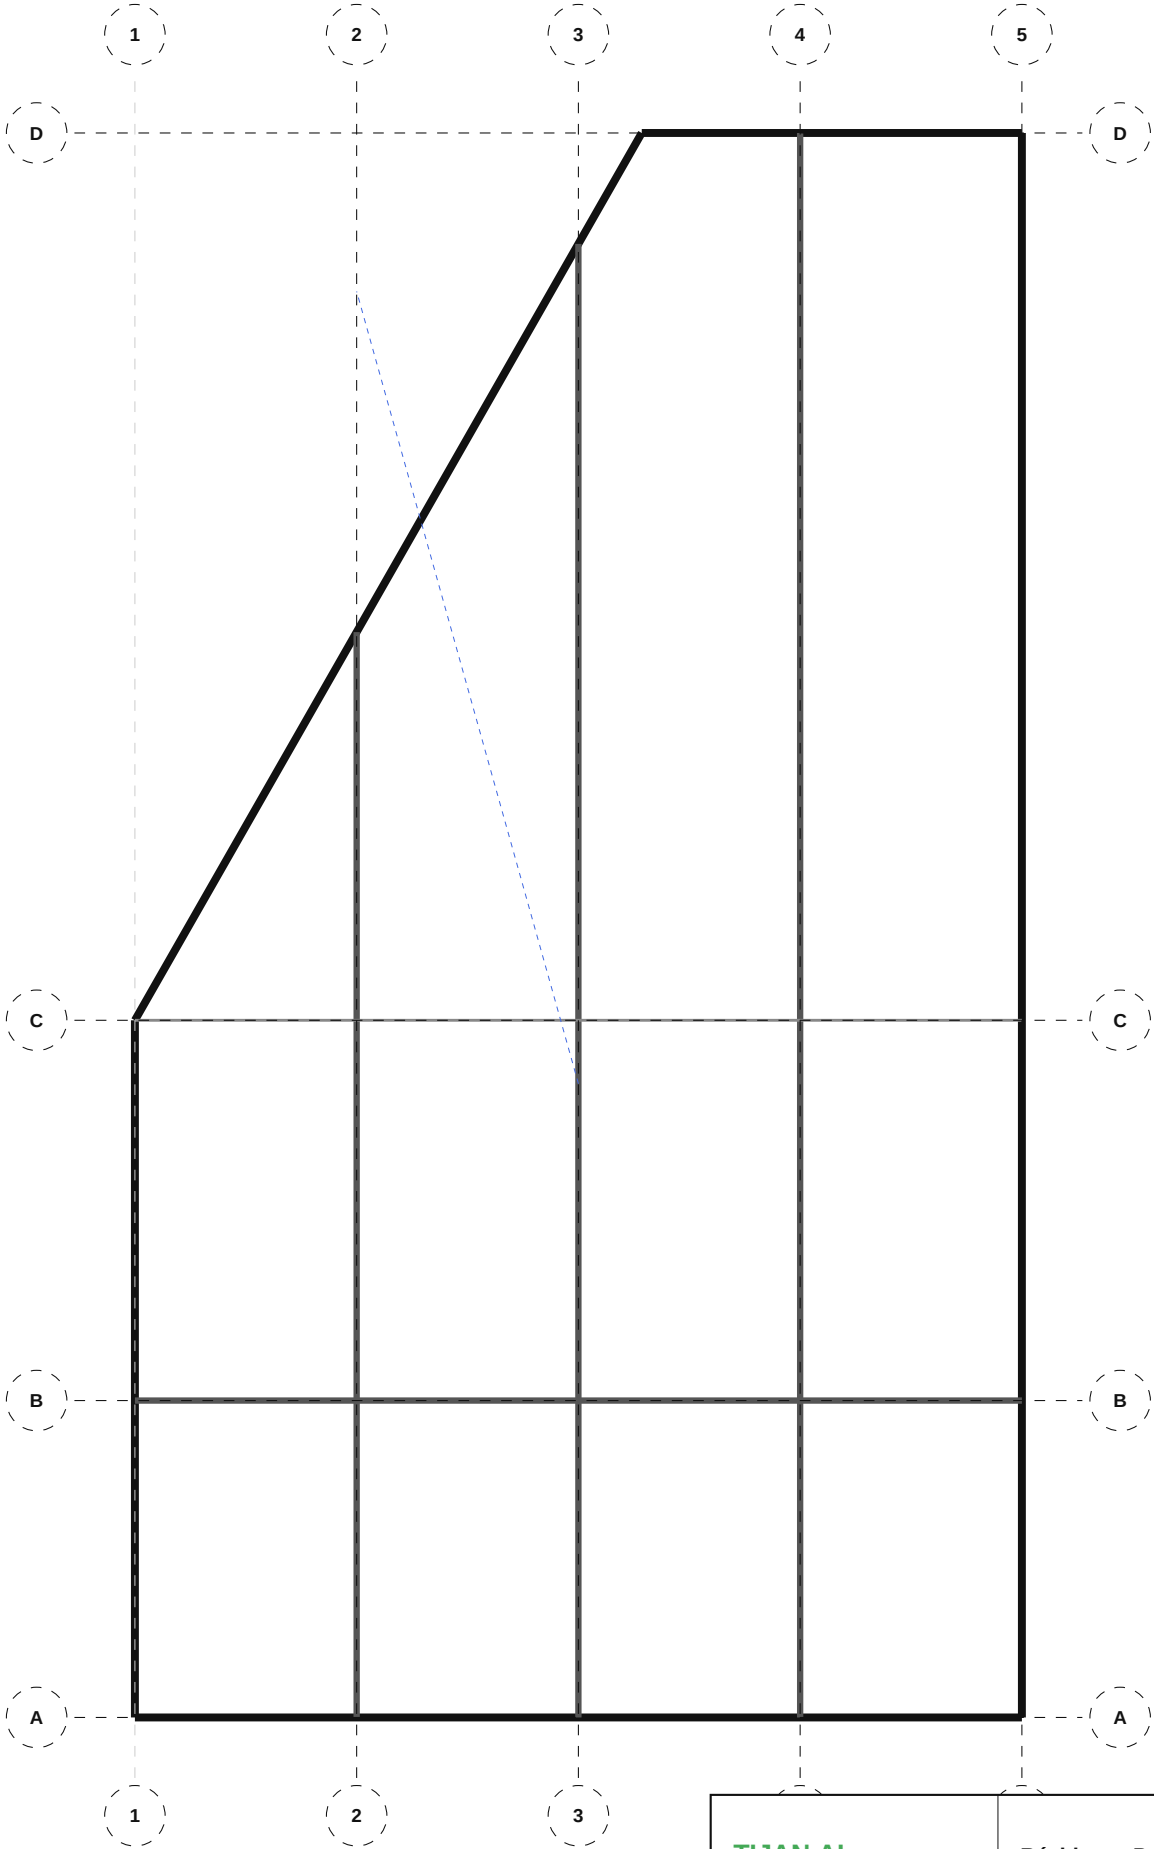

TIJAN AI Bureau d'Études Automatisé	Résidence Papa Oumar Sakho Dakar, Senegal	Éch: 1/100 Pl. 103/133
	520 LCU — Courants Faibles — Sous-Sol	
Date: 06/05/2026	Réf: 1711	BIM v.LCU-103 Phase: APD

520 LCU — Courants Faibles — RDC

1

2

3

4

5

B

B

A

A

NOMENCLATURE — 520 LCU — Courants Faibles

• Prise RJ45: 2

1

2

3

4

5

TIJAN AI

Bureau d'Études Automatisé

Résidence Papa Oumar Sakho

Dakar, Senegal

Éch: 1/100

Pl. 104/133


520 LCU — Courants Faibles — RDC

Date: 06/05/2026

Réf: 1711

BIM v.LCU-104


Phase: APD

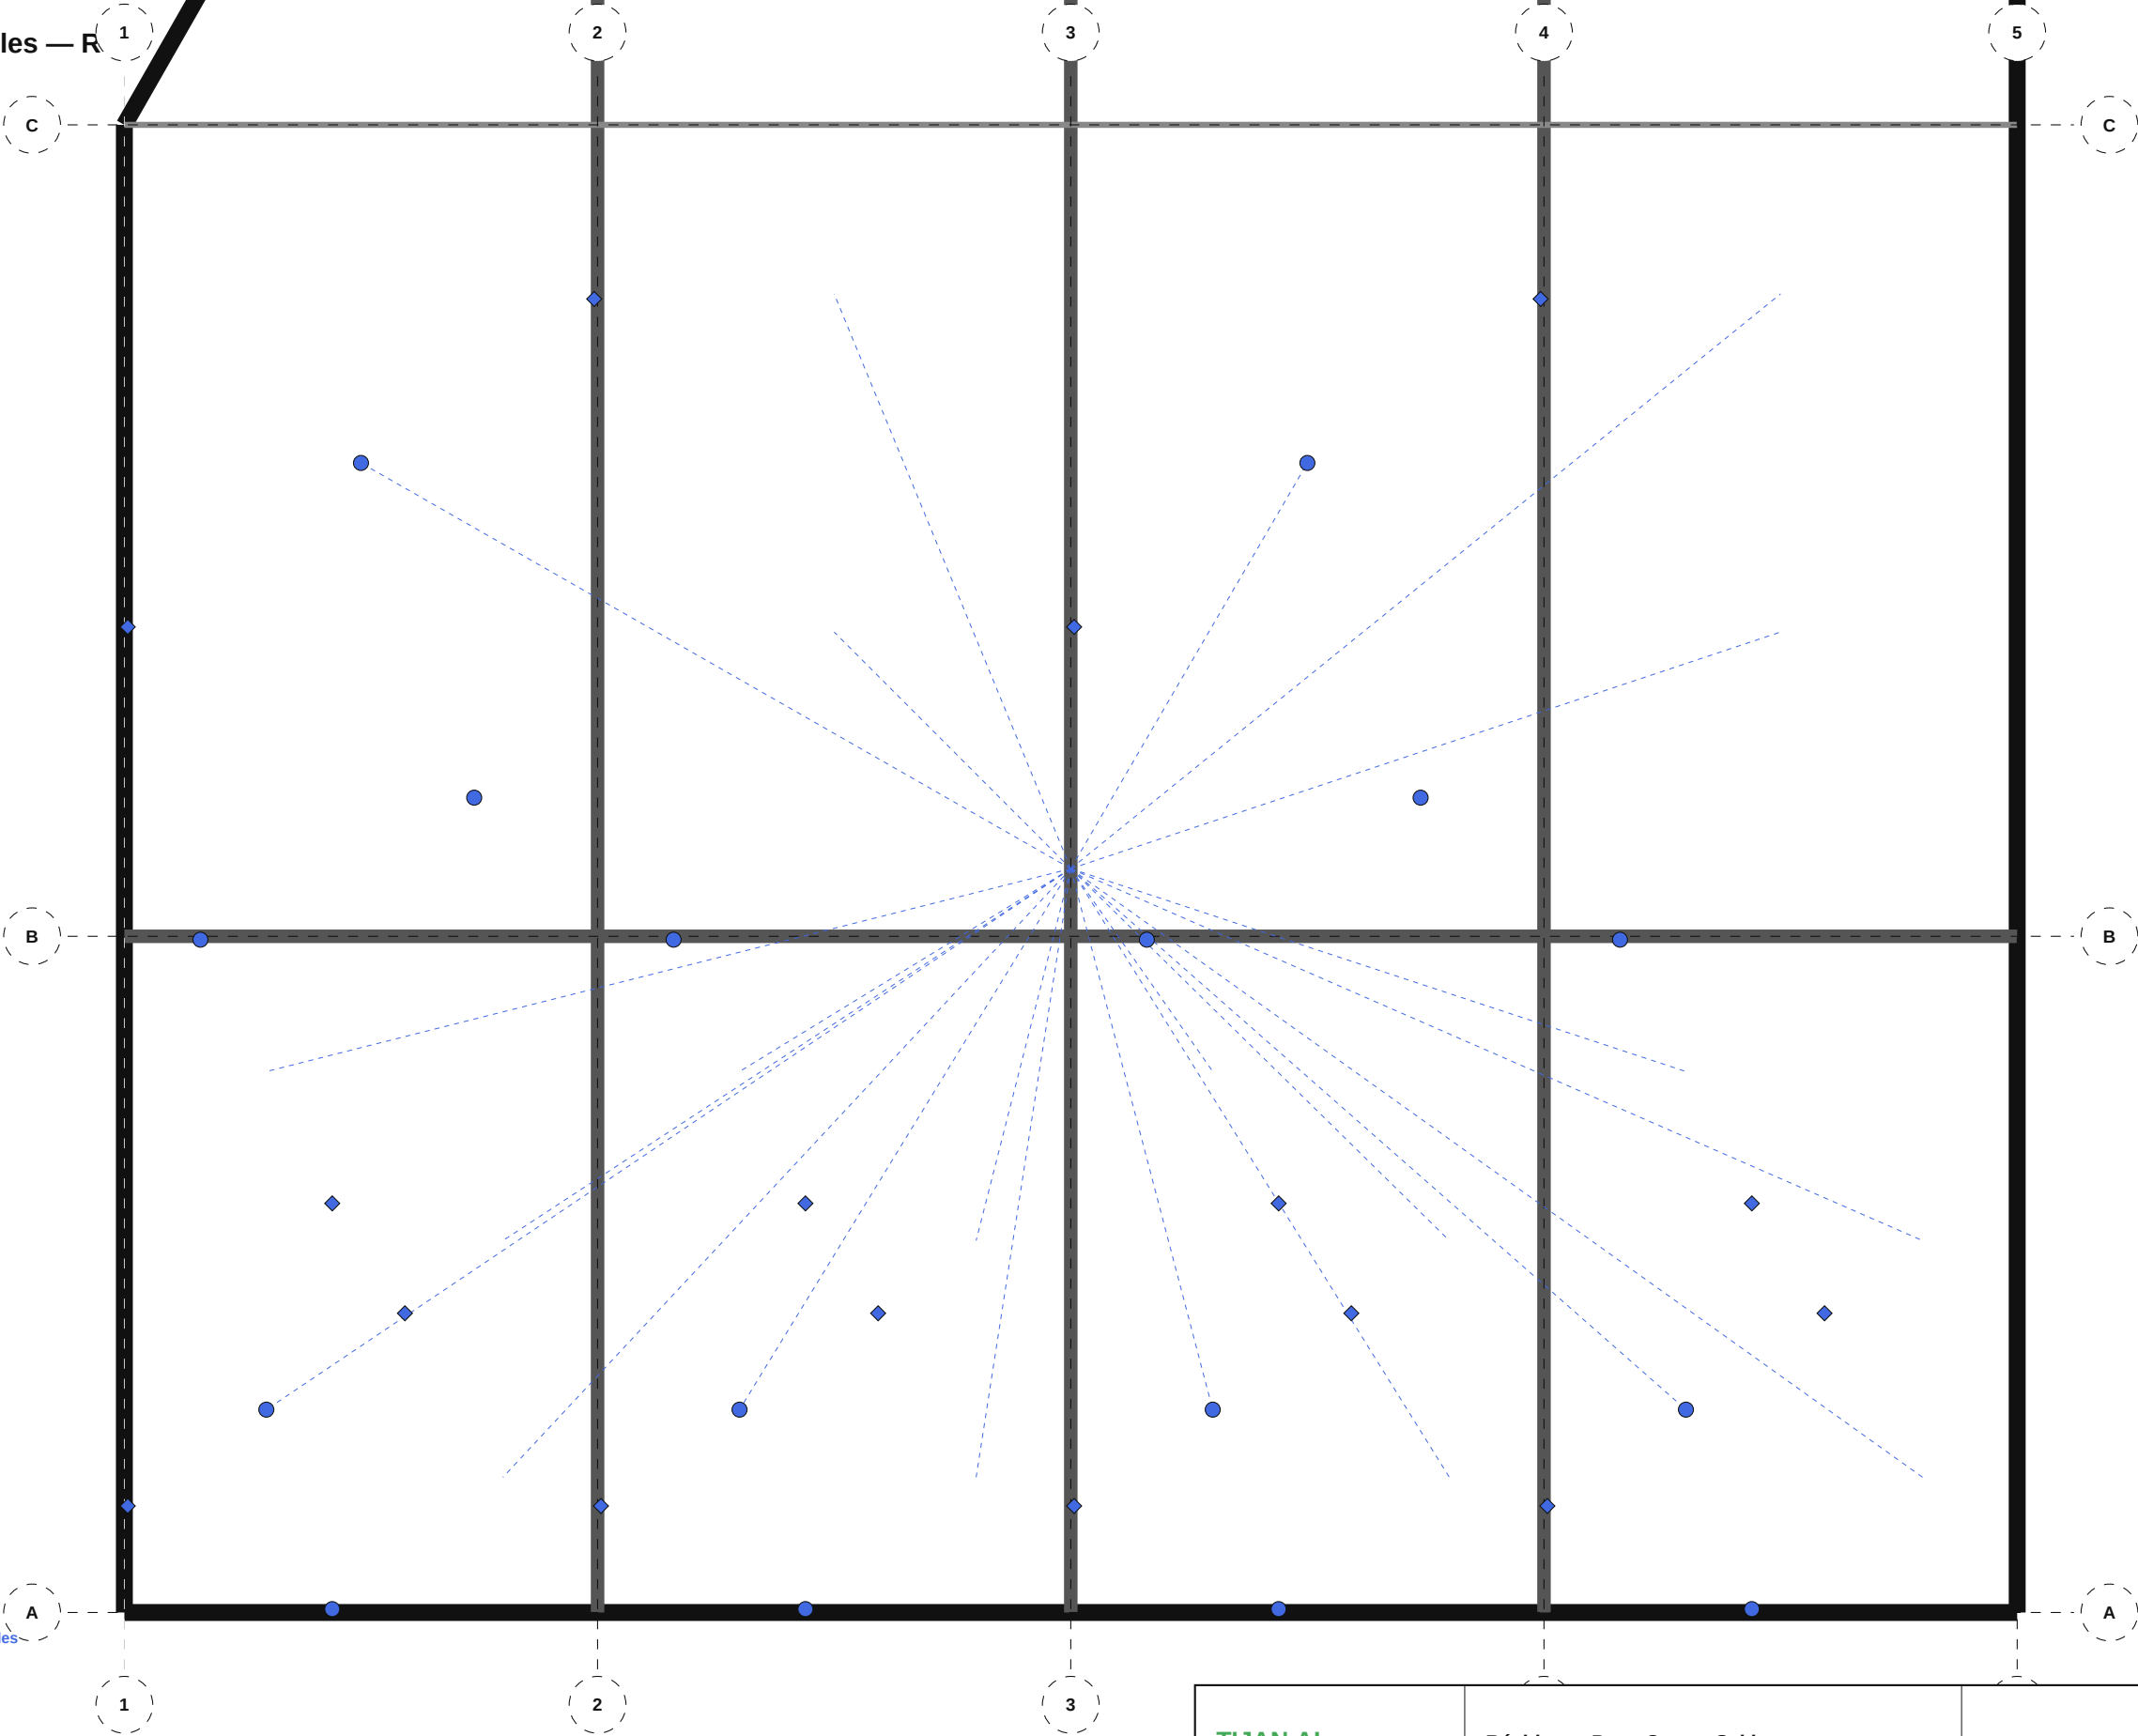

NOMENCLATURE — 520 LCU — Courants Faibles

- Prise RJ45: 16
- Prise TV: 10
- Point d'accès WiFi: 6


TIJAN AI Bureau d'Études Automatisé	Résidence Papa Oumar Sakho Dakar, Senegal	Éch: 1/100 Pl. 105/133
	520 LCU — Courants Faibles — R+1	
Date: 06/05/2026	Réf: 1711	BIM vLCU-105 Phase: APD

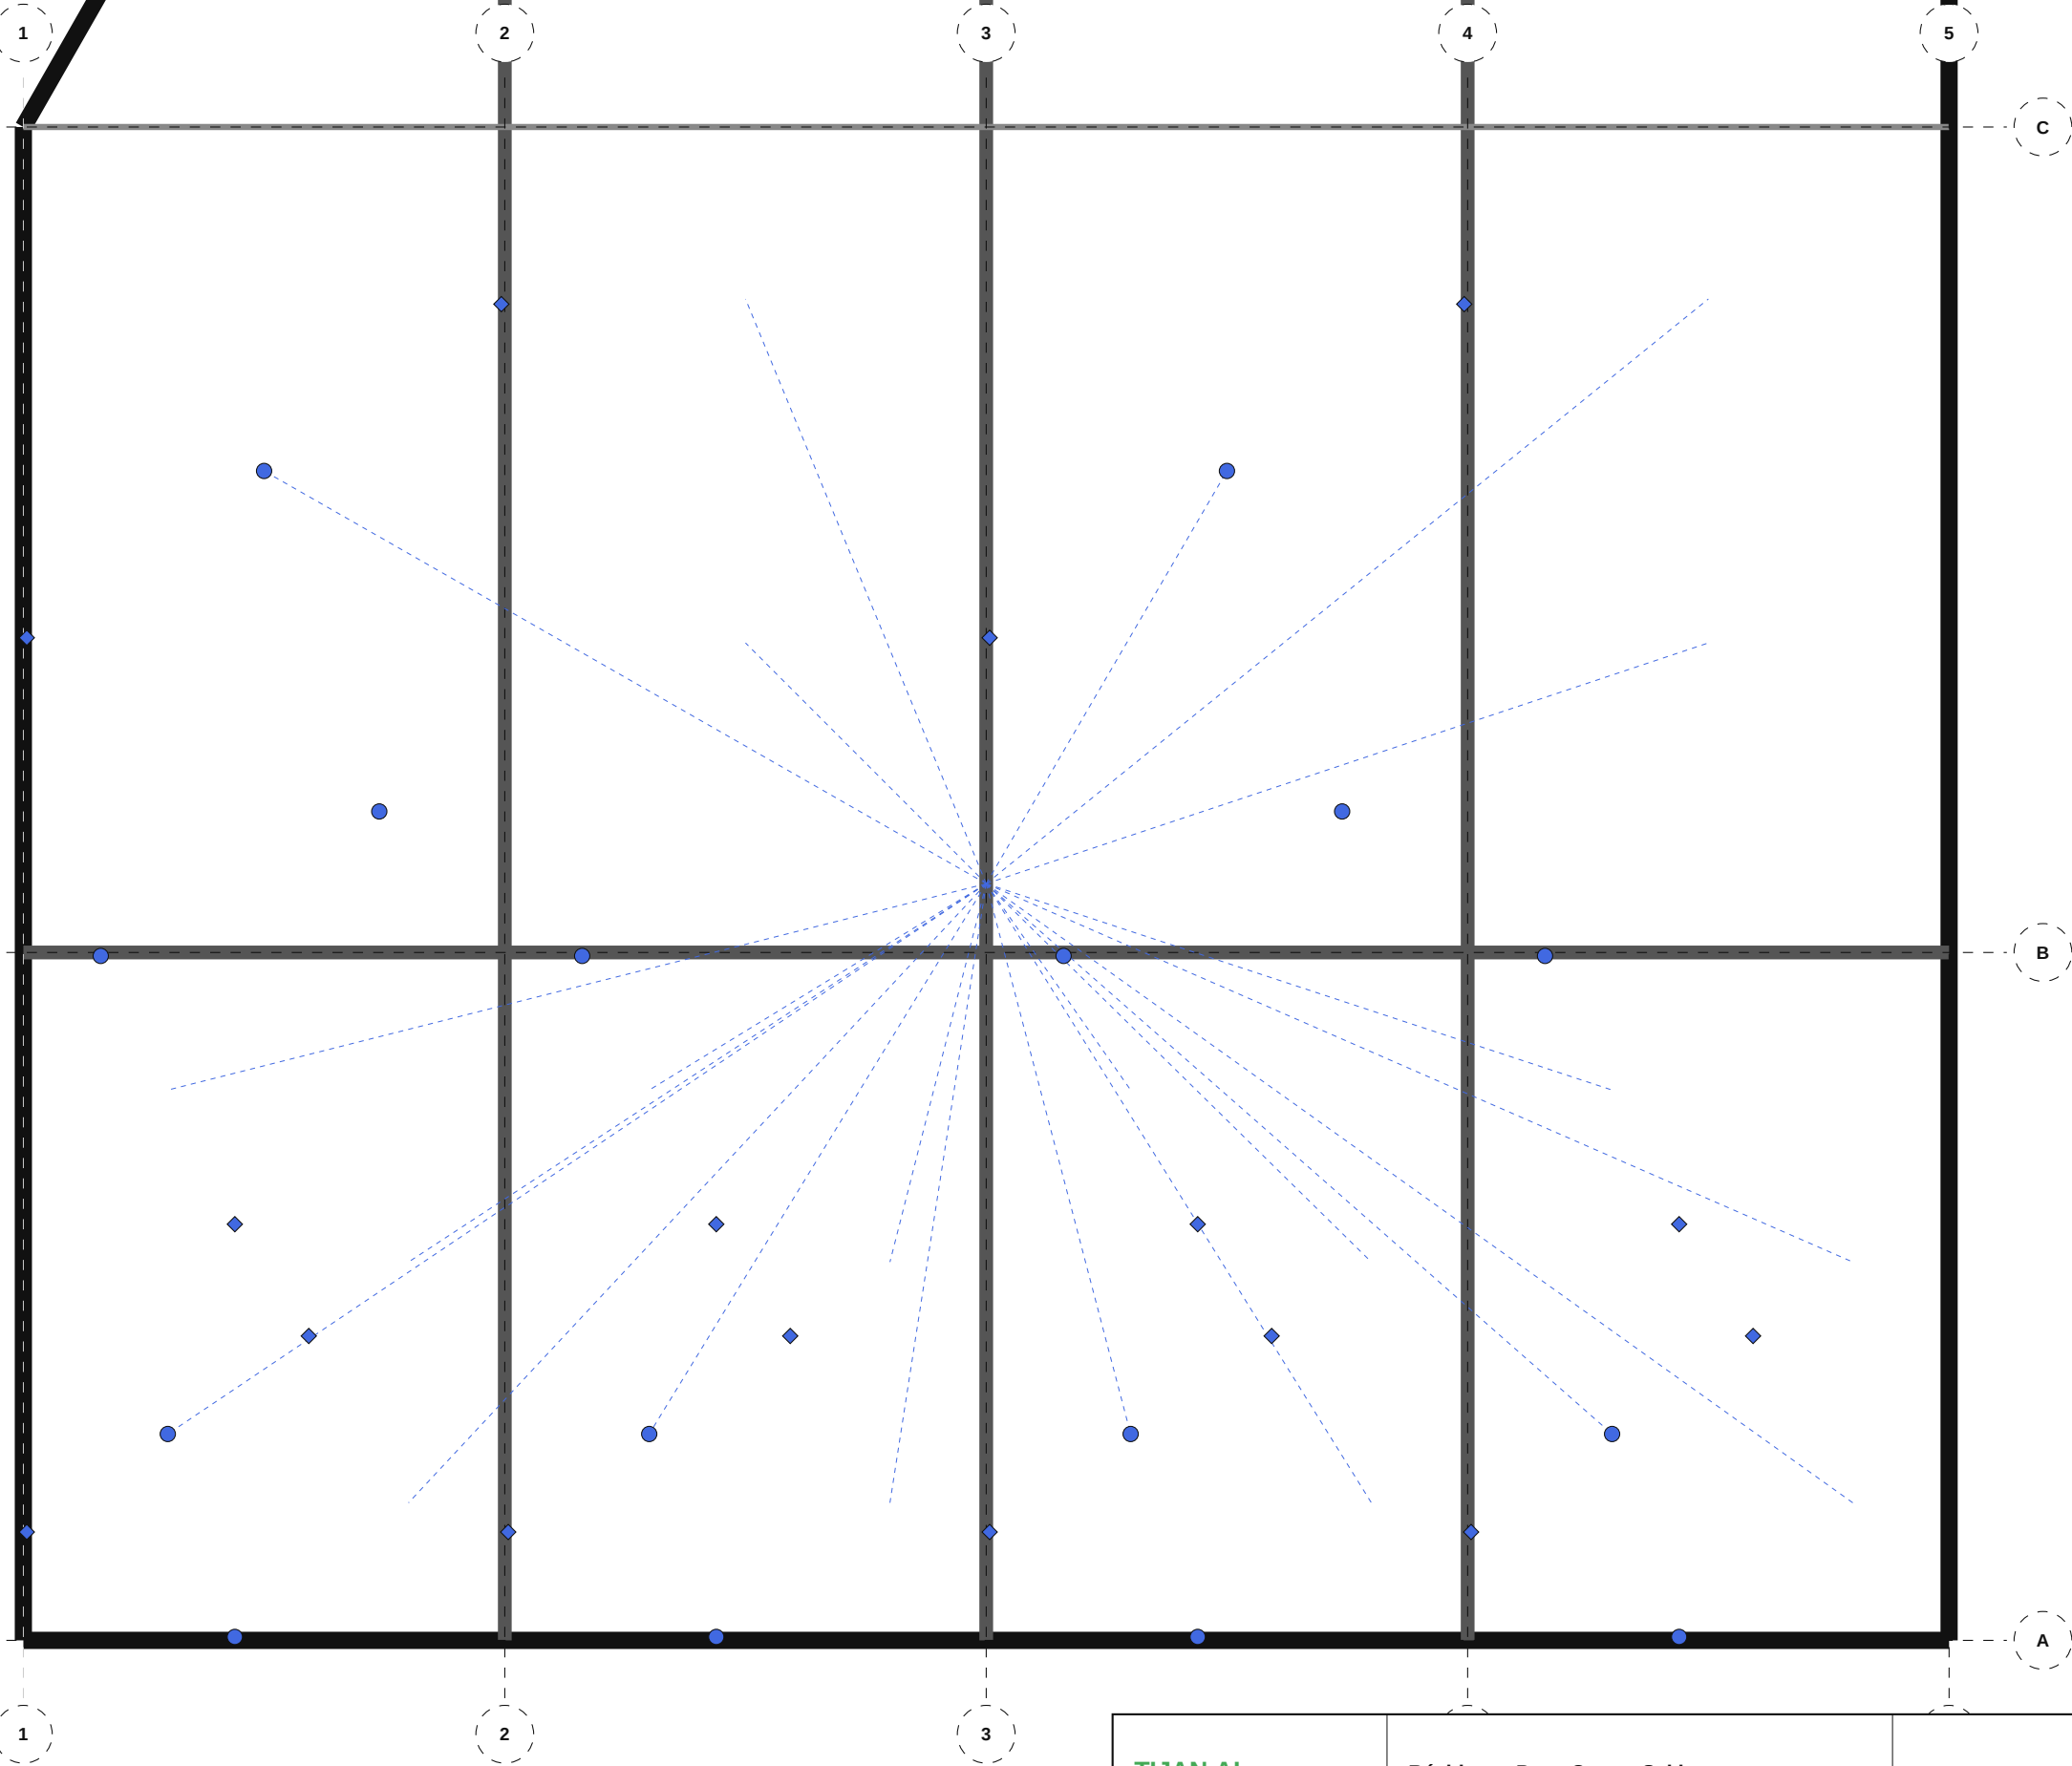

NOMENCLATURE — 520 LCU — Courants Faibles

- Prise RJ45: 16
- Prise TV: 10
- Point d'accès WiFi: 6


TIJAN AI Bureau d'Études Automatisé	Résidence Papa Oumar Sakho Dakar, Senegal	Éch: 1/100 Pl. 106/133
	520 LCU — Courants Faibles — R+2	
Date: 06/05/2026	Réf: 1711	BIM vLCU-106 Phase: APD

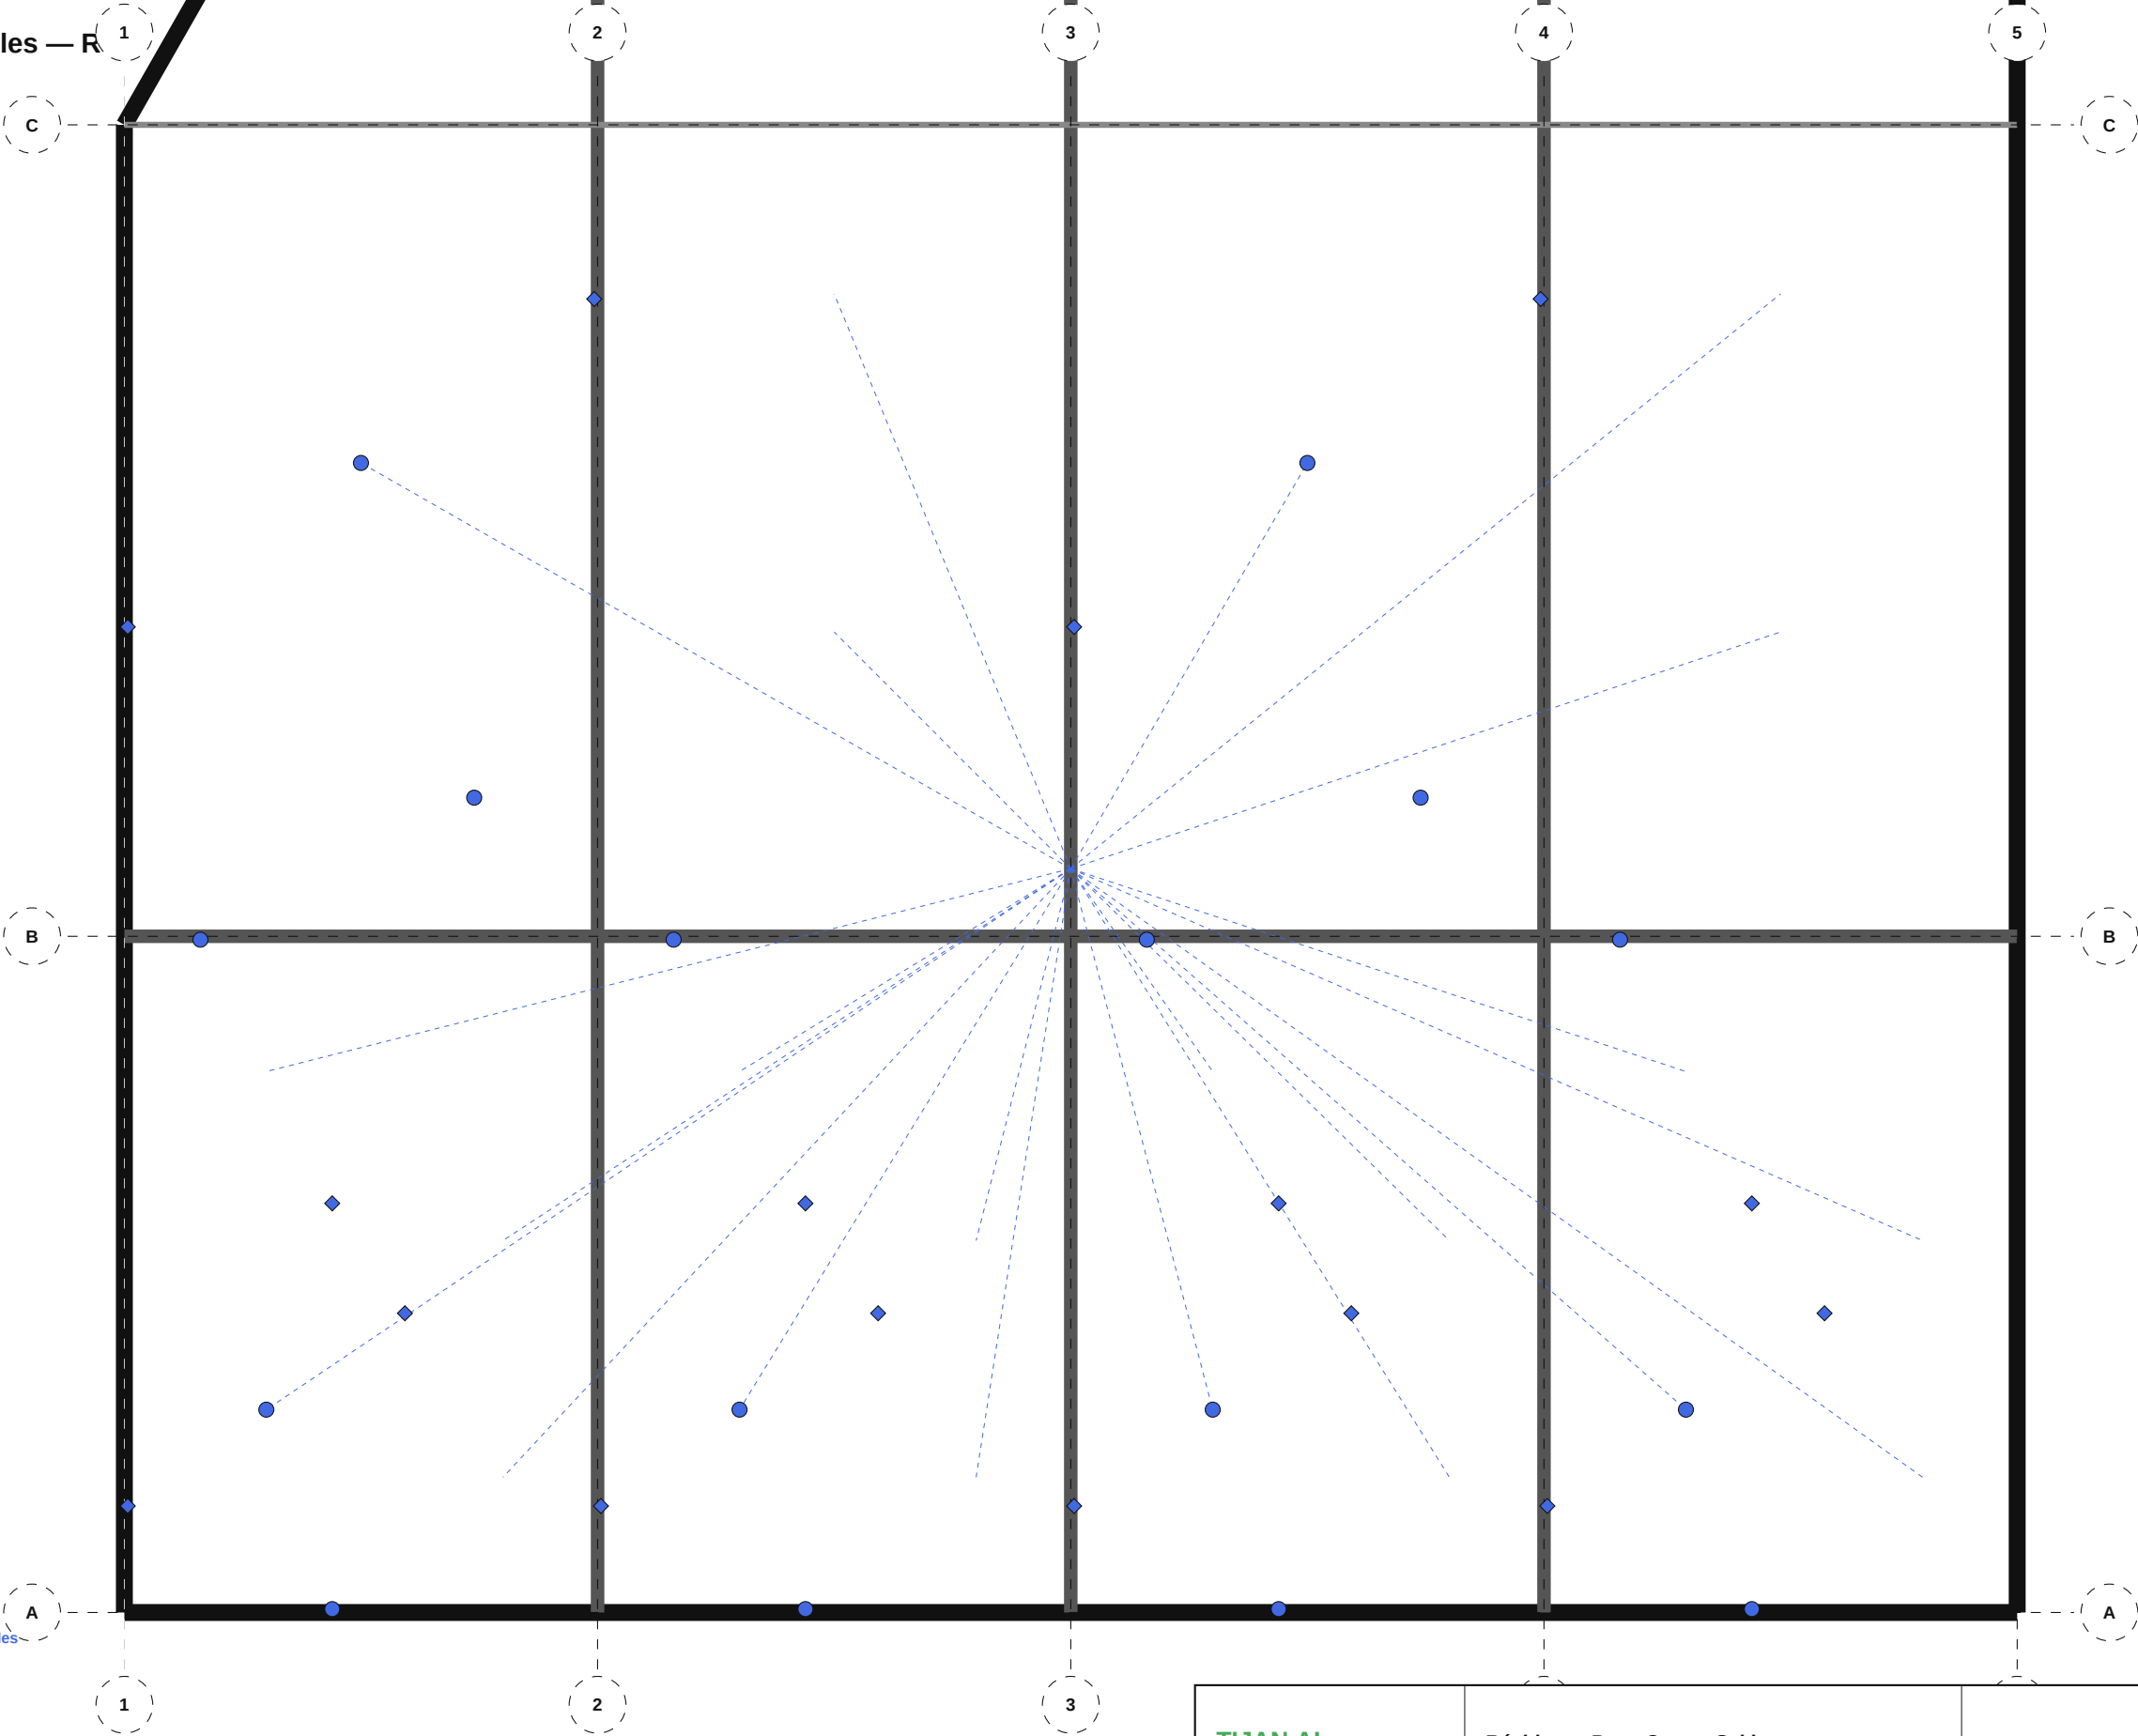

NOMENCLATURE — 520 LCU — Courants Faibles

- Prise RJ45: 16
- Prise TV: 10
- Point d'accès WiFi: 6


TIJAN AI Bureau d'Études Automatisé	Résidence Papa Oumar Sakho Dakar, Senegal	Éch: 1/100 Pl. 107/133
	520 LCU — Courants Faibles — R+3	
Date: 06/05/2026	Réf: 1711	BIM vLCU-107 Phase: APD

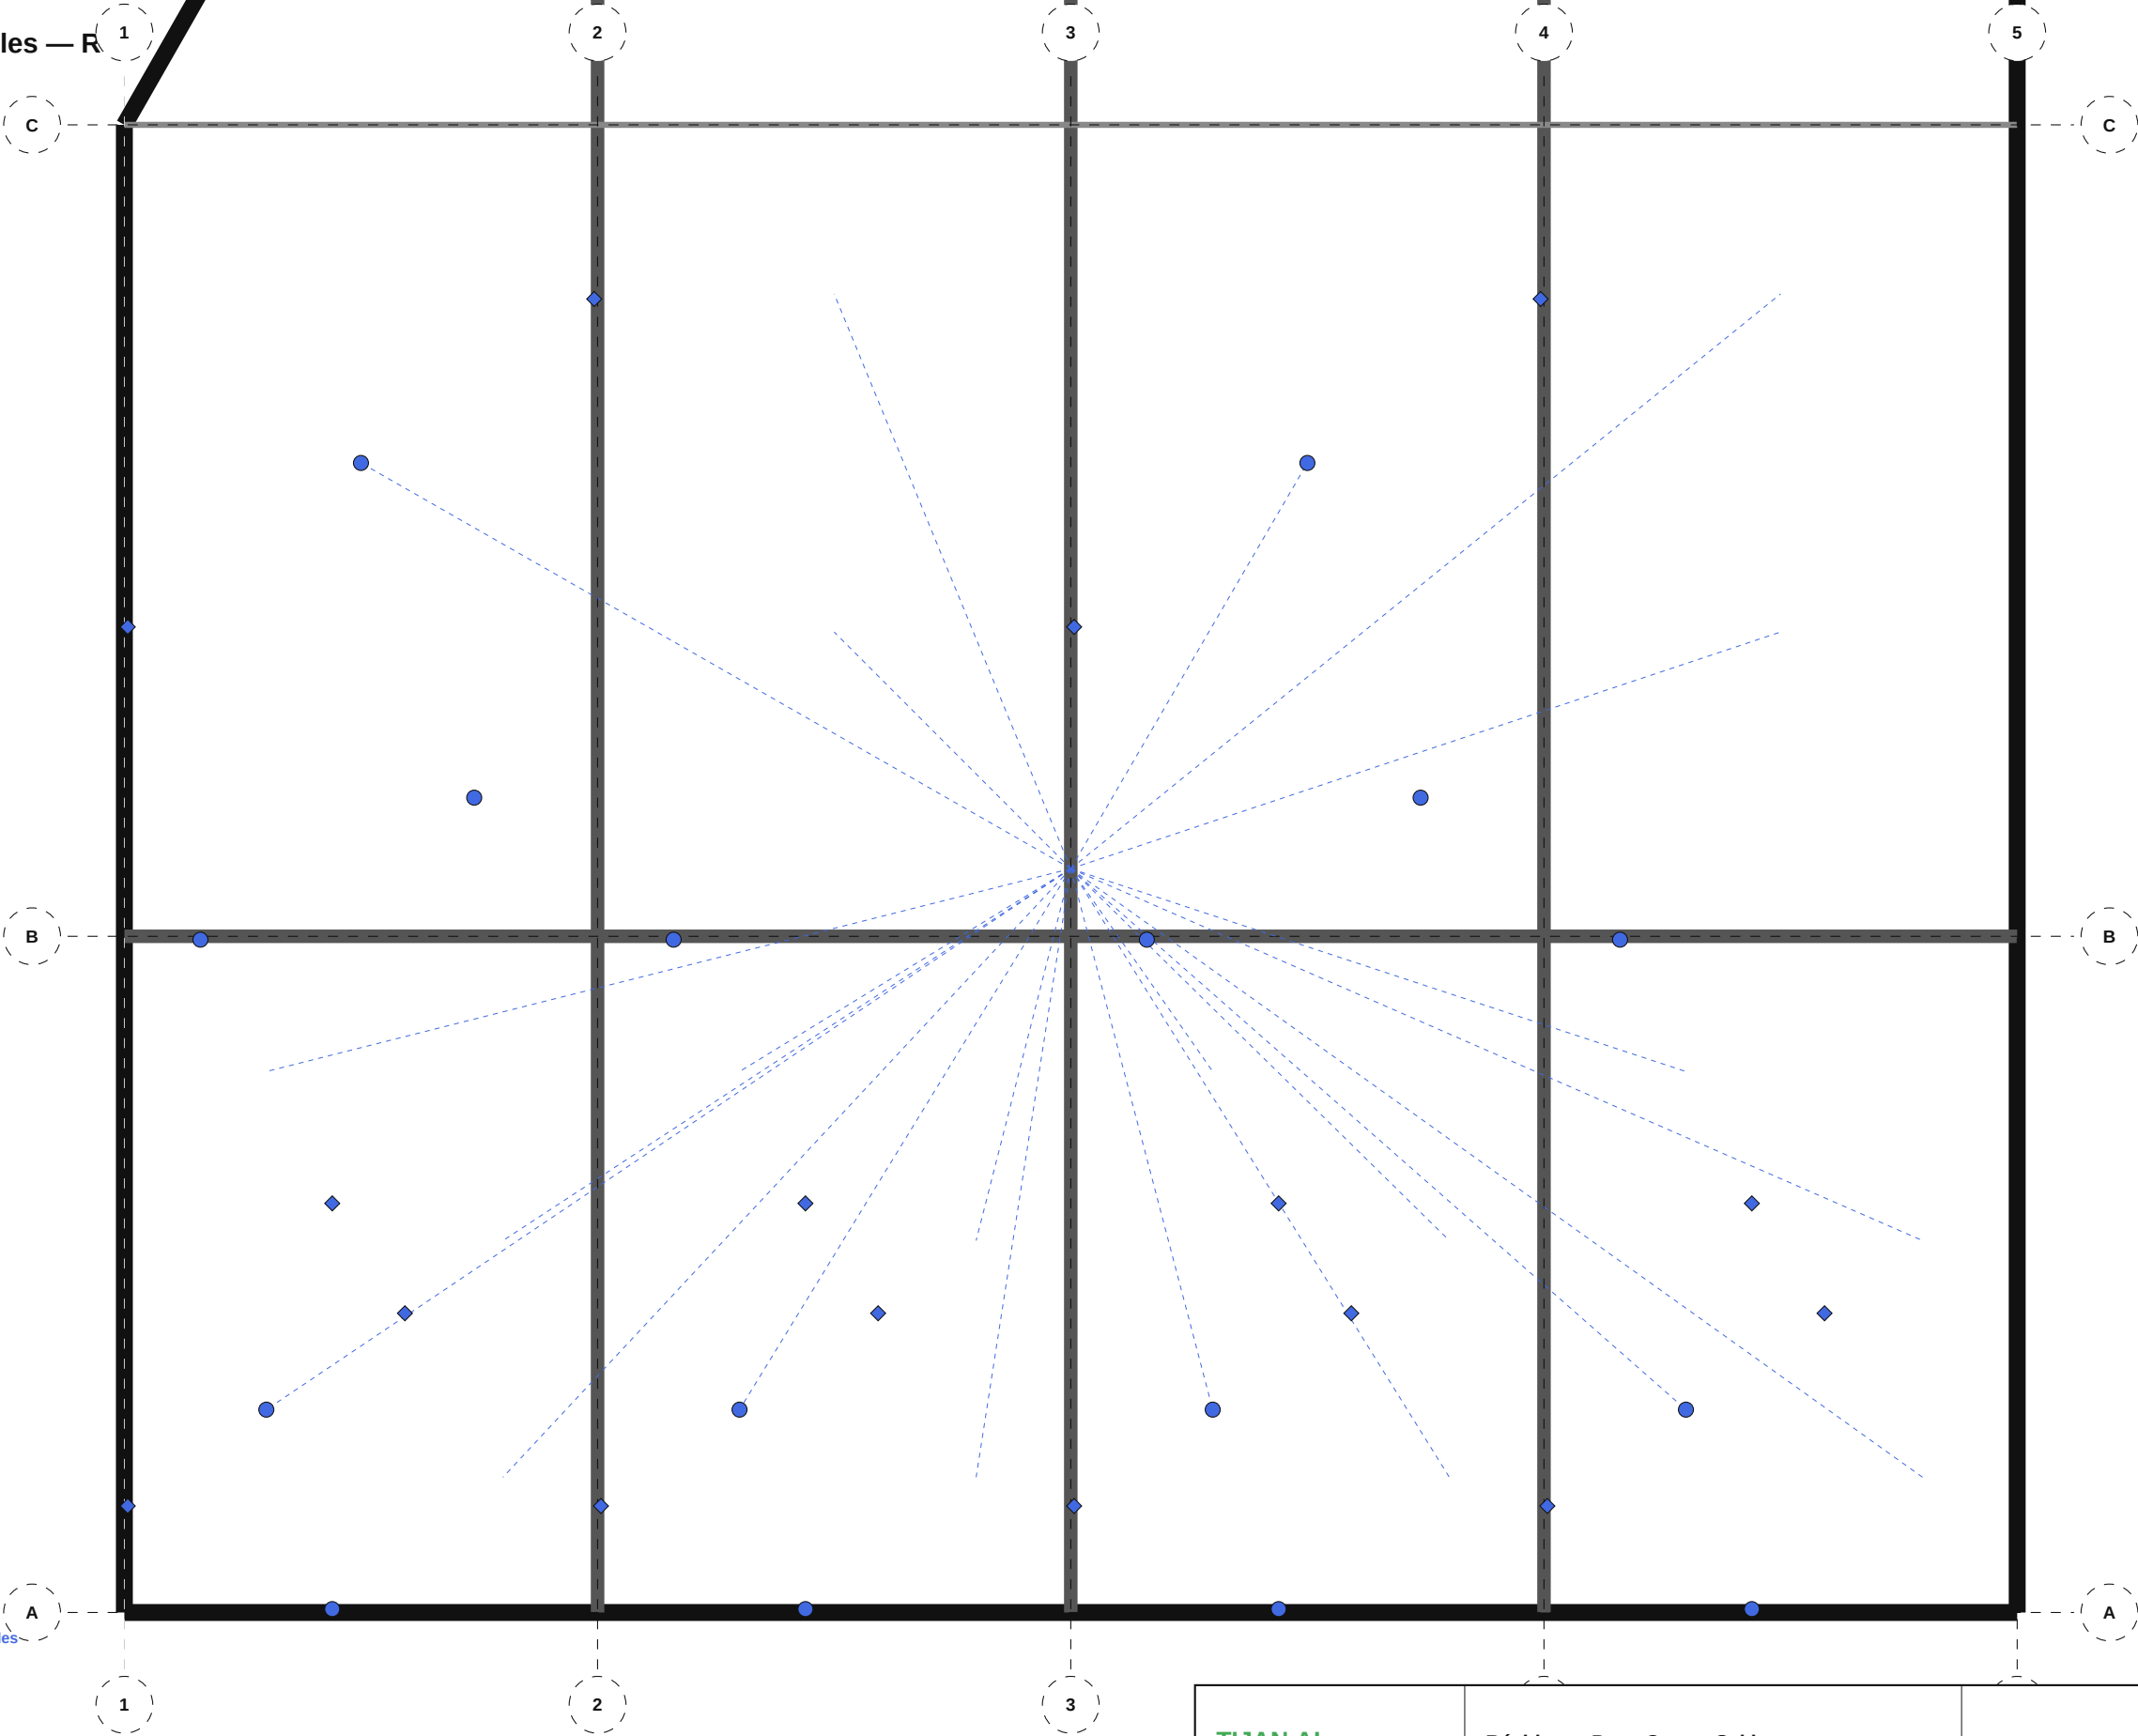

NOMENCLATURE — 520 LCU — Courants Faibles

- Prise RJ45: 16
- Prise TV: 10
- Point d'accès WiFi: 6


TIJAN AI Bureau d'Études Automatisé	Résidence Papa Oumar Sakho Dakar, Senegal	Éch: 1/100 Pl. 108/133
	520 LCU — Courants Faibles — R+4	
Date: 06/05/2026	Réf: 1711	BIM vLCU-108 Phase: APD

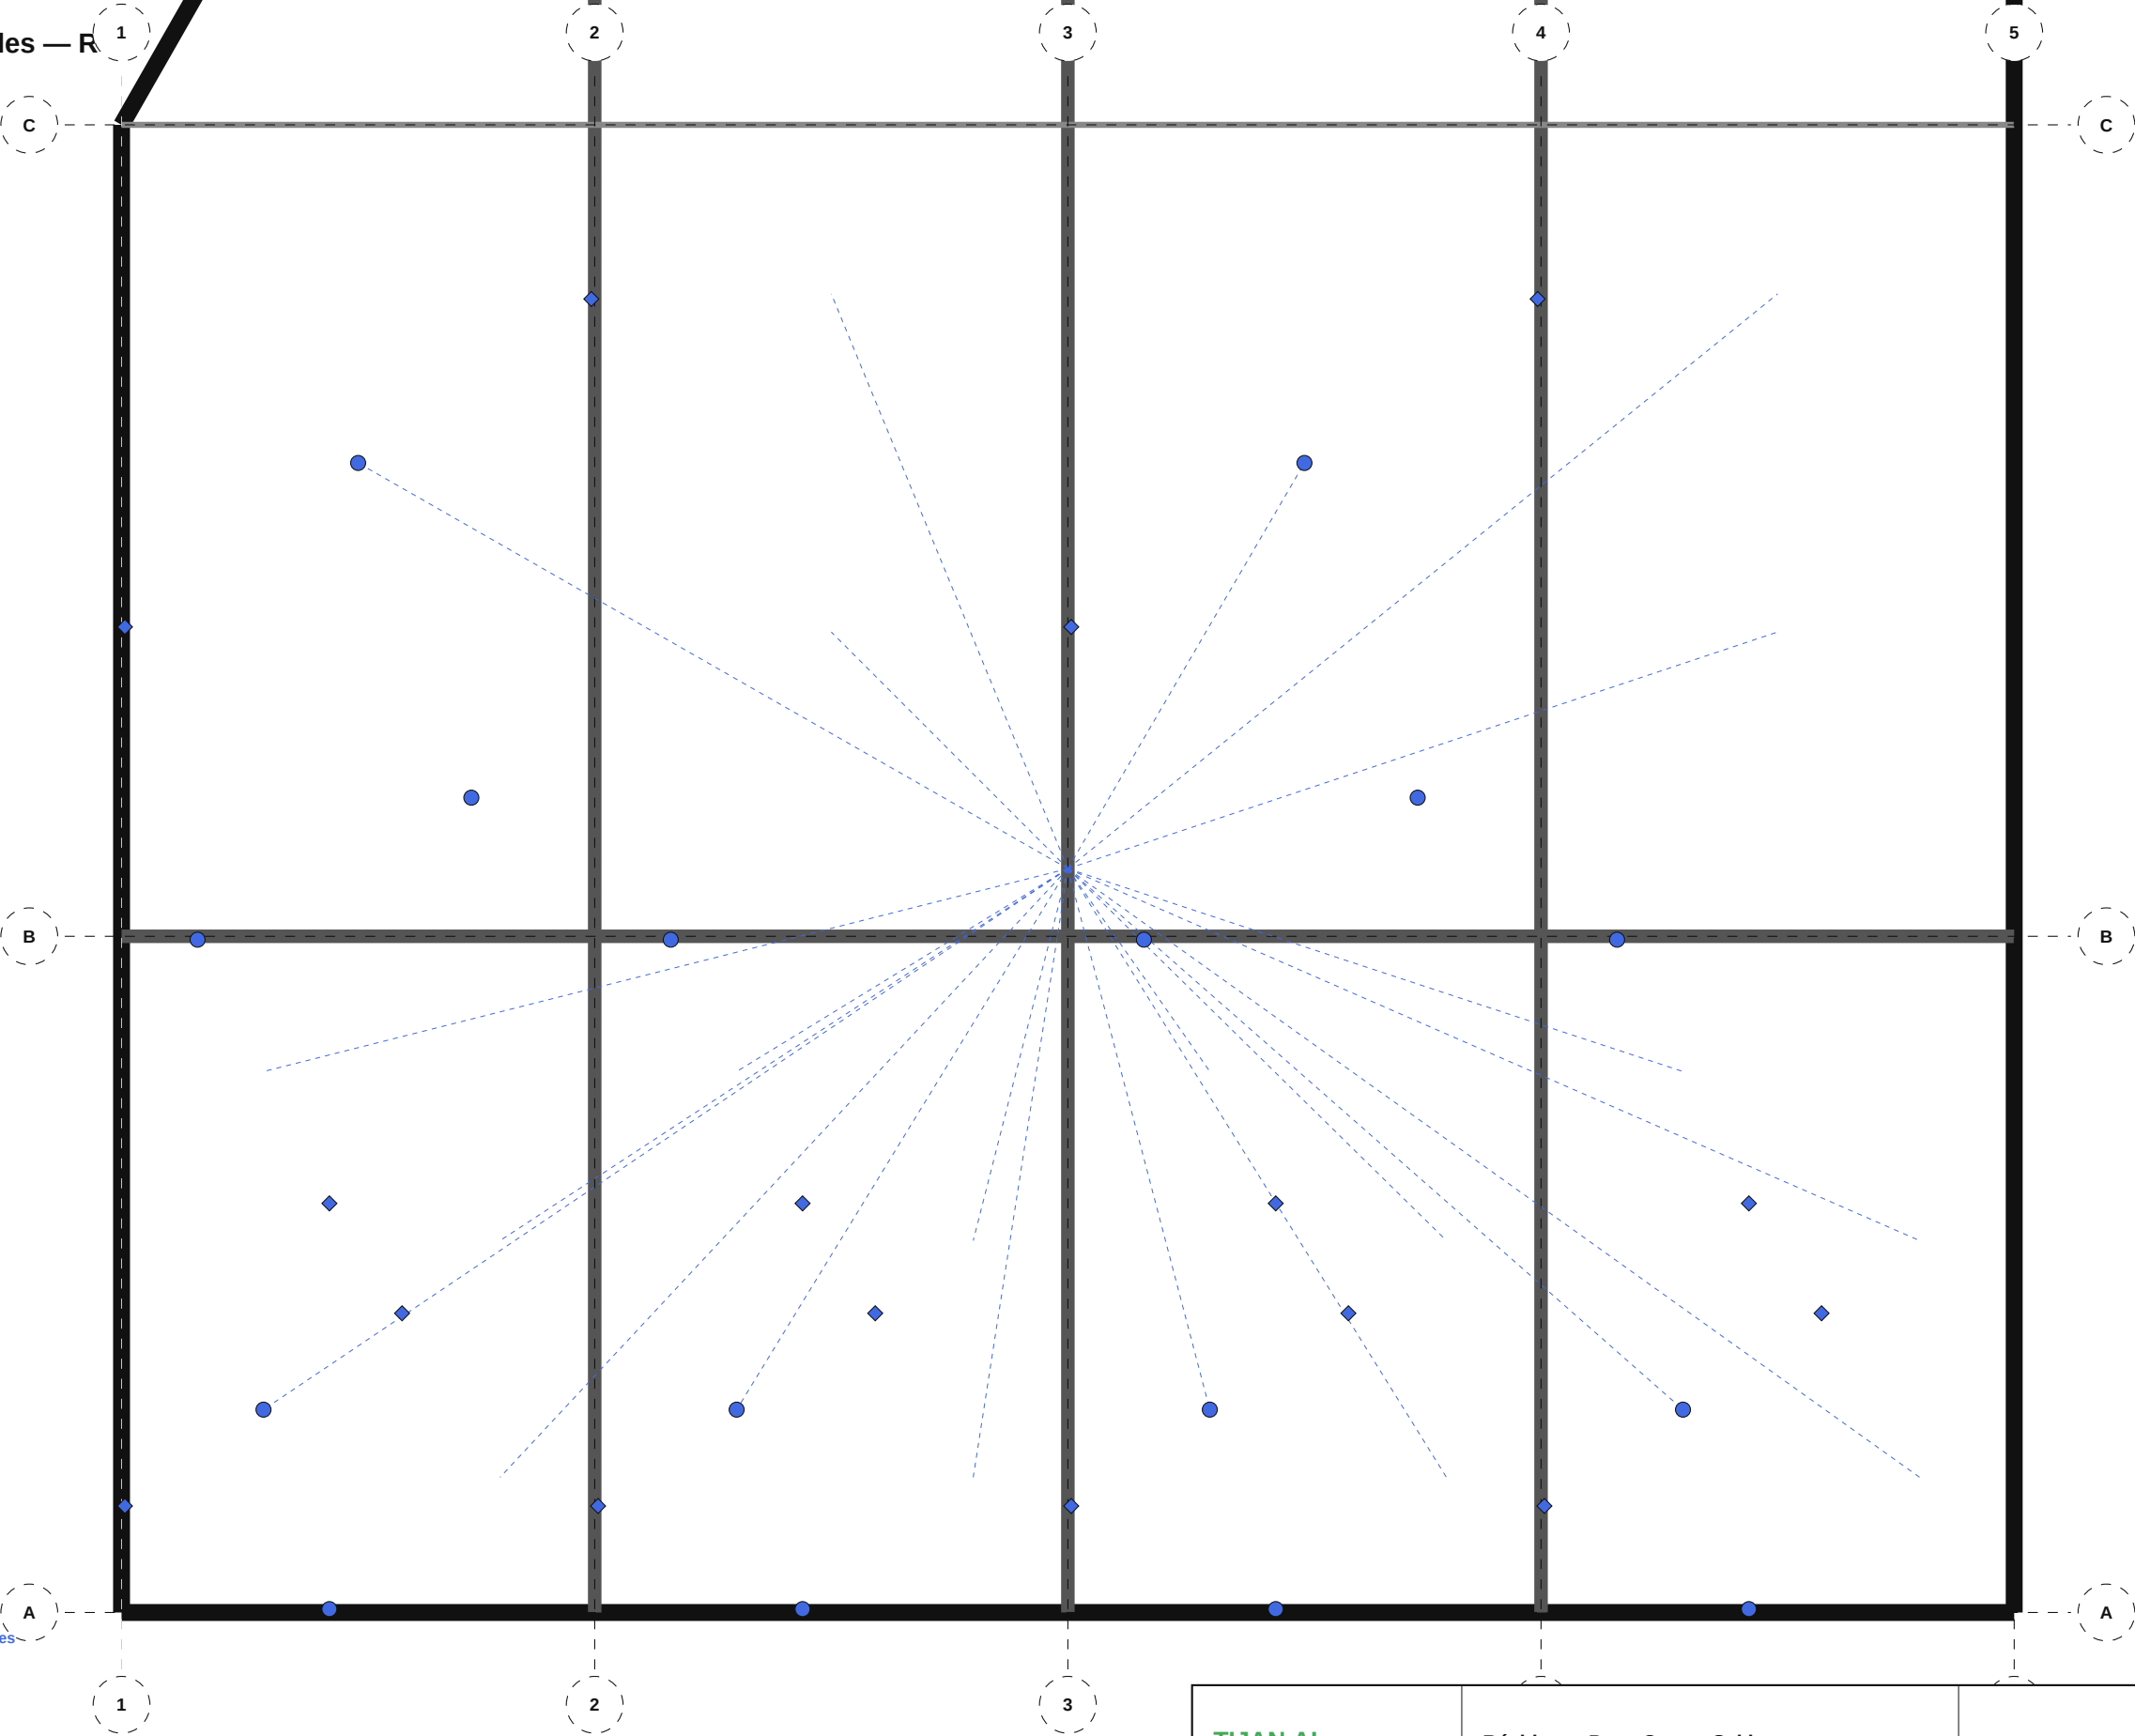

NOMENCLATURE — 520 LCU — Courants Faibles

- Prise RJ45: 16
- Prise TV: 10
- Point d'accès WiFi: 6


TIJAN AI Bureau d'Études Automatisé	Résidence Papa Oumar Sakho Dakar, Senegal	Éch: 1/100 Pl. 109/133
	520 LCU — Courants Faibles — R+5	
Date: 06/05/2026	Réf: 1711	BIM vLCU-109 Phase: APD

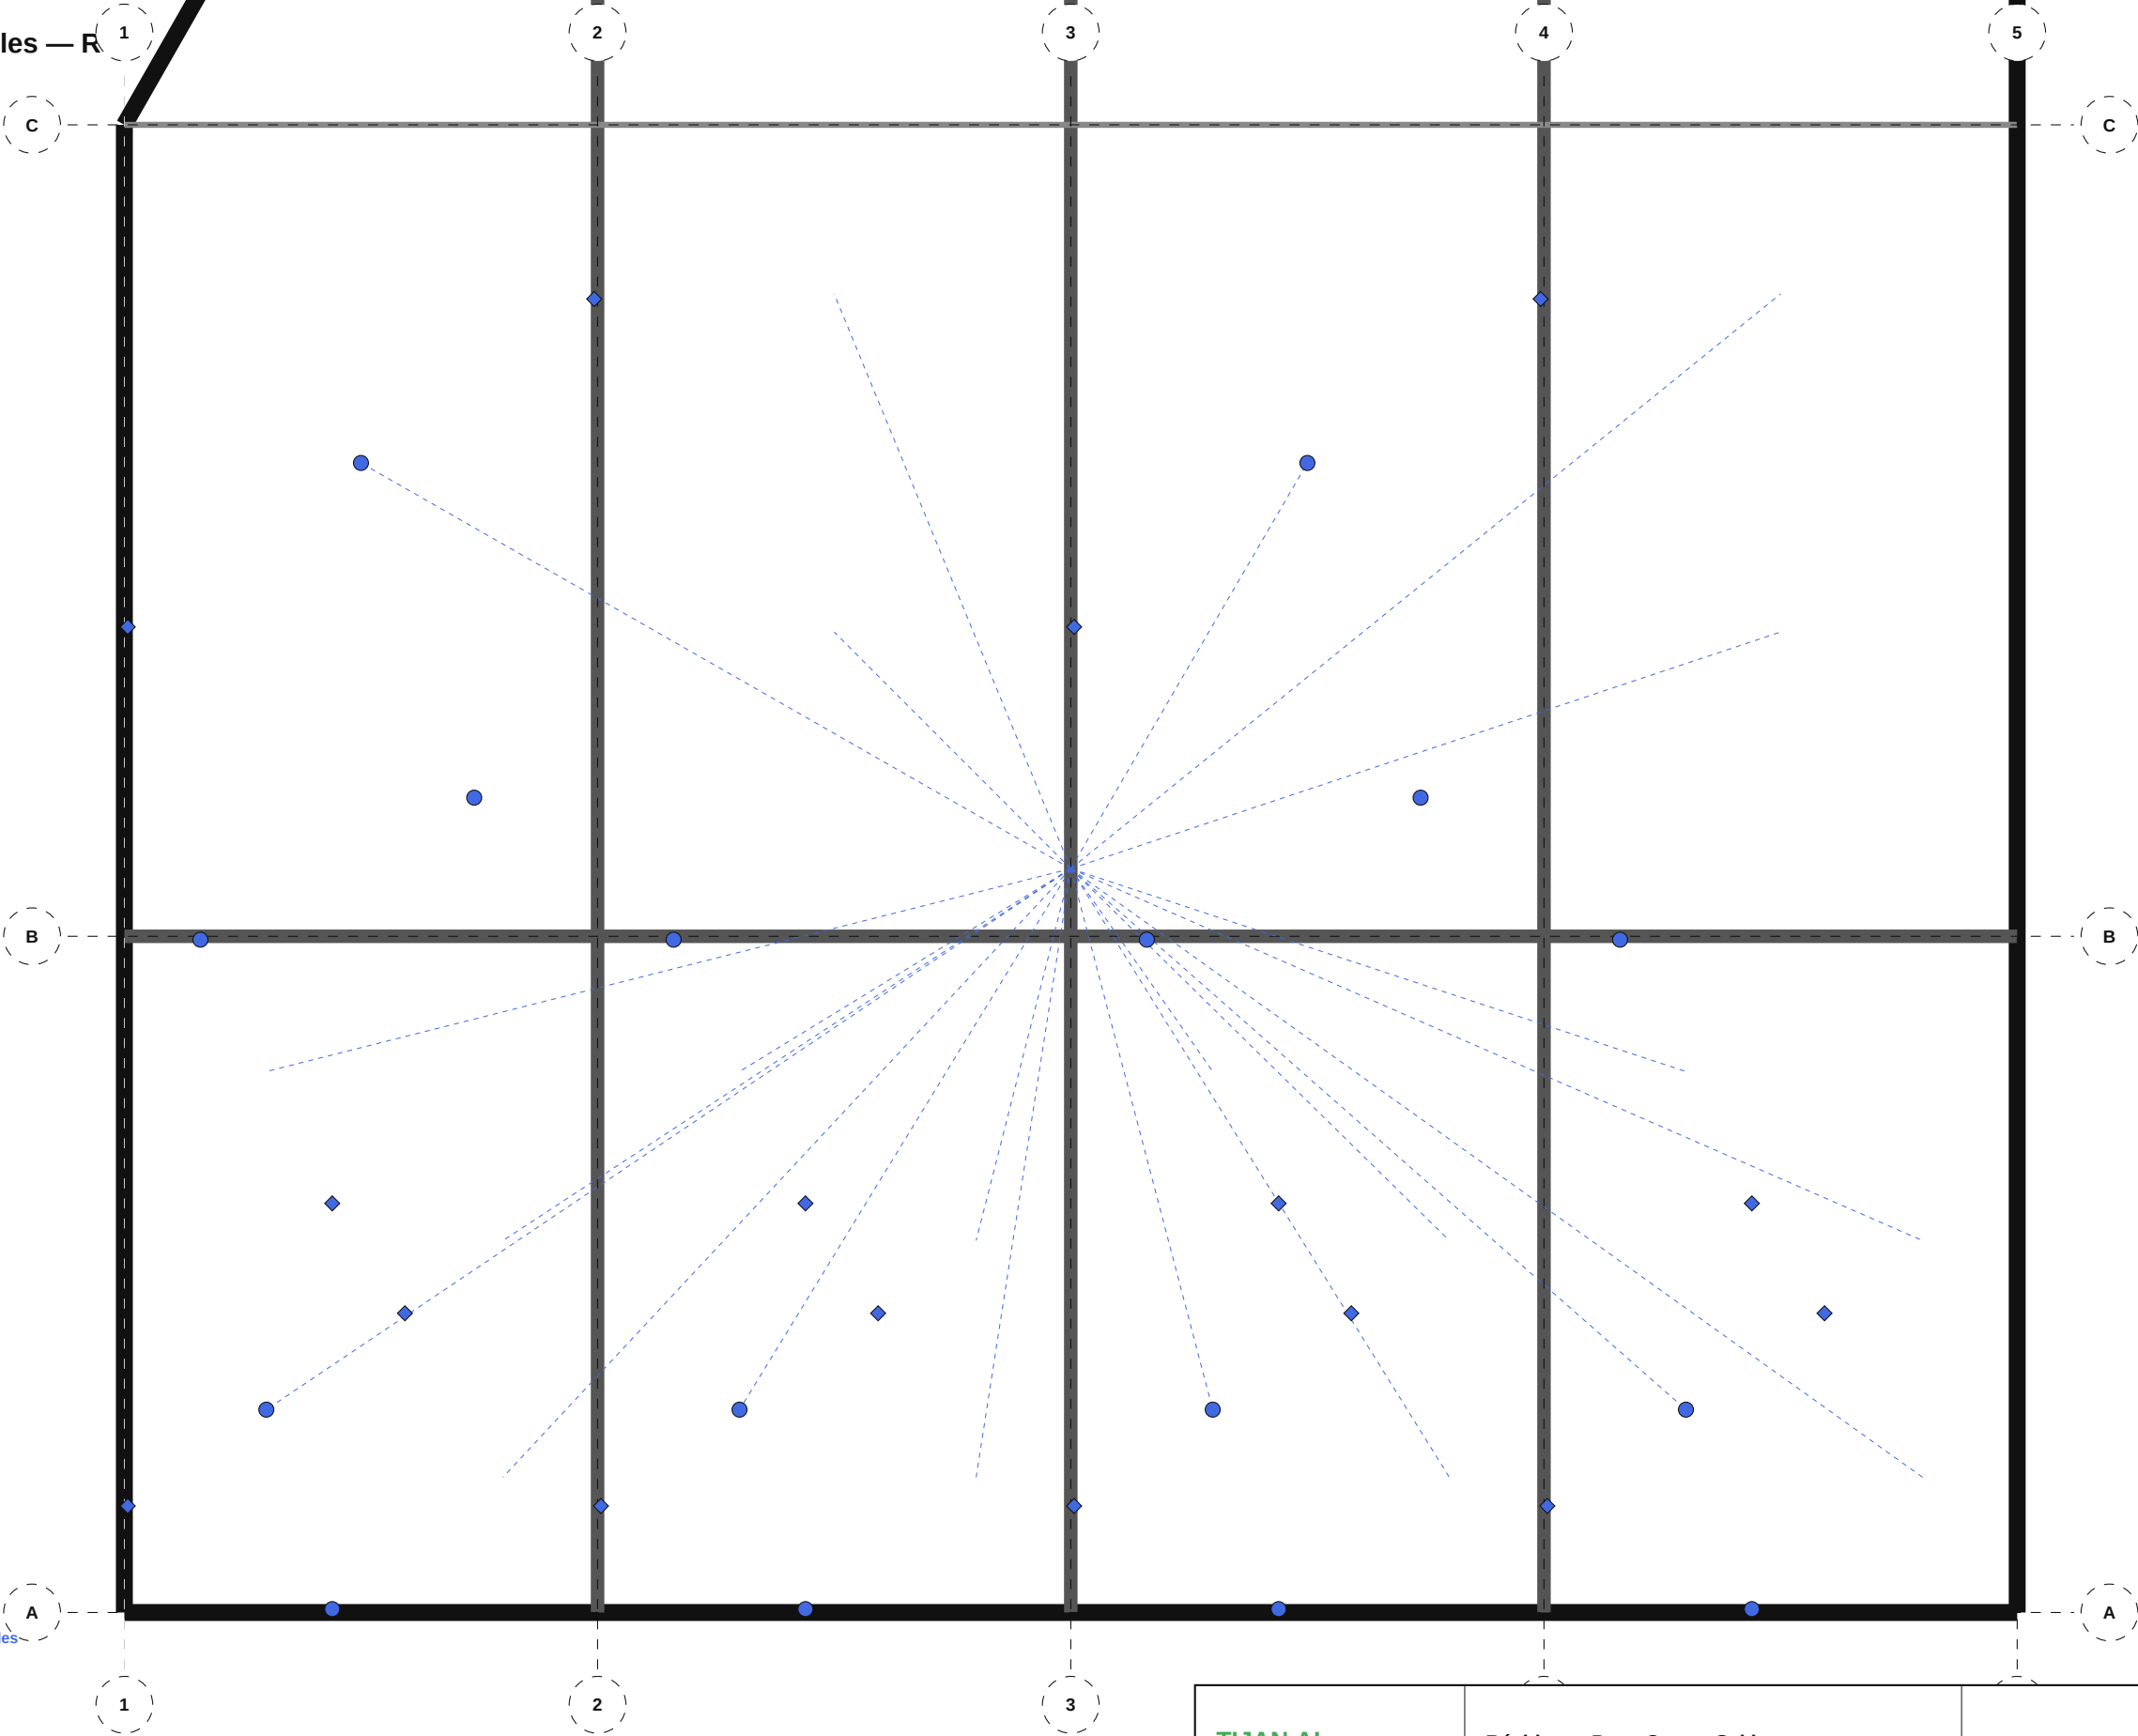

NOMENCLATURE — 520 LCU — Courants Faibles

- Prise RJ45: 16
- Prise TV: 10
- Point d'accès WiFi: 6


TIJAN AI Bureau d'Études Automatisé	Résidence Papa Oumar Sakho Dakar, Senegal	Éch: 1/100 Pl. 110/133
	520 LCU — Courants Faibles — R+6	
Date: 06/05/2026	Réf: 1711	BIM vLCU-110 Phase: APD

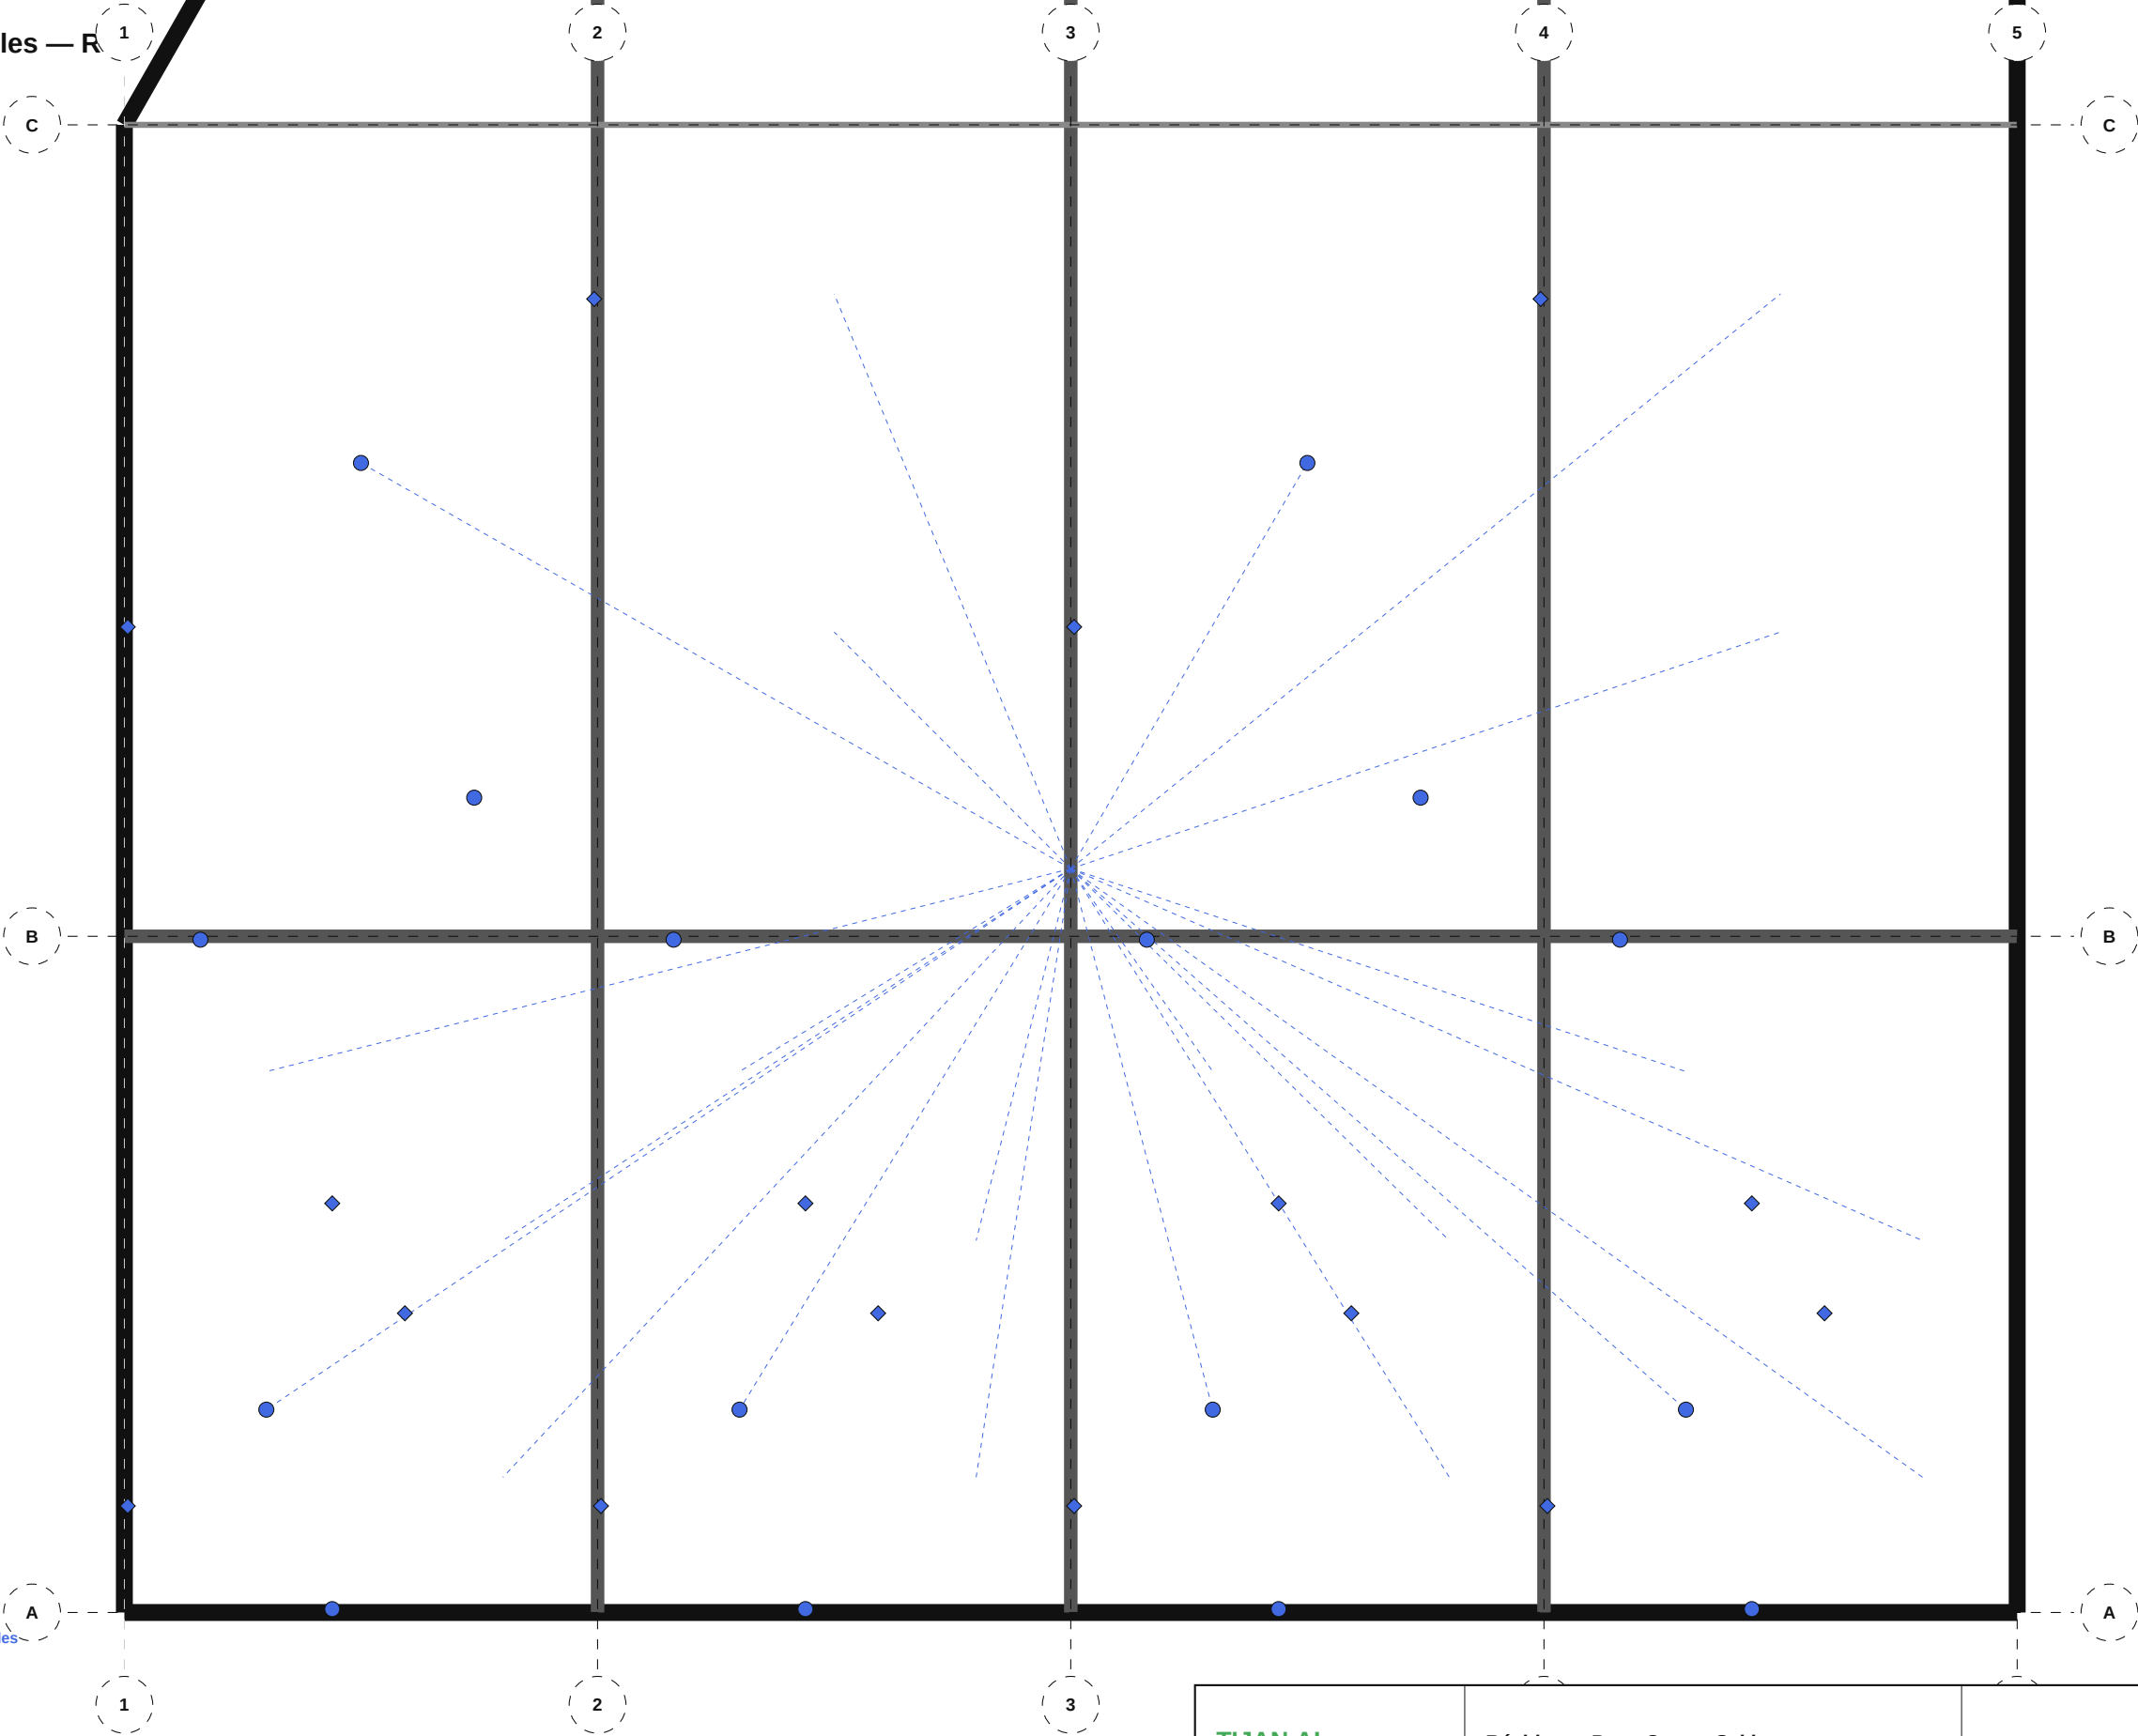


NOMENCLATURE — 520 LCU — Courants Faibles

- Prise RJ45: 16
- Prise TV: 10
- Point d'accès WiFi: 6

TIJAN AI Bureau d'Études Automatisé	Résidence Papa Oumar Sakho Dakar, Senegal	Éch: 1/100 Pl. 111/133
	520 LCU — Courants Faibles — R+7	
Date: 06/05/2026	Réf: 1711	BIM vLCU-111 Phase: APD

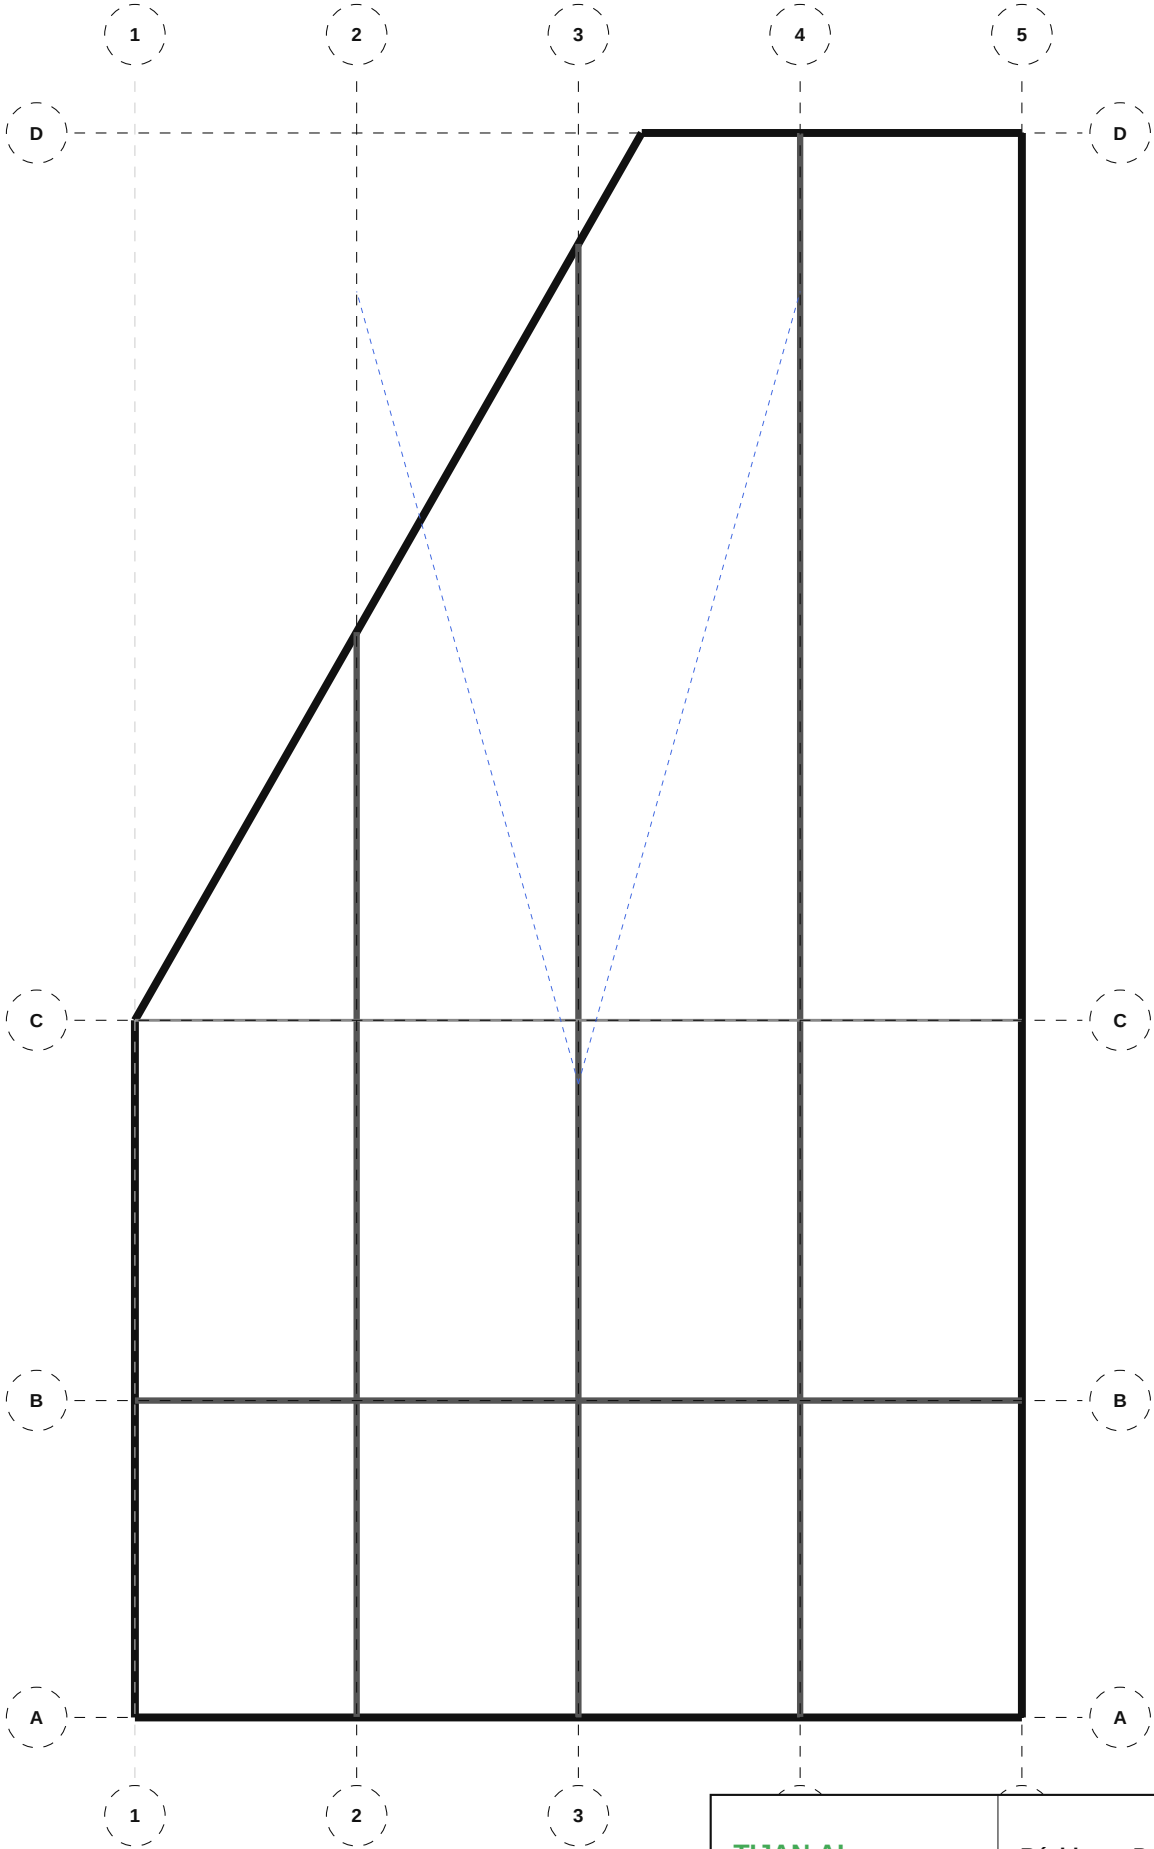

TIJAN AI Bureau d'Études Automatisé	Résidence Papa Oumar Sakho Dakar, Senegal	Éch: 1/100 Pl. 112/133
	520 LCU — Courants Faibles — R+8 Terrasse	
Date: 06/05/2026	Réf: 1711	BIM v.LCU-112 Phase: APD

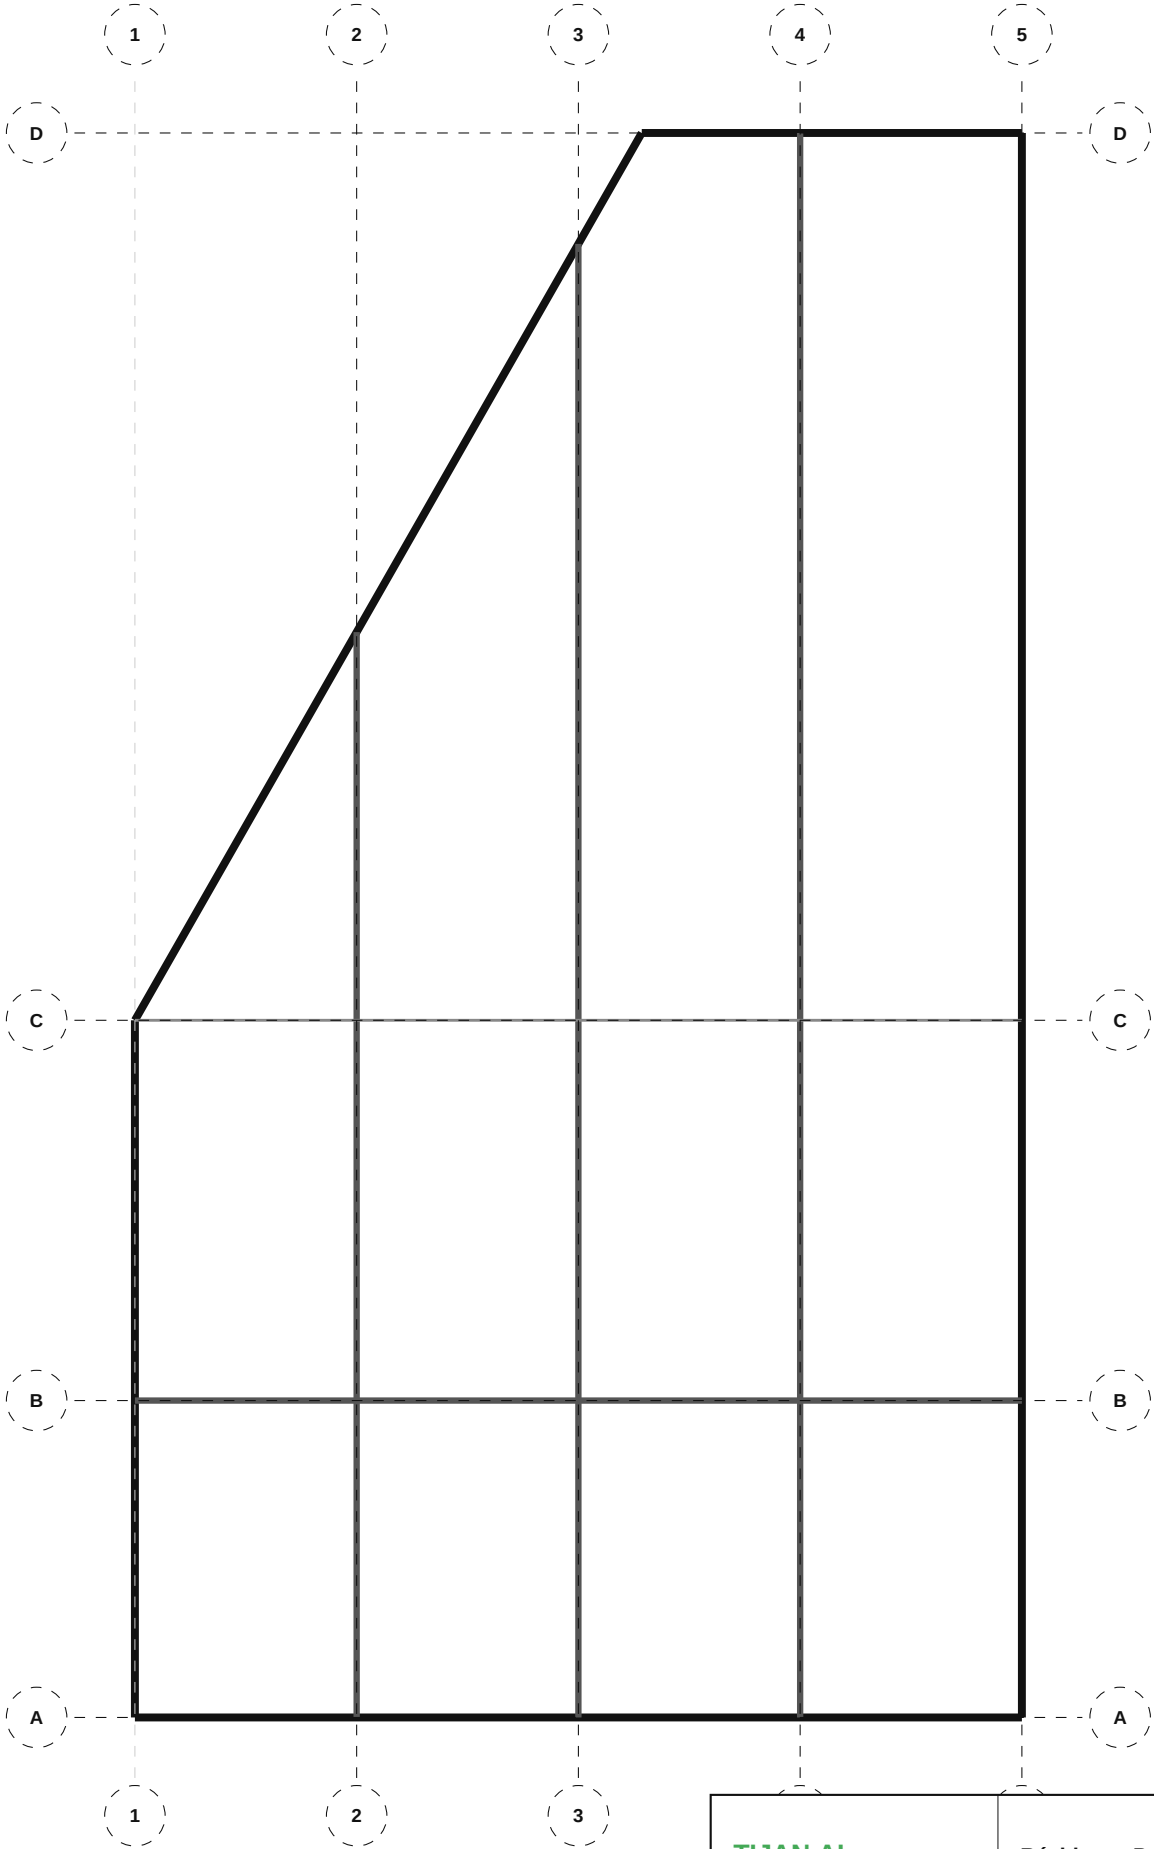

TIJAN AI Bureau d'Études Automatisé	Résidence Papa Oumar Sakho Dakar, Senegal	Éch: 1/100 Pl. 113/133
	113 RC — Faux Plafond — Sous-Sol	
Date: 06/05/2026	Réf: 1711	BIM VRC-113 Phase: APD

113 RC — Faux Plafond — RDC

1

2

3

4

5

B

B

A

A

1

2

3

4

5

TIJAN AI

Bureau d'Études Automatisé

Résidence Papa Oumar Sakho

Dakar, Senegal

Éch: 1/100

Pl. 114/133

113 RC — Faux Plafond — RDC

Date: 06/05/2026


Réf: 1711

BIM VRC-114


Phase: APD

The diagram shows a 2x4 grid of rectangles. The top row is shaded light blue, and the bottom row is white. The grid is bounded by thick black lines. Labels 'A', 'B', and 'C' are in dashed circles at the corners. Numbers 1-5 are in dashed circles at the midpoints of the top and bottom edges. A label 'R+1' is at the top left. A green box with 'FINNA' is at the bottom right.


TIJAN AI Bureau d'Études Automatisé	Résidence Papa Oumar Sakho Dakar, Senegal	Éch: 1/100 Pl. 115/133
	113 RC — Faux Plafond — R+1	
Date: 06/05/2026	Réf: 1711	BIM vRC-115 Phase: APD

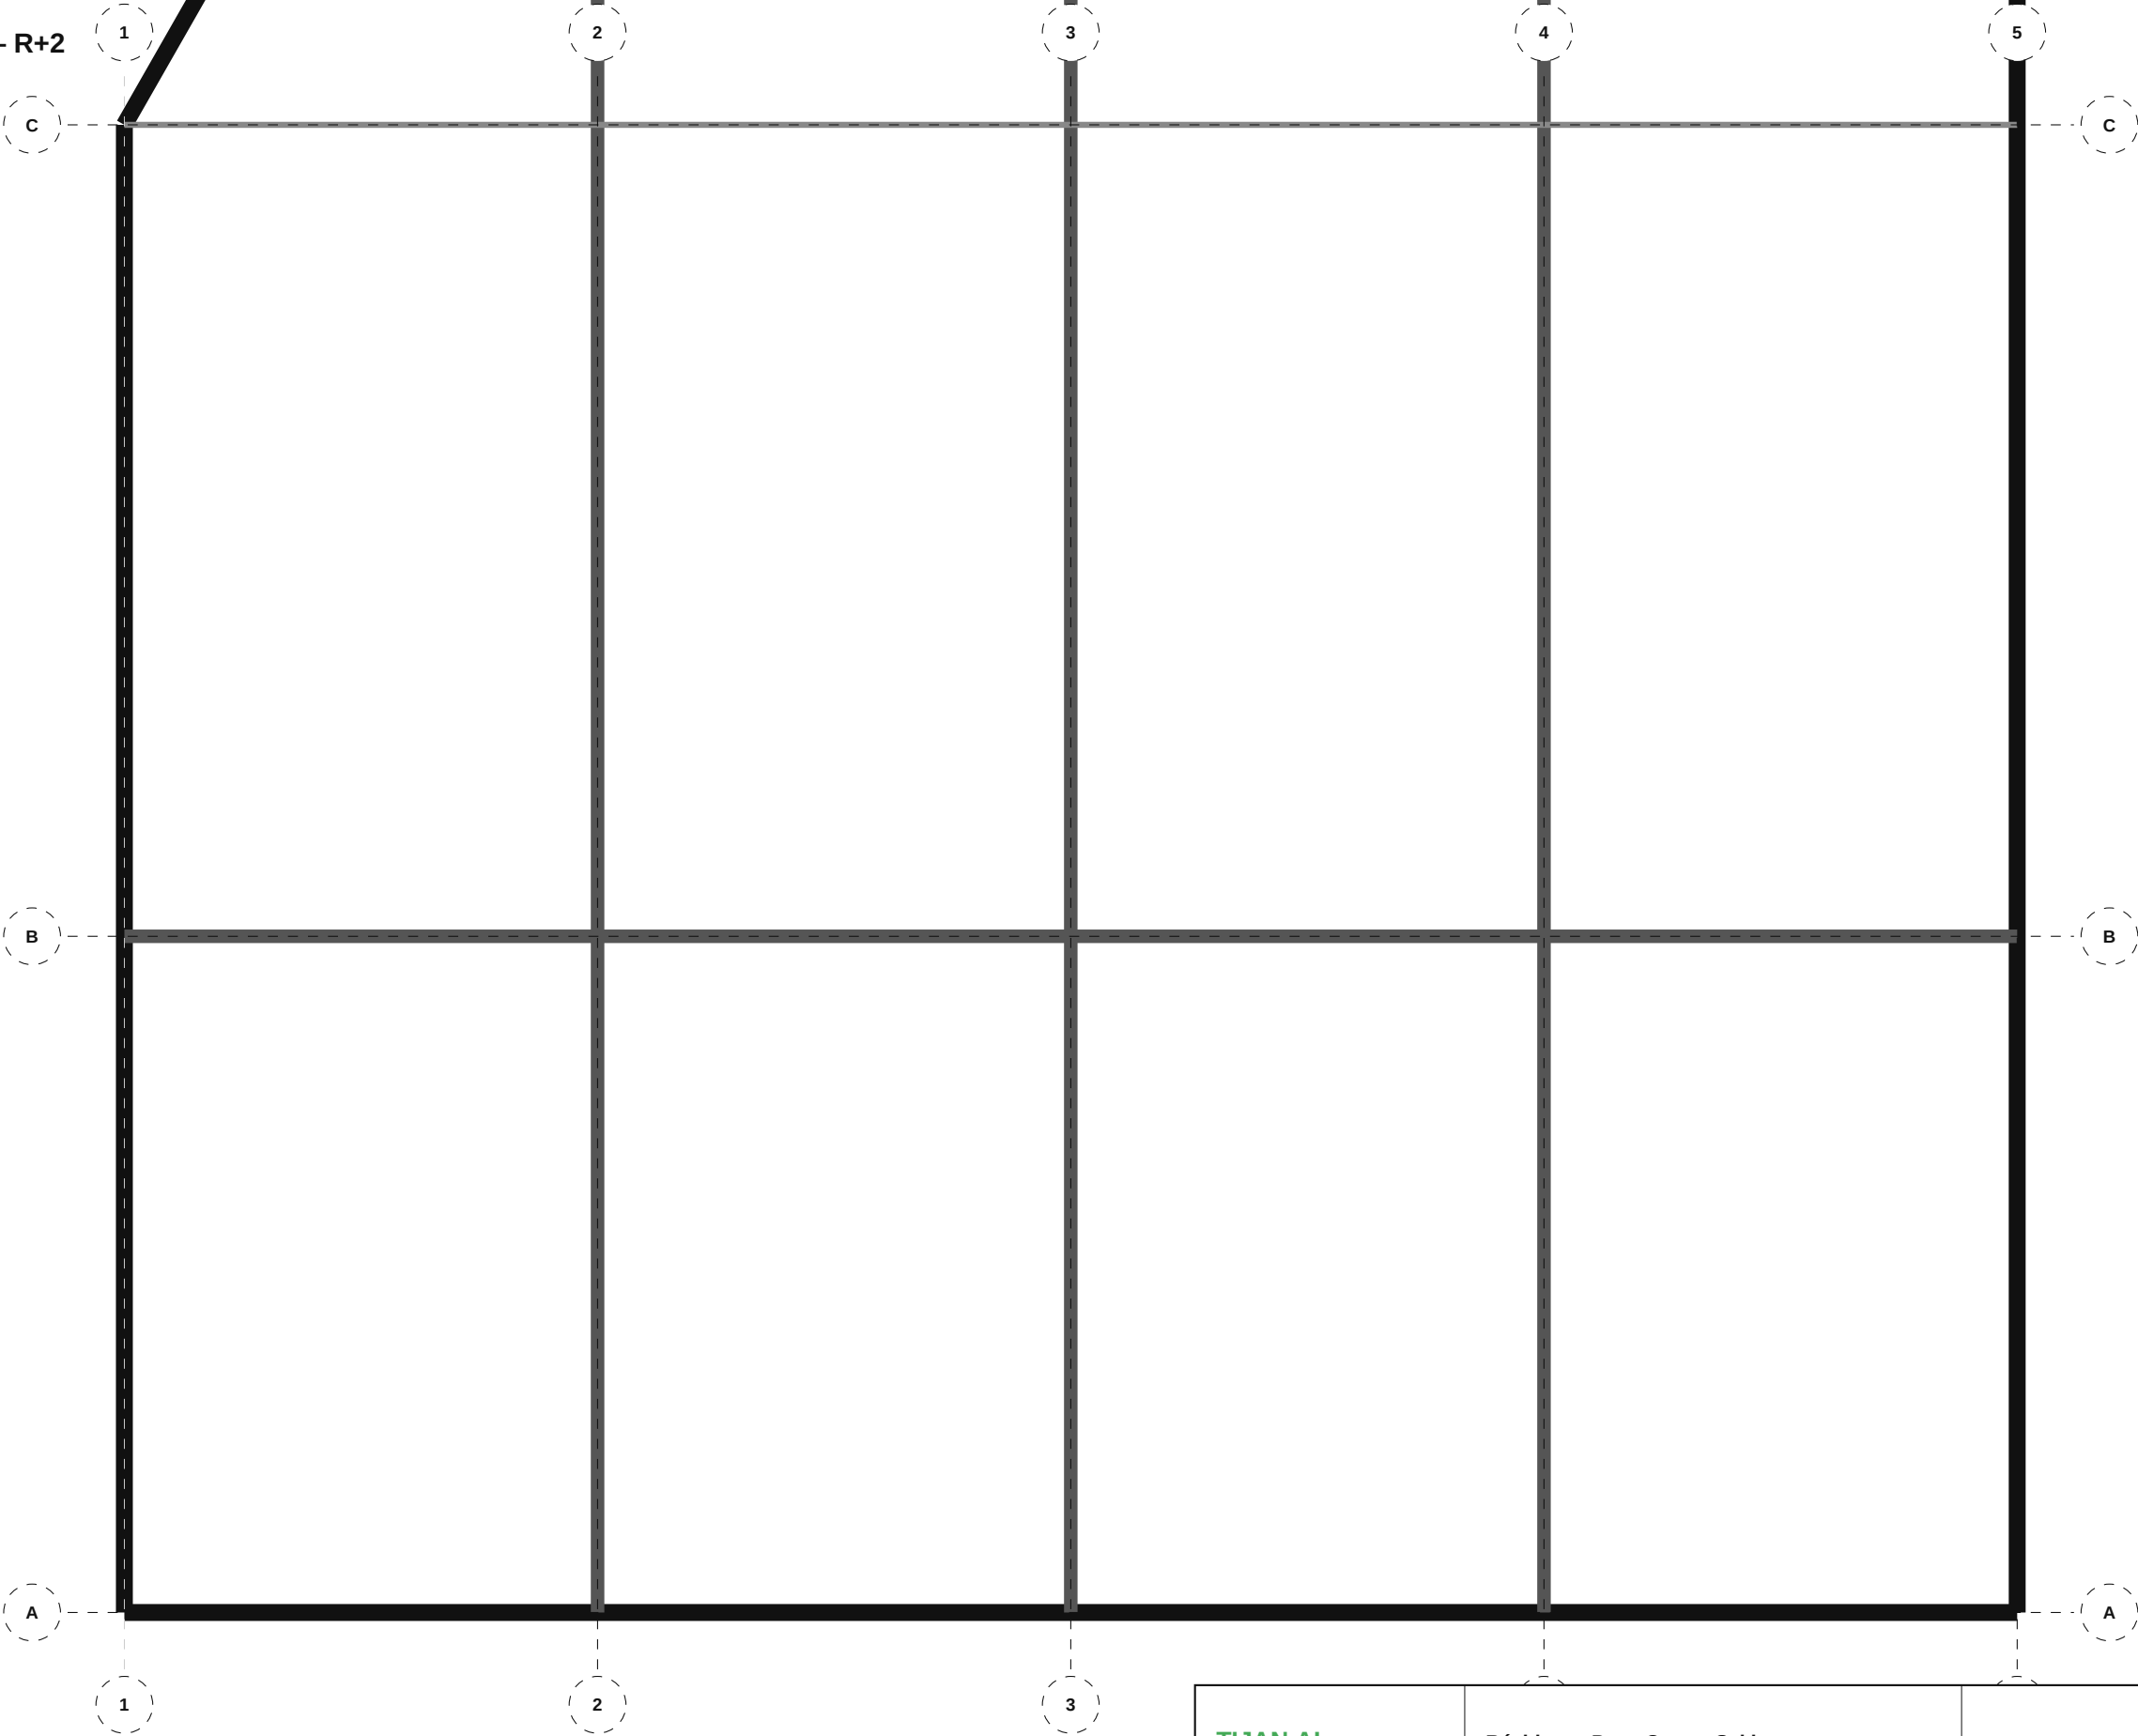

TIJAN AI Bureau d'Études Automatisé	Résidence Papa Oumar Sakho Dakar, Senegal	Éch: 1/100 Pl. 116/133
	113 RC — Faux Plafond — R+2	
Date: 06/05/2026	Réf: 1711	BIM VRC-116 Phase: APD

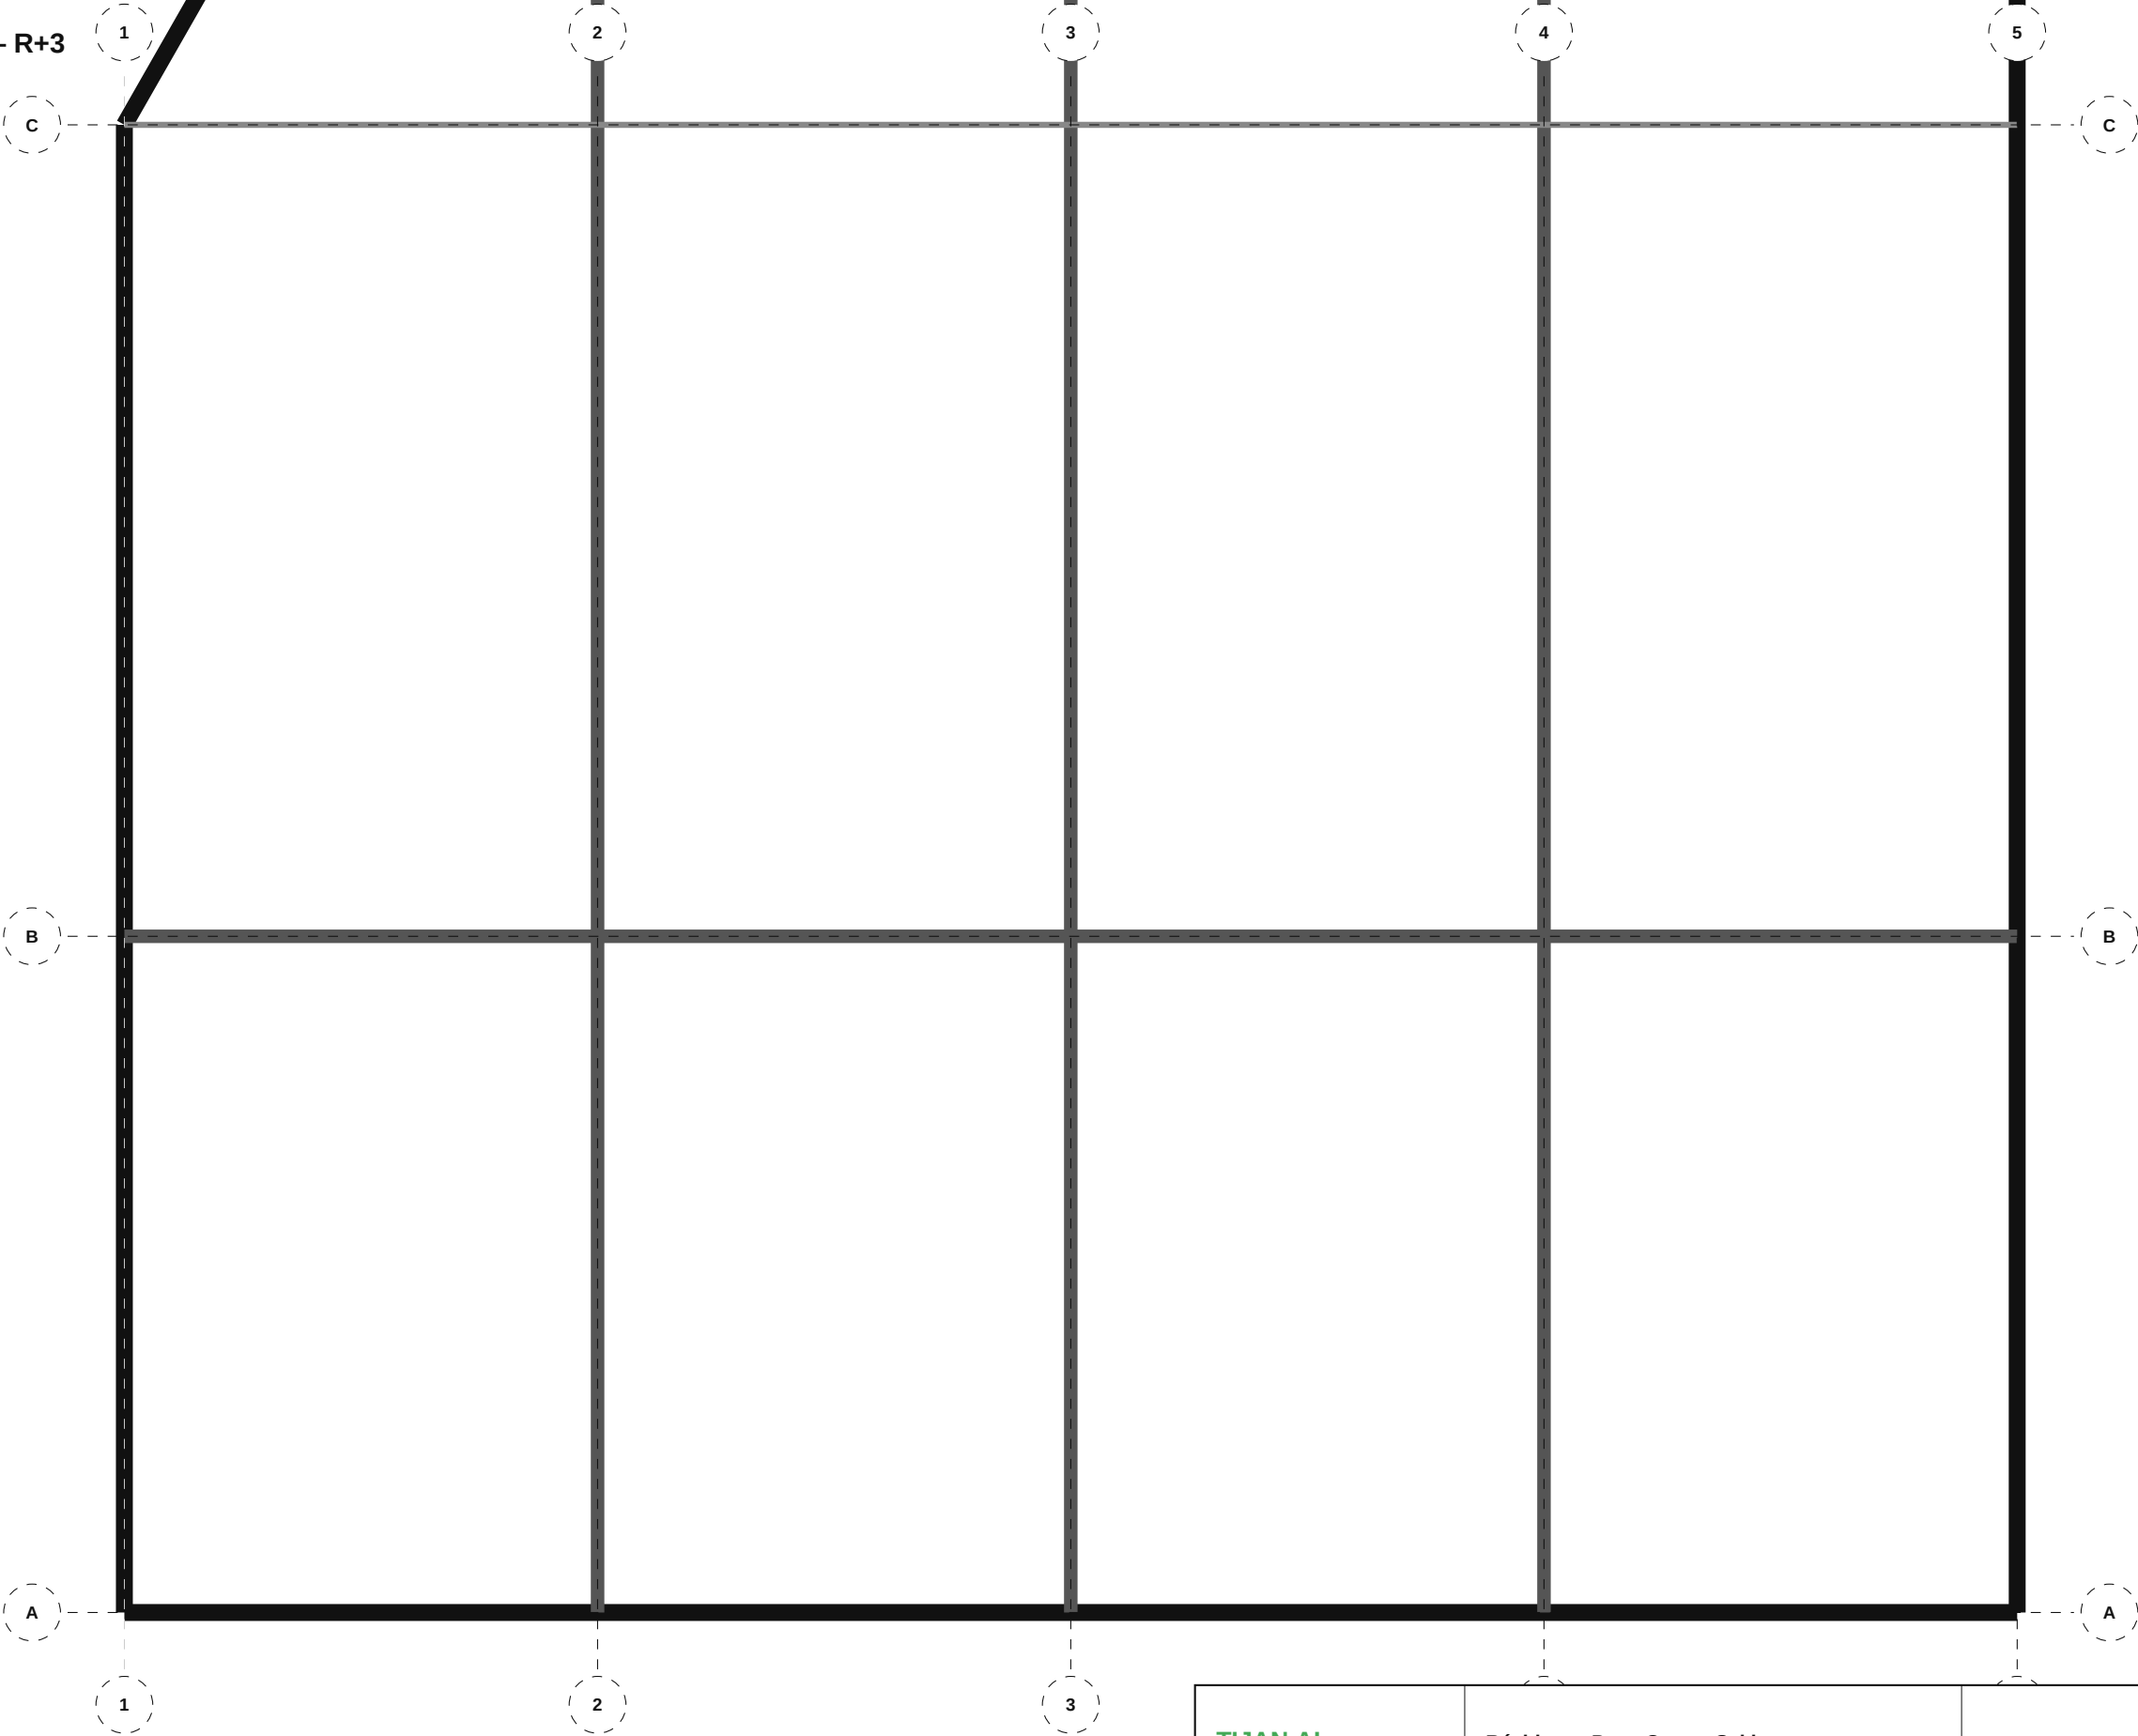

TIJAN AI Bureau d'Études Automatisé	Résidence Papa Oumar Sakho Dakar, Senegal	Éch: 1/100 Pl. 117/133
	113 RC — Faux Plafond — R+3	
Date: 06/05/2026	Réf: 1711	BIM VRC-117 Phase: APD

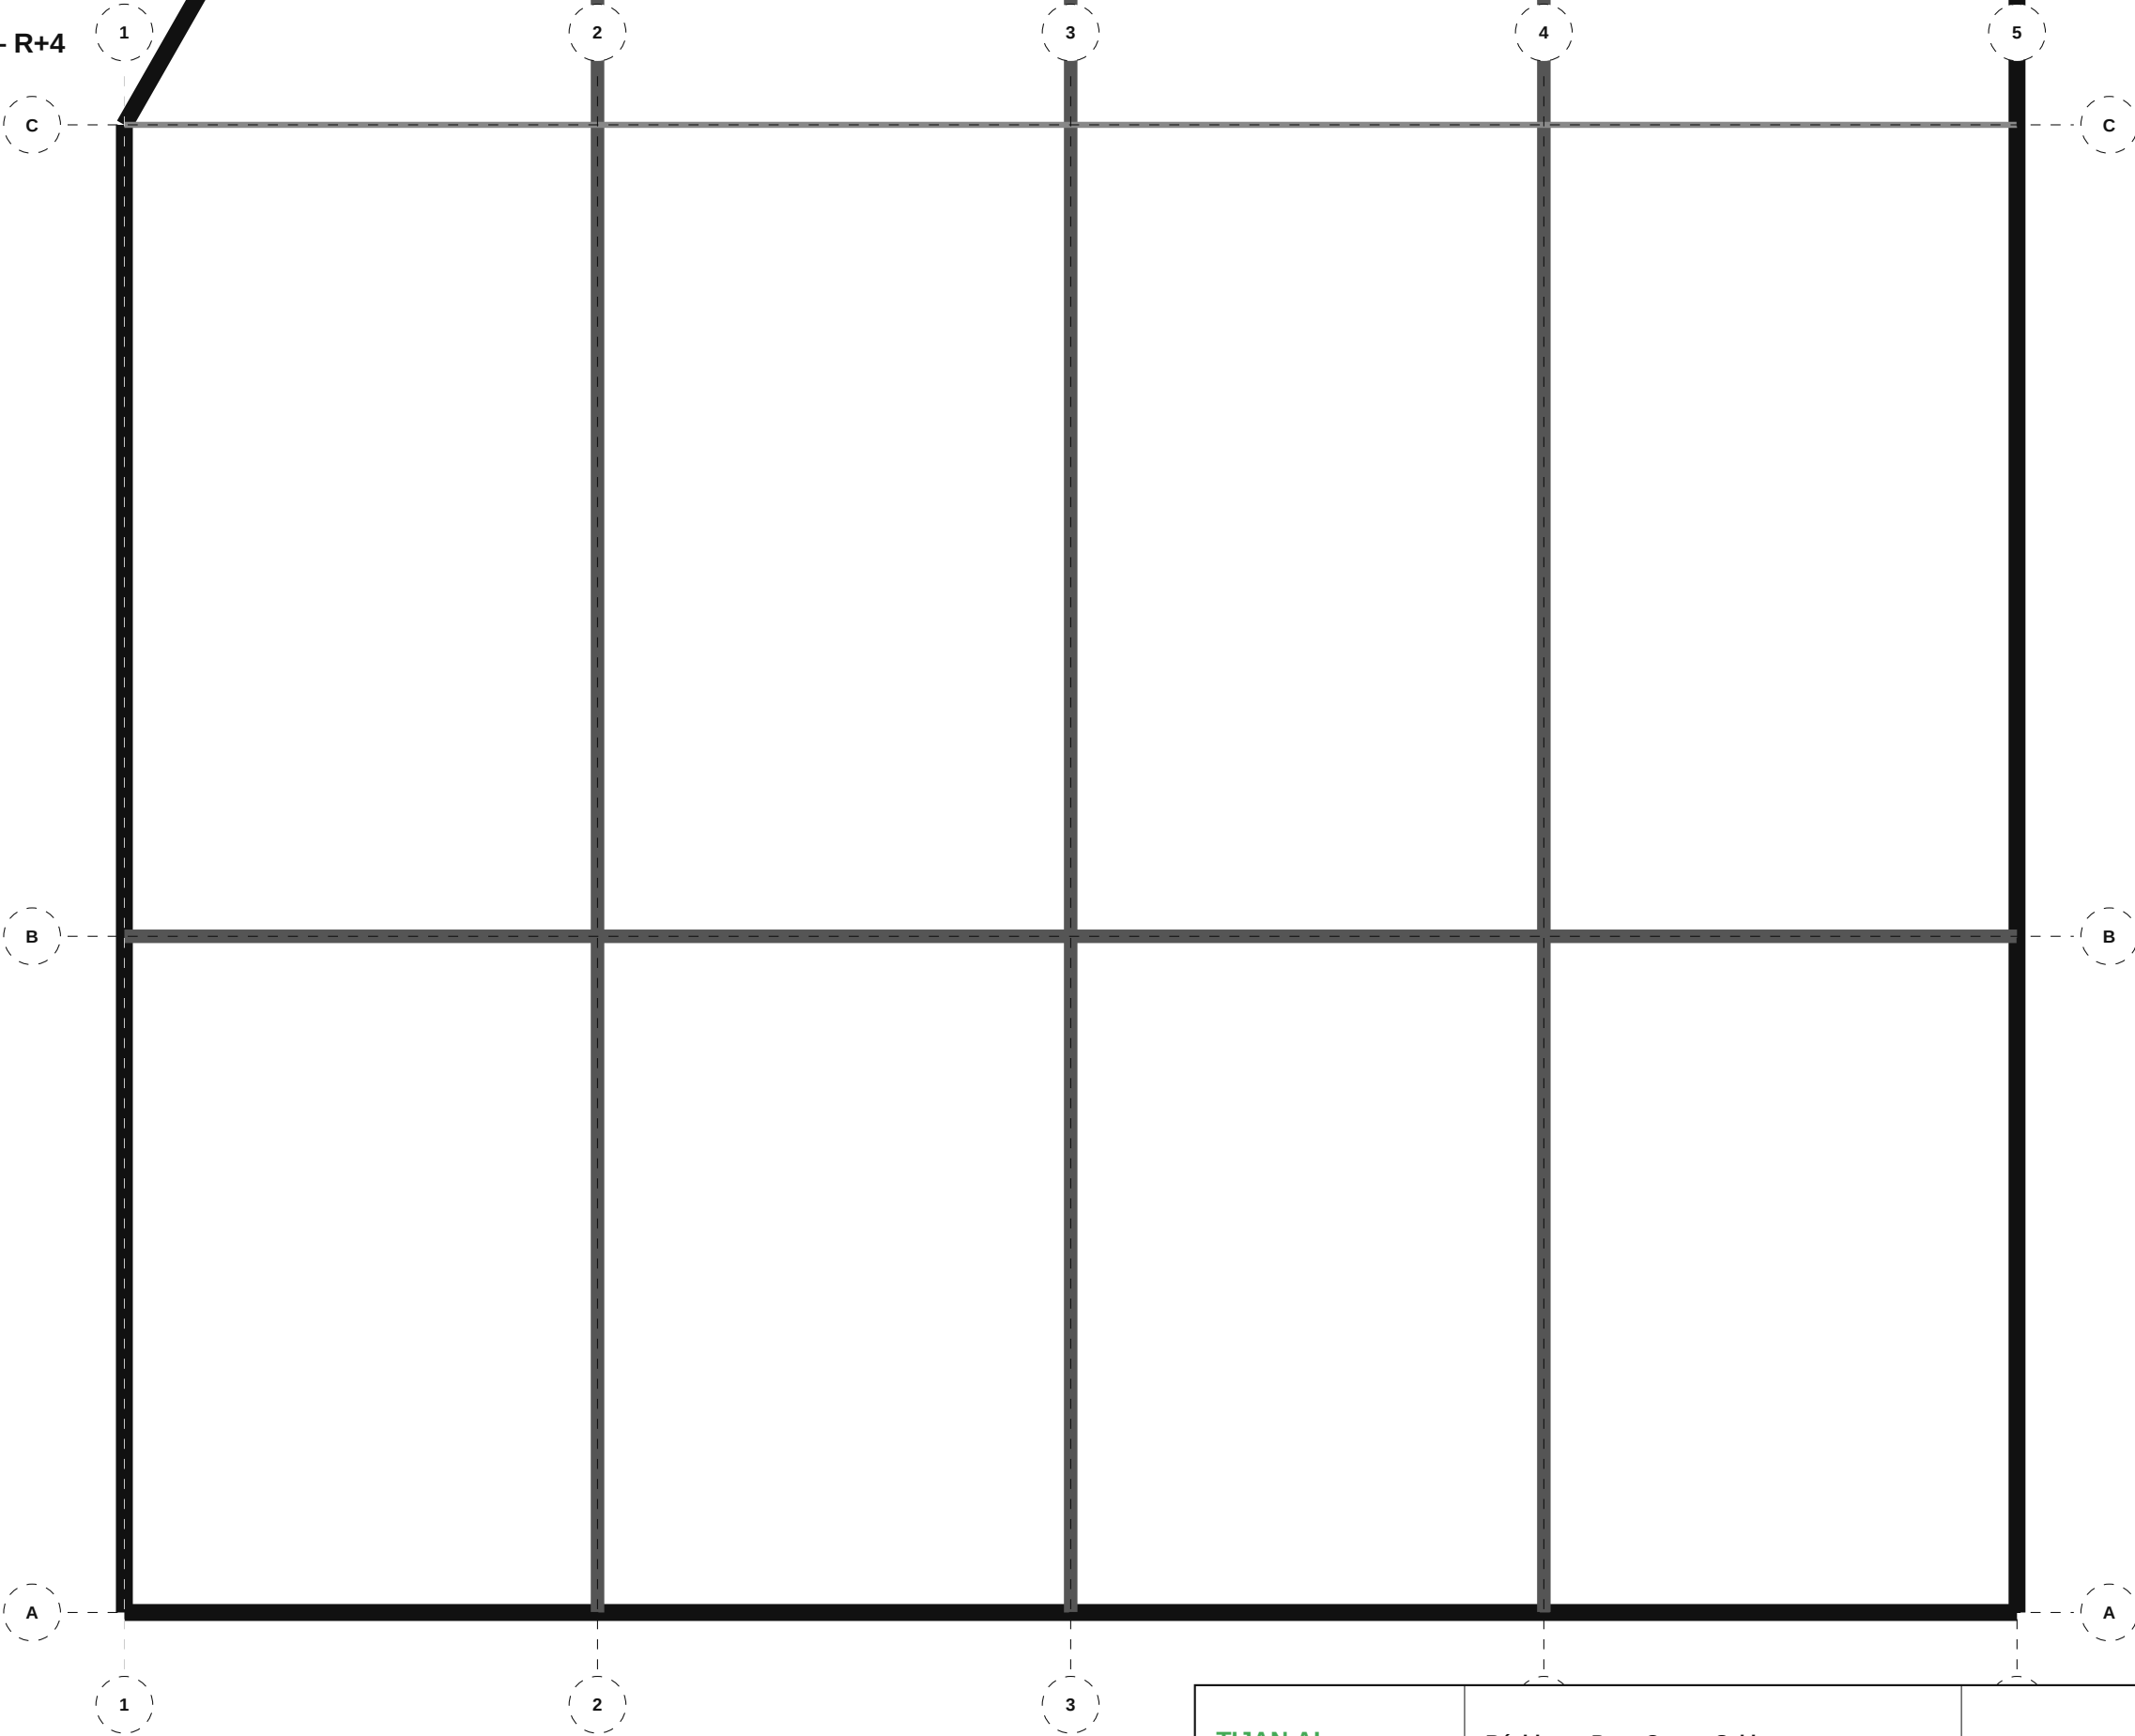

TIJAN AI
Bureau d'Études Automatisé

Résidence Papa Oumar Sakho
Dakar, Senegal


Éch: 1/100
Pl. 118/133

113 RC — Faux Plafond — R+4

Date: 06/05/2026

Réf: 1711

BIM vRC-118
Phase: APD

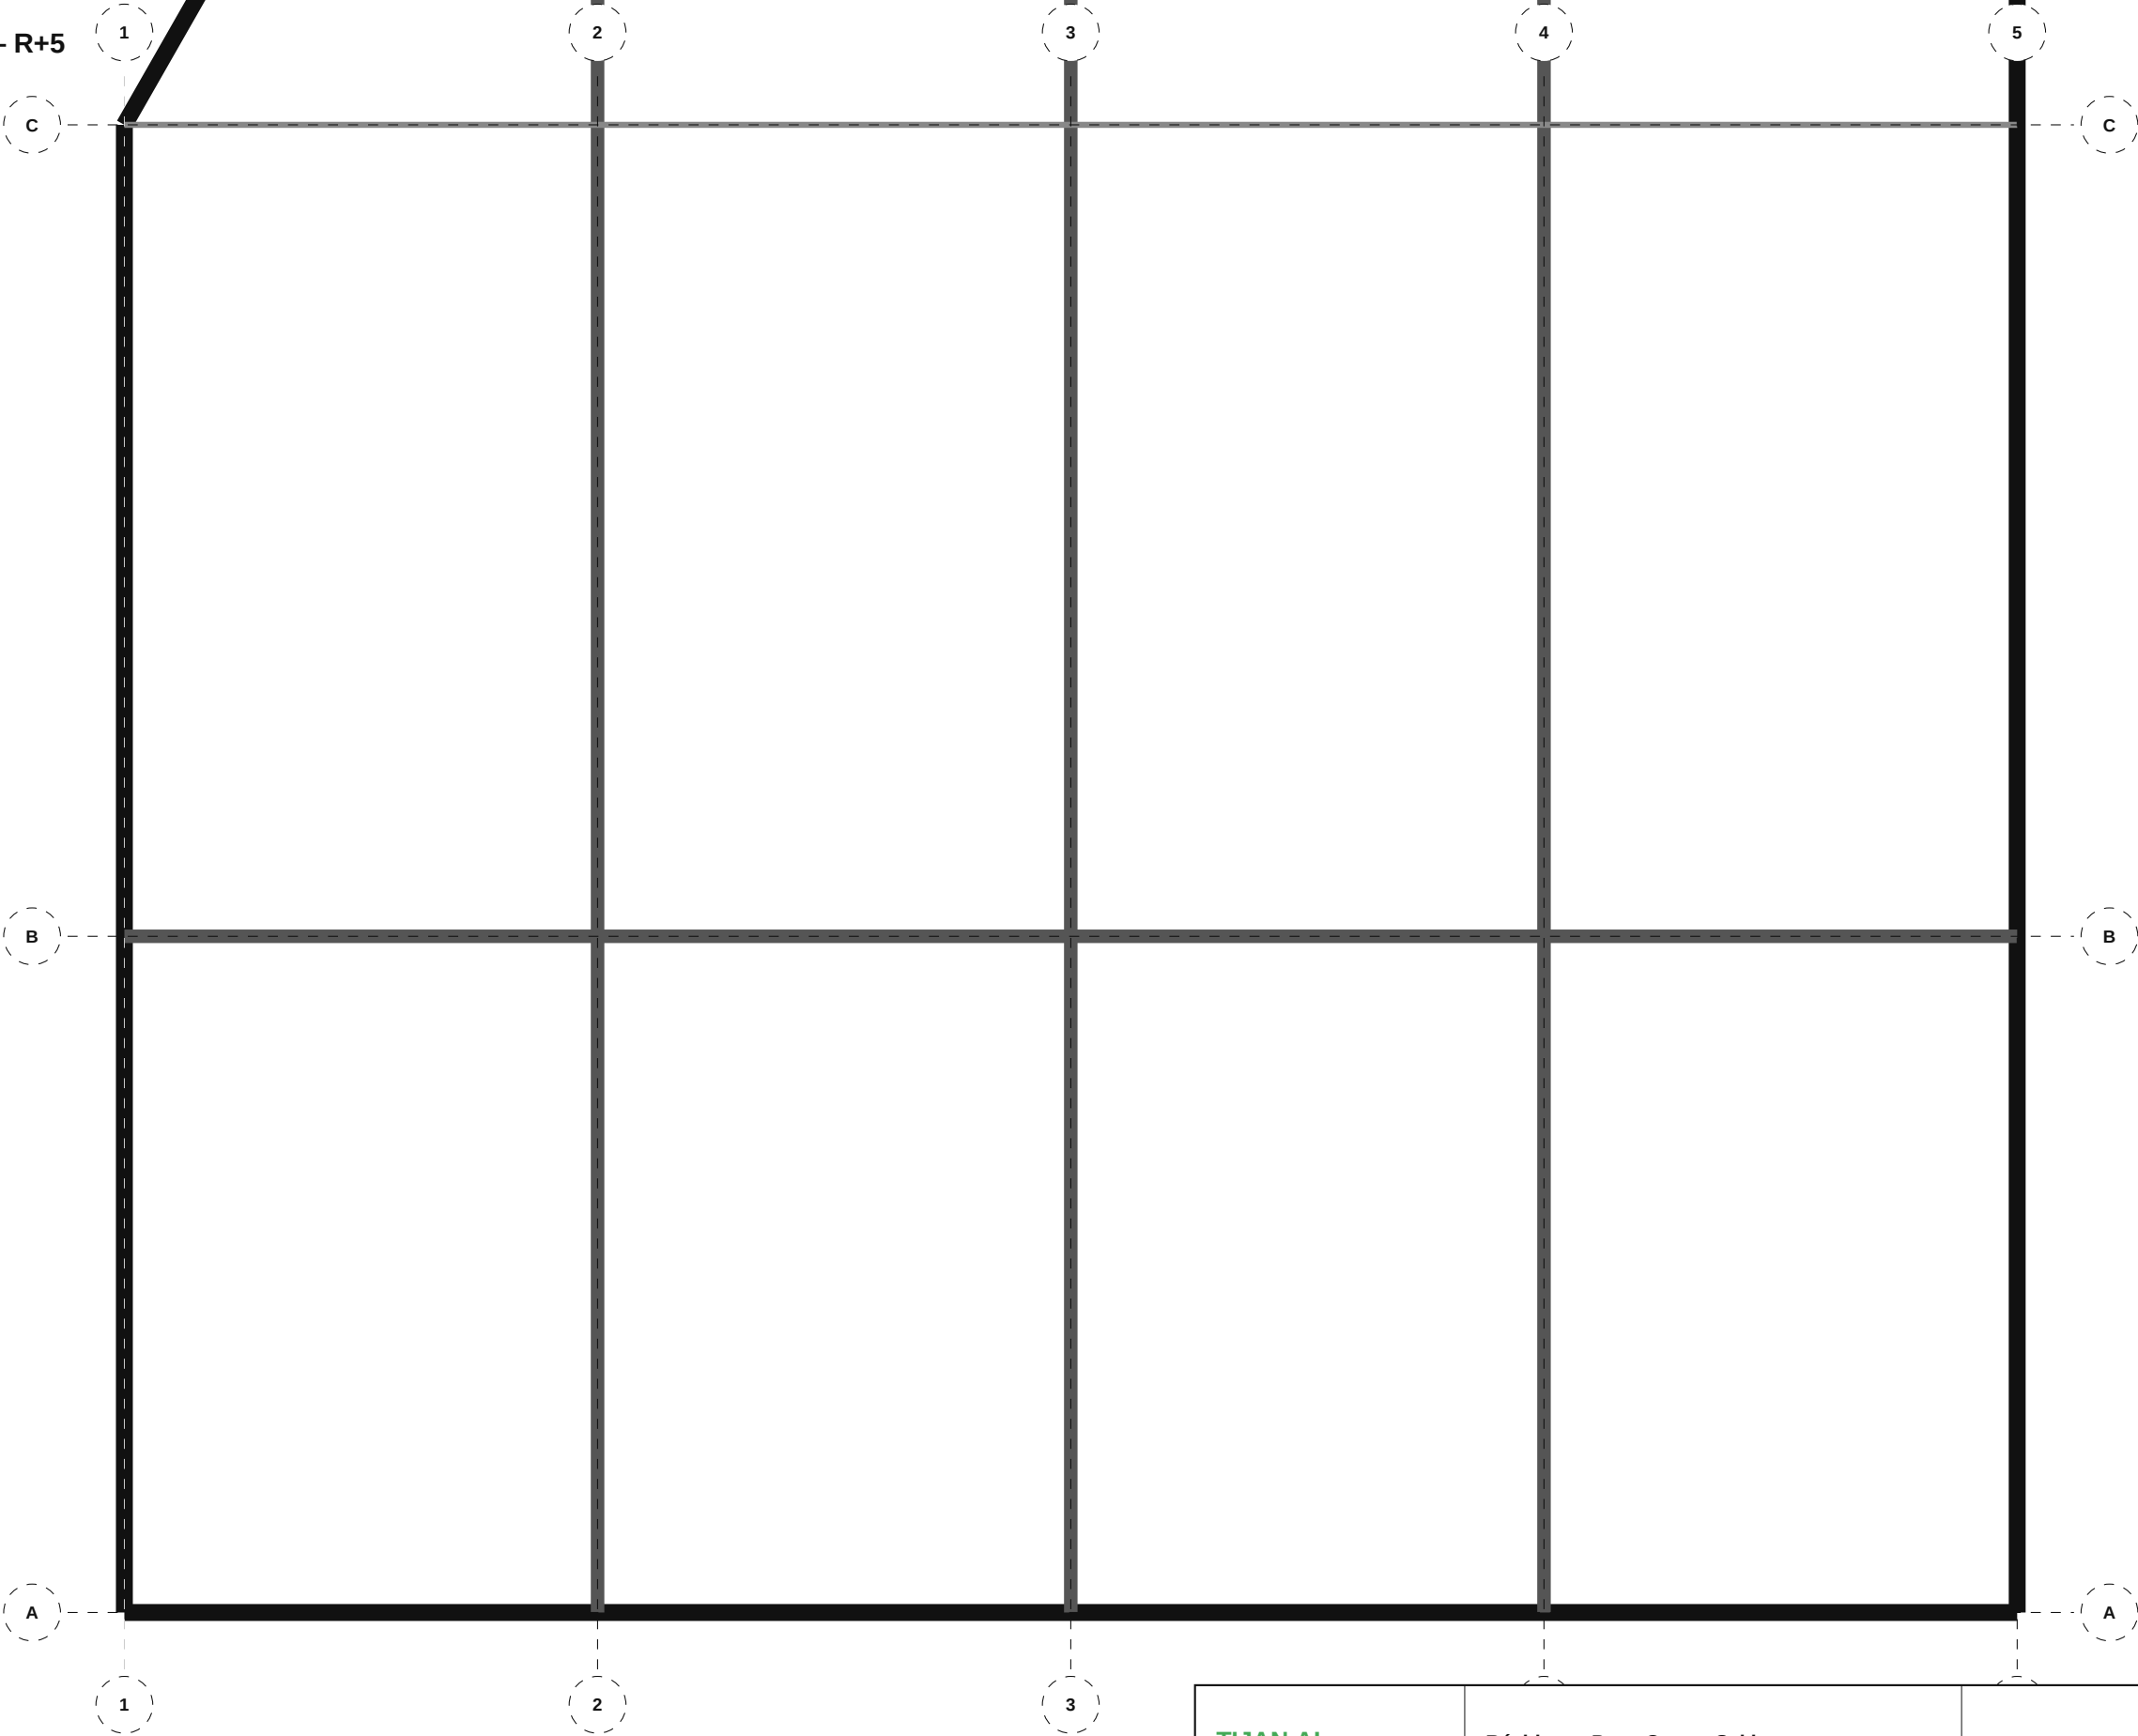

TIJAN AI

Bureau d'Études Automatisé

Résidence Papa Oumar Sakho

Dakar, Senegal

Éch: 1/100

Pl. 119/133

113 RC — Faux Plafond — R+5


Date: 06/05/2026

Réf: 1711


BIM VRC-119

Phase: APD

113 RC — Faux Plafond — R+6

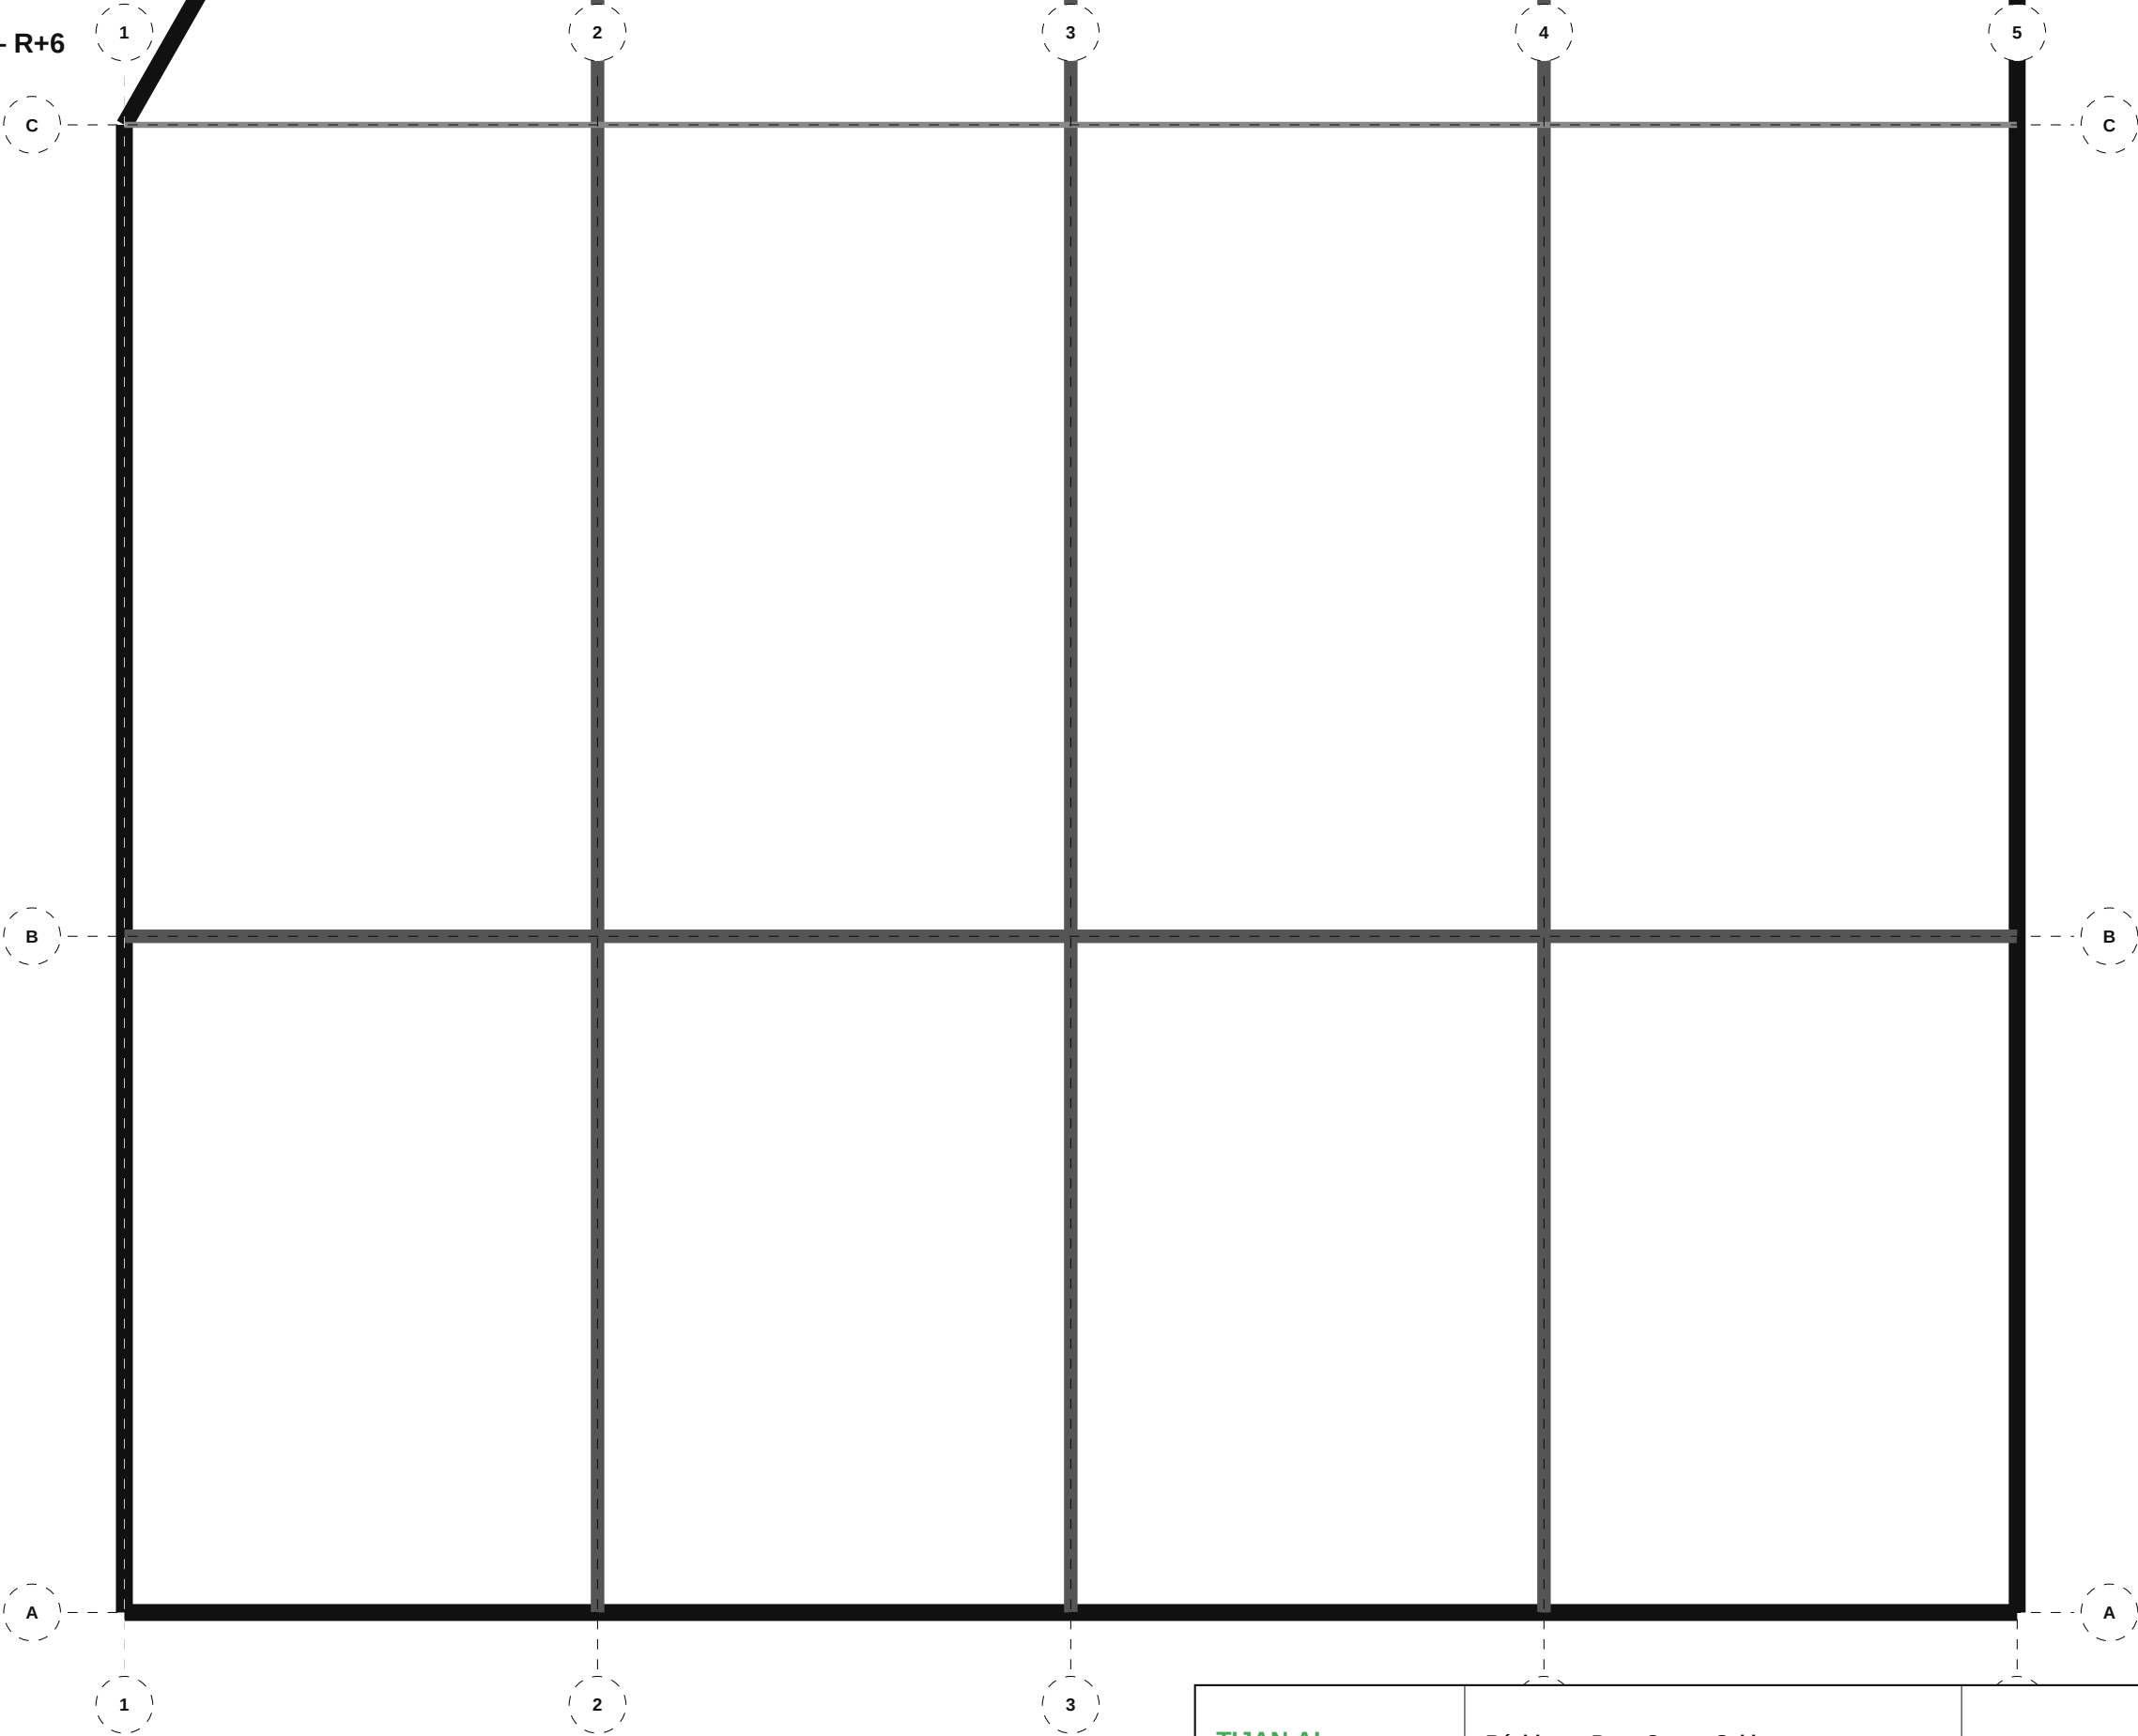

TIJAN AI Bureau d'Études Automatisé	Résidence Papa Oumar Sakho Dakar, Senegal	Éch: 1/100 Pl. 120/133
	113 RC — Faux Plafond — R+6	
Date: 06/05/2026	Réf: 1711	BIM vRC-120 Phase: APD

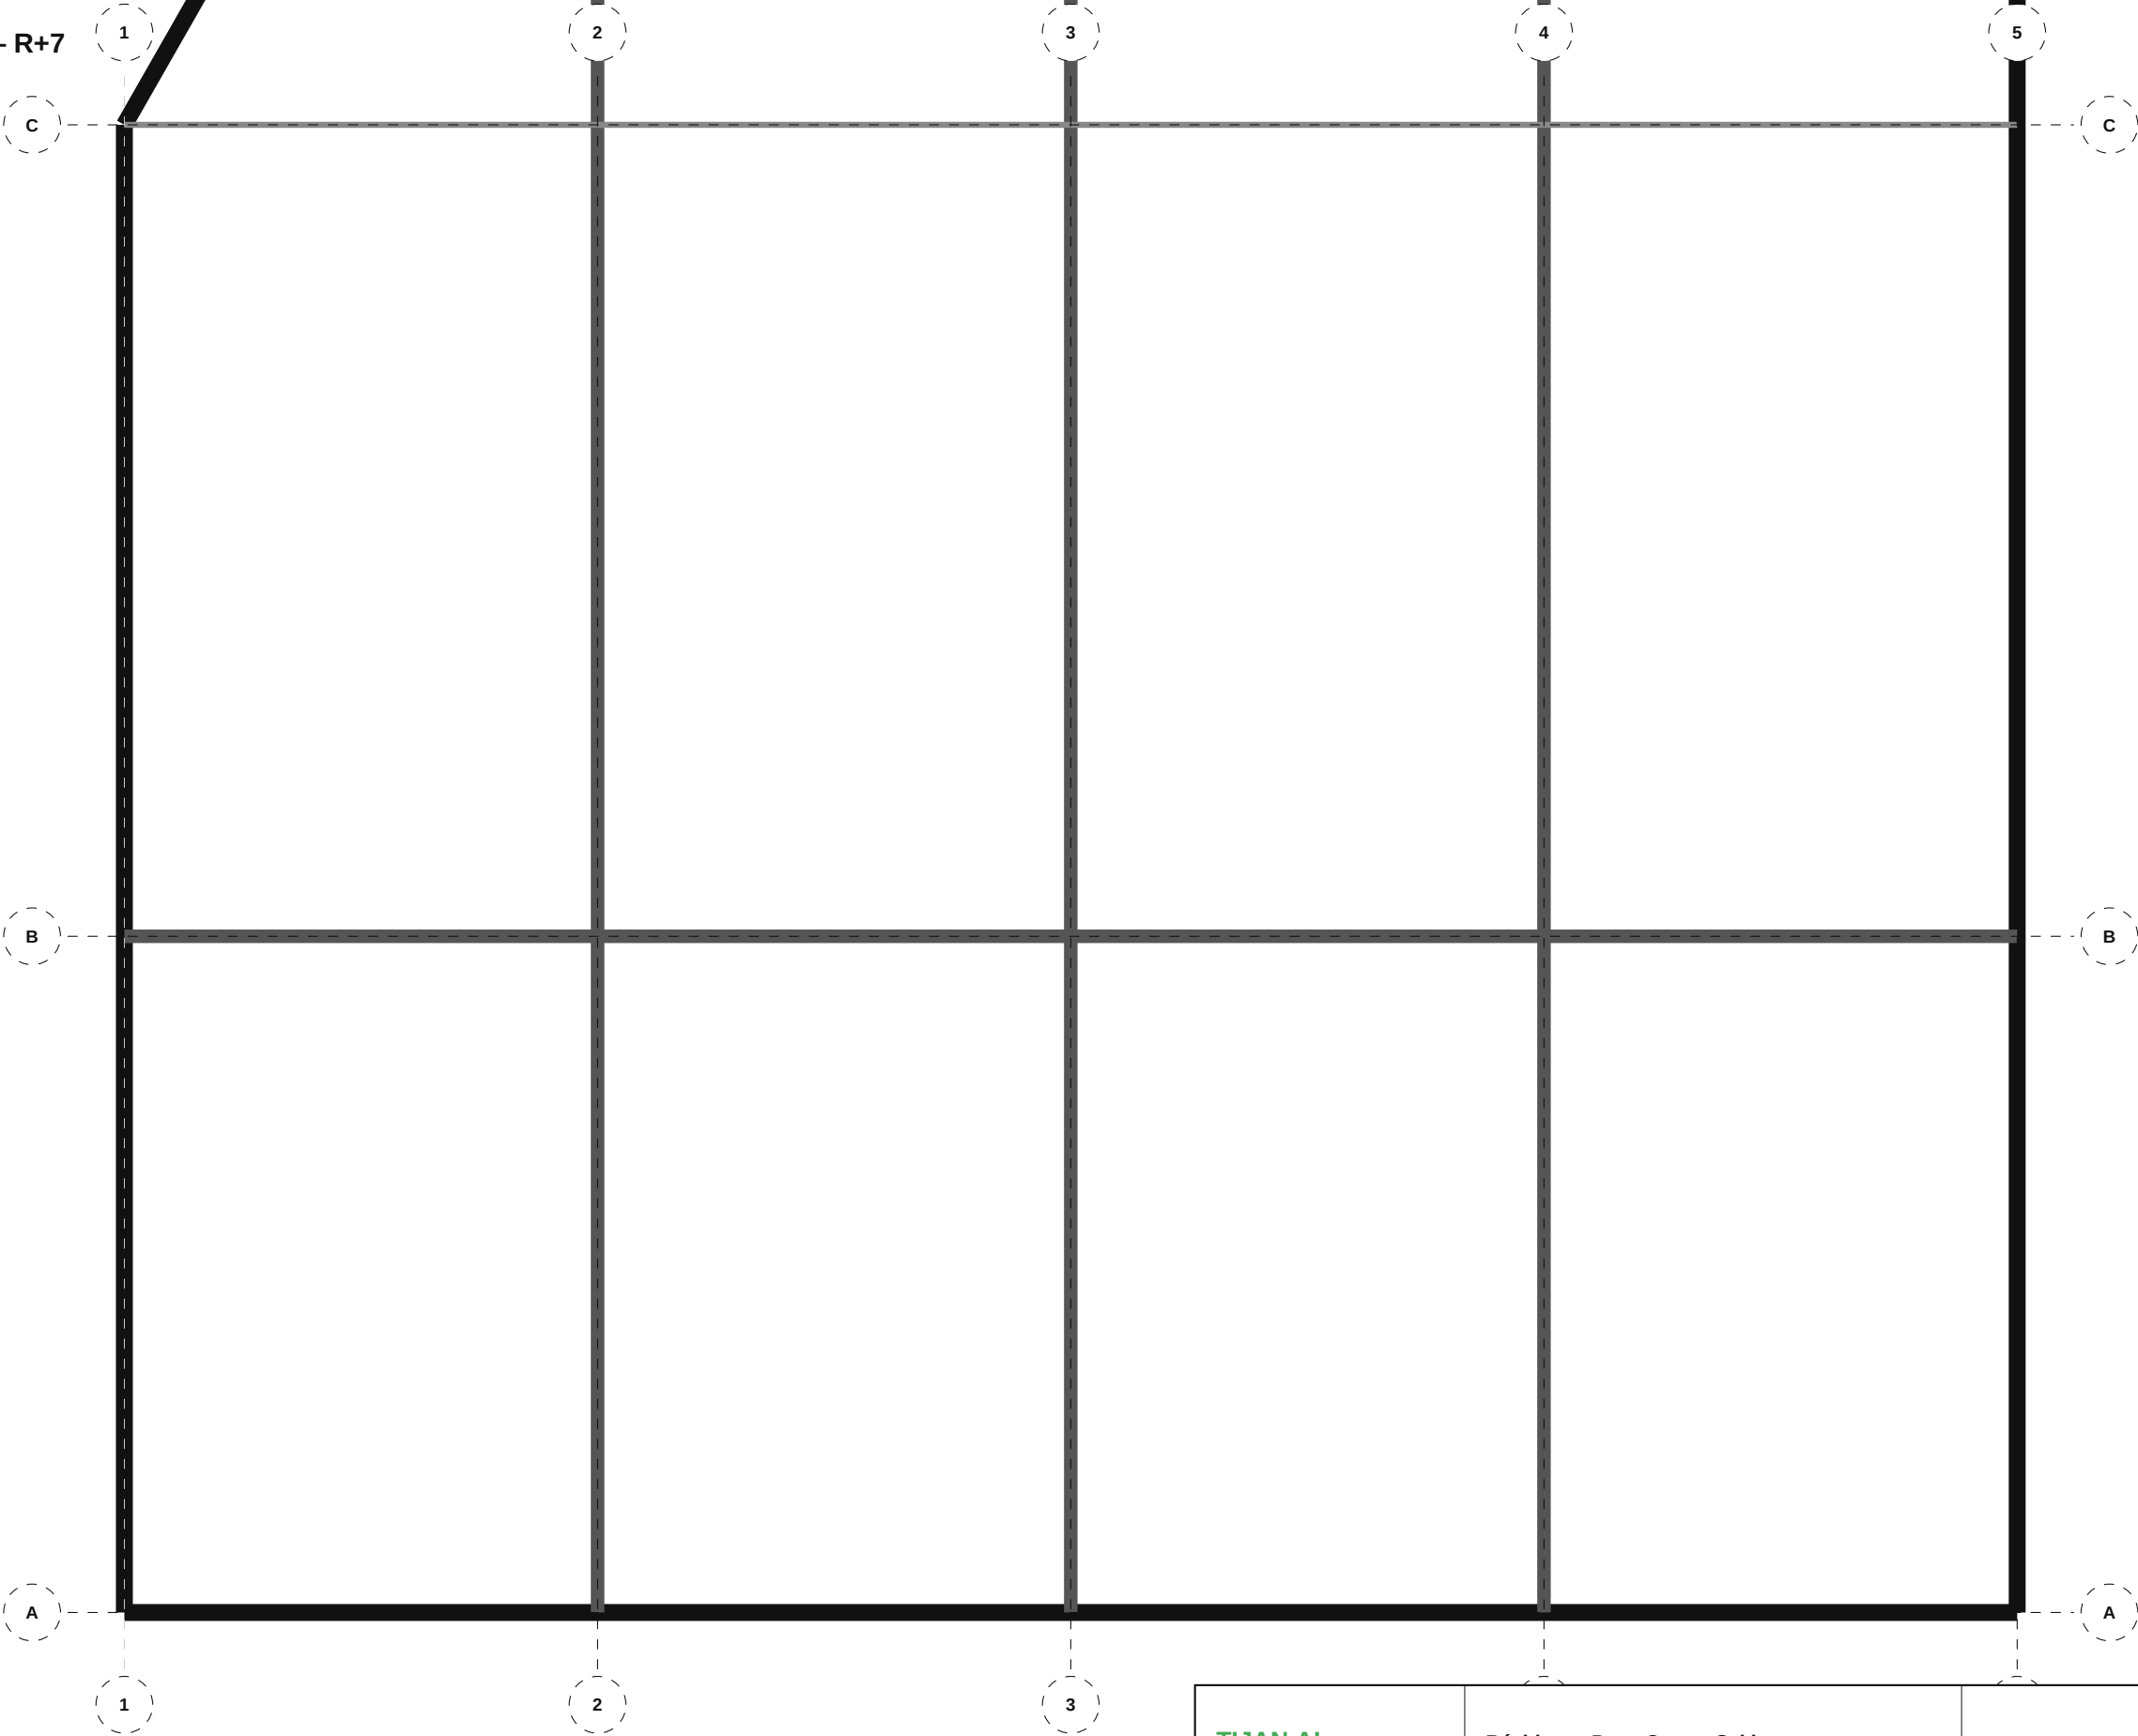

TIJAN AI

Bureau d'Études Automatisé

Résidence Papa Oumar Sakho

Dakar, Senegal

Éch: 1/100

Pl. 121/133


113 RC — Faux Plafond — R+7

Date: 06/05/2026

Réf: 1711

BIM VRC-121

Phase: APD

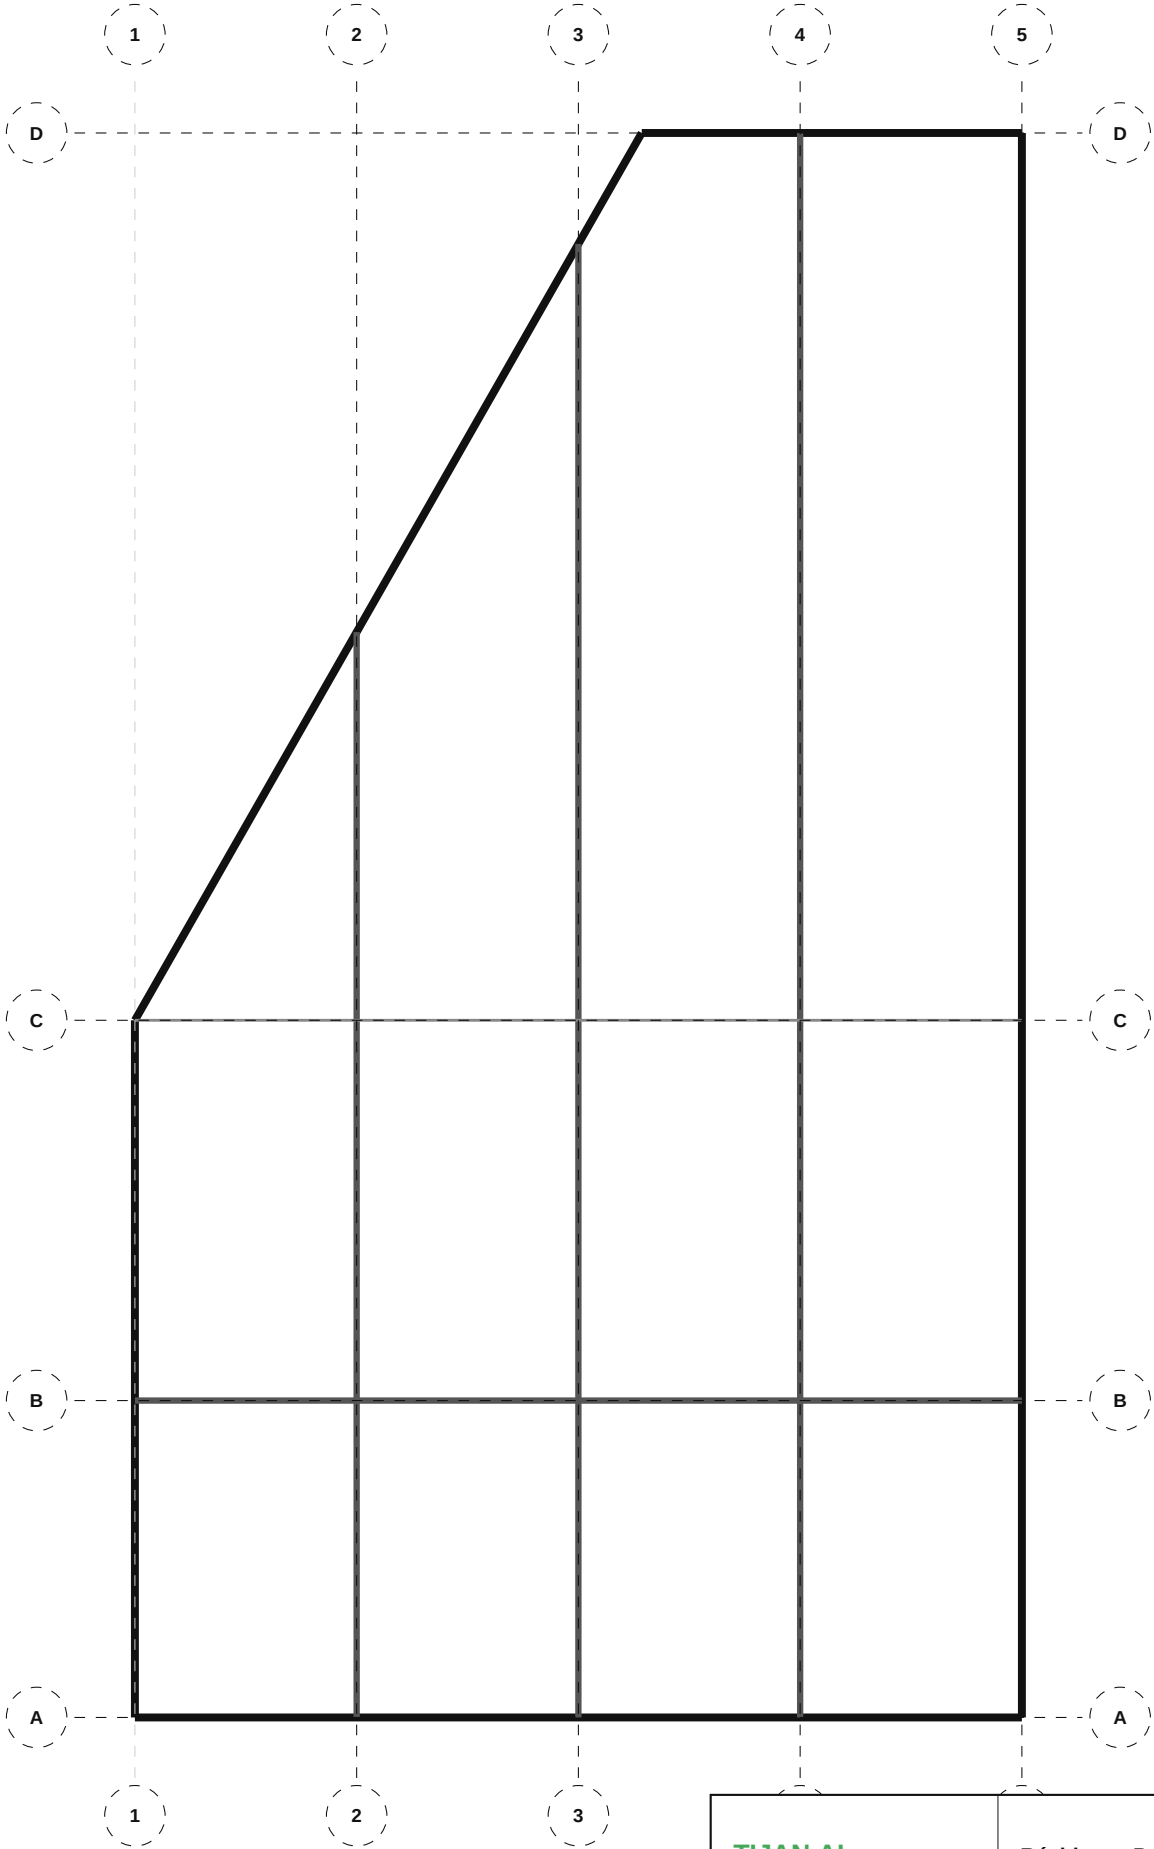

TIJAN AI Bureau d'Études Automatisé	Résidence Papa Oumar Sakho Dakar, Senegal	Éch: 1/100 Pl. 122/133
	113 RC — Faux Plafond — R+8 Terrasse	
Date: 06/05/2026	Réf: 1711	BIM VRC-122 Phase: APD


001 SYN — Synthèse — Sous-Sol

LÉGENDE RÉSEAUX

- EF — Eau Froide
- EC — Eau Chaude
- EU — Eaux Usées
- CLIM — Réfrigérant
- VMC — Extraction
- HCU — Courants Forts
- LCU — Courants Faibles
- SPK — Sprinkler

CONFLITS DÉTECTÉS

- Critiques: 14
- Dégagements: 0
- Croisements: 0

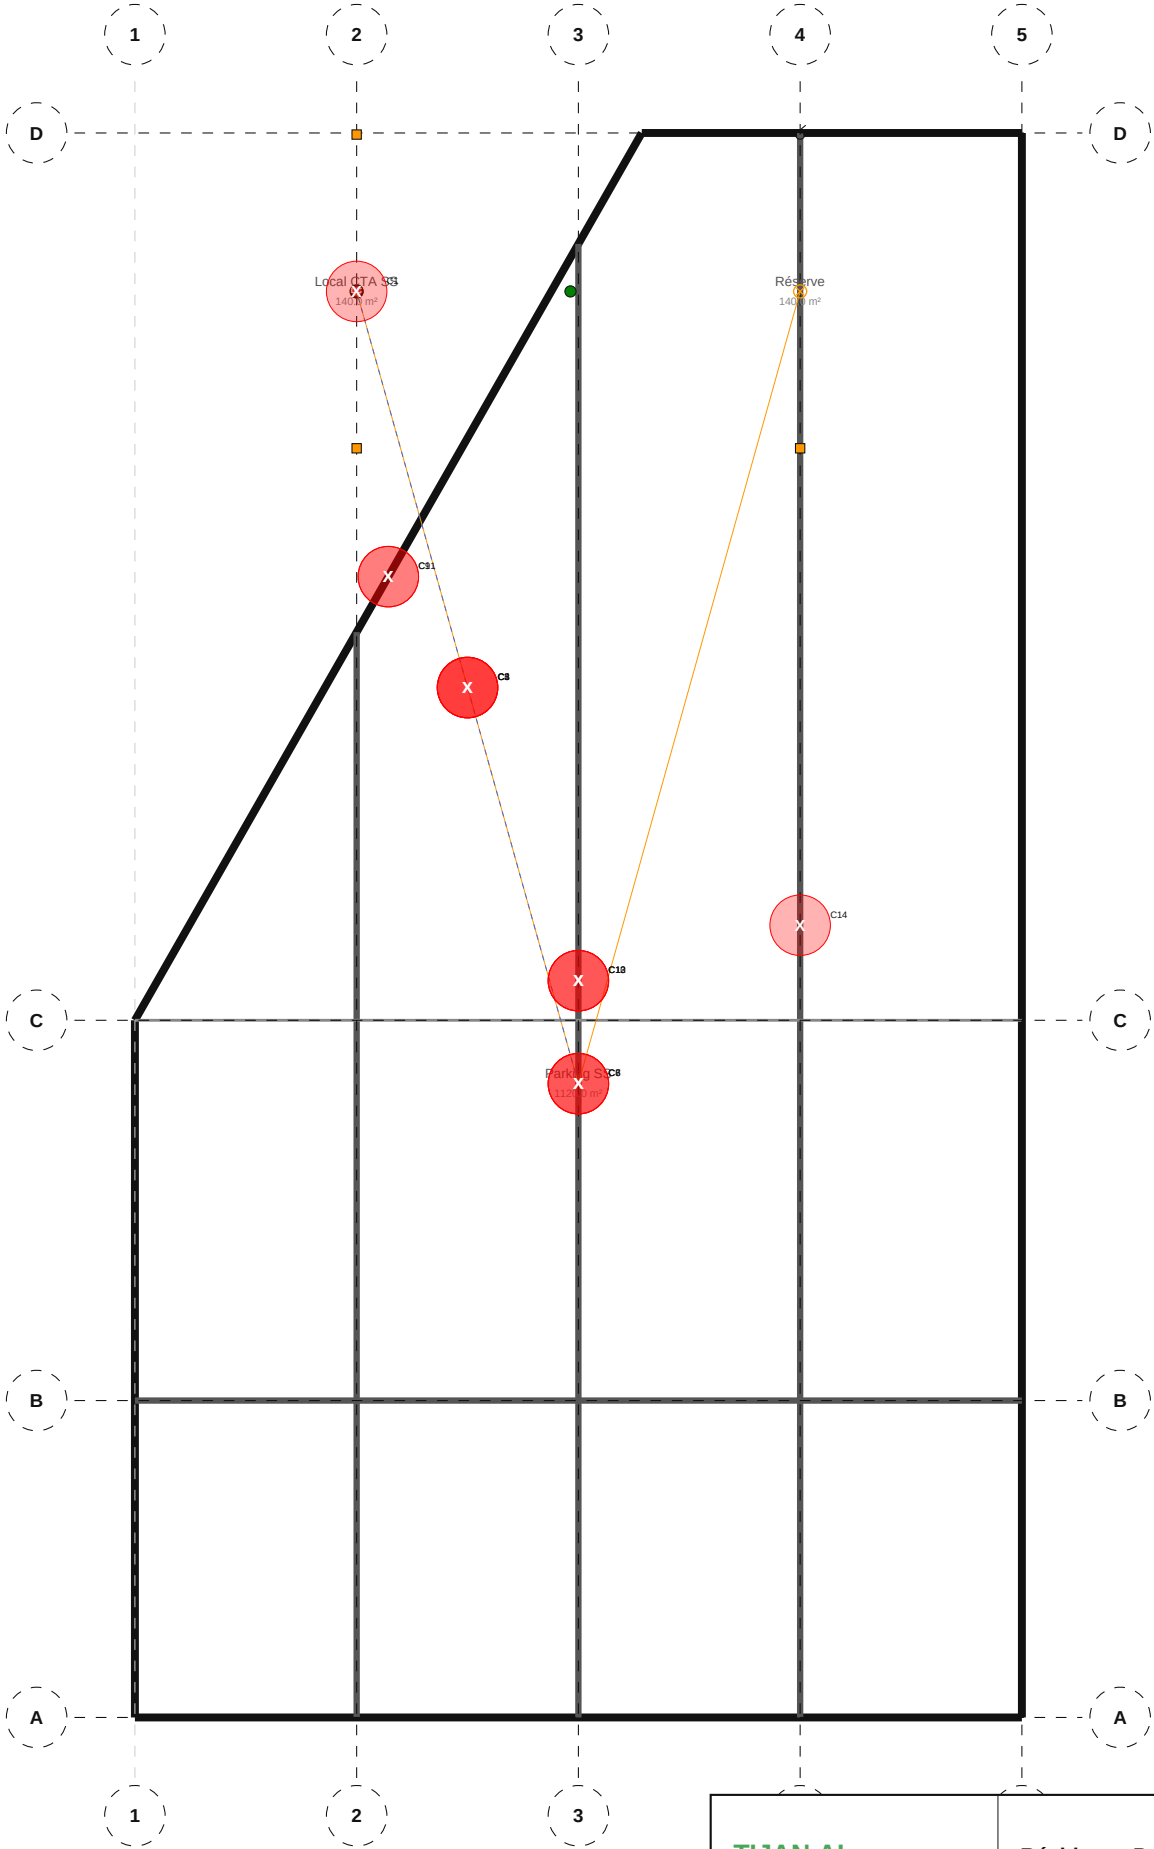

TIJAN AI Bureau d'Études Automatisé	Résidence Papa Oumar Sakho Dakar, Senegal	Éch: 1/100 Pl. 123/133
	001 SYN — Synthèse — Sous-Sol	
Date: 06/05/2026	Réf: 1711	BIM vSYN-123 Phase: APD


001 SYN — Synthèse — RDC

LÉGENDE RÉSEAUX

- EF — Eau Froide
- EC — Eau Chaude
- EU — Eaux Usées
- CLIM — Réfrigération
- VMC — Extraction
- HCU — Courant Hauts
- LCU — Courant Bas
- SPK — Sprinkler

CONFLITS DÉTECTÉS

- Critiques: 120
- Dégagements: 5
- Croisements: 0

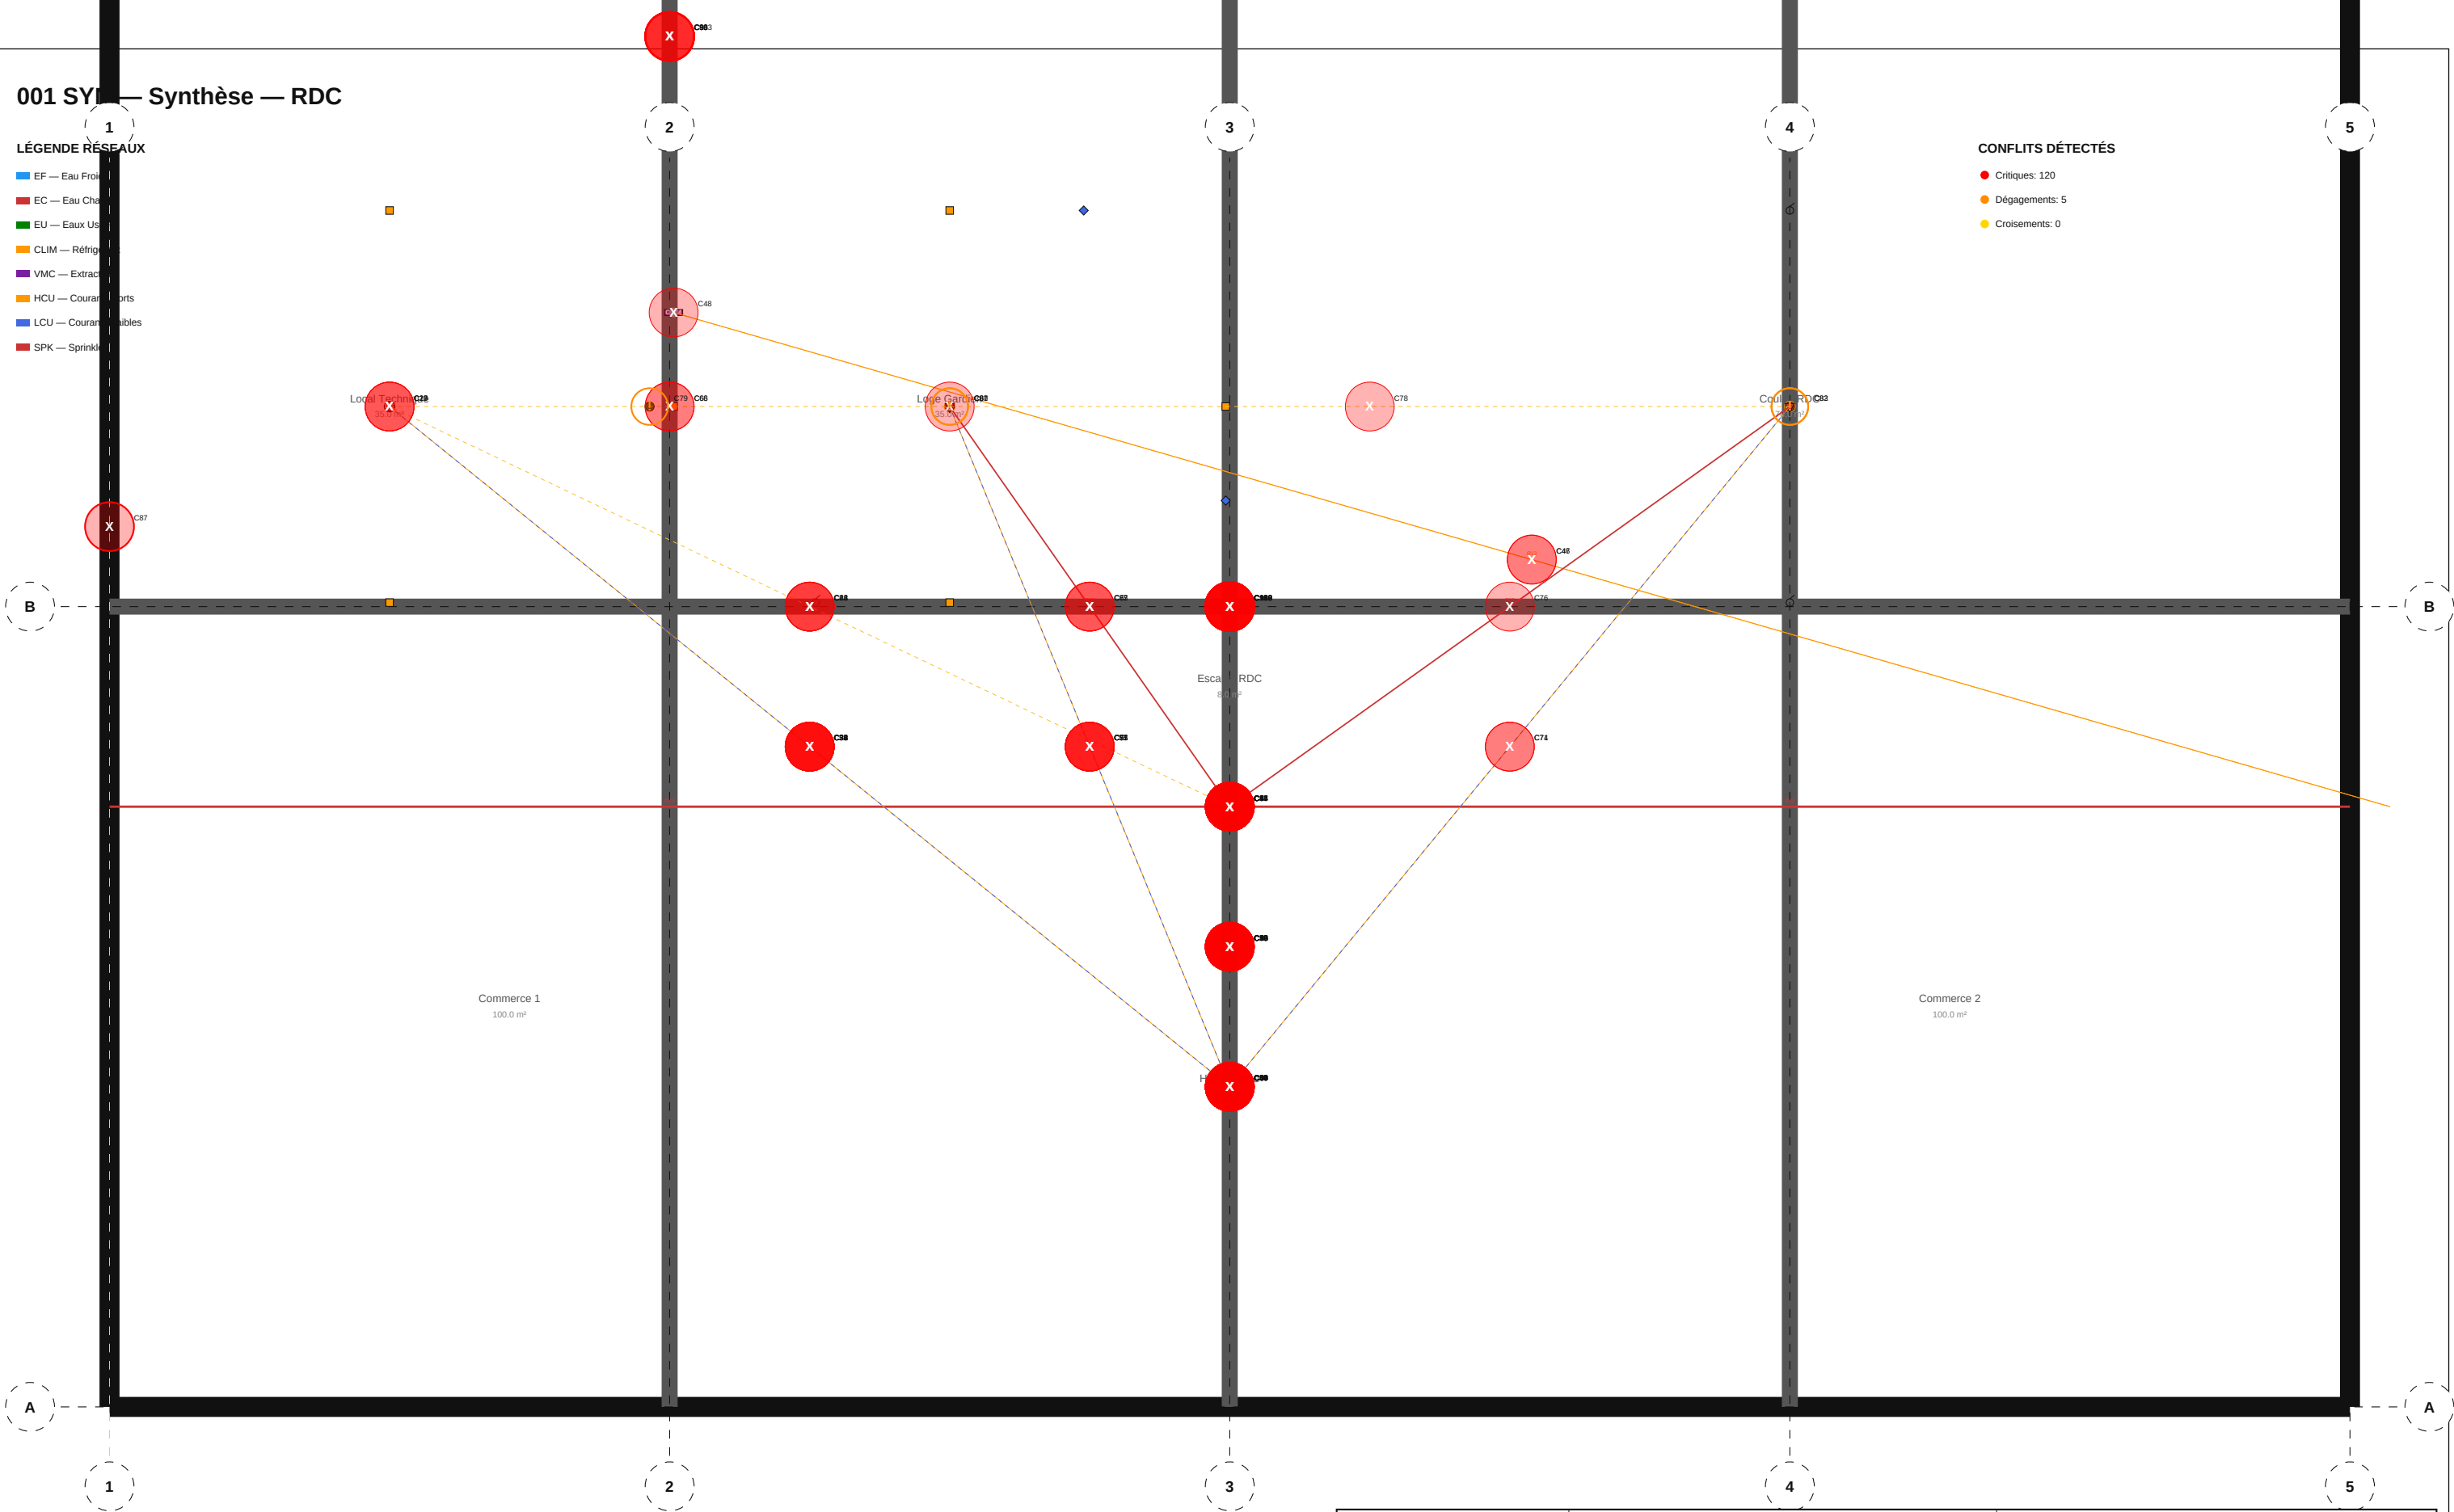

TIJAN AI Bureau d'Études Automatisé	Résidence Papa Oumar Sakho Dakar, Senegal	Éch: 1/100 Pl. 124/133
	001 SYN — Synthèse — RDC	
Date: 06/05/2026	Réf: 1711	BIM vSYN-124 Phase: APD


001 SYN — Synthèse — R+1

LÉGENDE RÉSEAUX

- EF — Eau Froide
- EC — Eau Chaude
- EU — Eaux Usées
- CLIM — Réfrigérant
- VMC — Extraction
- HCU — Courants Forts
- LCU — Courants Faibles
- SPK — Sprinkler

CONFLITS DÉTECTÉS

- Critiques: 77
- Dégagements: 832
- Croisements: 63

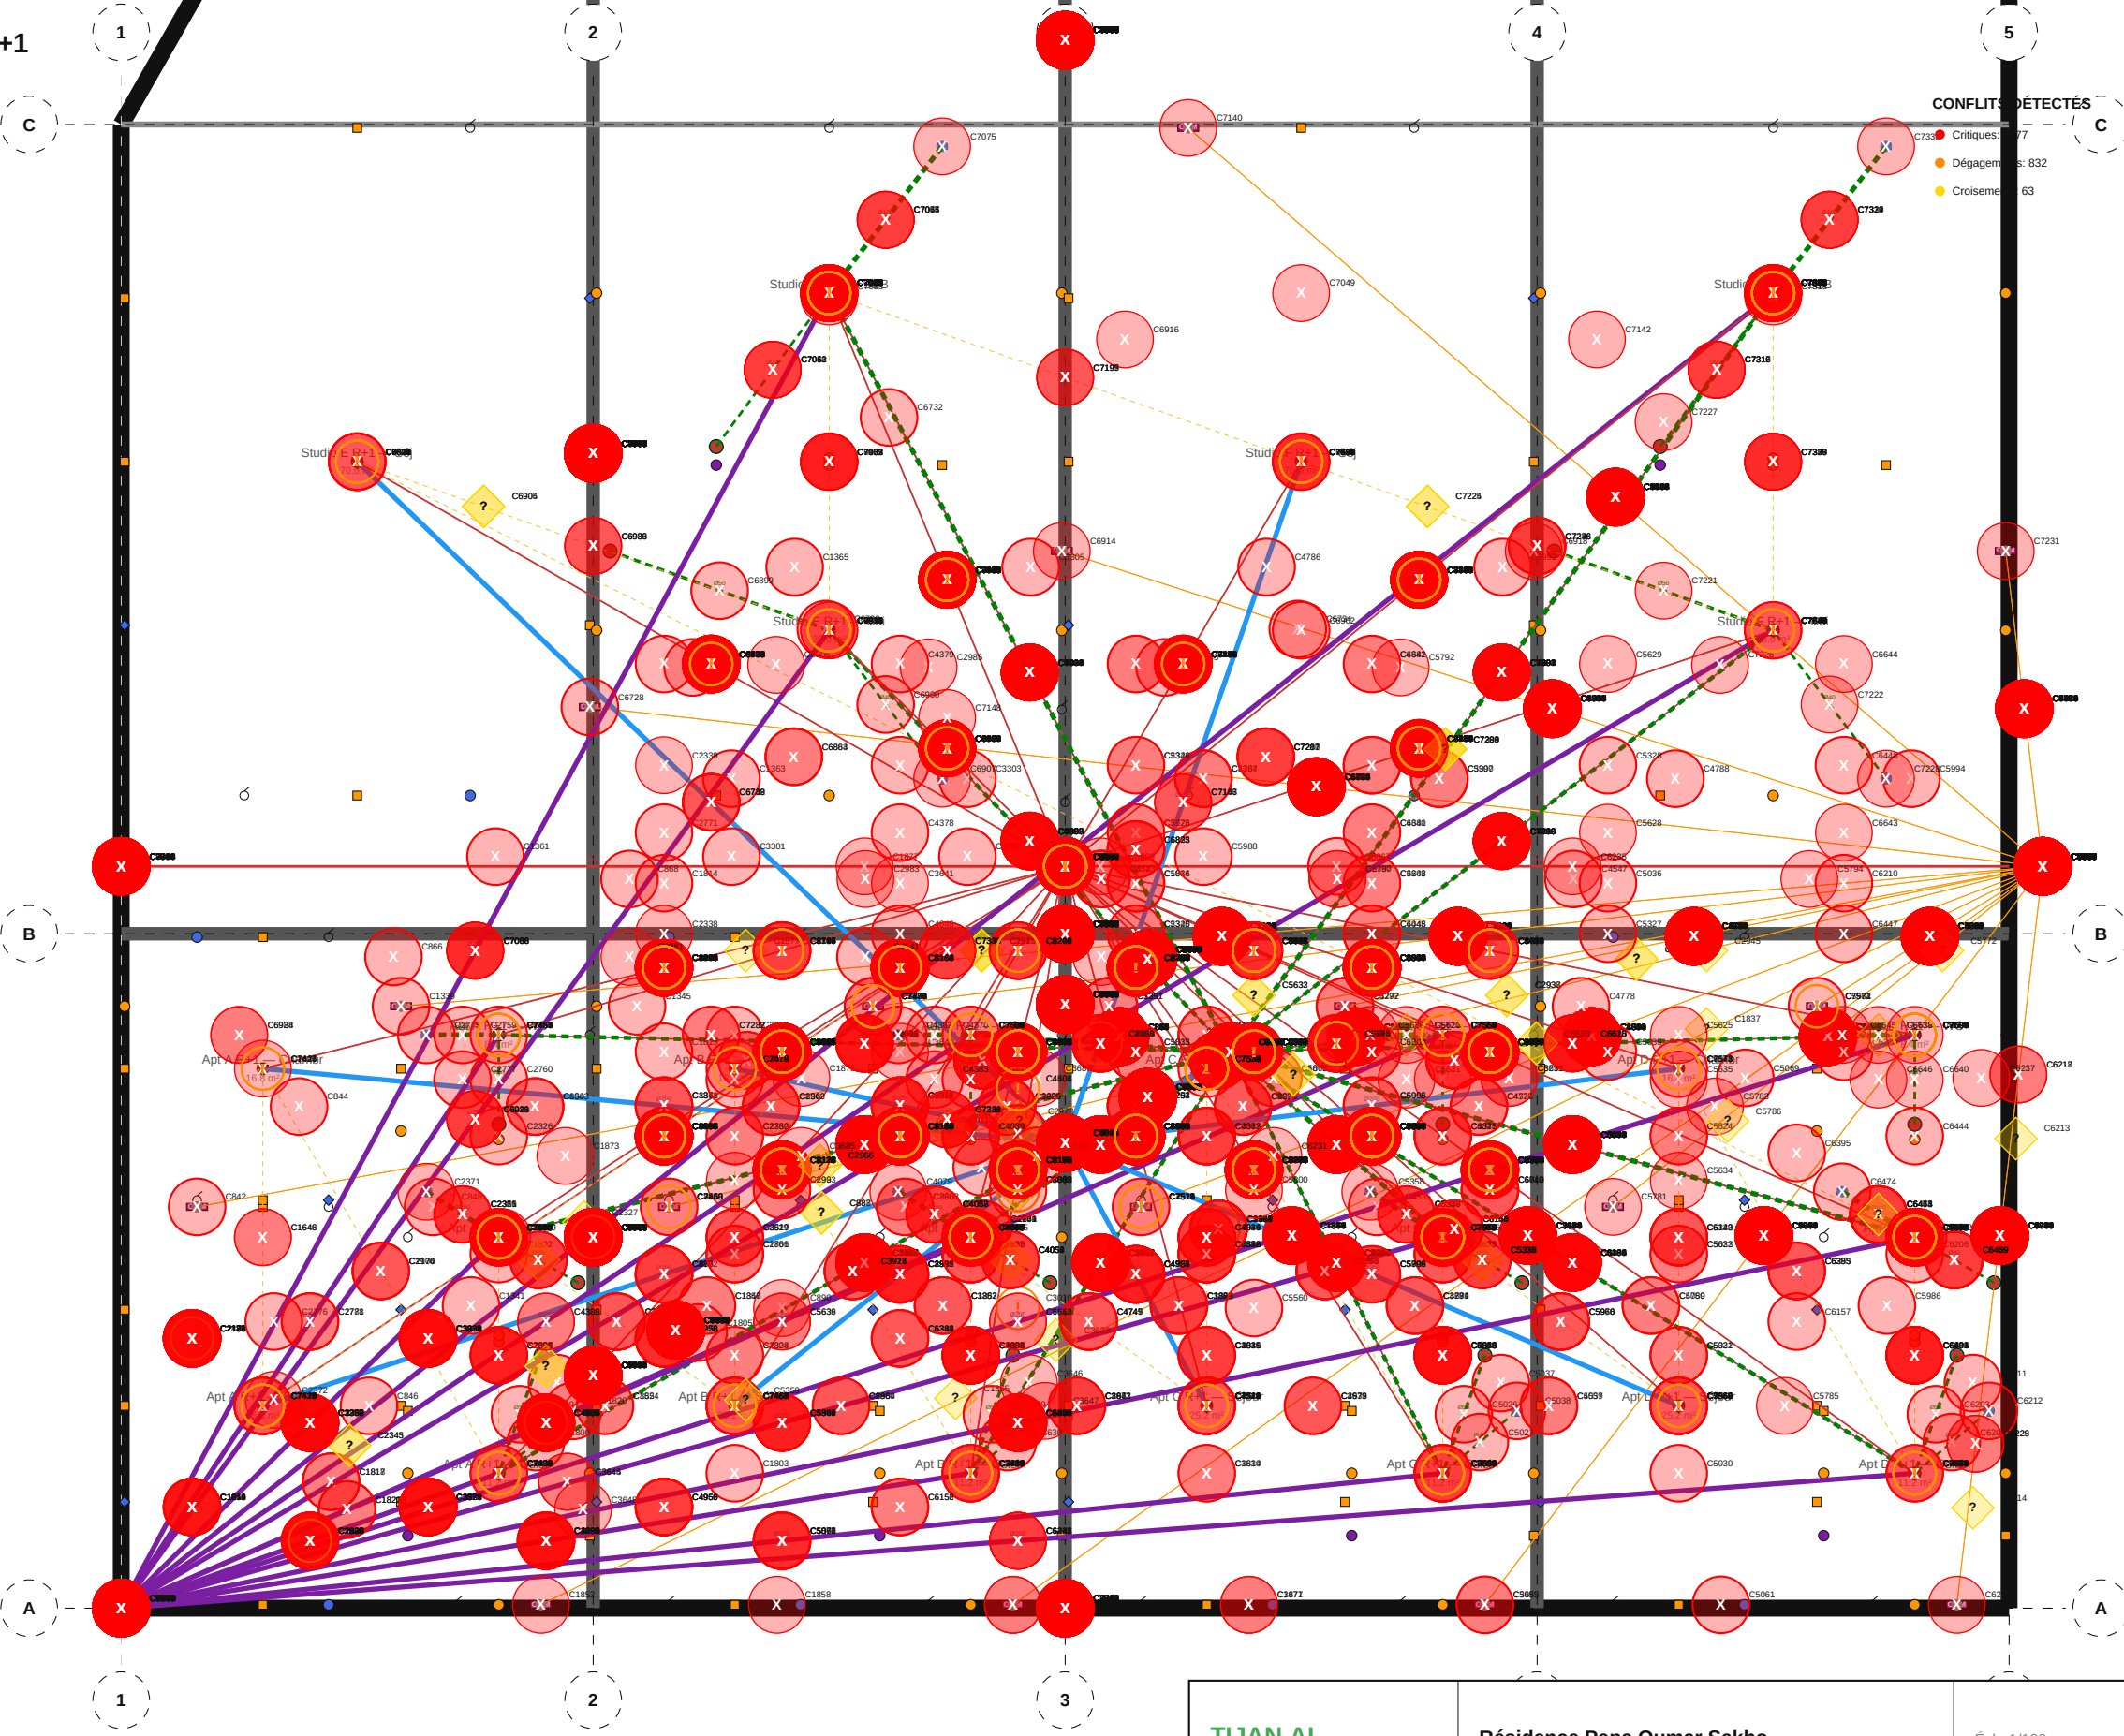

TIJAN AI Bureau d'Études Automatisé	Résidence Papa Oumar Sakho Dakar, Senegal	Éch: 1/100 Pl. 125/133
	001 SYN — Synthèse — R+1	
Date: 06/05/2026	Réf: 1711	BIM vSYN-125 Phase: APD


001 SYN — Synthèse — R+2

LÉGENDE RÉSEAUX

- EF — Eau Froide
- EC — Eau Chaude
- EU — Eaux Usées
- CLIM — Réfrigérant
- VMC — Extraction
- HCU — Courants Forts
- LCU — Courants Faibles
- SPK — Sprinkler

CONFLITS DÉTECTÉS

- Critiques: 34
- Dégagements: 871
- Croisements: 65

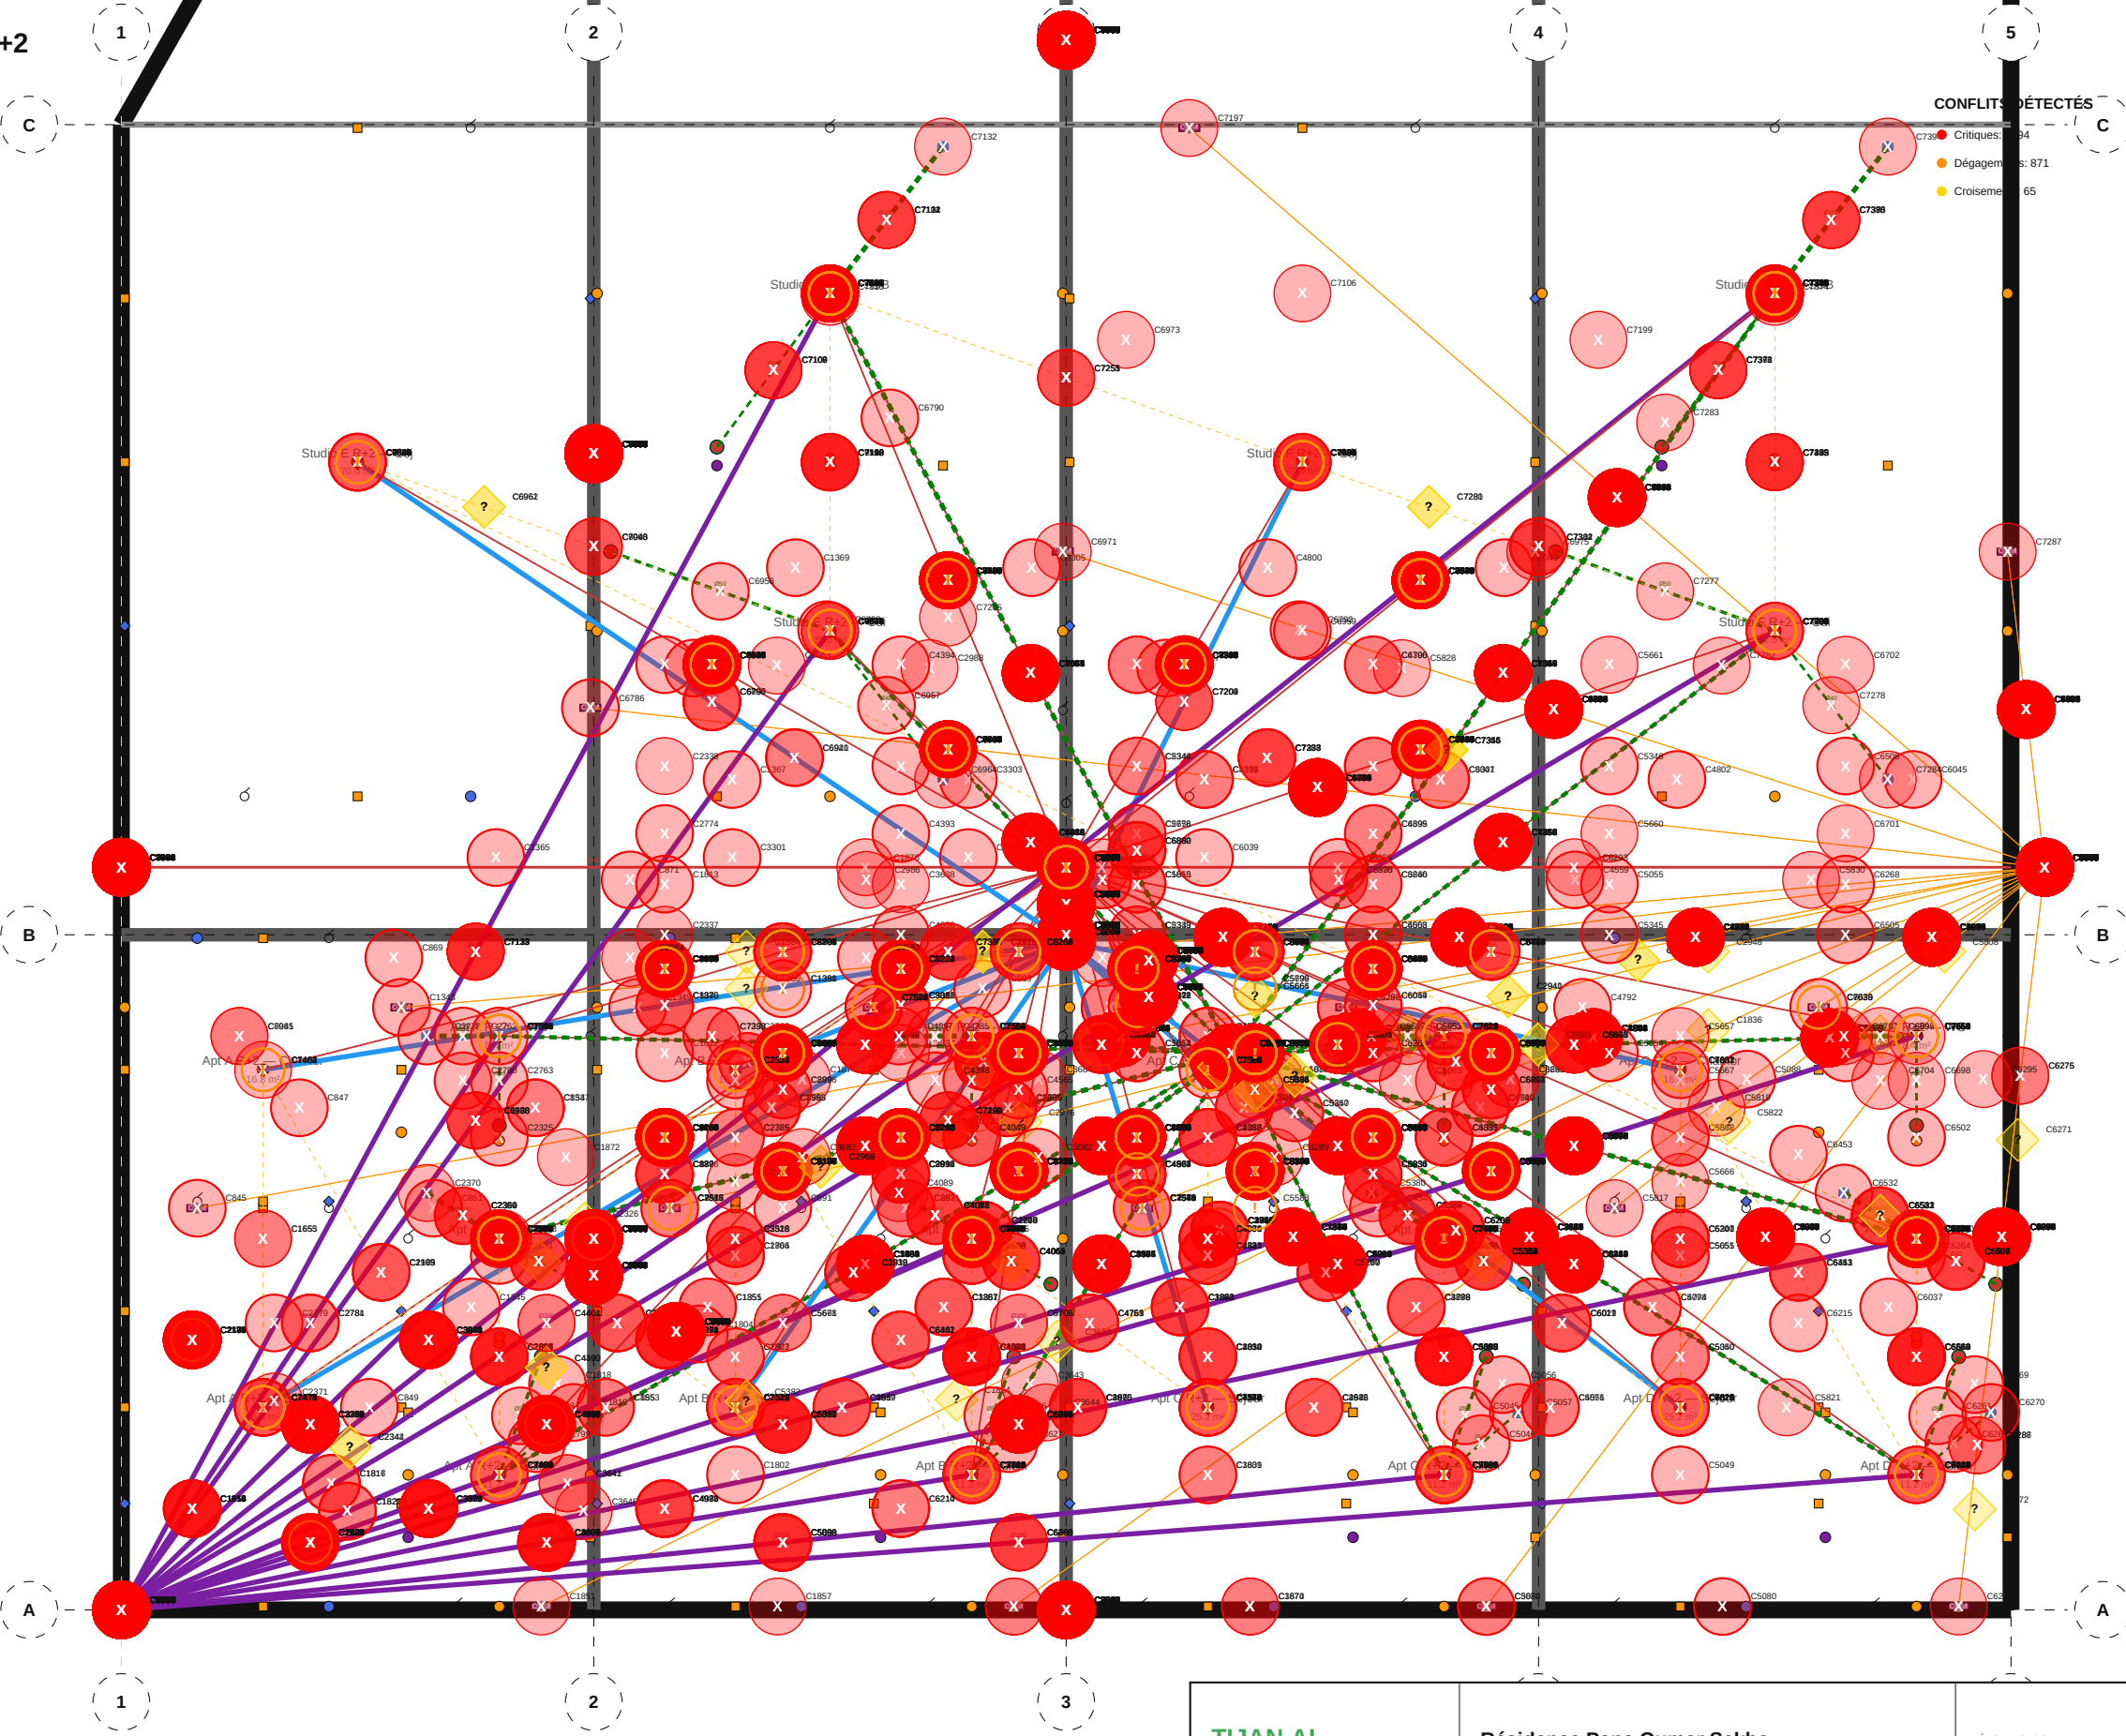

TIJAN AI
Bureau d'Études Automatisé

Résidence Papa Oumar Sakho
Dakar, Senegal

Éch: 1/100
Pl. 126/133

001 SYN — Synthèse — R+2

Date: 06/05/2026

Réf: 1711

BIM vSYN-126
Phase: APD


001 SYN — Synthèse — R+3

LÉGENDE RÉSEAUX

- EF — Eau Froide
- EC — Eau Chaude
- EU — Eaux Usées
- CLIM — Réfrigérant
- VMC — Extraction
- HCU — Courants Forts
- LCU — Courants Faibles
- SPK — Sprinkler

CONFLITS DÉTECTÉS

- Critiques: 13
- Dégagements: 827
- Croisements: 63

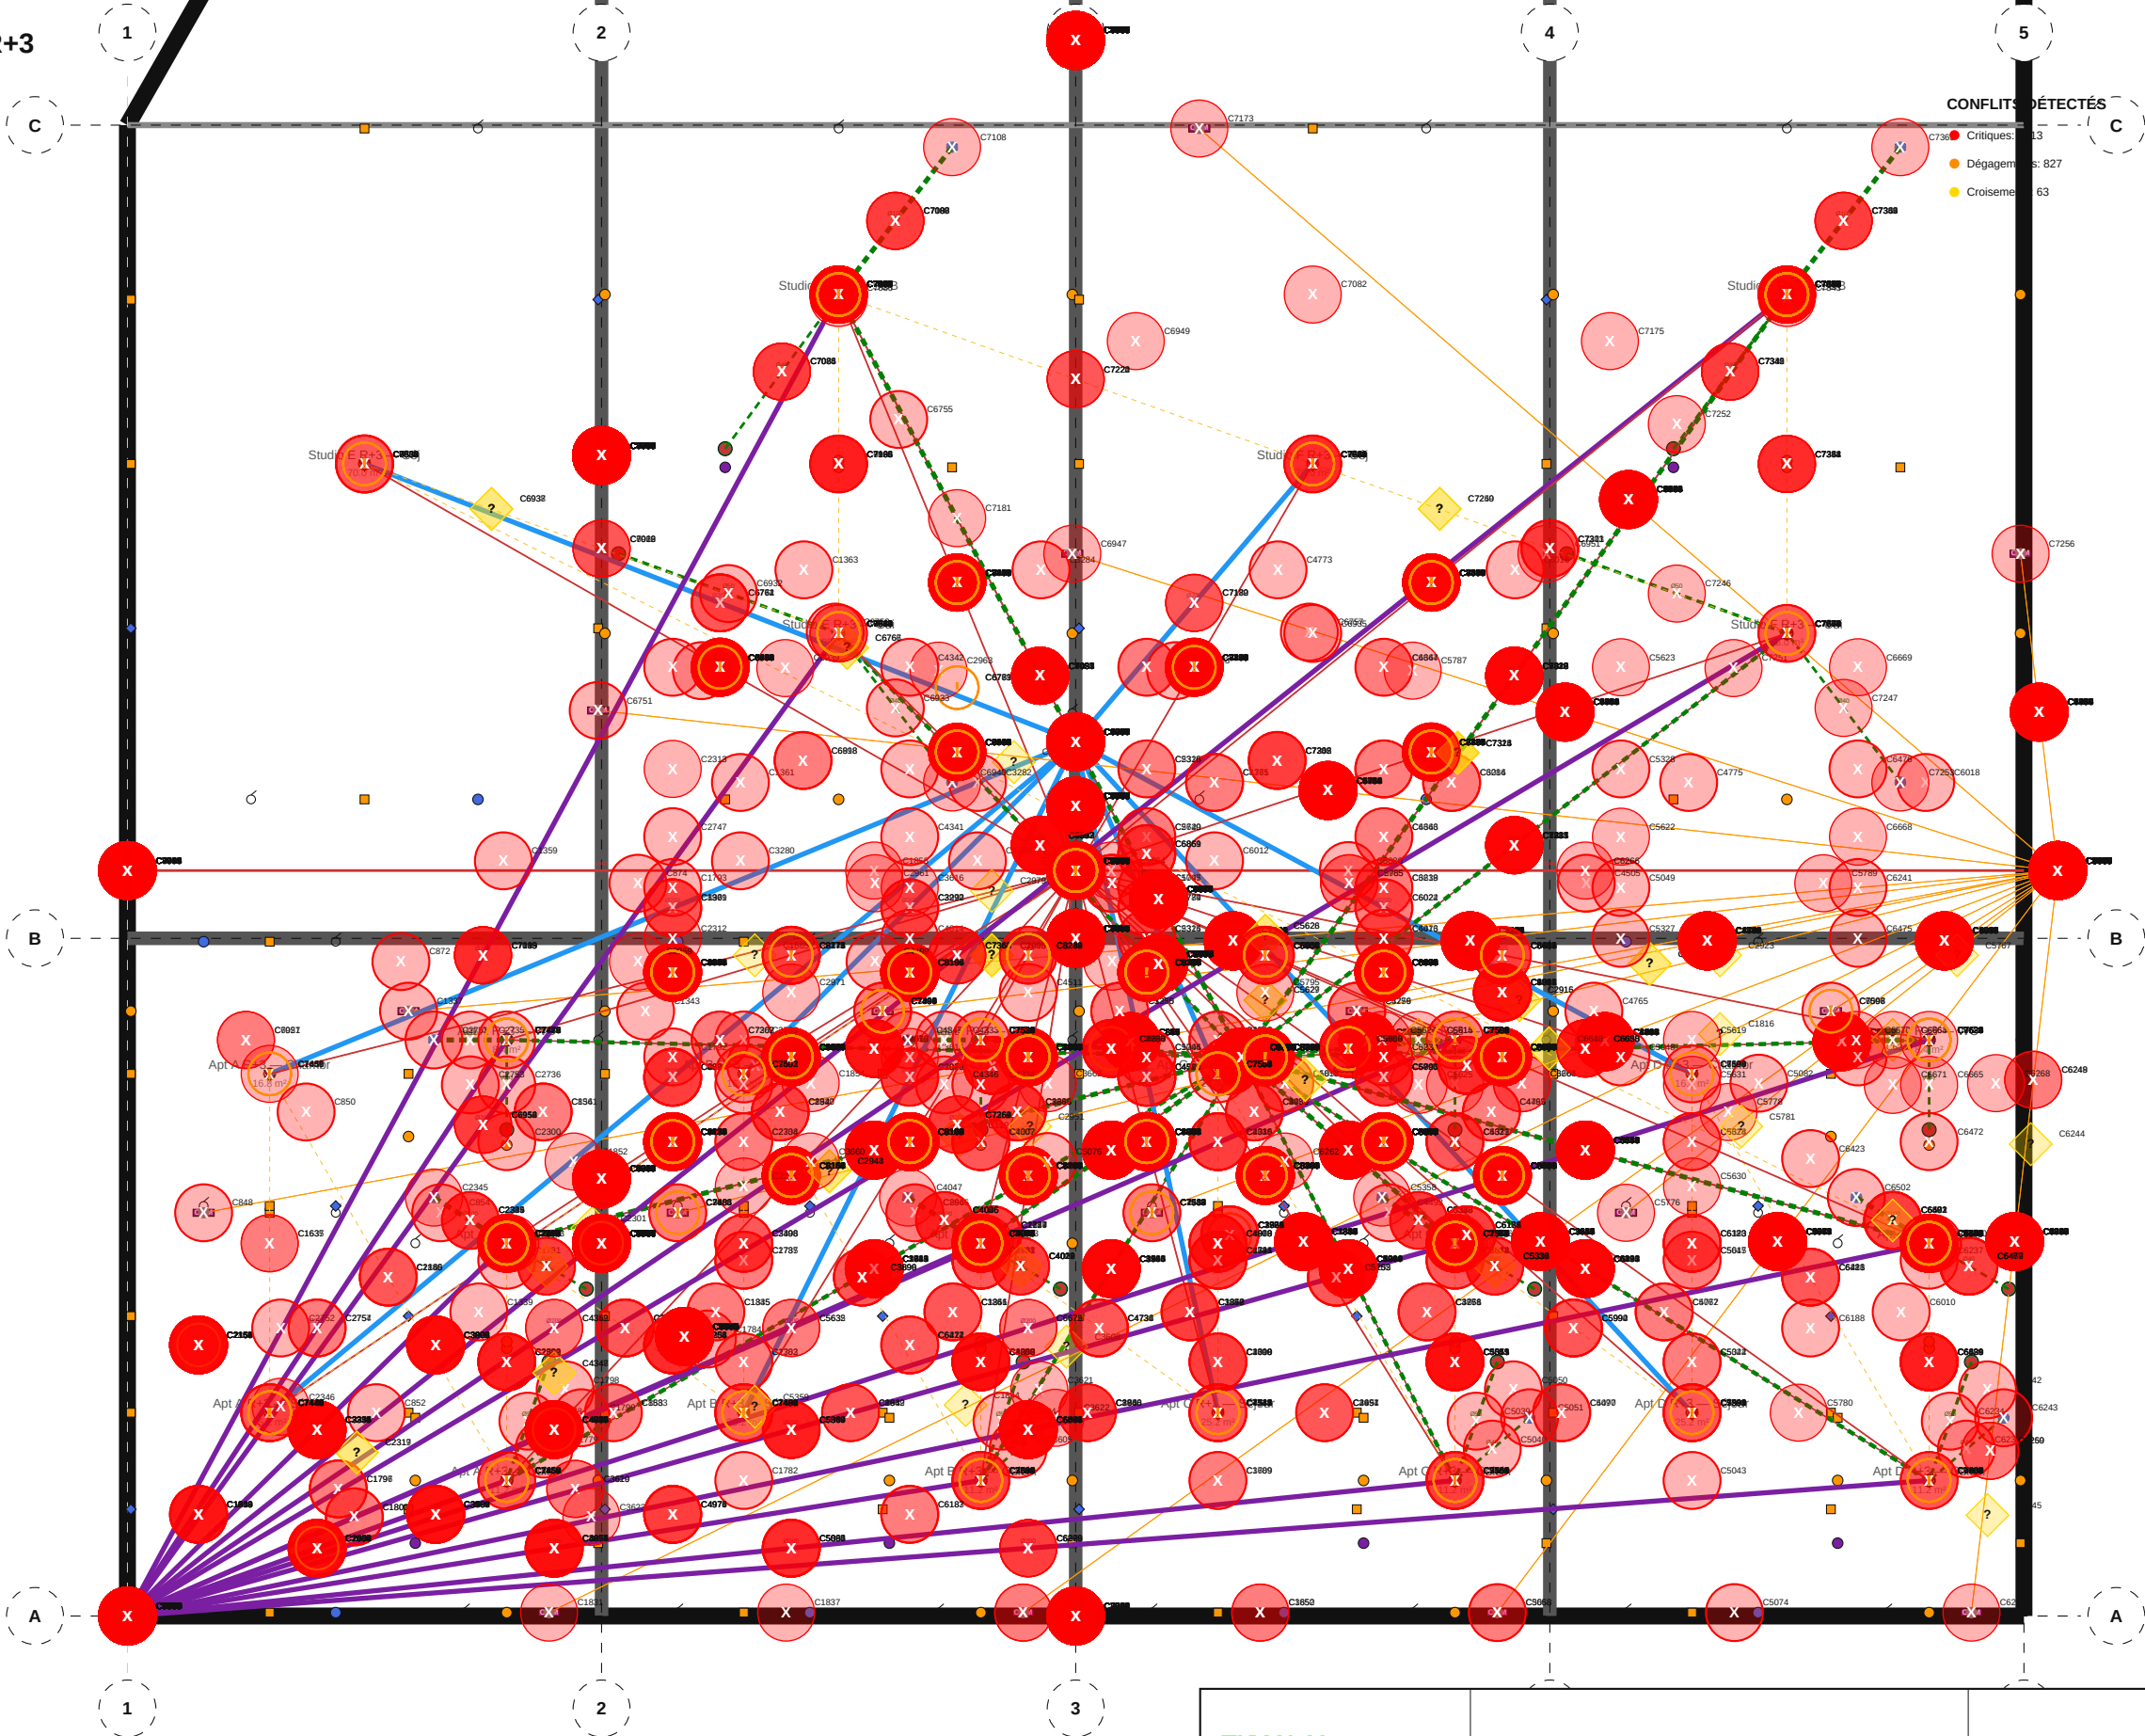

TIJAN AI

Bureau d'Études Automatisé

Résidence Papa Oumar Sakho

Dakar, Senegal

Éch: 1/100

Pl. 127/133

001 SYN — Synthèse — R+3

Date: 06/05/2026

Réf: 1711

BIM vSYN-127

Phase: APD


001 SYN — Synthèse — R+4

LÉGENDE RÉSEAUX

- EF — Eau Froide
- EC — Eau Chaude
- EU — Eaux Usées
- CLIM — Réfrigérant
- VMC — Extraction
- HCU — Courants Forts
- LCU — Courants Faibles
- SPK — Sprinkler

CONFLITS DÉTECTÉS

- Critiques: 102
- Dégagements: 825
- Croisements: 59

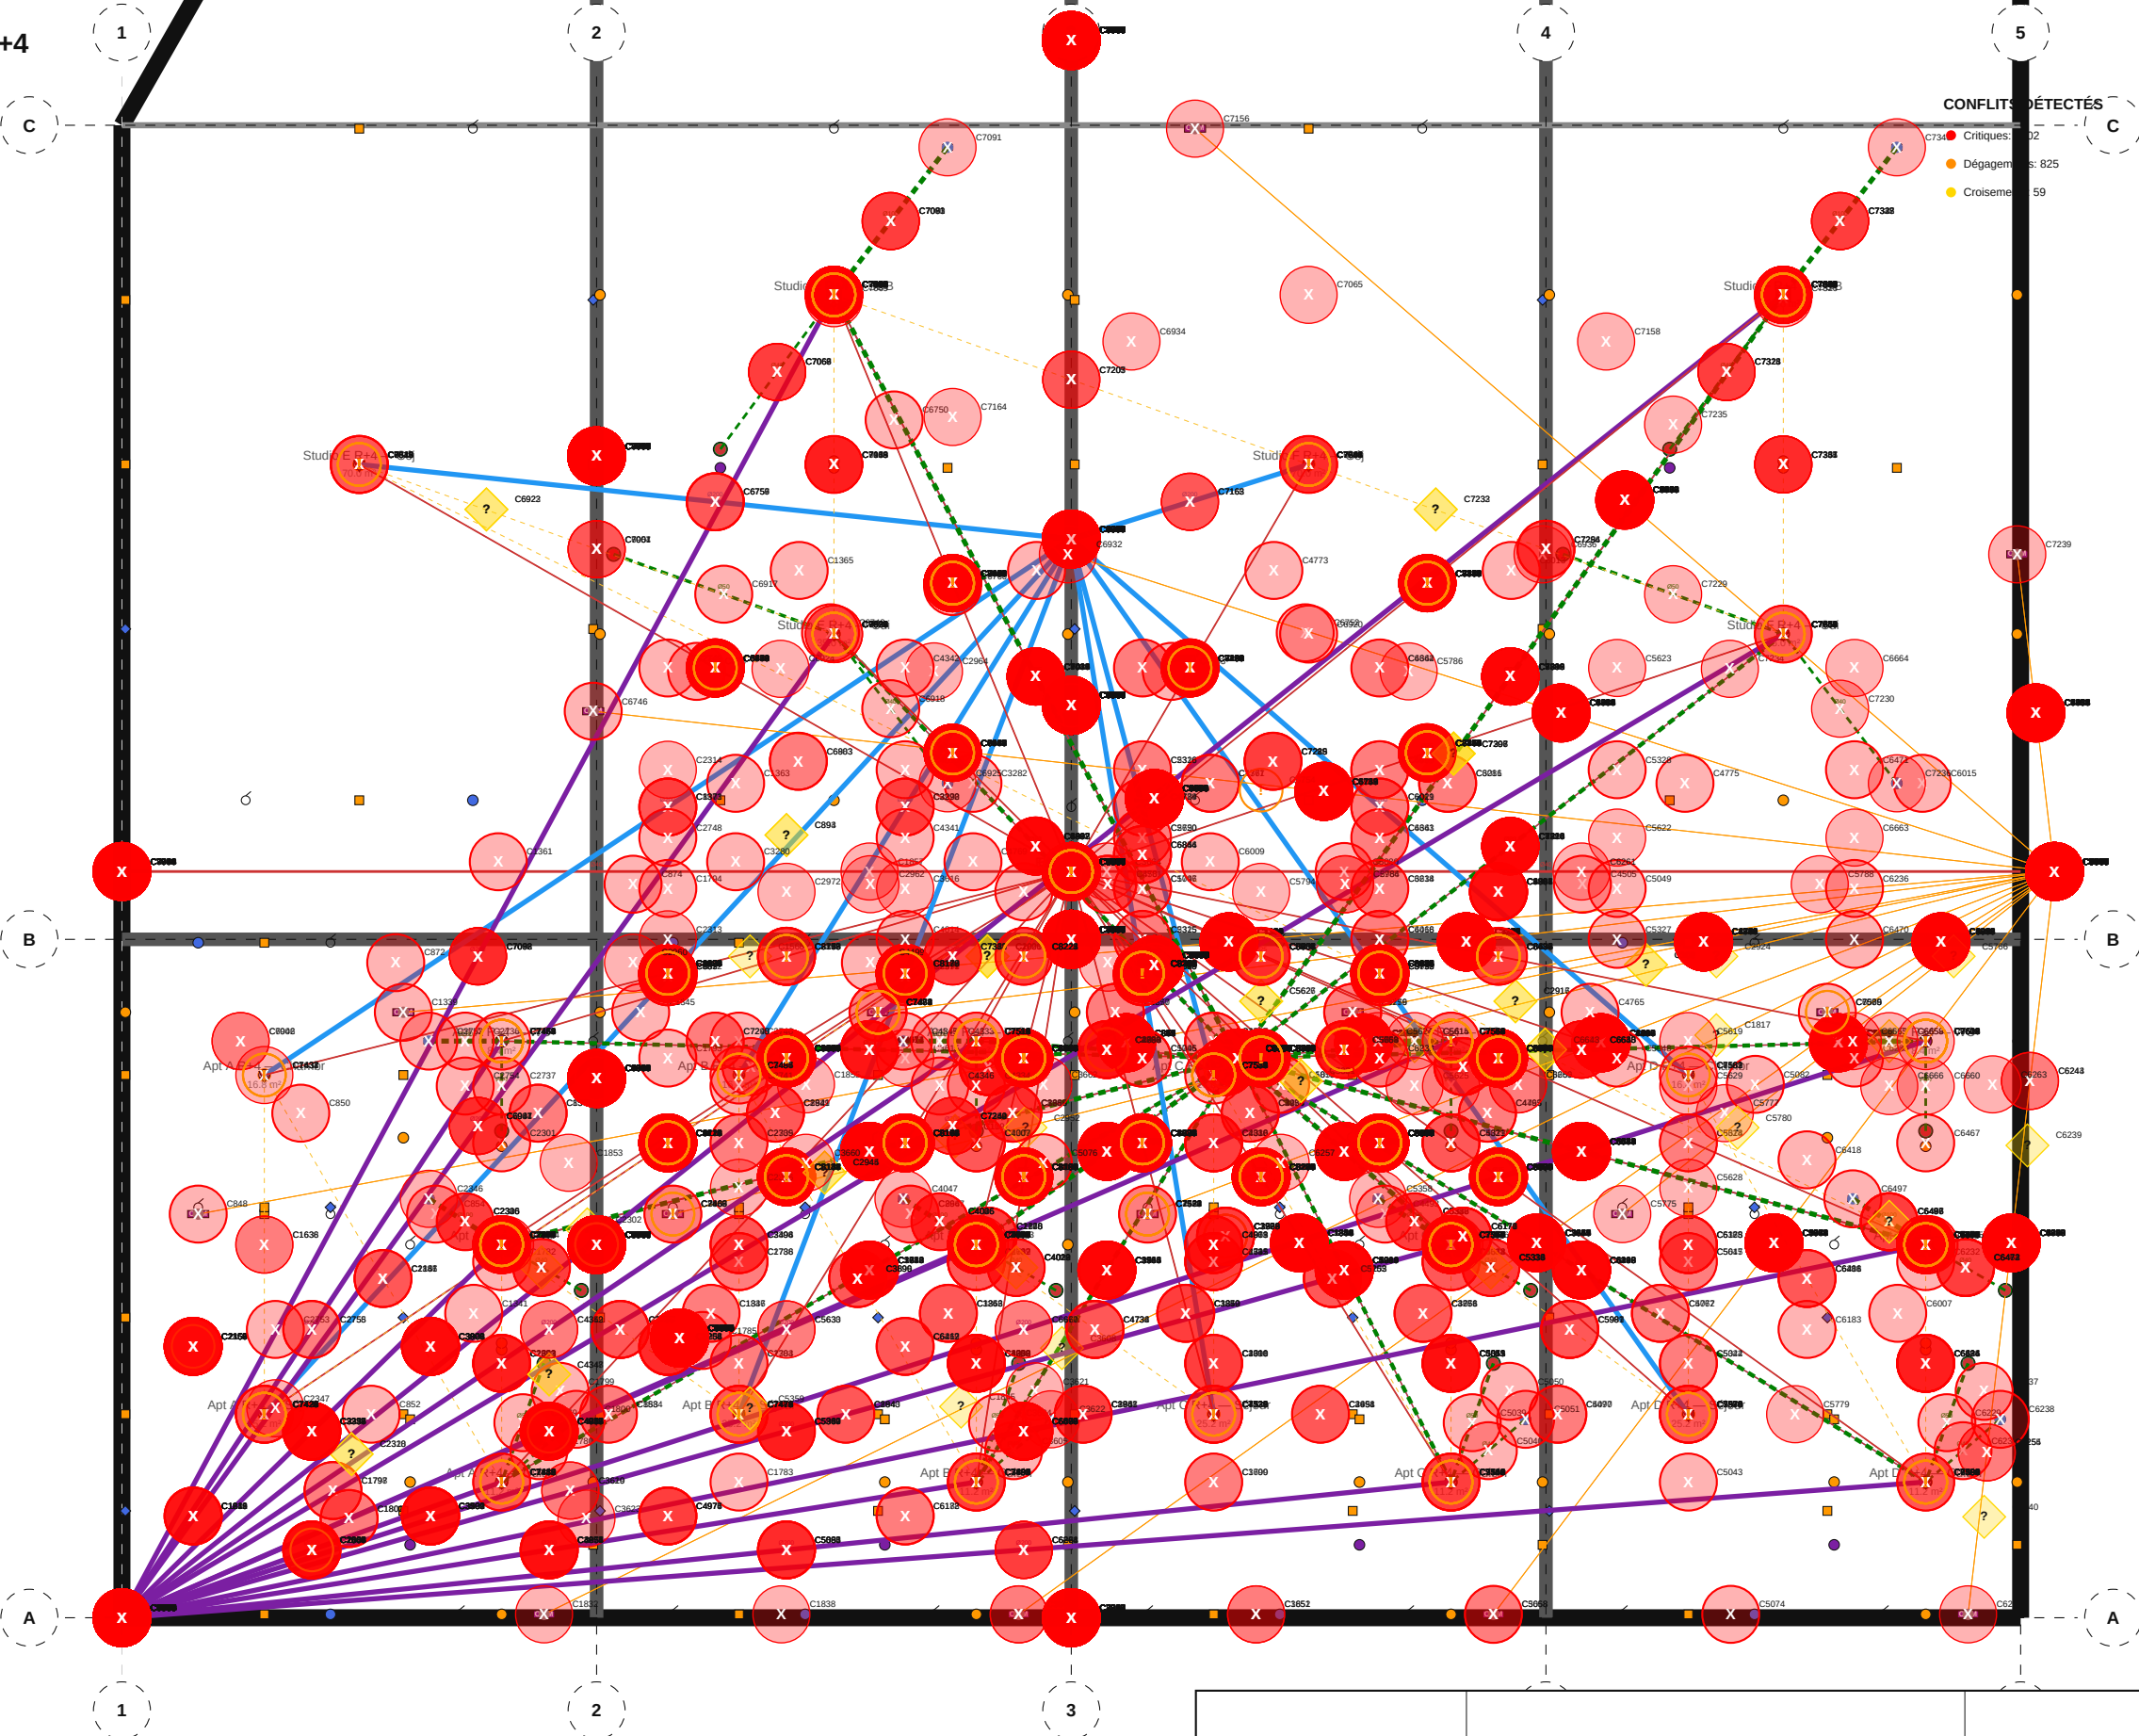

TIJAN AI

Bureau d'Études Automatisé

Résidence Papa Oumar Sakho

Dakar, Senegal

Éch: 1/100

Pl. 128/133

001 SYN — Synthèse — R+4

Date: 06/05/2026

Réf: 1711

BIM vSYN-128

Phase: APD

Phase: APD


001 SYN — Synthèse — R+6

LÉGENDE RÉSEAUX

- EF — Eau Froide
- EC — Eau Chaude
- EU — Eaux Usées
- CLIM — Réfrigérant
- VMC — Extraction
- HCU — Courants Forts
- LCU — Courants Faibles
- SPK — Sprinkler

CONFLITS DÉTECTÉS

- Critiques: 82
- Dégagements: 829
- Croisements: 57

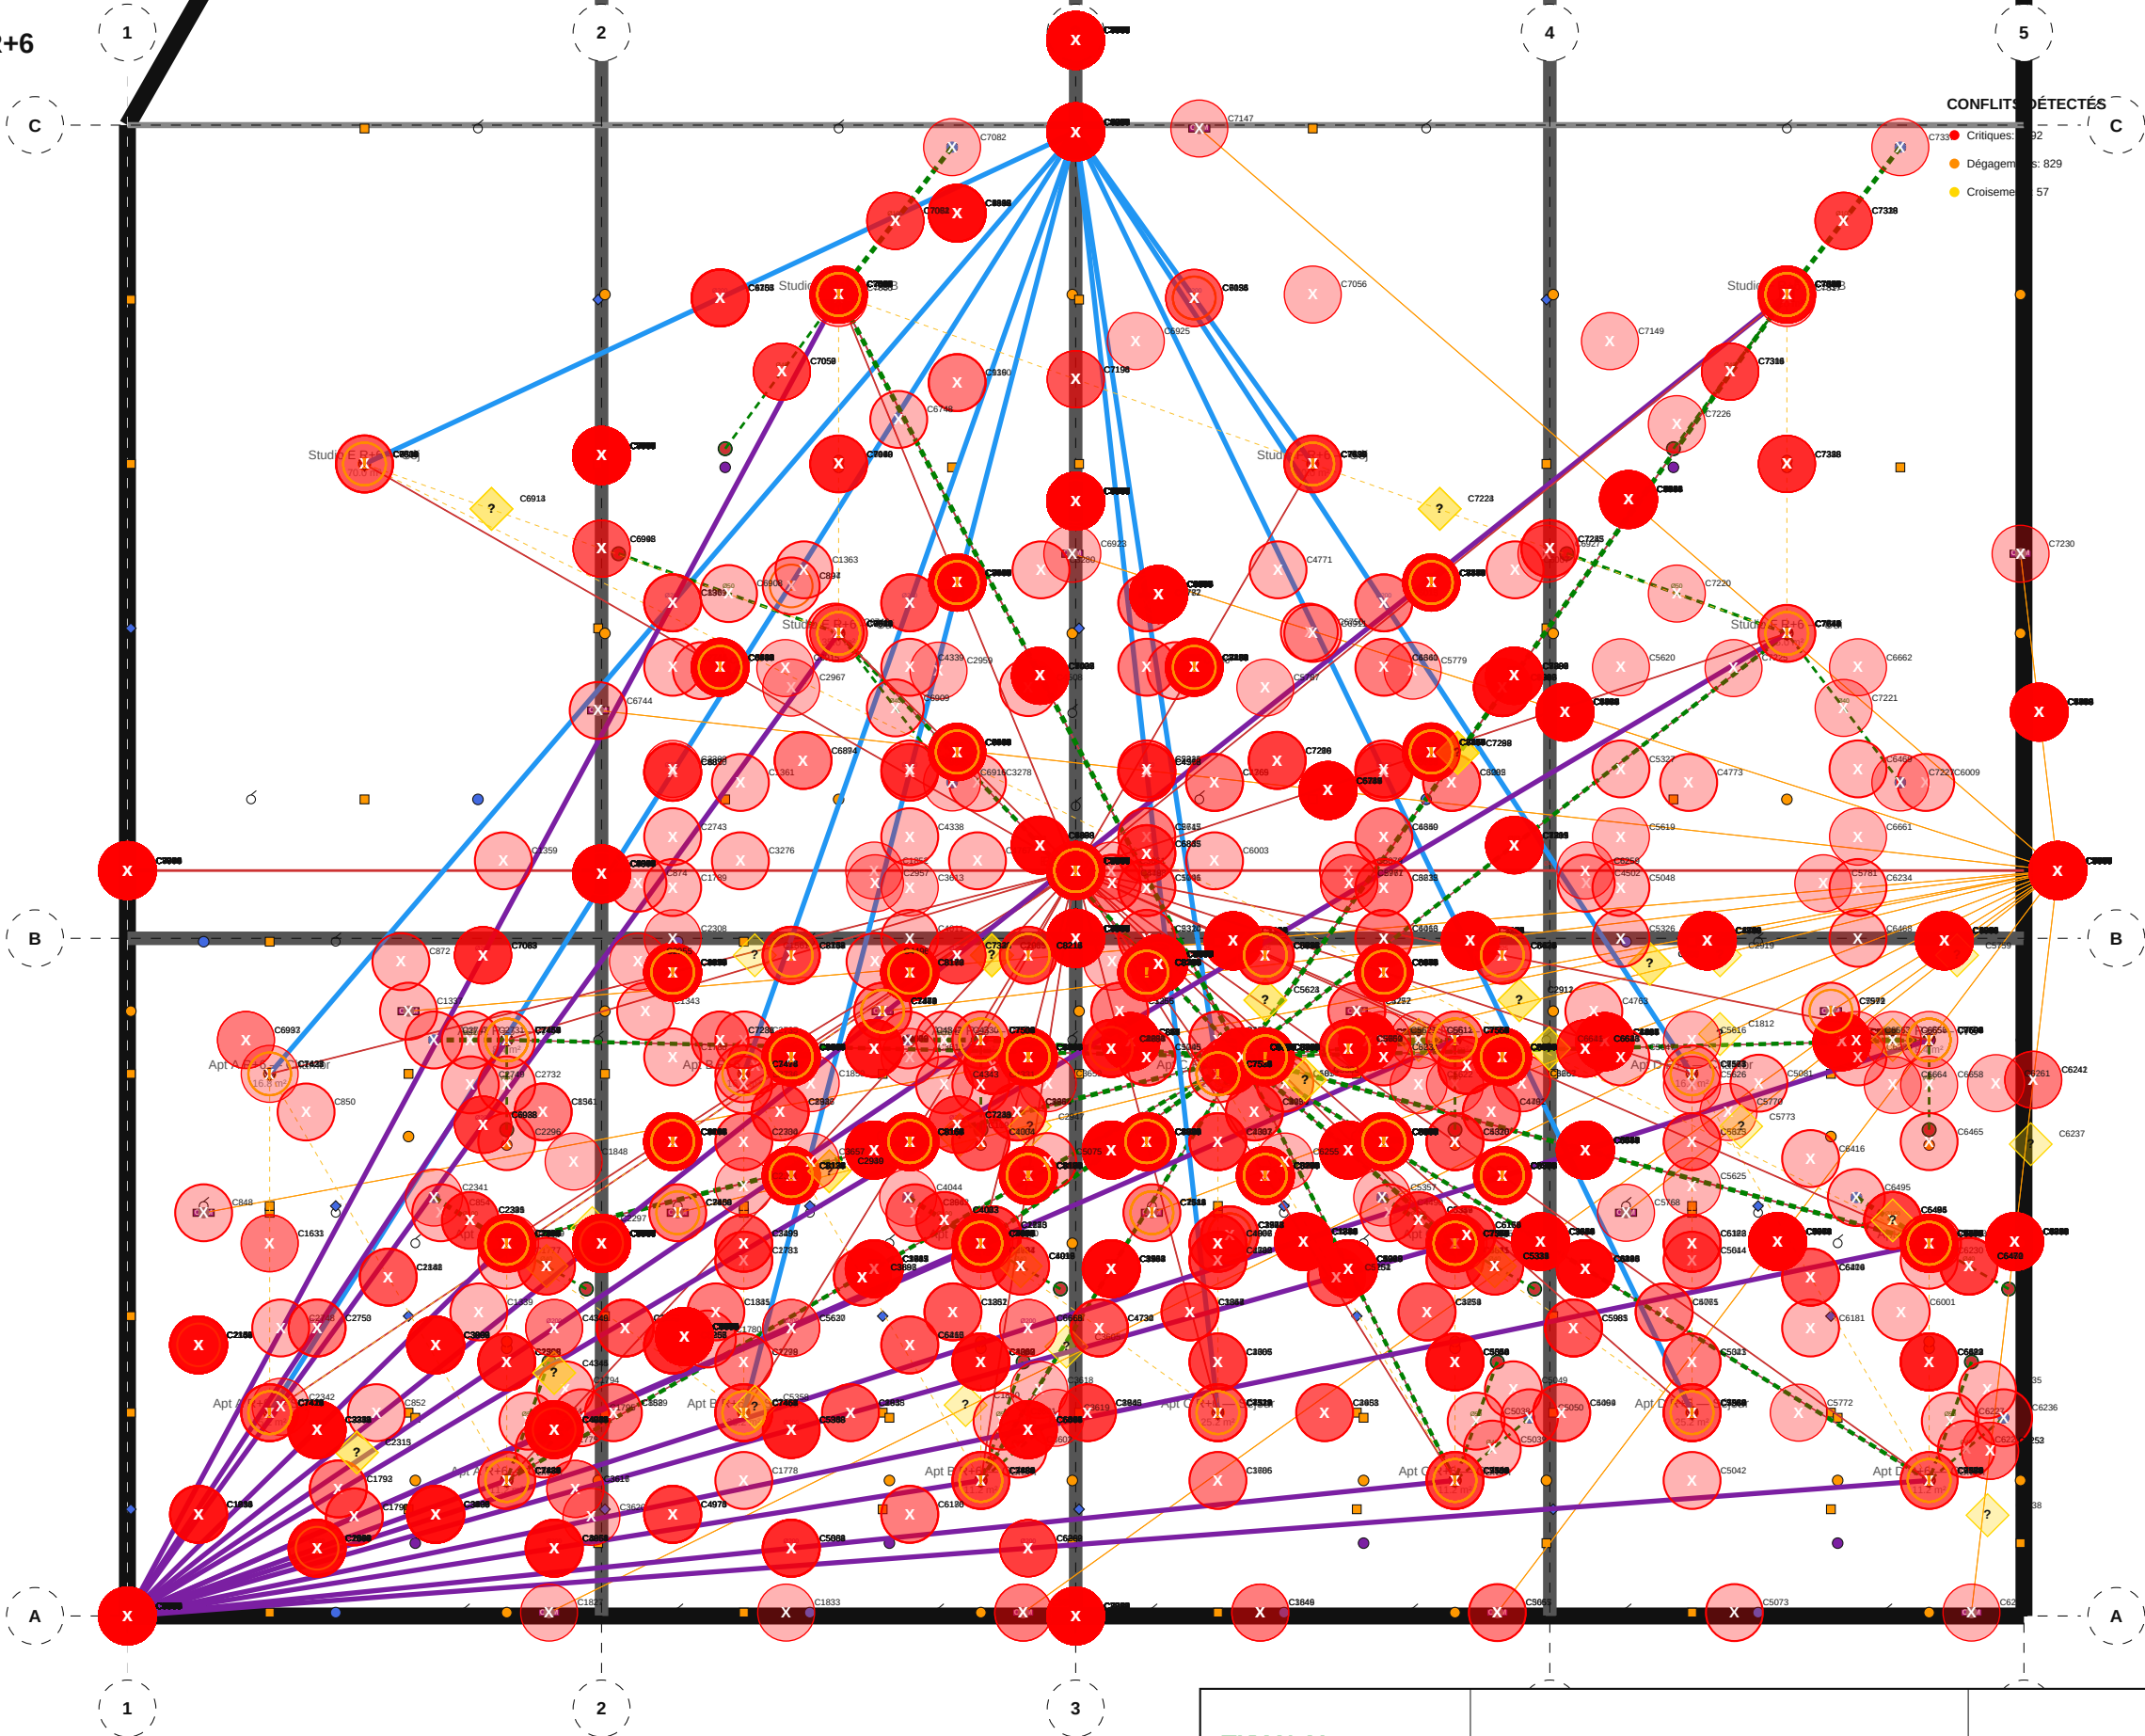

TIJAN AI

Bureau d'Études Automatisé

Résidence Papa Oumar Sakho

Dakar, Senegal

Éch: 1/100

Pl. 130/133

001 SYN — Synthèse — R+6

Date: 06/05/2026

Réf: 1711

BIM vSYN-130

Phase: APD


001 SYN — Synthèse — R+7

LÉGENDE RÉSEAUX

- EF — Eau Froide
- EC — Eau Chaude
- EU — Eaux Usées
- CLIM — Réfrigérant
- VMC — Extraction
- HCU — Courants Forts
- LCU — Courants Faibles
- SPK — Sprinkler

CONFLITS DÉTECTÉS

- Critiques: 77
- Dégagements: 837
- Croisements: 63

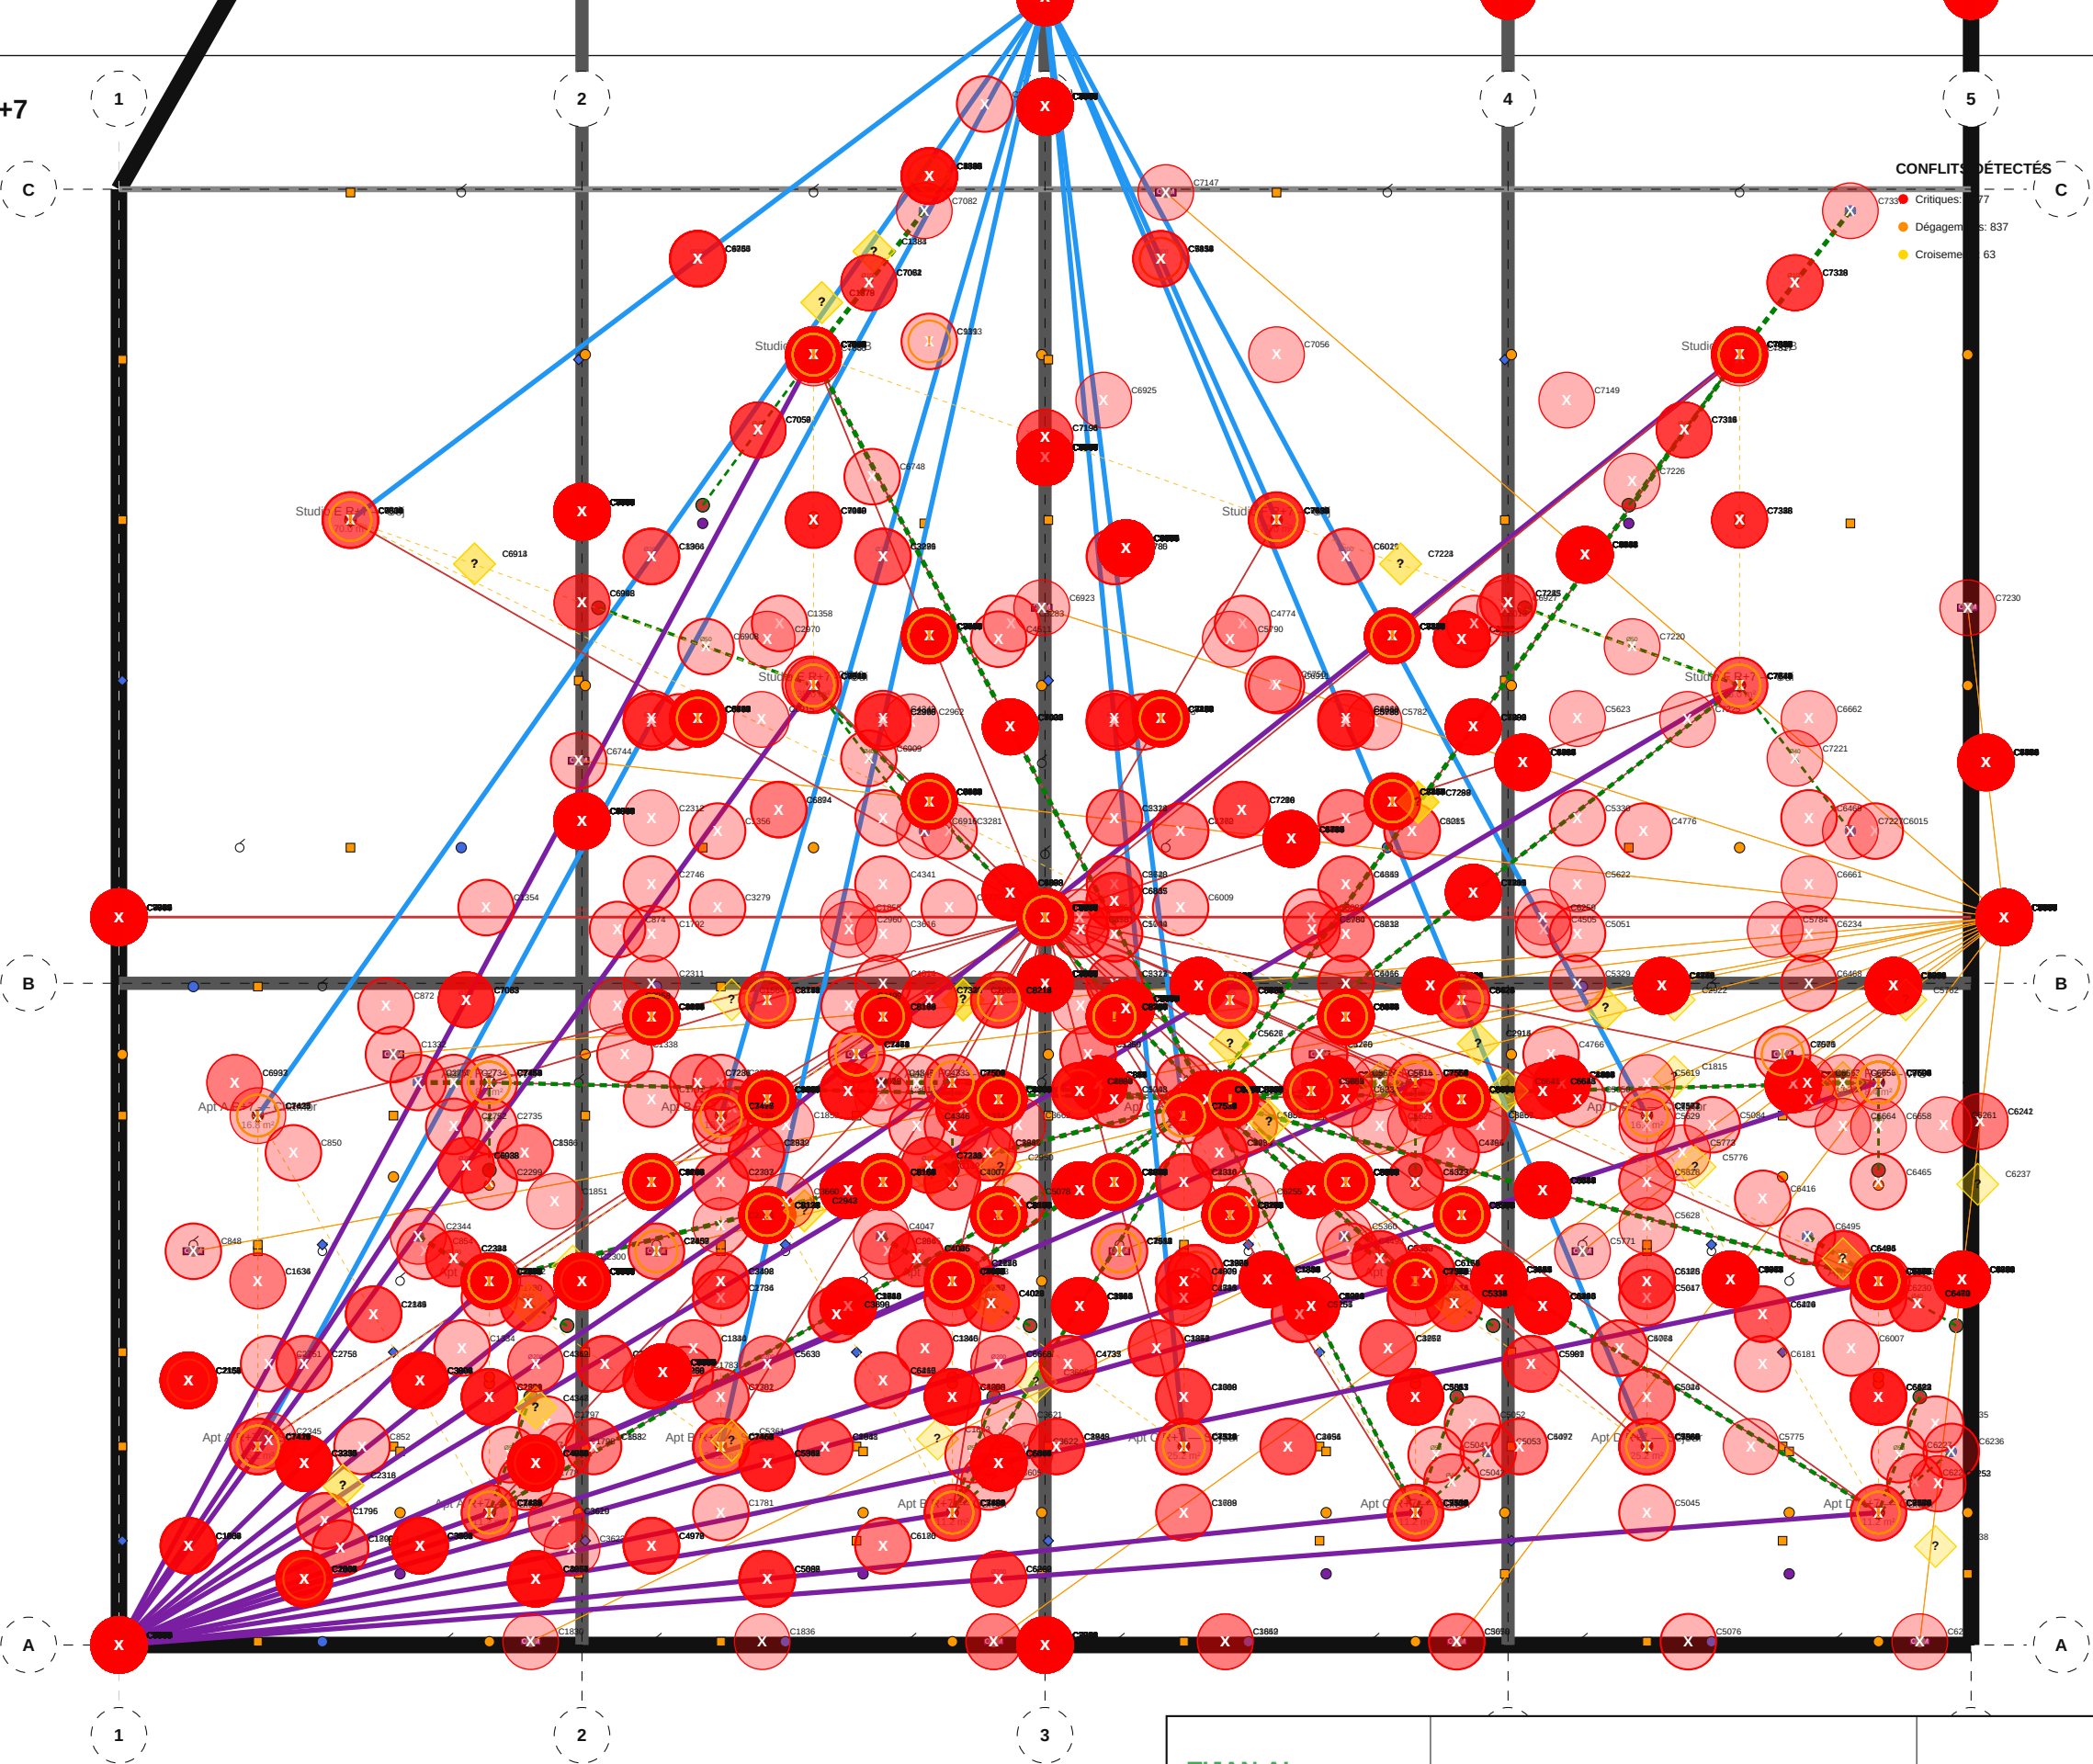

TIJAN AI

Bureau d'Études Automatisé

Résidence Papa Oumar Sakho

Dakar, Senegal

Éch: 1/100

Pl. 131/133

001 SYN — Synthèse — R+7

Date: 06/05/2026

Réf: 1711

BIM vSYN-131

Phase: APD


001 SYN — Synthèse — R+8 Terrasse

LÉGENDE RÉSEAUX

-  EF — Eau Froide
-  EC — Eau Chaude
-  EU — Eaux Usées
-  CLIM — Réfrigérant
-  VMC — Extraction
-  HCU — Courants Forts
-  LCU — Courants Faibles
-  SPK — Sprinkler

CONFLITS DÉTECTÉS

- Critiques: 32
- Dégagements: 1
- Croisements: 0

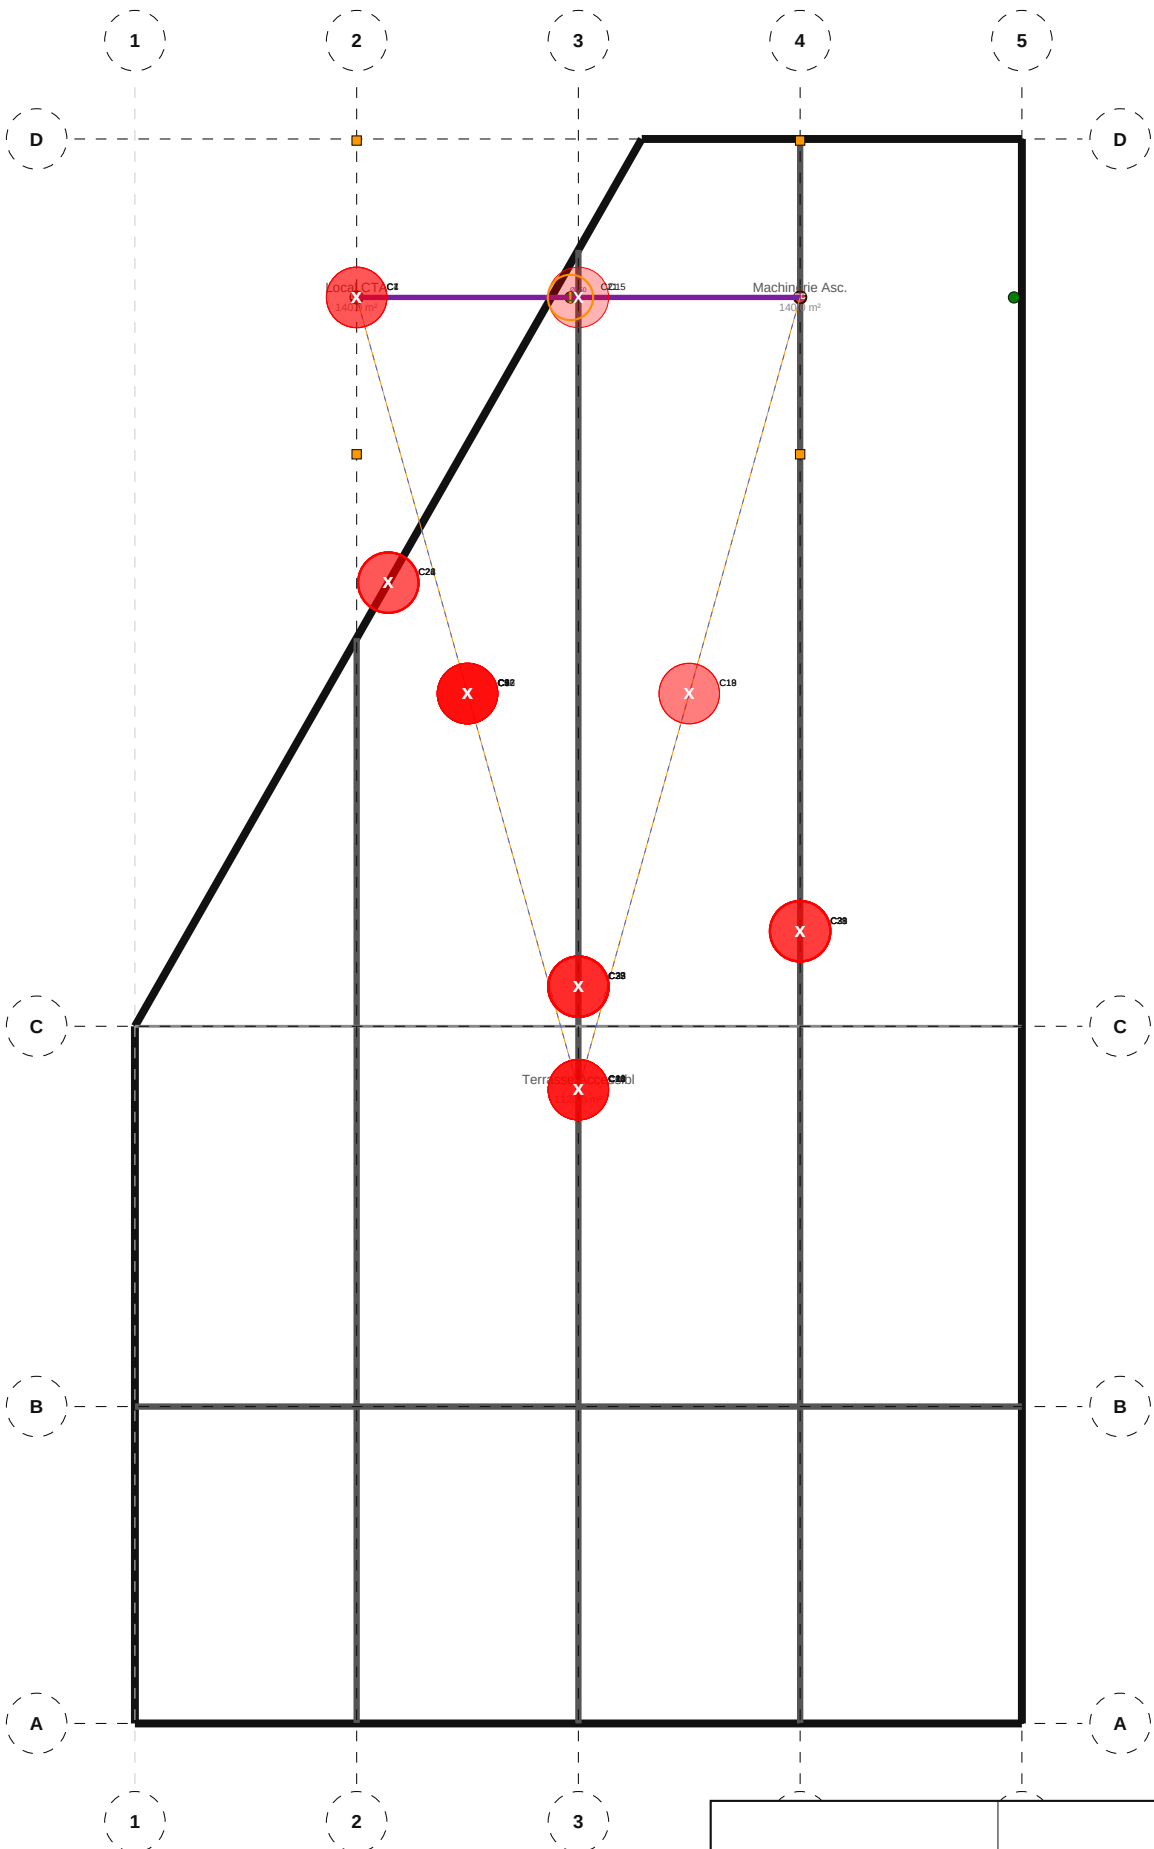

TIJAN AI Bureau d'Études Automatisé		Résidence Papa Oumar Sakho Dakar, Senegal	Éch: 1/100 Pl. 132/133
		001 SYN — Synthèse — R+8 Terrasse	
Date: 06/05/2026	Réf: 1711	BIM vSYN-132 Phase: APD	

RAPPORT DE COORDINATION — DÉTECTION DES CONFLITS

Total des conflits: 59613

Critiques (à corriger): 53324

Dégagements insuffisants: 5859

Croisements (à vérifier): 430

#	Sévérité	Niveau	Pièce	Élément A	Élément B	Distance	Requis	Description
C1	HARD	Sous-Sol	Local CTA SS	VMC Extraction Ø150m	VMC Extraction Ø100m	-125mm	100mm	Intersection physique entre VMC Extraction Ø1
C2	HARD	Sous-Sol	Local CTA SS	VMC Extraction Ø150m	Courant Fort Ø2mm	-76mm	150mm	Intersection physique entre VMC Extraction Ø1
C3	HARD	Sous-Sol	Local CTA SS	VMC Extraction Ø150m	Courant Faible Ø1mm	-76mm	150mm	Intersection physique entre VMC Extraction Ø1
C4	HARD	Sous-Sol	Local CTA SS	VMC Extraction Ø100m	Courant Fort Ø2mm	-51mm	150mm	Intersection physique entre VMC Extraction Ø1
C5	HARD	Sous-Sol	Local CTA SS	VMC Extraction Ø100m	Courant Faible Ø1mm	-50mm	150mm	Intersection physique entre VMC Extraction Ø1
C6	HARD	Sous-Sol	Local CTA SS	Courant Fort Ø2mm	Courant Faible Ø1mm	-2mm	30mm	Intersection physique entre Courant Fort Ø2mm
C7	HARD	Sous-Sol	Local CTA SS	Courant Fort Ø2mm	Courant Fort Ø2mm	-2mm	30mm	Intersection physique entre Courant Fort Ø2mm
C8	HARD	Sous-Sol	Local CTA SS	Courant Faible Ø1mm	Courant Fort Ø2mm	-2mm	30mm	Intersection physique entre Courant Faible Ø1
C9	HARD	Sous-Sol	—	Courant Fort Ø2mm	Mur facade (32.2m)	0mm	0mm	Courant Fort Ø2mm traverse un mur facade sans
C10	HARD	Sous-Sol	—	Courant Fort Ø2mm	Mur porteur (46.5m)	0mm	0mm	Courant Fort Ø2mm traverse un mur porteur san
C11	HARD	Sous-Sol	—	Courant Faible Ø1mm	Mur facade (32.2m)	0mm	0mm	Courant Faible Ø1mm traverse un mur facade sa
C12	HARD	Sous-Sol	—	Courant Faible Ø1mm	Mur porteur (46.5m)	0mm	0mm	Courant Faible Ø1mm traverse un mur porteur s
C13	HARD	Sous-Sol	—	Courant Fort Ø2mm	Mur porteur (46.5m)	0mm	0mm	Courant Fort Ø2mm traverse un mur porteur san
C14	HARD	Sous-Sol	—	Courant Fort Ø2mm	Mur porteur (50.0m)	0mm	0mm	Courant Fort Ø2mm traverse un mur porteur san
C15	HARD	RDC	—	Sprinkler Ø65mm	Sprinkler Ø40mm	-52mm	100mm	Intersection physique entre Sprinkler Ø65mm e
C16	HARD	RDC	—	Sprinkler Ø65mm	Sprinkler Ø40mm	-52mm	100mm	Intersection physique entre Sprinkler Ø65mm e
C17	HARD	RDC	Local Techni	Sprinkler Ø65mm	Détection Incendie Ø	-33mm	100mm	Intersection physique entre Sprinkler Ø65mm e
C18	HARD	RDC	Loge Gardien	Sprinkler Ø65mm	Sprinkler Ø25mm	-45mm	100mm	Intersection physique entre Sprinkler Ø65mm e
C19	HARD	RDC	Couloir RDC	Sprinkler Ø65mm	Sprinkler Ø25mm	-45mm	100mm	Intersection physique entre Sprinkler Ø65mm e
C20	HARD	RDC	—	Sprinkler Ø40mm	Sprinkler Ø40mm	-40mm	100mm	Intersection physique entre Sprinkler Ø40mm e
C21	HARD	RDC	Local Techni	Sprinkler Ø40mm	Détection Incendie Ø	-21mm	100mm	Intersection physique entre Sprinkler Ø40mm e
C22	HARD	RDC	Loge Gardien	Sprinkler Ø40mm	Sprinkler Ø25mm	-32mm	100mm	Intersection physique entre Sprinkler Ø40mm e
C23	HARD	RDC	Couloir RDC	Sprinkler Ø40mm	Courant Fort Ø2mm	-21mm	150mm	Intersection physique entre Sprinkler Ø40mm e
C24	HARD	RDC	Couloir RDC	Sprinkler Ø40mm	Courant Faible Ø1mm	-20mm	150mm	Intersection physique entre Sprinkler Ø40mm e
C25	HARD	RDC	Couloir RDC	Sprinkler Ø40mm	Sprinkler Ø25mm	-32mm	100mm	Intersection physique entre Sprinkler Ø40mm e
C26	HARD	RDC	Local Techni	Sprinkler Ø40mm	Courant Fort Ø2mm	-21mm	150mm	Intersection physique entre Sprinkler Ø40mm e
C27	HARD	RDC	Local Techni	Sprinkler Ø40mm	Courant Faible Ø1mm	-20mm	150mm	Intersection physique entre Sprinkler Ø40mm e
C28	HARD	RDC	Local Techni	Sprinkler Ø40mm	Détection Incendie Ø	-21mm	100mm	Intersection physique entre Sprinkler Ø40mm e
C29	HARD	RDC	Loge Gardien	Sprinkler Ø40mm	Courant Fort Ø2mm	-21mm	150mm	Intersection physique entre Sprinkler Ø40mm e
C30	HARD	RDC	Loge Gardien	Sprinkler Ø40mm	Courant Faible Ø1mm	-20mm	150mm	Intersection physique entre Sprinkler Ø40mm e
C31	HARD	RDC	Loge Gardien	Sprinkler Ø40mm	Sprinkler Ø25mm	-32mm	100mm	Intersection physique entre Sprinkler Ø40mm e
C32	HARD	RDC	Couloir RDC	Sprinkler Ø40mm	Sprinkler Ø25mm	-32mm	100mm	Intersection physique entre Sprinkler Ø40mm e
C33	HARD	RDC	Local Techni	VMC Extraction Ø150m	VMC Extraction Ø100m	-125mm	100mm	Intersection physique entre VMC Extraction Ø1
C34	HARD	RDC	Local Techni	VMC Extraction Ø150m	Courant Fort Ø2mm	-76mm	150mm	Intersection physique entre VMC Extraction Ø1
C35	HARD	RDC	Local Techni	VMC Extraction Ø150m	Courant Faible Ø1mm	-76mm	150mm	Intersection physique entre VMC Extraction Ø1
C36	HARD	RDC	Local Techni	VMC Extraction Ø150m	Détection Incendie Ø	-76mm	200mm	Intersection physique entre VMC Extraction Ø1
C37	HARD	RDC	Local Techni	VMC Extraction Ø150m	Détection Incendie Ø	-76mm	200mm	Intersection physique entre VMC Extraction Ø1
C38	HARD	RDC	Local Techni	VMC Extraction Ø100m	Courant Fort Ø2mm	-51mm	150mm	Intersection physique entre VMC Extraction Ø1
C39	HARD	RDC	Local Techni	VMC Extraction Ø100m	Courant Faible Ø1mm	-50mm	150mm	Intersection physique entre VMC Extraction Ø1
C40	HARD	RDC	Local Techni	VMC Extraction Ø100m	Détection Incendie Ø	-51mm	200mm	Intersection physique entre VMC Extraction Ø1

... et 59573 conflits supplémentaires

TIJAN AI Bureau d'Études Automatisé	Résidence Papa Oumar Sakho Dakar, Senegal	Éch: 1/100 Pl. 133/133
	Rapport de Coordination	
Date: 06/05/2026	Réf: 1711	BIM vSYN-133 Phase: APD